





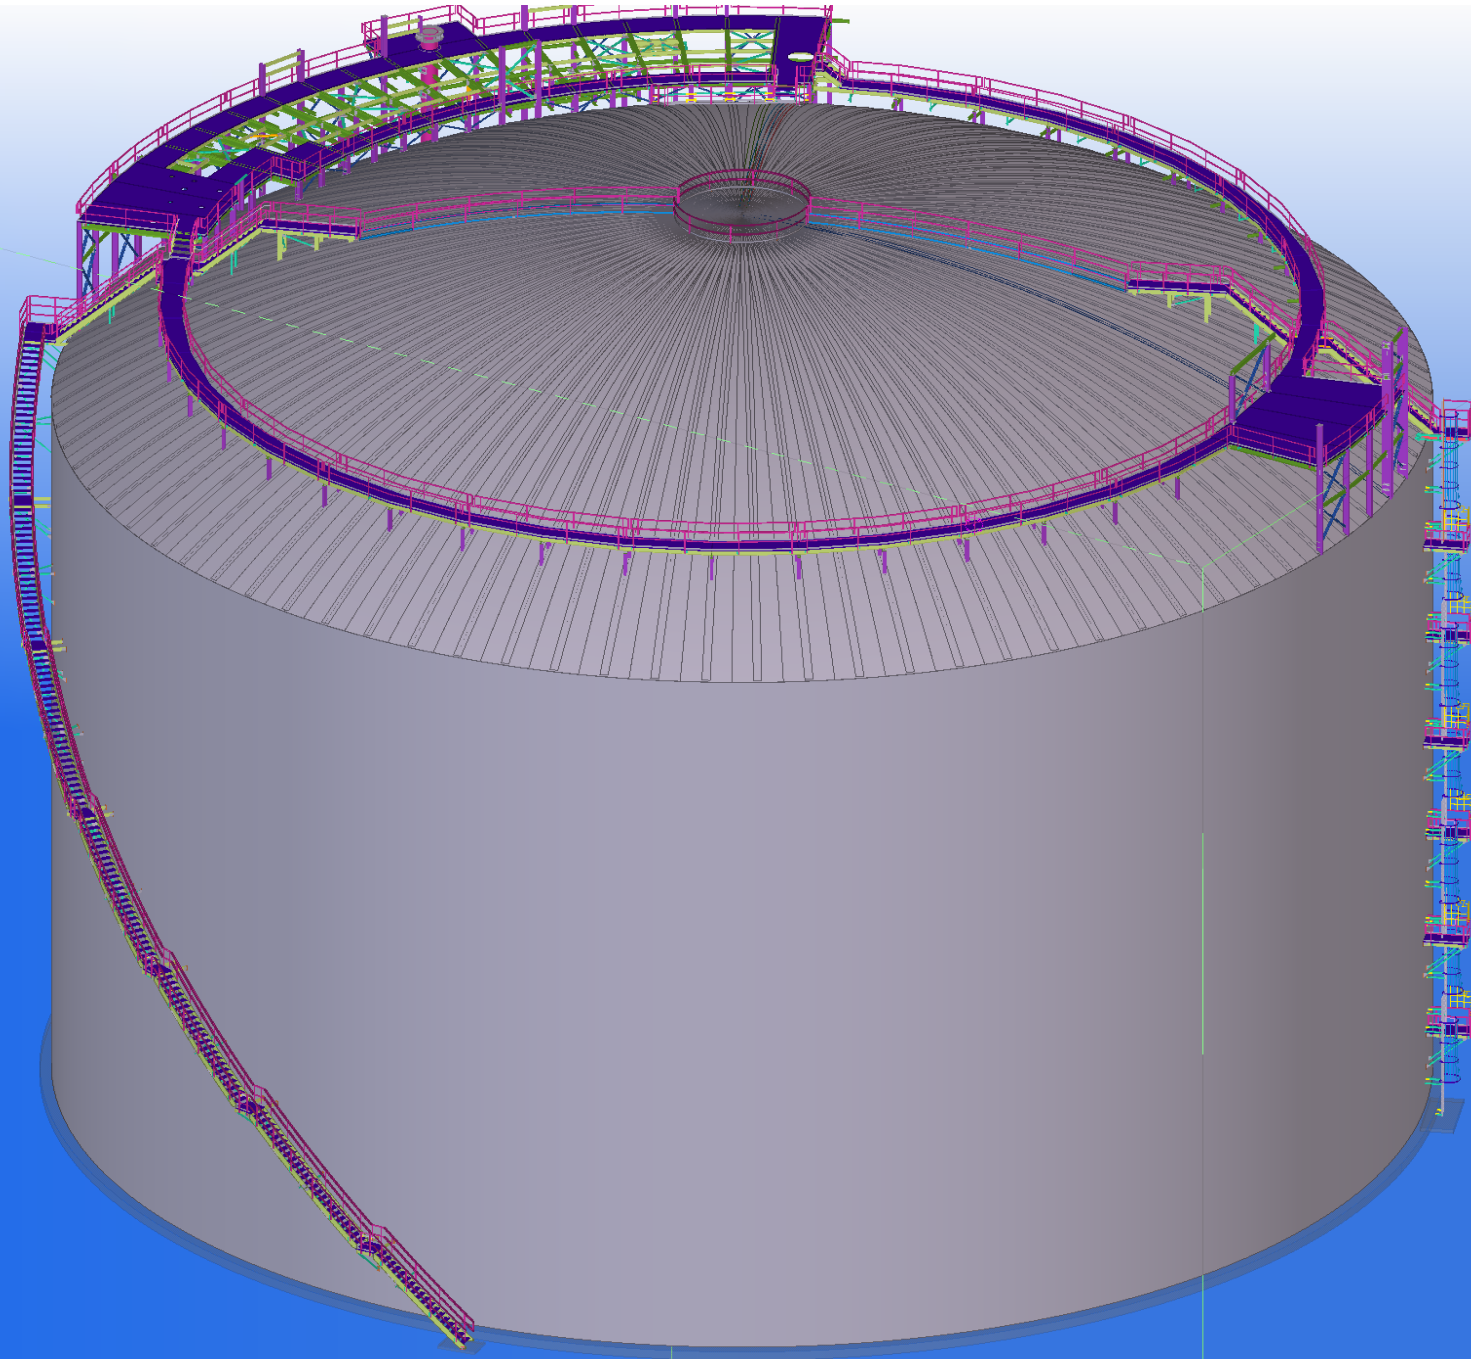

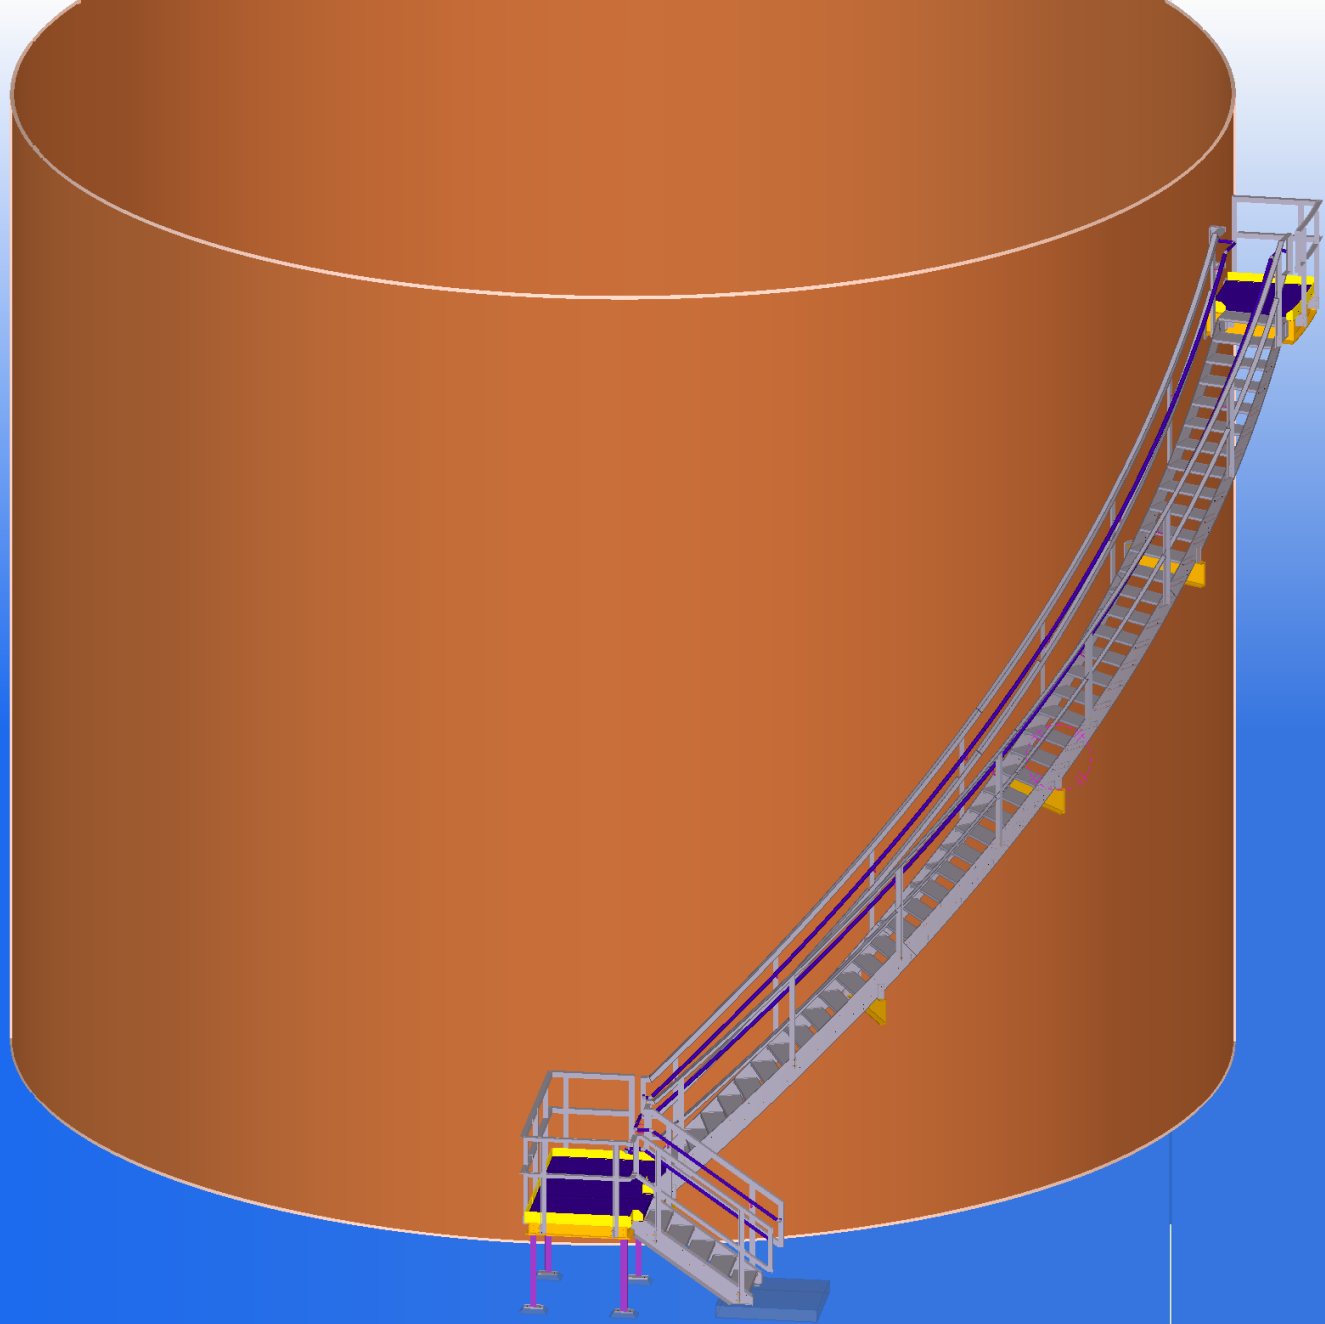

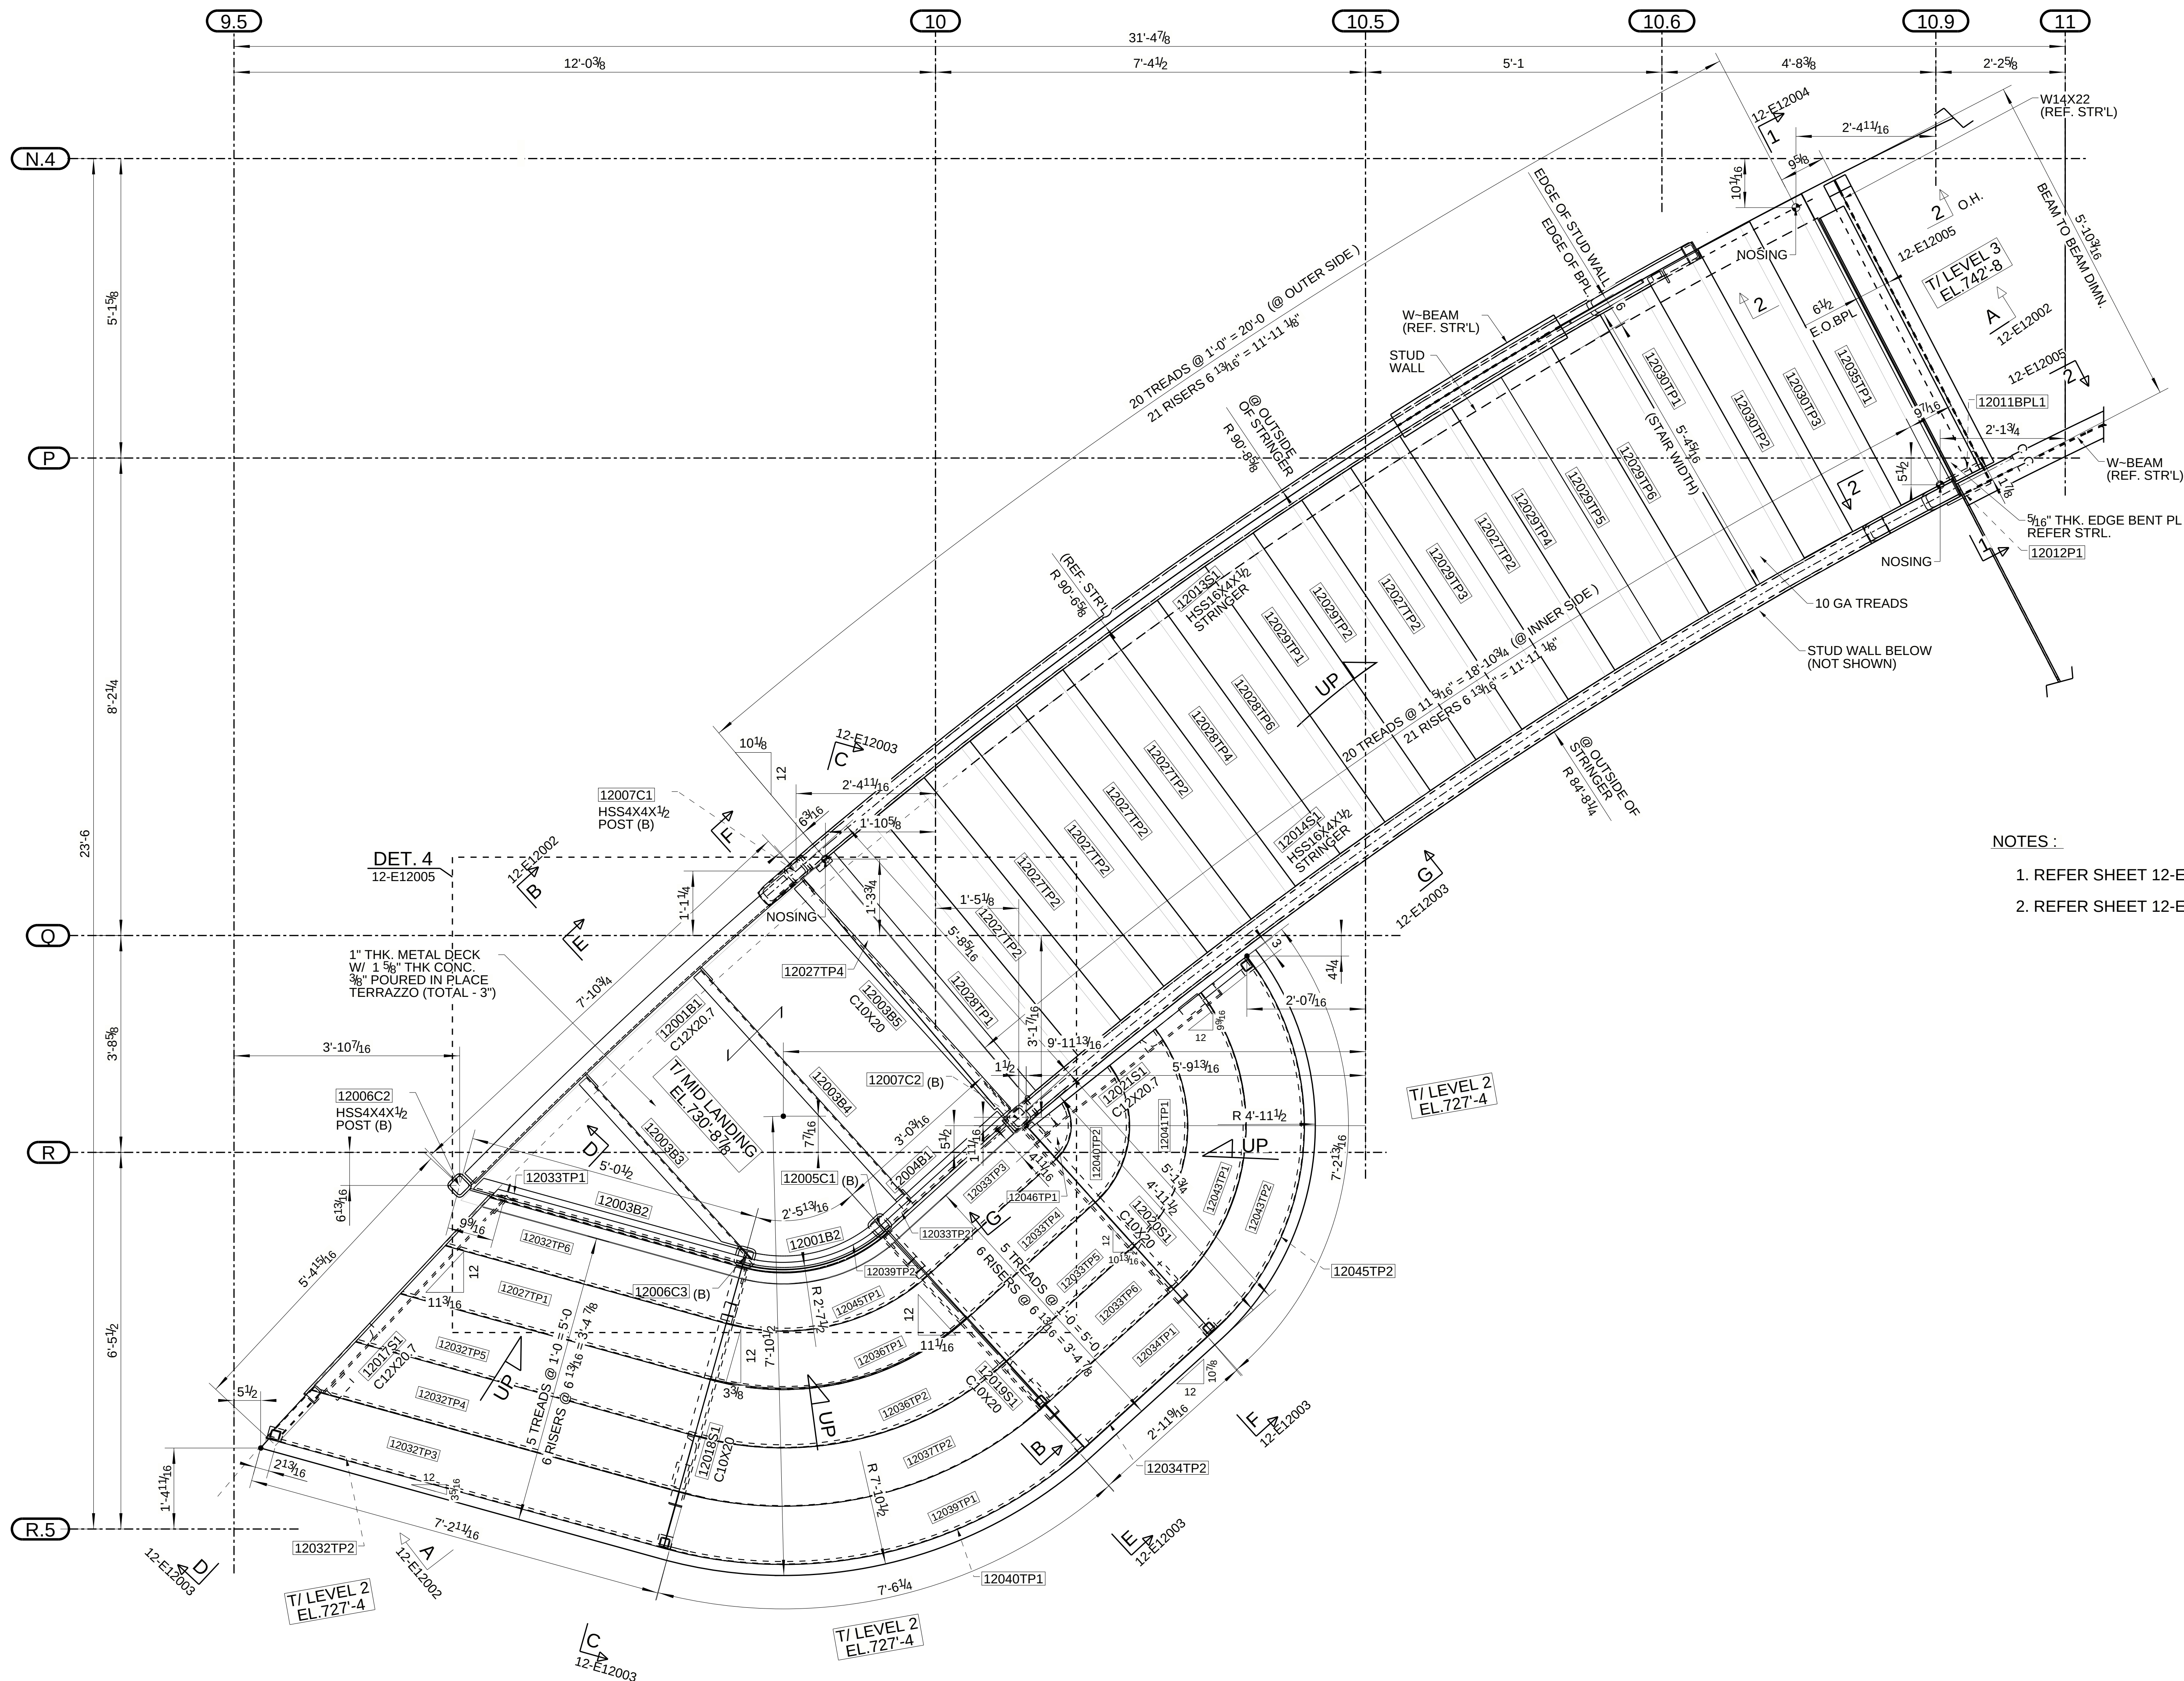

FRAMING PLAN FOR COMMON STAIR @ 2ND FLOOR (NORTH SIDE)
(REFER : COMMON STAIR - ENLARGED PLAN - A13/A7.01)

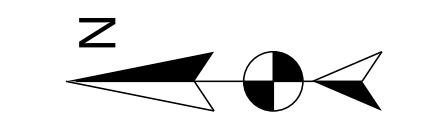


PROJECT NORTH

NOTES :

1. REFER SHEET 12-E12000 FOR GENERAL NOTES & 3D-VIEW.
2. REFER SHEET 12-E12002 TO 12-E12005 FOR ELEVATIONS.

FOR FIELD USE : 03/17/2021

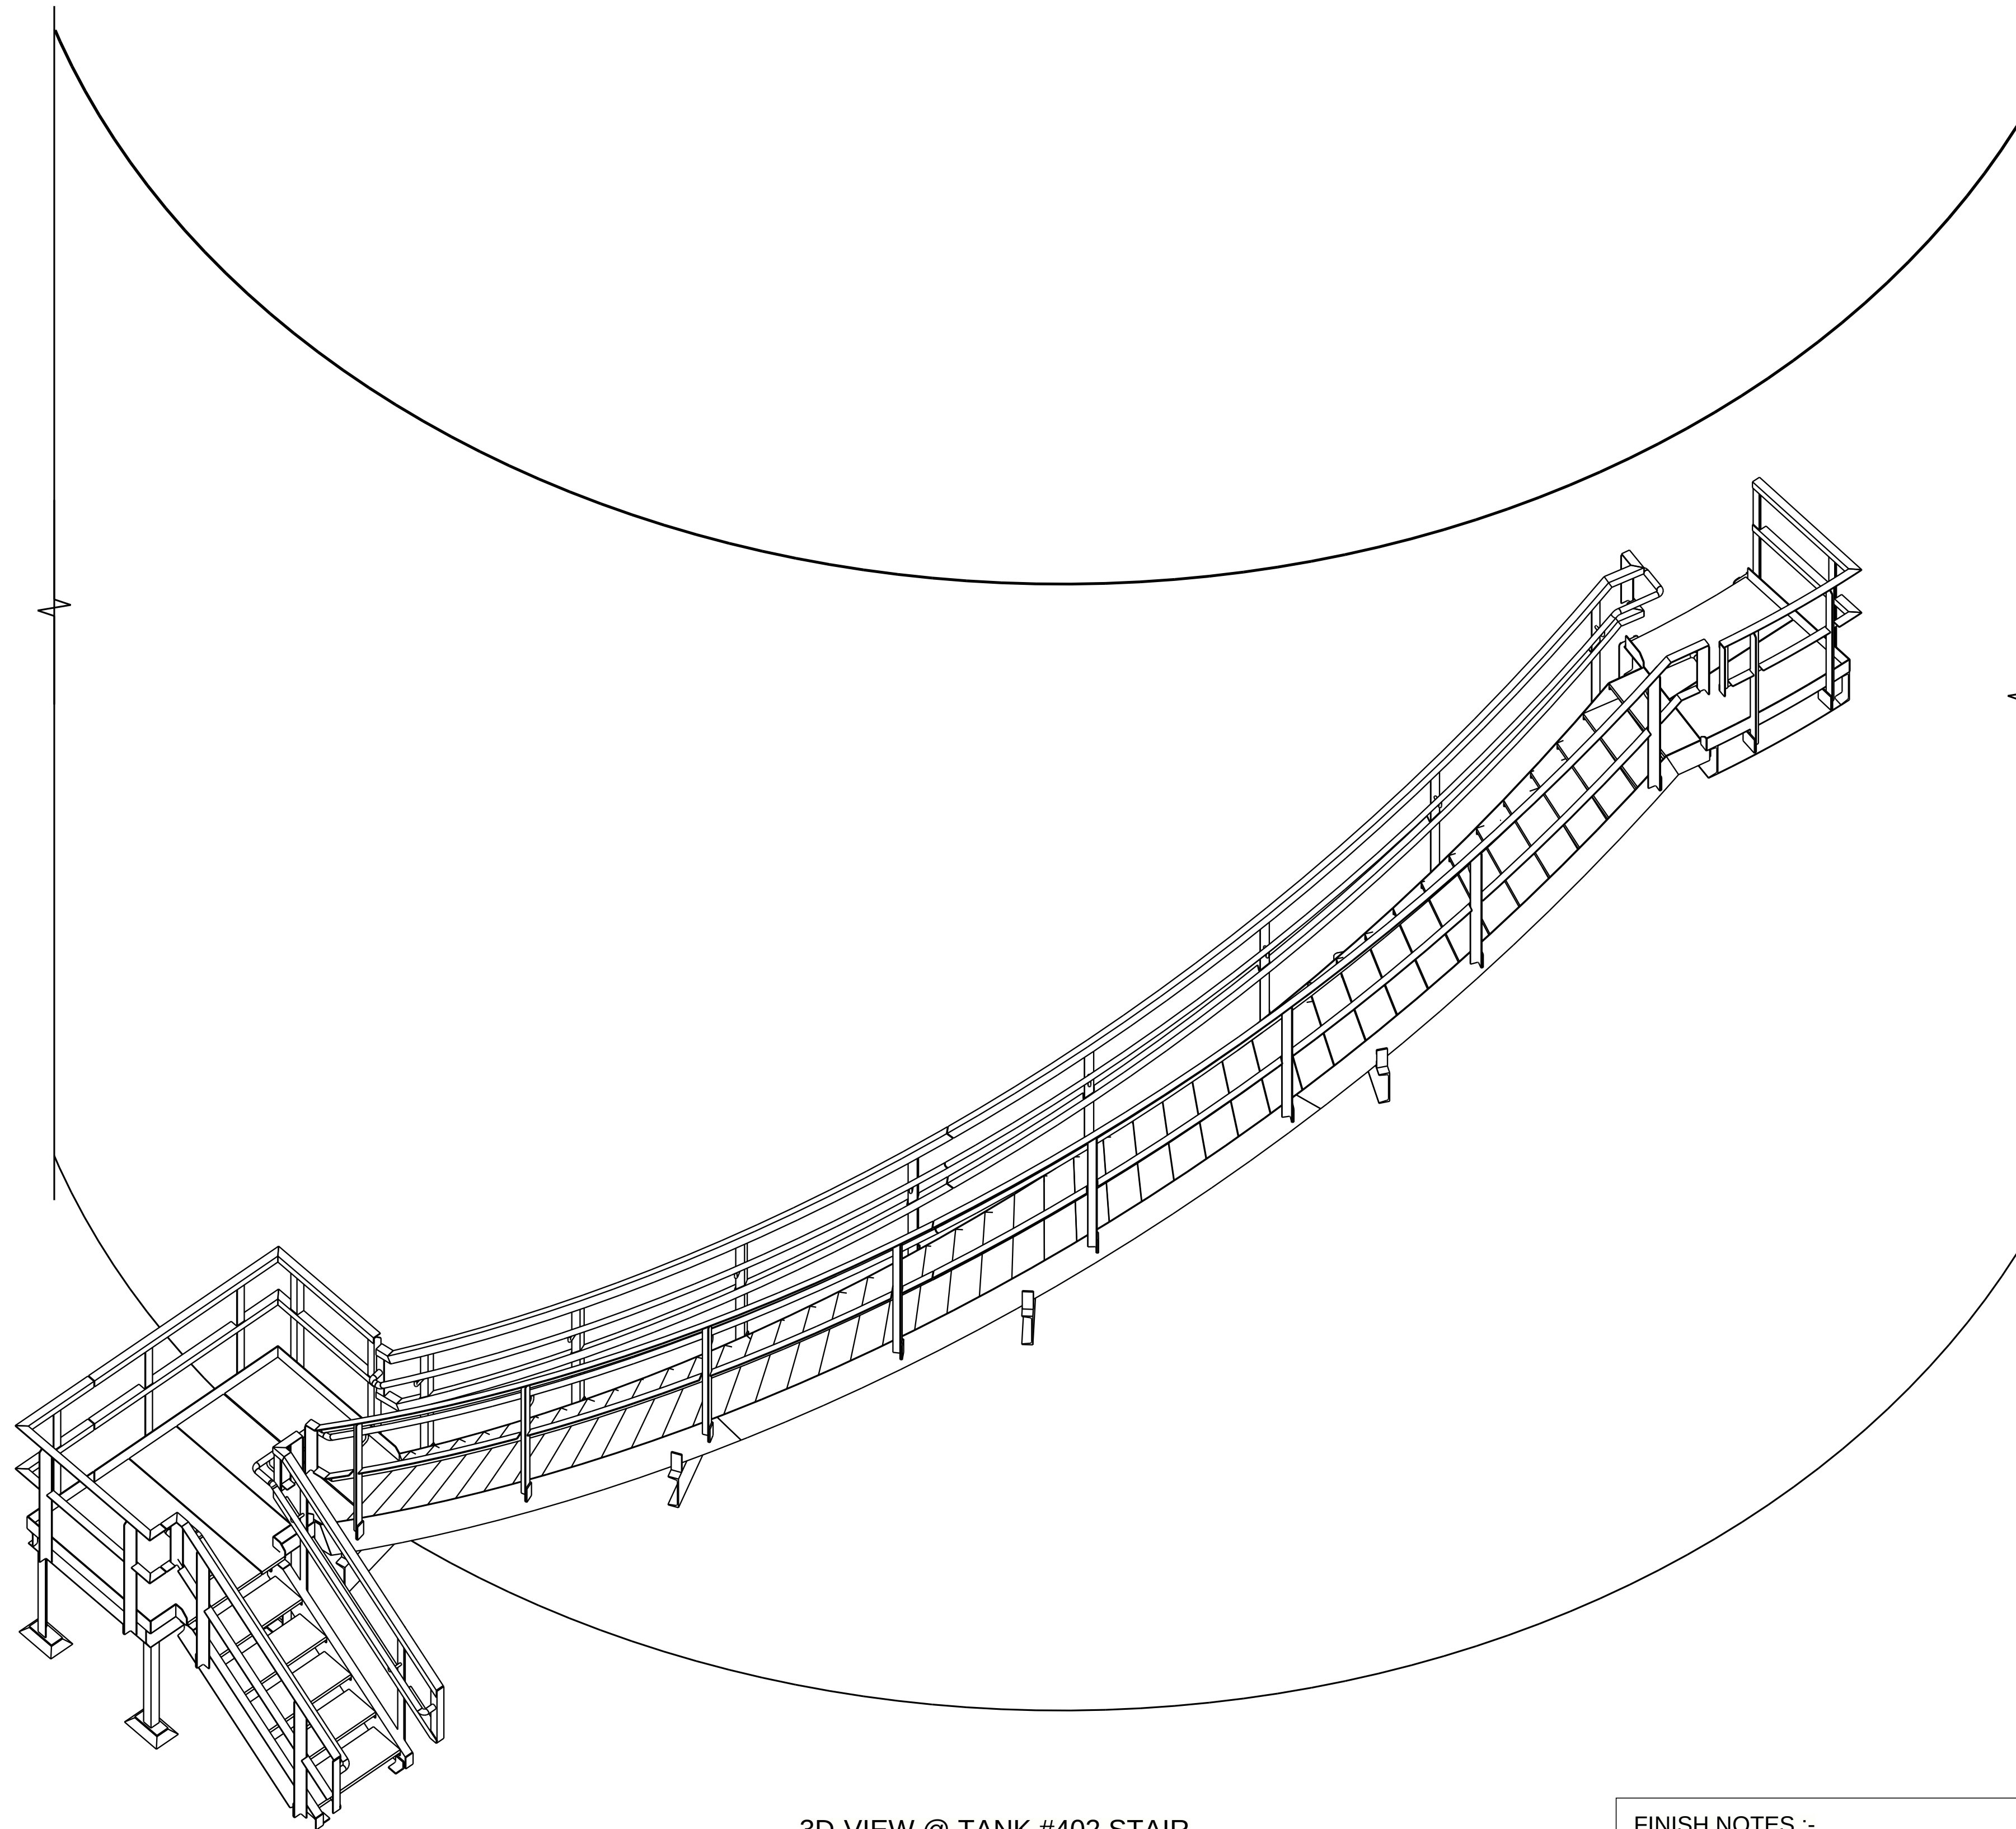


3D-VIEW @ TANK #402 STAIR


FINISH NOTES :-
ALL TANK #402 STAIR STEEL MEMBERS TO BE HOT DIP GALVANIZED.
SURFACE PREPARATION : SSPC-SP6/NACE 3


LANDING GRATING :
LANDING GRATING TO BE HOT-DIP GALVANIZED SERRATED WELDED GRATING
1 1/4" X 3/16" BEARING BARS SPACING @ 1 3/16" O.C. AND CROSS BARS
SPACING @ 4" O.C.


TREAD GRATING :
GRATING TREADS TO BE HOT-DIP GALVANIZED SERRATED WELDED GRATING
1 1/4" X 3/16" BEARING BARS SPACING @ 1 3/16" O.C. AND CROSS BARS
SPACING @ 4" O.C. W/ ABRASIVE NOSING.

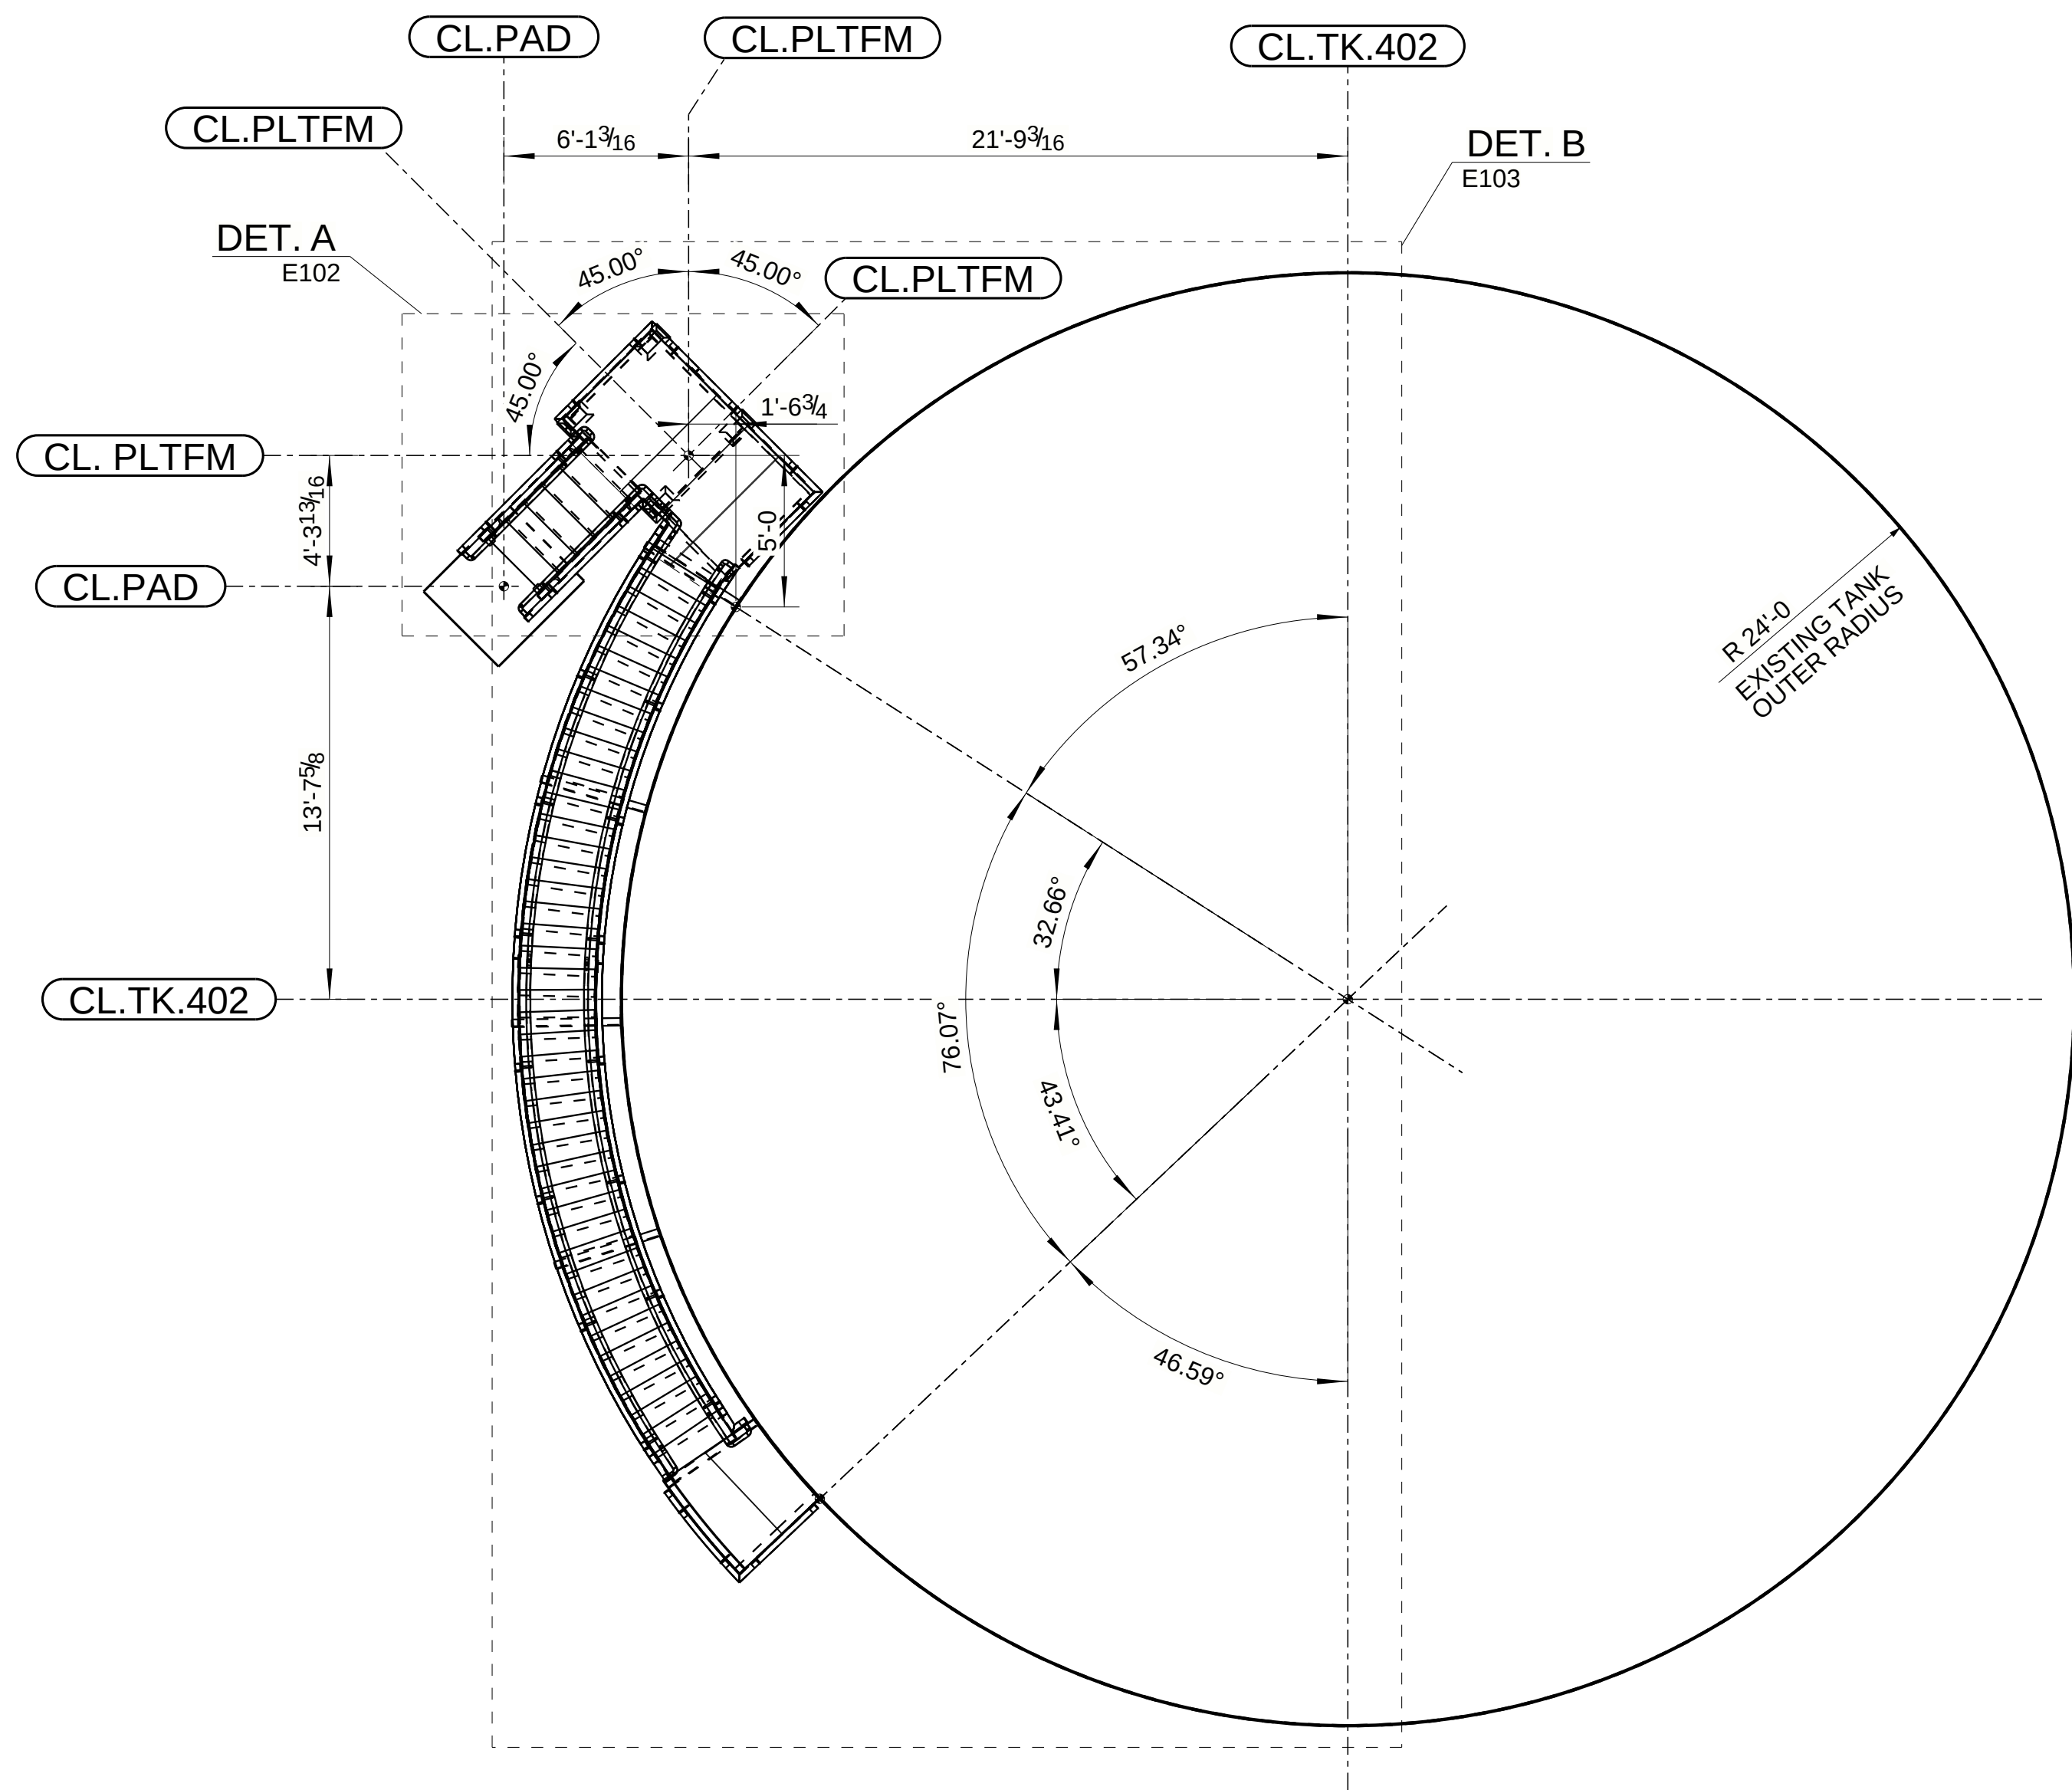

TK 402 STAIR LOCATION PLAN
(REFER : TK 402 STAIR LOCATION PLAN / D-400-3003-21)

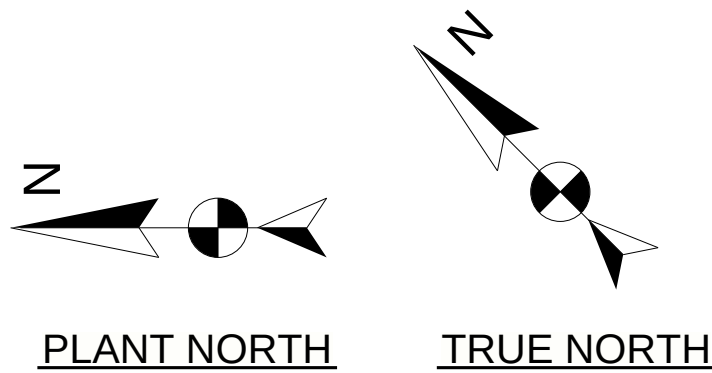


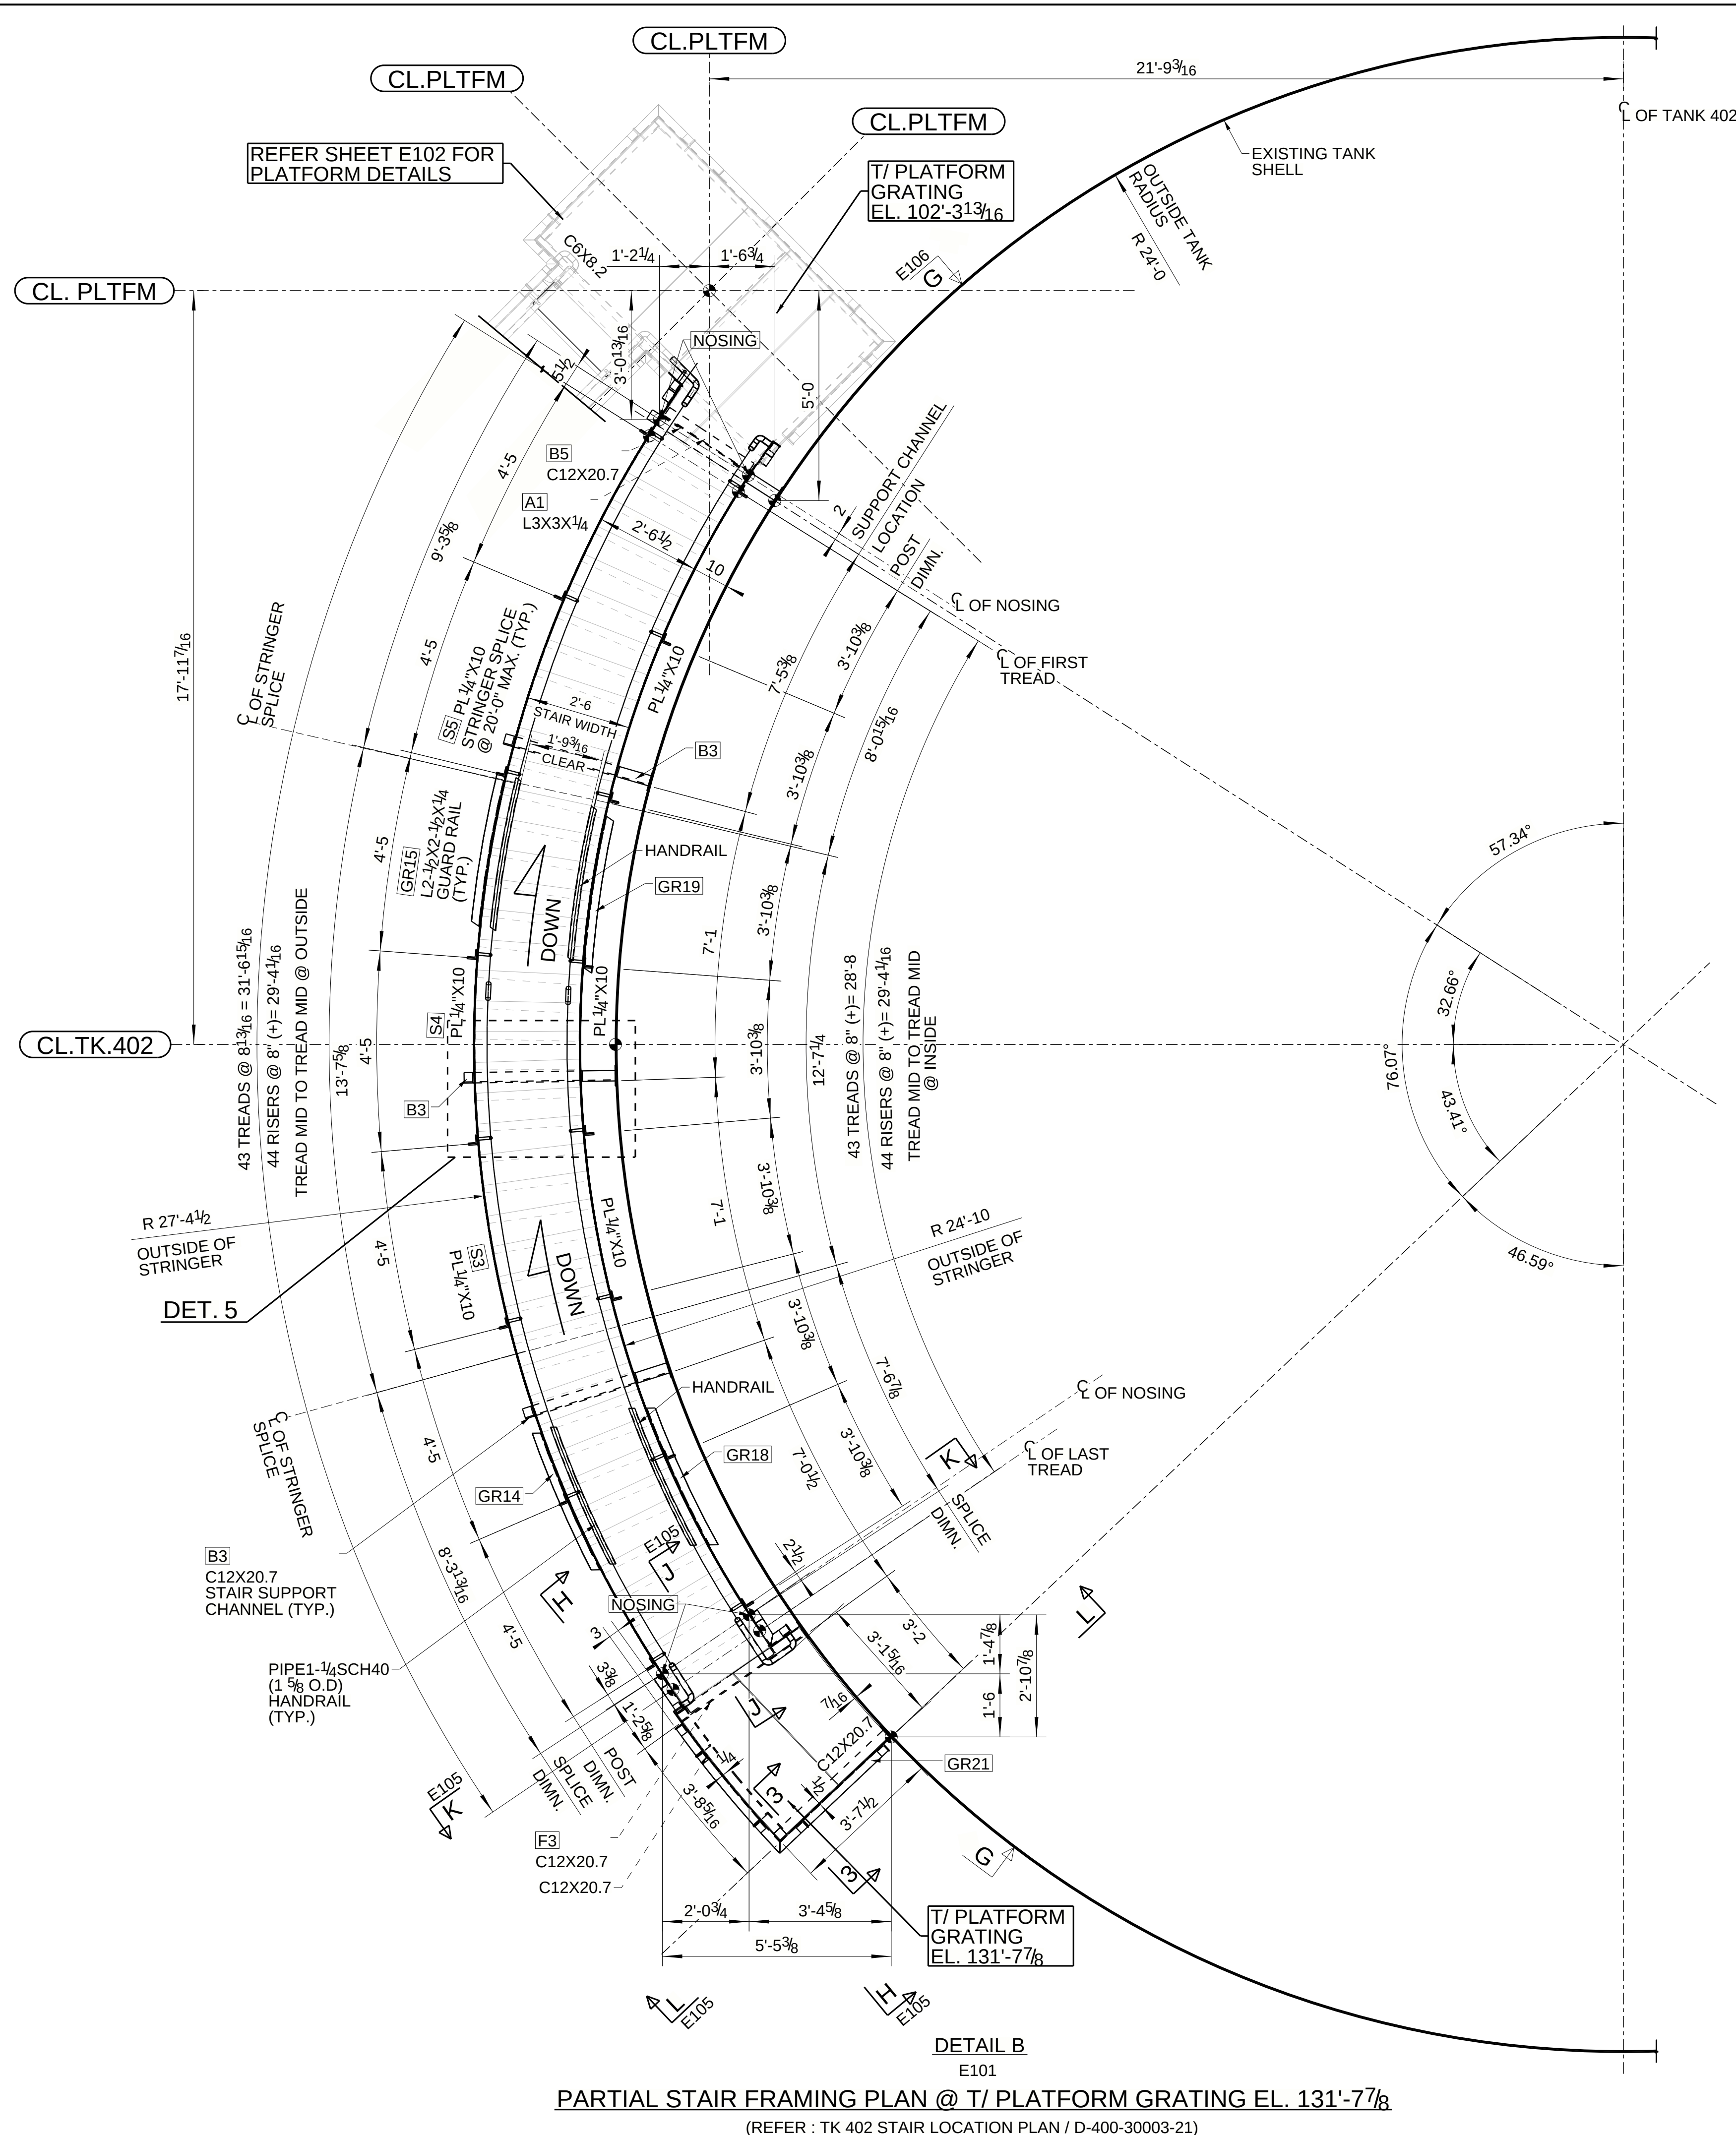

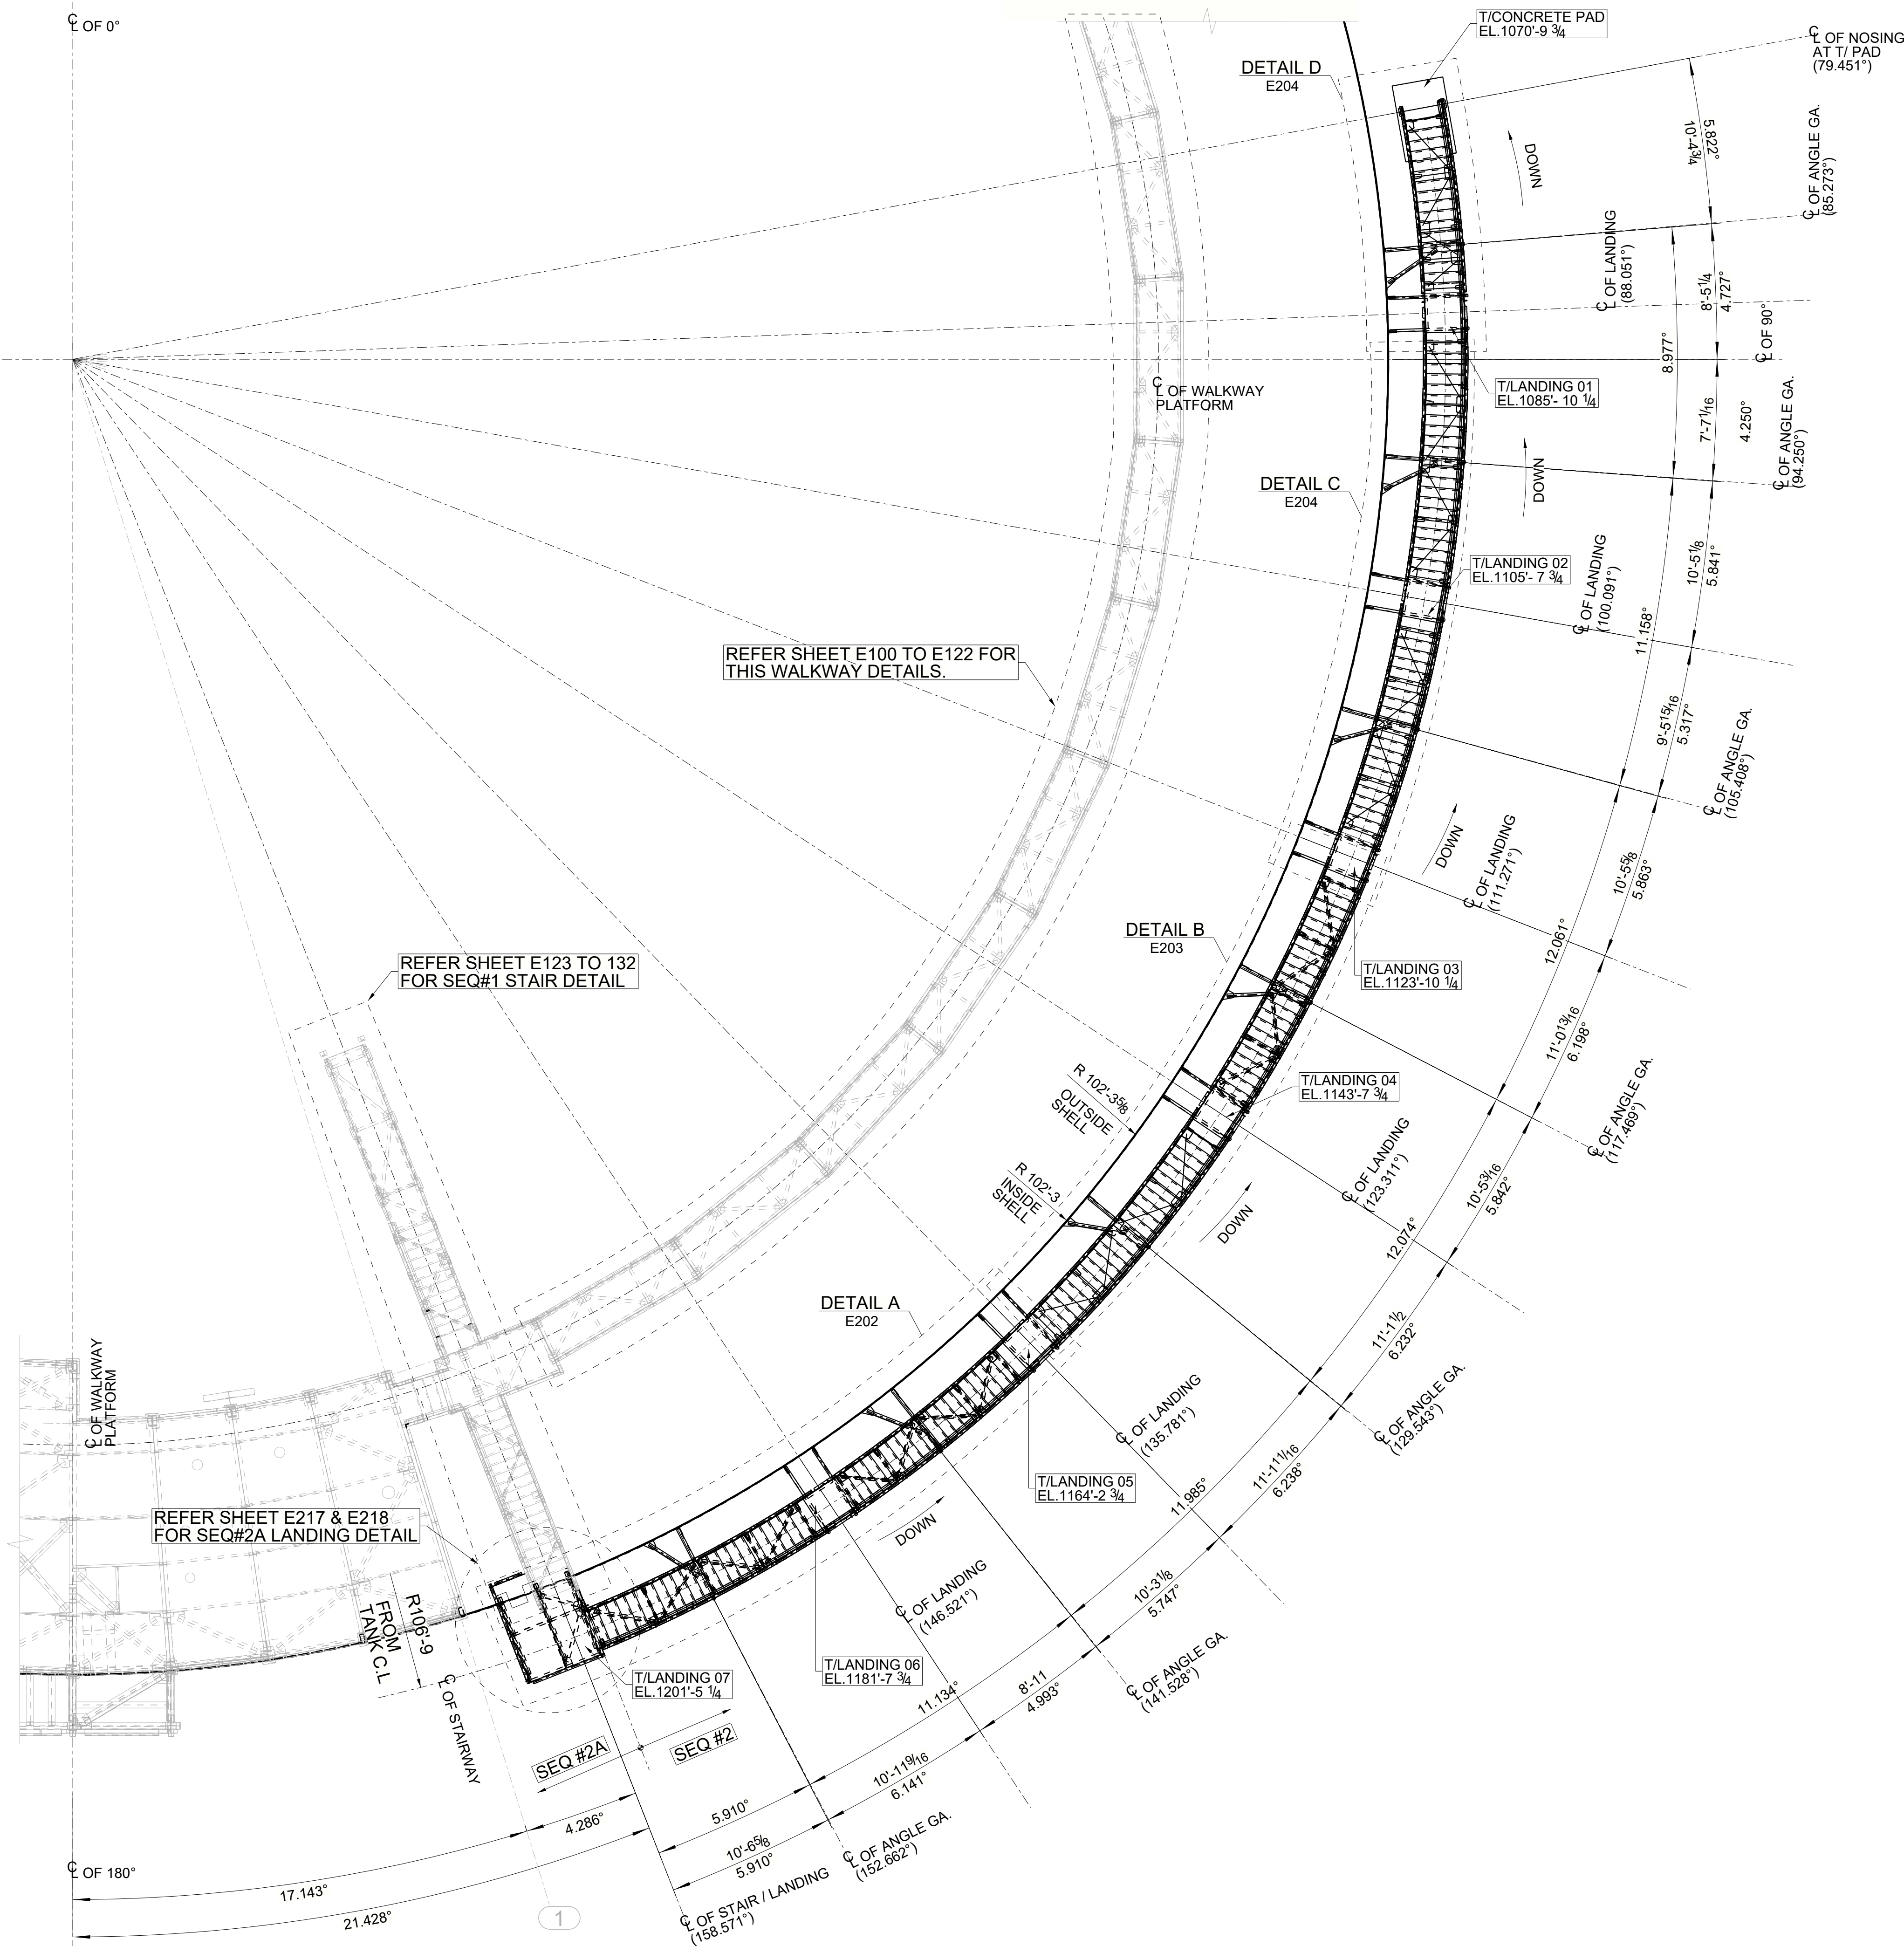


NOTES :-

- 1.REFER SHEET E100 FOR GENERAL NOTES AND OVERALL 3D-VIEW
- 2.REFER SHEET E200 FOR SPIRAL STAIR 3D-VIEW.
3. E.O.G - INDICATES EDGE OF GRATING.
4. - INDICATES DIRECTION OF GRATING SPAN.
5. * - INDICATES GRATING CUT DIMENSION.
6. - INDICATES STAIR NOSING STARTING POINT
7. - INDICATES WORKING POINT.
8. - INDICATES KNEE BRACE.
 - INDICATES VERTICAL BRACE.


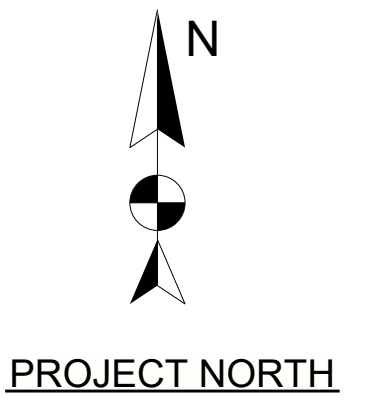


SEQ#2 SPIRAL STAIR KEY PLAN
(REFER : PLAN OF SPIRAL STAIRWAY /DW-10600-01)

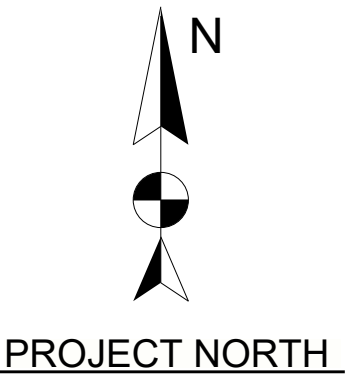

- NOTES :
1. REFER SHEET E100 FOR OVERALL 3D VIEW AND GENERAL NOTES
 2. REFER SHEET E200 FOR SEQ#2 SPIRAL STAIR 3D-VIEW
 3. REFER SHEET E201 FOR SEQ#2 SPIRAL STAIR KEY PLAN
 4. REFER SHEET E205 TO E211 FOR ELEVATIONS
 5. REFER SHEET E212 TO E214 FOR BRACE ELEVATIONS
 6. REFER SHEET E215 & E216 FOR SECTIONS AND DETAILS

DETAIL A
E201
PARTIAL SPIRAL STAIR FRAMING PLAN @ T/ LANDING 07 EL.1201'- 5 1/4
(REFER: PPLAN OF SPIRAL STAIRWAY /DW-10600-01)

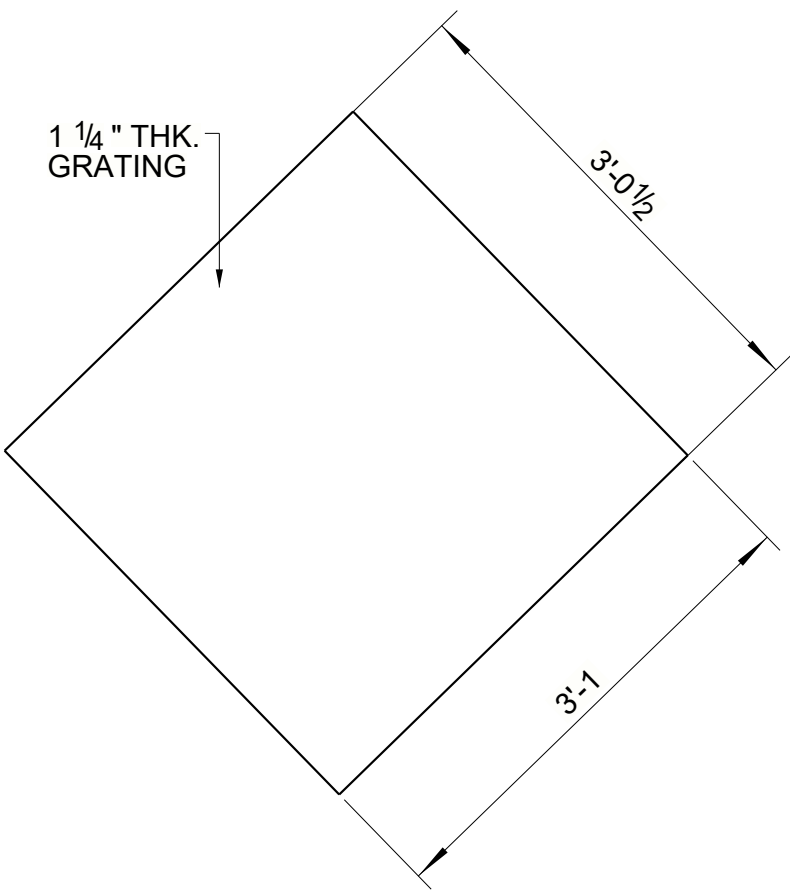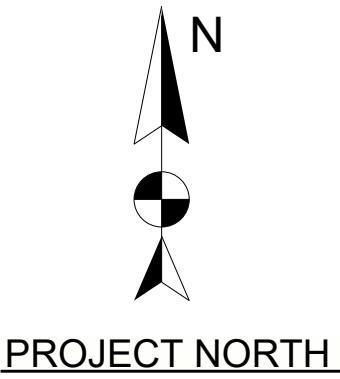


TYPICAL LANDING GRATING LAYOUT PLAN
@ LANDING 01, 02, 03, 04, 05, 06

- NOTES :
1. REFER SHEET E100 FOR OVERALL 3D VIEW AND GENERAL NOTES
 2. REFER SHEET E200 FOR SEQ#2 SPIRAL STAIR 3D-VIEW
 3. REFER SHEET E201 FOR SEQ#2 SPIRAL STAIR KEY PLAN
 4. REFER SHEET E205 TO E211 FOR ELEVATIONS
 5. REFER SHEET E212 TO E214 FOR BRACE ELEVATIONS
 6. REFER SHEET E215 & E216 FOR SECTIONS AND DETAILS




DETAIL B
E201
PARTIAL STAIR FRAMING PLAN @ T/LANDING 05 EL. 1164'-2 3/4"
(REFER: PPLAN OF SPIRAL STAIRWAY /DW-10600-01)

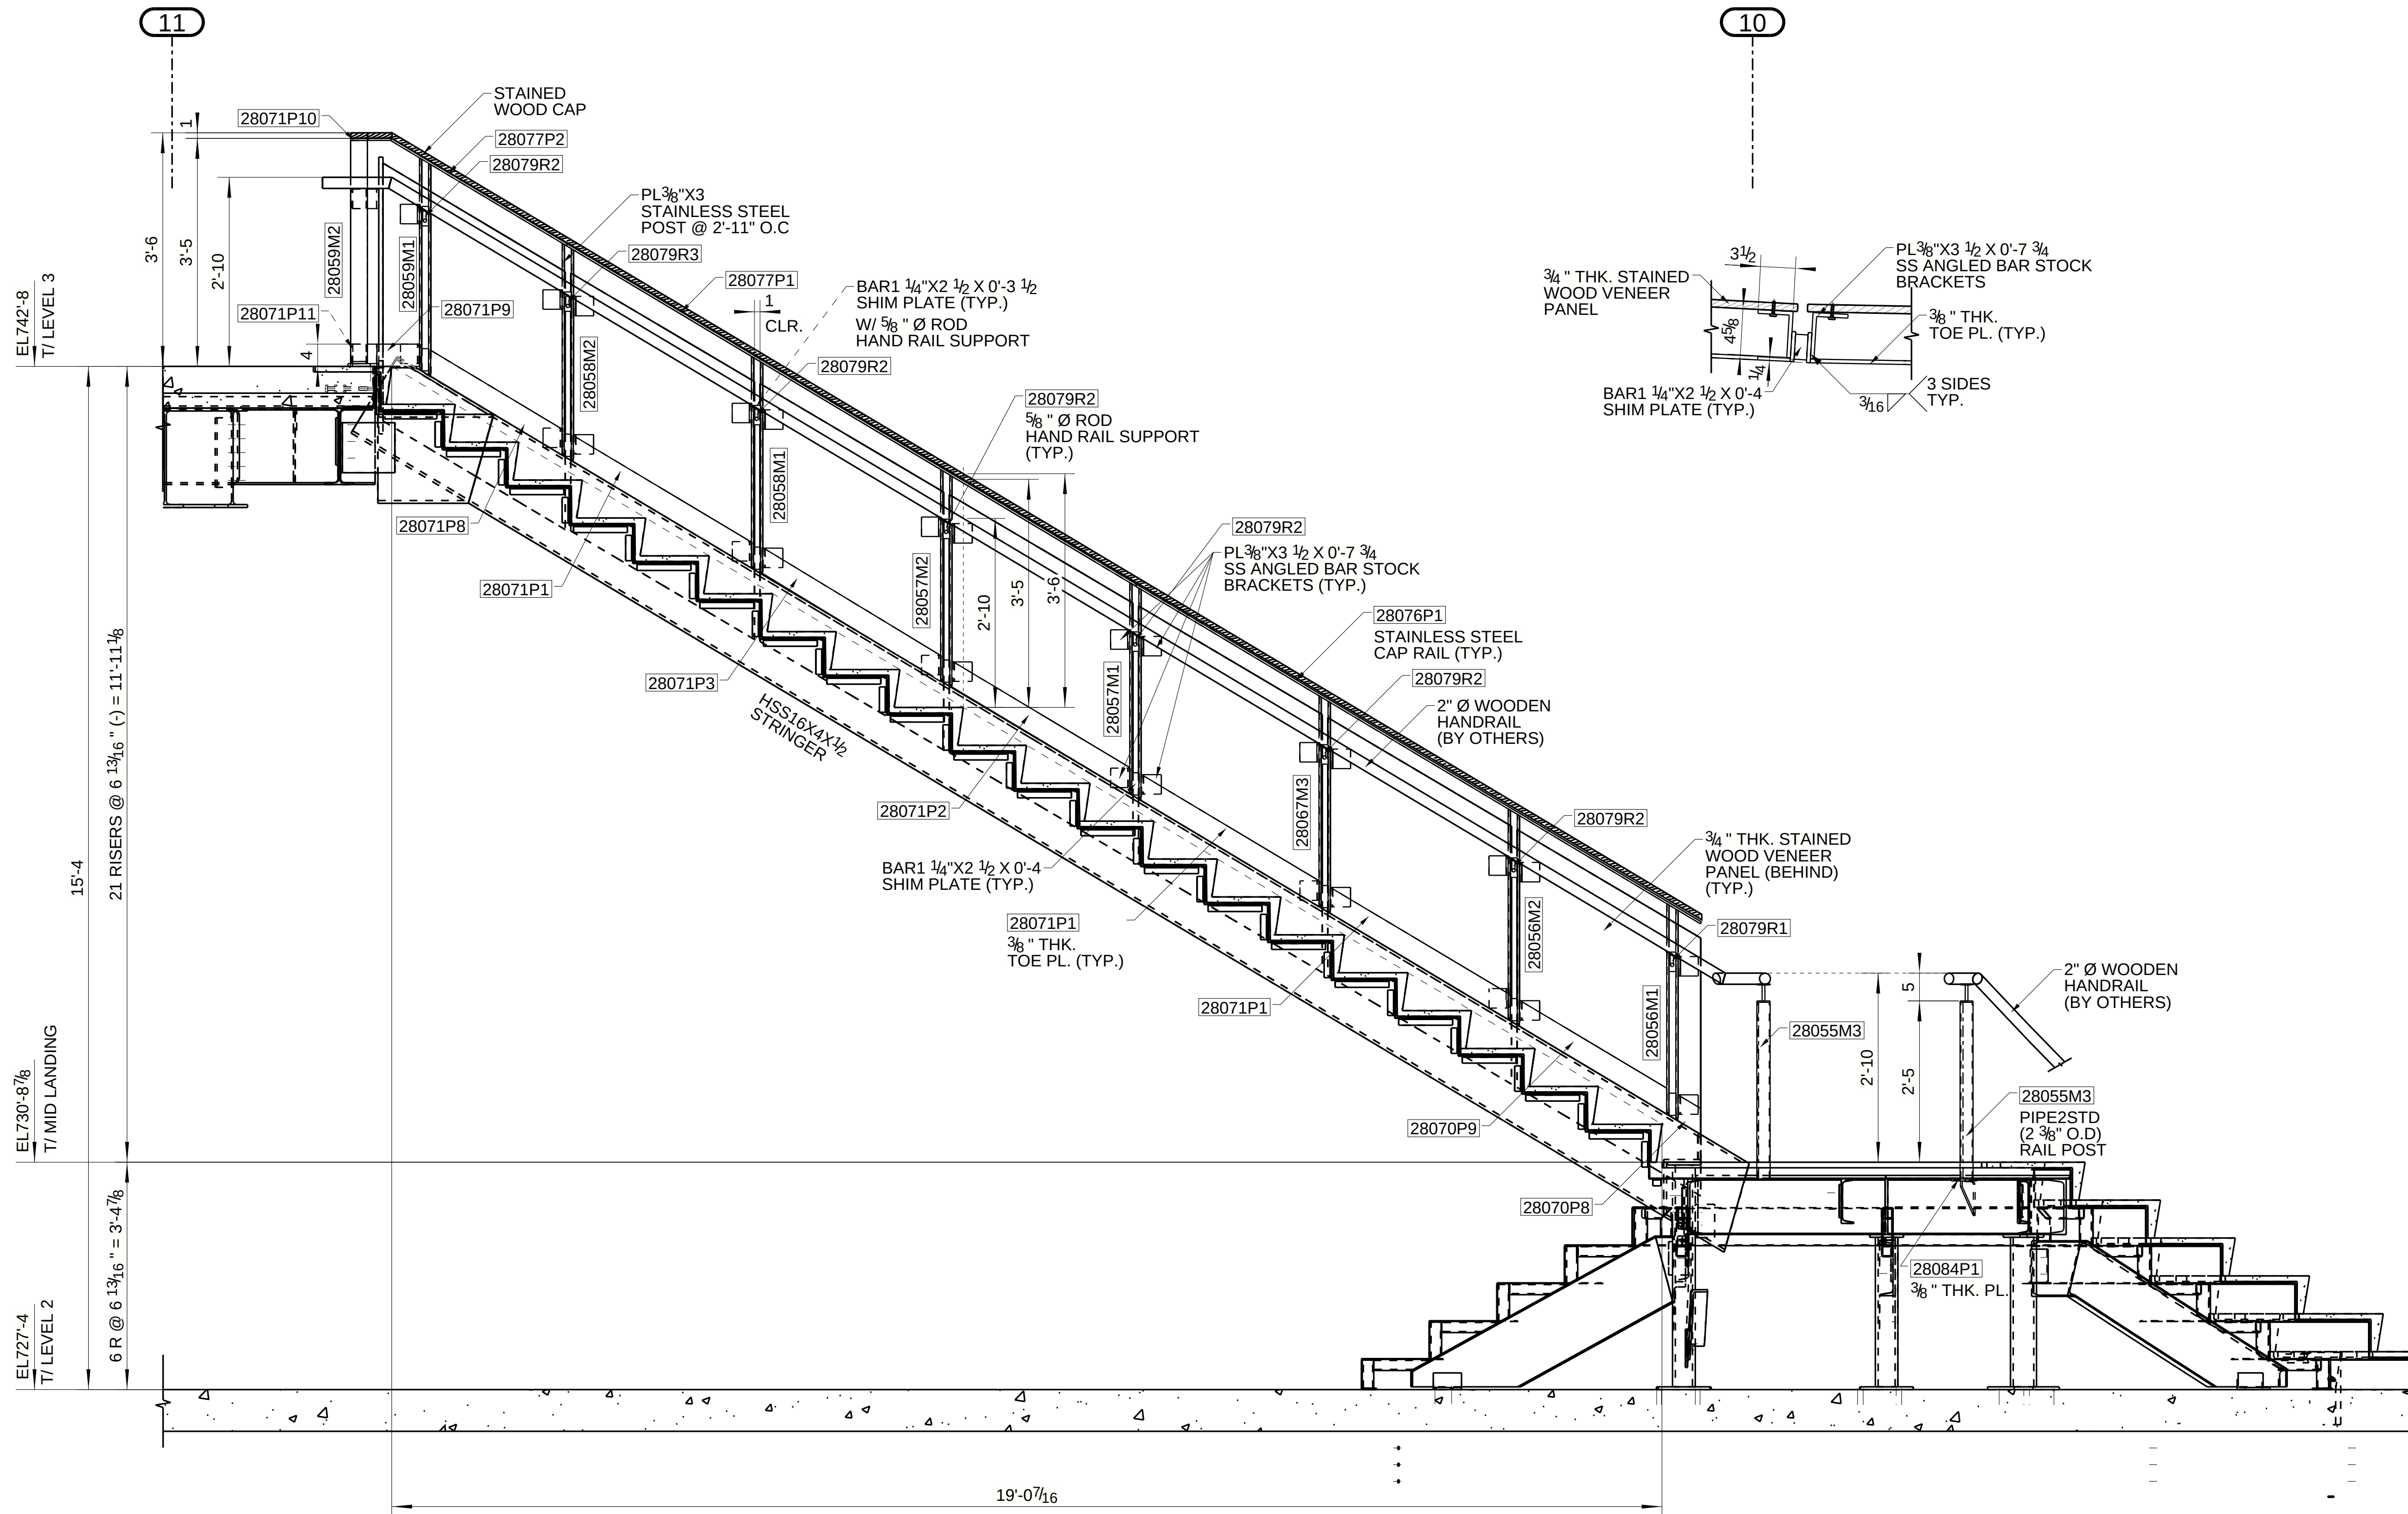

SECTION B - B
28-E28031

















NOTES :

1. REFER SHEET 28-E28029 FOR 3D-VIEW & GENERAL NOTES.
2. REFER SHEETS 28-E28031 TO 28-E28035 FOR RAIL LOCATION PLAN.
3. REFER SHEET 28-E28041 FOR TYPICAL SECTION & DETAILS.

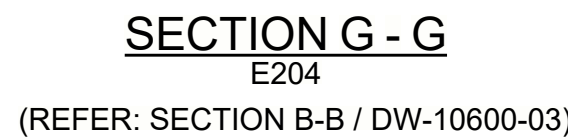

















1. REFER SHEET E202 TO E204 FOR PLAN.
2. (*) - INDICATED DIMENSIONS ARE FROM 90° AZIMUTH ON THE OUTSIDE OF TANK SHELL.







FOR FIELD USE : 12/20/2022

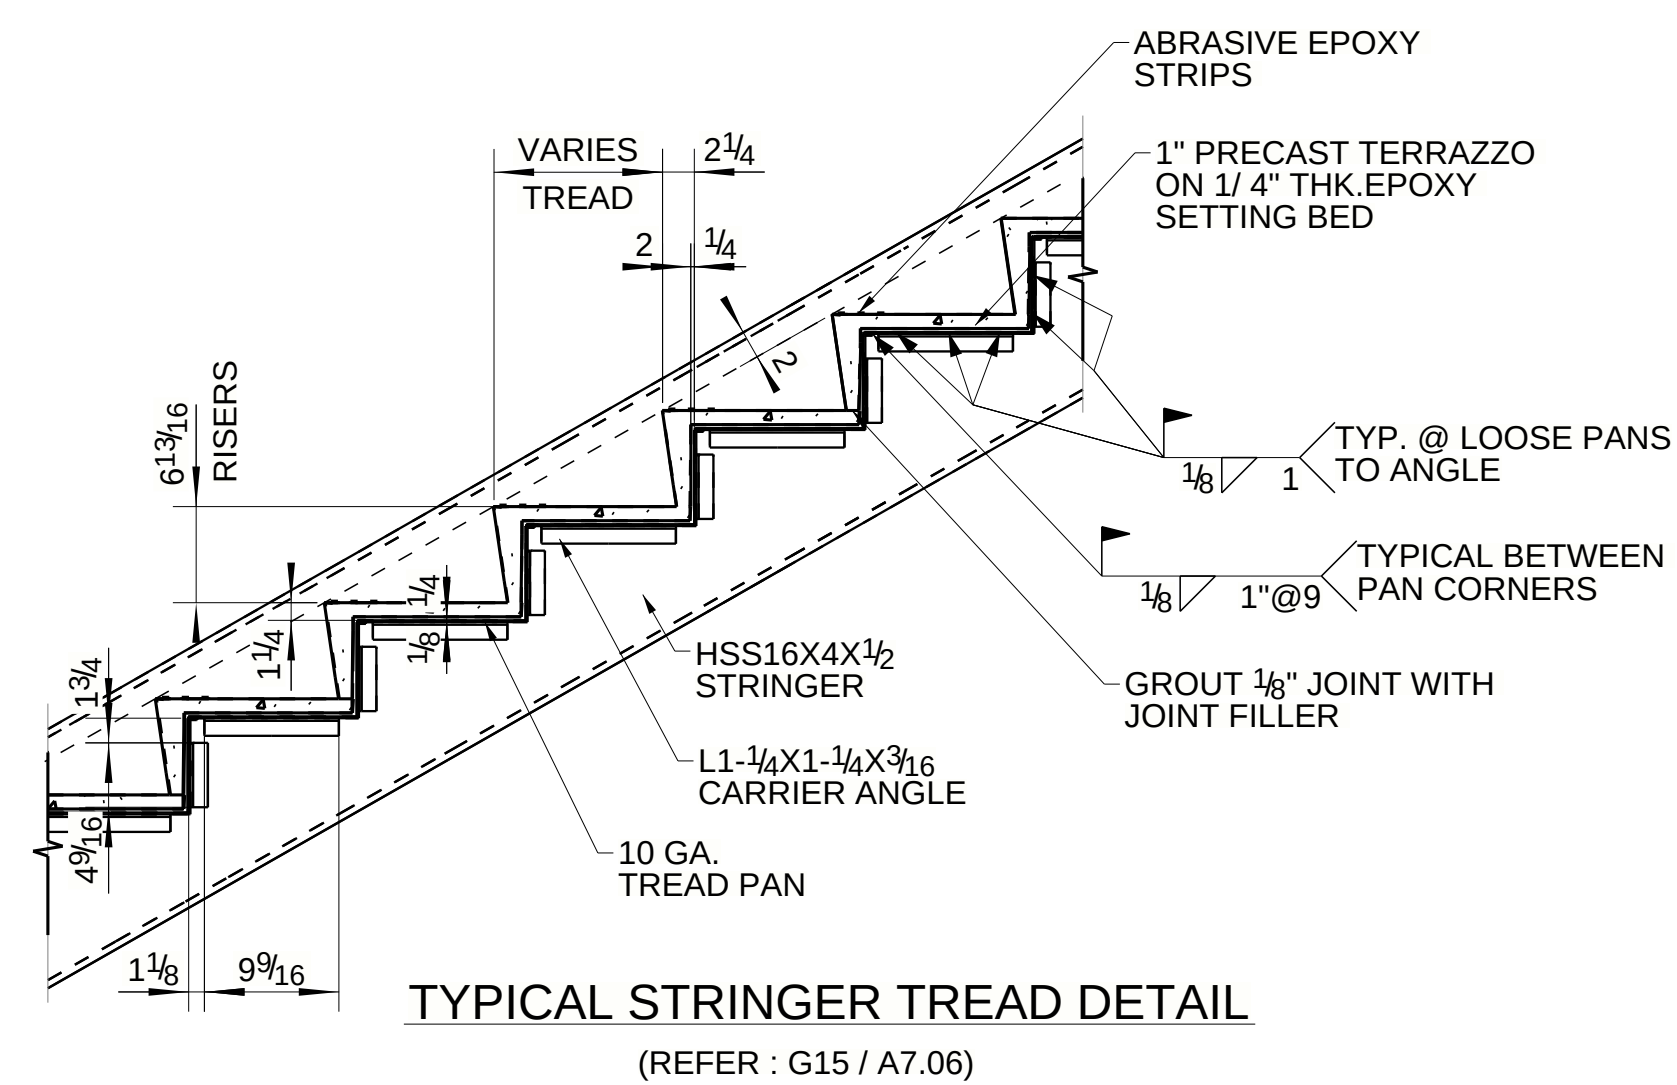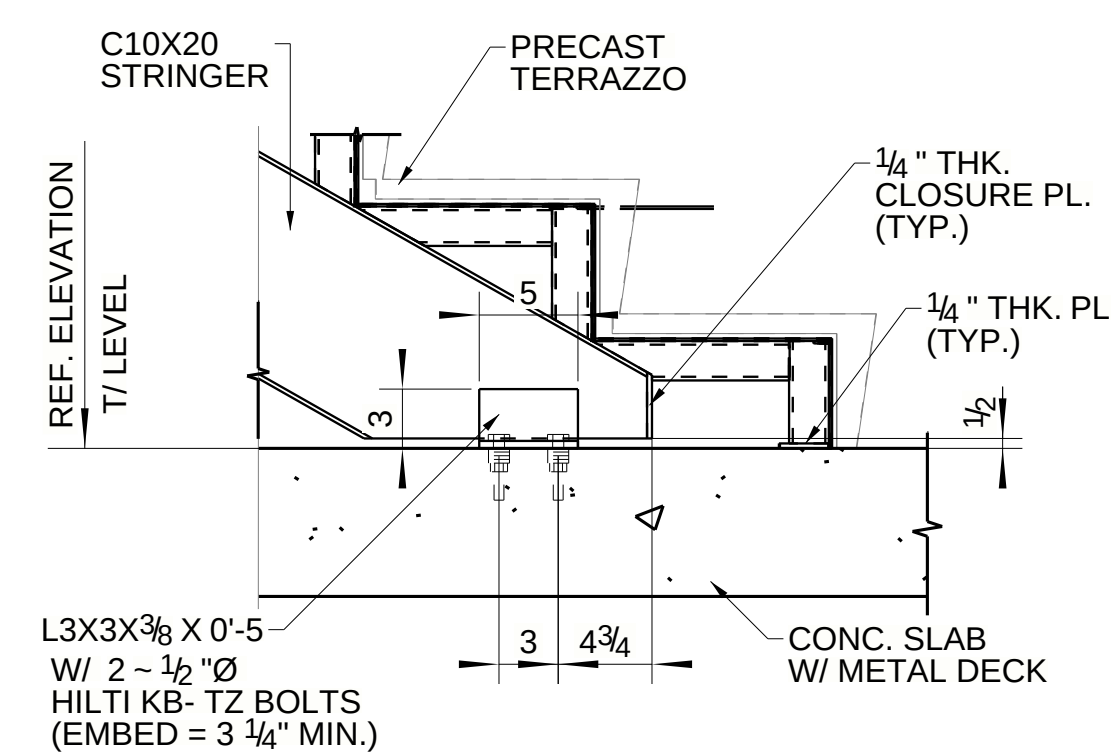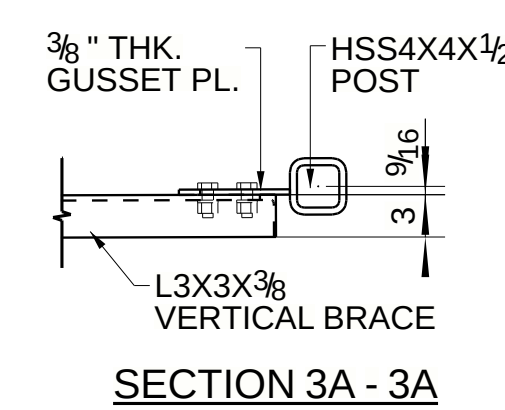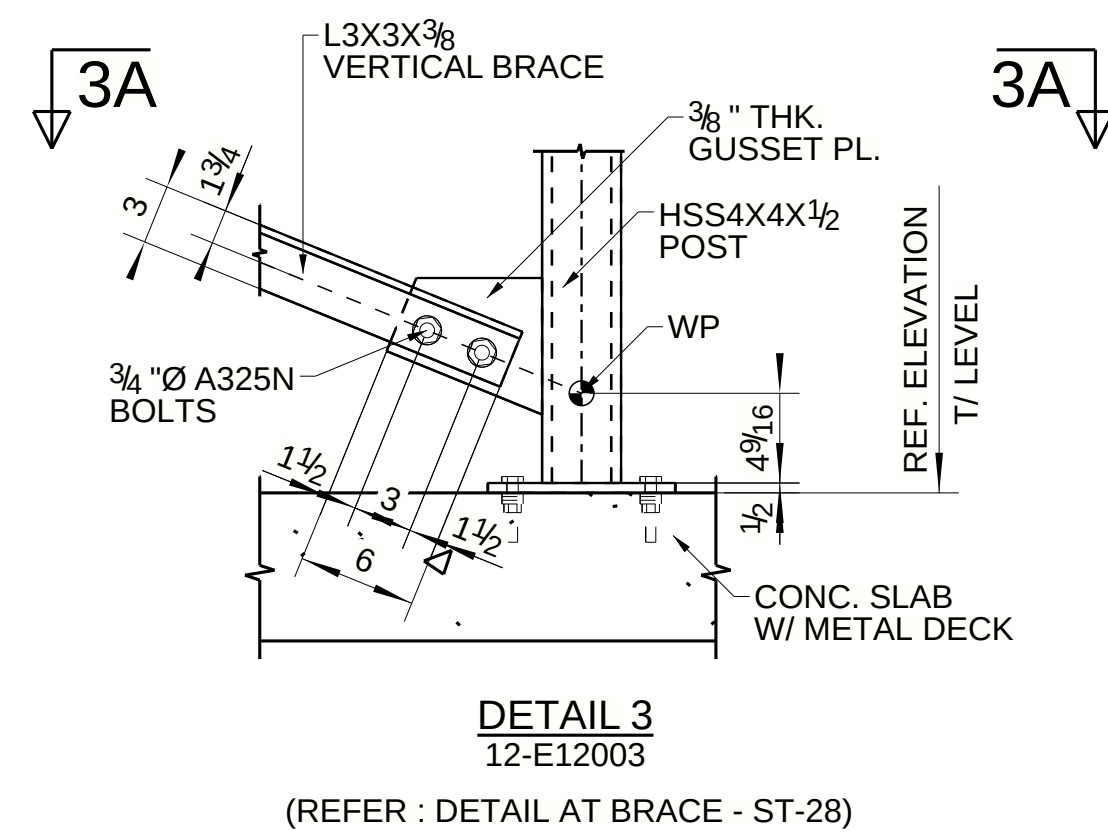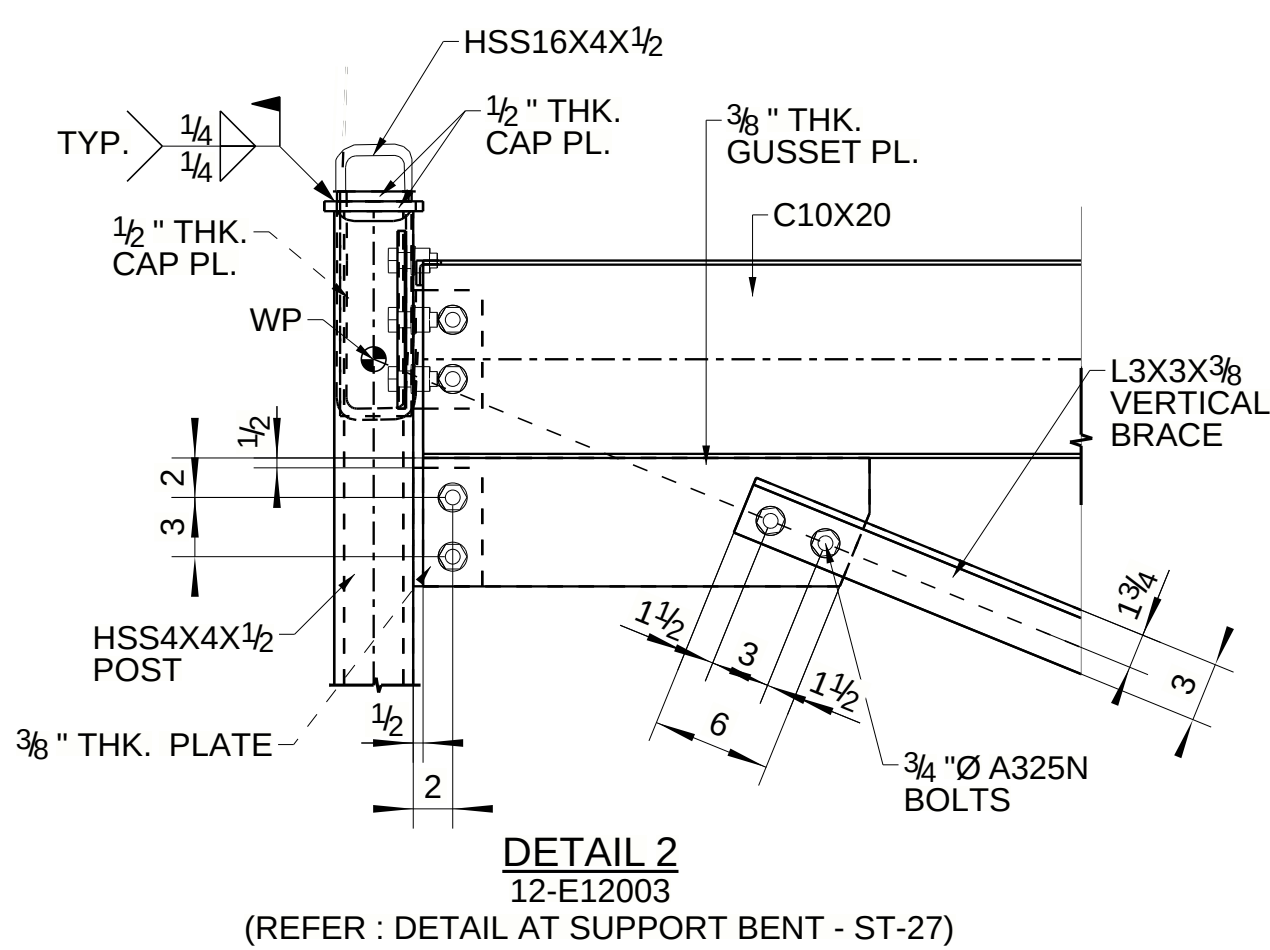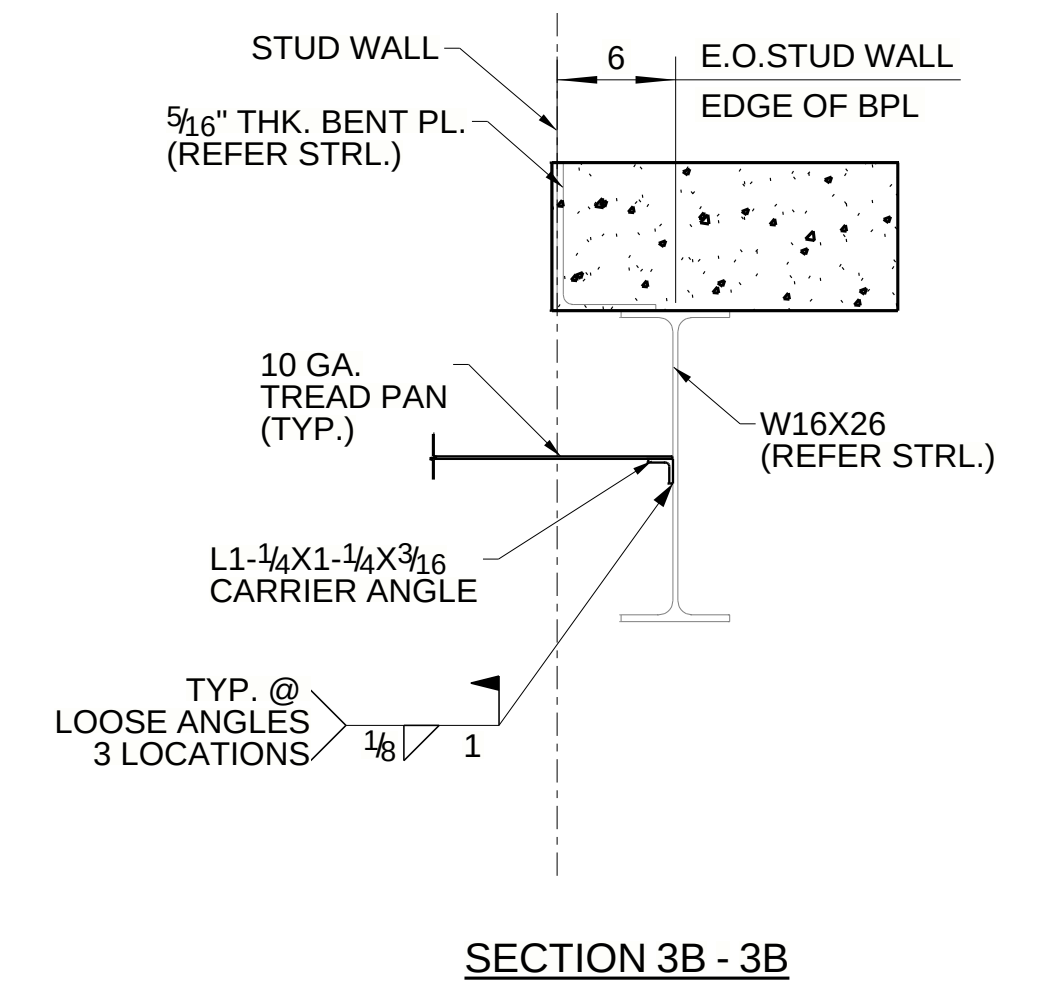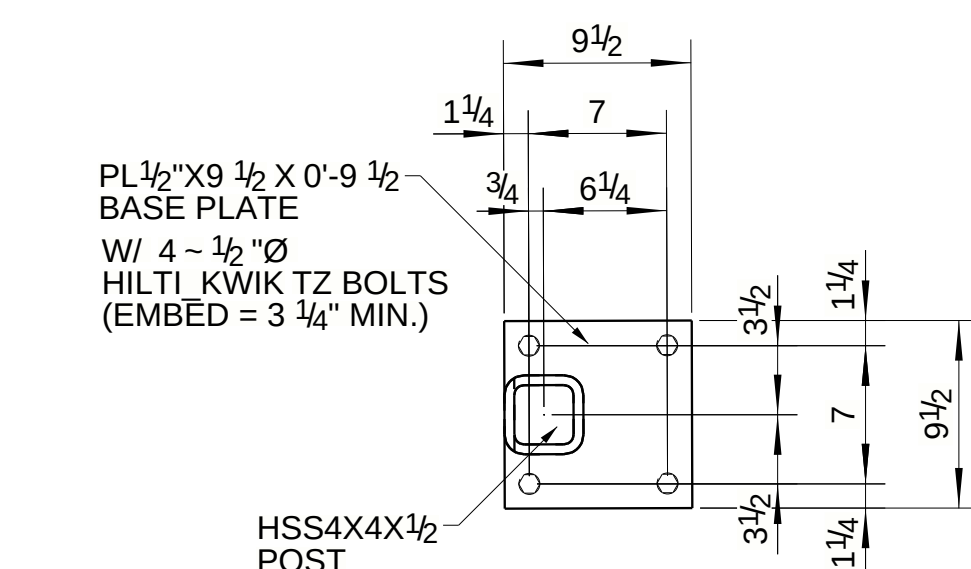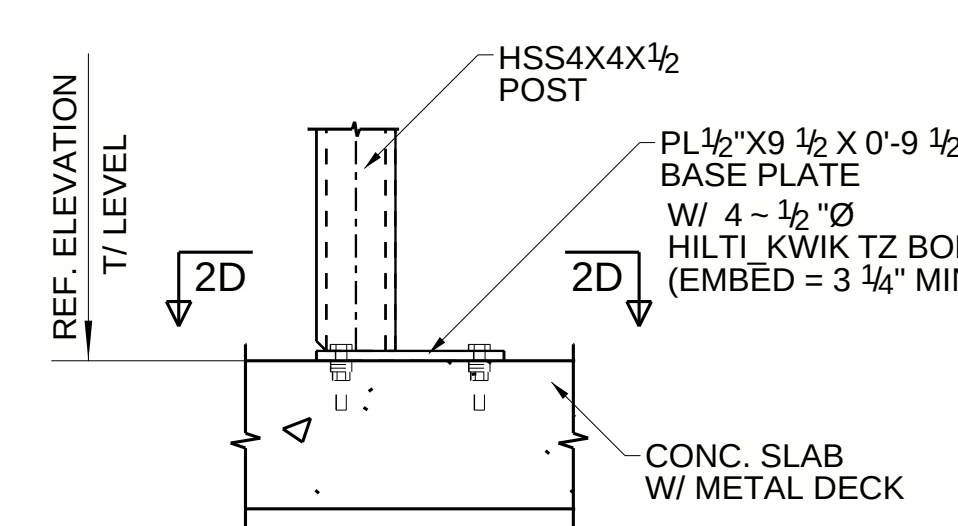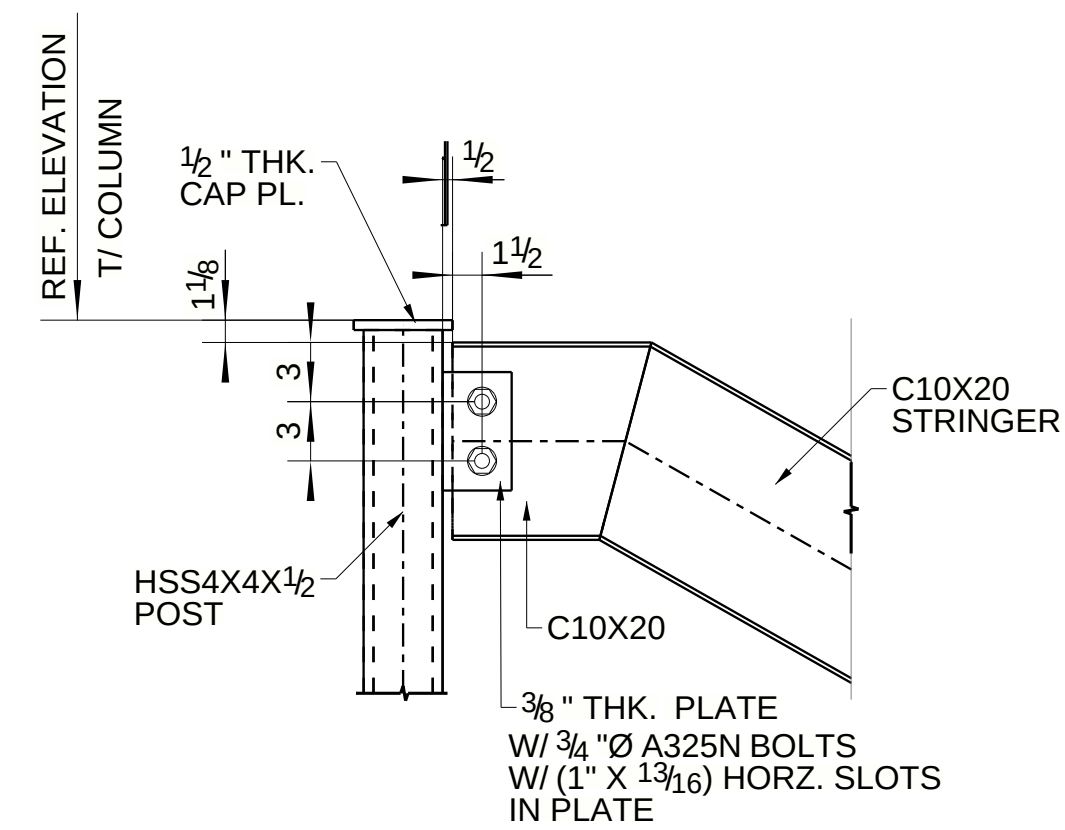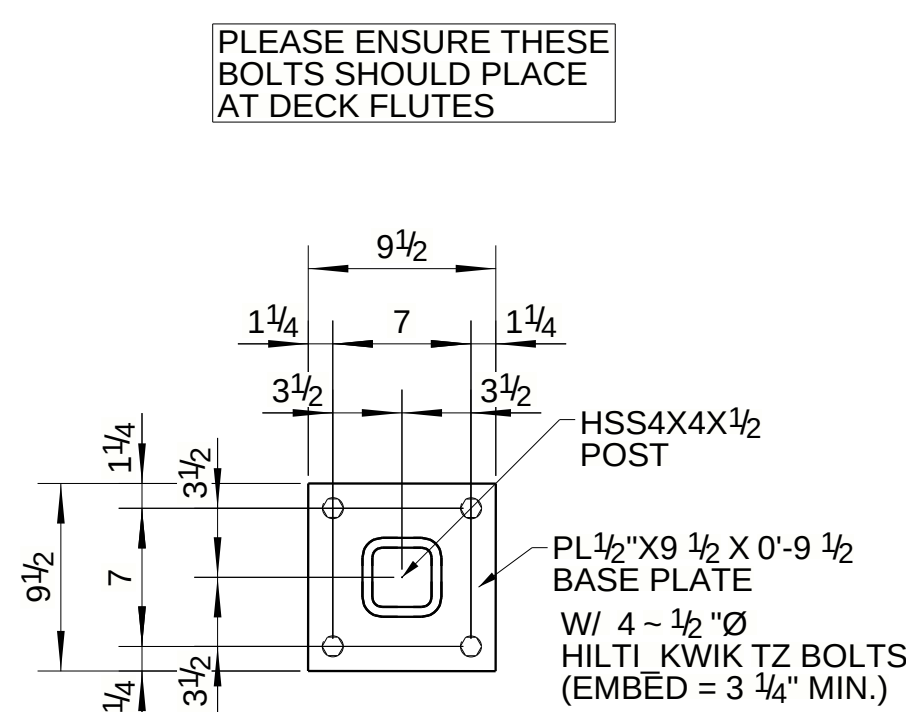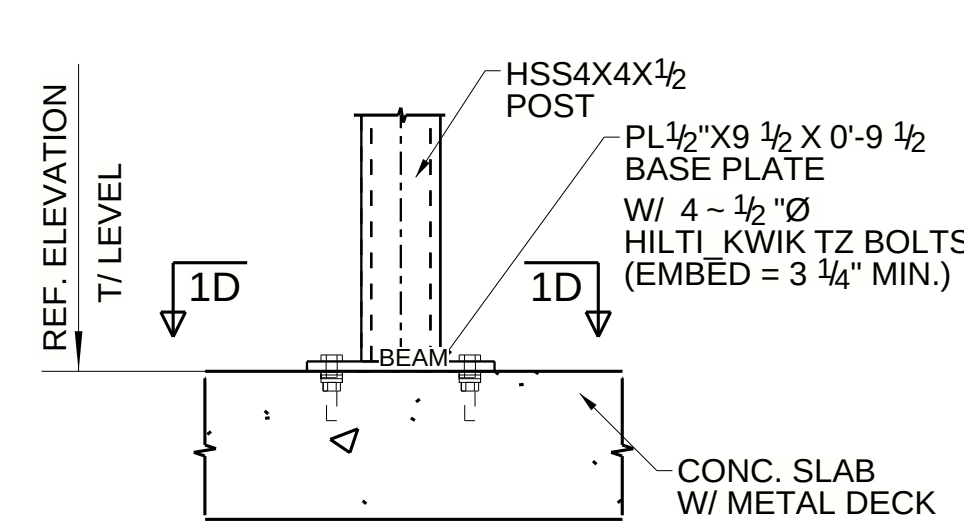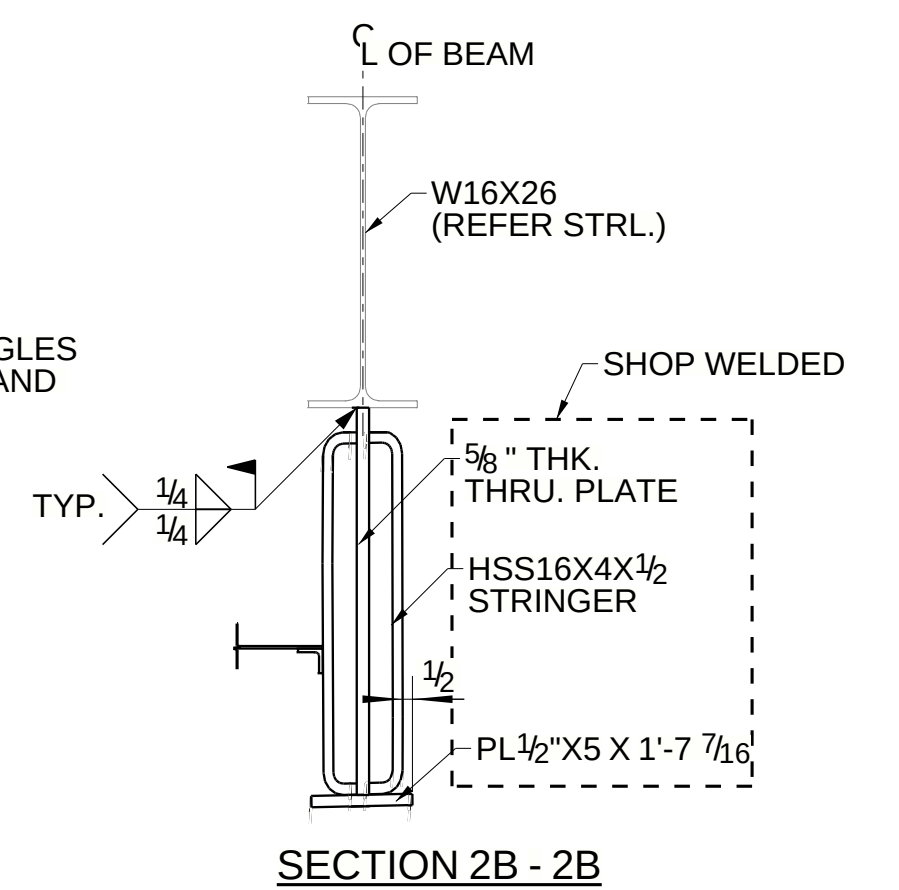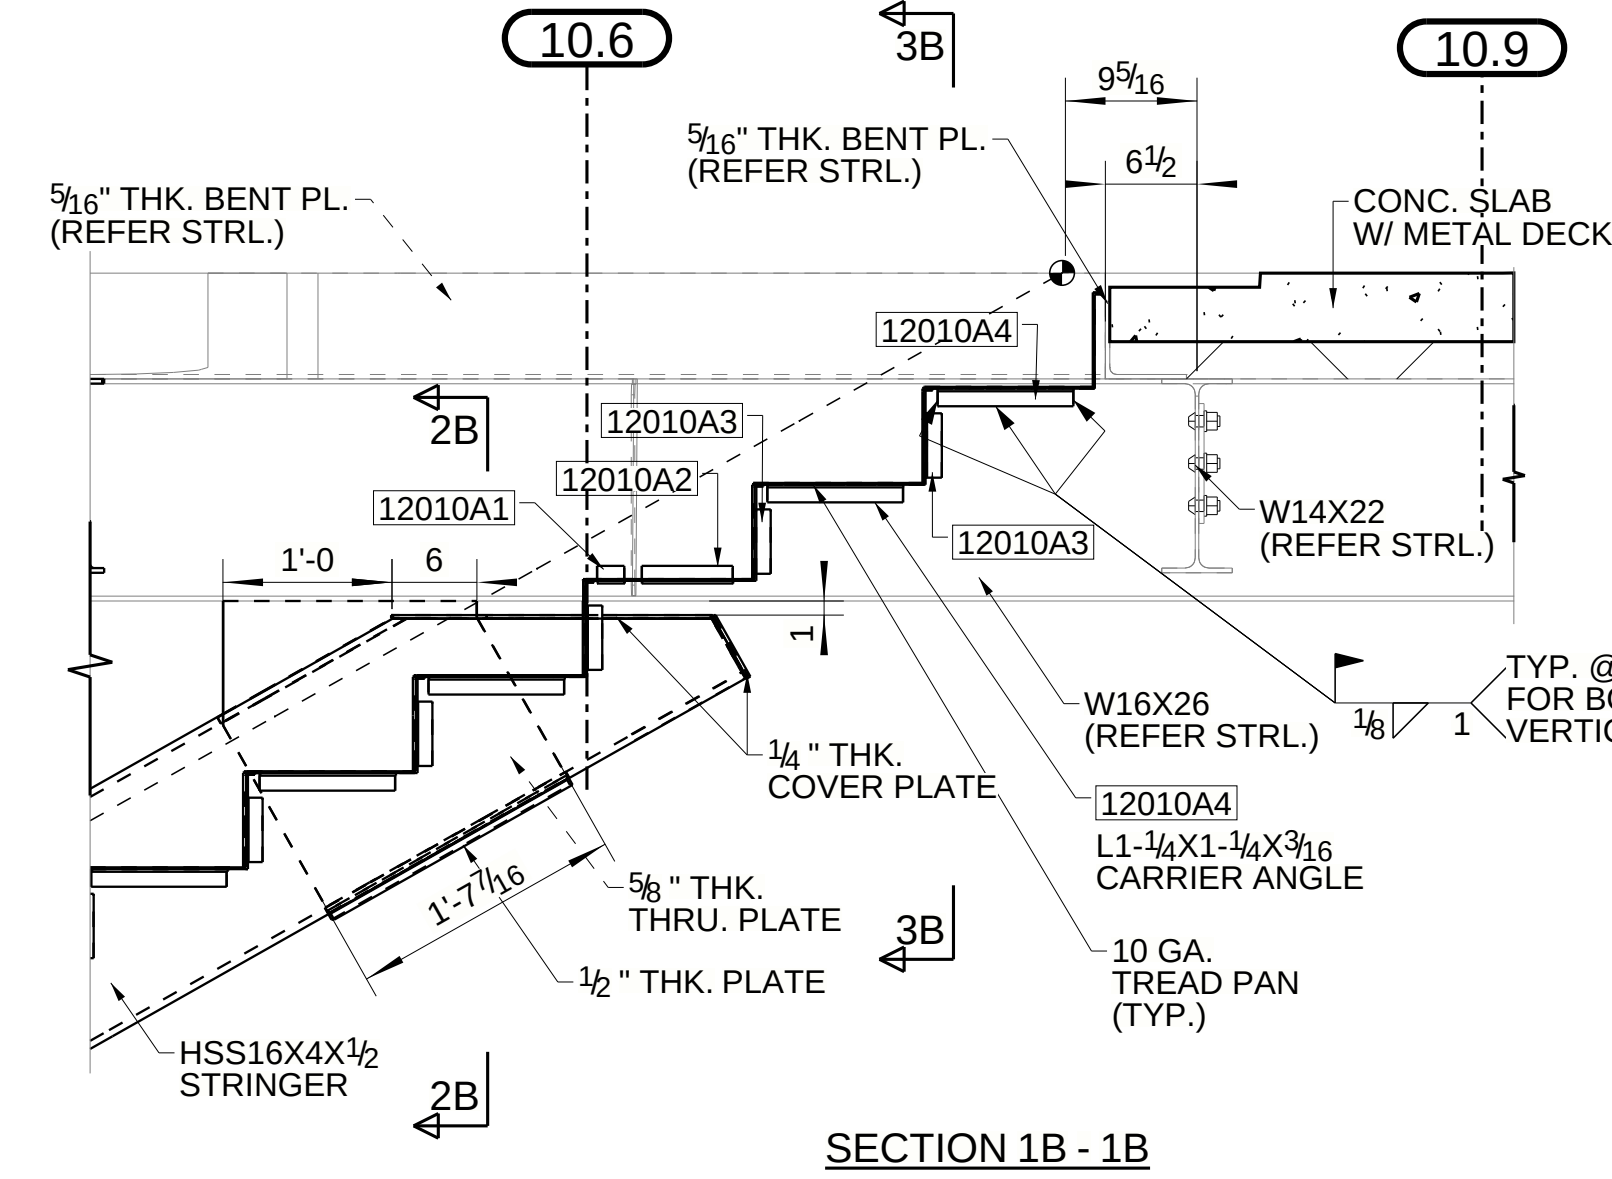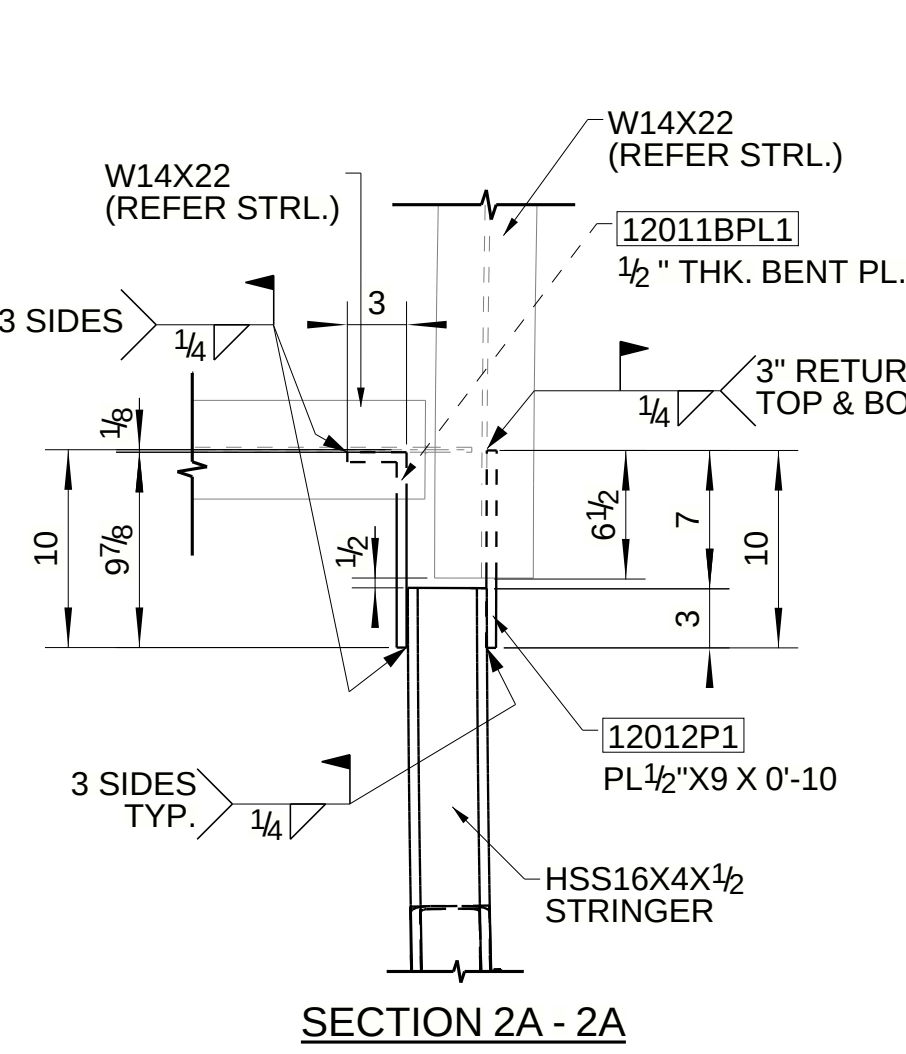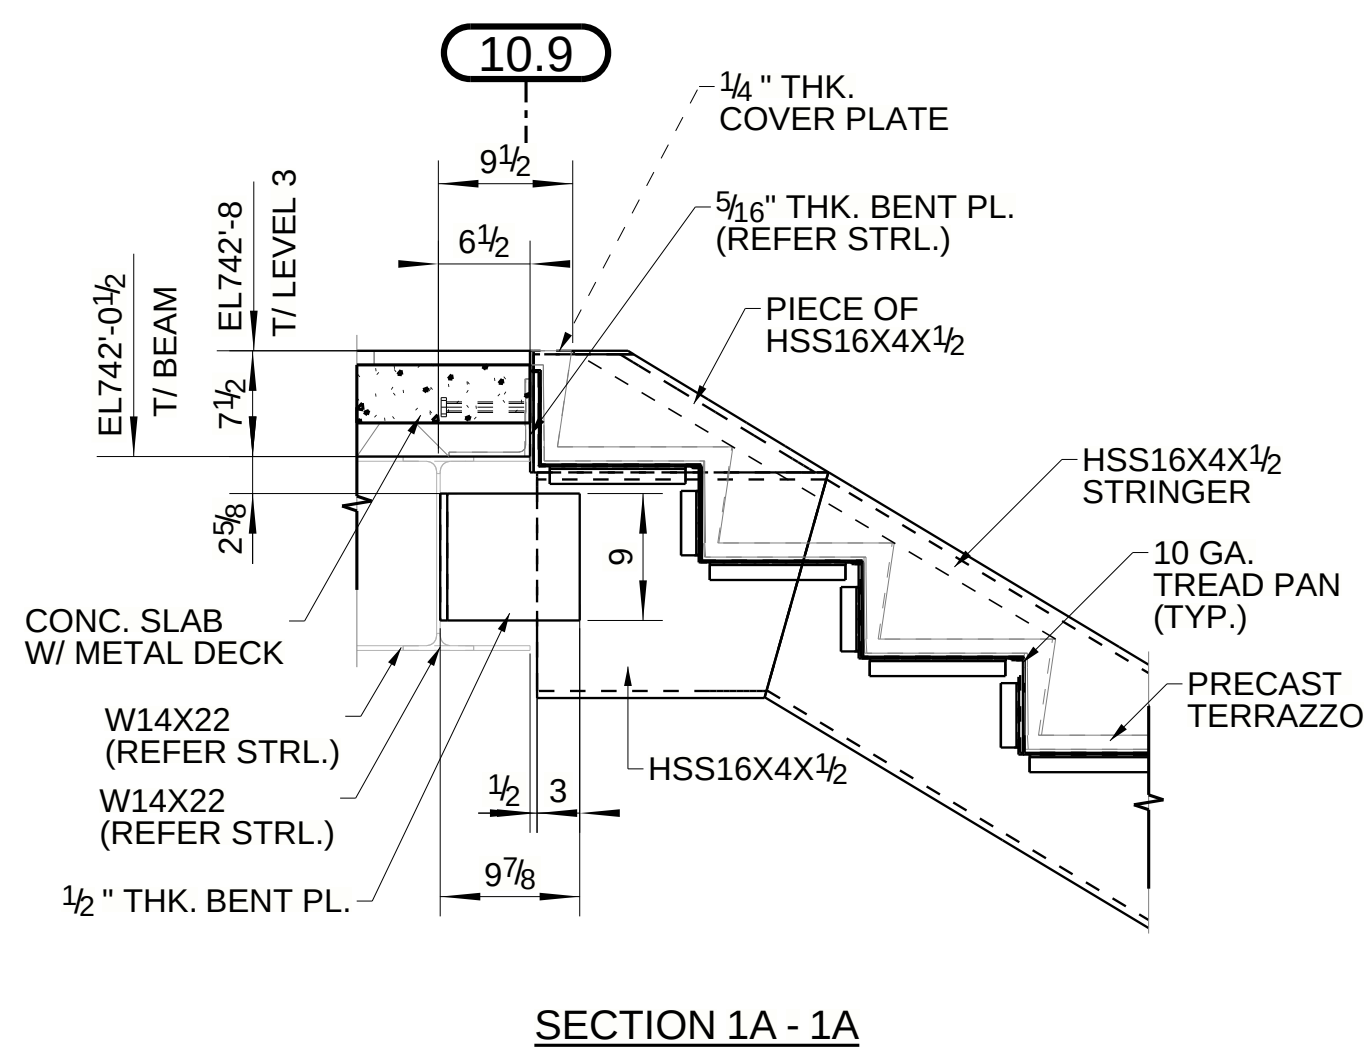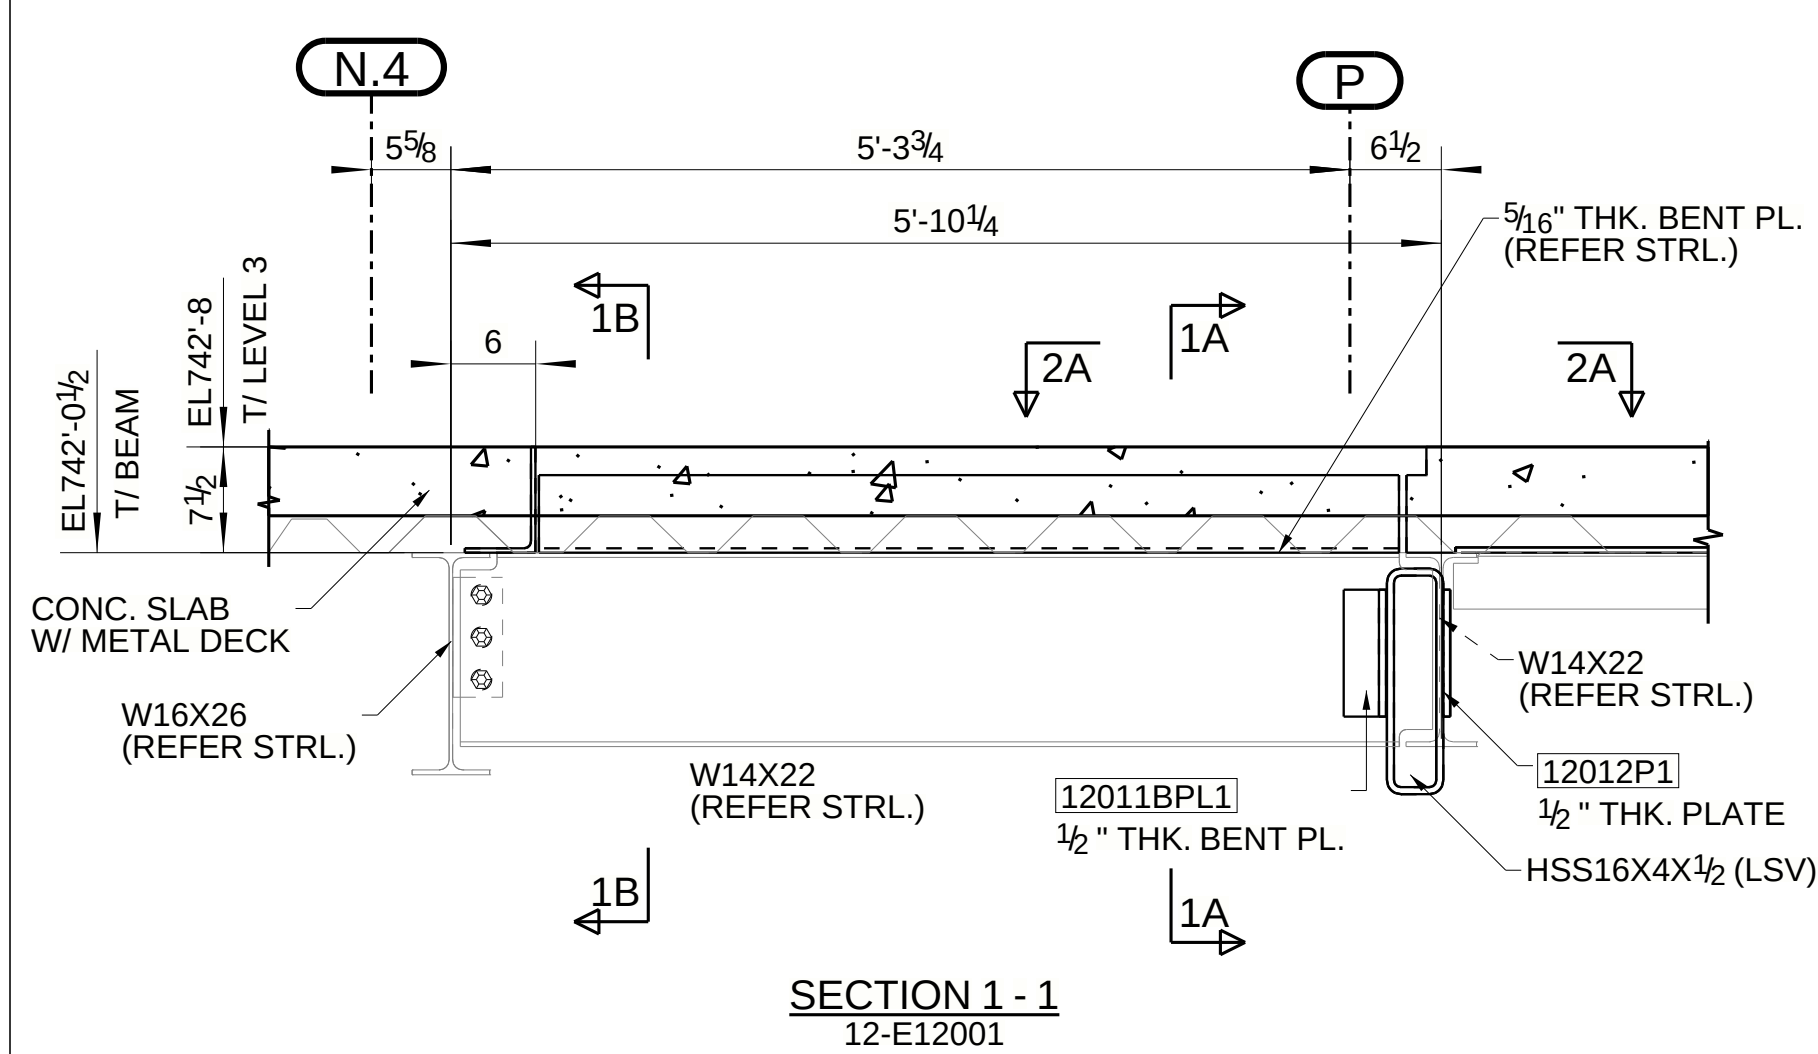

NOTES :

1. REFER SHEET 12-E12000 FOR 3D VIEW & GENERAL NOTES.

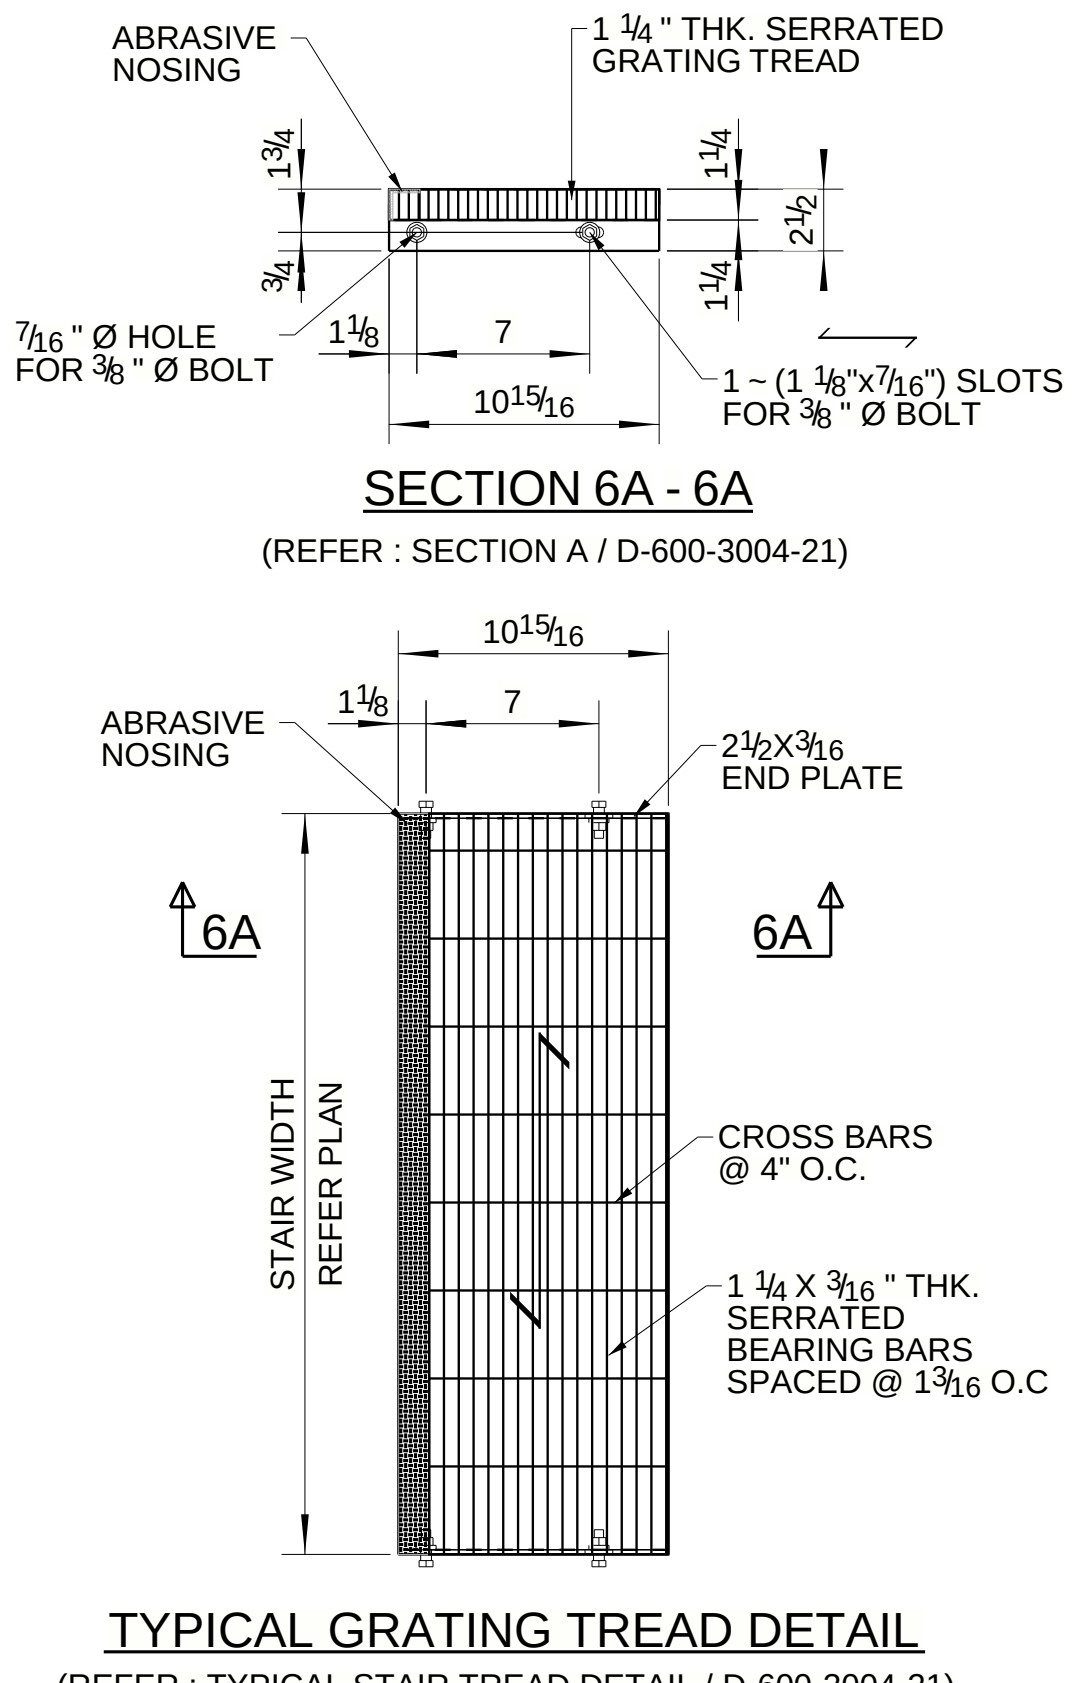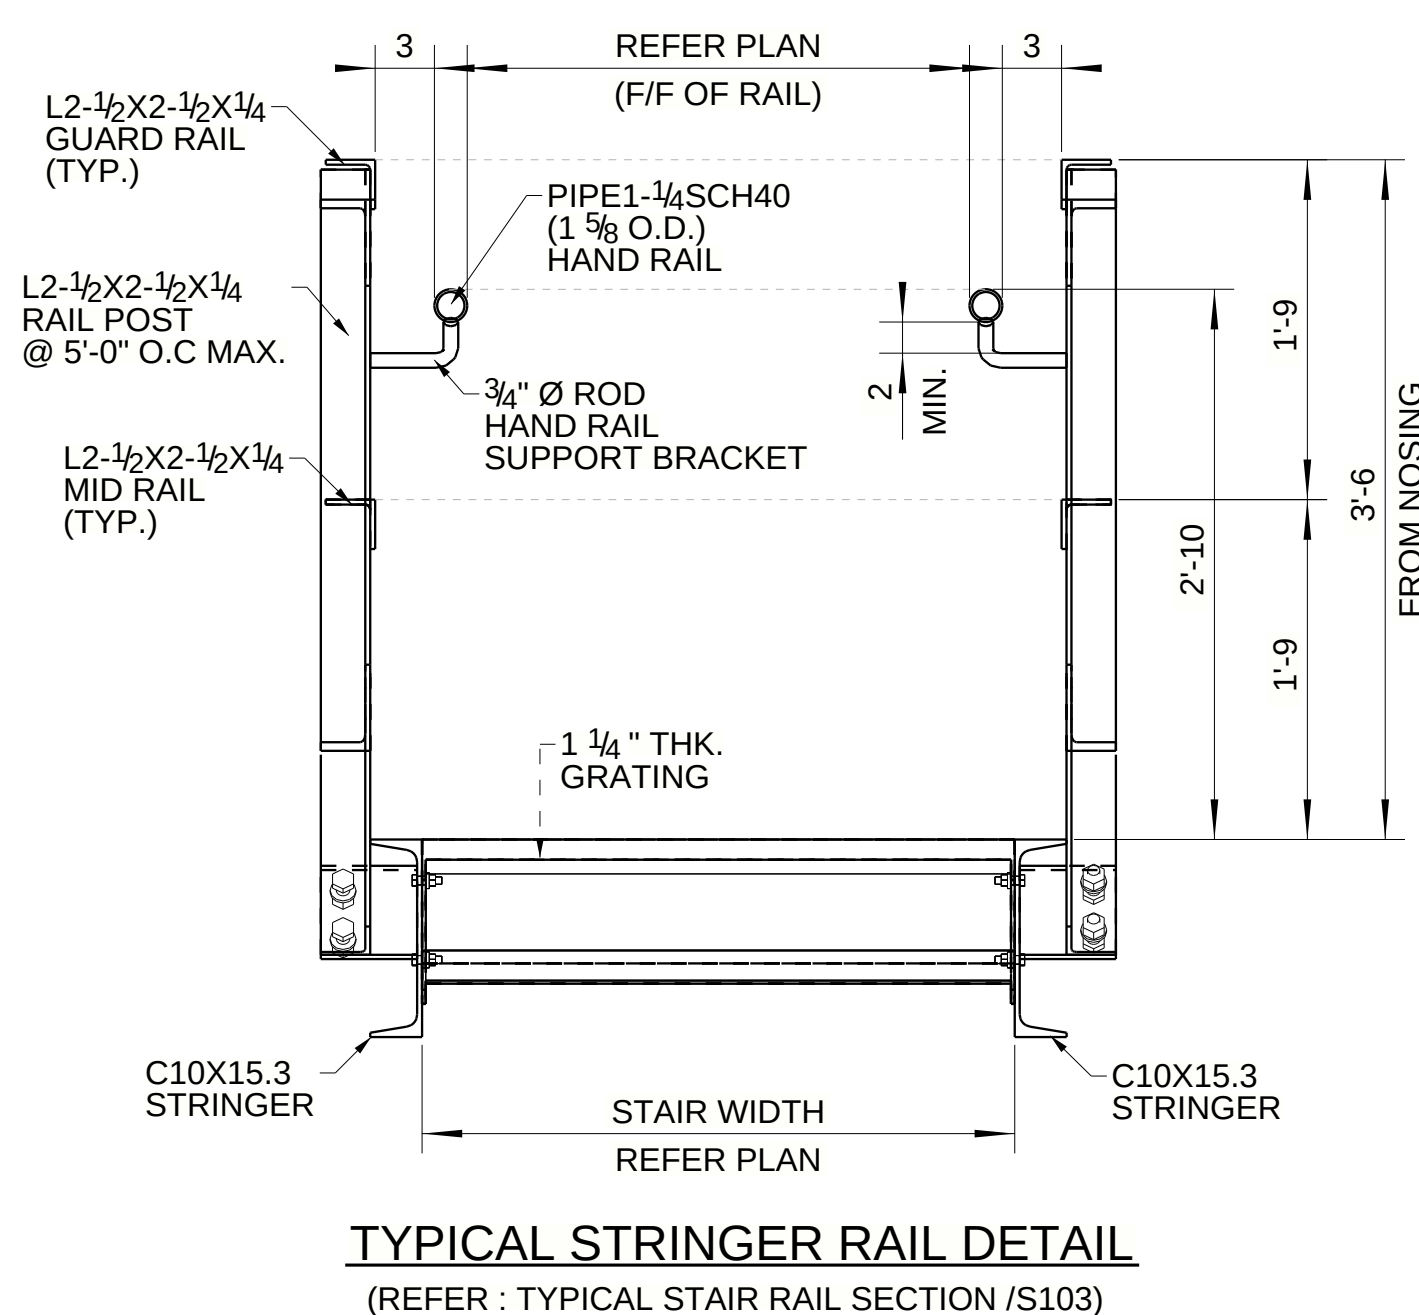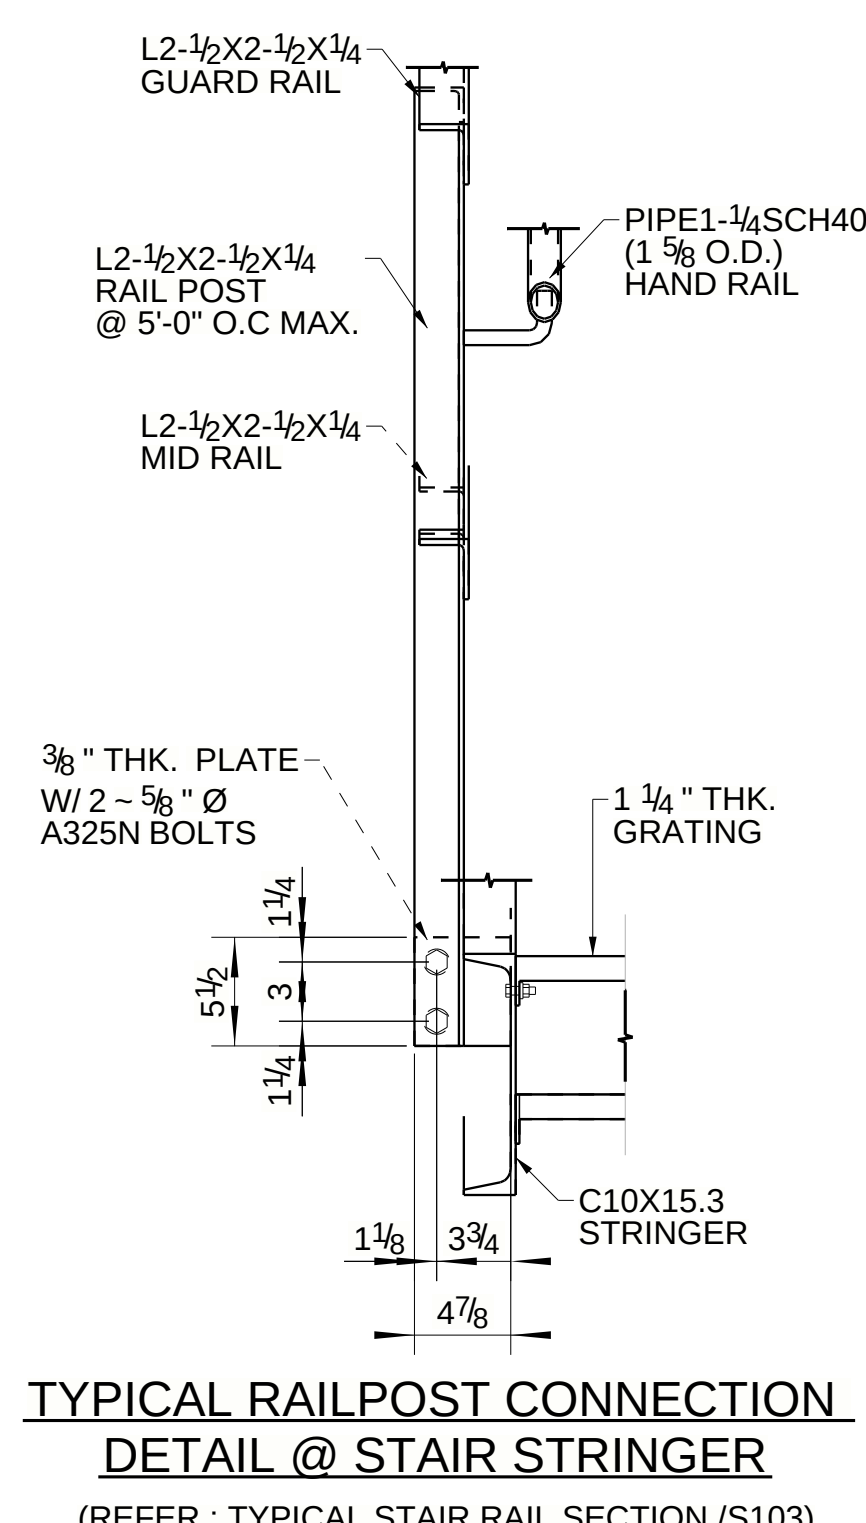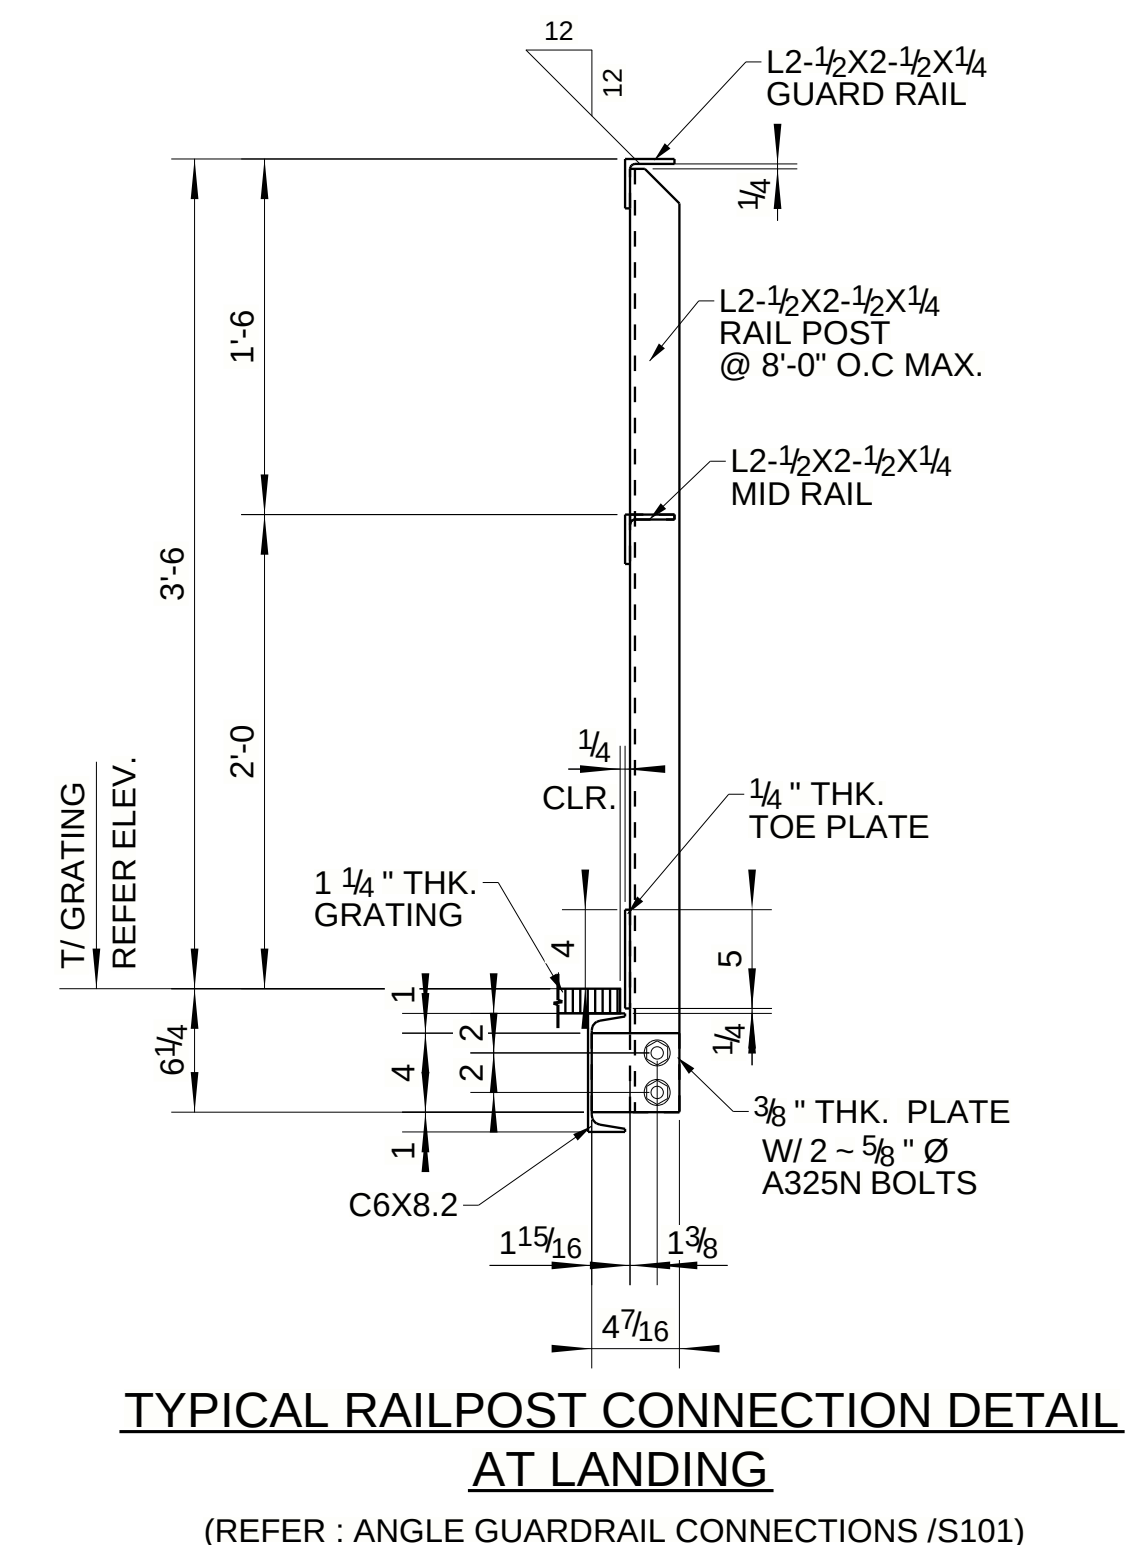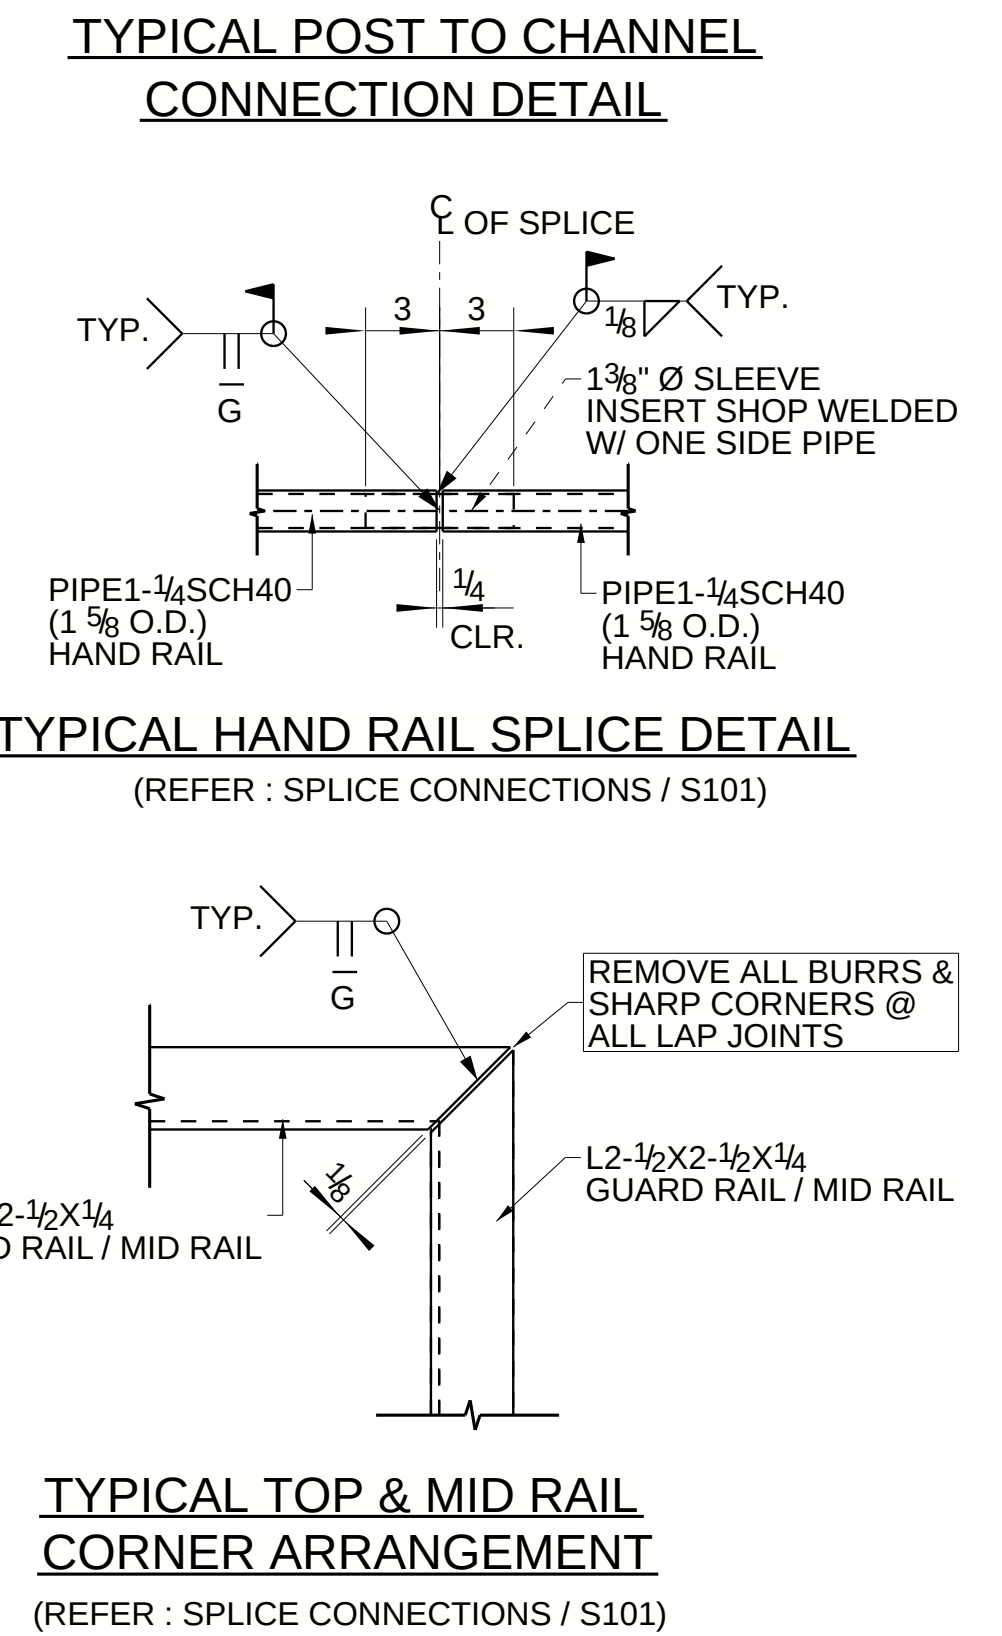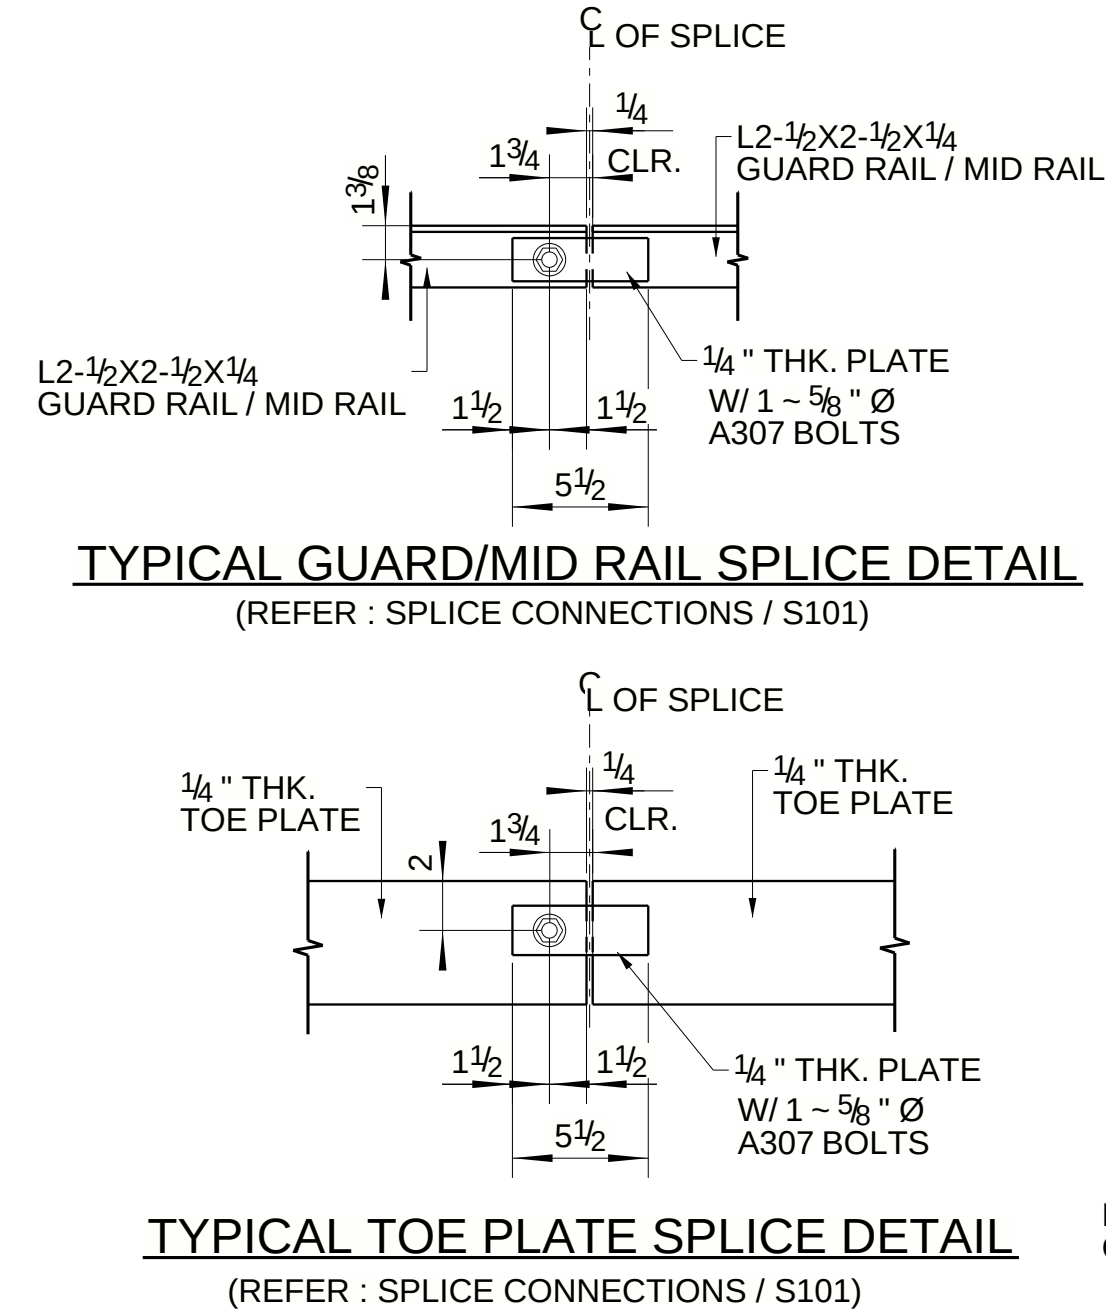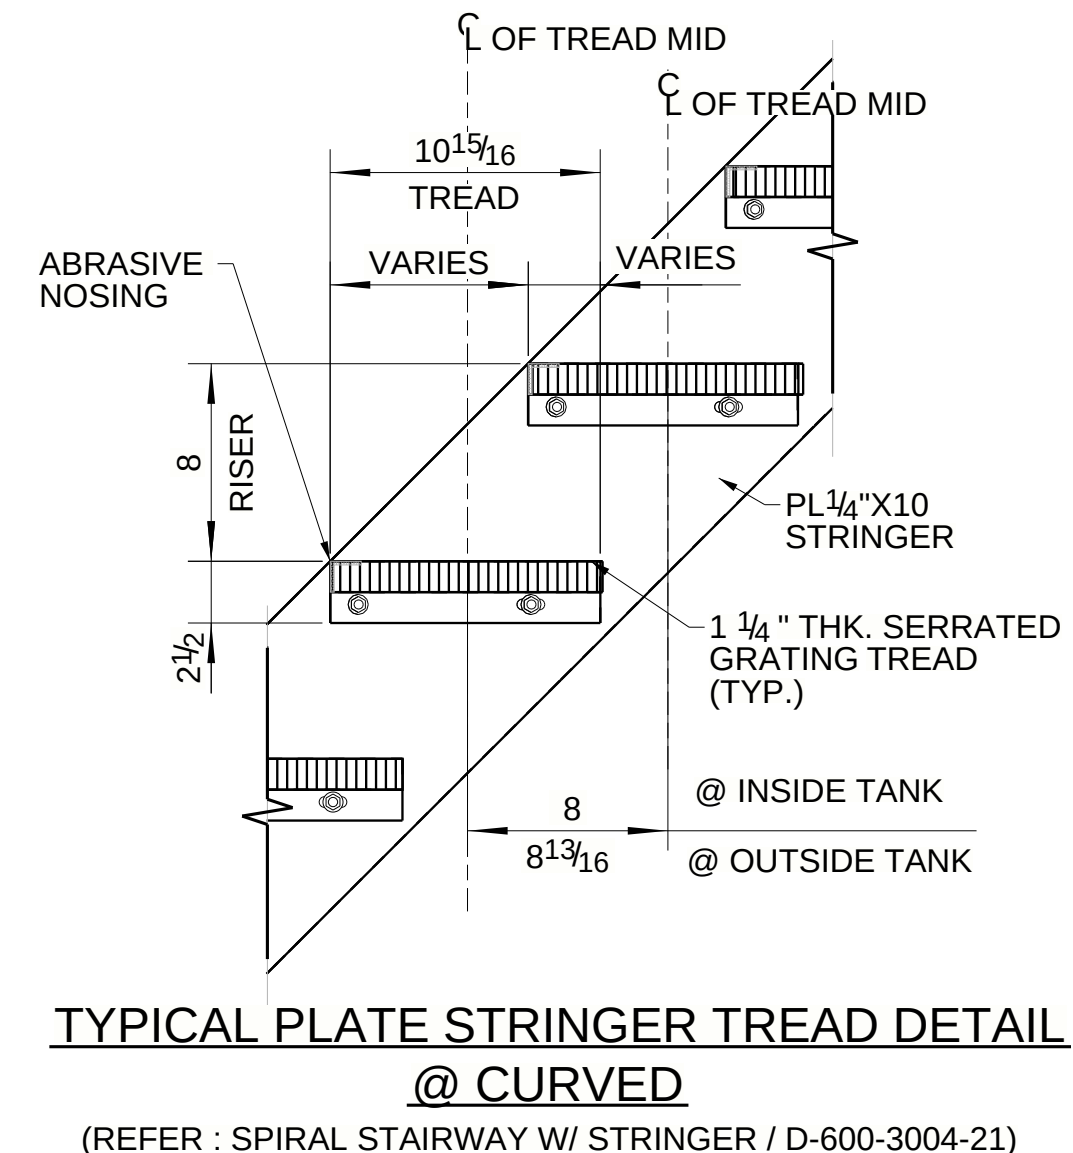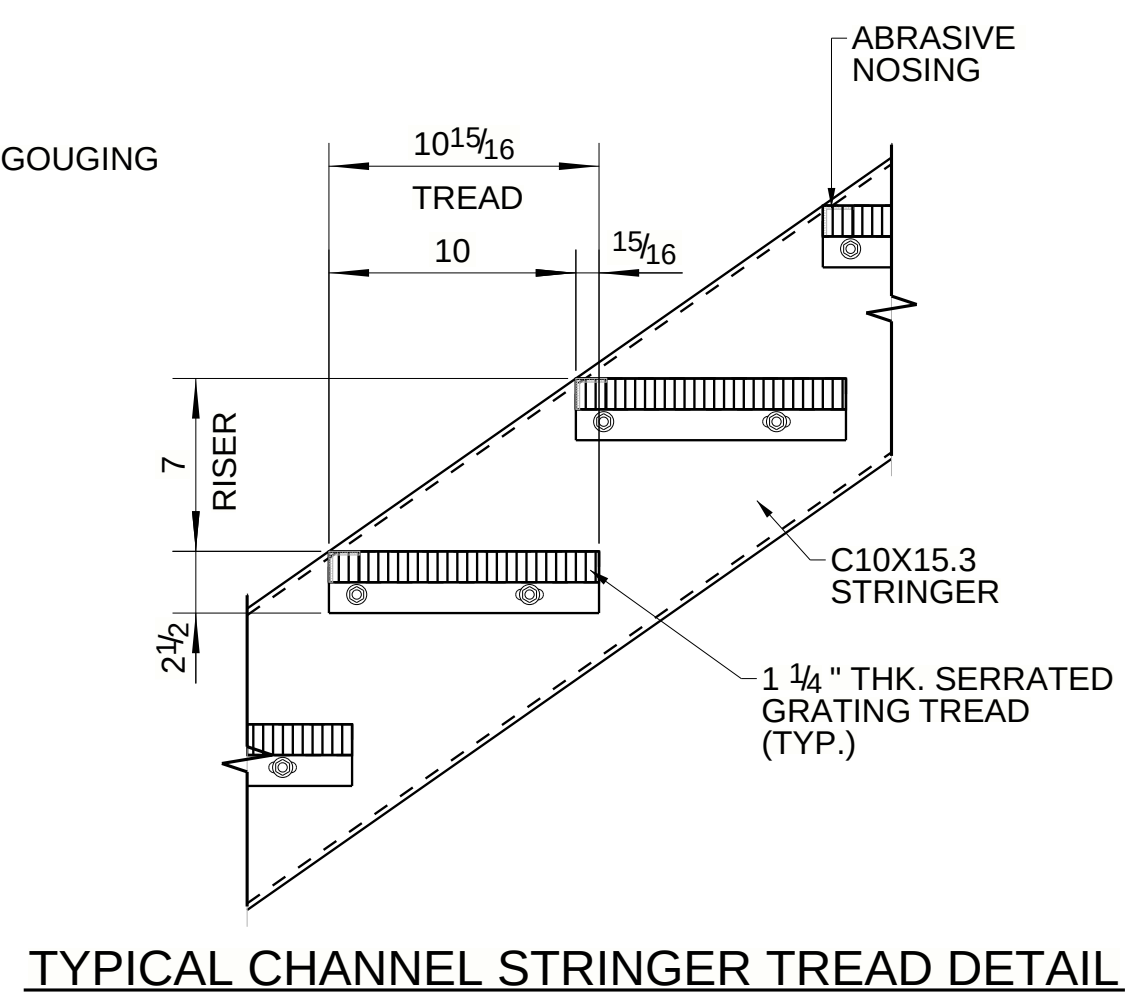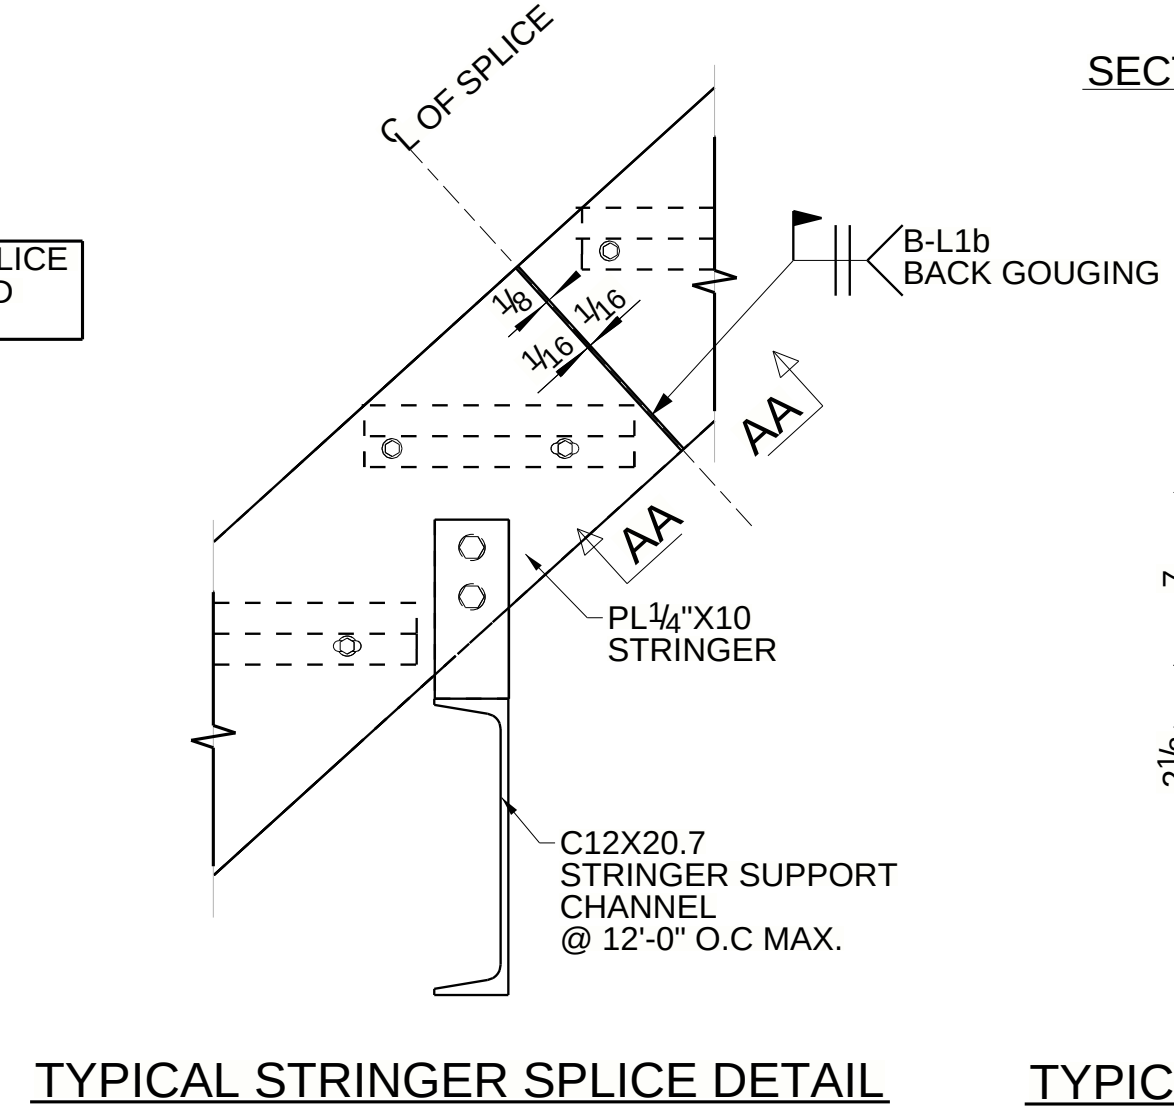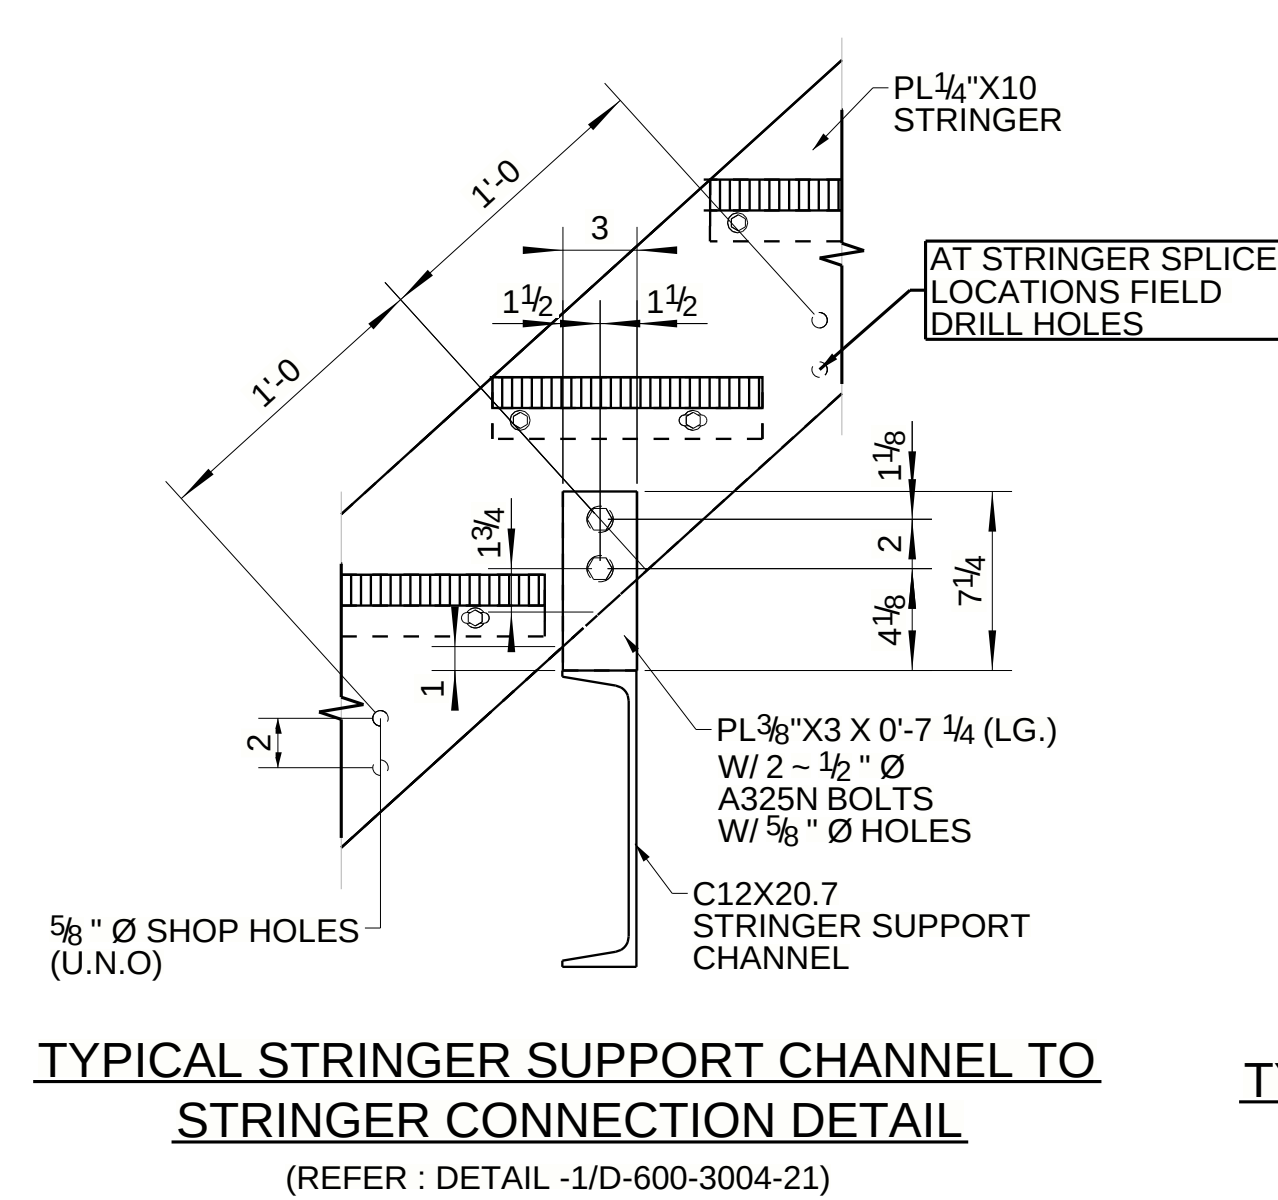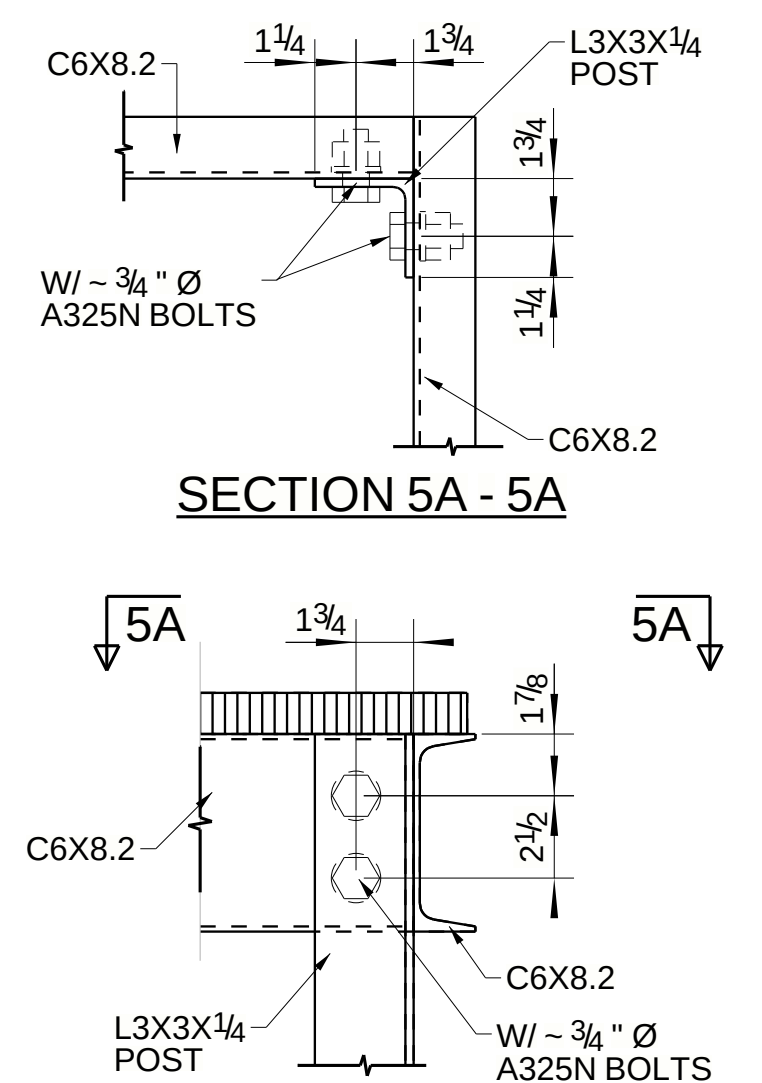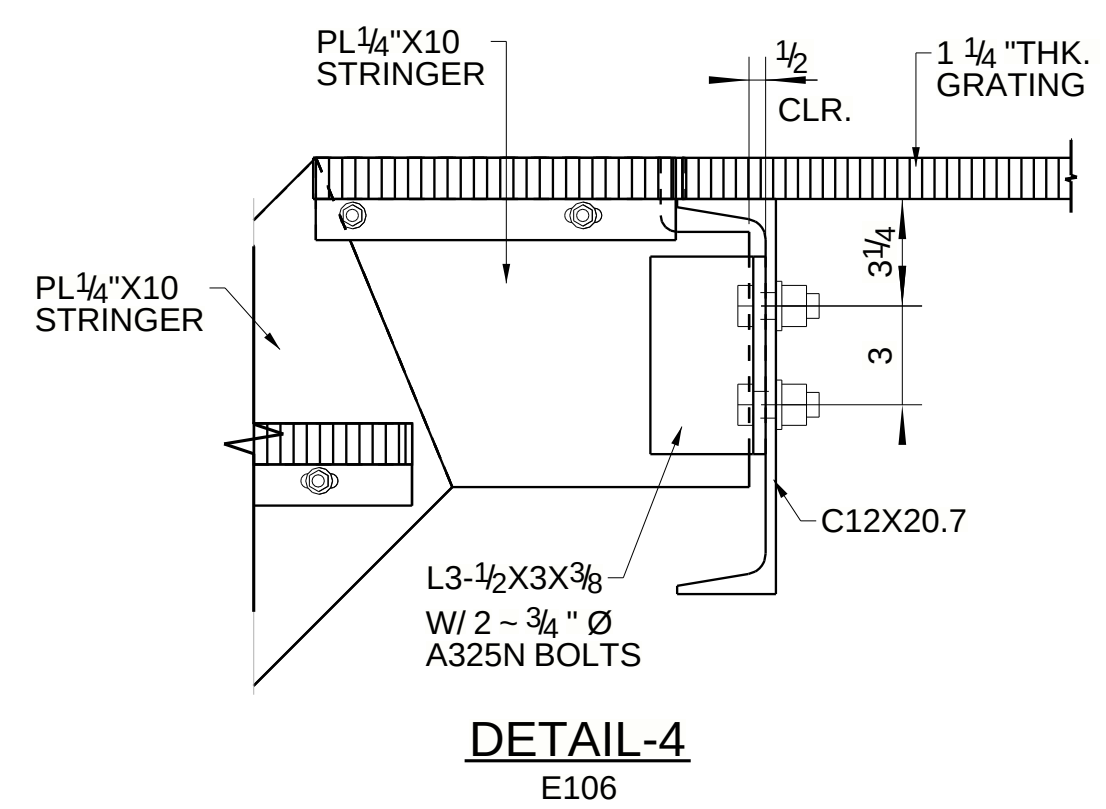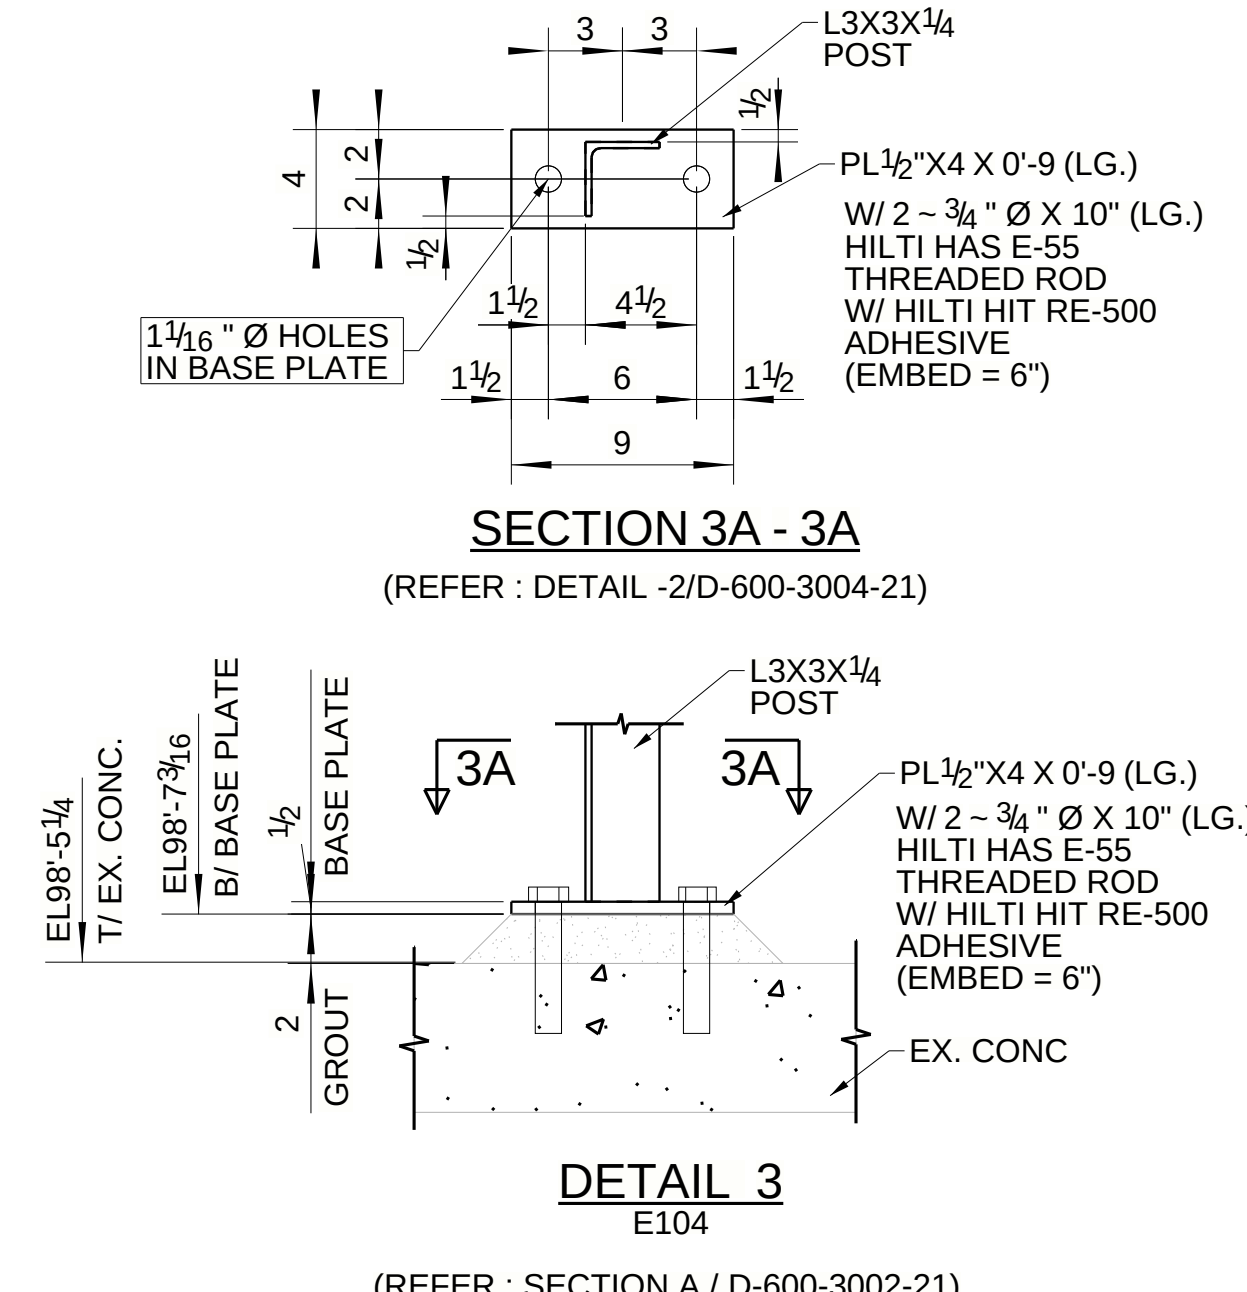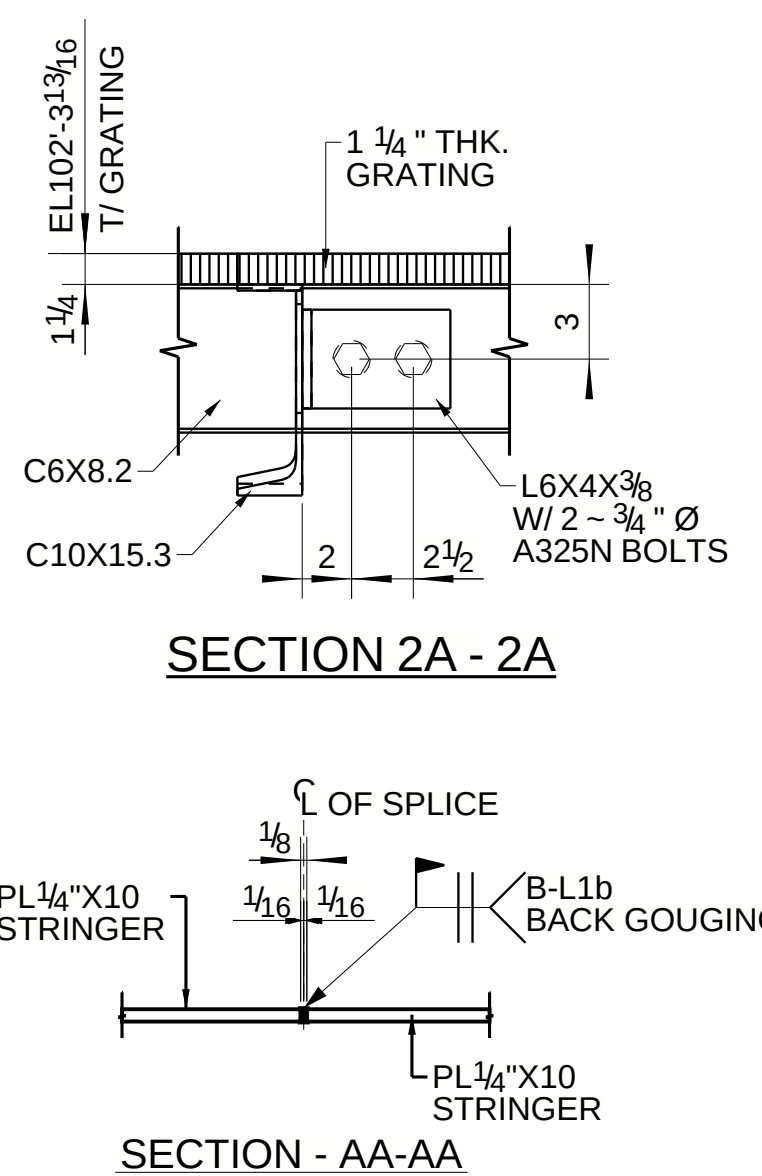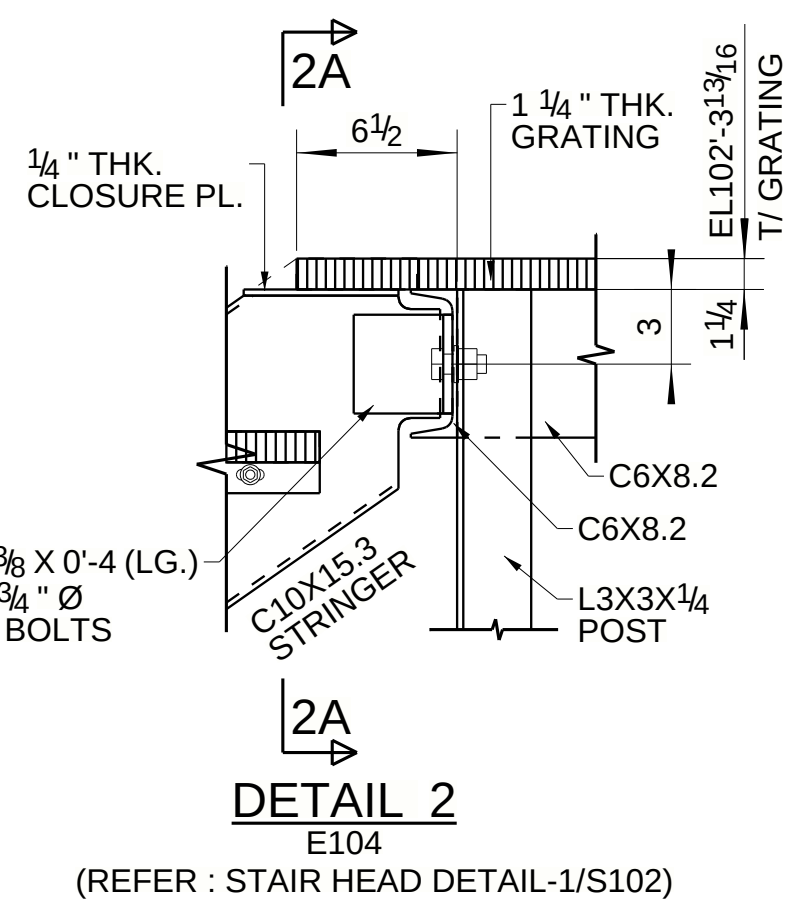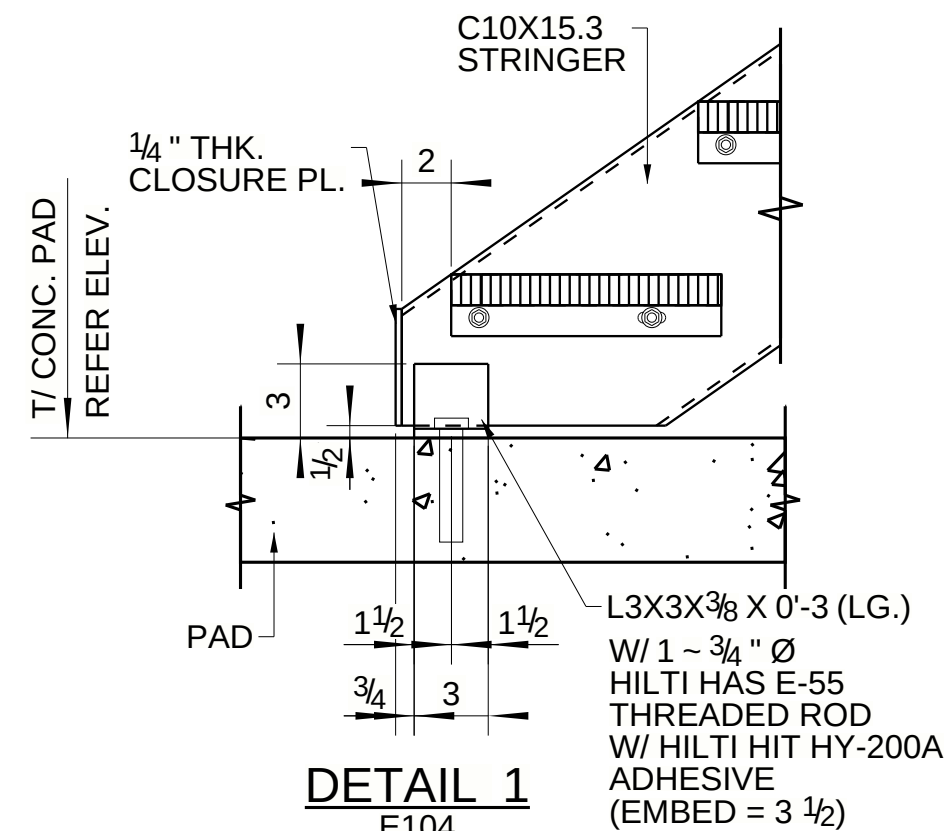

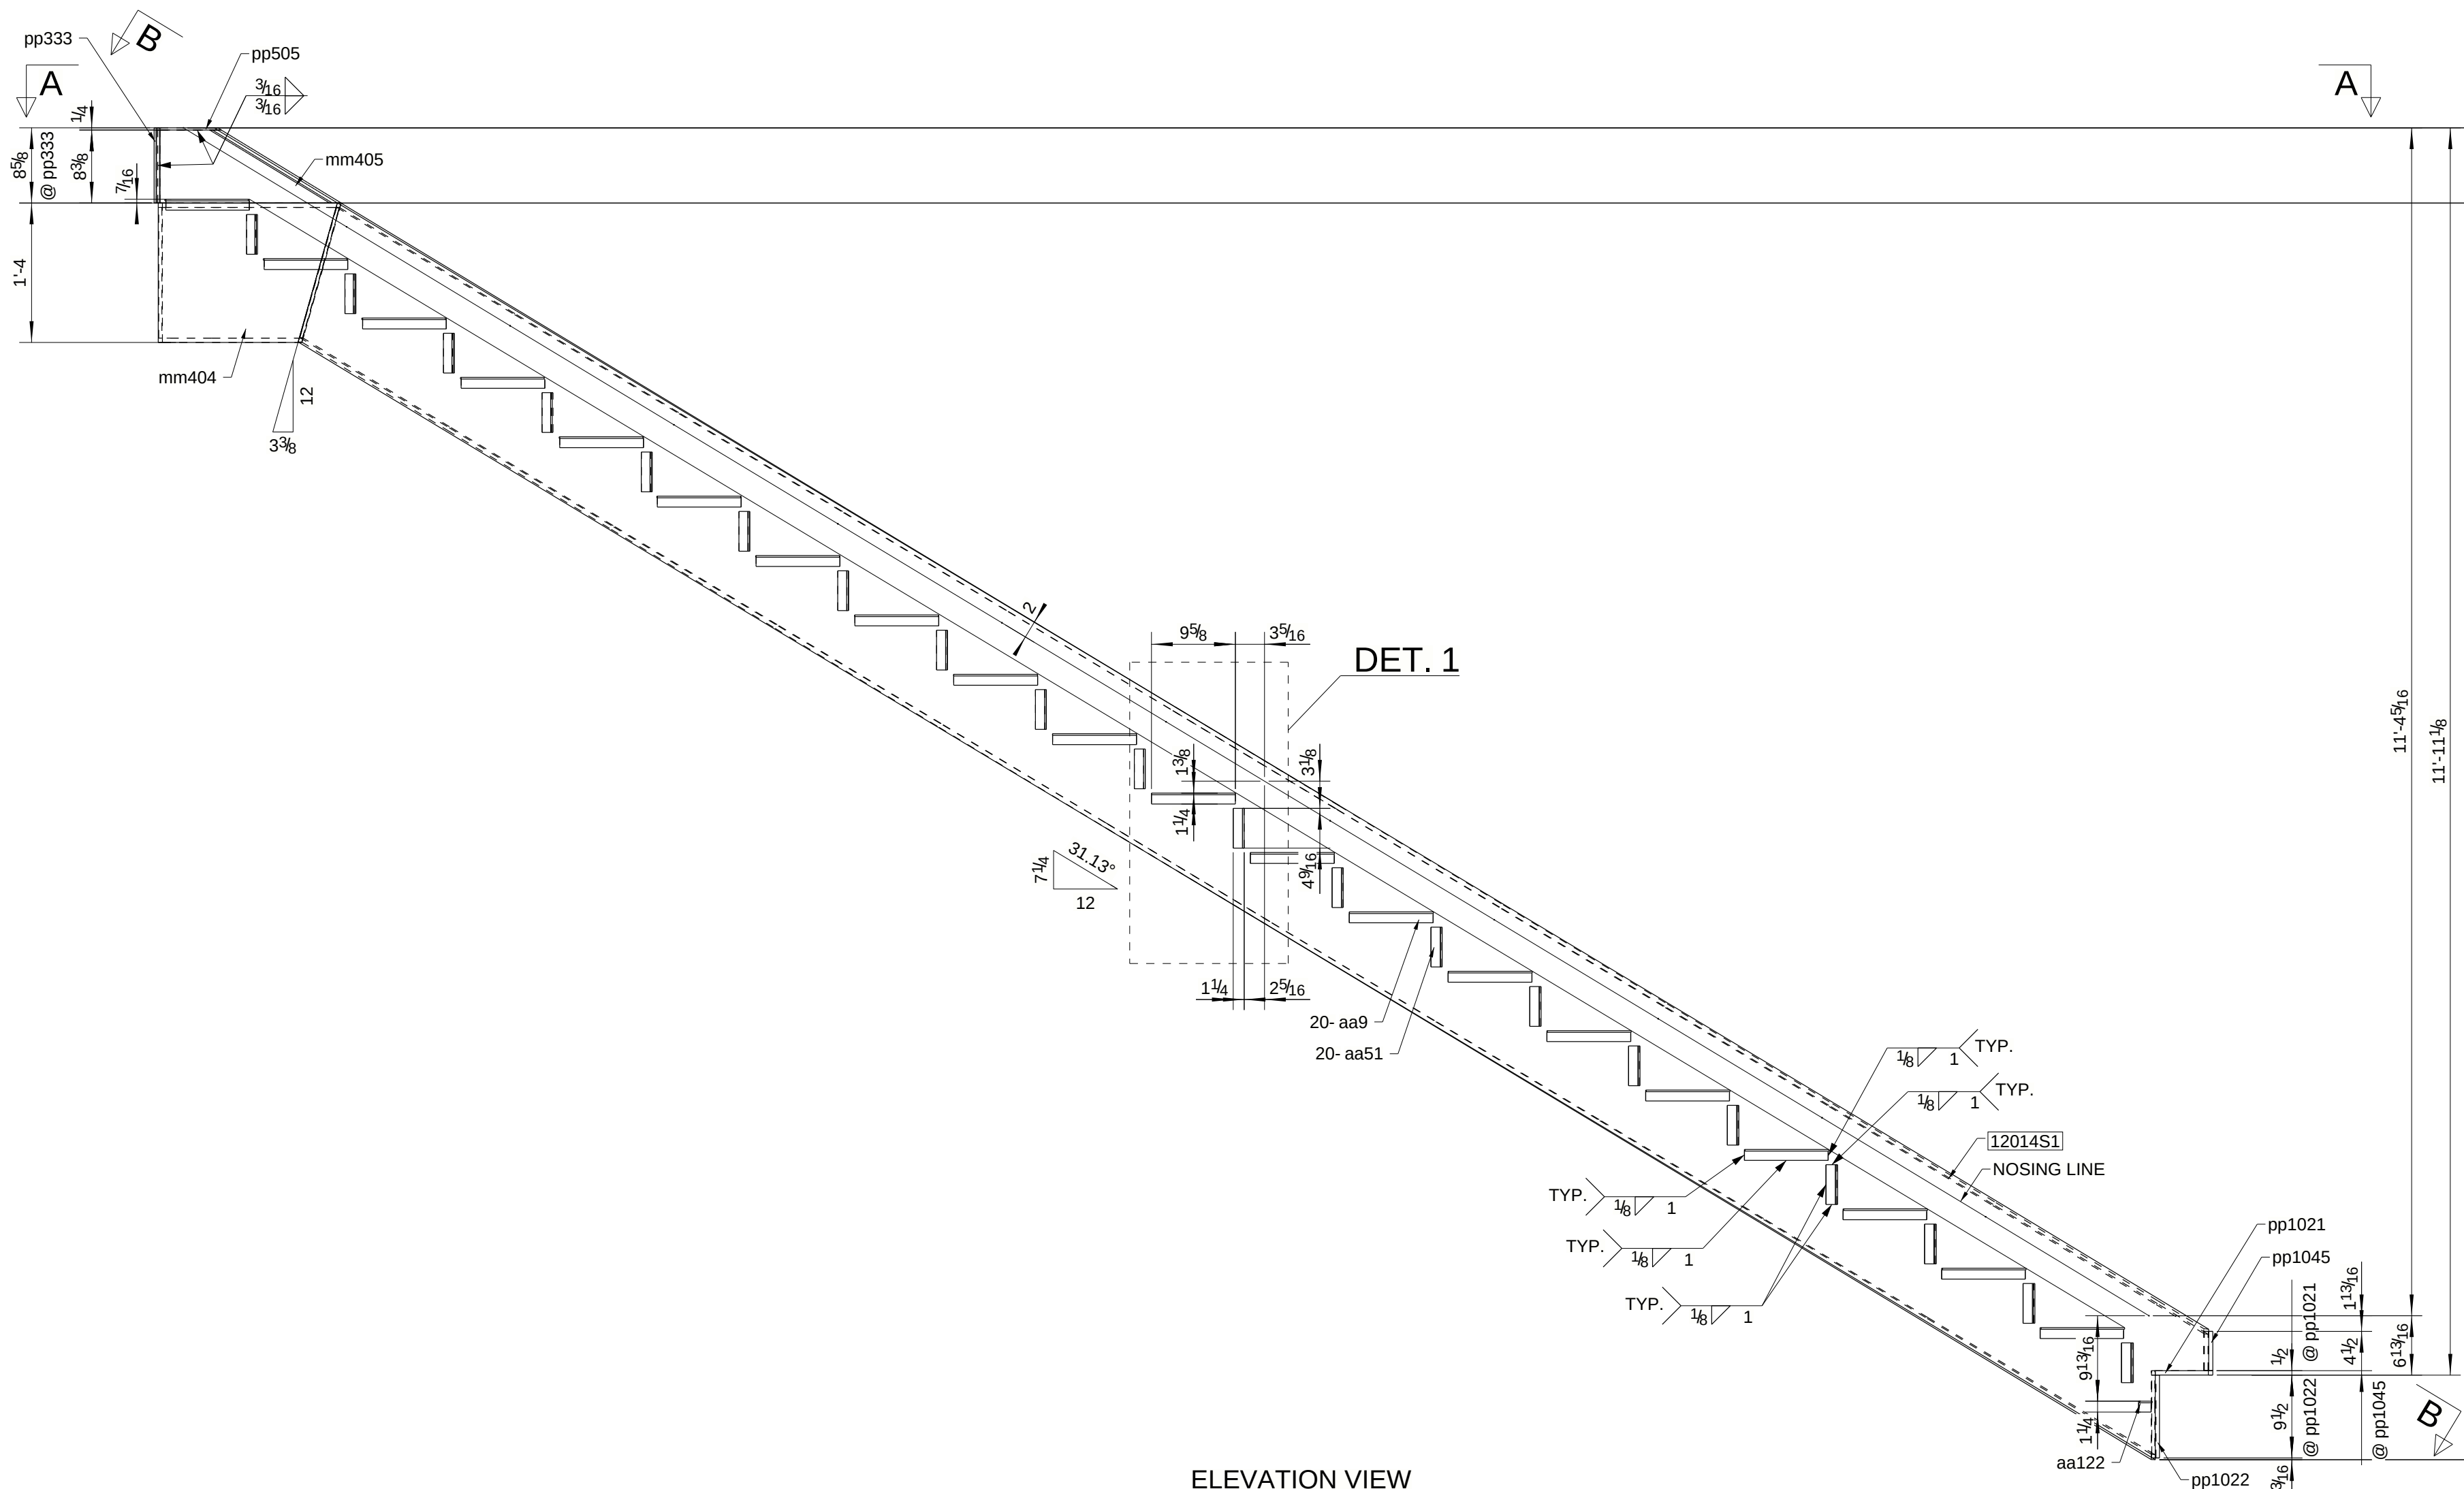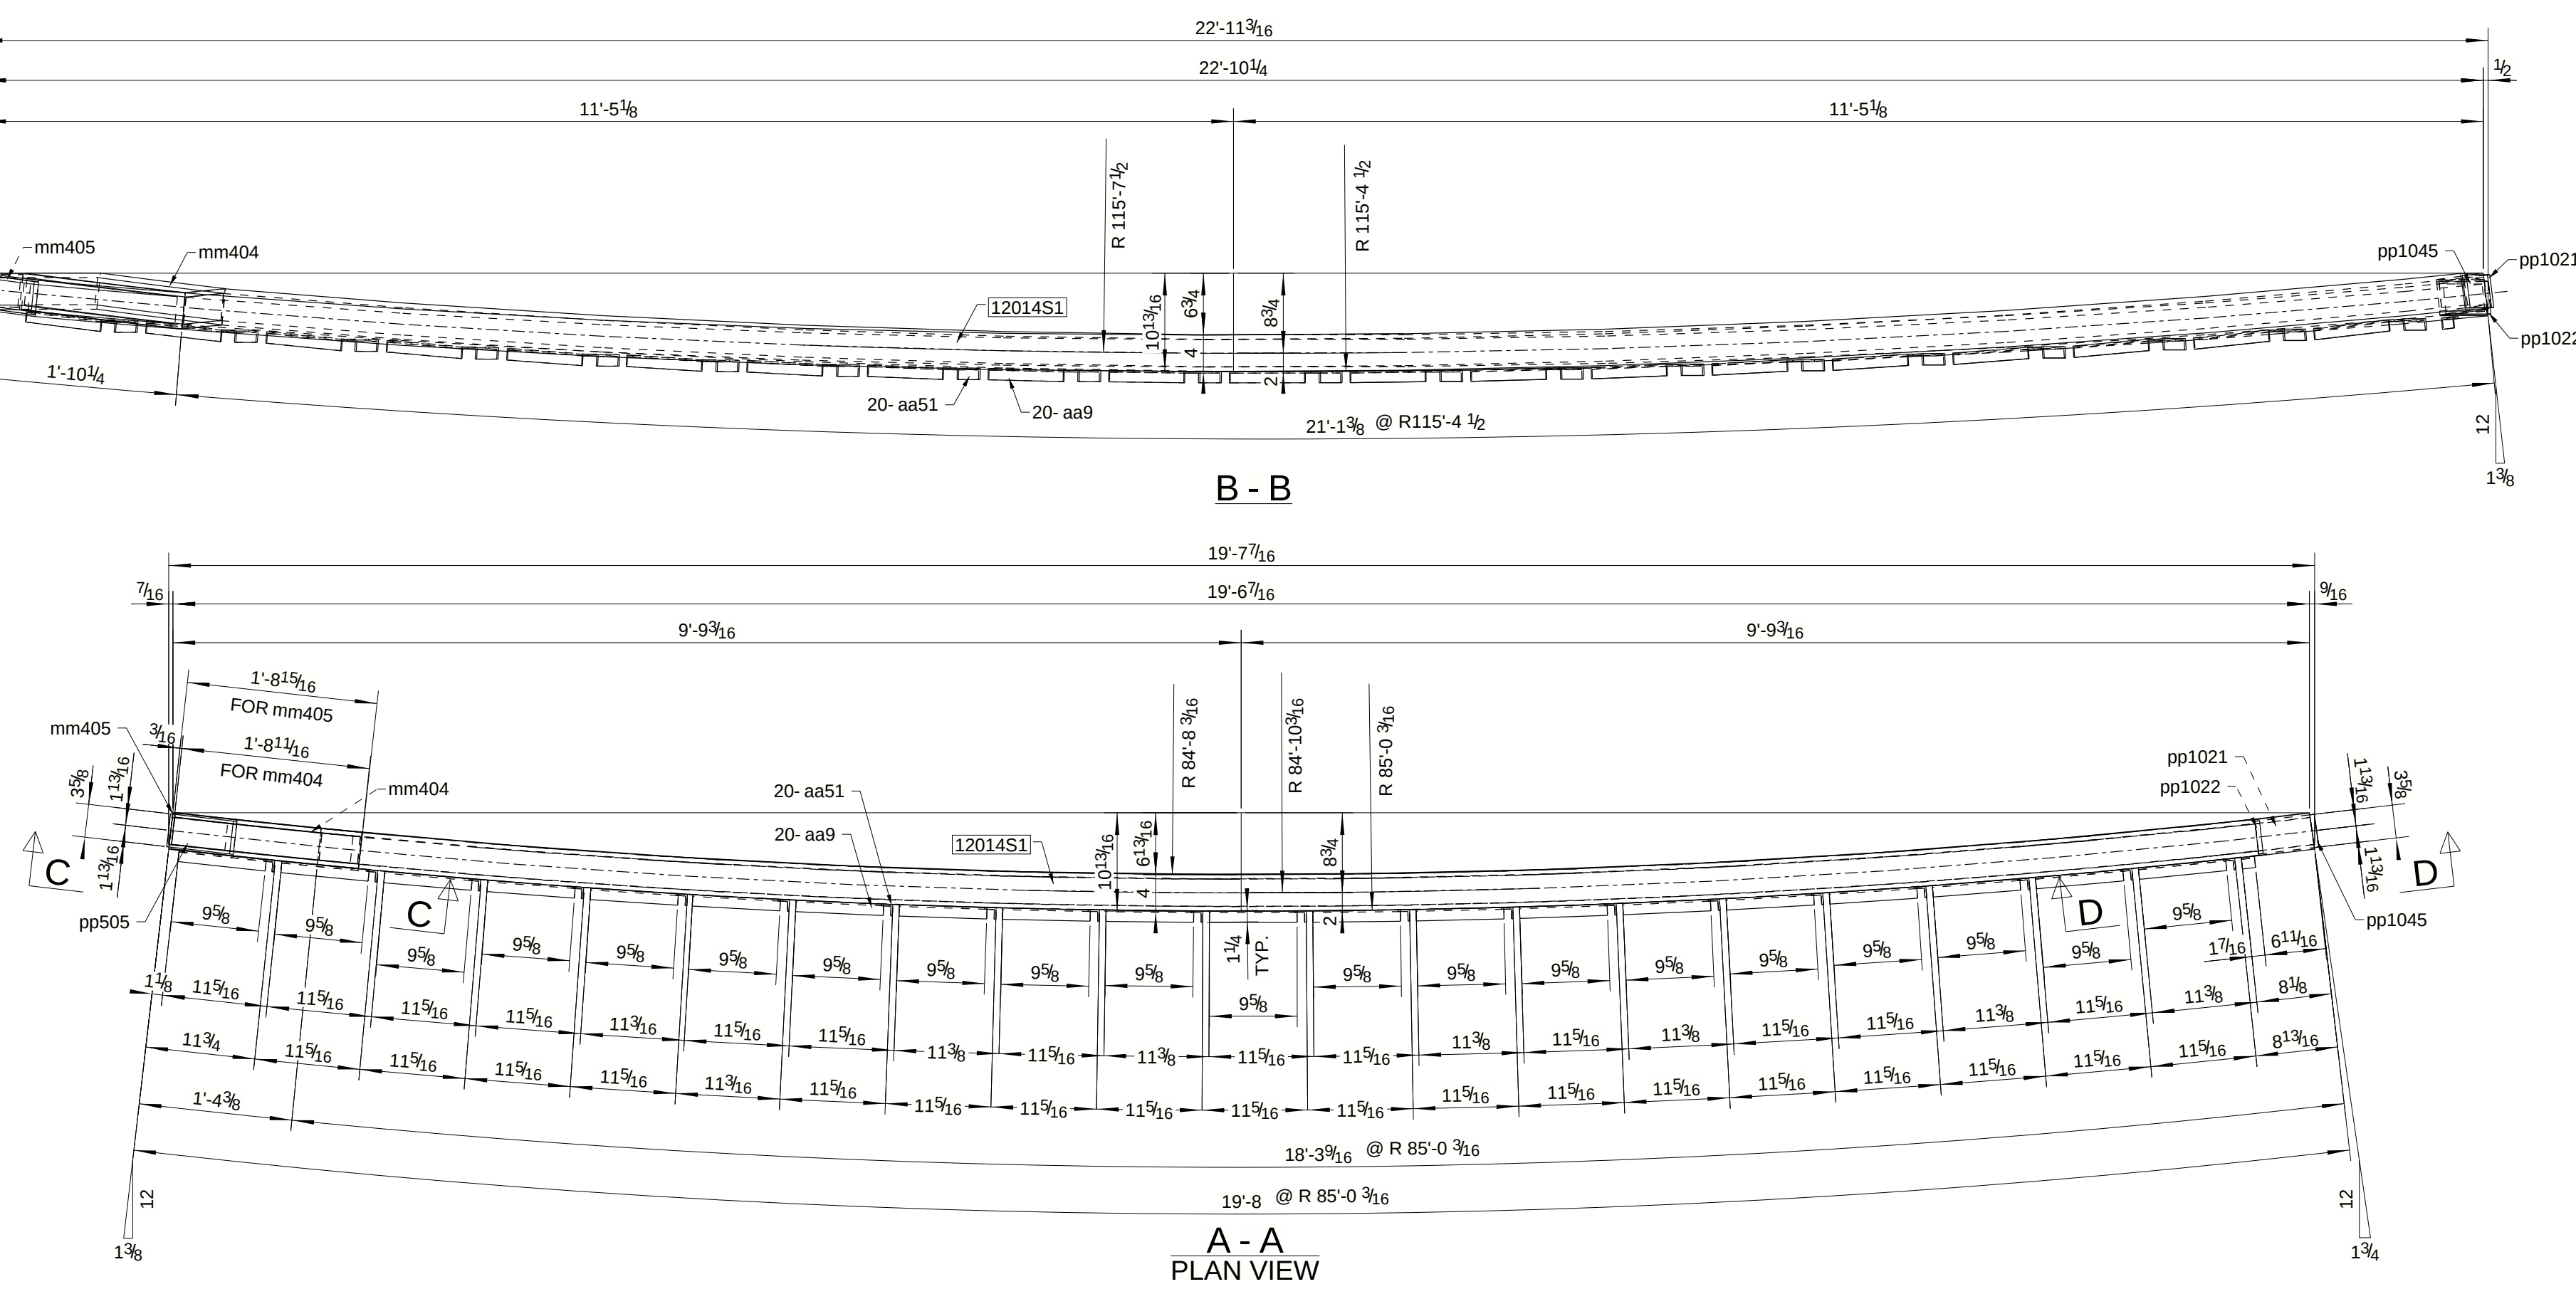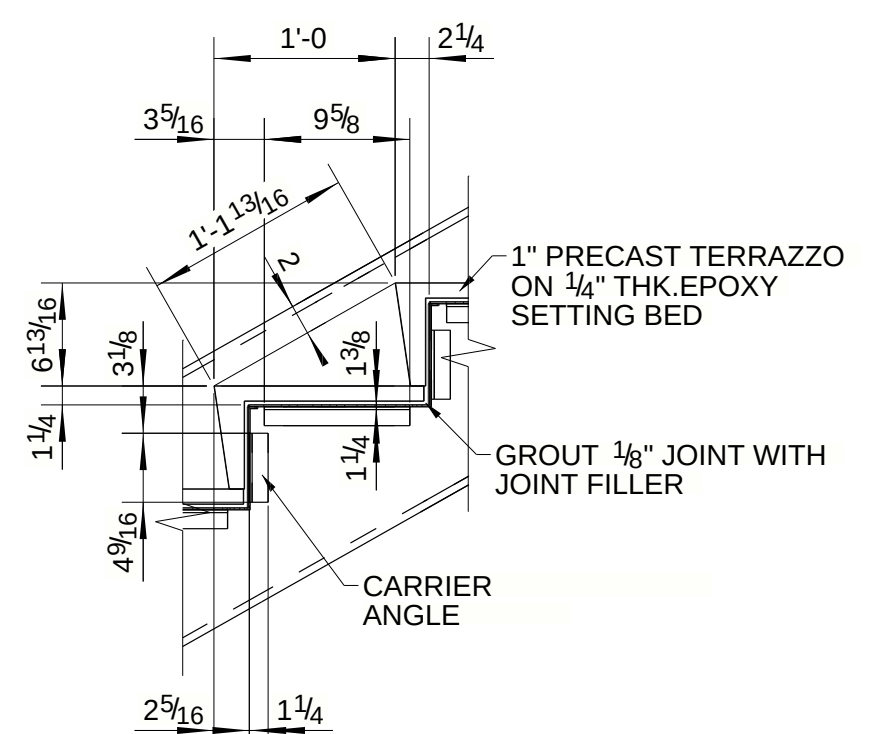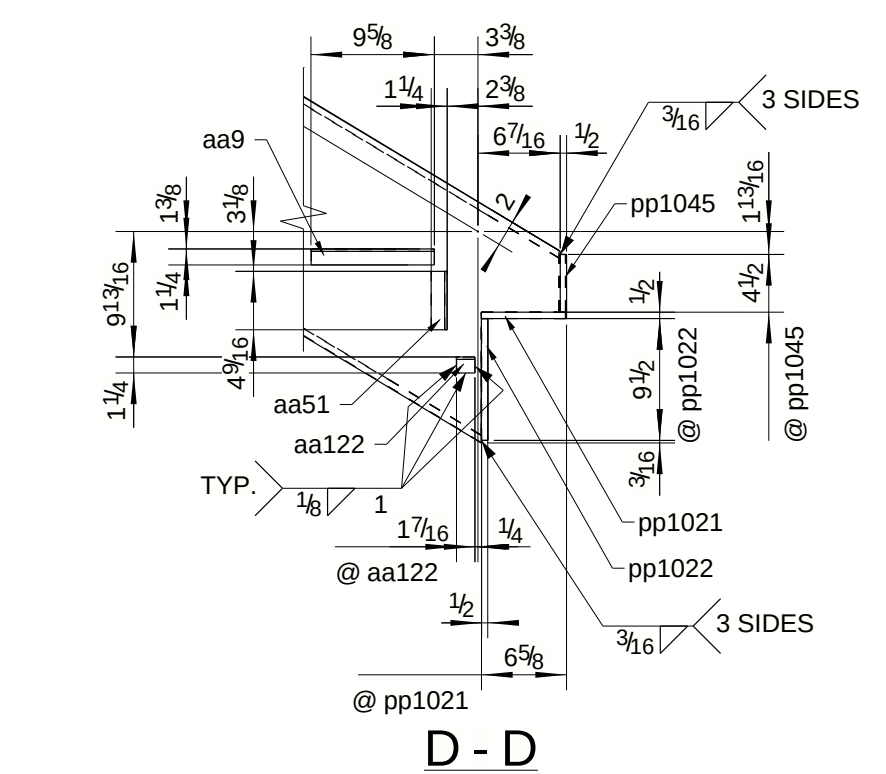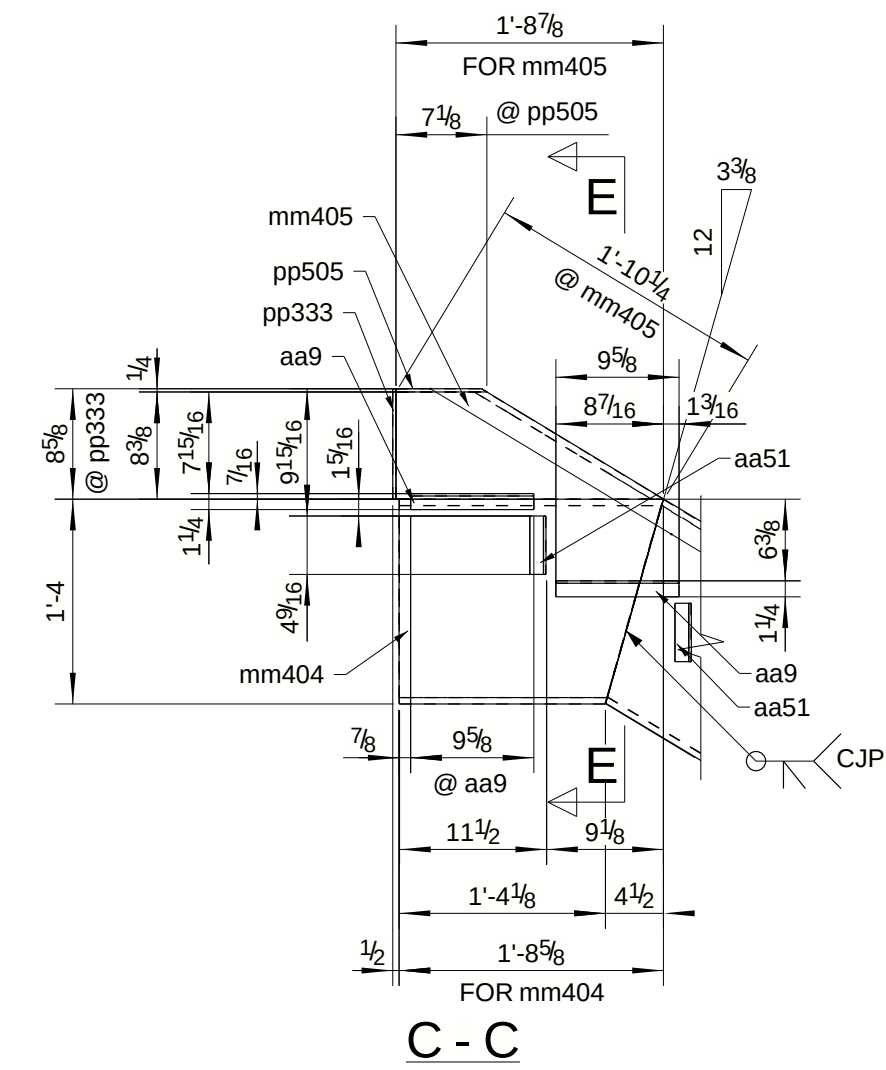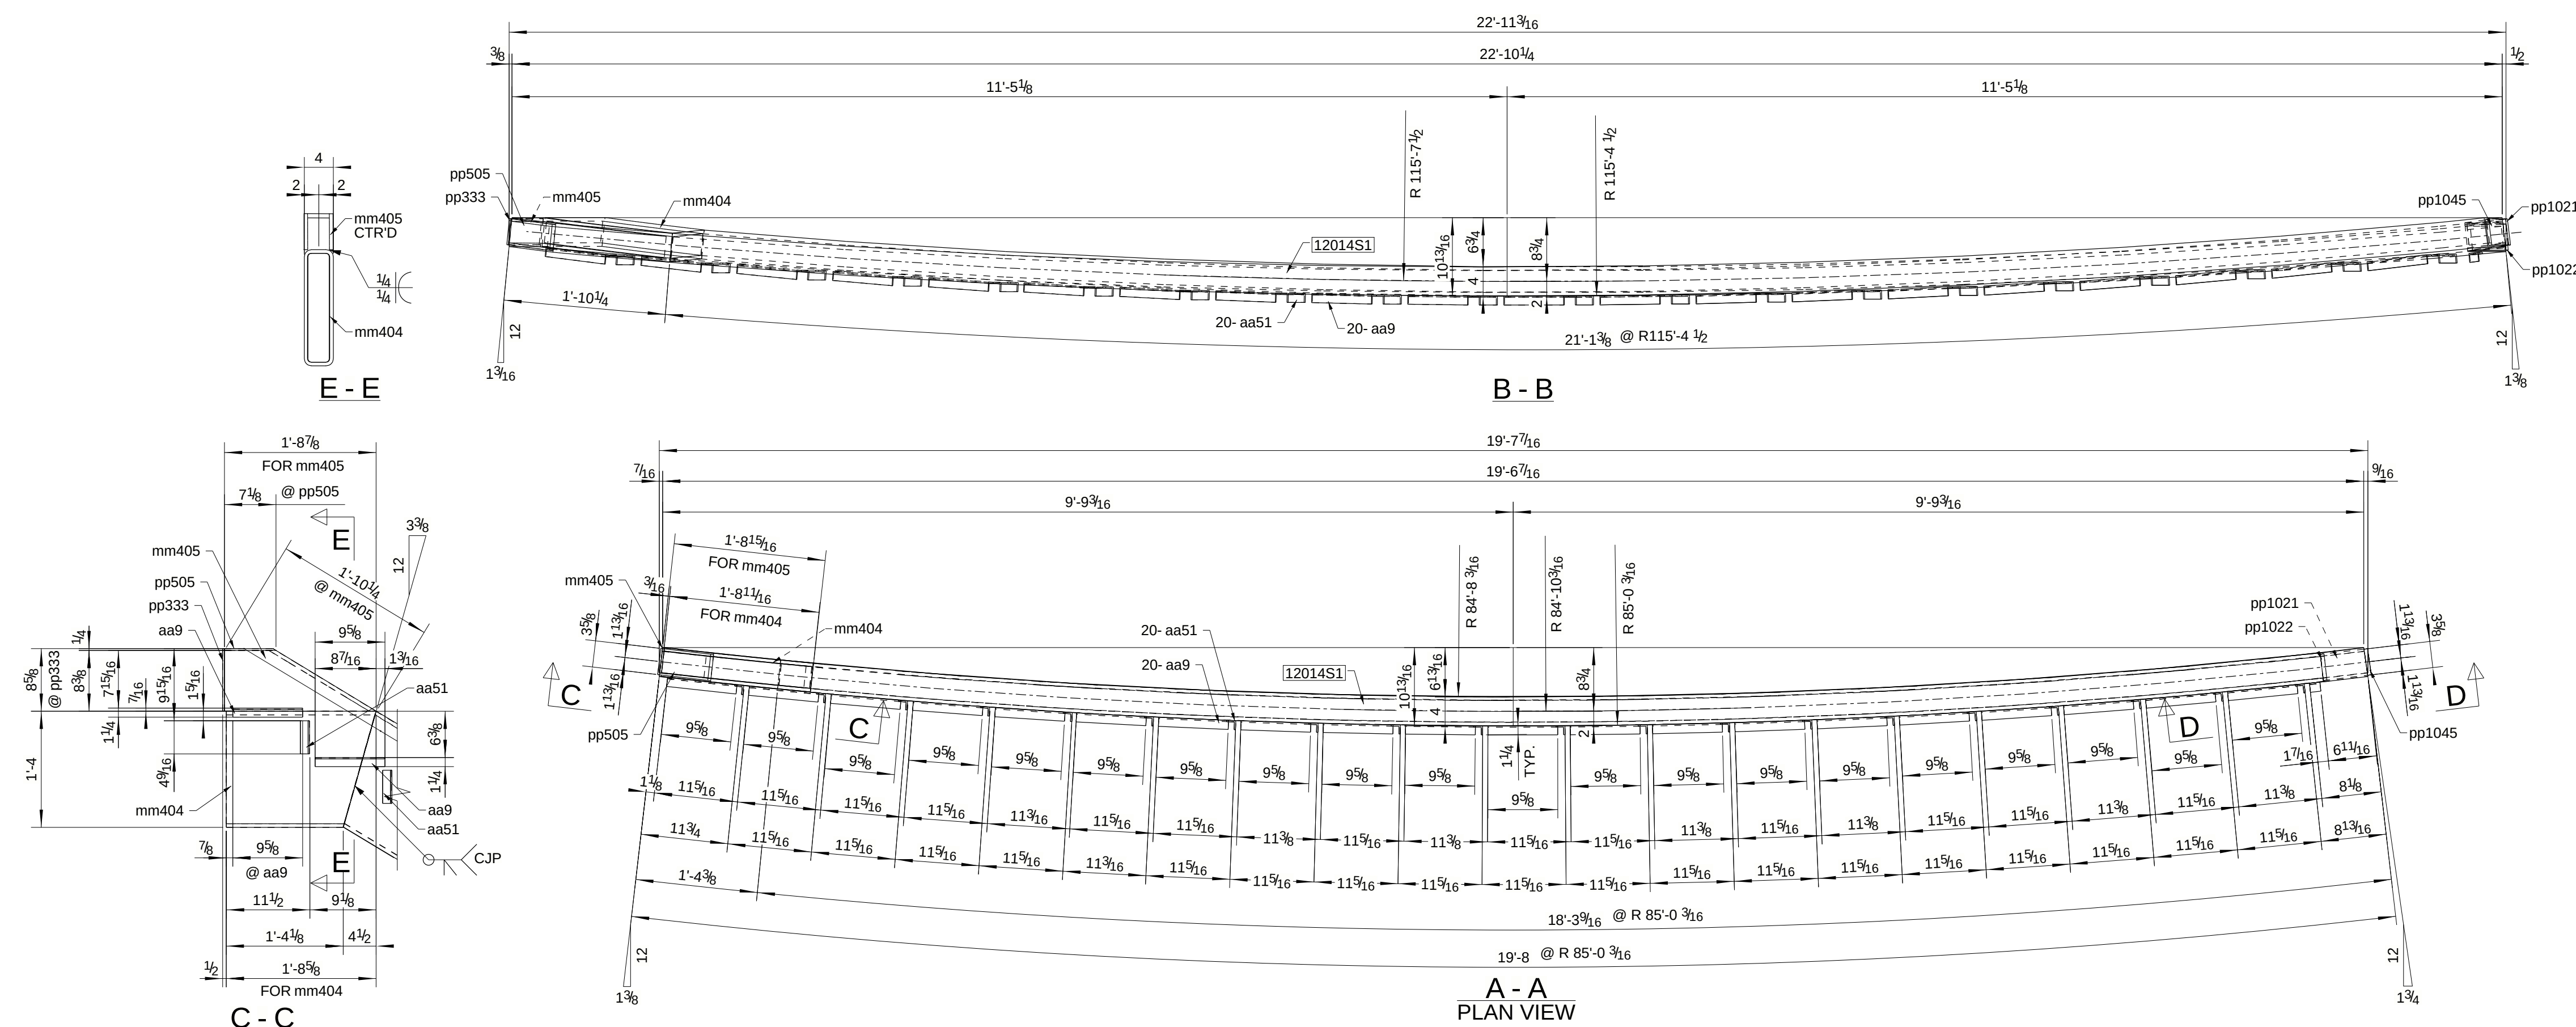




BILL OF MATERIAL					
MARK	QTY	DESCRIPTION	LENGTH	WEIGHT	REMARKS
1201451	1	STRINGER			ISQ-2
1201451	1	HSS16X4X1/2	21'-1 5/16"	1064	A500-GR-B
aa9	20	L1-1/4X1-1/4X3/16	0'-9 5/8"	24	A36
aa51	20	L1-1/4X1-1/4X3/16	0'-4 9/16"	11	A36
aa122	1	L1-1/4X1-1/4X3/16	0'-1 7/16"	0	A36
mm404	1	HSS16X4X1/2	1'-8 3/4"	101	A500-GR-B
mm405	1	HSS16X4X1/2	1'-10 5/16"	109	A500-GR-B
pp333	1	PL1/4"X3 5/8"	0'-8 5/8"	2	A36
pp505	1	PL1/4"X3 5/8"	0'-7 1/8"	2	A36
pp1021	1	PL1/2"X3 5/8"	0'-6 5/8"	3	A36
pp1022	1	PL1/2"X3 5/8"	0'-9 1/2"	5	A36
pp1045	1	PL1/2"X3 5/8"	0'-4 1/2"	2	A36
		TOTAL WEIGHT THIS DRAWING		1324	

- SHOP NOTES :
1. ALL WELDS TO BE 3/16" ALL AROUND OR DOUBLE SIDED FILLET WELD UNLESS SHOWN OTHERWISE.
 2. TAG ALL MEMBERS IN A VERTICAL POSITION ON LEFT END AS DETAILED.
 3. ALL SHARP EDGES SHALL BE GROUND SMOOTH AND CORNERS ROUNDED OFF.
 4. ALL TAIL (RUNNING) DIMENSIONS SHALL BE MEASURED FROM END OF BEAM, COLUMN,...ETC.
"RD" DENOTES RUNNING DIMENSION
 5. ALL COPES SHALL BE MEASURED FROM END OF BEAM.
 6. ALL BEAM COPES TO BE CUT WITH 1/2" RADIUS U.N.O.
 7. ALL CLIP ANGLES SHALL BE ATTACHED TO BEAM WITH 3/16" FILLET WELD ON THREE SIDES UNLESS SHOWN OTHERWISE.
 8. FOR INDIVIDUAL DETAILS OF PLATES, ANGLES, ETC..., SEE GATHER SHEETS/ SINGLE PART SHEETS.
 9. B.T.S. DENOTES BOLT TO SHIP WITH A307 BOLTS. ASSEMBLE AFTER PAINTING/GALV.
 10. SHOP CLOSE ALL GAPS.
 11. HOLE PATTERNS NOTED "A490SC_TC" ARE FOR SLIP CRITICAL BOLTS WITH TENSION CONTROL BOLTS. DO NOT ADD PAINT AT CONTACT SURFACES. CONTACT SURFACES ARE TO BE FREE OF BURRS AND ALL FOREIGN MATERIAL.

BILL OF MATERIAL					
MARK	NO	DESCRIPTION	LENGTH	WEIGHT	REMARKS
	PCS				
S6	1	PL1/4"X10"	17'-10 1/8"	162	A36
pp76	6	PL3/8"X2 3/4"	0'-5 1/2"	10	A36
pp29	1	PL1/4"X10"	17'-6"	155	A36
mm15	13	GRTG1 1/4"X10 15/16"	2'-5 5/8"	1531	A36
mm33	5	GRTG1 1/4"X10 15/16"	2'-5 5/8"	589	A36
52		3/8"Ø A307 BOLT	0'-1 1/4"	4	82 PLAIN WASHER 82 PLAIN WASHER
20		3/8"Ø A307 BOLT	0'-1 1/4"	1	82 PLAIN WASHER 82 PLAIN WASHER

- SHOP NOTES:
1. ALL WELDS TO BE 3/16" ALL AROUND OR DOUBLE SIDED FILLET WELD UNLESS SHOWN OTHERWISE.
 2. TAG ALL MEMBERS IN A VERTICAL POSITION ON LEFT END AS DETAILED.
 3. ALL SHARP EDGES SHALL BE GROUND SMOOTH AND CORNERS ROUNDED OFF.
 4. ALL TAIL (RUNNING) DIMENSIONS SHALL BE MEASURED FROM END OF BEAM, COLUMN,, ETC.
 5. ALL COPES SHALL BE MEASURED FROM END OF BEAM.
 6. ALL BEAM COPES TO BE CUT WITH 1/2" RADIUS U.N.O.
 7. ALL CLIP ANGLES SHALL BE ATTACHED TO BEAM WITH 3/16" FILLET WELD ON THREE SIDES UNLESS SHOWN OTHERWISE.
 8. FOR INDIVIDUAL DETAILS OF PLATES, ANGLES, ETC... SEE GATHER SHEETS/ SINGLE PART SHEETS.
 9. B.T.S. DENOTES BOLT TO SHIP WITH A307 BOLTS. ASSEMBLE AFTER PAINTING/GALV.
 10. SHOP CLOSE ALL GAPS.
 11. ALL JOINTS TO BE SEAL WELDED WITH CONT. 1/8" FILLET OR BUTT WELD AS REQ'D
 12. PROVIDE VENT HOLES AS REQ'D FOR GALV.
 13. PLUG VENT HOLES AFTER GALV.

WORK THIS SHEET WITH S6-1

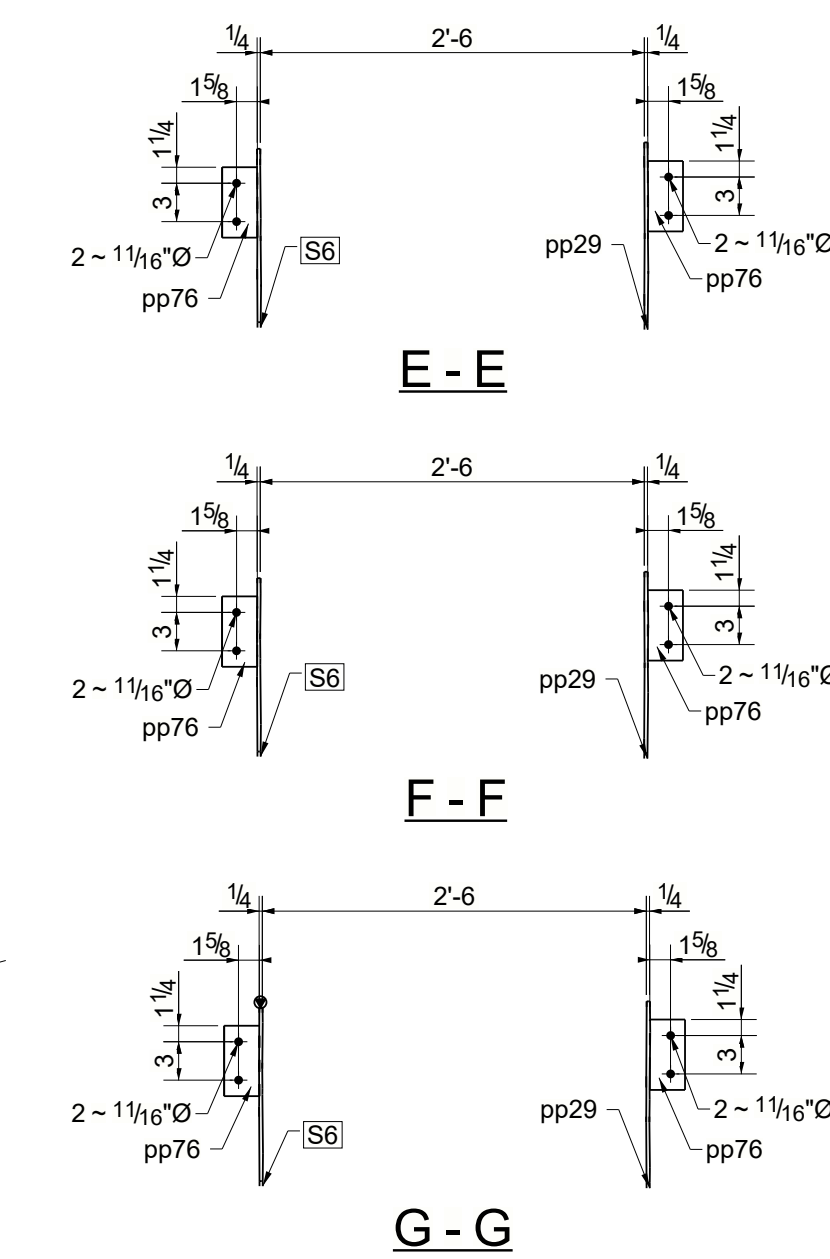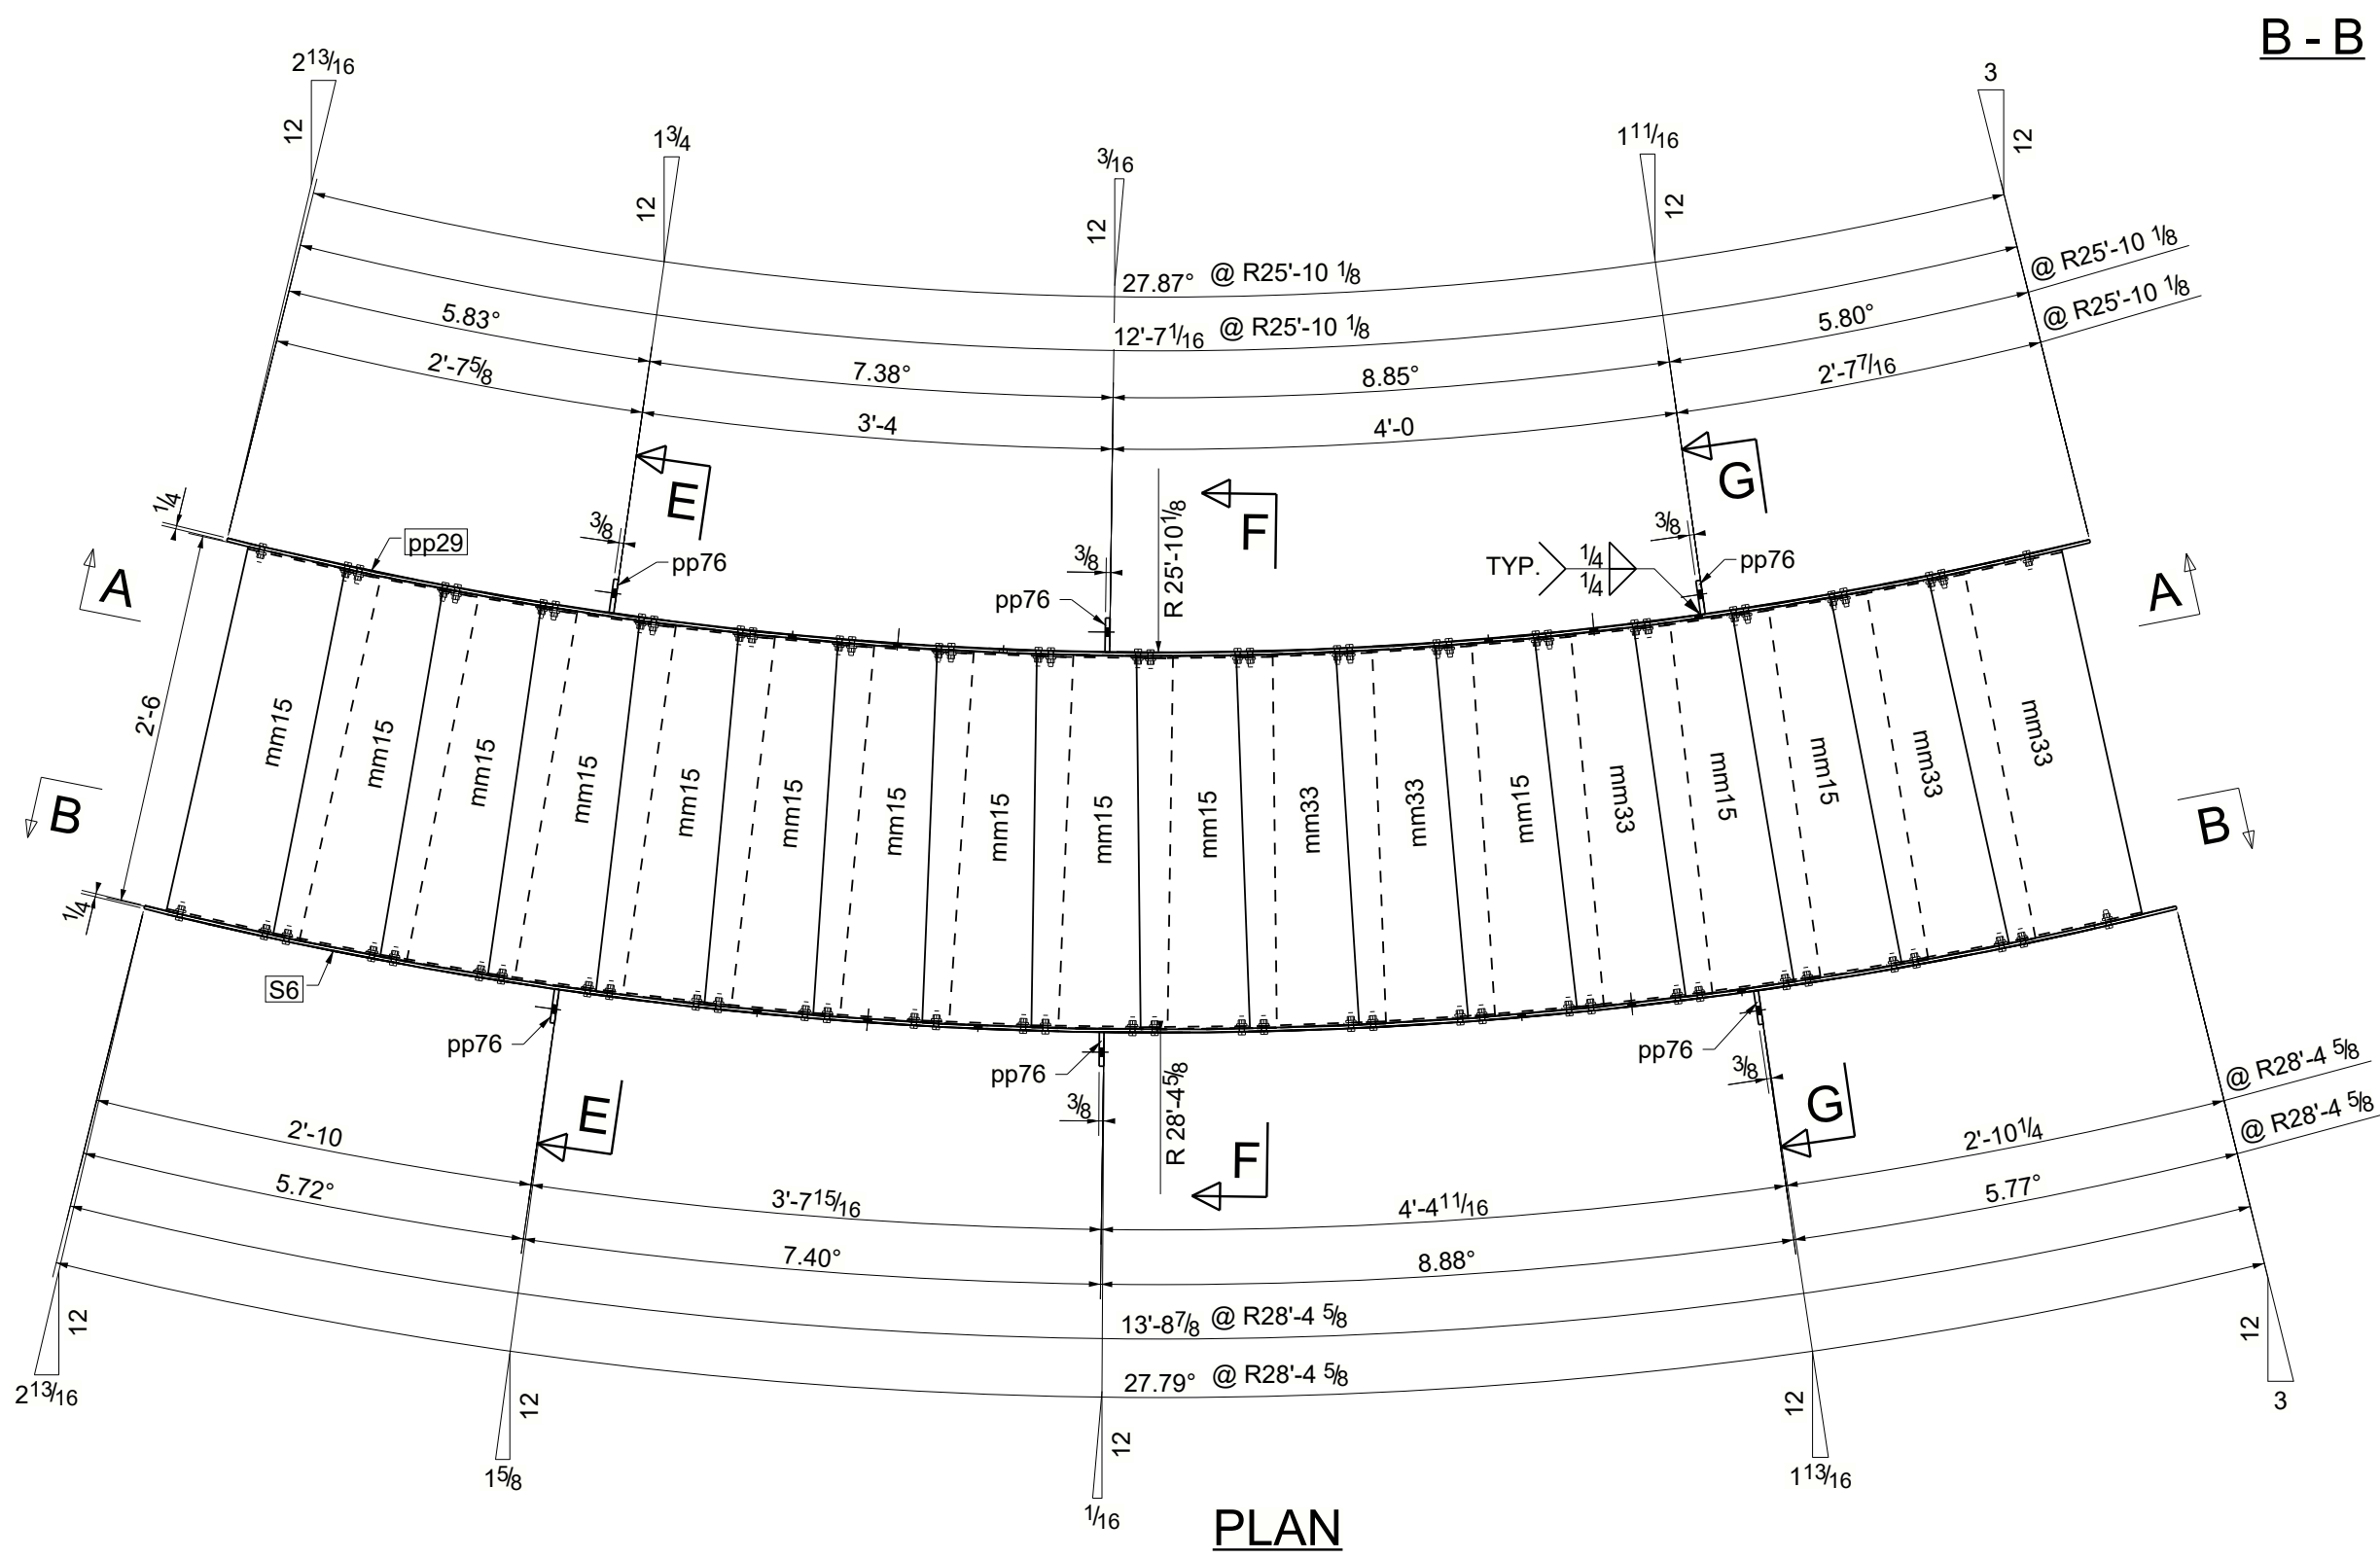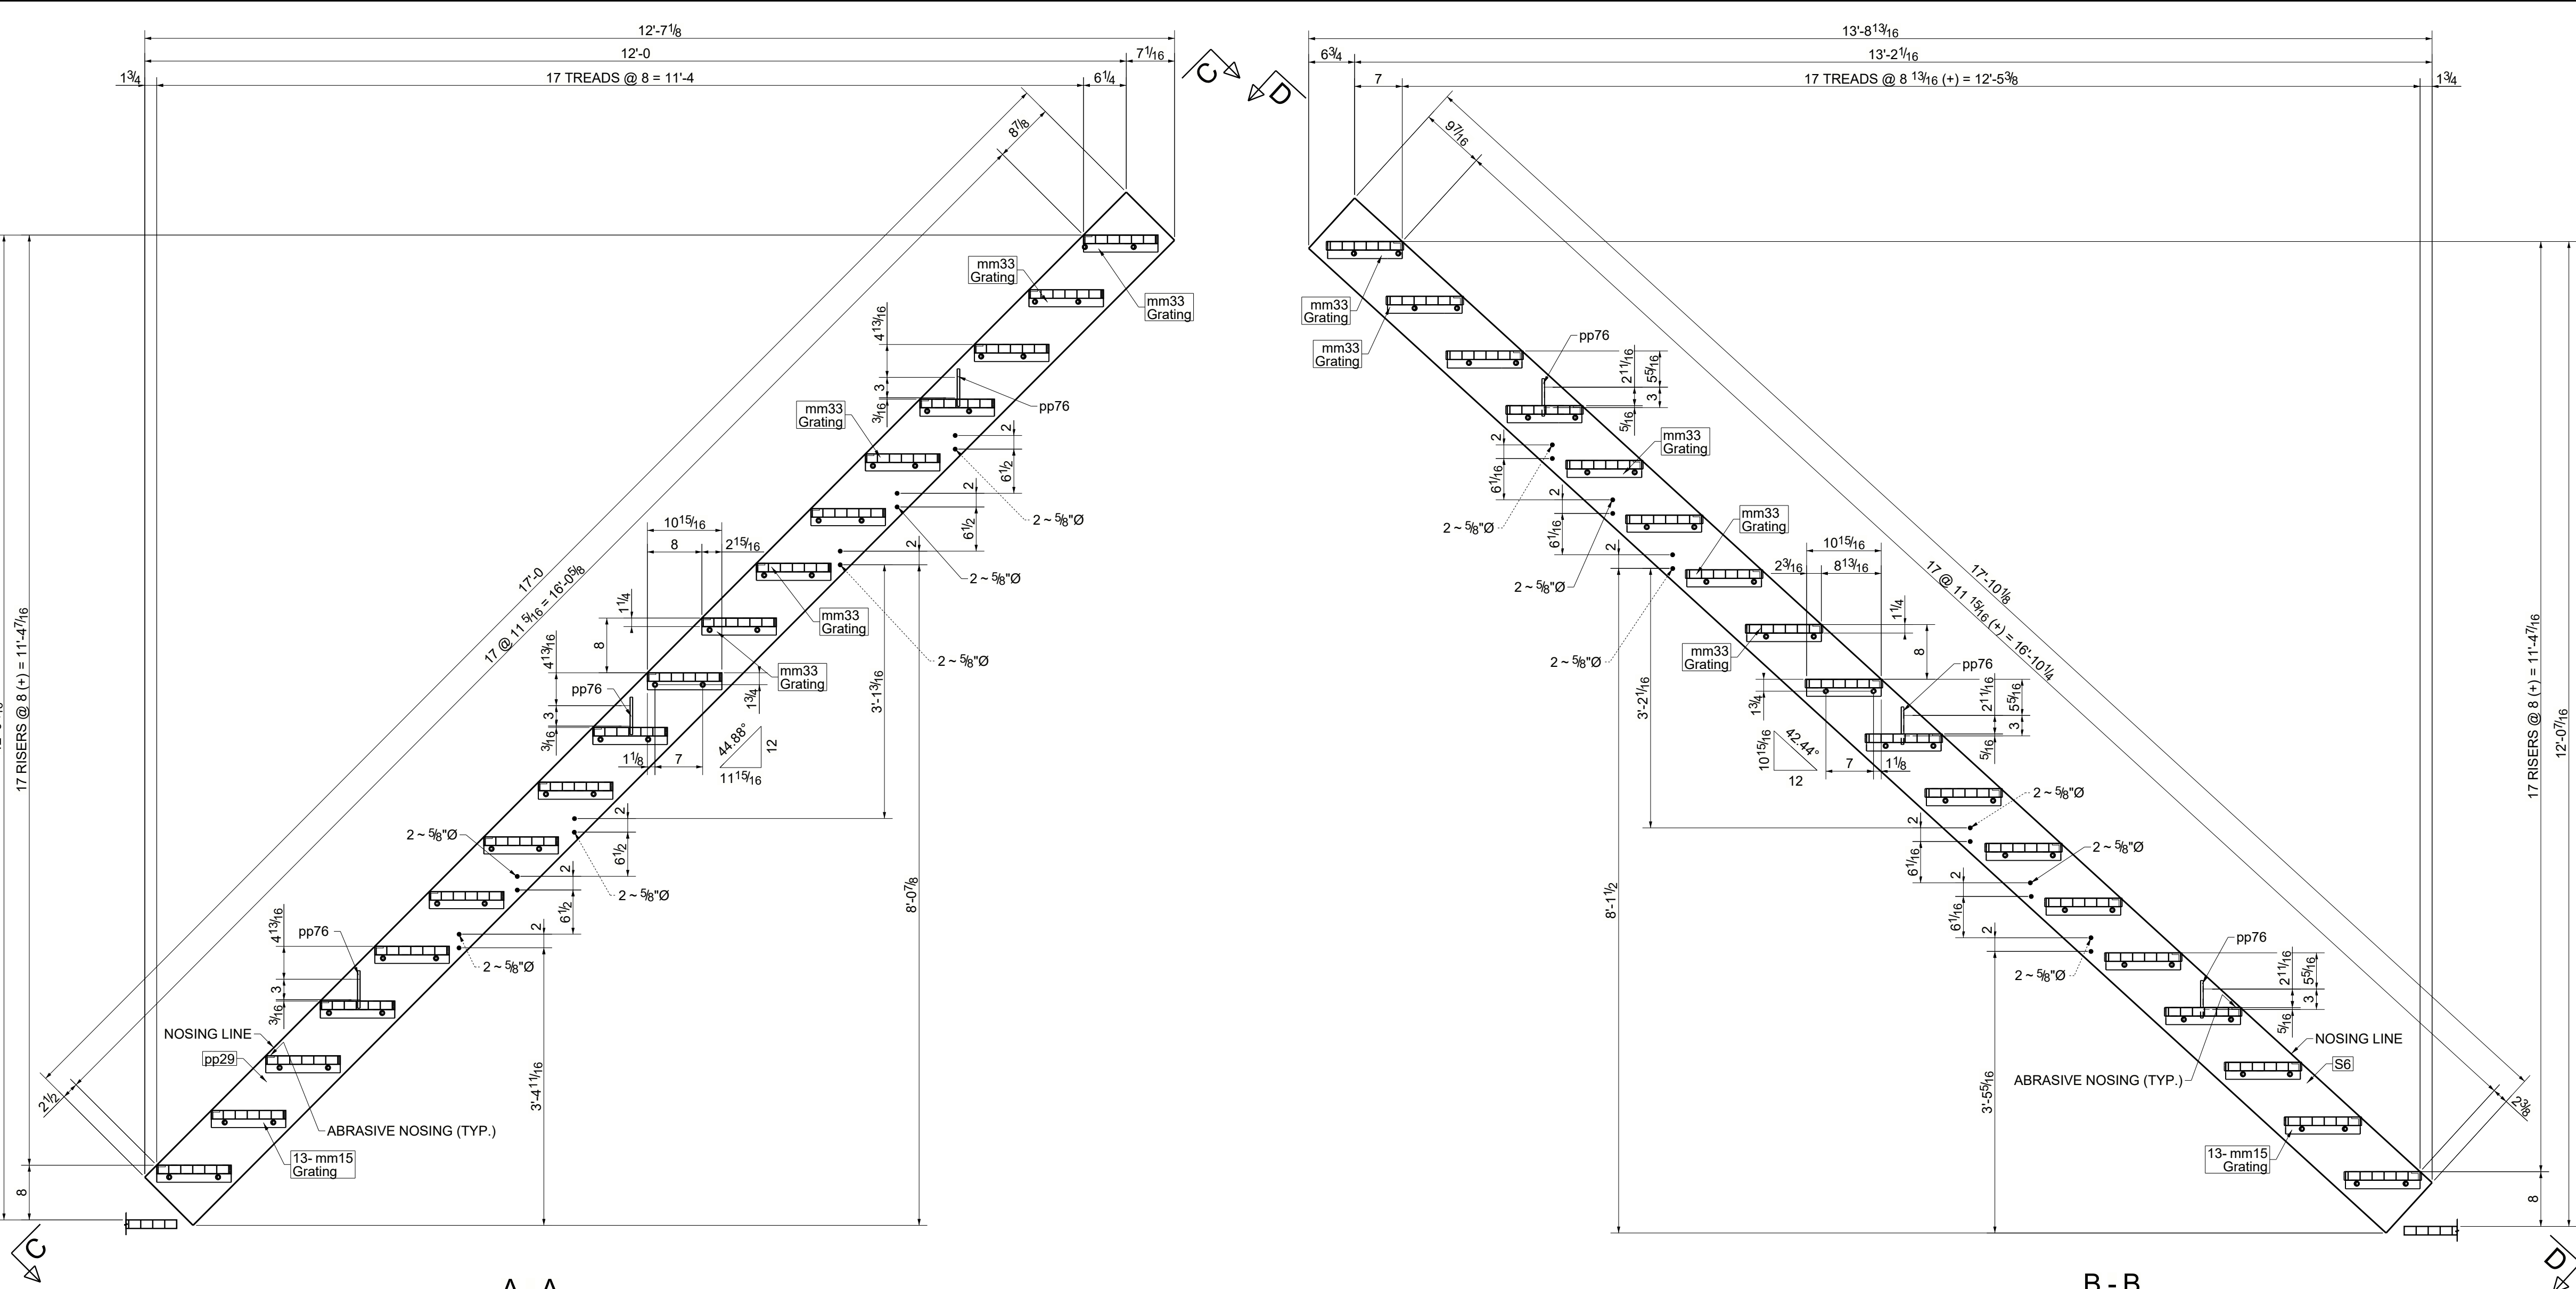

ONE - STAIR - S6