



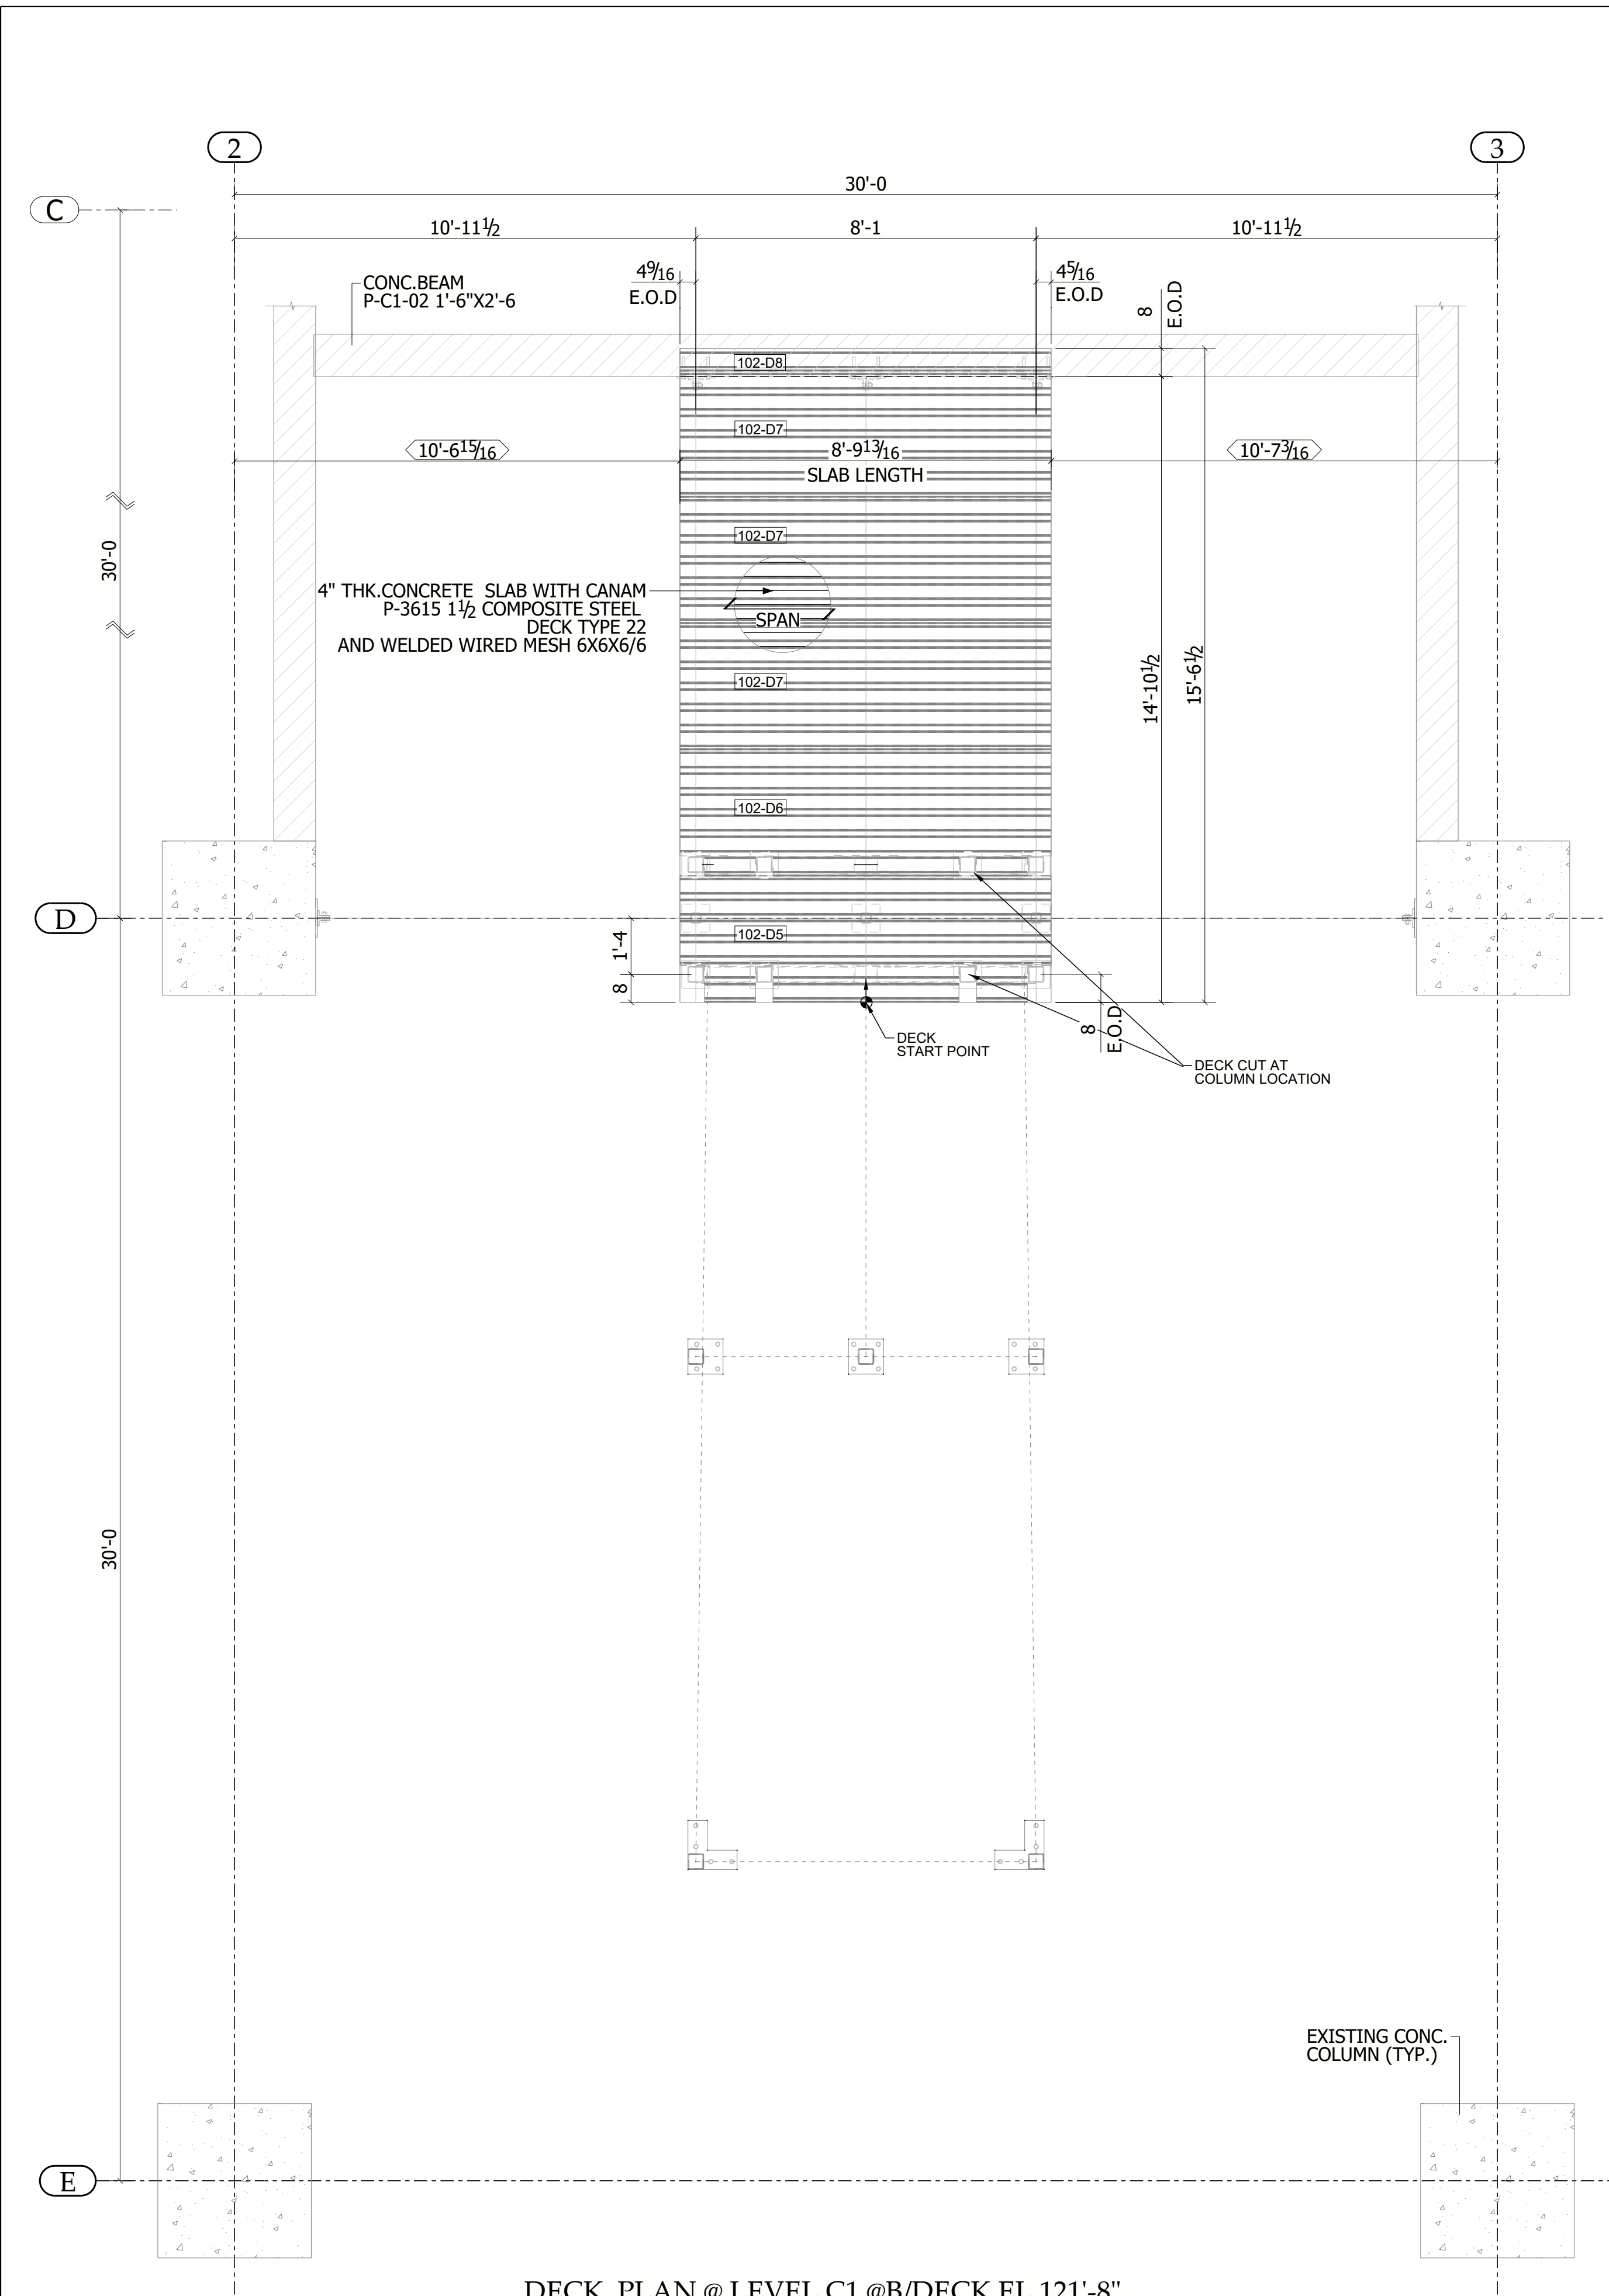

DECK PLAN @ LEVEL C1 @B/DECK EL.121'-8"

(REFER : VUE EN PLAN -PARTIELLE C1- S2.0)

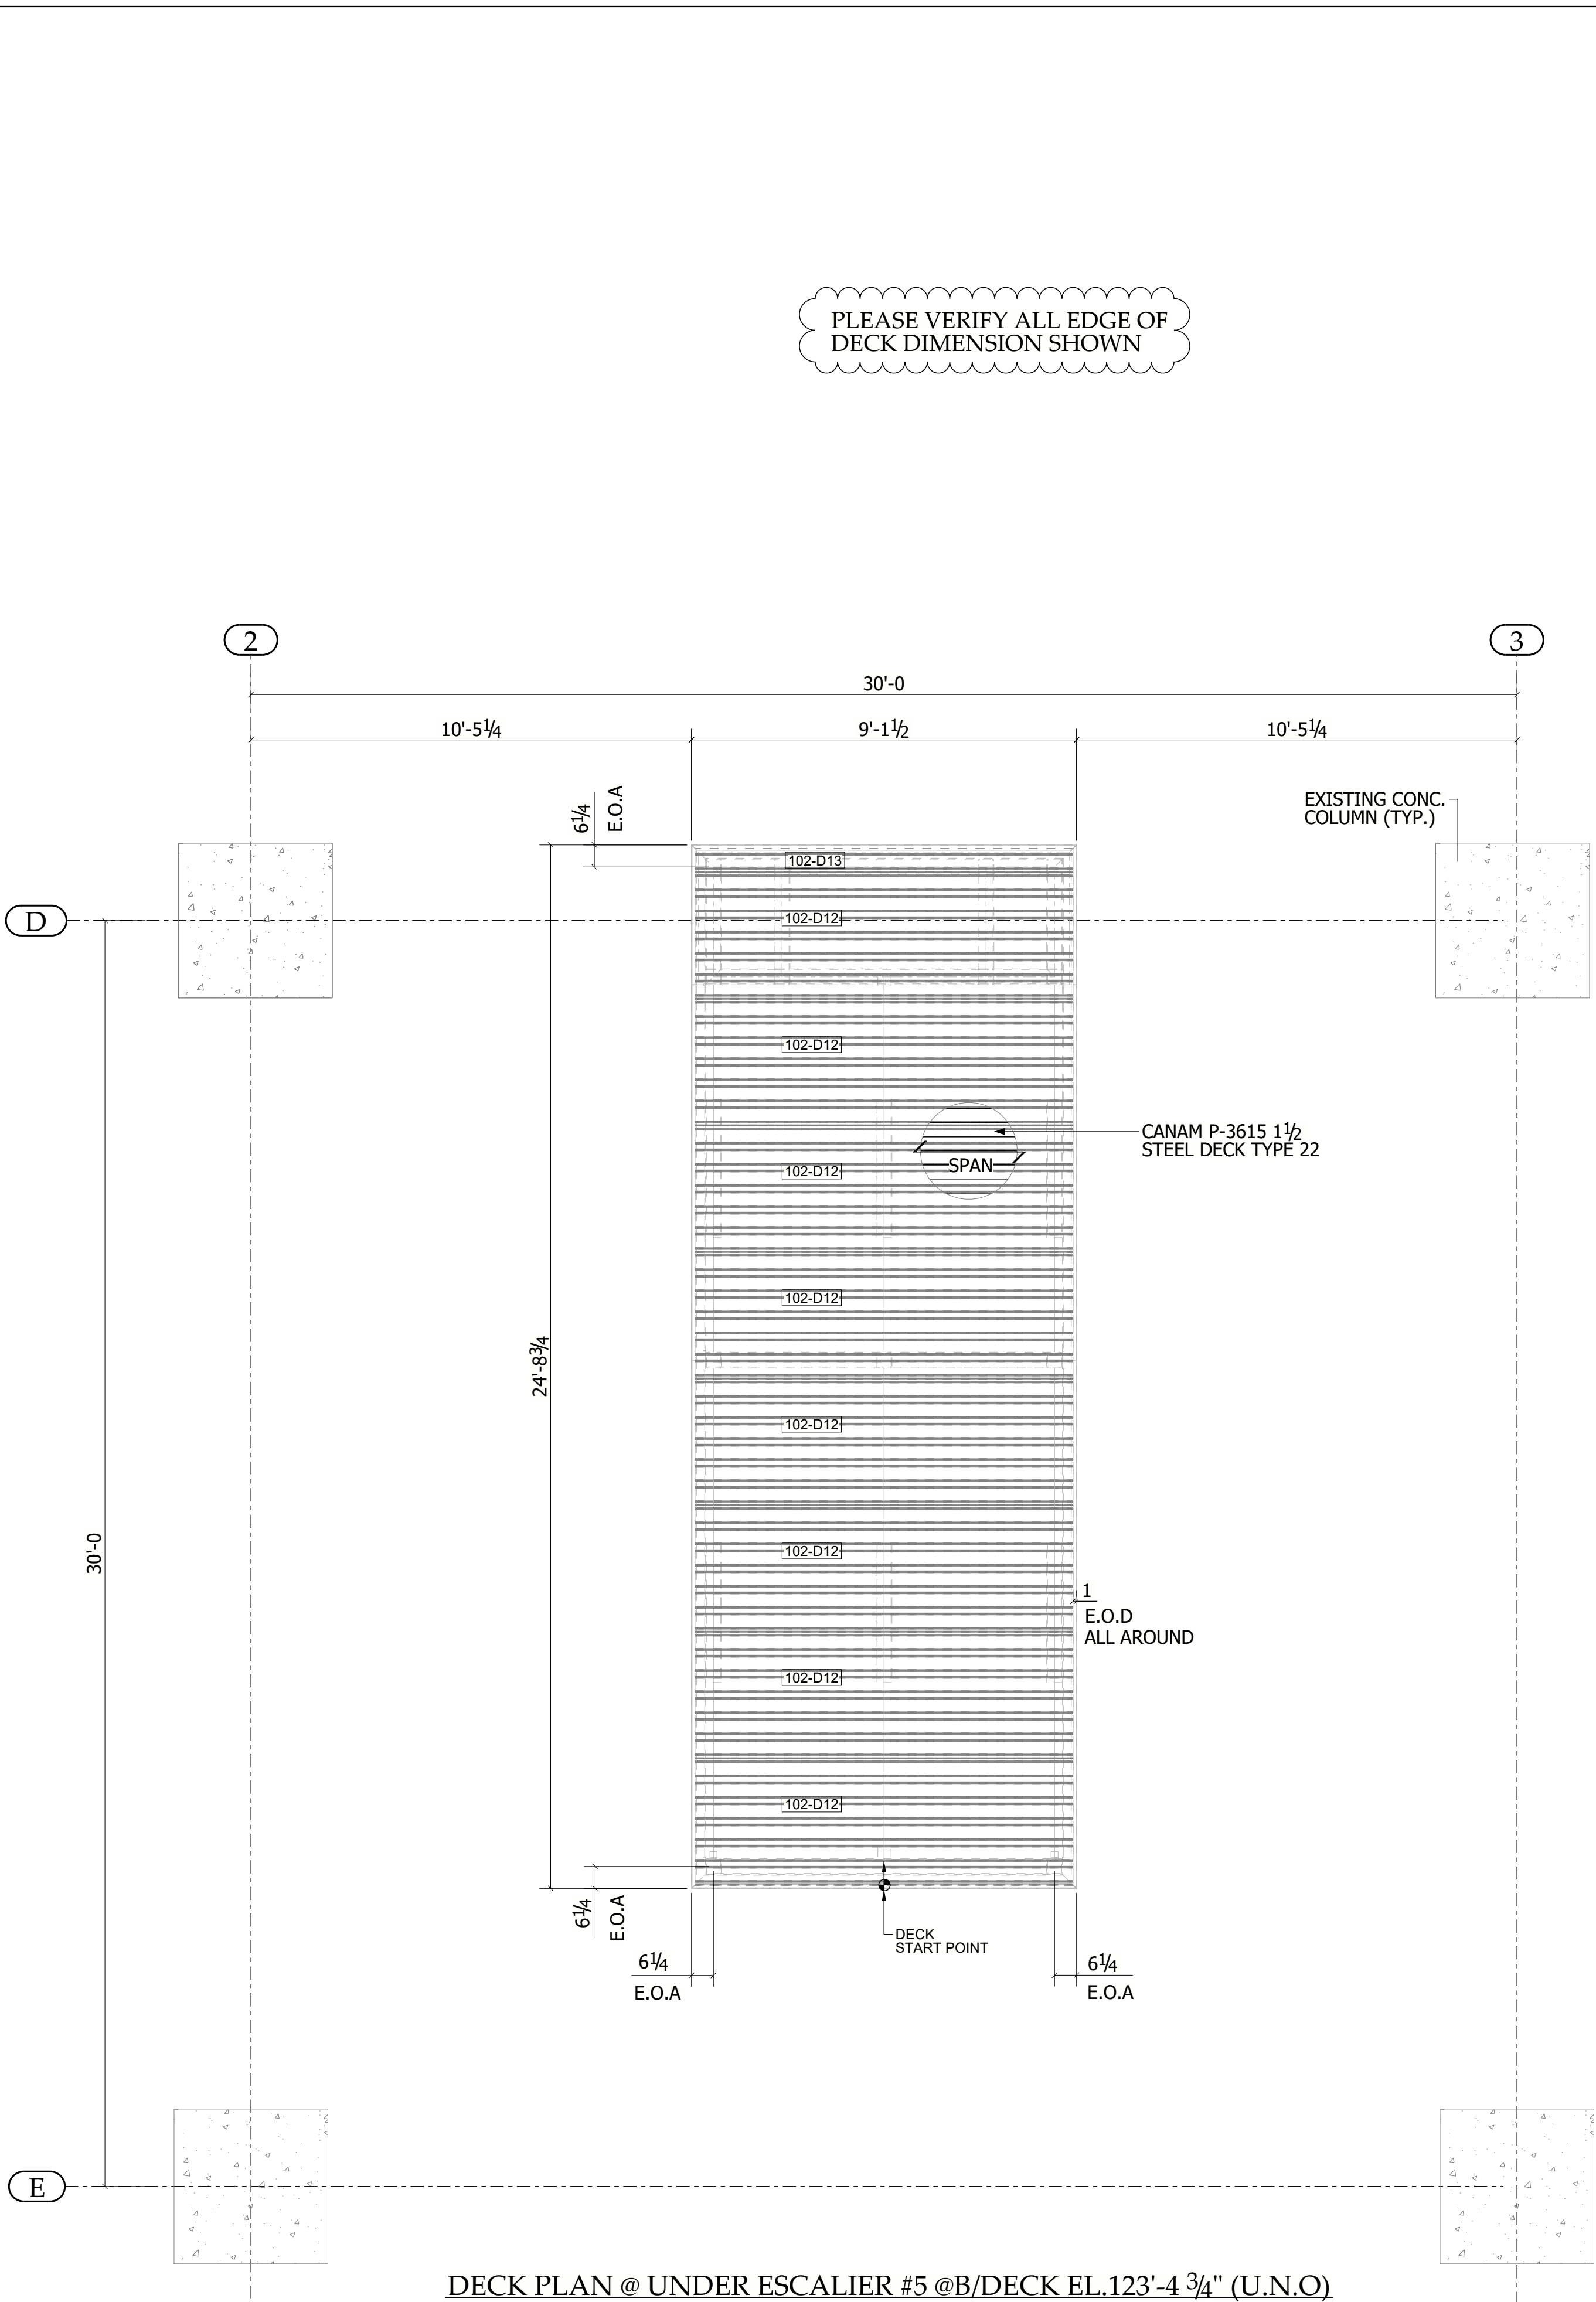


DECK PLAN @ UNDER ESCALIER #5 @B/DECK EL.123'-4 3/4" (U.N.O)


(REFER : VUE EN PLAN -STRUCTURE D'ACIER SOUS ESCALIER 5- S2.0)

LEGENDE:	
	= ARCH/EOR SVP VALIDER DIMENSION
	= DIMENSION À VÉRIFIER AU CHANTIER
	= DIMENSION VÉRIFIÉE AU CHANTIER

- NOTE(S):
- 1 .E.O.D - EDGE OF DECK
 - 2.E.O.A - EDGE OF ANGLE

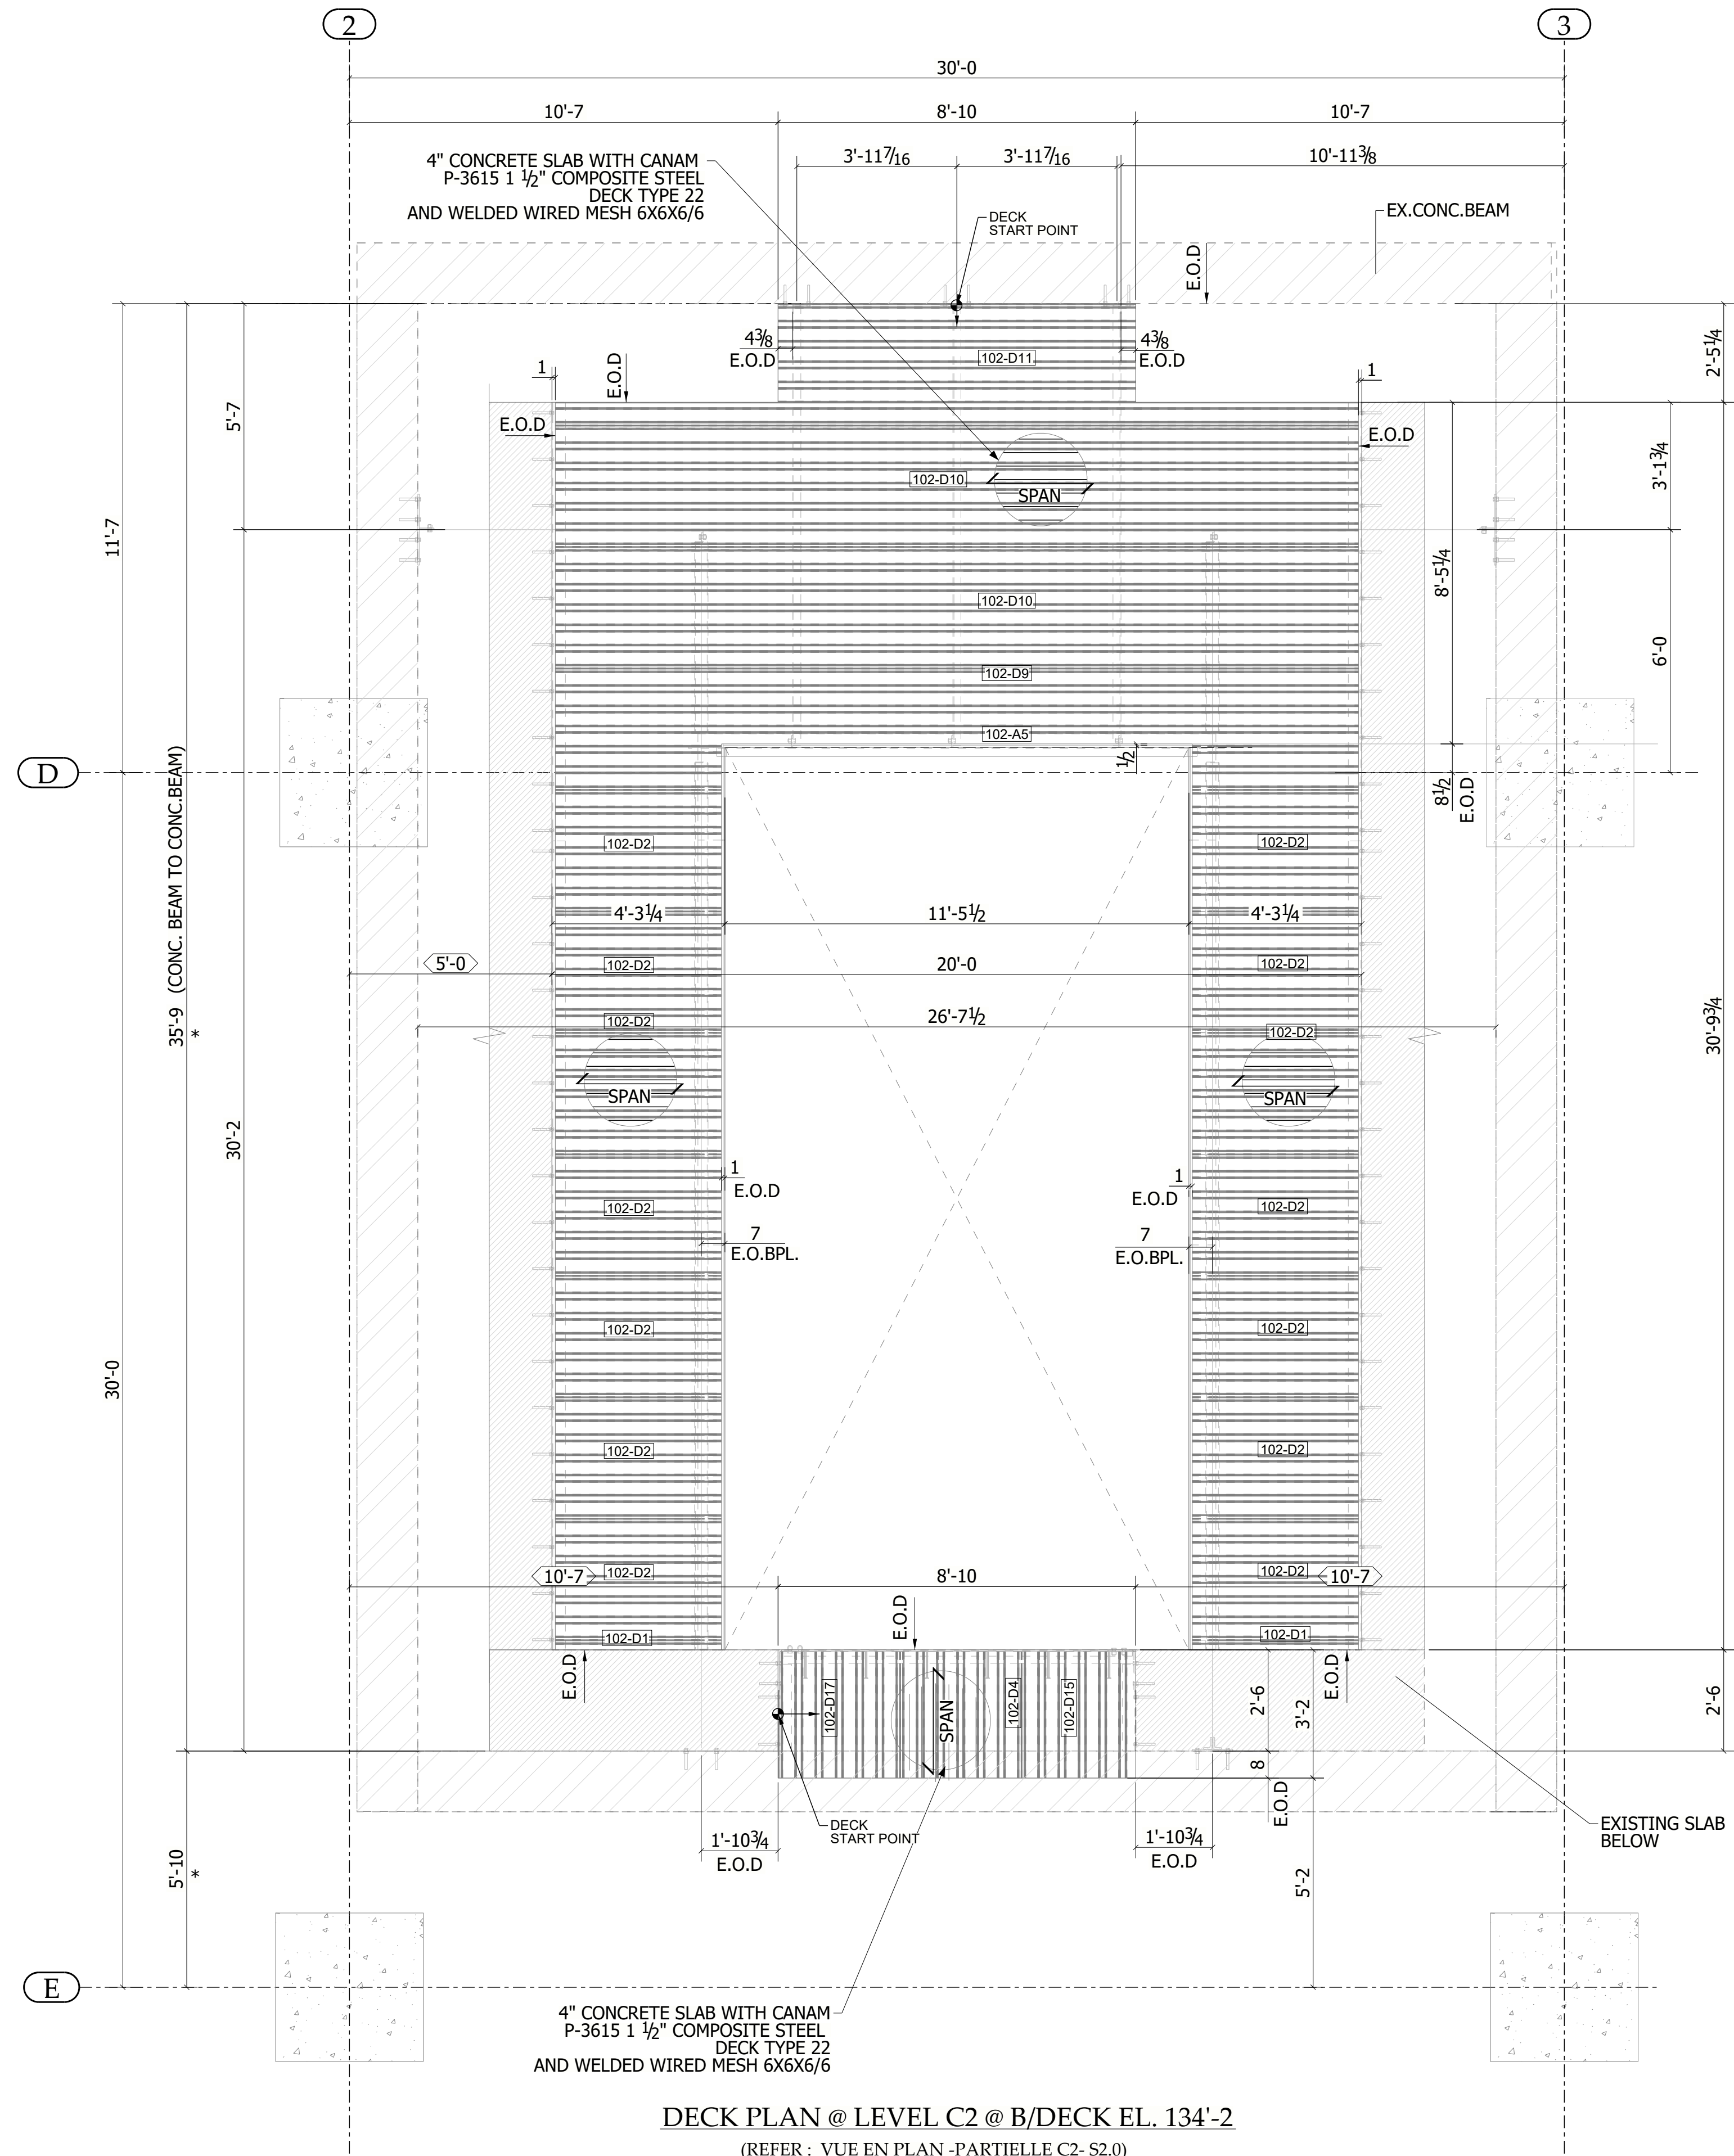

DECK PLAN @ LEVEL C2 @ B/DECK EL. 134'-2
(REFER : VUE EN PLAN -PARTIELLE C2- S2.0)

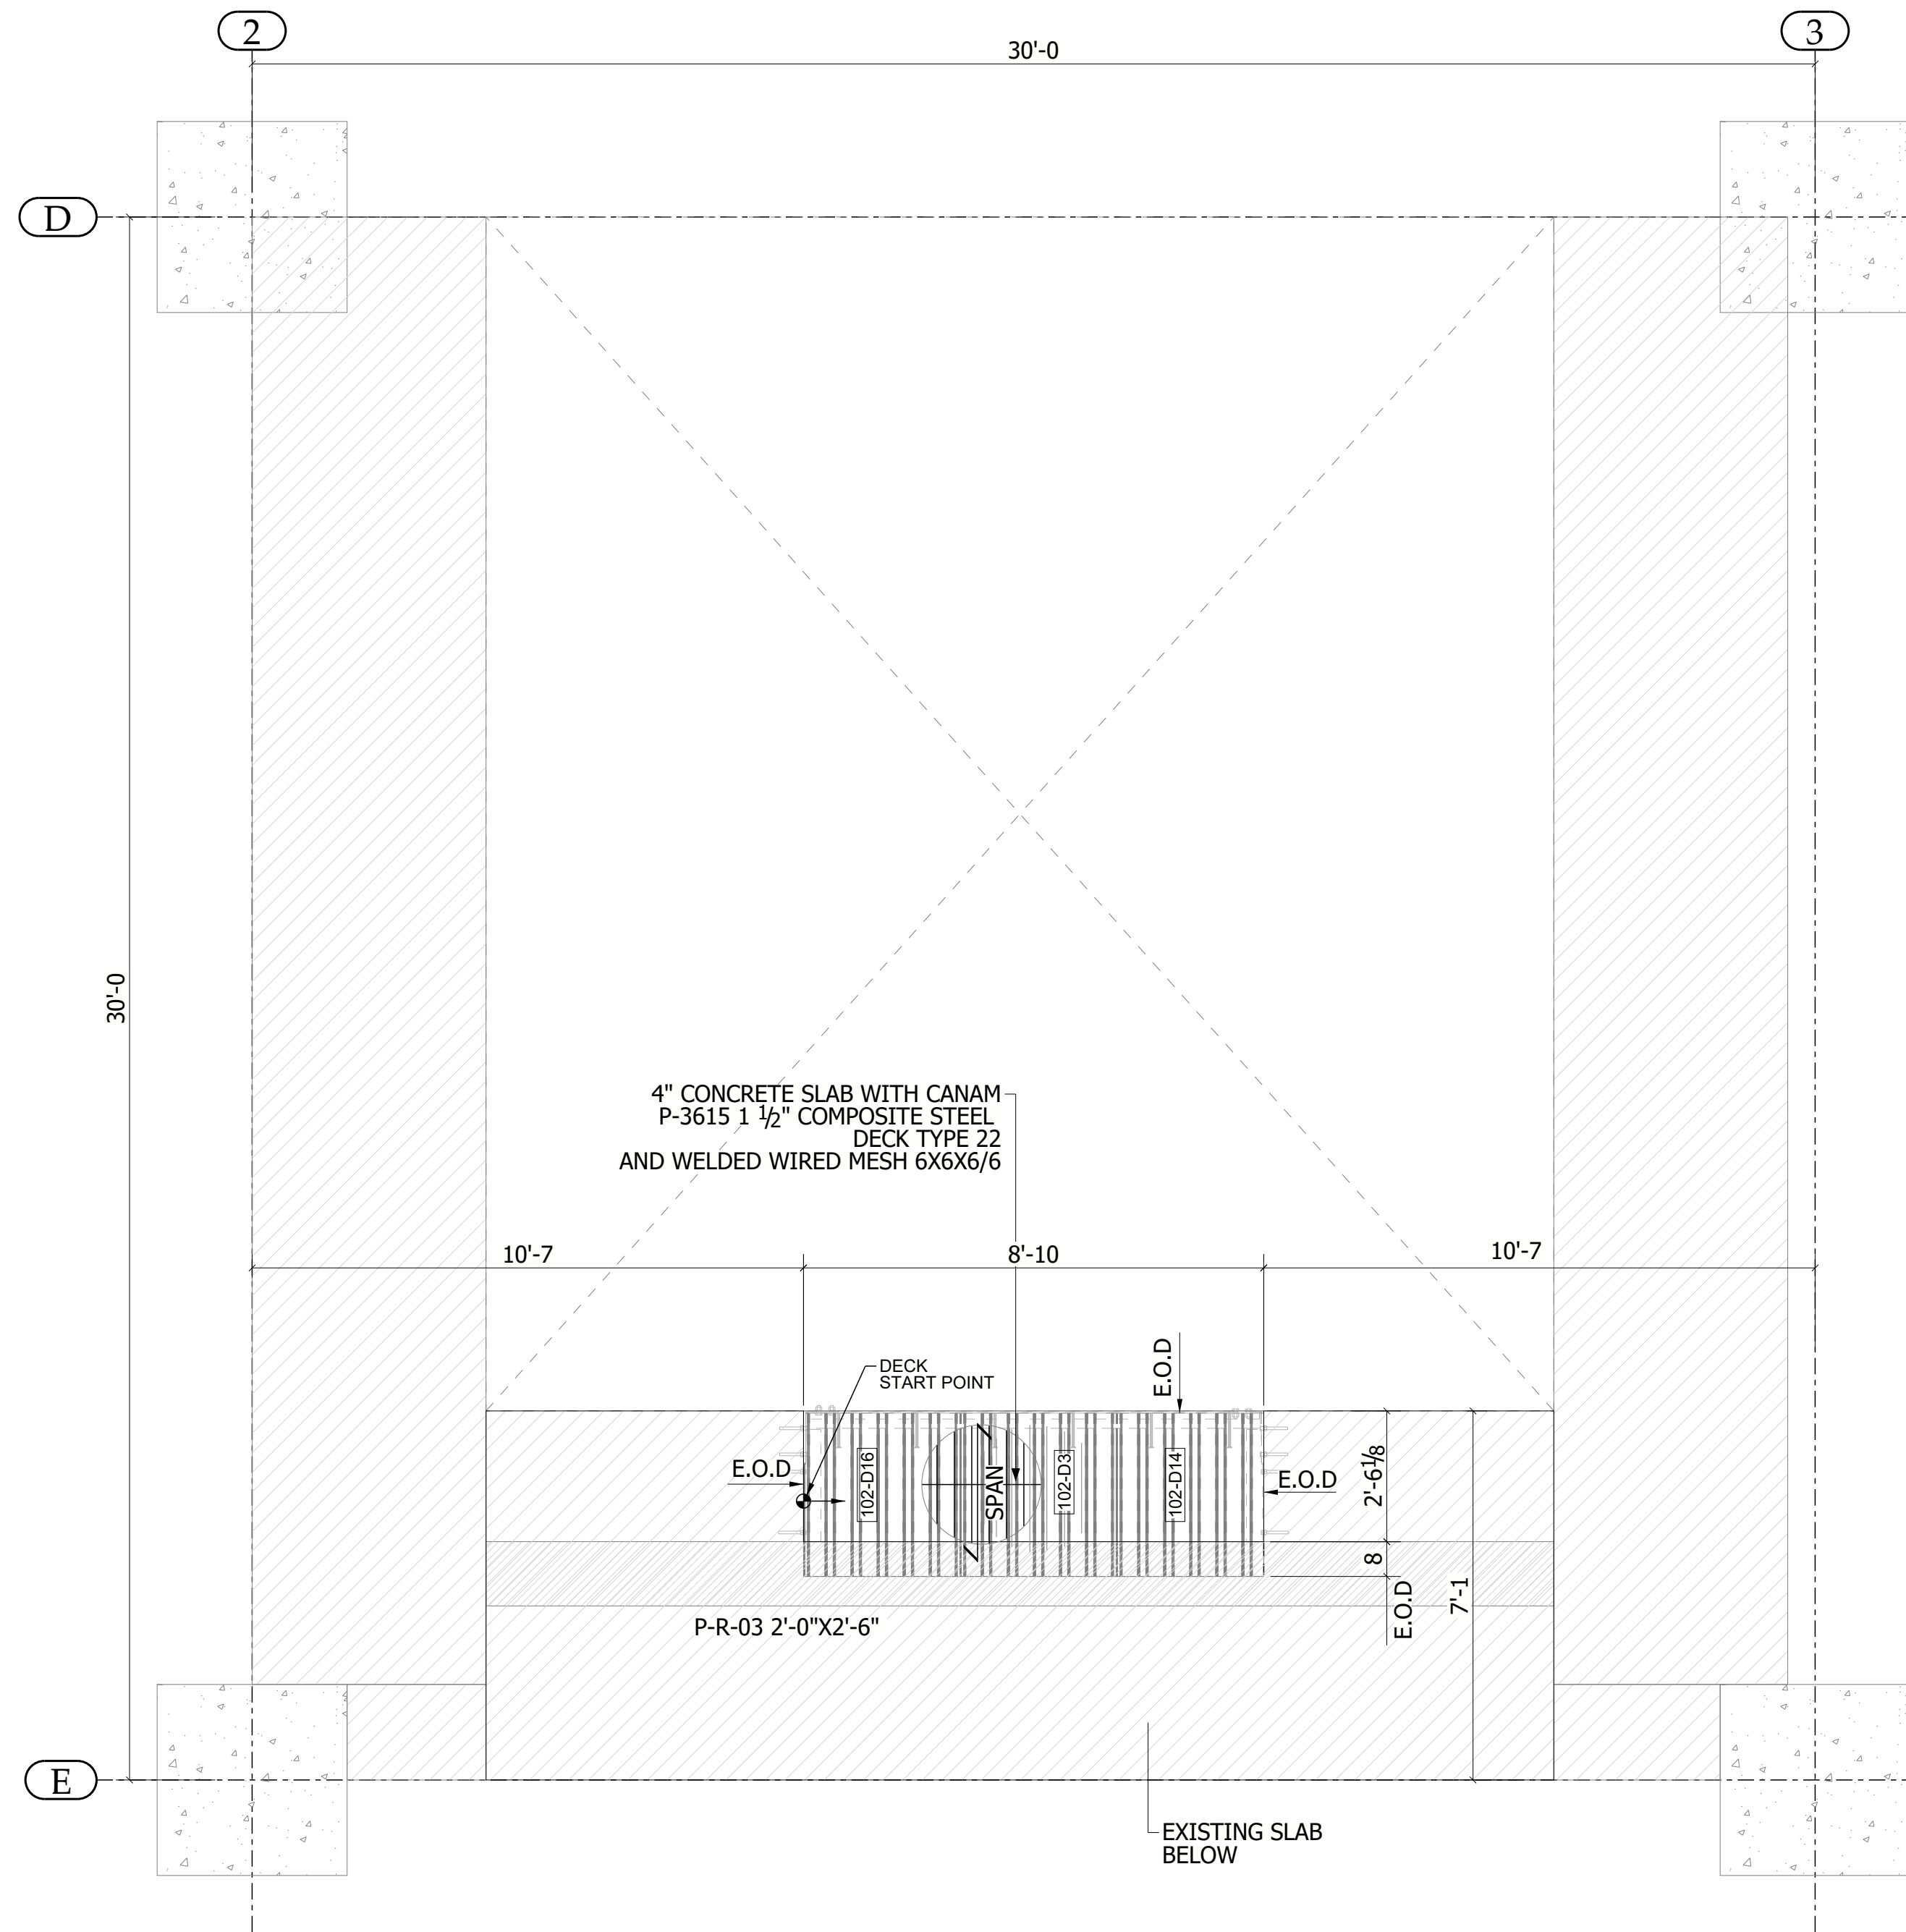


DECK PLAN @ RDC @ B/DECK EL. 146'-8
(REFER : VUE EN PLAN -PARTIELLE RDC- S2.0)

- LEGENDE:
- (DIMENSION) = ARCH/EOR SVP
VALIDER DIMENSION
 - < DIMENSION > = DIMENSION À VÉRIFIER
AU CHANTIER
 - DIMENSION * = DIMENSION VÉRIFIÉE
AU CHANTIER


NOTE(S):

RÉQUISITION D'ACHAT

[illegible]

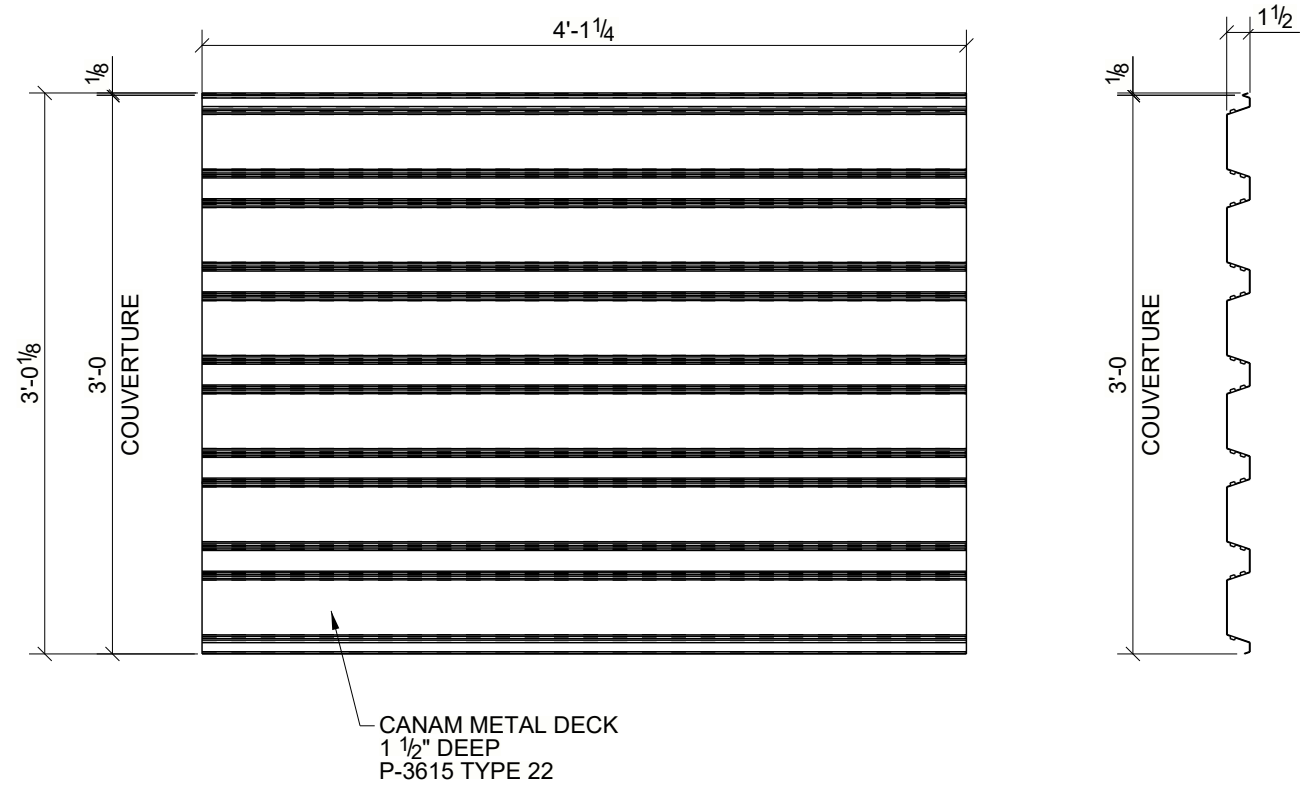

STEEL ASTM	300W	UNO
ELECTRODES	E70XX	UNO
WELDS	1/4	UNO
OPEN HOLES	Ø13/16	UNO
BOLTS	Ø3/4" A325N	UNO
FINISH	PRÉGALVANISÉ	UNO

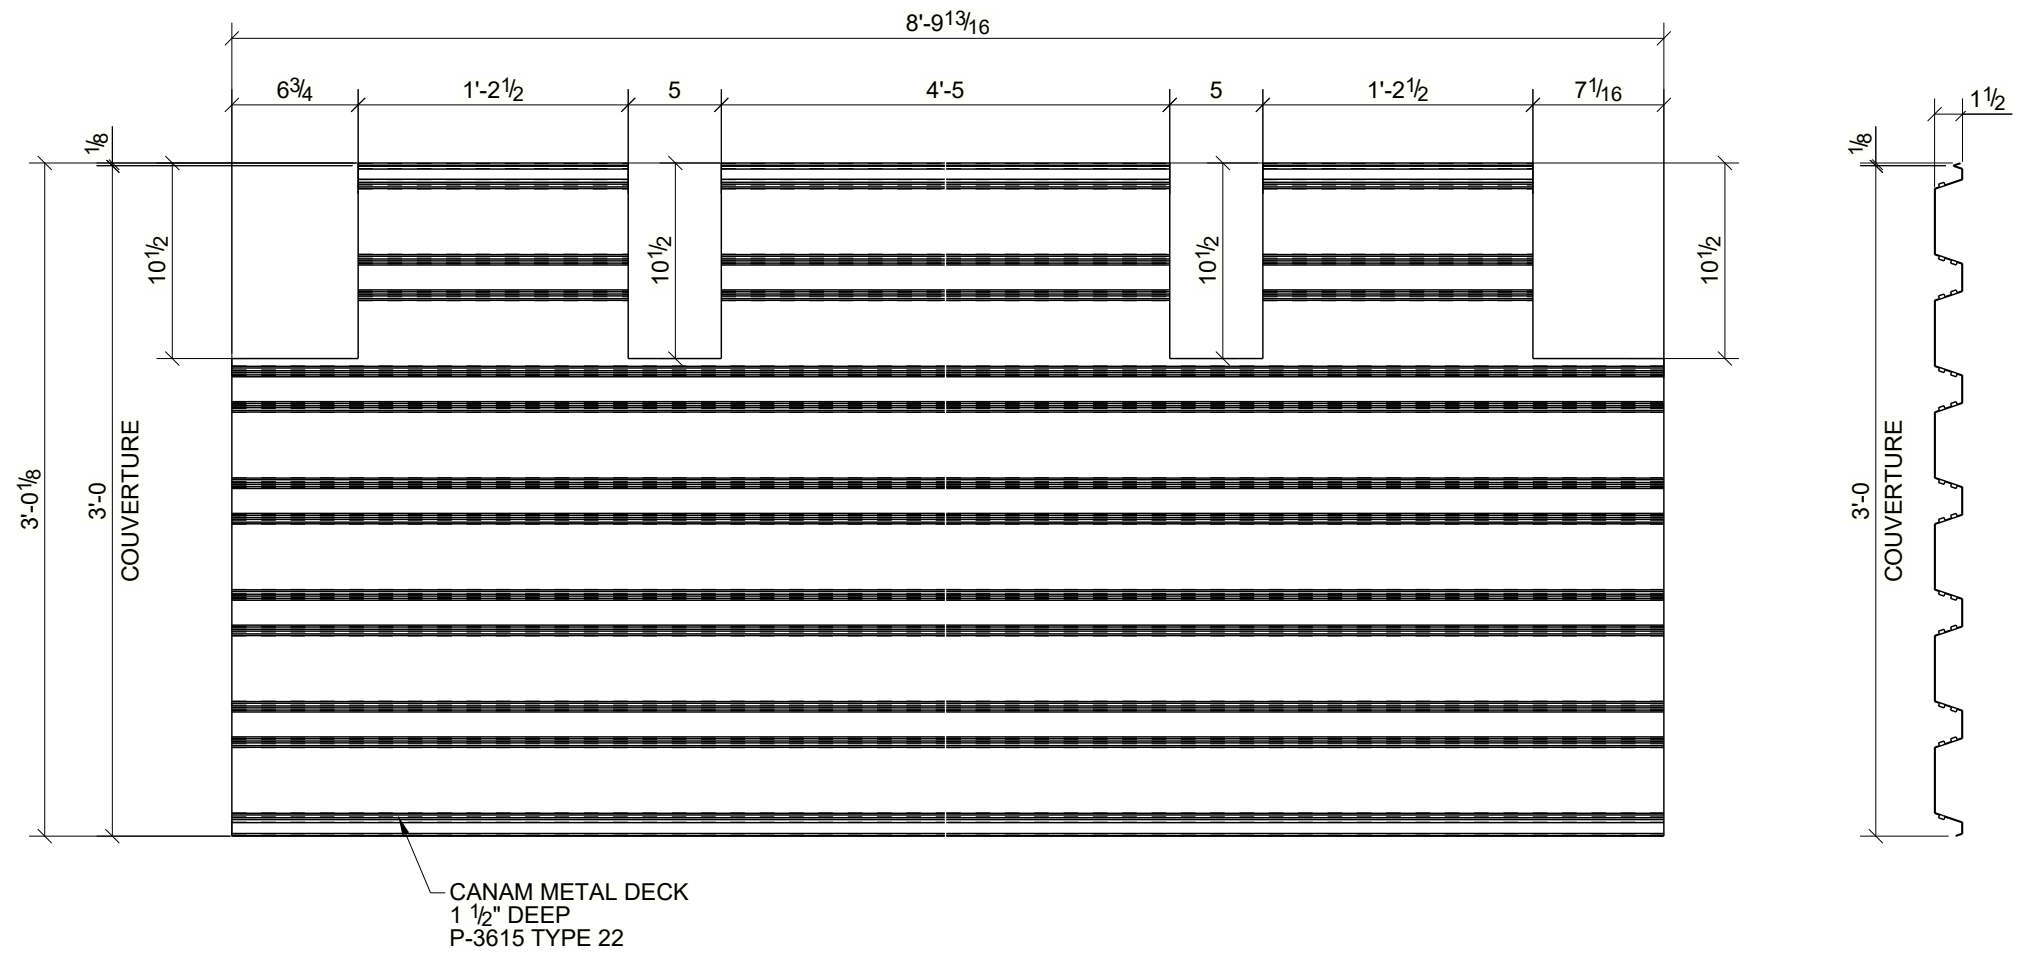

STEEL ASTM	300W	UNO
ELECTRODES	E70XX	UNO
WELDS	1/4	UNO
OPEN HOLES	Ø13/16	UNO
BOLTS	Ø3/4" A325N	UNO
FINISH	PRÉGALVANISÉ	UNO