





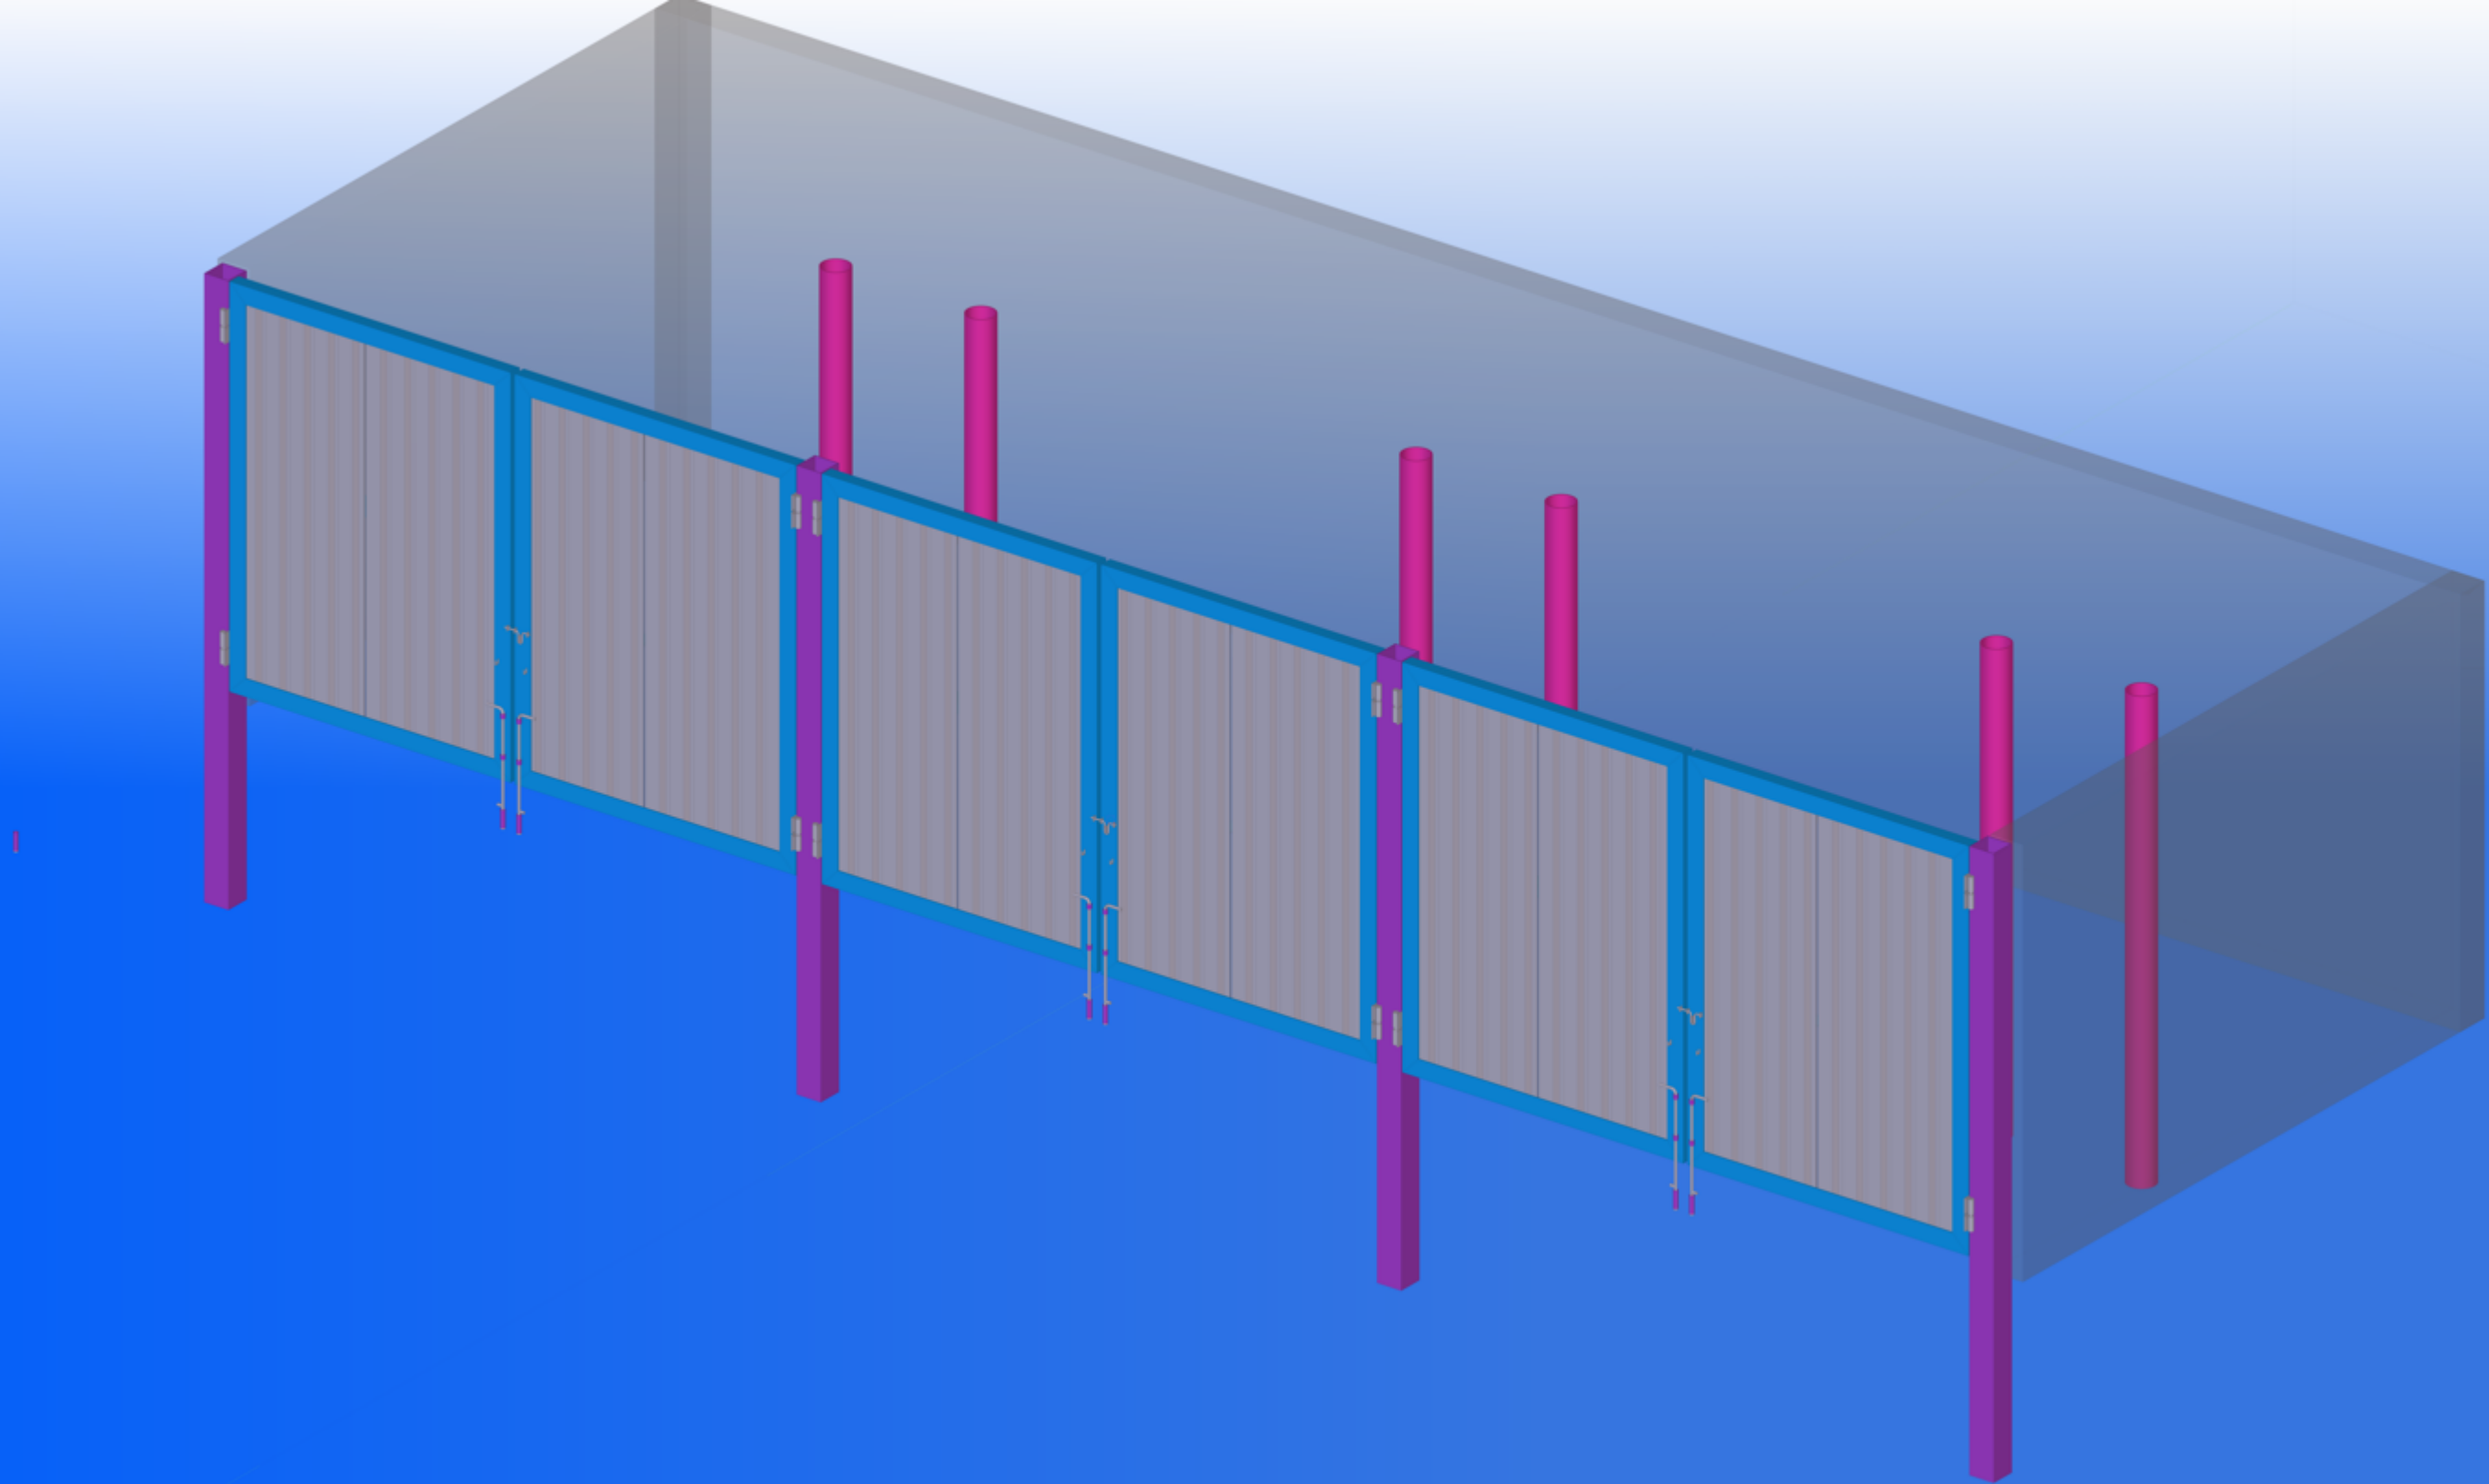

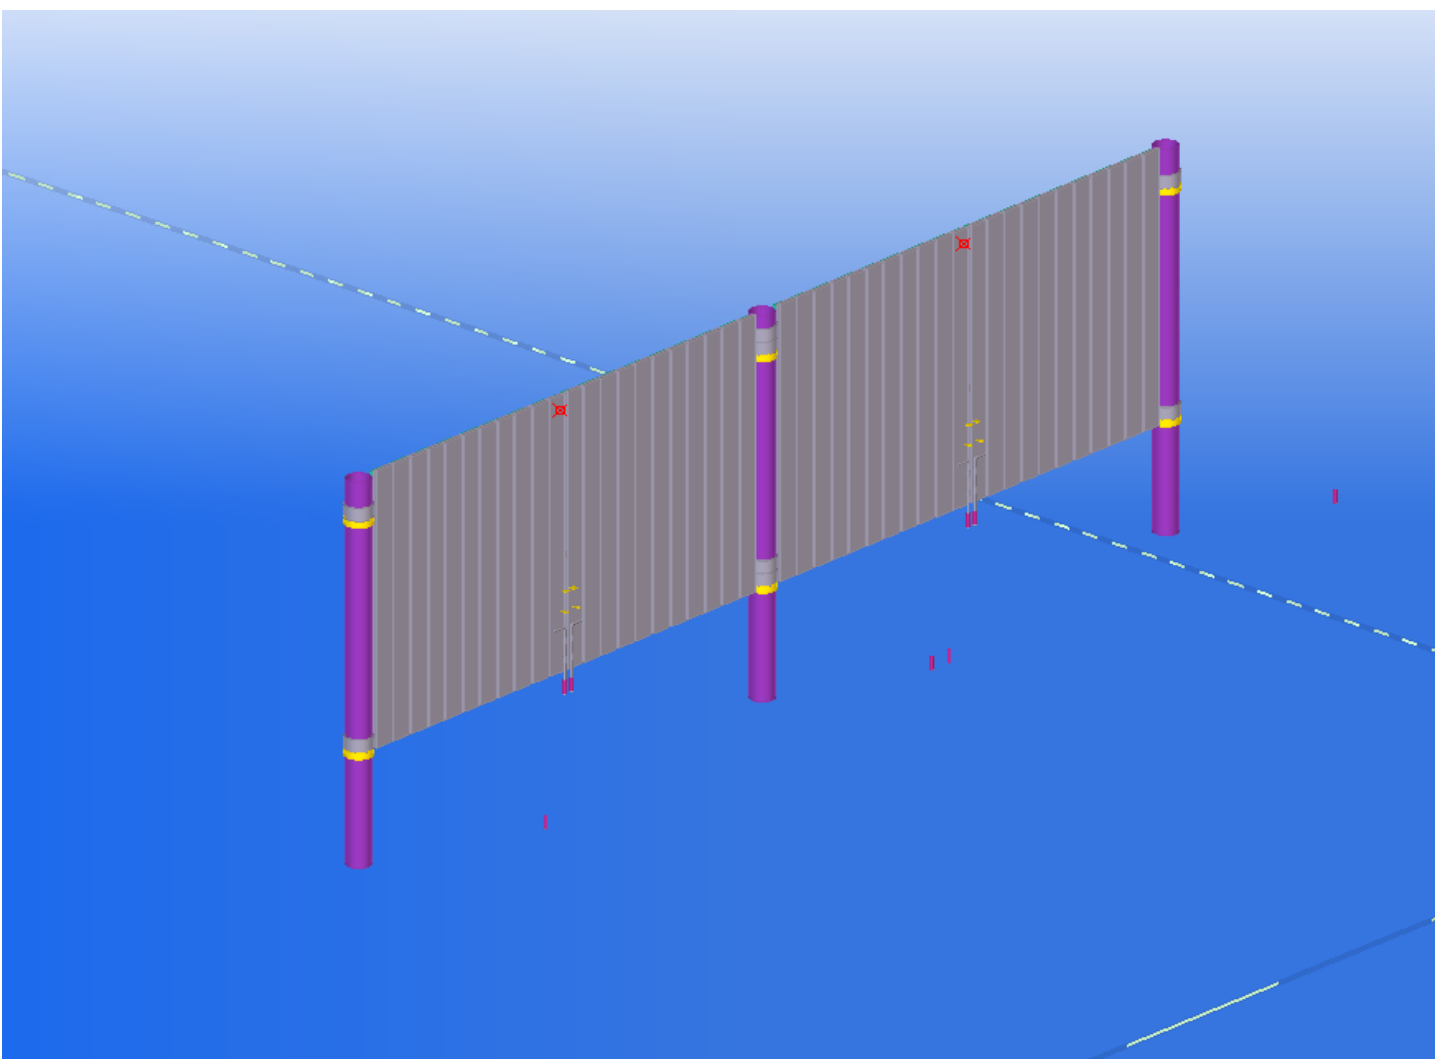

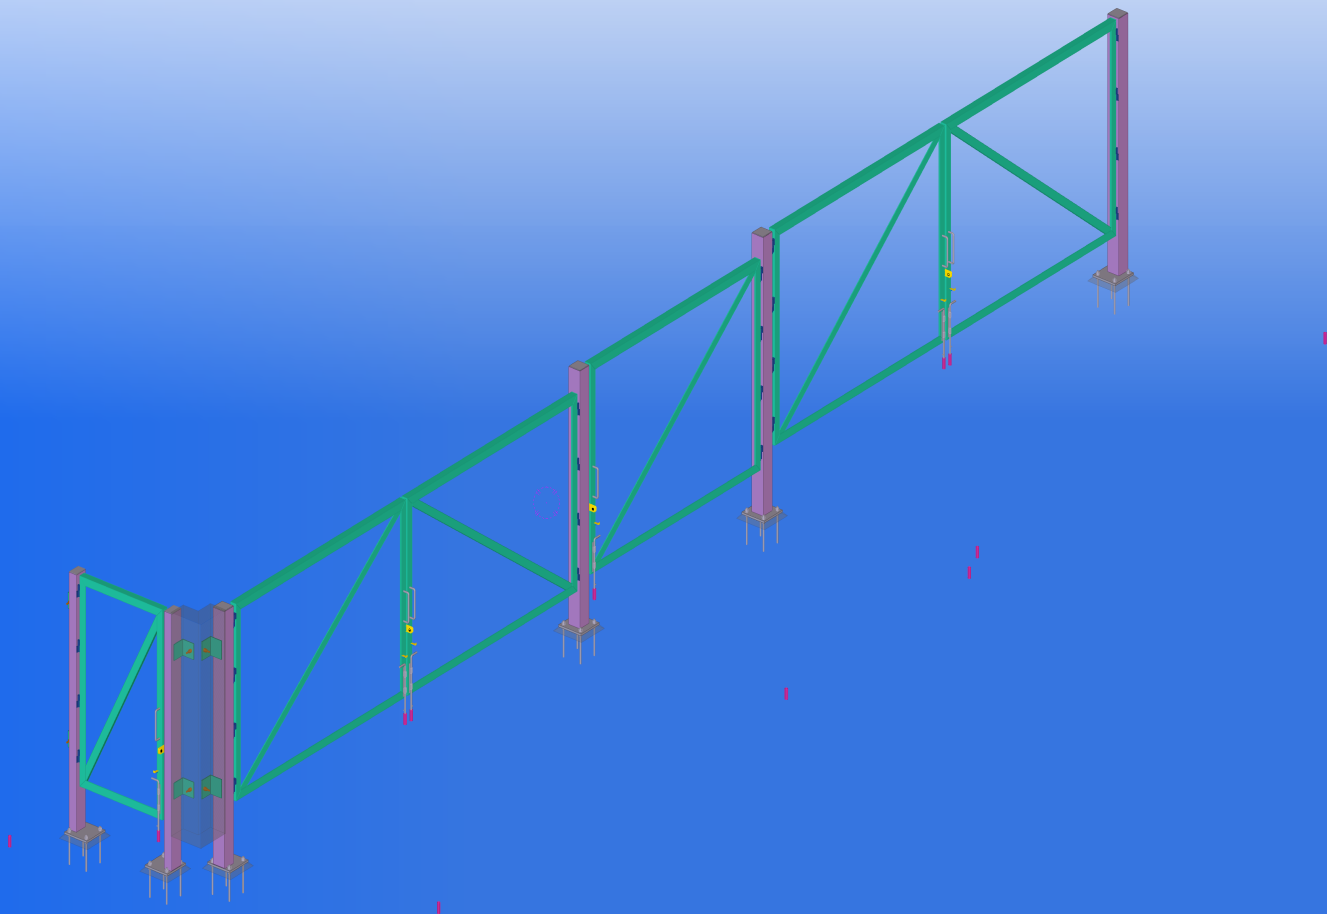

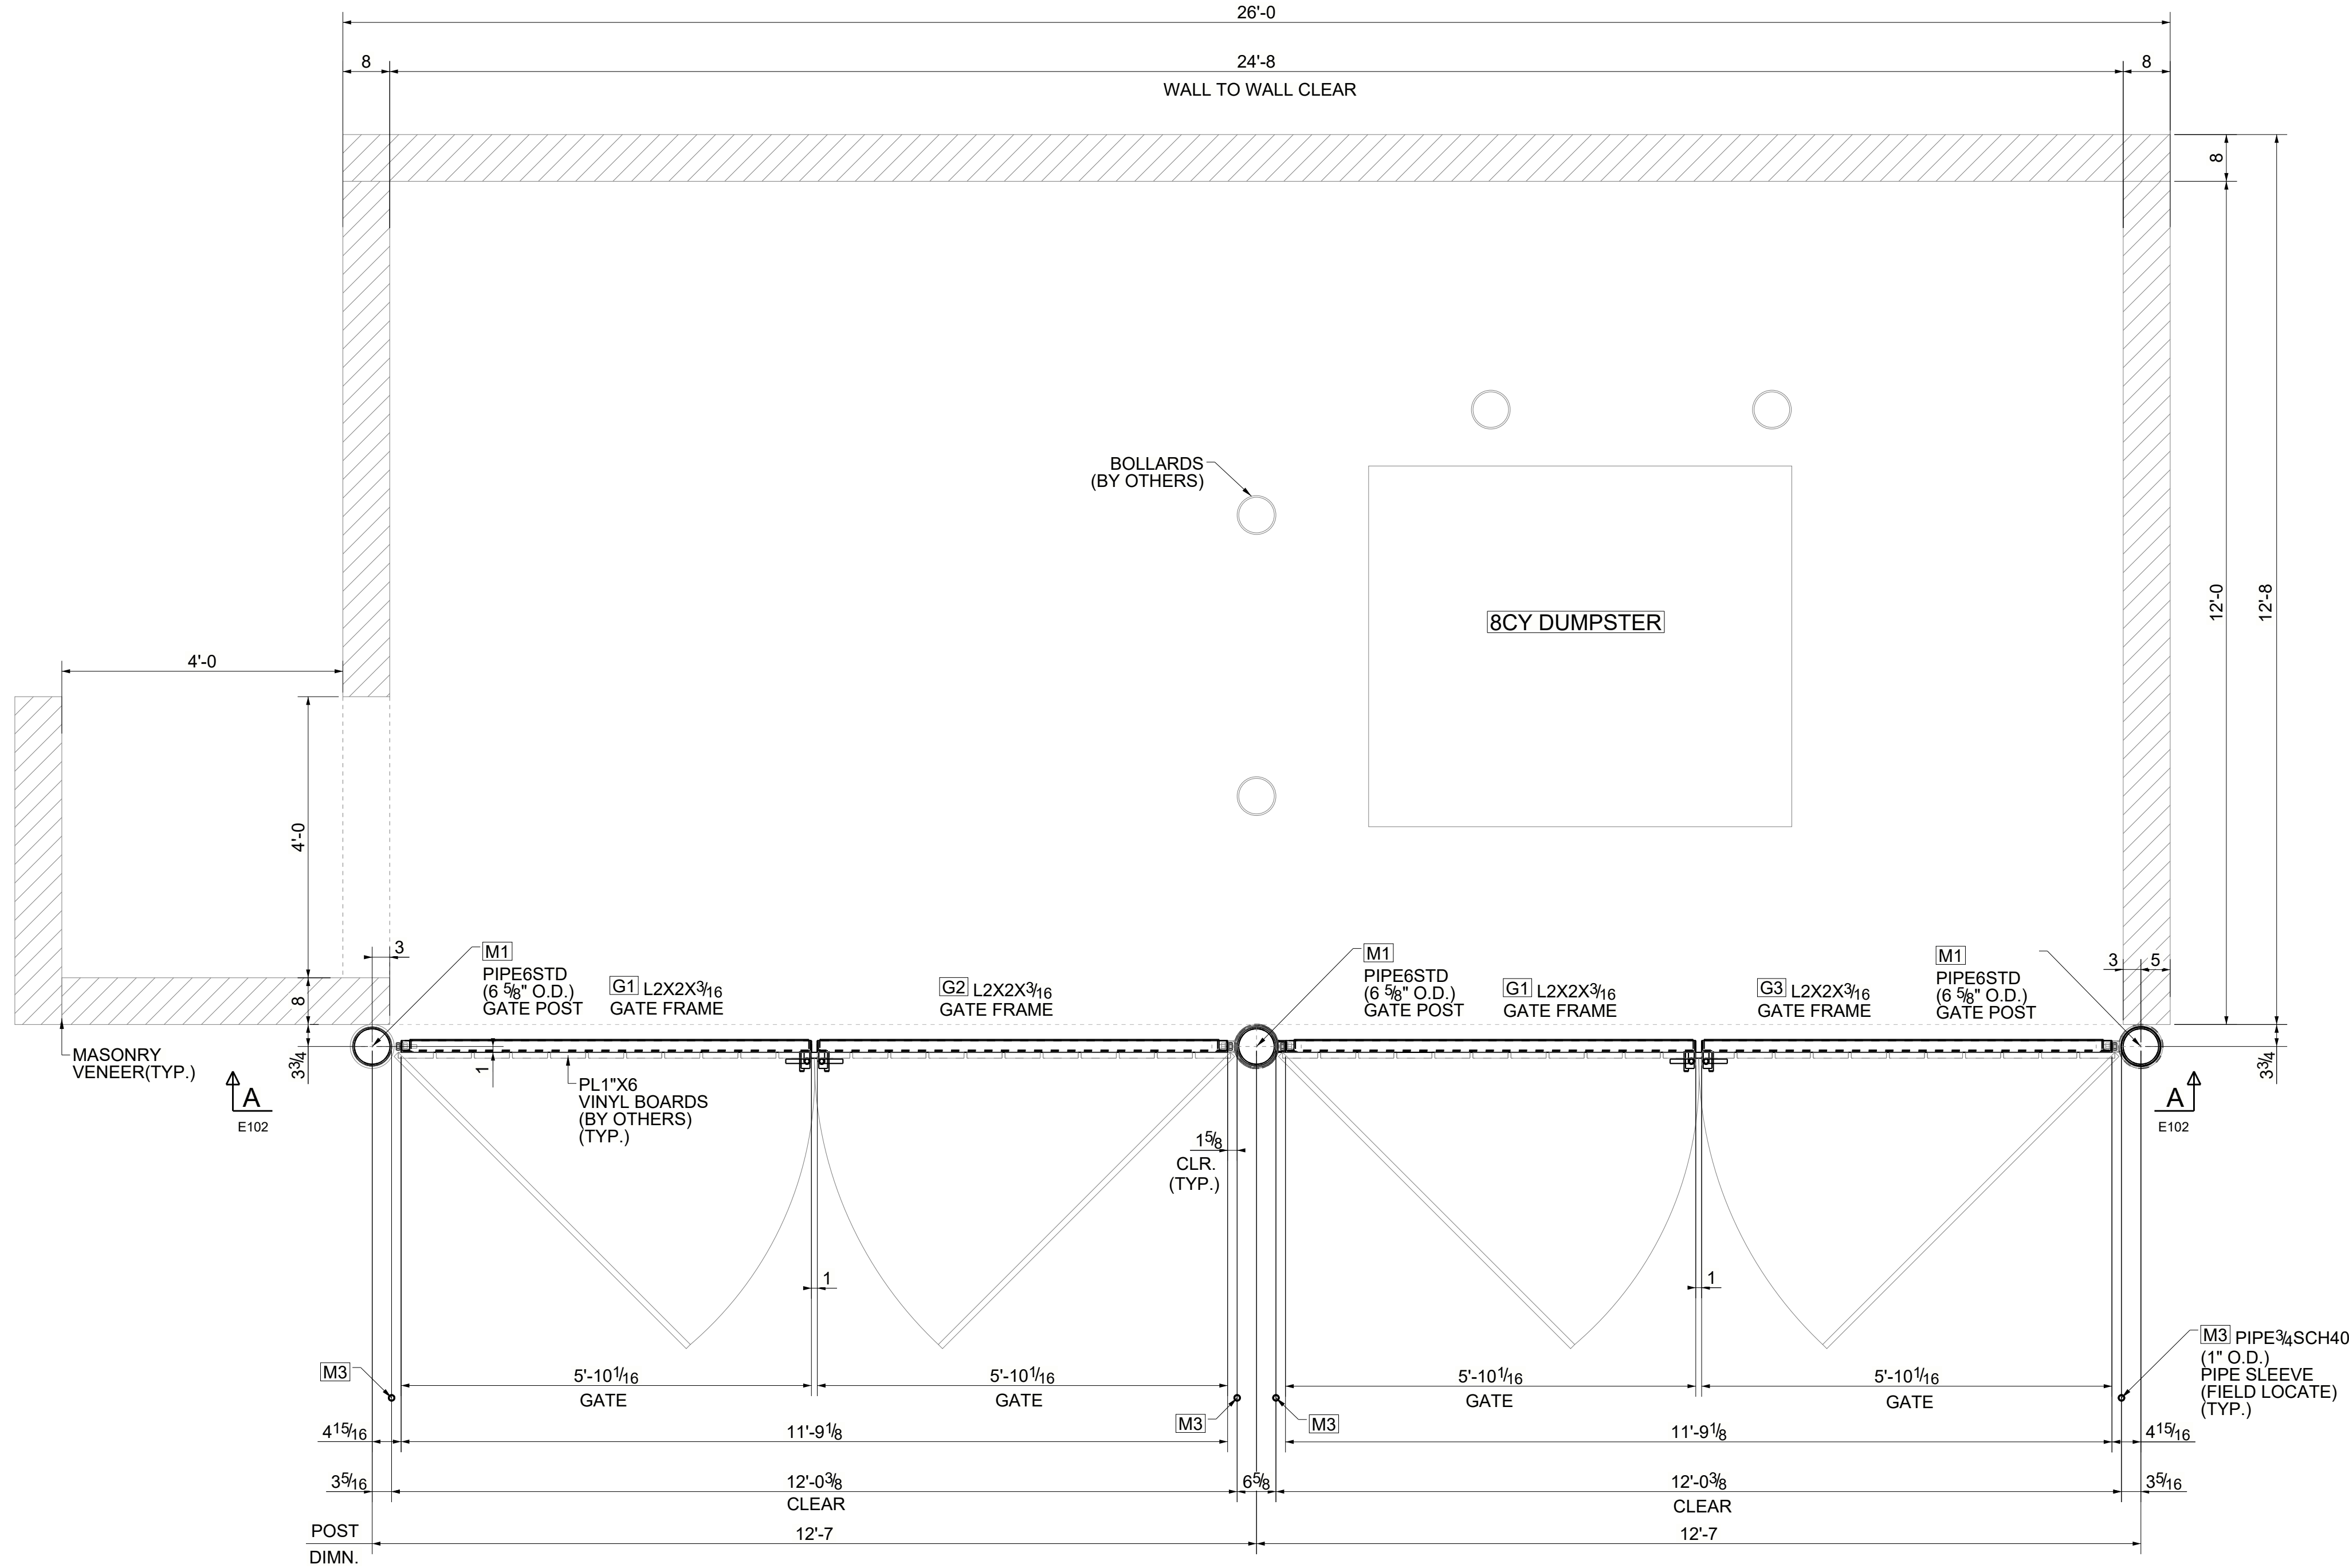


DUMPSTER GATE & BOLLARD LOCATION PLAN
(REFER : DUMPSTER ENCLOSURE-11/SP7)

- NOTES :
- TOP OF FINISH FLOOR ELEVATION = 0'-0" = DATUM ELEVATION.
 - REFER SHEET E102 FOR ELEVATION & SECTIONS.
 - MATERIAL GRADE:
 - ALL PLATES, ANGLES, ROD - ASTM A36
 - ALL PIPES - ASTM A53


FINISH NOTES :

ALL GATE FRAME STEEL MEMBERS TO BE HOT DIPPED GALVANIZED.

SURFACE PREPARATION : AS PER SPECS.

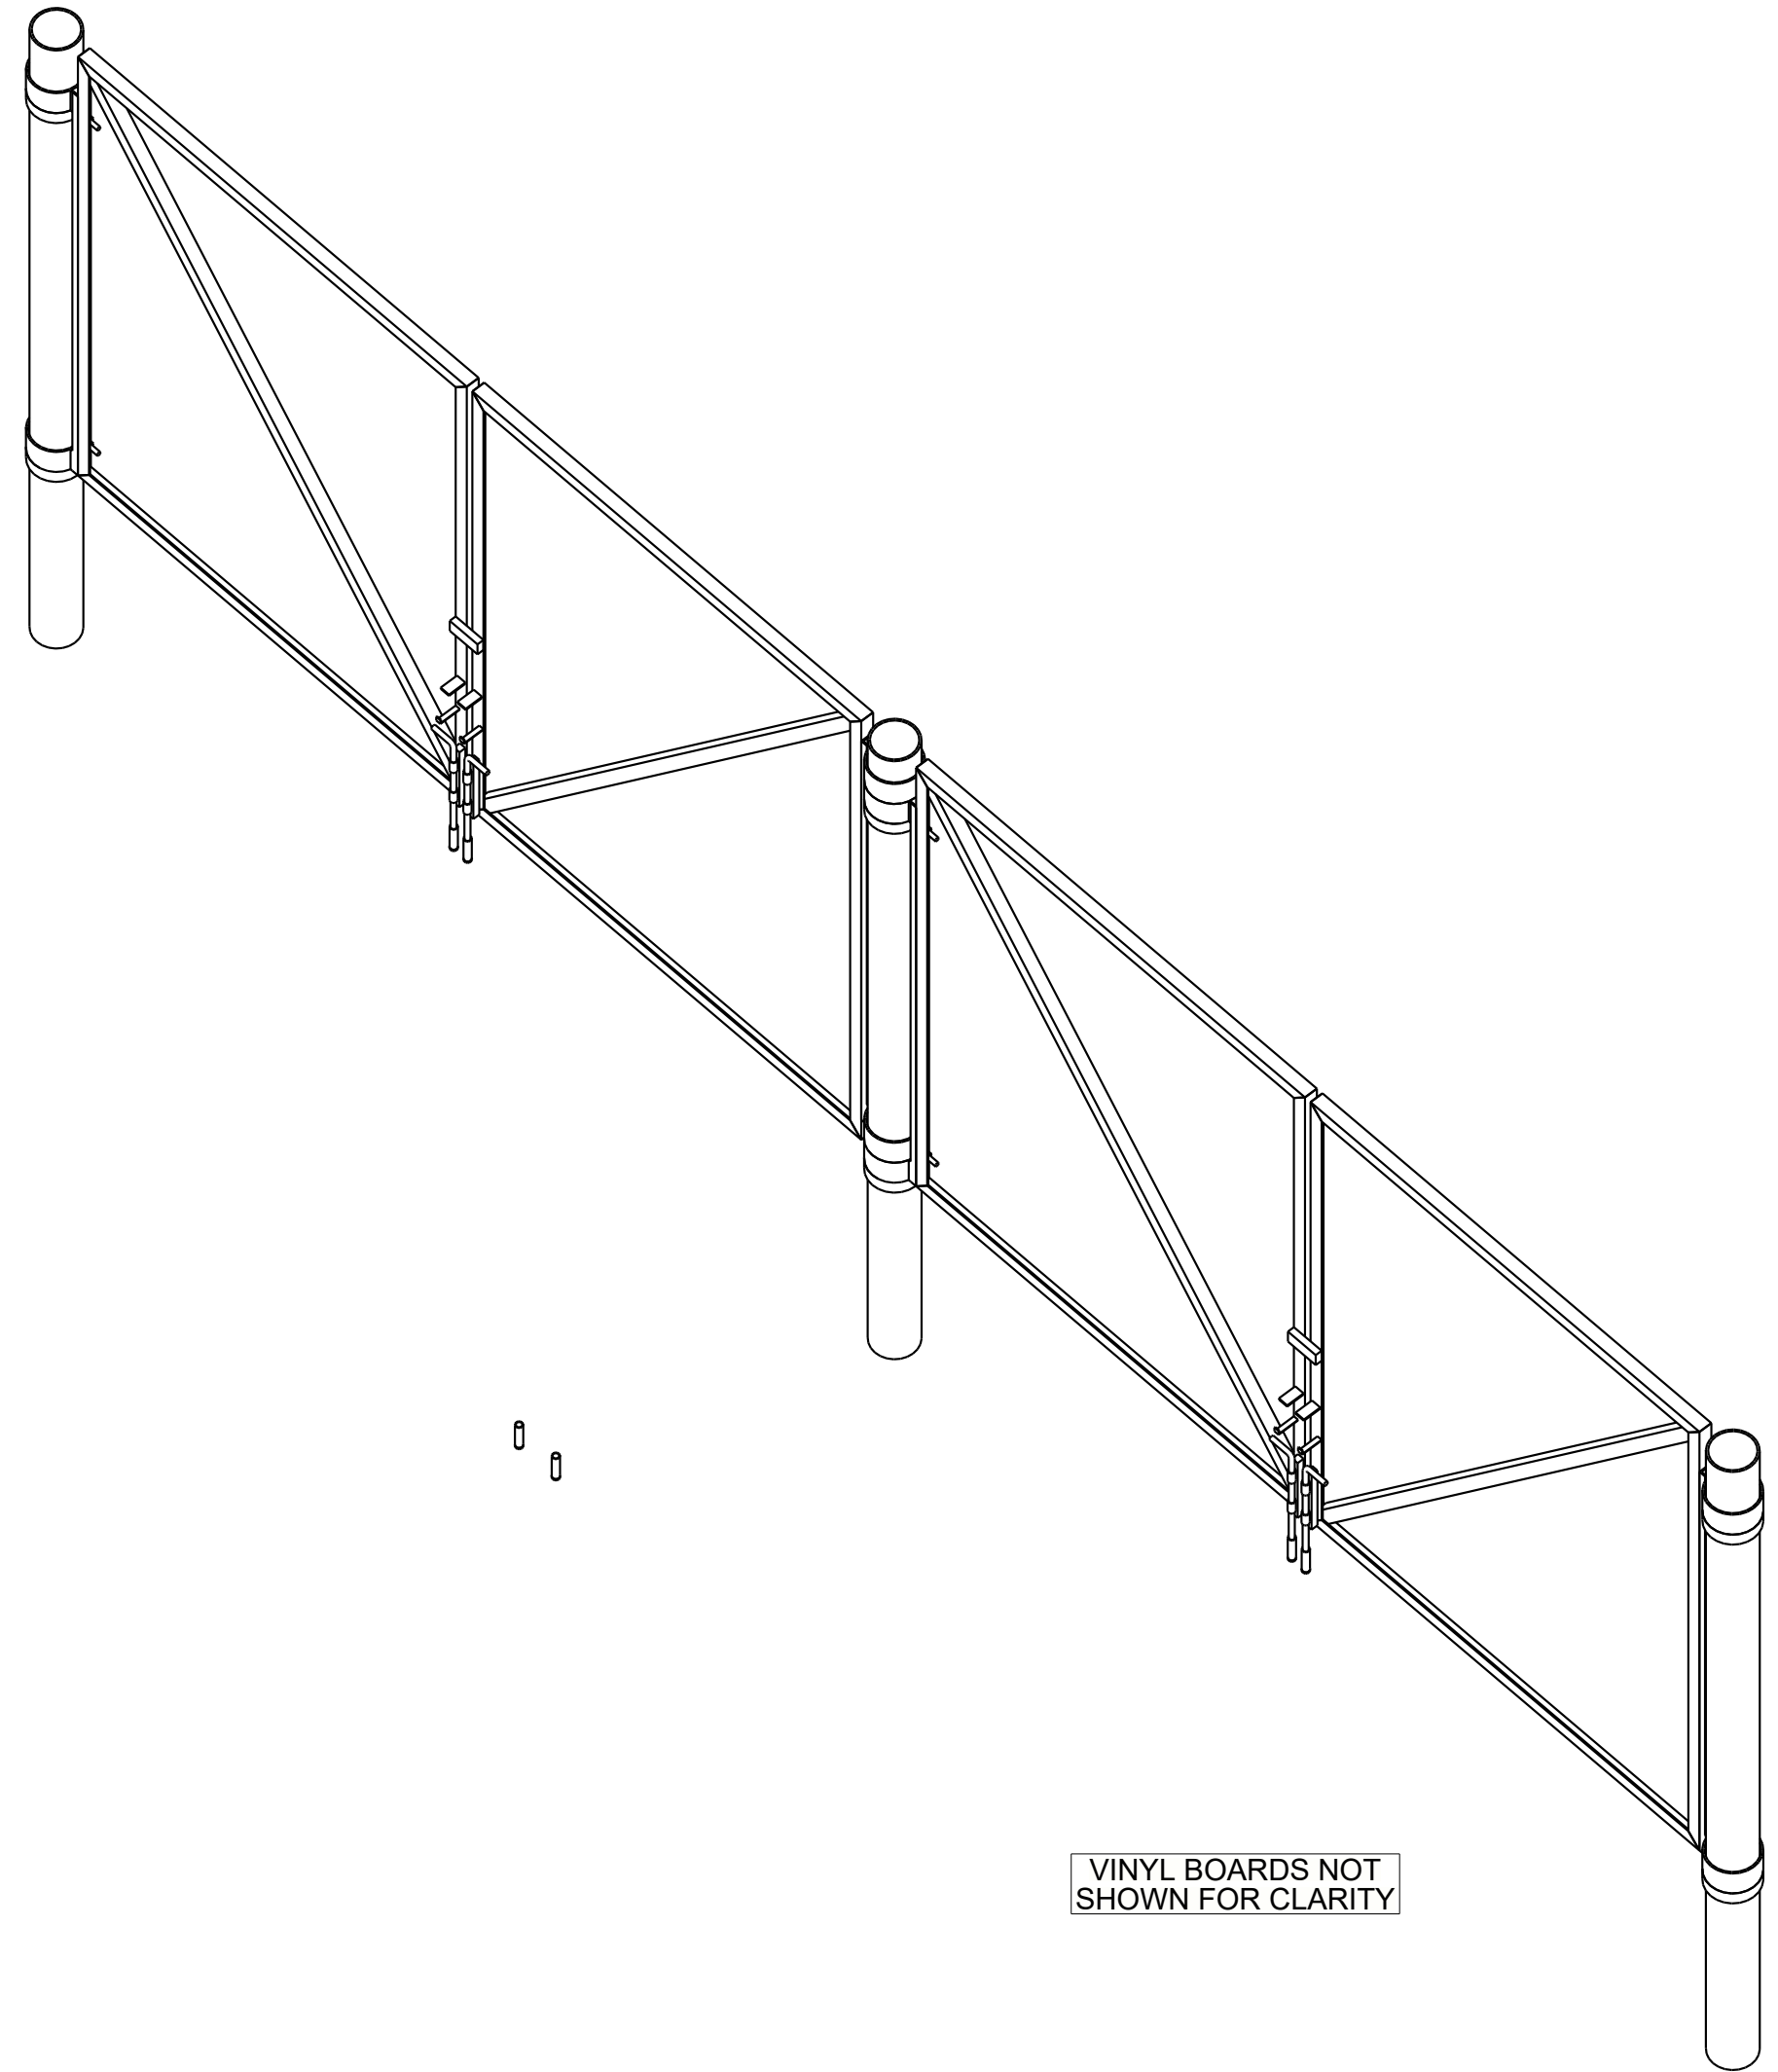

3D VIEW - DUMPSTER GATE & BOLLARD

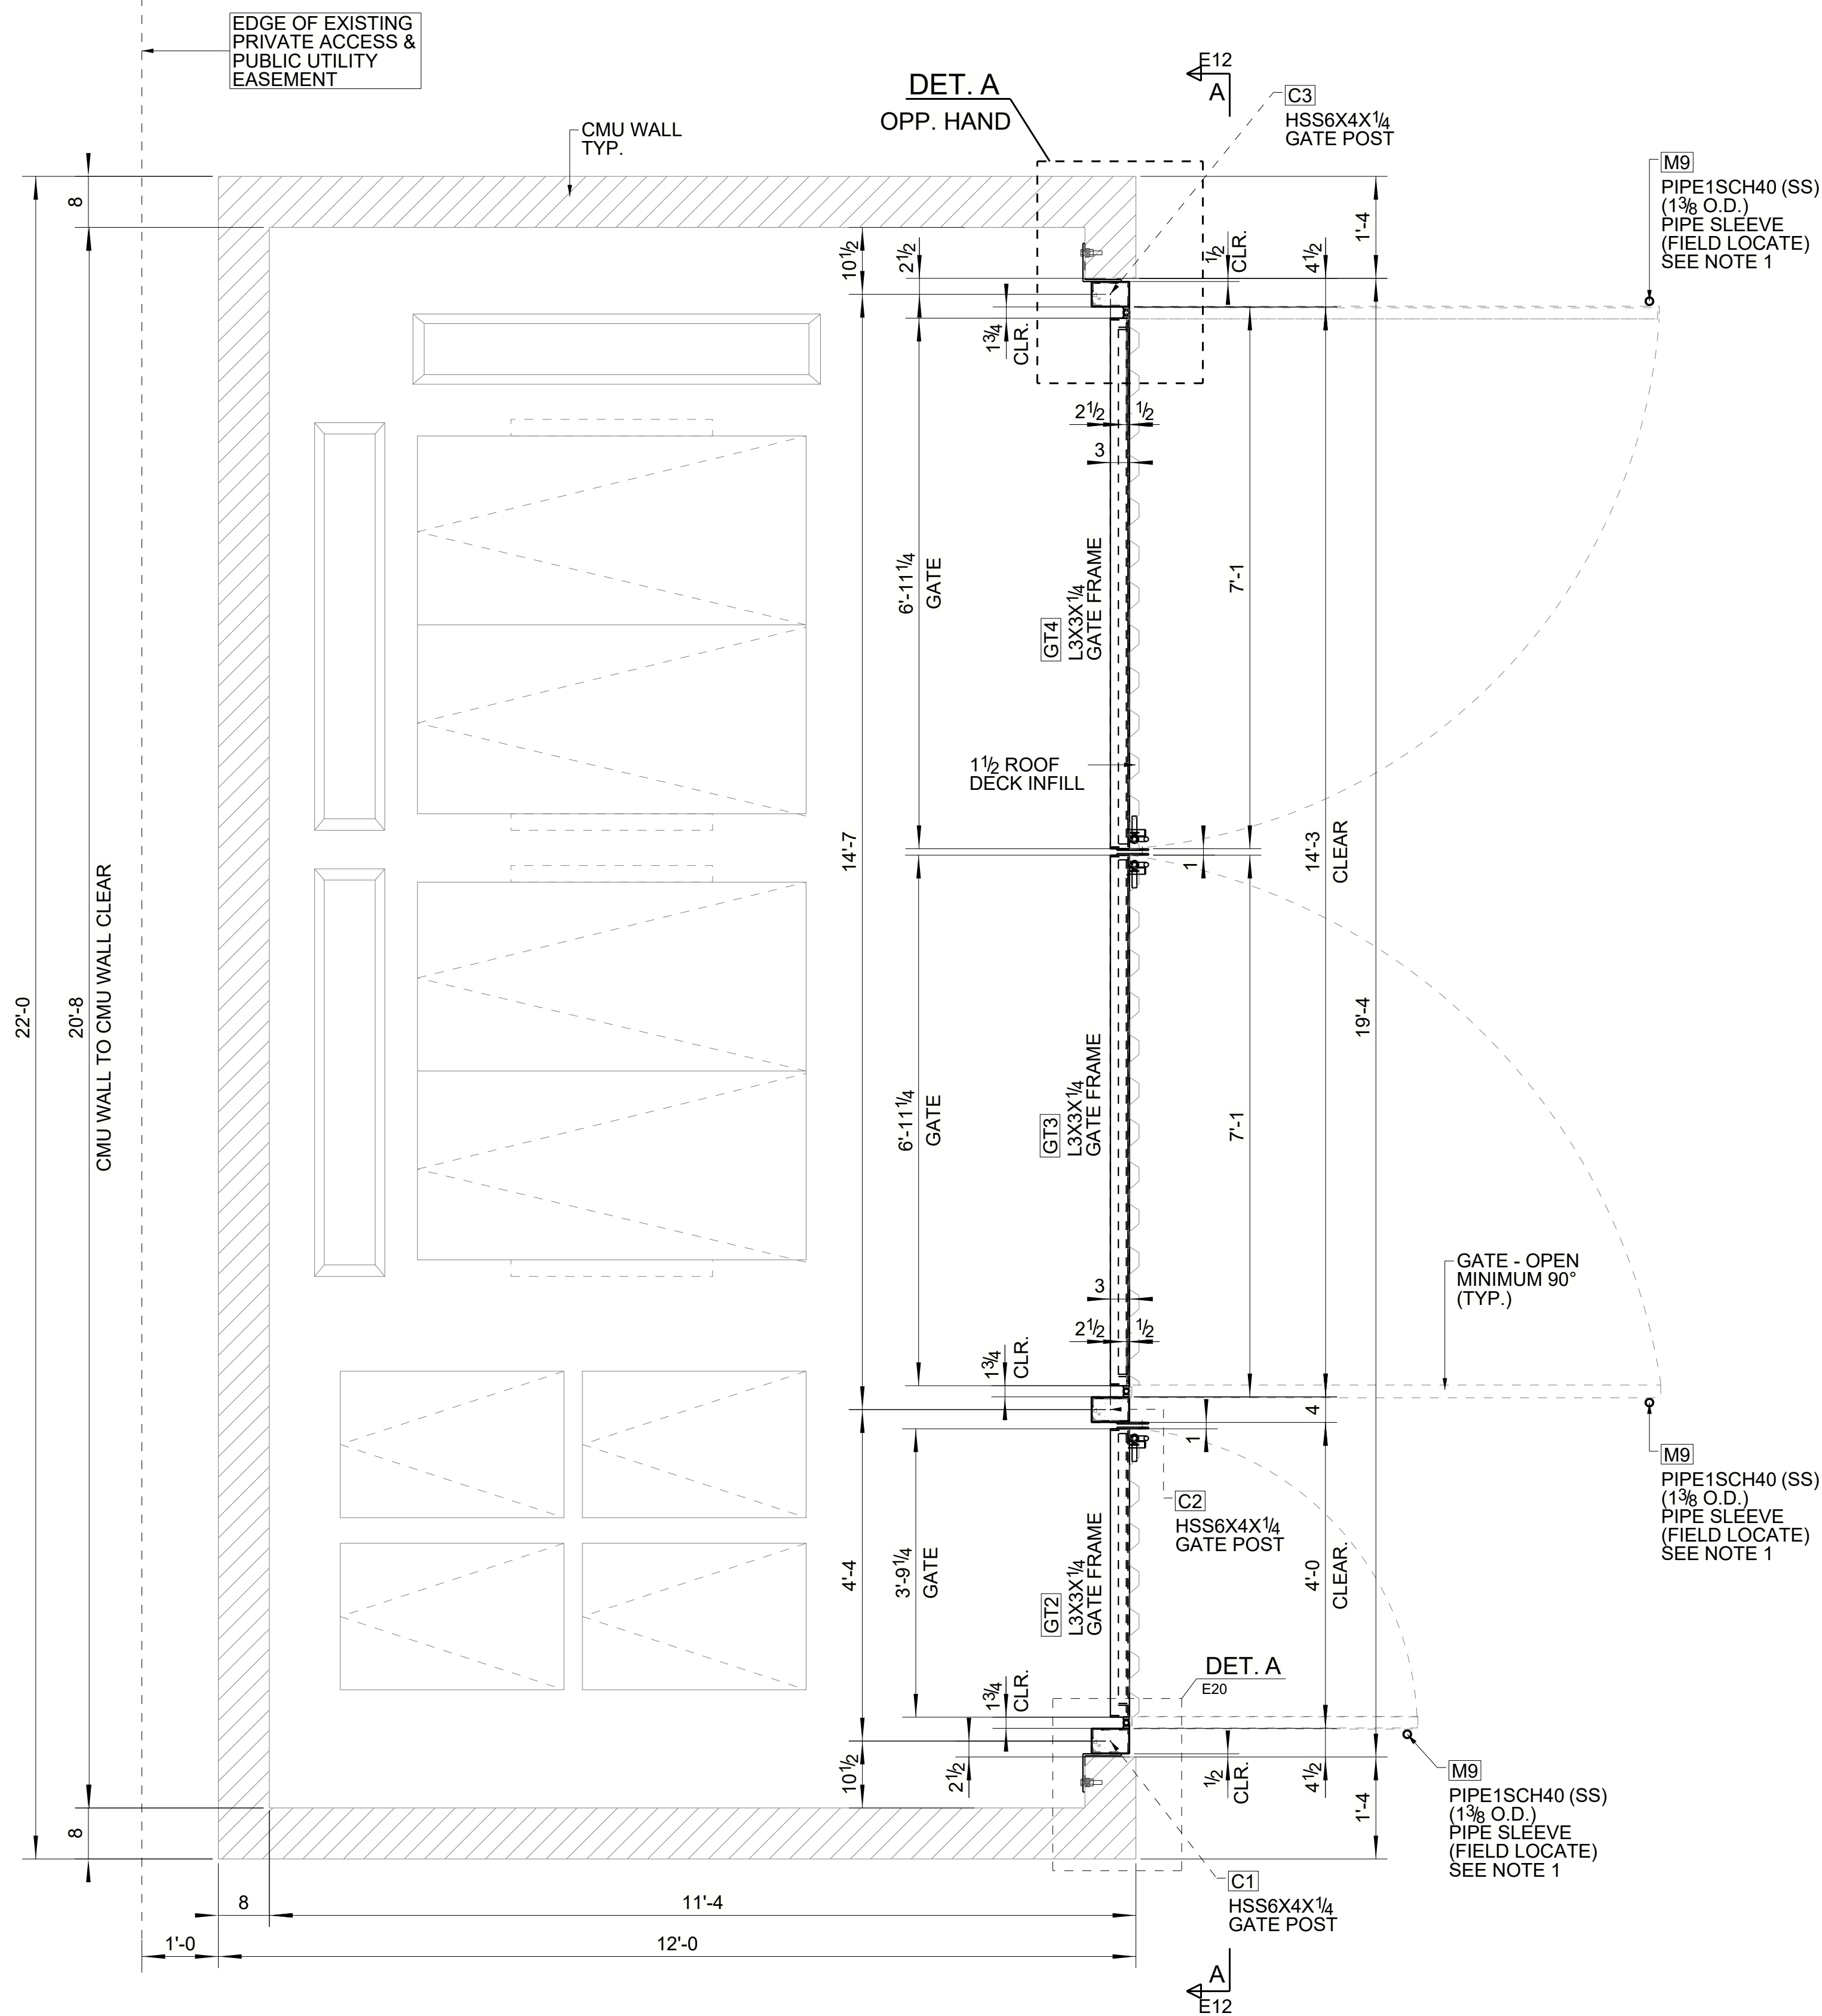



TRASH ENCLOSURE GATE LOCATION PLAN
(REFER : TRASH ENCLOSURE PLAN- 6/A102 & 2/S1)



- NOTES:**
1. REFER SHEET E12 FOR ELEVATION.
 2. REFER SHEET E20 FOR GATE TYPICAL SECTIONS & DETAILS.

ERECTOR NOTE :
ALL BOLTS MUST BE LOCATED IN CORE
THAT MUST BE GROUTED SOLIDS


FINISH NOTES :
ALL TRASH ENCLOSURE GATE STEEL MEMBERS IN THIS SHEET SHALL
RECEIVE SHERWIN WILLIAMS - SW7015 REPOSE GRAY PAINT.
ALL CANE BOLT, CANE BOLT GUIDE PLATE AND RECEIVER SLEEVES
TO BE STAINLESS STEEL (SS 316 GRADE)

NOTE 1:
PROVIDE RECESSED BOLT RECEIVER SLEEVE
FLUSH WITH PAVEMENT AT EACH GATE LEAF
AT CLOSED AND OPEN POSITIONS. LOCATE
RECEIVERS TO ALLOW GATES TO SWING A
MINIMUM OF 90 DEGREES

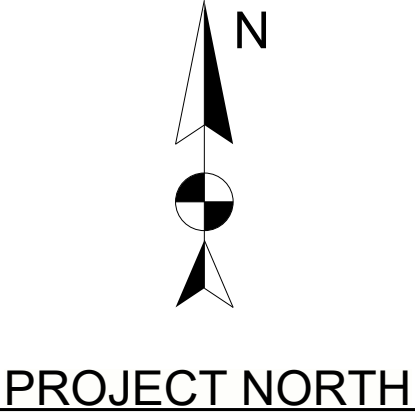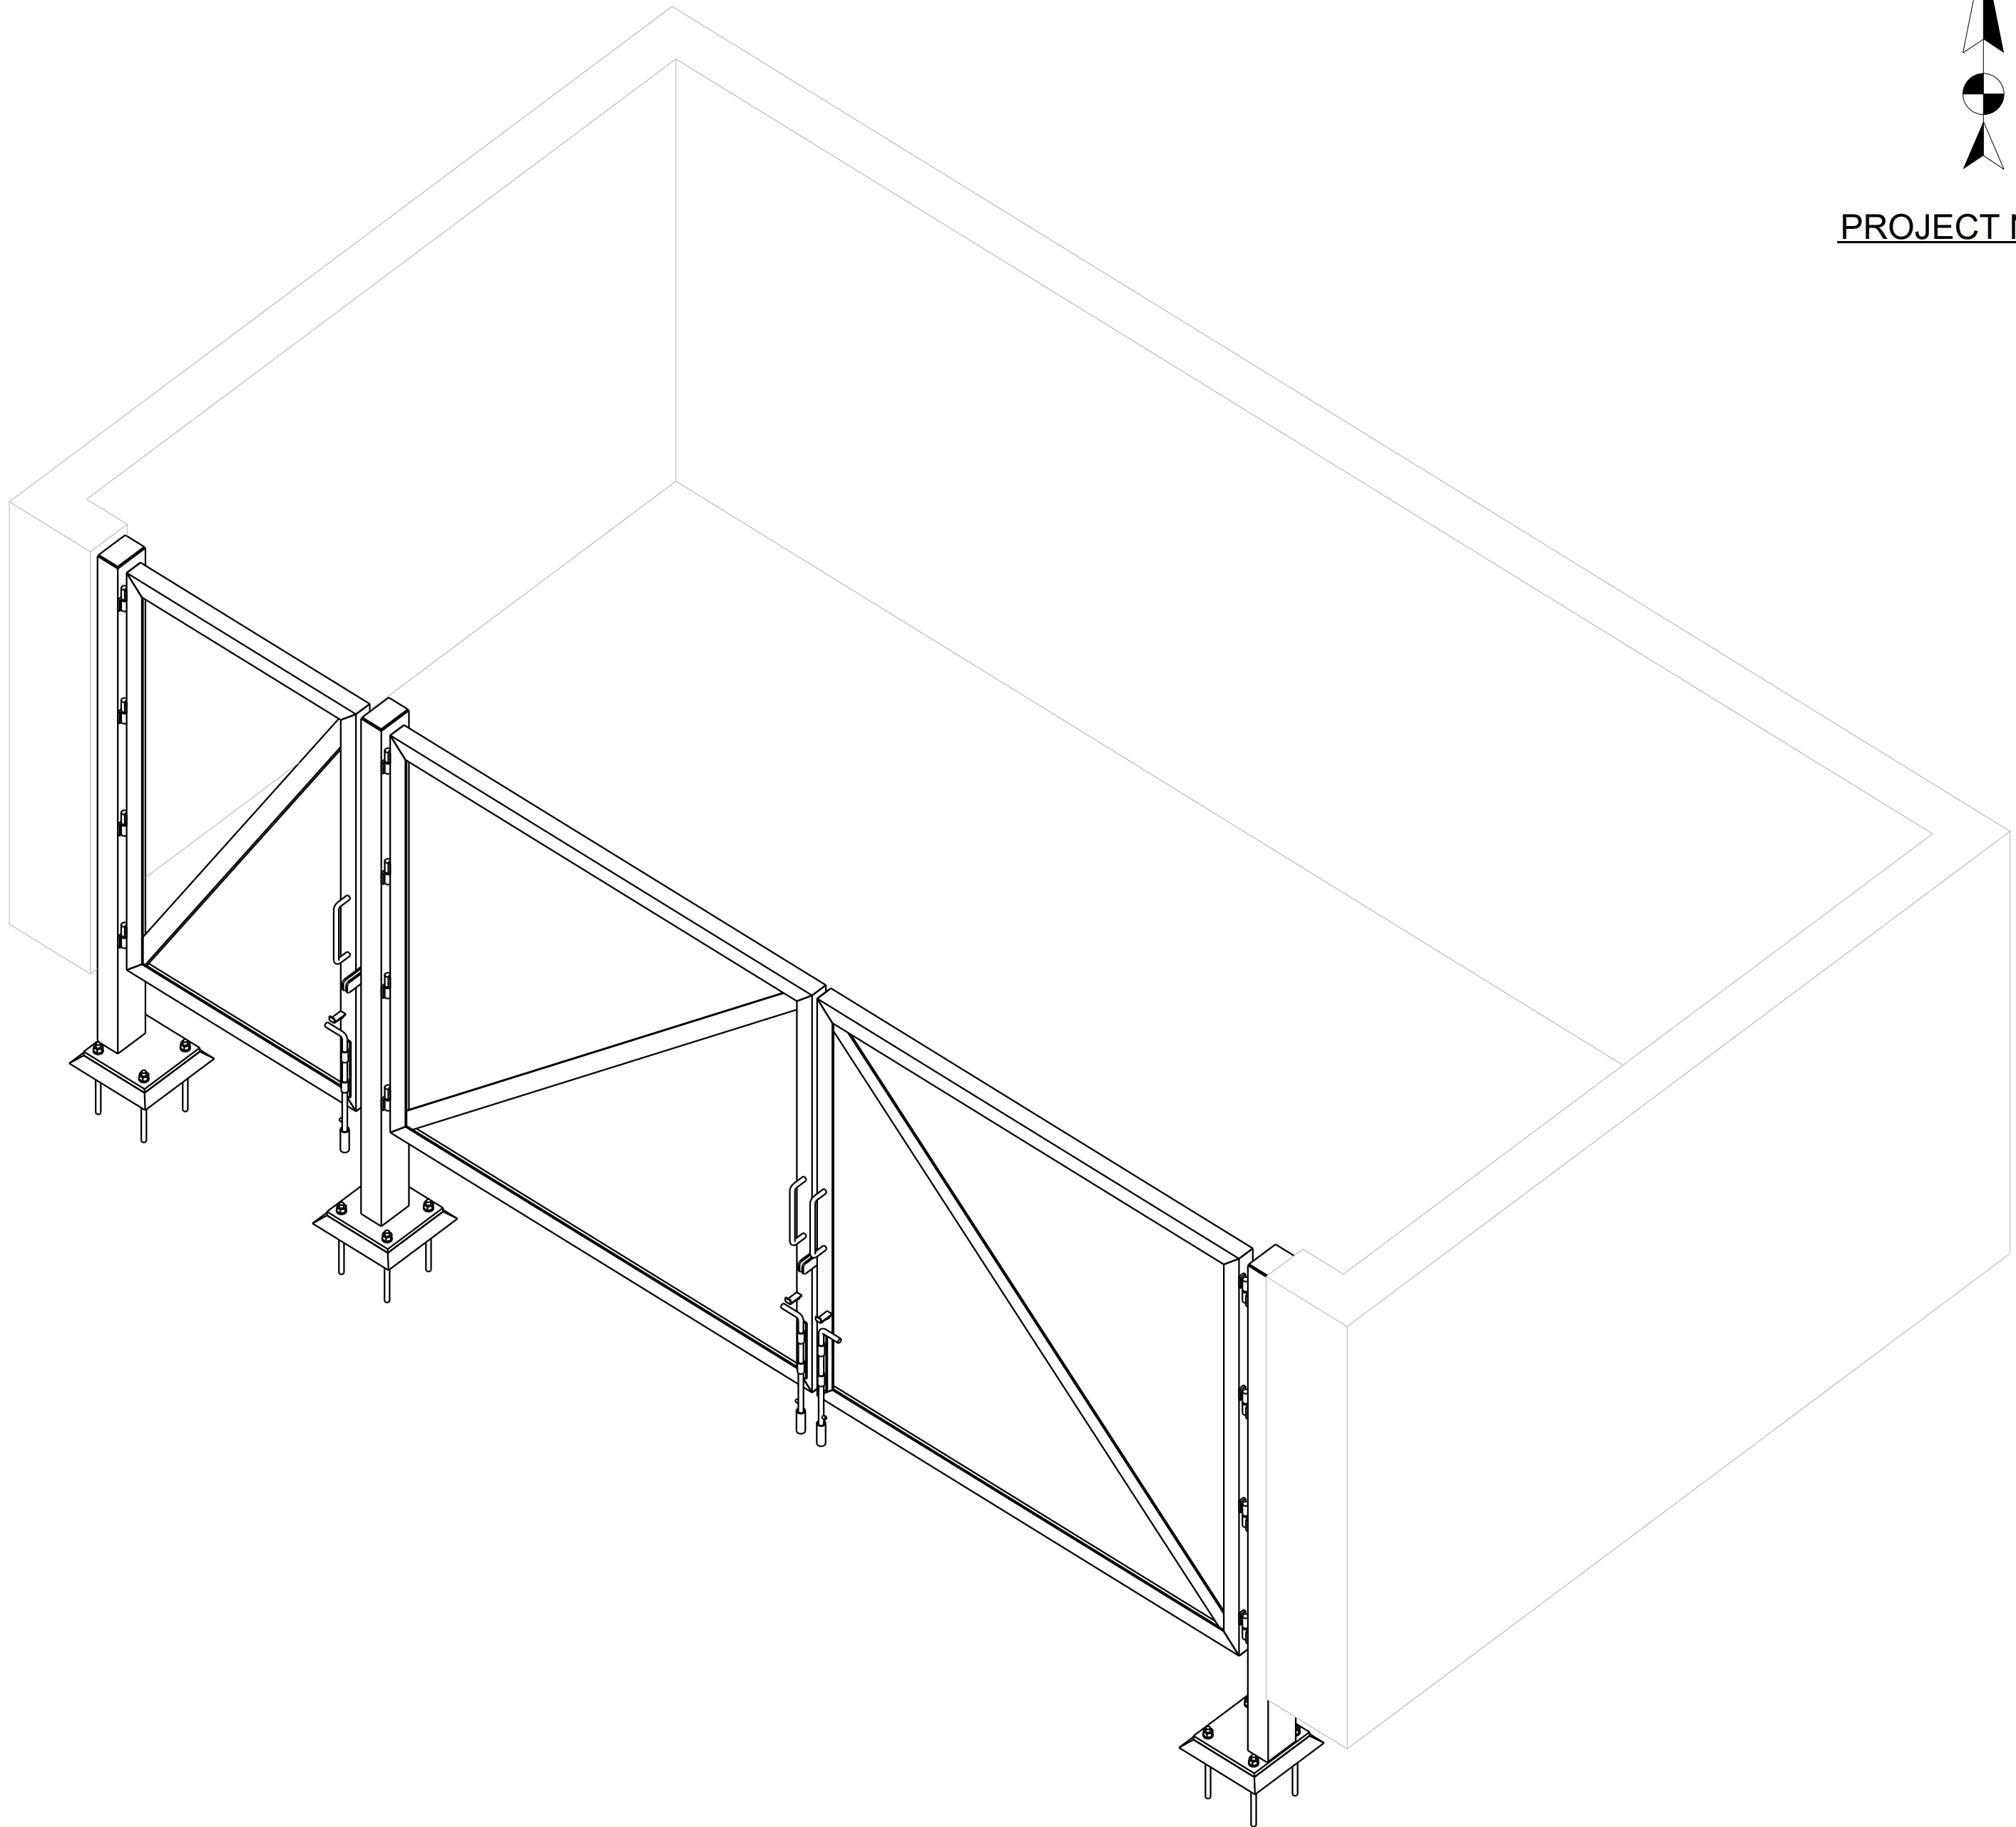

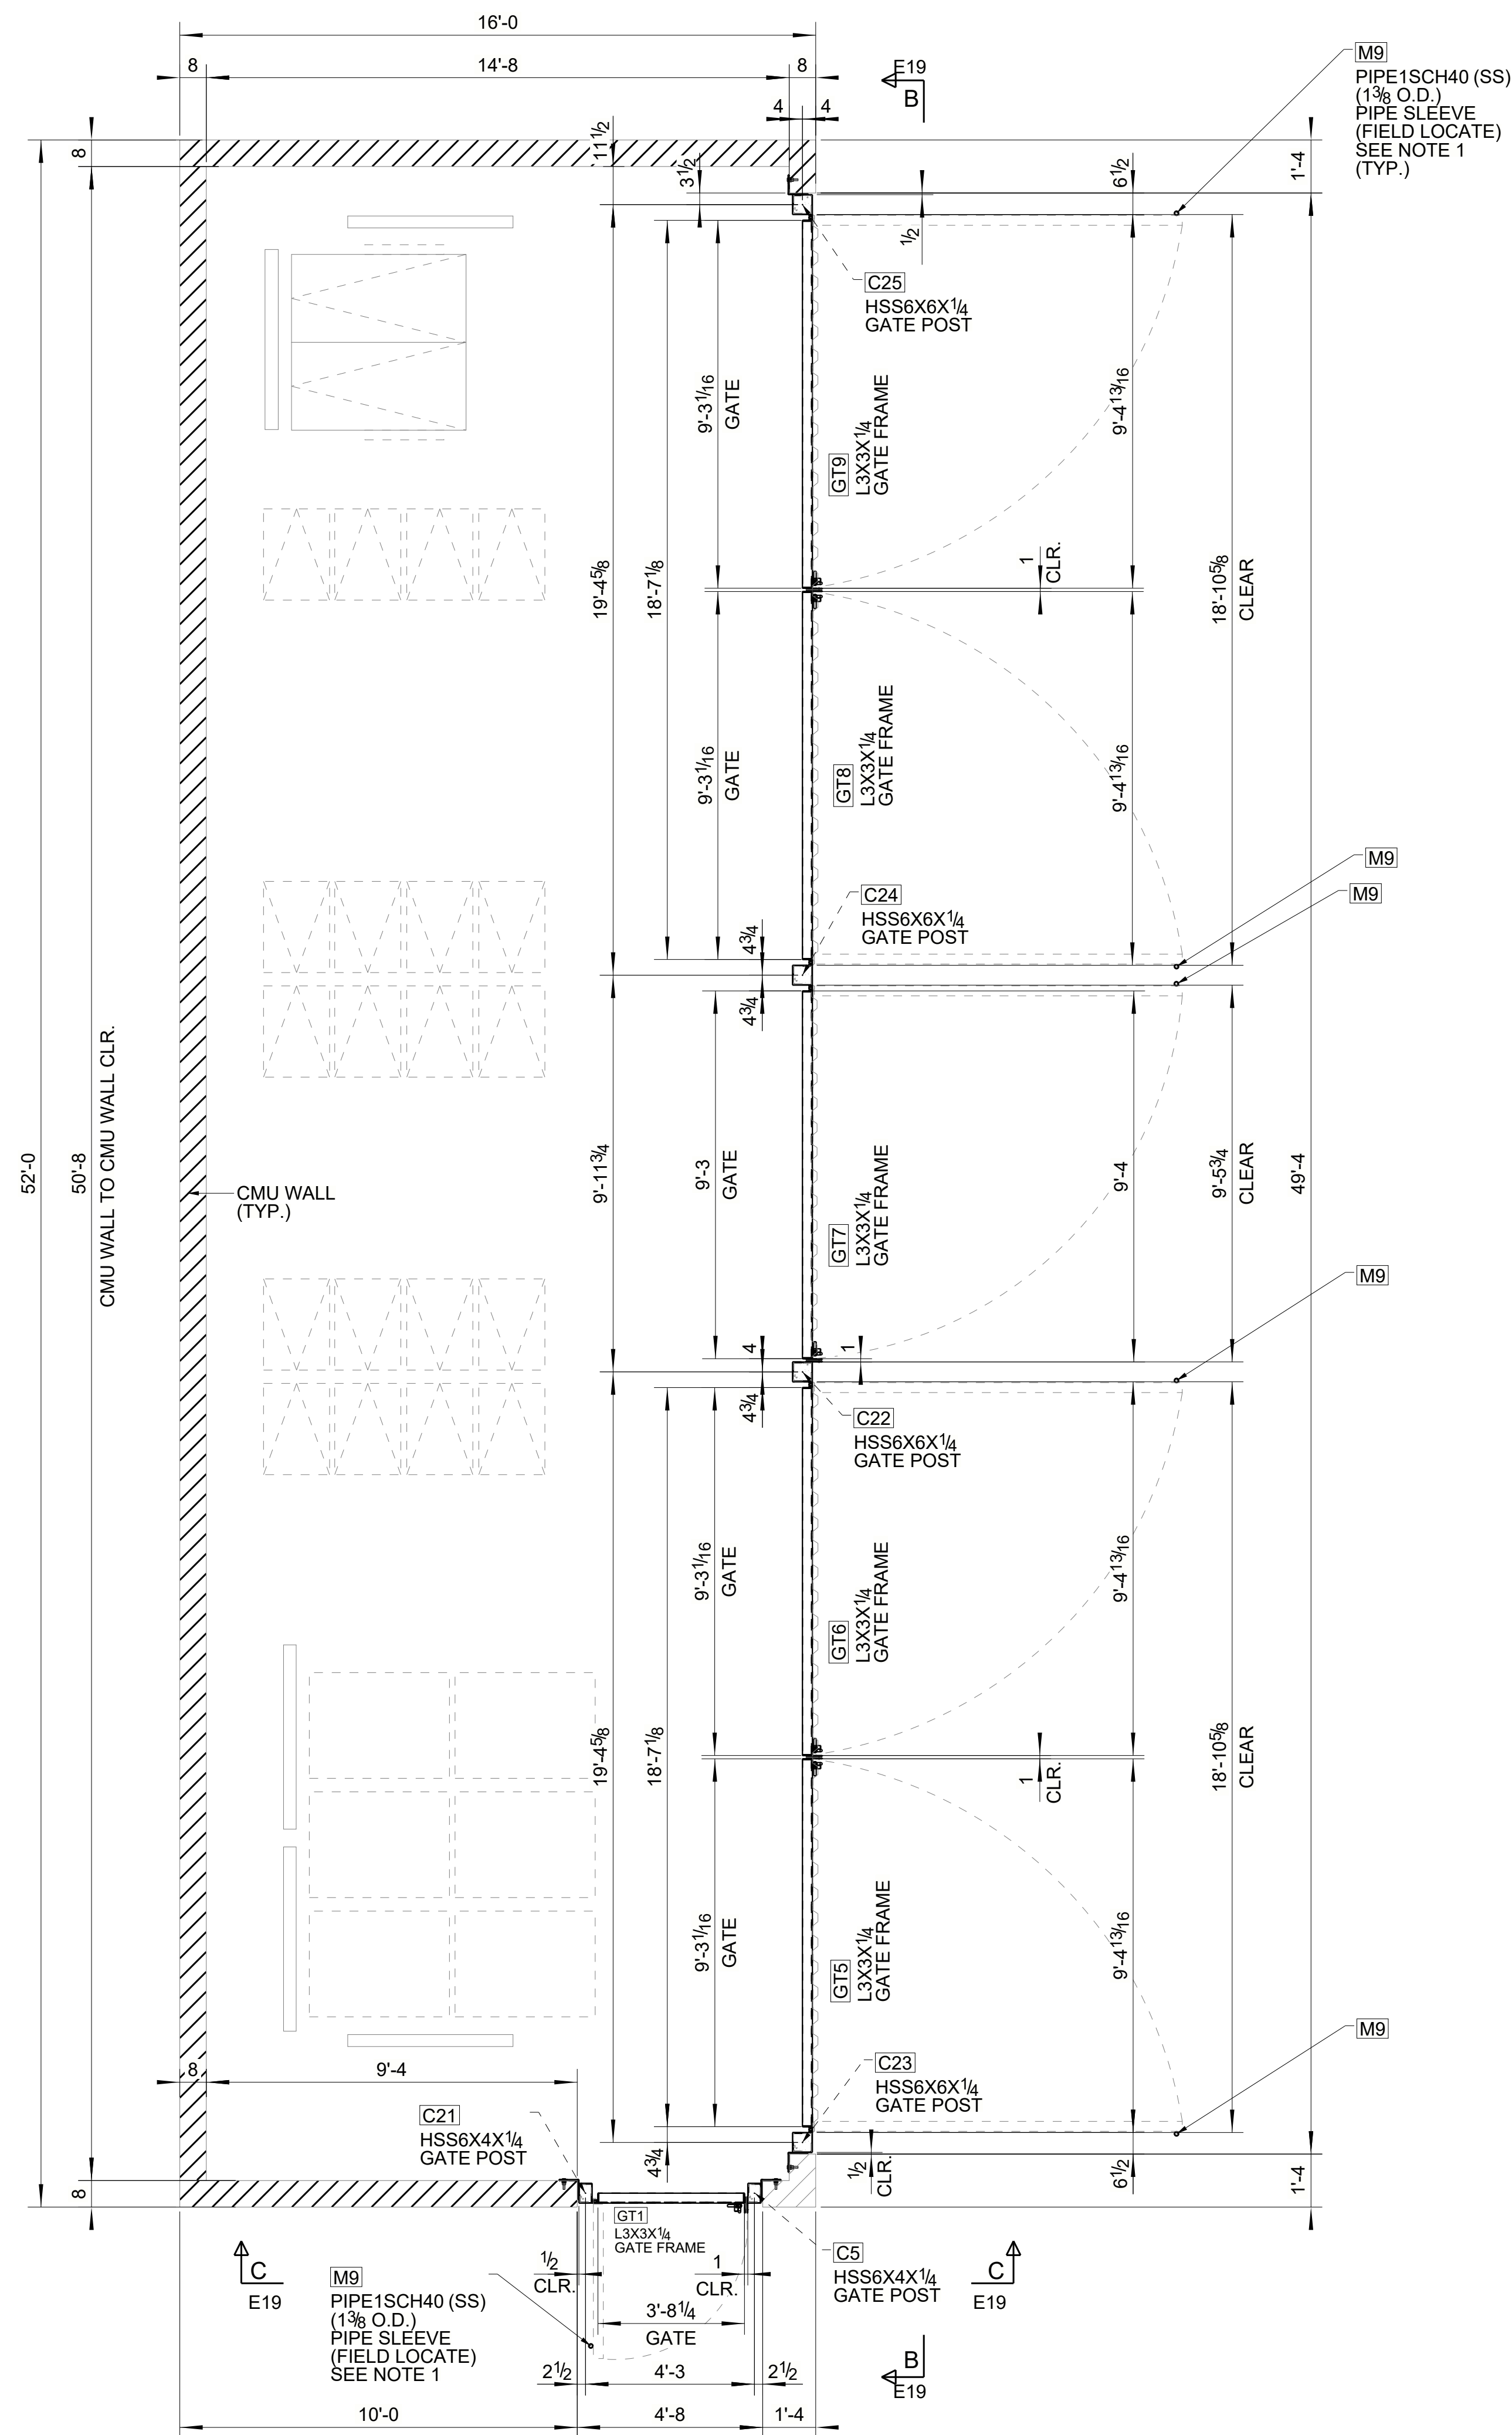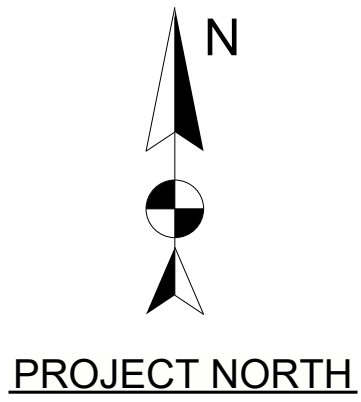

LARGE TRASH ENCLOSURE GATE LOCATION PLAN
(REFER : LARGE TRASH ENCLOSURE ENLARGED PLAN- 7/A104, 8/A101.5)

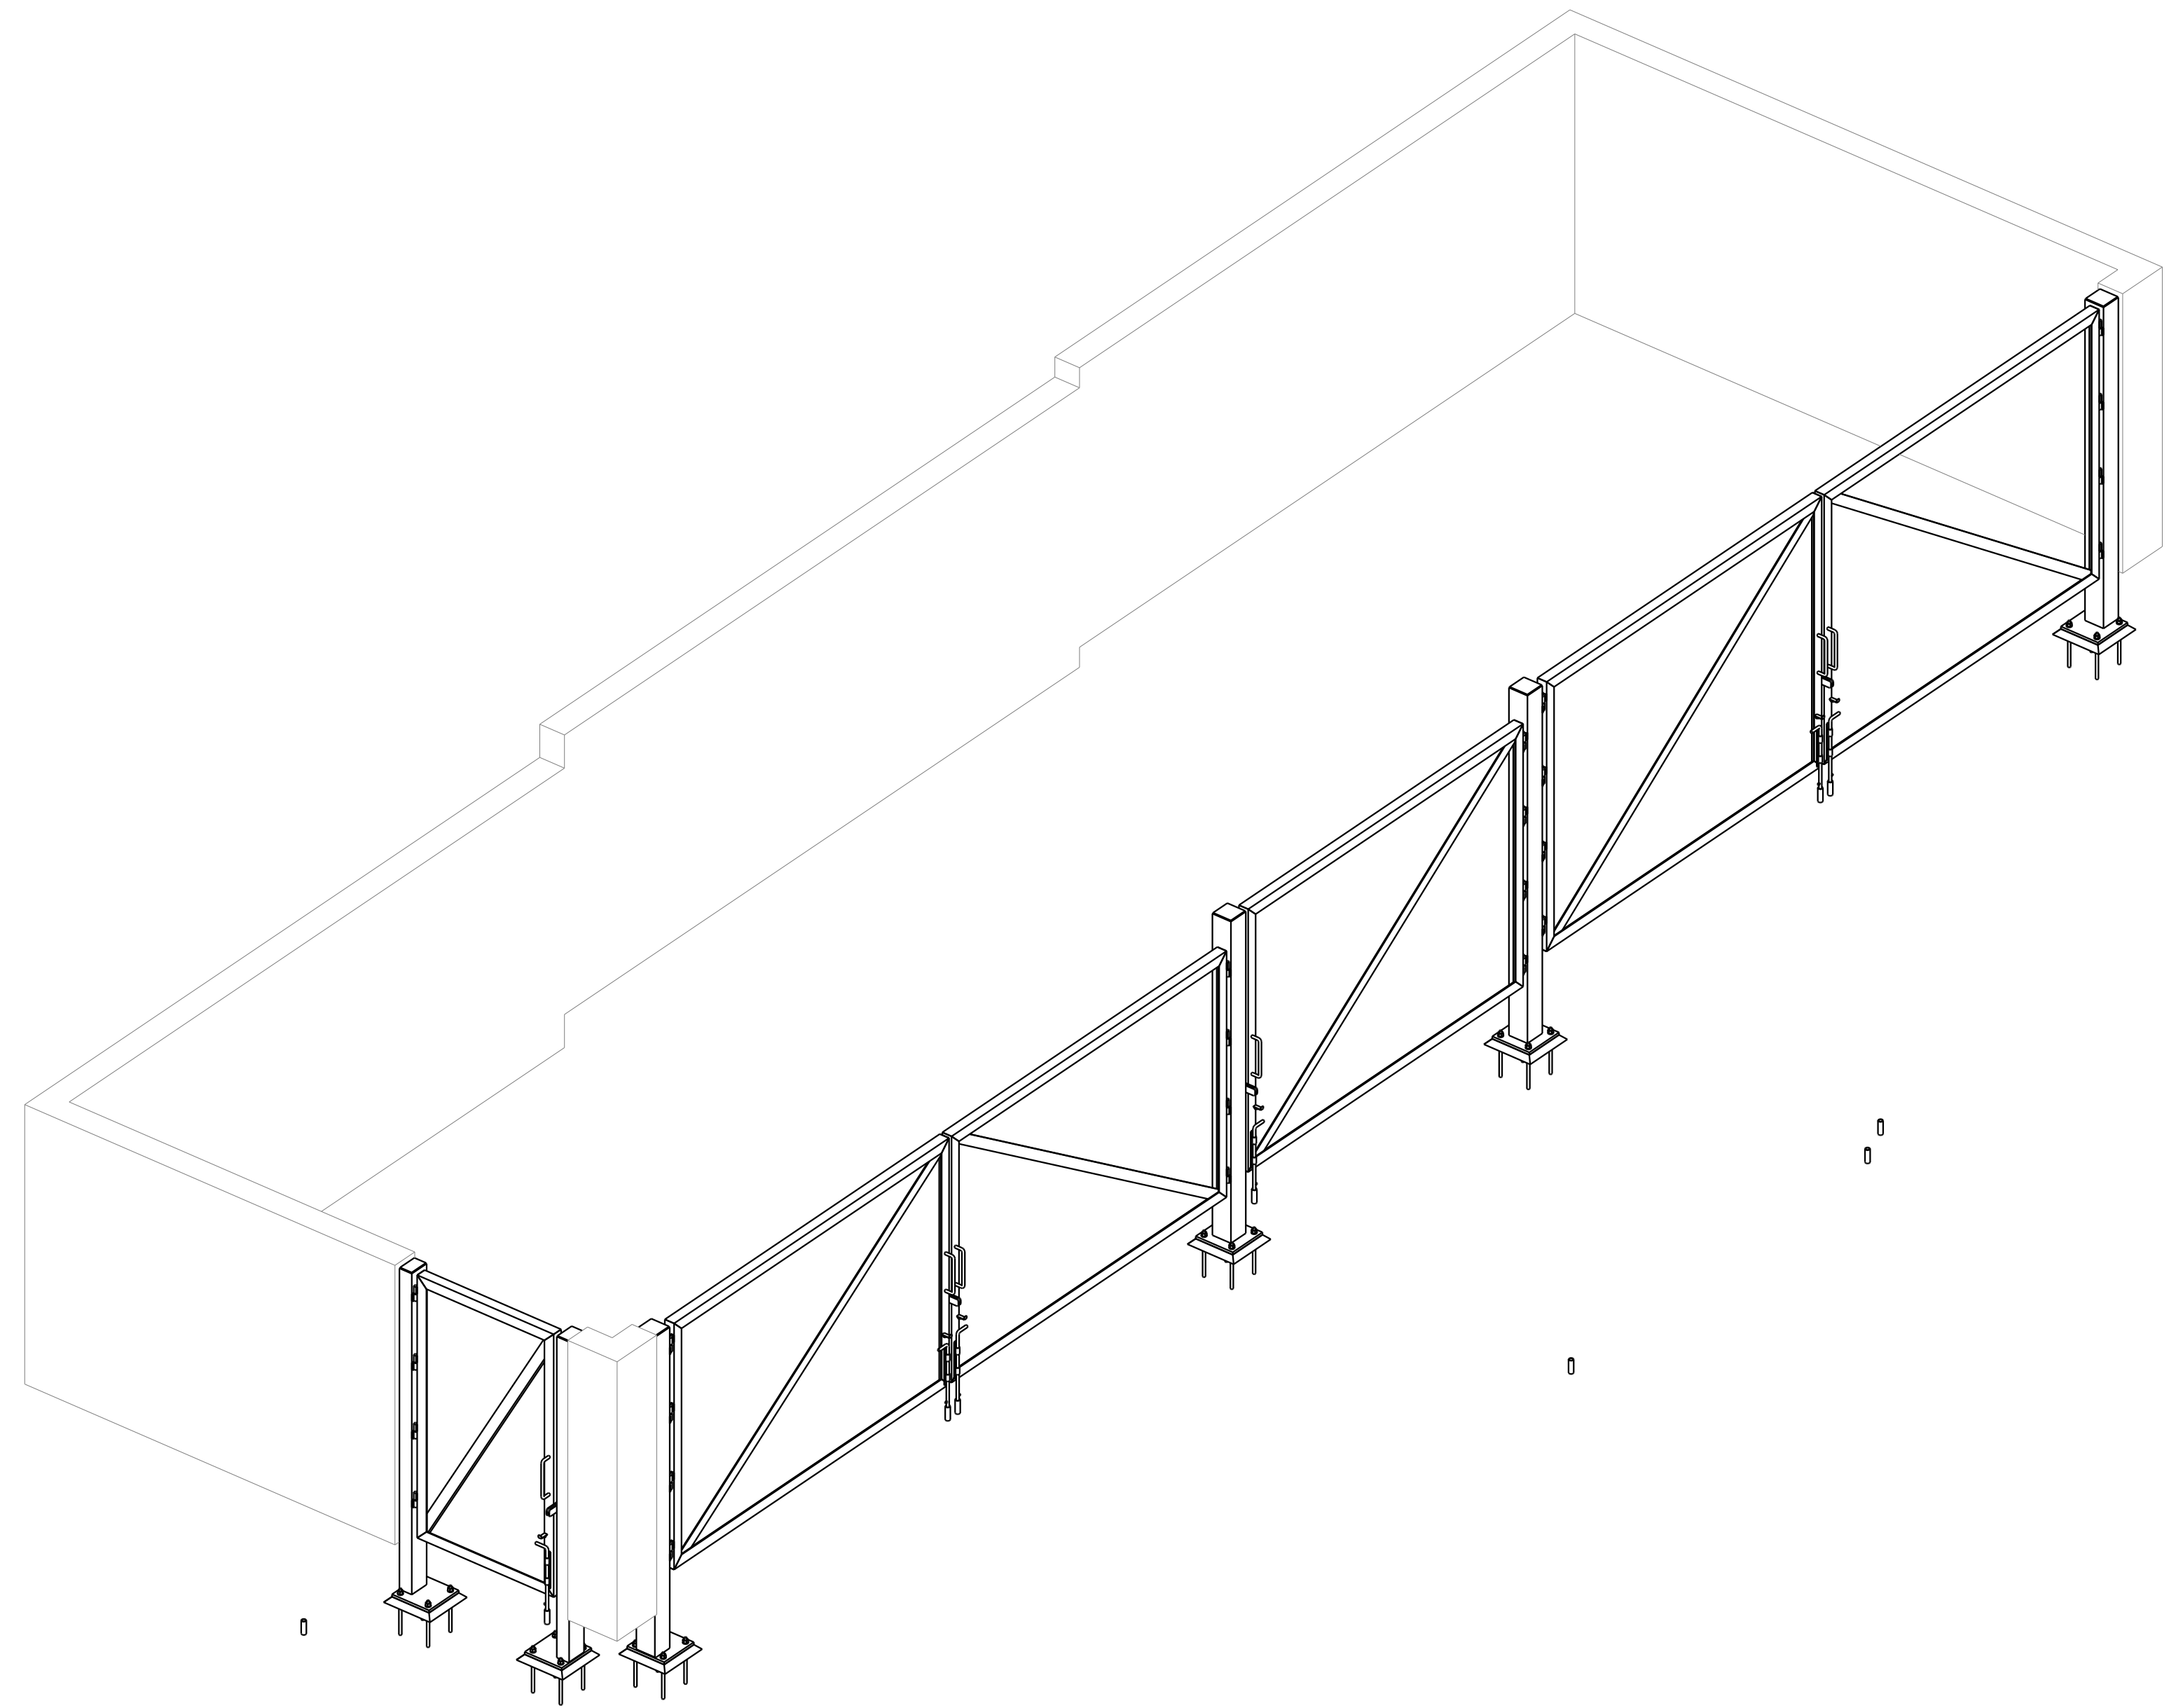







3D VIEW -LARGE TRASH ENCLOSURE GATE

NOTE 1 :
PROVIDE RECESSED BOLT RECEIVER SLEEVE FLUSH WITH PAVEMENT AT EACH GATE LEAF AT CLOSED AND OPEN POSITIONS. LOCATE RECEIVERS TO ALLOW GATES TO SWING A MINIMUM OF 90 DEGREES

ERECTOR NOTE :
ALL BOLTS MUST BE LOCATED IN CORE THAT SHOULD BE GROUTED SOLIDS







FINISH NOTES :
ALL TRASH ENCLOSURE GATE STEEL MEMBERS IN THIS SHEET SHALL RECEIVE SHERWIN WILLIAMS - SW7015 REPOSE GRAY PAINT.
ALL CANE BOLT, CANE BOLT GUIDE PLATE AND RECEIVER SLEEVES TO BE STAINLESS STEEL (SS 316 GRADE)

- NOTES :**
1. REFER SHEET E19 FOR ELEVATION
 2. REFER SHEET E20 FOR TYPICAL SECTION & DETAILS.

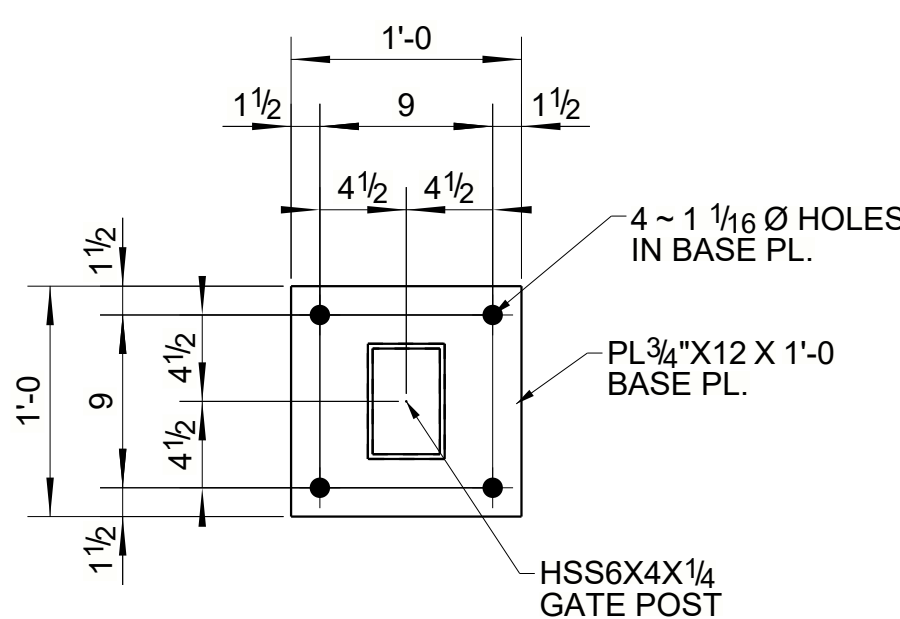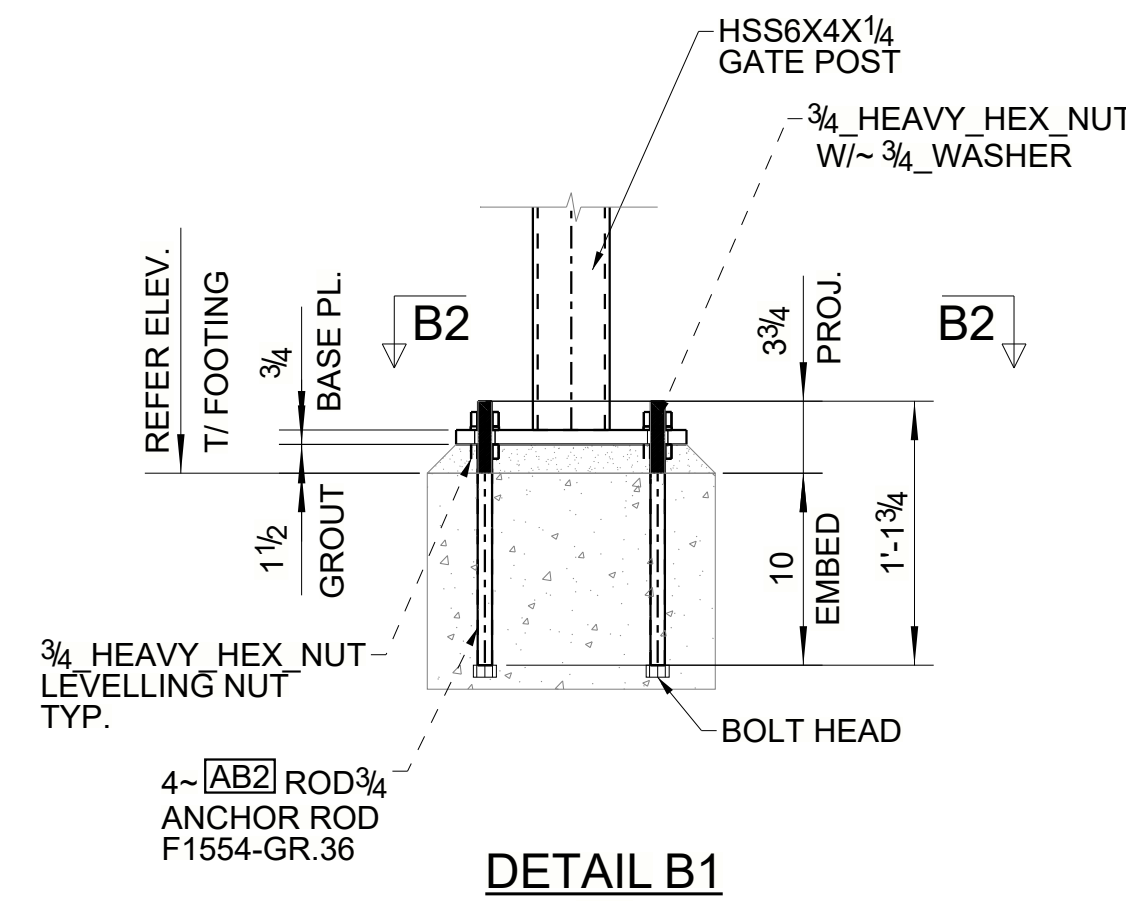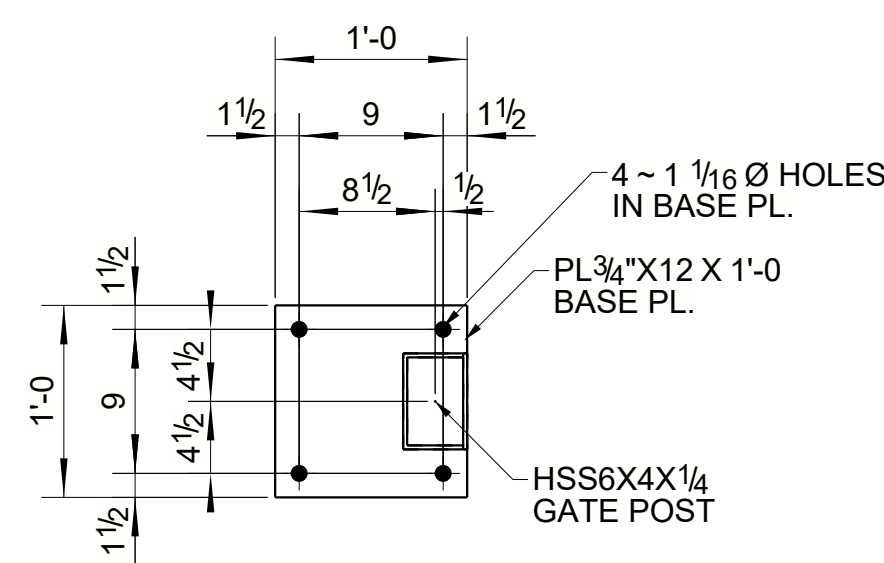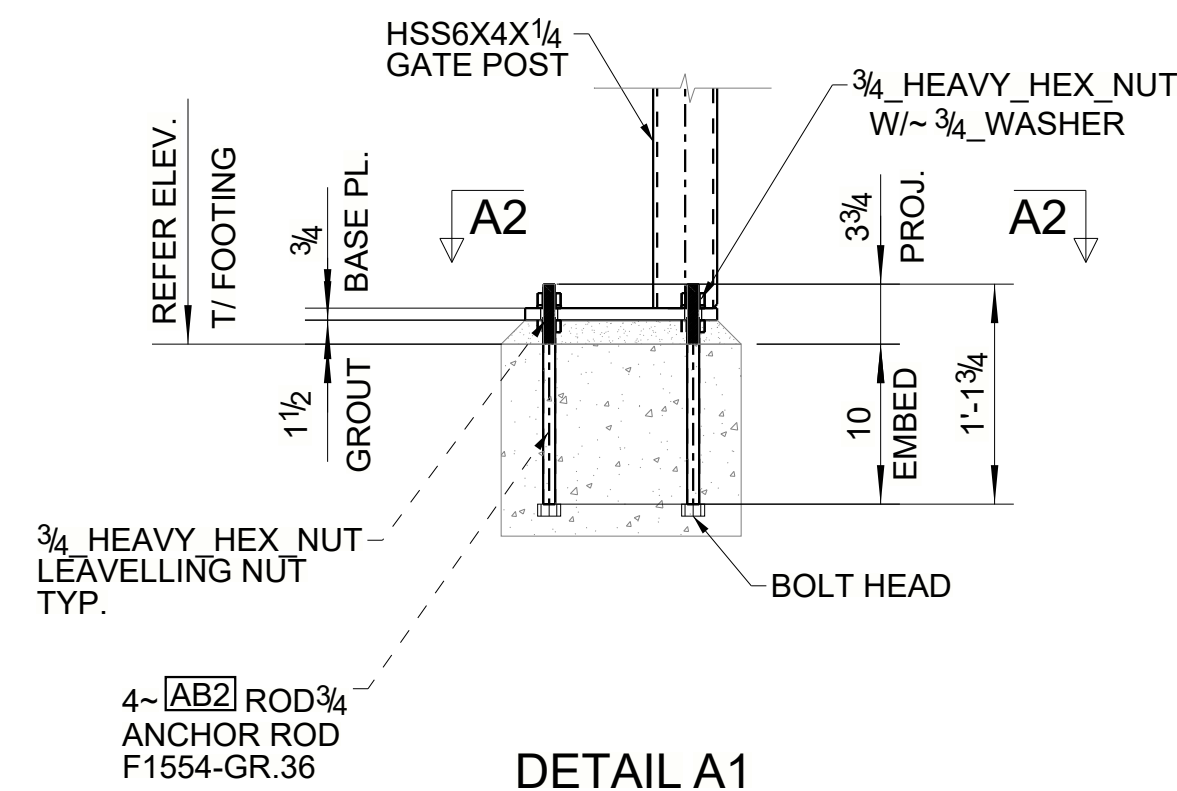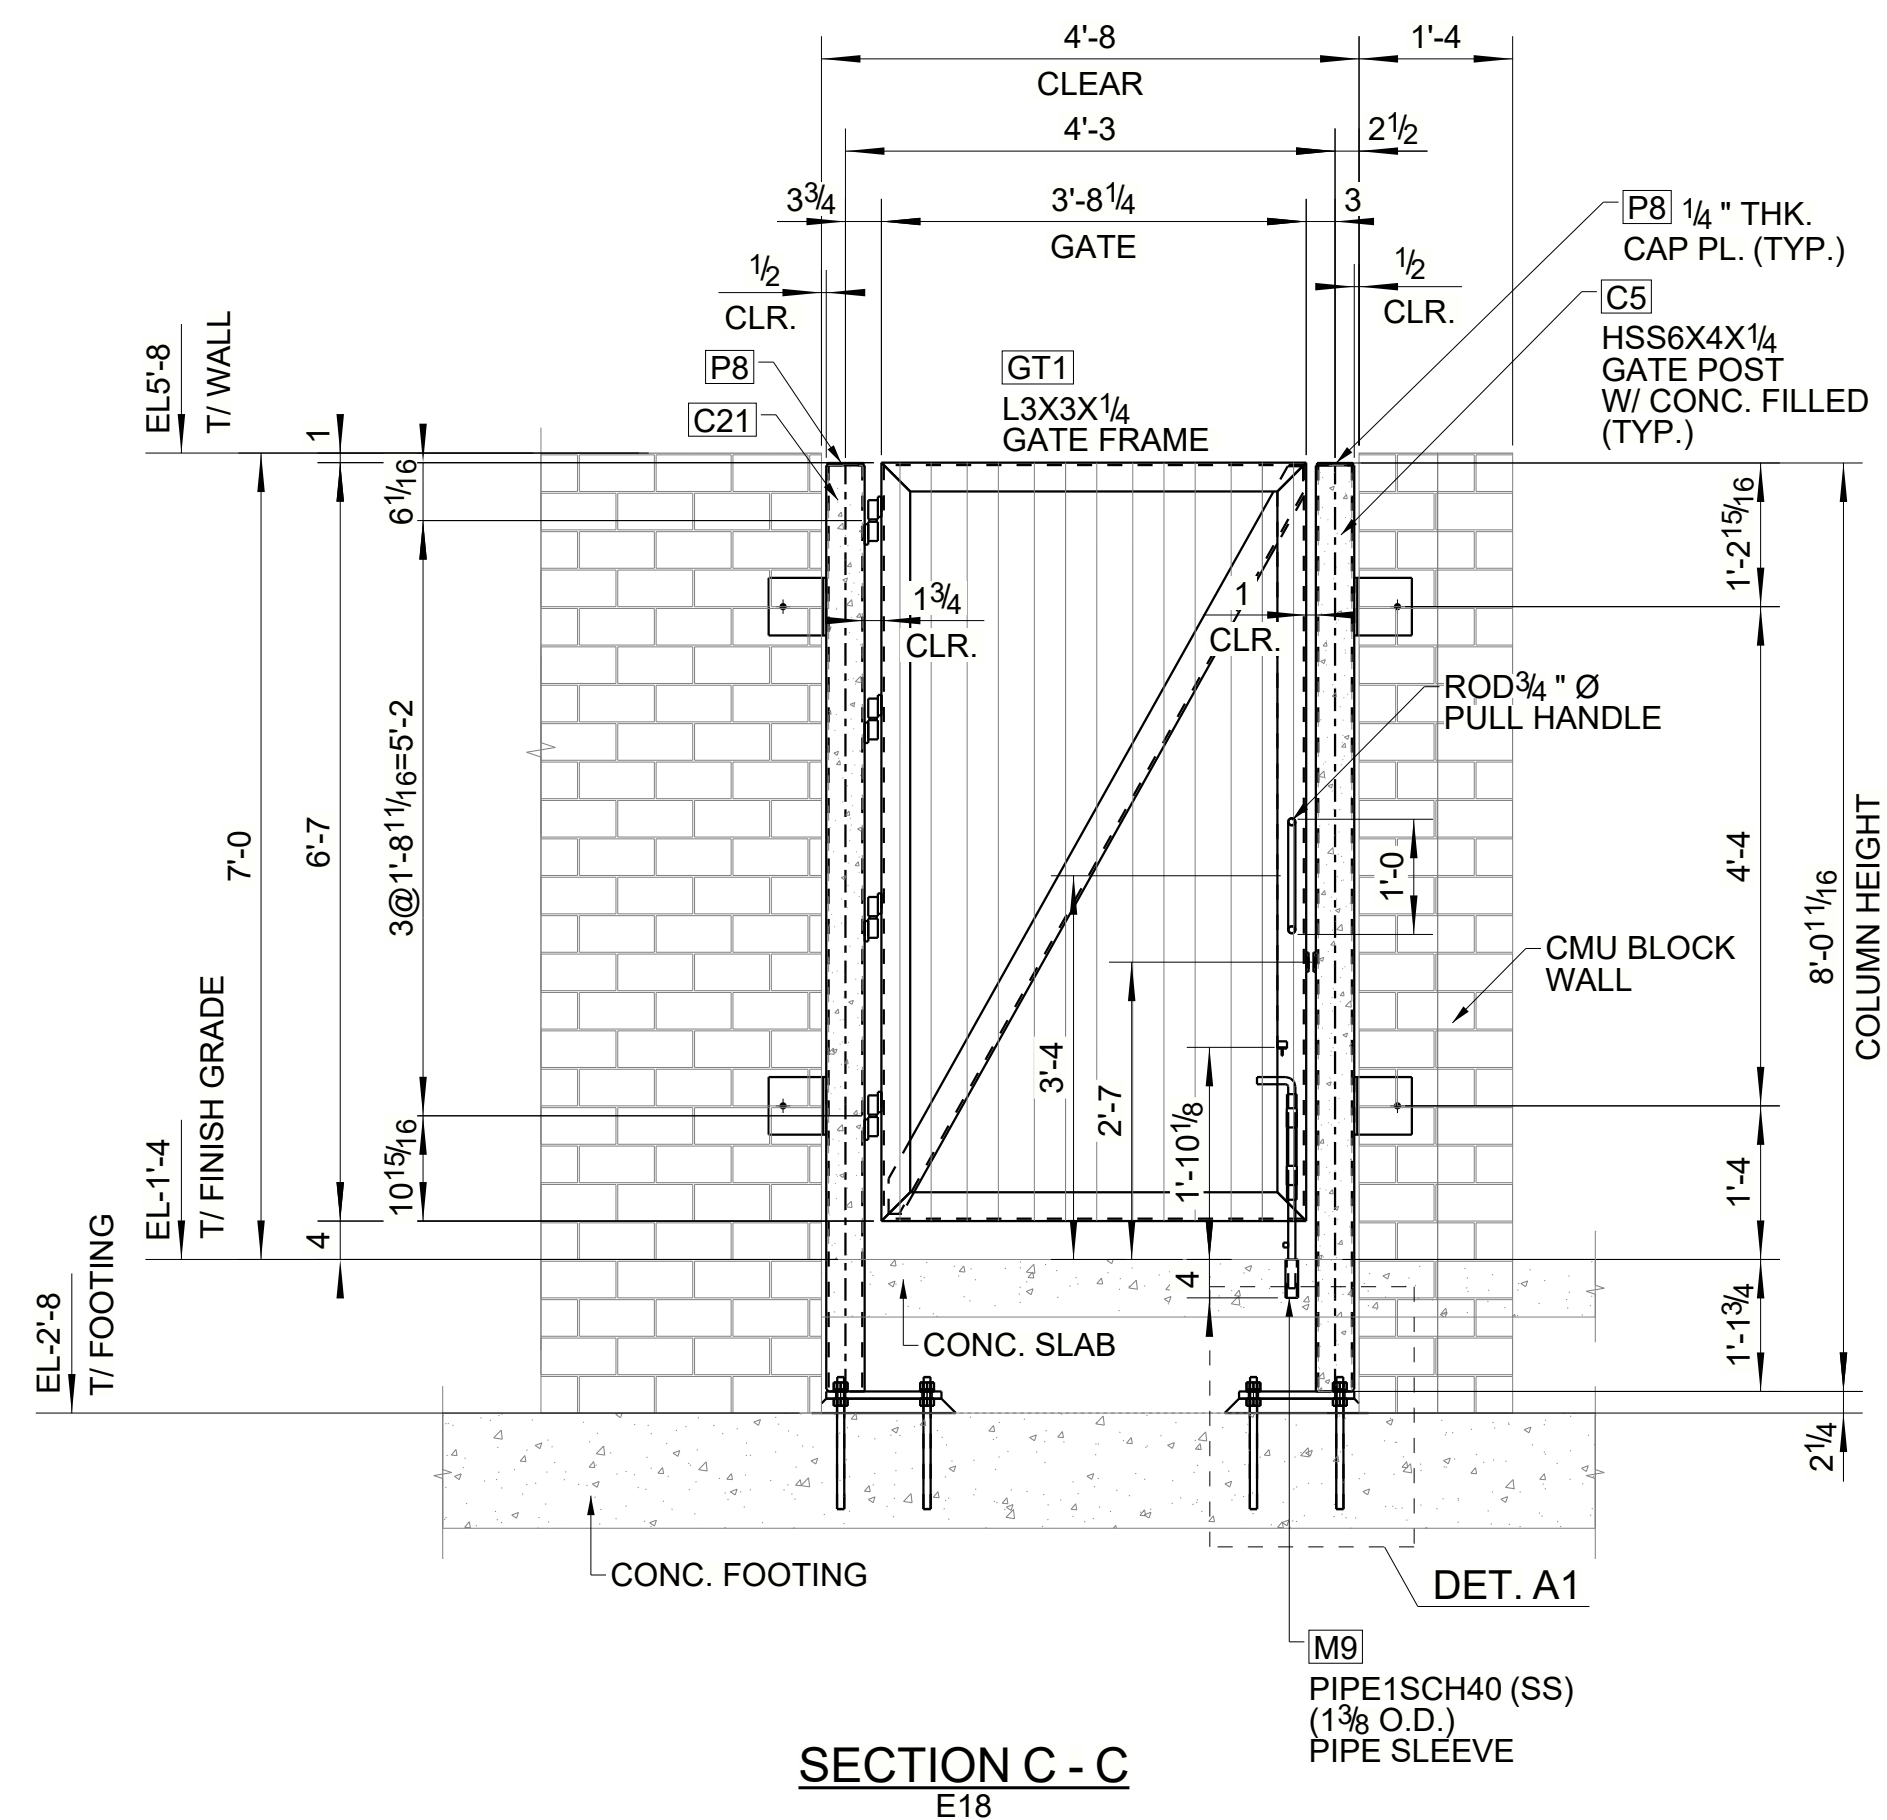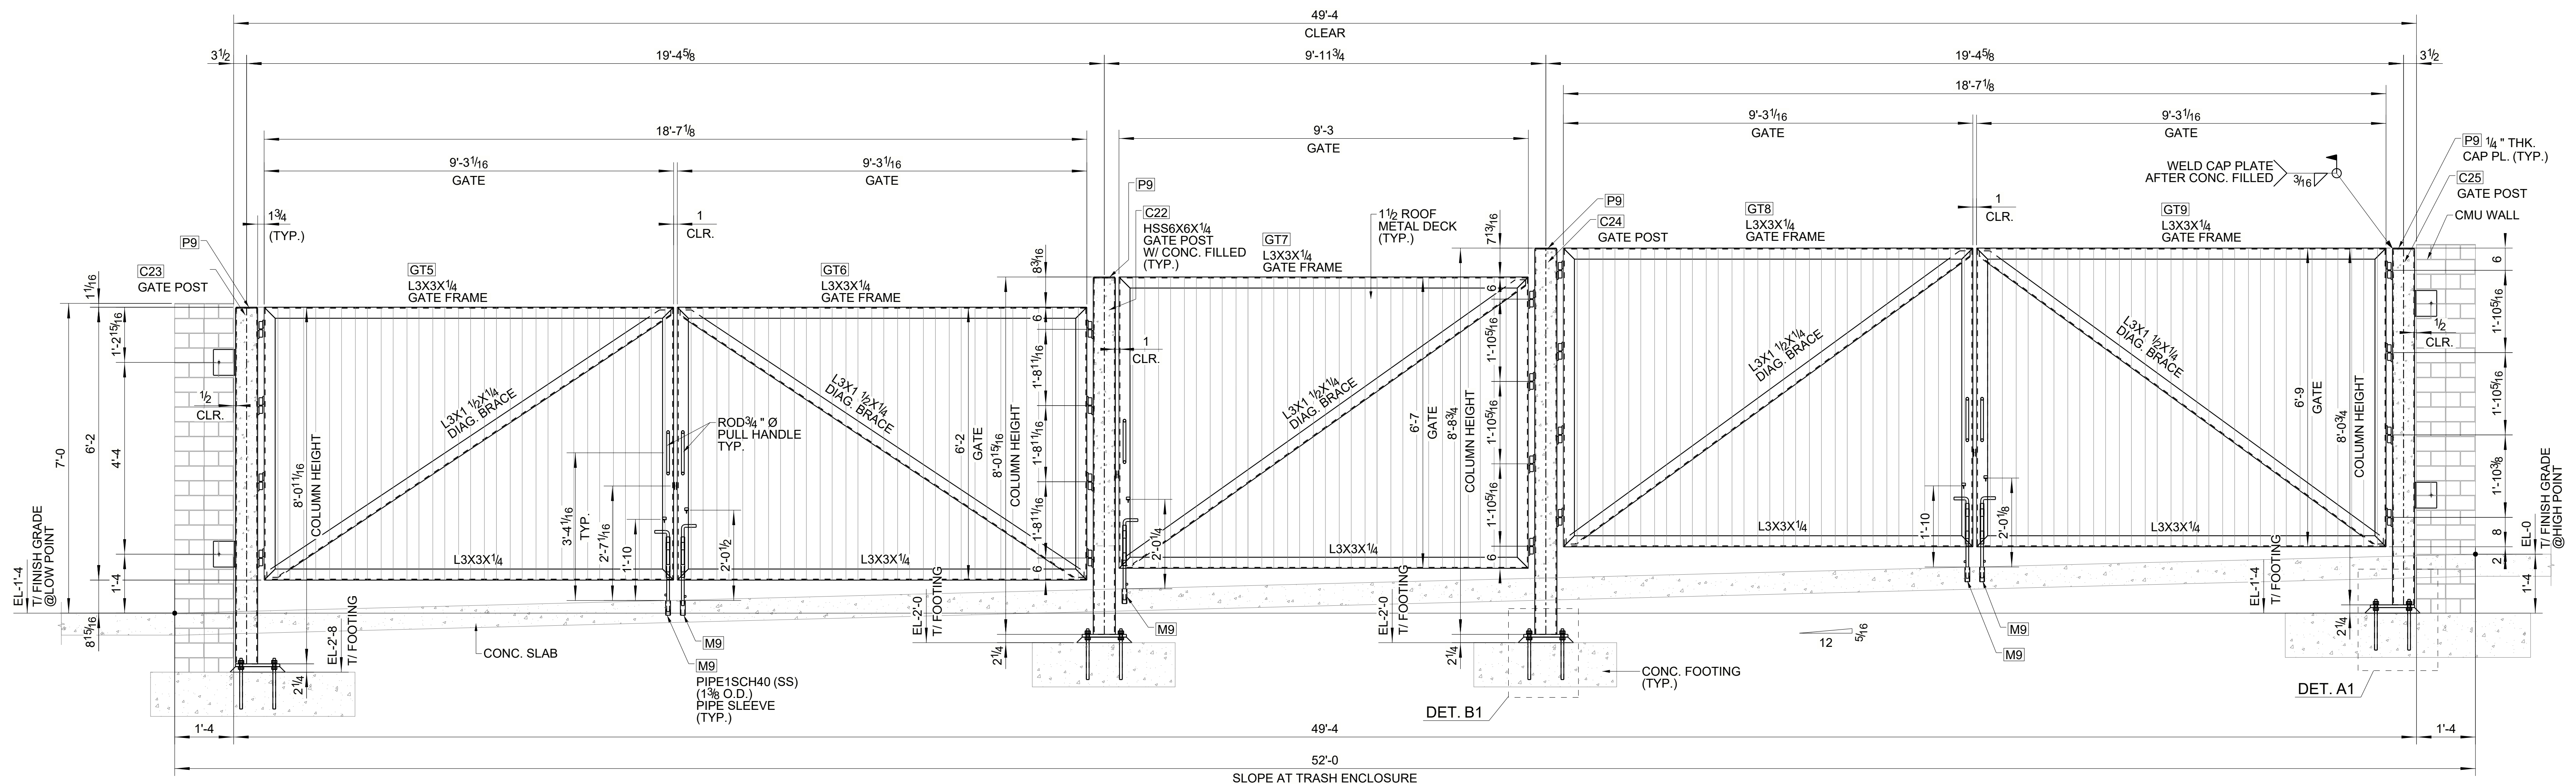

NOTES :

1. REFER SHEET E18 FOR GATE LOCATION PLAN.
2. REFER SHEET E20 FOR GATE TYPICAL SECTION.

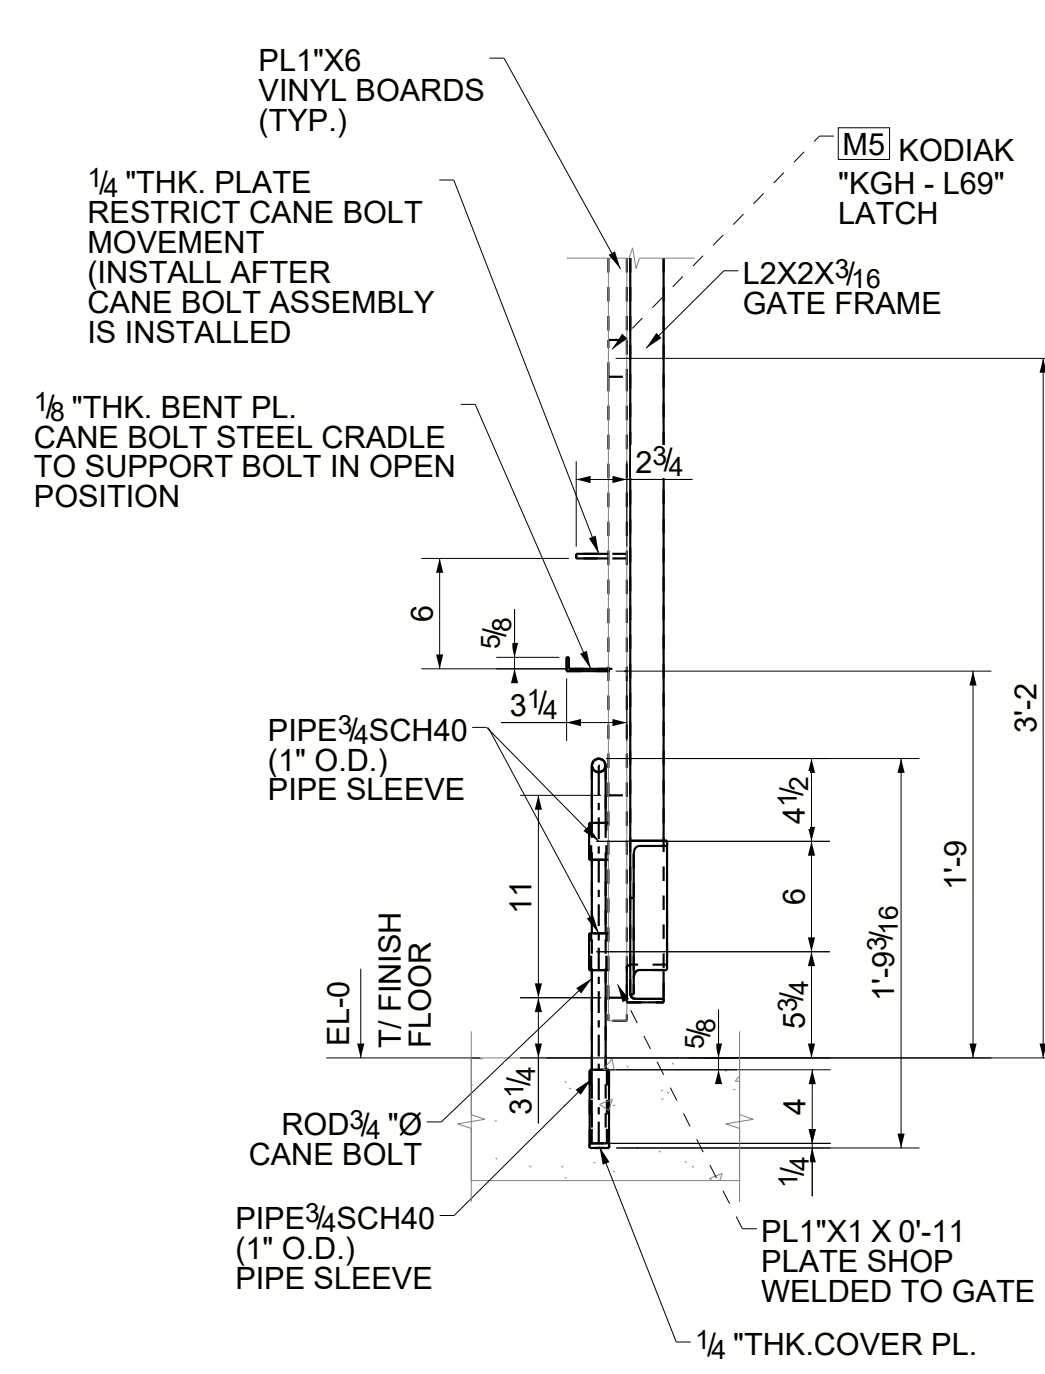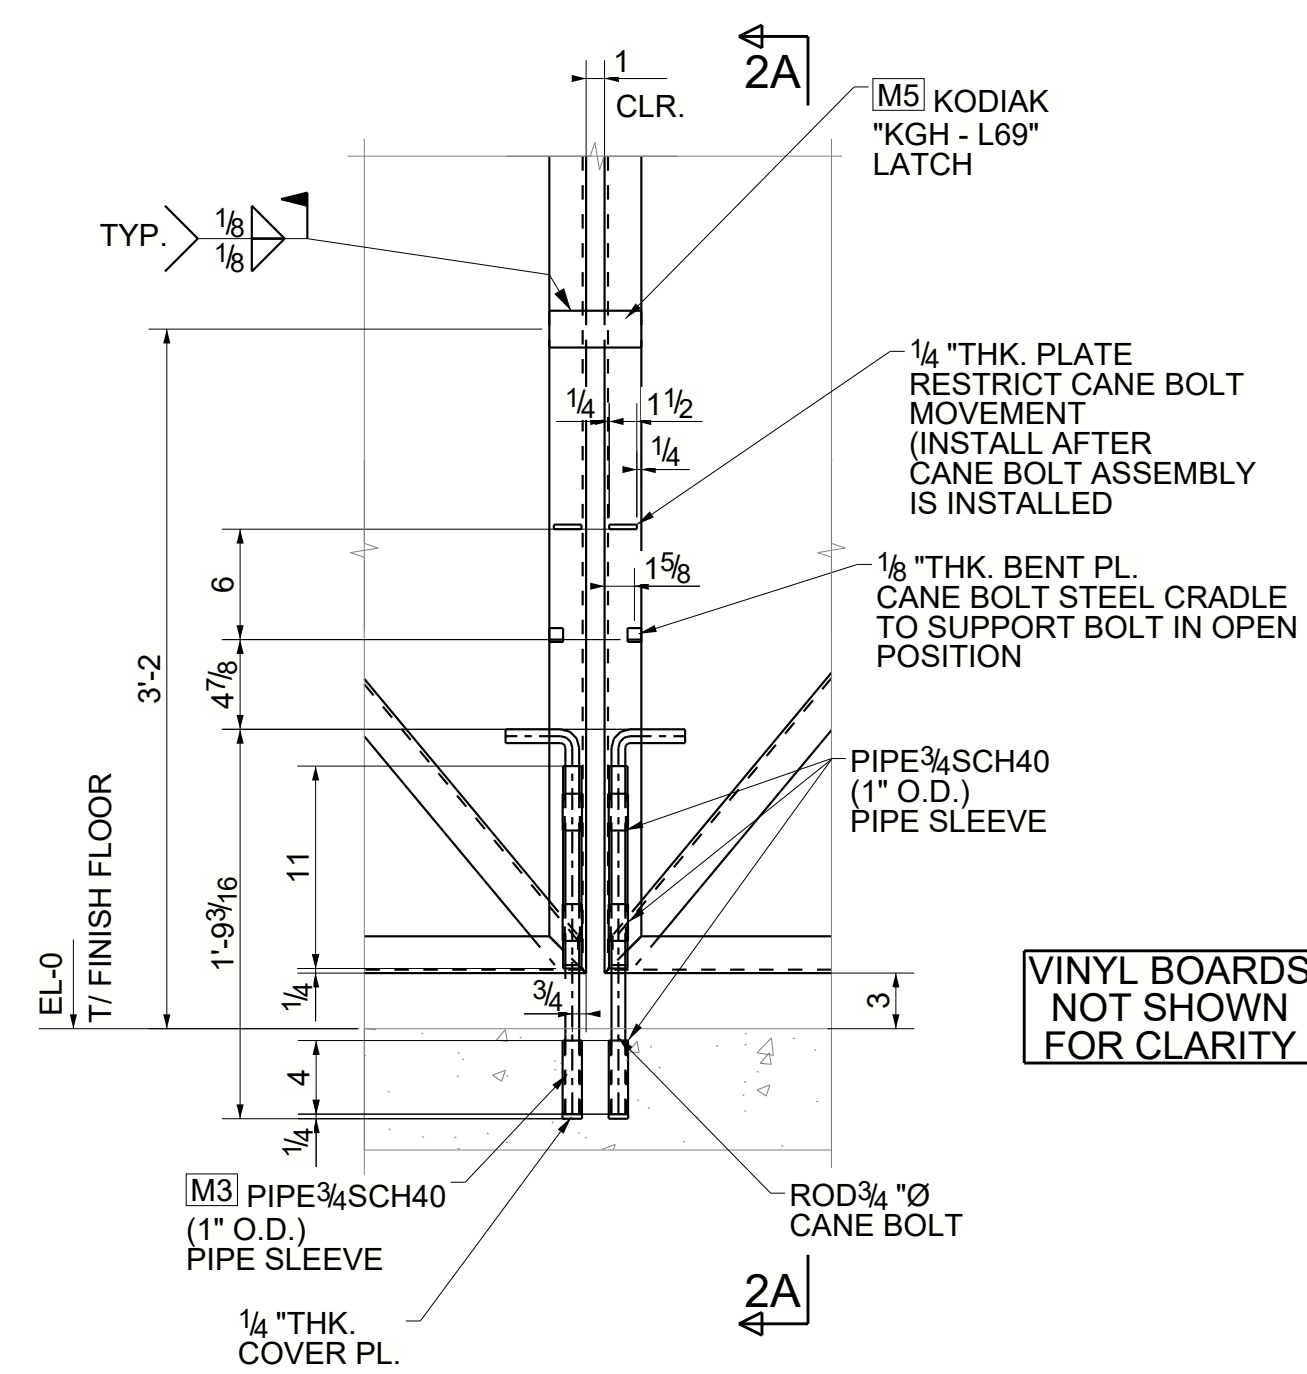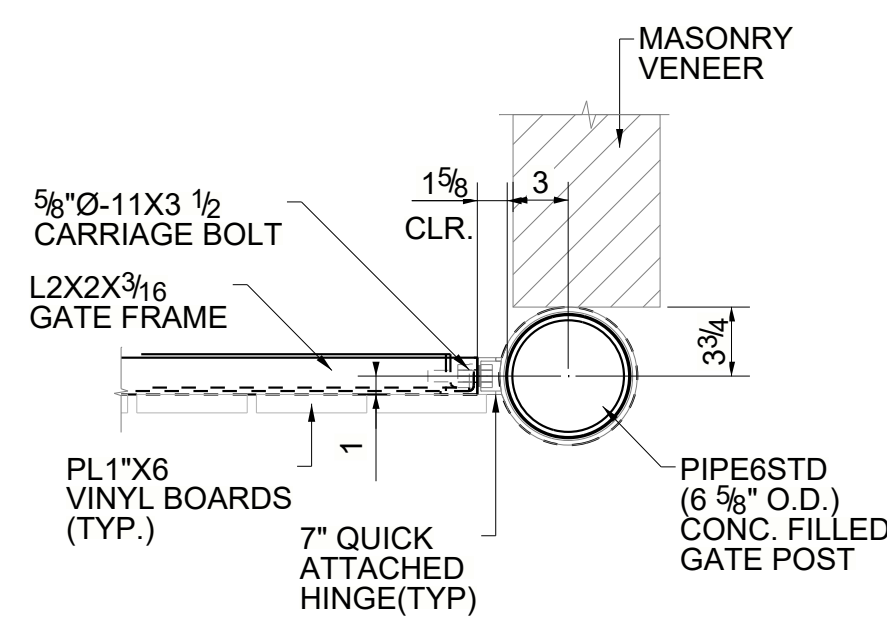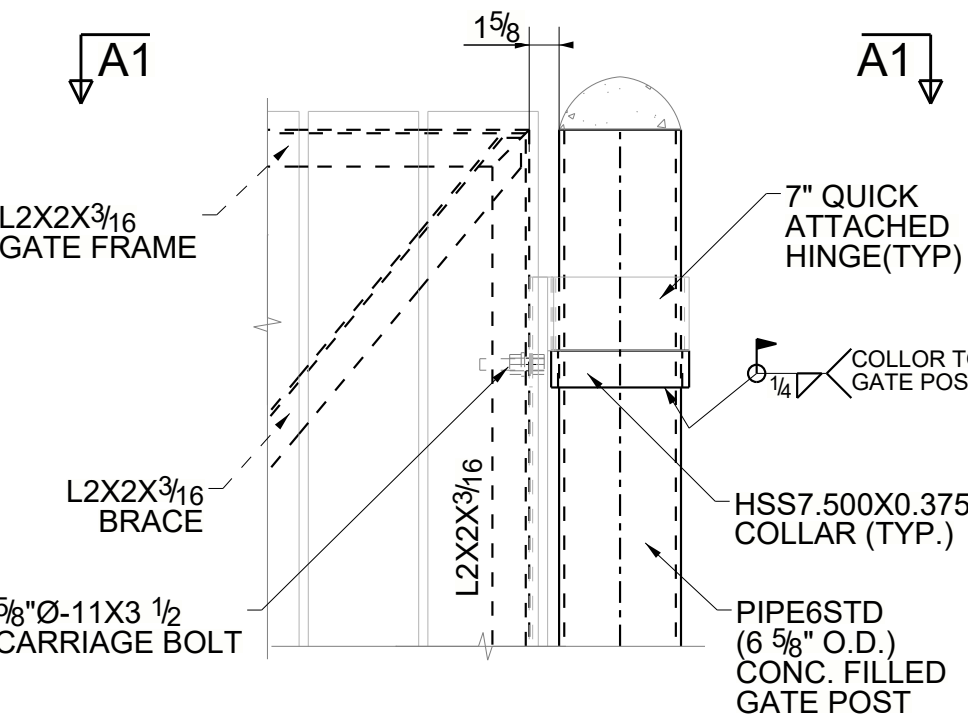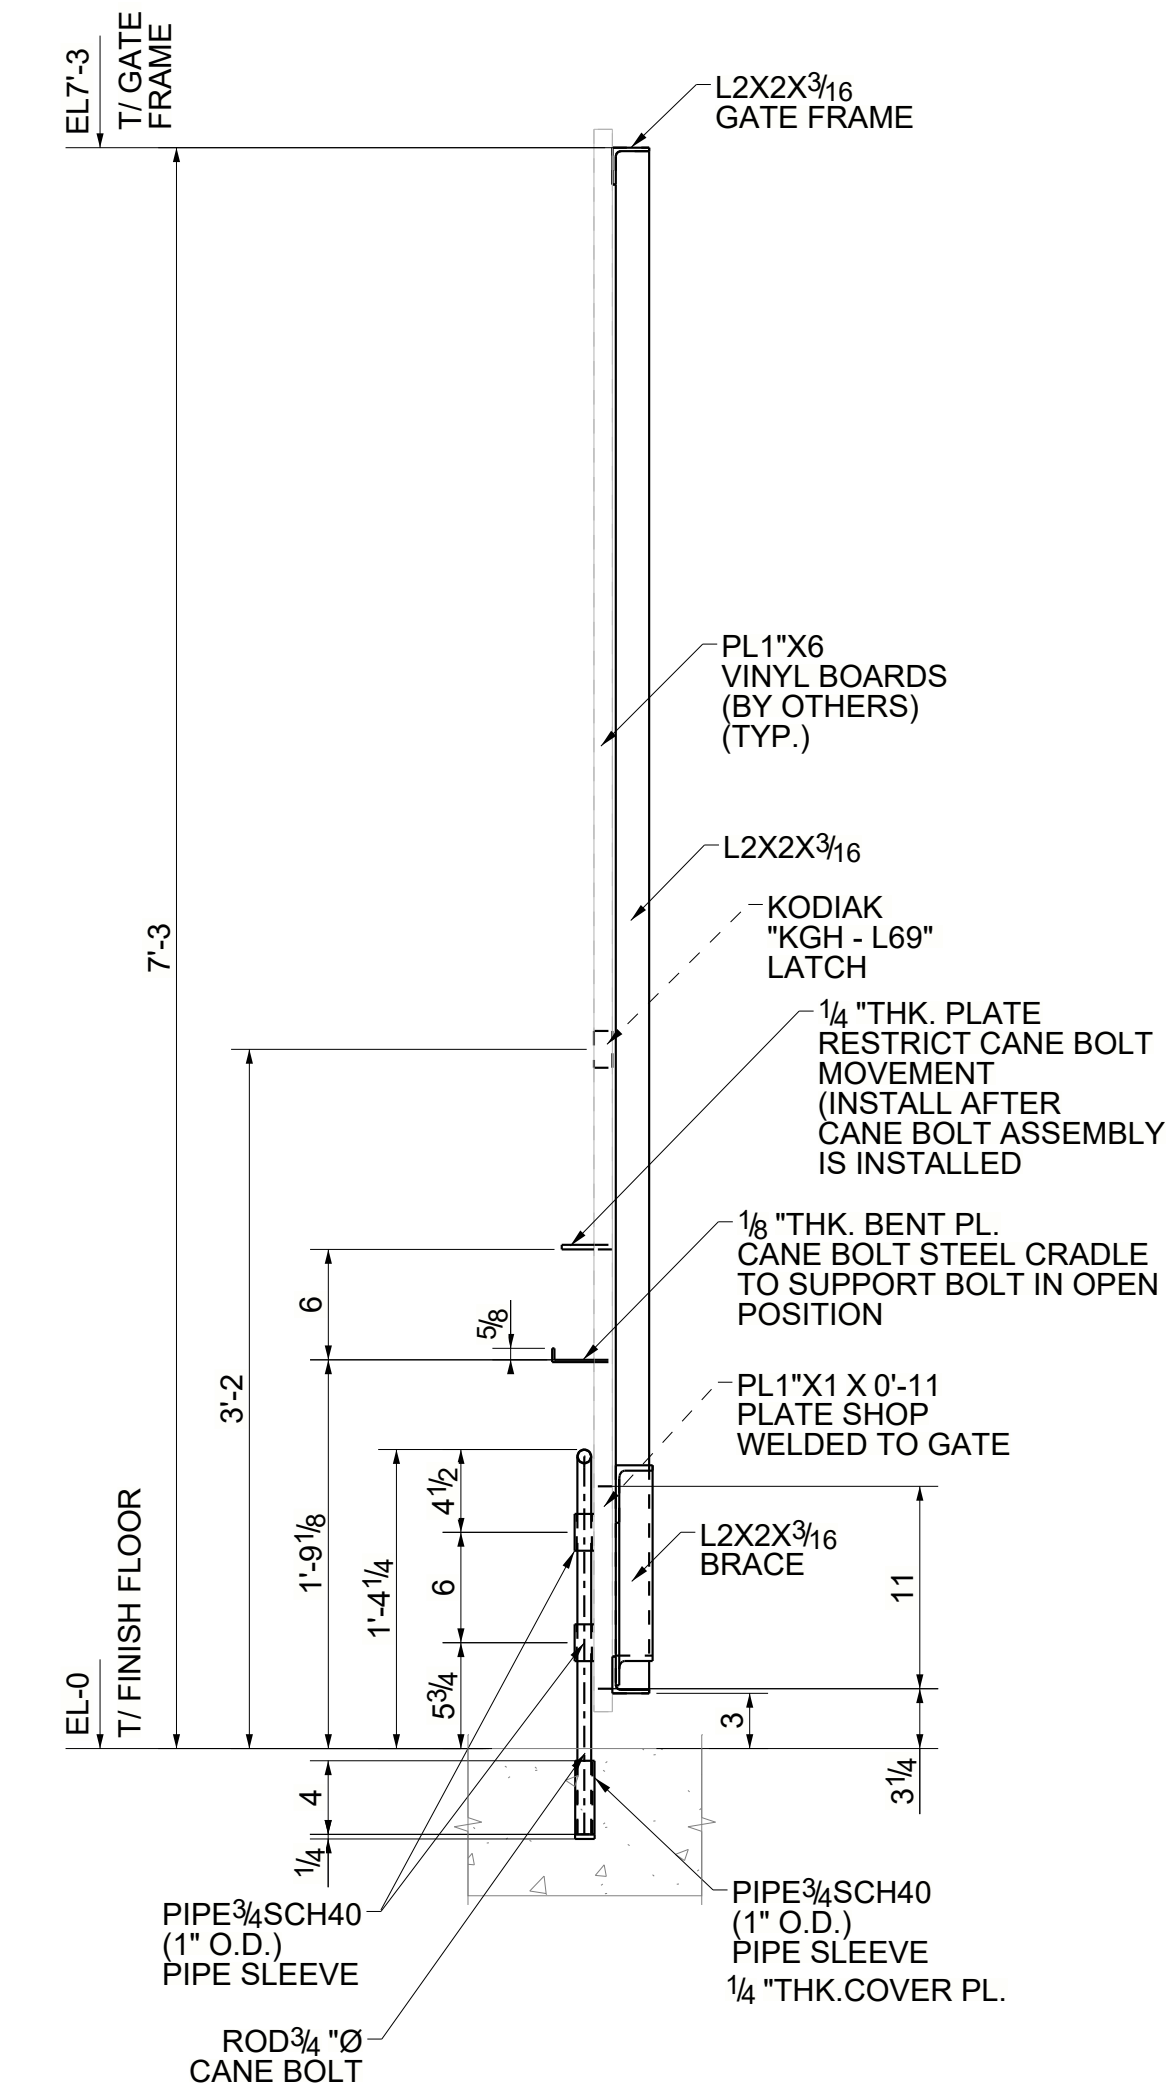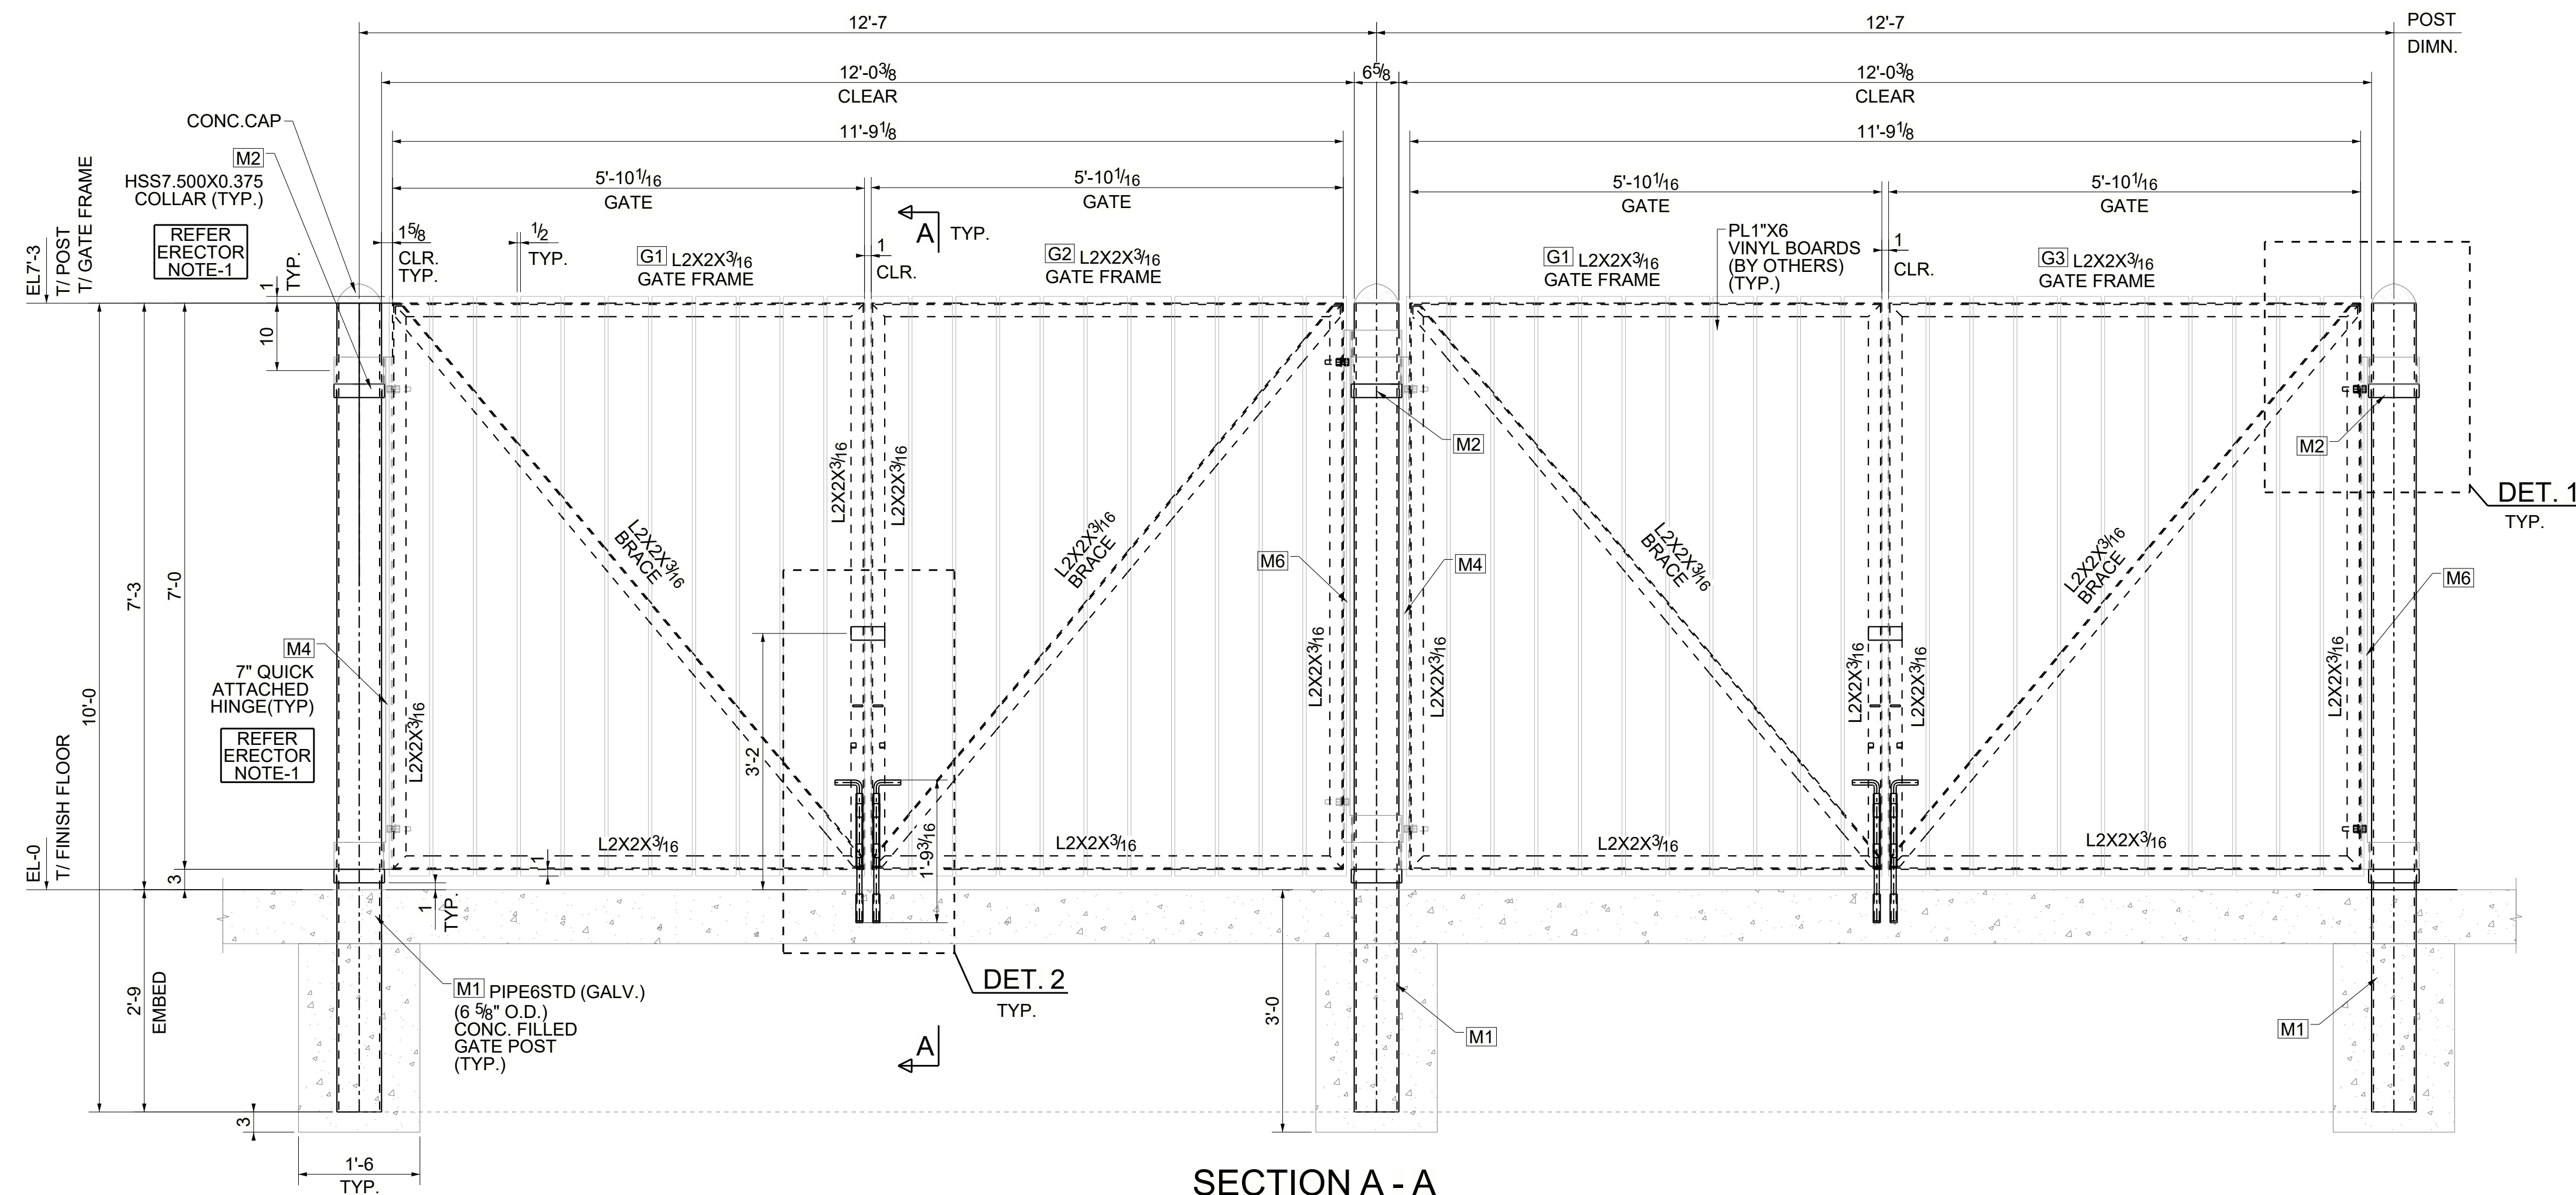


NOTES :



1. REFER SHEET E101 FOR 3D VIEW, GENERAL NOTES AND LOCATION PLAN.

ERECTOR NOTE-1 :


PLEASE INSERT HINGE BEFORE FIELD WELDING COLLARS IN POSITION.

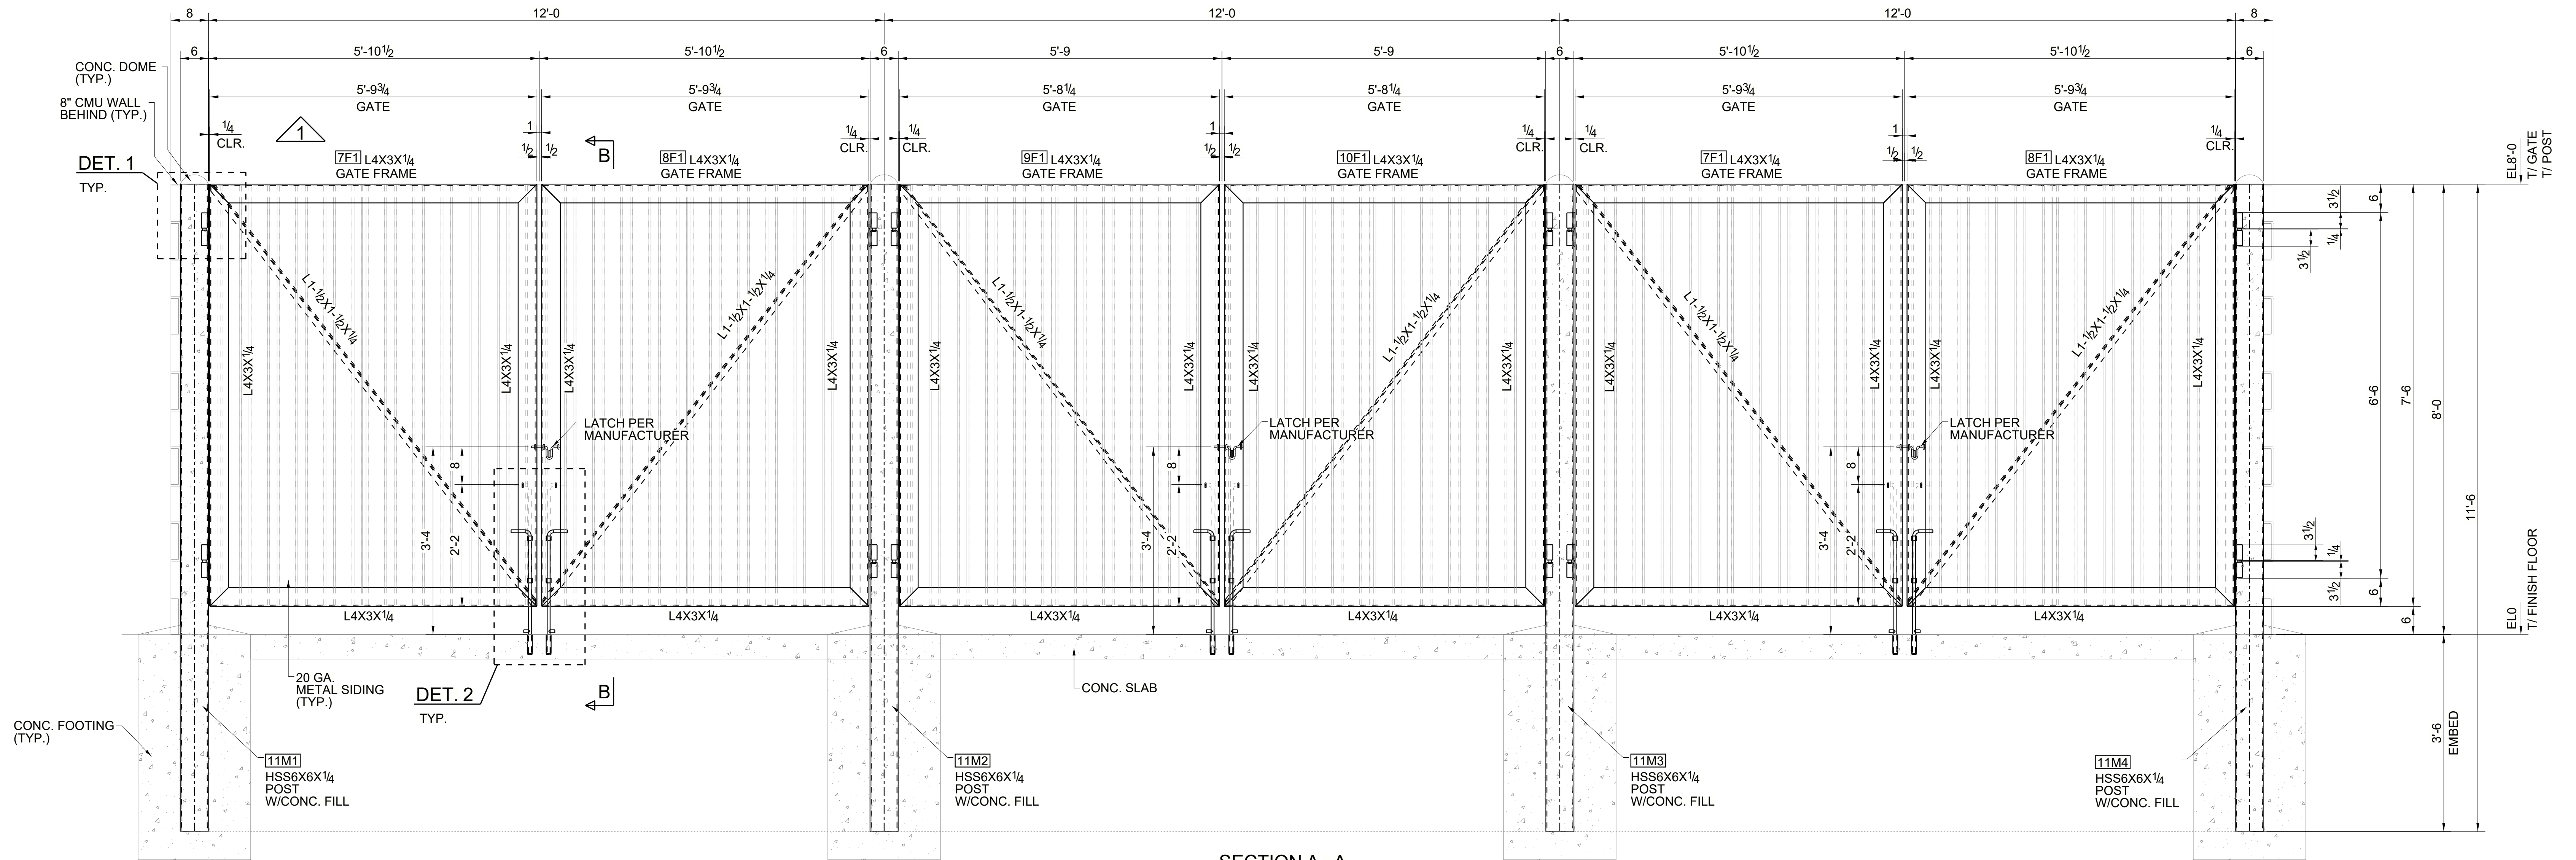

SECTION A - A
E6
(REFER: TRASH ENCLOSURE - FRONT ELEVATION - 15/ SP2.1)

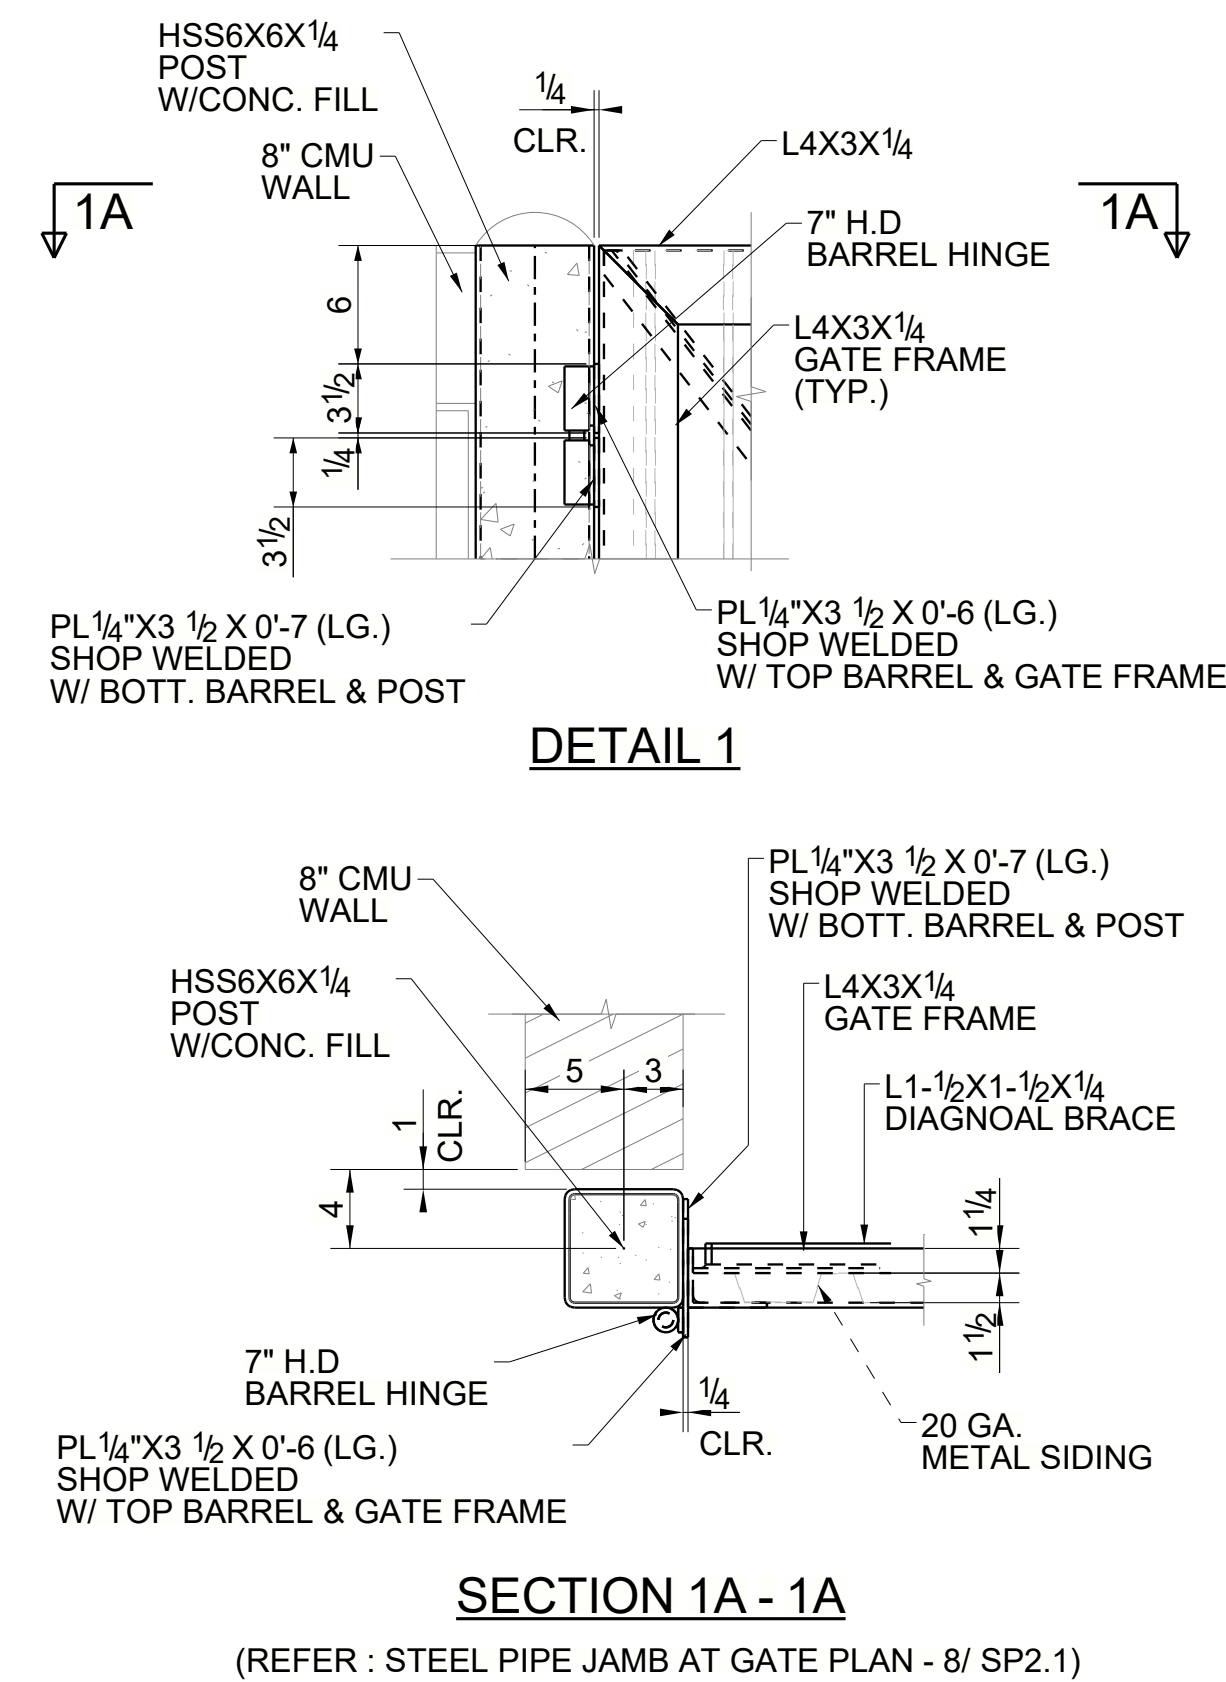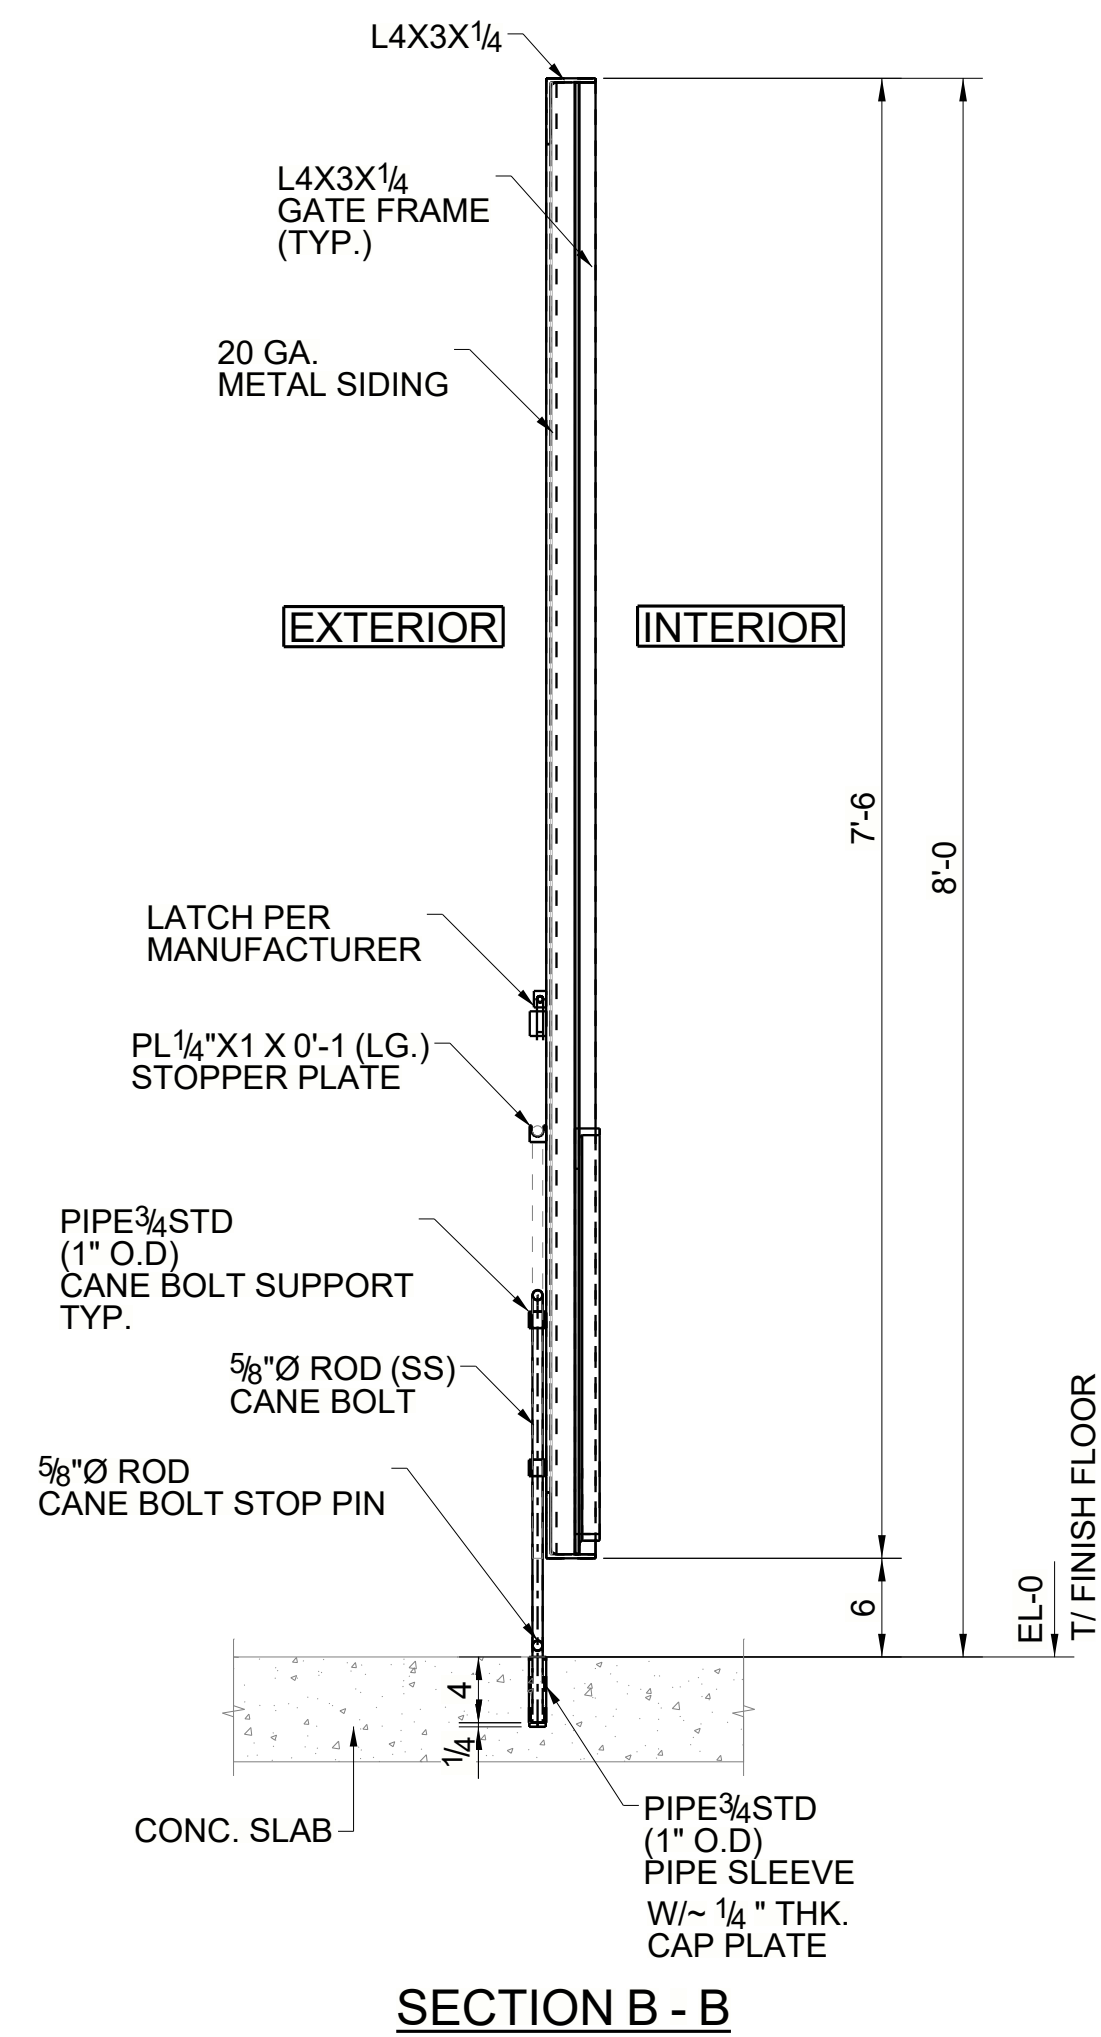


SECTION 1A - 1A
(REFER : STEEL PIPE JAMB AT GATE PLAN - 8/ SP2.1)

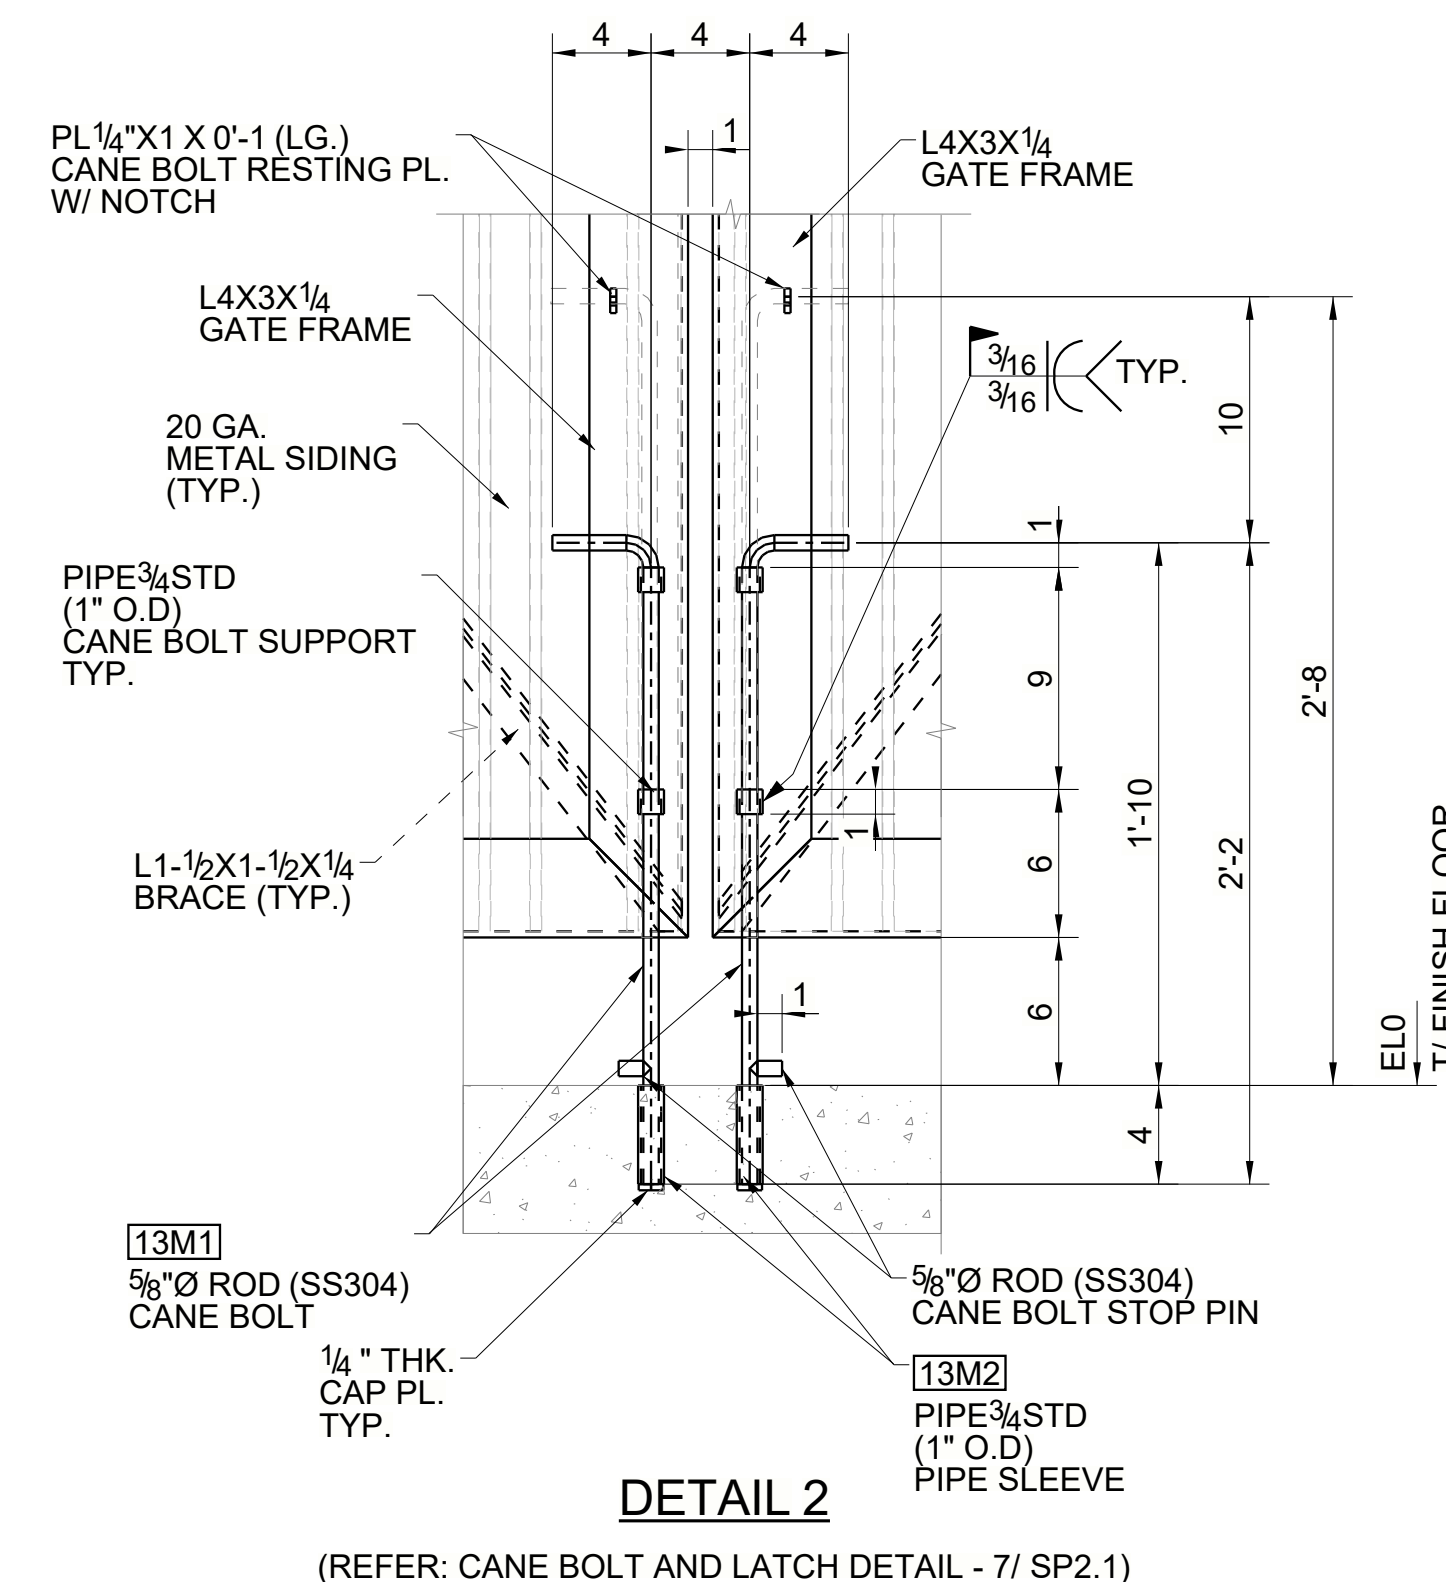

DETAIL 2
(REFER: CANE BOLT AND LATCH DETAIL - 7/ SP2.1)

NOTES:-

1. REFER SHEET E5 FOR GATE 3D-VIEW.
2. REFER SHEET E6 FOR GATE LOCATION PLAN.

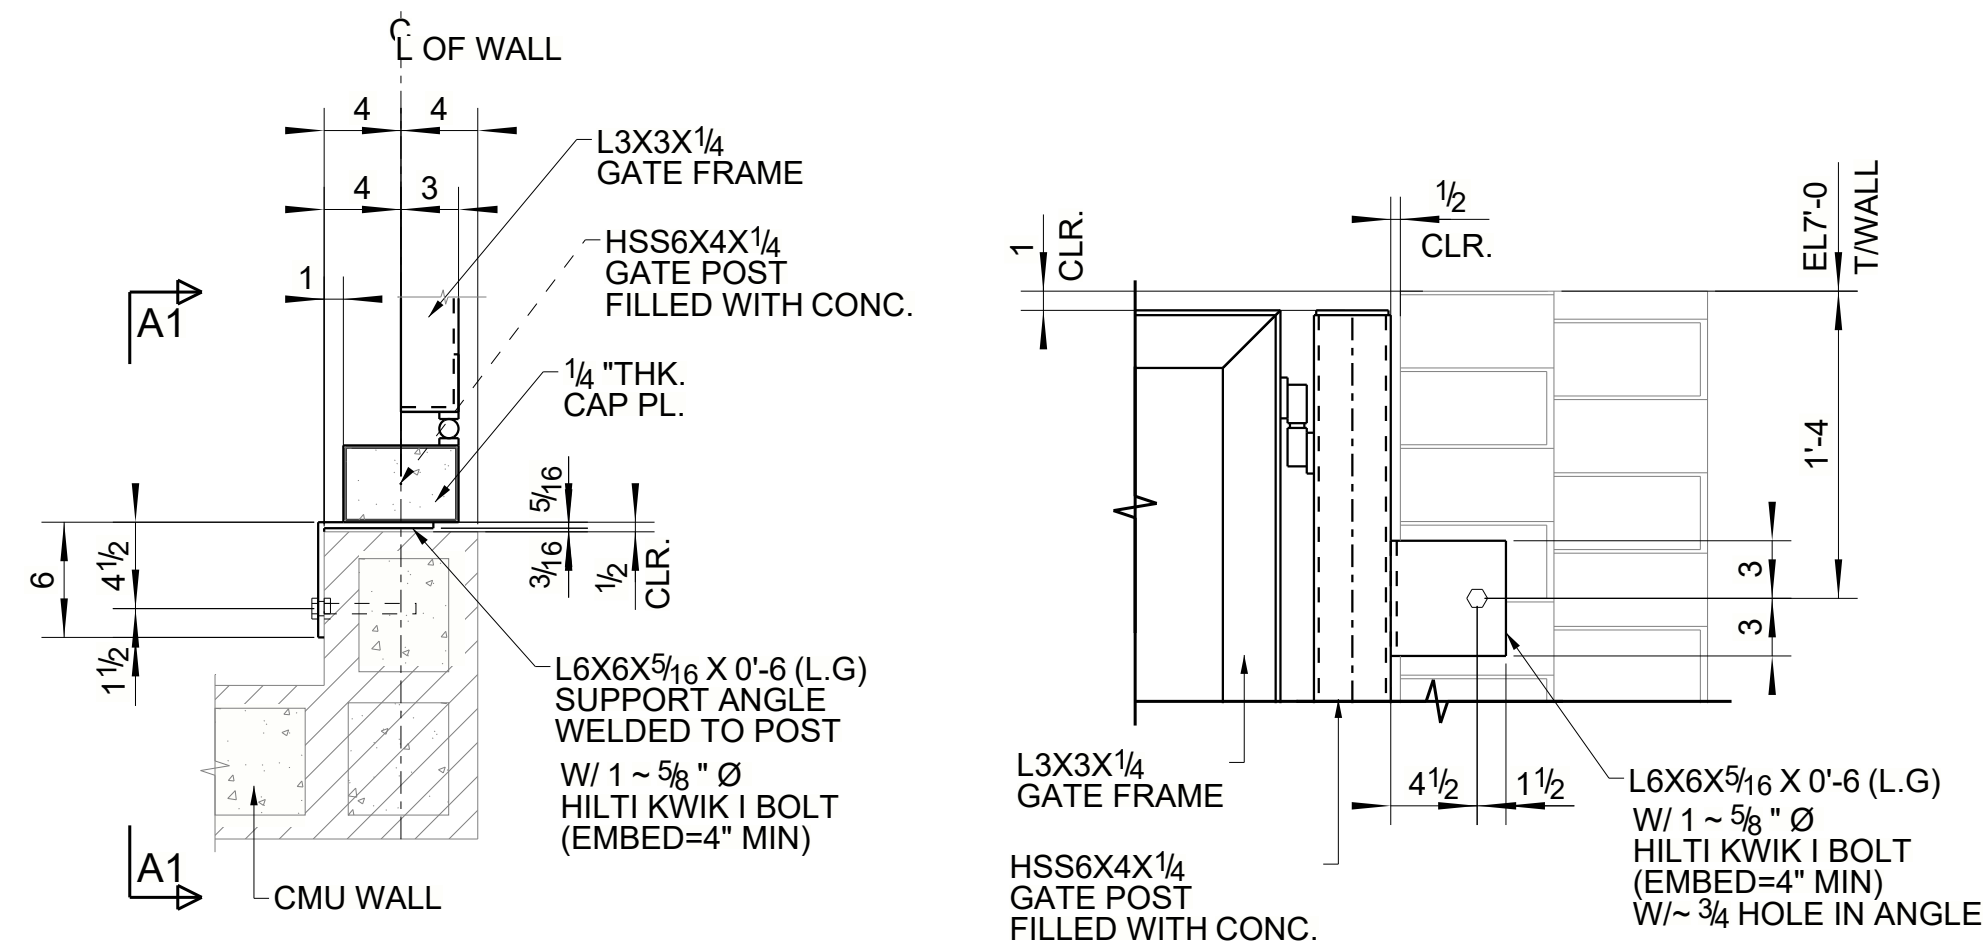


DETAIL A
E11

(REFER: GATE POST TO CMU CONNECTION
DETAIL -13/A102)


SECTION A1 - A1

(REFER: TRASH ENCLOSURE ENLARGED ELEVATION -11/A102)

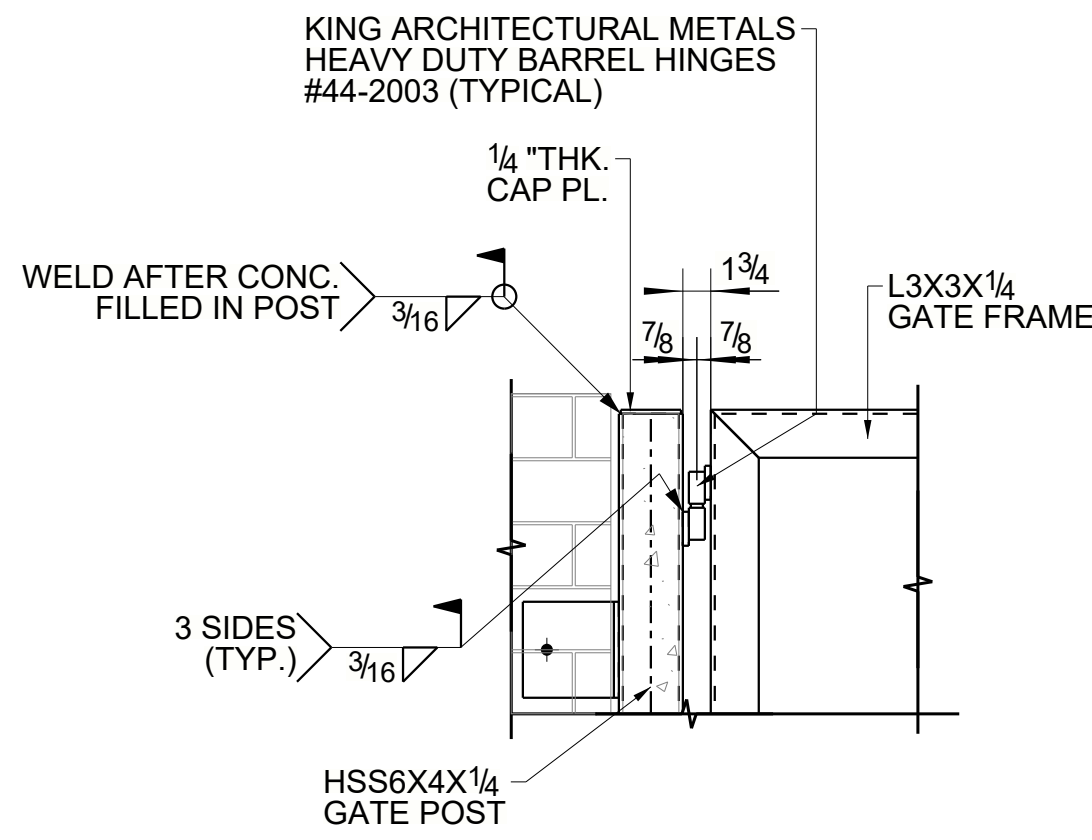

DETAIL C
E12

(REFER: TRASH ENCLOSURE ENLARGED ELEVATION -11/A102)

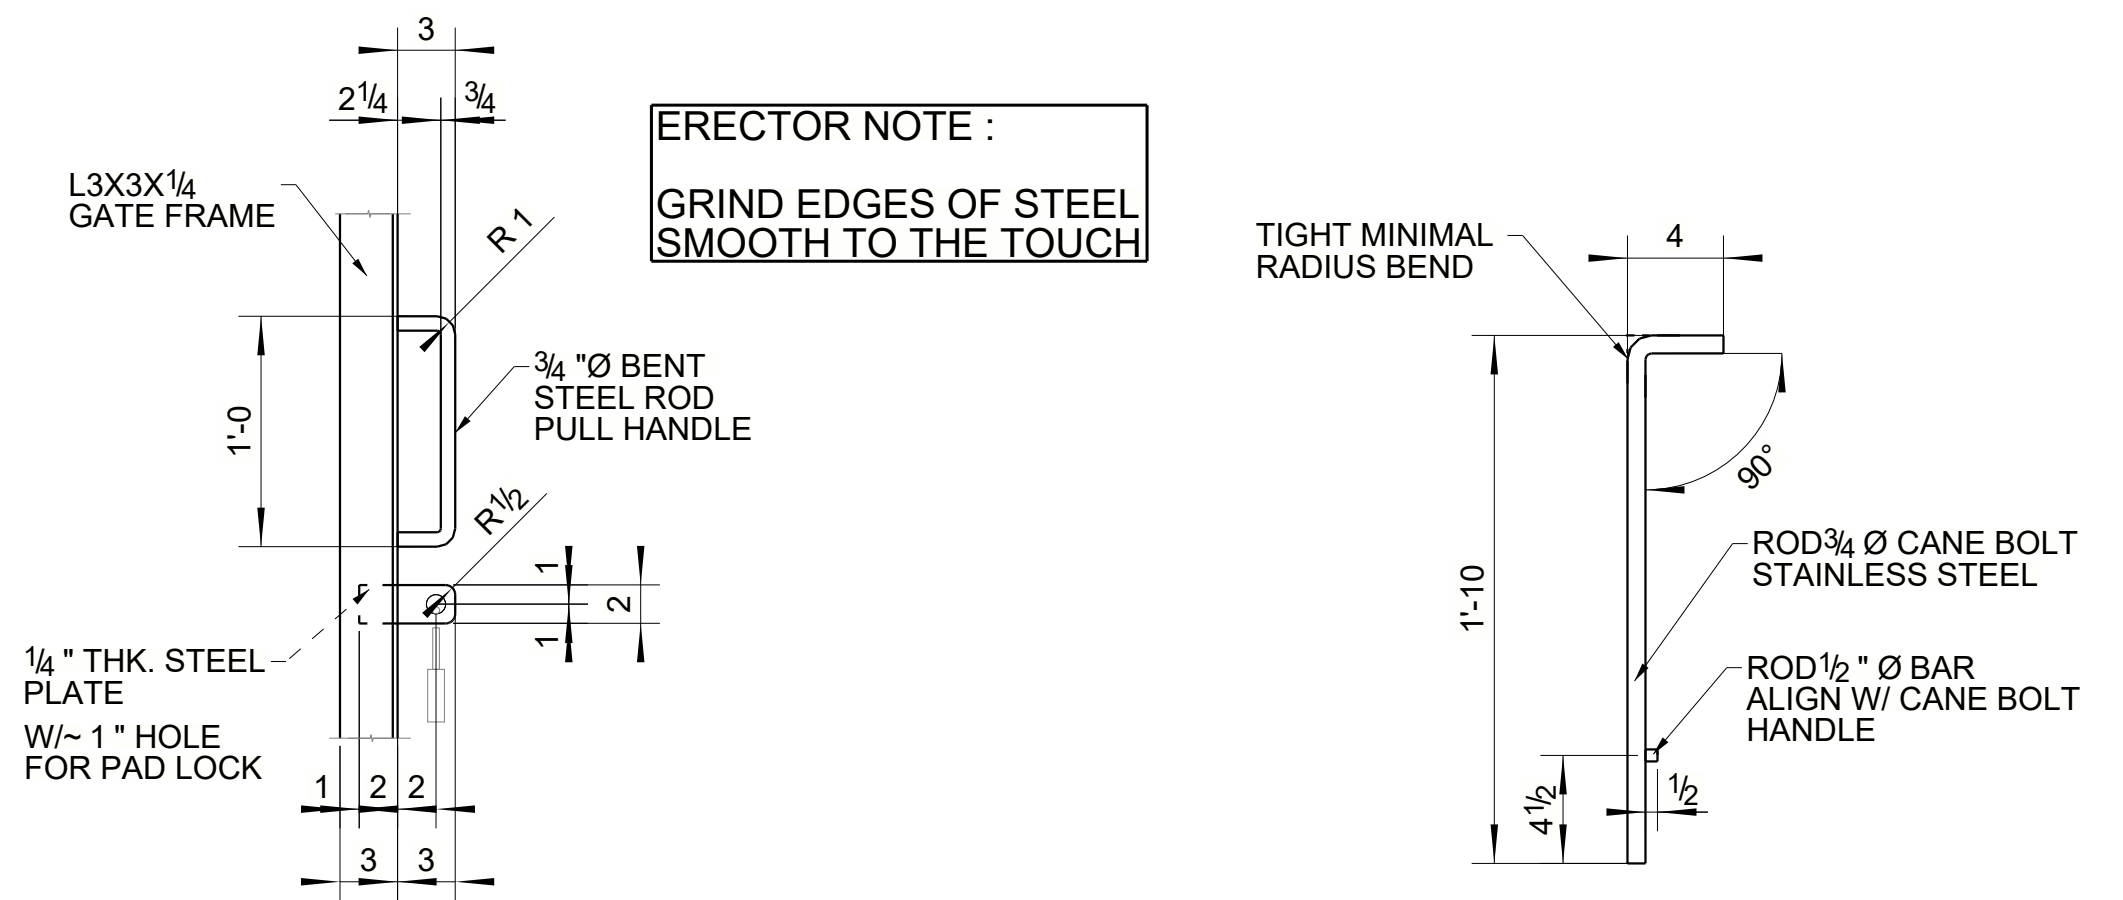


TYPICAL HANDLE AND PAD LOCK DETAIL

(REFER : HANDLE DETAIL 9/A103 & PSDLOCK 10/A103)


TYPICAL CANE BOLT DETAIL

(REFER : TYPICAL CANE BOLT 13/A103)

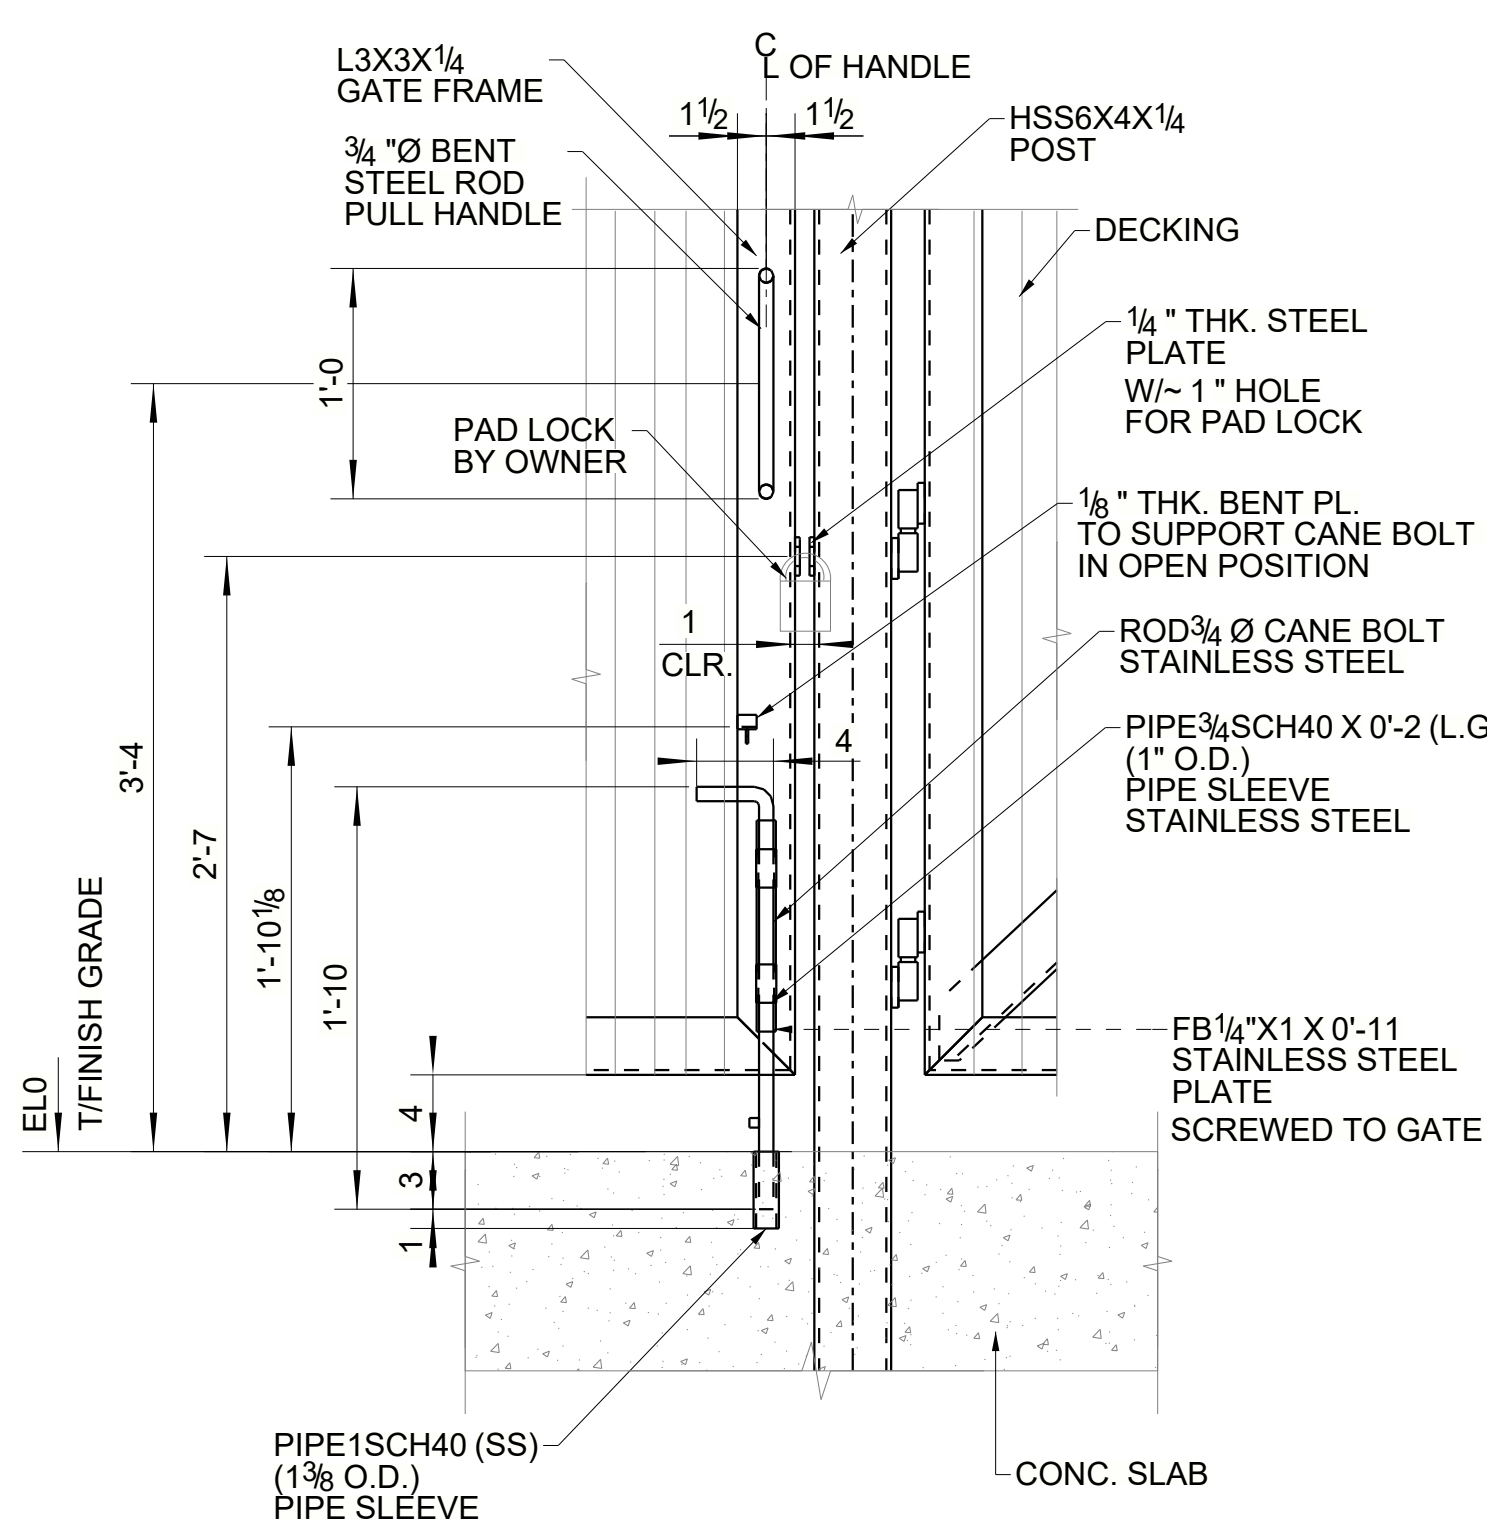


TYPICAL SINGLE GATE LOCK DETAIL

(REFER : SINGLE GATE LOCK DETAIL 08/A103)

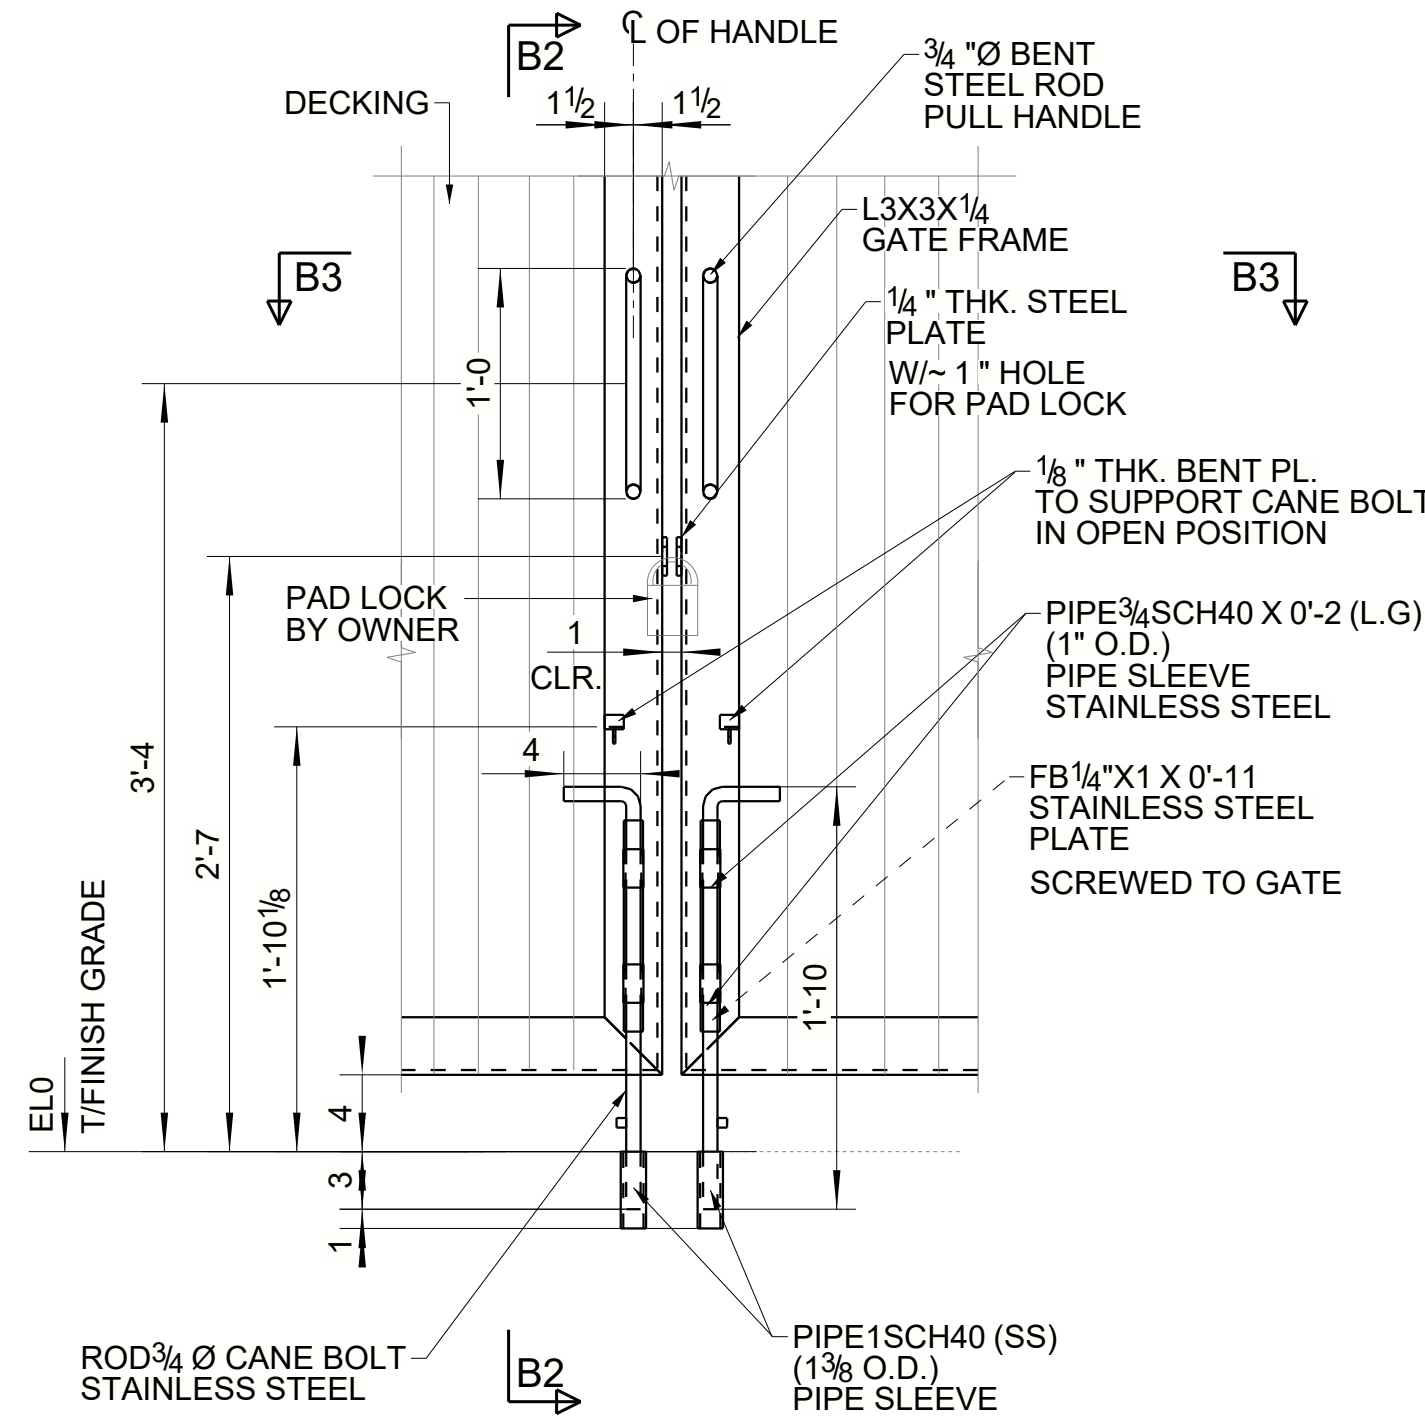


TYPICAL DOUBLE GATE LOCK DETAIL

(REFER : DOUBLE GATE LOCK DETAIL 07/A103)

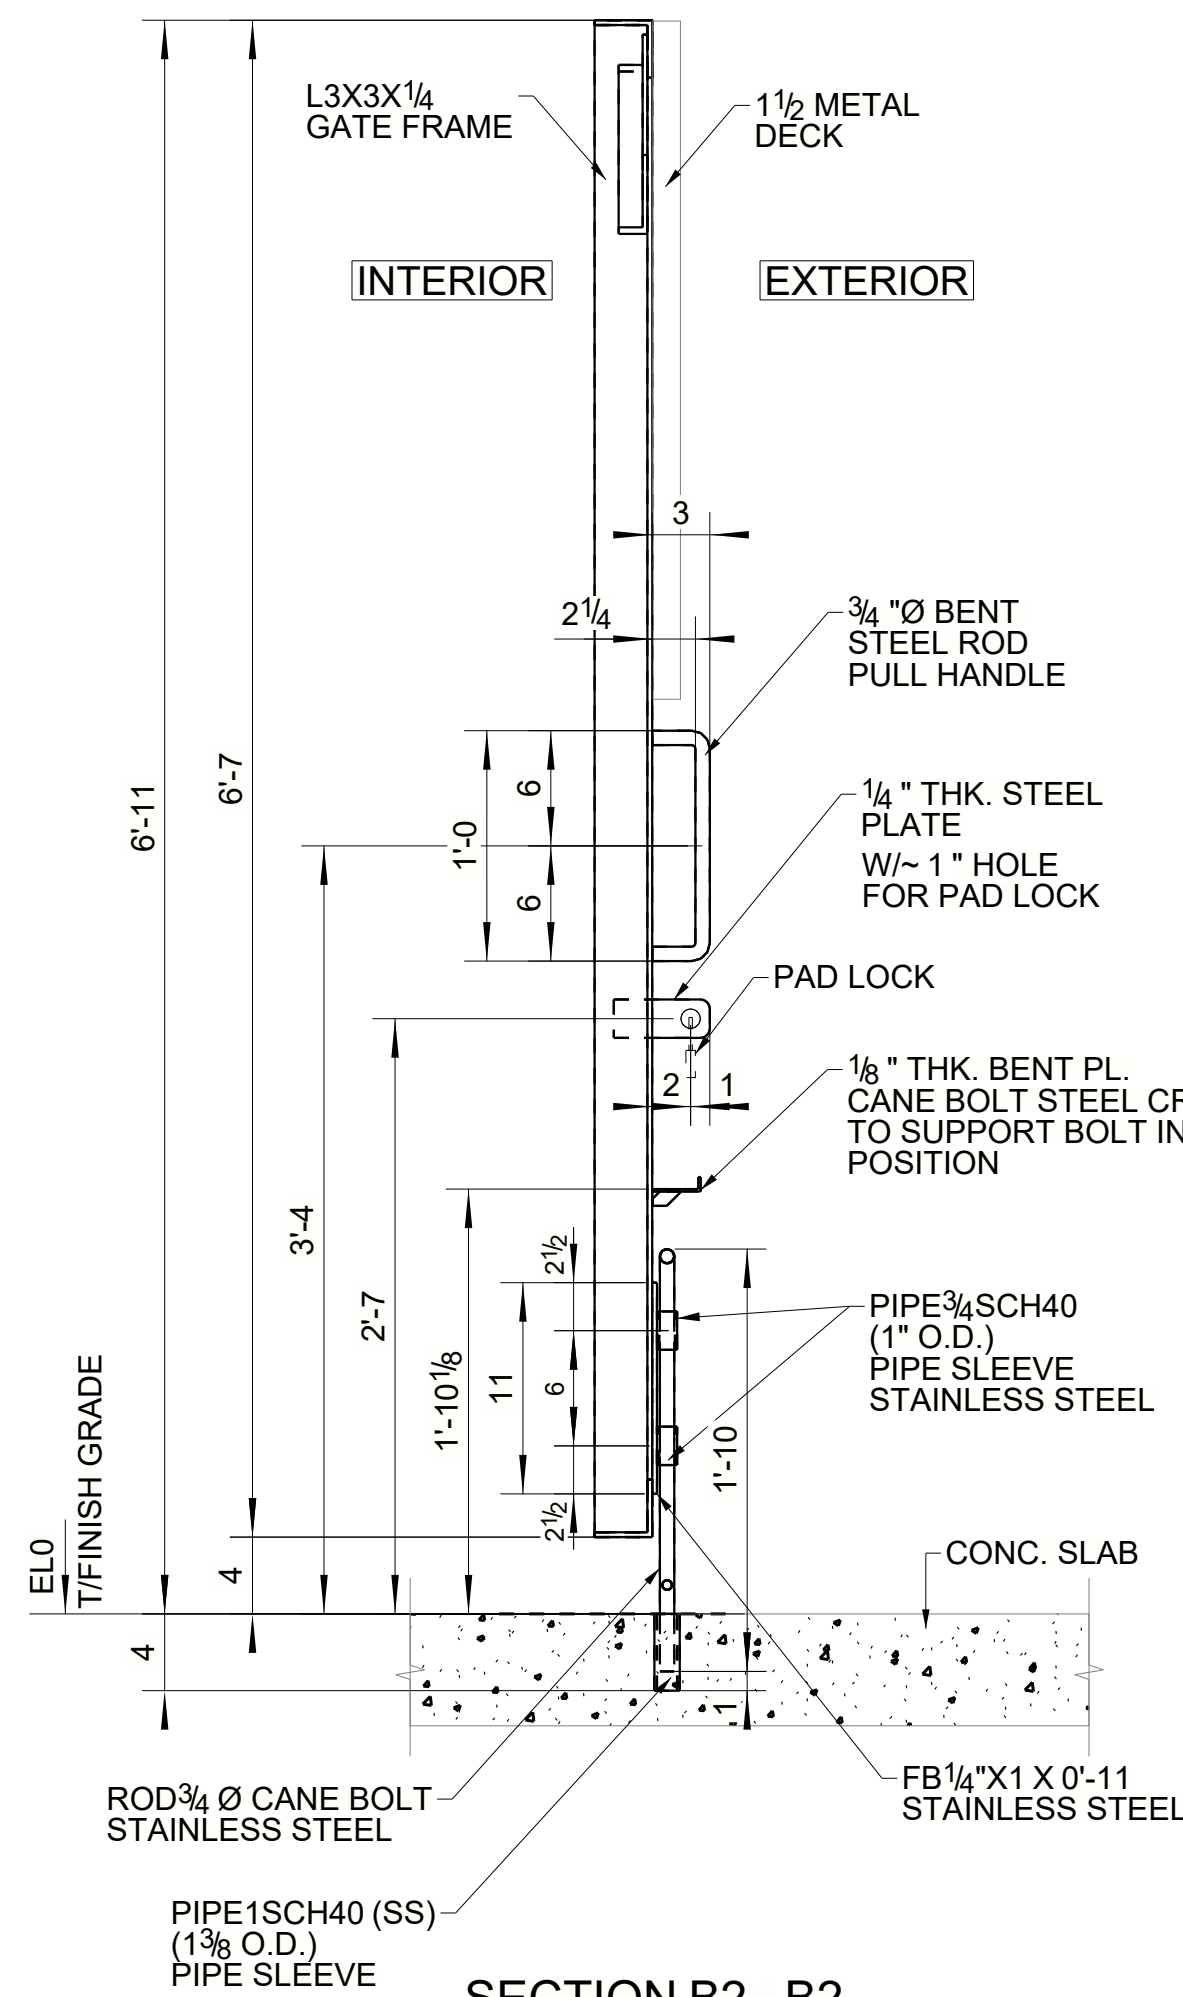


SECTION B2 - B2

(REFER : GATE SECTION - 4/A103)

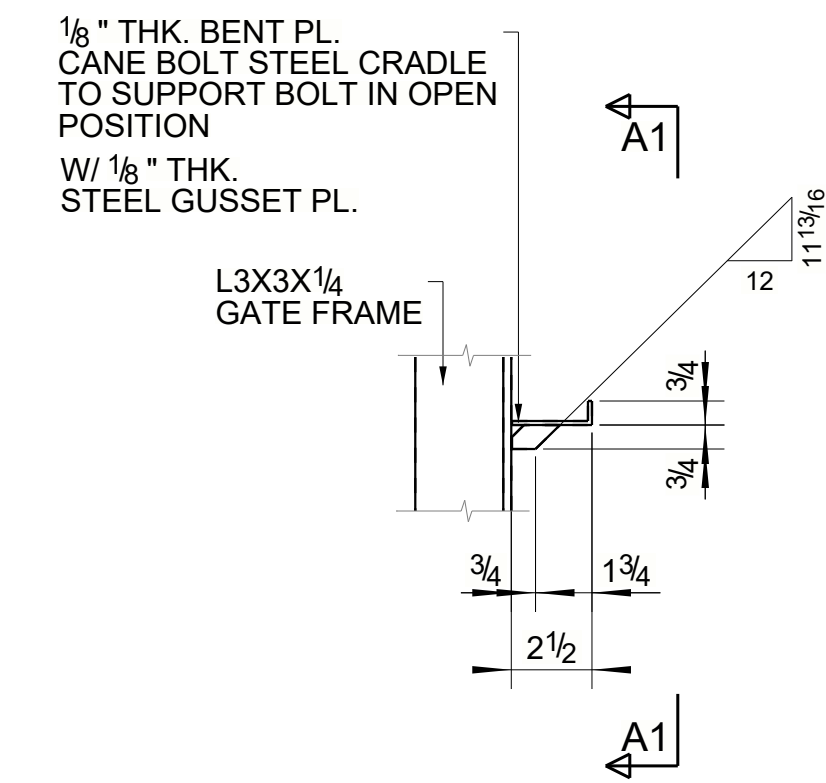


TYPICAL CANE BOLT HOLD OPEN SUPPORT TAB

(REFER : TYPICAL CANE BOLT HOLD OPEN SUPPORT TAB 11/A103)

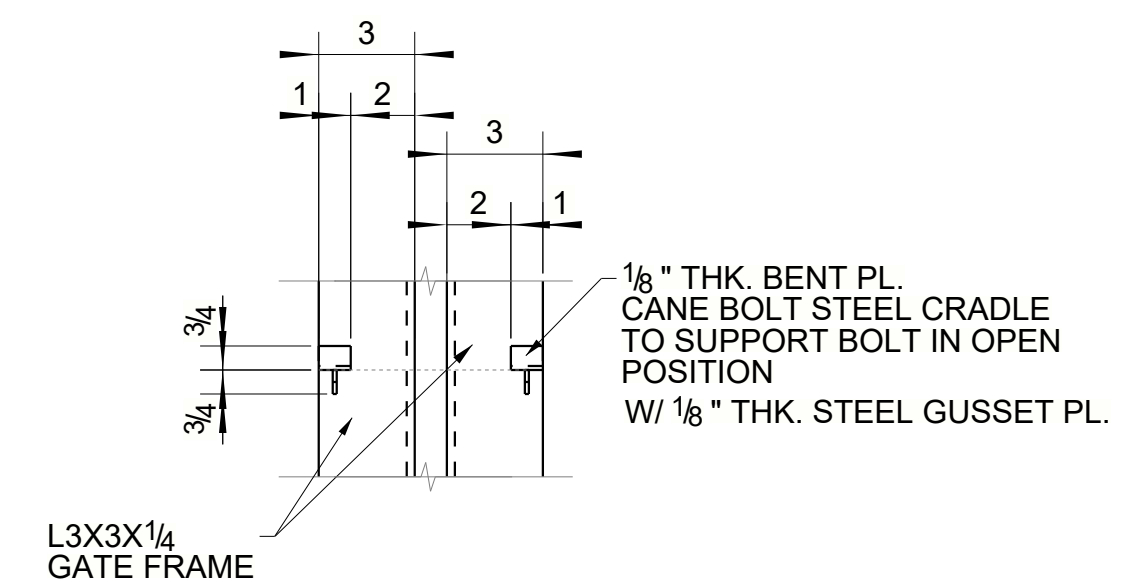


SECTION A1 - A1

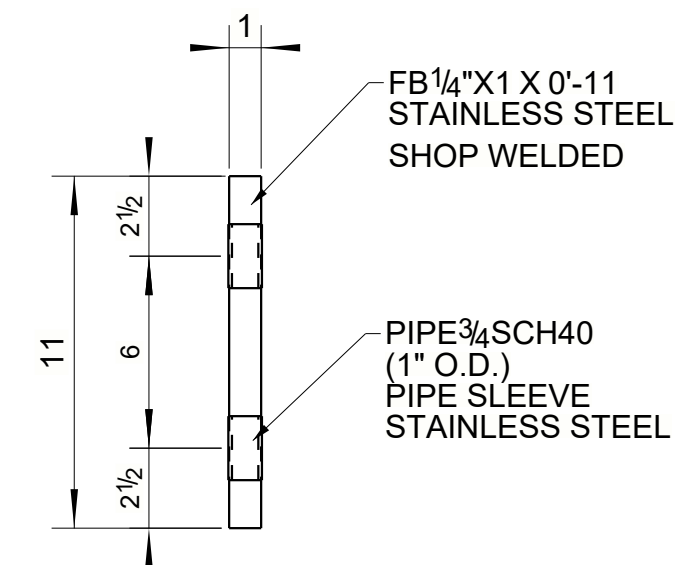

TYPICAL CANE BOLT GUIDE DETAIL

(REFER : TYPICAL CANE BOLT GUIDE DETAIL : 12/A103)

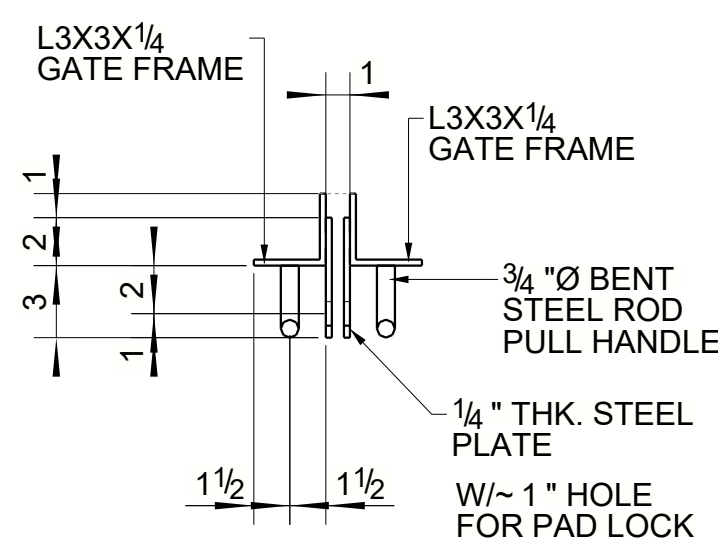

SECTION B3 - B3

(REFER: PADLOCK MOUNT DETAIL-10/A103)

NOTE :

PLEASE PROVIDE METAL DECK LOW FLUTE
TO RUN PARALLEL TO THE PULL HANDLE AND
CANE BOLT LOCATION.

NOTES :

1. REFER SHEET E11 & E18 FOR GATE LOCATION PLAN.
2. REFER SHEET E12 & E19 FOR GATE ELEVATIONS.