



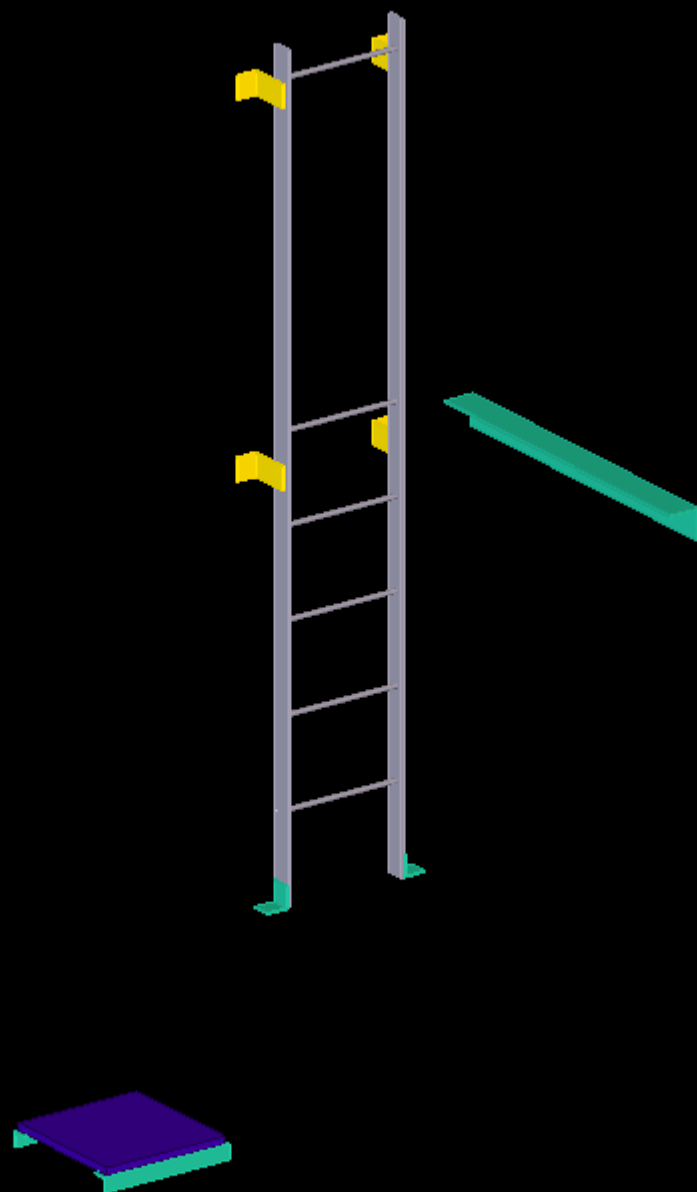

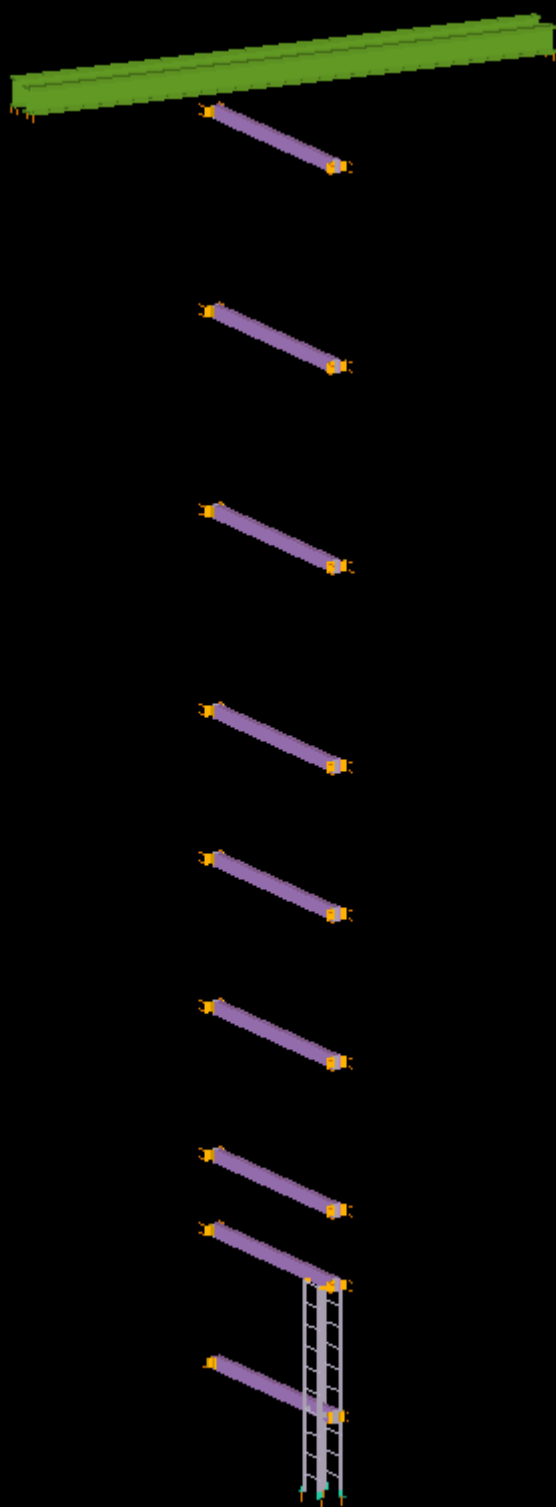





SECTION 1A - 1A

SECTION 1B - 1B


(REFER : TYPICAL RUNG ATTACHMENT DETAIL /A644-S3000004)

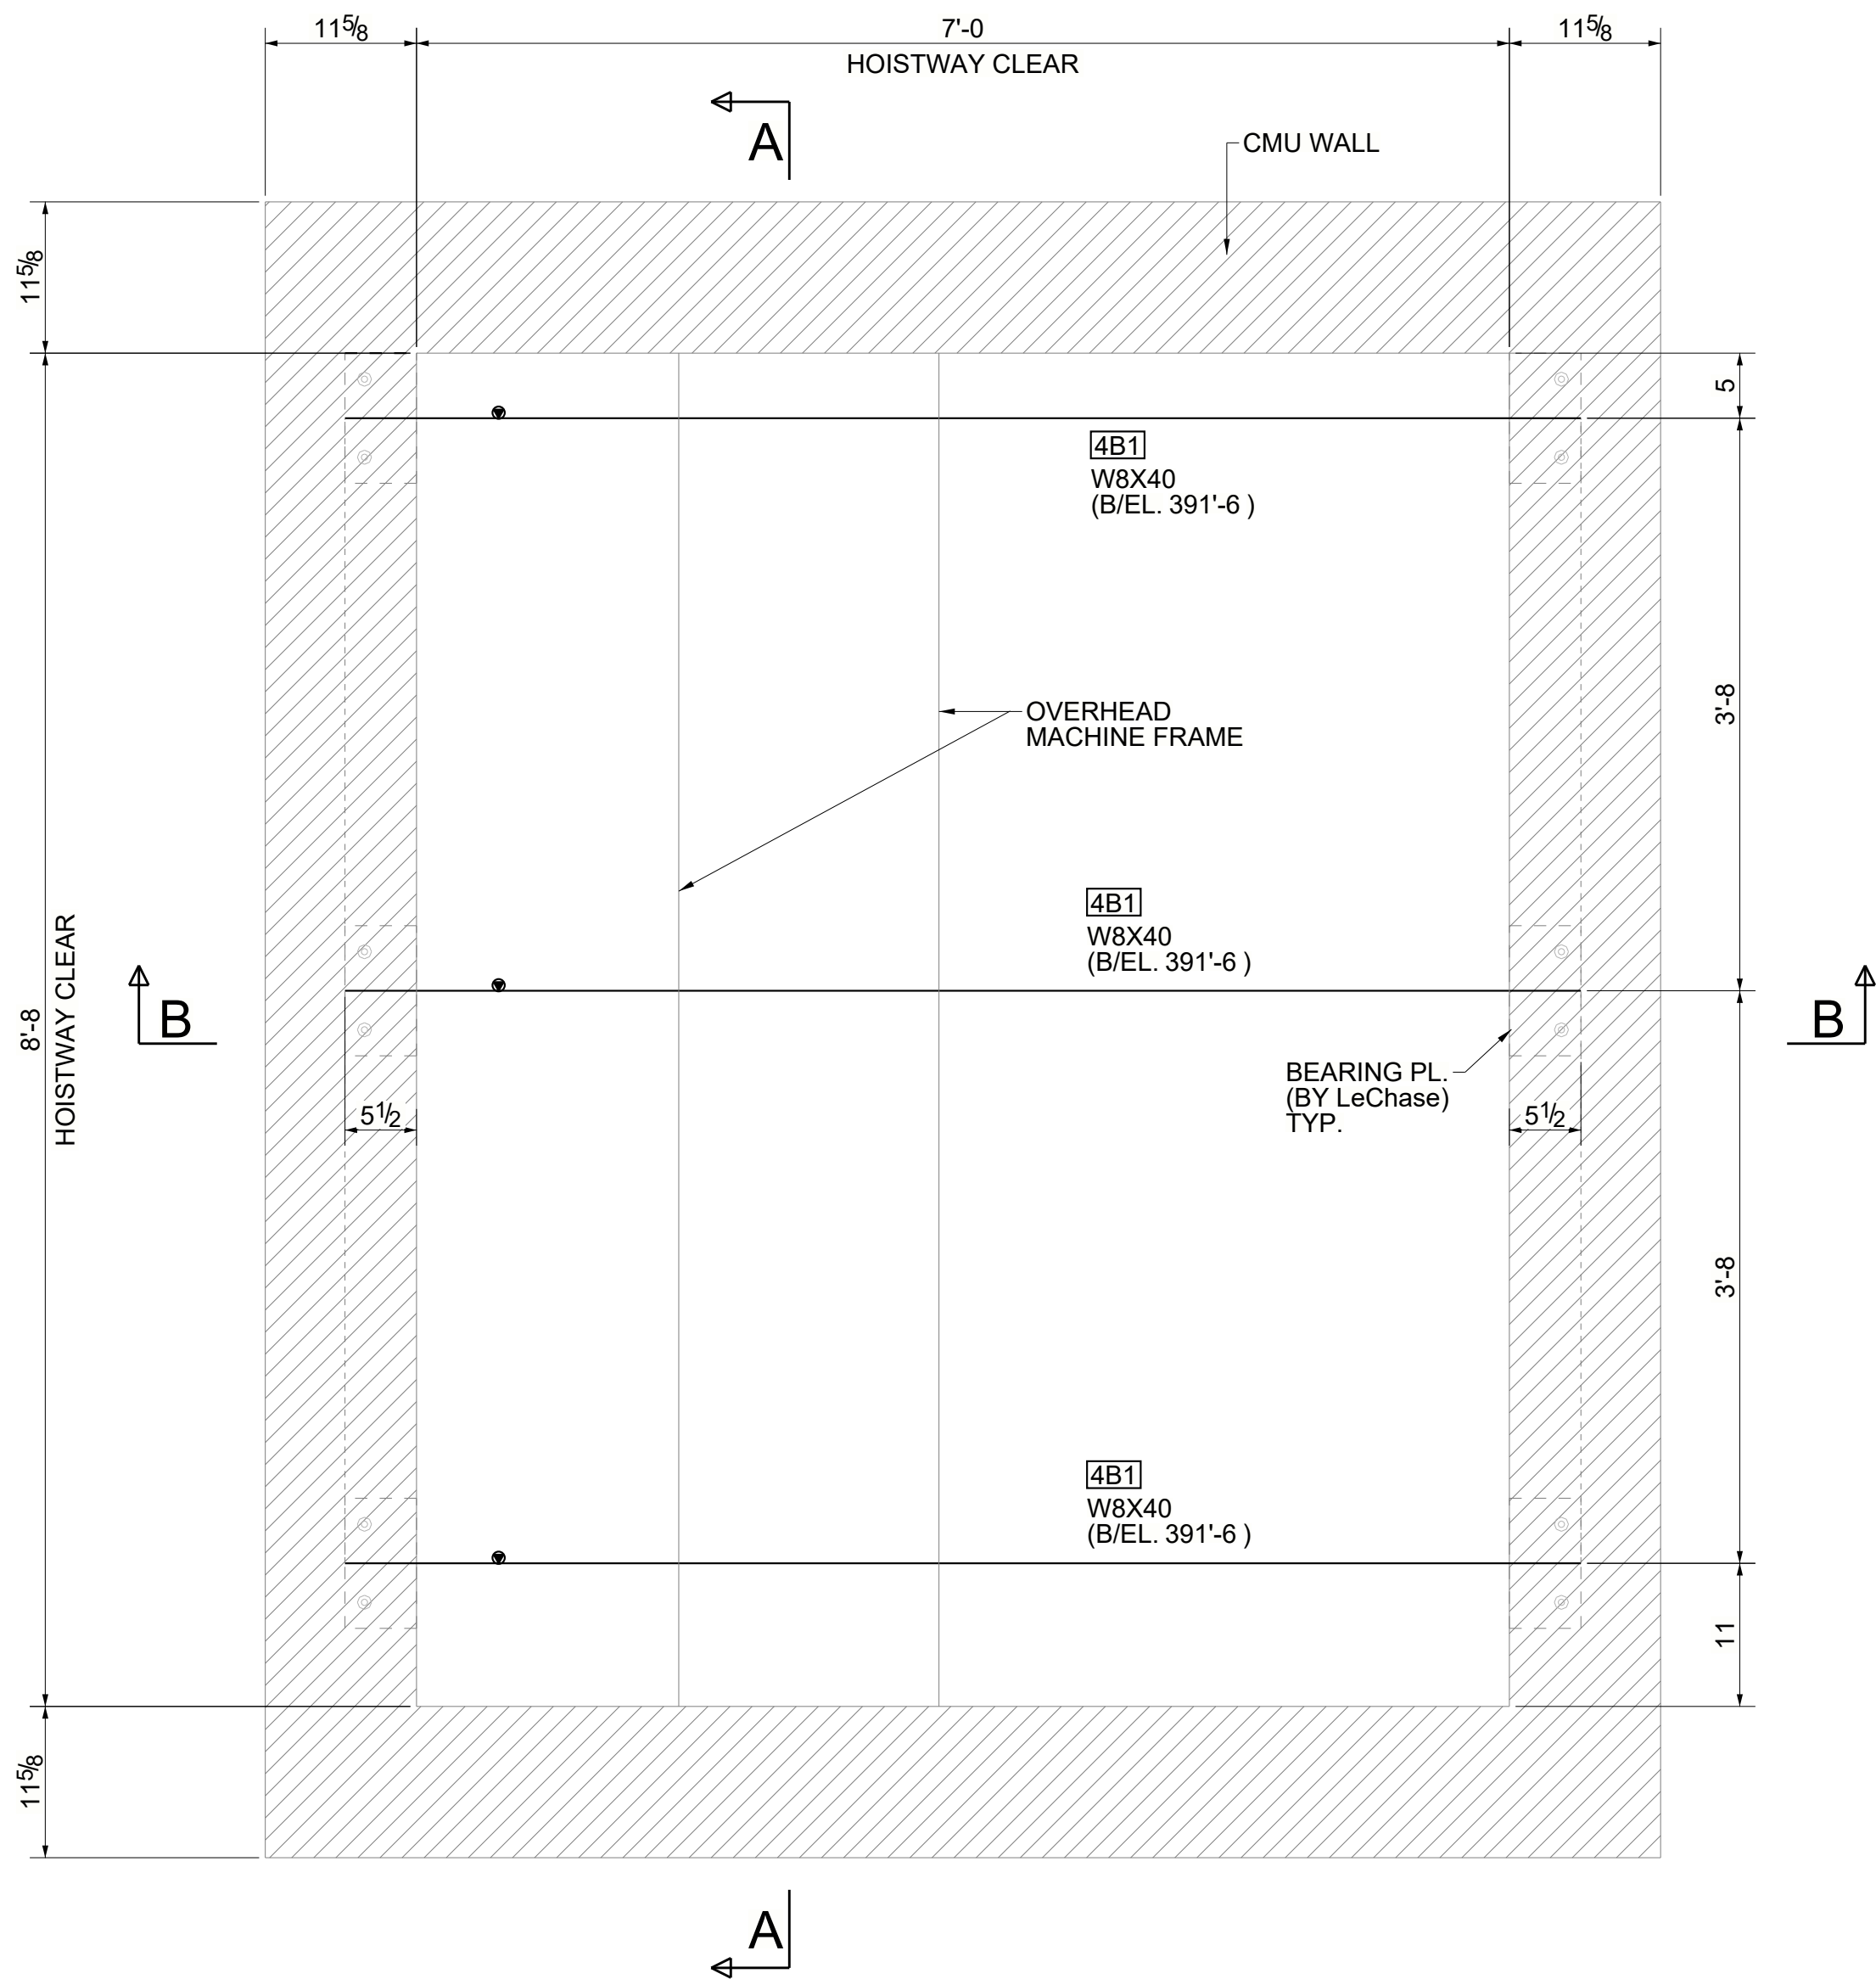


**PERSONNEL ELEVATOR -HOISTWAY BEAM LOCATION PLAN**  
(REFER : PERSONNEL ELEVATOR -HOISTWAY CAP PLAN-6/A644-A5300301 & A644-S3000004)

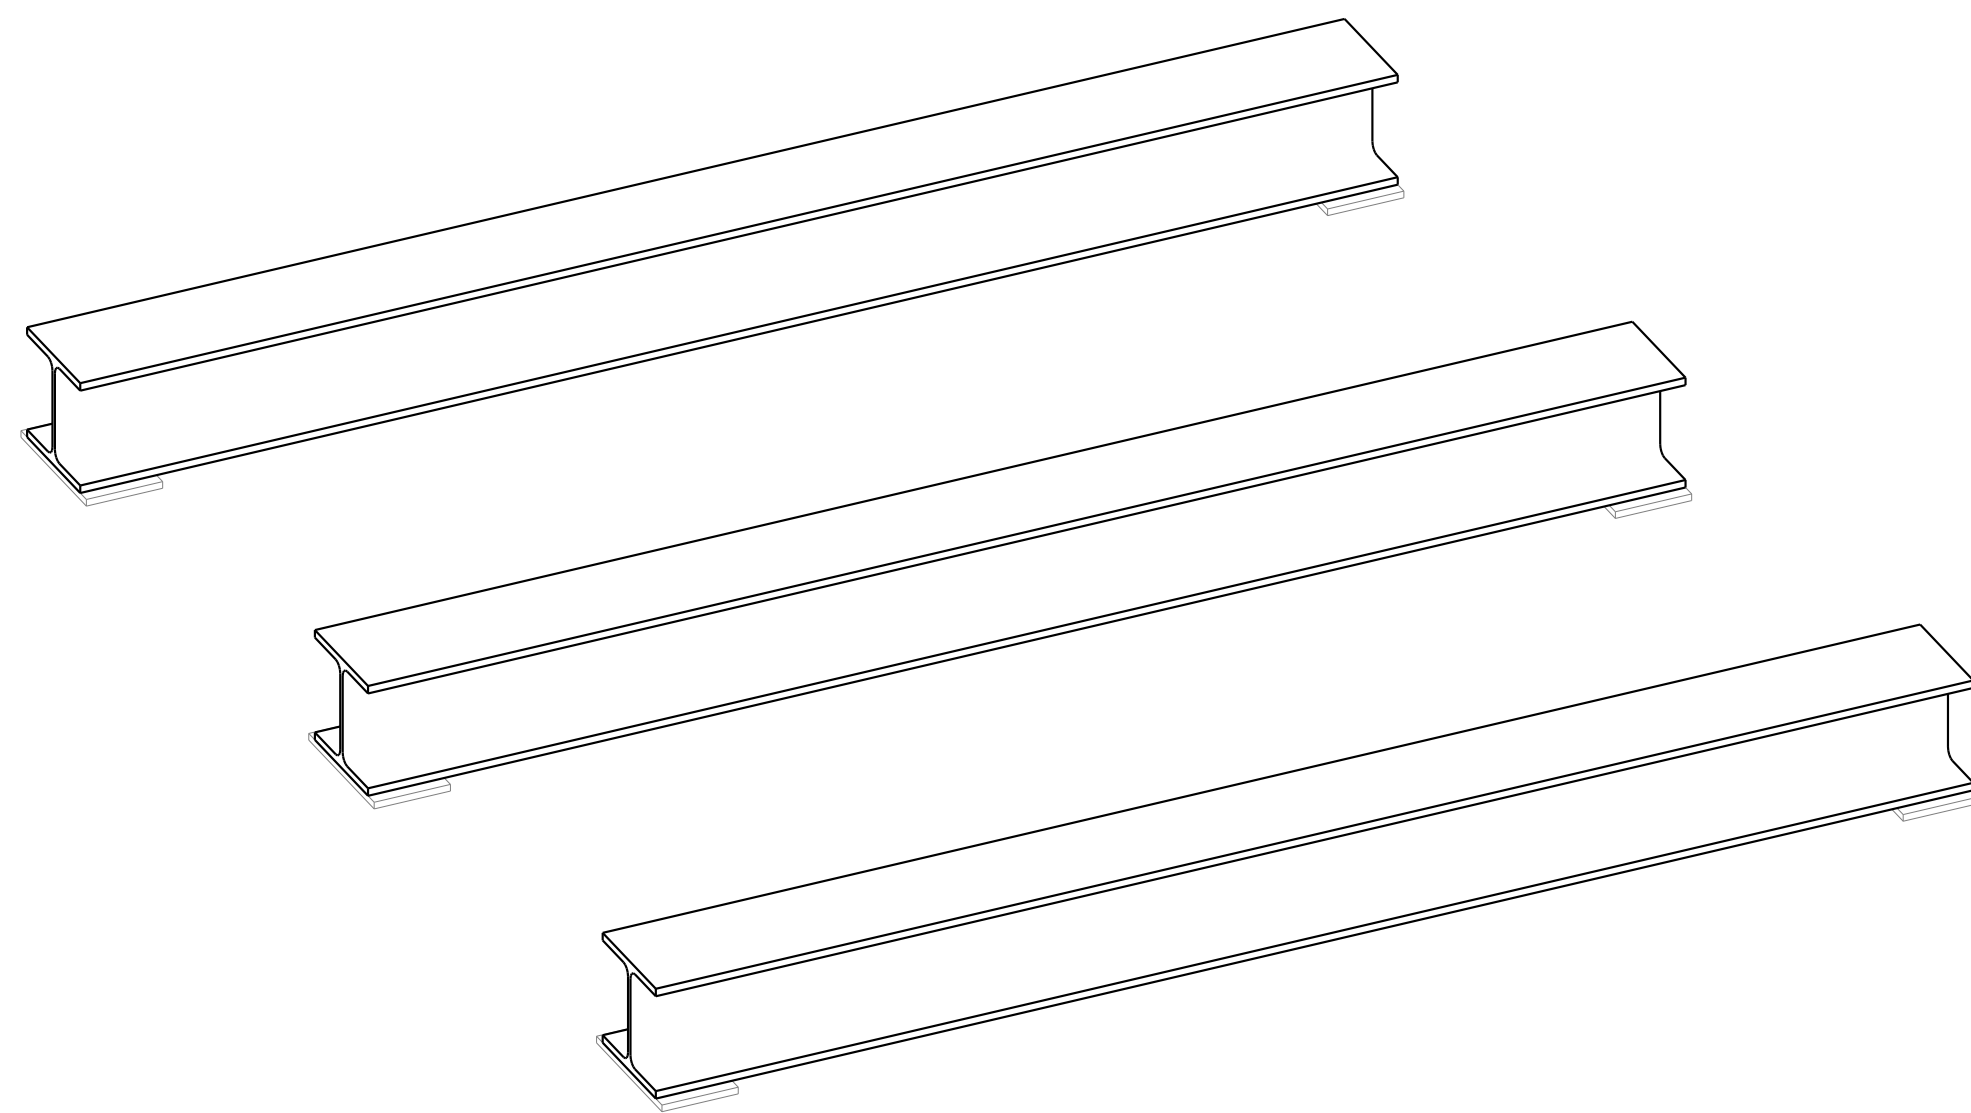

**3D VIEW OF PERSONNEL ELEVATOR -HOISTWAY BEAM**

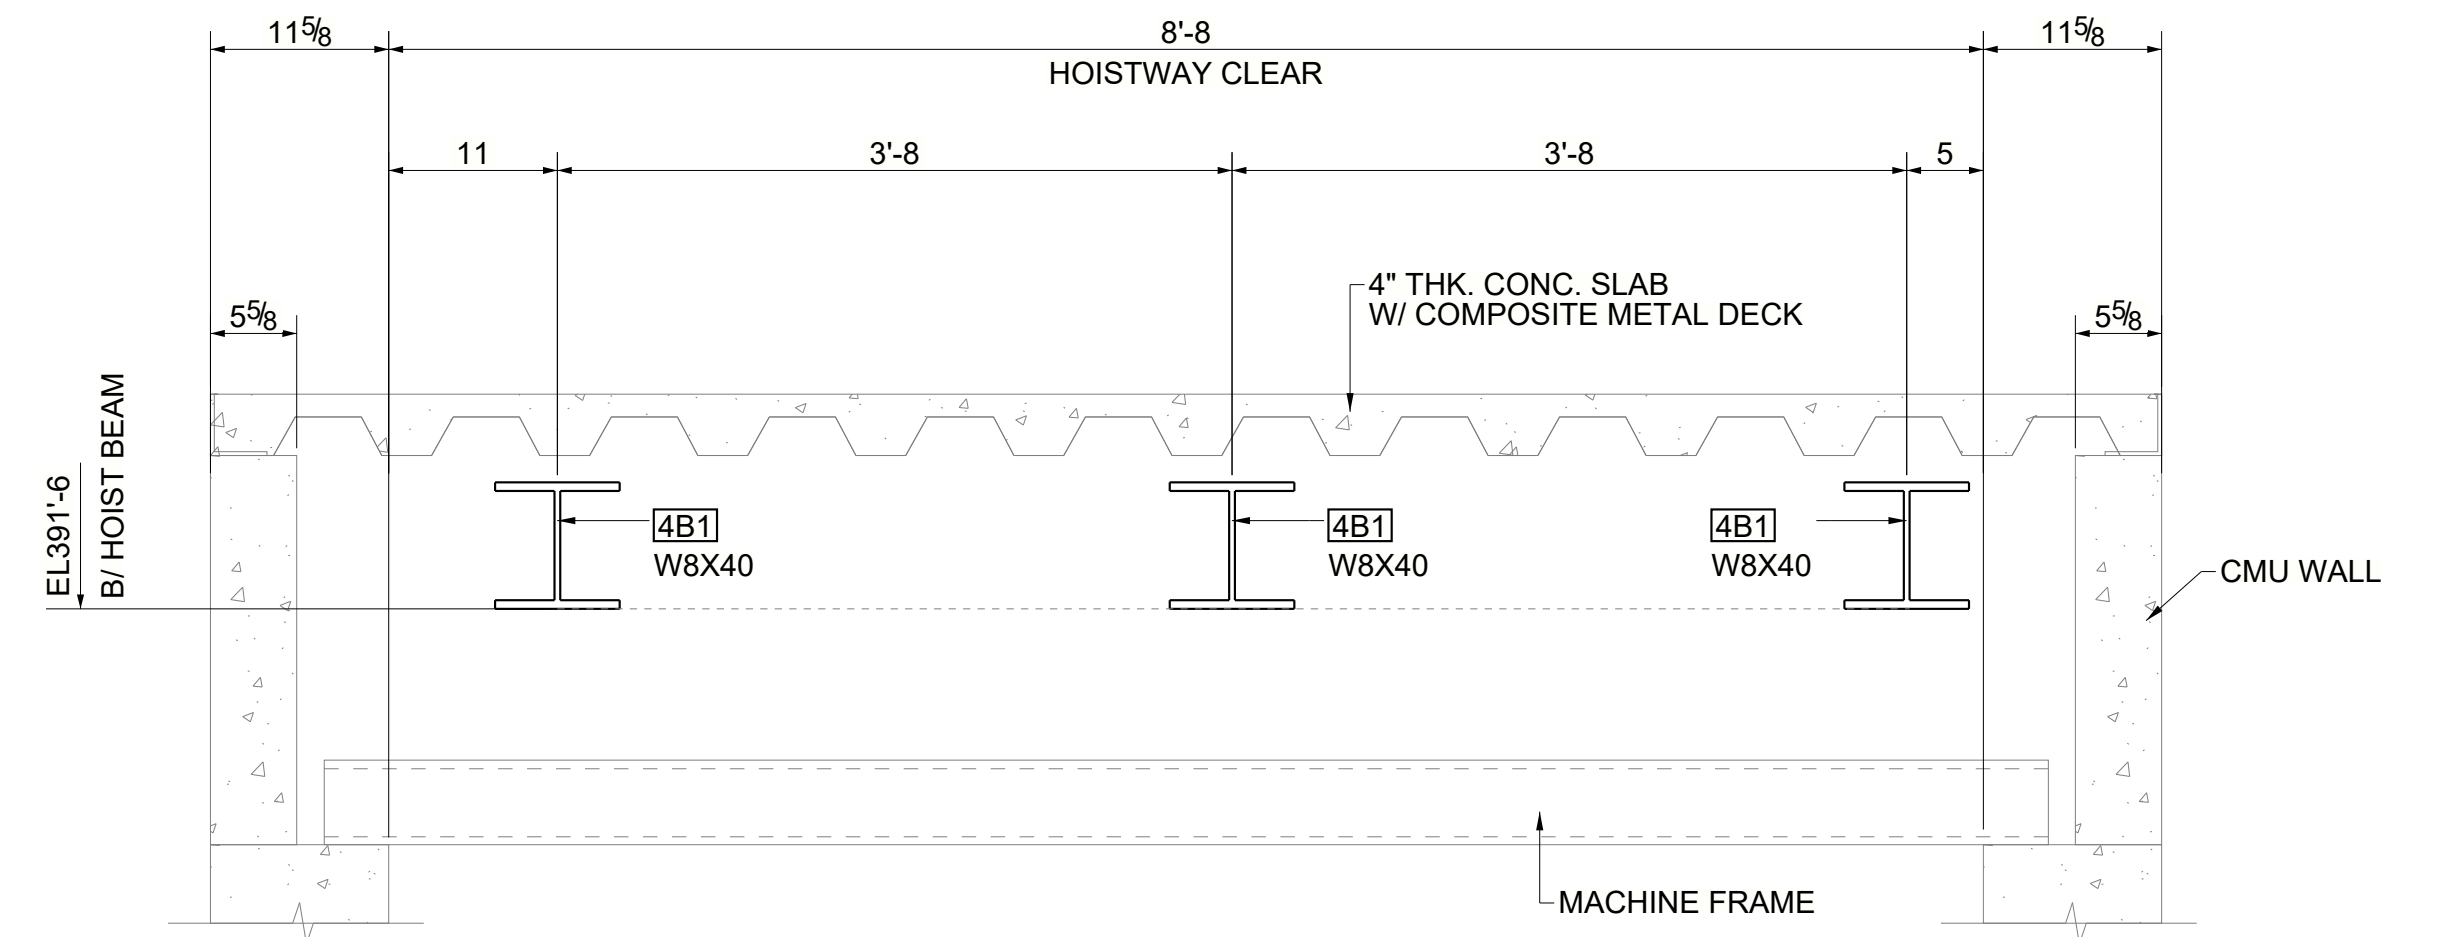

**SECTION A - A**  
(REFER : SECTION-2/ A644-S3000004)

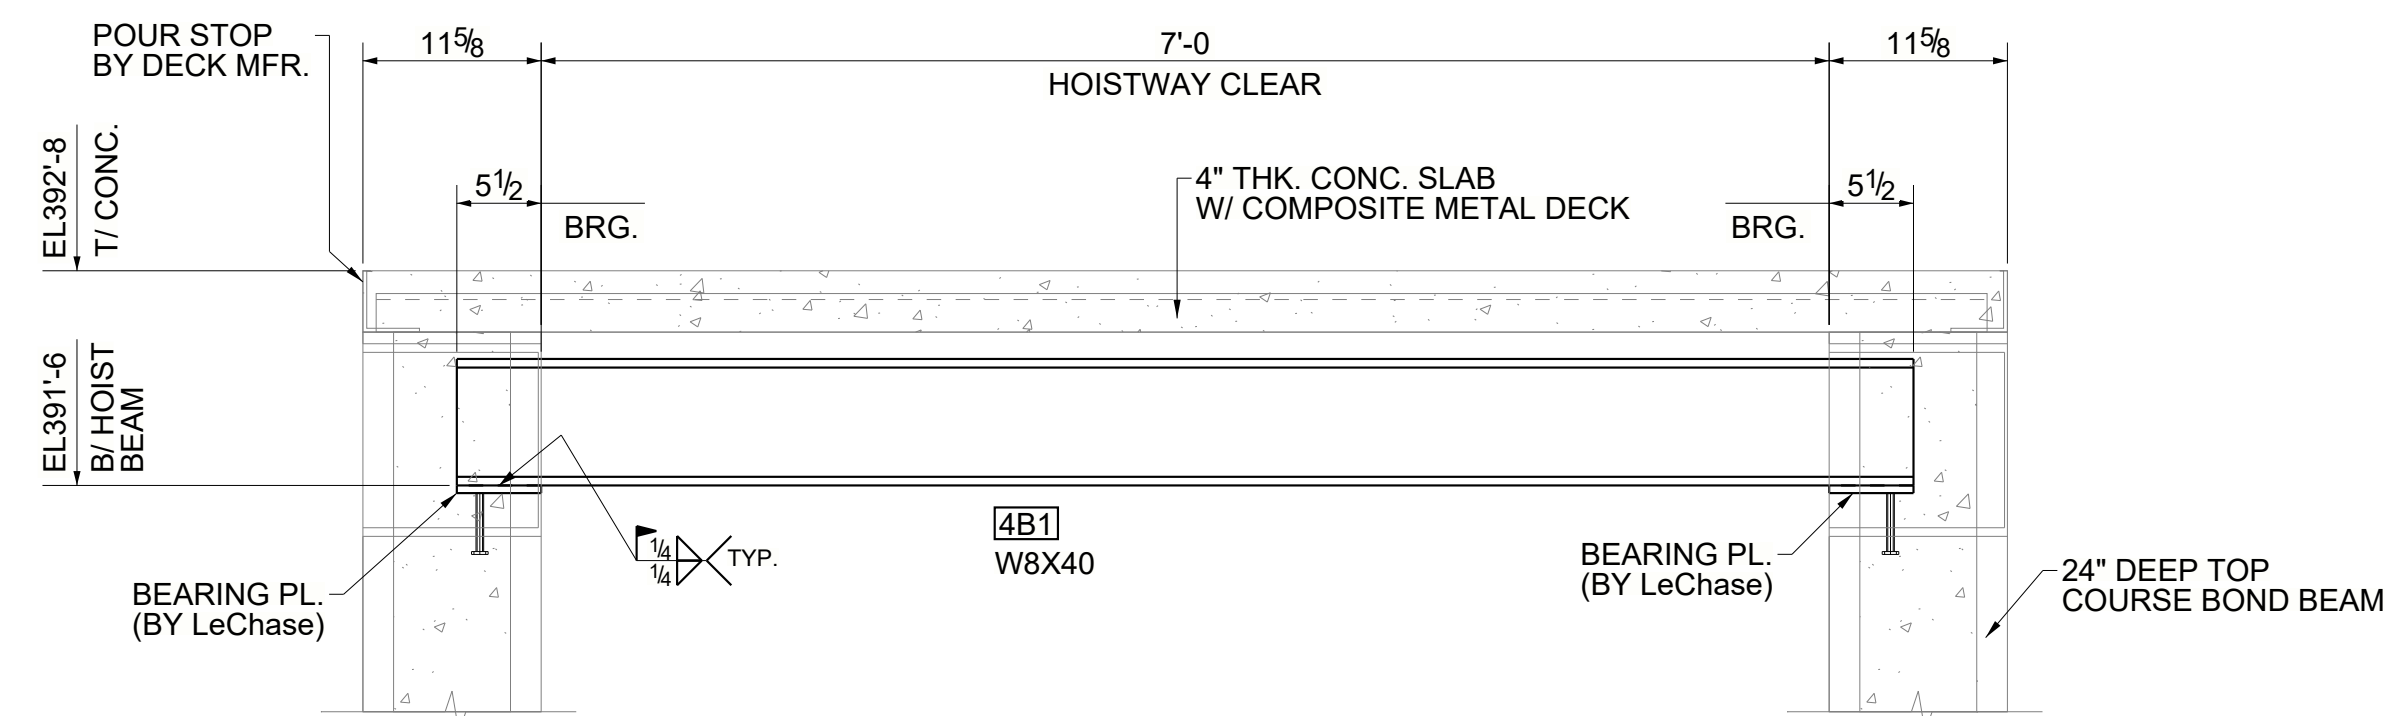


**SECTION B - B**  
(REFER : SECTION-1/ A644-S3000004)


**NOTE !**  
AT HOIST BEAM LOCATIONS REMOVE BOND BEAM SIDE WALL SUFFICIENT TO ALLOW INSTALLATION OF BEAM. FORM AND FILL ERECTION VOID IN BOND BEAM WITH GROUT FOLLOWING BEAM PLACEMENT

**FINISH NOTE :**  
ALL HOIST WAY BEAMS SHALL RECEIVE ONE SHOP COAT PRIMER.


**NOTES :**

1. MATERIAL GRADES :  
W~BEAM : A992  
PLATES & ANGLE : A36  
HSS~TUBES : A500 GRADE C

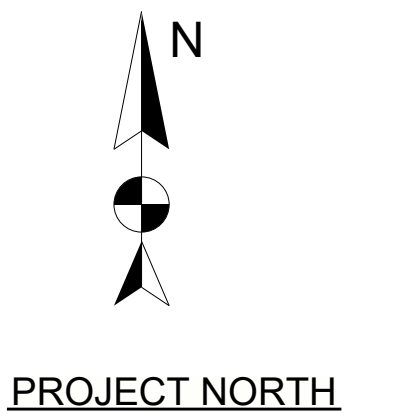


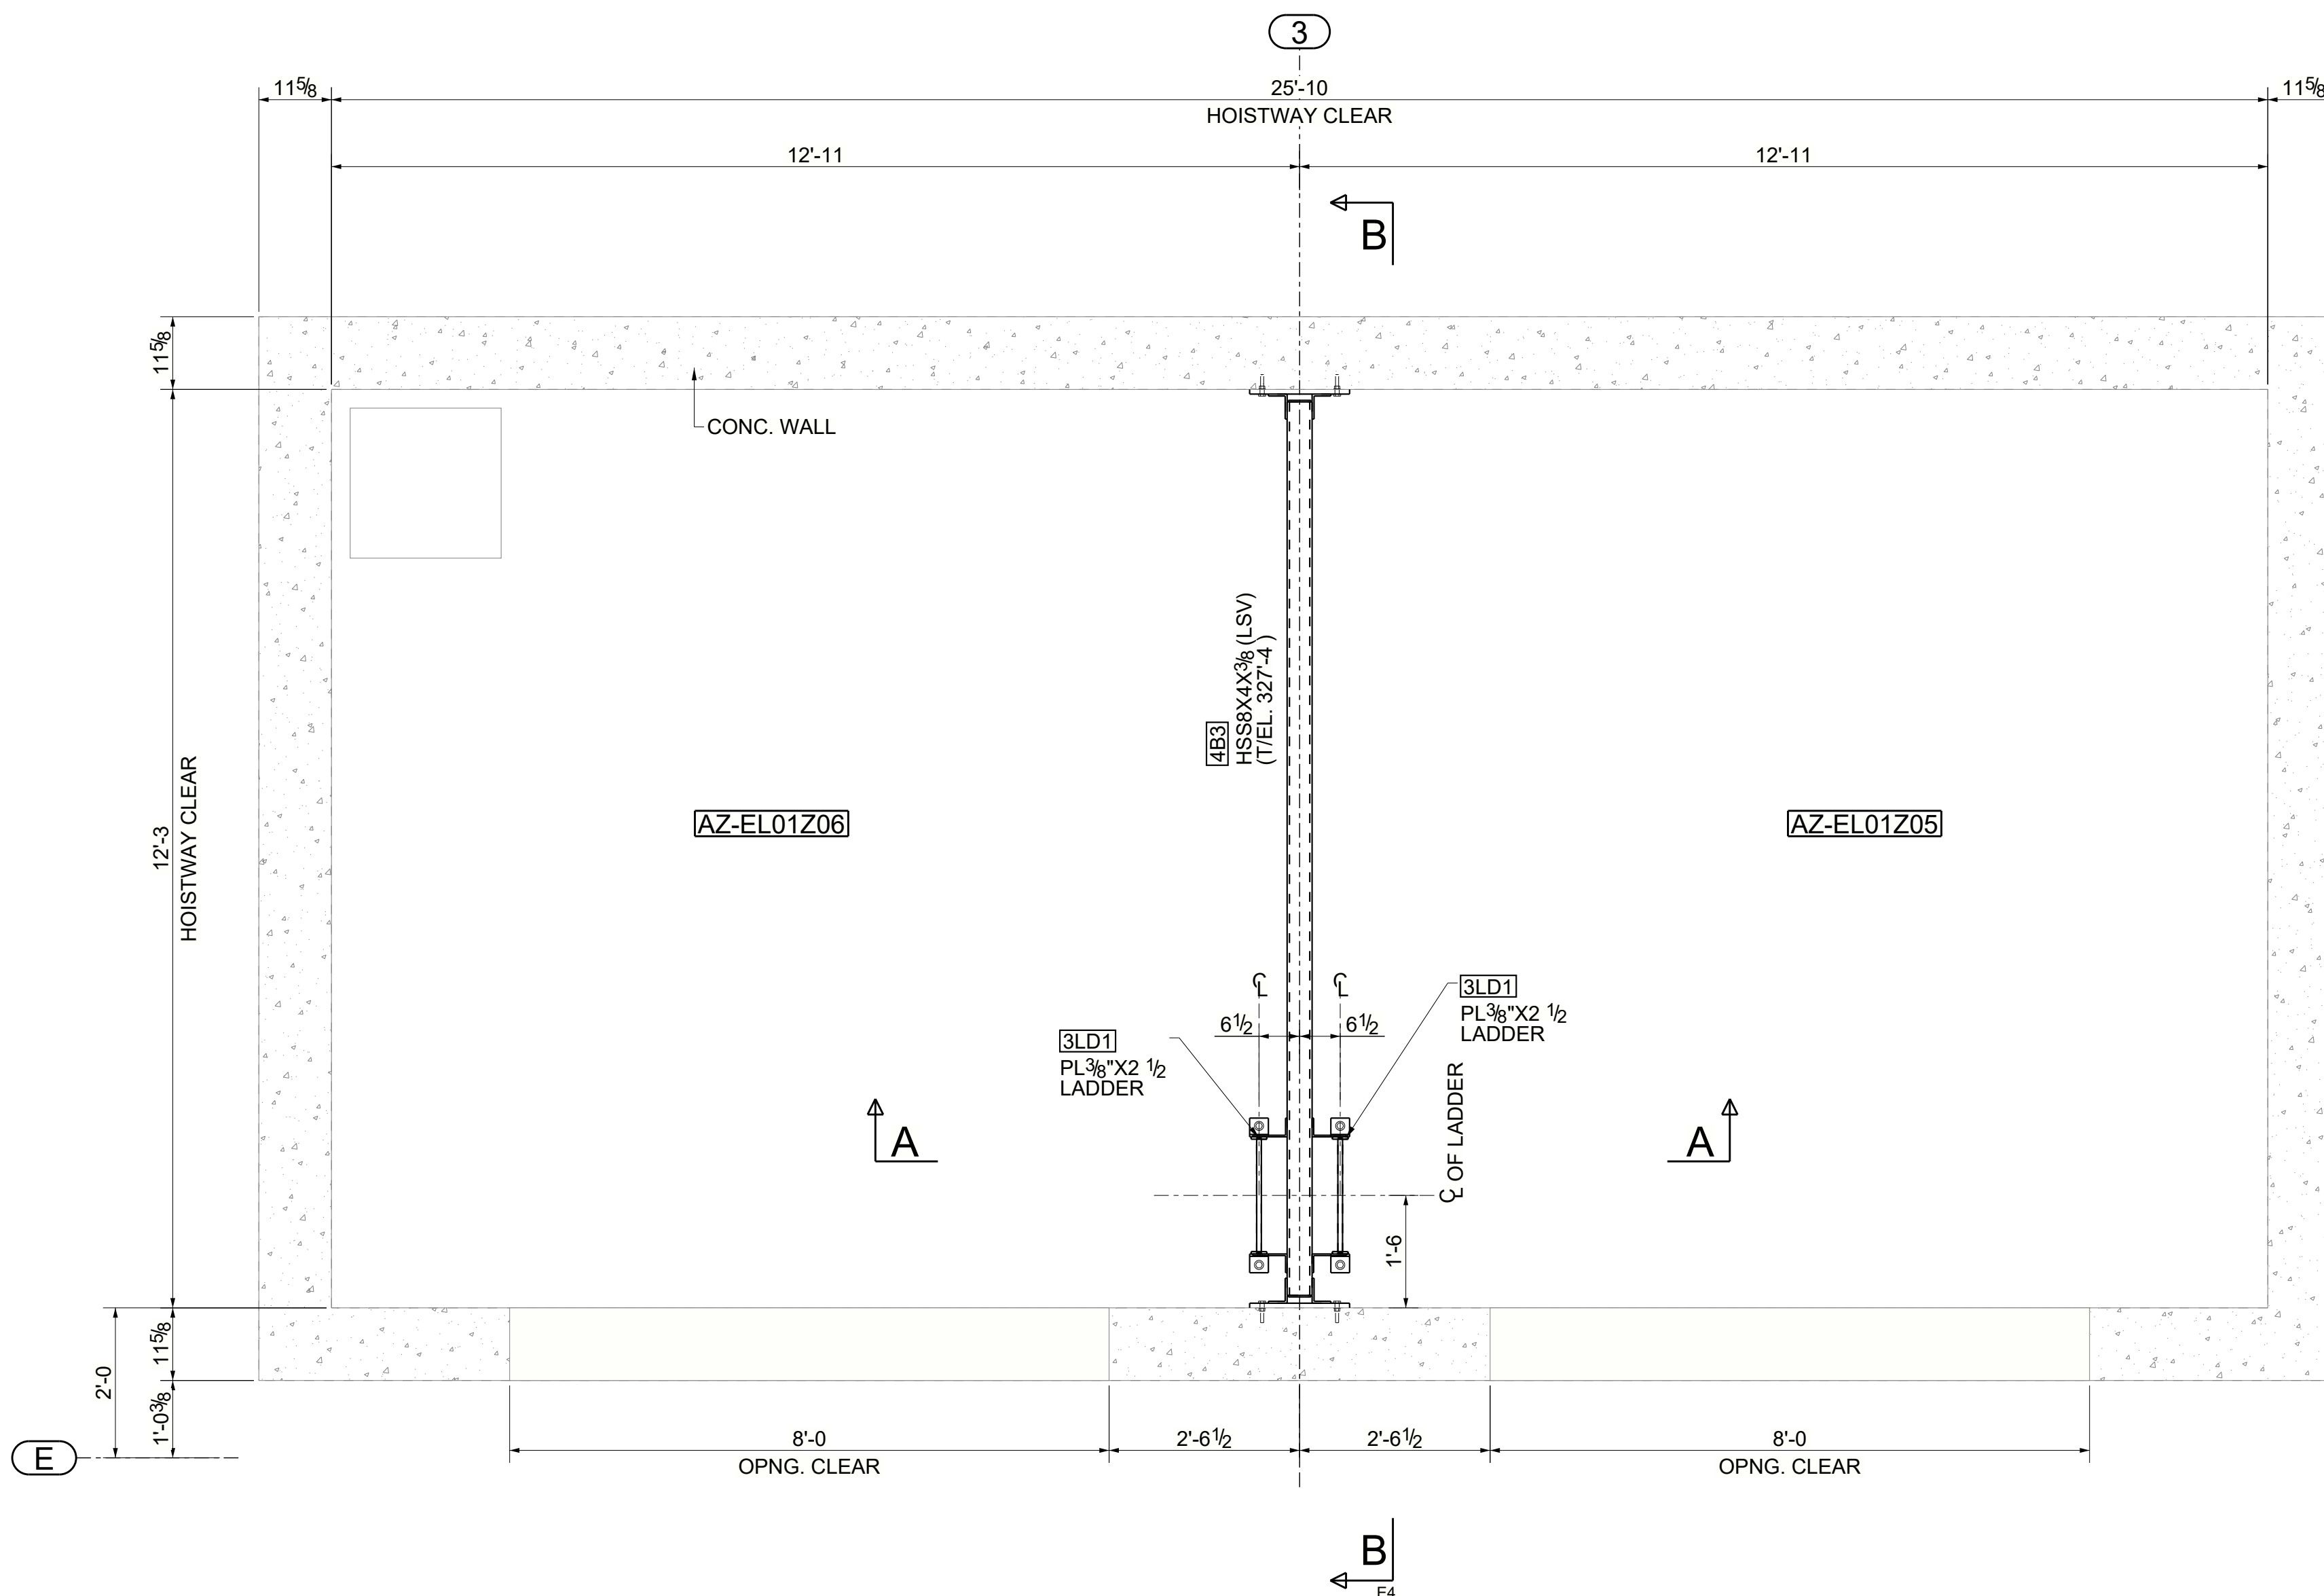


**SERVICE ELEVATOR -PIT LADDER LOCATION PLAN**  
(REFER : SERVICE ELEVATORS -ELEVATOR PIT PLAN-1/A644-A5300301 & A644-S3000004)

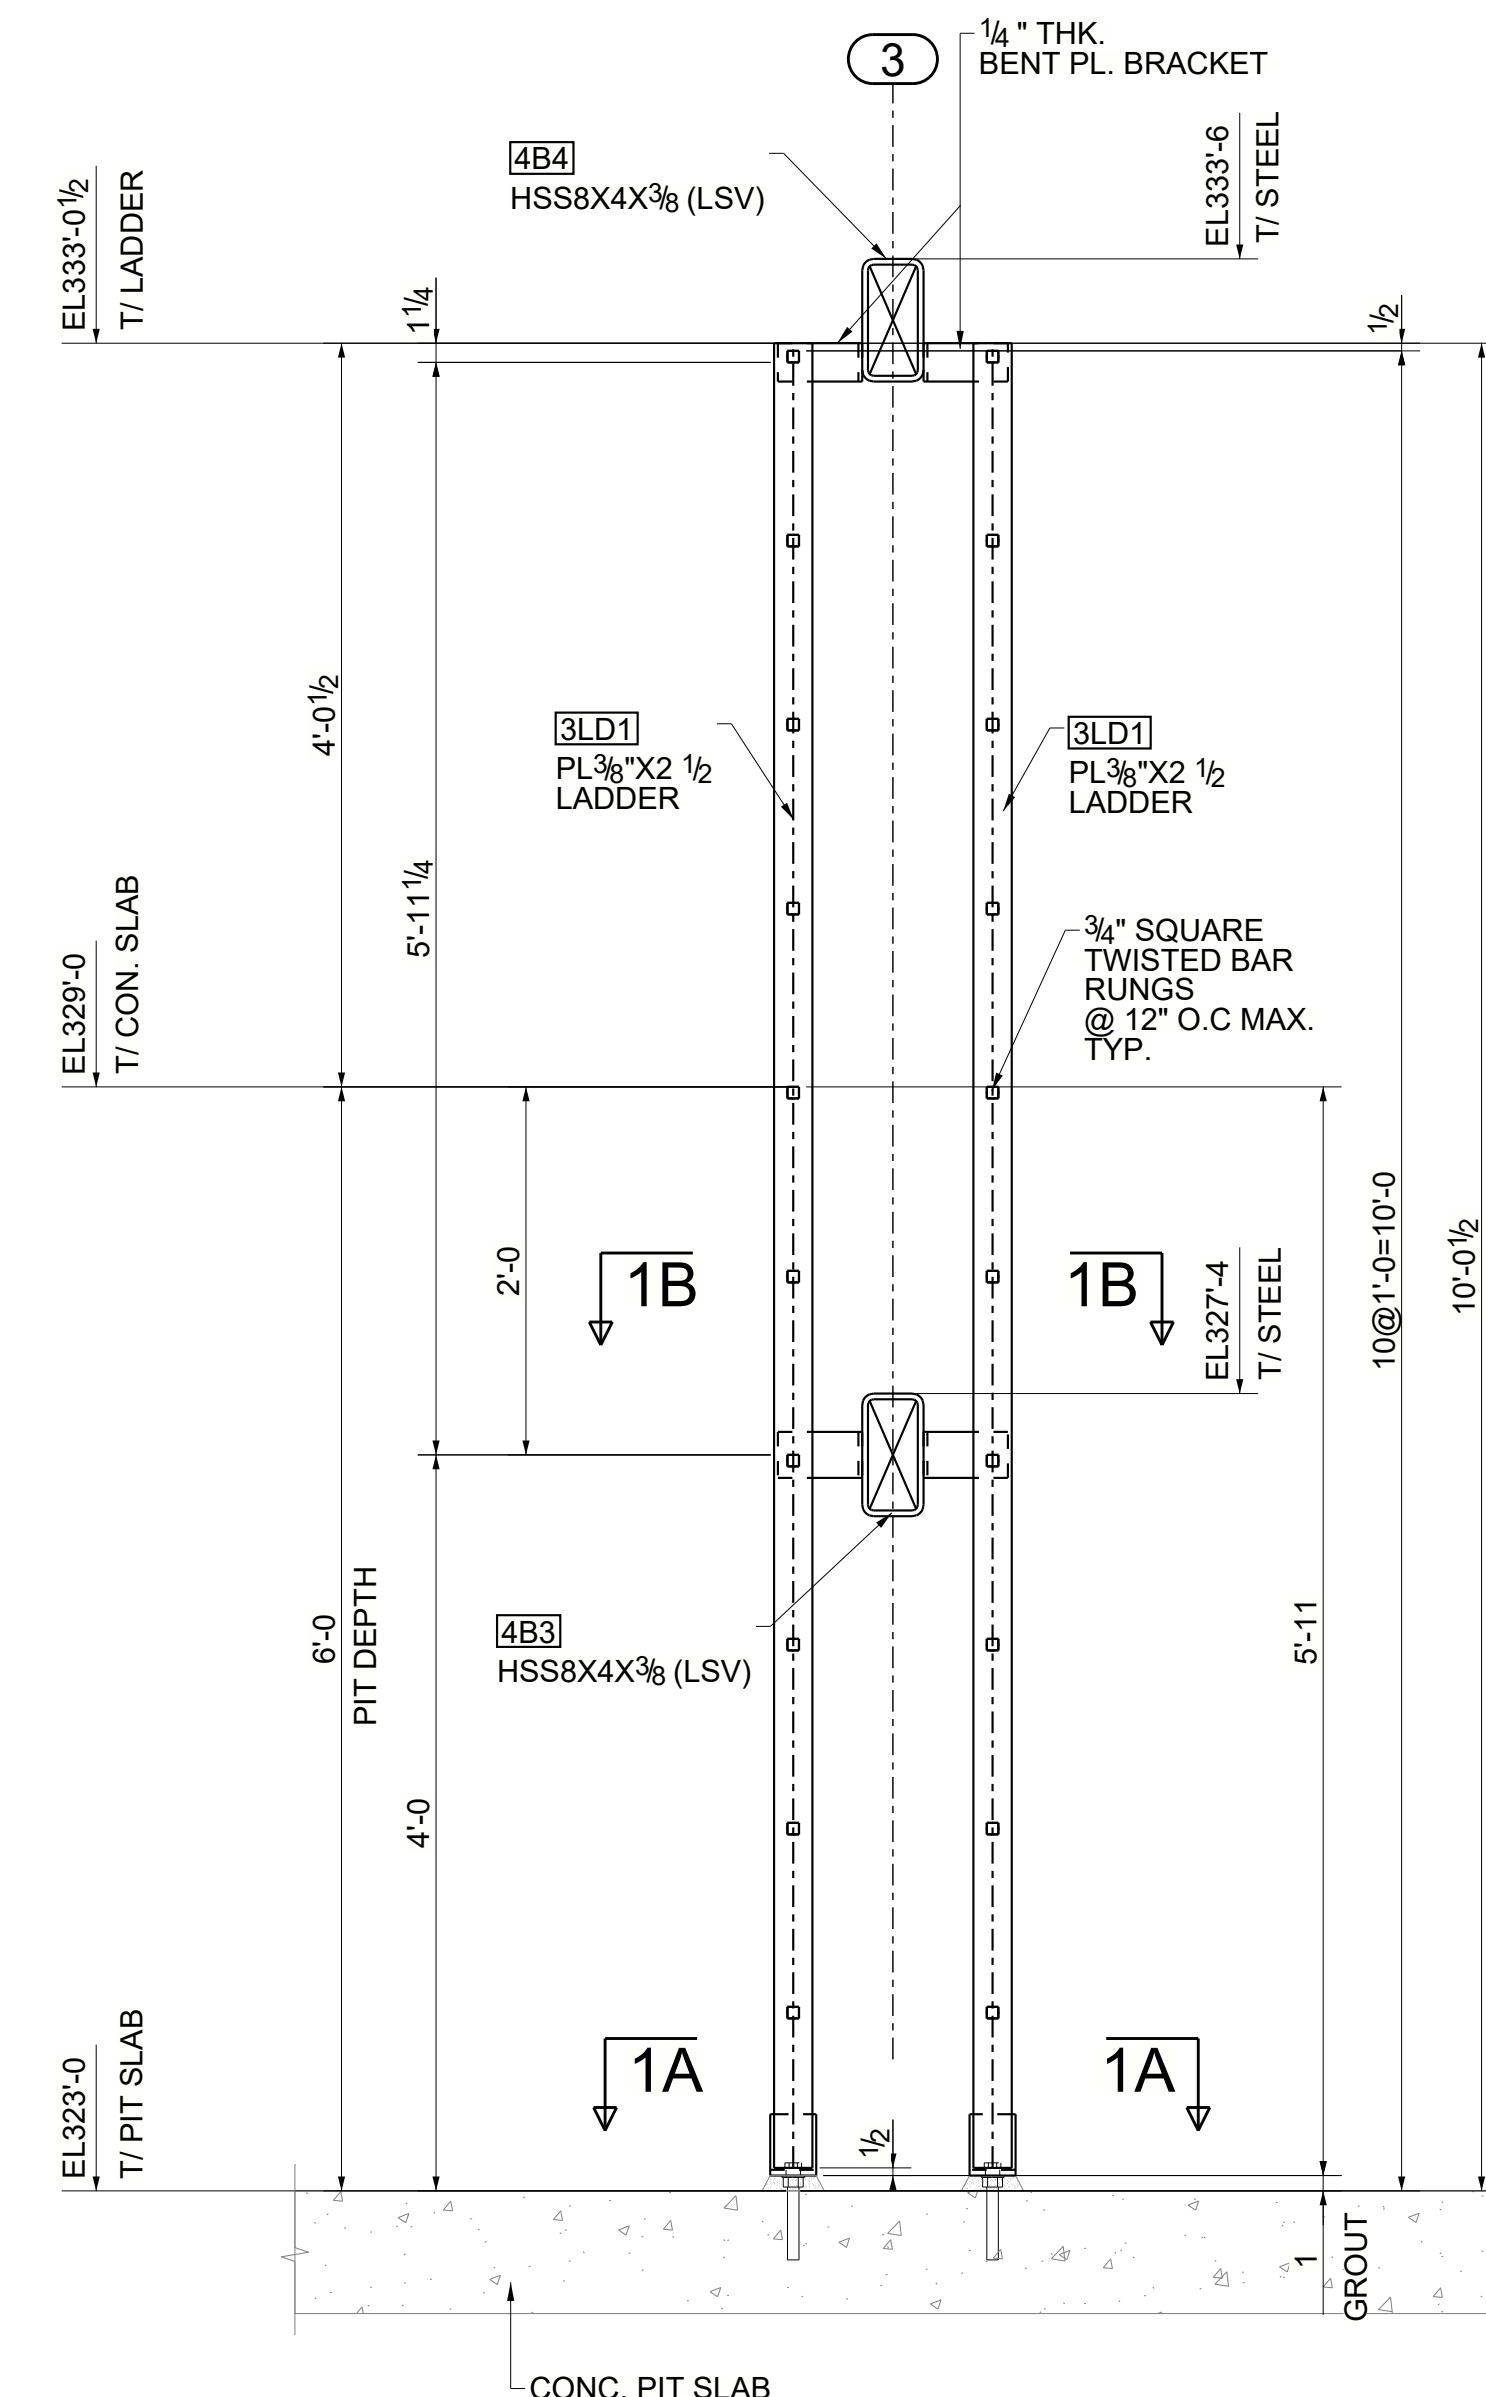


**SECTION A - A**  
(REFER : SECTION -6 /A644-A3000004)

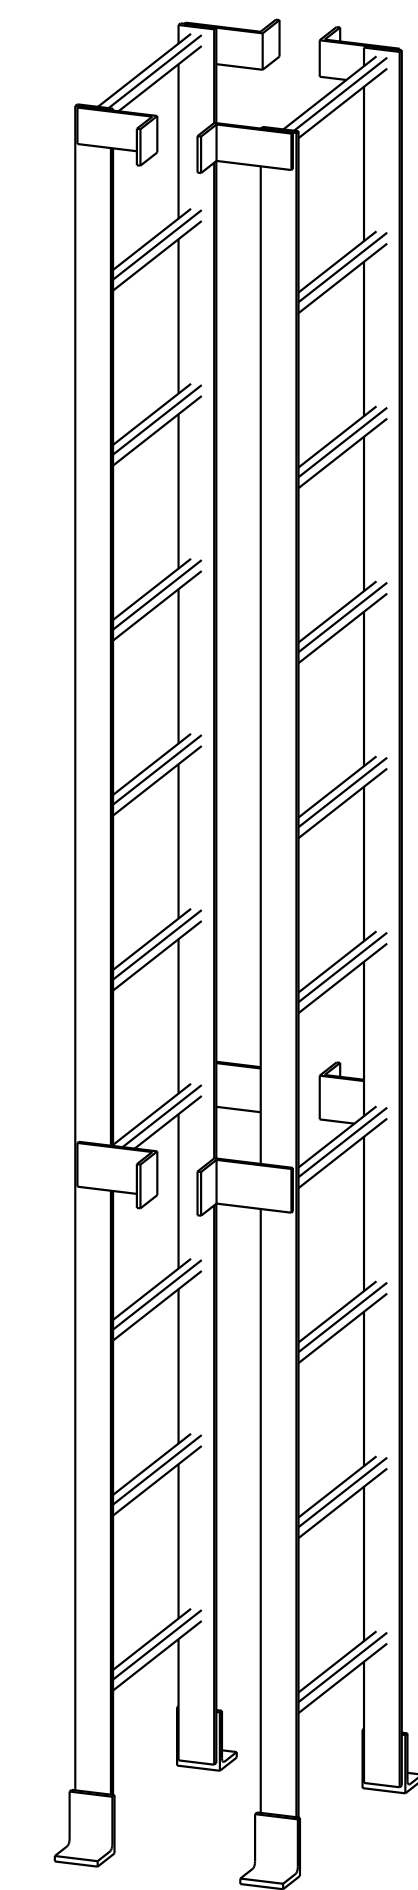


**3D VIEW OF SERVICE ELEVATOR -PIT LADDER**

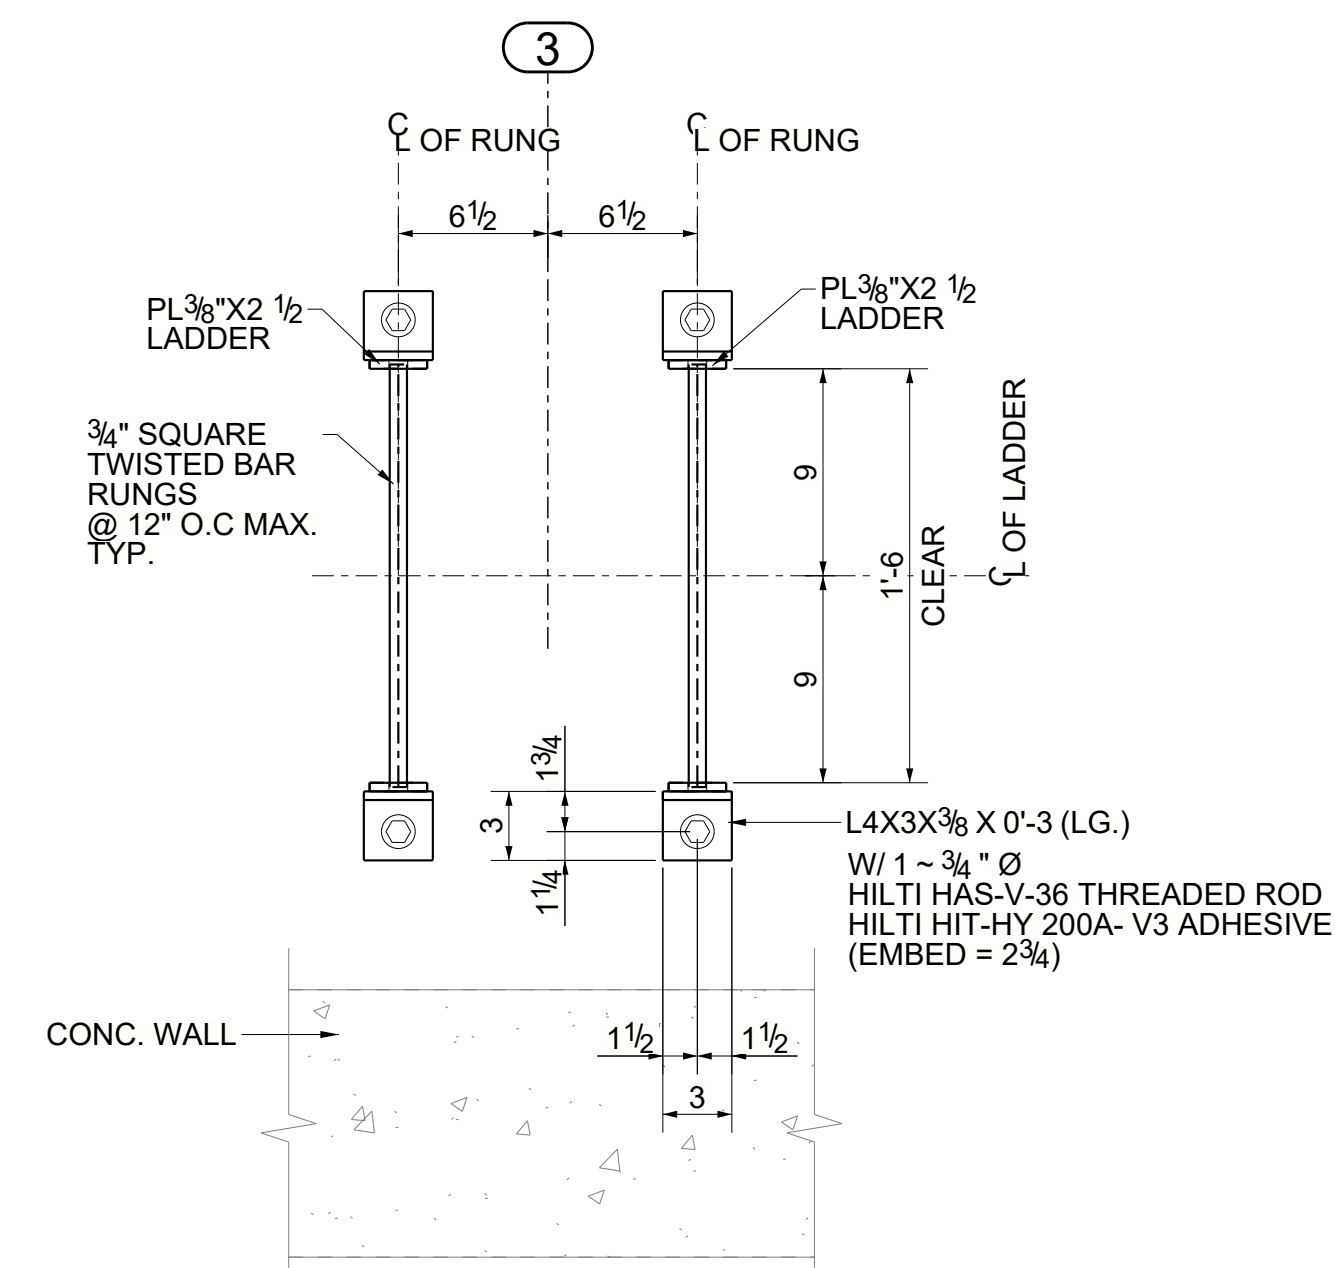

**SECTION 1A - 1A**

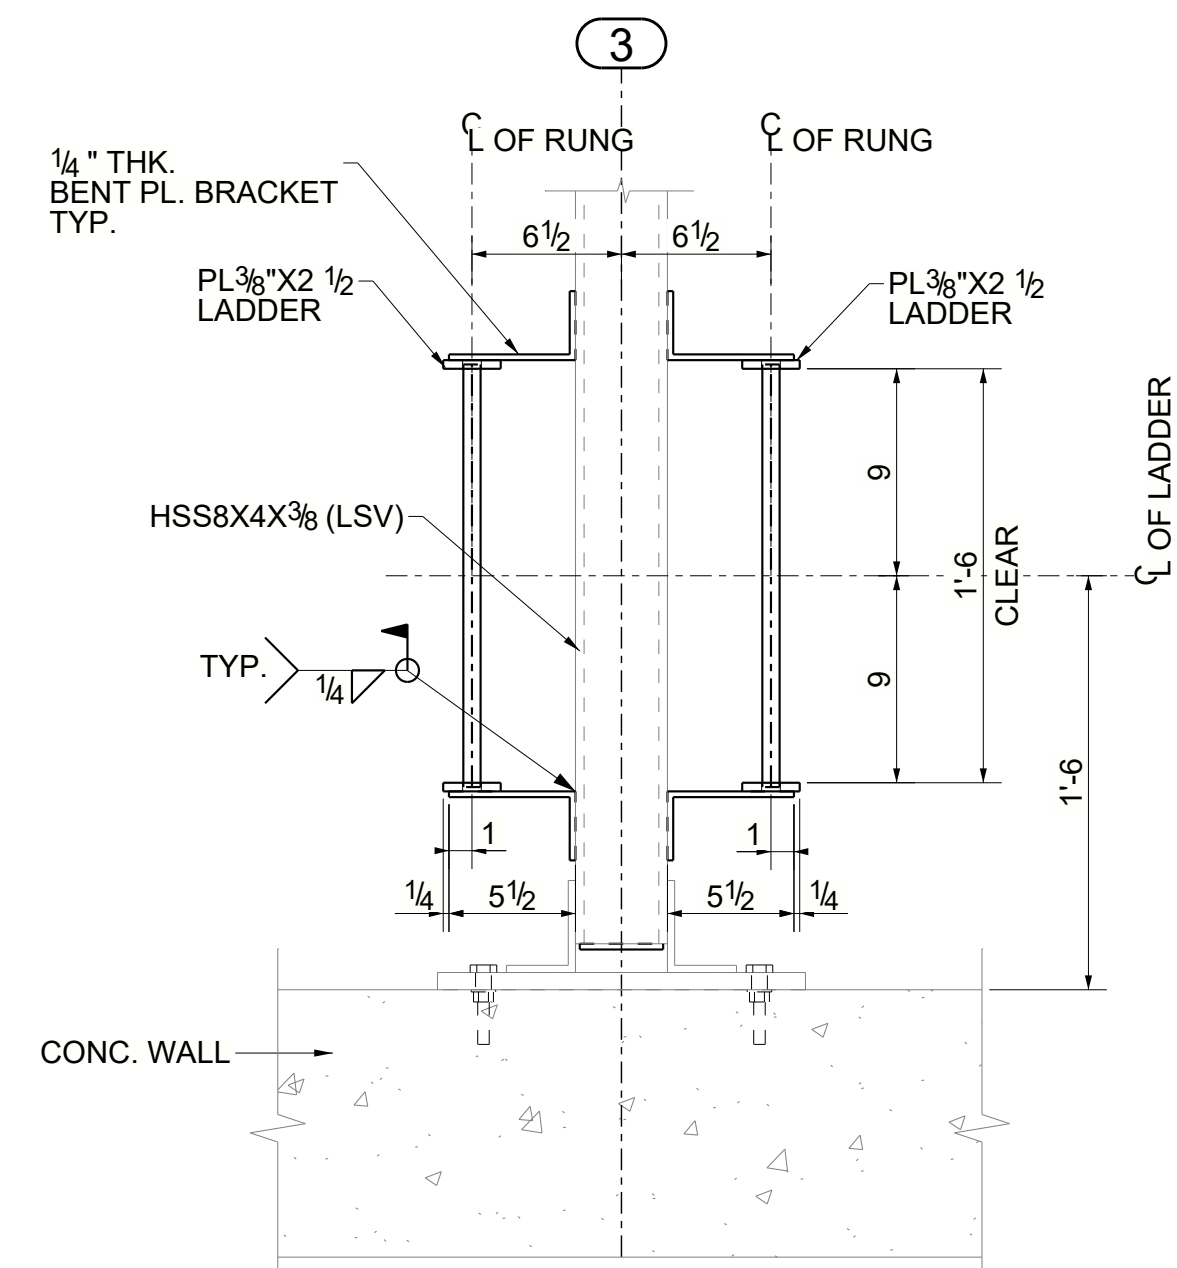


**SECTION 1B - 1B**

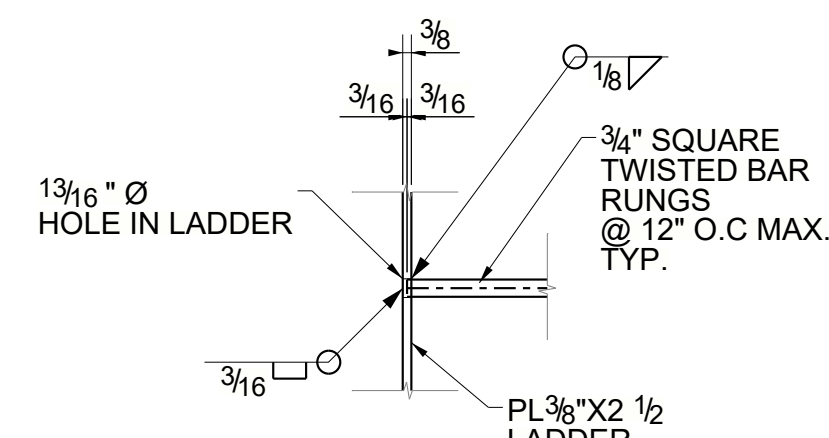


**TYPICAL RUNG ATTACHMENT DETAIL**  
(REFER : TYPICAL RUNG ATTACHMENT DETAIL /A644-S3000004)


**FINISH NOTE :**  
**ALL LADDER STEEL MEMBERS TO BE HOT-DIP GALVANIZED.**

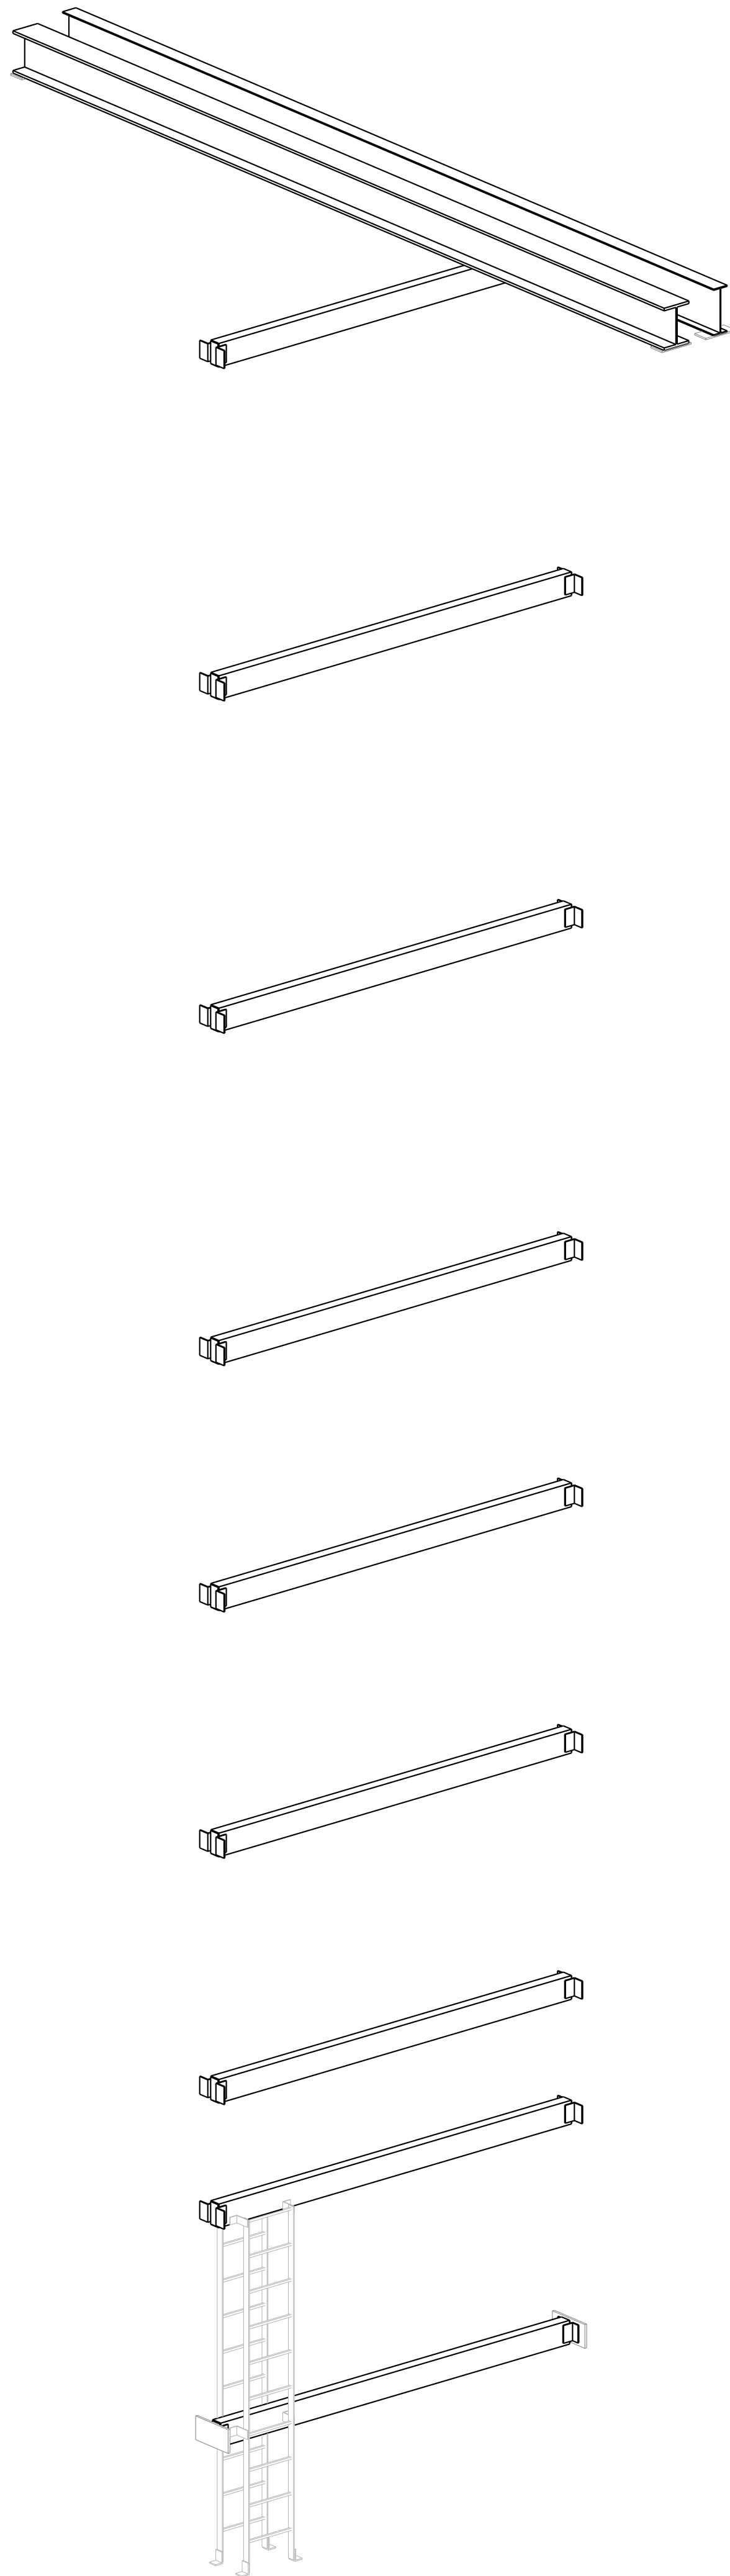


3D VIEW OF SERVICE ELEVATOR STEEL

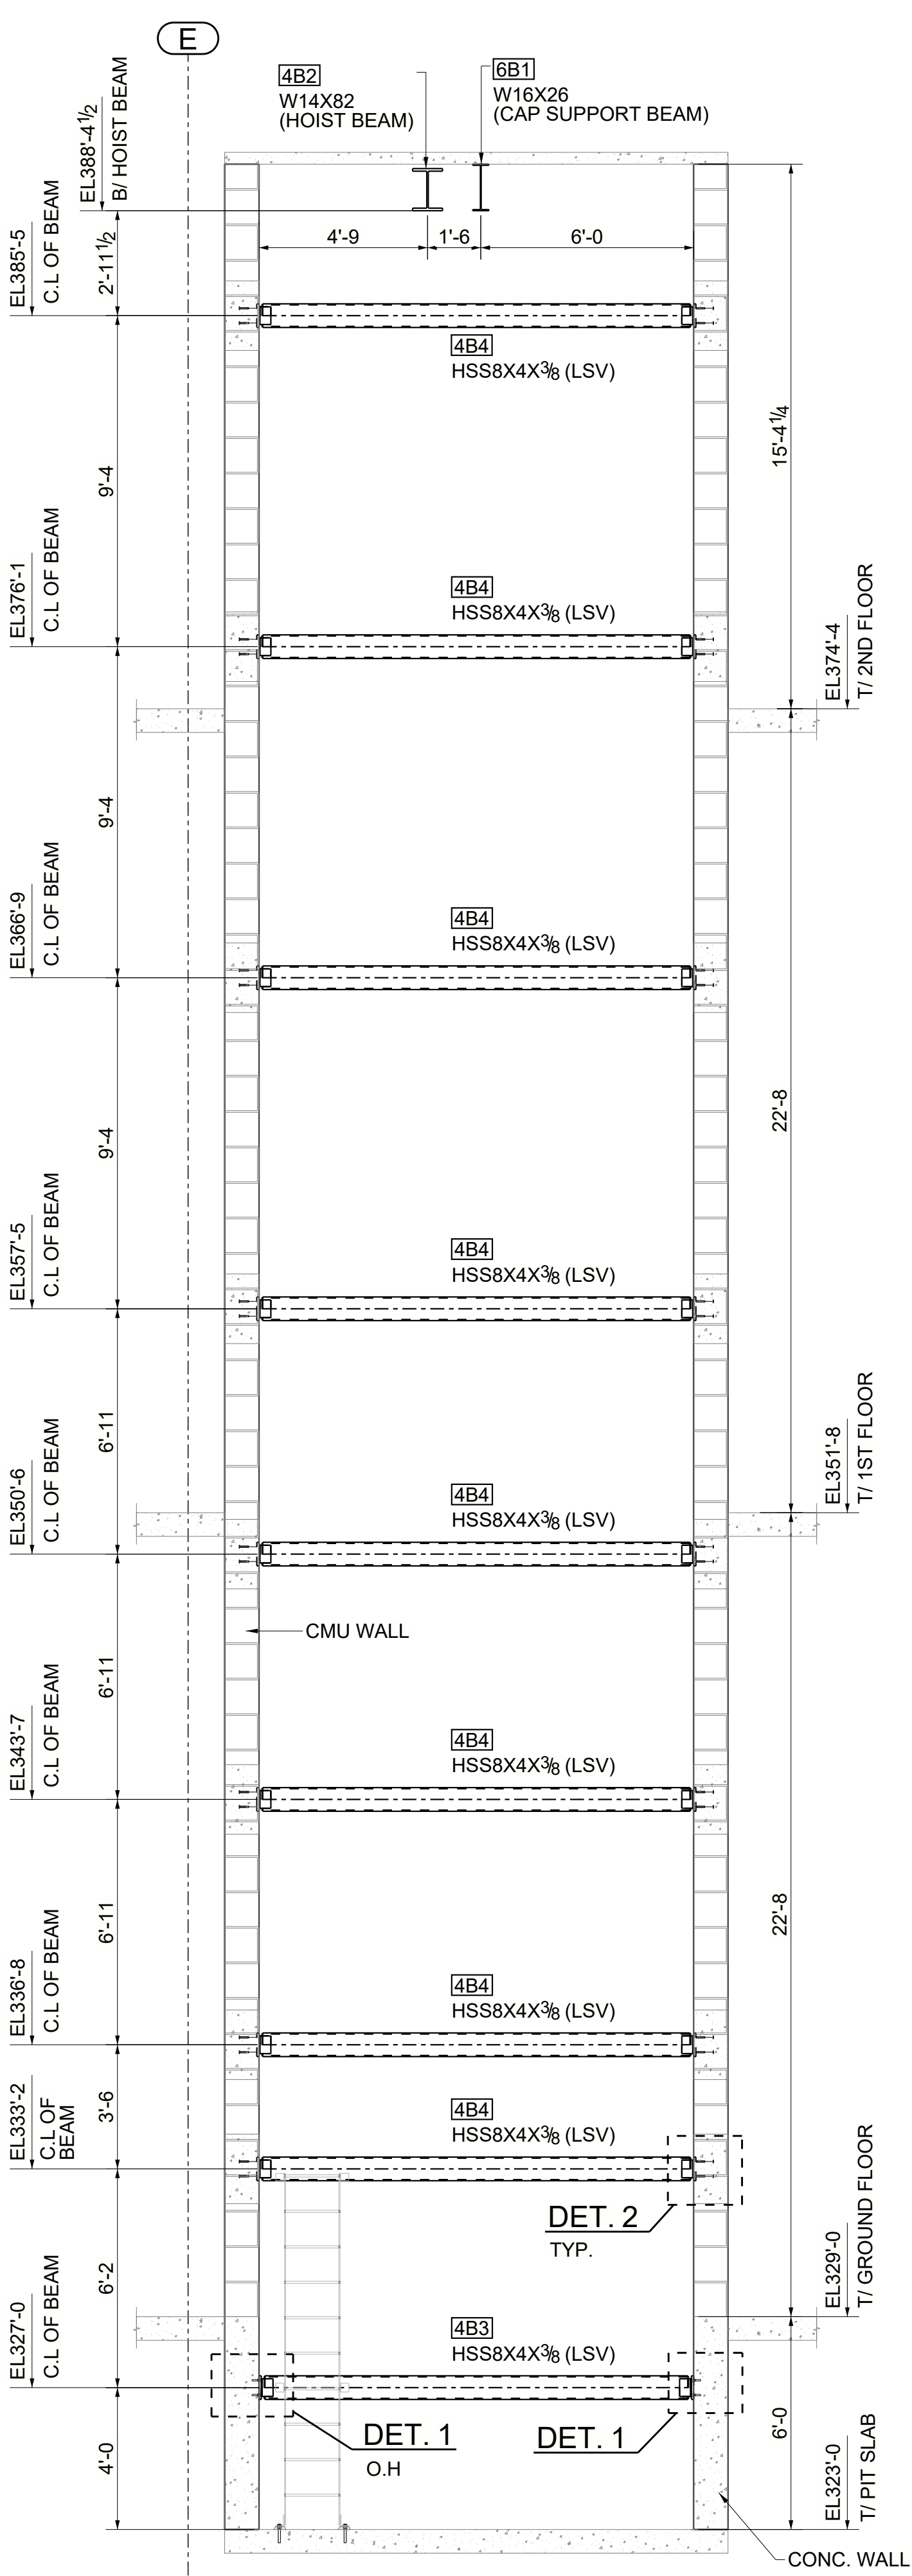


SECTION B - B  
E3  
(REFER : SSECTION -SERVICE ELEVATORS N/S-7/A644-A5300301)

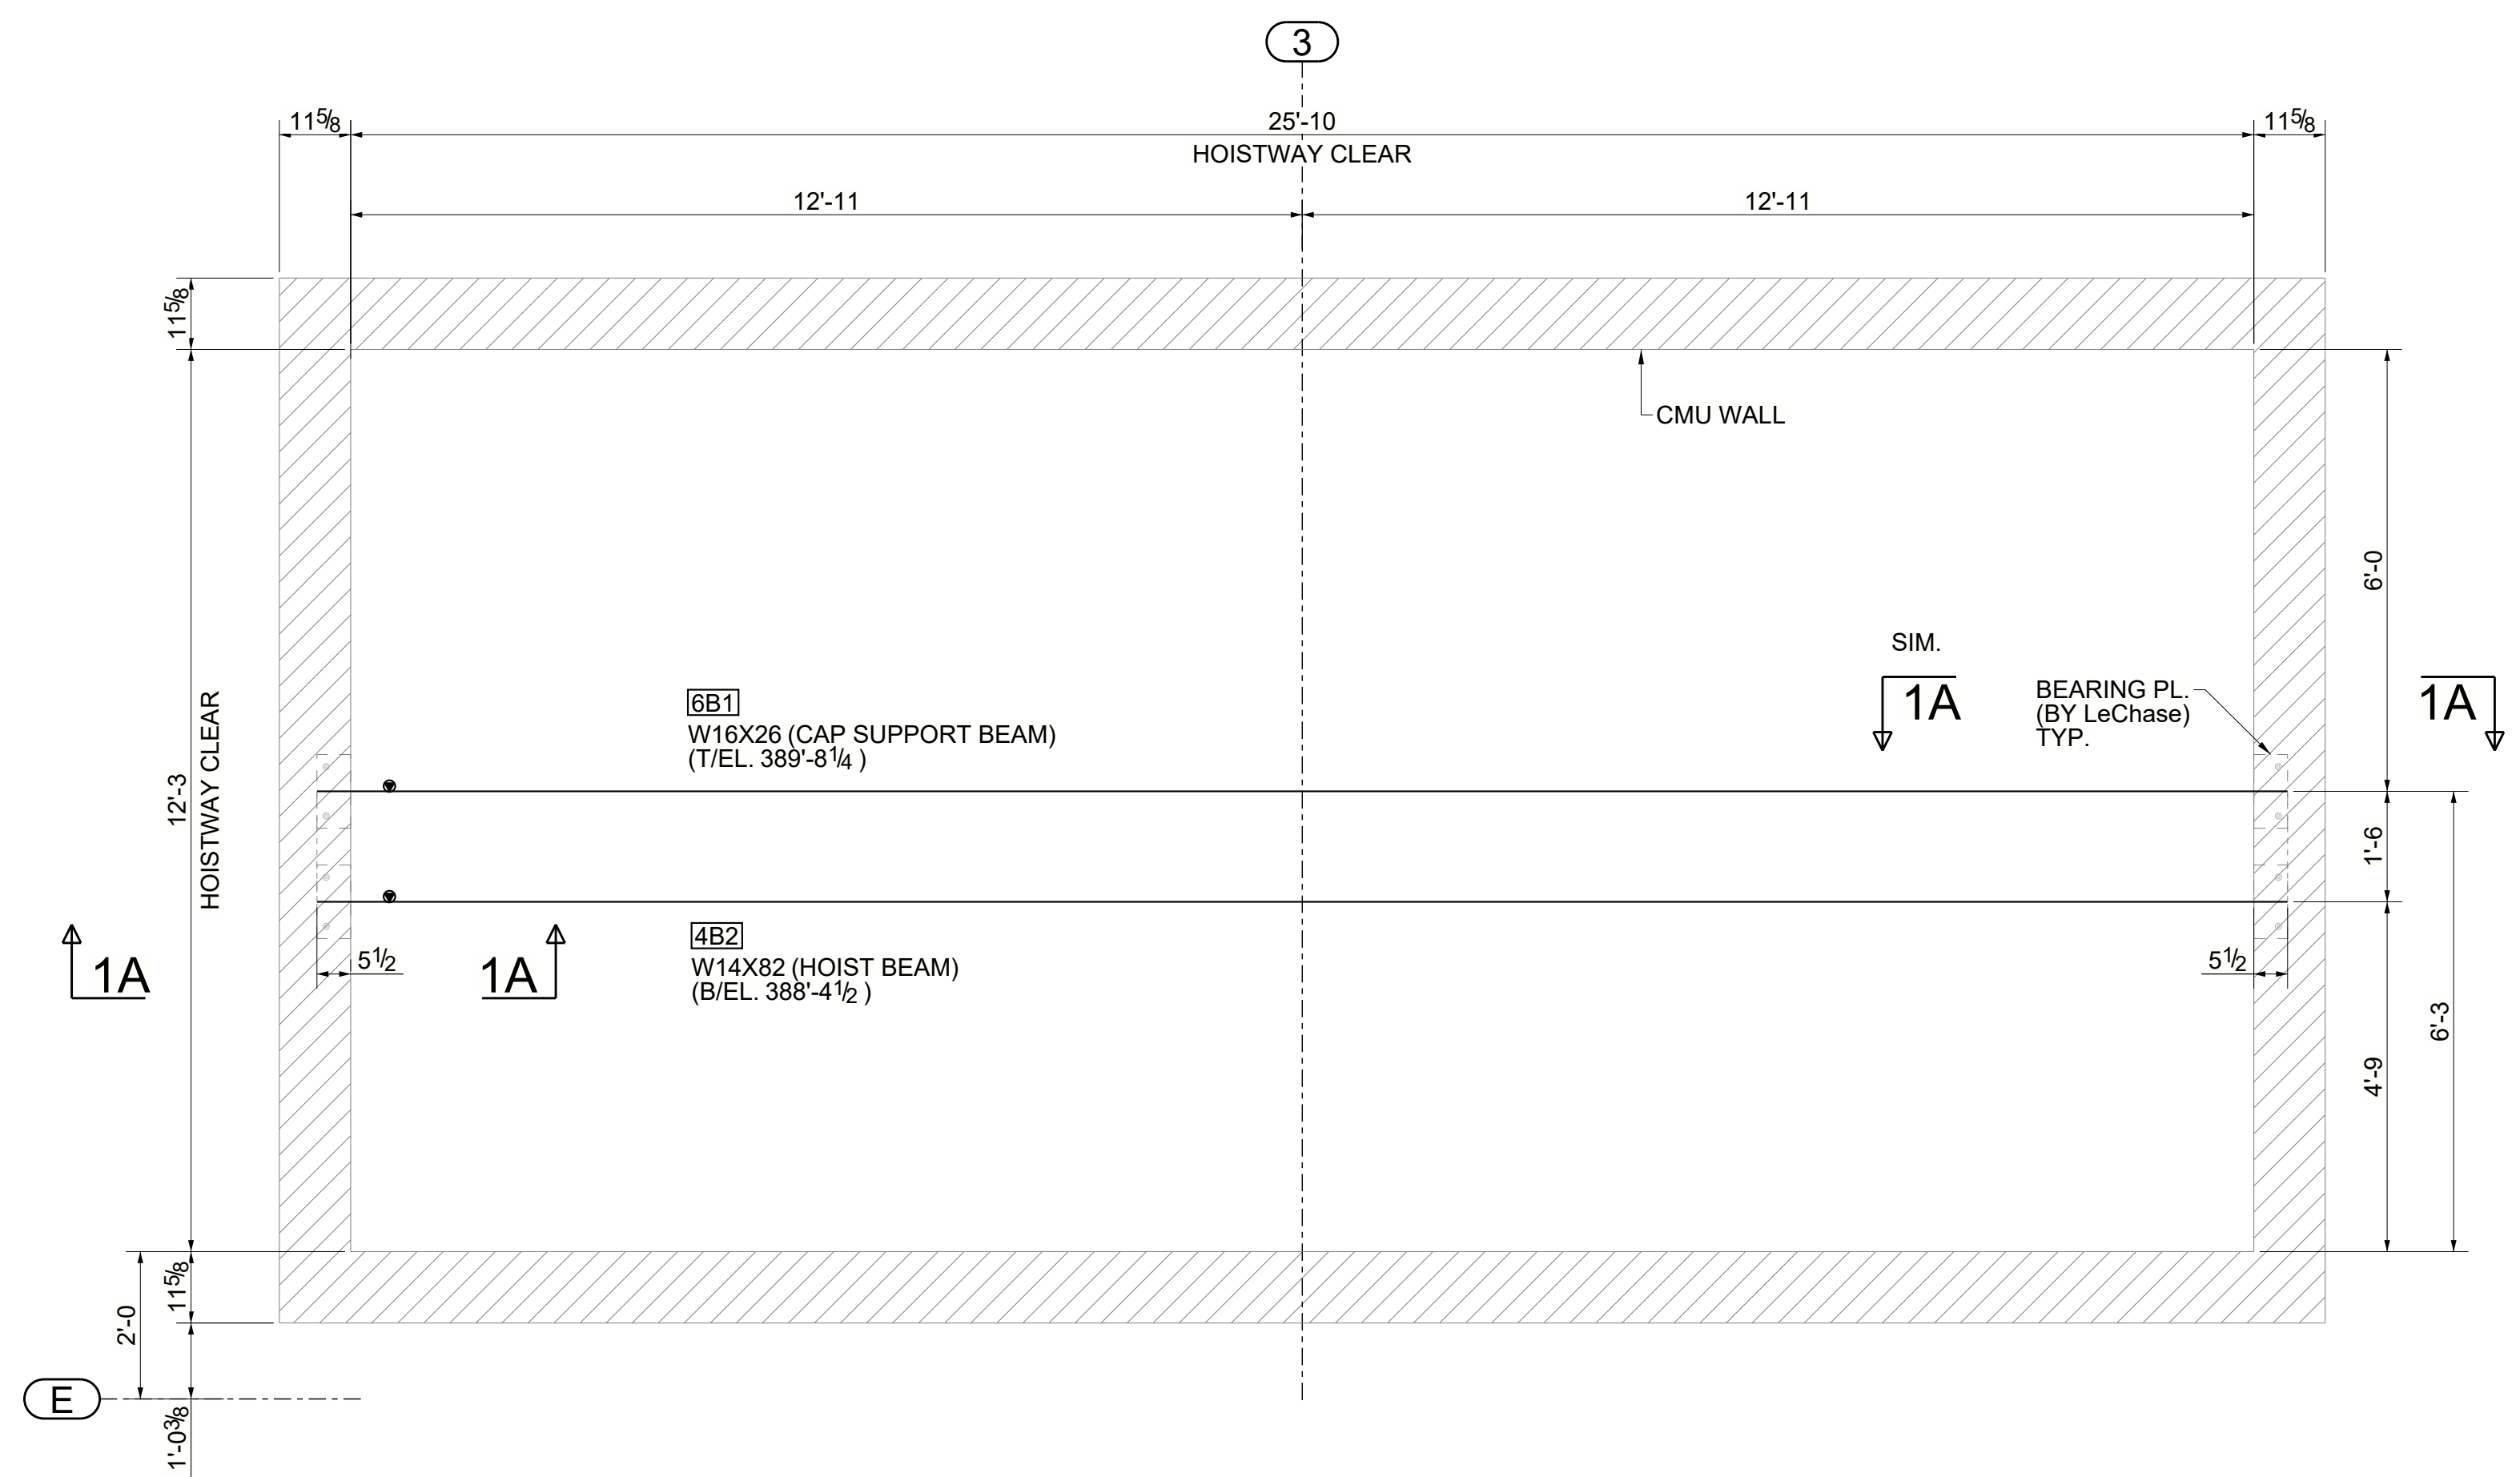


SERVICE ELEVATOR -HOISTWAY BEAM LOCATION PLAN  
(REFER : SERVICE ELEVATORS -HOISTWAY CAP PLAN - 3/A644-A5300301 & A644-S3000004)

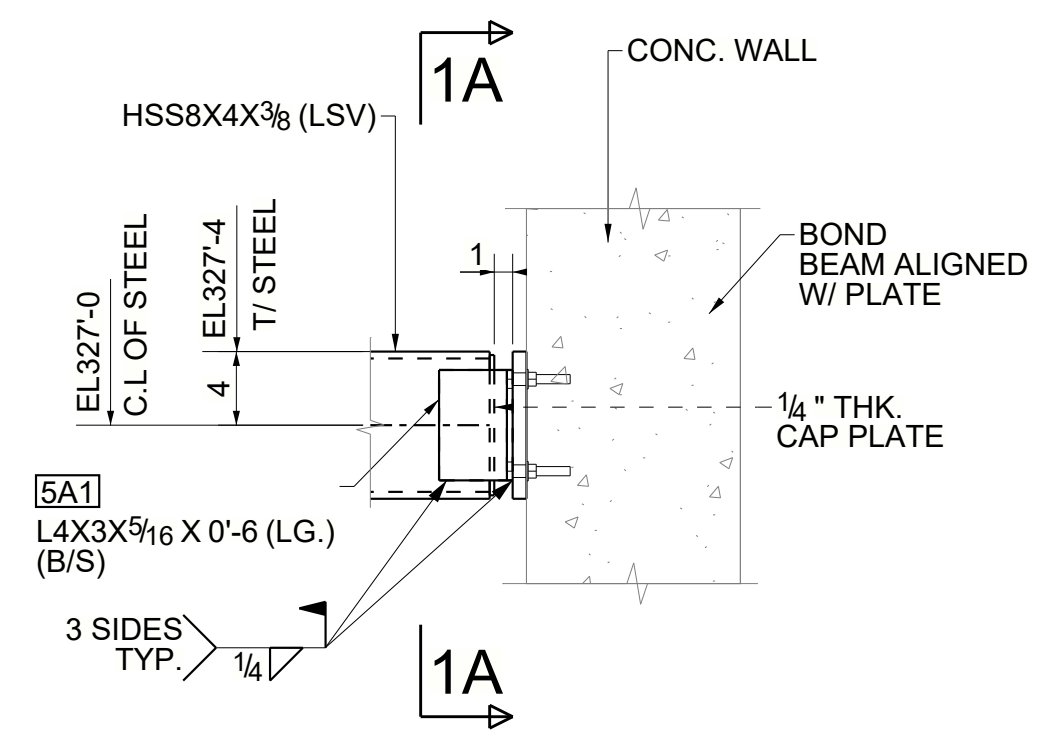


DETAIL 1  
(REFER : SECTION-5/ A644-S3000004)

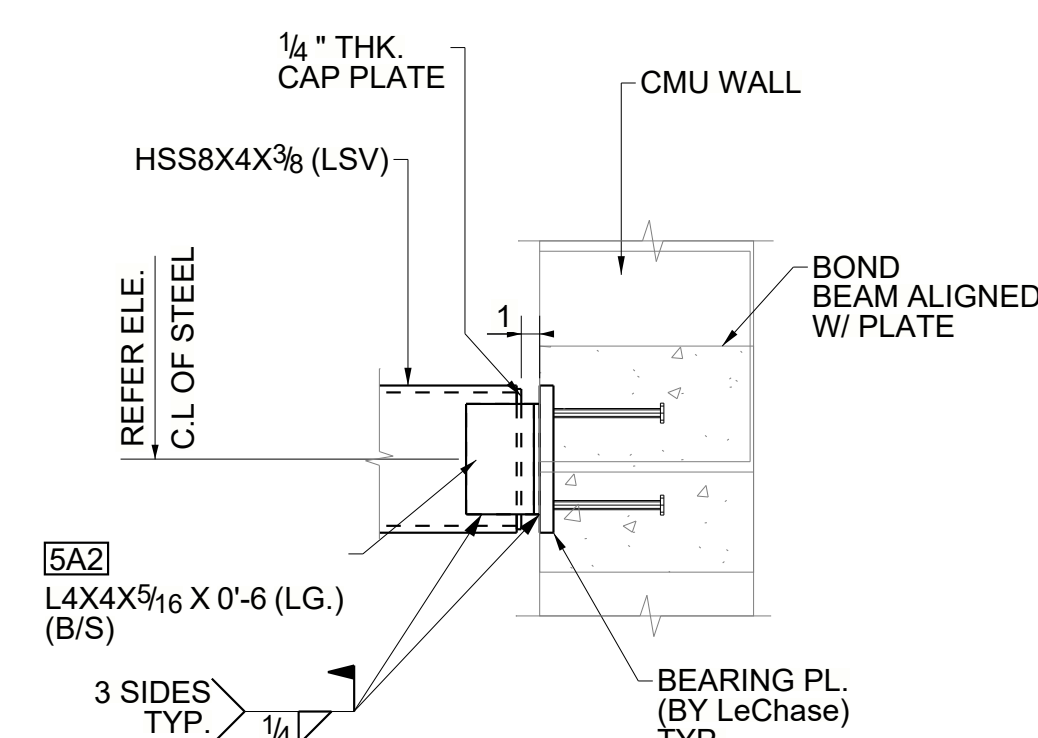

DETAIL 2  
(REFER : SECTION-5/ A644-S3000004)

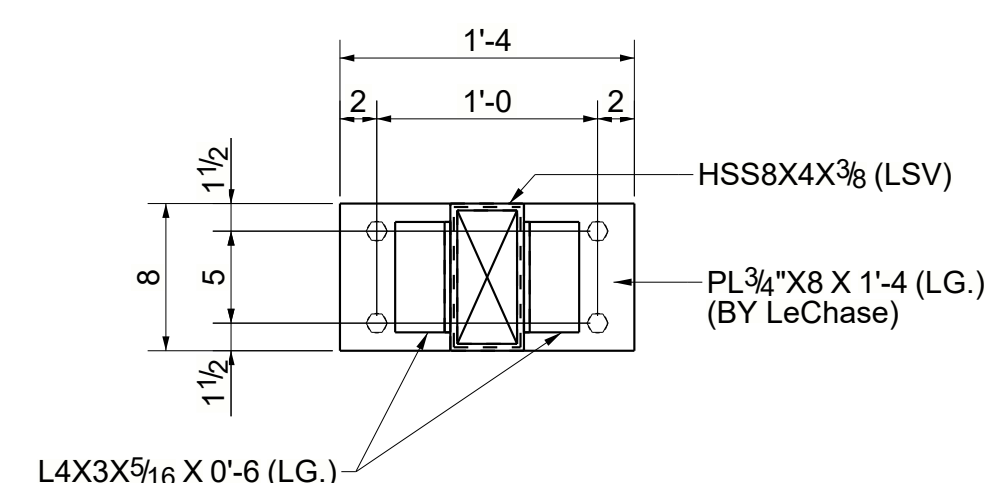

SECTION 1A - 1A

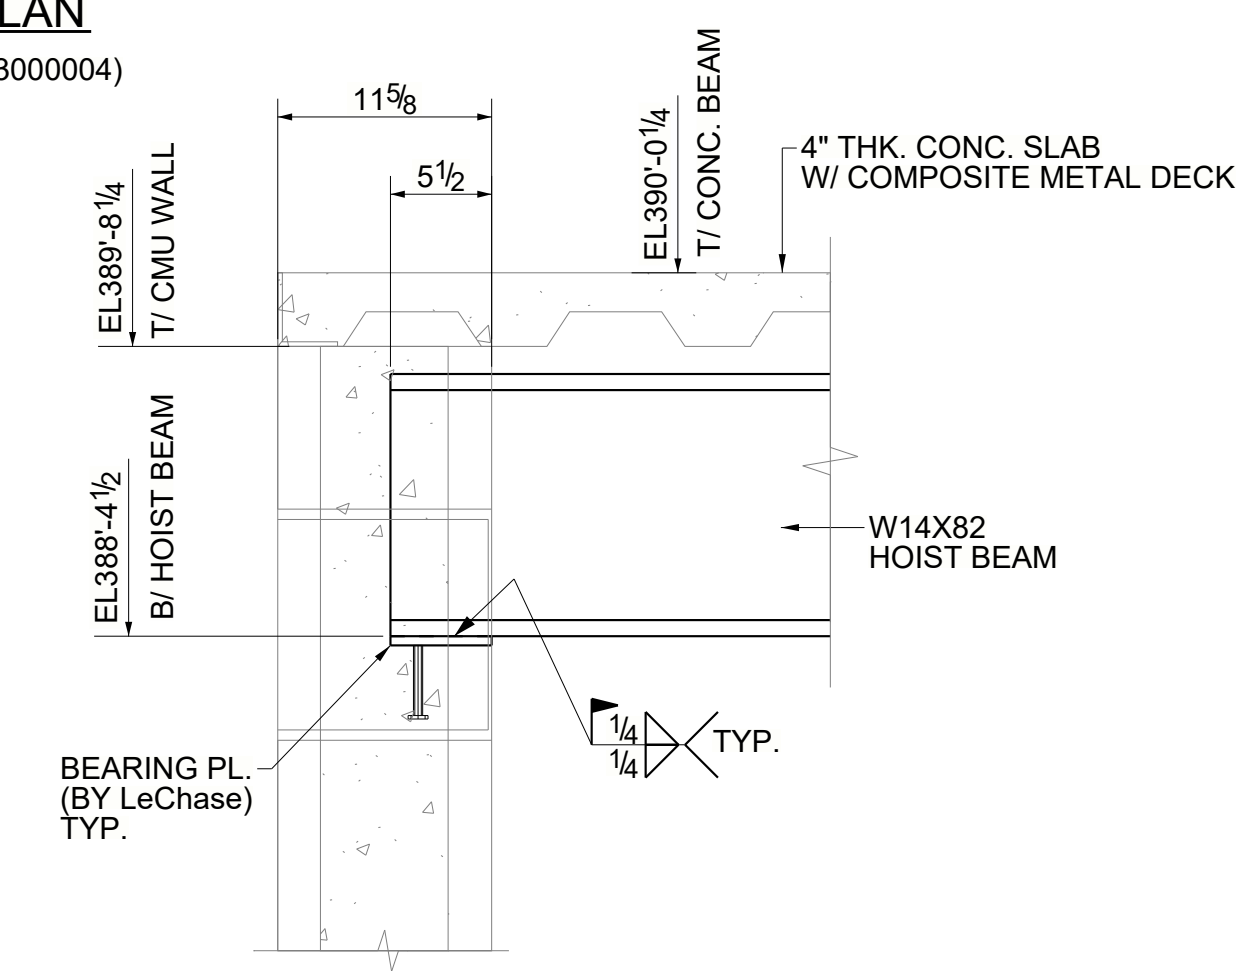


SECTION 1A - 1A  
(REFER : SECTION-3/ A644-S3000004)

NOTE !  
AT HOIST BEAM LOCATIONS REMOVE BOND BEAM SIDE WALL SUFFICIENT TO ALLOW INSTALLATION OF BEAM. FORM AND FILL ERECTION VOID IN BOND BEAM WITH GROUT FOLLOWING BEAM PLACEMENT


FINISH NOTE :  
ALL ELEVATOR STEEL MEMBERS SHALL RECEIVE ONE SHOP COAT PRIMER.  
CAP SUPPORT (FIREPROOFED) BEAM TO BE "NO PAINT"

FIREPROOFING NOTE FOR CAP SUPPORT BEAM :  
OMIT FIREPROOFING ON TOP SURFACE OF TOP FLANGE. COORDINATE WITH ELEVATOR VENDOR FOR TIMING OF INSTALLATION OF FIREPROOFING AND RAIL BRACKETS.




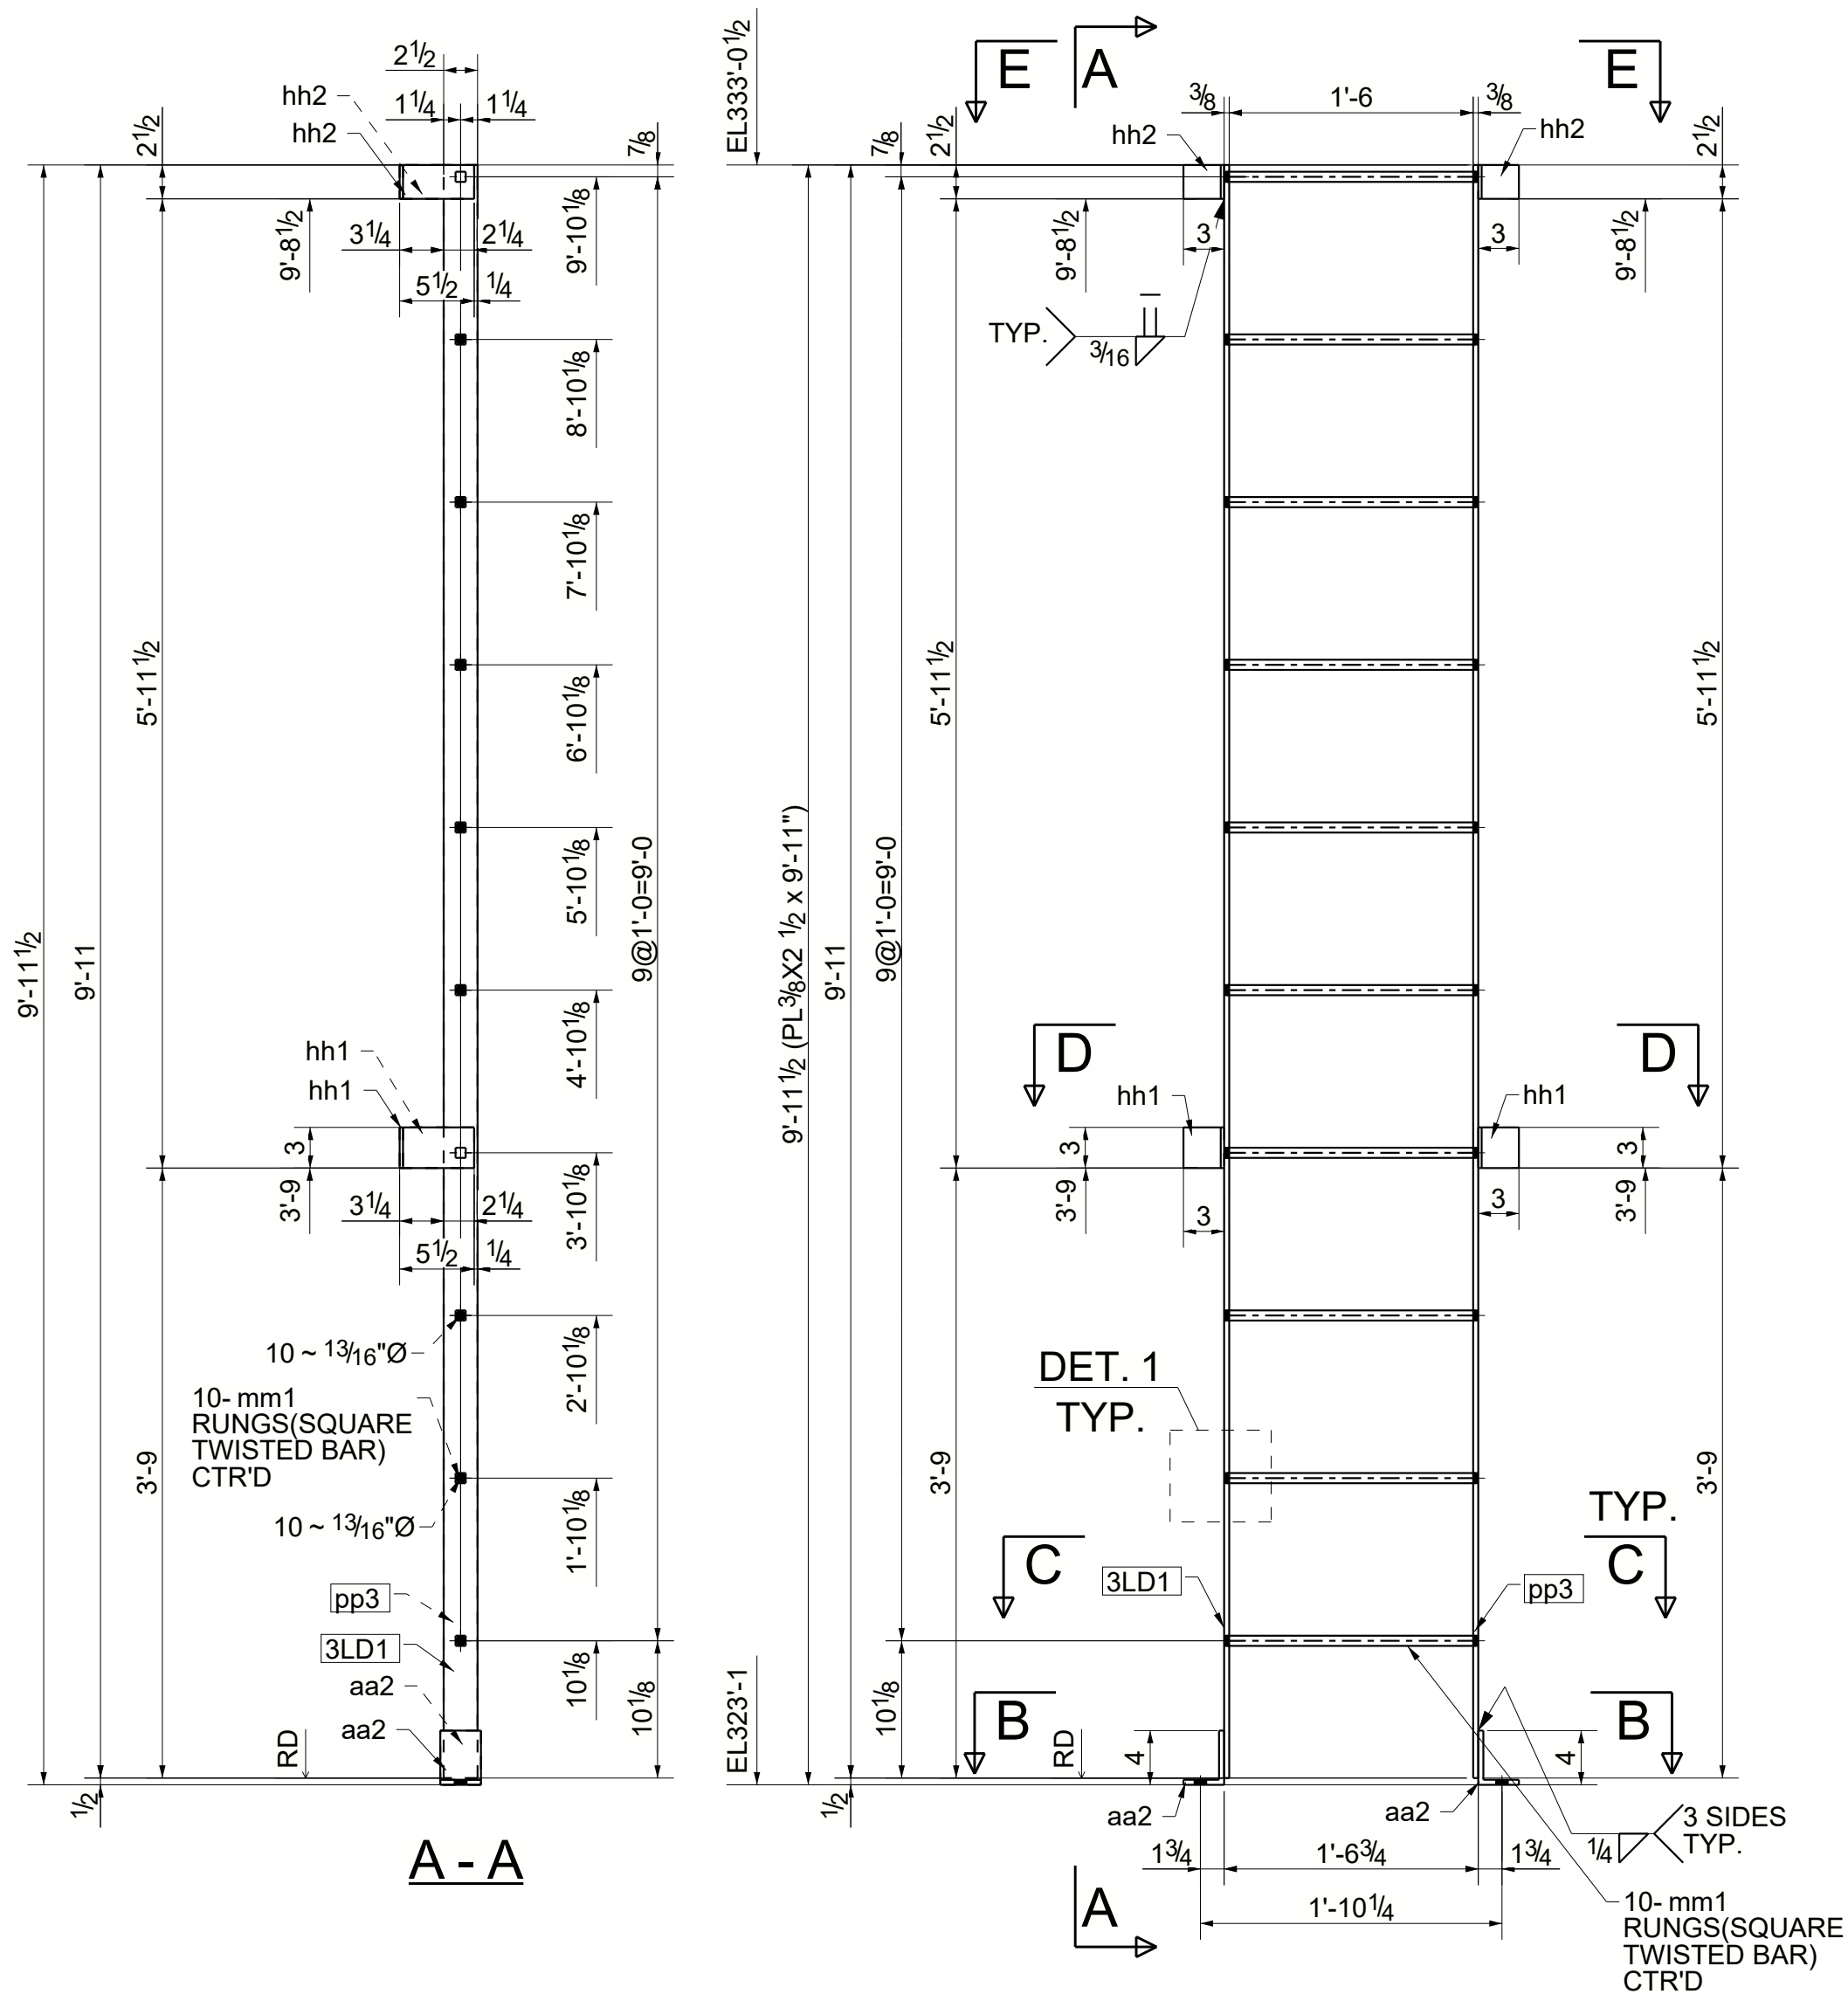


2 - LADDERS - 3LD1

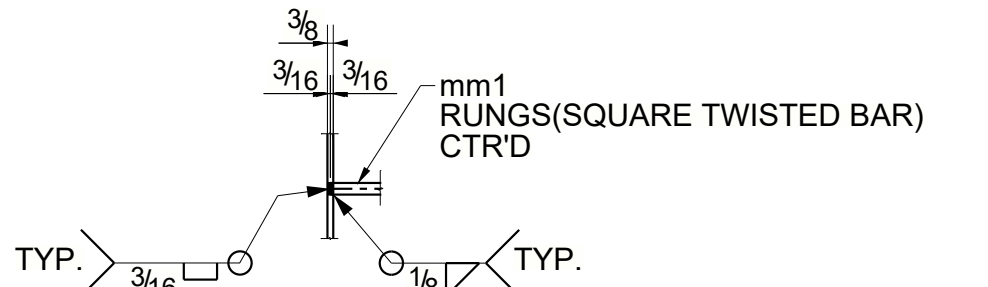


DETAIL 1

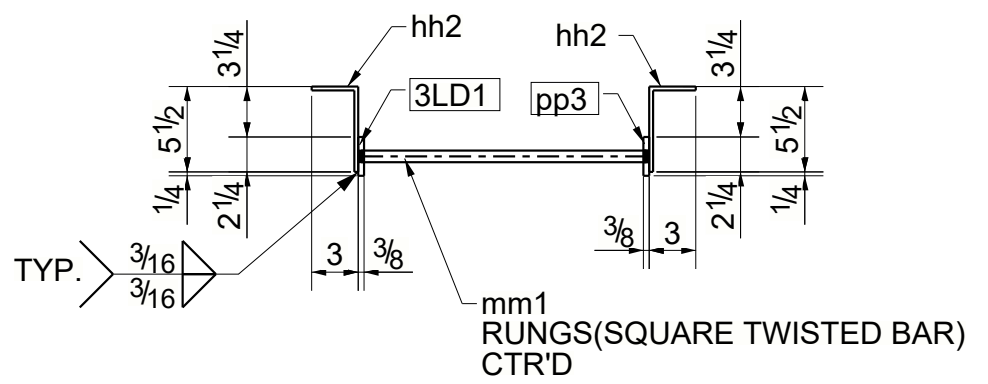


E - E

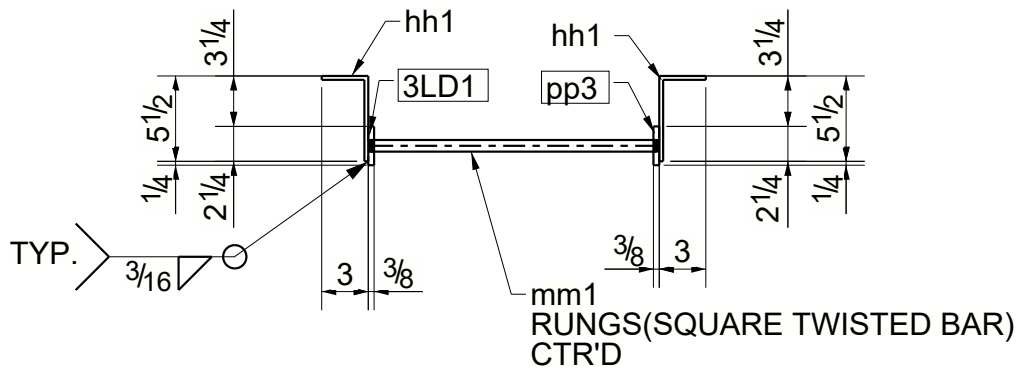

D - D

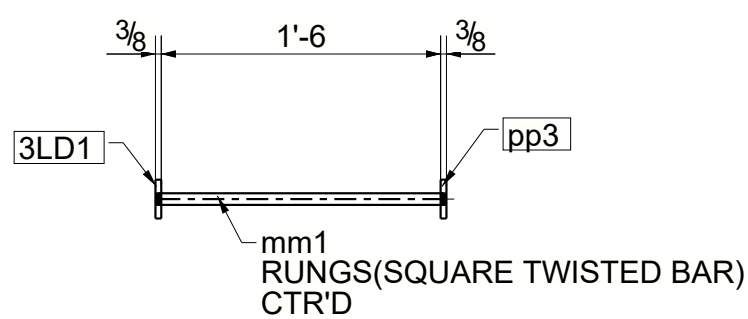

C - C

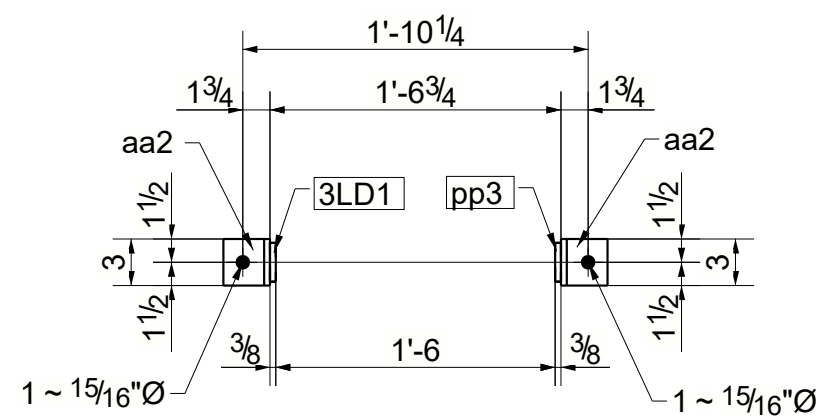


B - B

## BILL OF MATERIAL


| MARK                      | QTY | DESCRIPTION   | LENGTH    | WEIGHT | REMARKS   |
|---------------------------|-----|---------------|-----------|--------|-----------|
| 3LD1                      | 2   | LADDERS       |           |        | SQ-2      |
| 3LD1                      | 2   | PL3/8"X2 1/2" | 9'-11"    | 63     | GALV. A36 |
| aa2                       | 4   | L4X3X3/8      | 0'-3"     | 8      | GALV. A36 |
| hh1                       | 4   | PL1/4"X3"     | 0'-8"     | 7      | GALV. A36 |
| hh2                       | 4   | PL1/4"X2 1/2" | 0'-8"     | 6      | GALV. A36 |
| mm1                       | 20  | PL3/4"X3/4"   | 1'-6 3/8" | 59     | GALV. A36 |
| pp3                       | 2   | PL3/8"X2 1/2" | 9'-11"    | 63     | GALV. A36 |
| TOTAL WEIGHT THIS DRAWING |     |               |           | 207    |           |

- SHOP NOTES :
1. ALL WELDS TO BE 3/16" ALL AROUND OR DOUBLE SIDED FILLET WELD UNLESS SHOWN OTHERWISE.
  2. TAG ALL MEMBERS IN A VERTICAL POSITION ON LEFT END AS DETAILED.
  3. ALL SHARP EDGES SHALL BE GROUND SMOOTH AND CORNERS ROUNDED OFF.
  4. ALL TAIL (RUNNING) DIMENSIONS SHALL BE MEASURED FROM END OF BEAM, COLUMN,..ETC.
  5. ALL COPIES SHALL BE MEASURED FROM END OF BEAM.
  6. ALL CLIP ANGLES SHALL BE ATTACHED TO BEAM WITH 3/16" FILLET WELD ON THREE SIDES UNLESS SHOWN OTHERWISE.
  7. FOR INDIVIDUAL DETAILS OF PLATES, ANGLES, ETC..., SEE SINGLE PART SHEET DETAILS.
  8. ALL JOINTS TO BE SEAL WELDED WITH CONT. 1/8 FILLET OR BUTT WELD AS REQ'D.
  9. ALL COPE CORNERS ARE 1/2" RADIUS U.N.O
  10. ALL JOINTS TO BE SEAL WELDED WITH CONT. 1/8 FILLET OR BUTT WELD AS REQ'D
  11. PROVIDE VENT HOLES AS REQ'D FOR GALV.
  12. PLUG VENT HOLES AFTER GALV.


GENERAL SHOP NOTES:  
MATERIAL: WIDE FLANGE SHAPES = A992  
HSS MATERIALS = A500 GRADE C  
CHANNEL = A36  
ANGLE = A36  
PLATE = A36 U.N.O  
ALL OTHER MATERIAL: A36  
WELD: E70XX  
SURFACE PREP: PER SPECS  
PAINT : HOT DIP GALVANIZED U.N.O

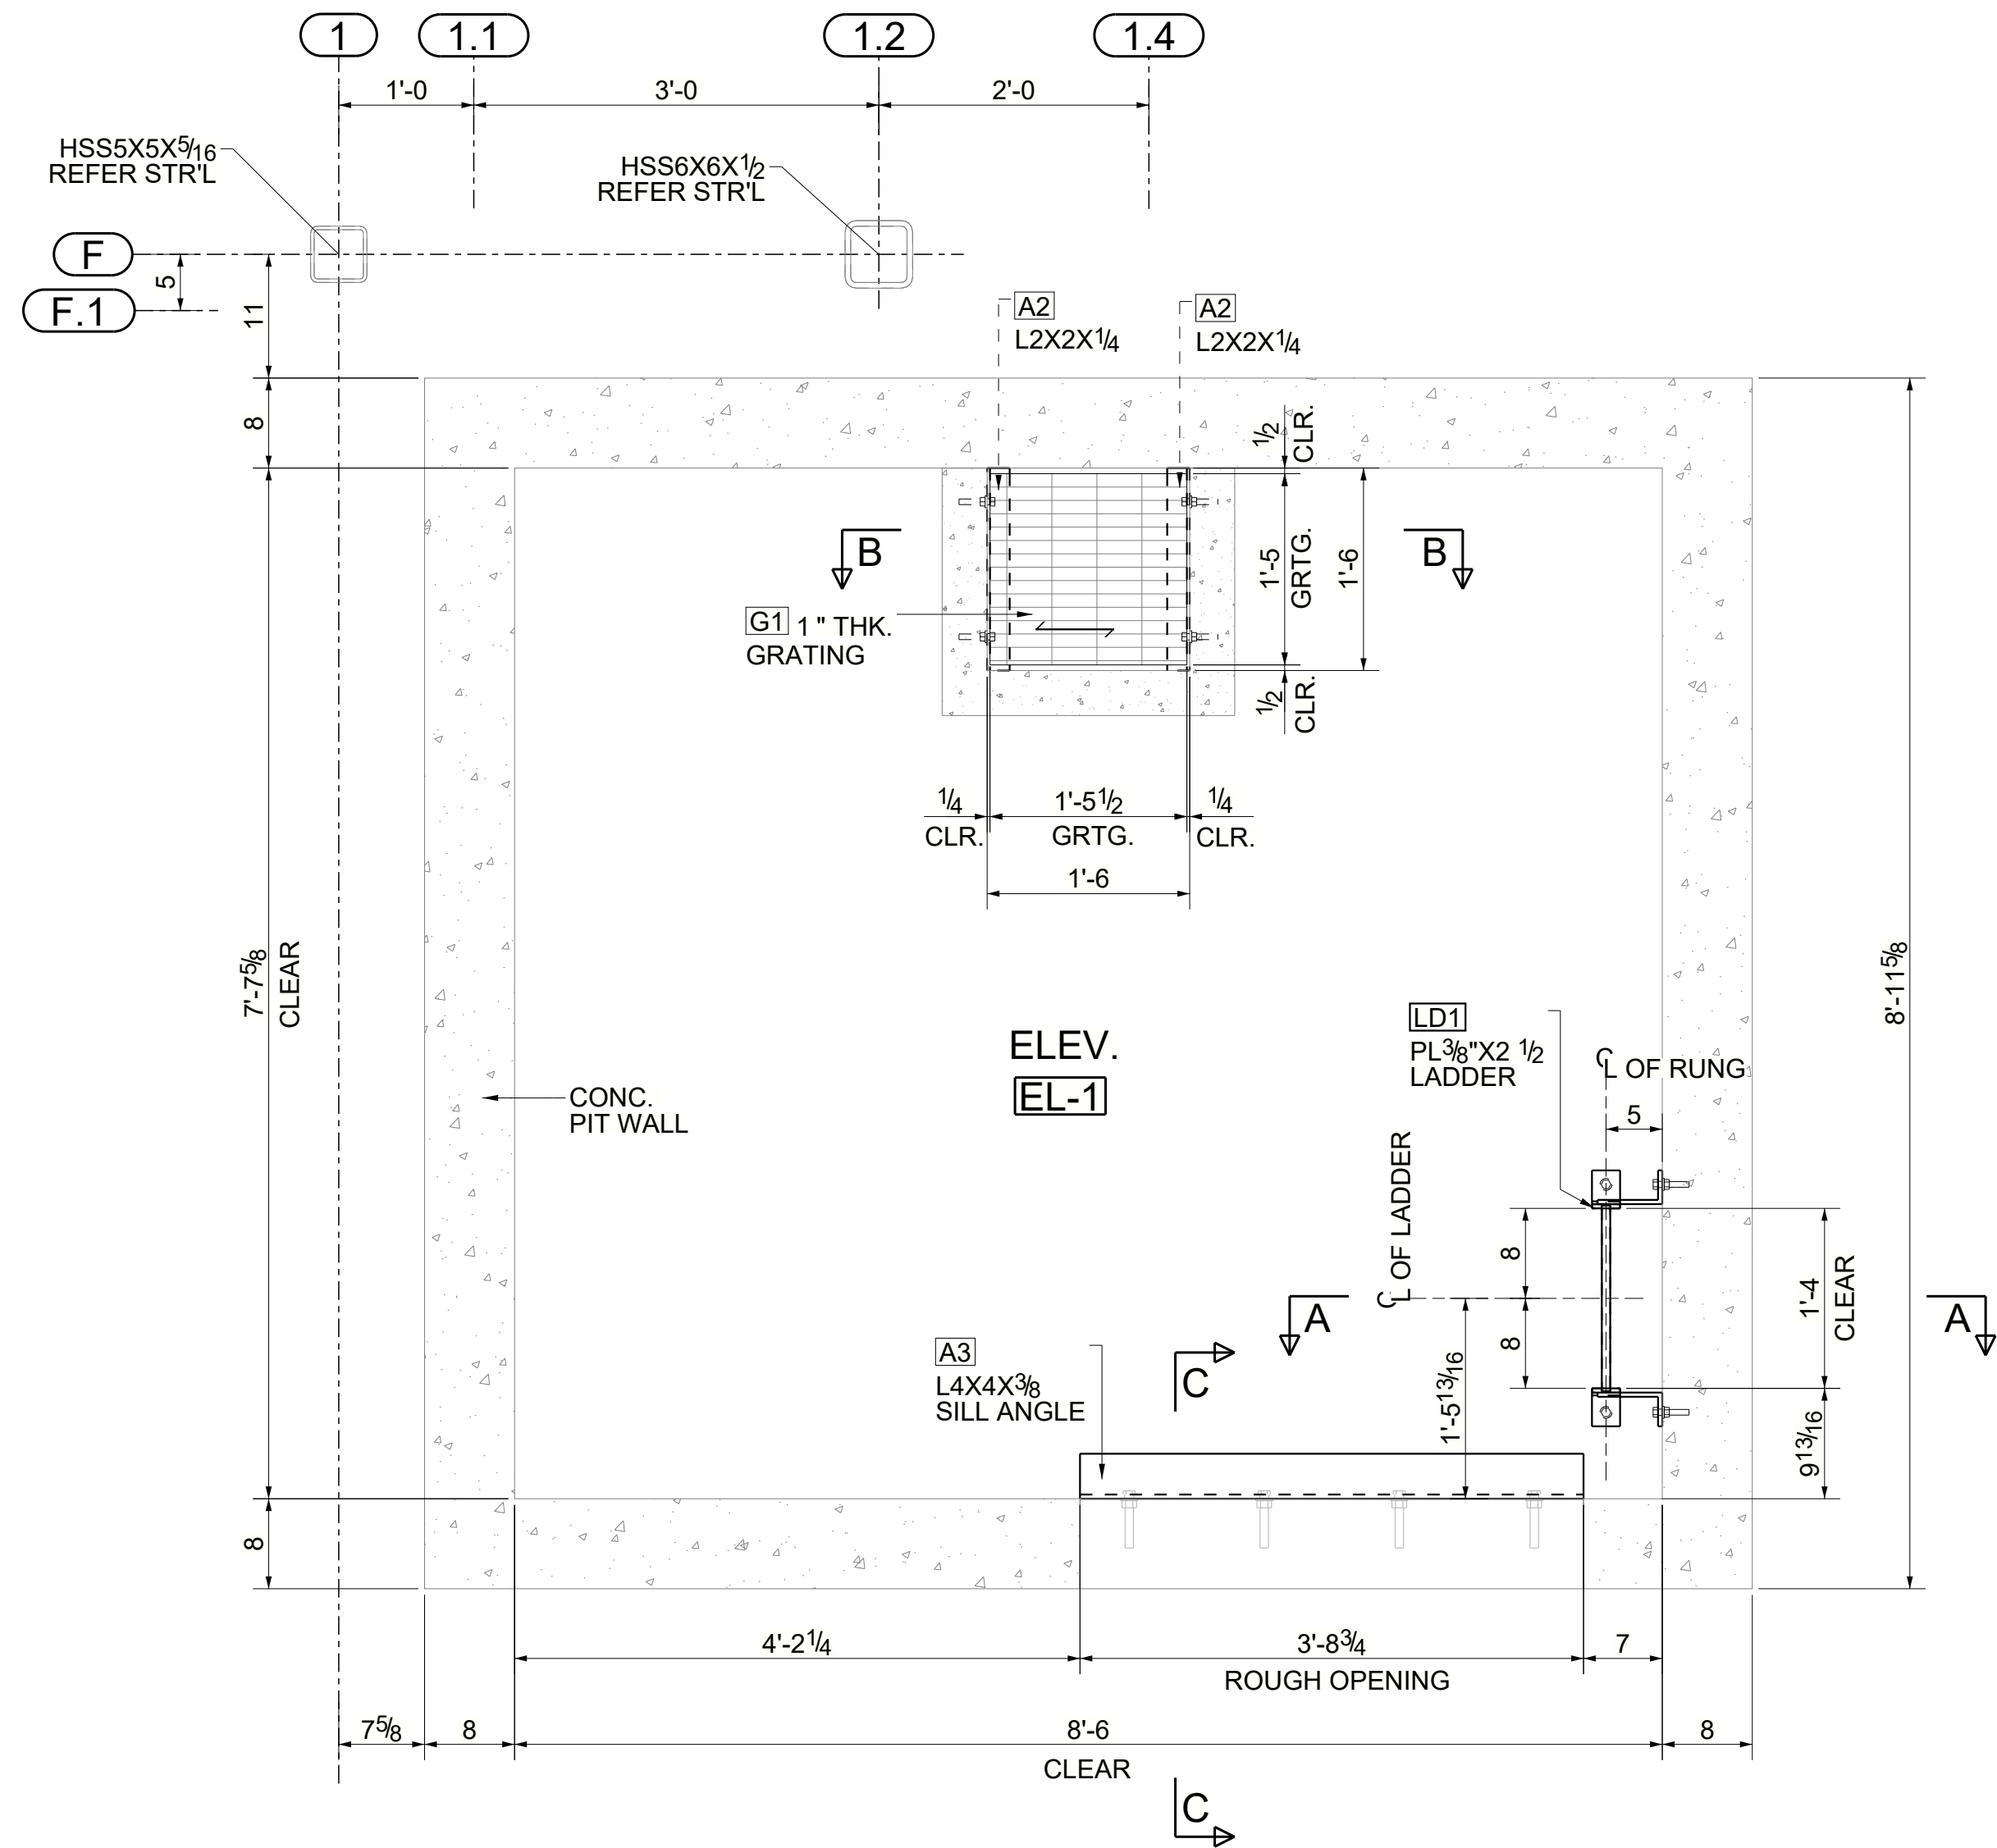



ELEVATOR PIT LADDER AND SUMP PIT GRATING LOCATION PLAN  
(REFER : ELEVATED ENLARGED PLAN - GROUND LEVEL/ 1/A710)

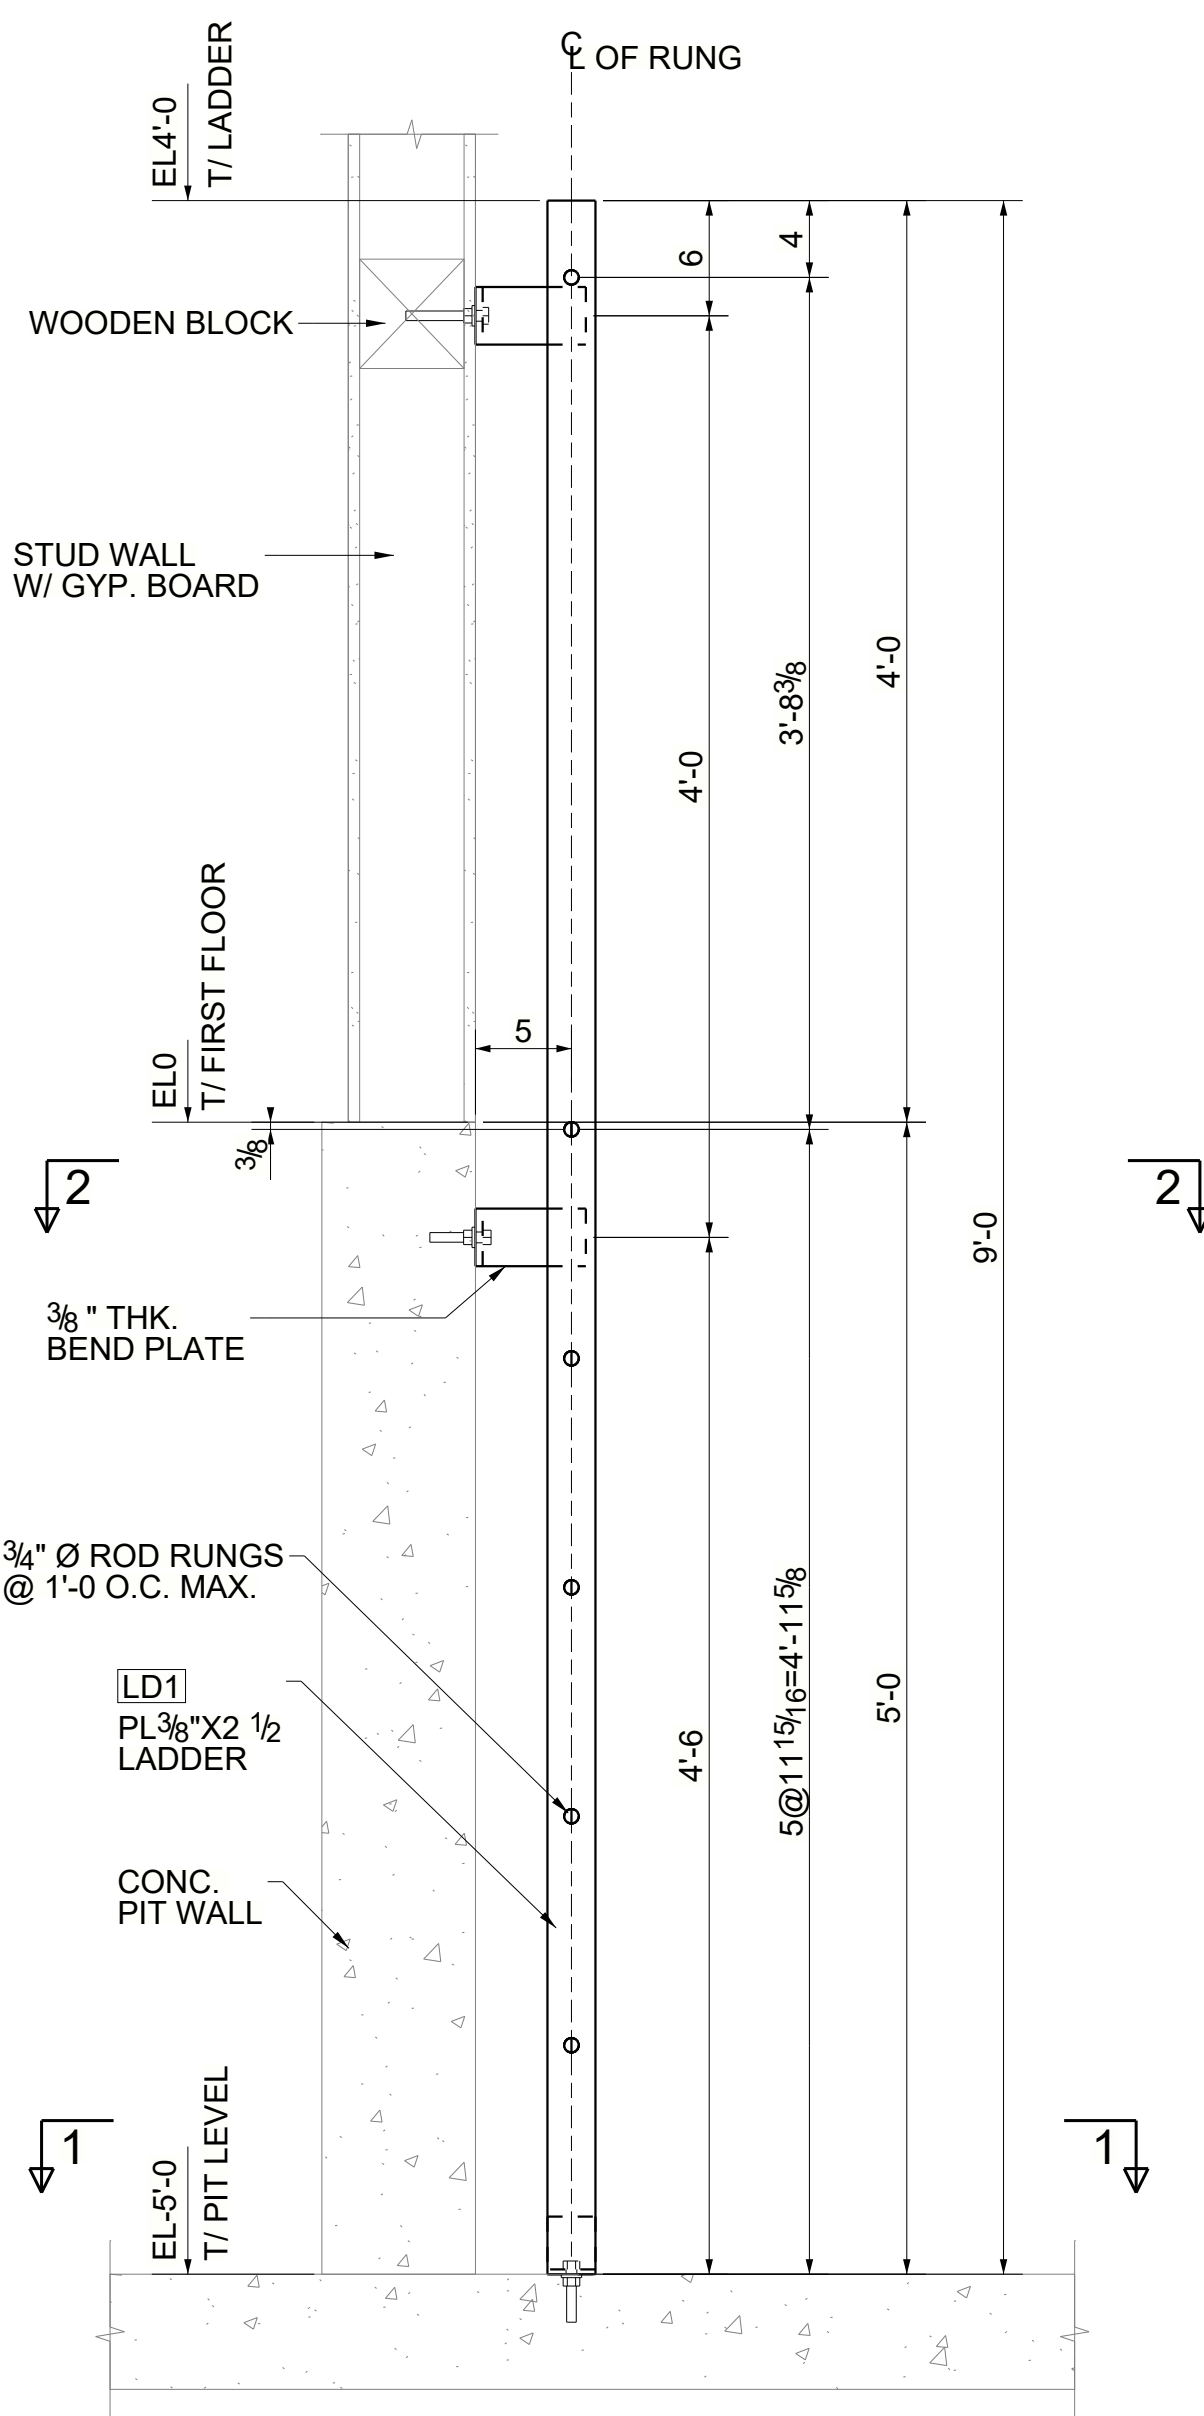


SECTION A - A

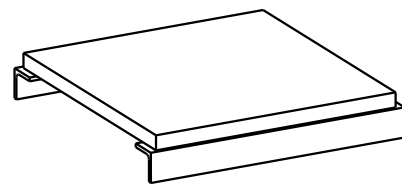


3D VIEW - ELEVATOR PIT LADDER & GRATING

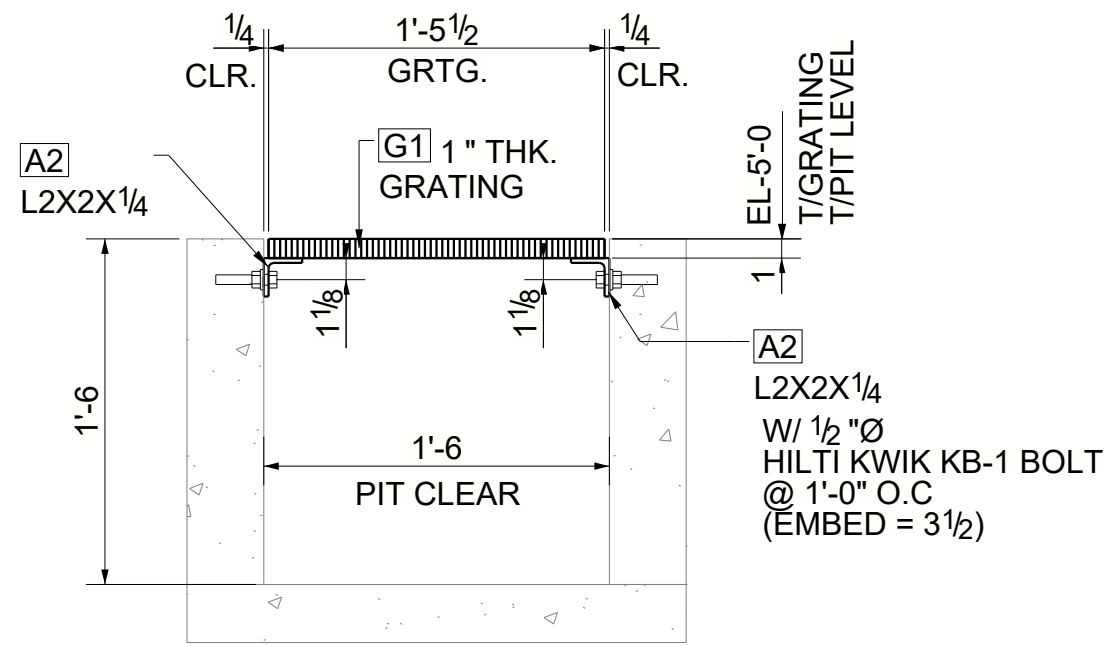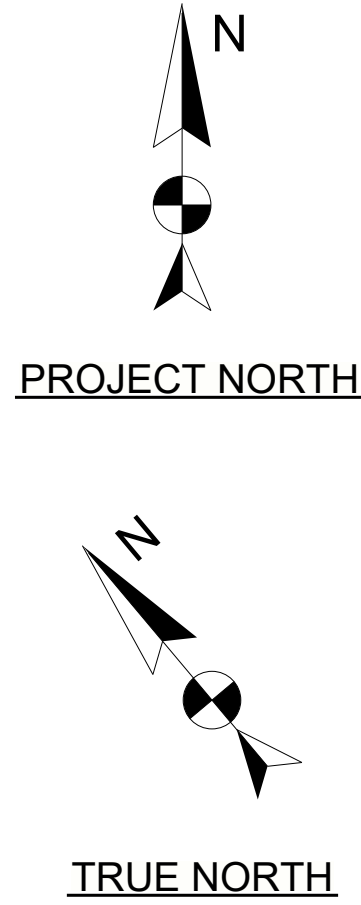


SECTION B - B

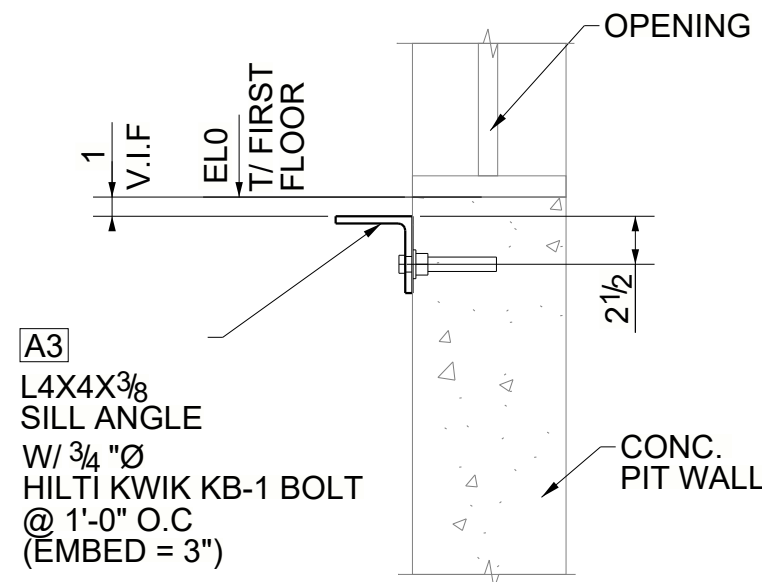


SECTION C - C

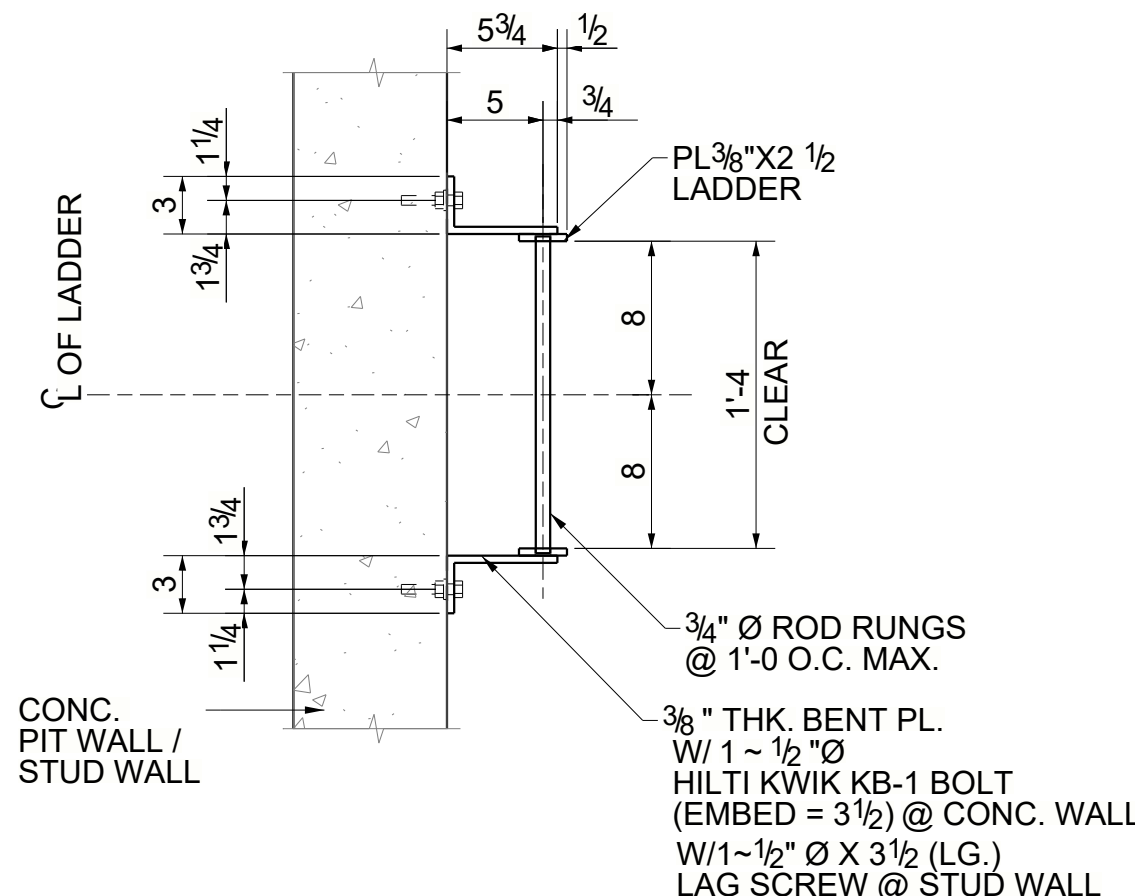

SECTION 2 - 2

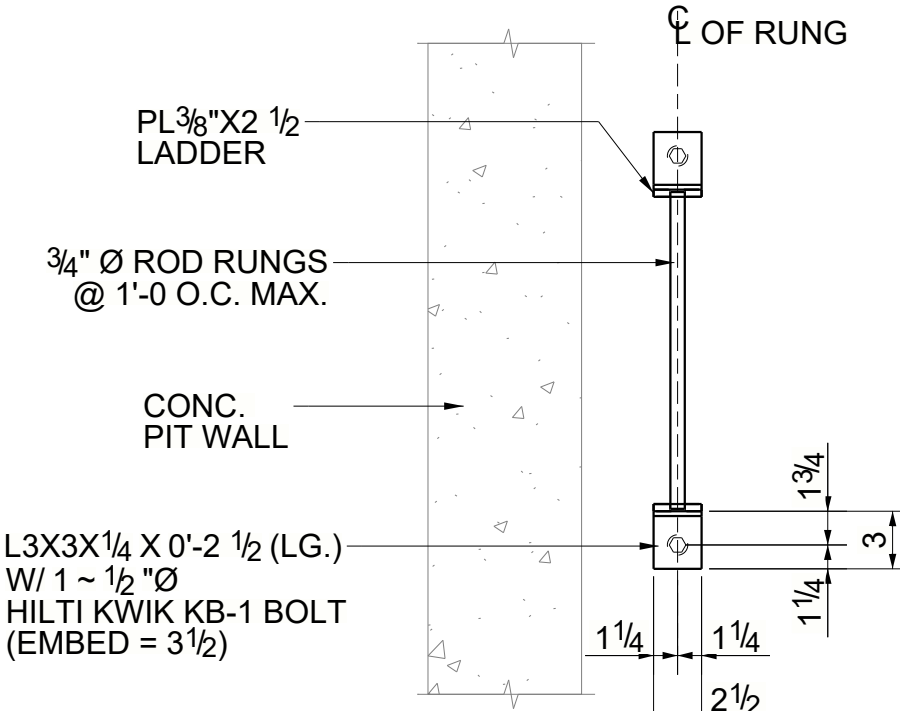

SECTION 1 - 1

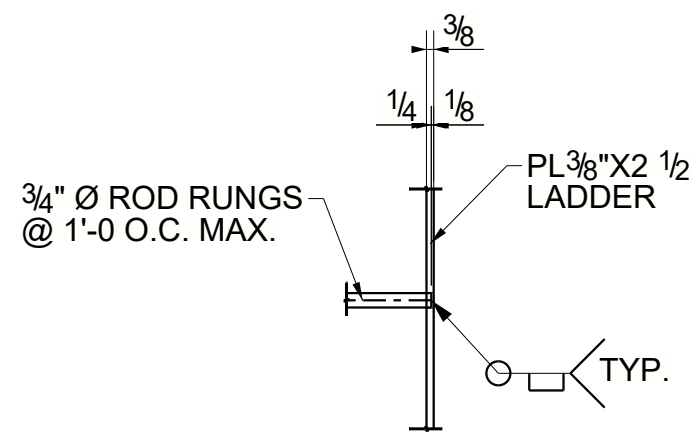

TYPICAL RUNG DETAIL

- NOTES:-
- 1.REFER SHEET E400 FOR MISC. KEY PLAN.
  2. ALL RUNGS TOP SURFACE TO BE NON-SLIP.
  3. V.I.F - INDICATES VERIFY IN FIELD.

GRATING NOTES :


GRATING SHALL BE PRIMED, 19-W-4, 1 X 3/16 WELDED TYPE PLAIN BAR GRATING (SMOOTH SURFACE.)

BEARING BARS SPACING @ 13 1/16 O.C AND CROSS BAR SPACING @ 4\" O.C

FINISH NOTE :

ALL PIT LADDER, SILL ANGLE AND SUMP PIT ANGLE STEEL MEMBERS IN THIS SHEET SHALL RECEIVE ONE SHOP COAT PRIMER.

ALL GRATING SECTIONS IN A SINGLE STRAIGHT RUN TO HAVE CROSS BARS THE SAME DISTANCE FROM COMMON EDGE(TYPICAL)

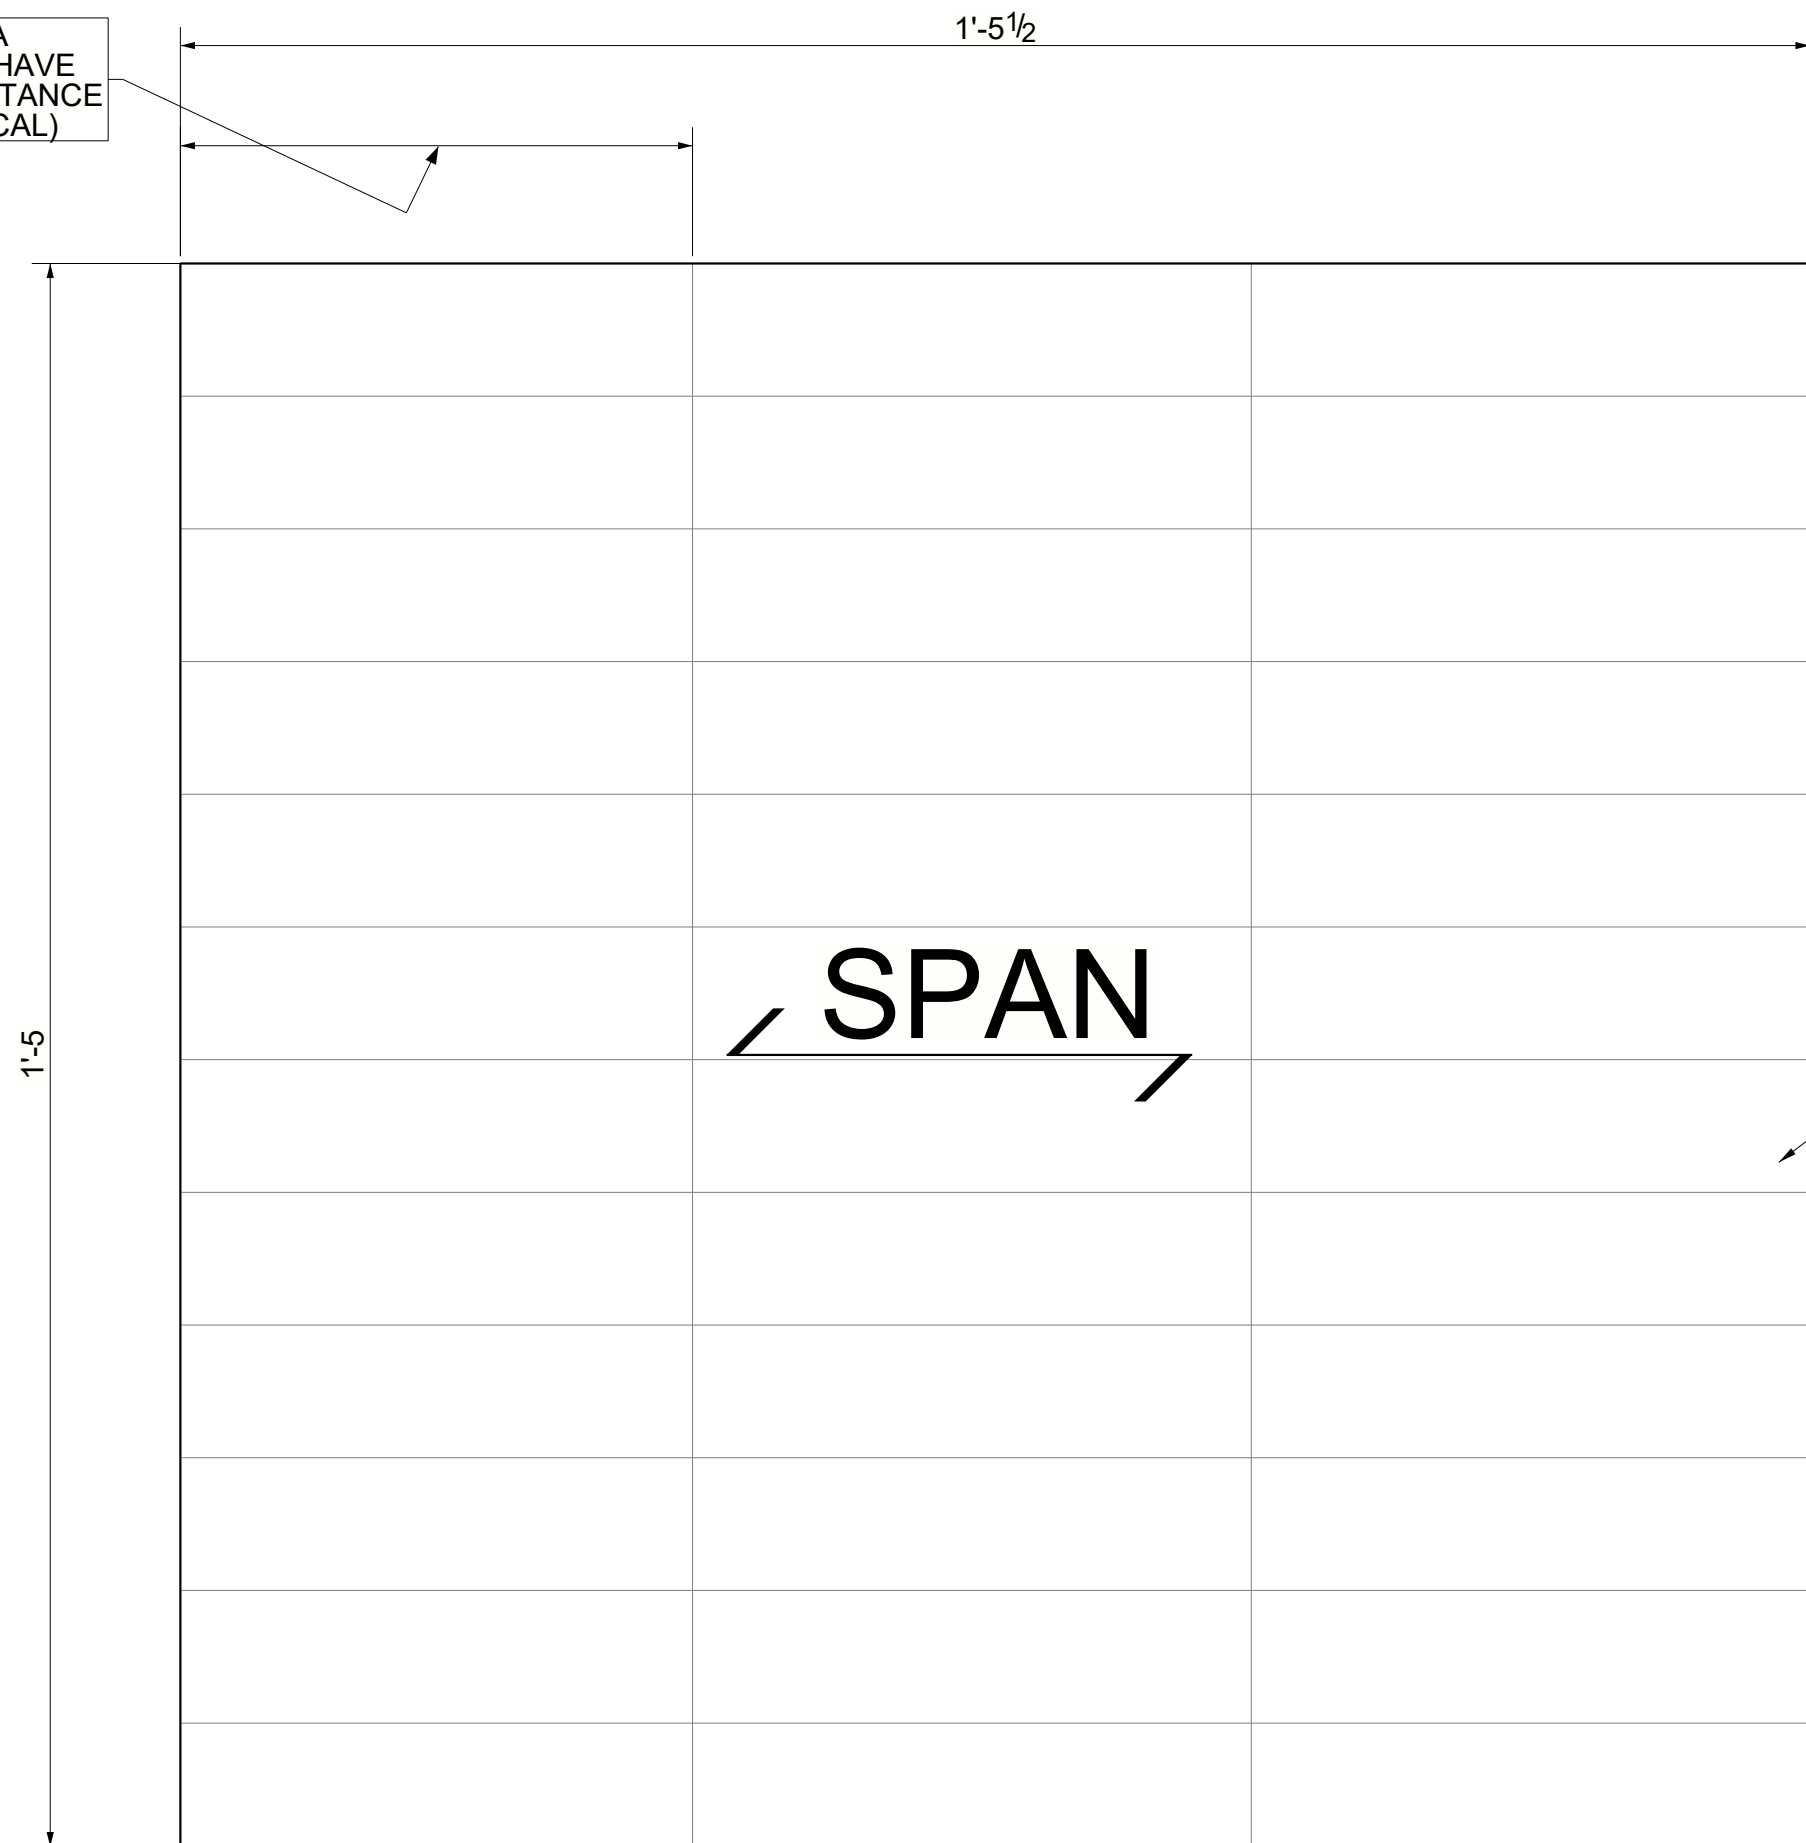


G1  
19-W-4 SMOOTH SURFACE GRATING  
GRTG1\"/>

- SHOP NOTES:
1. ALL WELDS TO BE 3/16" ALL AROUND OR DOUBLE SIDED FILLET WELD UNLESS SHOWN OTHERWISE.
  2. TAG ALL MEMBERS IN A VERTICAL POSITION ON LEFT END AS DETAILED.
  3. ALL SHARP EDGES SHALL BE GROUND SMOOTH AND CORNERS ROUNDED OFF.
  4. ALL TAIL (RUNNING) DIMENSIONS SHALL BE MEASURED FROM END OF BEAM, COLUMN,...ETC.
  - "RD" DENOTES RUNNING DIMENSION
  5. ALL COPEs SHALL BE MEASURED FROM END OF BEAM.
  6. ALL BEAM COPEs TO BE CUT WITH 1/2" RADIUS U.N.O.
  7. ALL CLIP ANGLES SHALL BE ATTACHED TO BEAM WITH 3/16" FILLET WELD ON THREE SIDES UNLESS SHOWN OTHERWISE.
  8. FOR INDIVIDUAL DETAILS OF PLATES, ANGLES, ETC... SEE SINGLE PARTS DETAIL SHEETS.
  9. SHOP CLOSE ALL GAPS.



| BILL OF MATERIAL |     |                           |           |        |         |
|------------------|-----|---------------------------|-----------|--------|---------|
| MARK             | QTY | DESCRIPTION               | LENGTH    | WEIGHT | REMARKS |
| G1               | 1   | GRATING                   |           |        | SQ-2    |
| G1               | 1   | GRTG1"X17"                | 1'-5 1/2" | 84     | A36     |
|                  |     | TOTAL WEIGHT THIS DRAWING |           | 84     |         |

ONE - GRATING - G1


| GRID LOCATION | BOTTOM ELEVATION |
|---------------|------------------|
| 1.4-2***      | -5'-0"           |

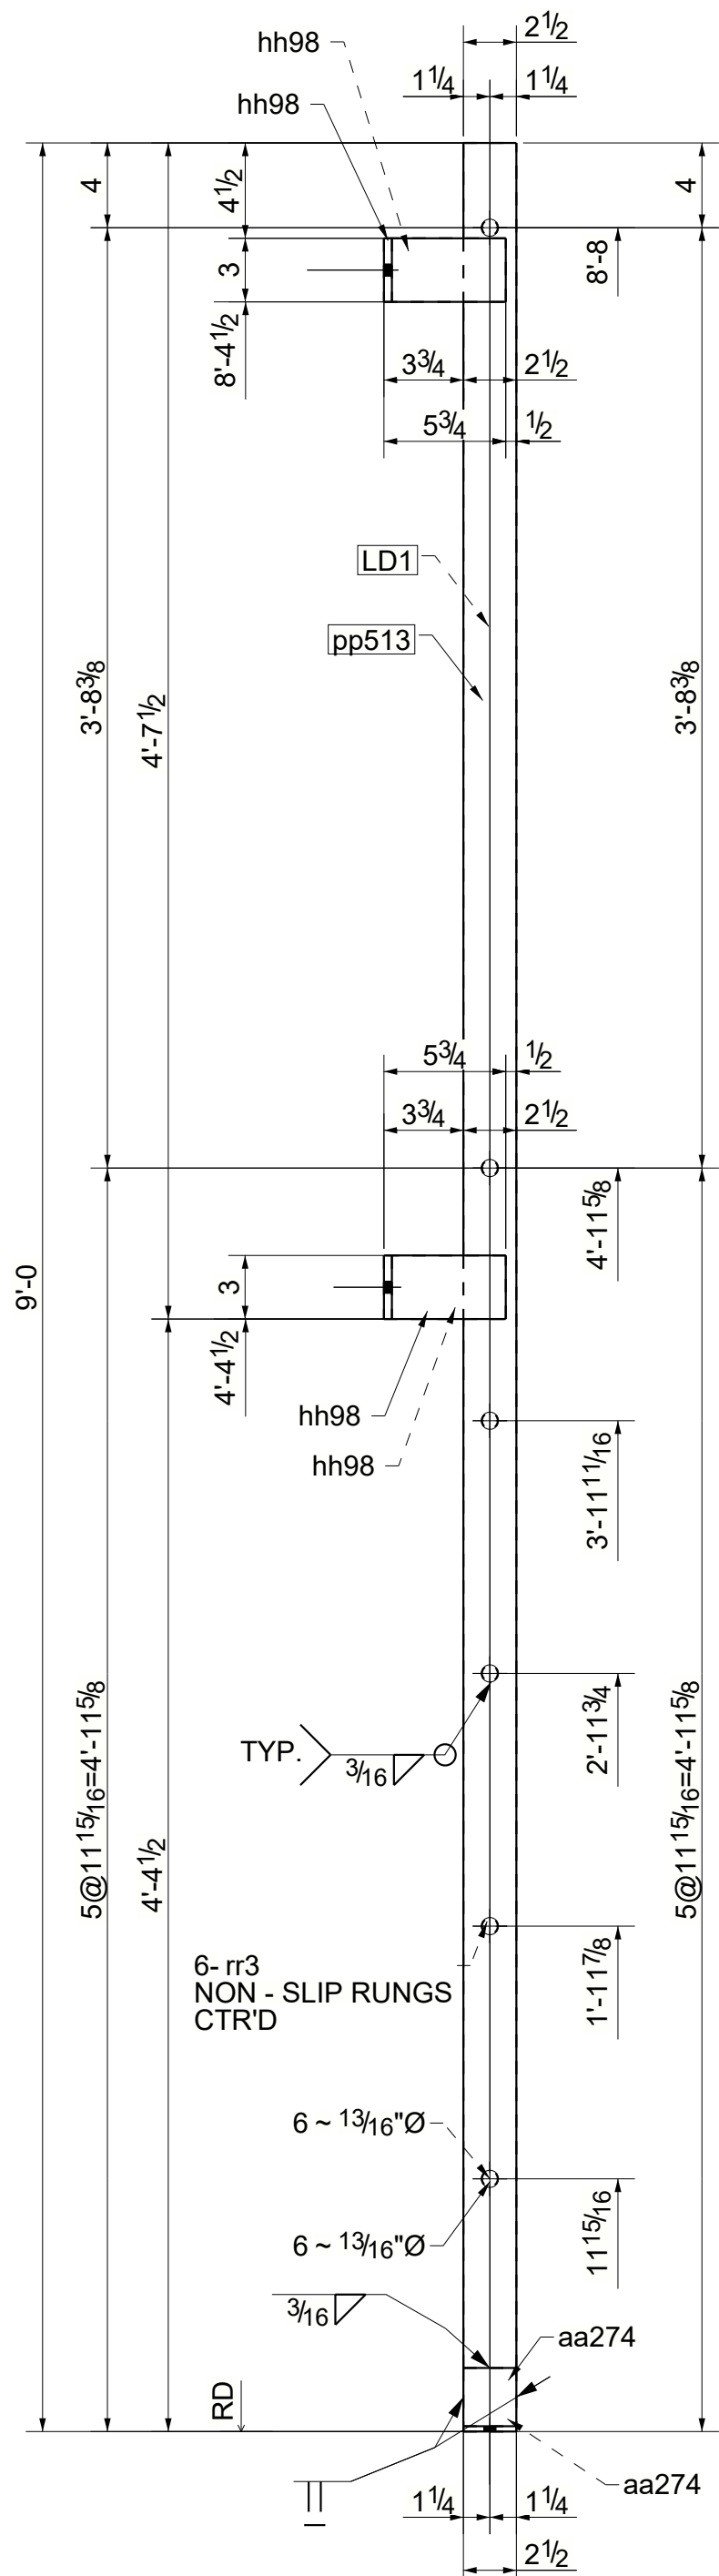


A - A

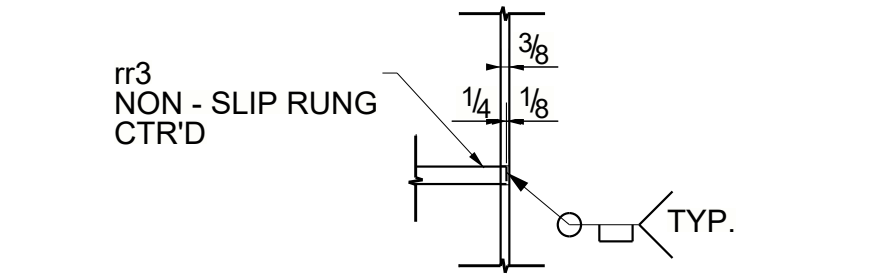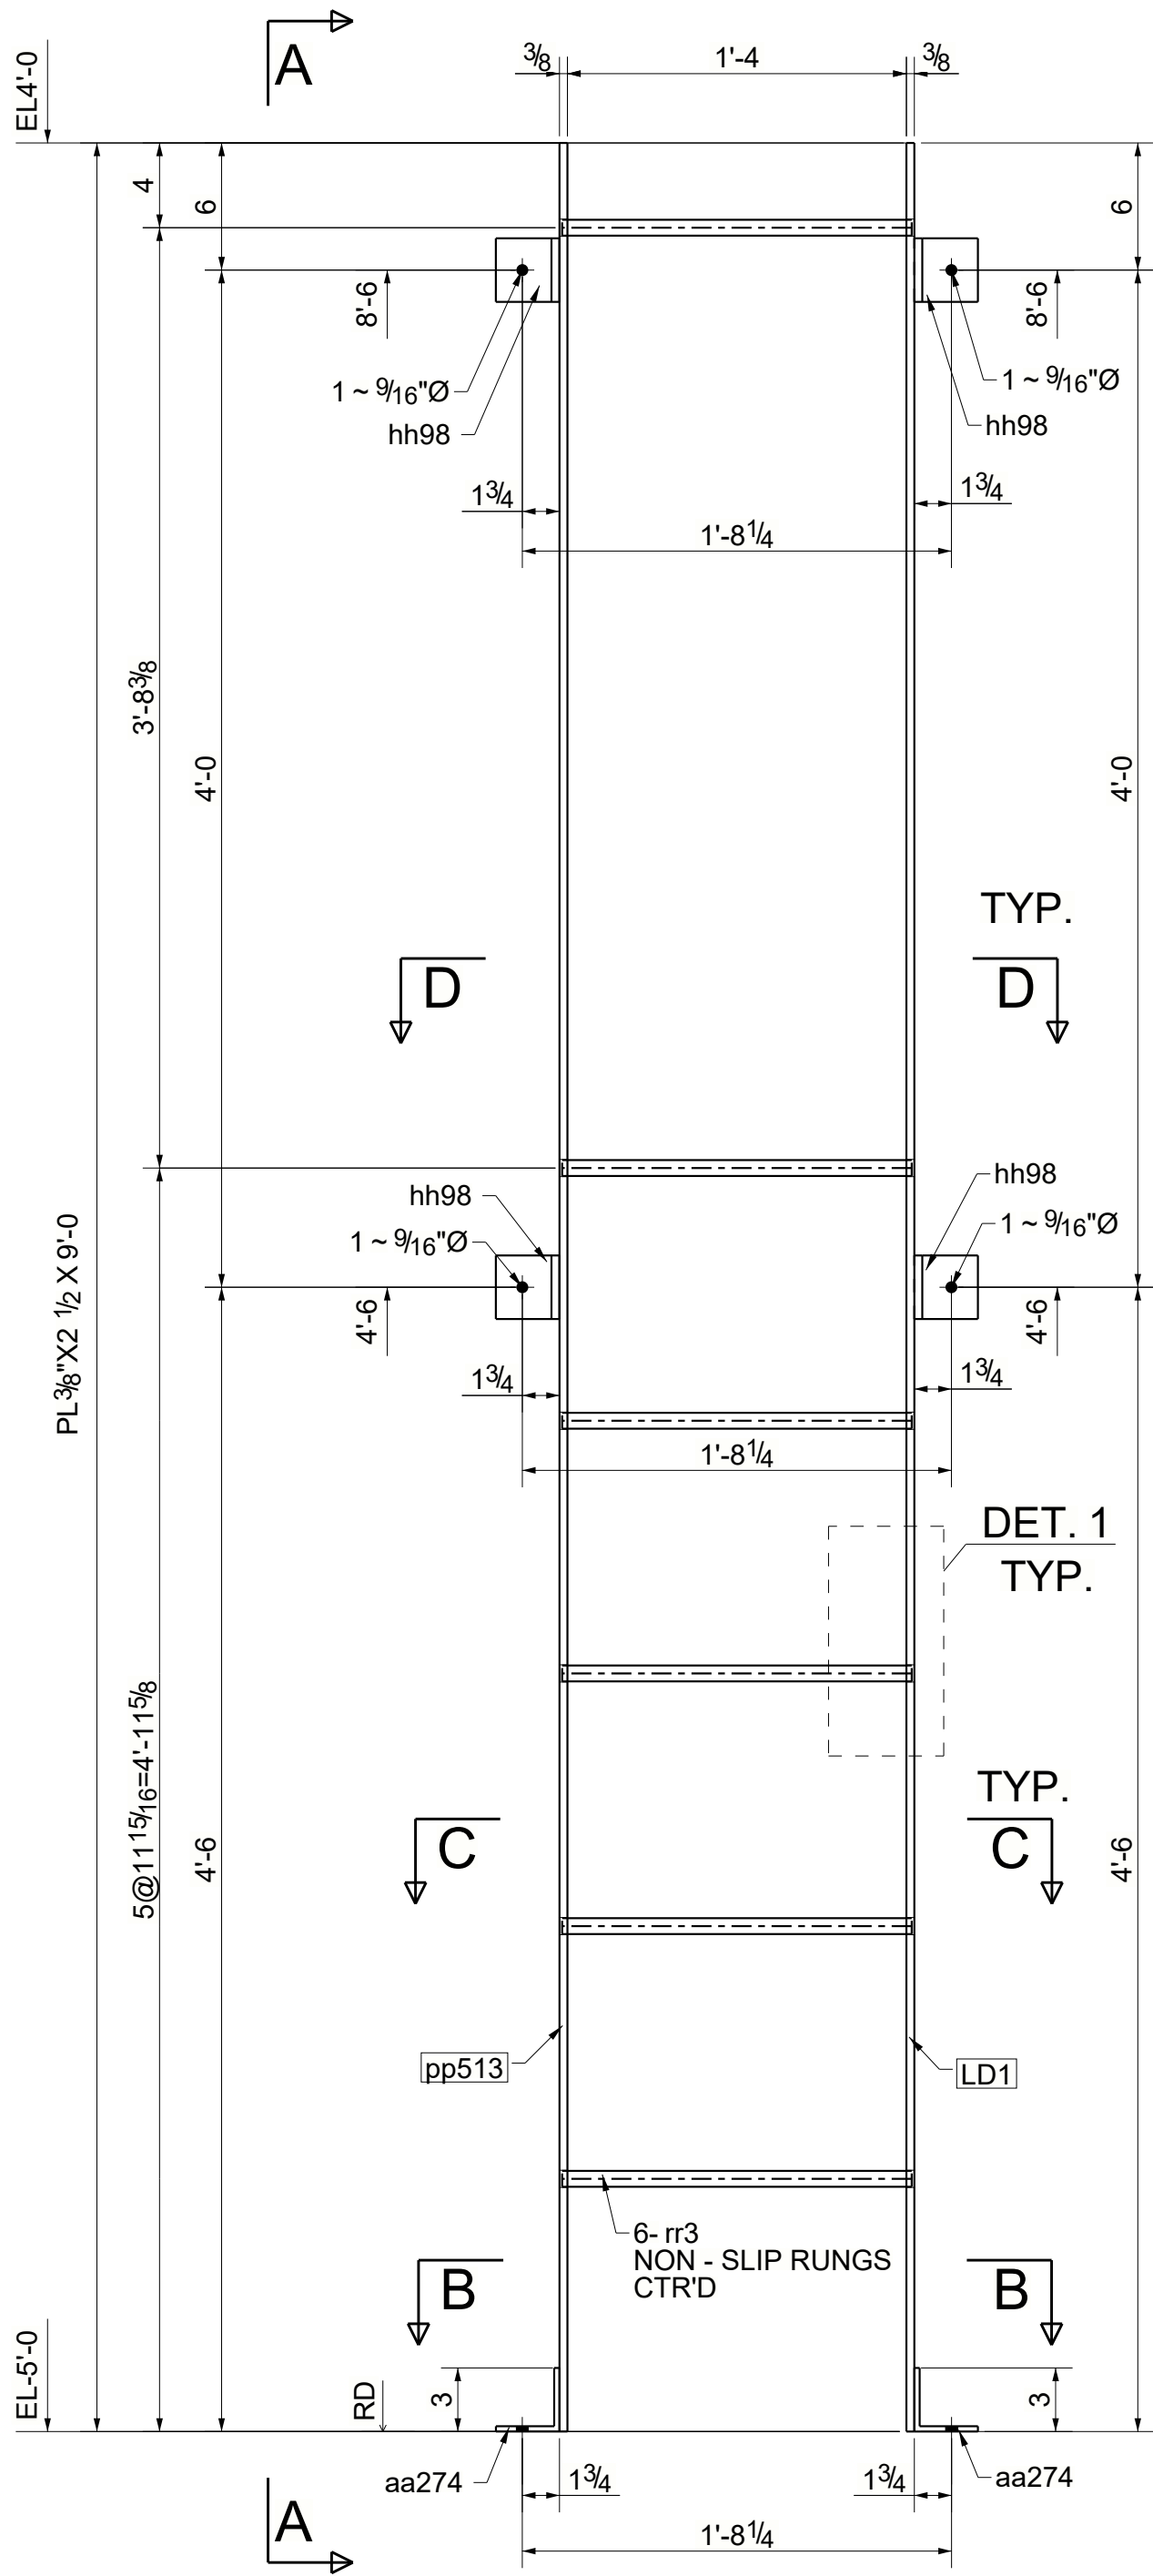


DETAIL 1

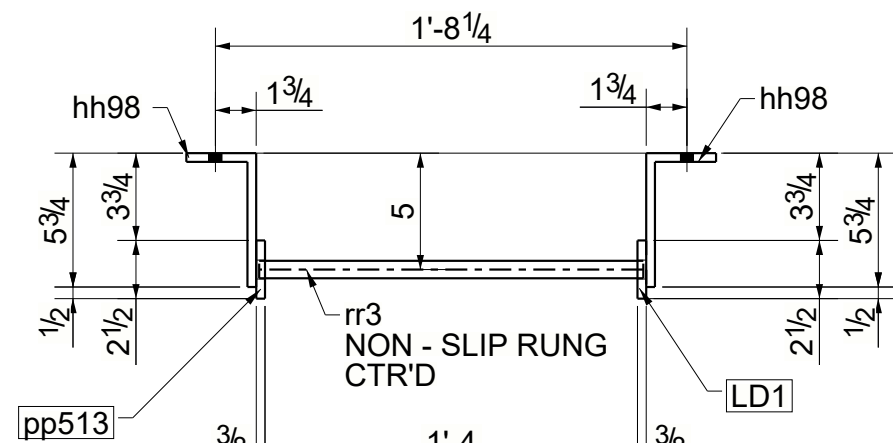

D - D

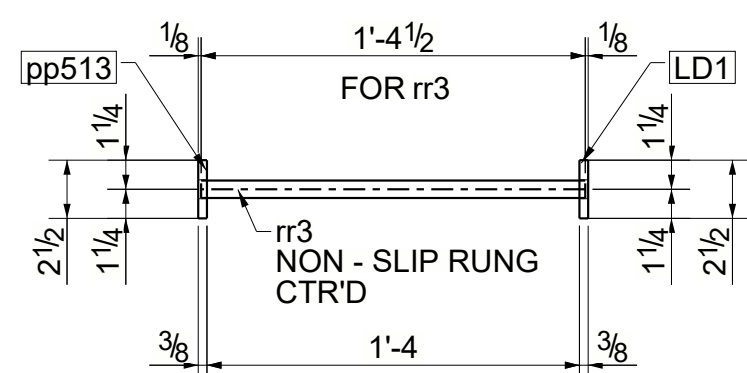

C - C

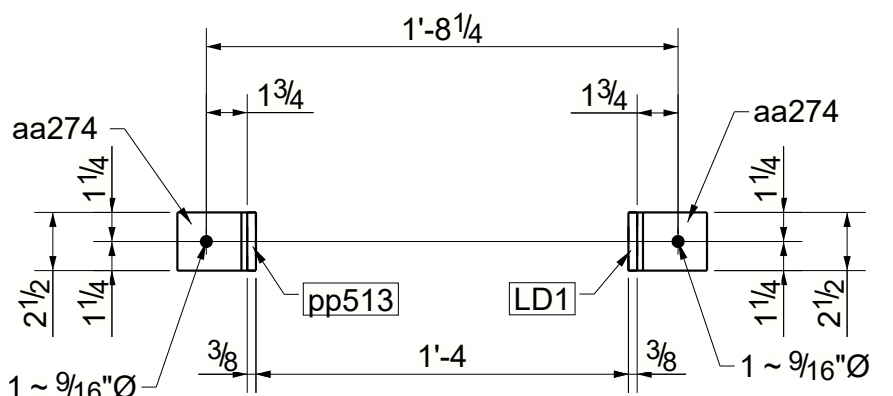

B - B

- SHOP NOTES:
1. ALL WELDS TO BE 3/16" ALL AROUND OR DOUBLE SIDED FILLET WELD UNLESS SHOWN OTHERWISE.
  2. TAG ALL MEMBERS IN A VERTICAL POSITION ON LEFT END AS DETAILED.
  3. ALL SHARP EDGES SHALL BE GROUND SMOOTH AND CORNERS ROUNDED OFF.
  4. ALL TAIL (RUNNING) DIMENSIONS SHALL BE MEASURED FROM END OF BEAM, COLUMN,..ETC.
  - "RD" DENOTES RUNNING DIMENSION
  5. ALL COPES SHALL BE MEASURED FROM END OF BEAM.
  6. ALL BEAM COPES TO BE CUT WITH 1/2" RADIUS U.N.O.
  7. ALL CLIP ANGLES SHALL BE ATTACHED TO BEAM WITH 3/16" FILLET WELD ON THREE SIDES UNLESS SHOWN OTHERWISE.
  8. FOR INDIVIDUAL DETAILS OF PLATES, ANGLES, ETC., SEE SINGLE PARTS DETAIL SHEETS.
  9. SHOP CLOSE ALL GAPS.

## BILL OF MATERIAL

| MARK                      | QTY | DESCRIPTION   | LENGTH    | WEIGHT | REMARKS |
|---------------------------|-----|---------------|-----------|--------|---------|
| LD1                       | 1   | LADDER        |           |        | SQ-2    |
| LD1                       | 1   | PL3/8"X2 1/2" | 9'-0"     | 29     | A36     |
| aa274                     | 2   | L3X3X1/4      | 0'-2 1/2" | 2      | A36     |
| hh98                      | 4   | PL3/8"X3"     | 0'-8"     | 11     | A36     |
| pp513                     | 1   | PL3/8"X2 1/2" | 9'-0"     | 29     | A36     |
| rr3                       | 6   | ROD3/4"       | 1'-4 1/2" | 11     | A36     |
| TOTAL WEIGHT THIS DRAWING |     |               |           | 81     |         |

ONE - LADDER - LD1