






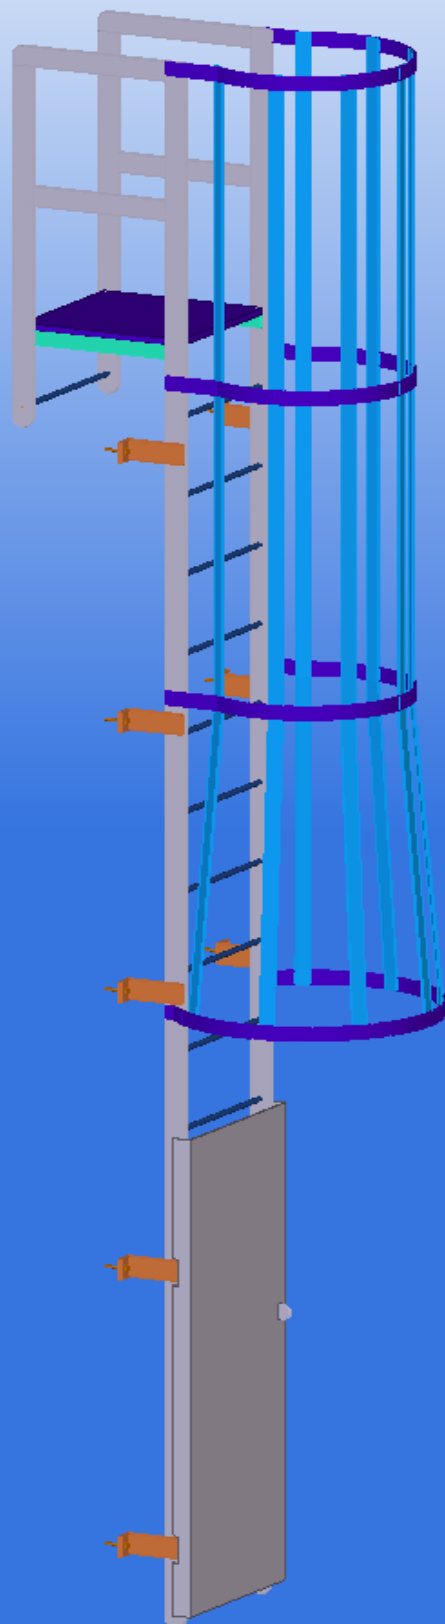

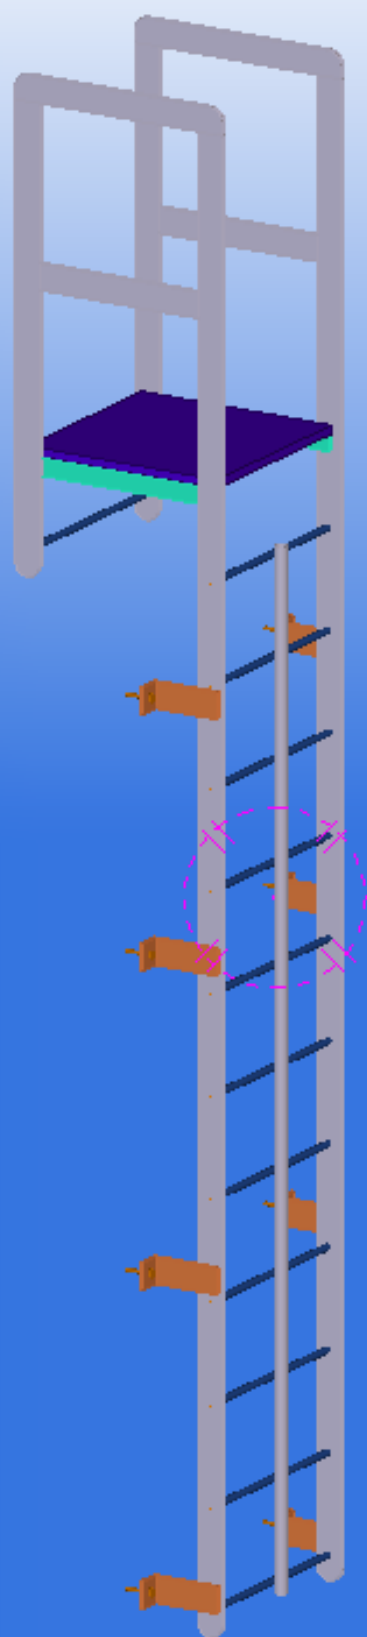

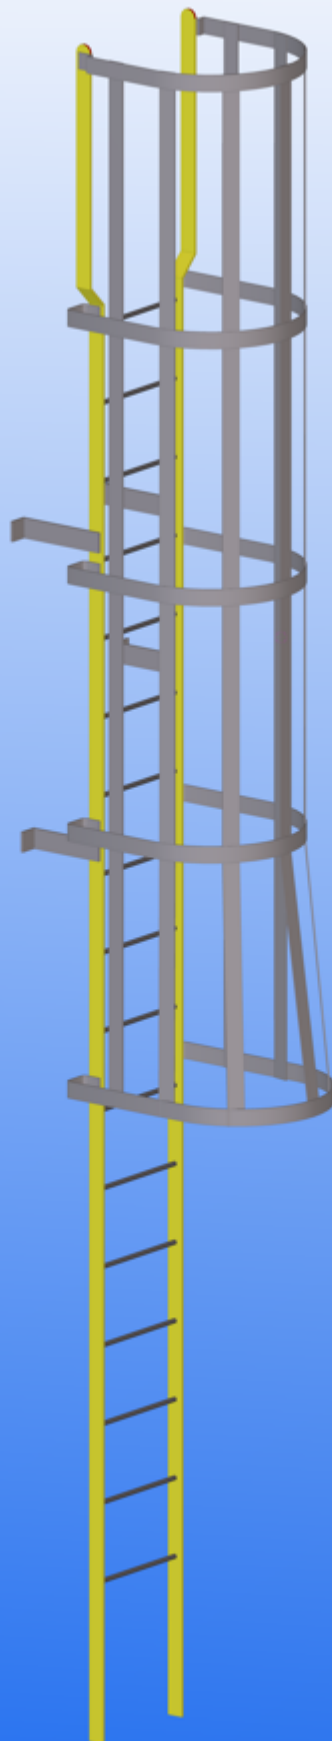

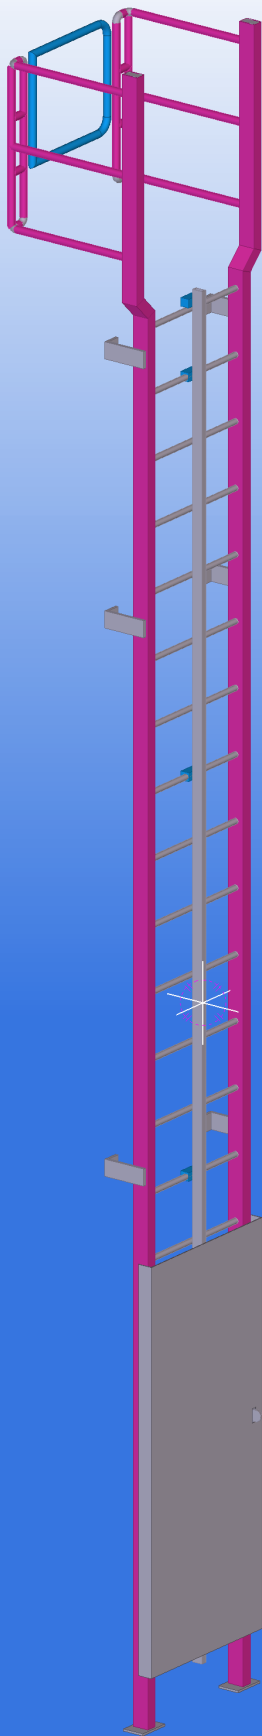

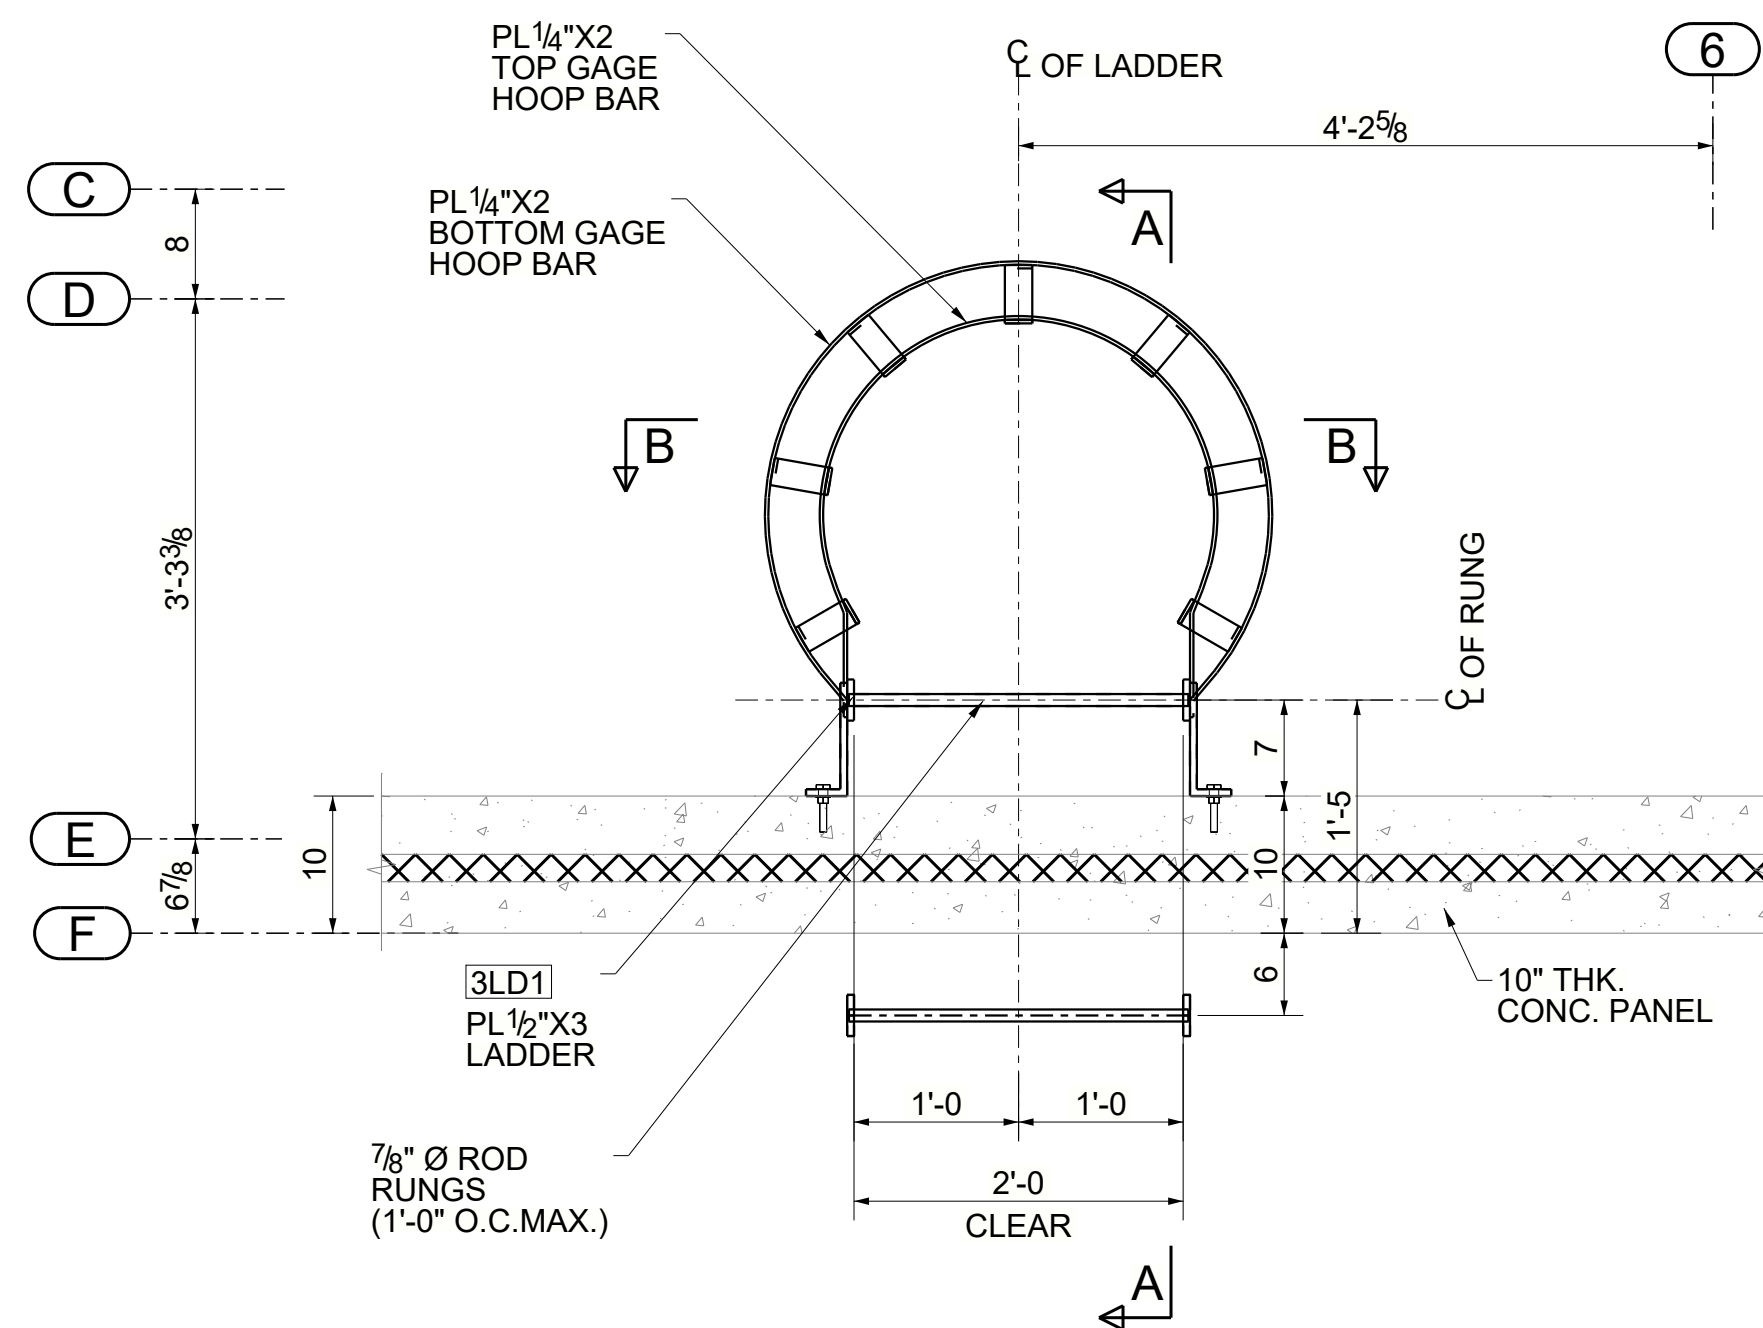


ROOF ACCESS LADDER LOCATION PLAN
(REFER : OVERALL ROOF PLAN-01/A104)


GC NOTE :
GC TO COORDINATE WITH MECHANICAL EQUIPEMENT
IN SITE TO AVOID CLASHING WITH CAGE LADDER.

FINISH NOTE:-
ALL LADDER MEMBERS TO BE HOT DIP GALVANIZED.

- NOTES:-**
1. REFER SHEET ME301 FOR KEY PLAN.
 2. ALL LADDER RUNGS TOP SURFACE MUST BE NON-SLIP.
 3. V.I.F - INDICATES VERIFY IN FIELD.

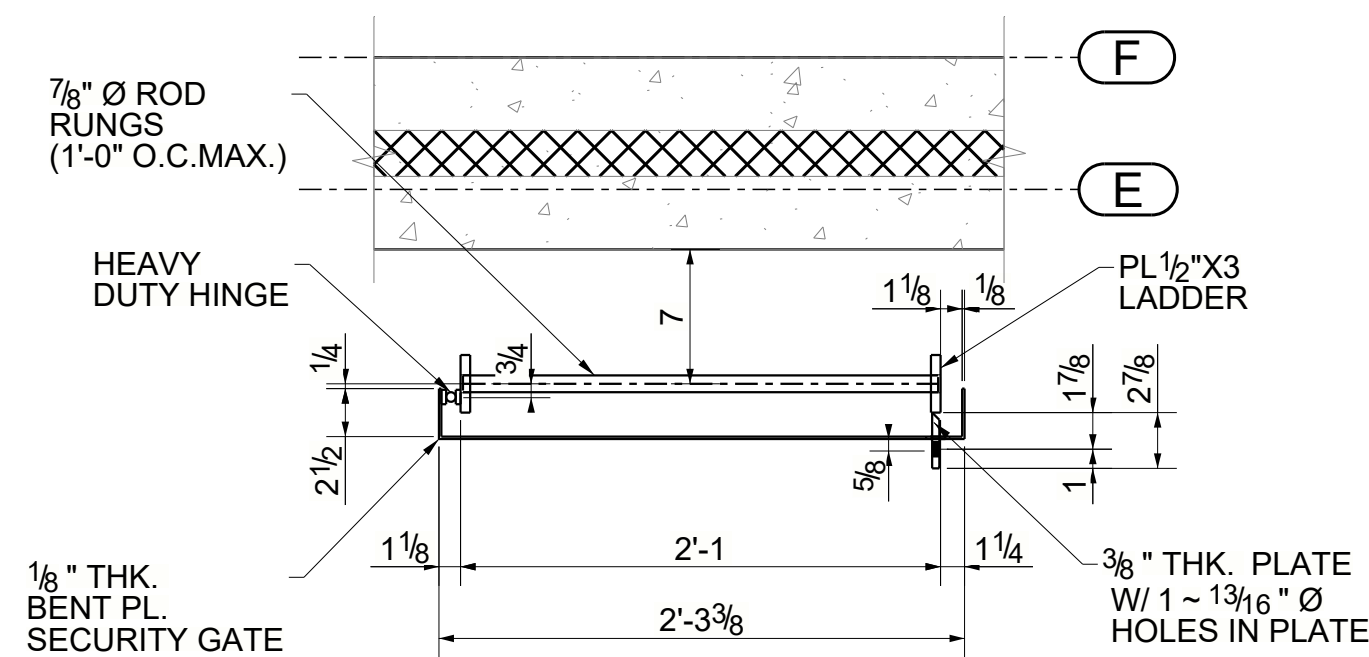


SECTION B1 - B1

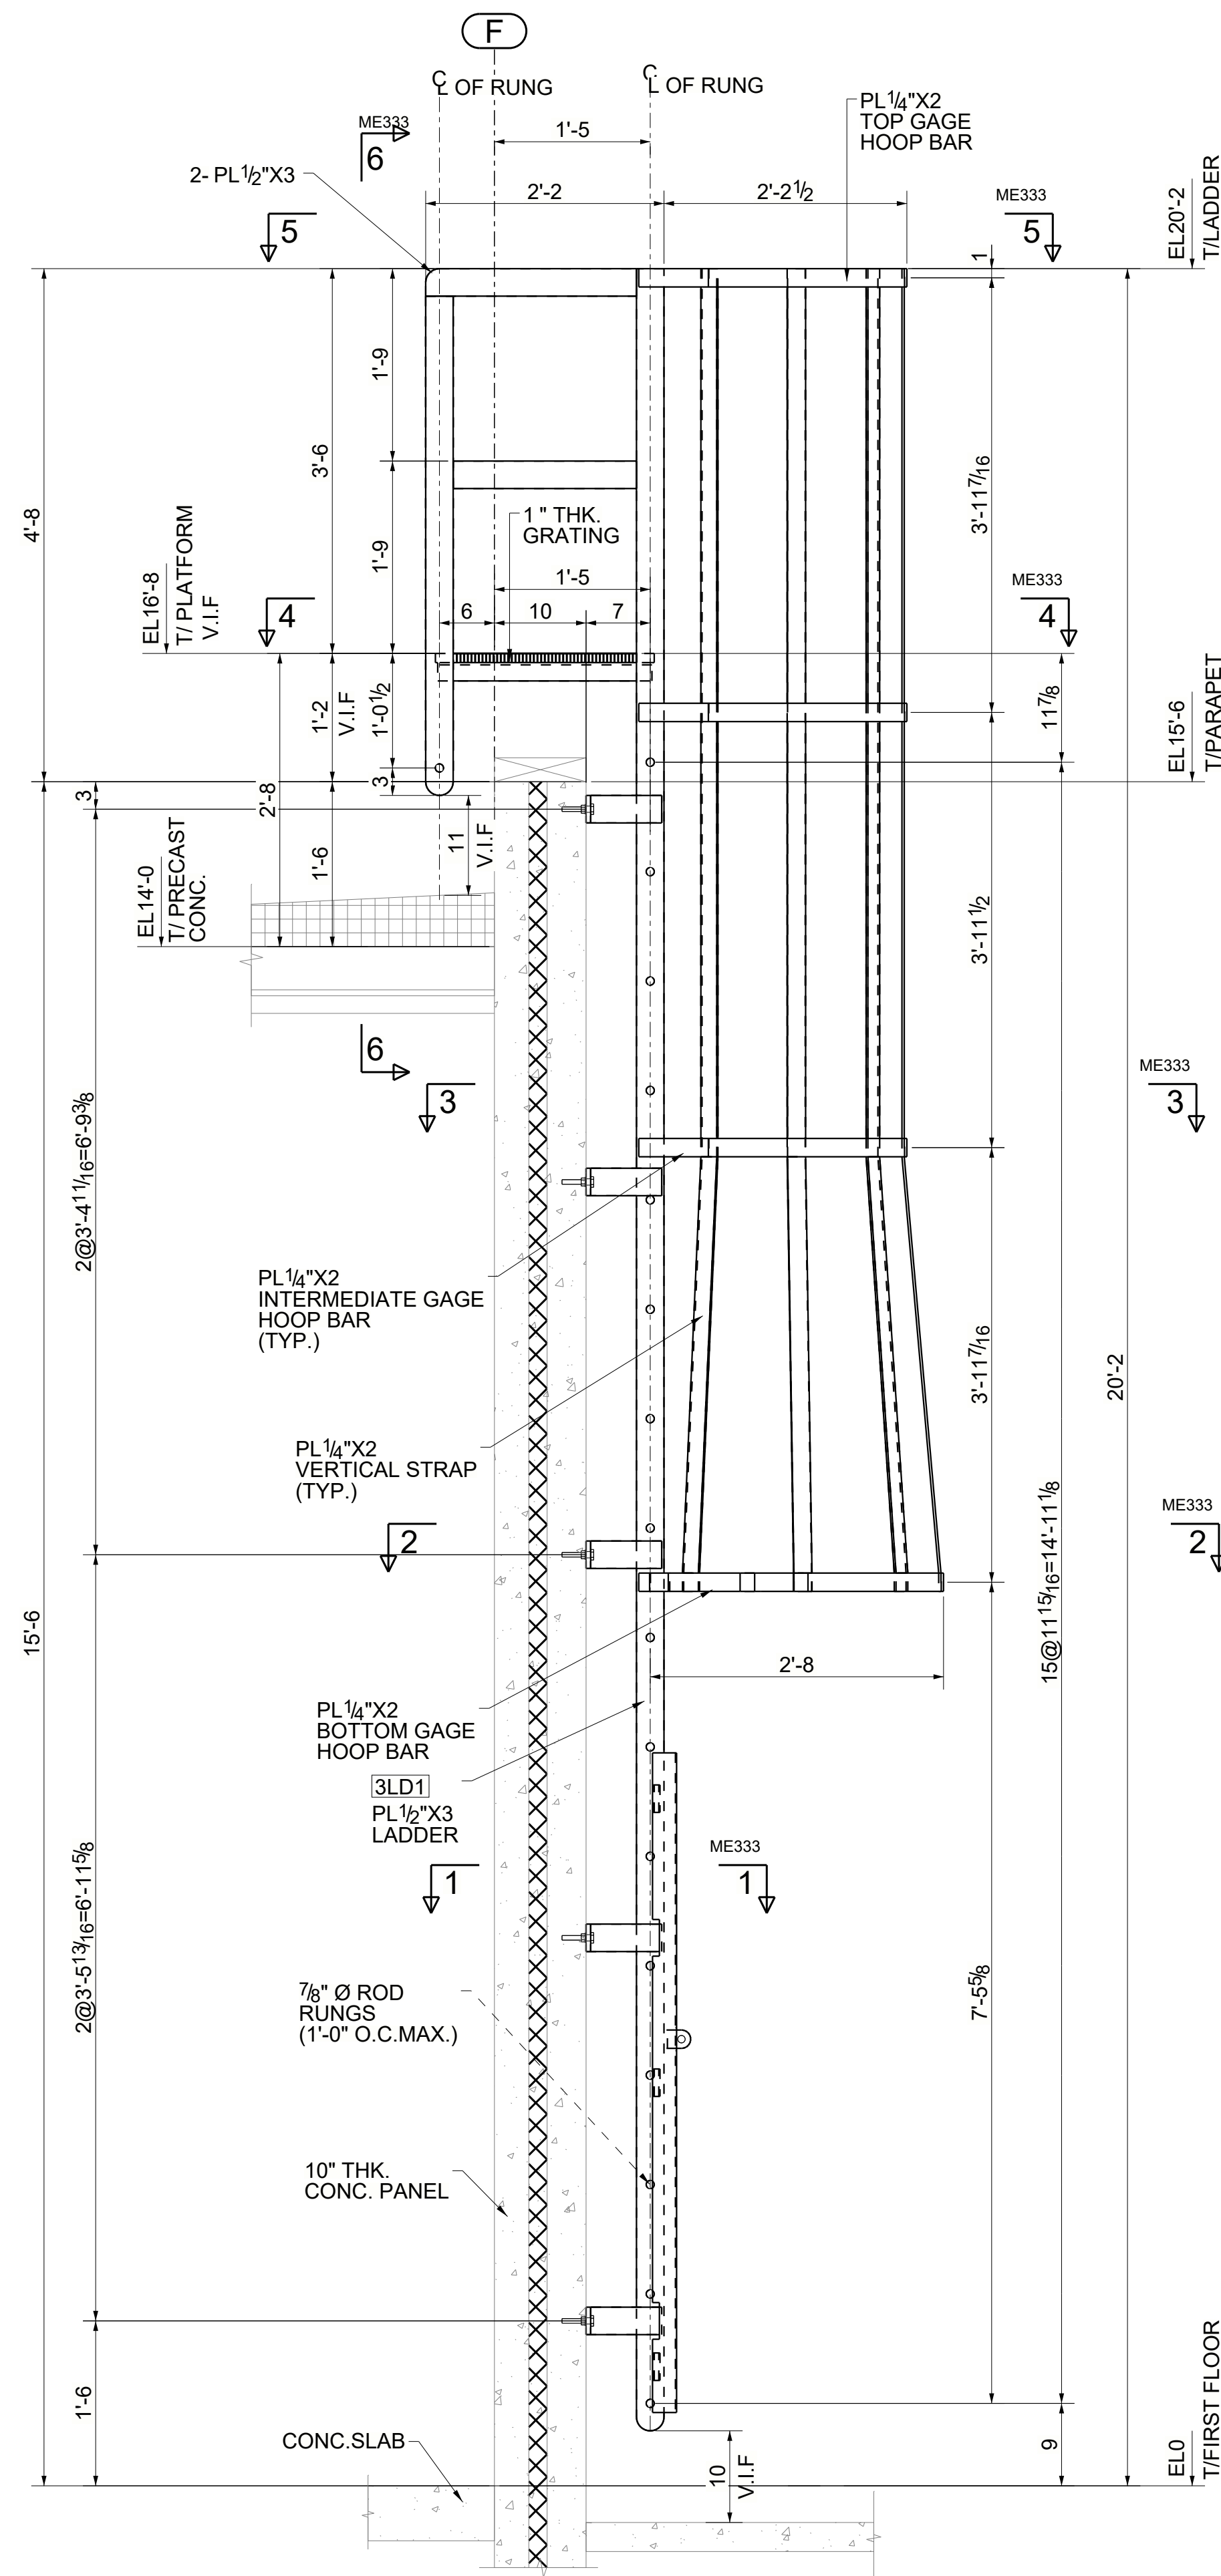


SECTION A - A


(REFER : WALL SECTION - 01/A402)

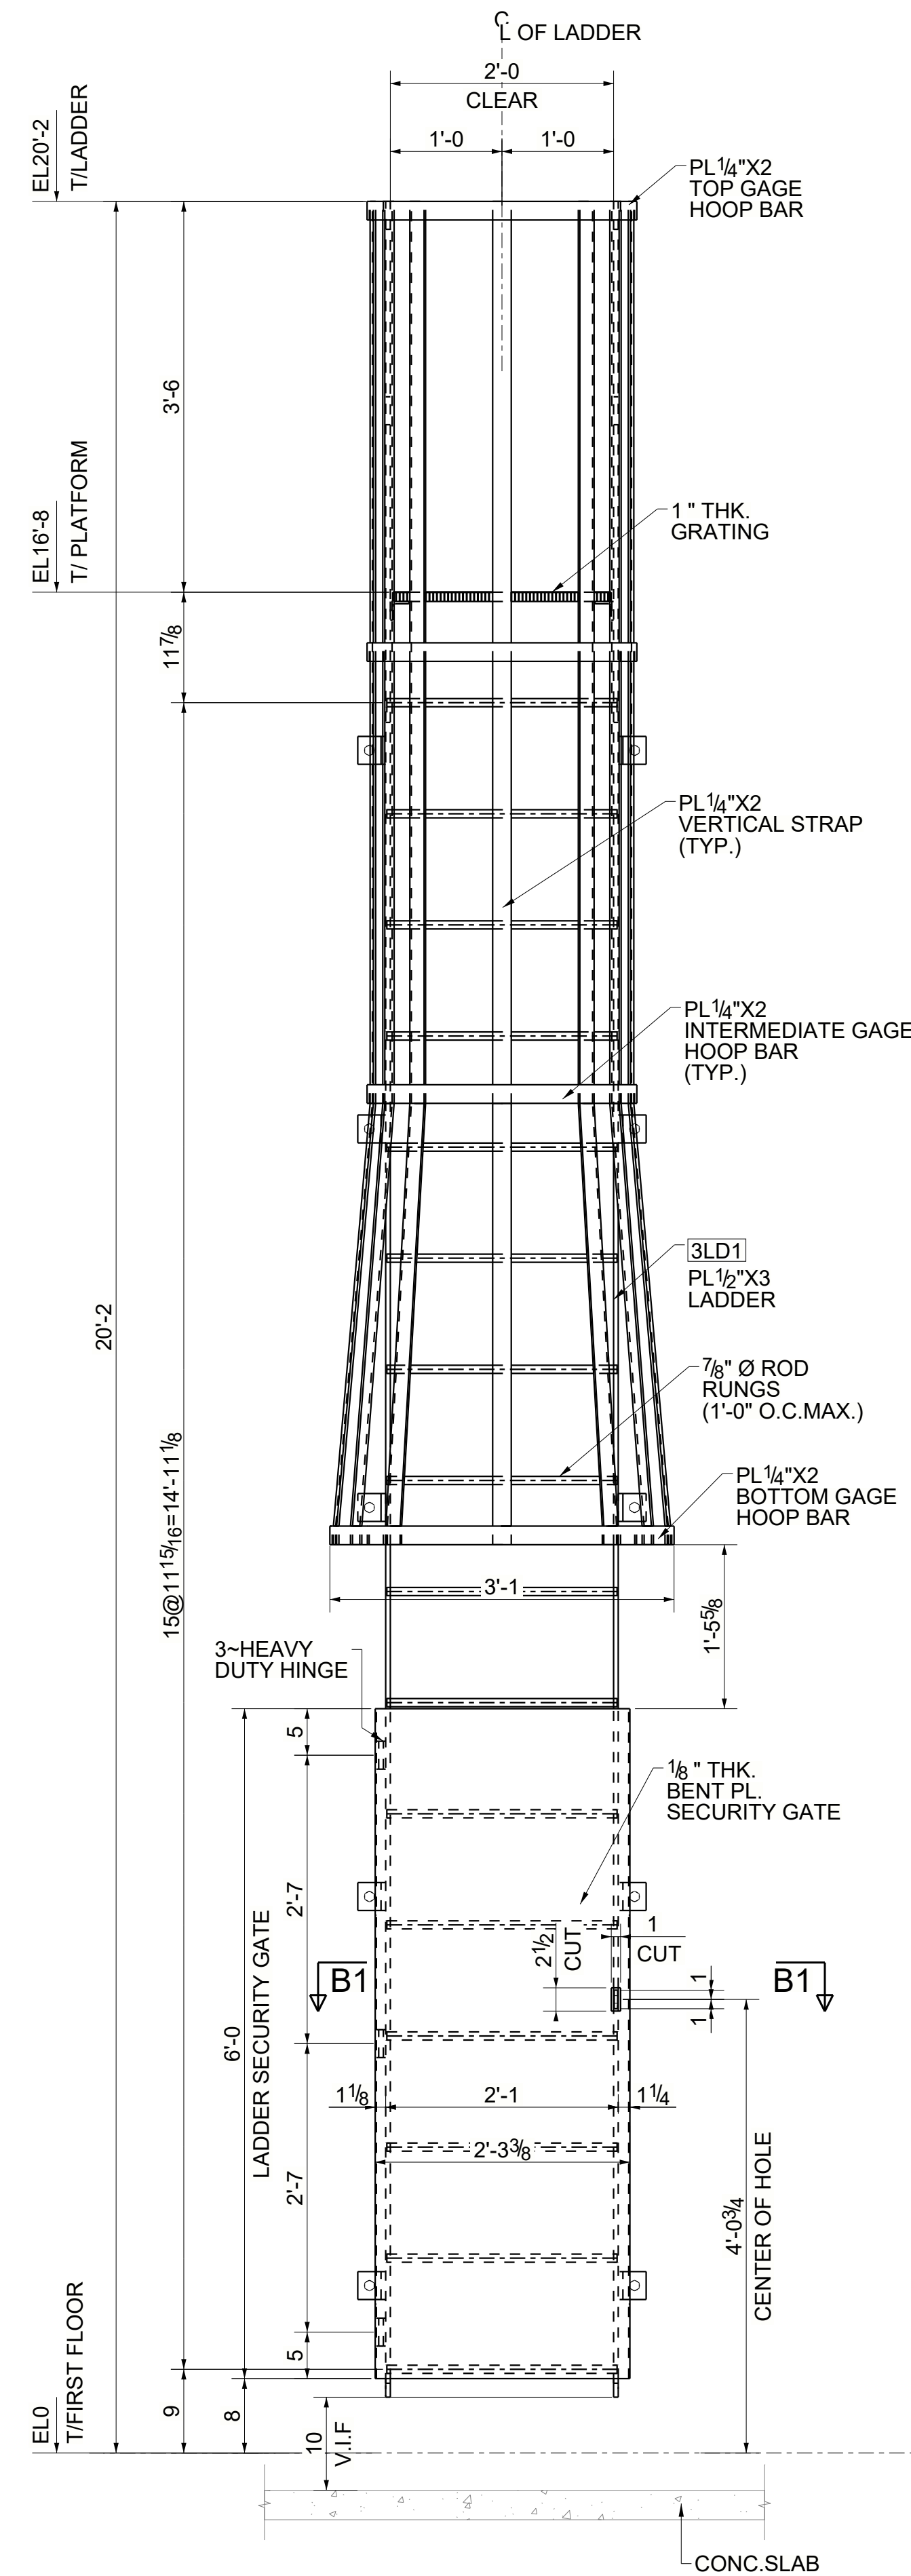

SECTION B - B

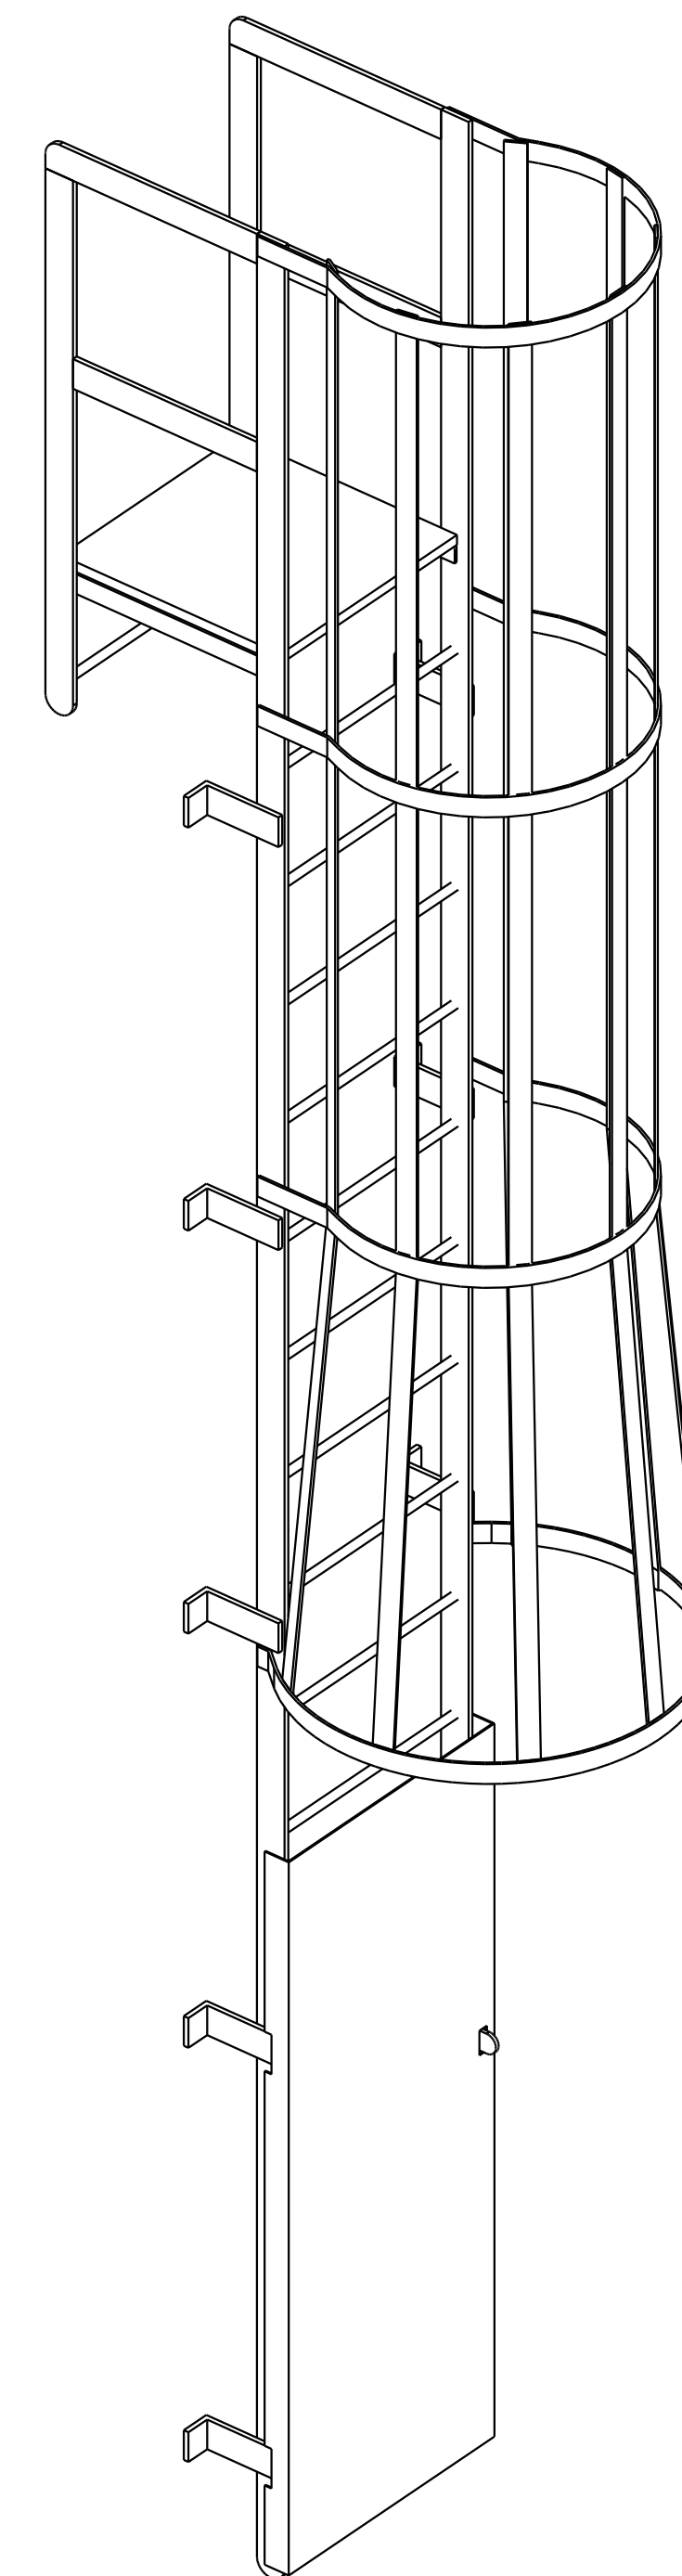

3D-VIEW

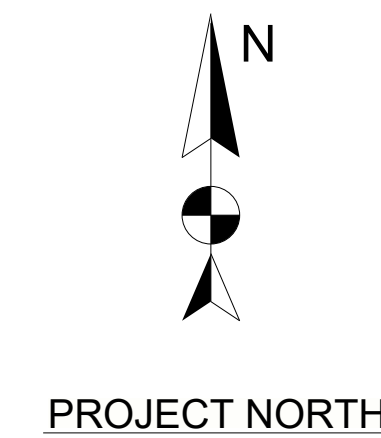





NOTES :-

1. REFER SHEET ME301 FOR MISC. KEY PLAN.
2. ALL LADDER RUNGS TOP SURFACE SHOULD BE NON-SLIP.
3. V.I.F - INDICATES VERIFY IN FIELD.




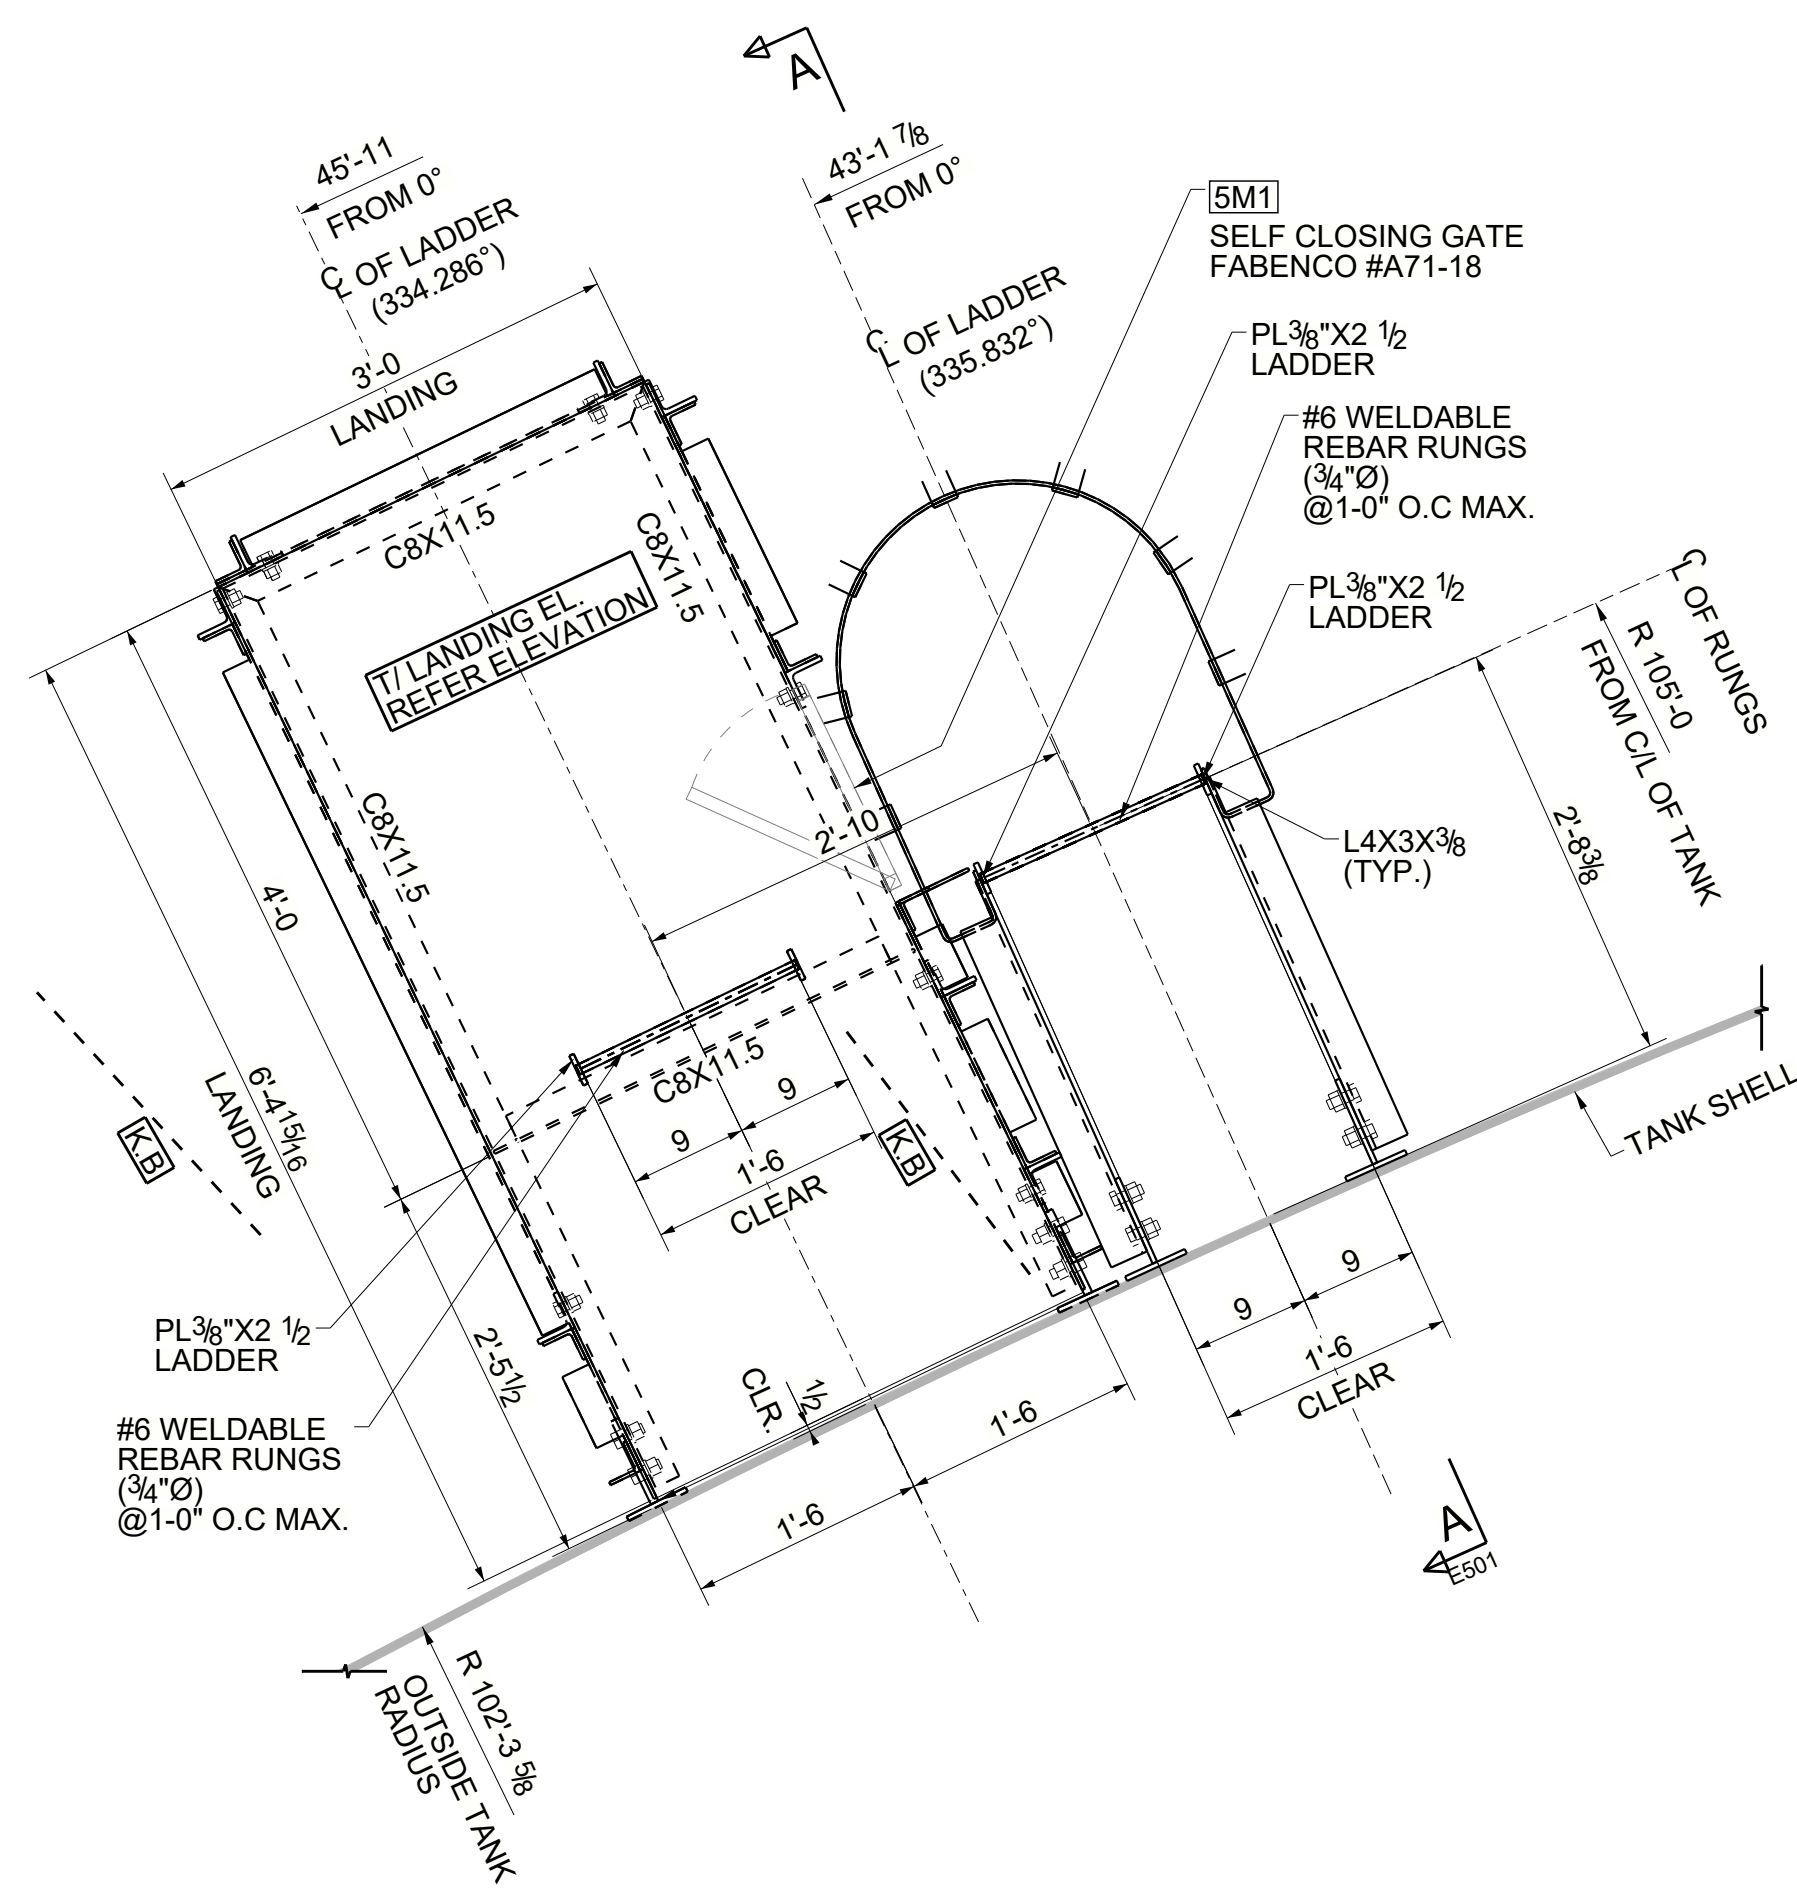


LADDER LOCATION PLAN AT LANDING 01, 03 AND 05
AT EL. 1086'-3 1/4", EL. 1124'-3 1/4 AND EL. 1162'-3 1/4
 (REFER: PLAN OF EMERGENCY LADDER /DW-10600-01)

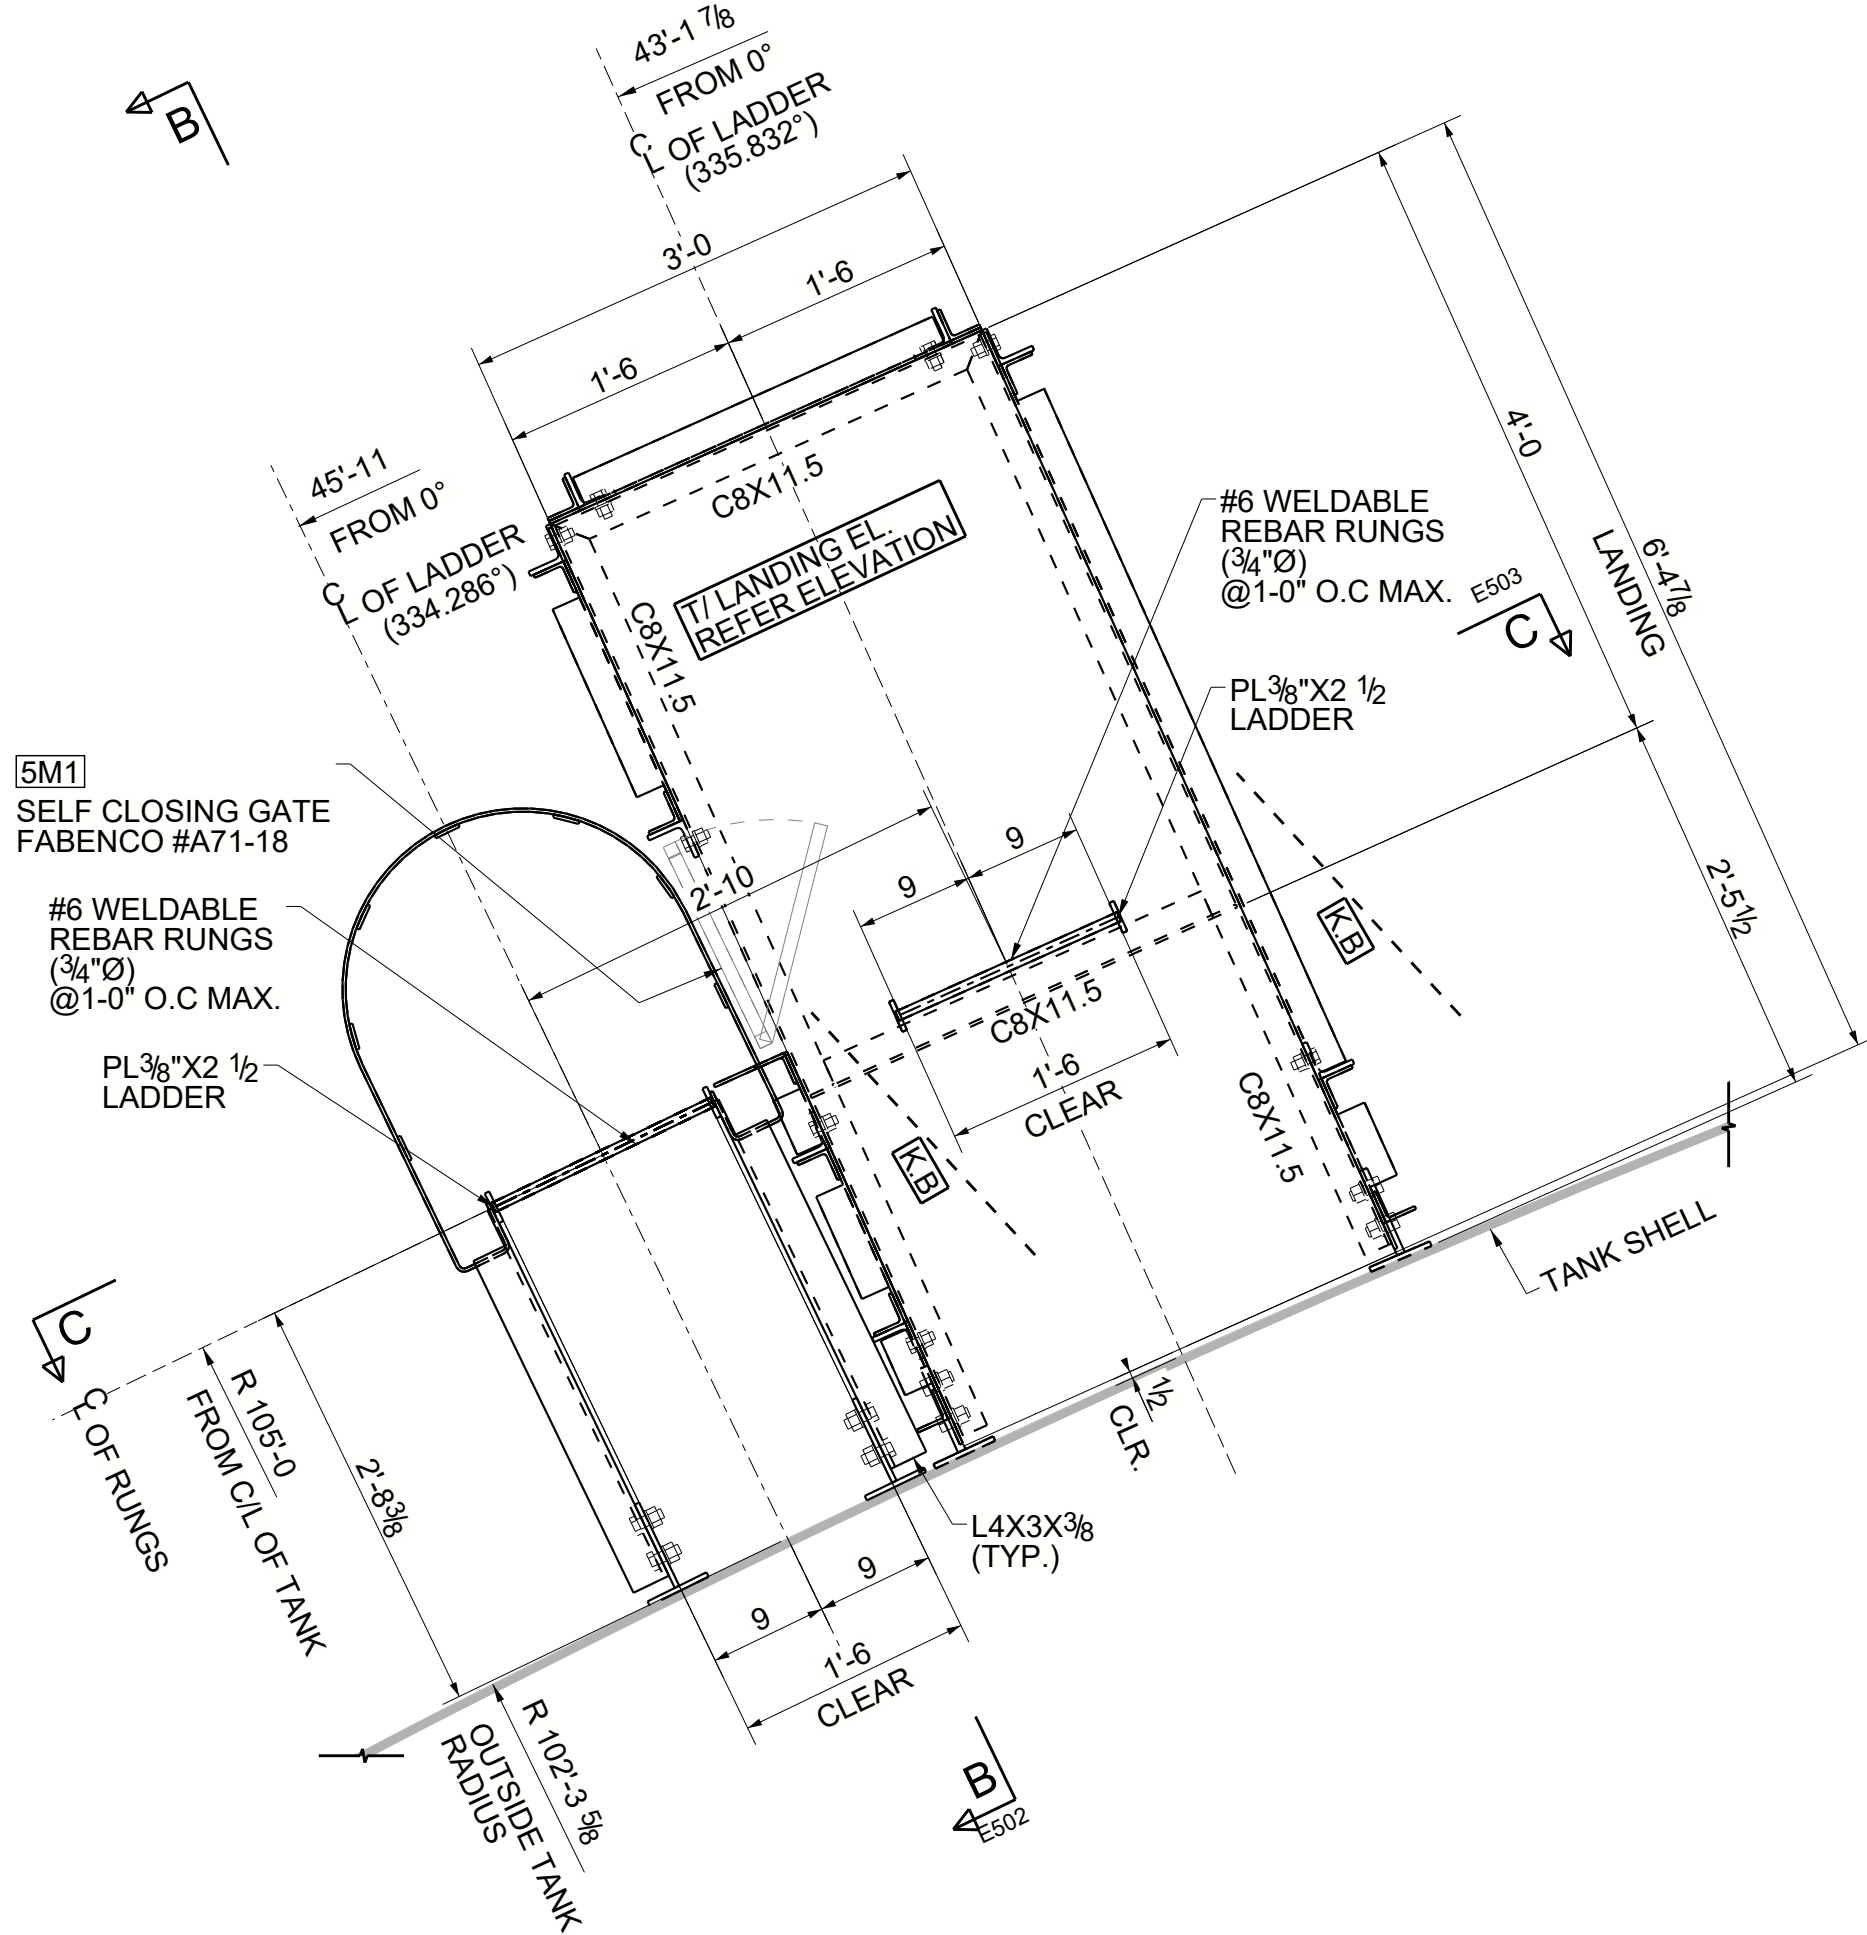


LADDER LOCATION PLAN AT LANDING 02, 04 AND 06
AT EL. 1105'-3 1/4", 1143'-3 1/4 AND 1181'-3 1/4
 (REFER: PLAN OF EMERGENCY LADDER /DW-10600-01)

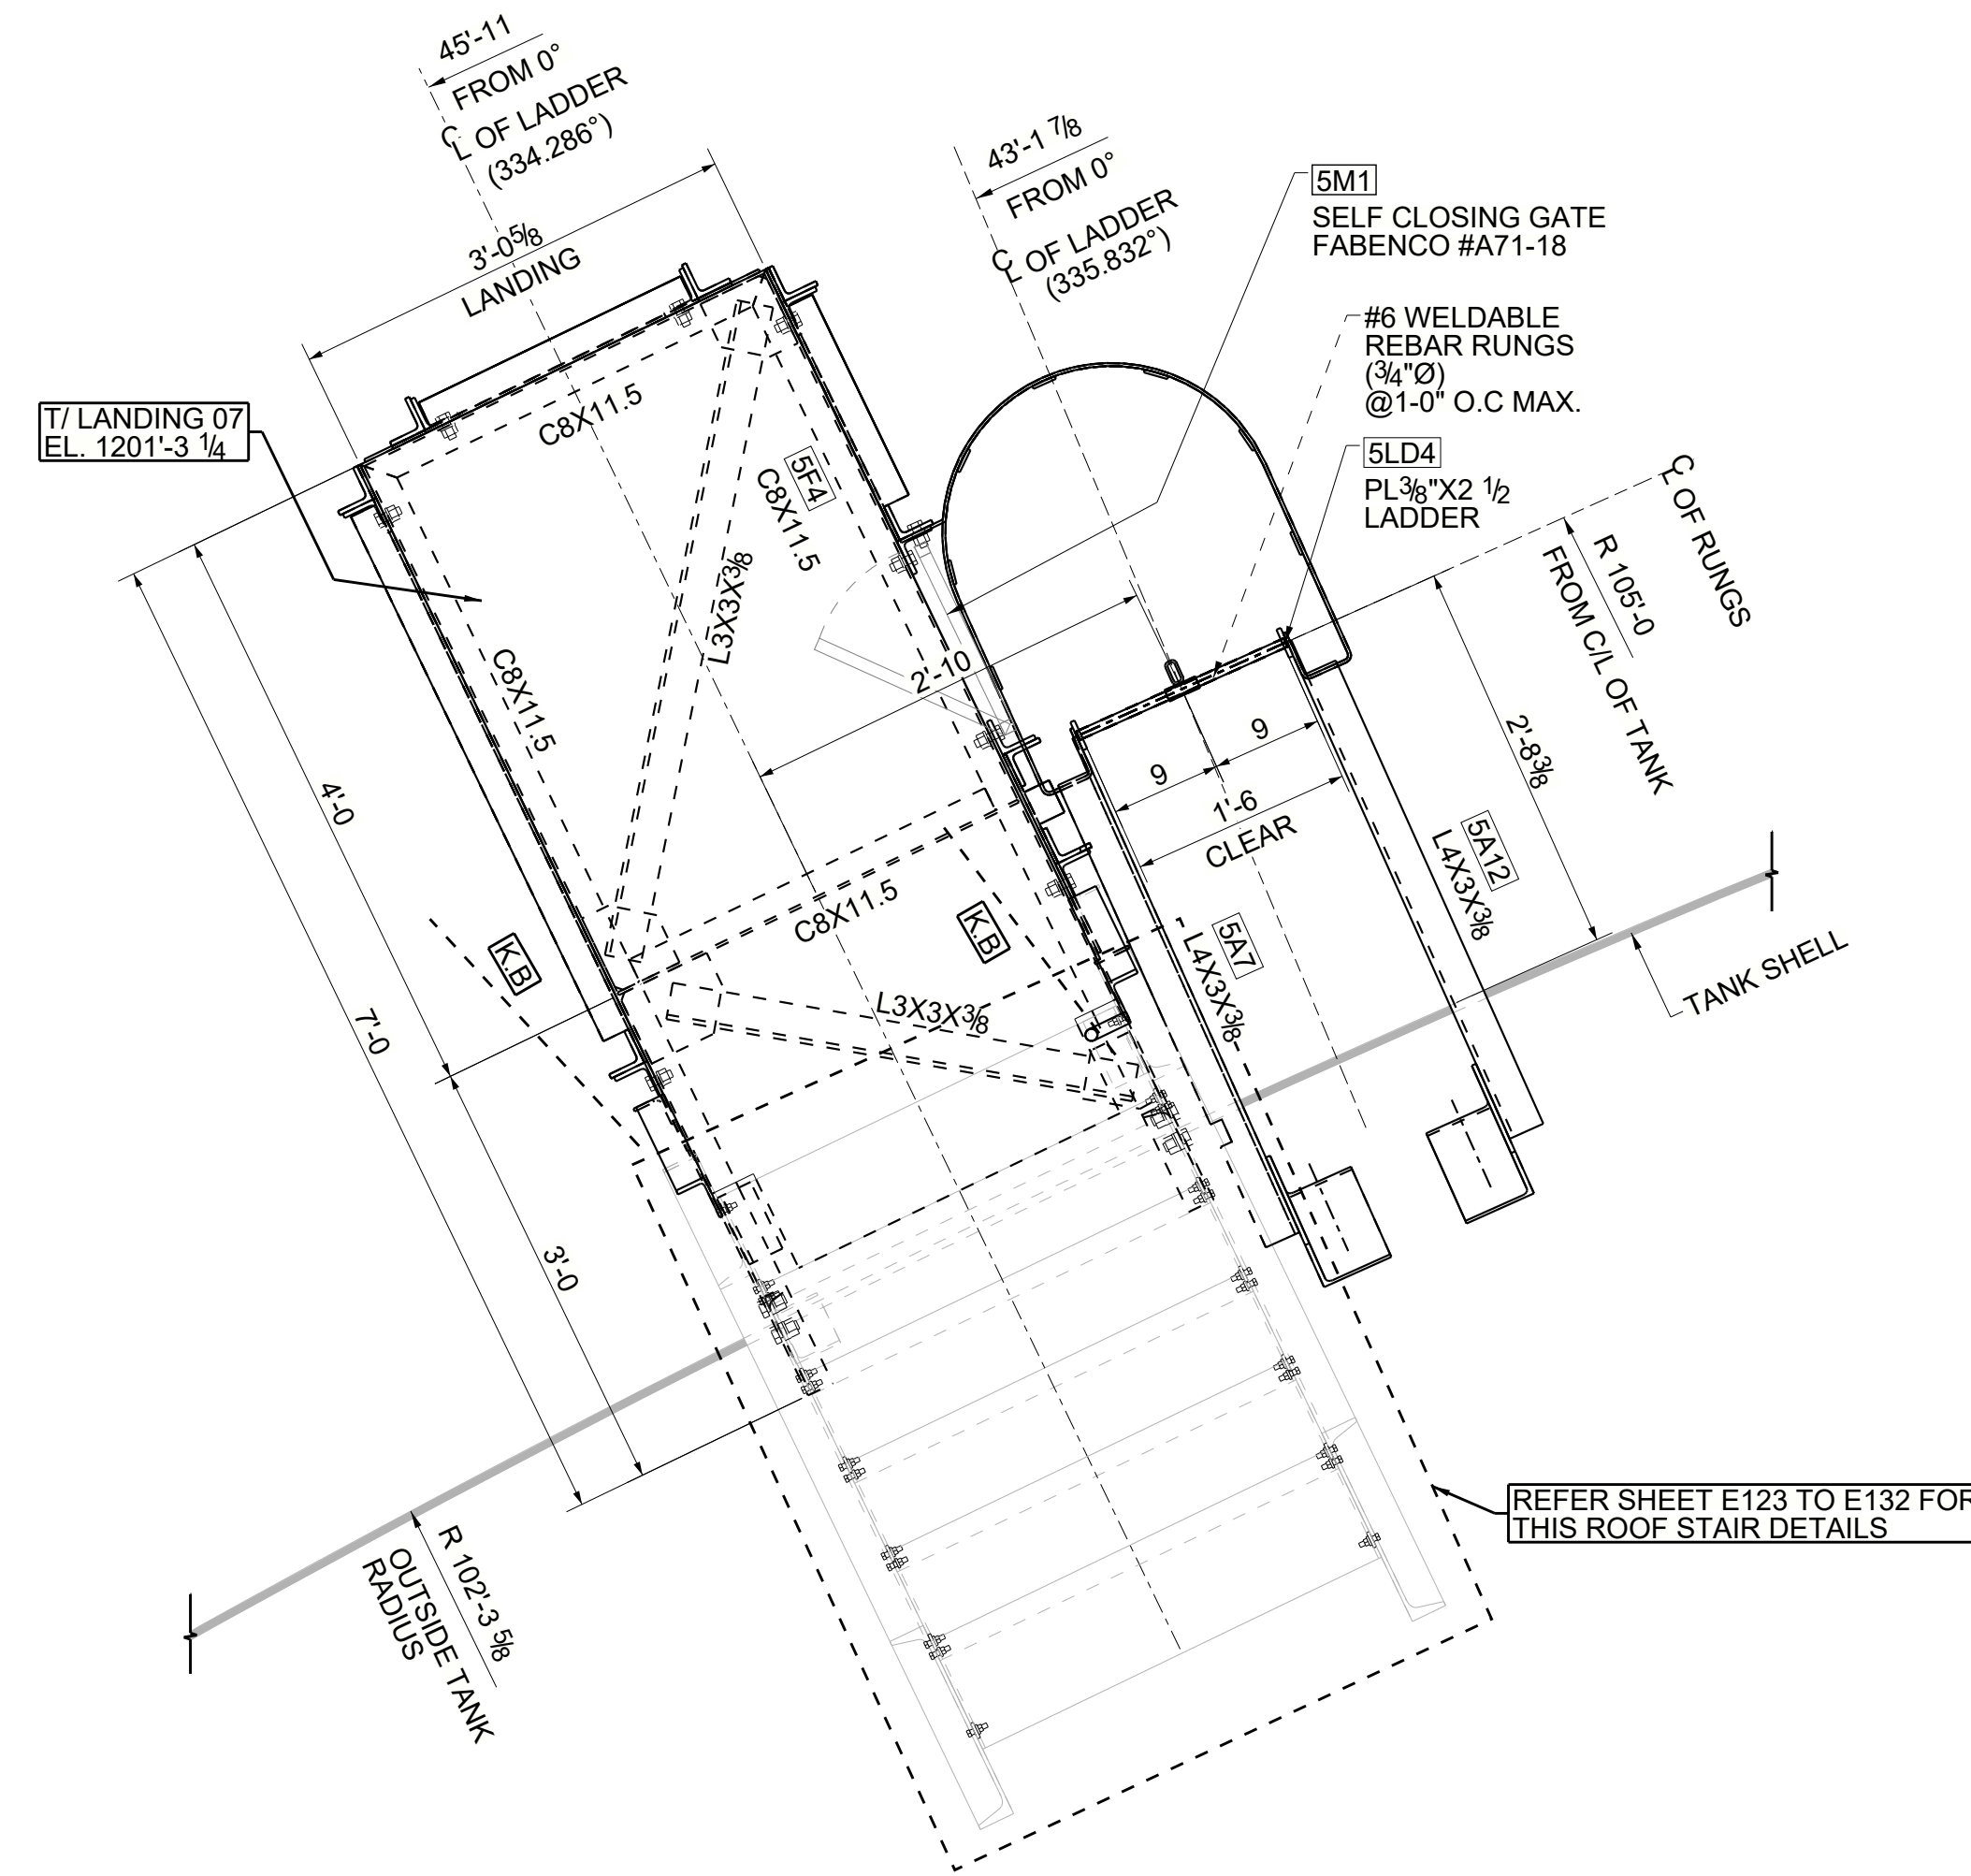

LADDER LOCATION PLAN AT LANDING 07 EL. 1201'-3 1/4
 (REFER: PLAN OF EMERGENCY LADDER /DW-10600-01)

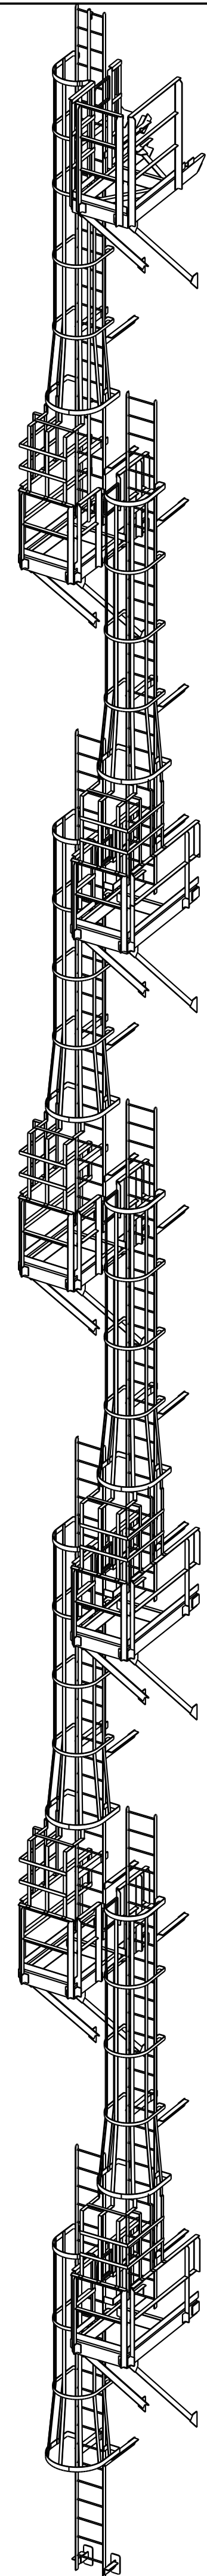

3D VIEW @ EMERGENCY LADDER

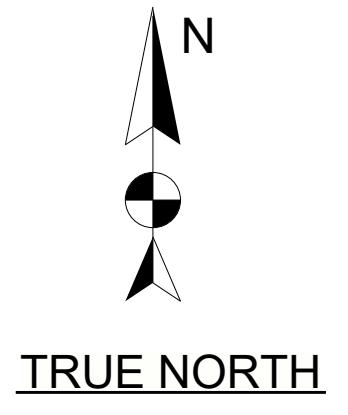

BOLT NOTE :
 A325 N BOLTS SHOWN IN SECTION AND TYPICAL
 DETAILS -- INDICATES ASTM F3125, GRADE A325 , TYPE -1

FINISH NOTE :
 ALL STEEL MEMBERS IN THIS PROJECT
 TO BE HOT DIPPED GALVANIZED PER ASTM A123
 SURFACE PREPARATION TO BE SSPC-SP3
 FOR ALL STEELS

GRATING NOTE :
 GRATING SHALL BE GALVANIZED WELDED TYPE WITH 1 1/4 X 3/16 BEARING BARS
 AT 13/16 C/C WITH CROSS BARS AT 4" C/C, AND SMOOTH WEARING SURFACE.
 FASTEN GRATING TO ALL SUPPORT STEEL WITH GALVANIZED G-STYLE CLIPS OR
 APPROVED AT 18" MAXIMUM CENTERS. WITH A MINIMUM OF 2 CLIPS ACROSS
 THE PANEL WIDTH AT EACH SUPPORT MEMBER.

- NOTES:**
1. REFER SHEET E501 TO E503 FOT LADDER ELEVATION.
 2. REFER SHEET E505 AND 506 FOR SECTIONS.




1. REFER 10-E1002 SHEET FOR GENERAL NOTES.
2. REFER 33-E3302 SHEET FOR LADDER SECTIONS & DETAILS.


ALL LADDER STEEL WILL BE
HOT DIPPED GALVANIZED TYPICAL




(REFER : CAGE LADDER SECTION (11/ A504))

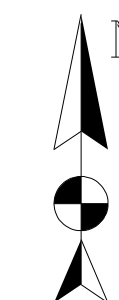


PROJECT NORTH

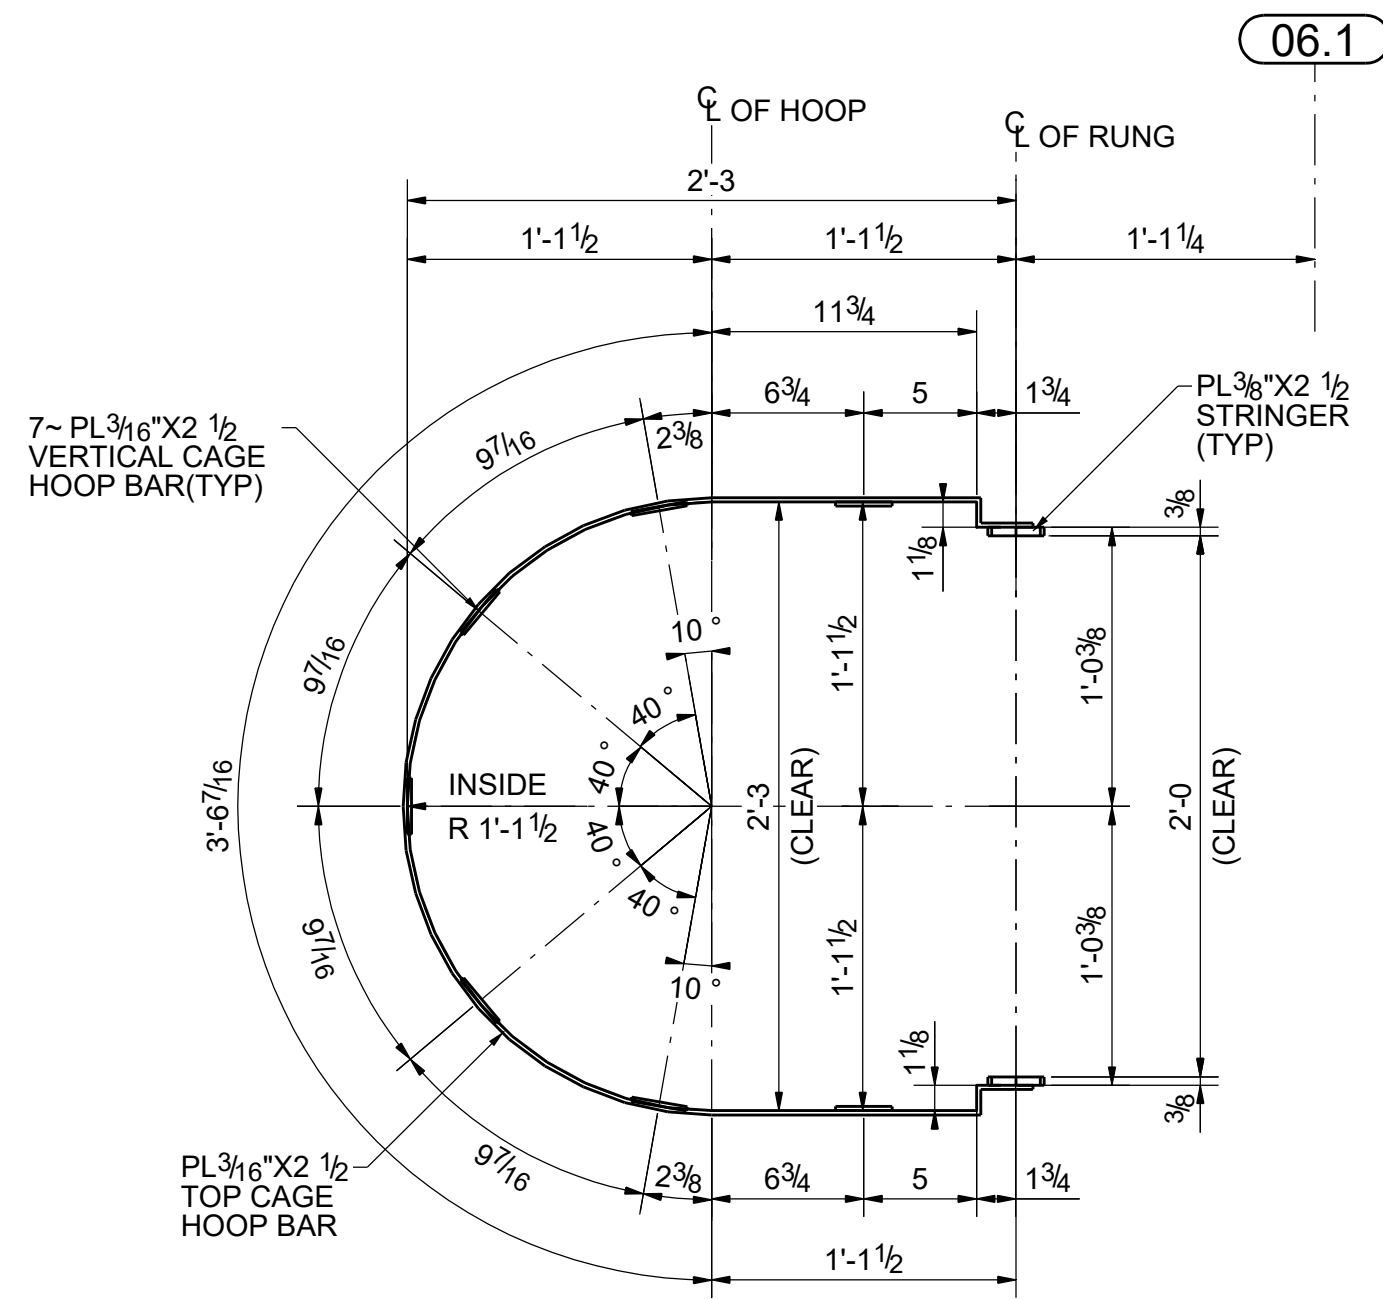


SECTION 1 - 1
33-E3301
TOP CAGE HOOP BAR DETAIL

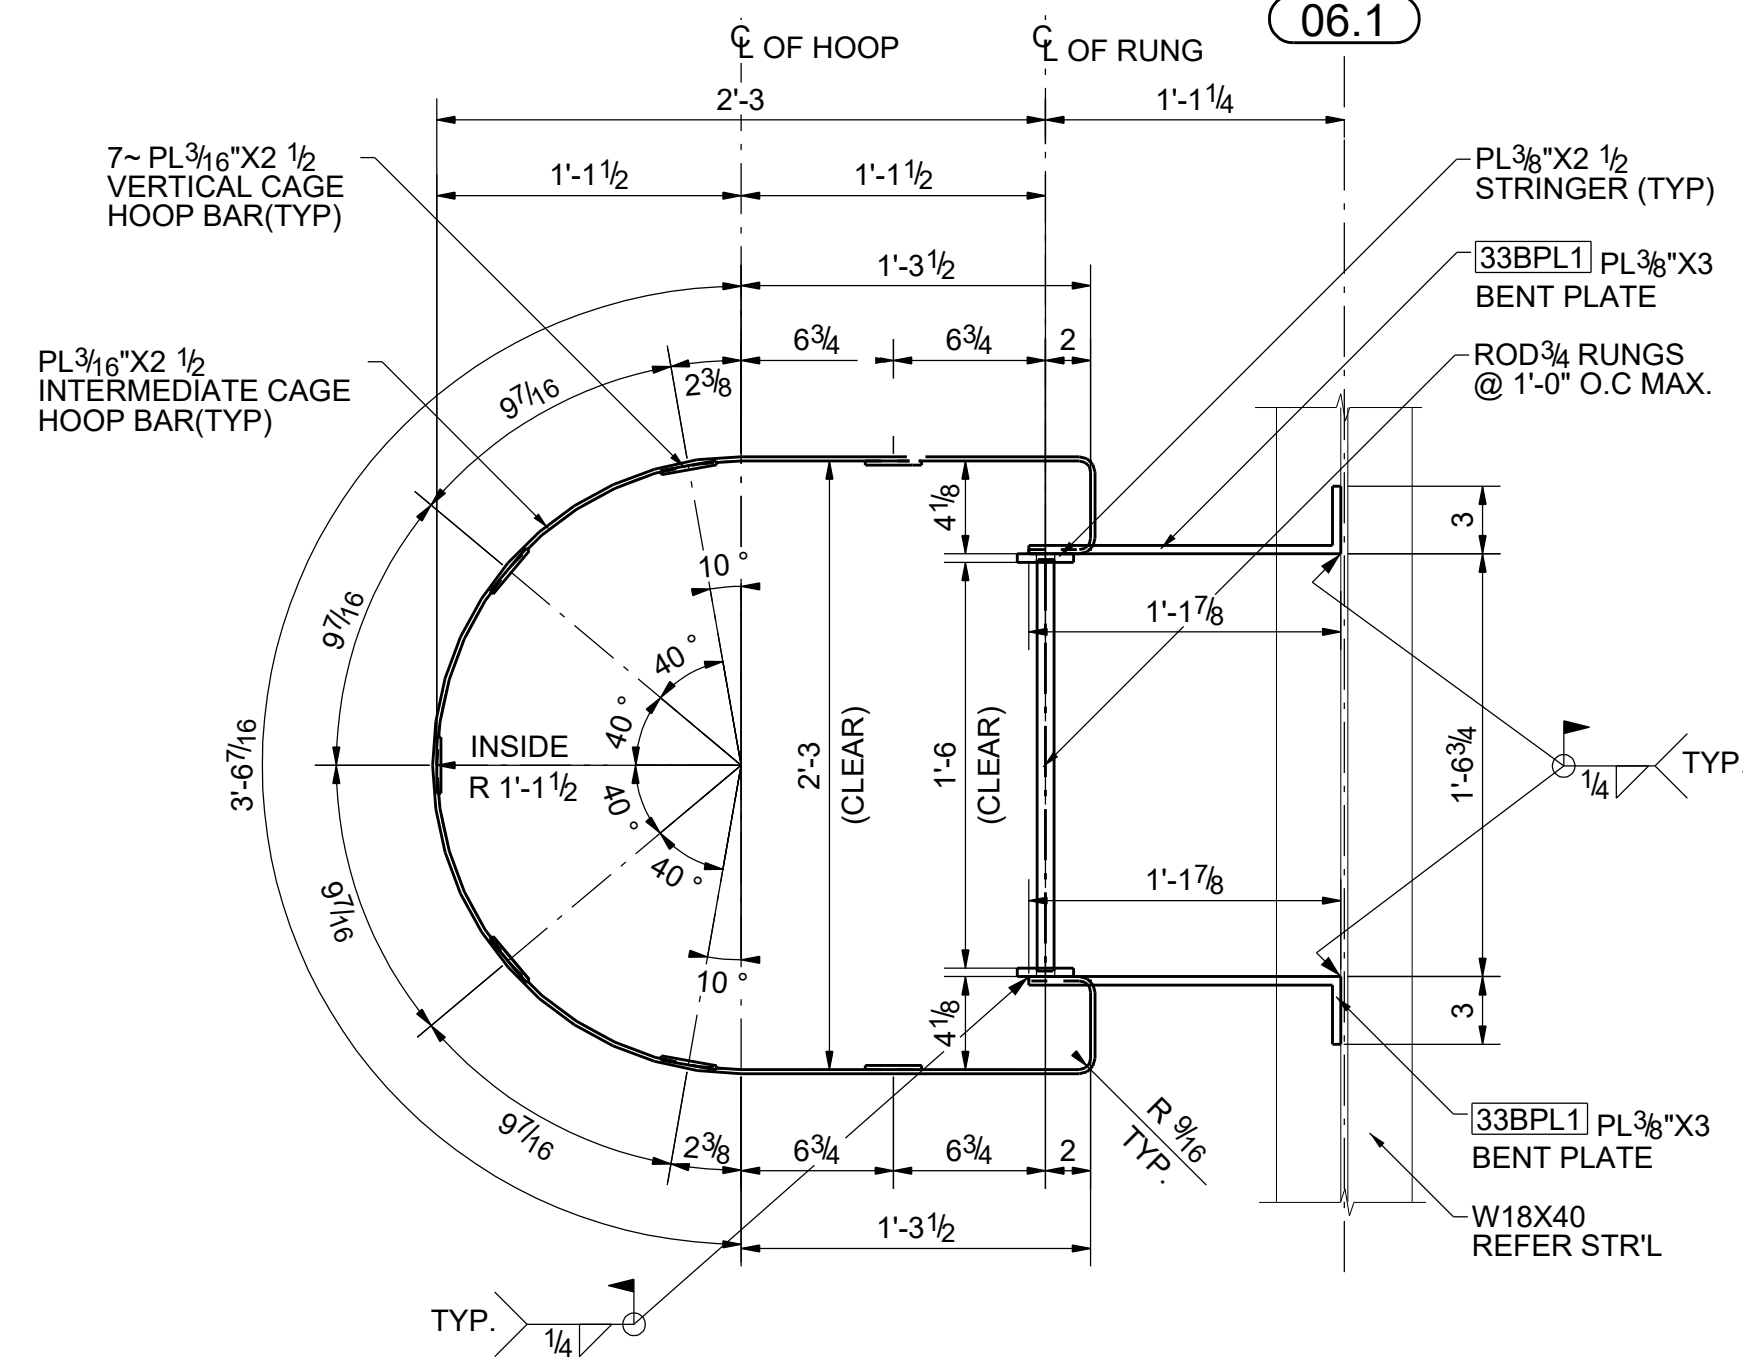


SECTION 2 - 2
33-E3301
INTERMEDIATE CAGE HOOP BAR DETAIL

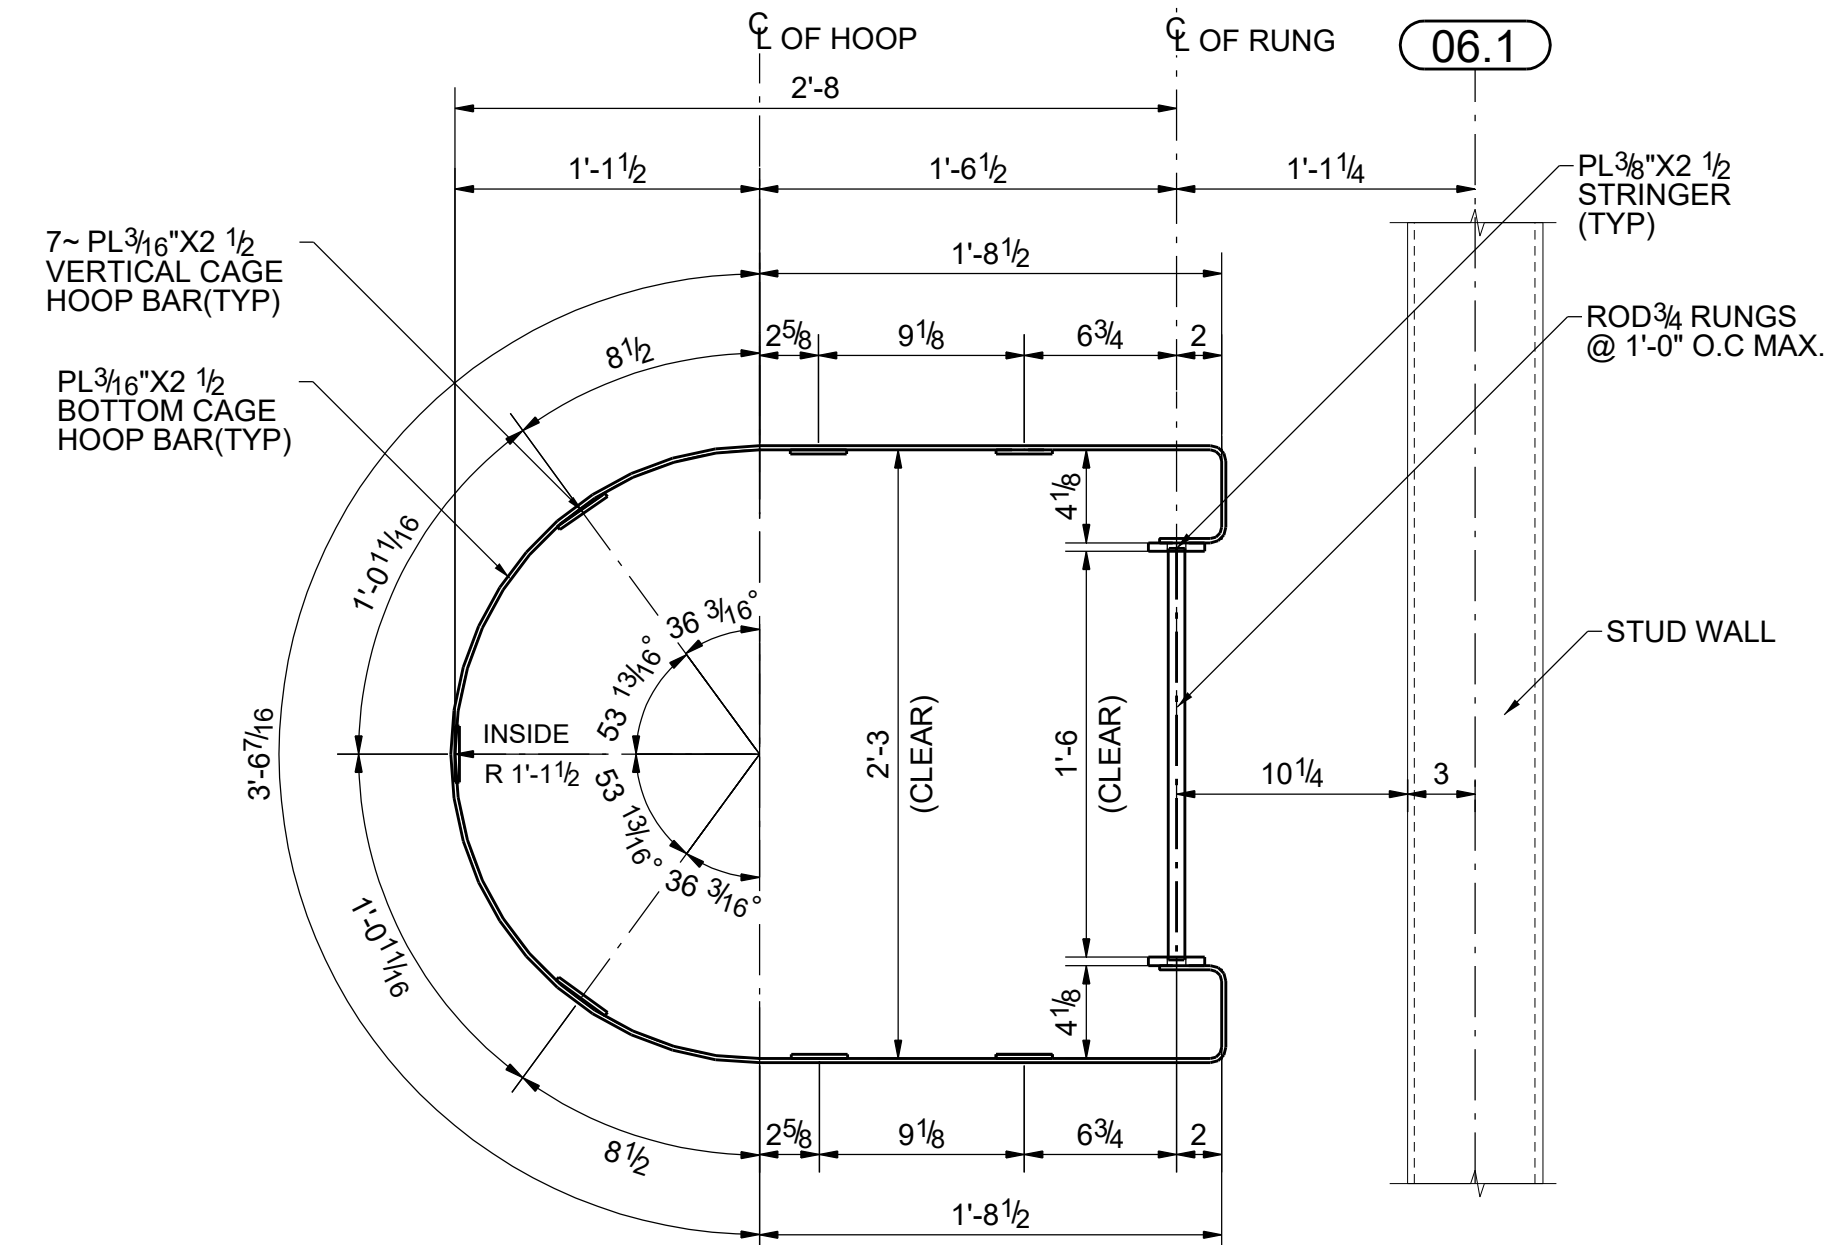


SECTION 3 - 3
33-E3301
BOTTOM CAGE HOOP BAR DETAIL

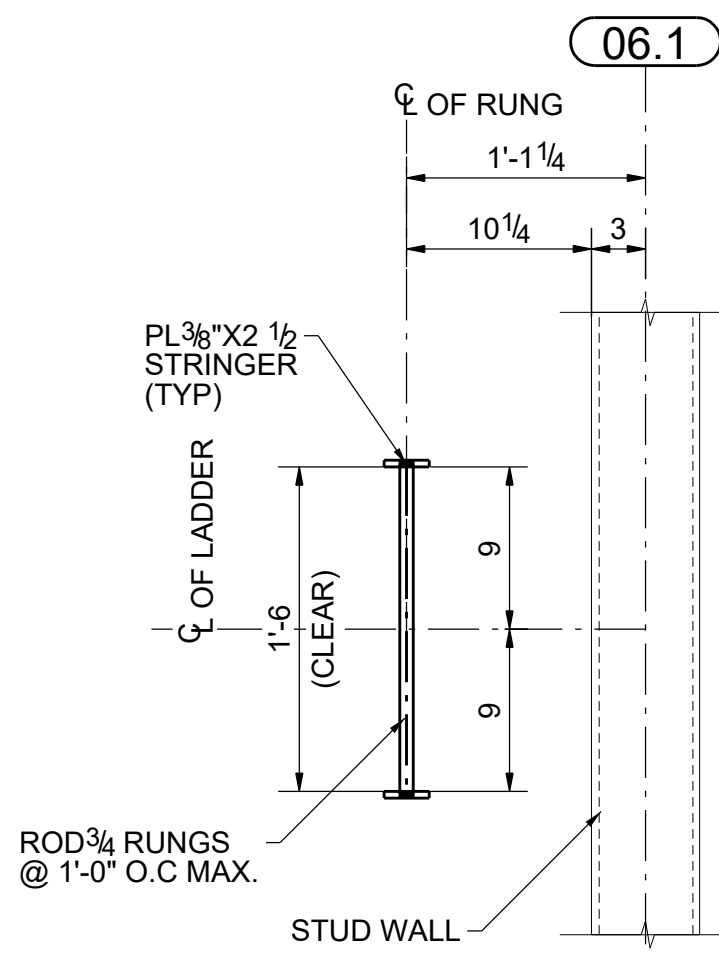


SECTION 4 - 4
33-E3301

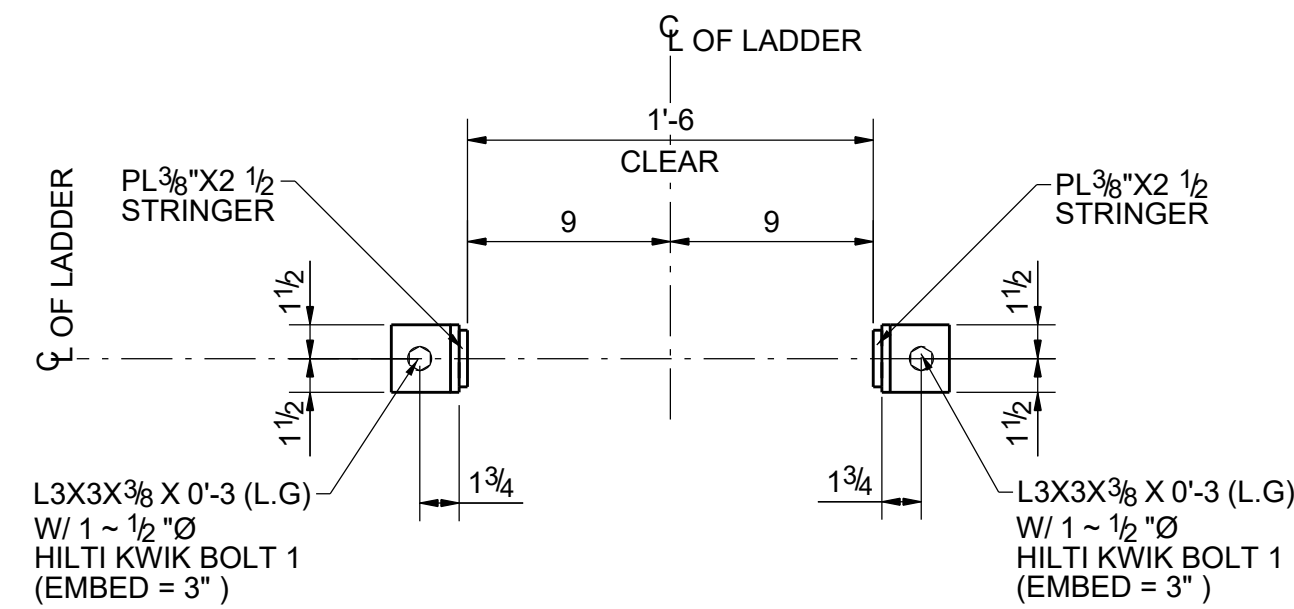

SECTION 5 - 5
33-E3301






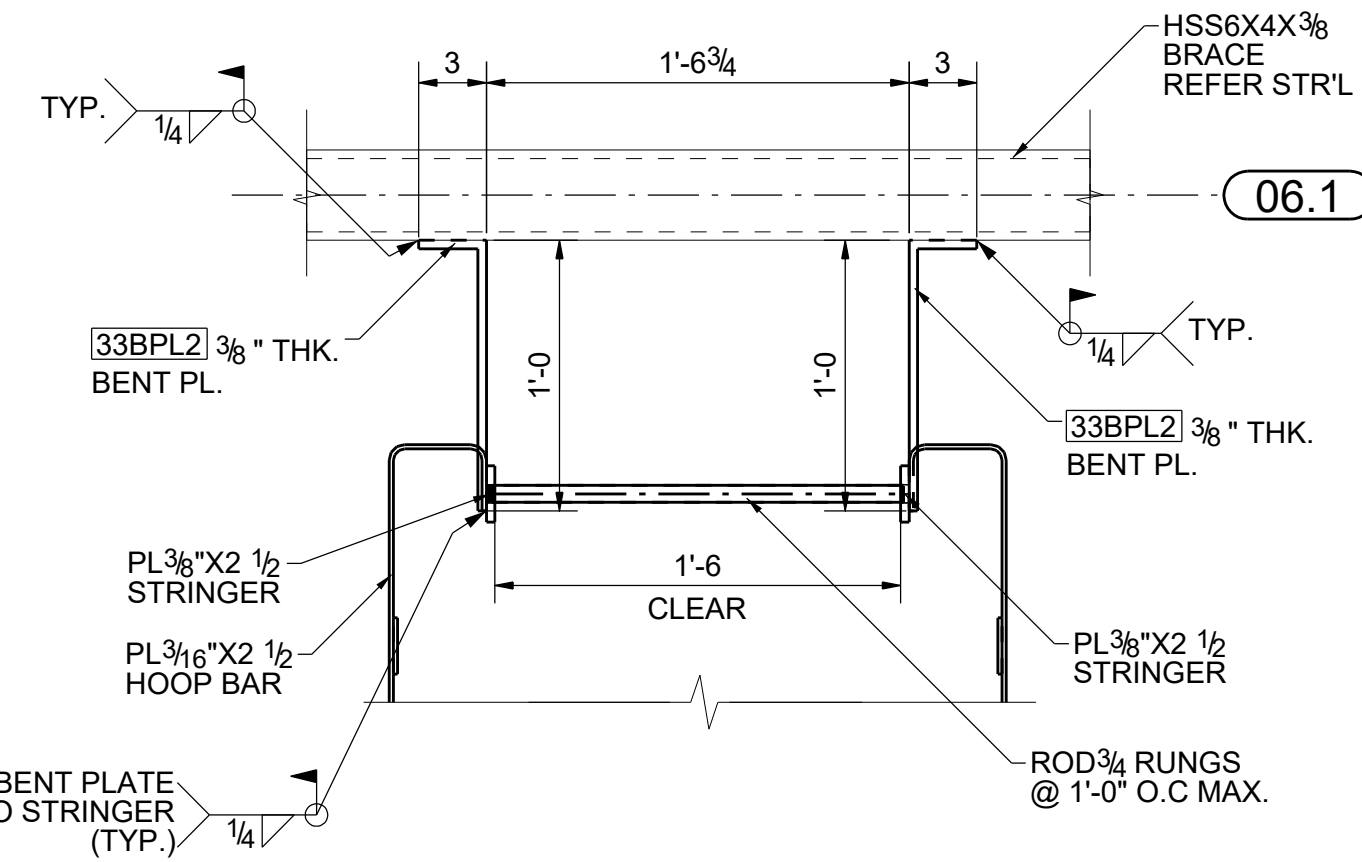


SECTION 6 - 6
33-E3301

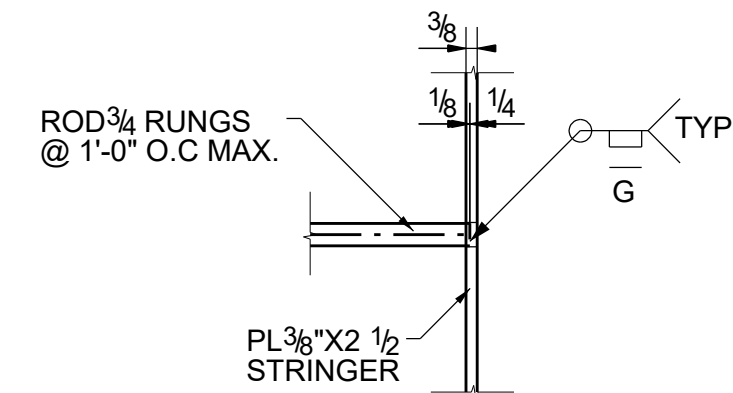

TYPICAL ROD RUNG CONNETION DETAIL

NOTES :
1. REFER SHEET 33-E3301 FOR ELEVATIONS.

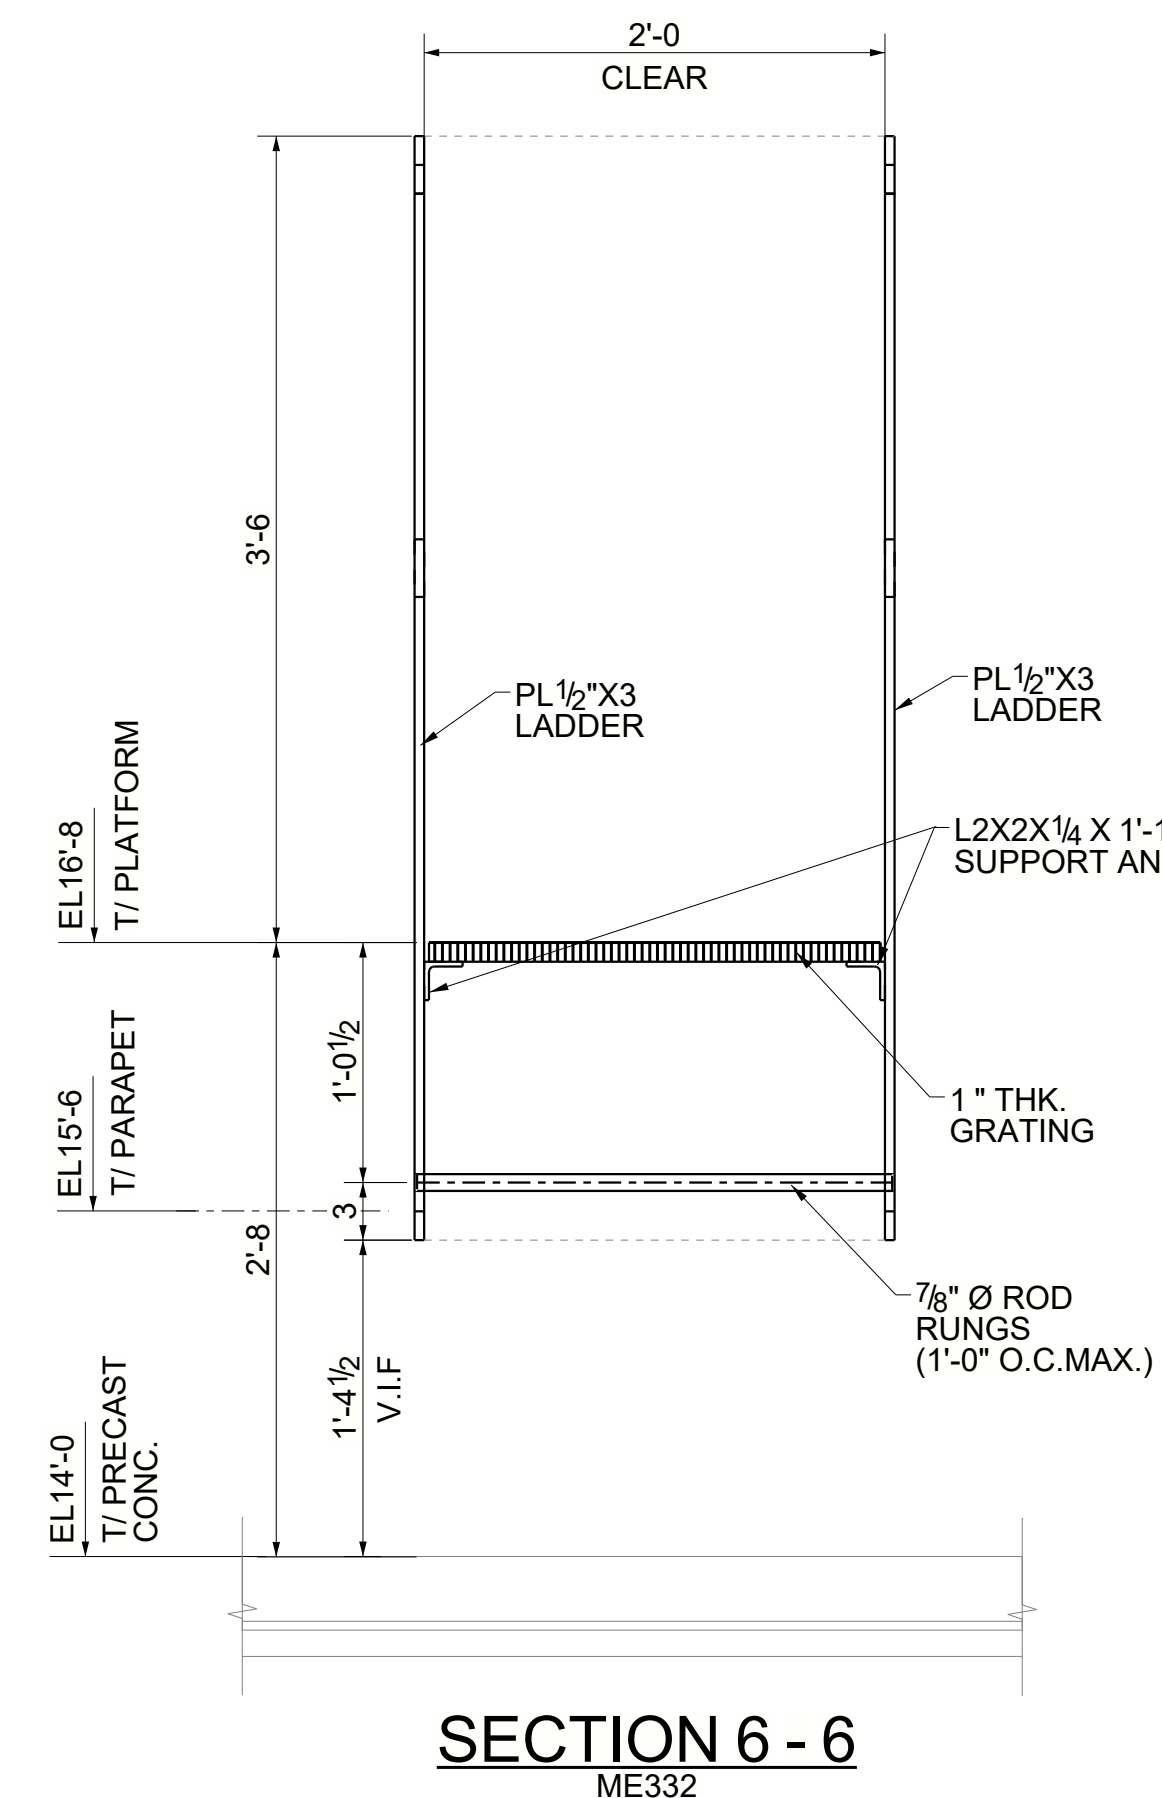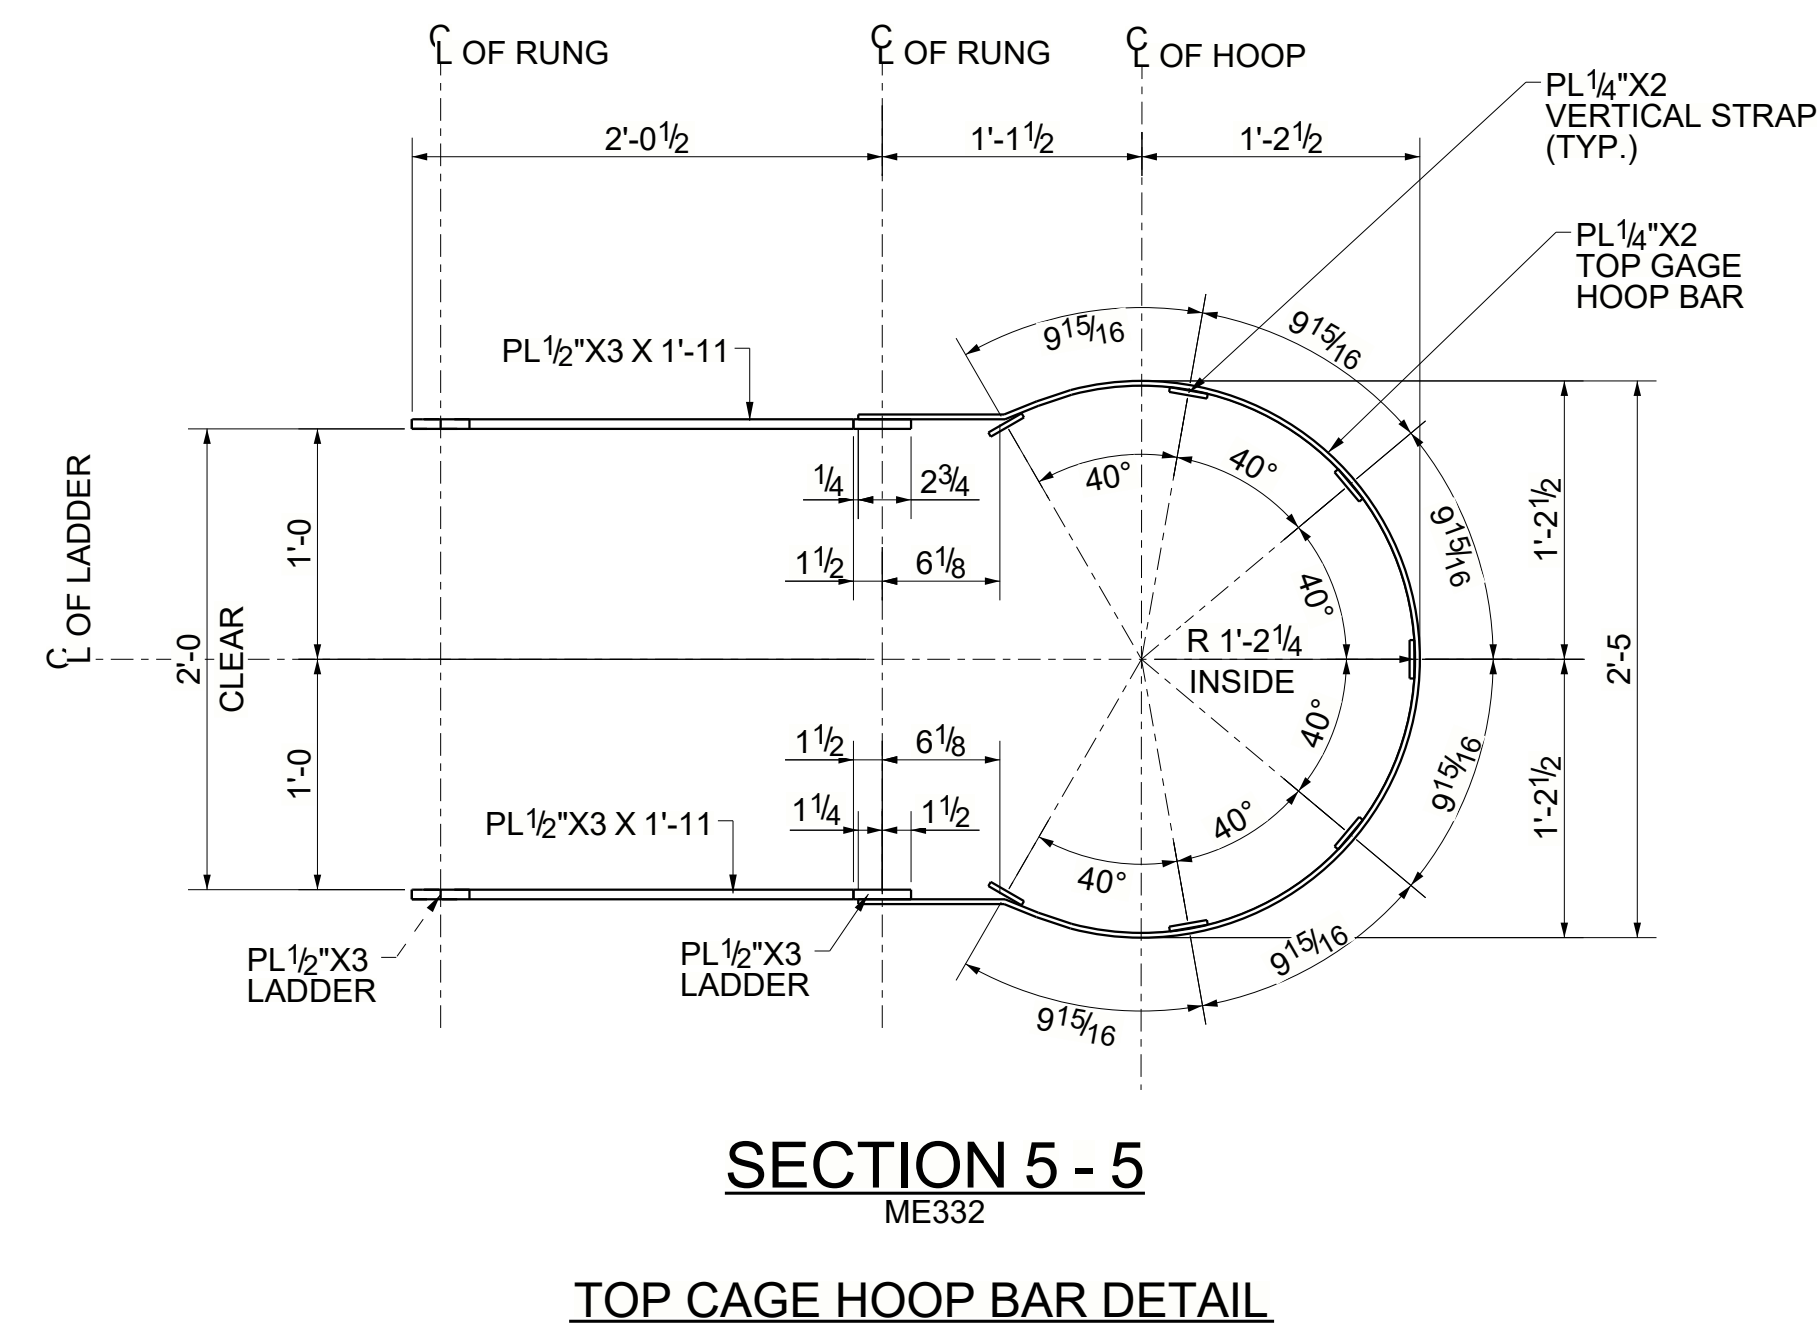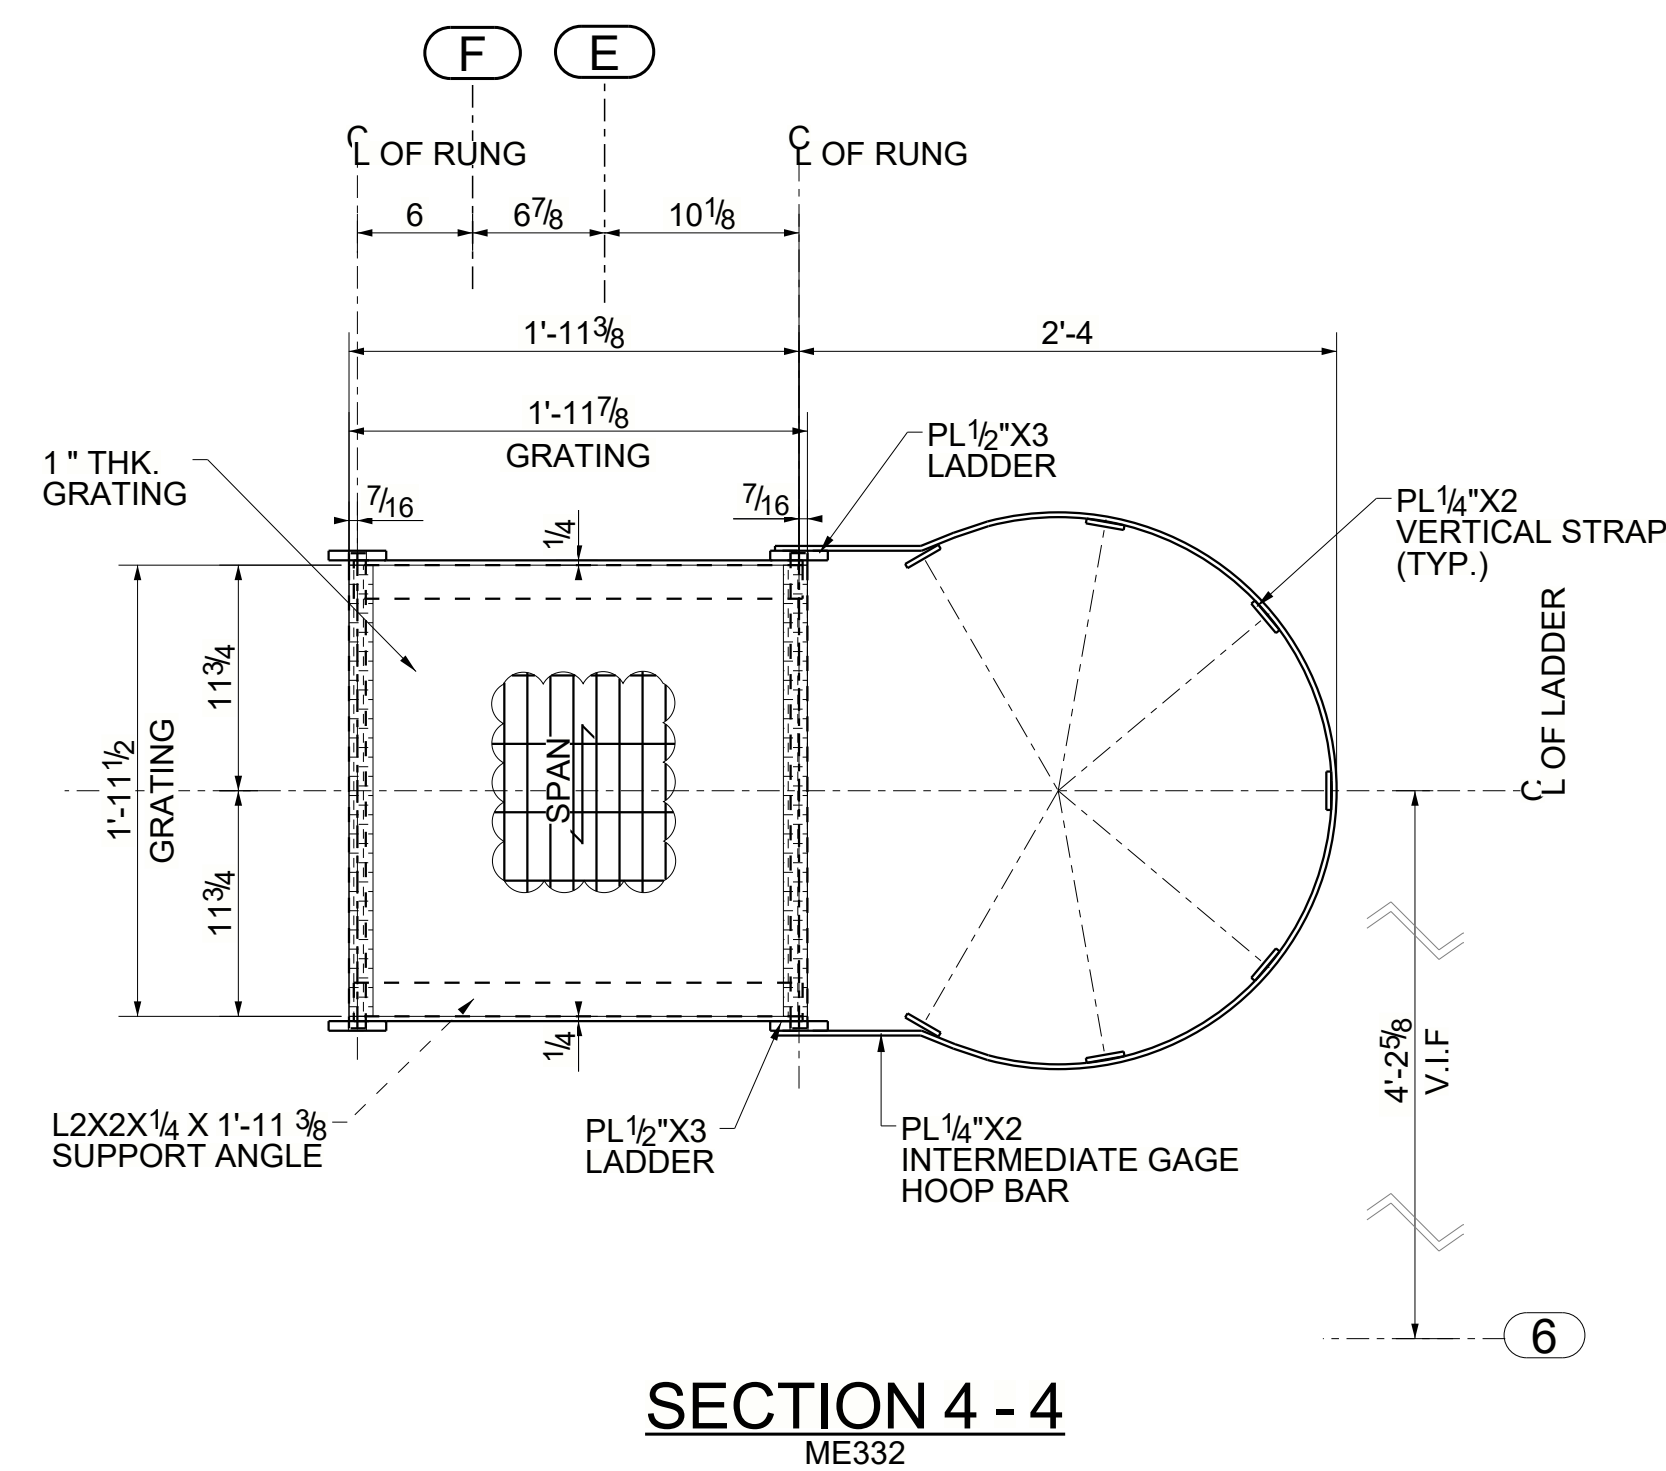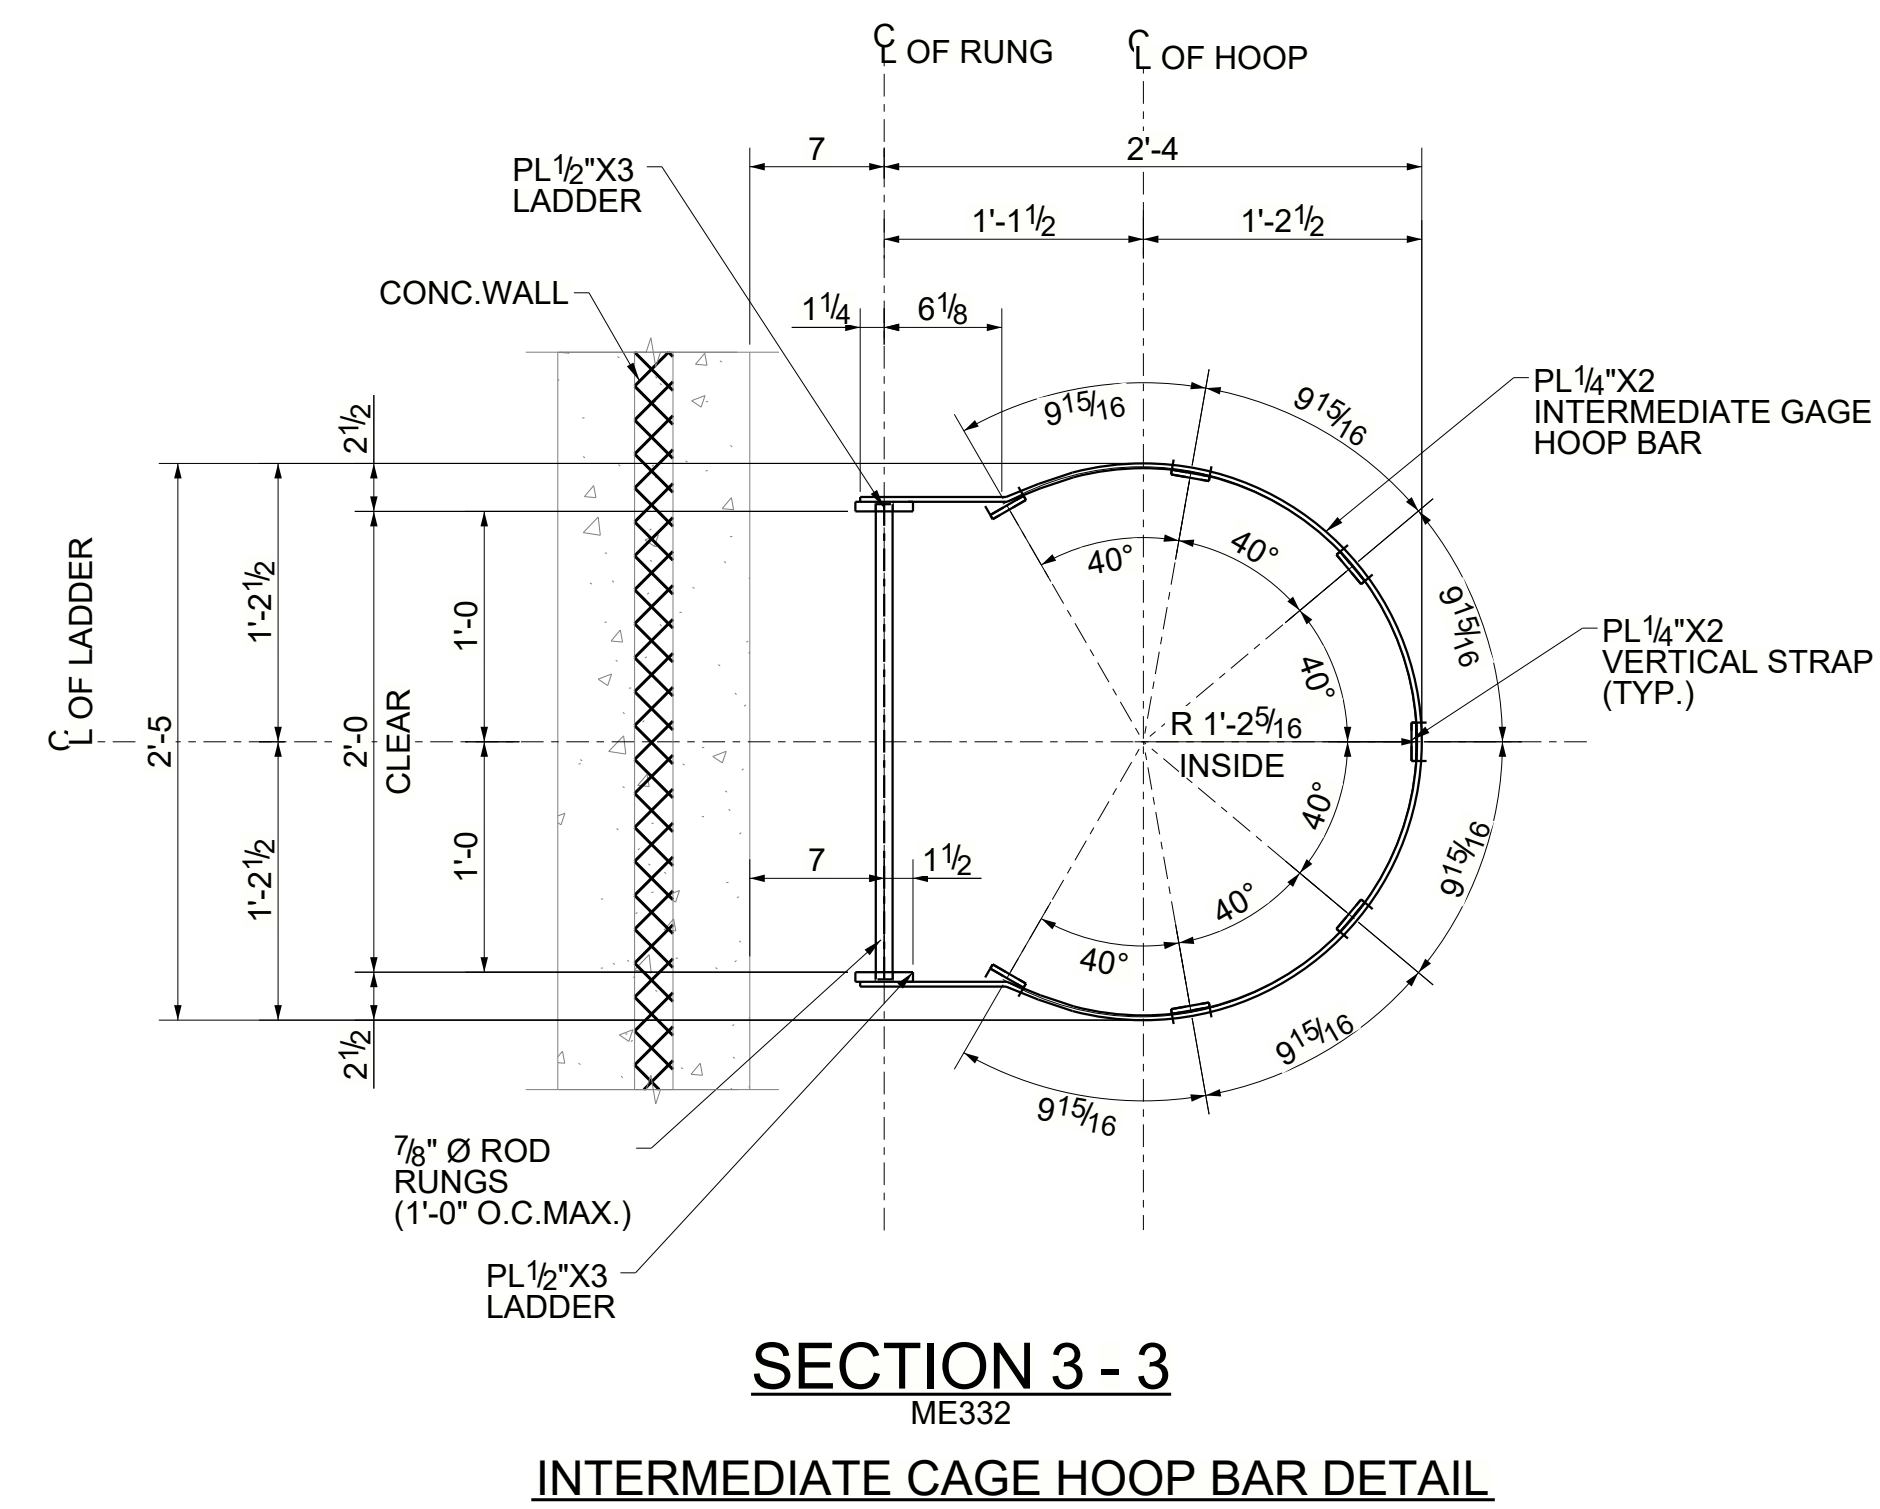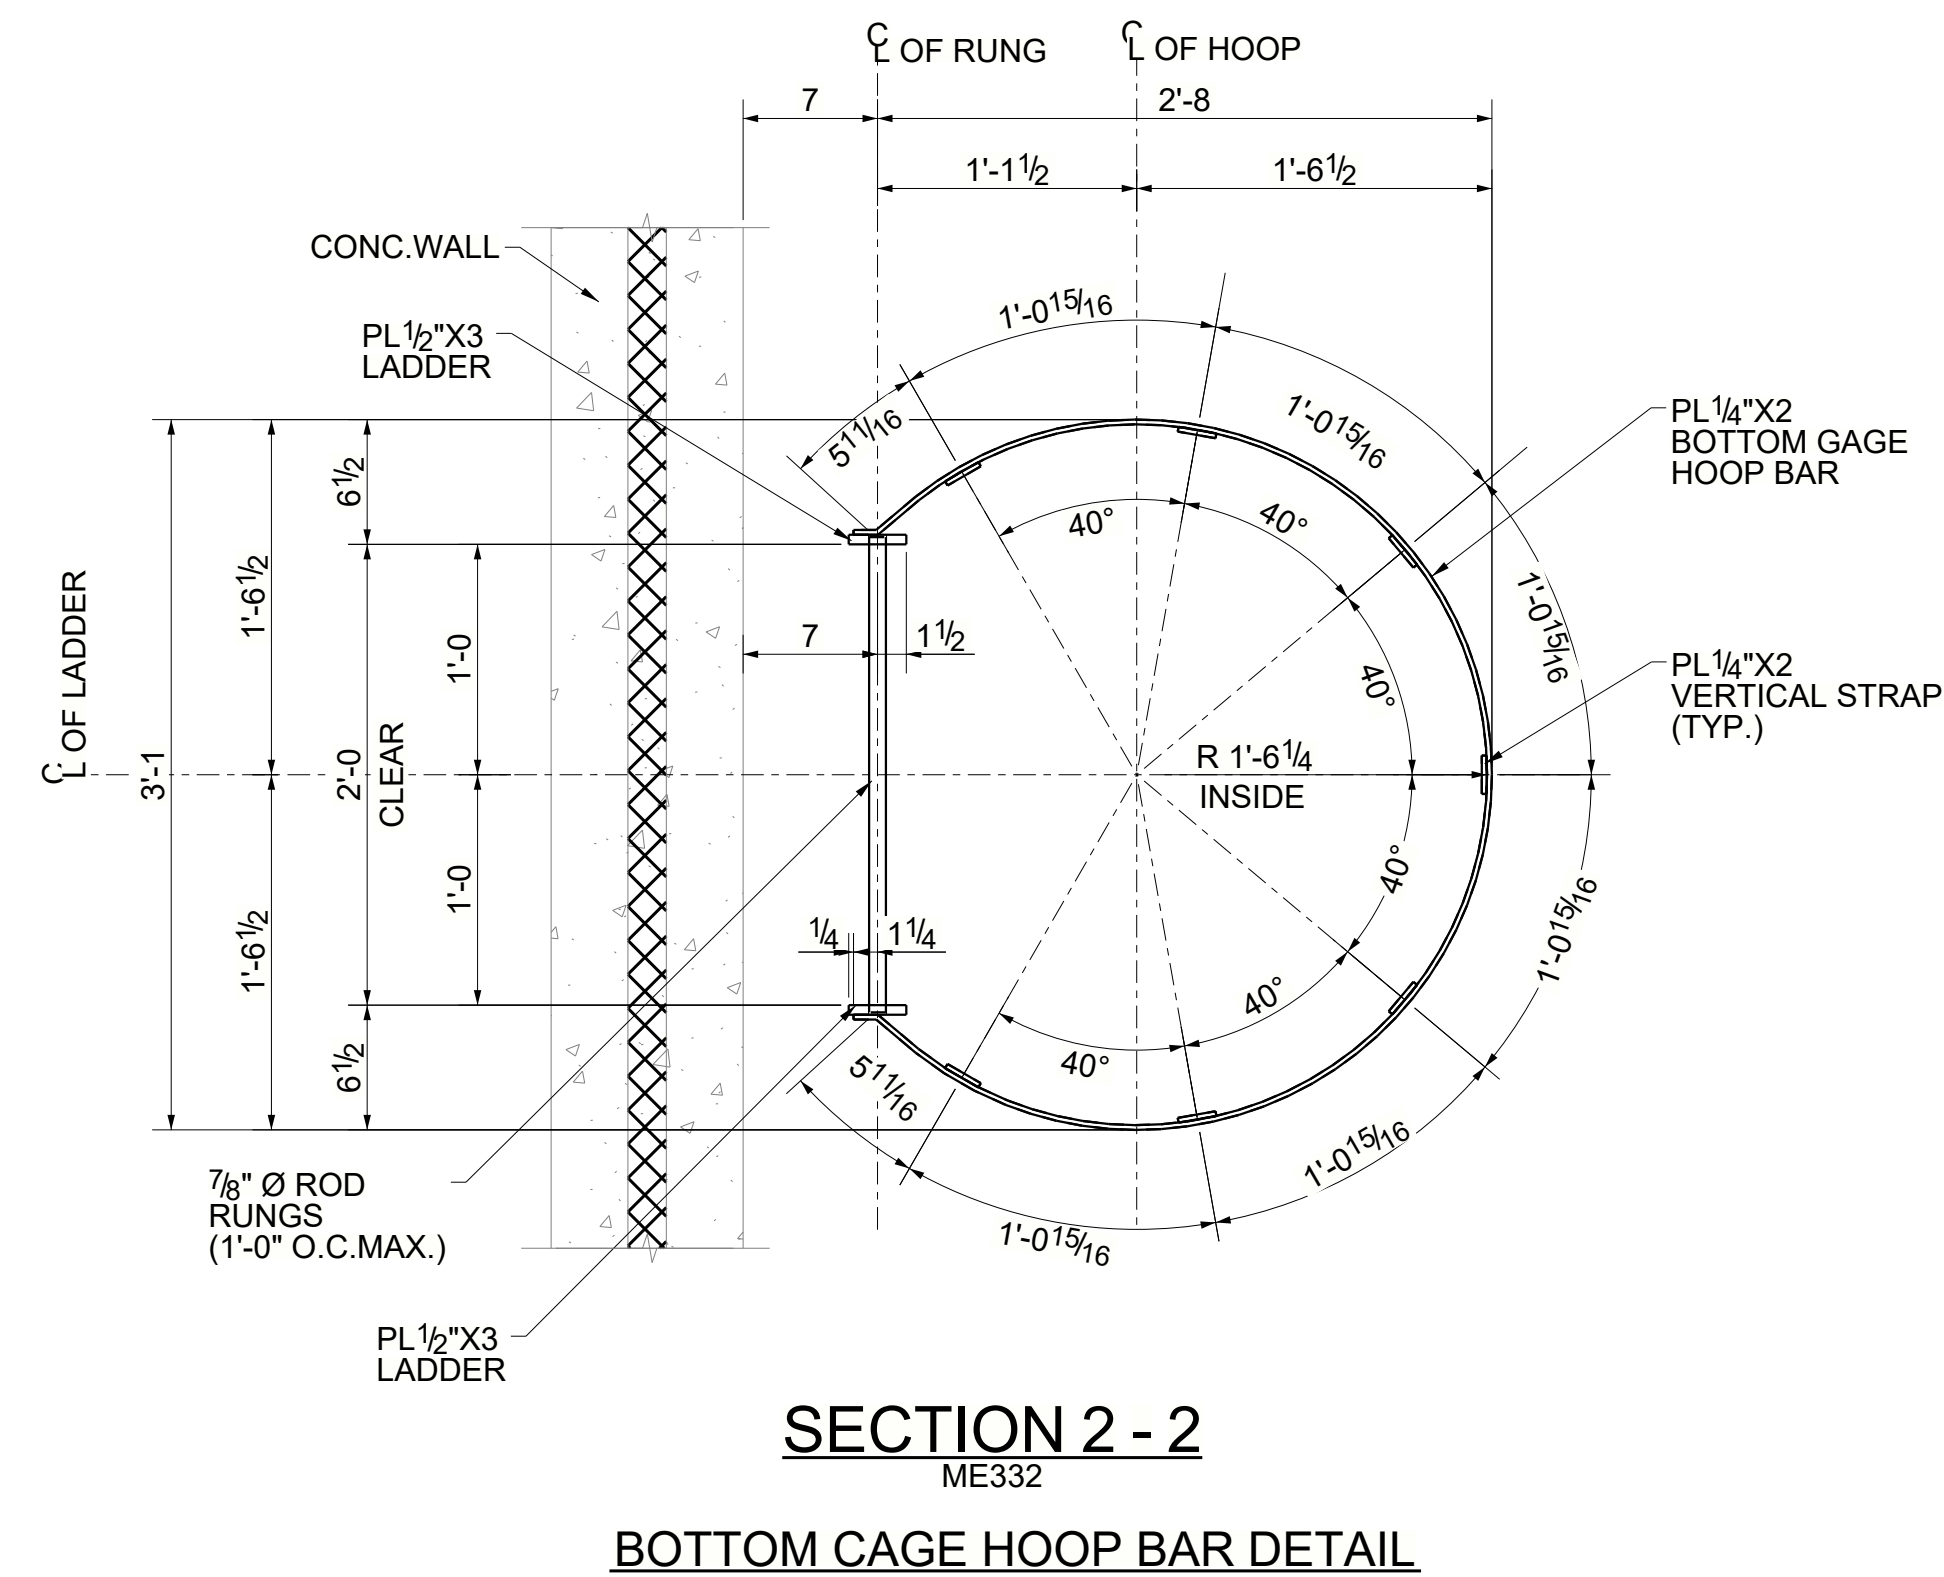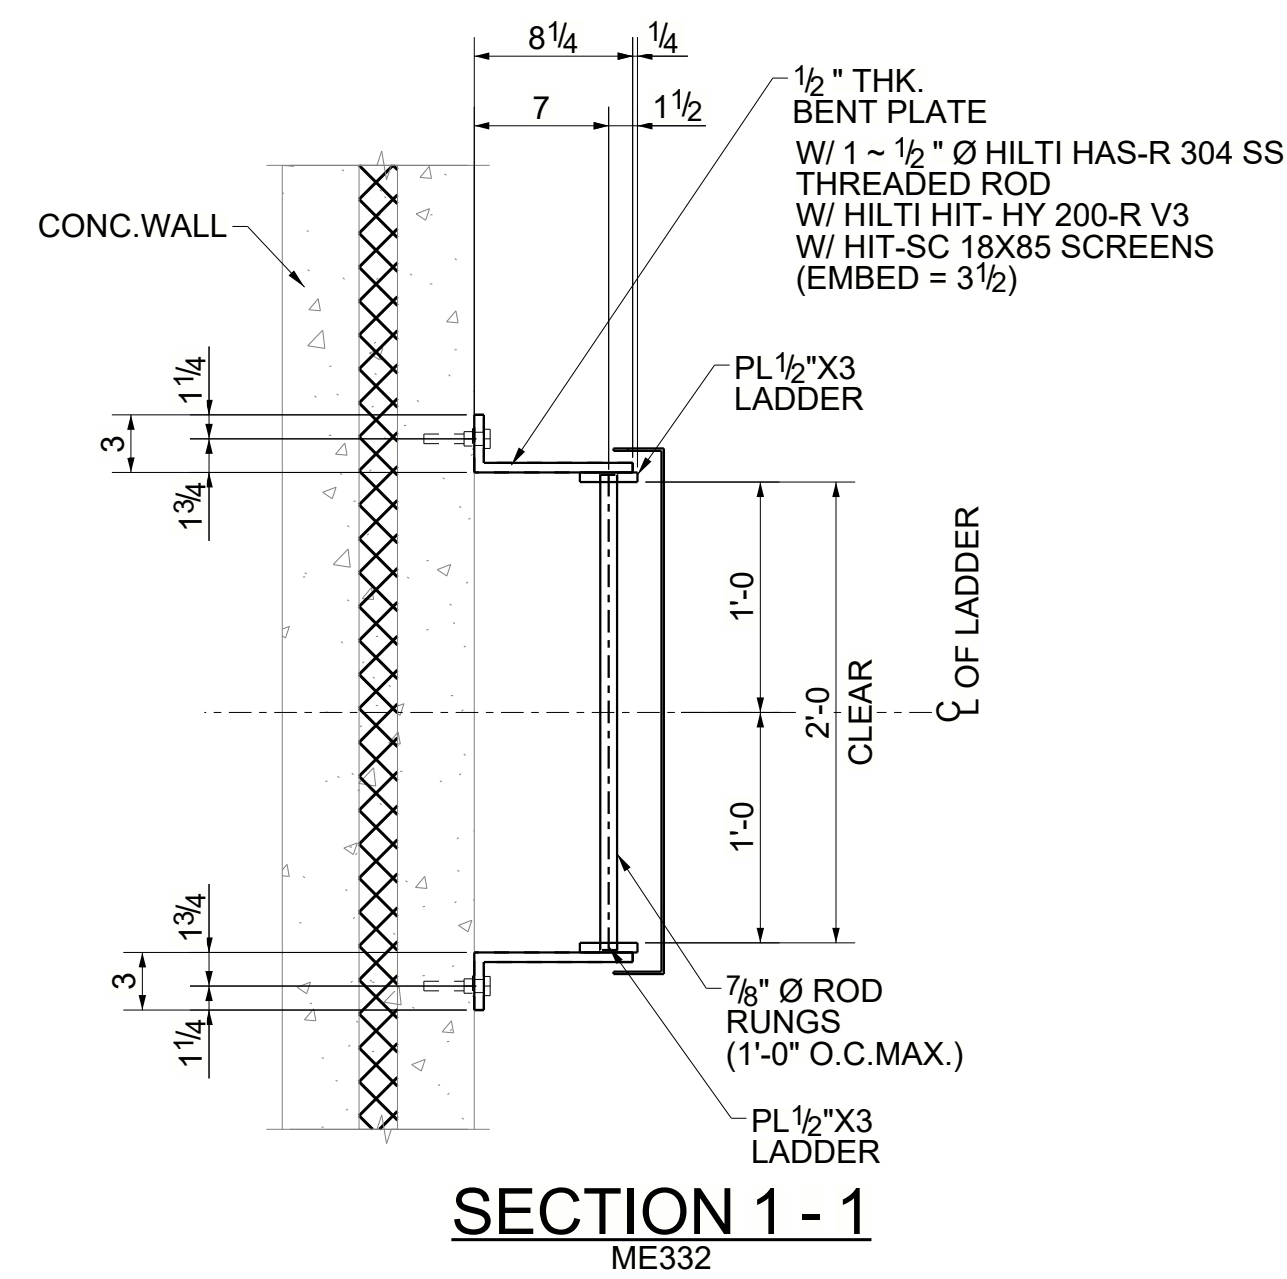

NOTES:-

1. REFER SHEET ME301 FOR KEY PLAN.
2. REFER SHEET ME332 FOR LADDER LOCATION PLAN & ELEVATION.
3. V.I.F - INDICATES VERIFY IN FIELD.

GRATING NOTE :

GRATING (McMICHOOLS) 19-W-4, 1X $3\frac{1}{16}$ METAL BAR
GRATING, BEARING BAR SPACED $13\frac{1}{16}$ O.C. AND CROSS BAR
@ 4" O.C. WITH CHECKERED PLATE NOSING.