





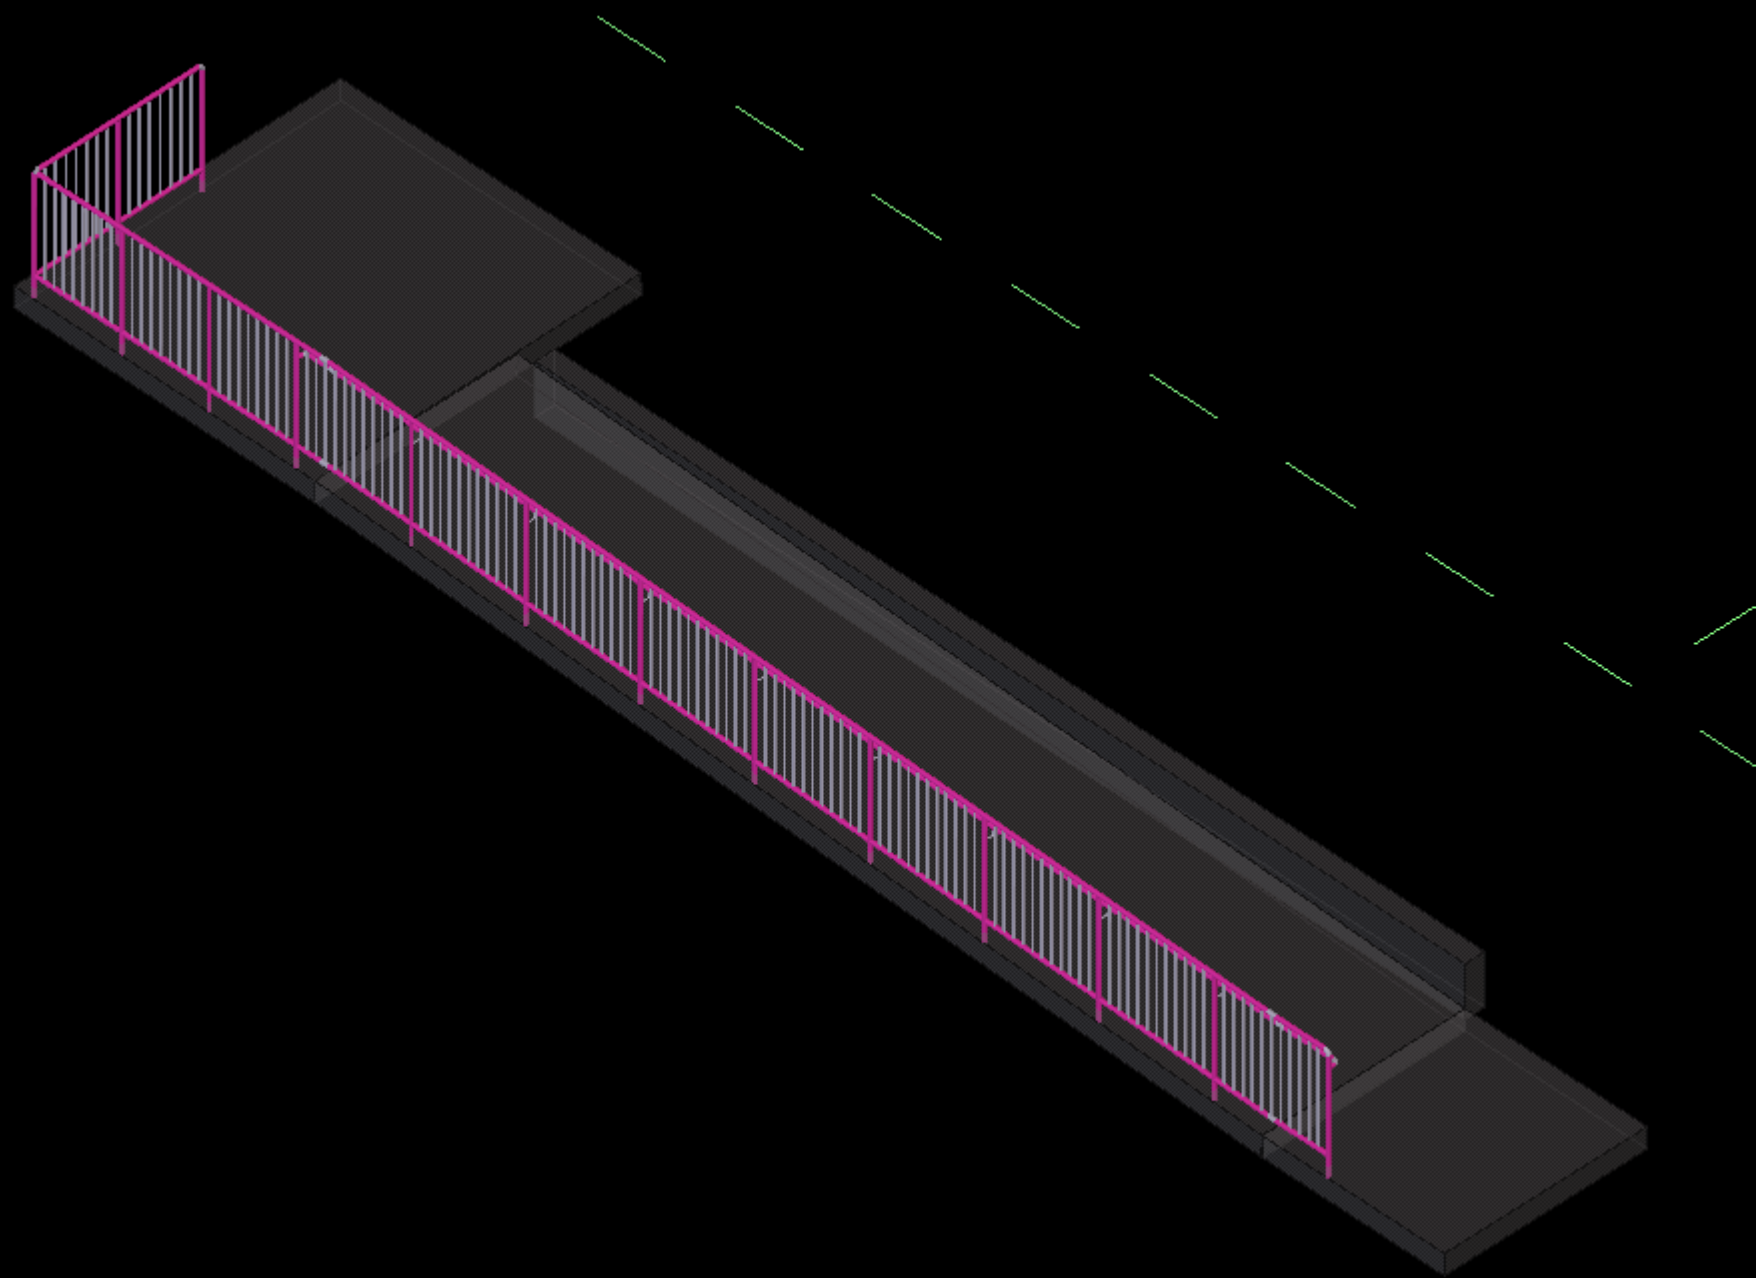

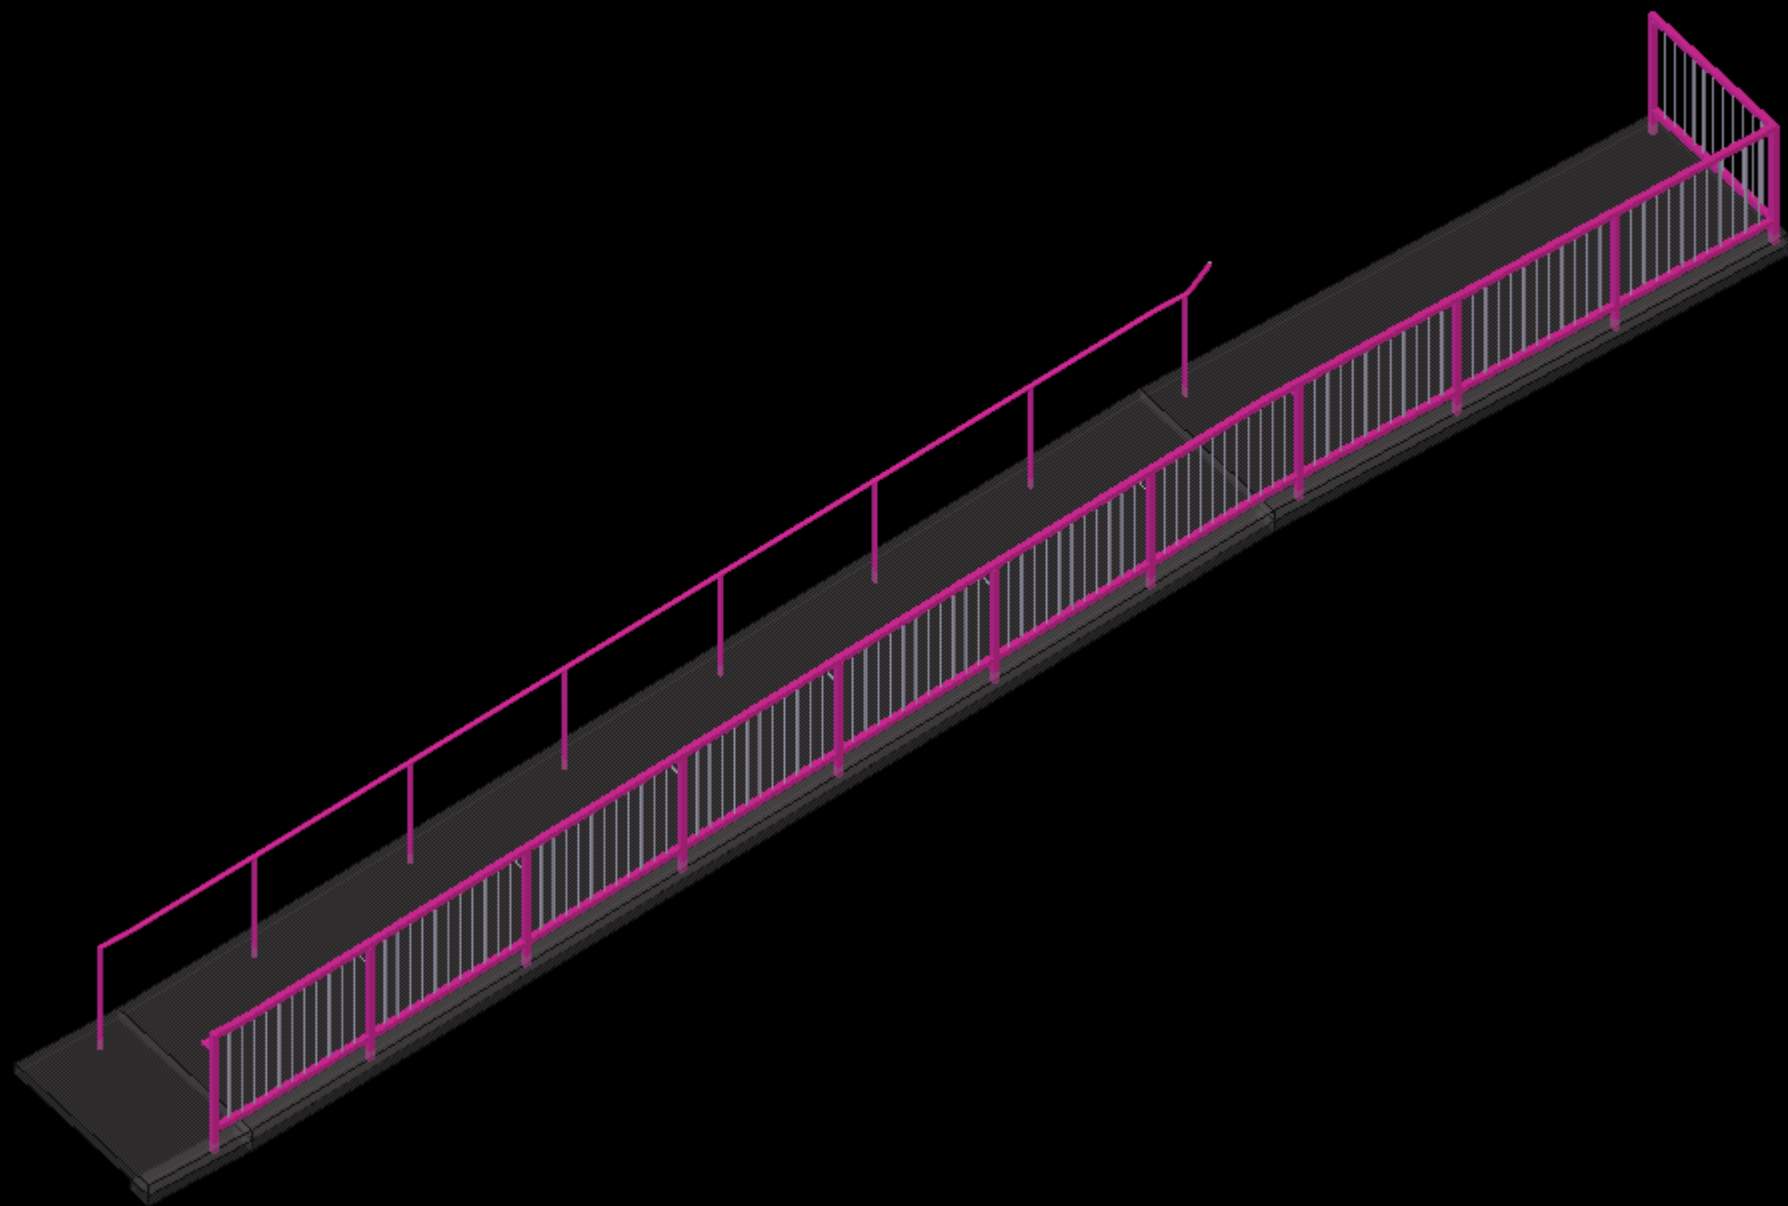


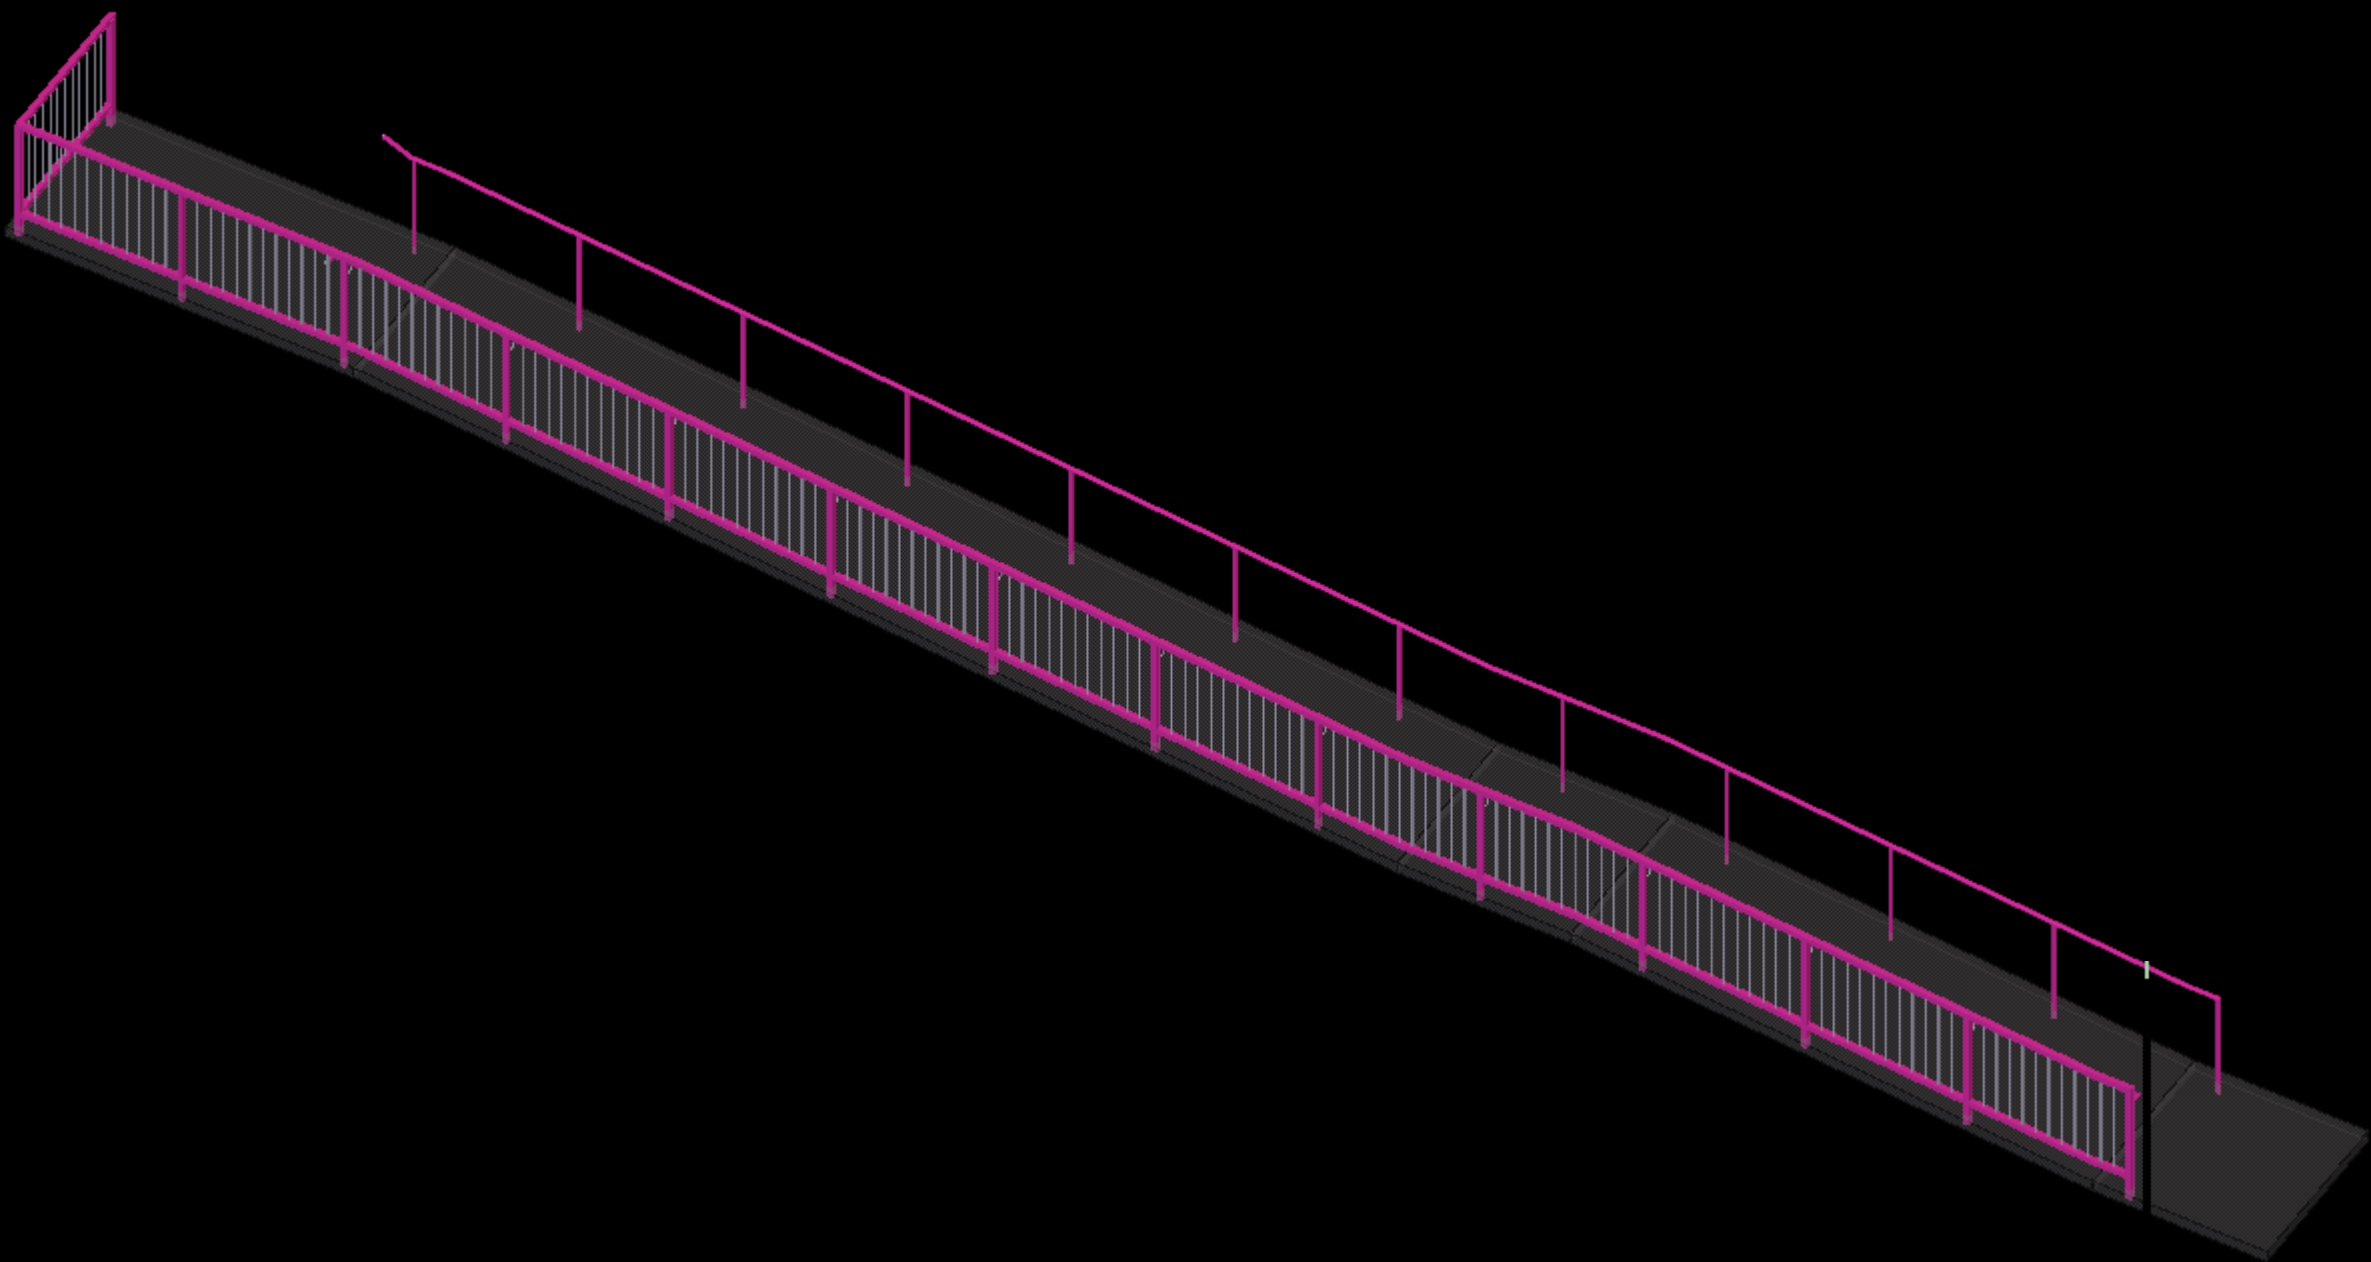

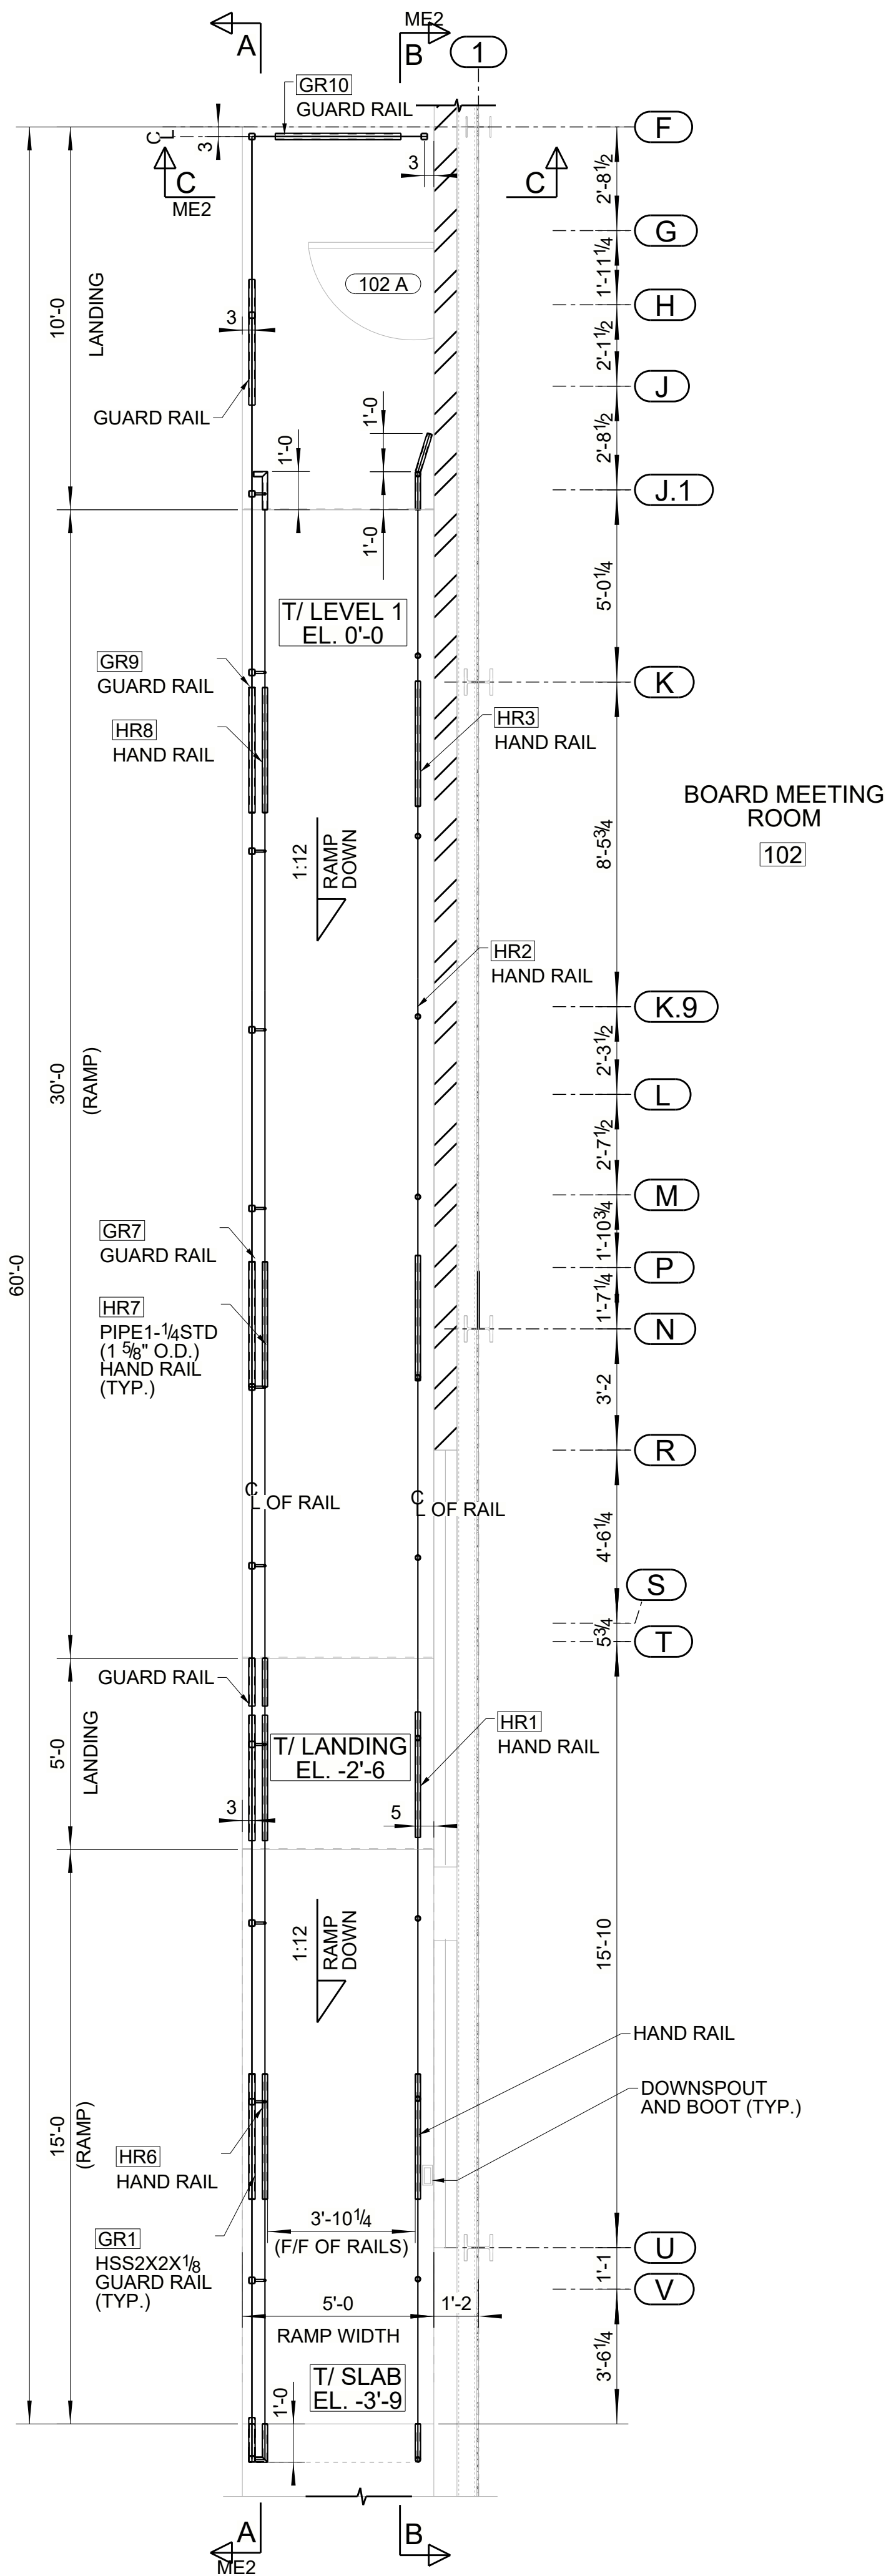

RAMP RAIL LOCATION PLAN

(REFER : COMPOSITE FLOOR PLAN- FIRST FLOOR-A2.10 & RAMP PLAN-7/A8.01)

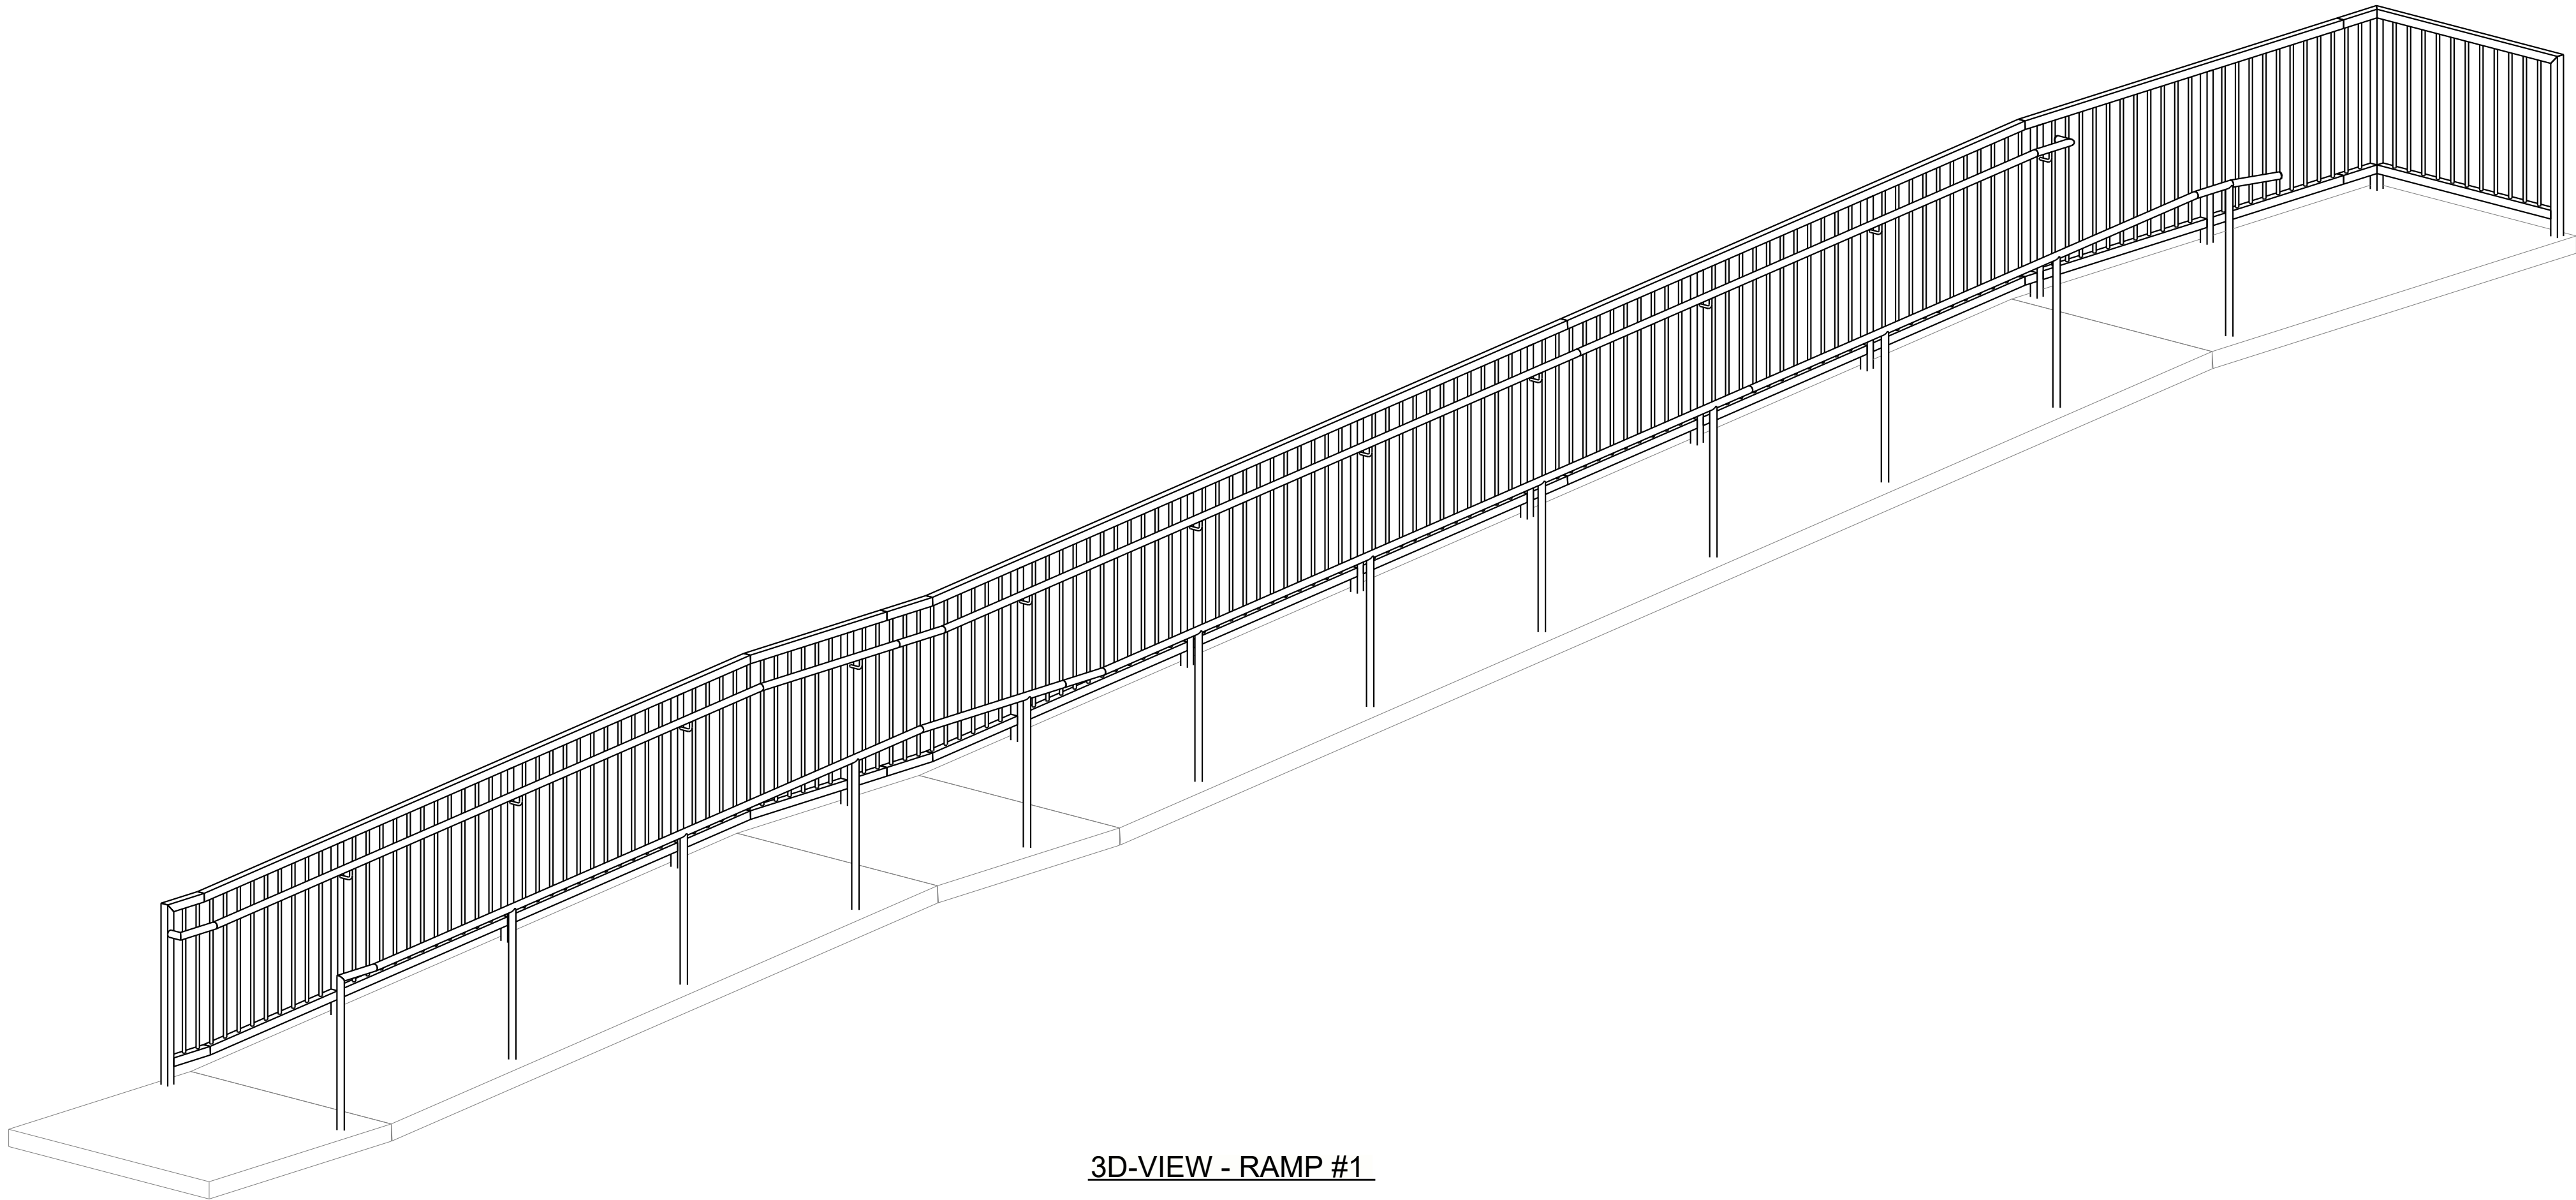

3D-VIEW - RAMP #1

NOTES :-


1. REFER SHEET ME0 FOR MISC. KEY PLAN.
2. REFER SHEET ME2 FOR ELEVATIONS.

FINISH DETAILS :

ALL RAMP RAIL STEEL MEMBERS
TO BE HOT DIP GALVANIZED

NOTE :

FIELD MEASURE PRIOR TO FABRICATION

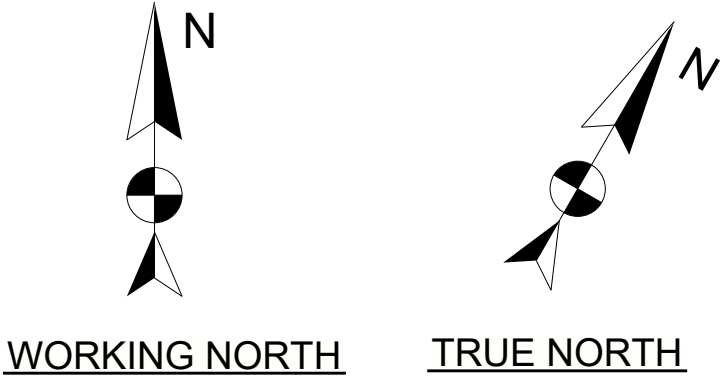

FOR FIELD USE : 08/29/2022


ELECTRODE	E70XX	UNLESS NOTED
HOLES	13/16 Ø	UNLESS NOTED
PAINT	SEE PLAN	

REVISION

0

DRAWING NUMBER:

ME1

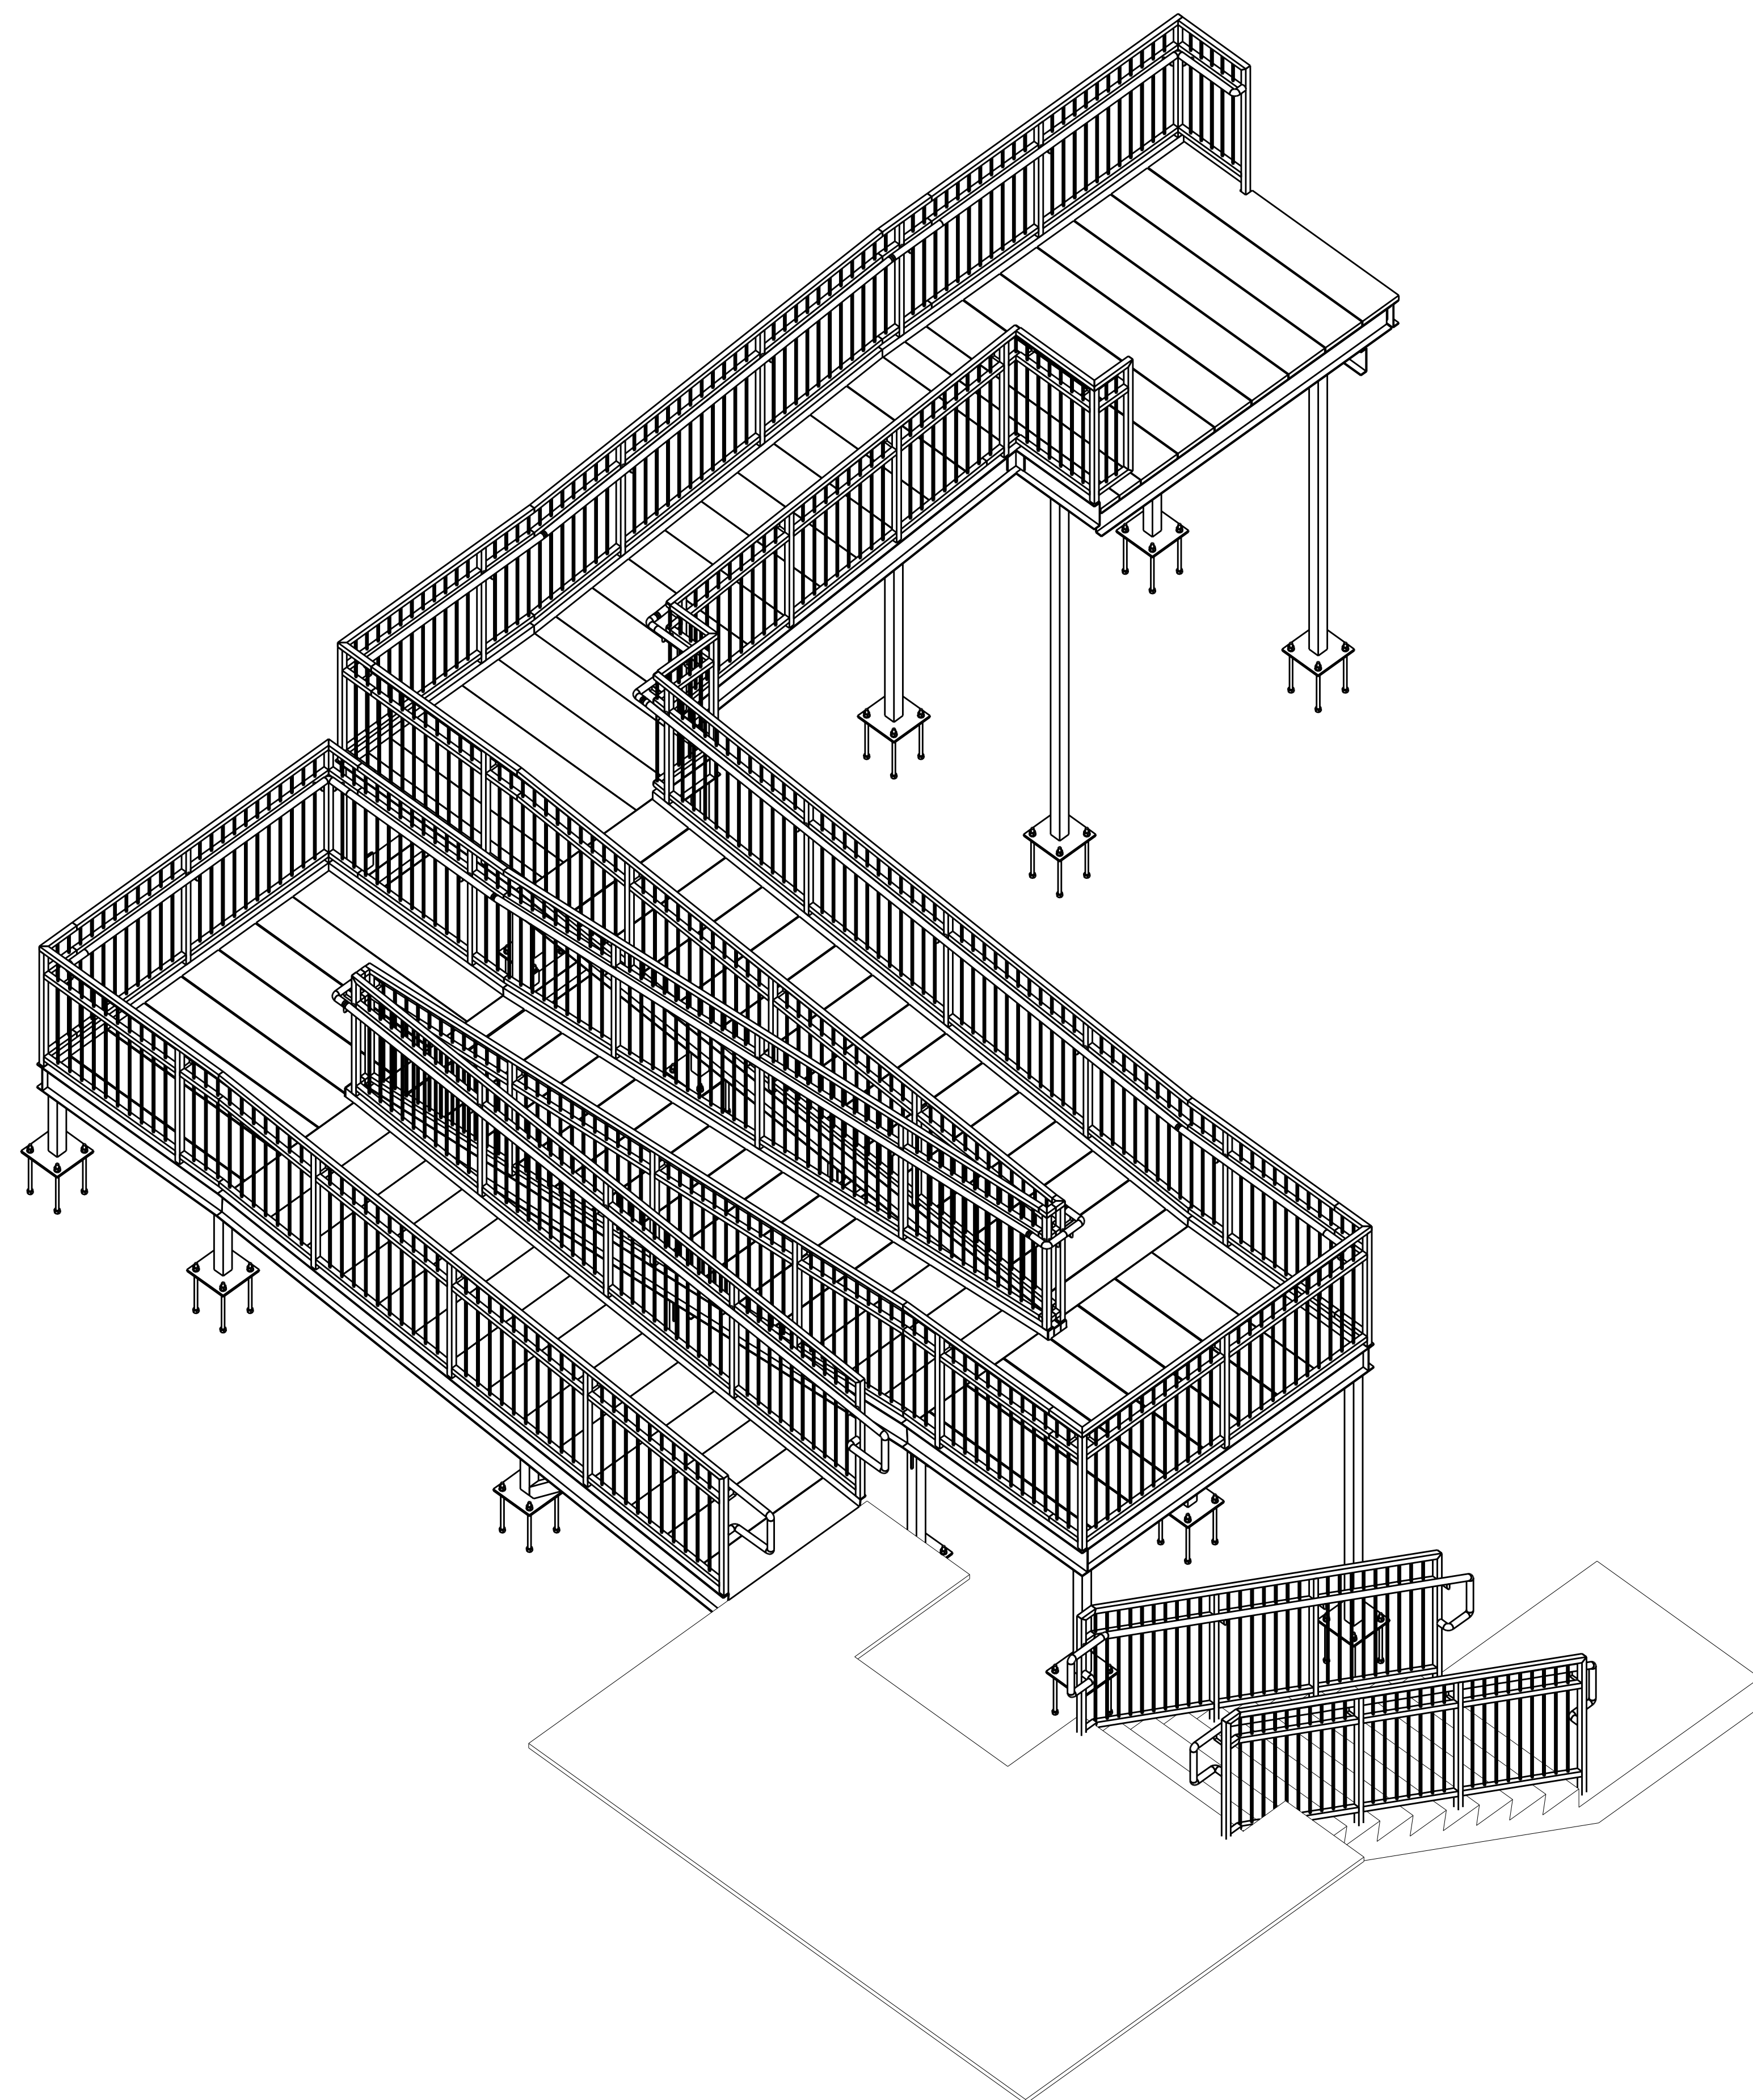

3D-VIEW



ERECTOR NOTES :-

- 1) THESE DRAWINGS ARE FOR THE ERECTION OF STEEL PROVIDED BY PADUCAH PRODUCTIONS AND NOT FOR USE BY OTHERS TRADES.
- 2) ALL HSS MATERIAL = A500 GR. B
ALL PIPE MATERIAL = A53
ALL OTHER MATERIALS = A36
- 3) REFER TO ERECTION PLANS FOR PIECE MARKS AND OTHER INFORMATION

ALL STEEL WILL RECEIVE ONE COAT
GRAY SHOP PRIMER. (U.N.O)

GENERAL NOTES :-

1. FINISH FLOOR ELEVATION = 549.66' = 0'-0 = DATUM ELEVATION
2. ▼ - INDICATES ORIENTATION OF MEMBERS
3. (B) INDICATES BELOW

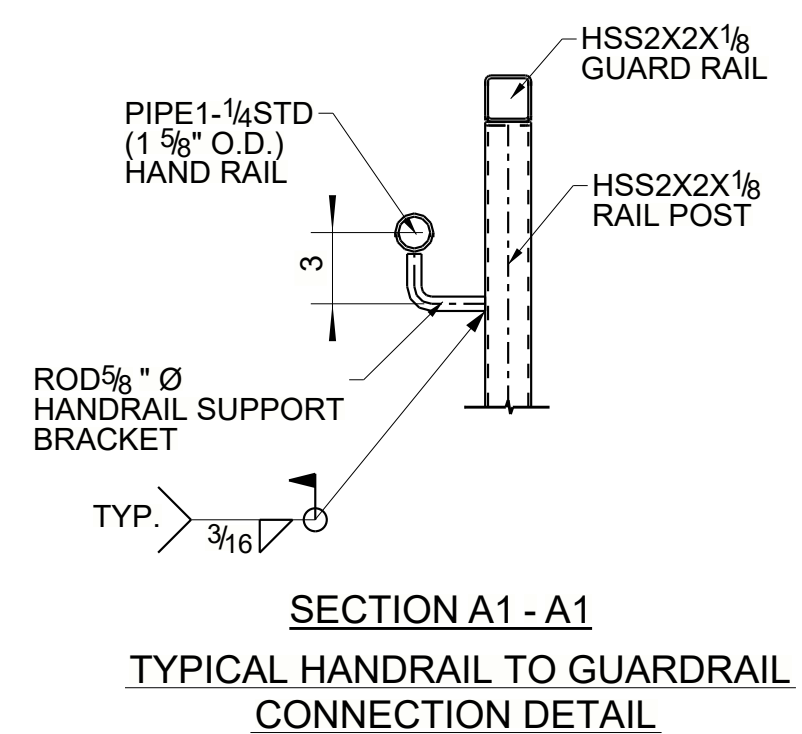
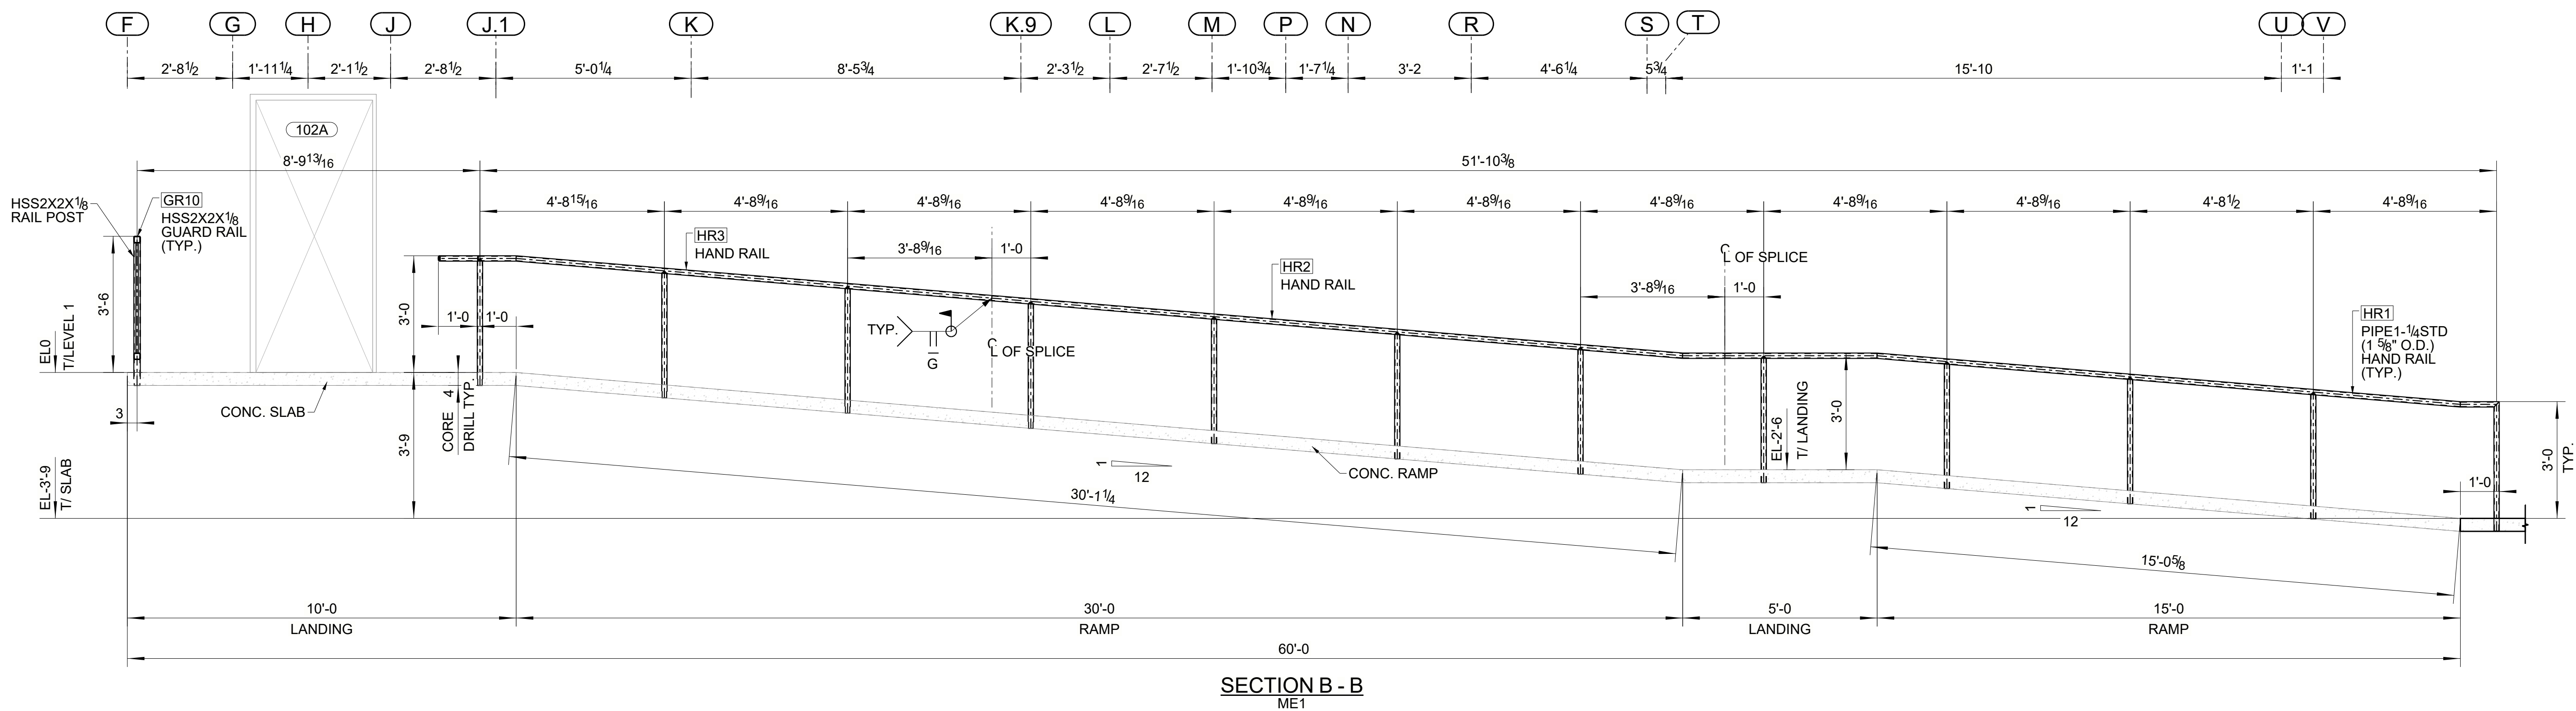


NOTE :
FIELD MEASURE PRIOR TO FABRICATION


ELECTRODE	<u>E70XX</u>	UNLESS NOTED
HOLES	<u>13/16 Ø</u>	UNLESS NOTED
PAINT	SEE PLAN	



ME2

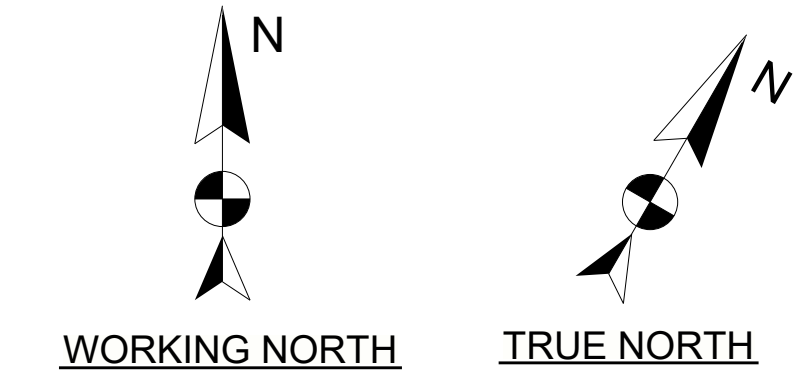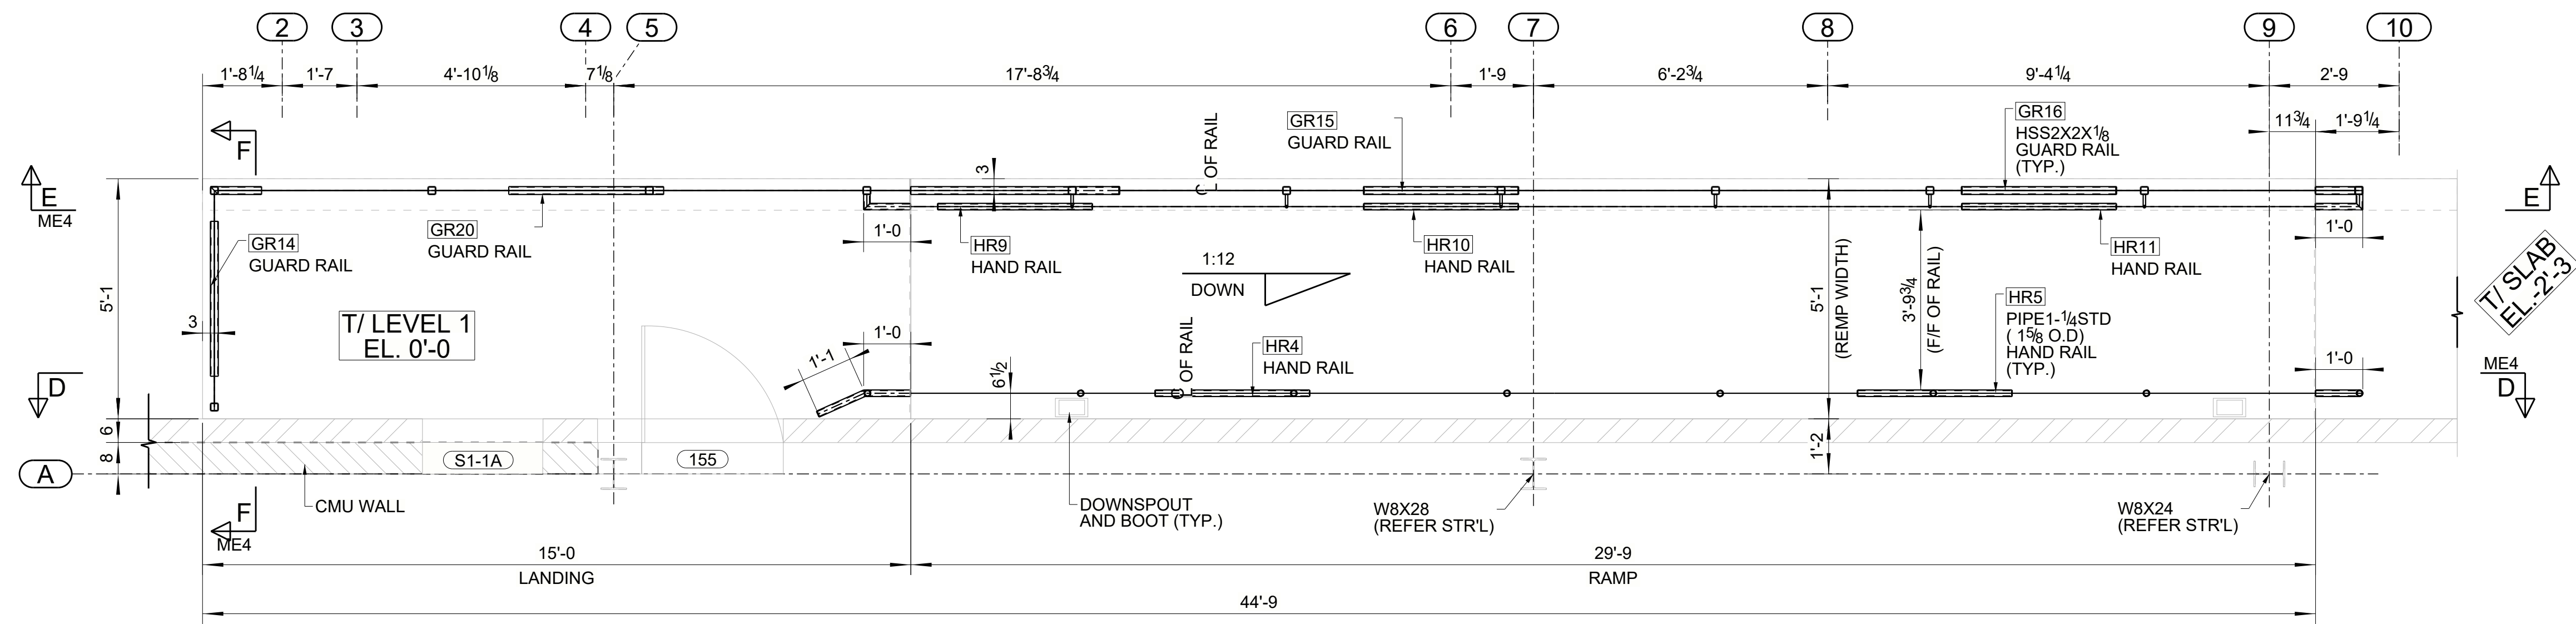

RAMP RAIL LOCATION PLAN
(REFER : COMPOSITE FLOOR PLAN- FIRST FLOOR- A2.10 & RAMP PLAN-8/ A8.01)

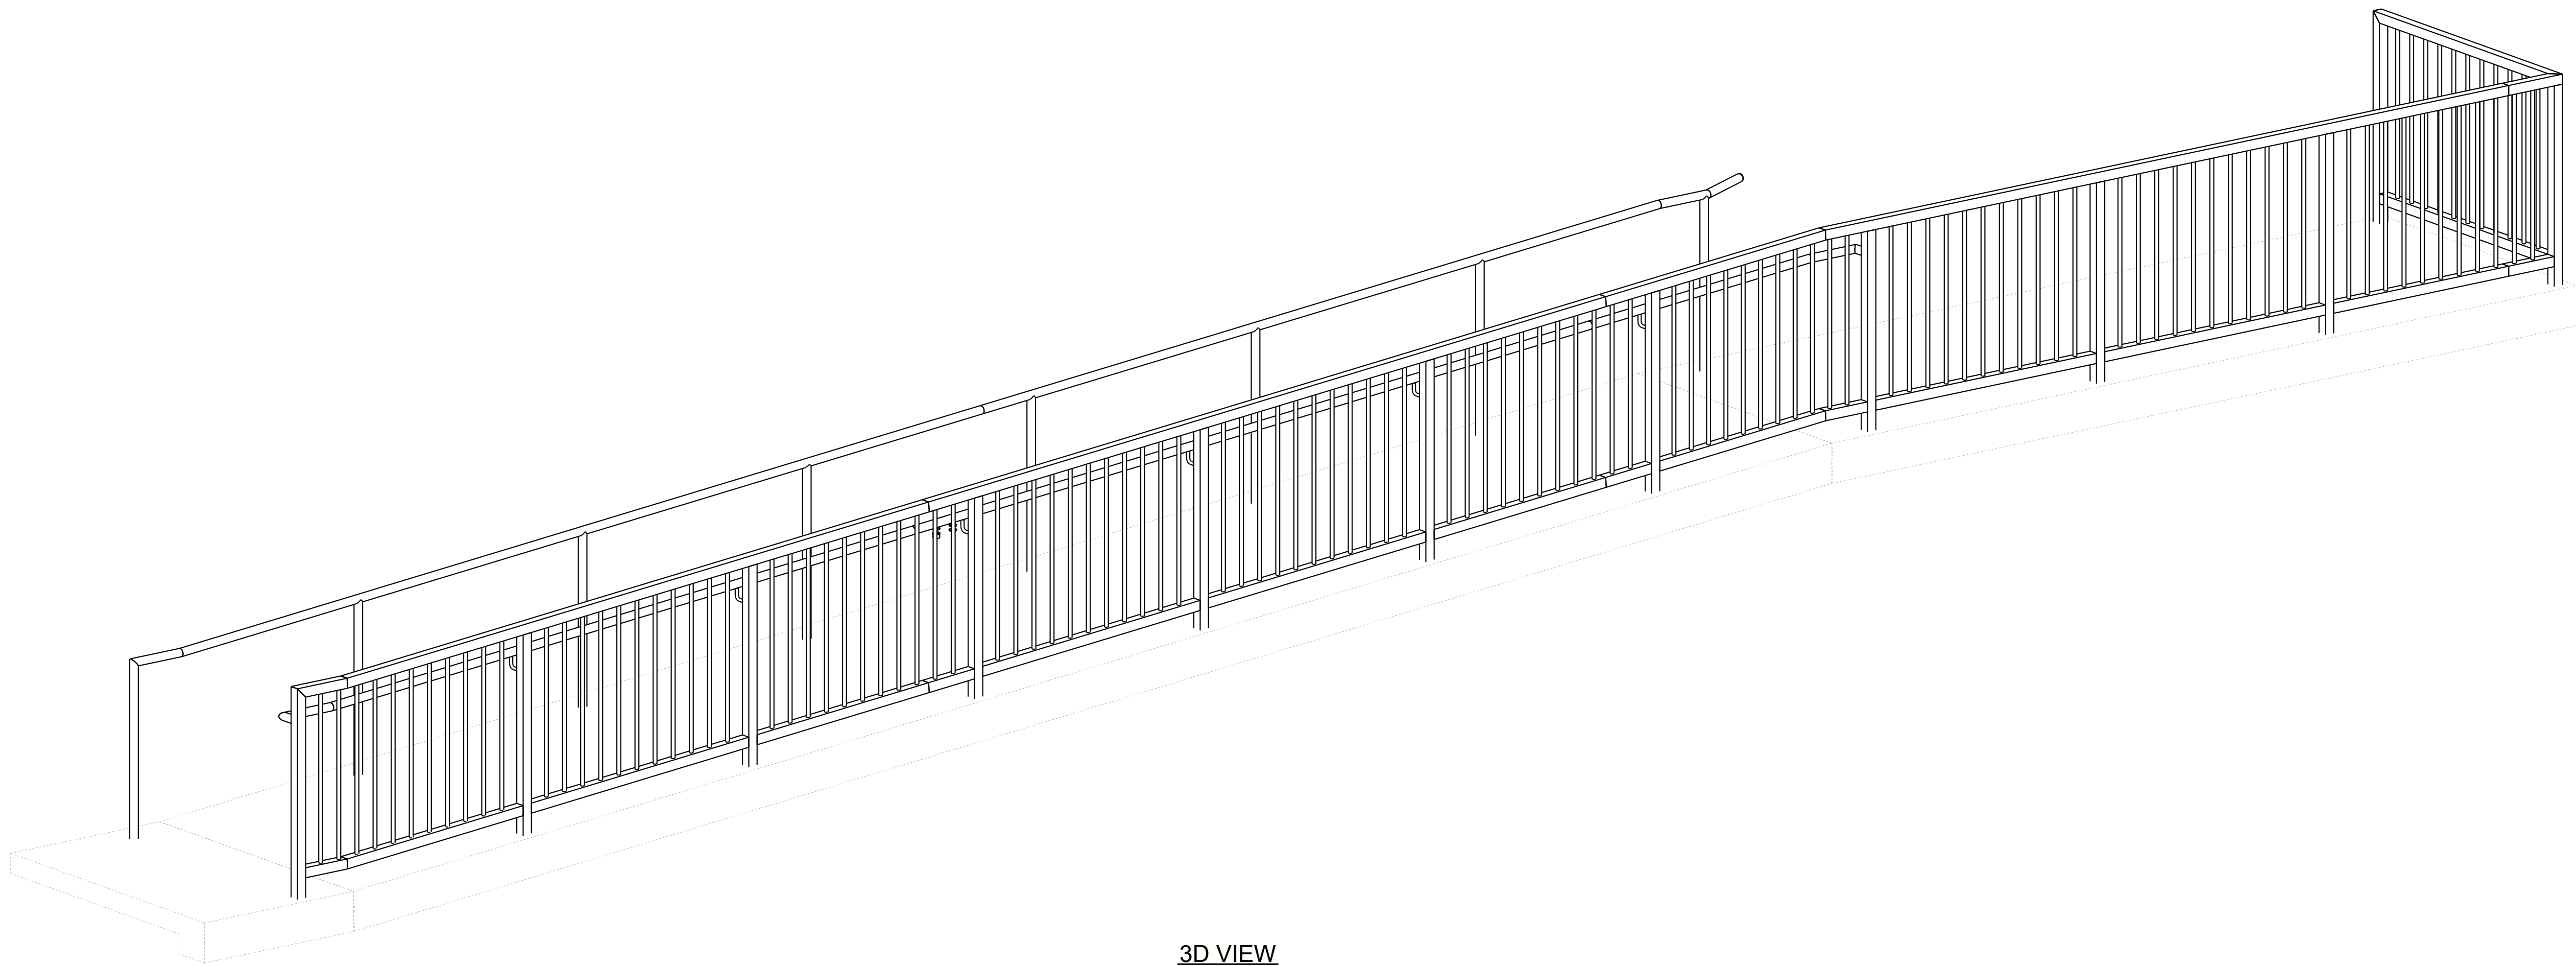

3D VIEW

- NOTES :-
- 1. REFER SHEET ME0 FOR KEY PLAN.
 - 2. REFER SHEET ME4 FOR ELEVATIONS.


FINISH DETAILS :
ALL RAMP RAIL STEEL MEMBERS
TO BE HOT DIP GALVANIZED

NOTE :
FIELD MEASURE PRIOR TO FABRICATION


FOR FIELD USE : 08/29/2022

ELECTRODE	E70XX	UNLESS NOTED	REVISION 0
HOLES	13/16 Ø	UNLESS NOTED	
PAINT	SEE PLAN		


DRAWING NUMBER:
ME3

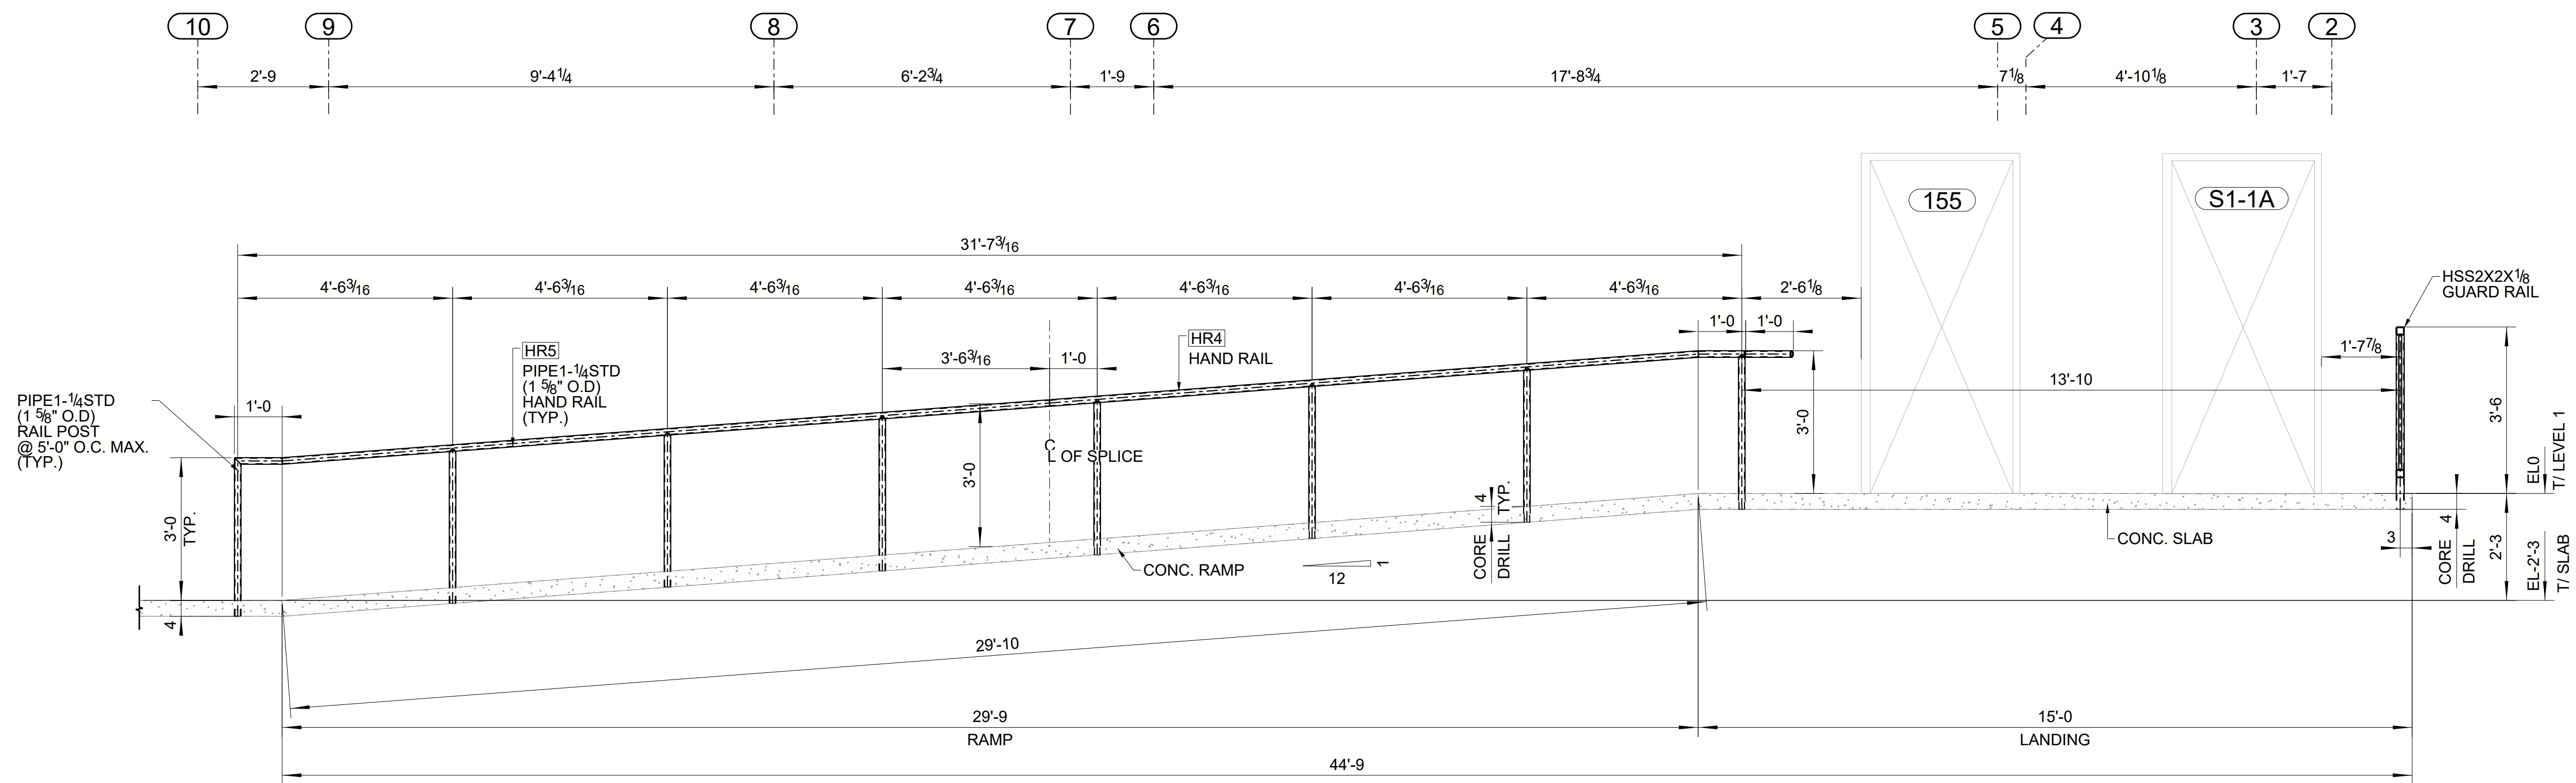

SECTION D - D
ME3

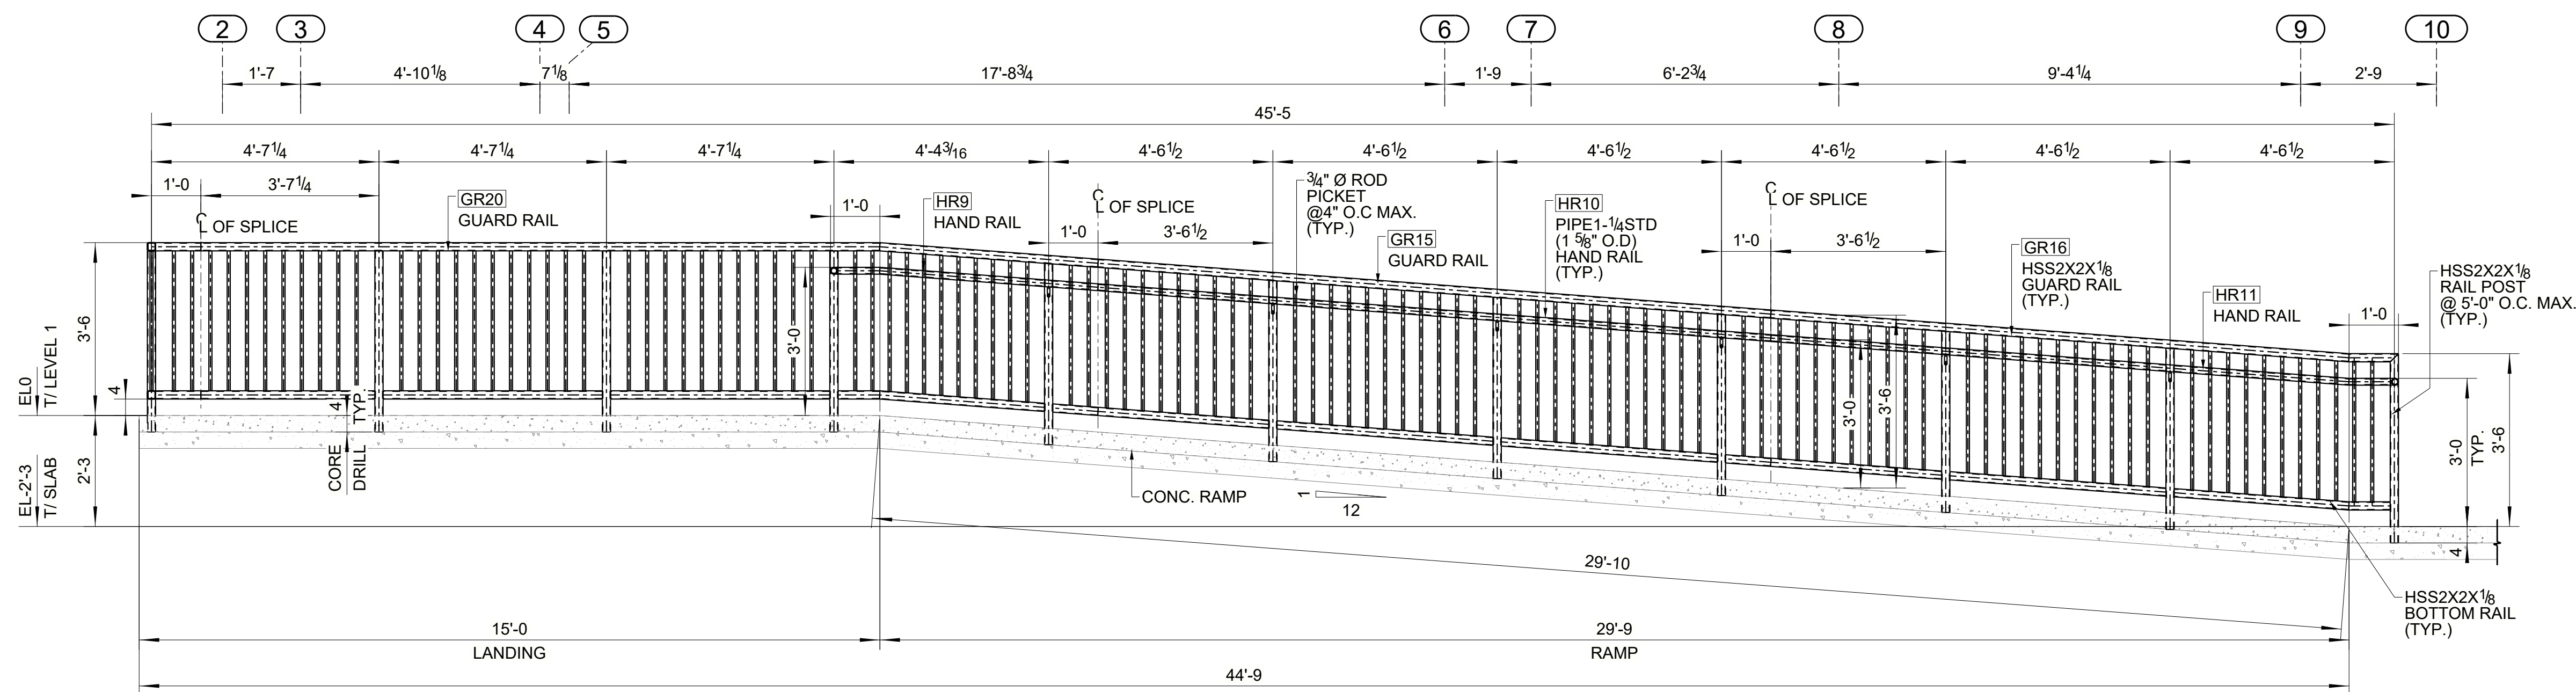

SECTION E - E
ME3

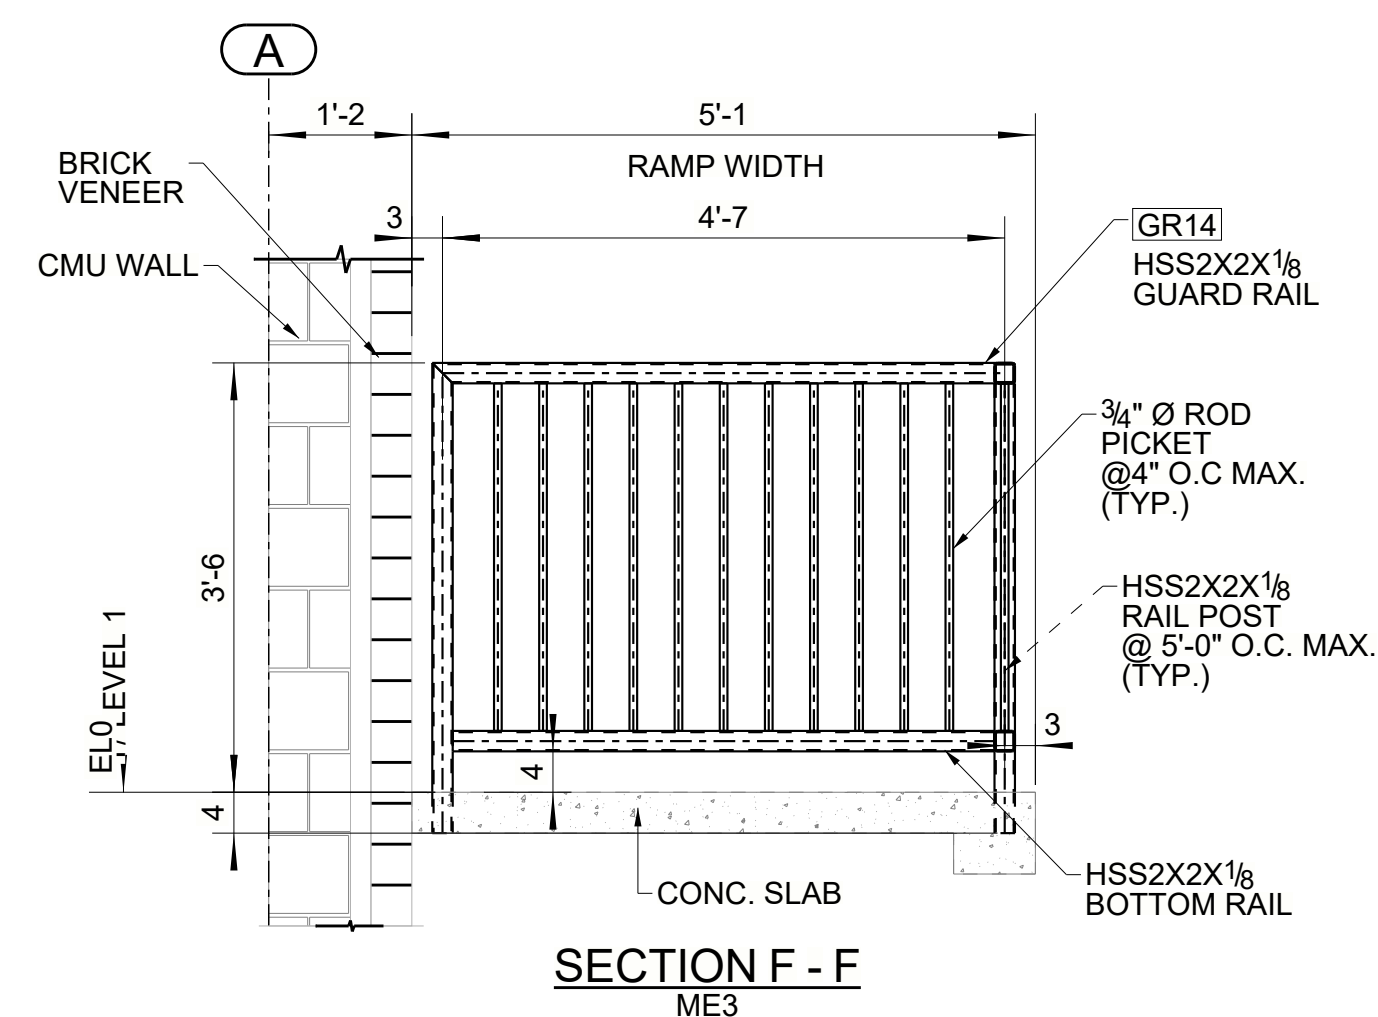

SECTION F - F
ME3

NOTES :-

1. REFER SHEET ME0 FOR KEY PLAN.
2. REFER SHEET ME3 FOR LOCATION PLAN & 3D VIEW.

NOTE :
FIELD MEASURE PRIOR TO FABRICATION

FOR FIELD USE : 08/29/2022



ELECTRODE	E70XX	UNLESS NOTED
HOLES	13/16 Ø	UNLESS NOTED
PAINT	SEE PLAN	

REVISION
0

DRAWING NUMBER:

ME4

BILL OF MATERIAL					
MARK	QTY	DESCRIPTION	LENGTH	GRADE	REMARKS
GR7	1	GUARD RAIL		A500-GR.B	
		HSS2X2X1/8	51'-7 1/8"	A500-GR.B	Total Length
		ROD3/4"	124'-10 5/16"	A36	Total Length
TOTAL WEIGHT (lbf)					316.2

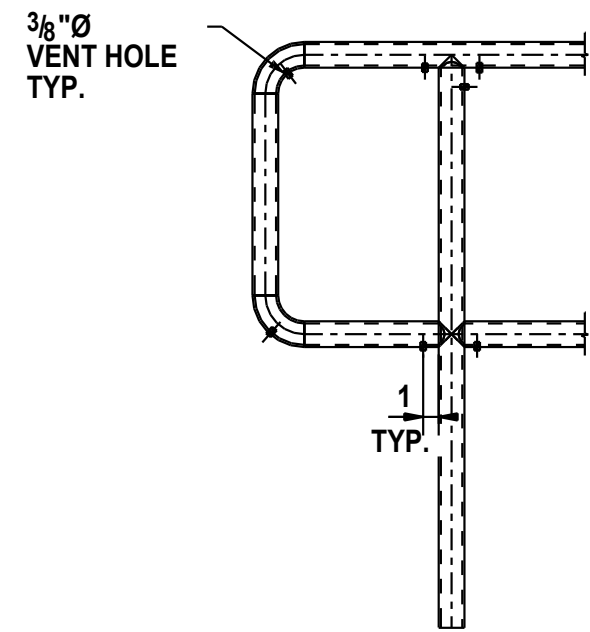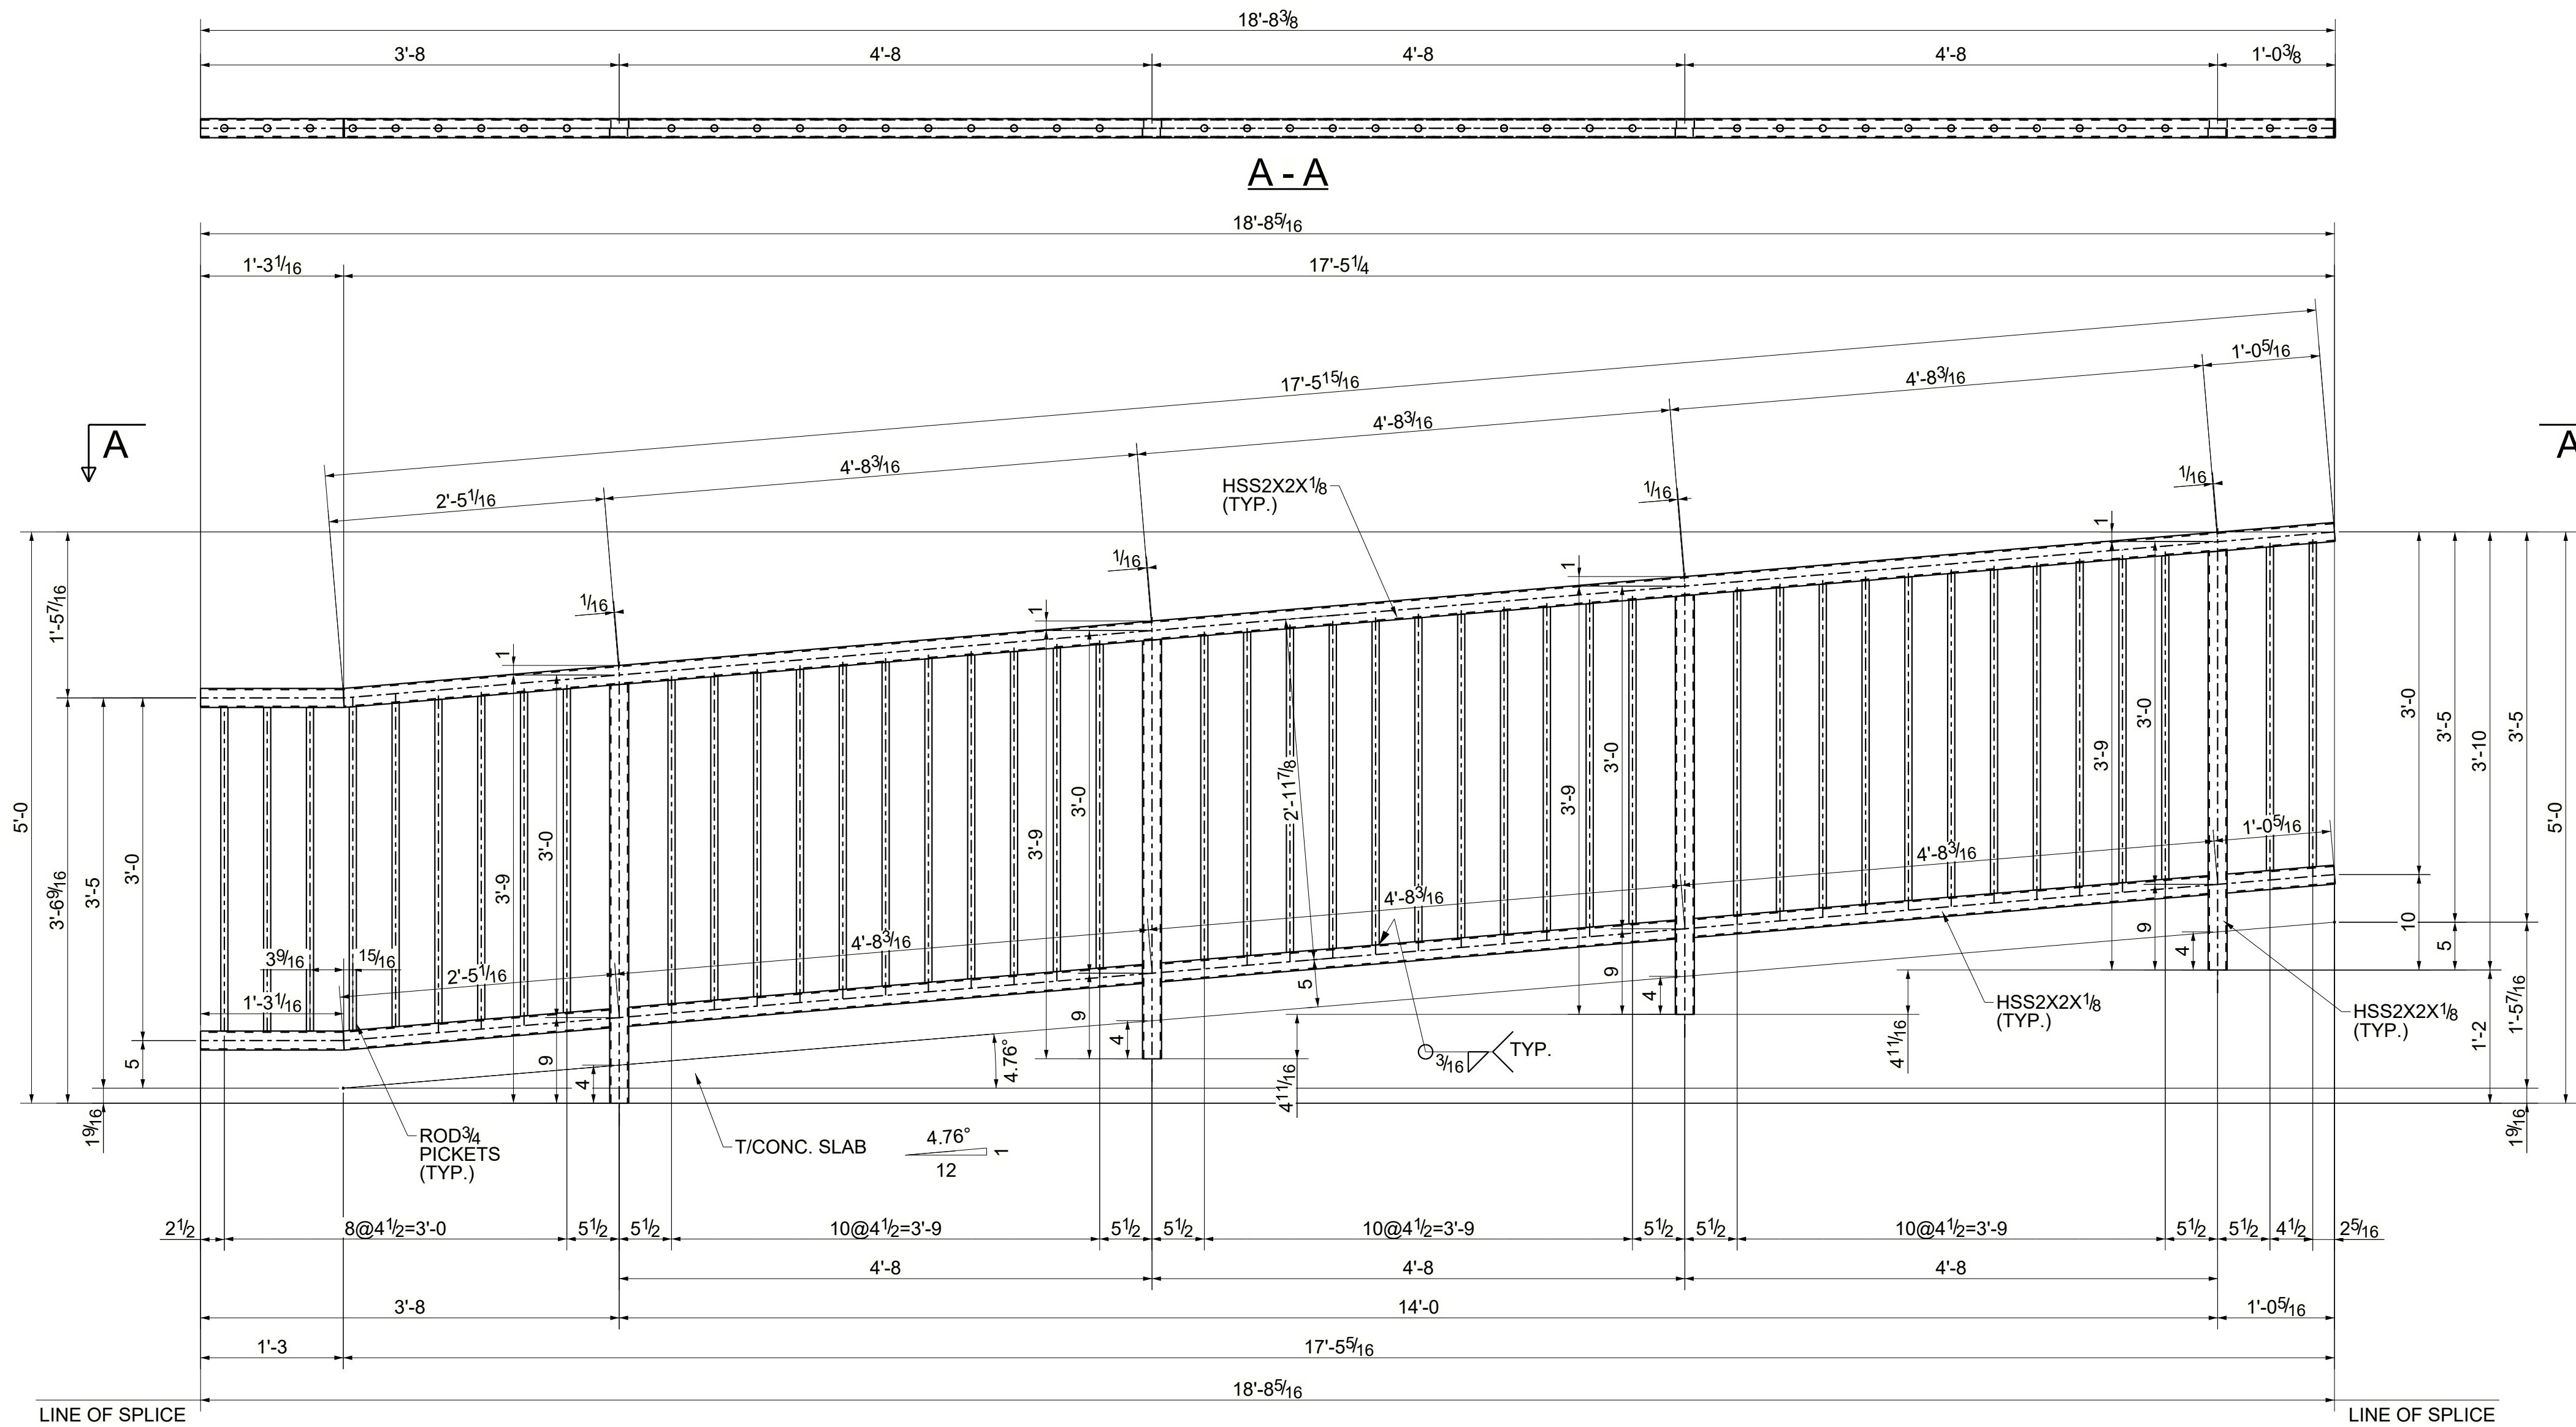

TYPICAL VENT HOLE DETAIL

FIELD MEASURE PRIOR TO FABRICATION

ONE - GUARD RAIL - GR7

- GALVANIZED SHOP NOTE :
- 1) ALL JOINTS TO BE SEAL WELDED WITH CONT. 1/8" FILLET OR BUTT WELD AS REQ'D
 - 2) PROVIDE VENT HOLES AS REQ'D FOR GALV.
 - 3) PLUG VENT HOLES AFTER GALV.



FOR FABRICATION : 08/29/2022

ELECTRODE	E70XX	UNLESS NOTED	REVISION 0
HOLES	13/16 Ø	UNLESS NOTED	
PAINT	GALVANIZED U.N.O		

DRAWING NUMBER:

GR7

BILL OF MATERIAL					
MARK	QTY	DESCRIPTION	LENGTH	GRADE	REMARKS
GR16	1	GUARD RAIL		A500-GR.B	
		HSS2X2X1/8	36'-2 3/8"	A500-GR.B	Total Length
		ROD3/4"	87'-11 1/4"	A36	Total Length
TOTAL WEIGHT (lbf)					222.4

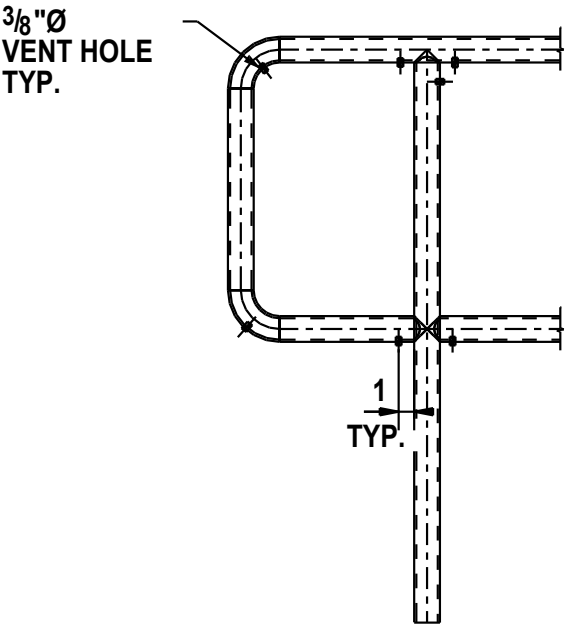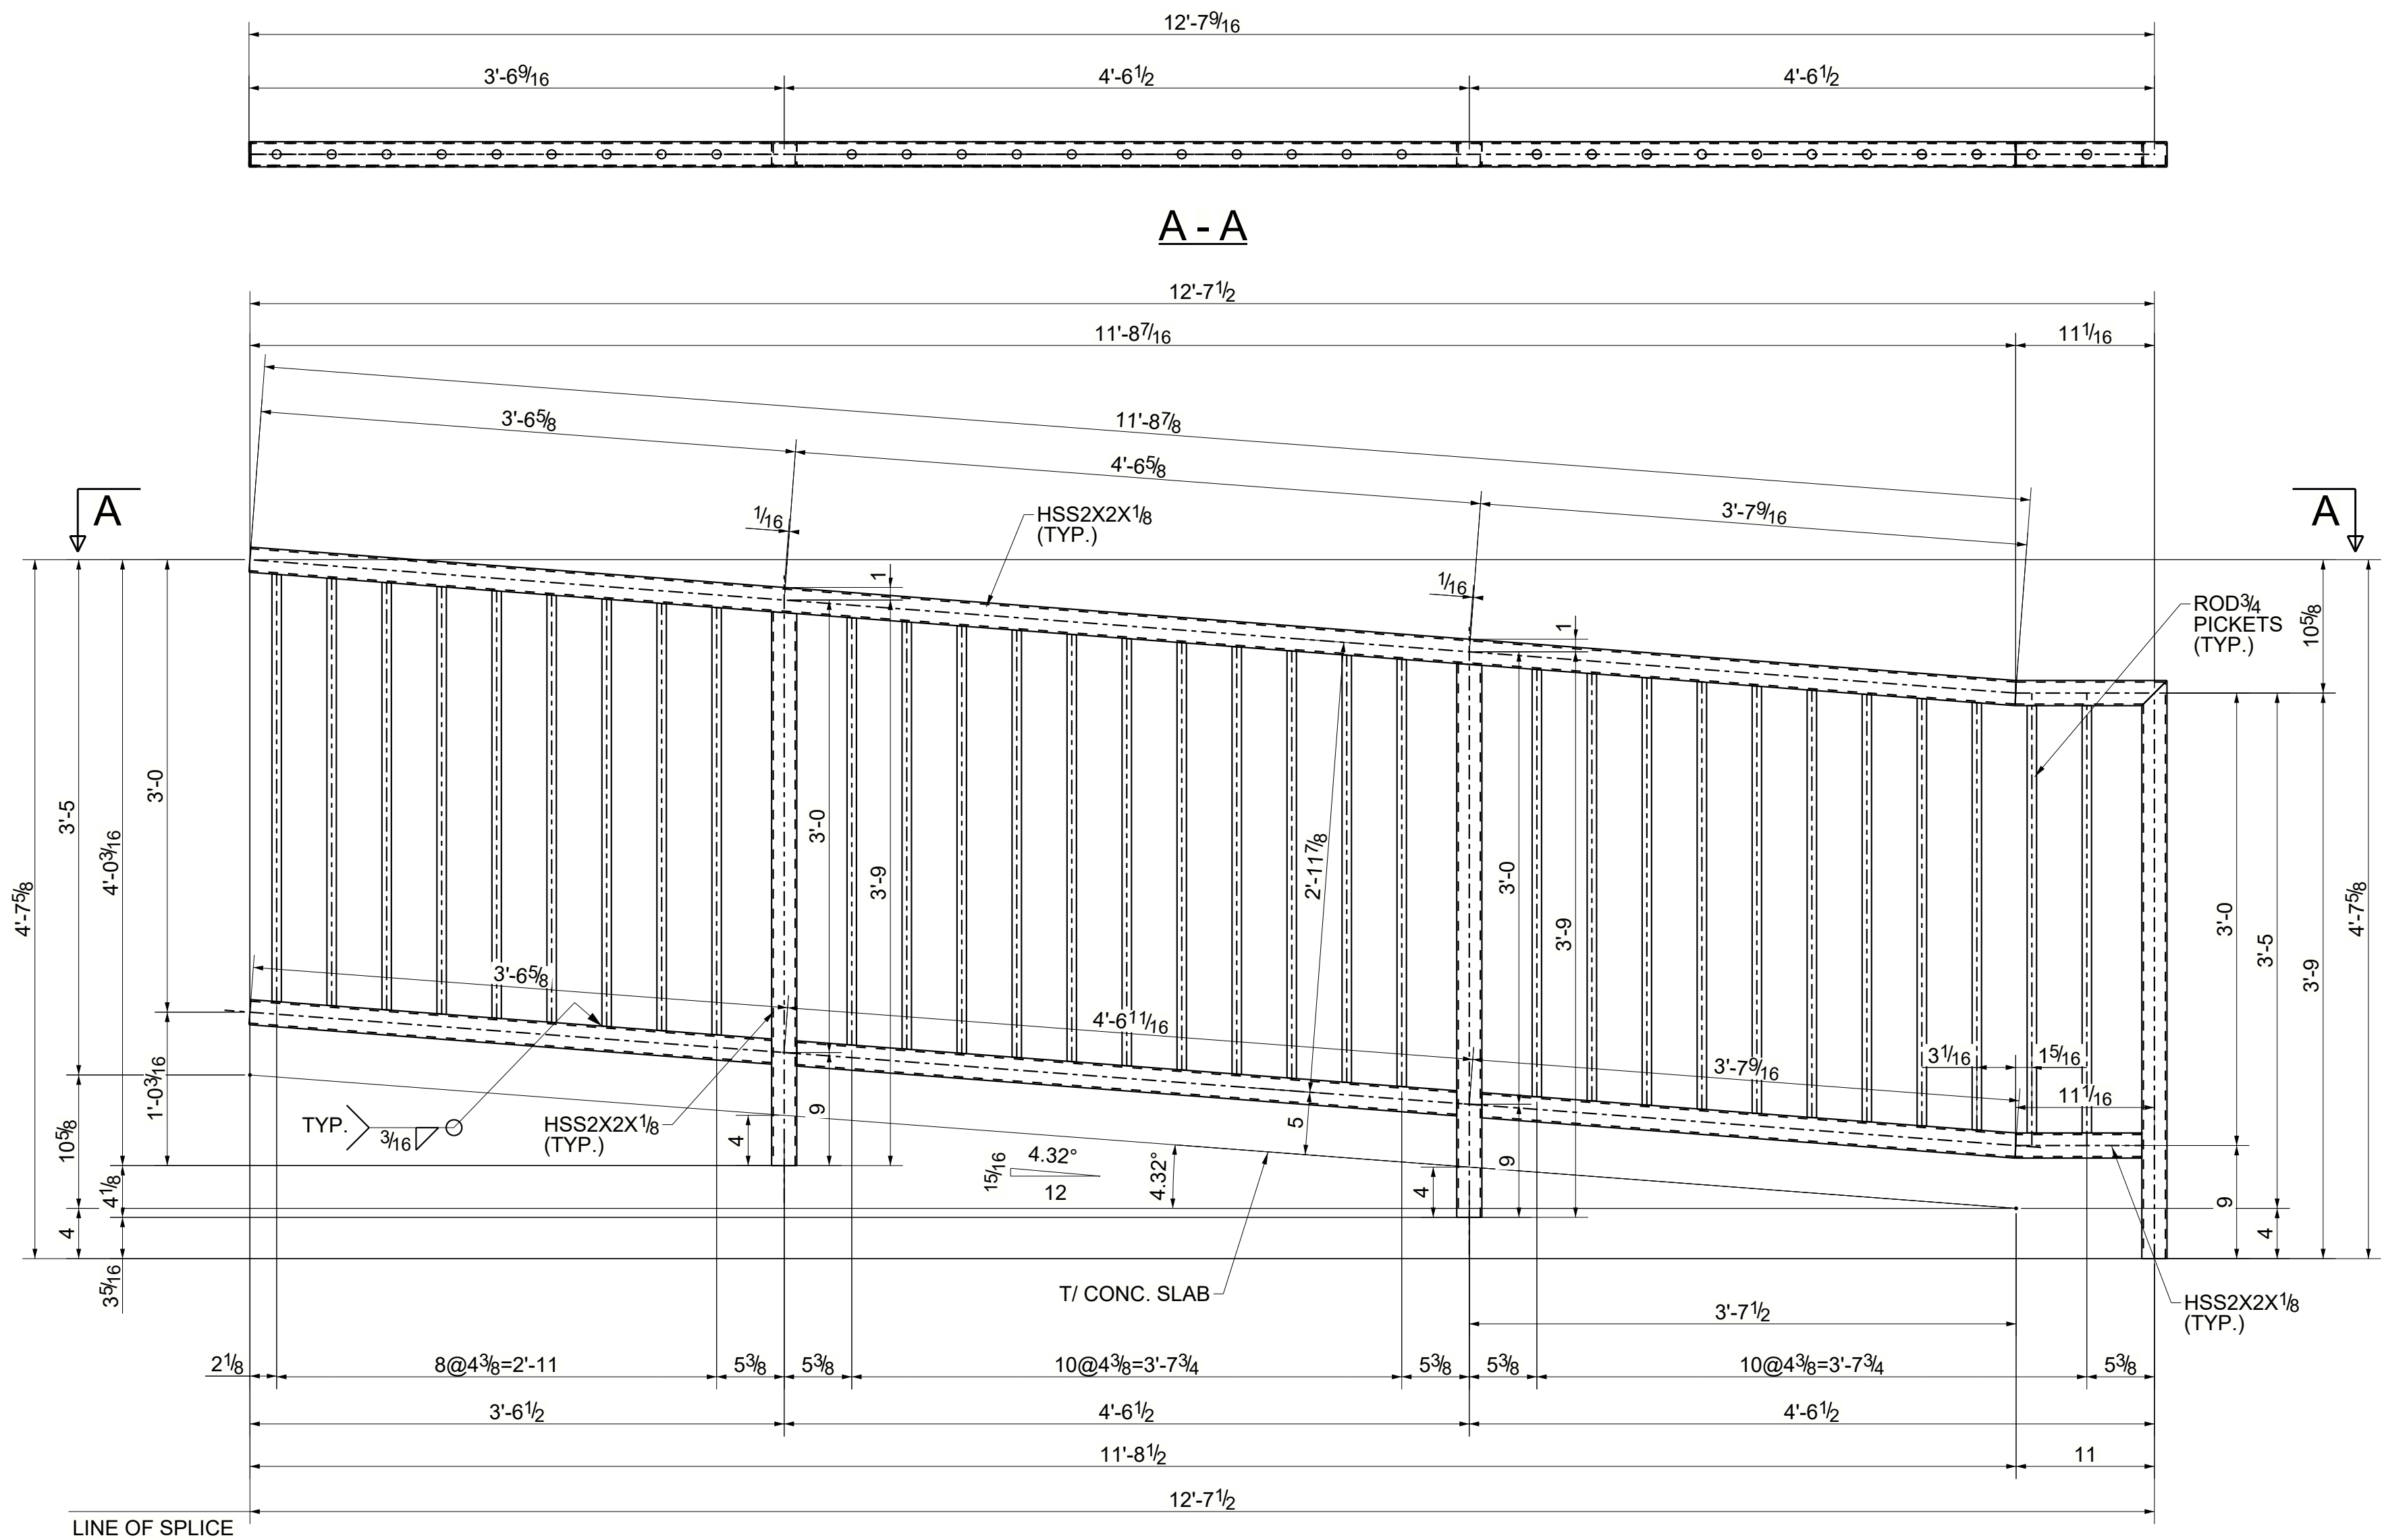

FIELD MEASURE PRIOR TO FABRICATION

ONE - GUARD RAIL - GR16

- GALVANIZED SHOP NOTE :
- 1) ALL JOINTS TO BE SEAL WELDED WITH CONT. 1/8" FILLET OR BUTT WELD AS REQ'D
 - 2) PROVIDE VENT HOLES AS REQ'D FOR GALV.
 - 3) PLUG VENT HOLES AFTER GALV.

FOR FABRICATION : 08/29/2022


ELECTRODE	E70XX	UNLESS NOTED
HOLES	13/16 Ø	UNLESS NOTED
PAINT	GALVANIZED U.N.O	

REVISION
0


DRAWING NUMBER:

GR16

BILL OF MATERIAL					
MARK	QTY	DESCRIPTION	LENGTH	GRADE	REMARKS
HR4	1	HAND RAIL		A53	
		PIPE 1-1/4 STD	28'-9 11/16"	A53	Total Length
261p	1	PL 3/16" X 1 5/8"	0'-1 5/8"	A36	
TOTAL WEIGHT (lb)					61.9

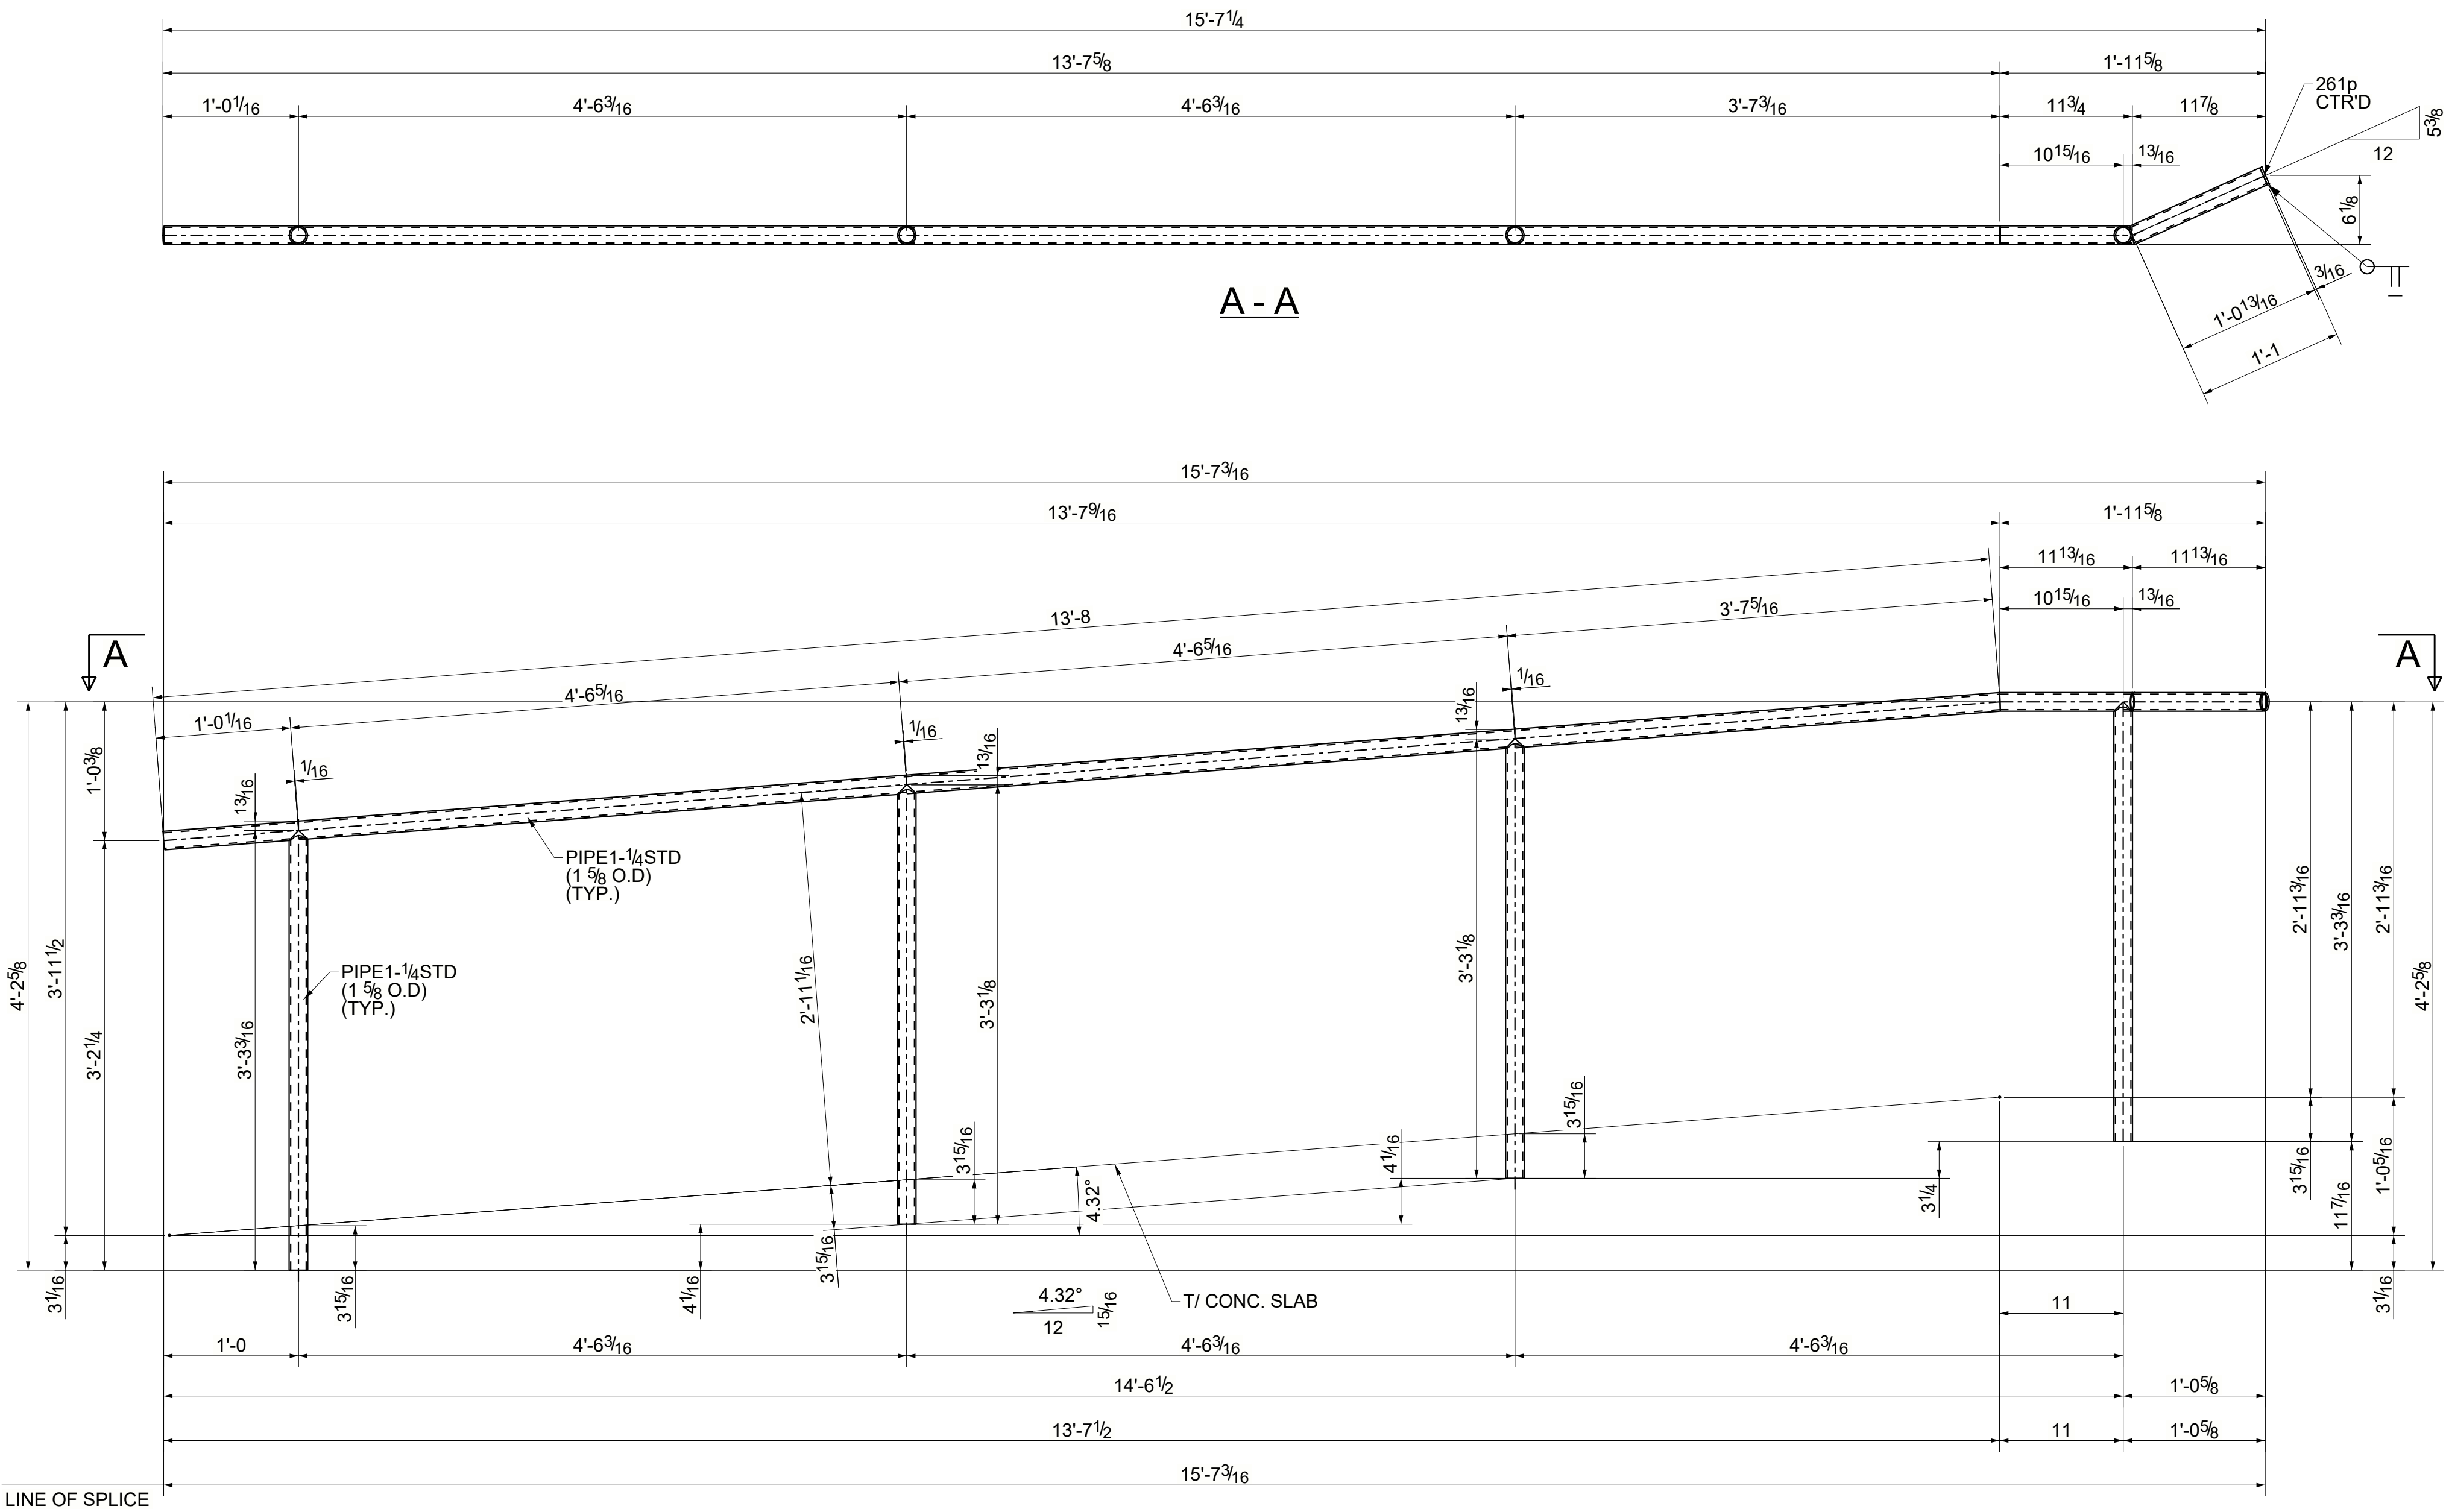

FIELD MEASURE PRIOR TO FABRICATION

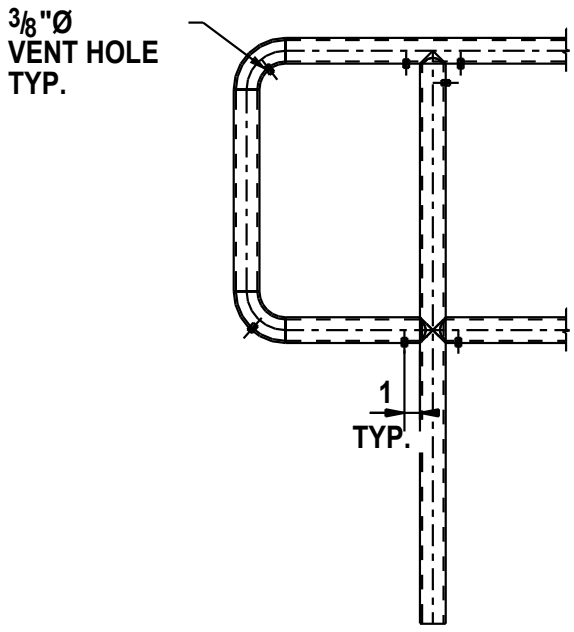

TYPICAL VENT HOLE DETAIL

ONE - HAND RAIL - HR4

- GALVANIZED SHOP NOTE :
- 1) ALL JOINTS TO BE SEAL WELDED WITH CONT. 1/8" FILLET OR BUTT WELD AS REQ'D
 - 2) PROVIDE VENT HOLES AS REQ'D FOR GALV.
 - 3) PLUG VENT HOLES AFTER GALV.

FOR FABRICATION : 08/29/2022

ELECTRODE	E70XX	UNLESS NOTED
HOLES	13/16 Ø	UNLESS NOTED
PAINT	GALVANIZED U.N.O	
REVISION		
0		

DRAWING NUMBER:

HR4