



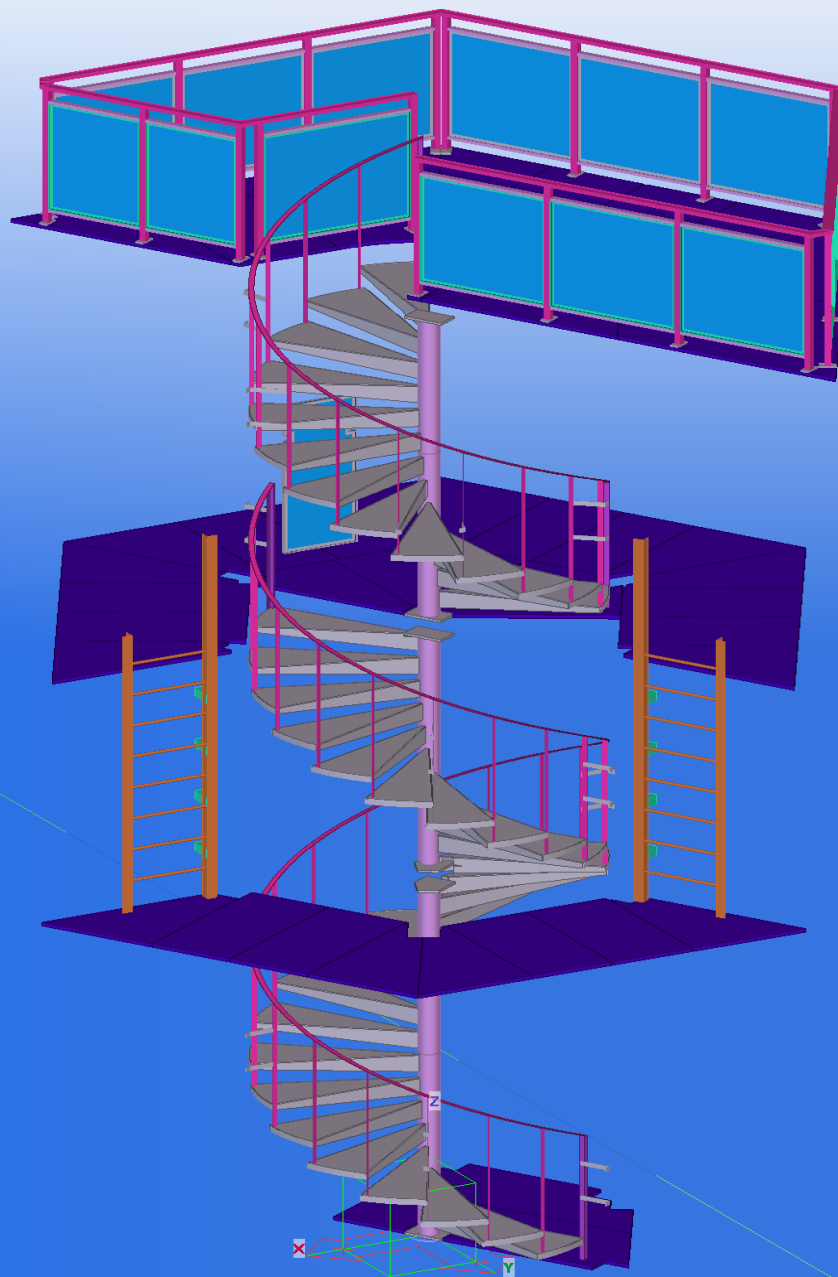

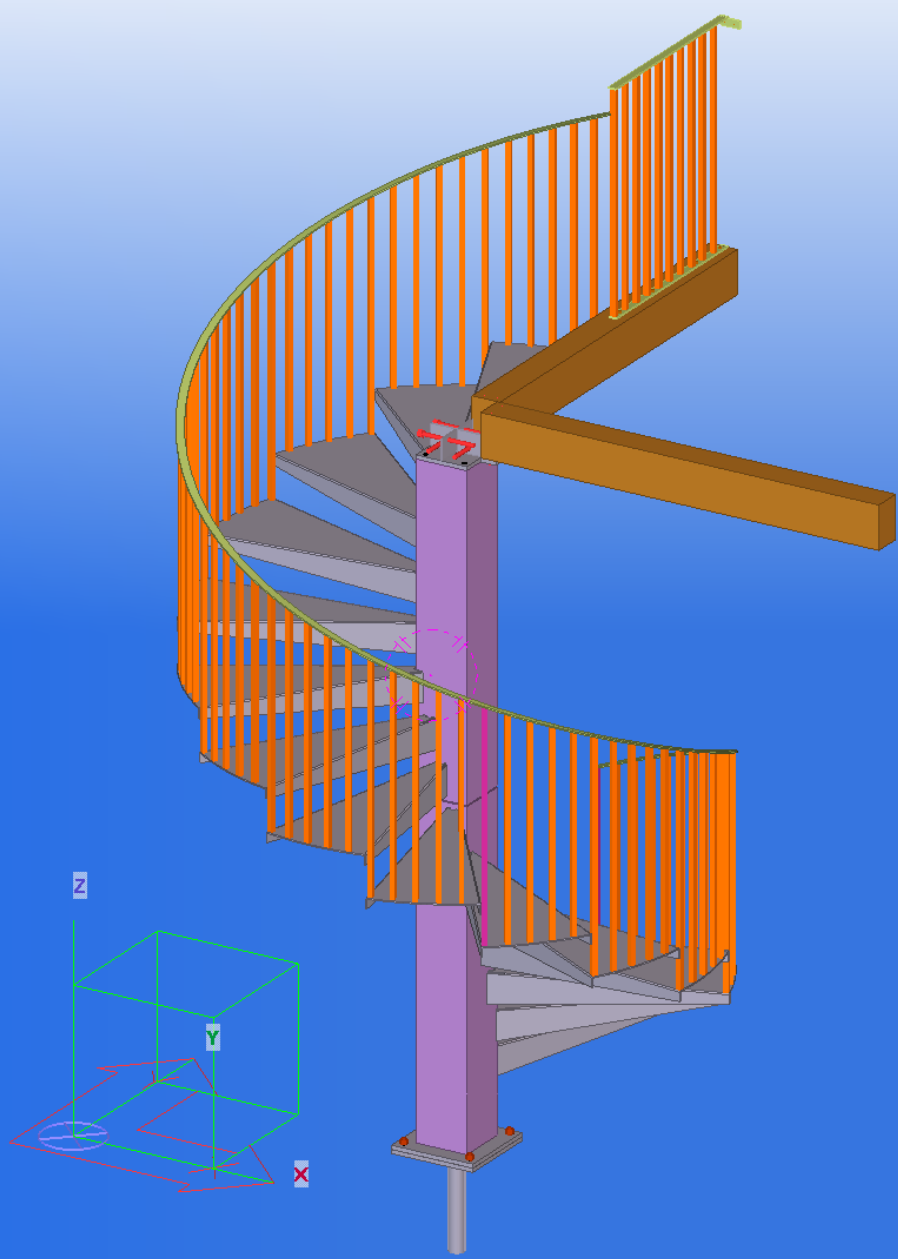



GENERAL NOTES :

1. ELEVATIONS SHOWN IN PLAN ARE REFERRED TO TOP OF STEEL ELEVATION (U.N.O).
2. MATERIAL GRADES USED :
ALL HSS : A500-GR.C
ALL W- SHAPES : 350W
OTHER STEEL : 300W
3. (XX) - INDICATES TREAD NUMBER
4. ALL SPRIAL STAIR STEEL MEMBERS TO BE NO PAINT


3D VIEW - SOUTH CABIN




1. REFER SHEET ME100 FOR 3D -VIEW.
2. REFER SHEET ME104 FOR ELEVATION.
3. REFER SHEET ME105 FOR SECTIONS.




PROJECT NORTH

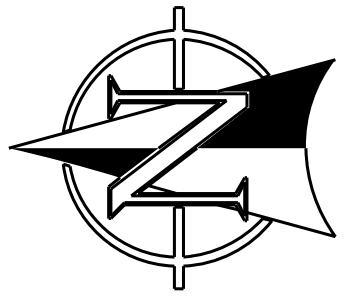

TRUE NORTH

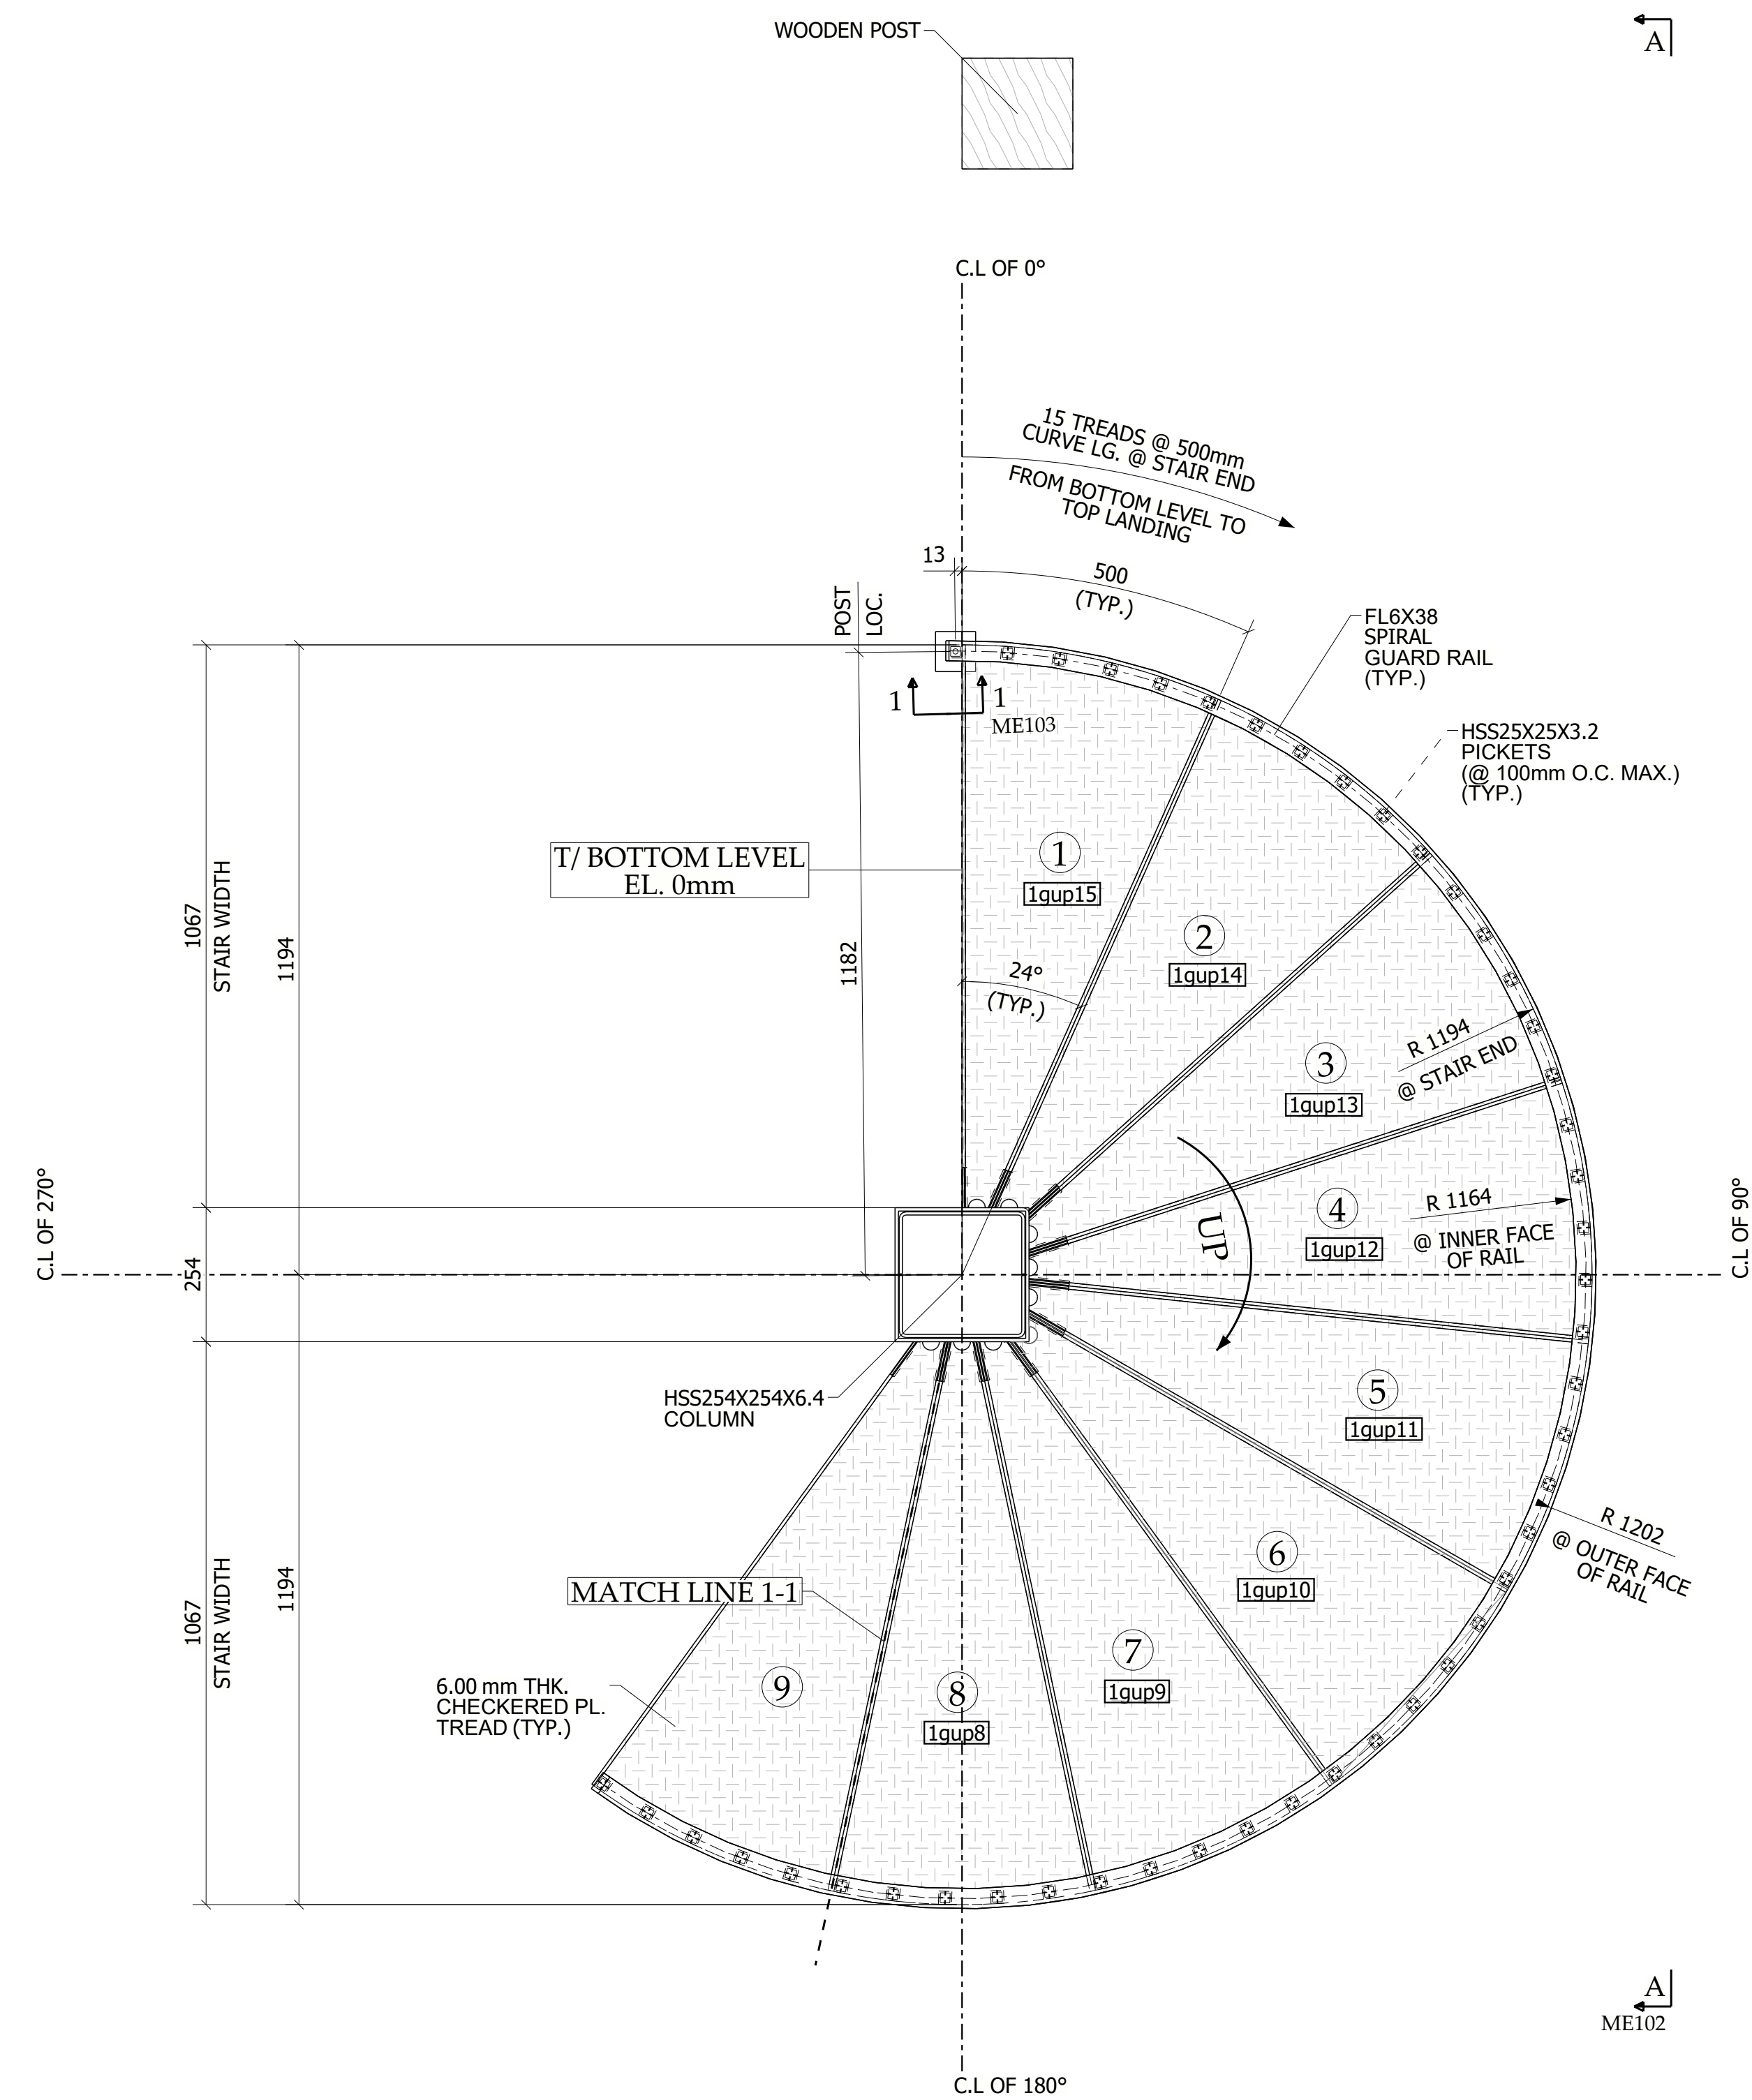


PARTIAL STAIR FRAMING PLAN @ T/BOTTOM LEVEL EL. 0 mm

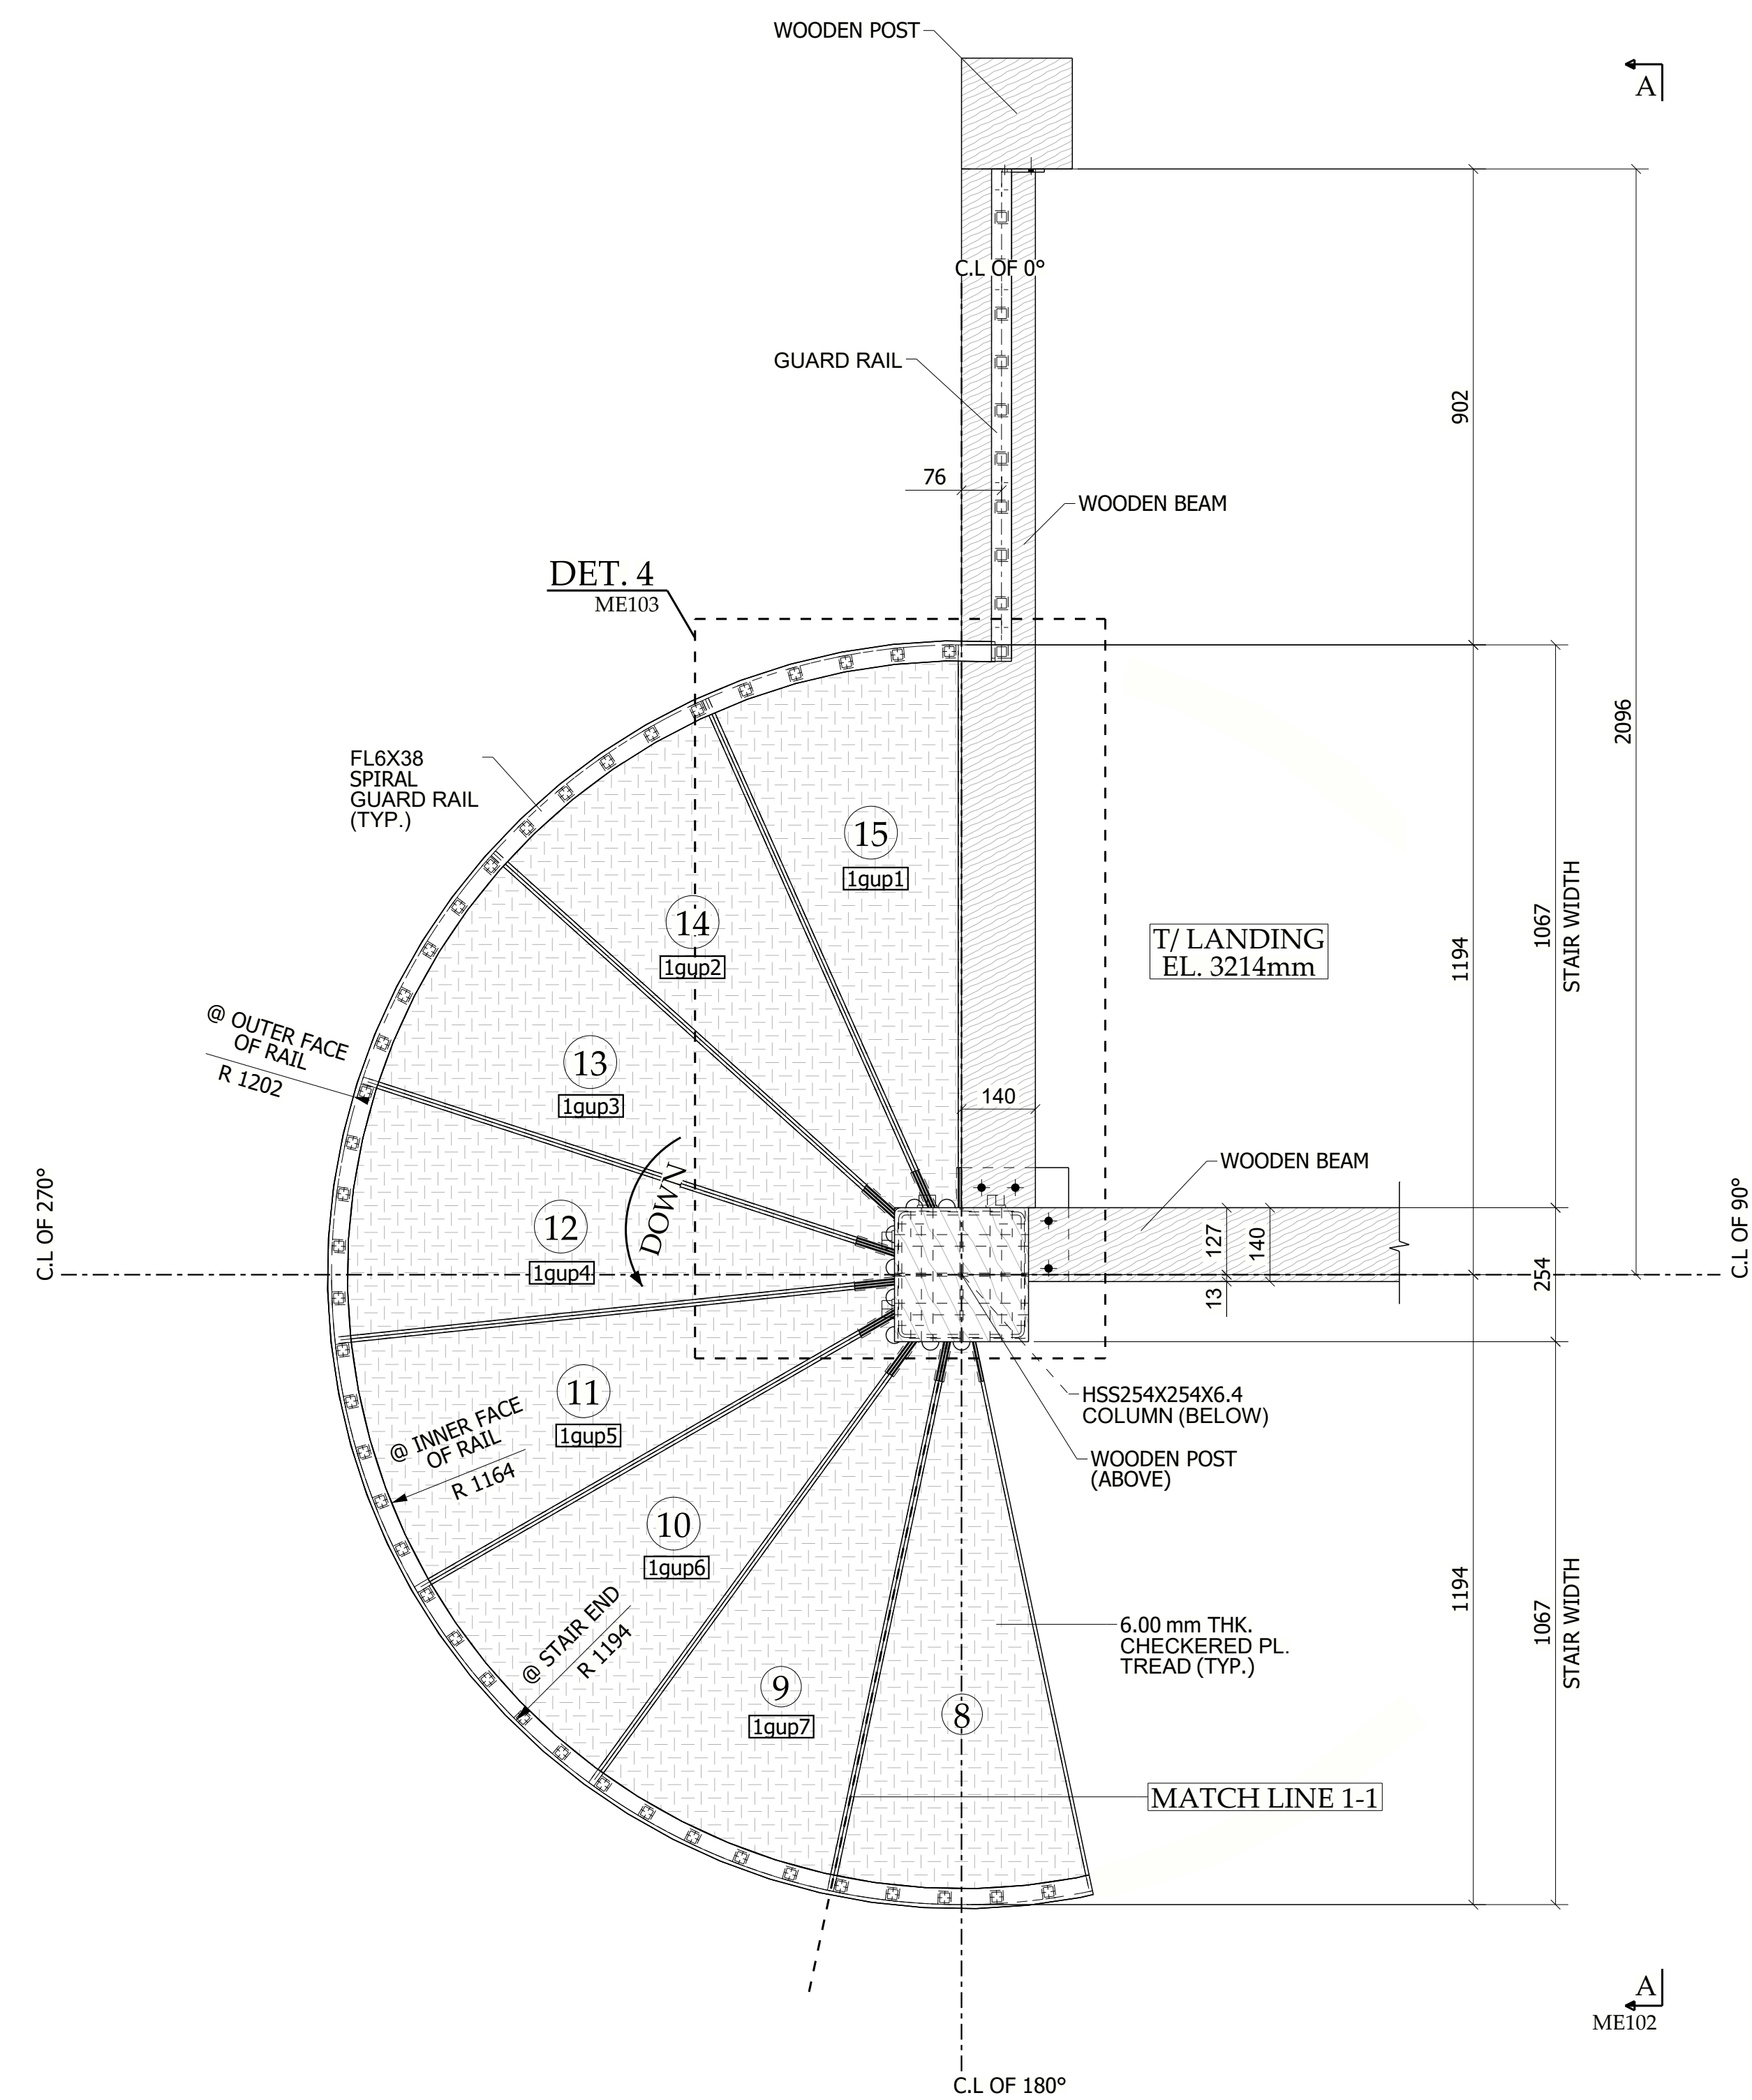


PARTIAL STAIR FRAMING PLAN @ T/LANDING EL. 3214mm

NOTES :-

1. REFER SHEET ME100 FOR 3D-VIEW.
2. REFER SHEET ME102 FOR ELEVATION.
3. REFER SHEET ME103 FOR TYPICAL SECTION AND DETAILS.

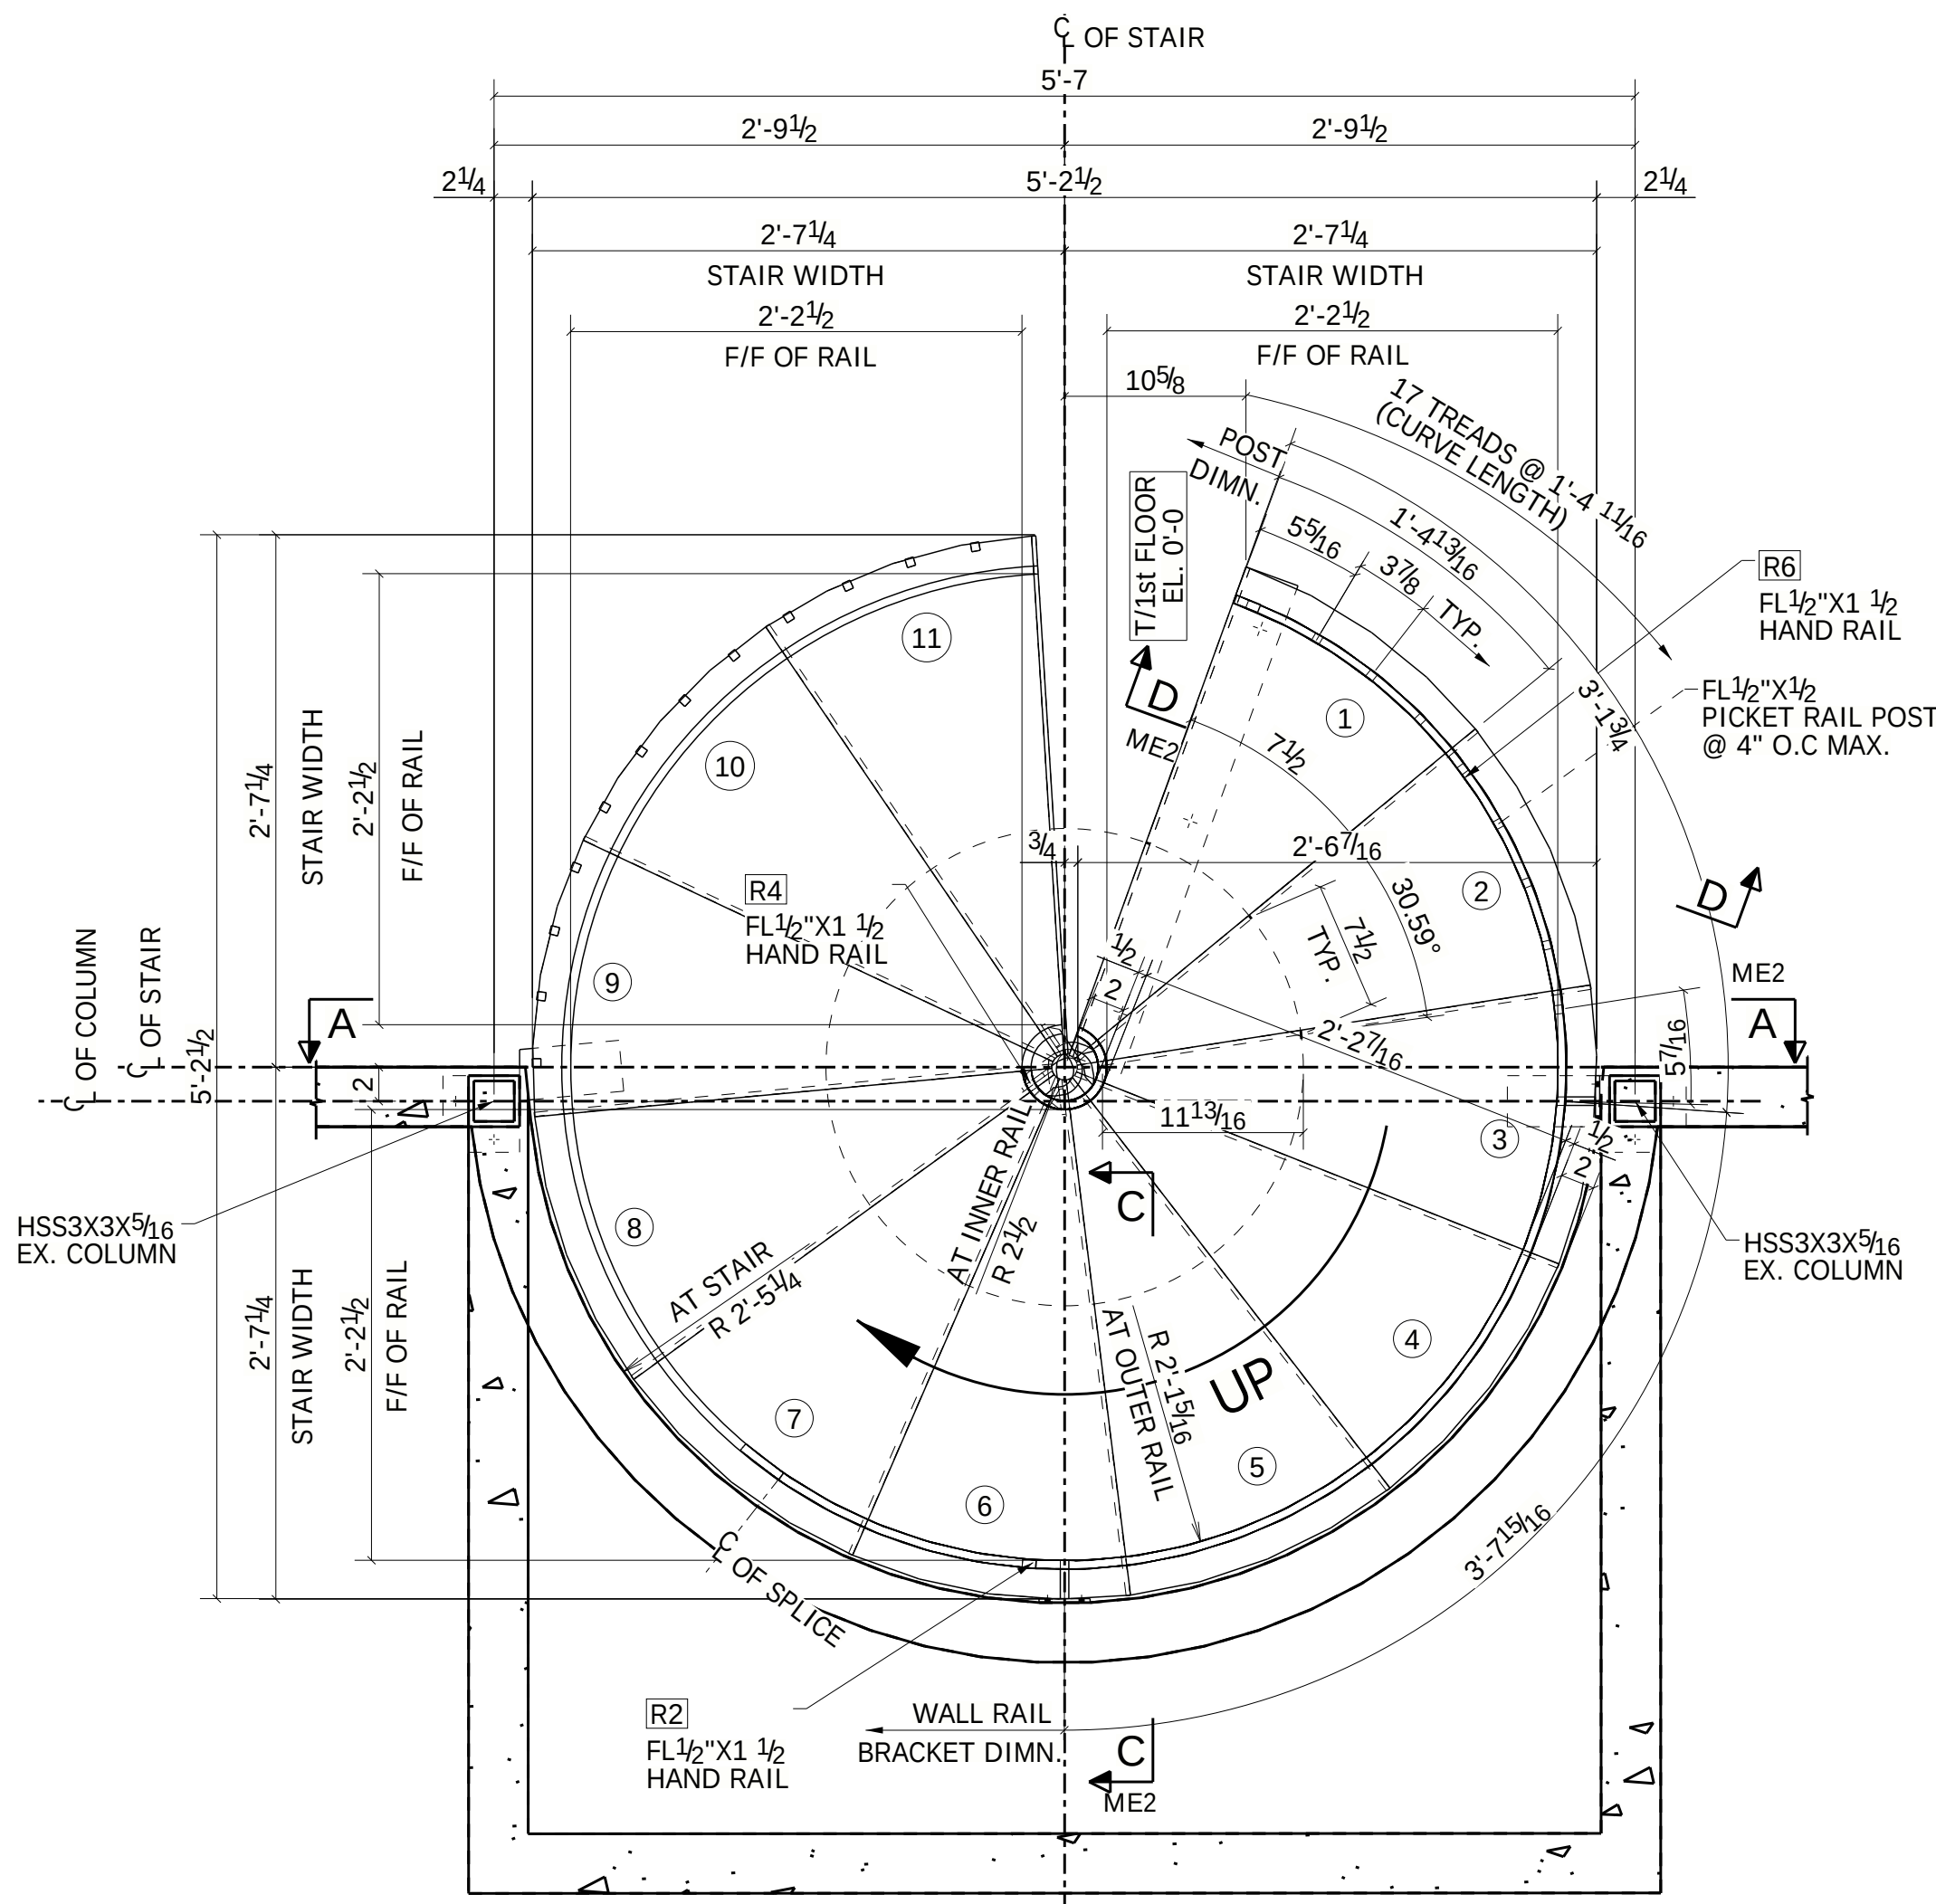


PARTIAL SPIRAL STAIR PH1 FRAMING PLAN AT FIRST FLOOR AT EL. 0
REFER : 1st FLOOR PLAN (1/A2.1)

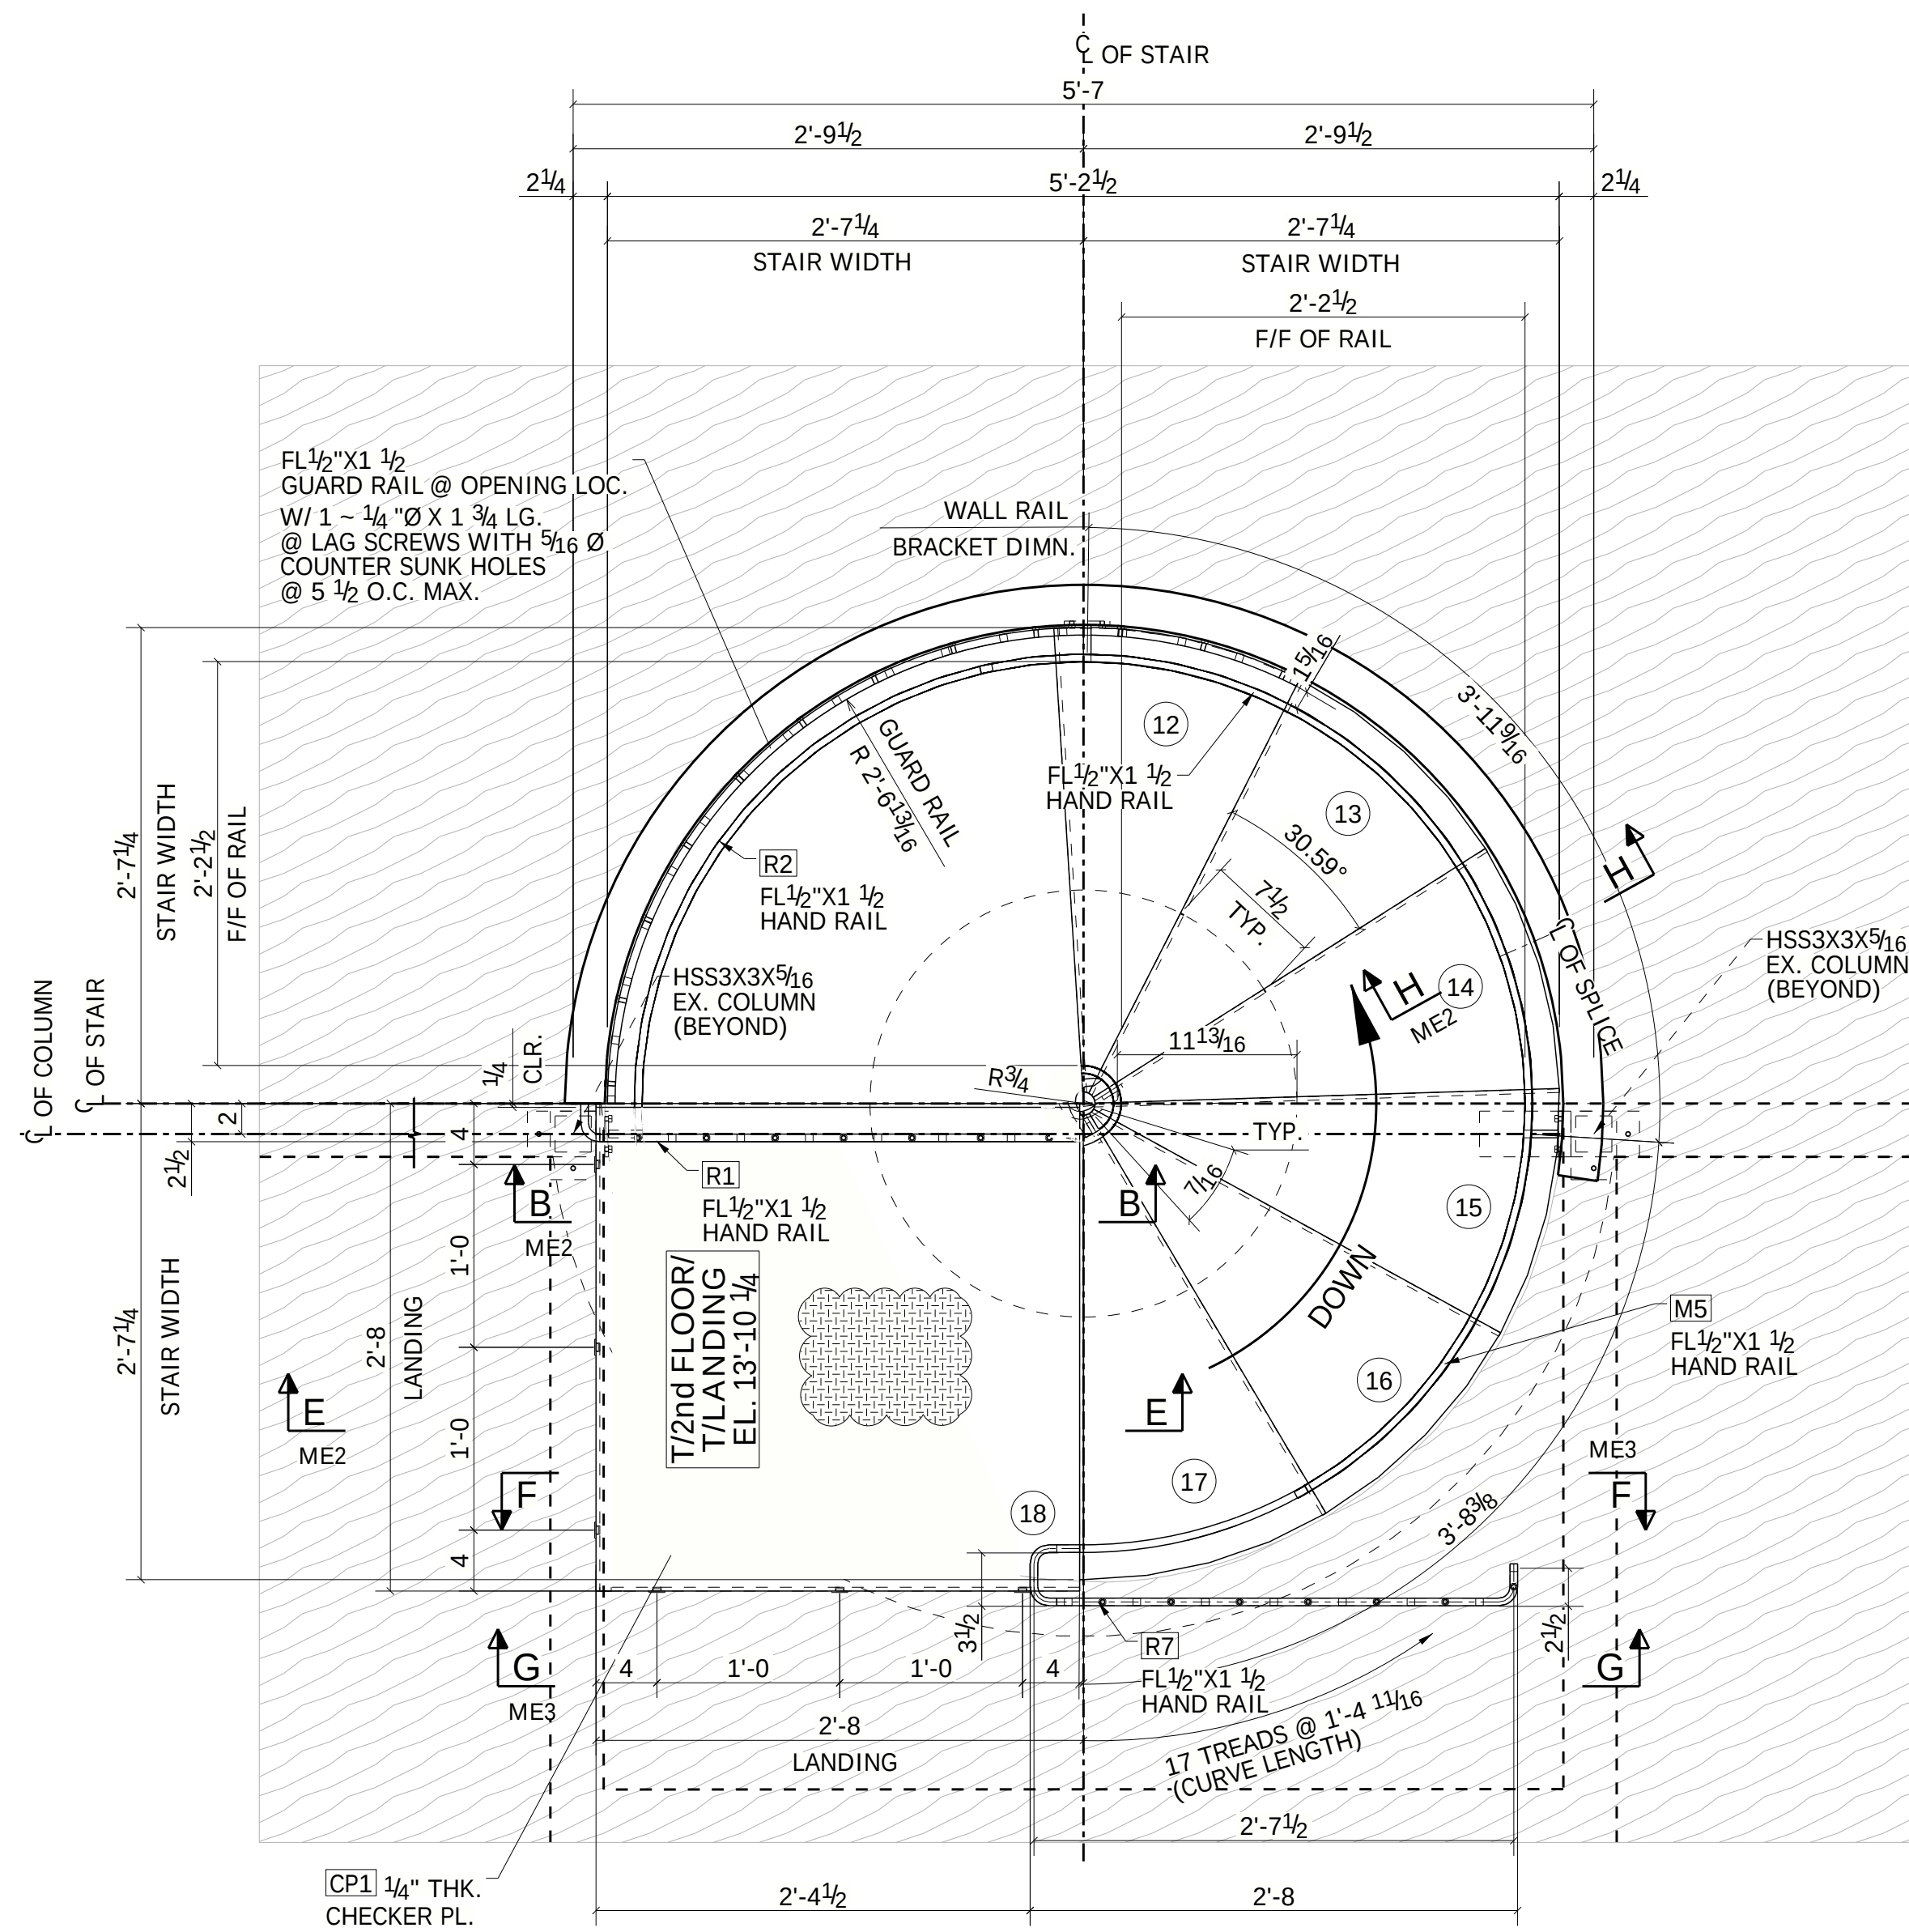

PARTIAL SPIRAL STAIR PH1 FRAMING PLAN AT SECOND FLOOR AT EL. 13'-10 1/4
REFER : 2nd FLOOR PLAN (2/A2.1)

NOTES :-


1. FINISH FLOOR ELEVATION = 0'-0
2. MATERIAL GRADES USED :
ALL CHANNELS : 300W
ALL HSS TUBES : A500 GRADE B
PLATES AND ANGLES : 300W
ALL CHECKERED PLATE : ANSI 304
3. (XX) - INDICATES TREAD NUMBER
4. ALL SPIRAL STAIR MEMBERS TO BE UNFINISHED, NO PRIMER

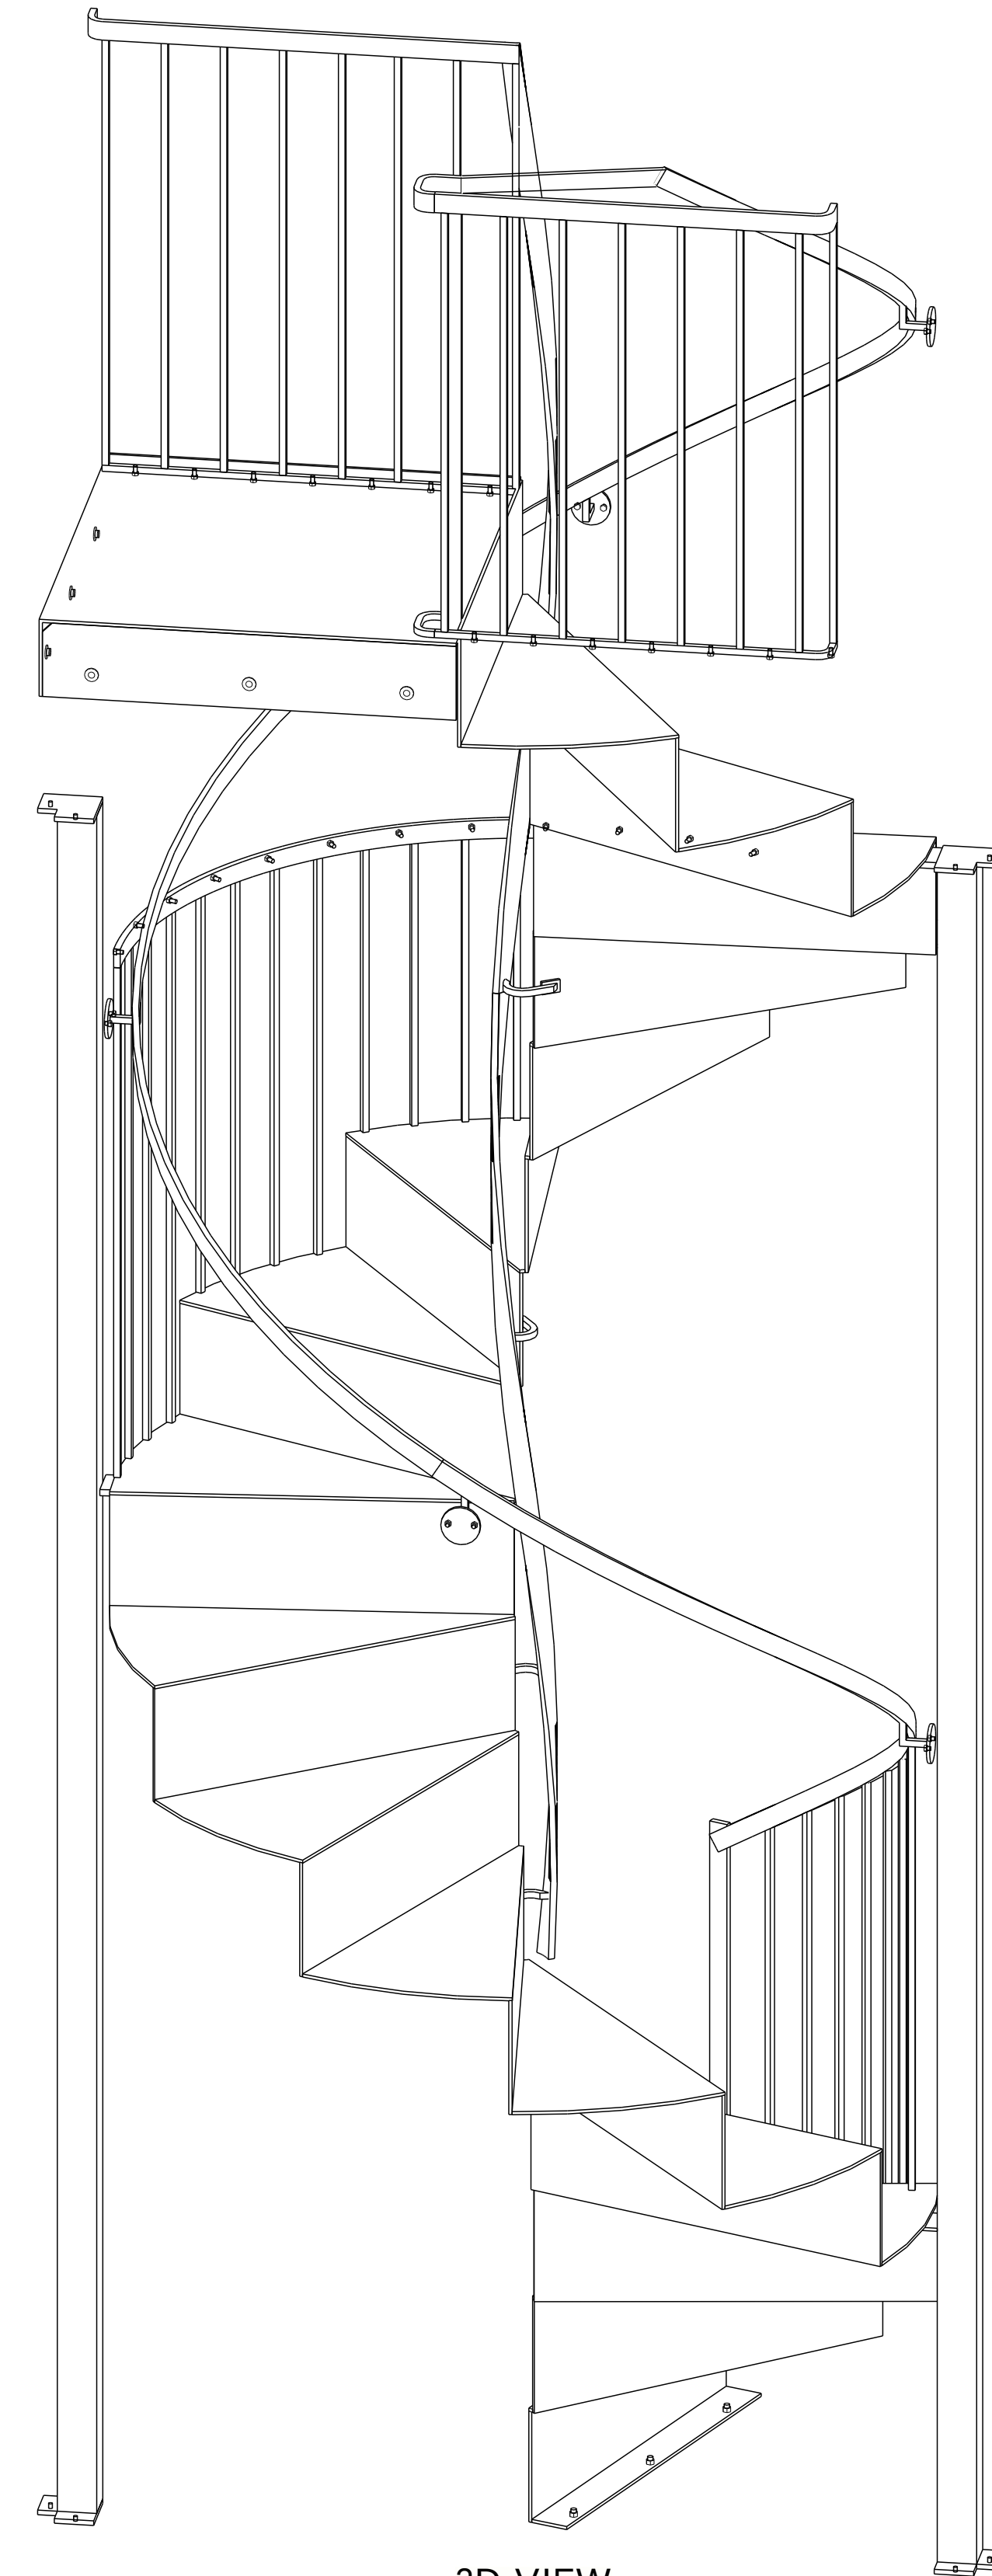


3D-VIEW




PROJECT NORTH

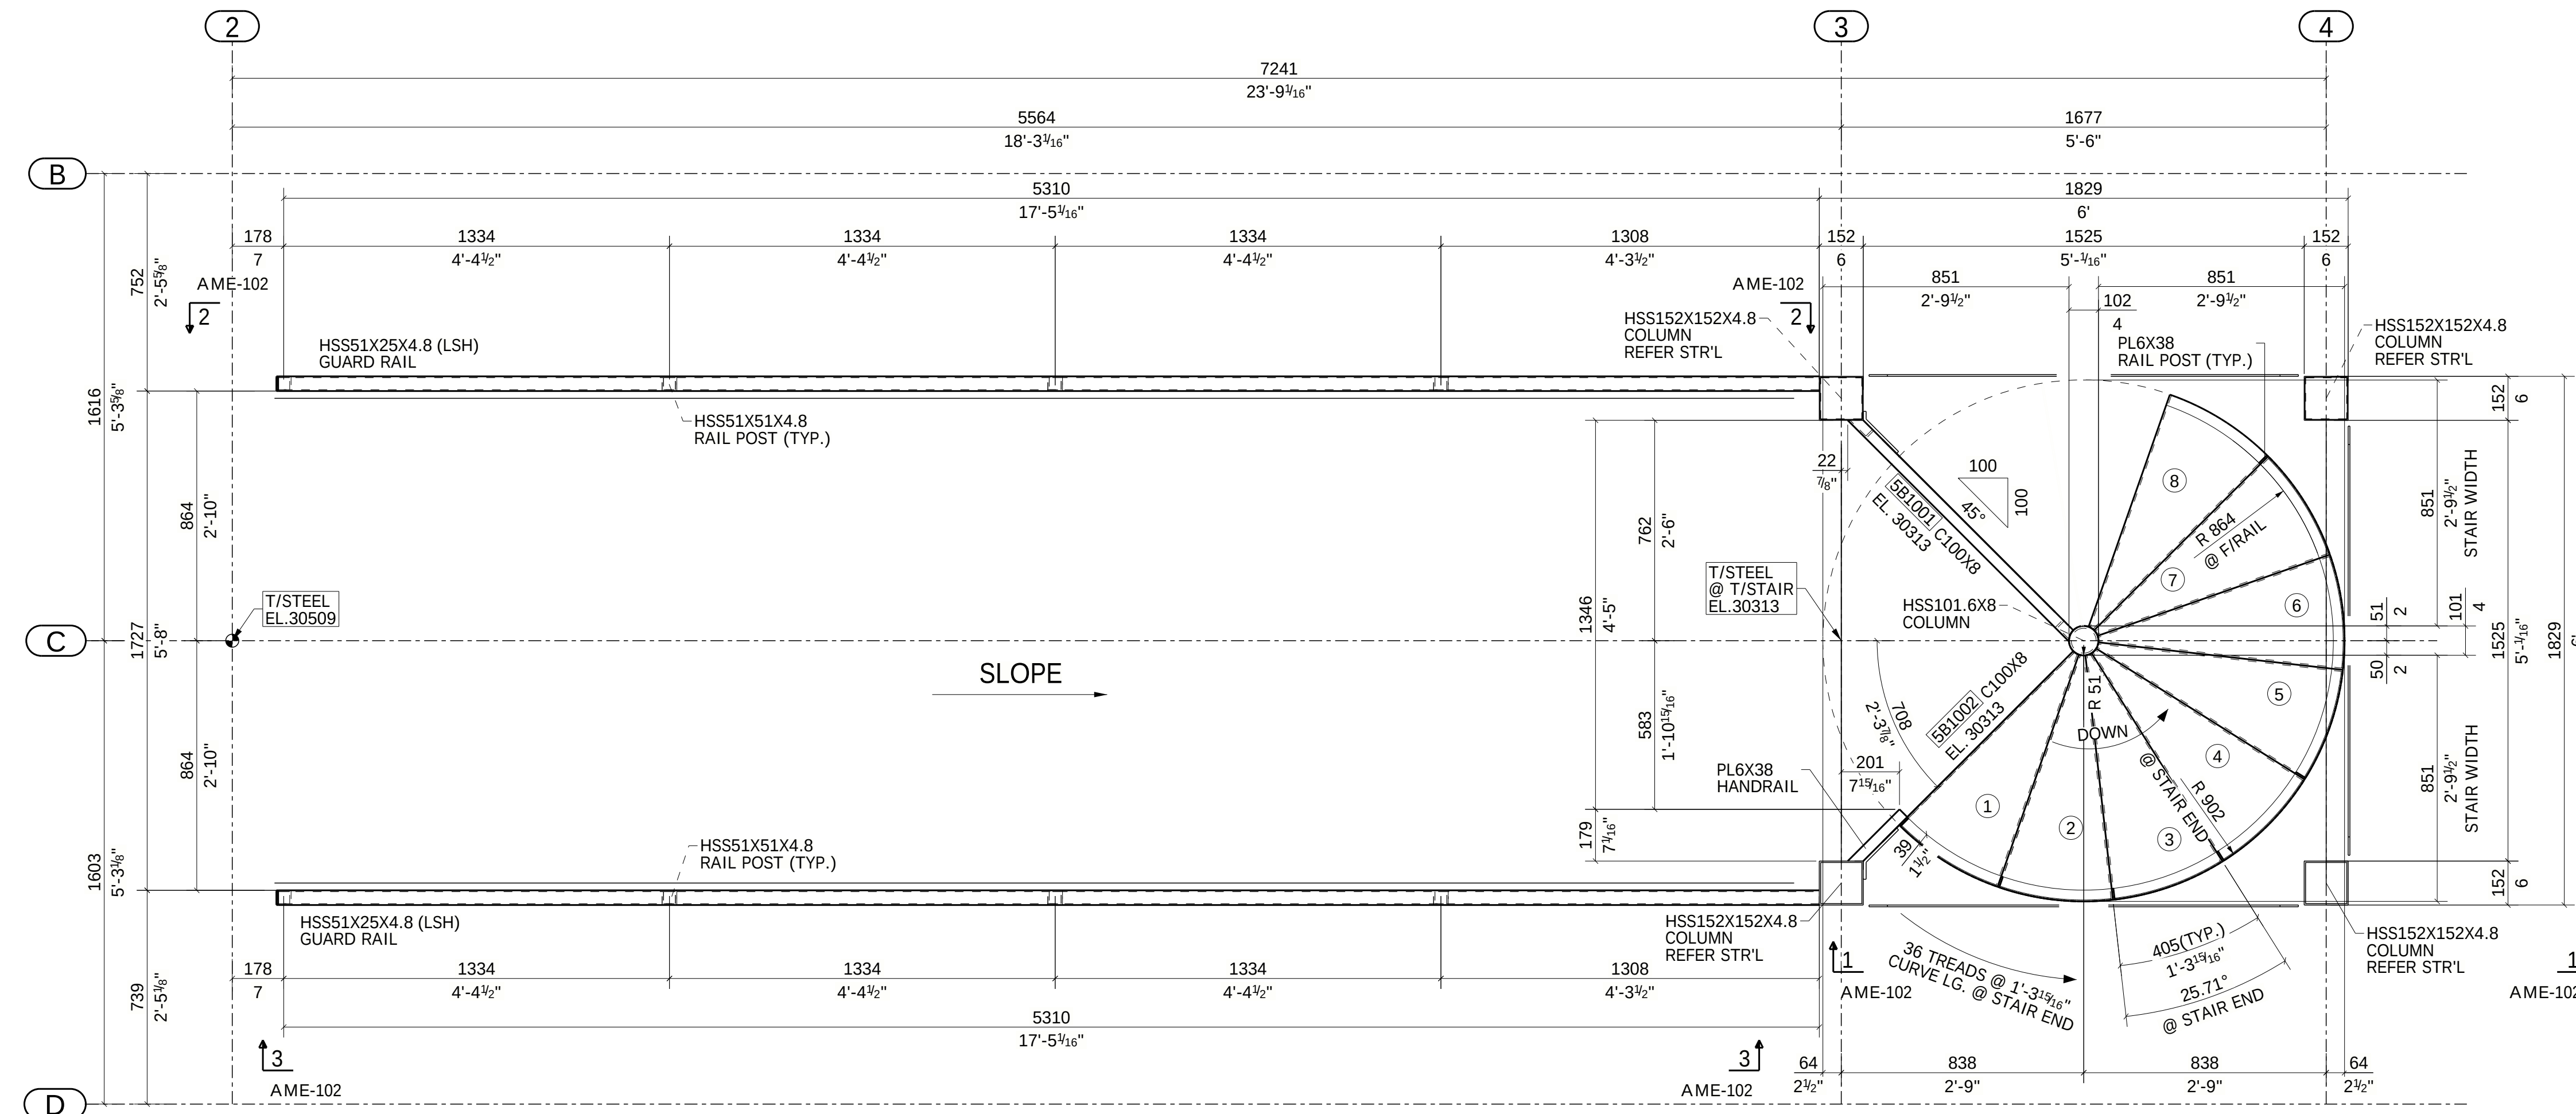


FRAMING PLAN @ WALKWAY - SOUTH CABIN
(REFER : PLAN 1:A01/A04)

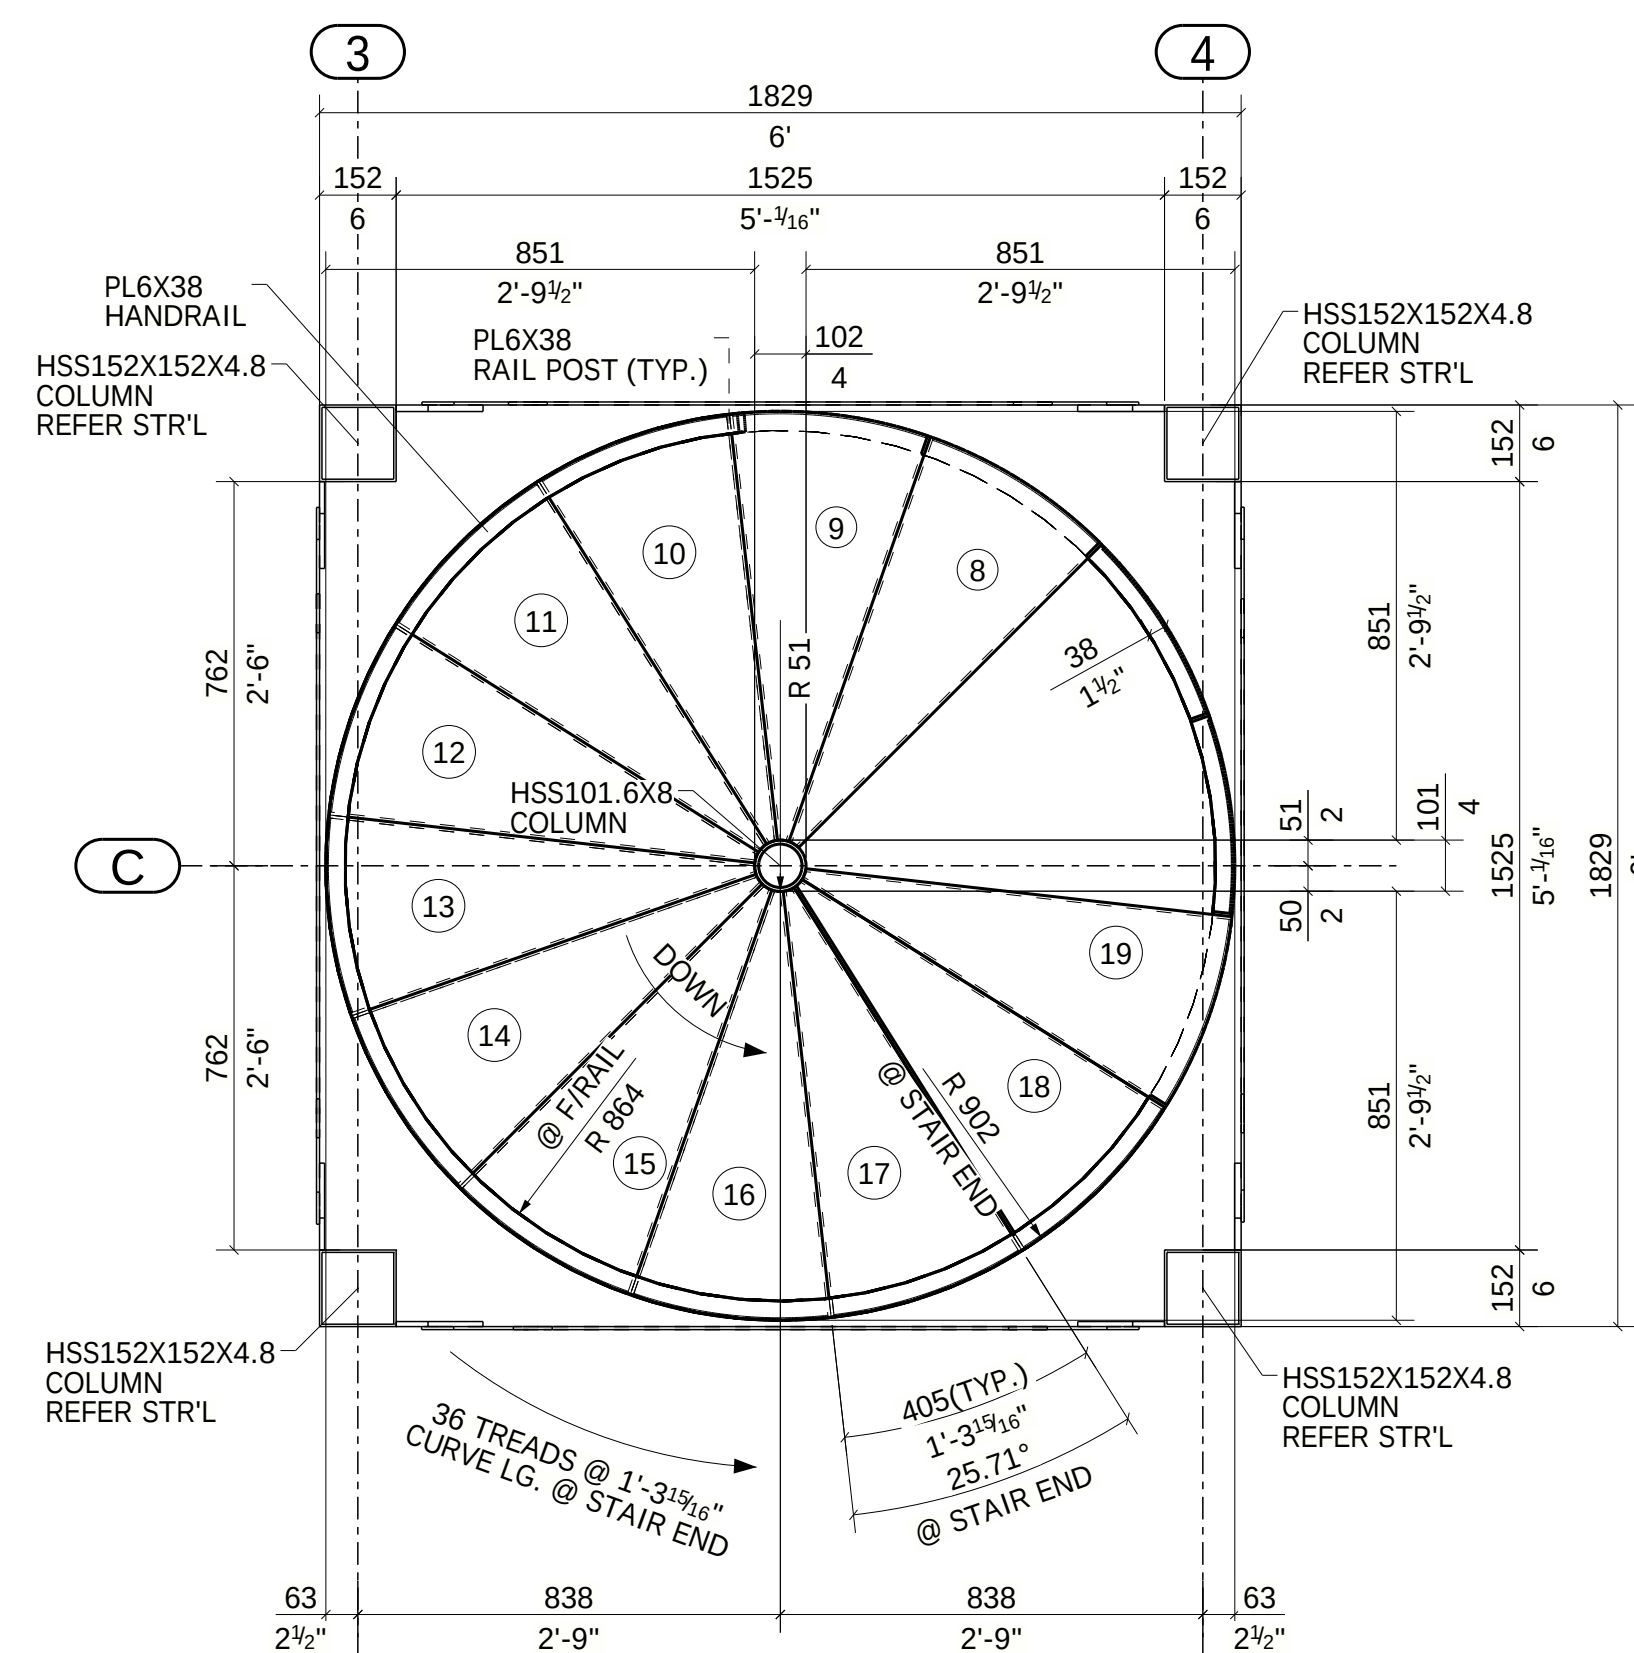

PARTIAL FRAMING PLAN - SOUTH CABIN

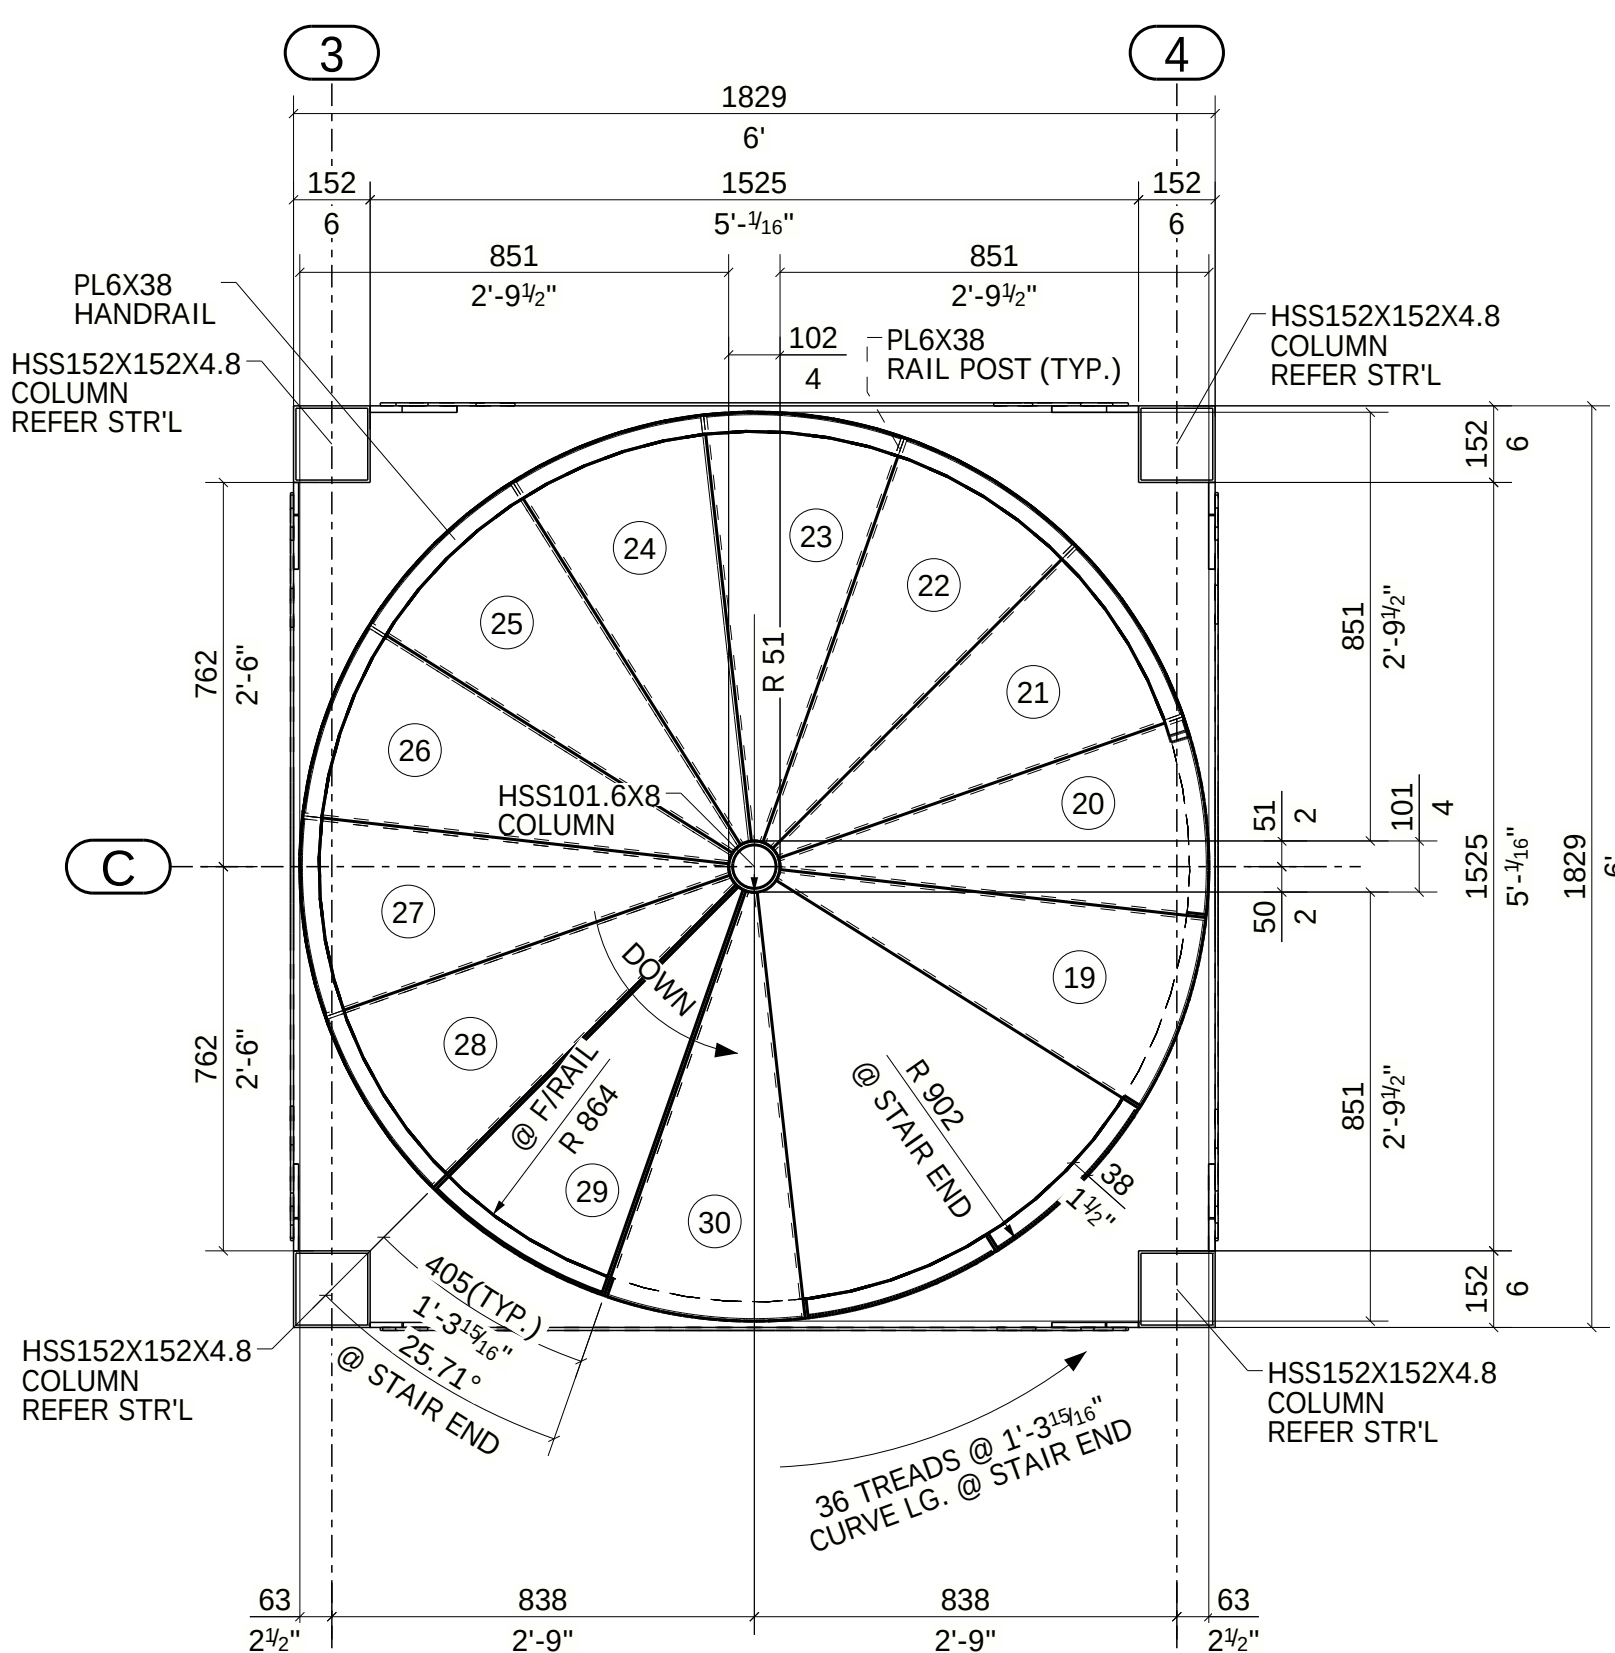


PARTIAL FRAMING PLAN - SOUTH CABIN

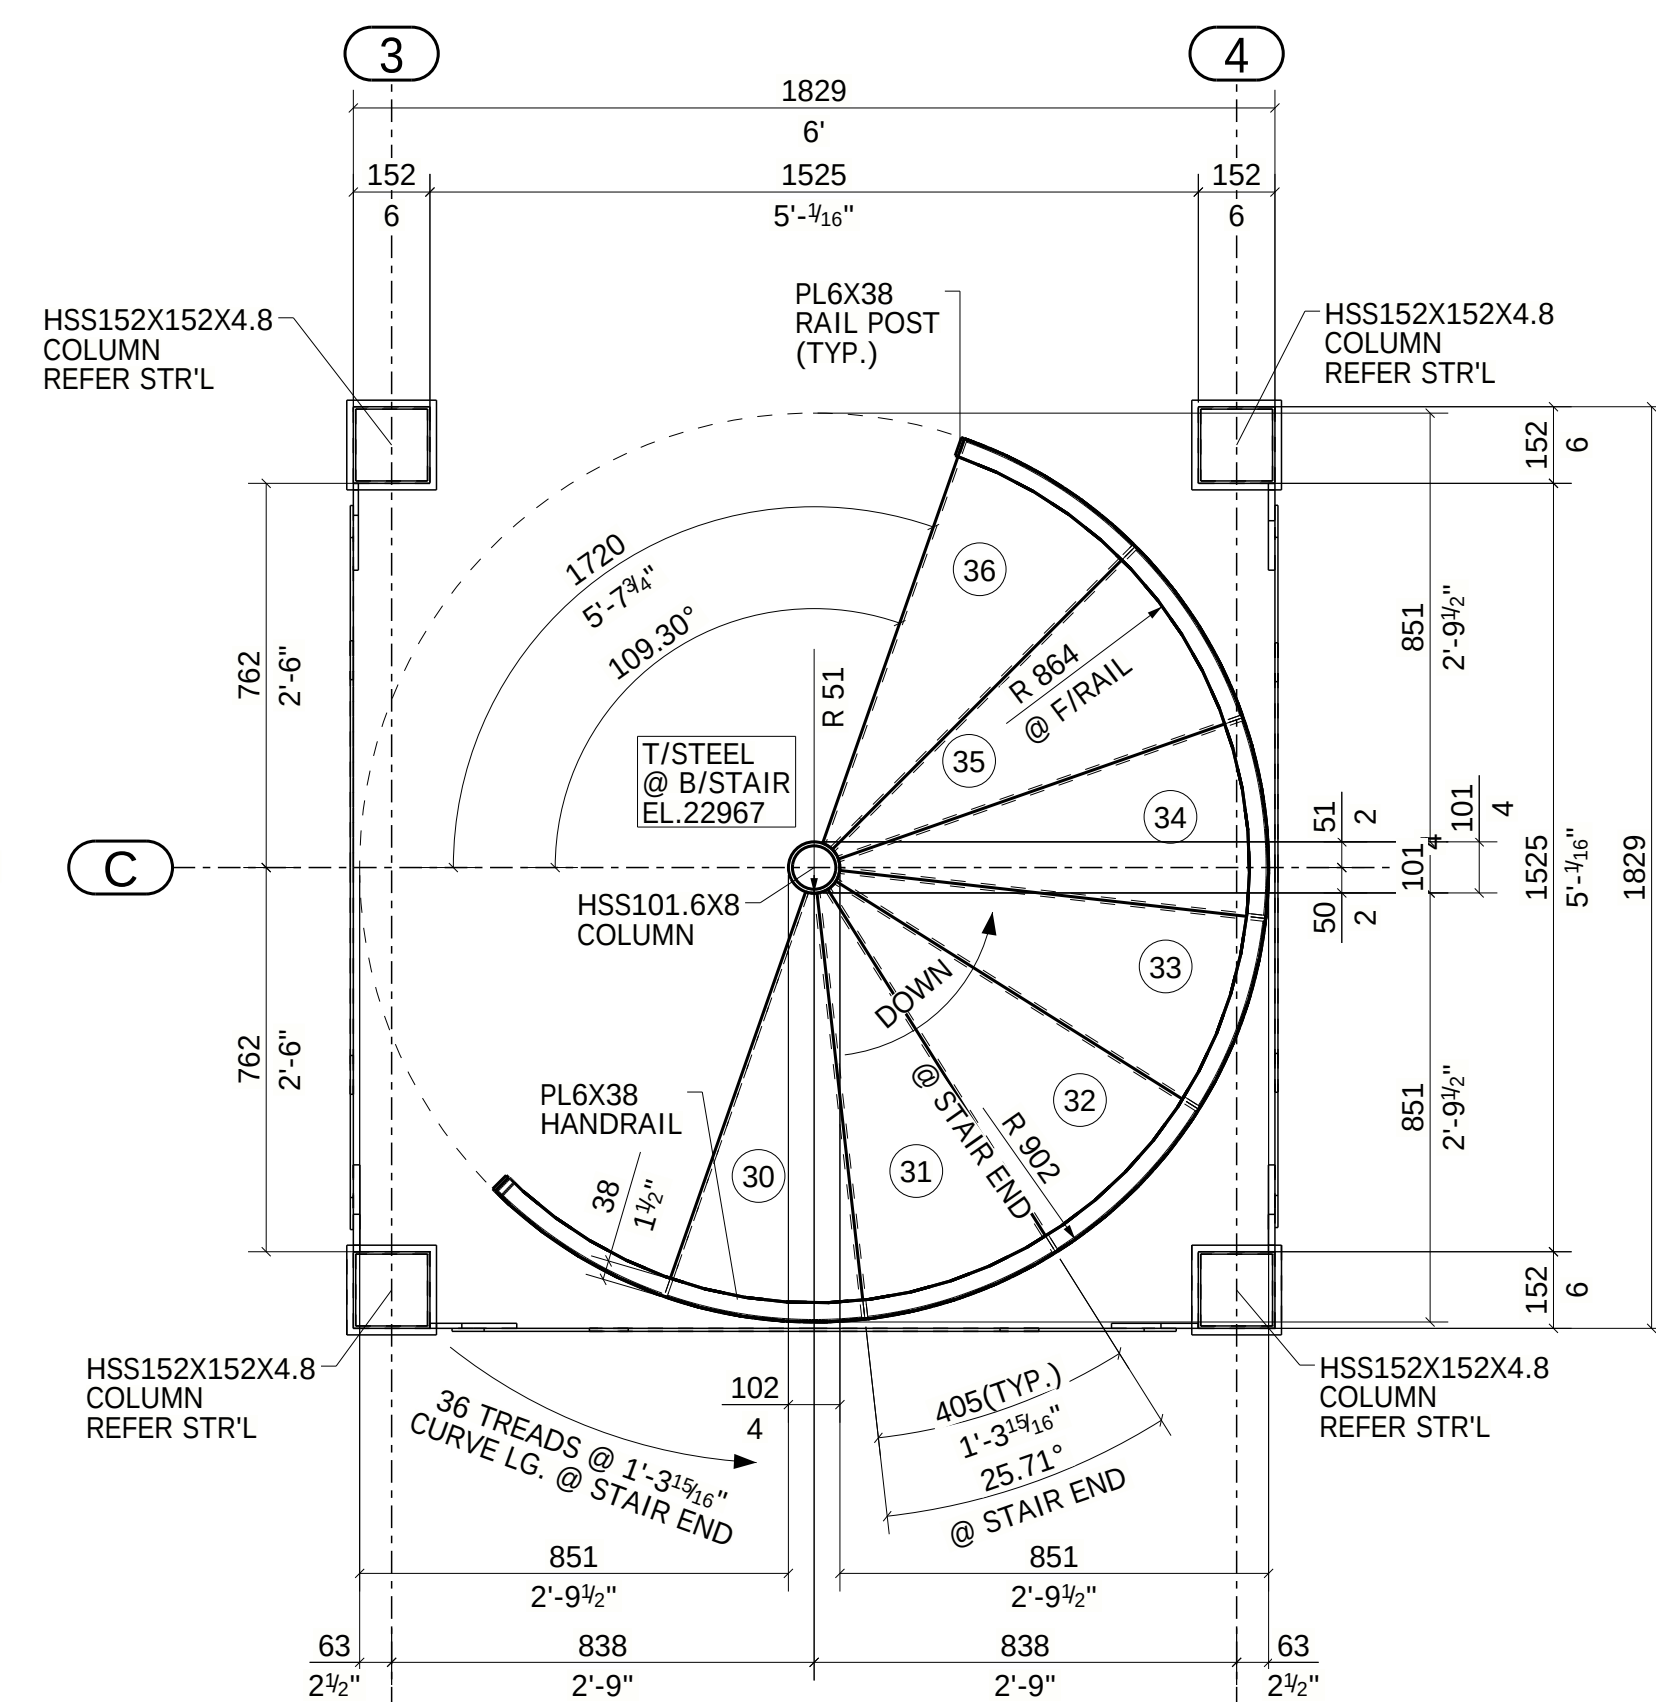


PARTIAL FRAMING PLAN - SOUTH CABIN



- NOTES:
1. REFER SHEET ME100 FOR 3D VIEW.
 2. REFER SHEETS ME101 TO ME103 FOR FRAMING PLANS.
 3. REFER SHEET ME105 FOR TYPICAL SECTIONS AND ELEVATIONS.

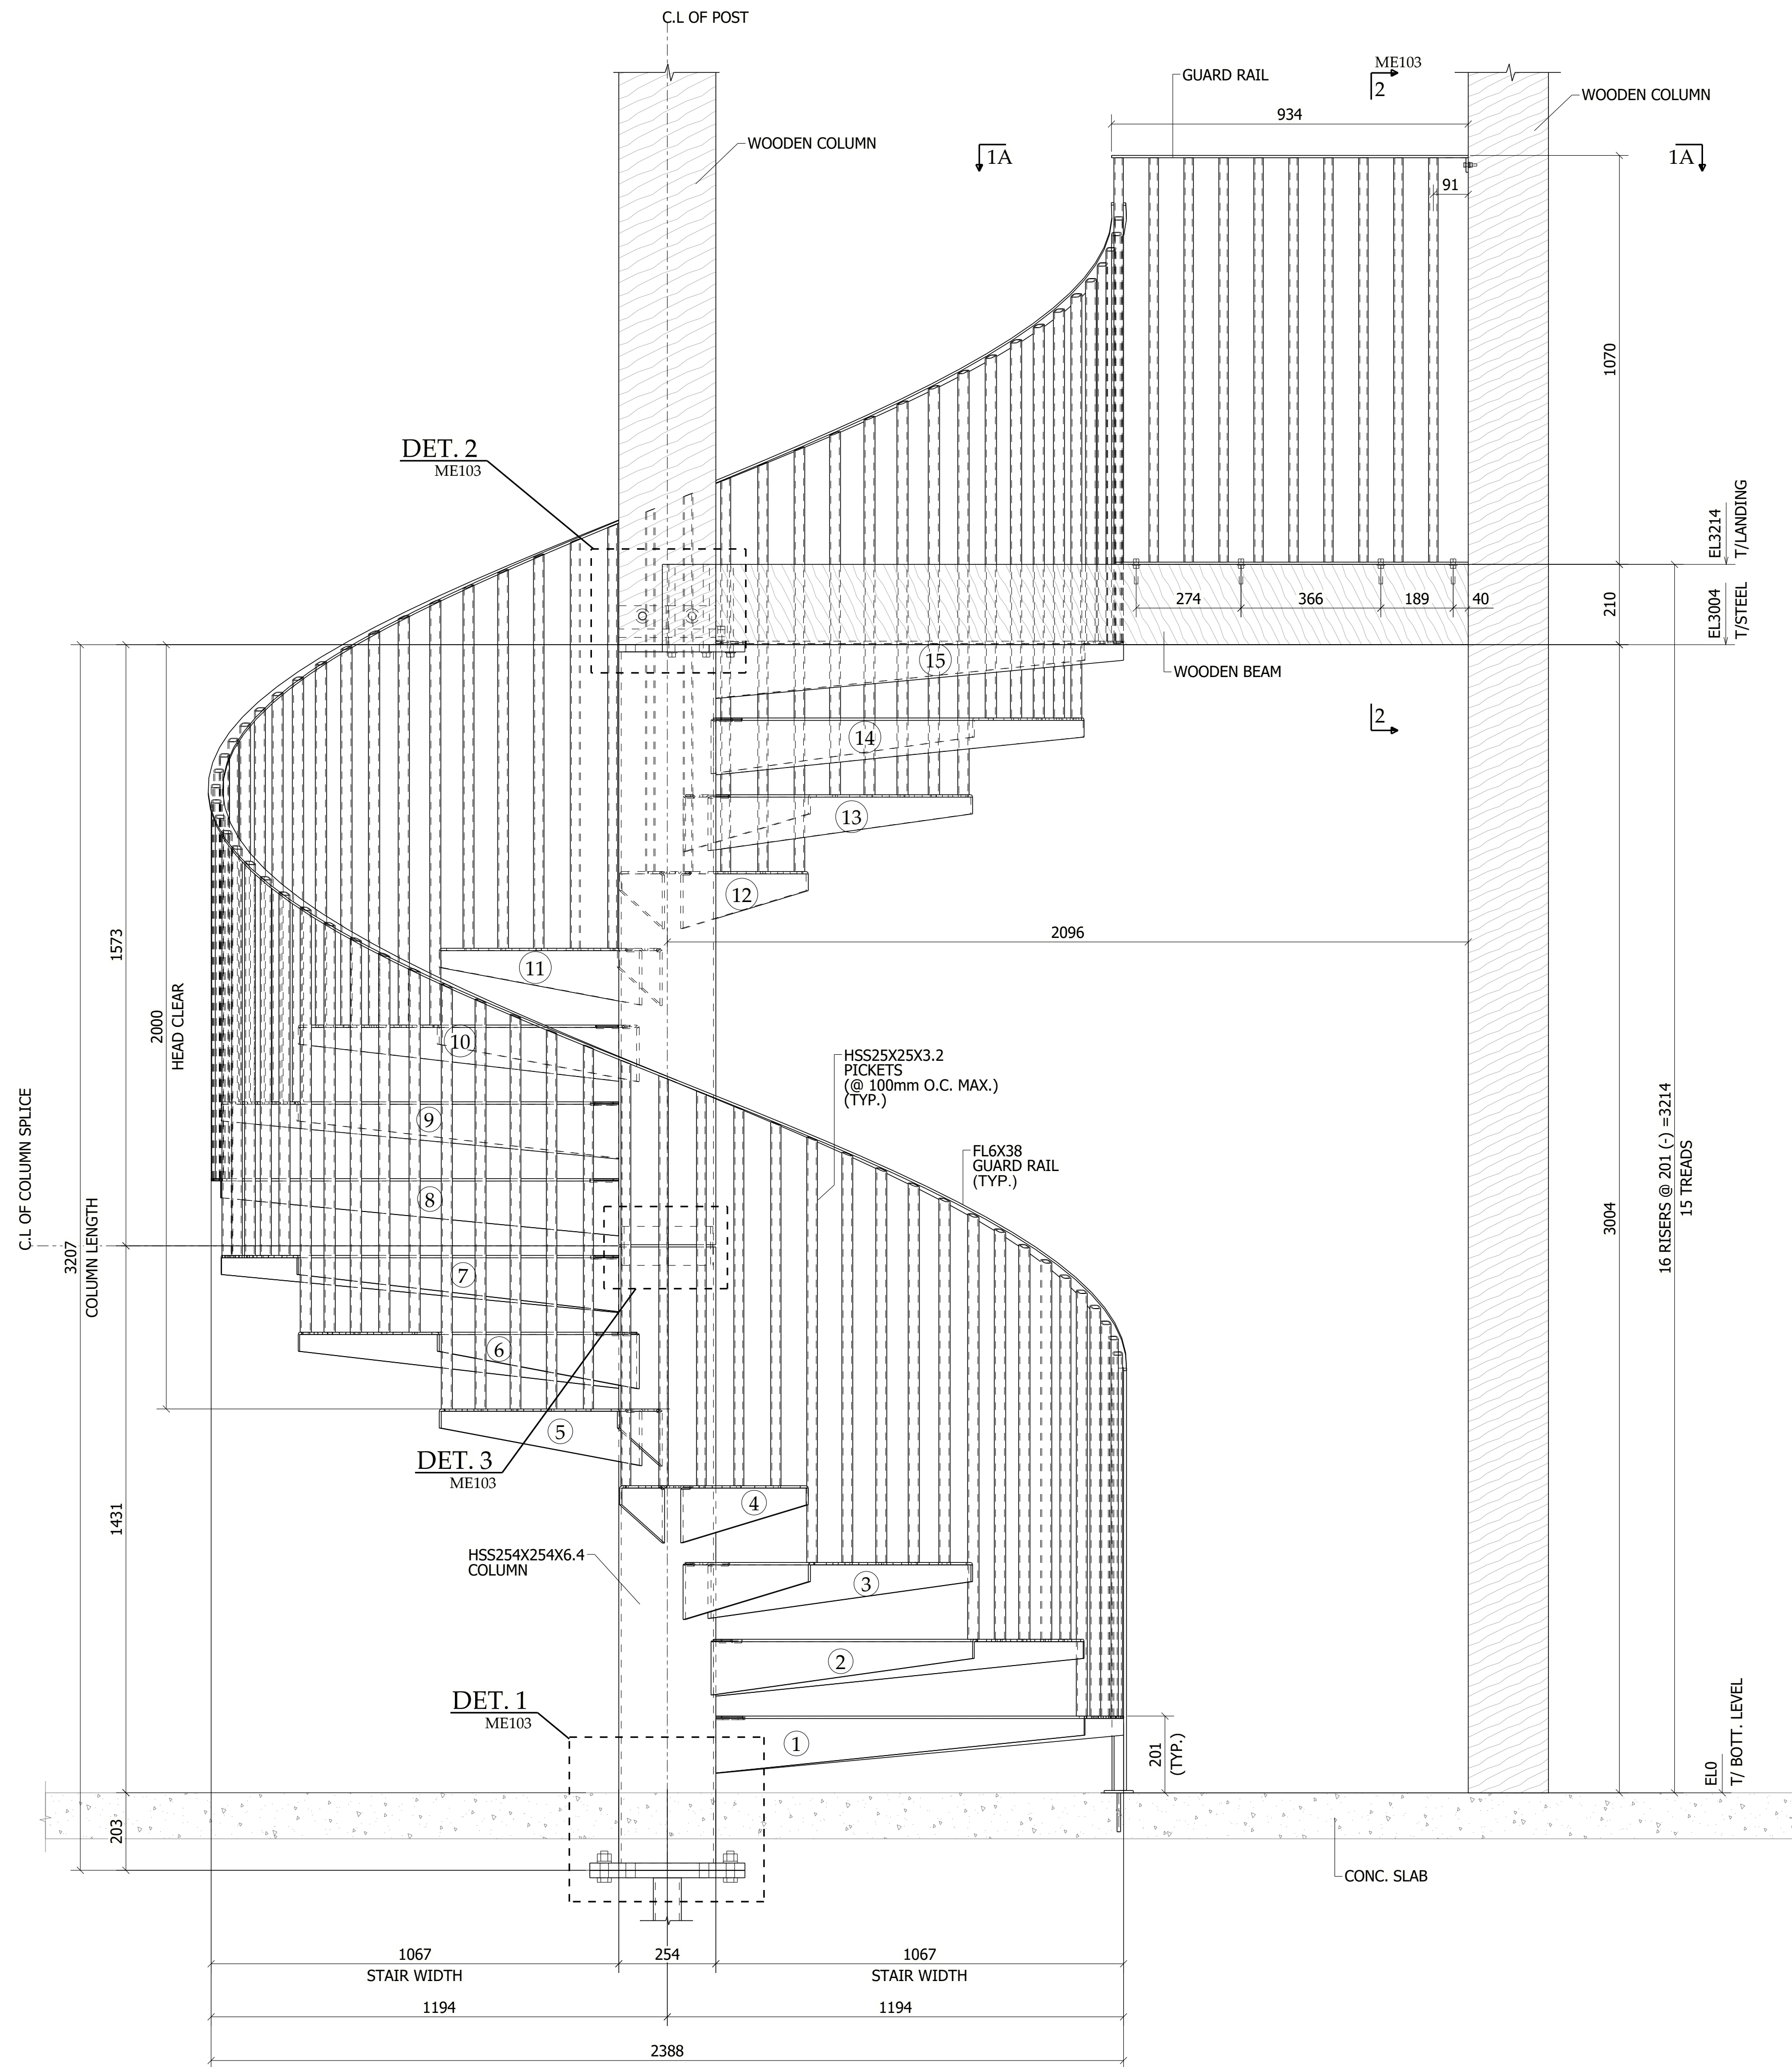


SECTION A - A
ME101
(REFER : COUPE GENERALE C-C/ 351)

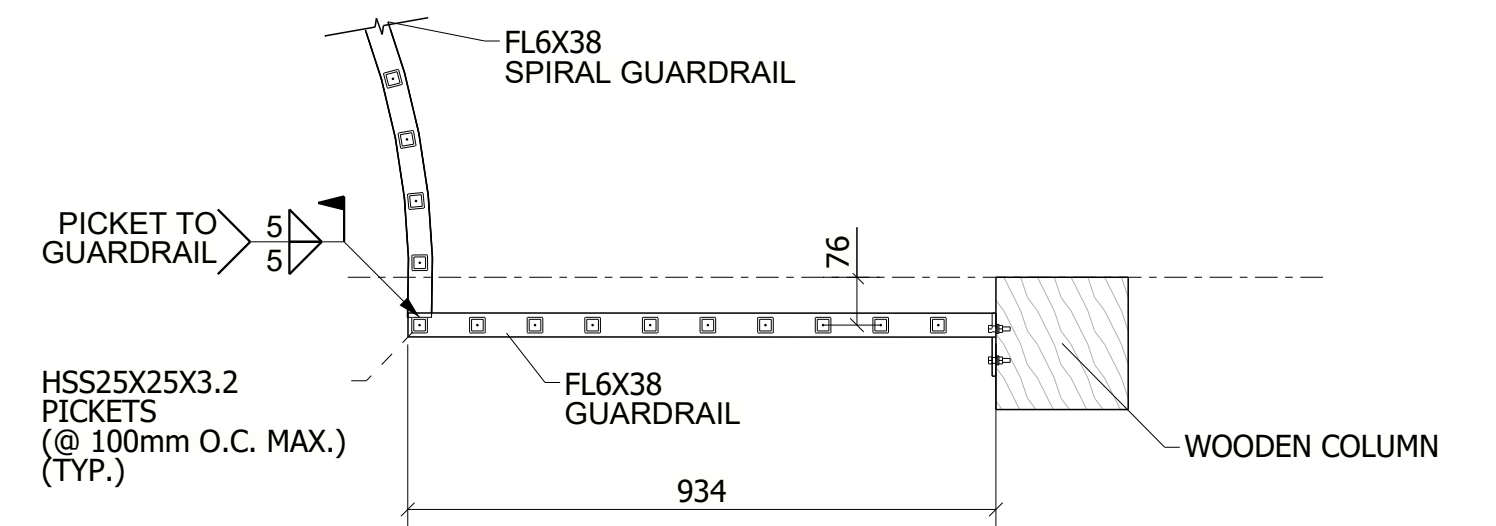

SECTION 1A - 1A


NOTES:

1. REFER SHEET ME100 FOR 3D-VIEW.
2. REFER SHEET ME101 FOR SPIRAL STAIR FRAMING PLAN
3. REFER SHEET ME103 FOR TYPICAL SECTION & DETAILS.

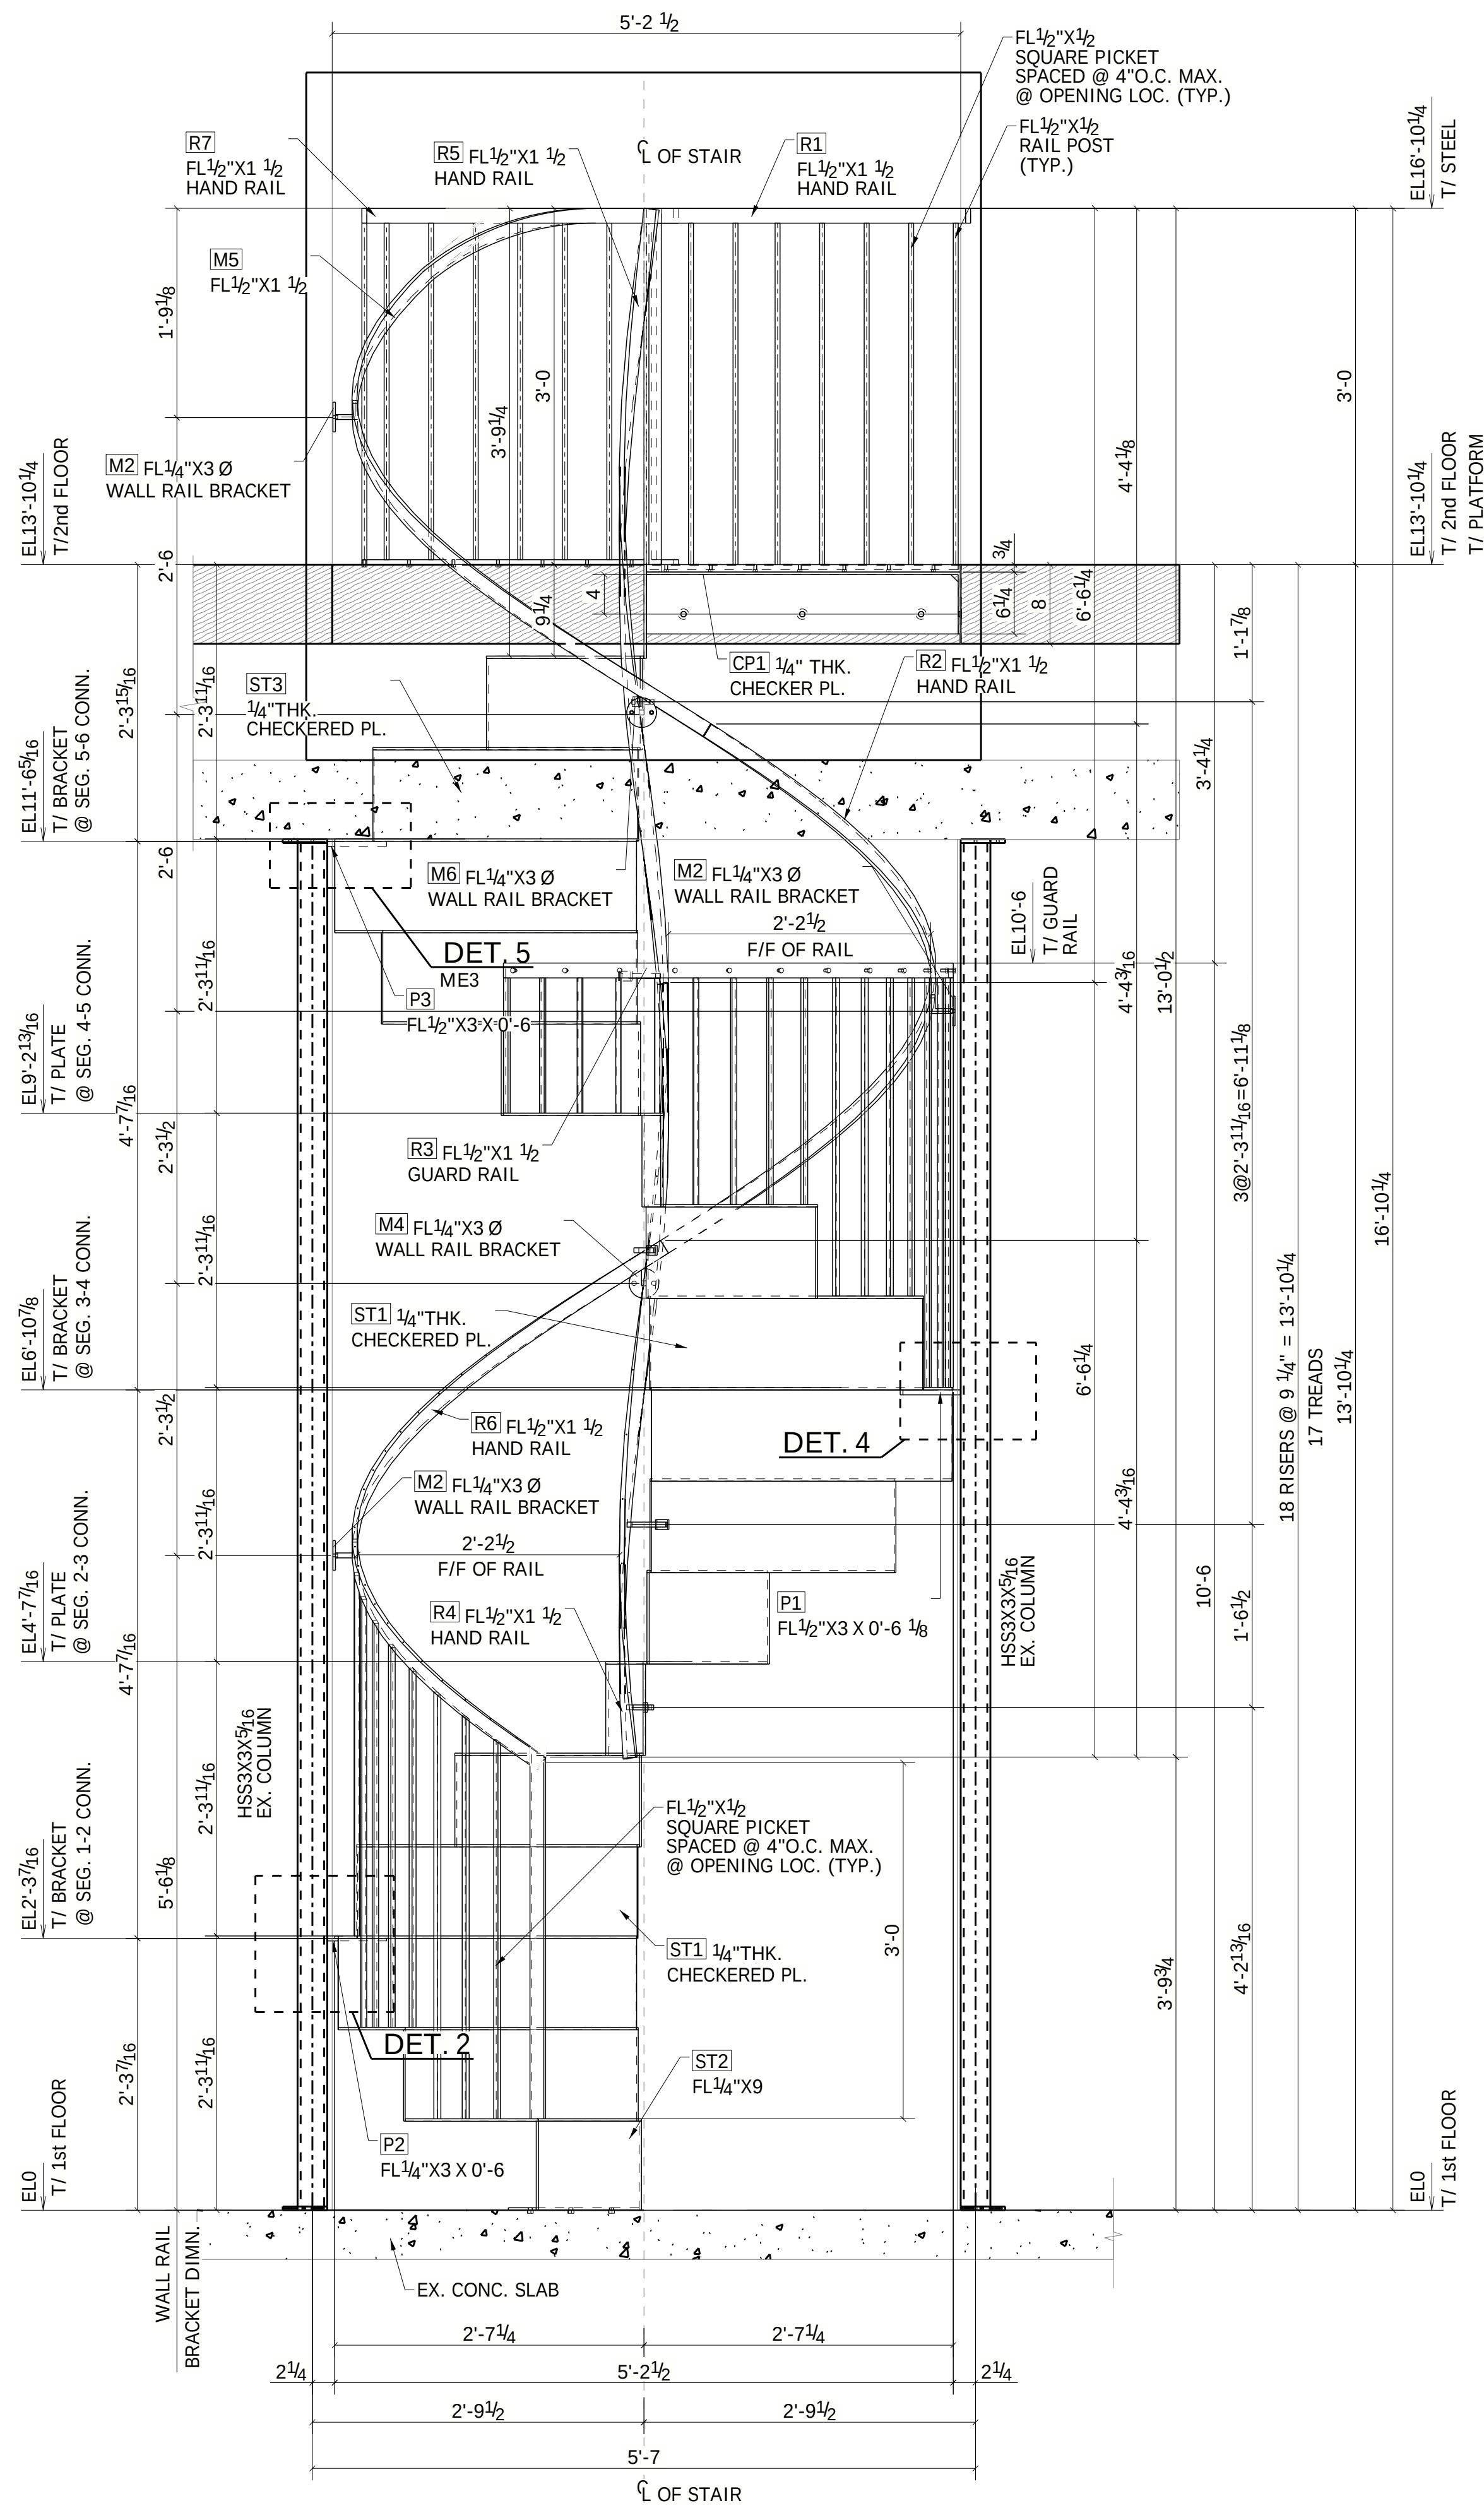


SECTION A - A
ME1

REFER : PH1 STAIR SECTION & ELEVATION (5 & 6/A2.1)

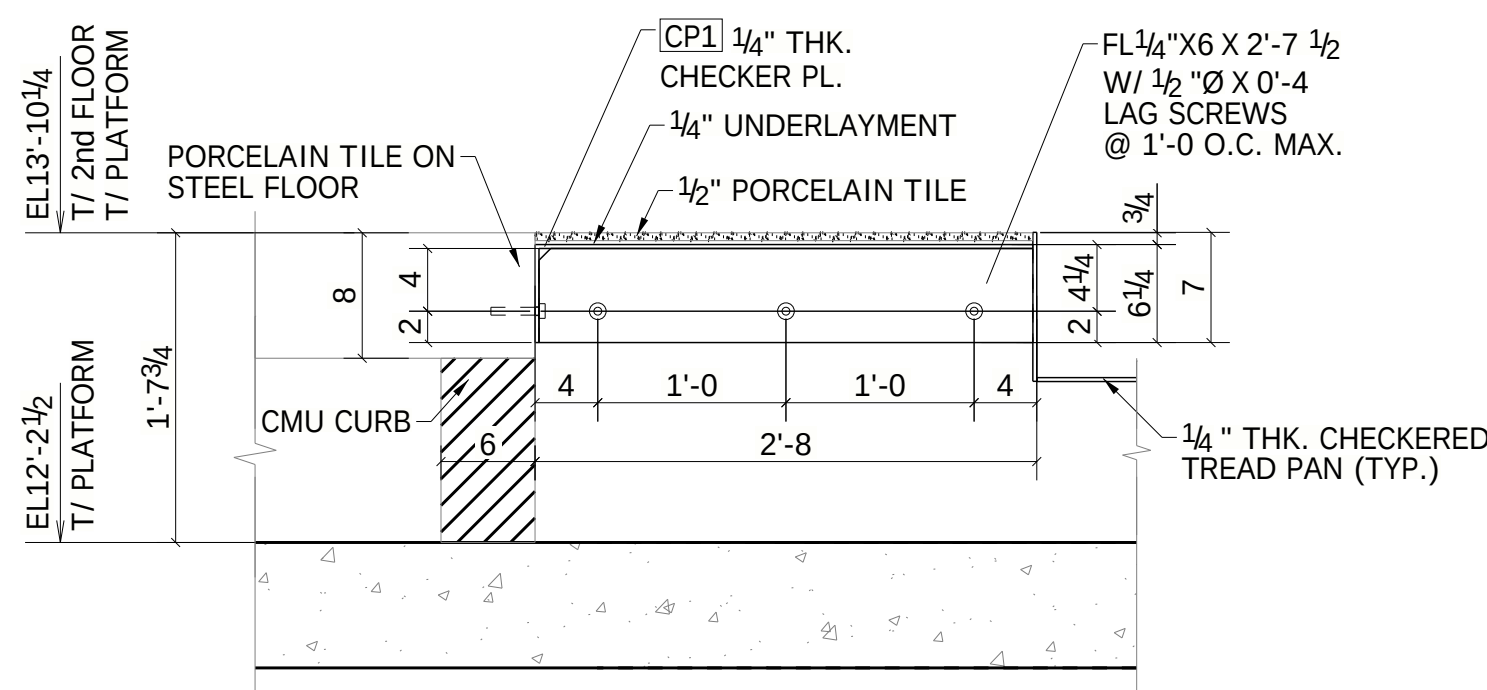


SECTION E - E
ME1

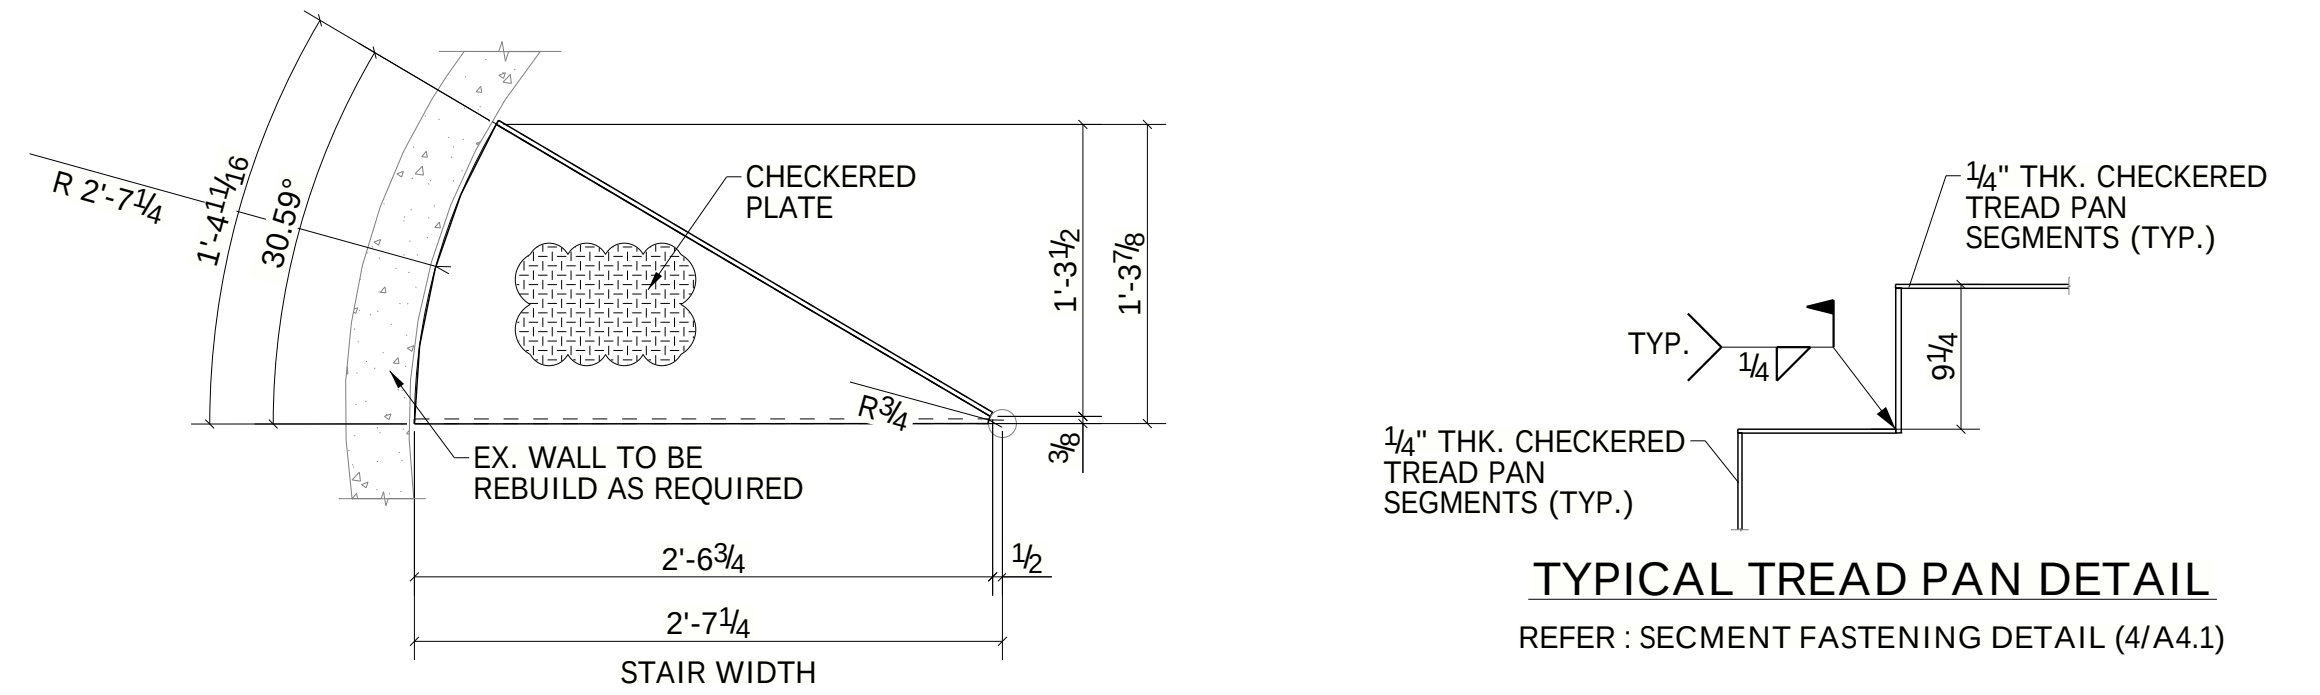


TYPICAL CHECKERED PLATE TREAD PAN DETAIL


REFER : TREAD PLAN DETAIL (3/A2.1)

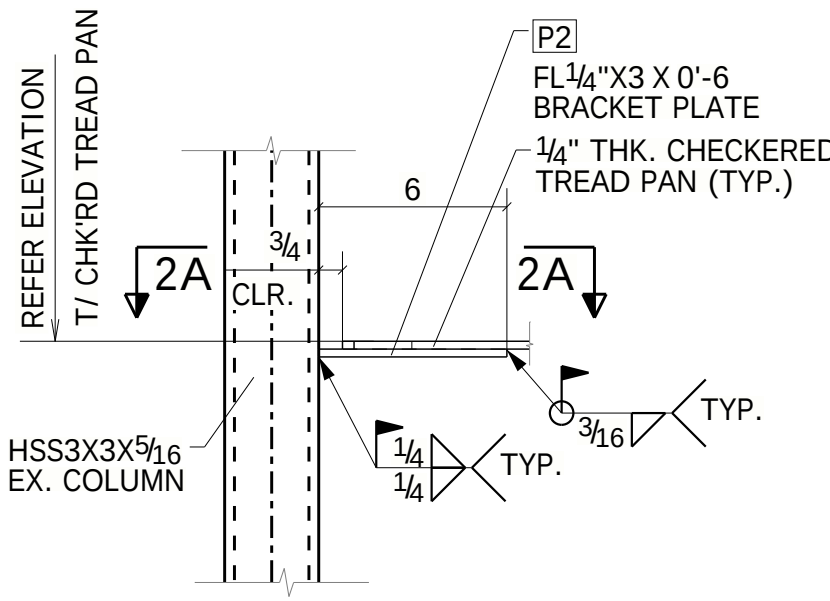


DETAIL 2

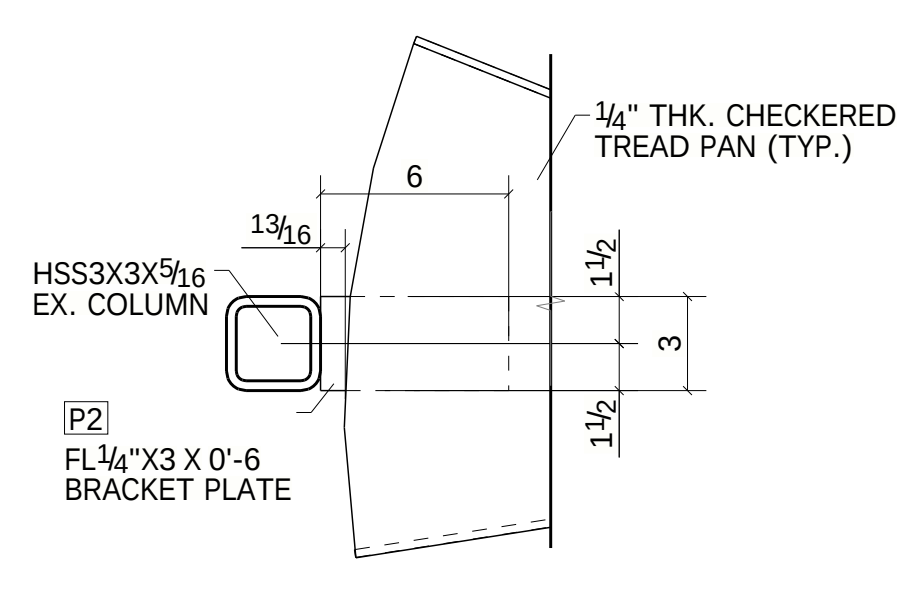


SECTION 2A - 2A

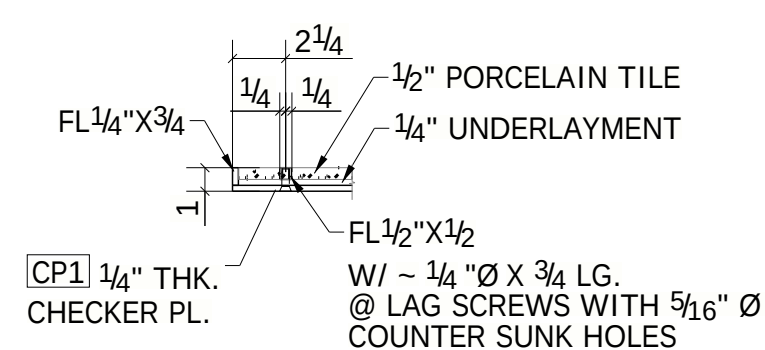


SECTION B1 - B1

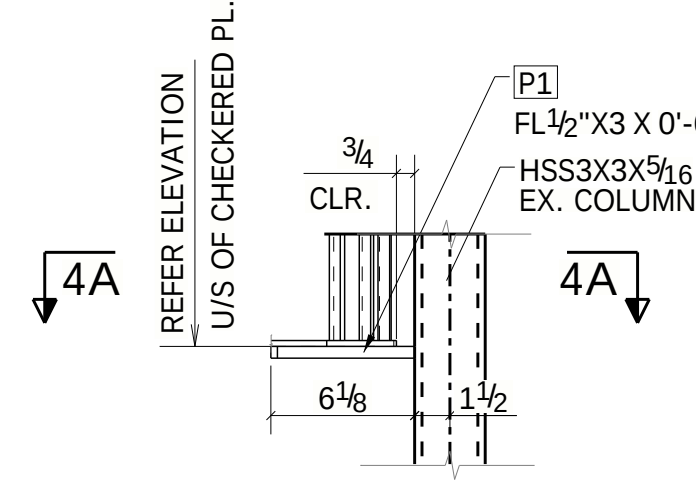

DETAIL 4

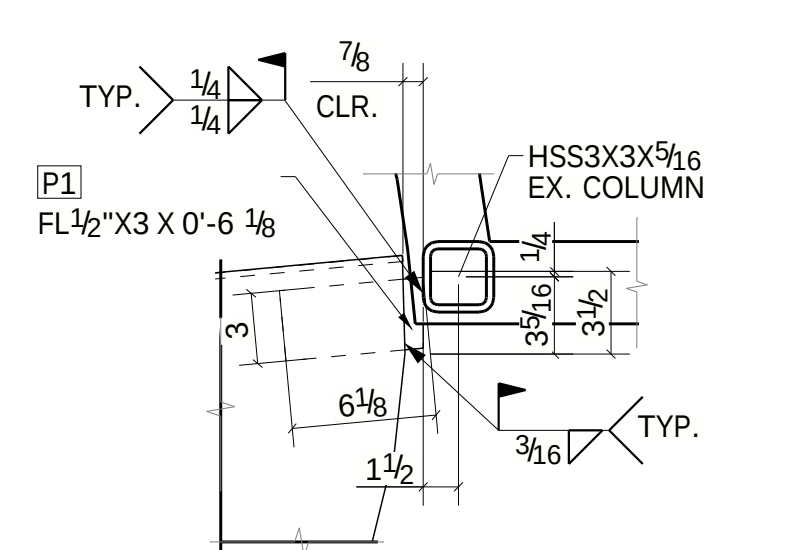


SECTION 4A - 4A

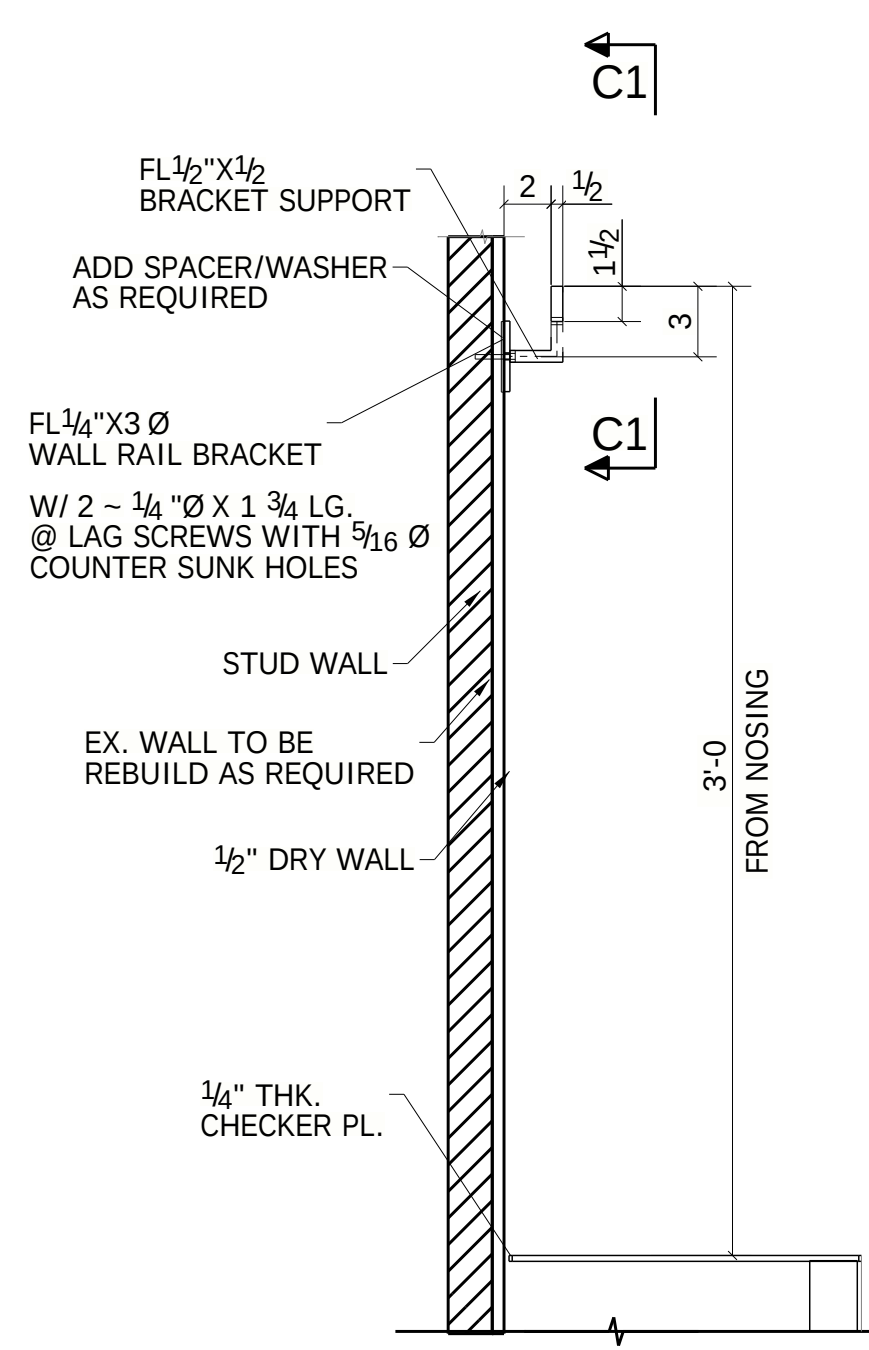


SECTION C - C
ME1

REFER : HANDRAIL PROFILE (5/A4.1)

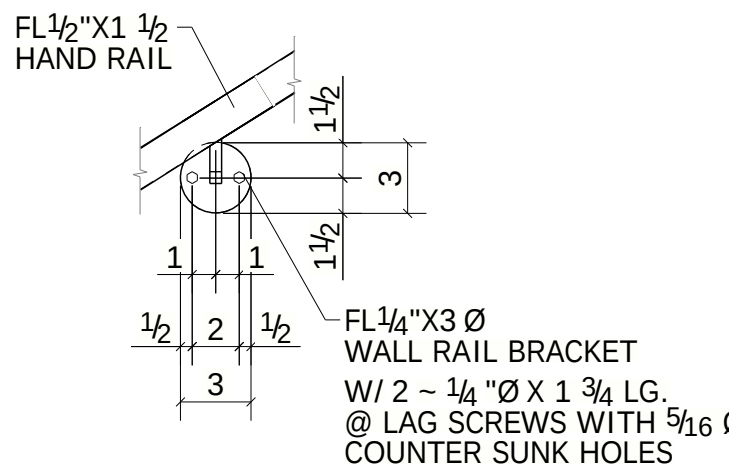


SECTION C1 - C1

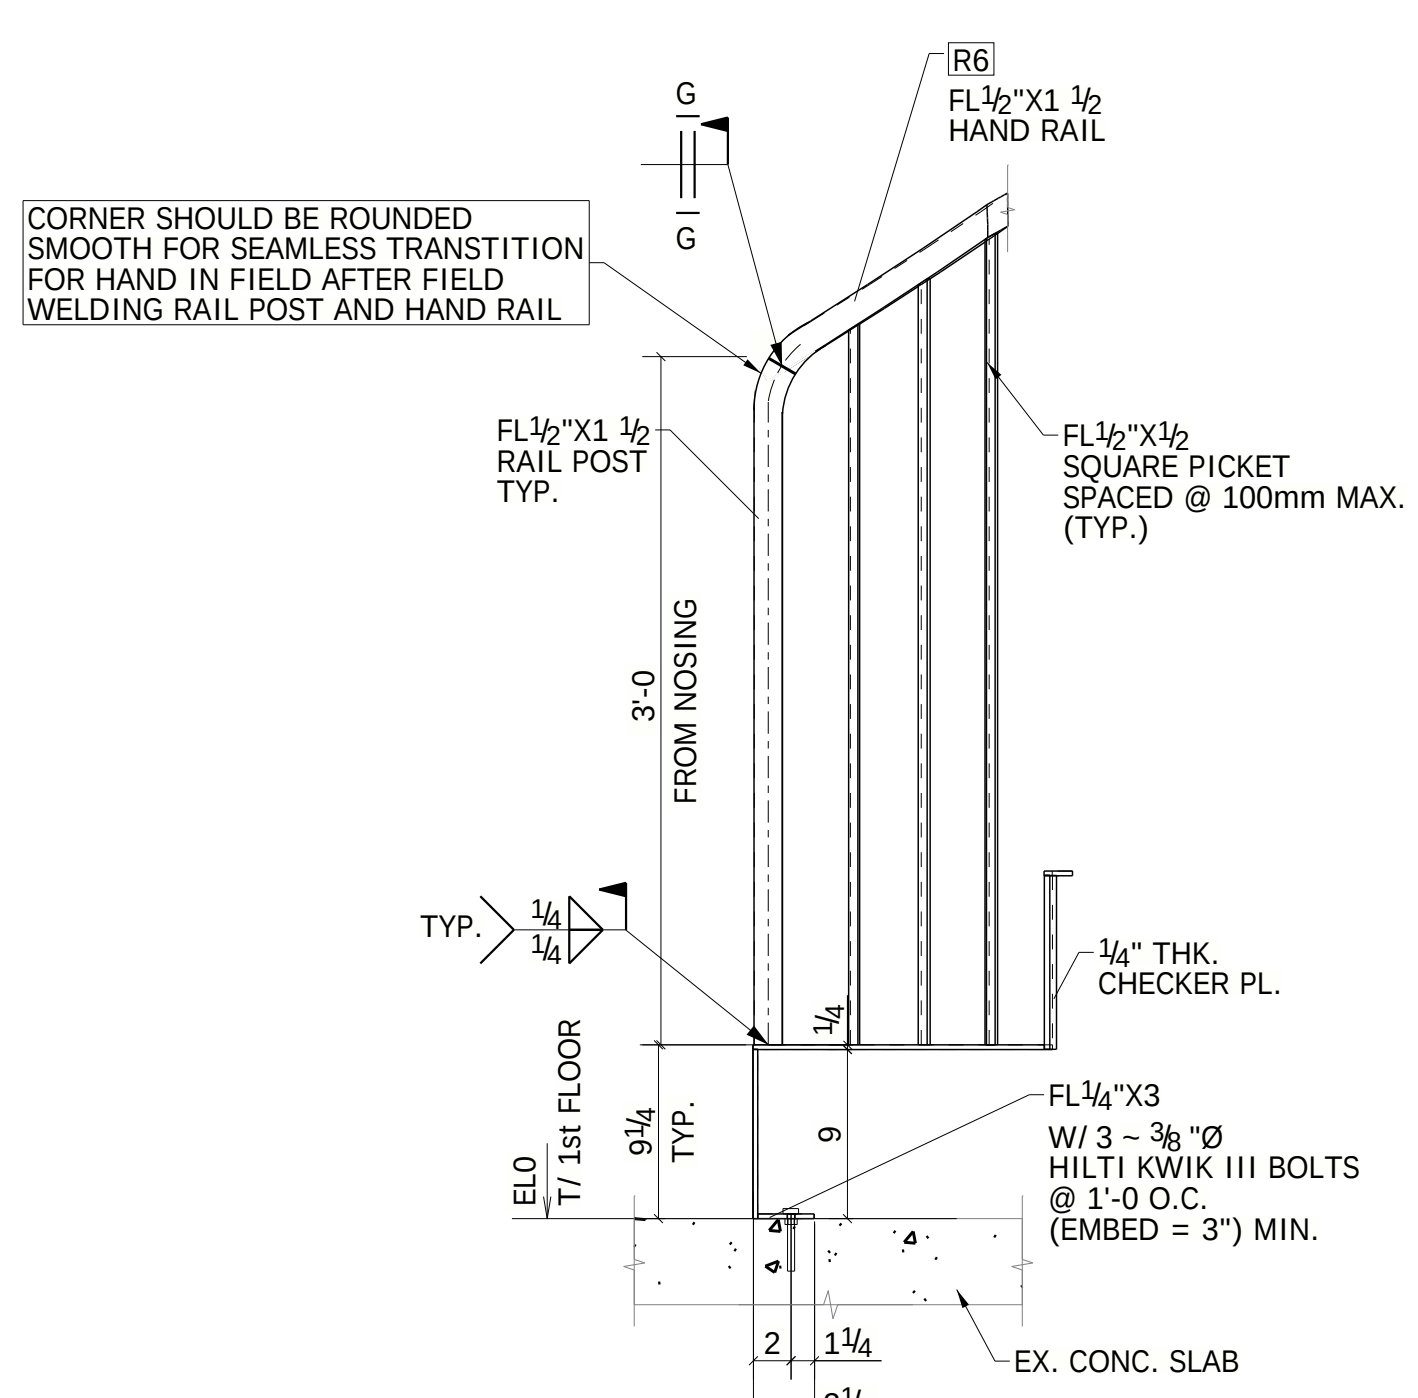


SECTION D - D
ME1


REFER : BASE DETAIL (2/A4.1)

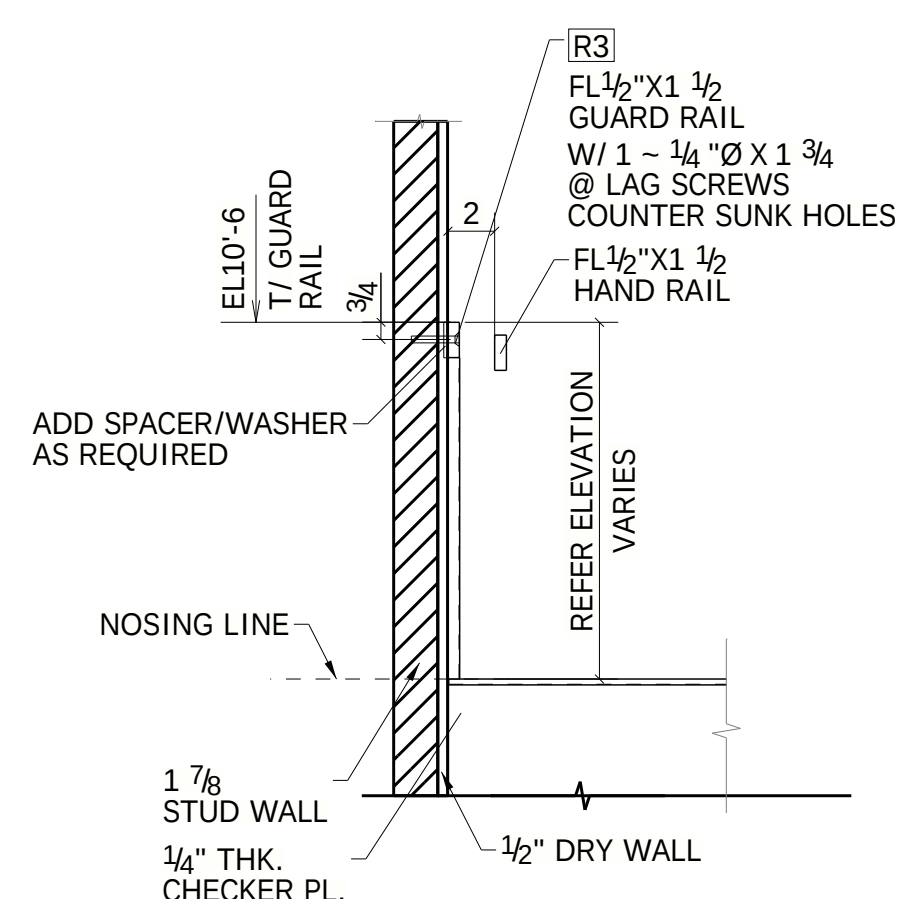


SECTION H - H
ME1

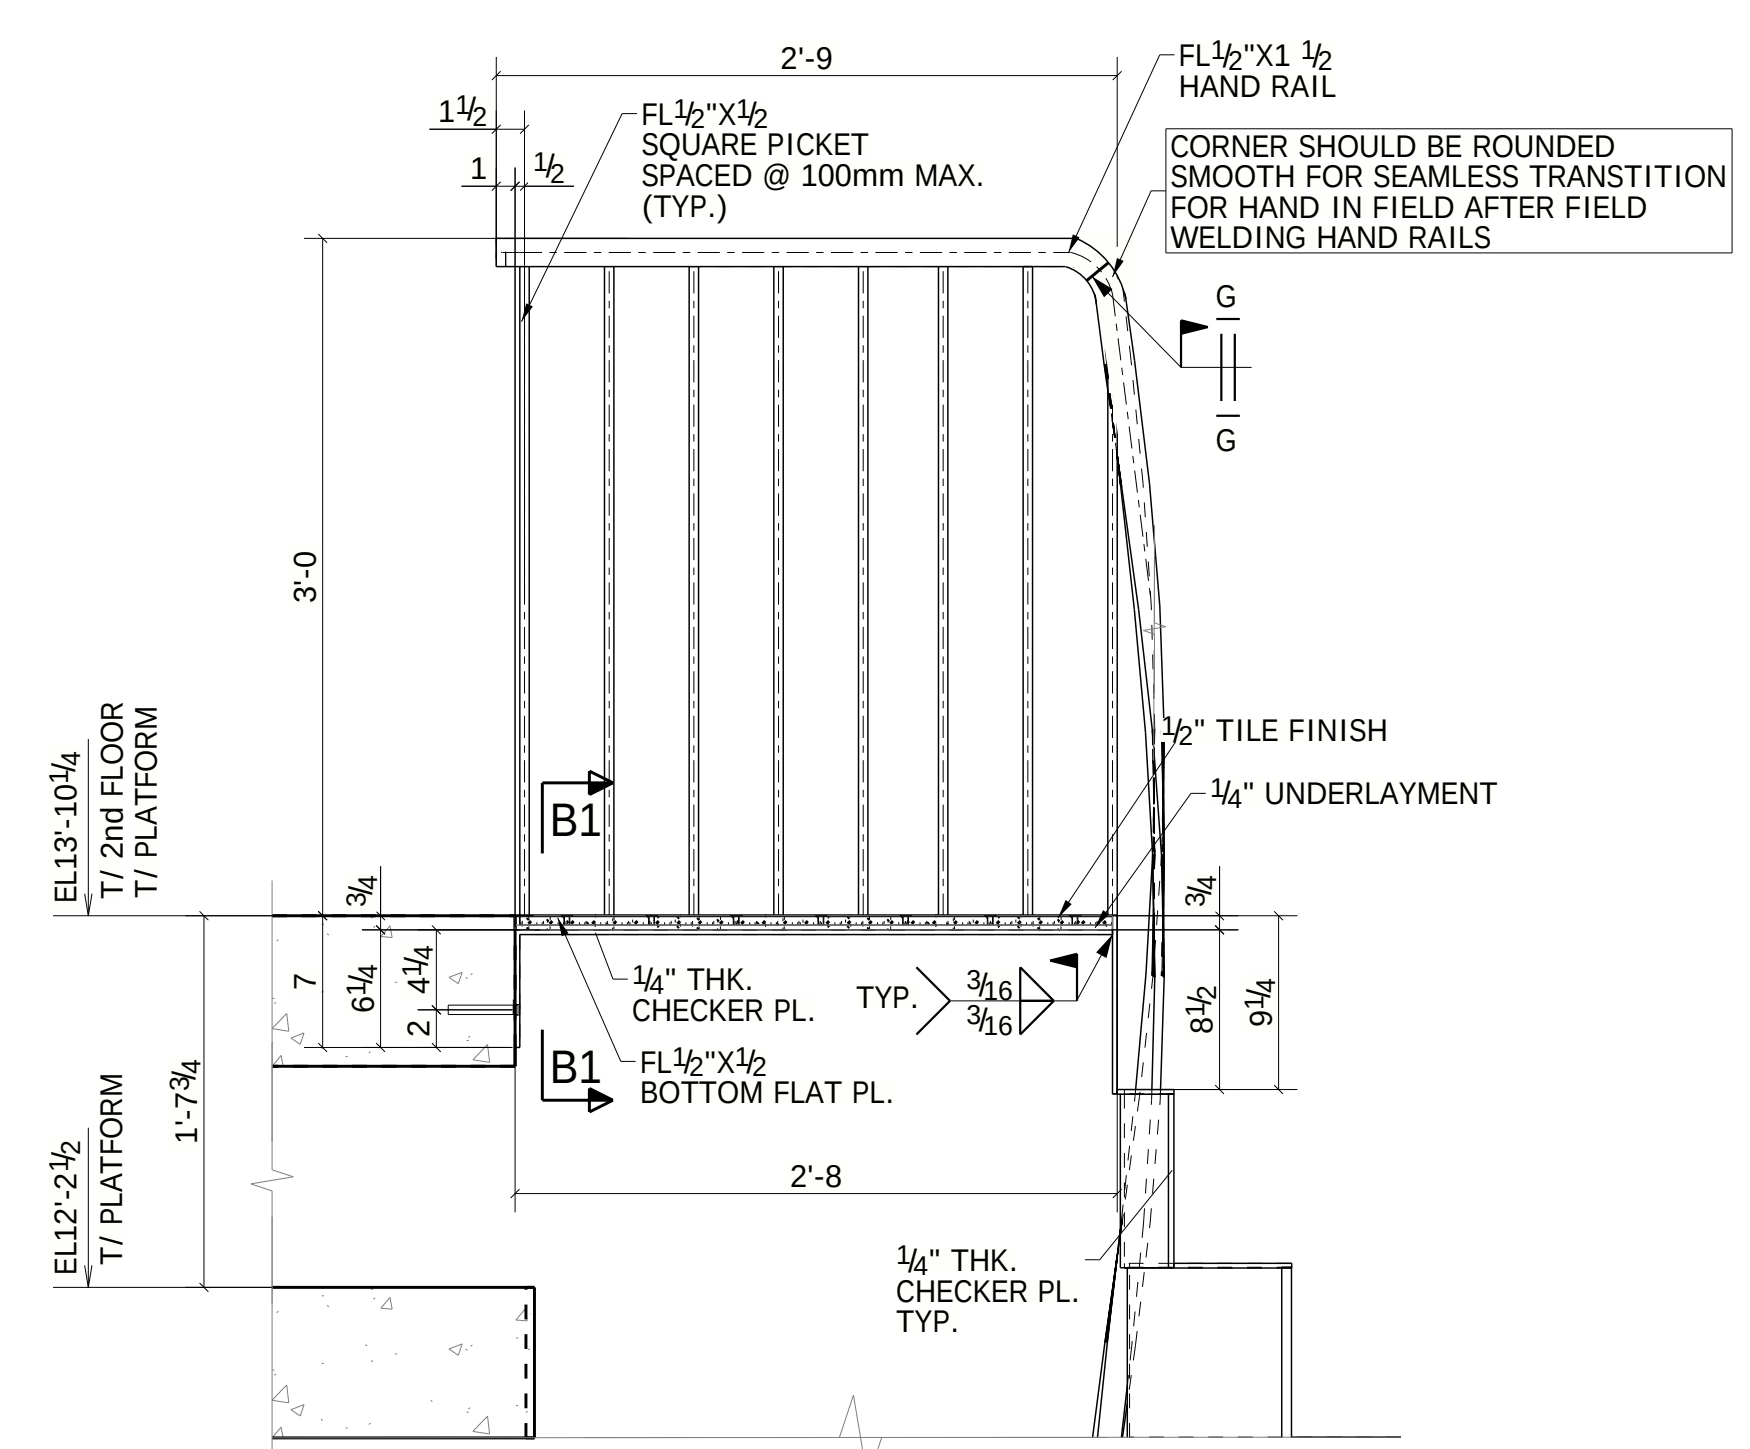


SECTION B - B
ME1

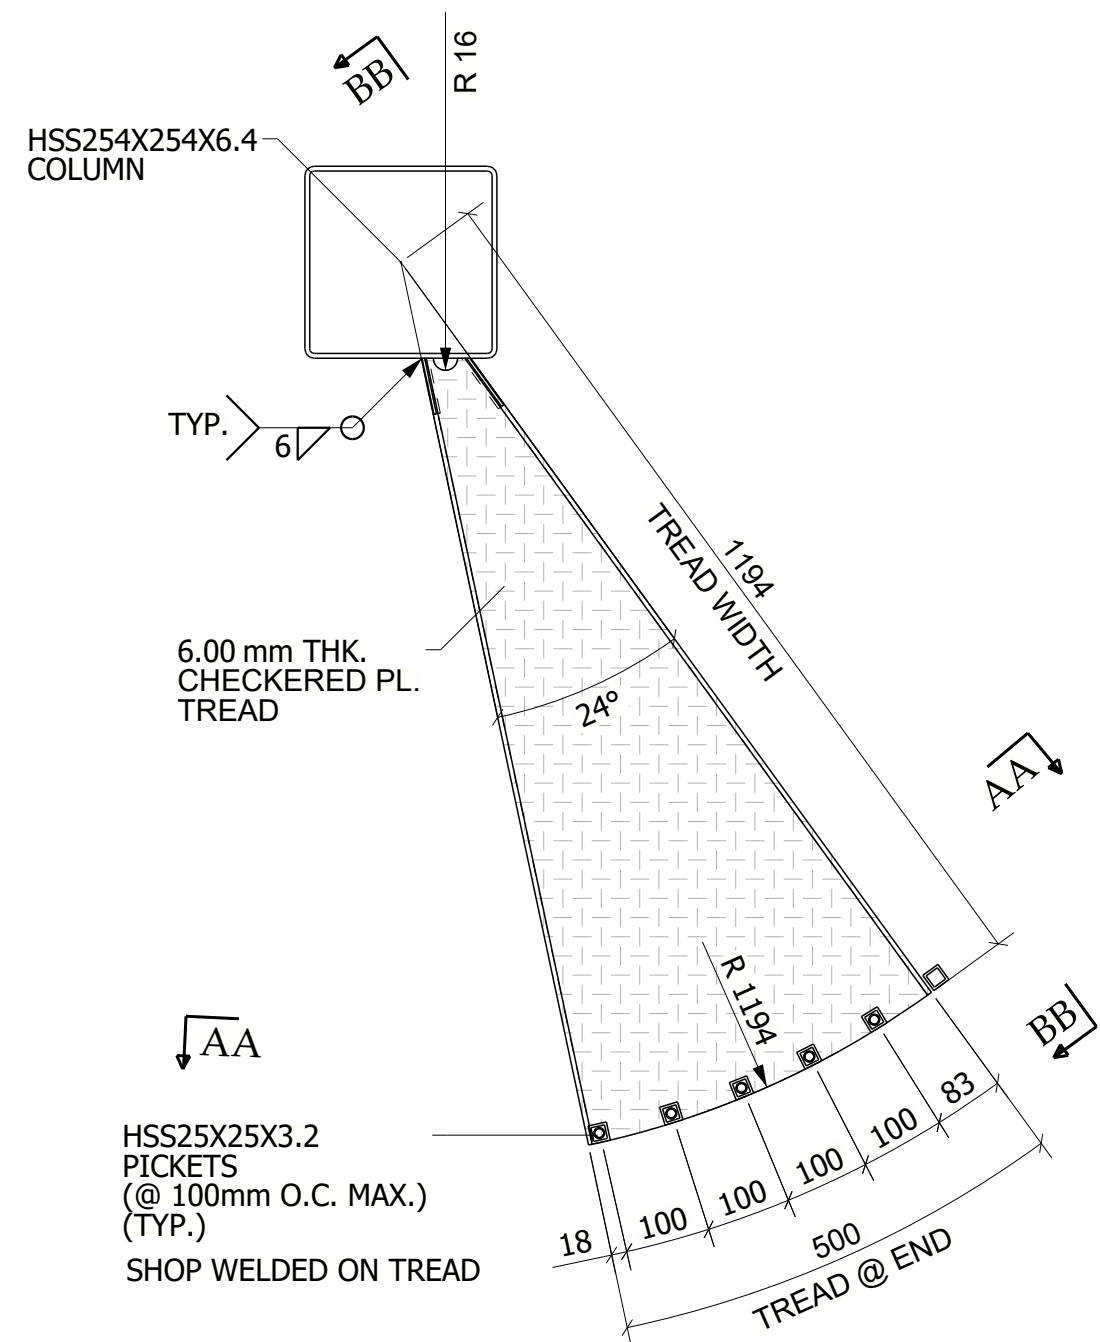


TYPICAL STAIR TREAD DETAIL

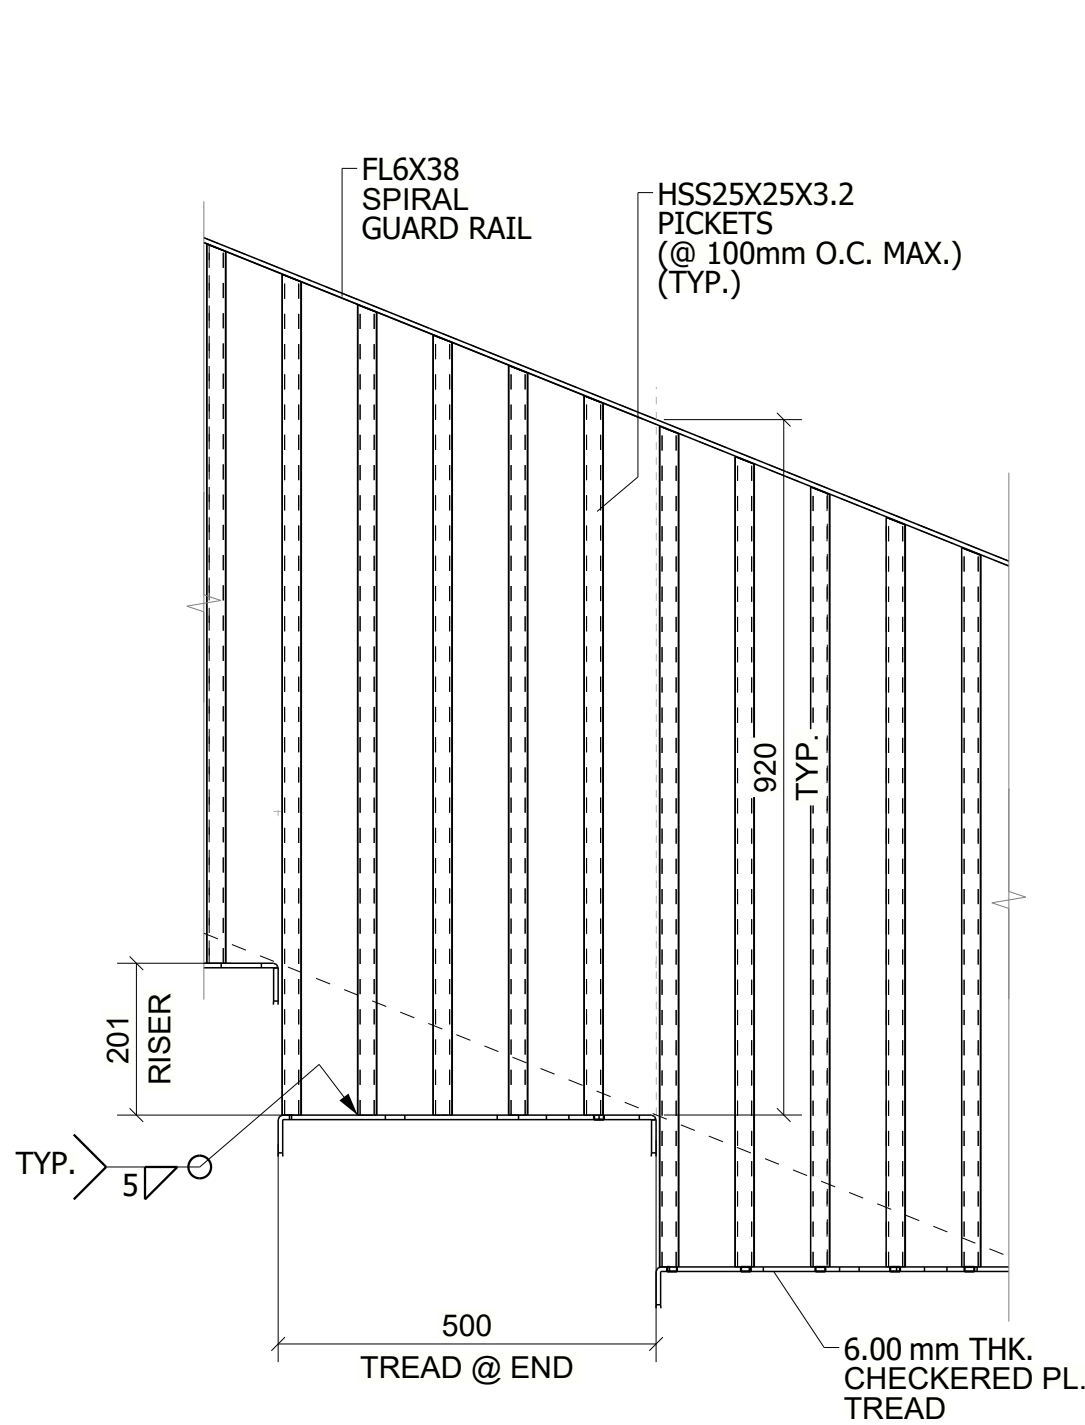


SECTION AA - AA

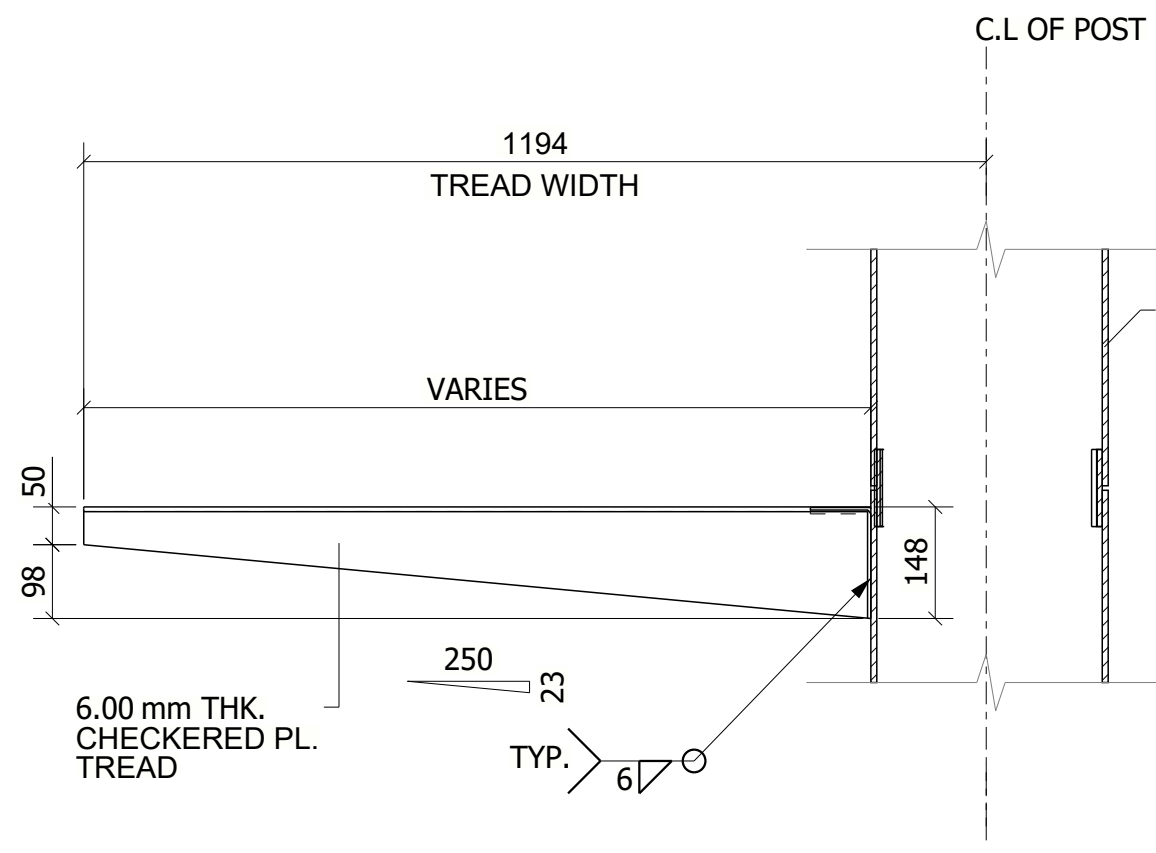


SECTION BB - BB

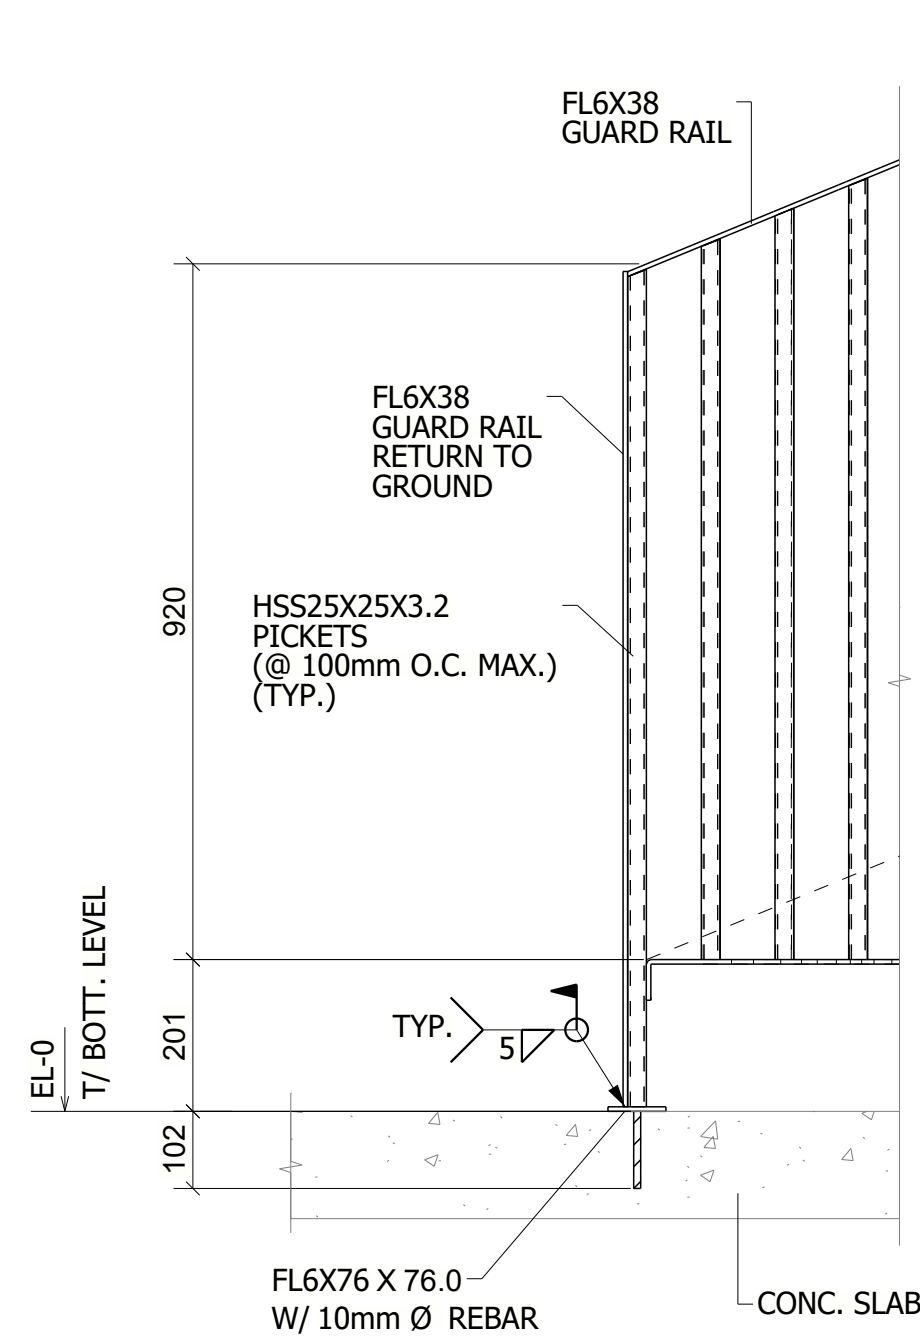


SECTION 1 - 1
ME101

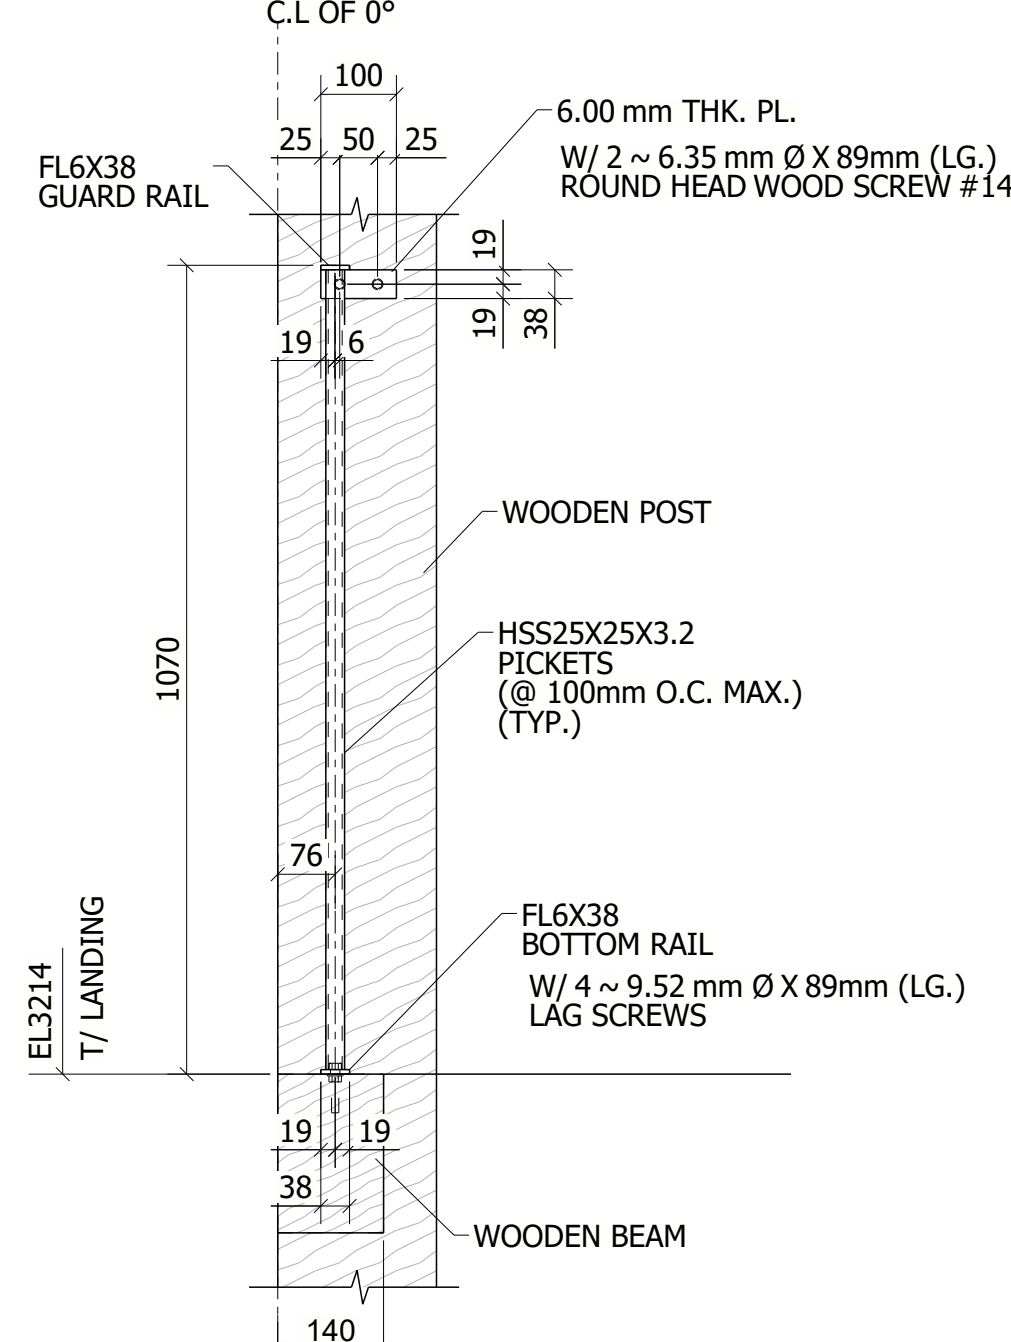


SECTION 2 - 2
ME102

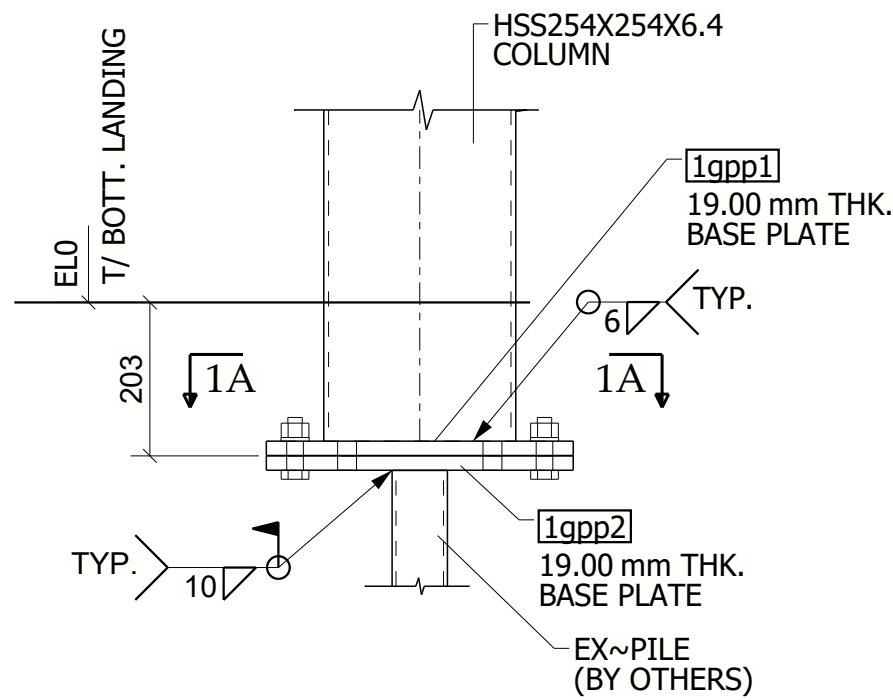


DETAIL-1
ME102

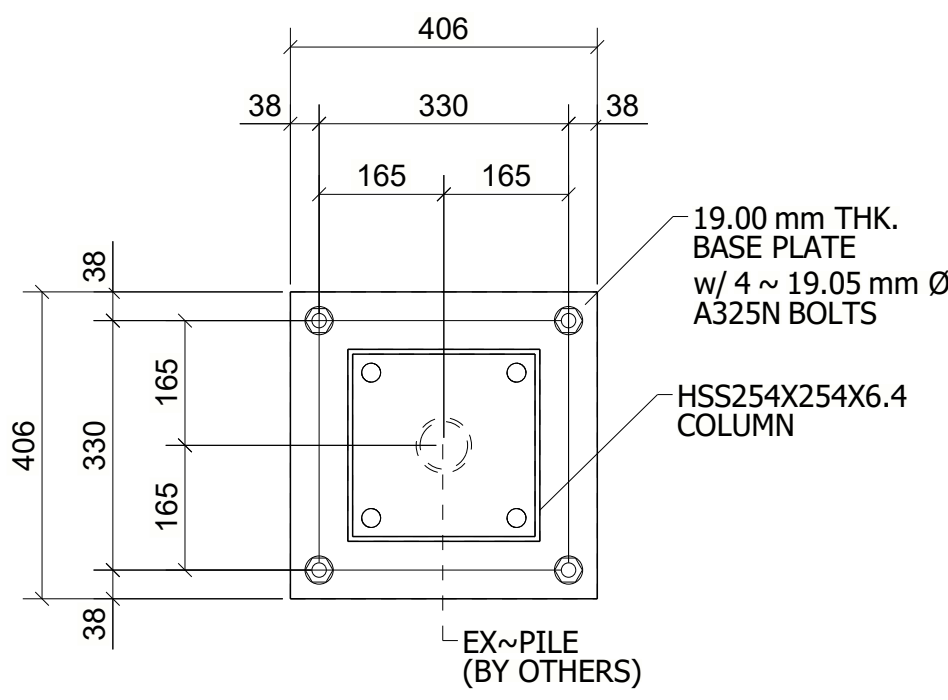


SECTION 1A - 1A

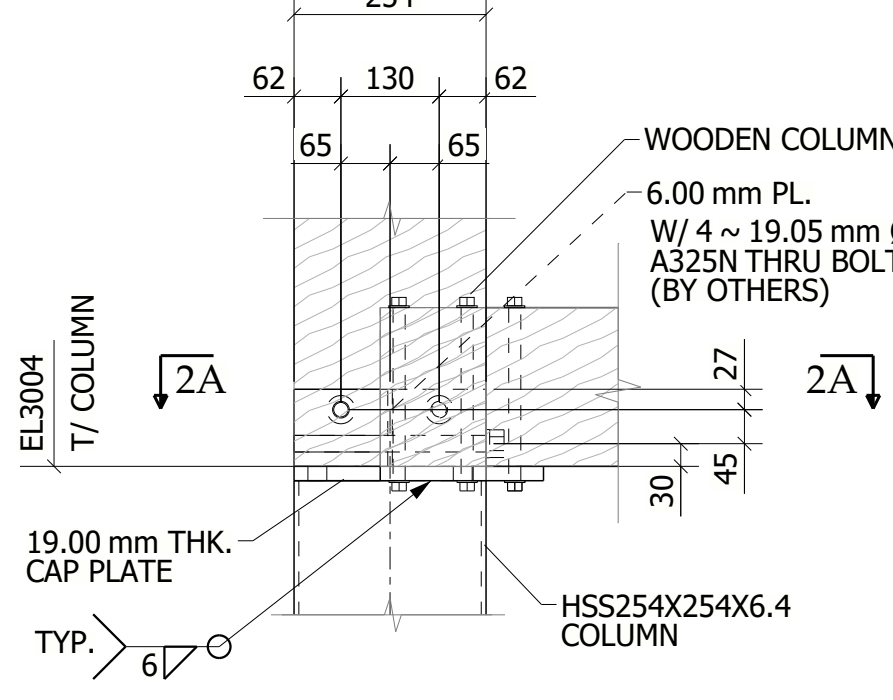


DETAIL-2
ME102

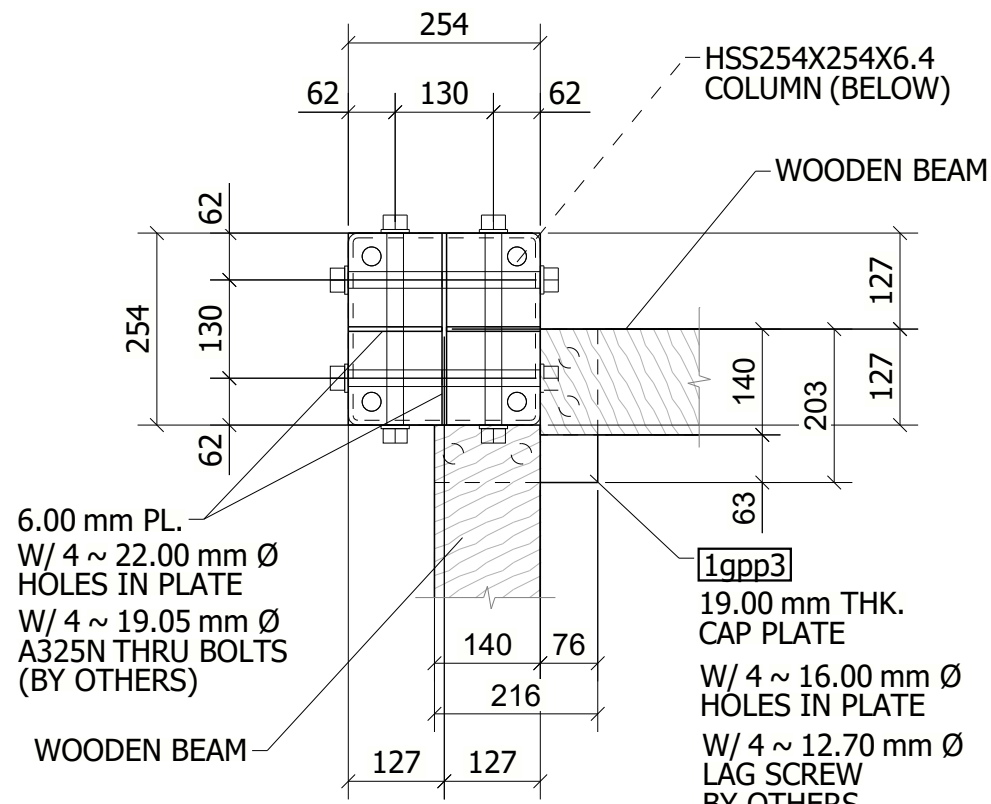


SECTION 2A - 2A

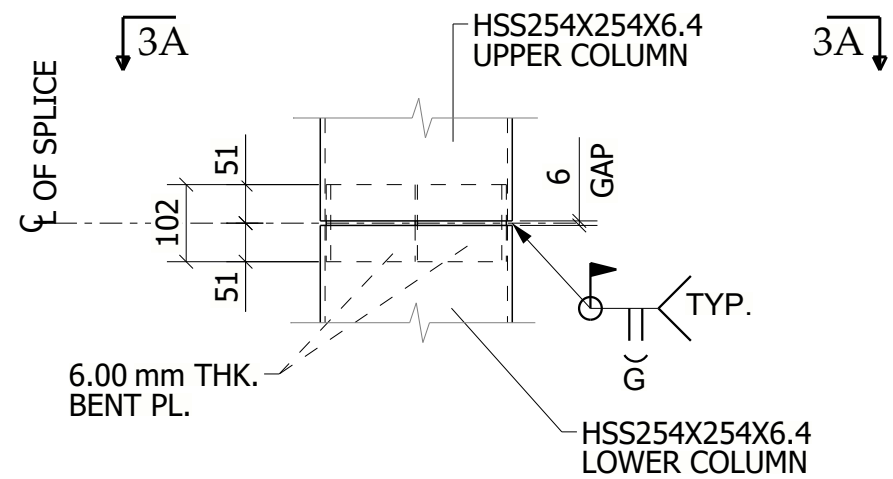

DETAIL-3
ME102

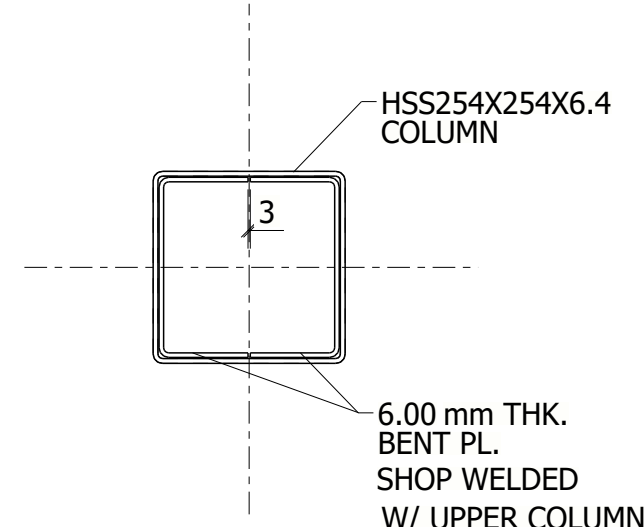


SECTION 3A - 3A

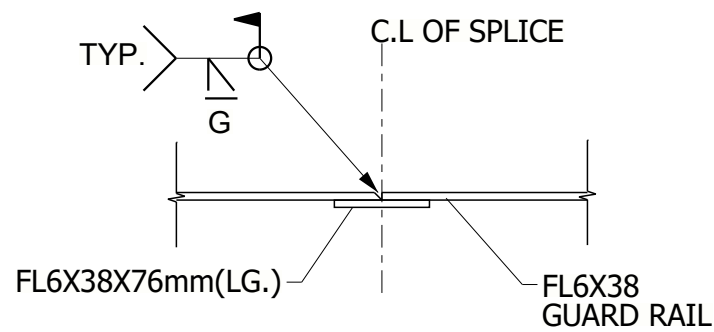


TYPICAL RAIL SPLICE DETAIL

NOTES :-


1. REFER SHEET ME100 FOR 3D -VIEW.
2. REFER SHEET ME101 FOR FRAMING PLAN.
3. REFER SHEET ME102 FOR ELEVATION.

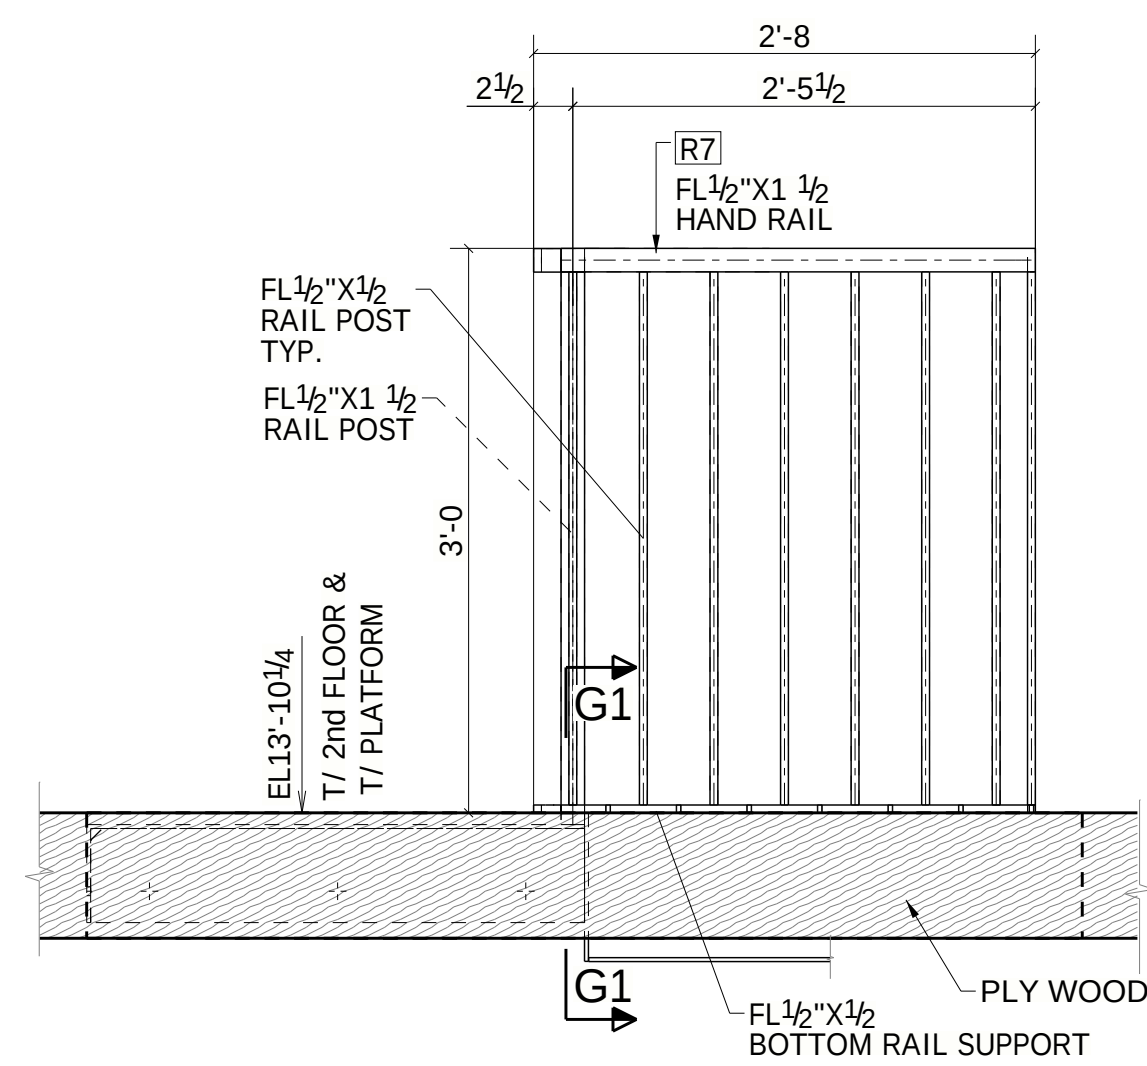


SECTION G - G
ME1

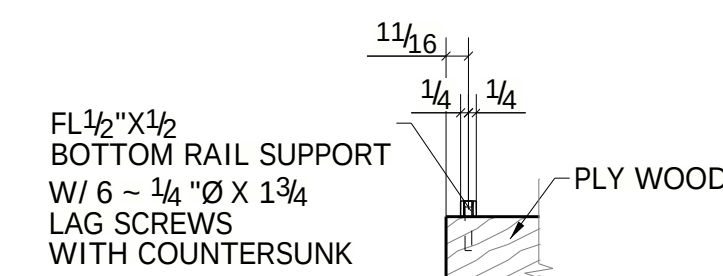


SECTION G1 - G1

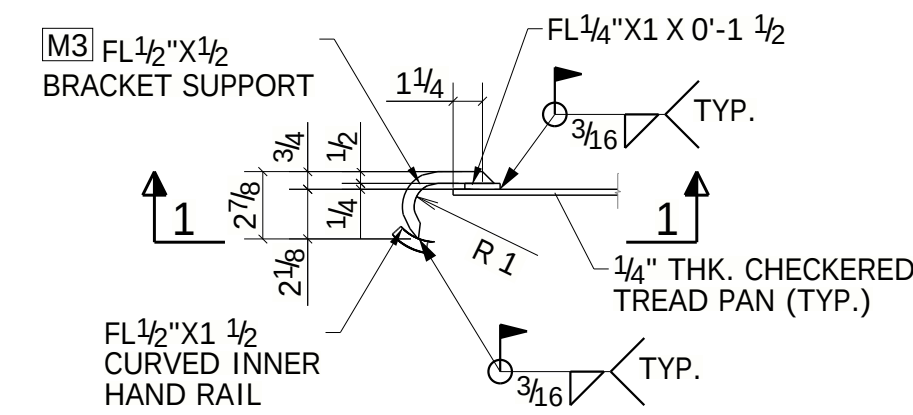


TYPICAL INNER HAND RAIL TO TREAD PAN
CONNECTION DETAIL

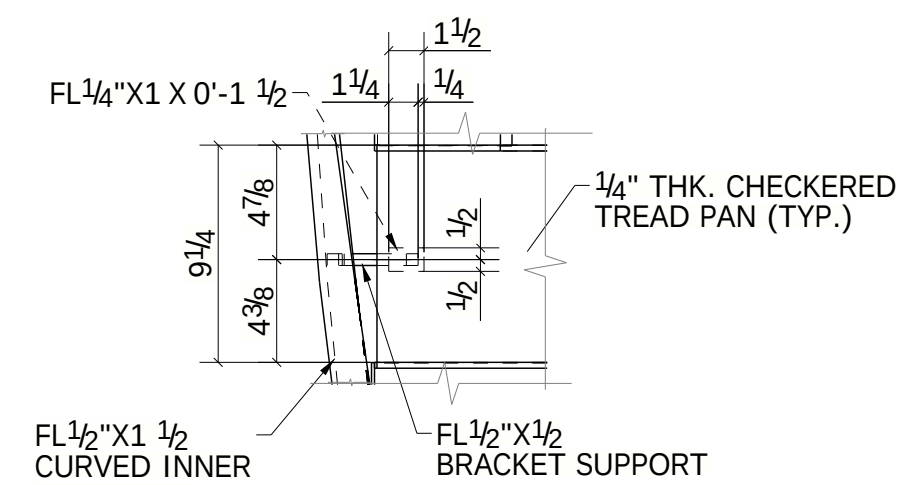


SECTION 1 - 1

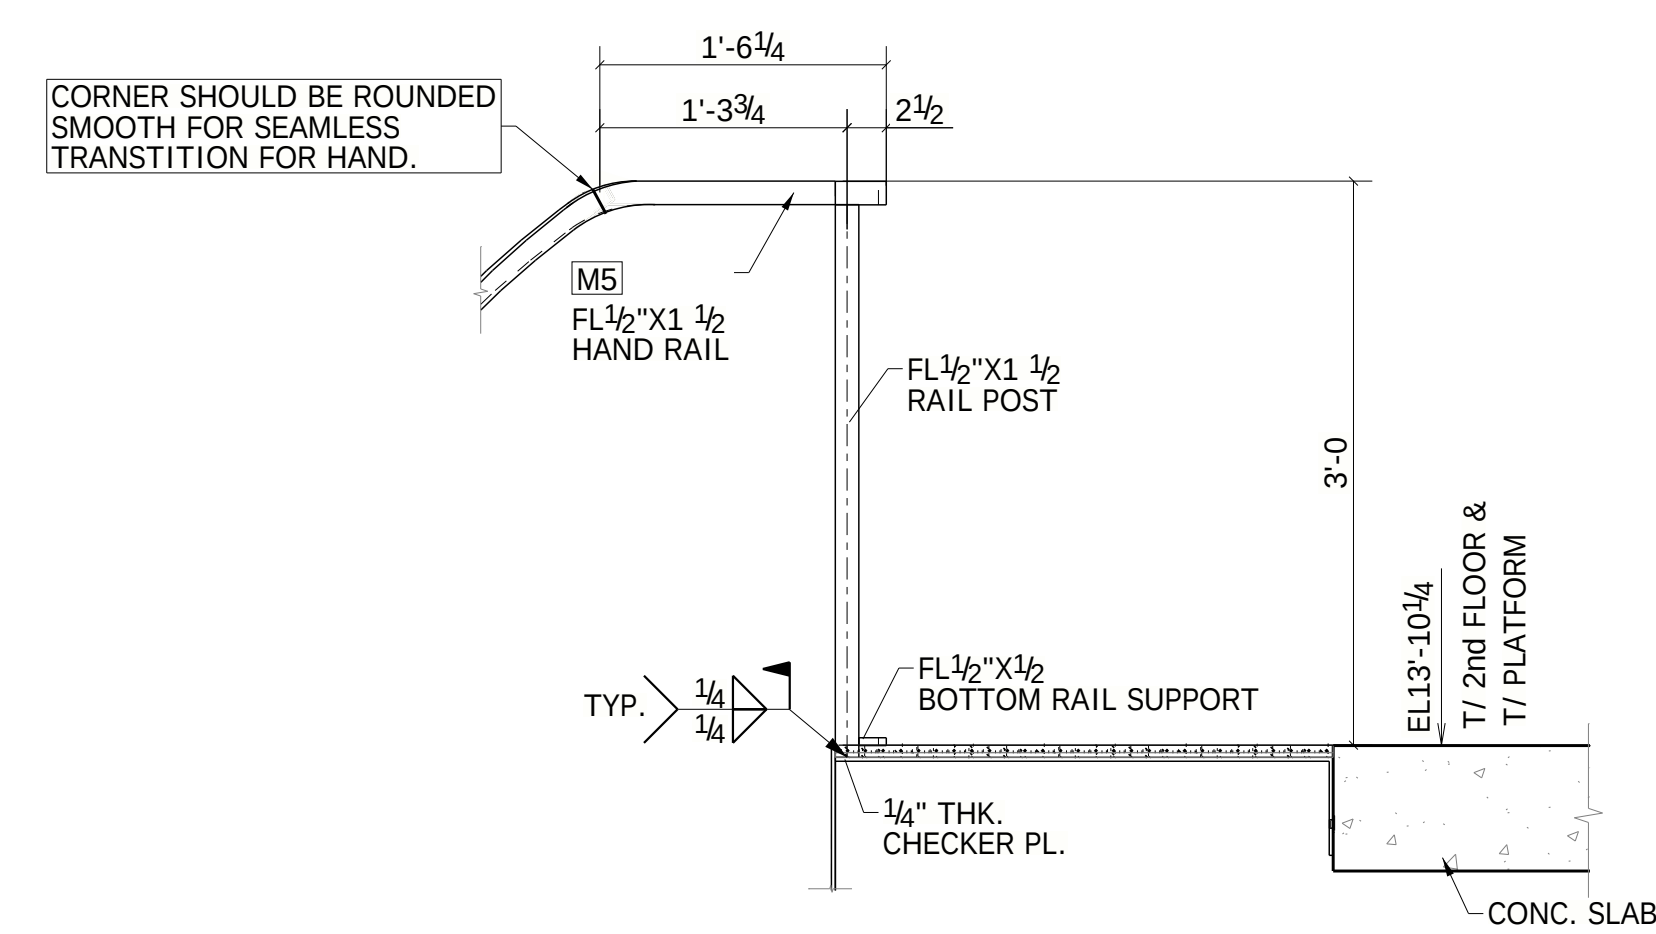


SECTION F - F
ME1

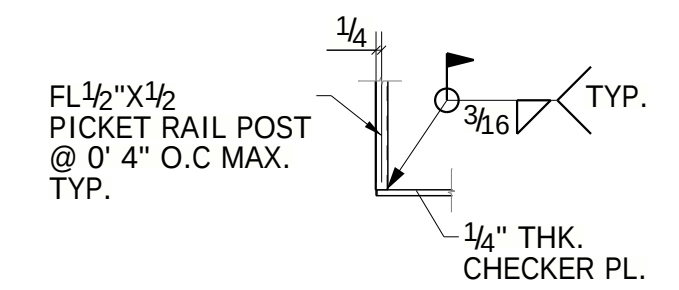


SECTION 2 - 2

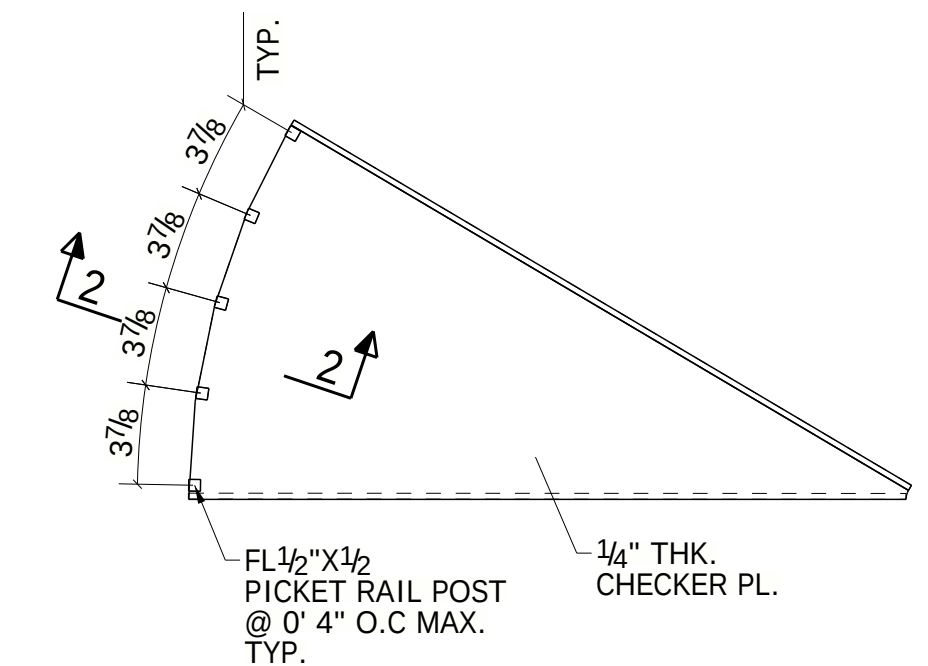


TYPICAL CHECKERED PLATE TO PICKET RAIL POST
CONNECTION DETAILS

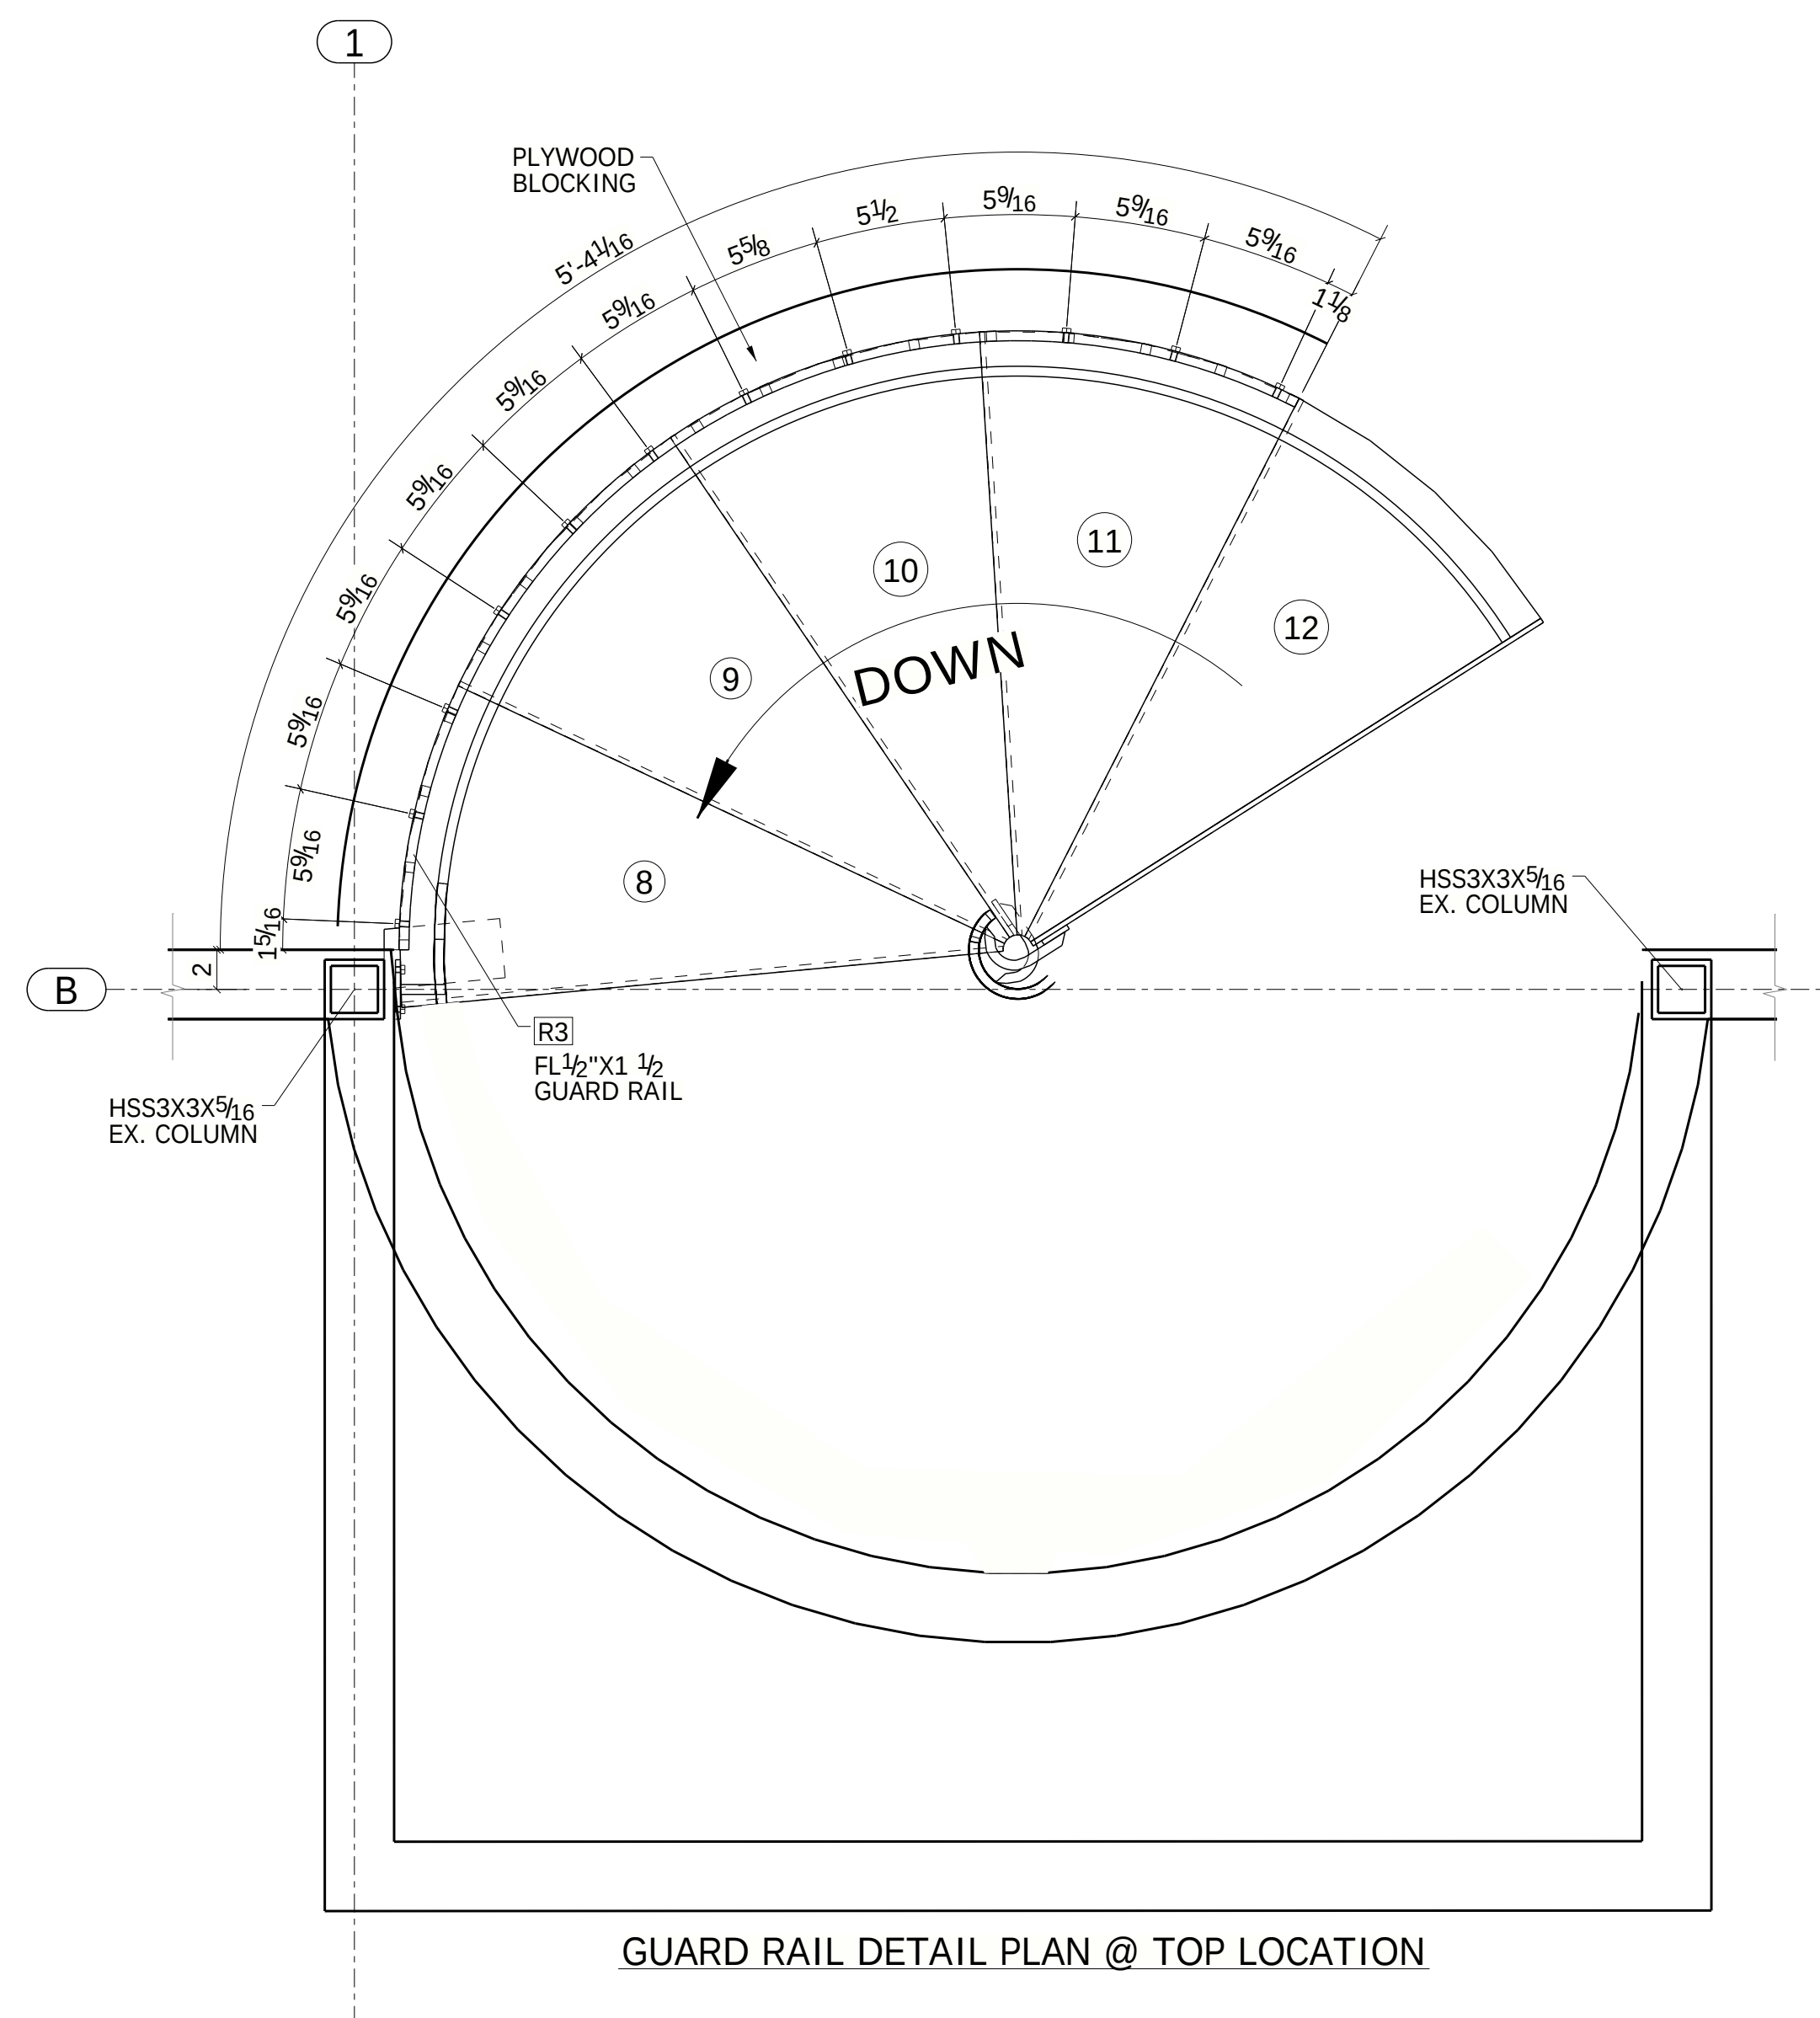


GUARD RAIL DETAIL PLAN @ TOP LOCATION

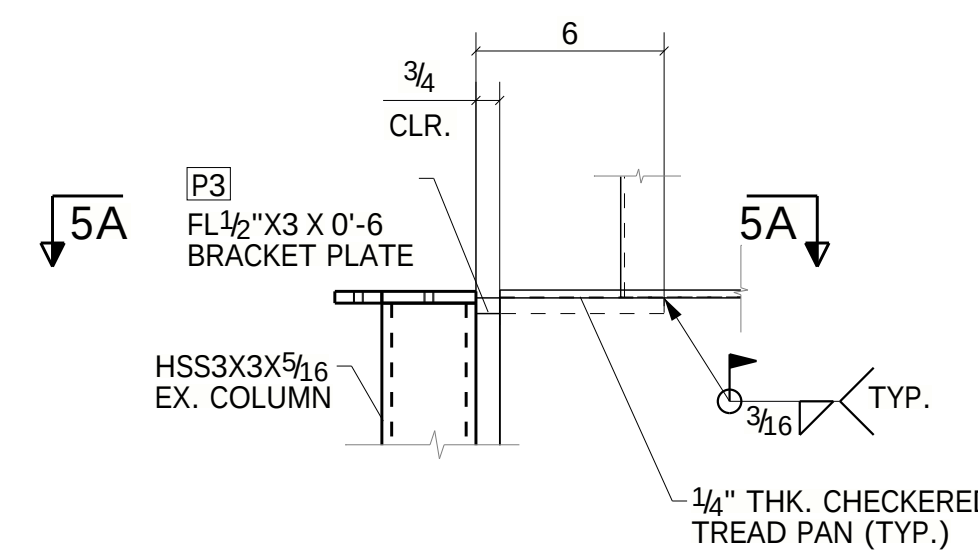




DETAIL 5
ME2

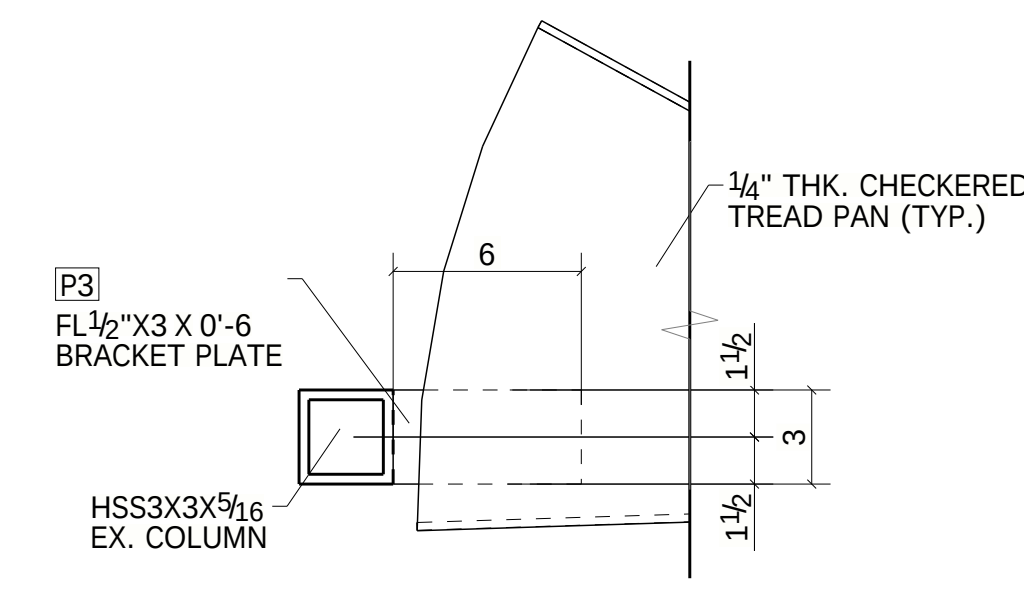

SECTION 5A - 5A

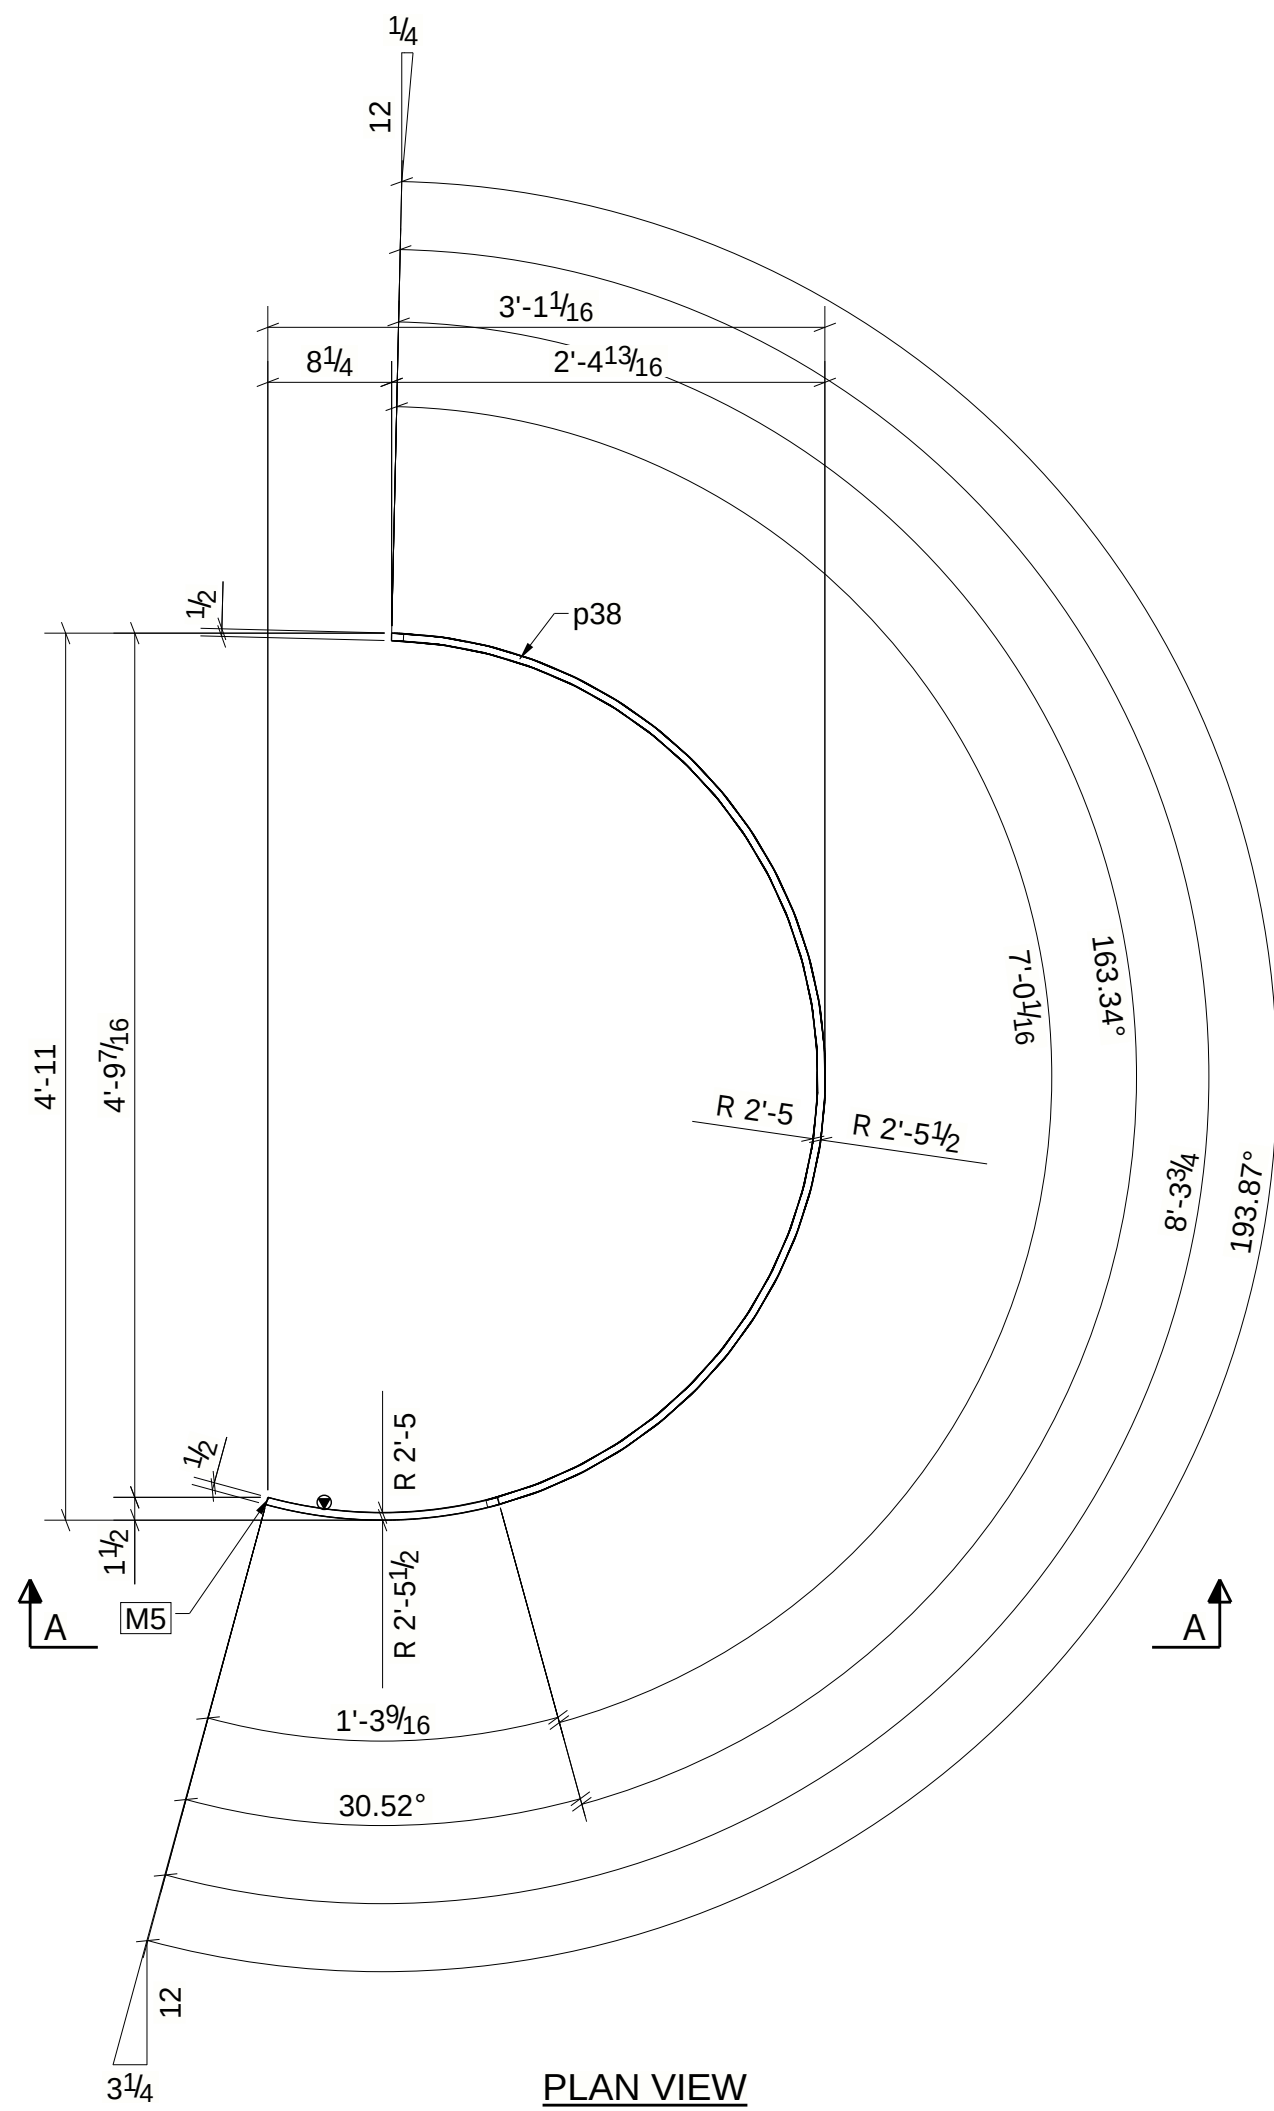


PLAN VIEW

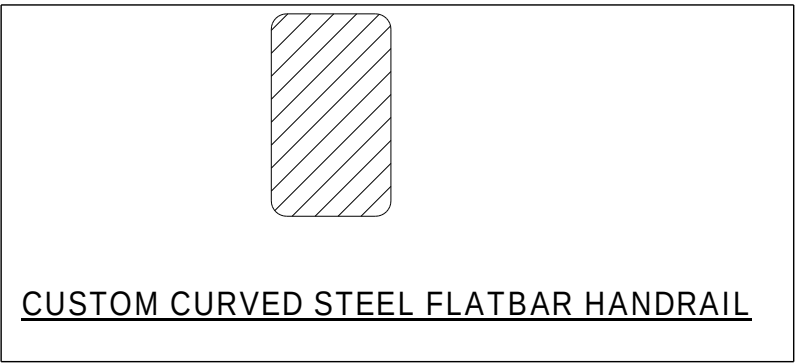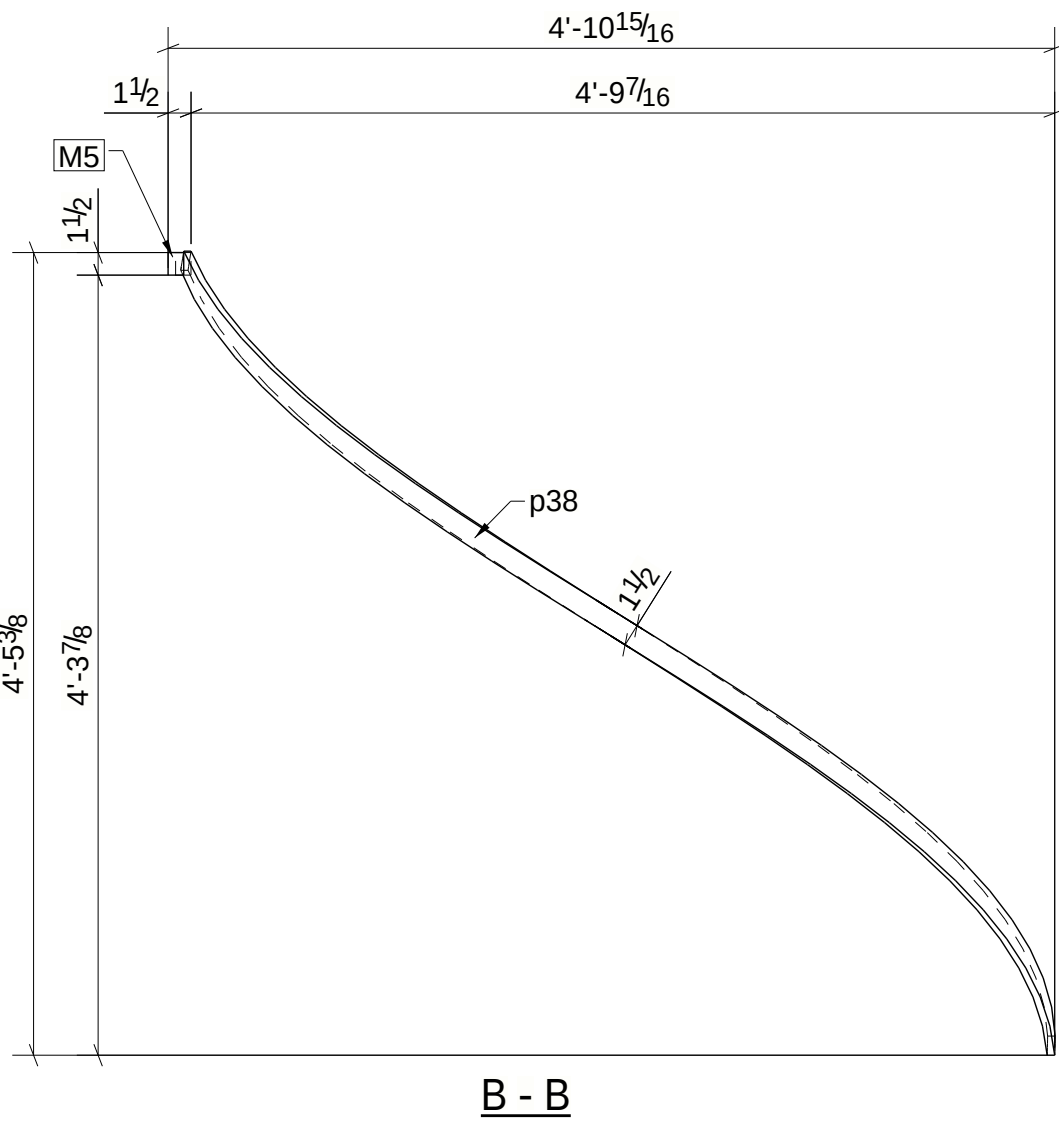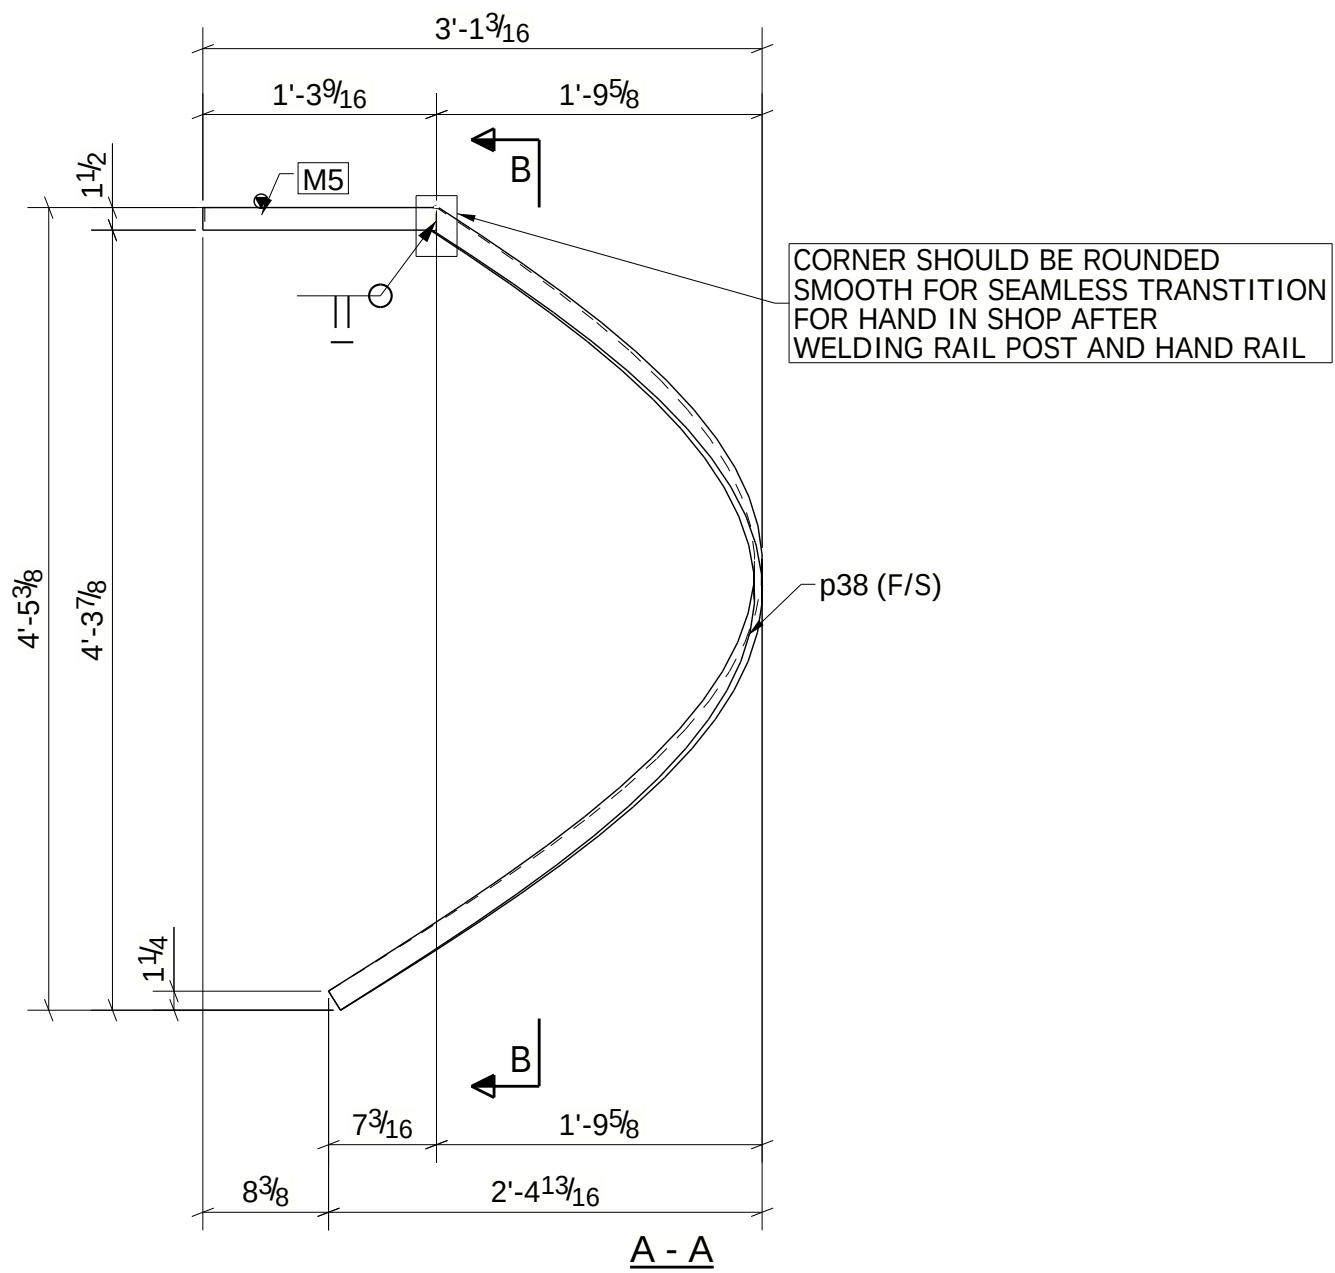

ONE - PLATE - M5


BILL OF MATERIAL					
MARK	QTY	DESCRIPTION	LENGTH	WEIGHT	REMARKS
M5	1	PLATE			SQ-2
M5	1	FL1/2"X1 1/2"	1'-3 9/16"	3	300W
p38	1	FL1/2"X1 1/2"	8'-2 3/8"	21	300W
		TOTAL WEIGHT THIS DRAWING		24	

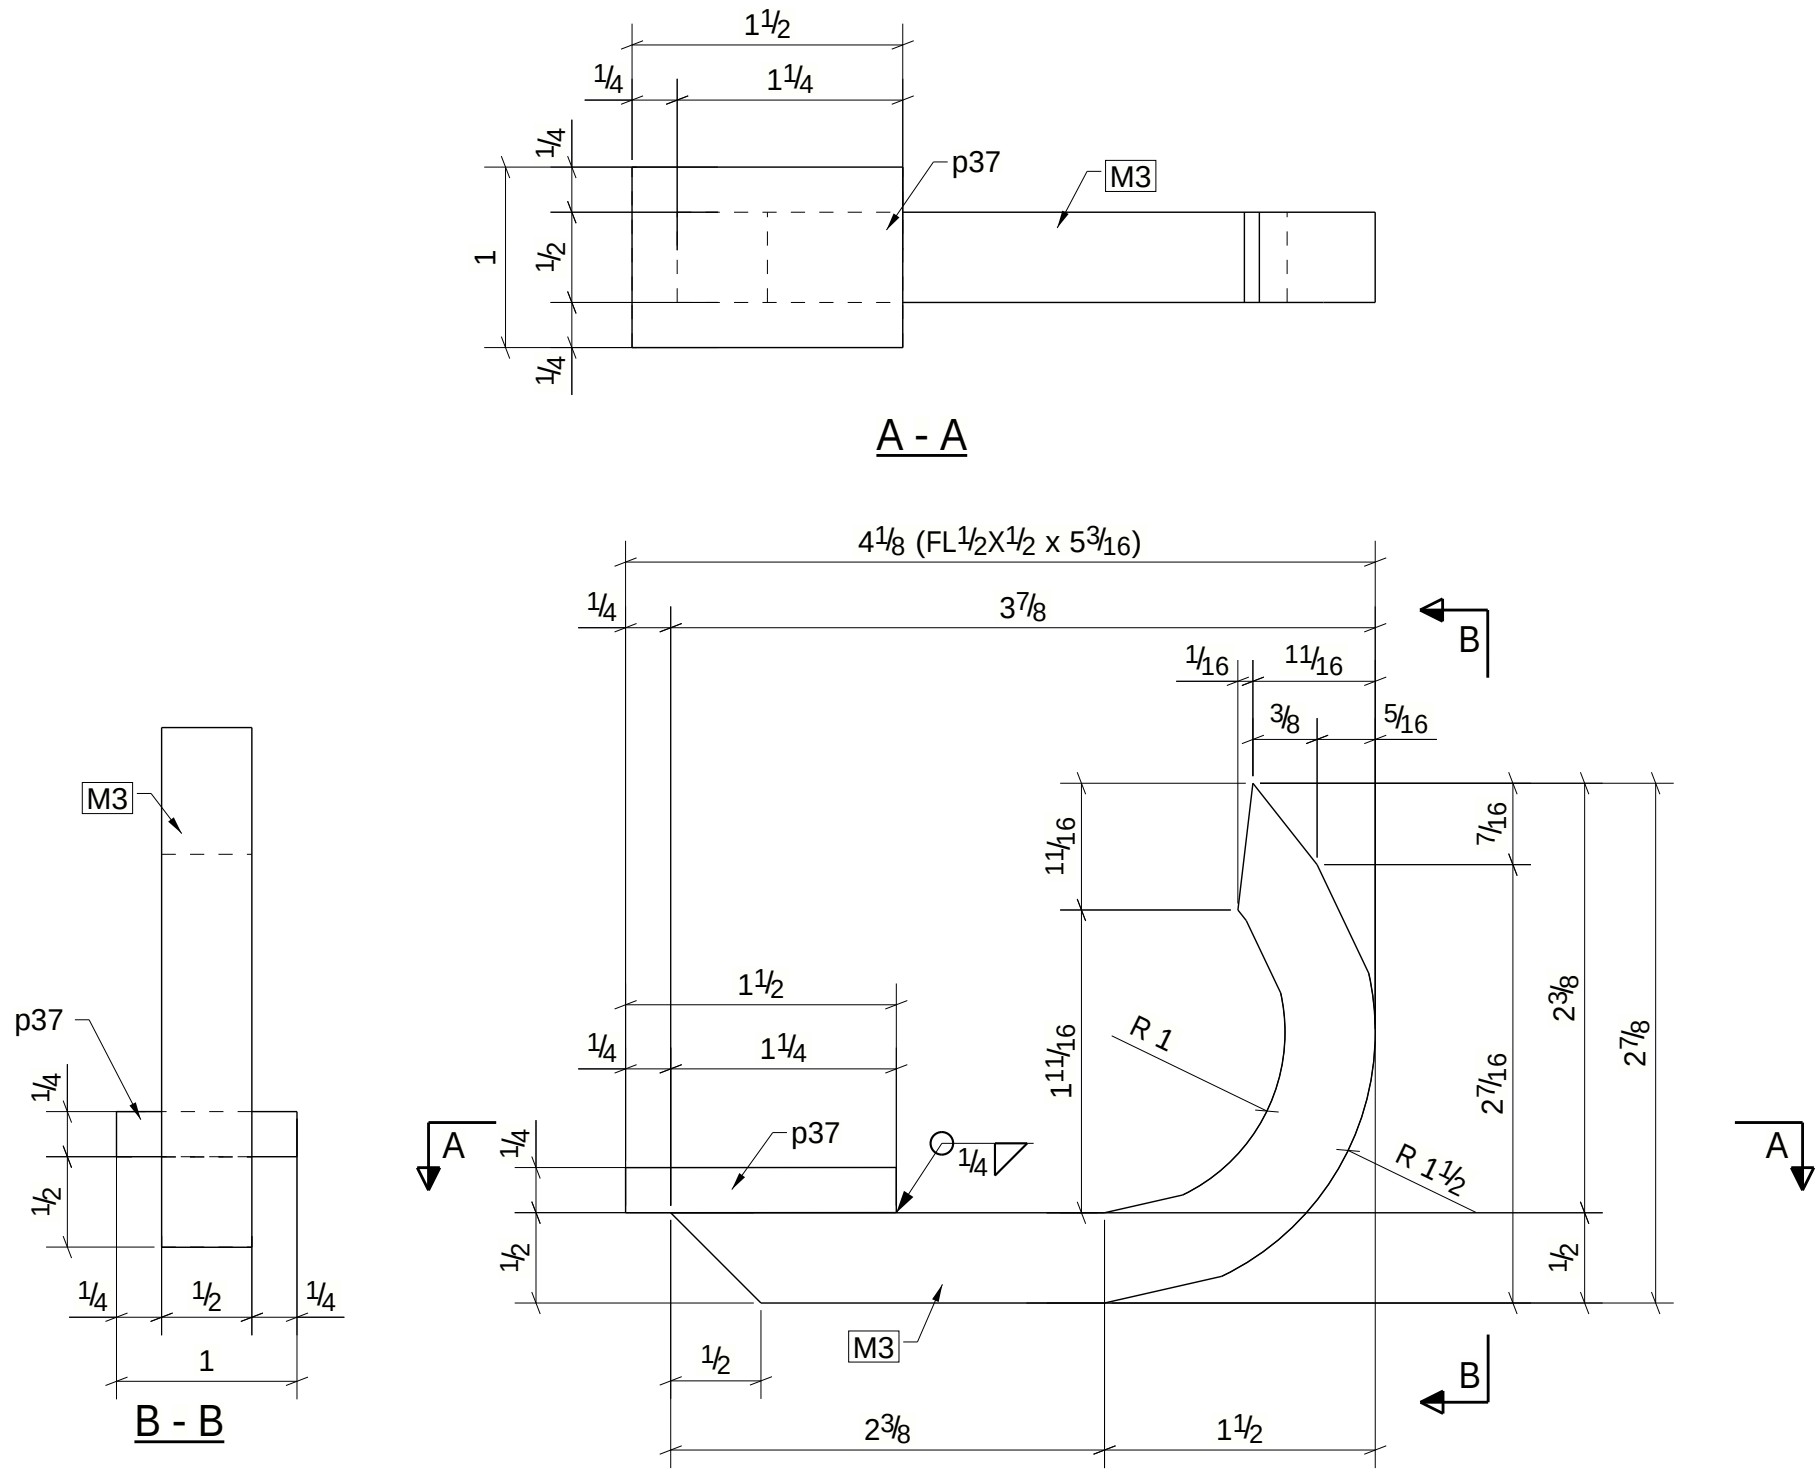

5 - BARS - M3




BILL OF MATERIAL

MARK	QTY	DESCRIPTION	LENGTH	WEIGHT	REMARKS
M3	5	BARS			SQ-2
M3	5	FL $1\frac{1}{2} \times 1\frac{1}{2}$ "	0'-5 $\frac{3}{16}$ "	2	300W
p37	5	FL $1\frac{1}{4} \times 1$ "	0'-1 $\frac{1}{2}$ "	1	300W
		TOTAL WEIGHT THIS DRAWING		2	

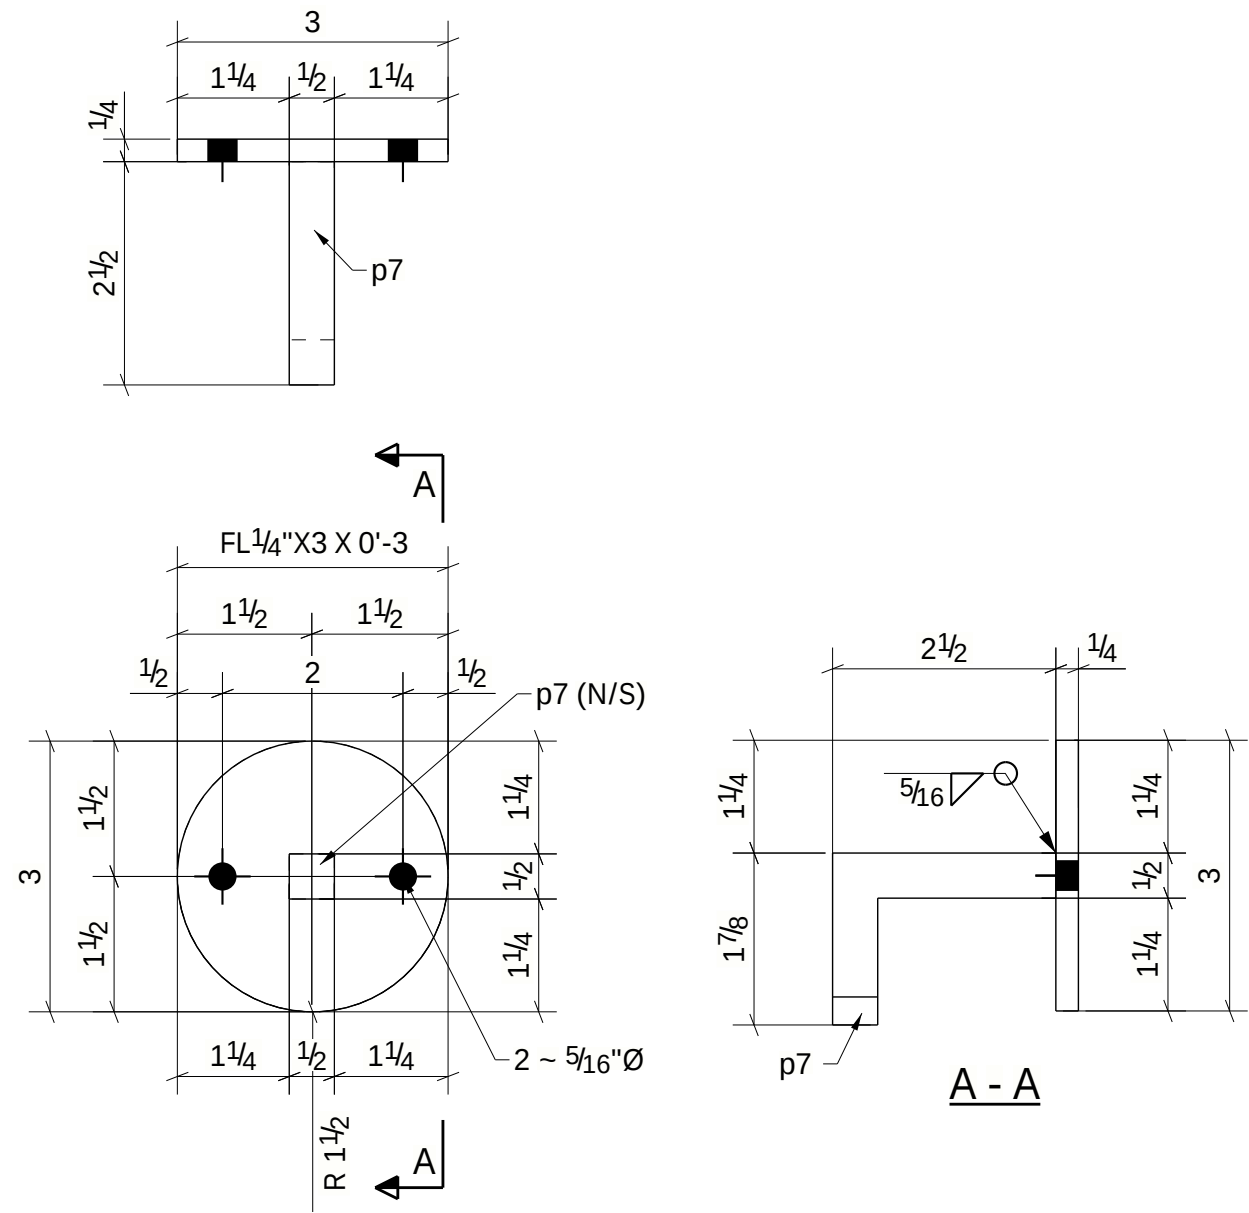

ONE - BRACKET - M6

BILL OF MATERIAL					
MARK	QTY	DESCRIPTION	LENGTH	WEIGHT	REMARKS
M6	1	BRACKET			SQ-2
M6	1	FL1/4"X3"	0'-3"	0	300W
p7	1	FL1/2"X1/2"	0'-3 7/8"	0	300W
		TOTAL WEIGHT THIS DRAWING		1	

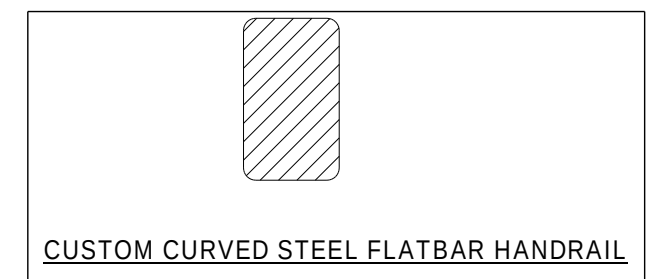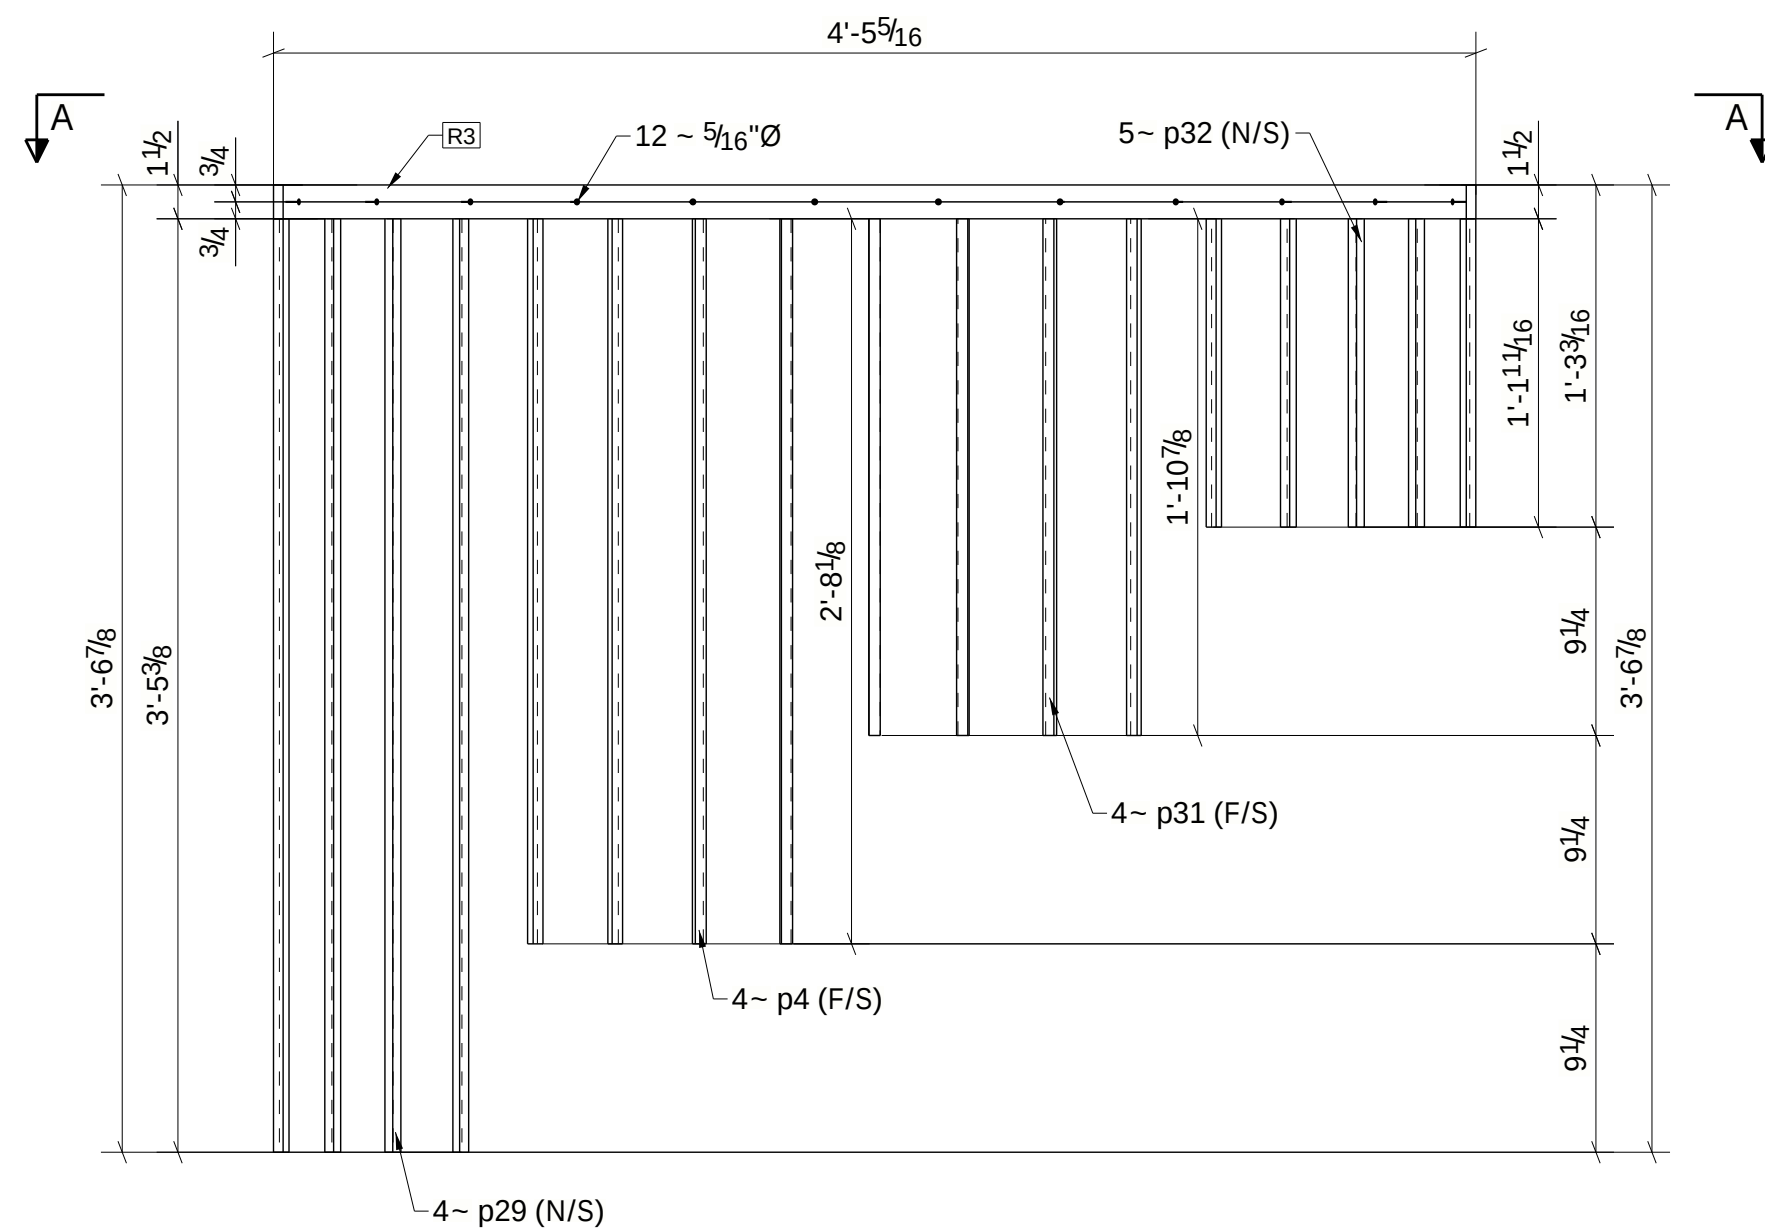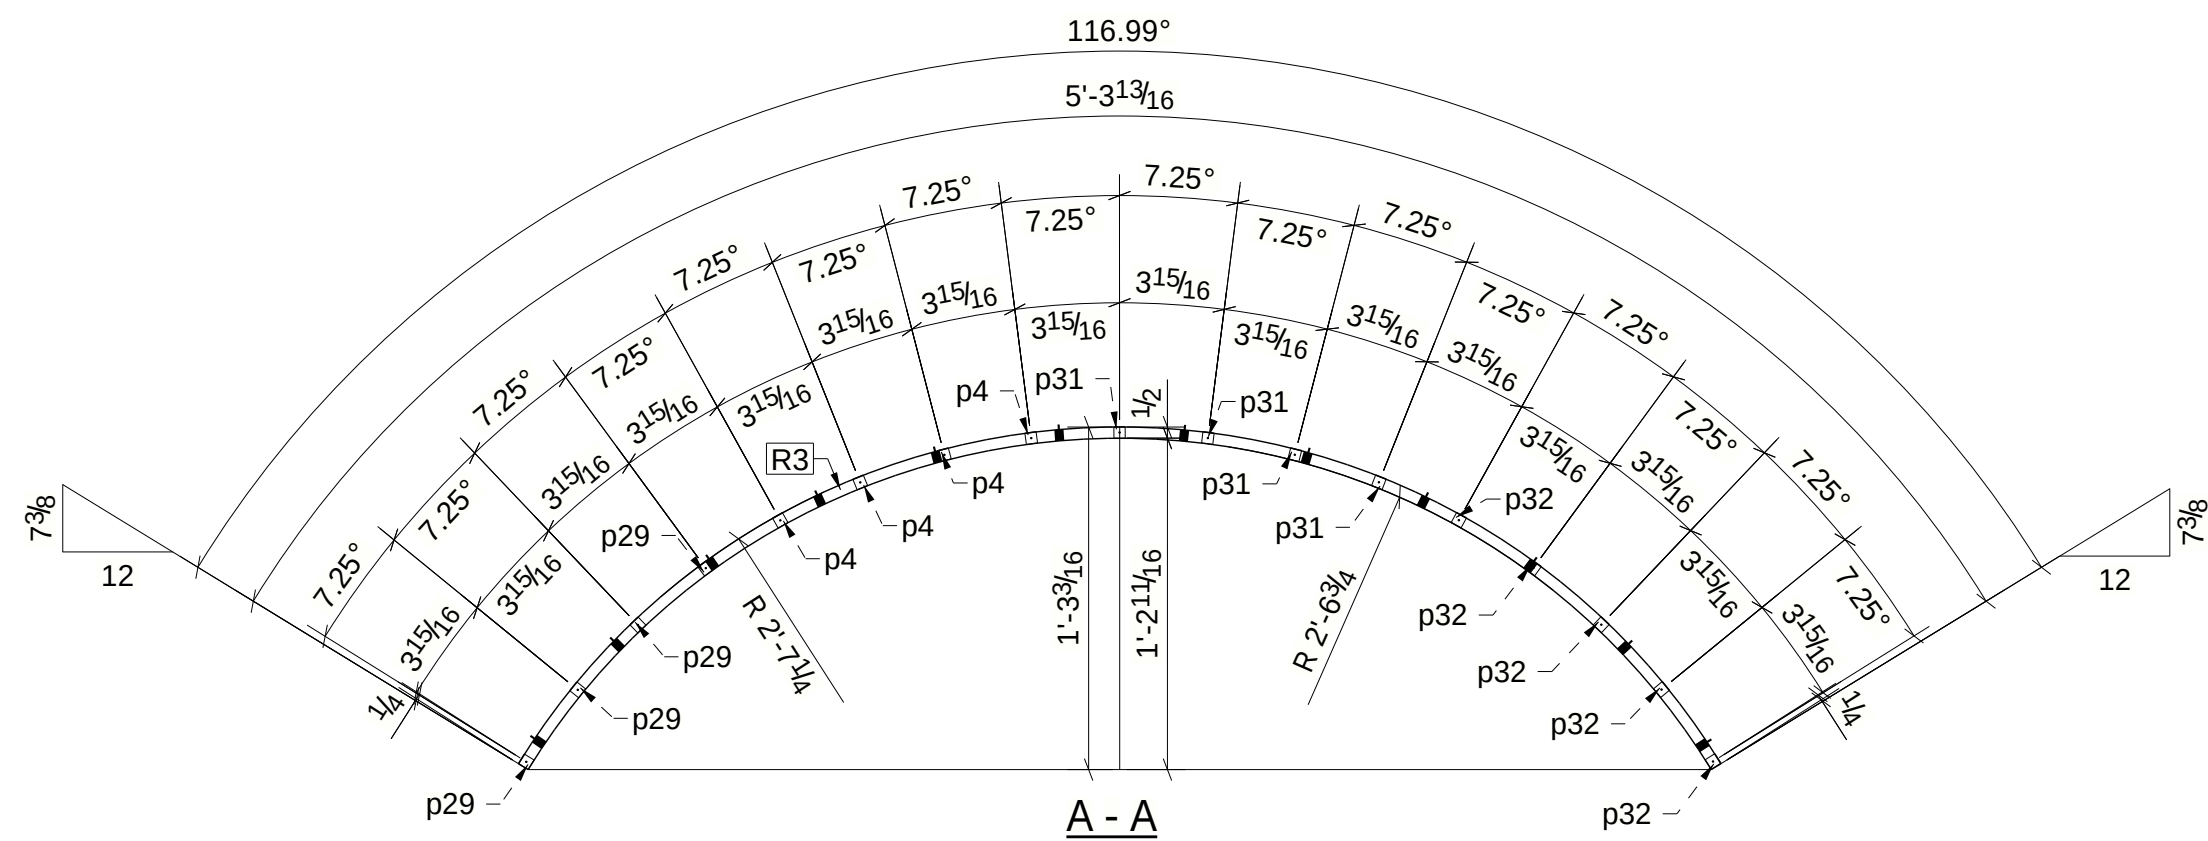

ONE - RAIL - R3

BILL OF MATERIAL

MARK	QTY	DESCRIPTION	LENGTH	WEIGHT	REMARKS
R3	1	RAIL			SQ-2
R3	1	FL1/2"X1 1/2"	5'-3 5/16"	13	300W
p4	4	FL1/2"X1/2"	2'-8 1/8"	9	300W
p29	4	FL1/2"X1/2"	3'-5 3/8"	12	300W
p31	4	FL1/2"X1/2"	1'-10 7/8"	6	300W
p32	5	FL1/2"X1/2"	1'-1 11/16"	5	300W
		TOTAL WEIGHT THIS DRAWING		46	

