






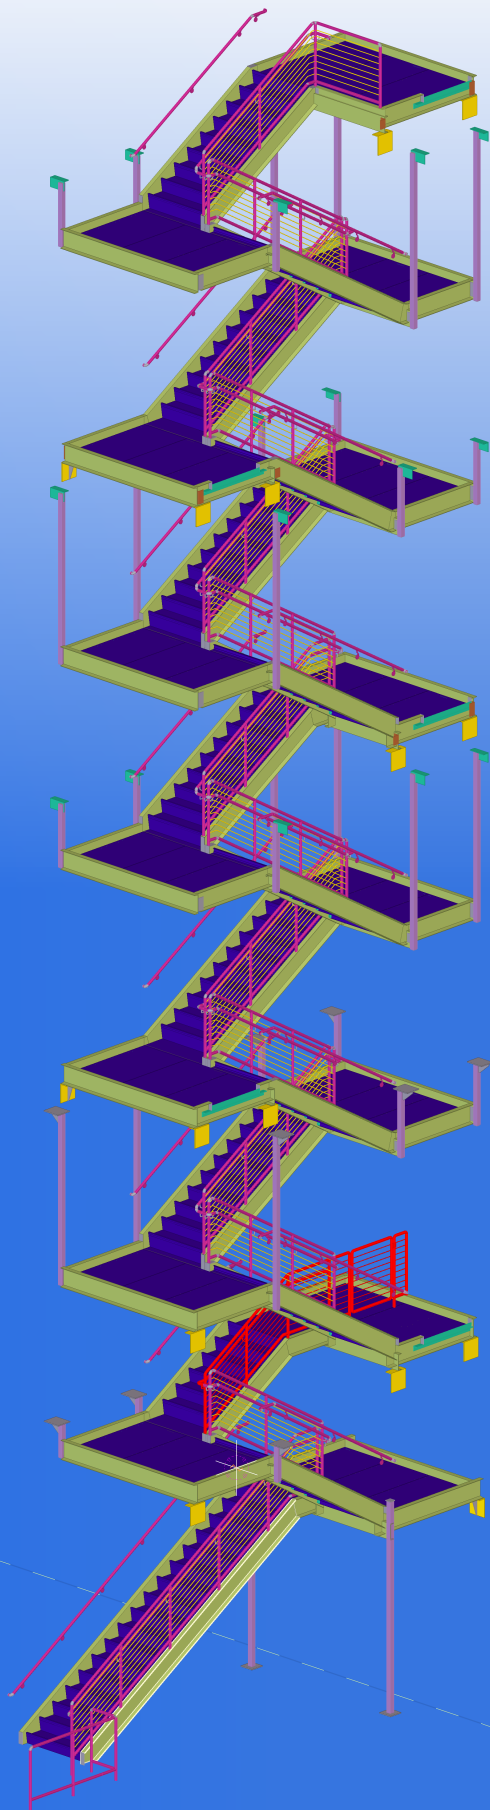

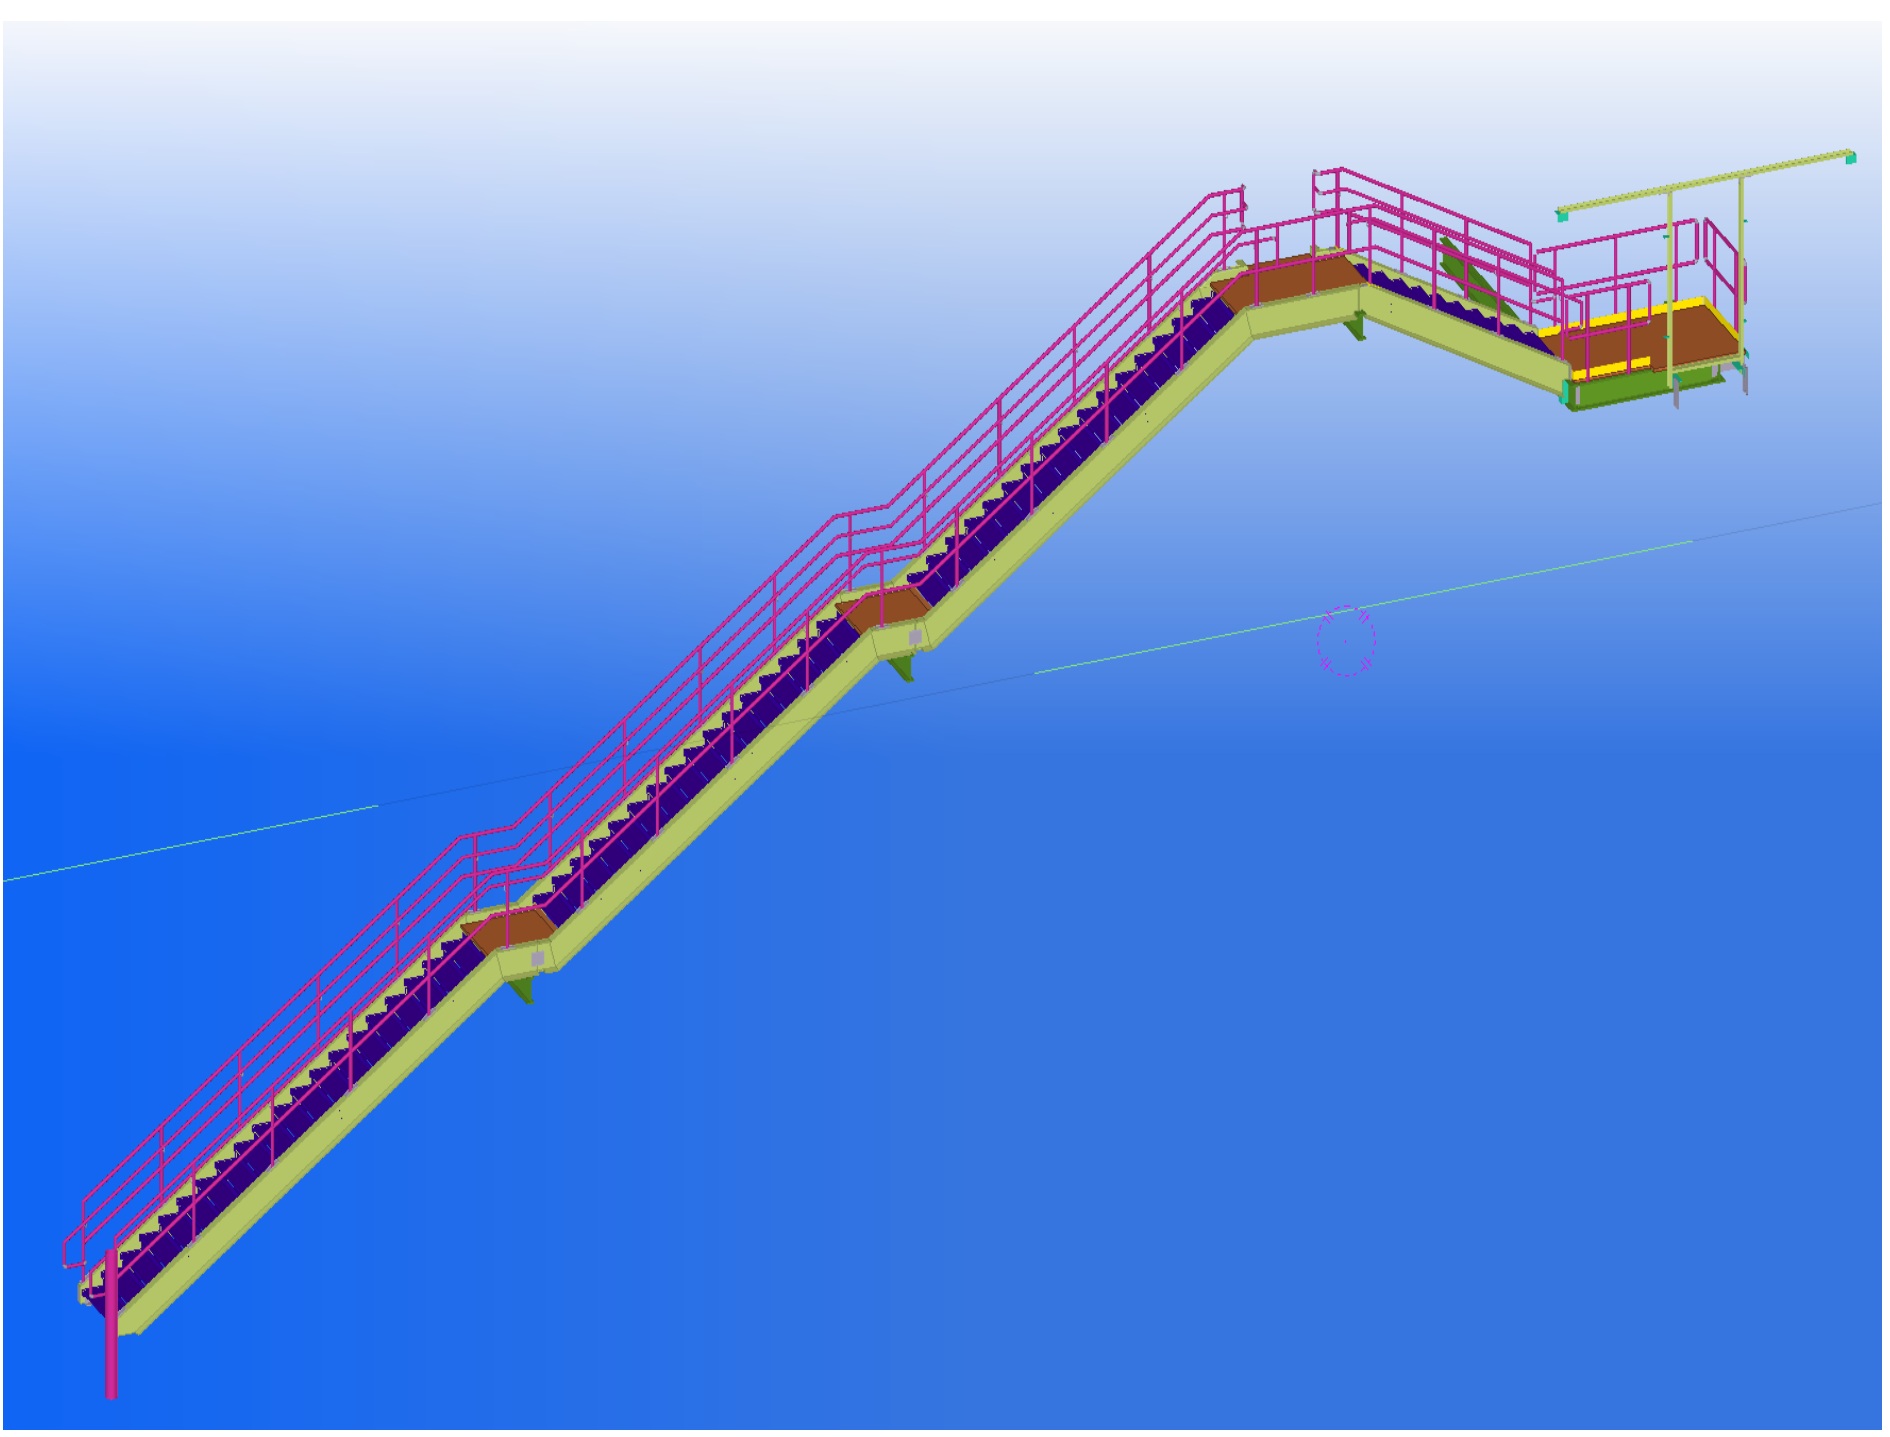

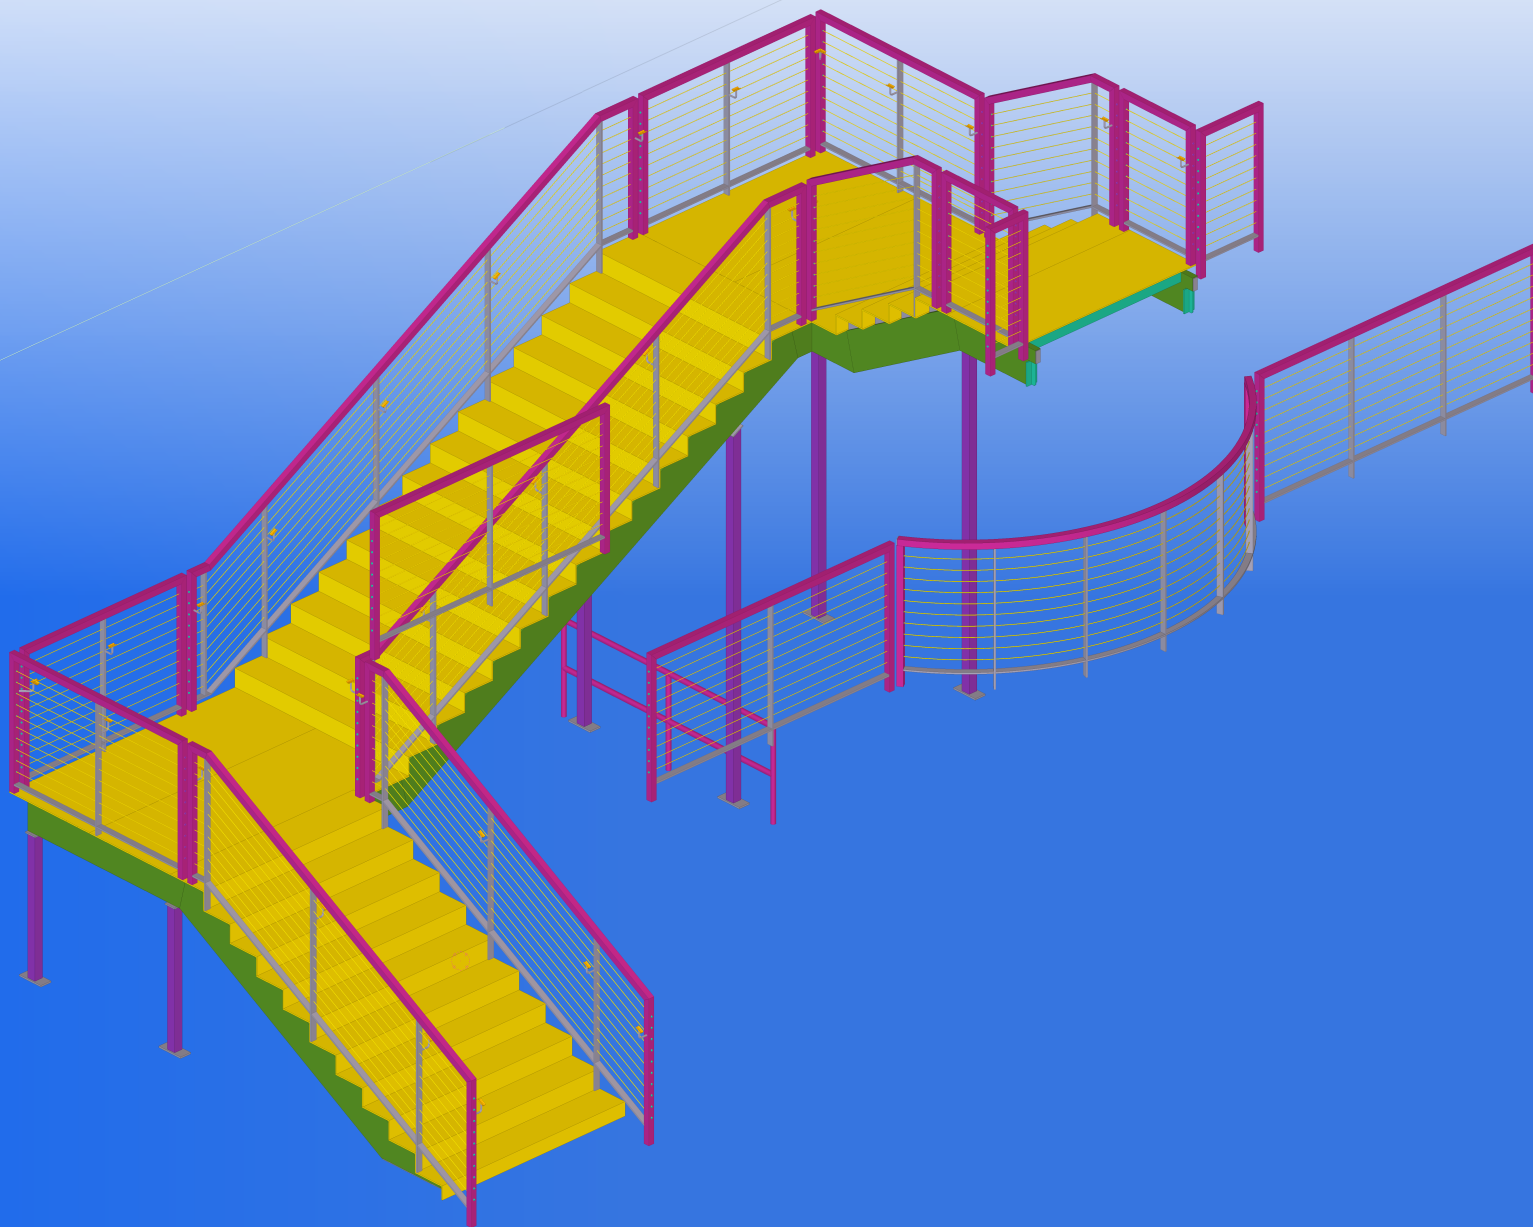

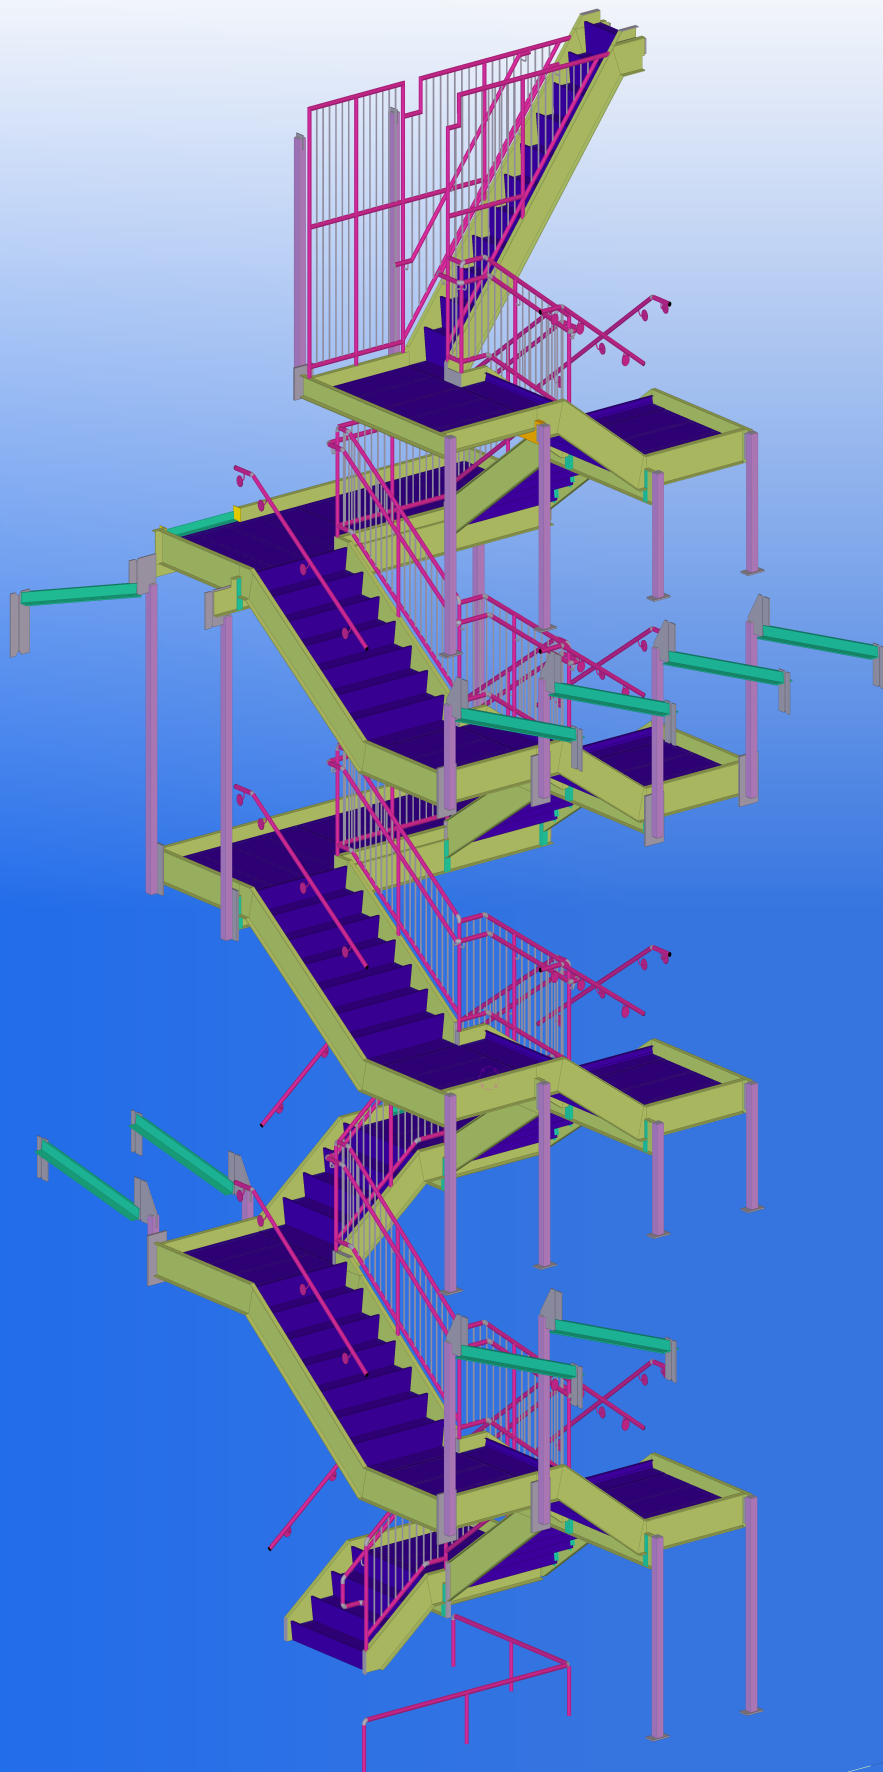

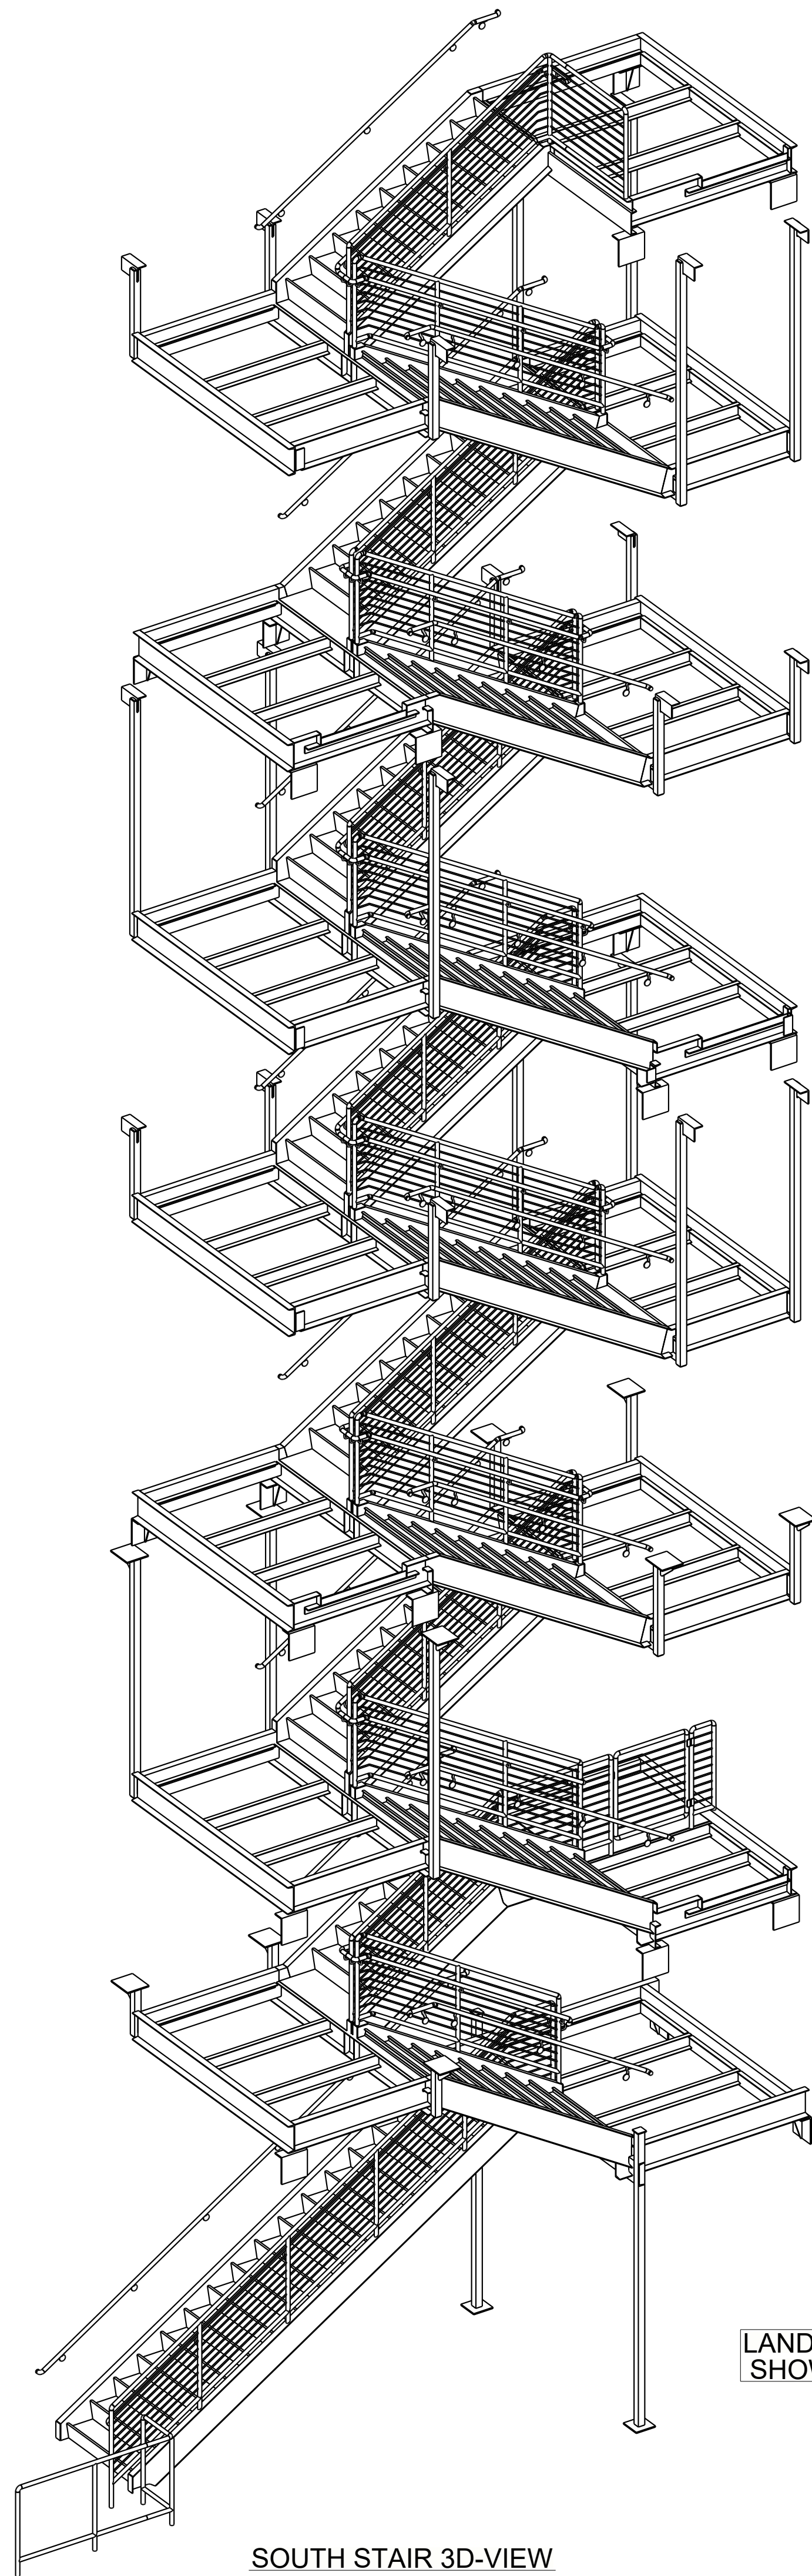

SOUTH STAIR 3D-VIEW



LANDING PLATES NOT
SHOWN FOR CLARITY

FINISH NOTE:

ALL SOUTH STAIR STEEL MEMBERS SHALL
RECEIVE ONE SHOP COAT STANDARD PRIMER.


SURFACE PREPARATION : SSPC-SP3

FOR FIELD USE : 02/26/2024

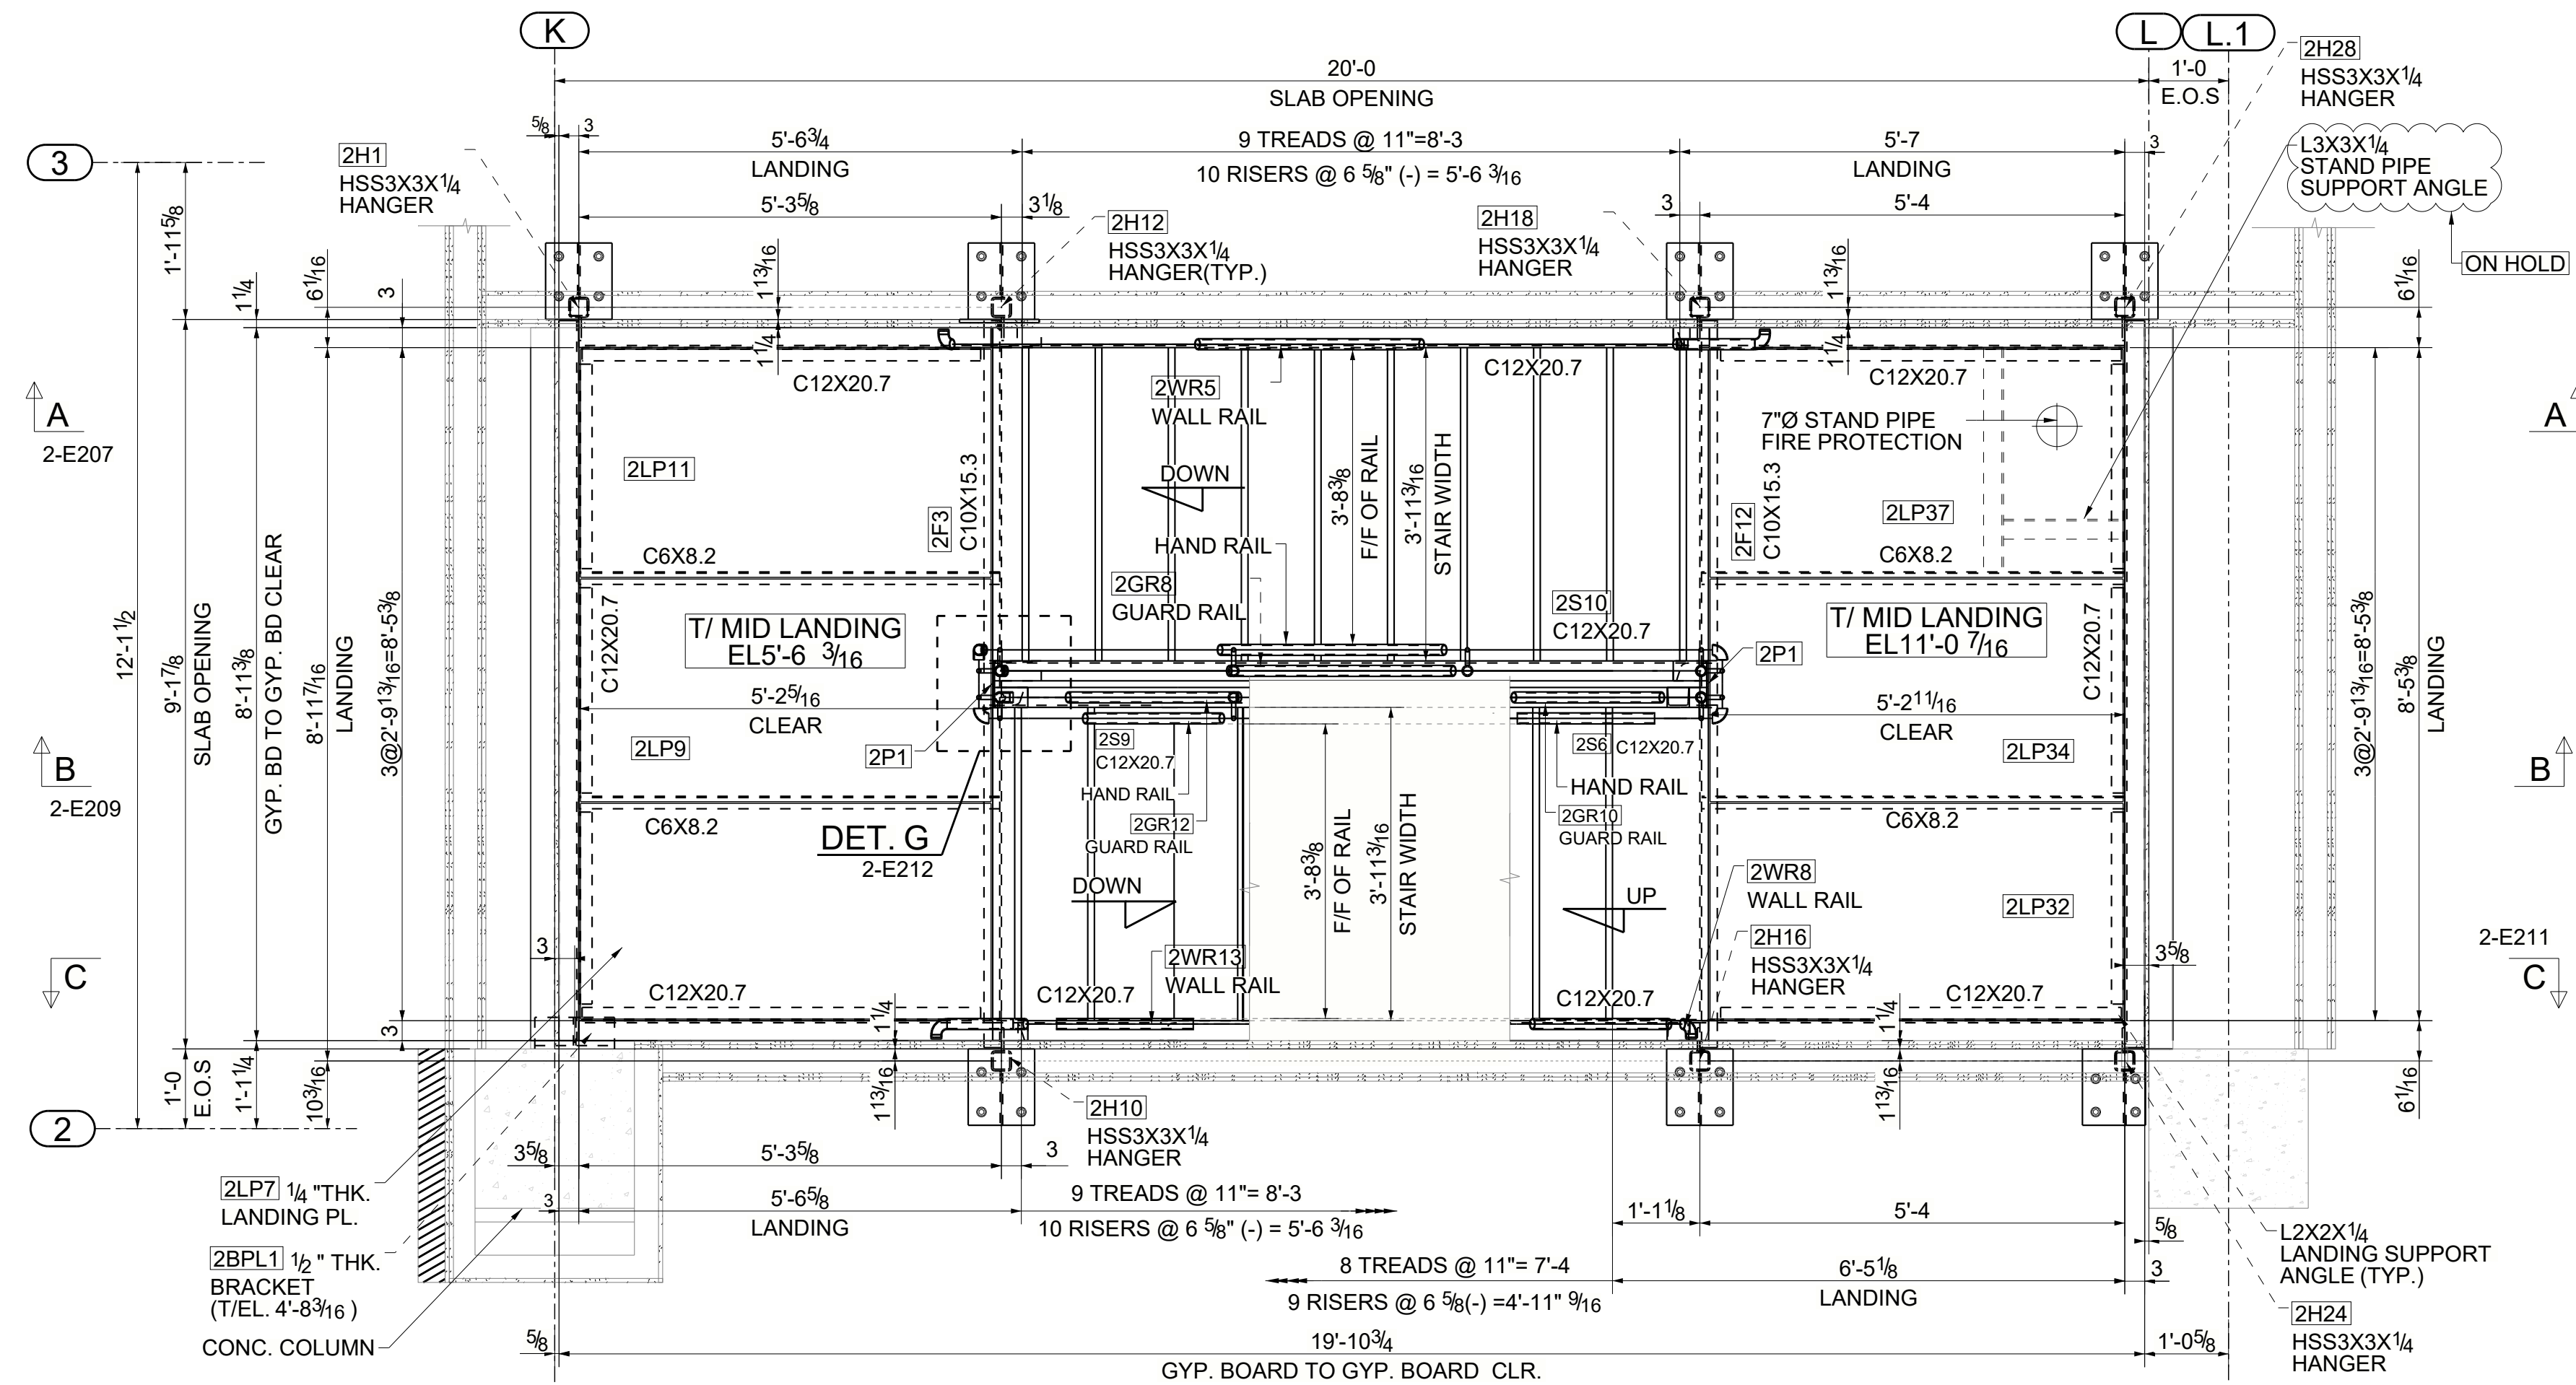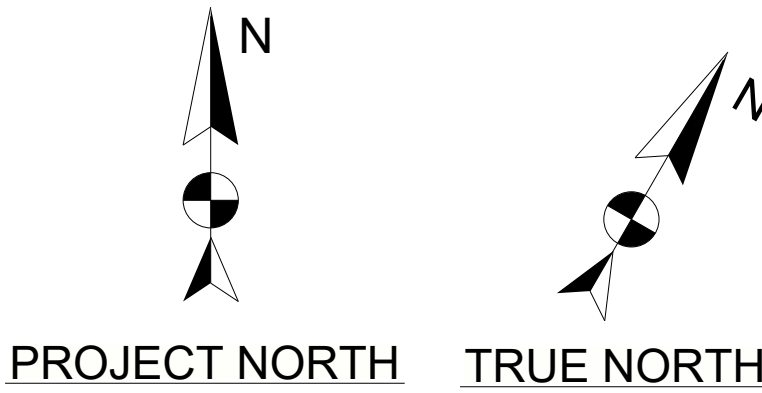

PARTIAL FRAMING PLAN OF SOUTH STAIR @ T/MID LANDING EL. 11'-0 7/16

(REFER : FIRST FLOOR PLAN-SOUTH STAIR 1/ A400& A-101A)

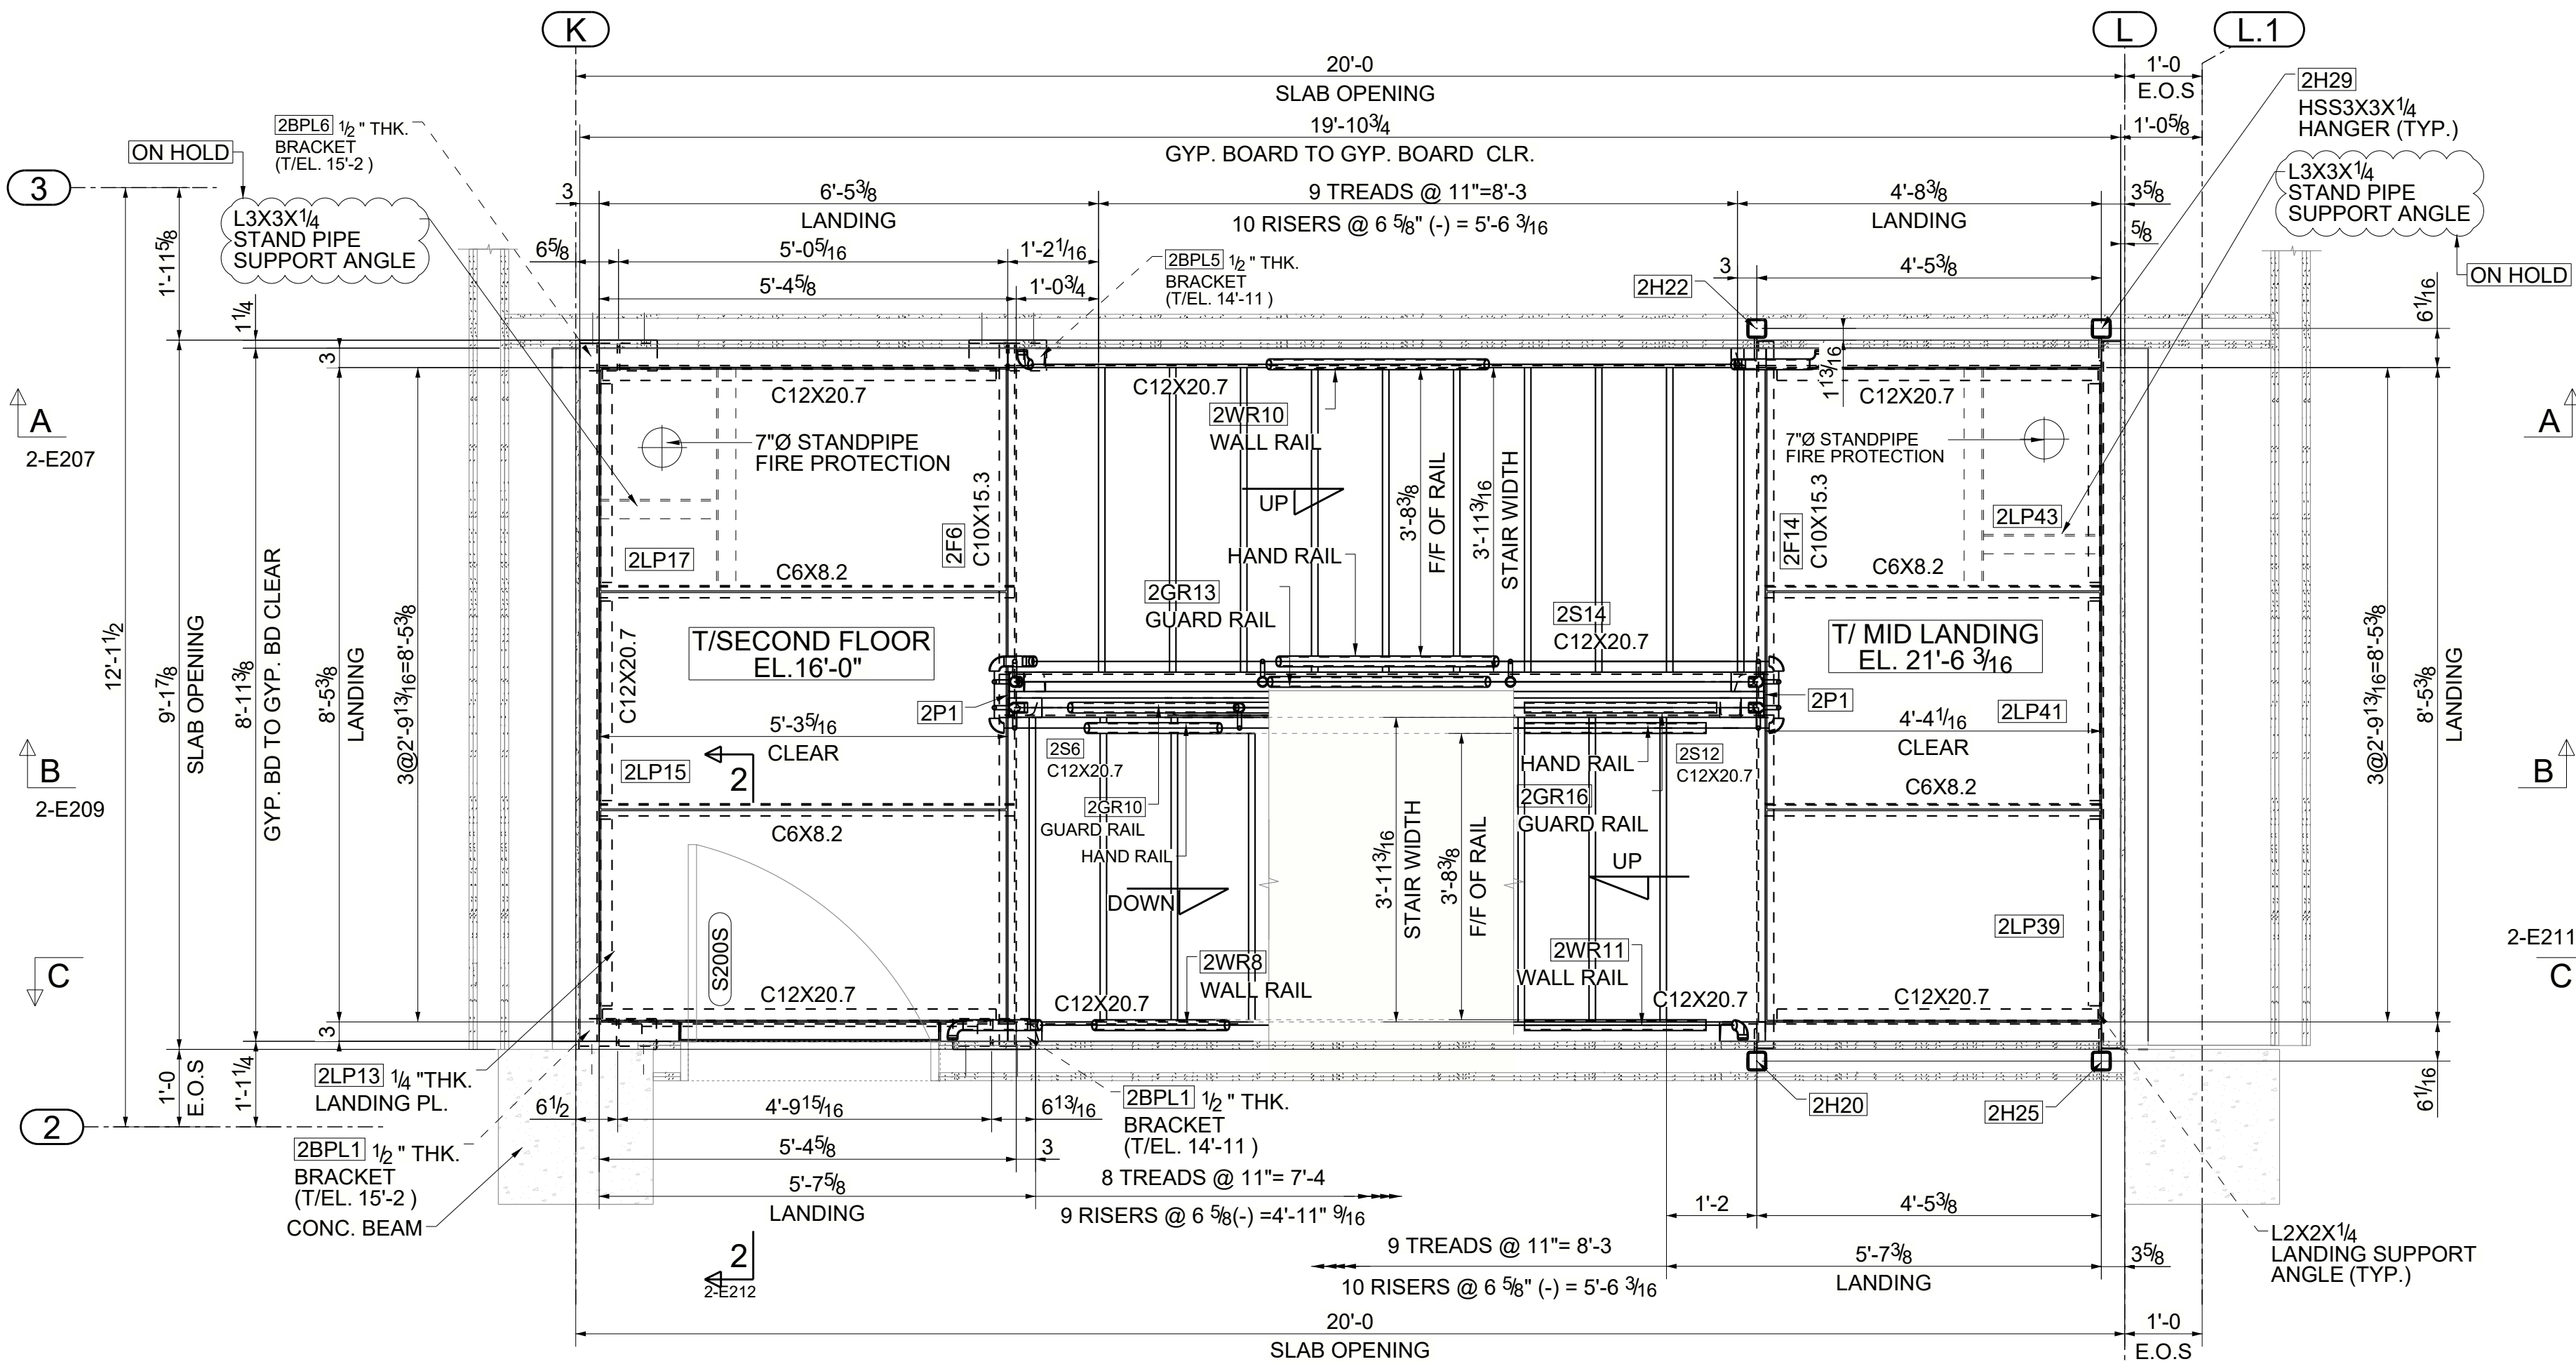


PARTIAL FRAMING PLAN OF SOUTH STAIR @ T/SECOND FLOOR EL. T/ EL. 16'-0

(REFER : SECOND FLOOR PLAN-SOUTH STAIR 2/ A400& A-102A)

NOTES:-

1. REFER SHEET 2-E200 FOR OVER ALL MISC. KEY PLAN.
2. REFER SHEET 2-E201 FOR 3D VIEW.
3. REFER SHEET 2-E206 TO 2-E211 FOR ELEVATIONS.
4. REFER SHEET 2-E212 FOR TYPICAL SECTIONS AND DETAILS.


FOR FIELD USE : 02/26/2024

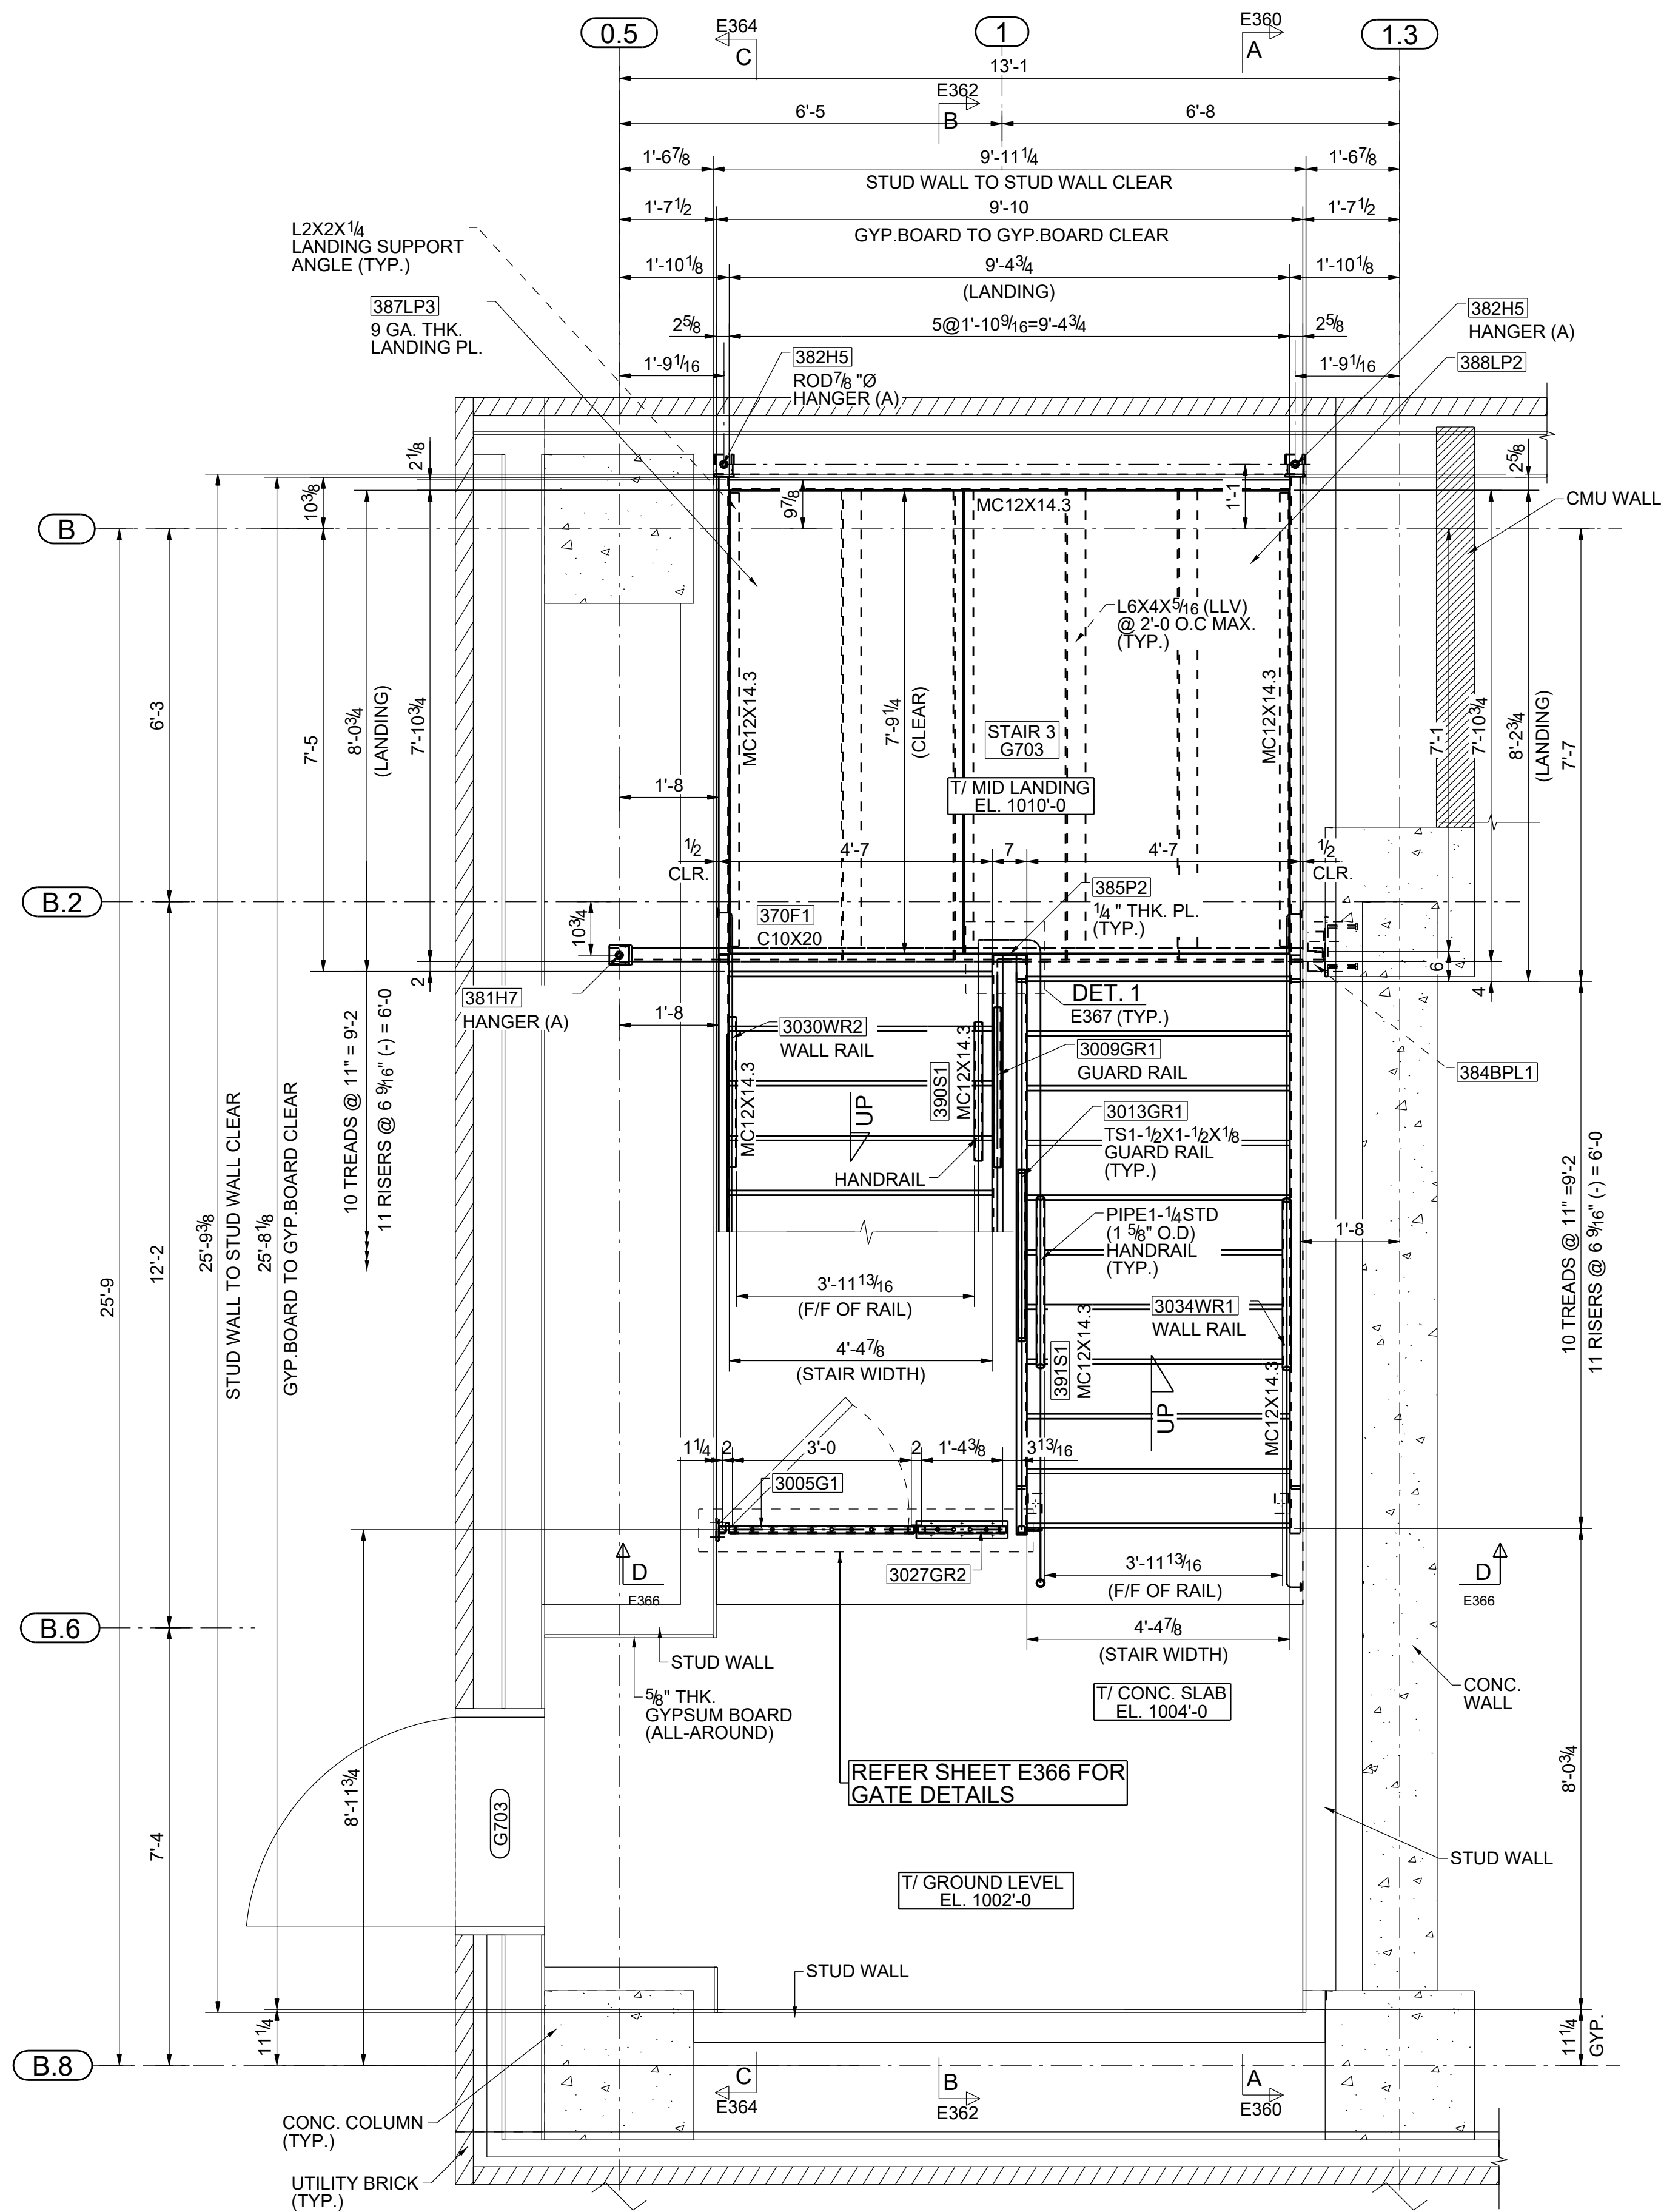


STAIR # 3 PARTIAL FRAMING PLAN @ GROUND LEVEL (T/SLAB AT STAIR LOCATION EL.1004'-0")
(REF: GROUND LEVEL - ENLARGED PLAN - STAIR WEST - 0/ A507/ EDGE OF SLAB PLAN - GROUND FLOOR - WEST - 1/ S250A)


NOTES :

1. REFER SHEET E353 FOR GENERAL NOTES
2. REFER SHEETS FROM E360 TO E365 FOR ELEVATIONS
3. REFER SHEET E366 E367 FOR TYPICAL SECTIONS & DETAILS

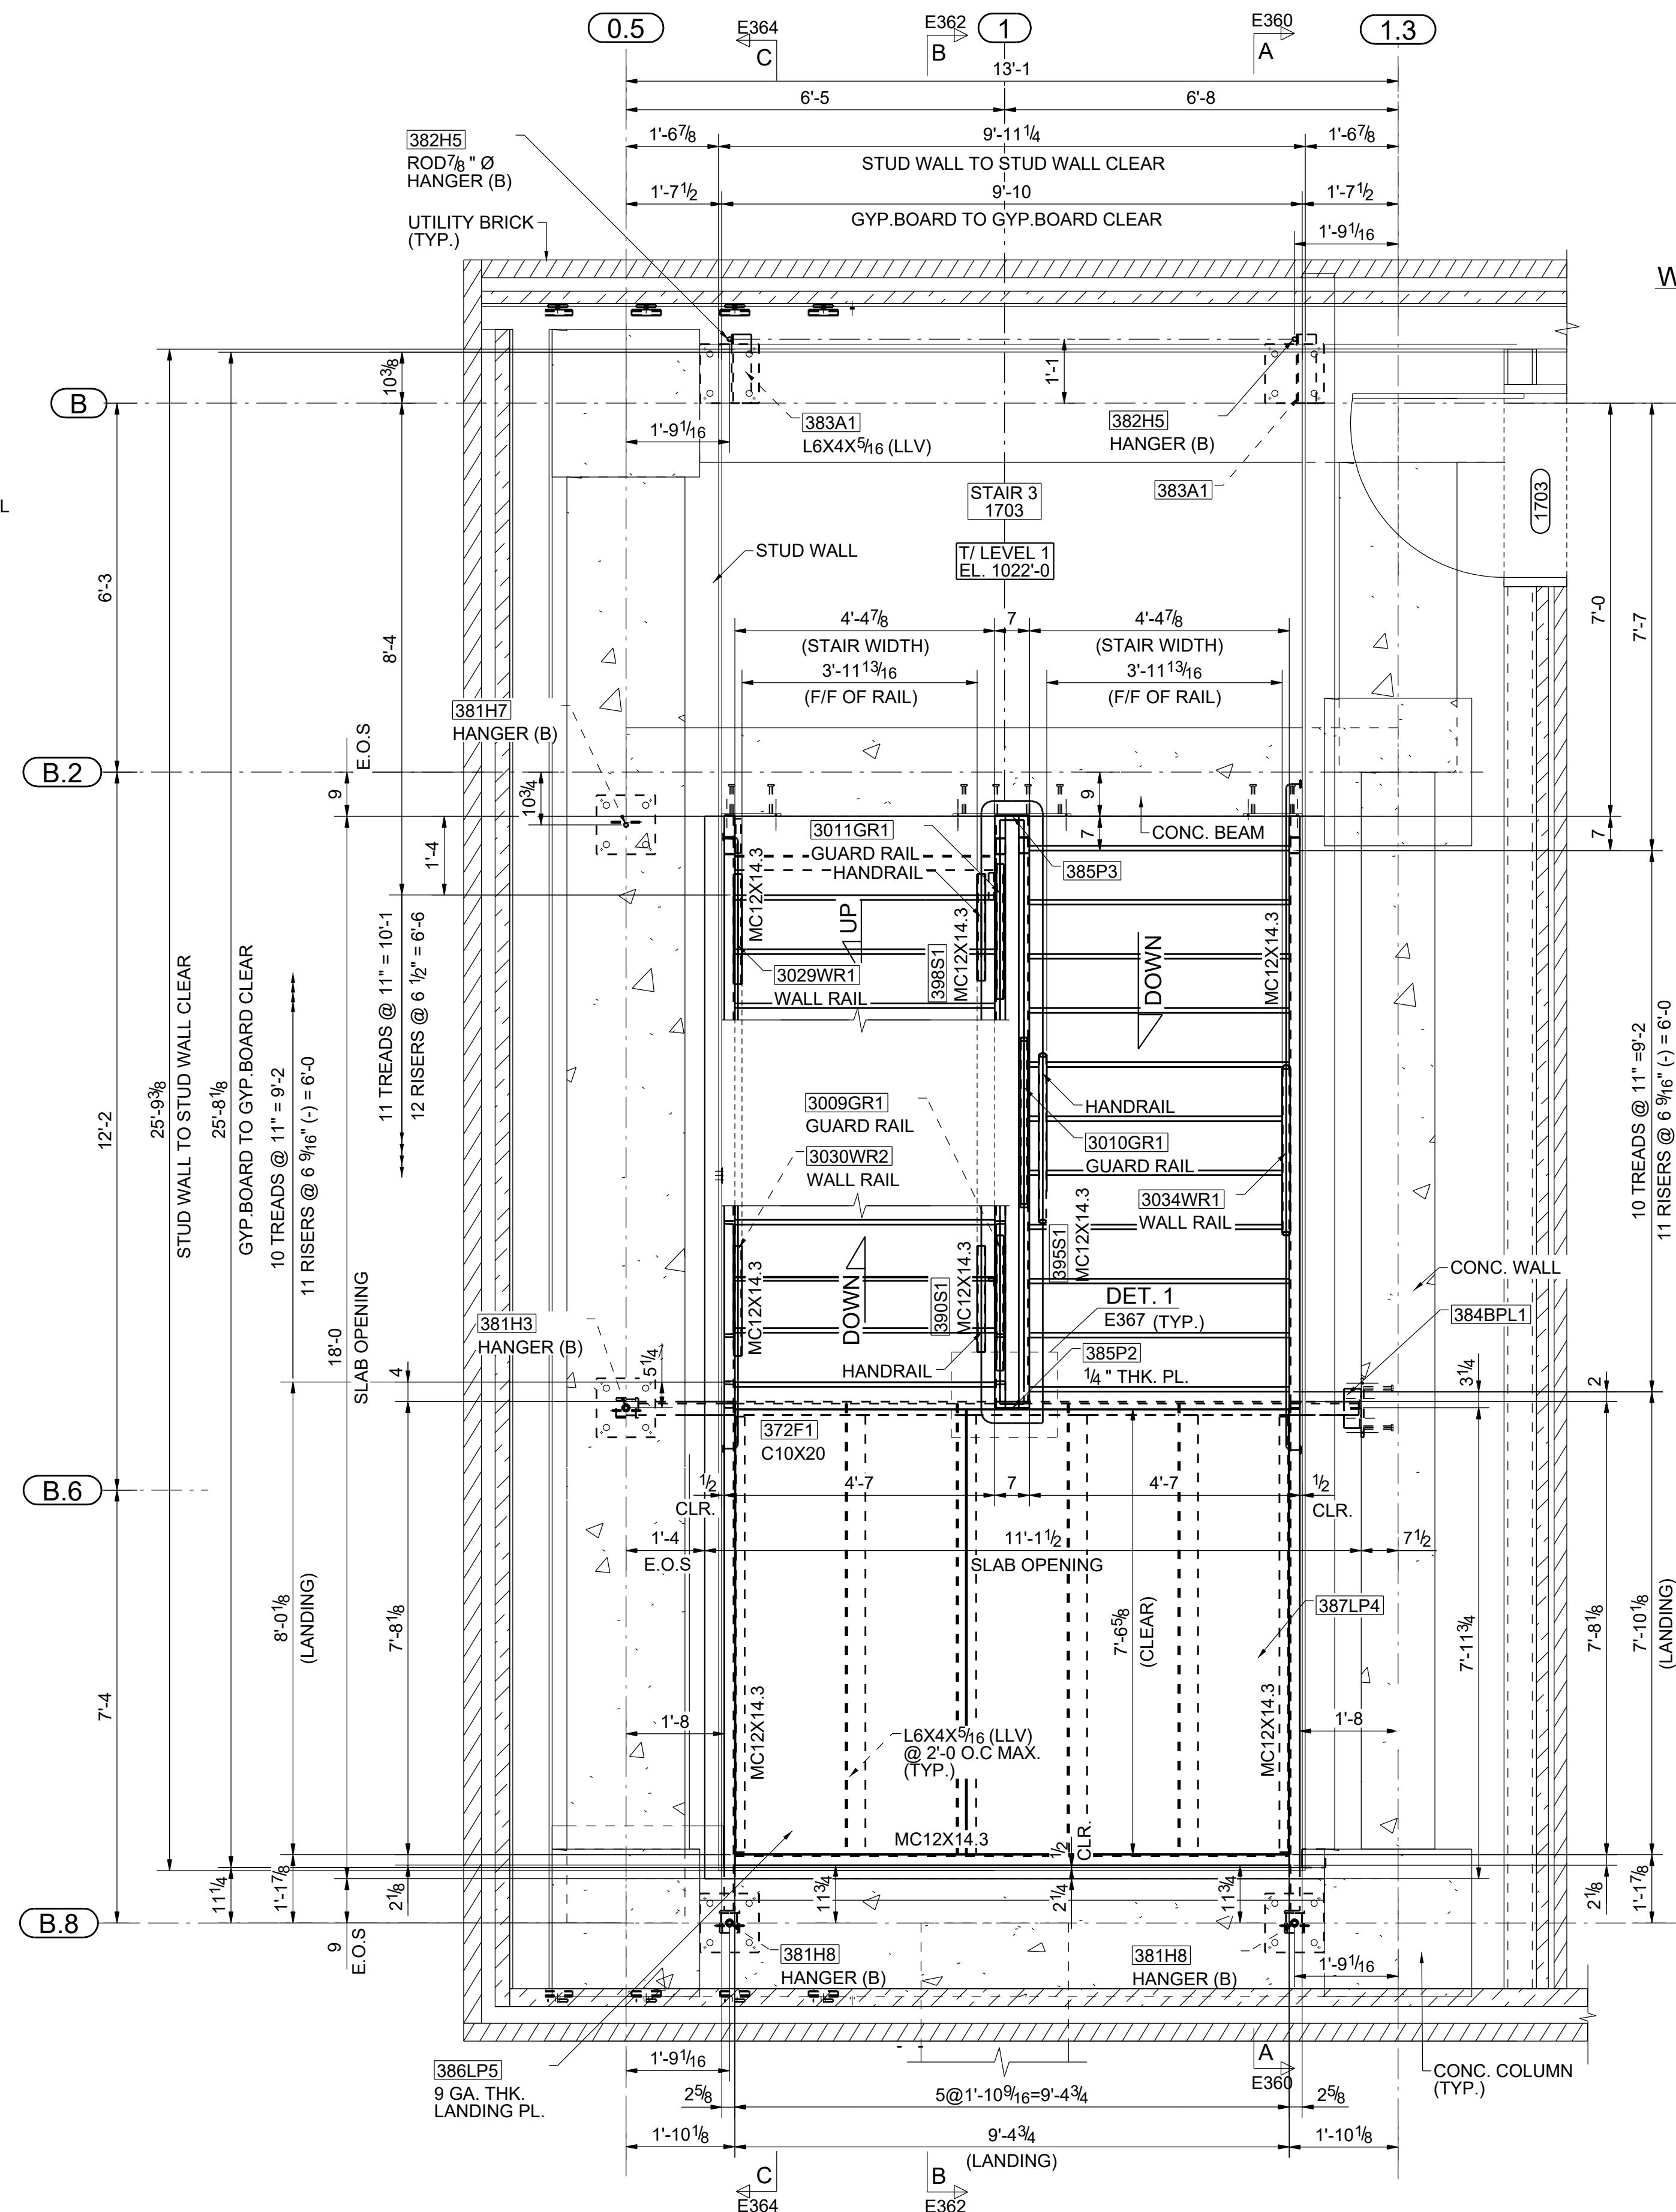


STAIR # 3 PARTIAL FRAMING PLAN @ LEVEL 1 (EL. 1022'-0")
(REF: LEVEL 1 - ENLARGED PLAN - STAIR WEST - 1/ A507/ SLAB EDGE - LEVEL 1 - WEST - 1/ S251A)

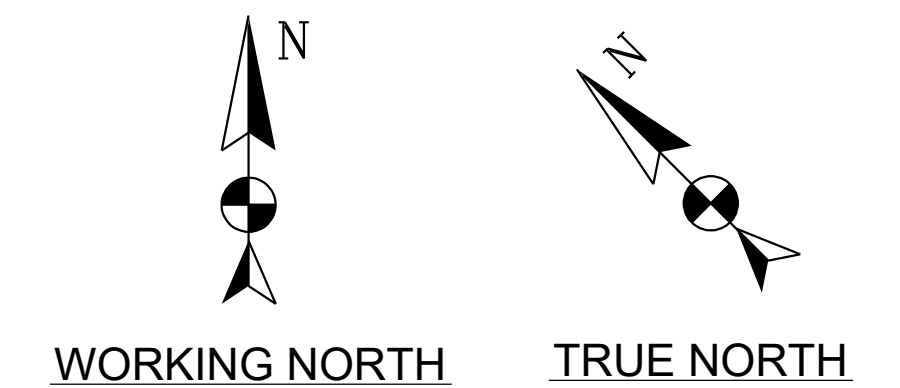

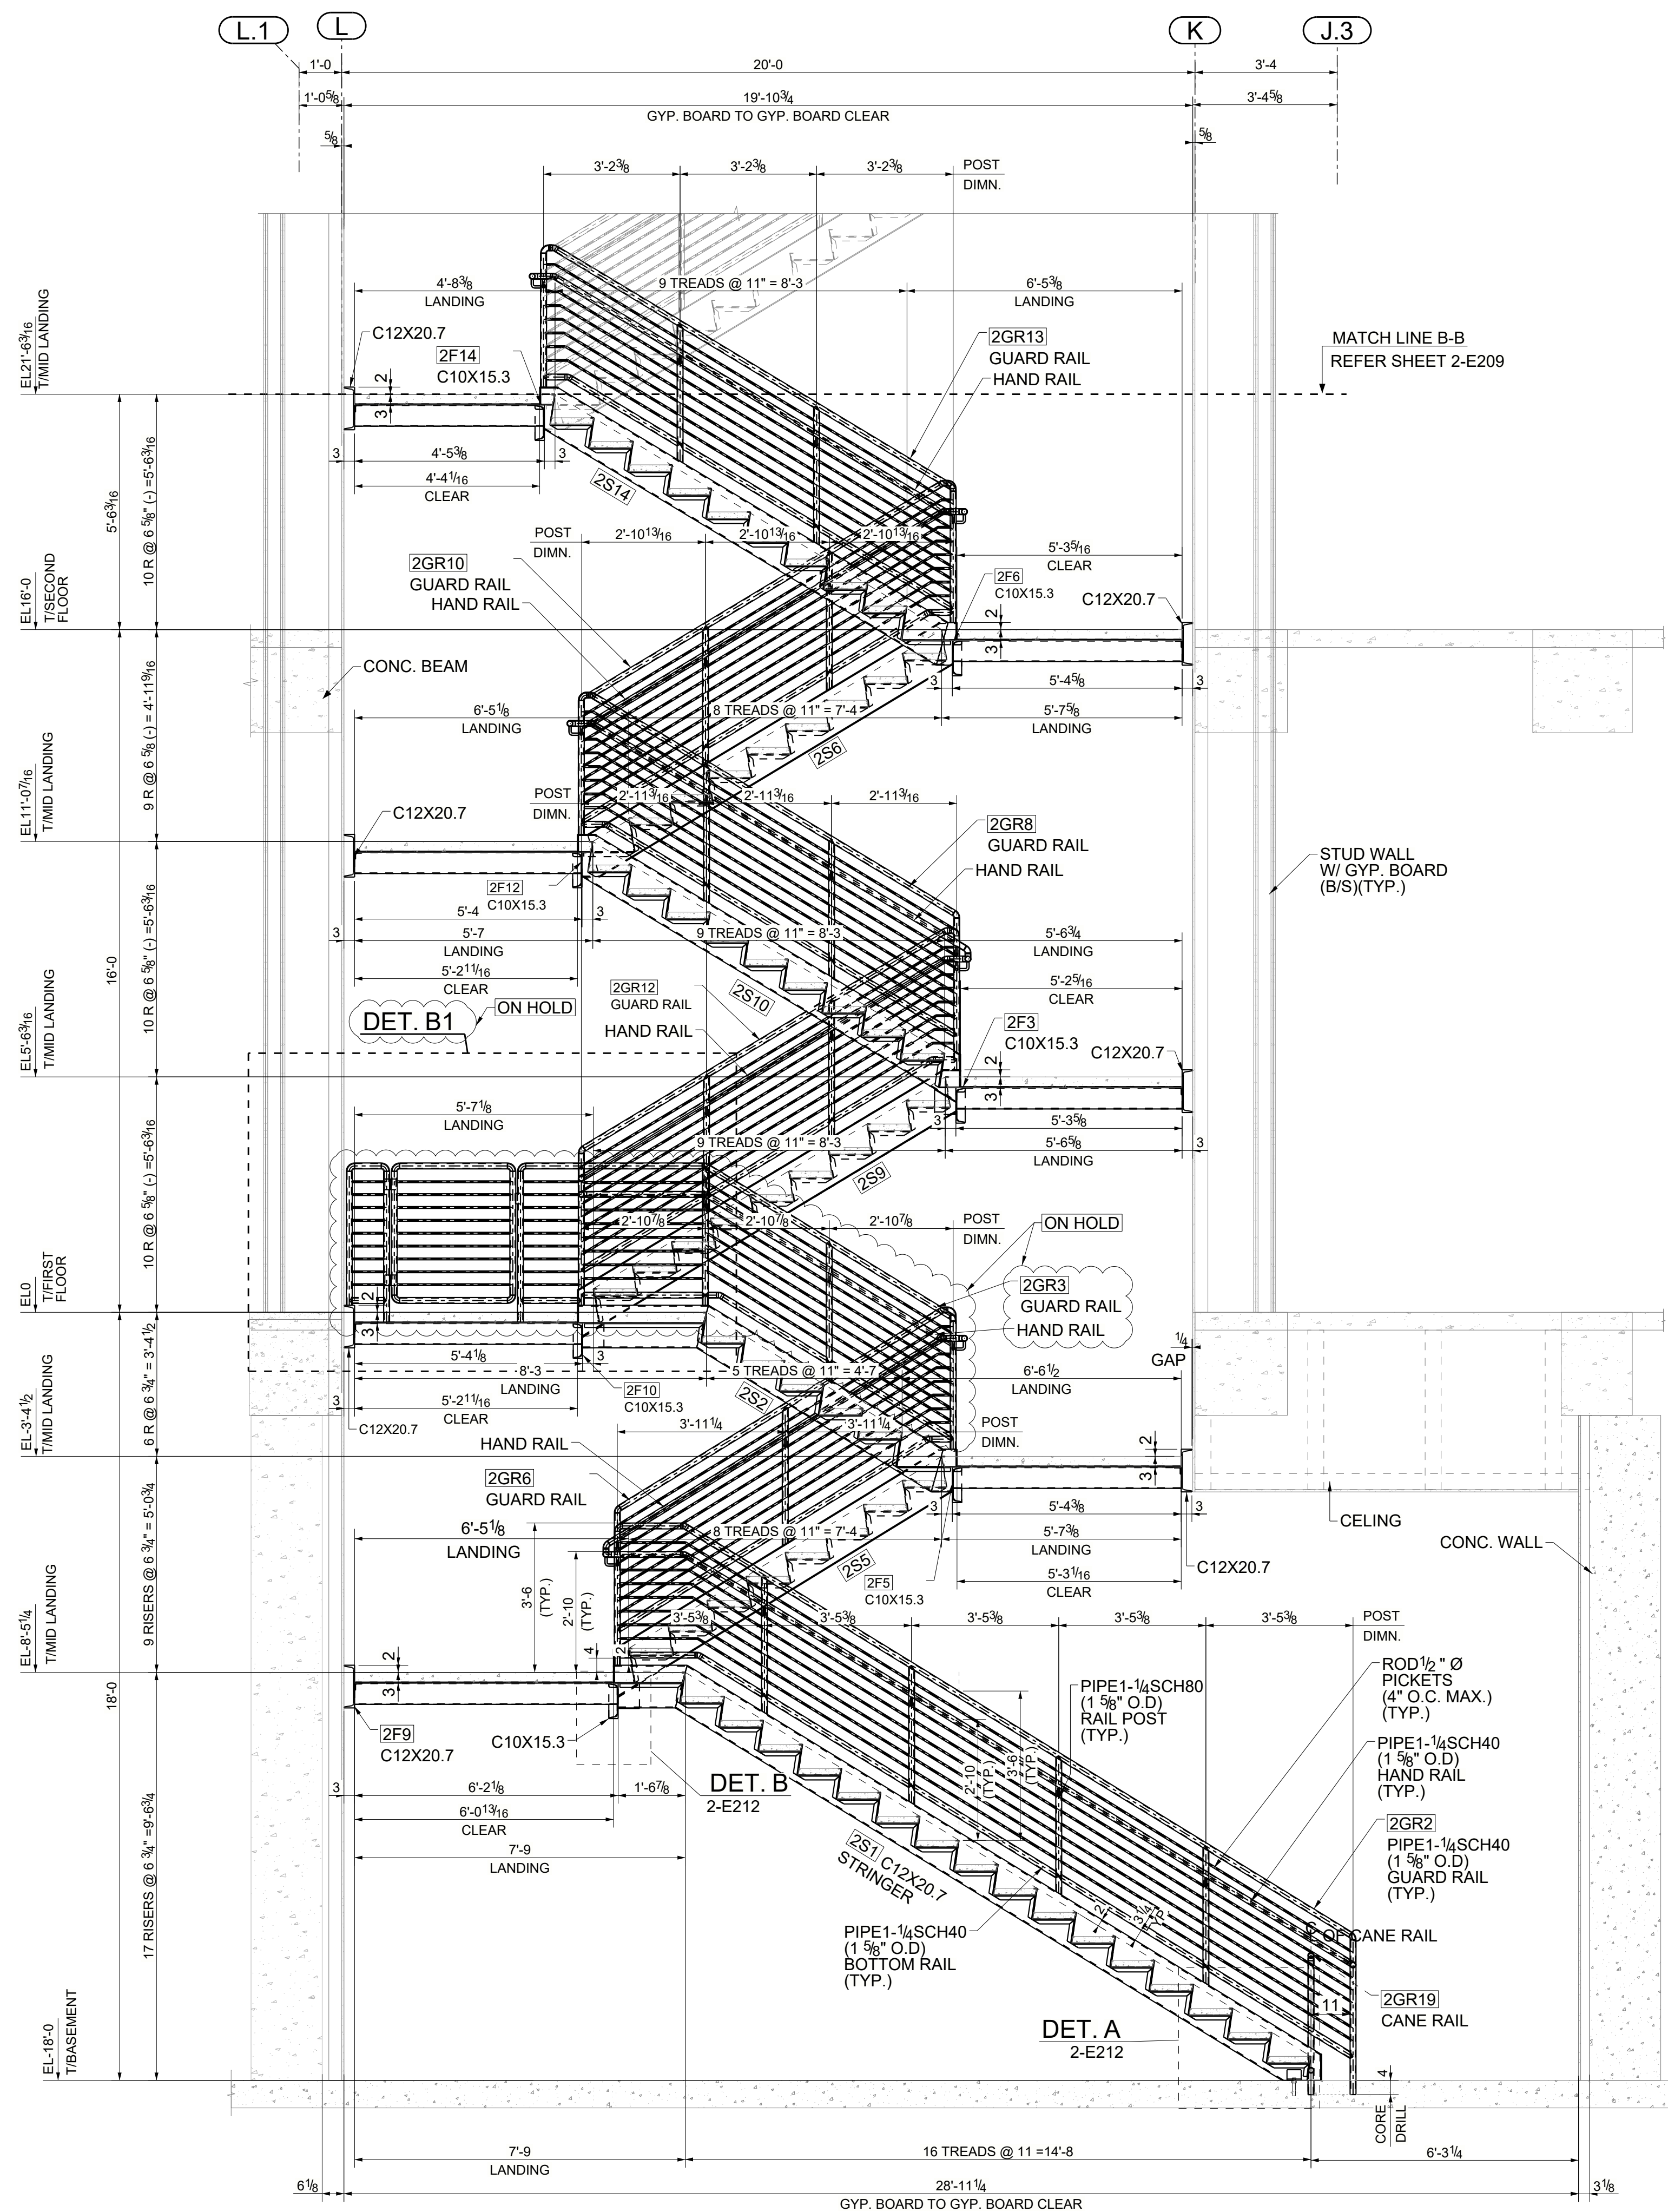

SECTION B - B 2-E202

(REFER : SOUTH STAIR SECTION -6/A-400)

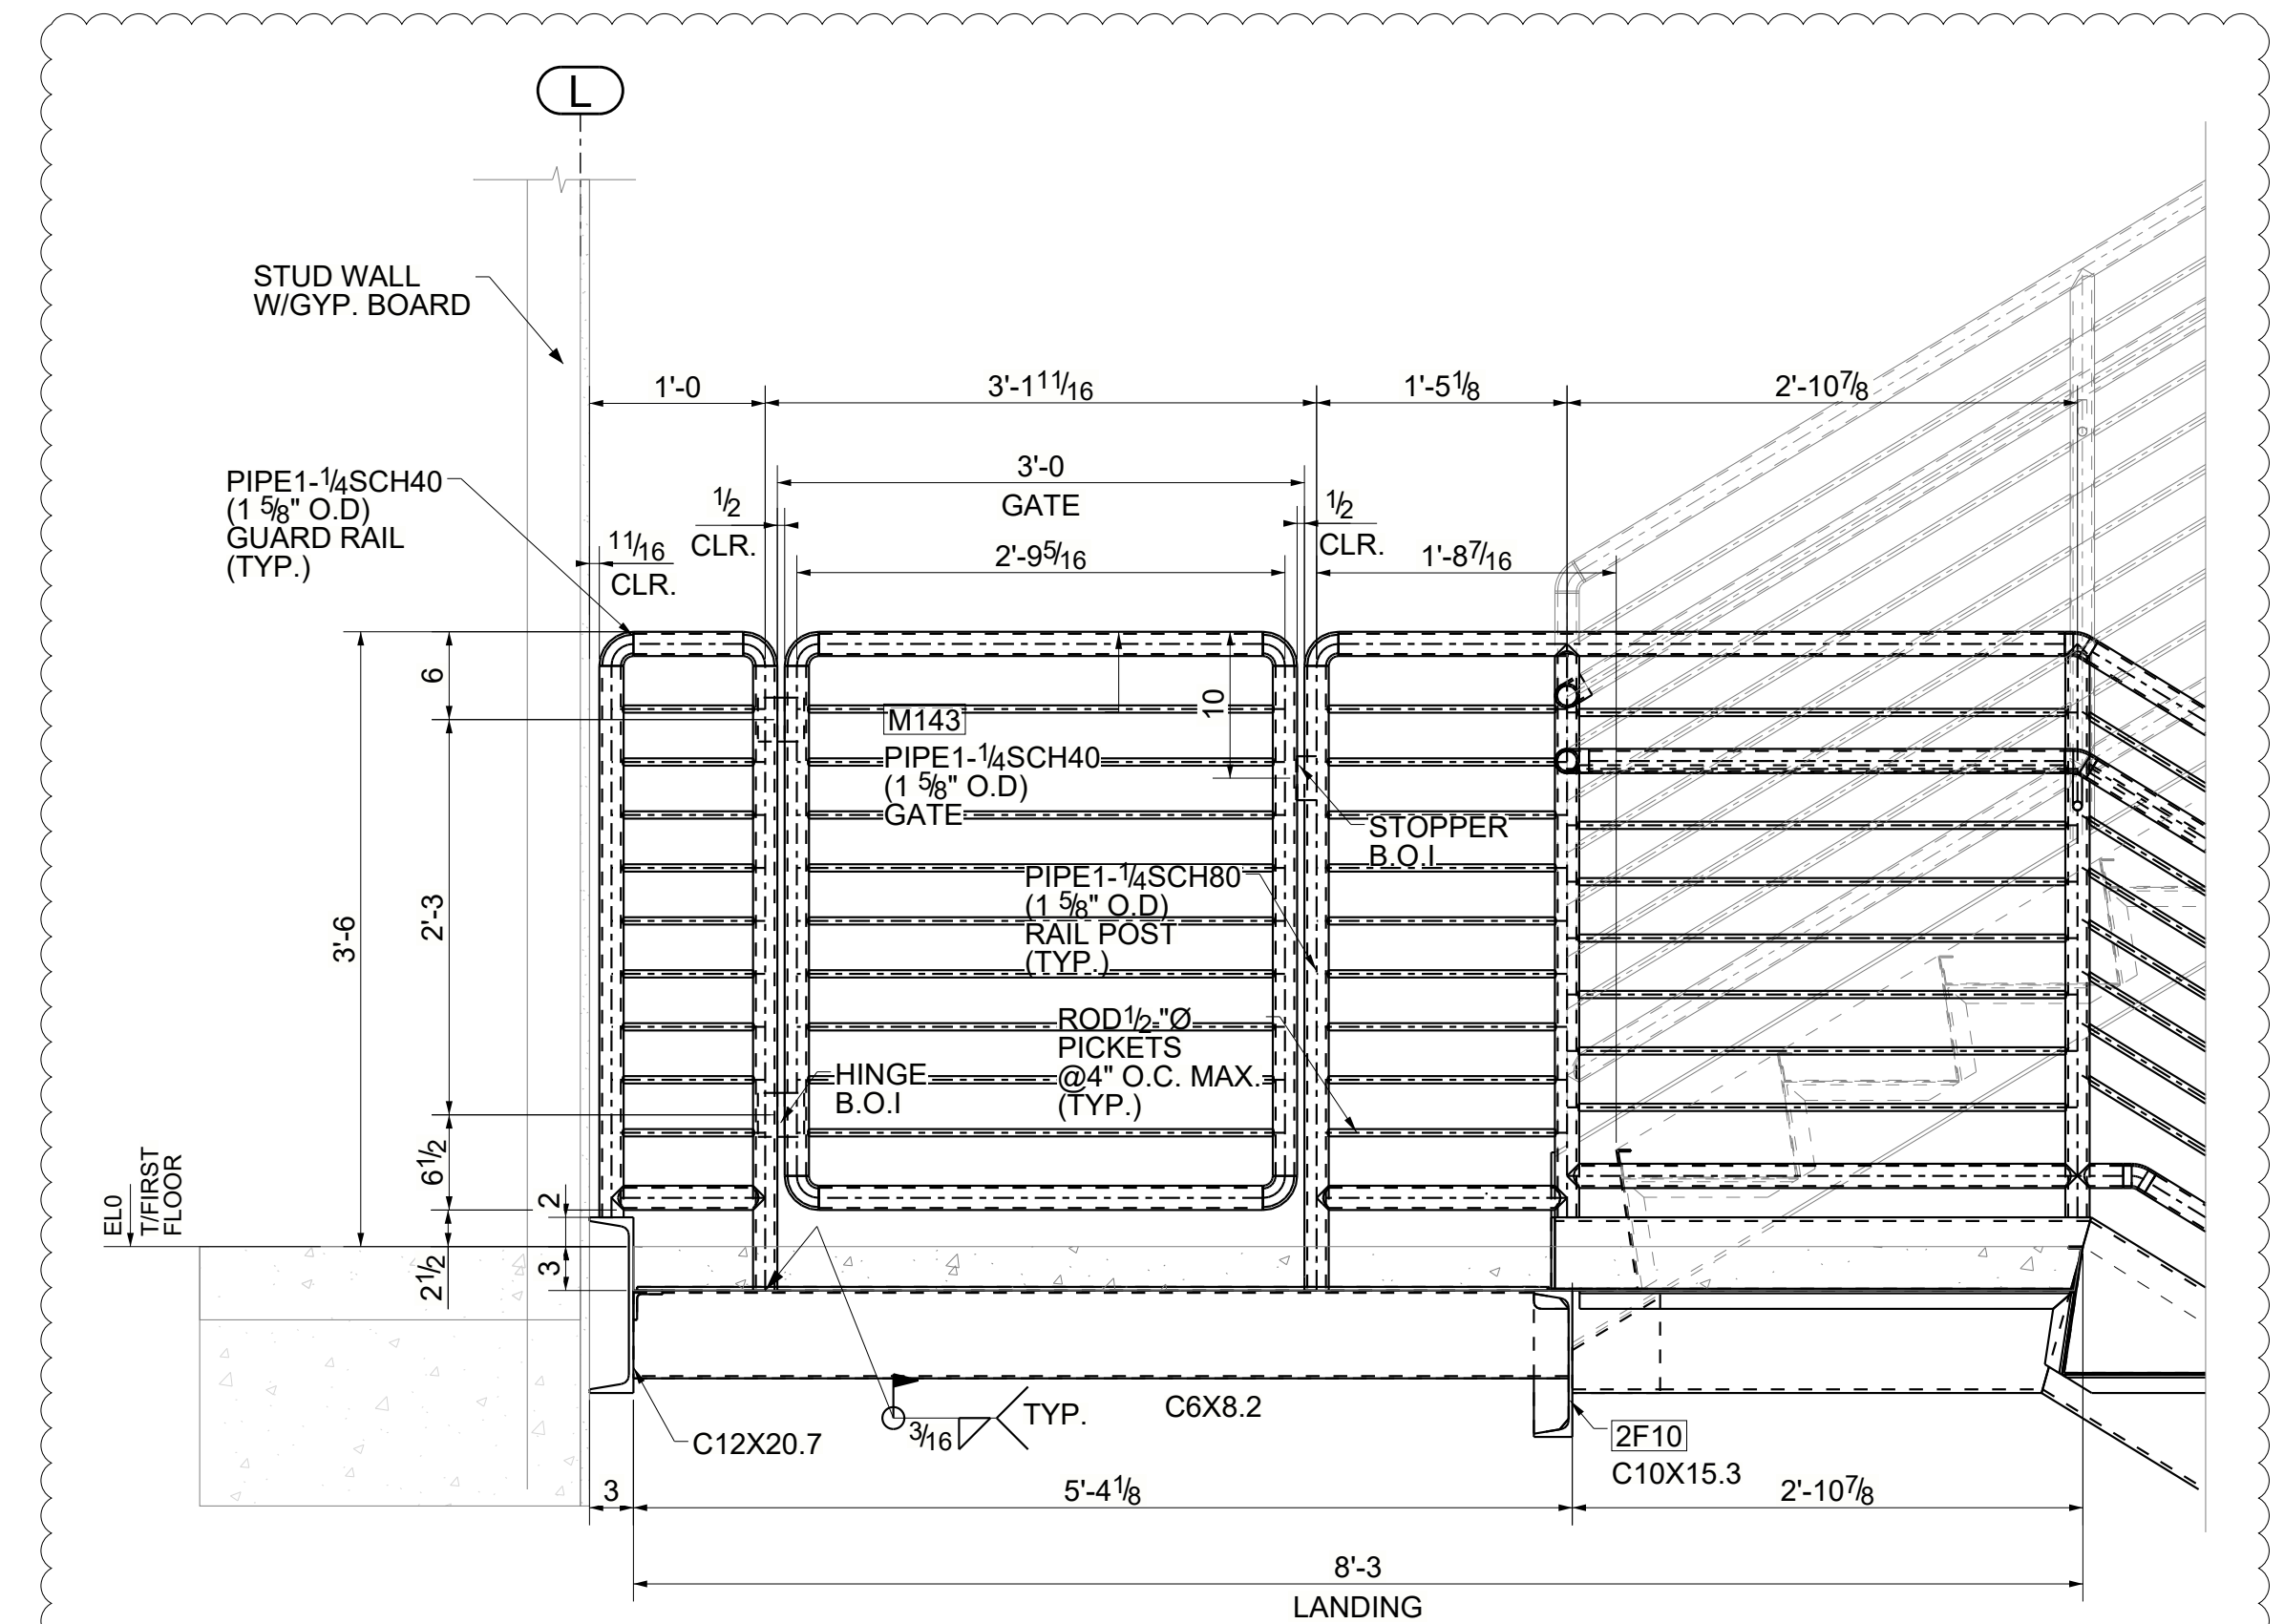


DETAIL B1

ON HOLD

NOTES :

1. REFER SHEET 2-E201 FOR 3D VIEW.
2. REFER SHEET 2-E202 TO 2-E205 FOR FRAMING PLAN.
3. REFER SHEET 2-E212 FOR TYPICAL SECTIONS AND DETAILS.

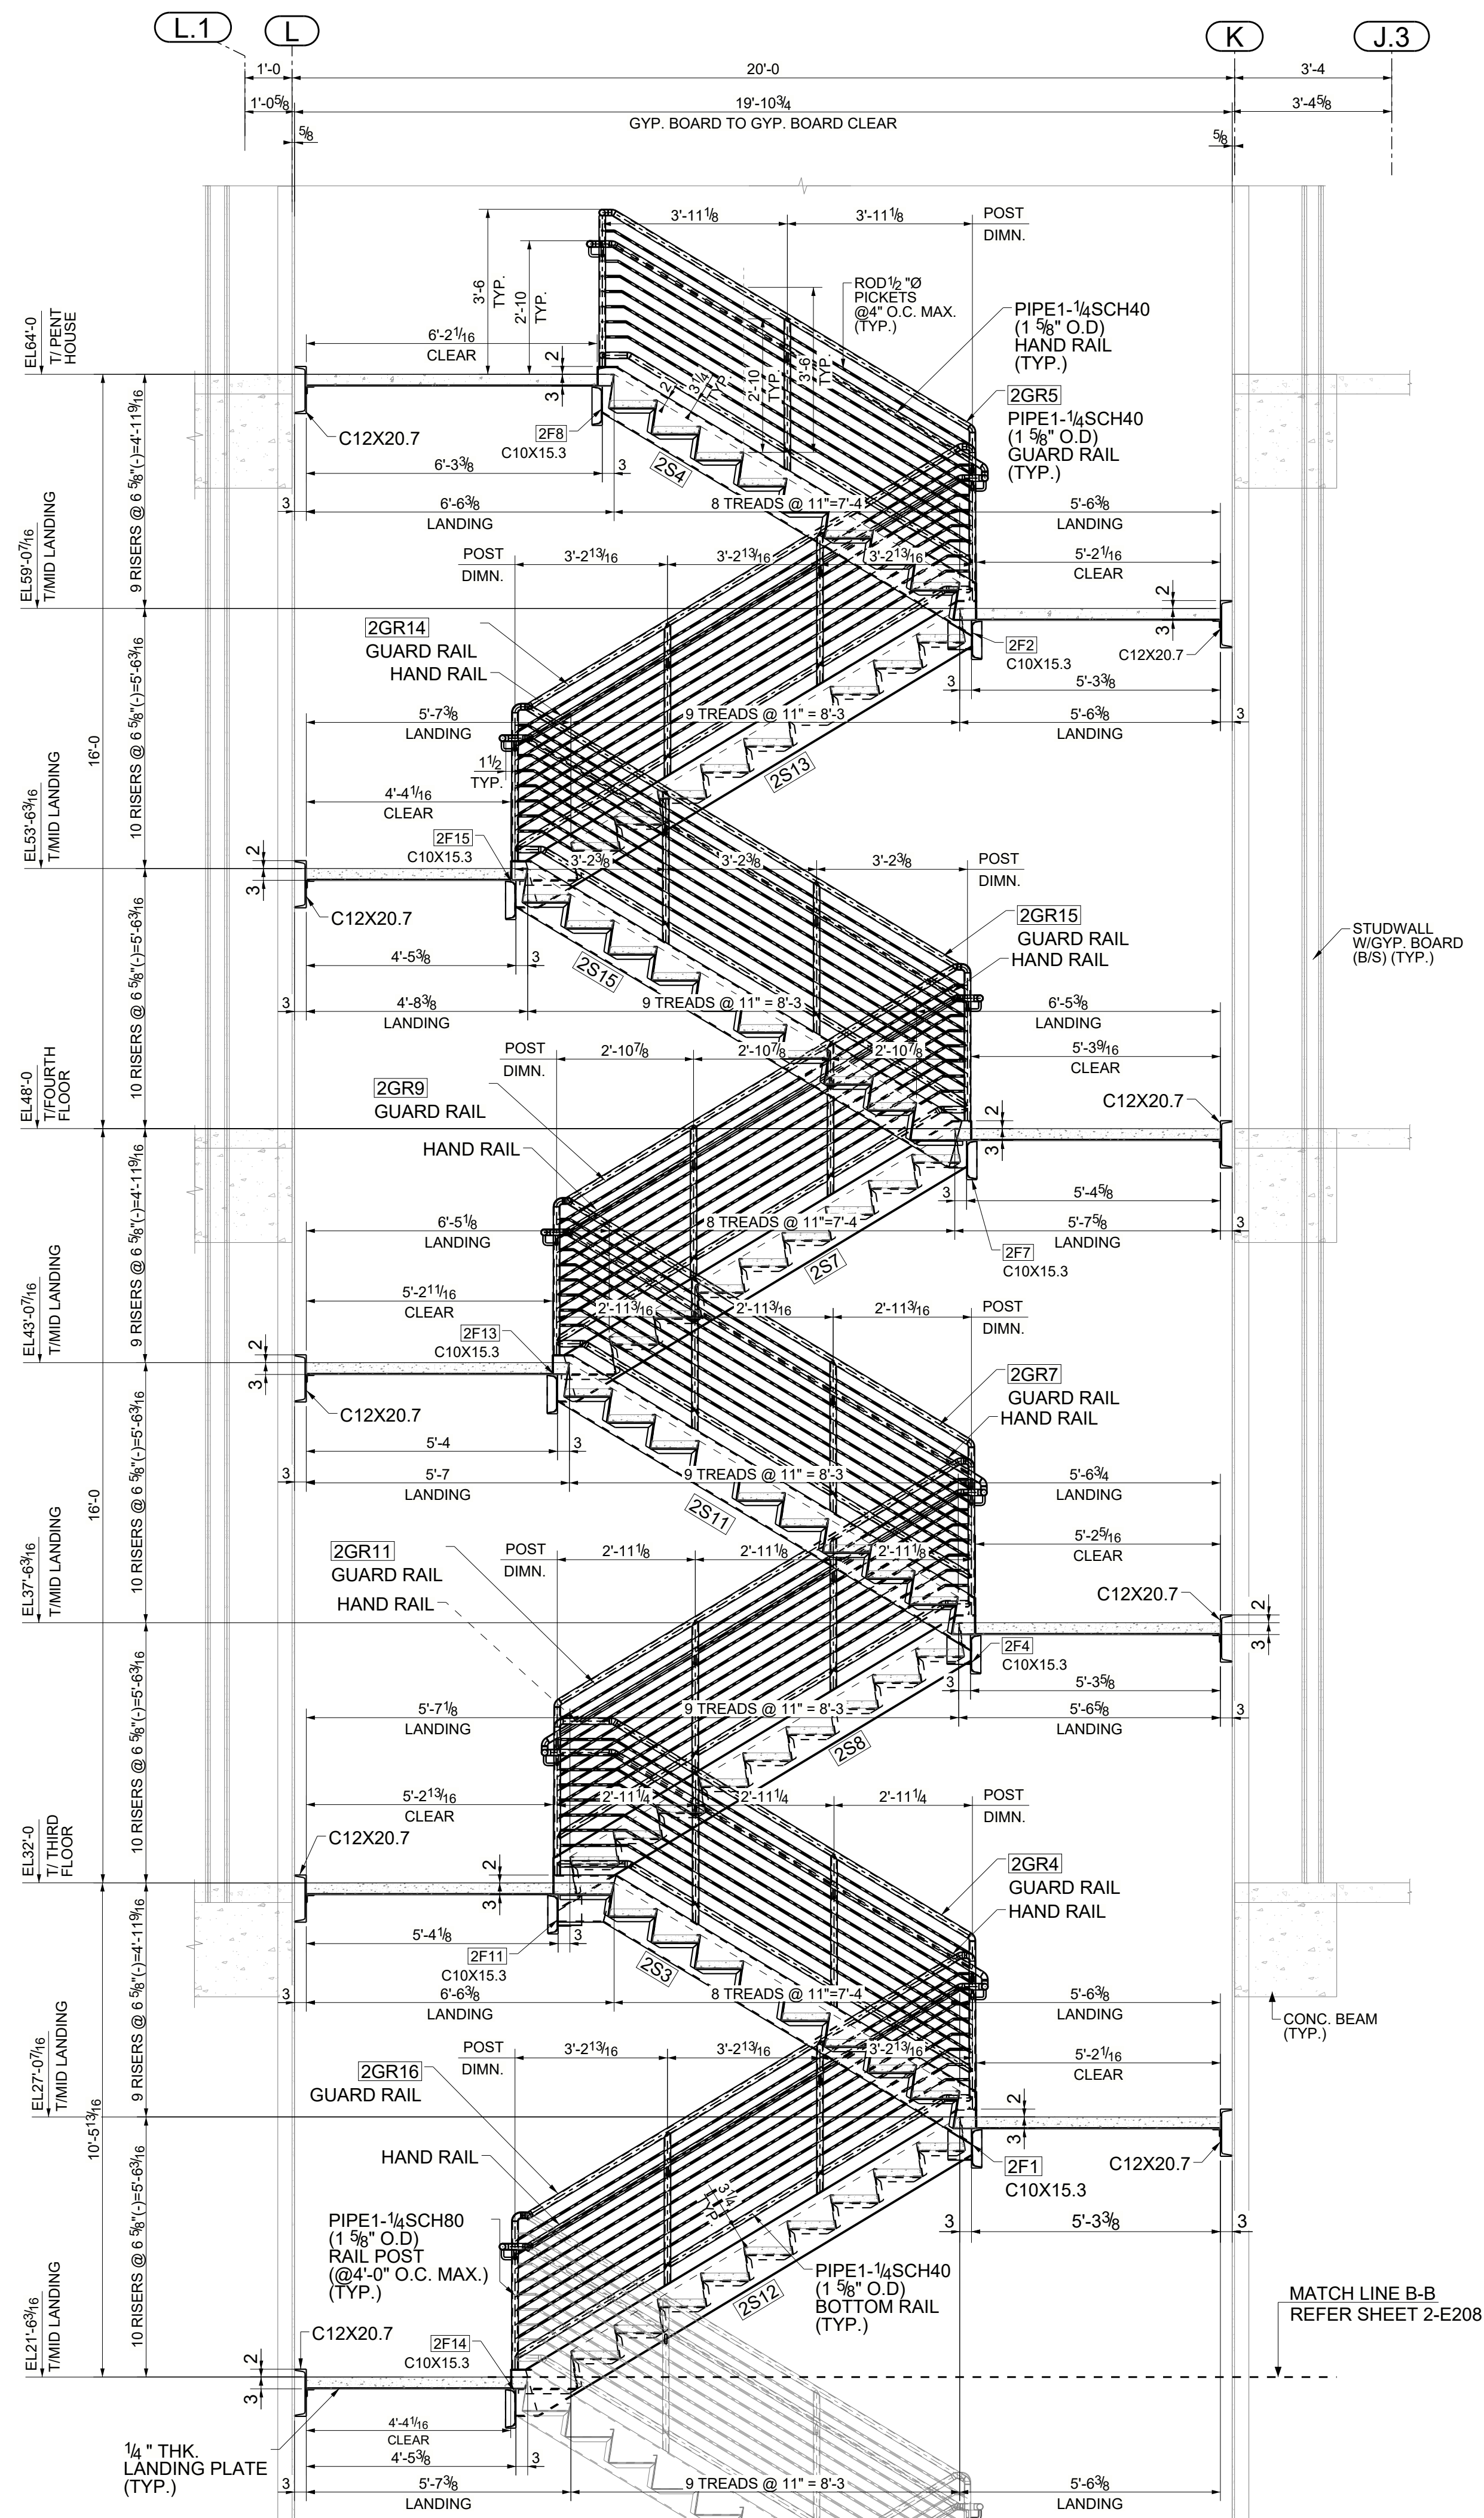

SECTION B - B

2-E202
(REFER: SOUTH STAIR SECTION -6/A-400)

NOTES :

1. REFER SHEET 2-E201 FOR 3D VIEW.
2. REFER SHEET 2-E202 TO 2-E205 FOR FRAMING PLAN.
3. REFER SHEET 2-E212 FOR TYPICAL SECTIONS AND DETAILS.





SECTION 1C - 1C

NOTES :-

1. REFER SHEET E353 FOR GENERAL NOTES.
2. REFER SHEET E354 TO E359 FOR FRAMING PLANS.
3. REFER SHEET E366 & E367 FOR TYPICAL SECTIONS & DETAILS.


REFER SHEET E313 TO E317 FOR
STAIR #3 EMBED LOCATION PLANS

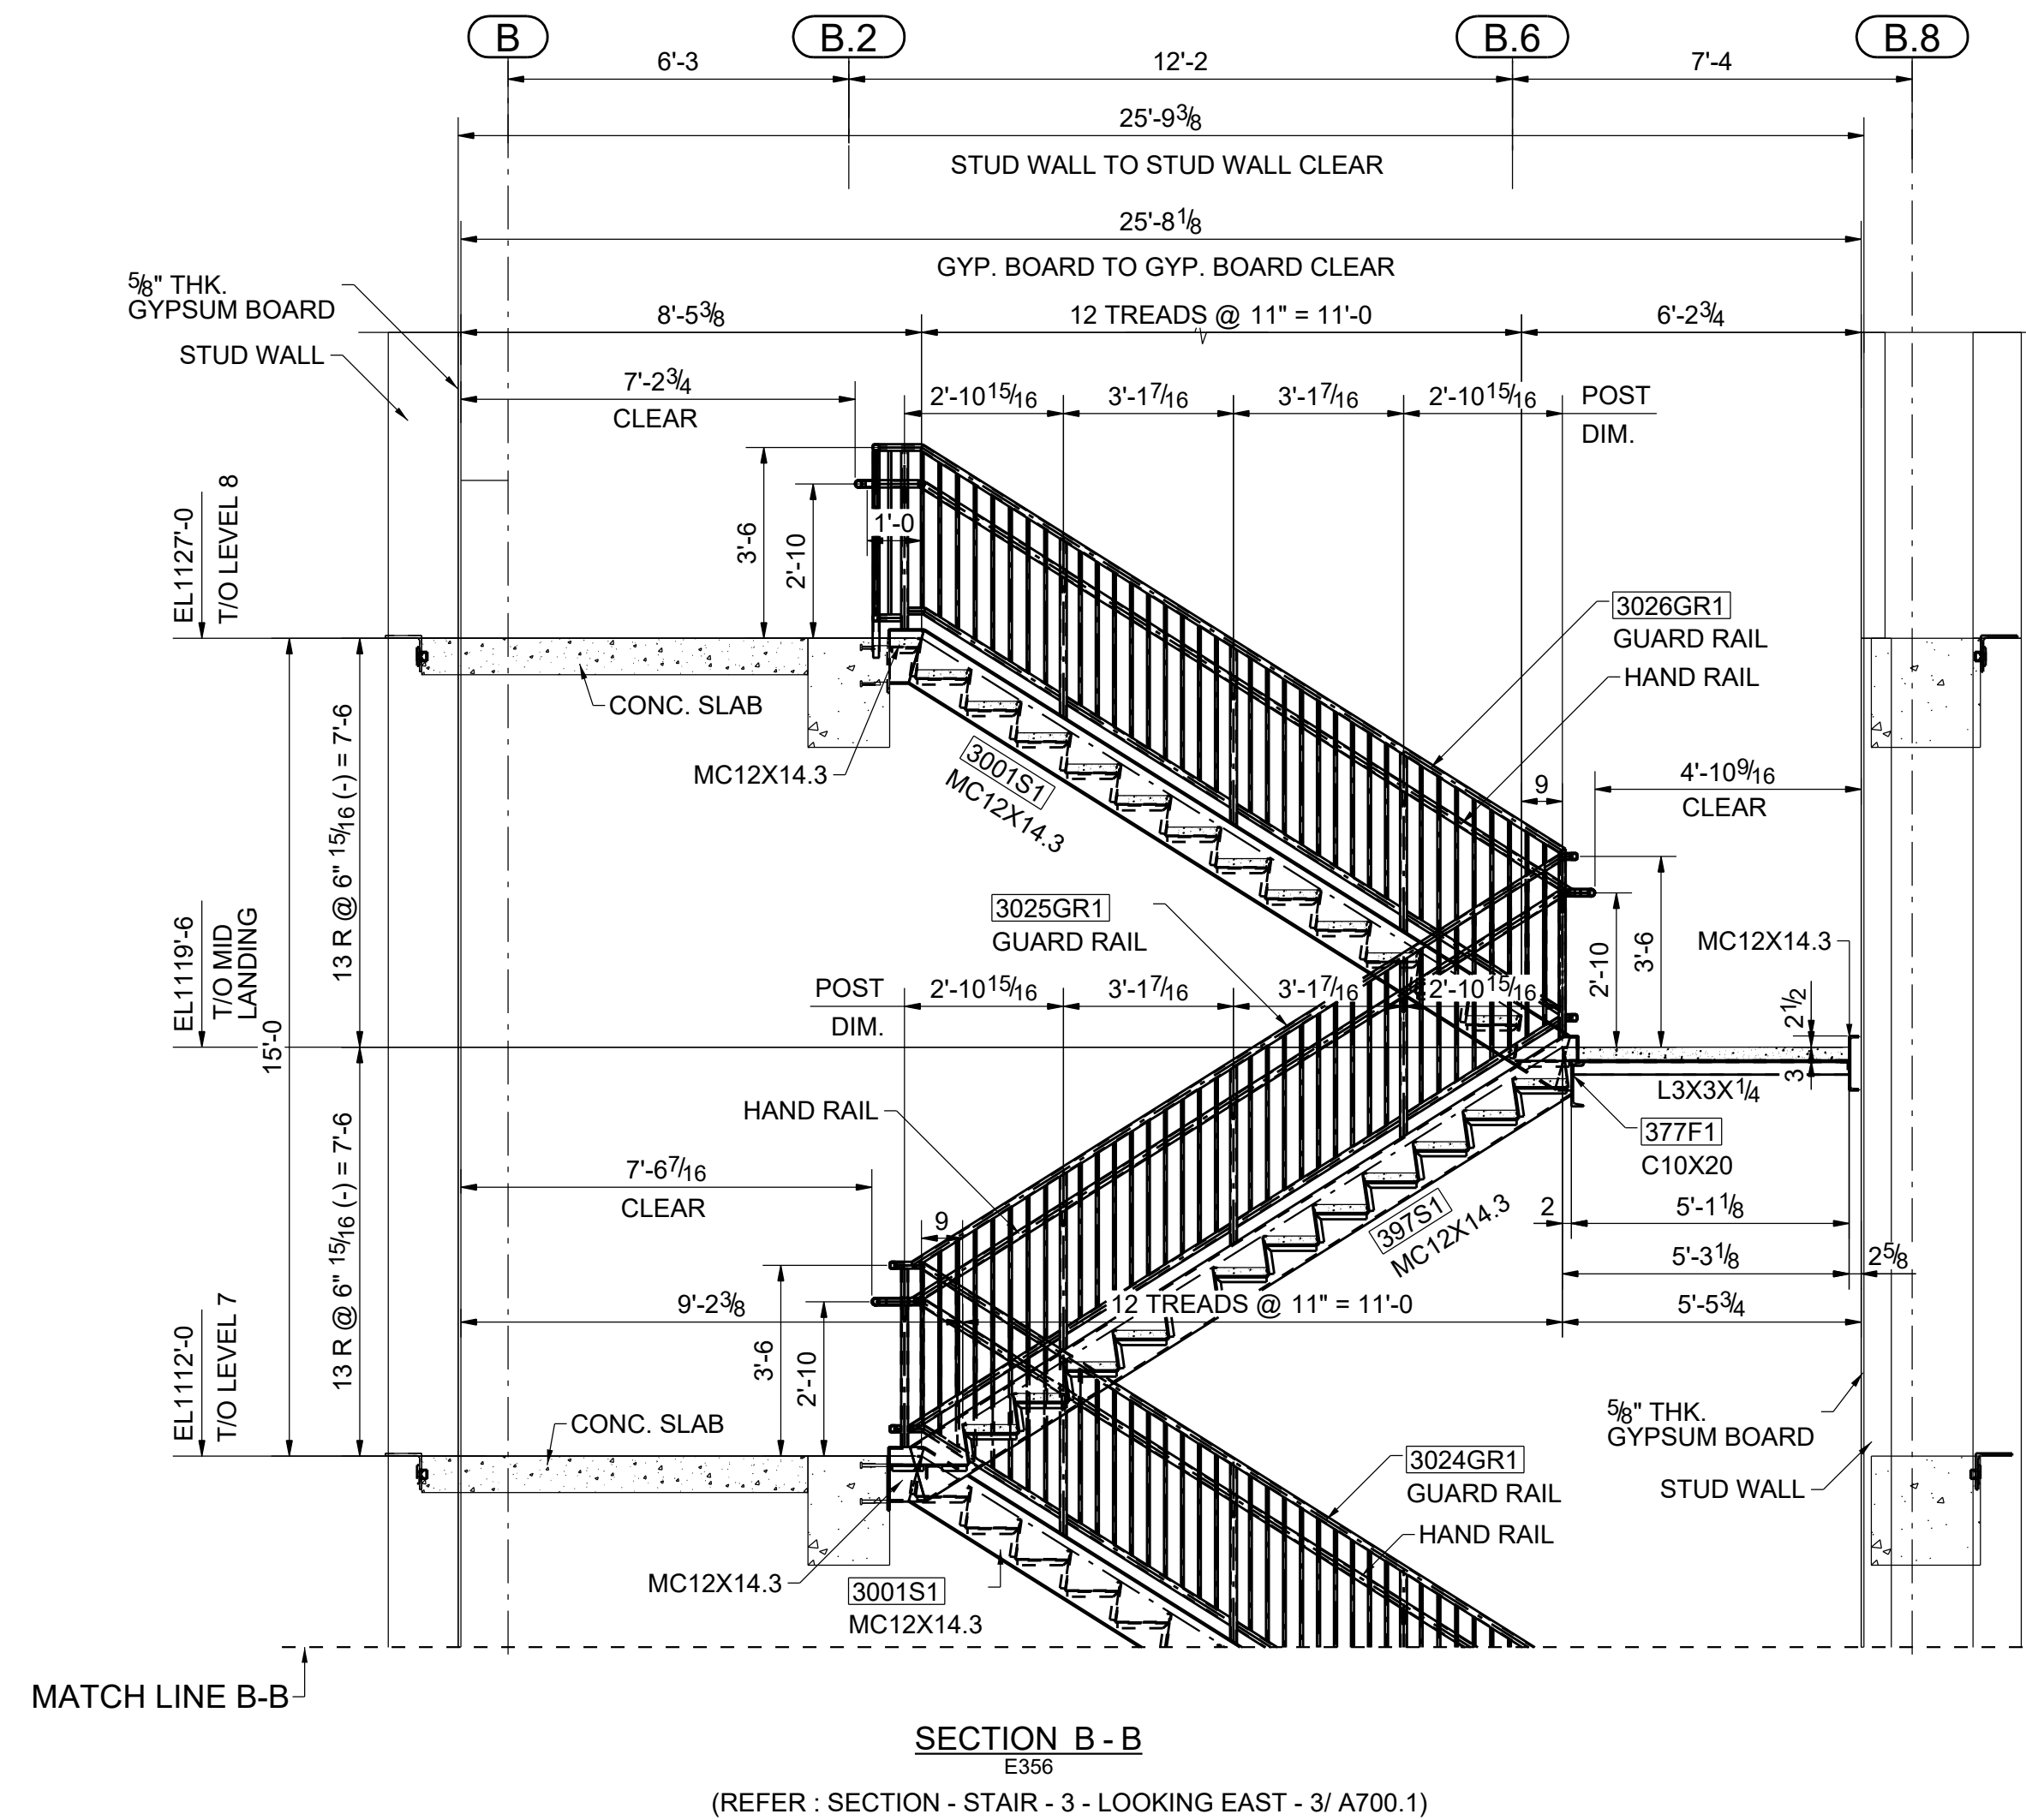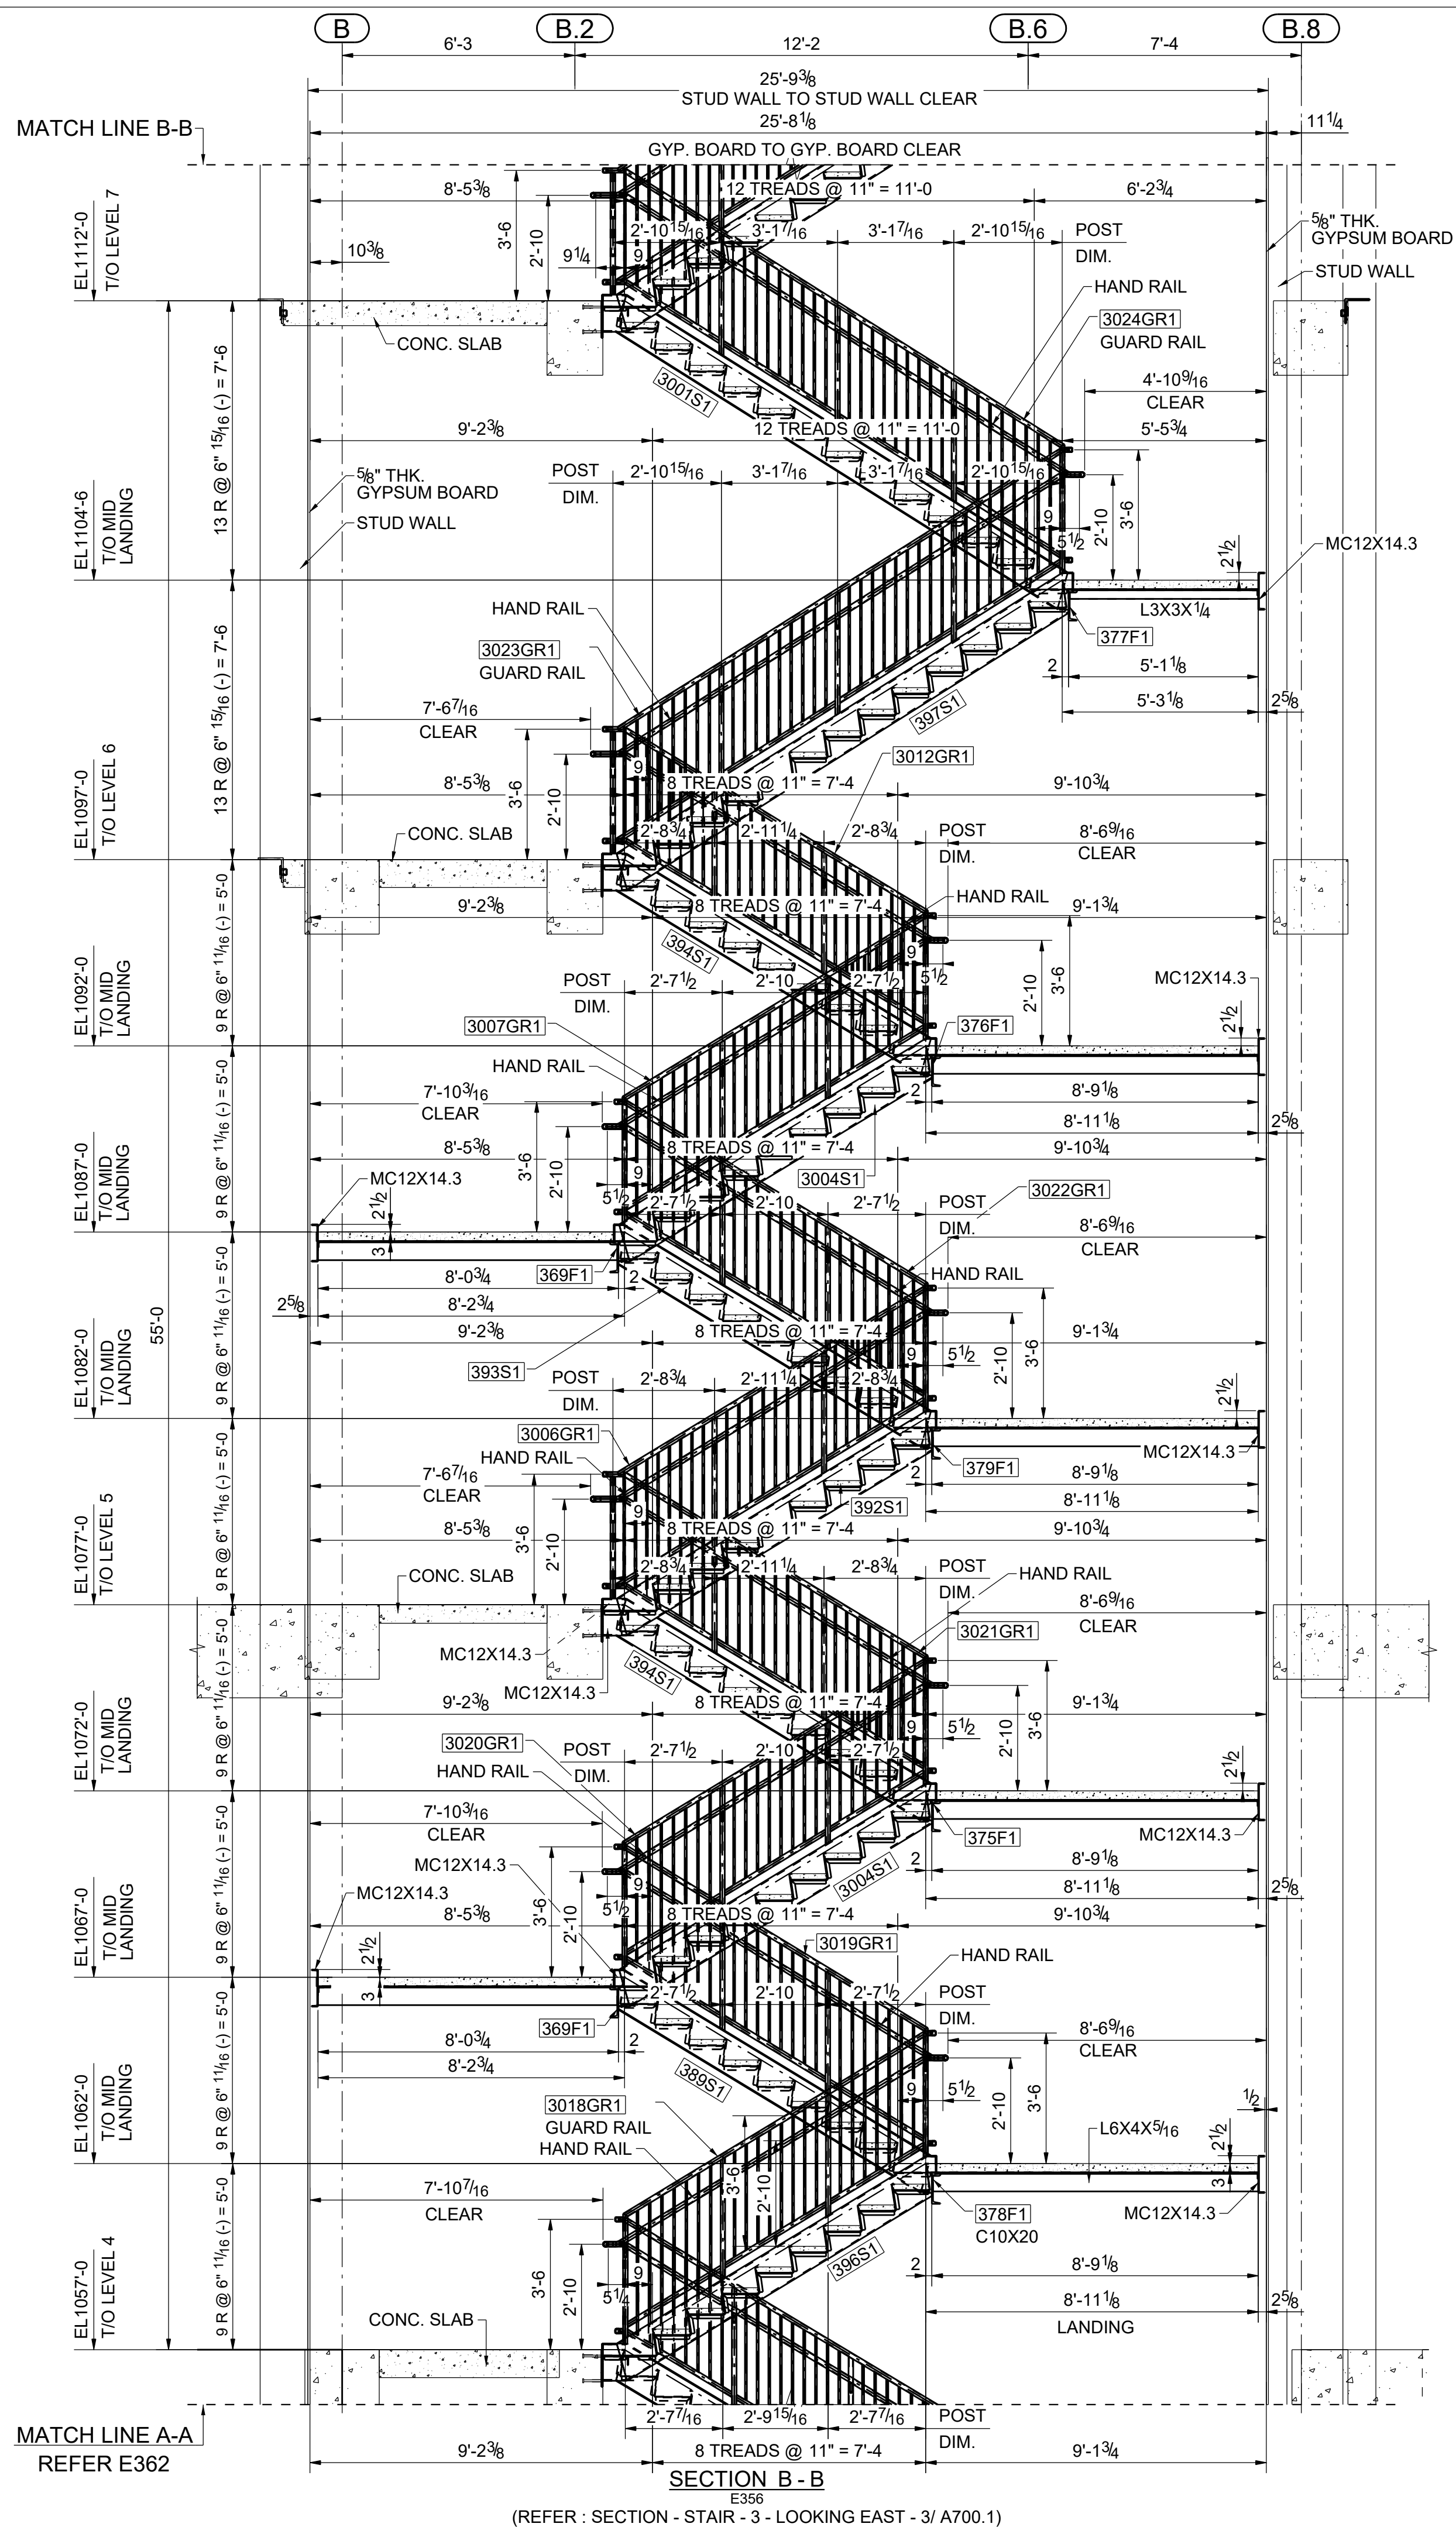


NOTES :-

1. REFER SHEET E353 FOR GENERAL NOTES.
2. REFER SHEET E354 TO E359 FOR FRAMING PLANS.
3. REFER SHEET E366 & E367 FOR TYPICAL SECTIONS & DETAILS.


REFER SHEET E313 TO E317 FOR
STAIR #3 EMBED LOCATION PLANS

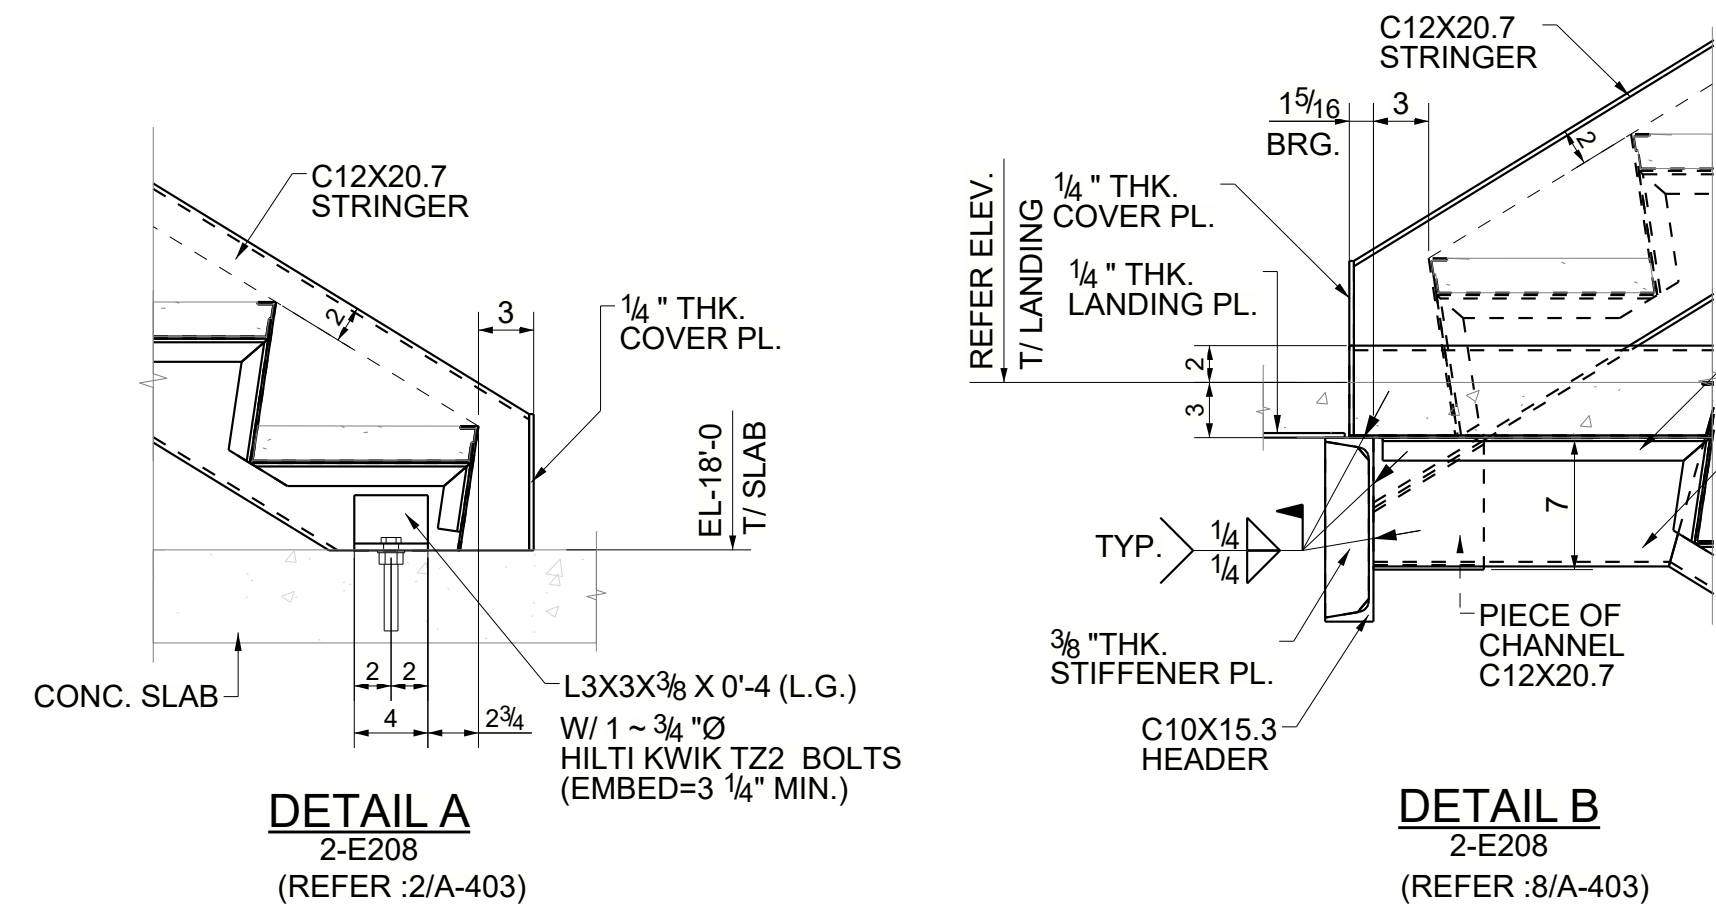


DETAIL B
2-E208
(REFER :3/A-403)

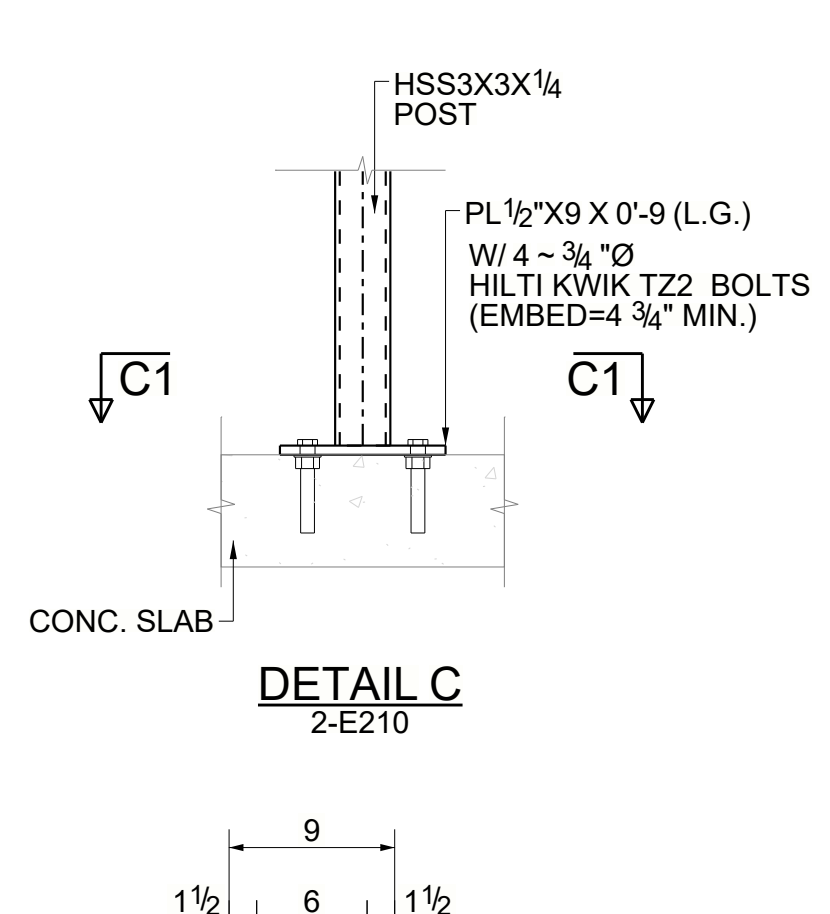


DETAIL C
2-E210

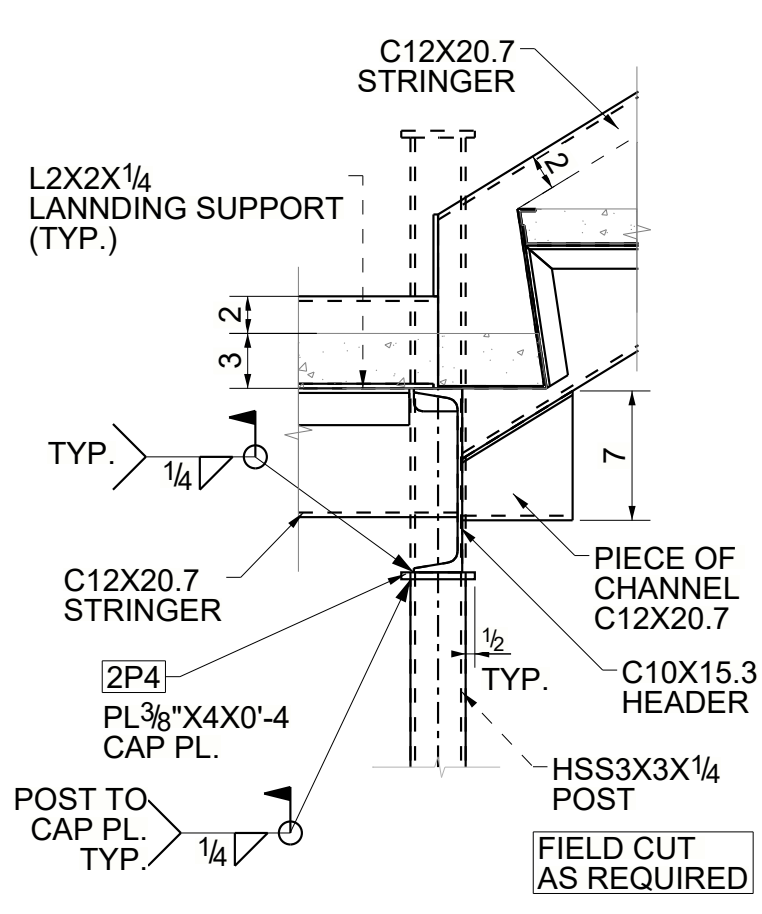


DETAIL D
2-E210

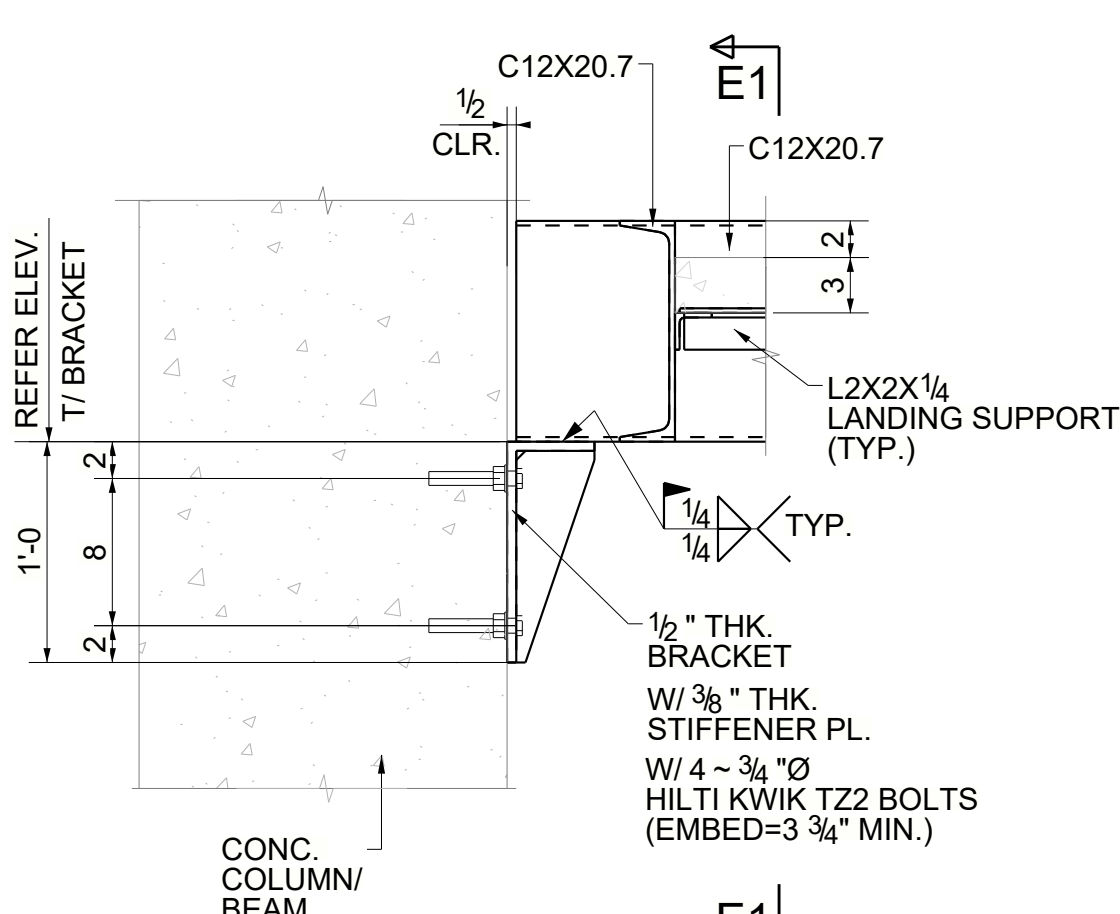


DETAIL E
2-E210

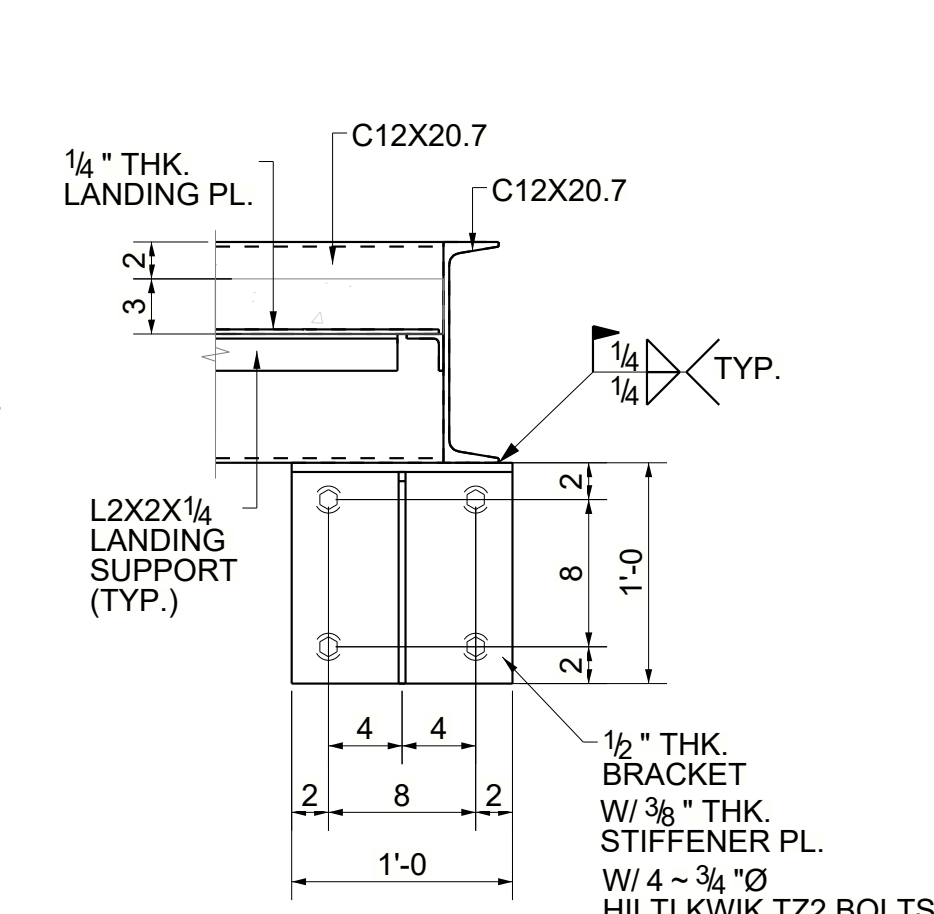


SECTION E1 - E1

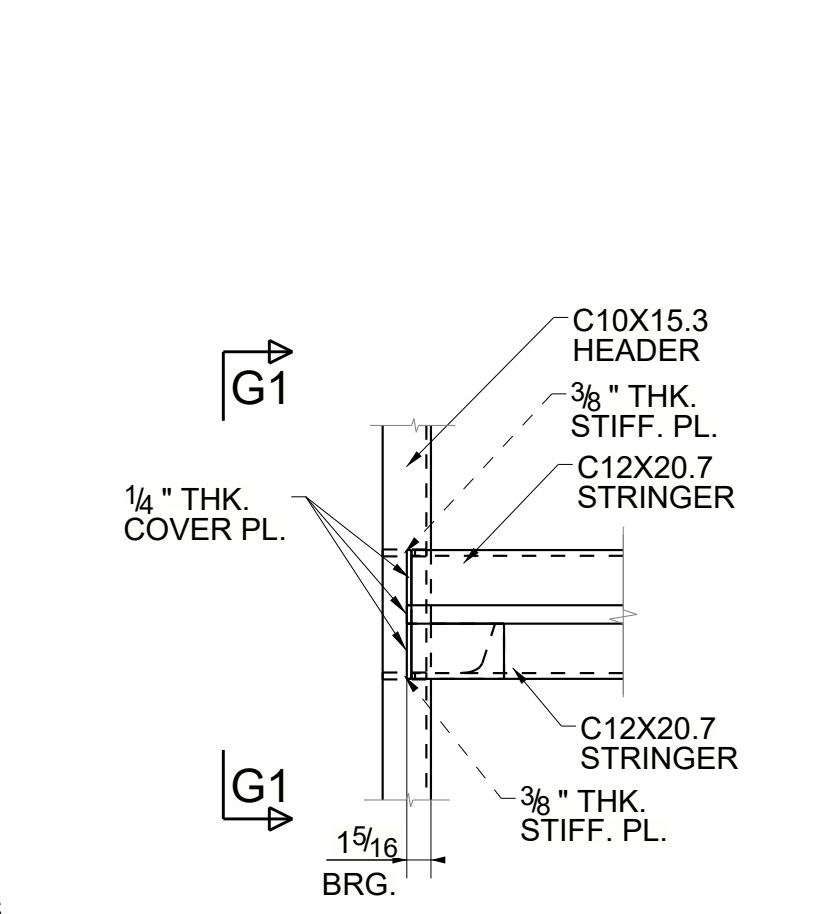


DETAIL G
2-E203

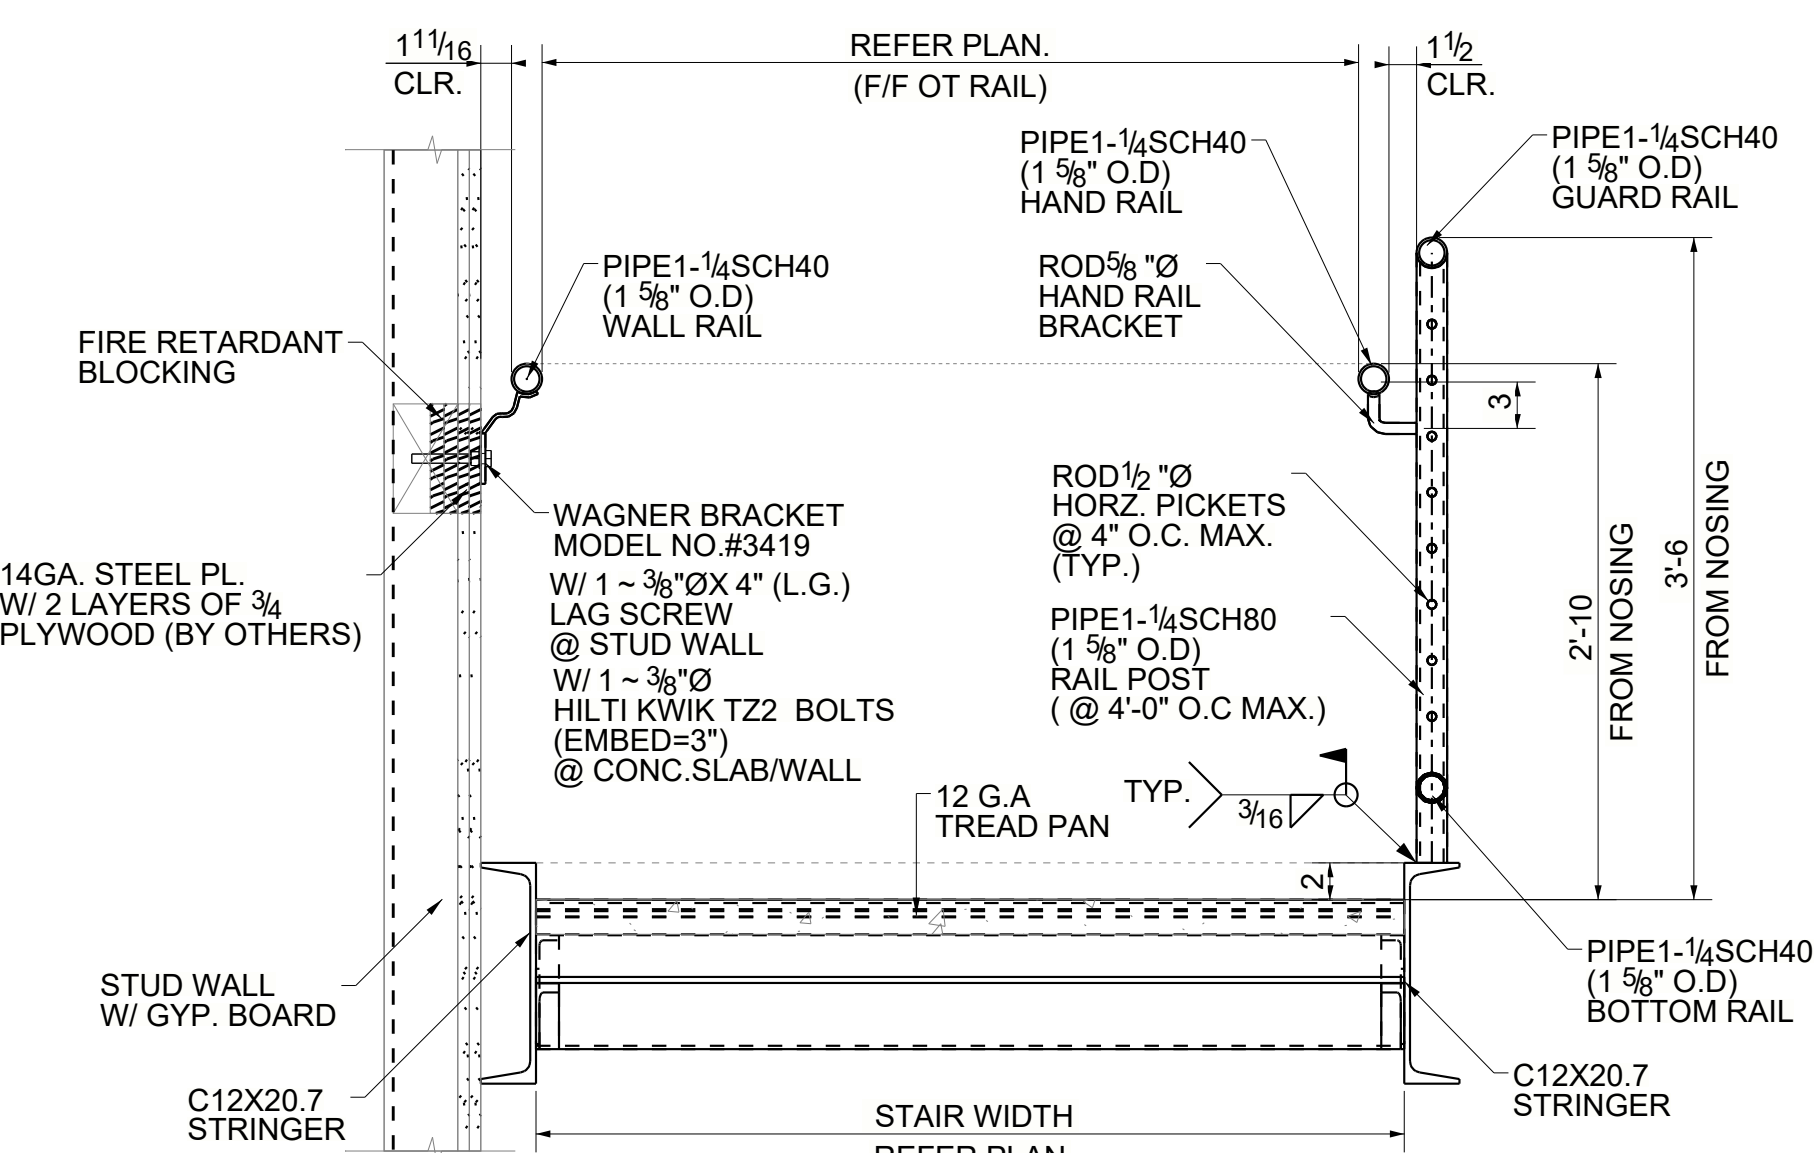


TYPICAL STRINGER RAIL DETAIL
(REFER :SECTION AT STRINGER : 17/A403)

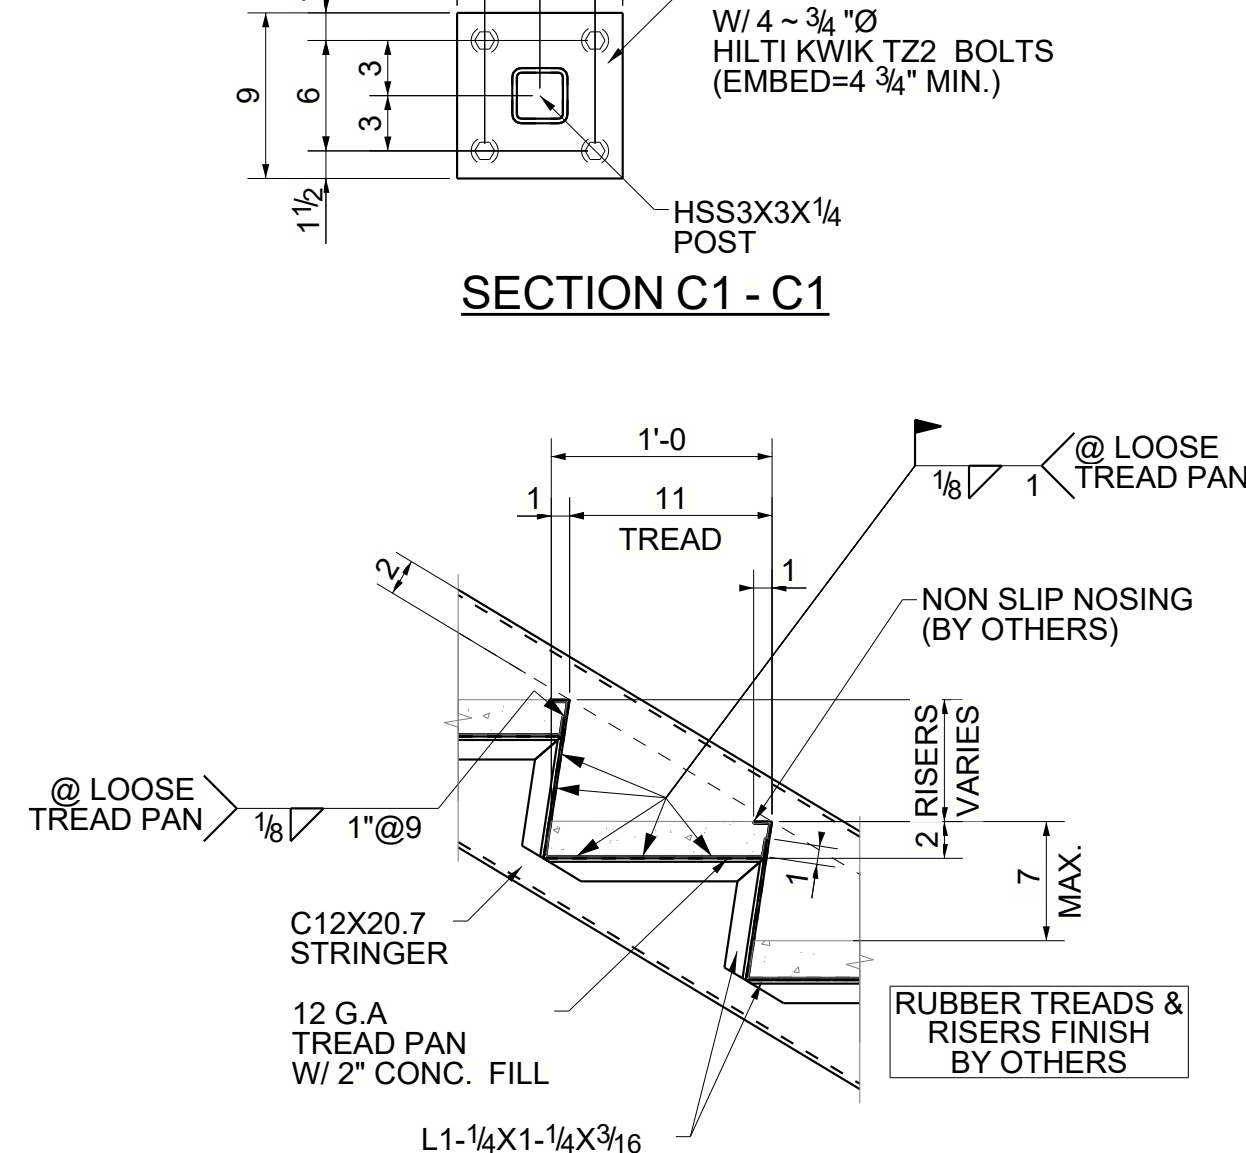


TYPICAL STRINGER TREAD DETAIL

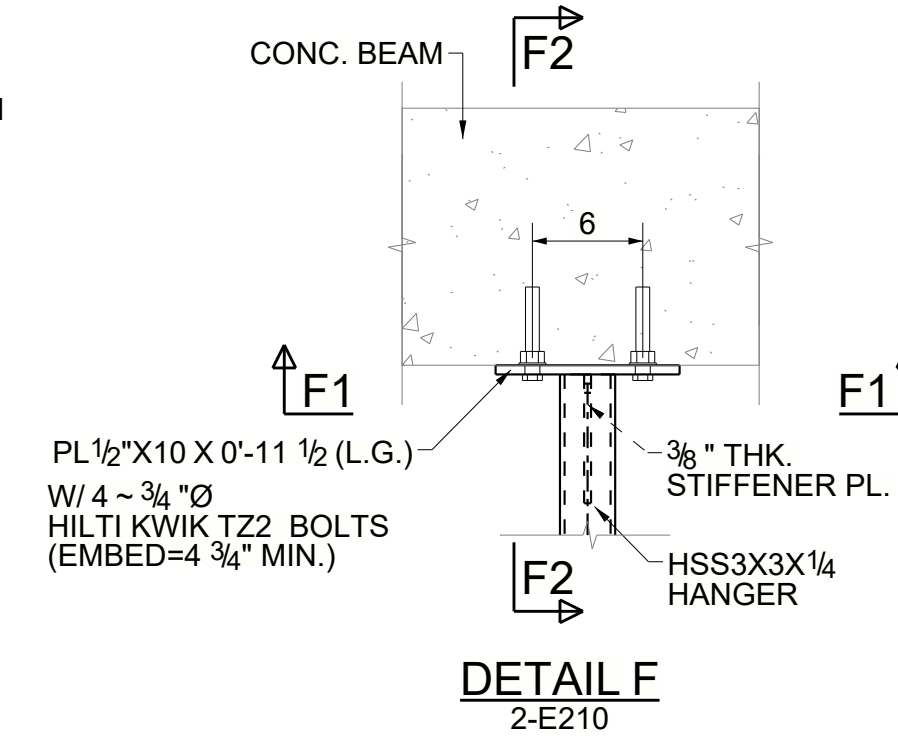


DETAIL F
2-E210

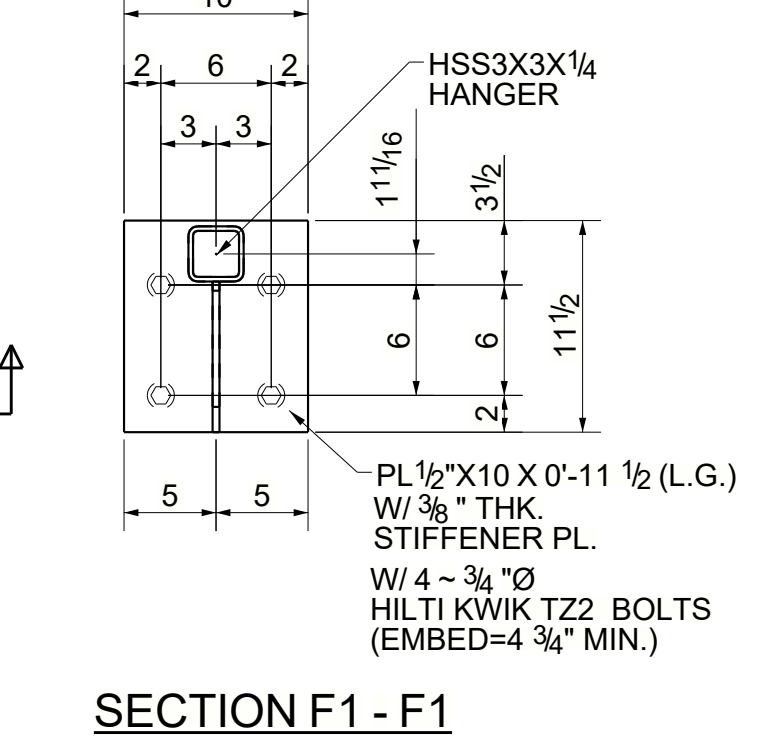


SECTION F1 - F1

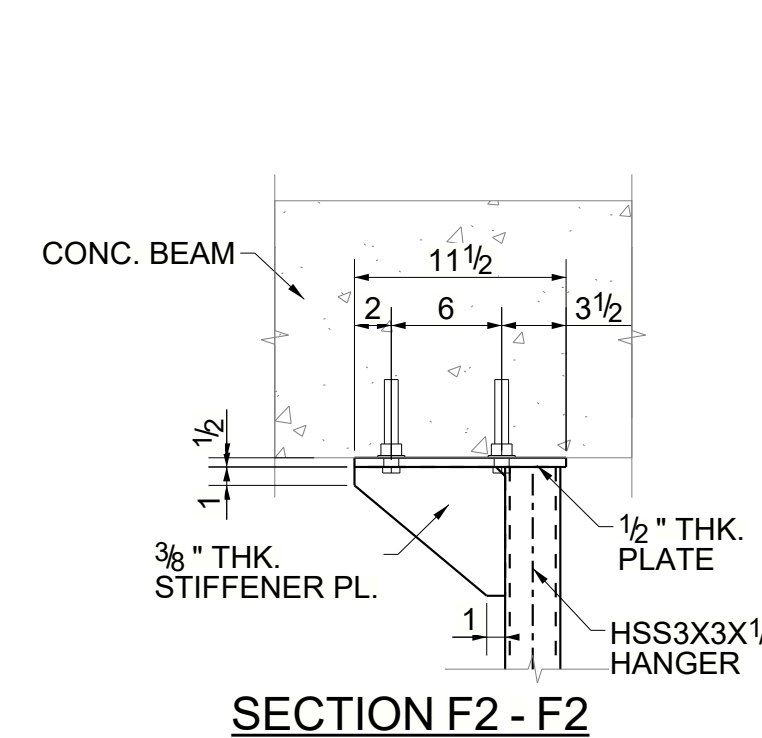


SECTION F2 - F2

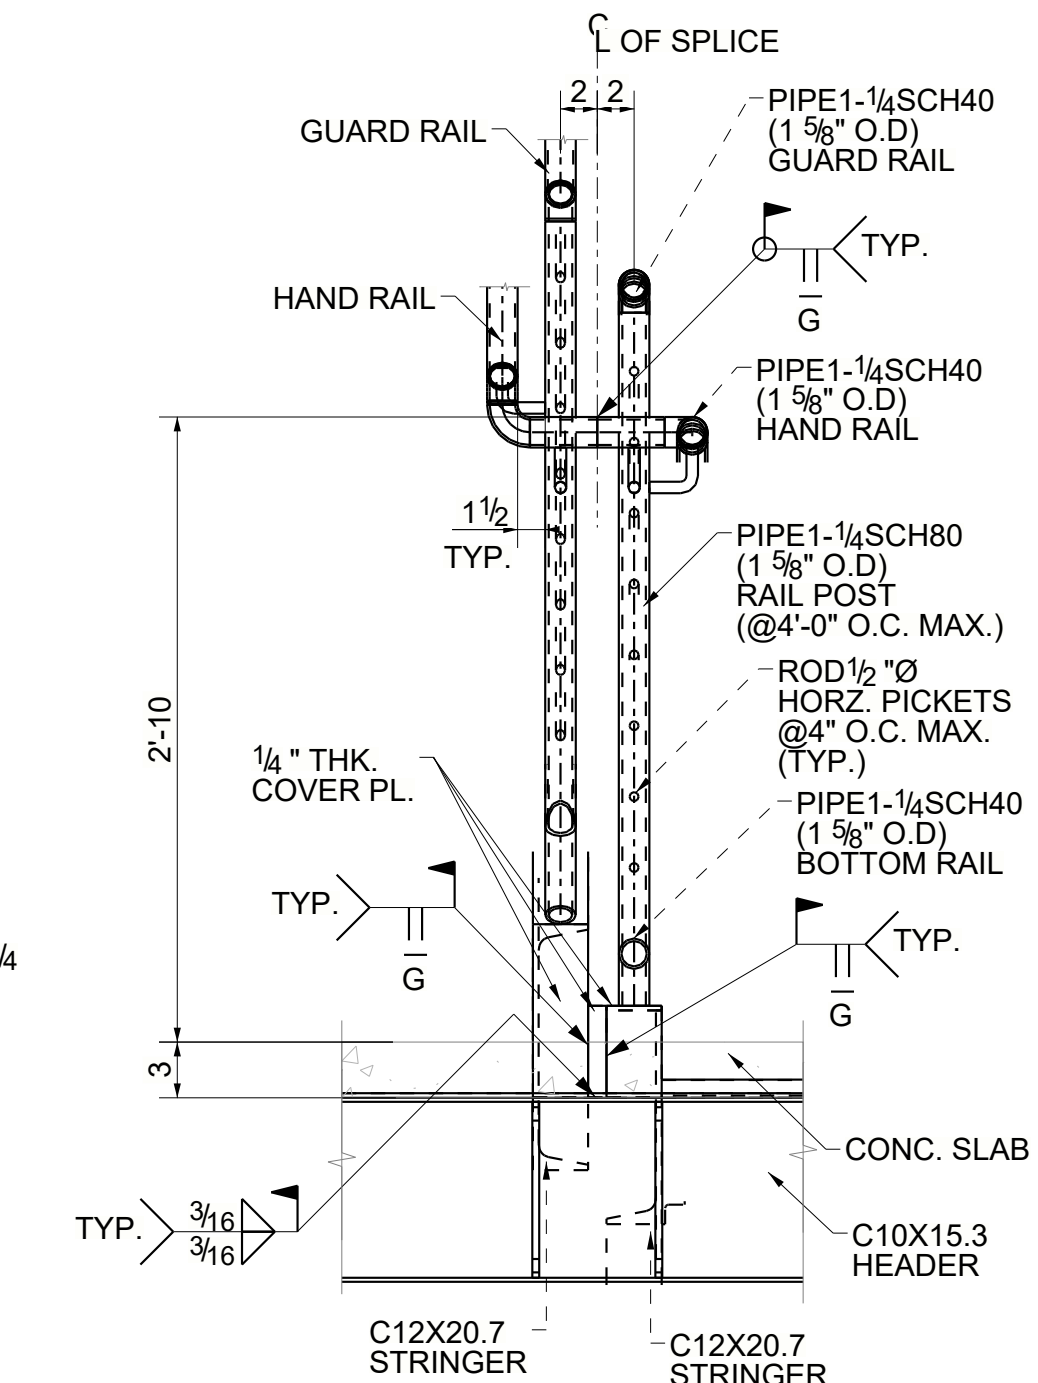


SECTION G1 - G1

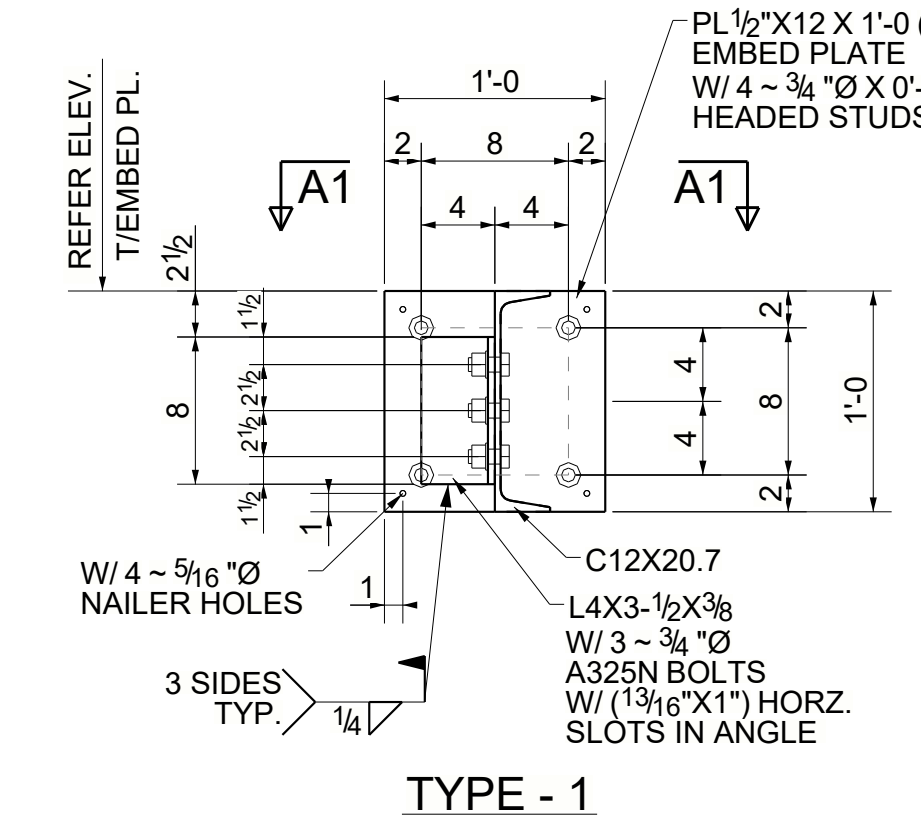


TYPE - 1

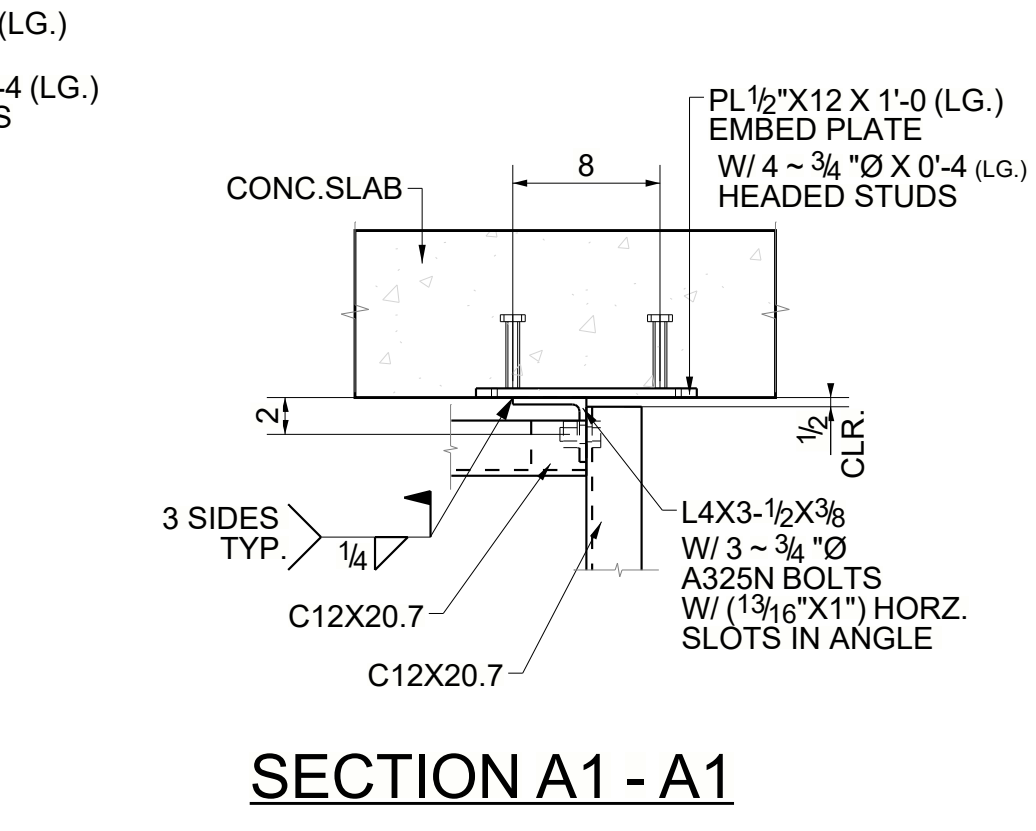


SECTION A1 - A1

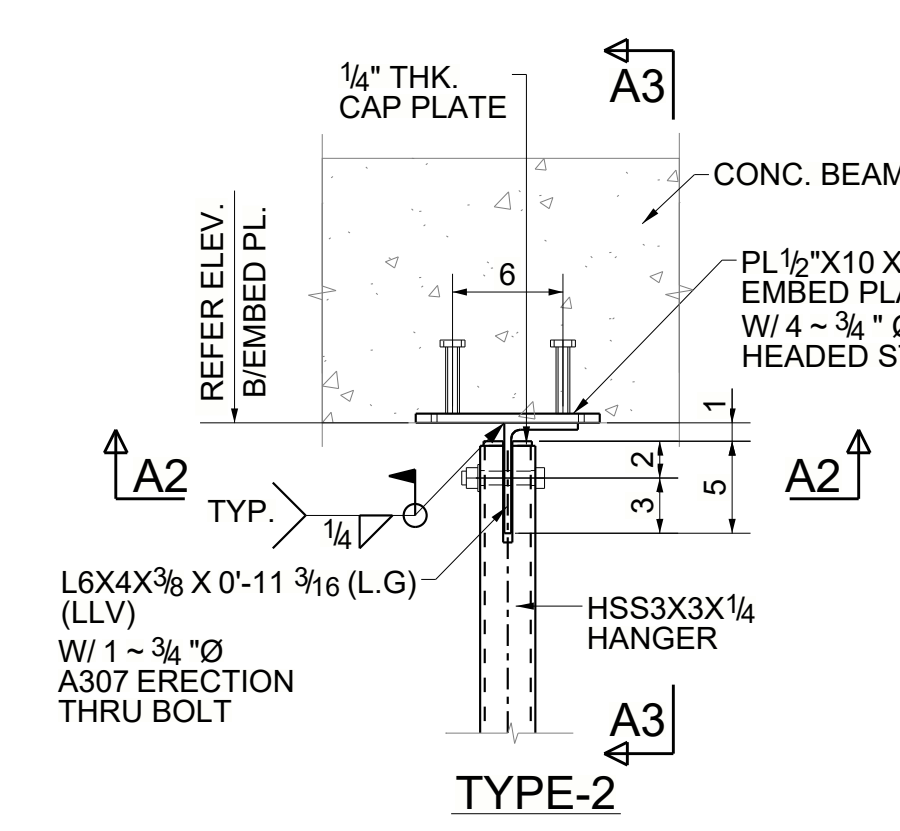

TYPE-2

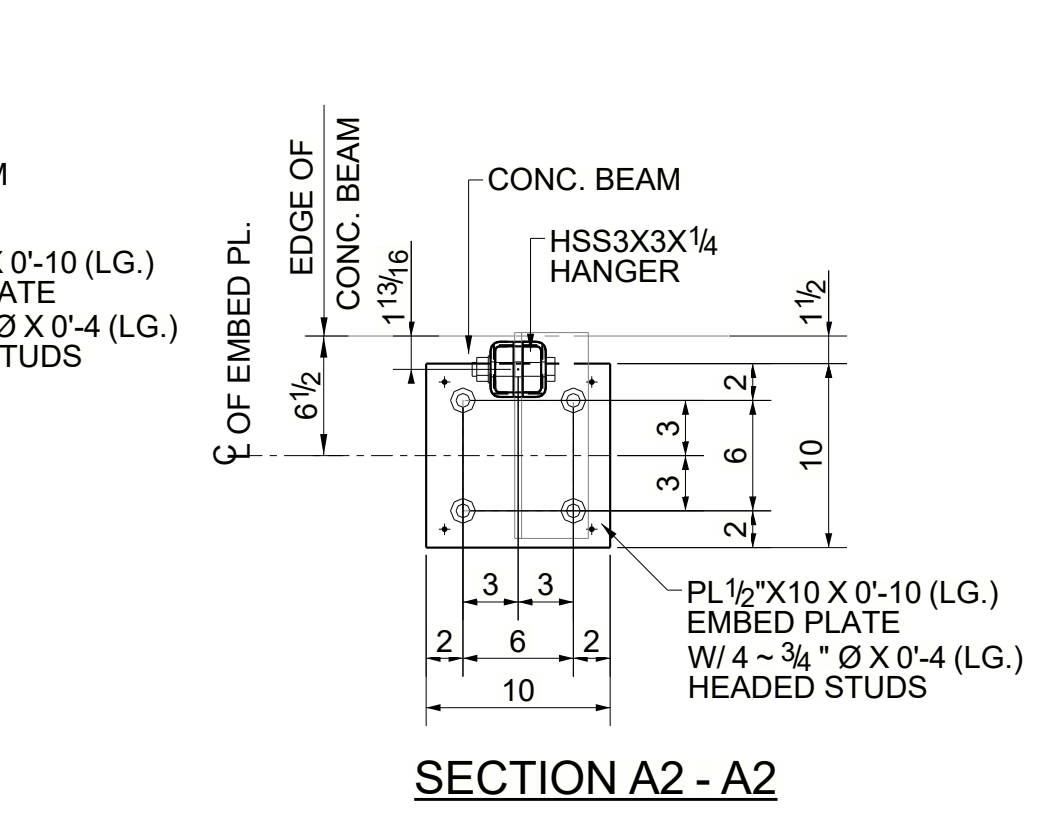


SECTION A2 - A2

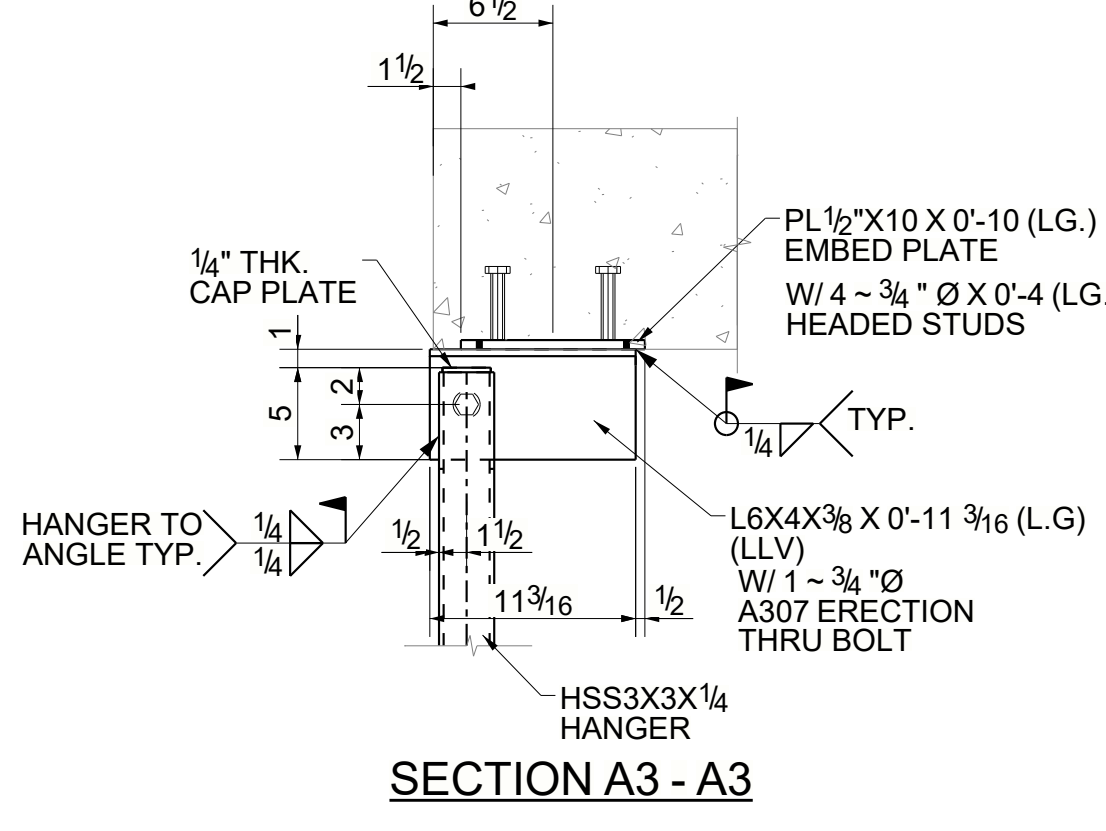


SECTION A3 - A3


- NOTES:-**
1. REFER SHEET 2-E201 FOR 3D VIEW
 2. REFER SHEET 2-E202 TO 2-E205 FOR PLAN
 3. REFER SHEET 2-E206 TO 2-E211 FOR ELEVATION

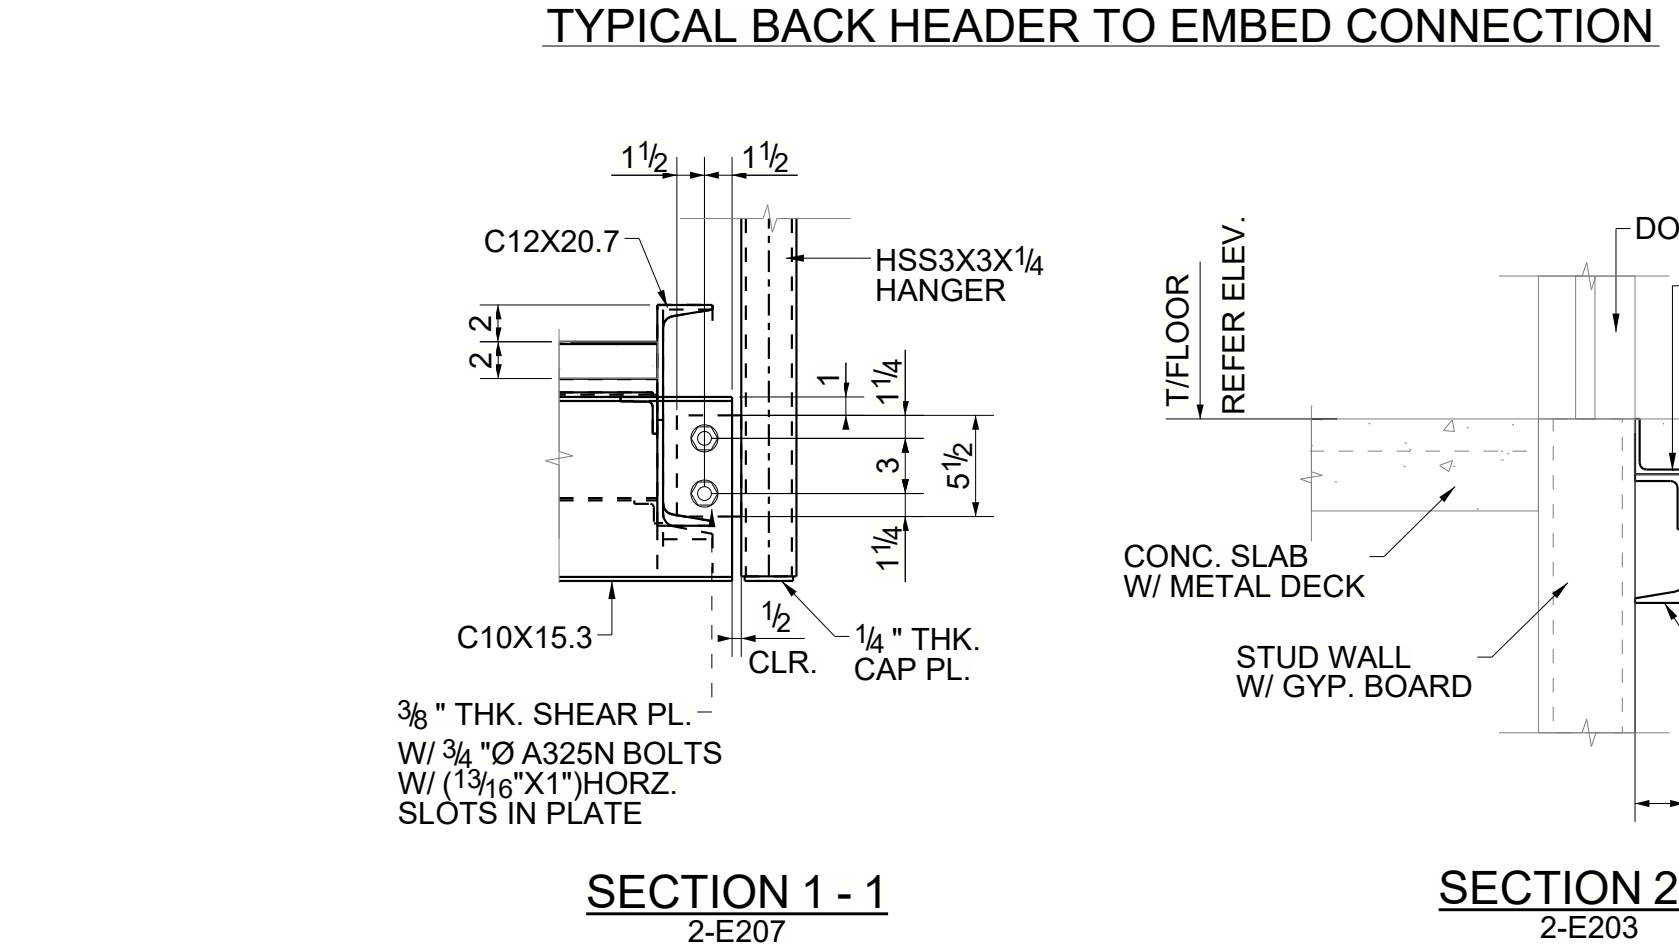


SECTION 1 - 1
2-E207

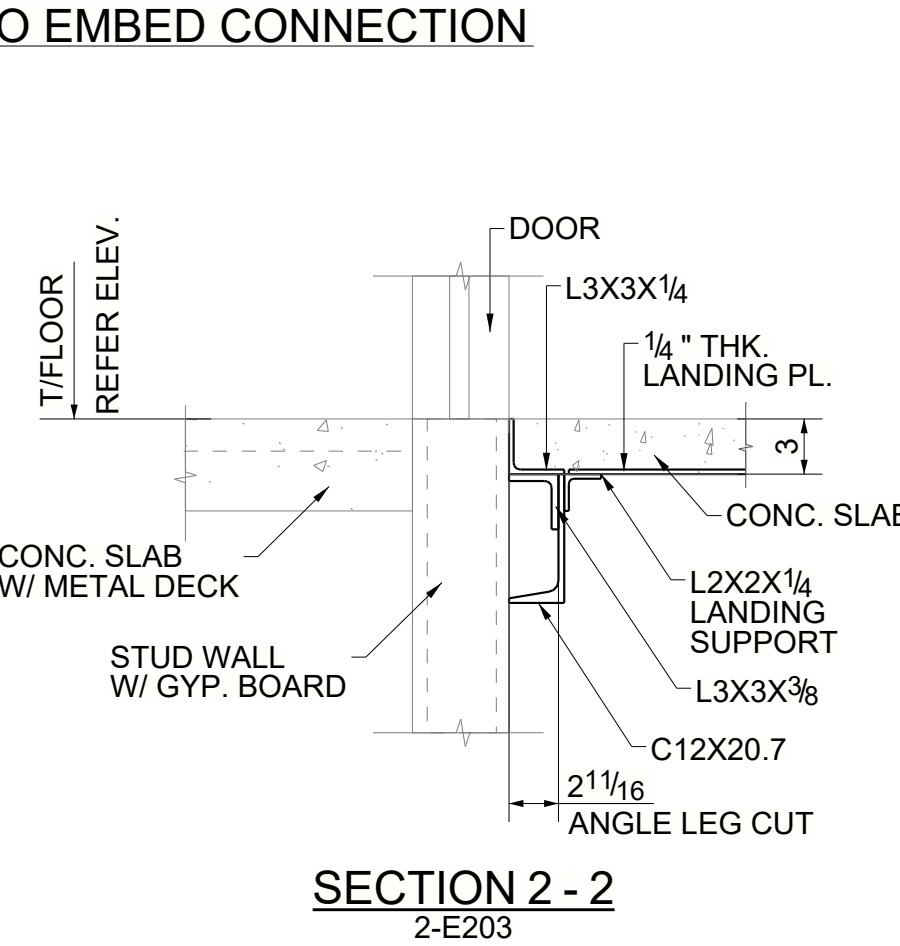


















SECTION 2 - 2
2-E203

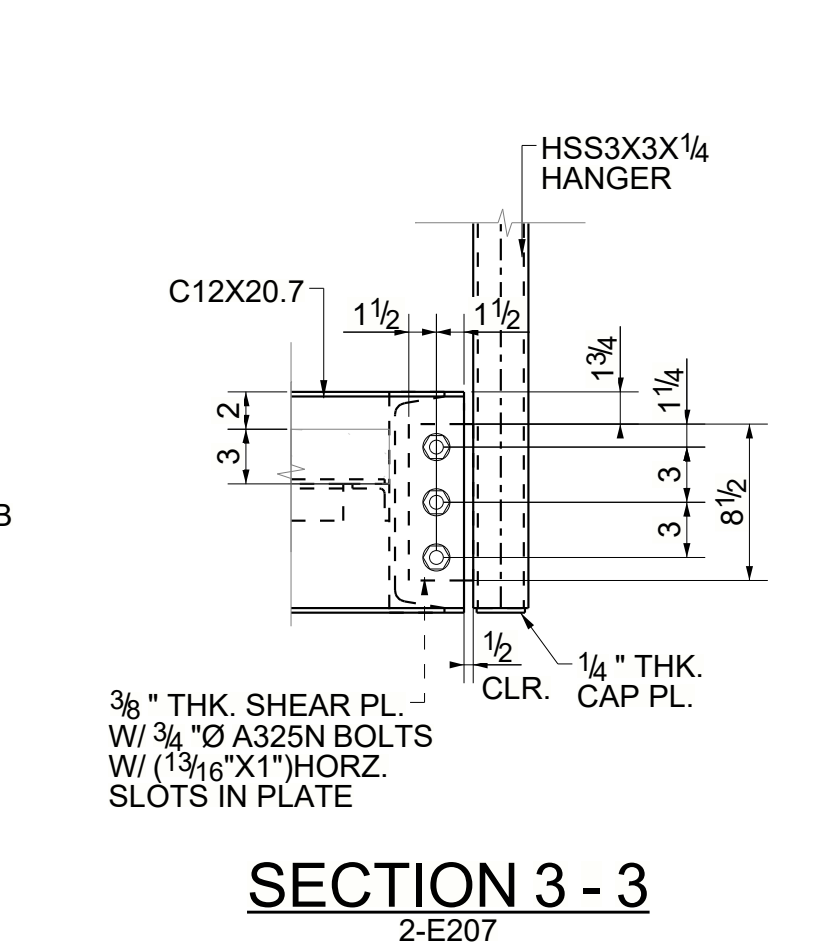


SECTION 3 - 3
2-E207

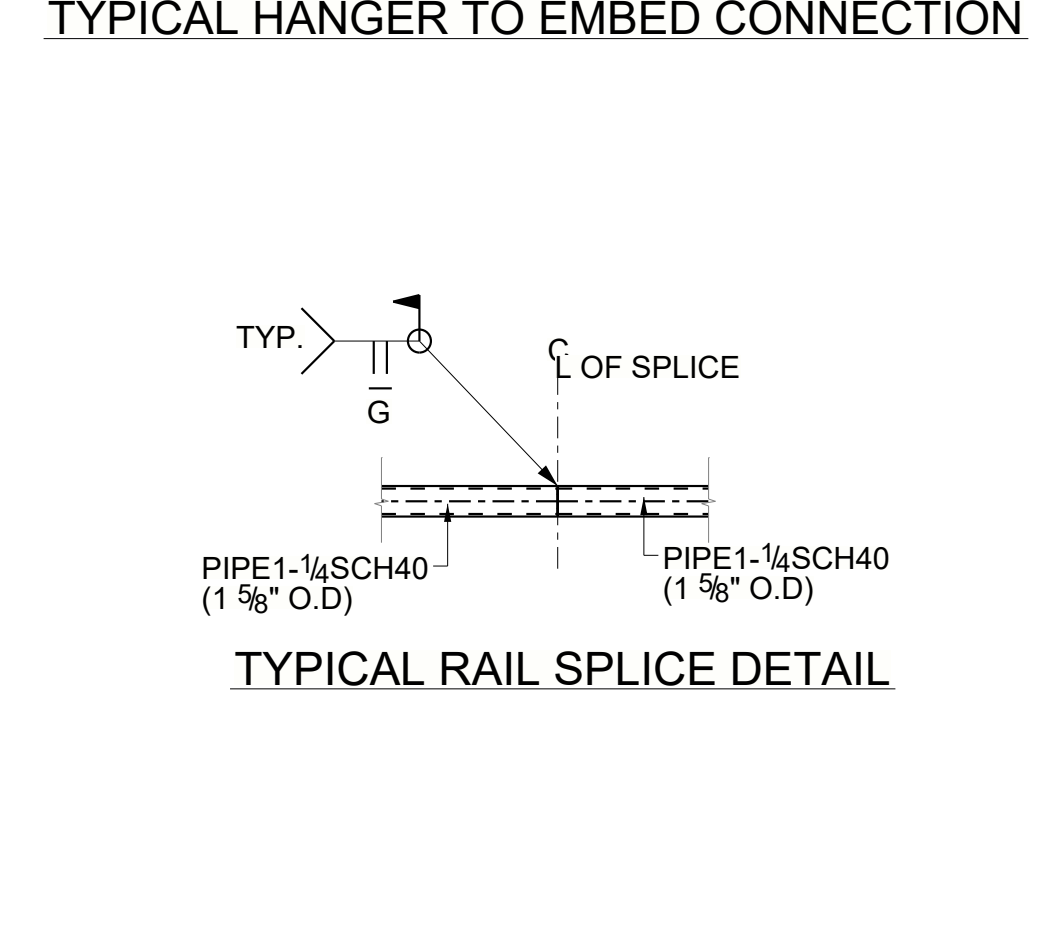

TYPICAL RAIL SPLICE DETAIL

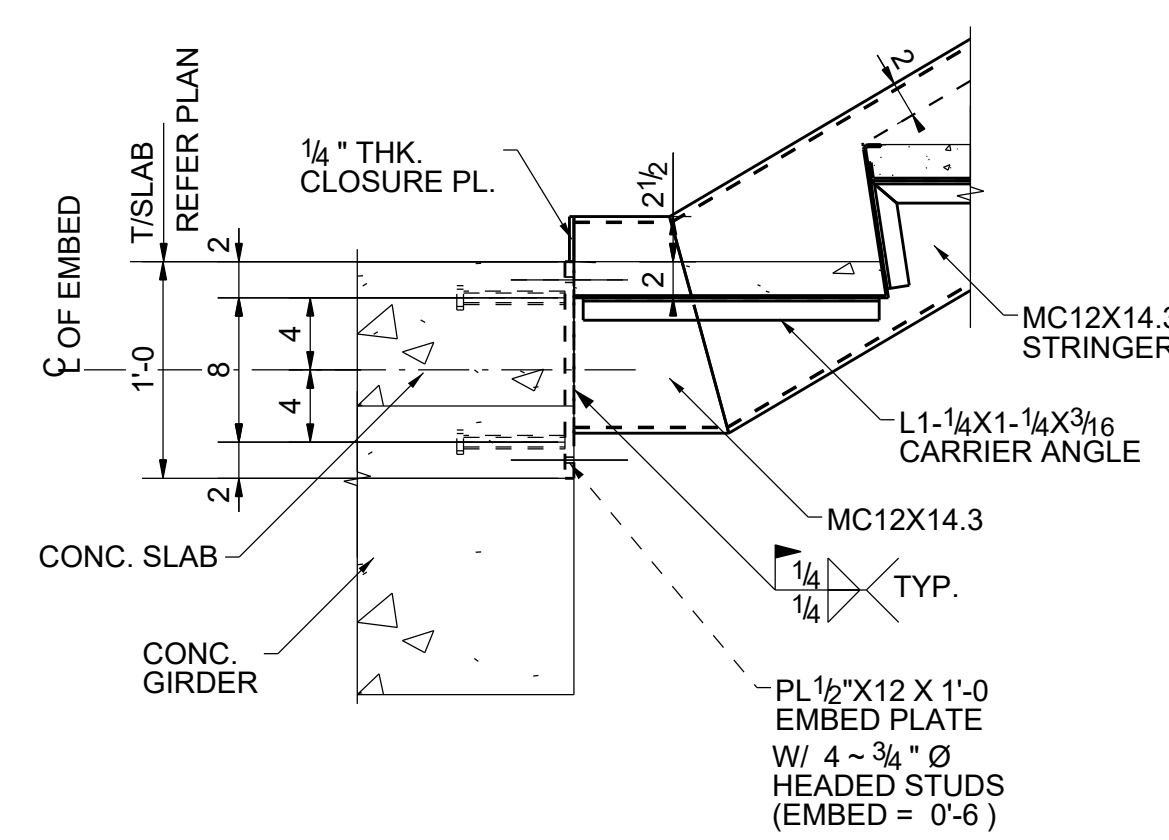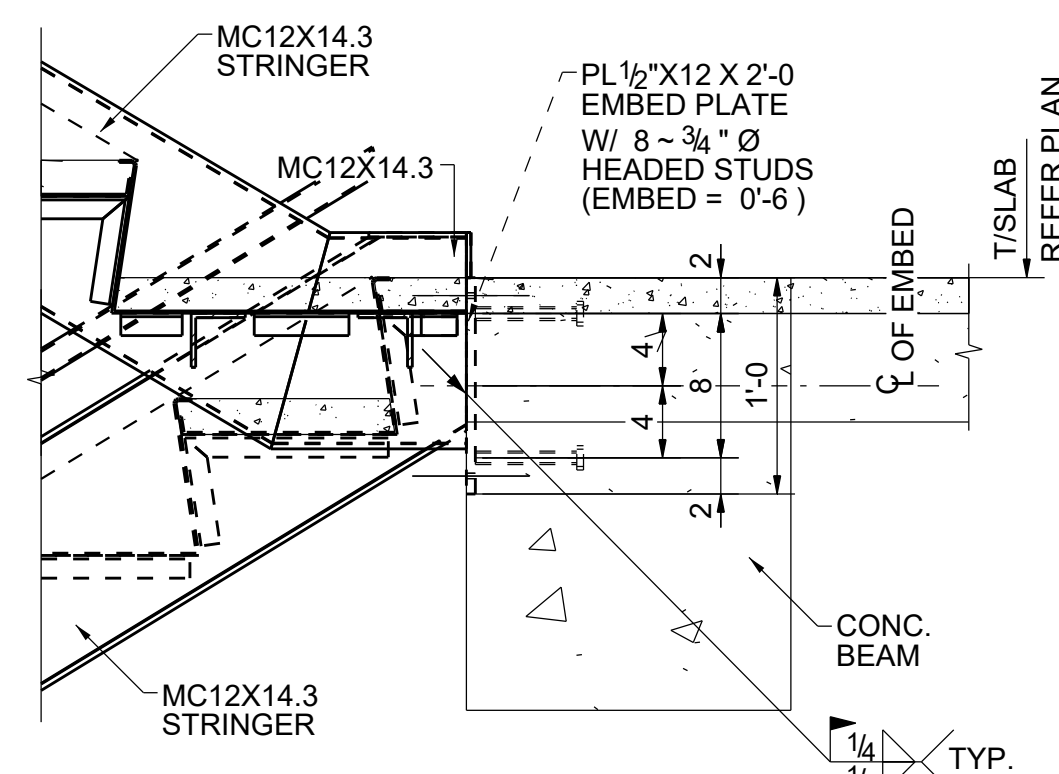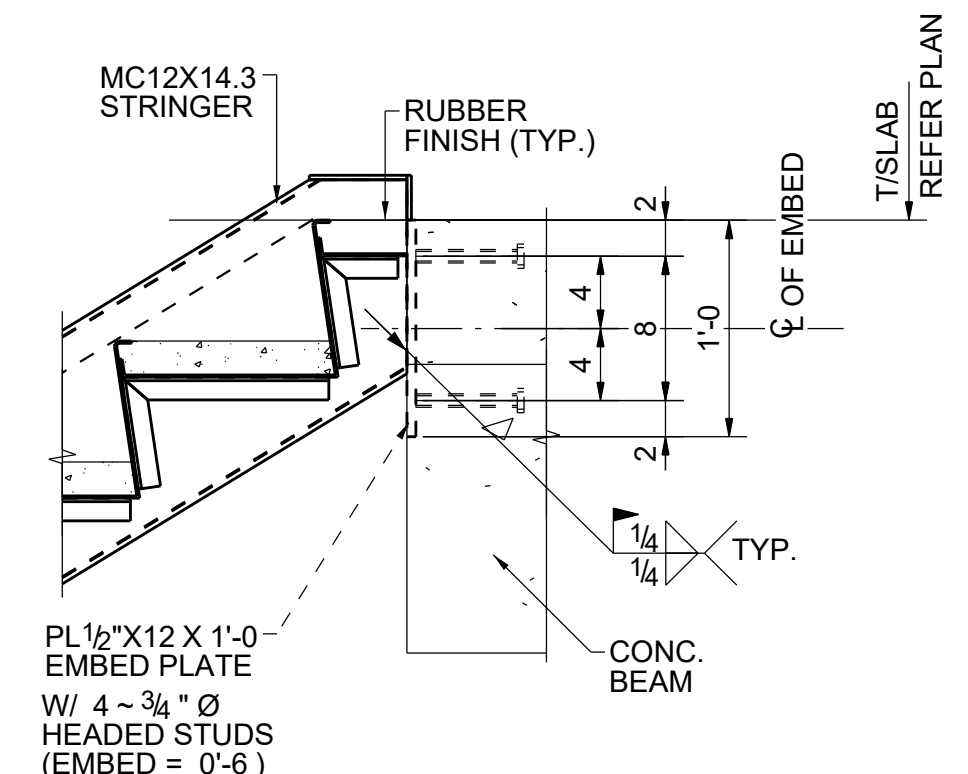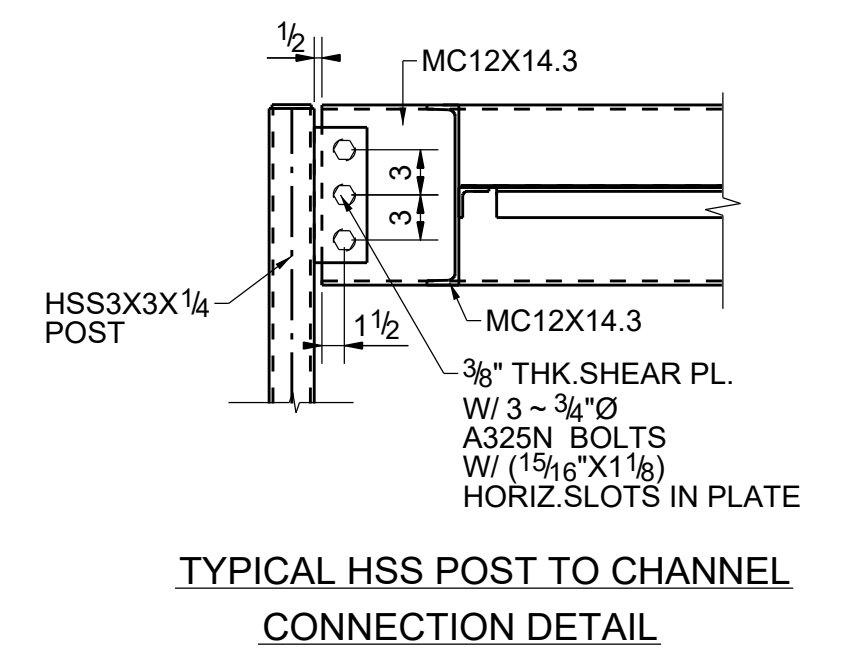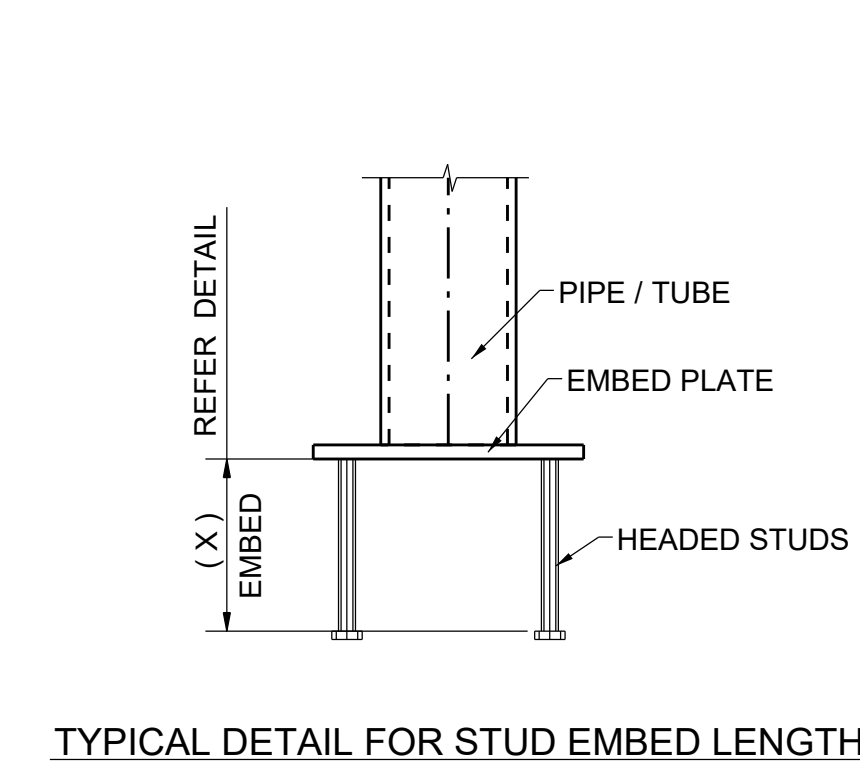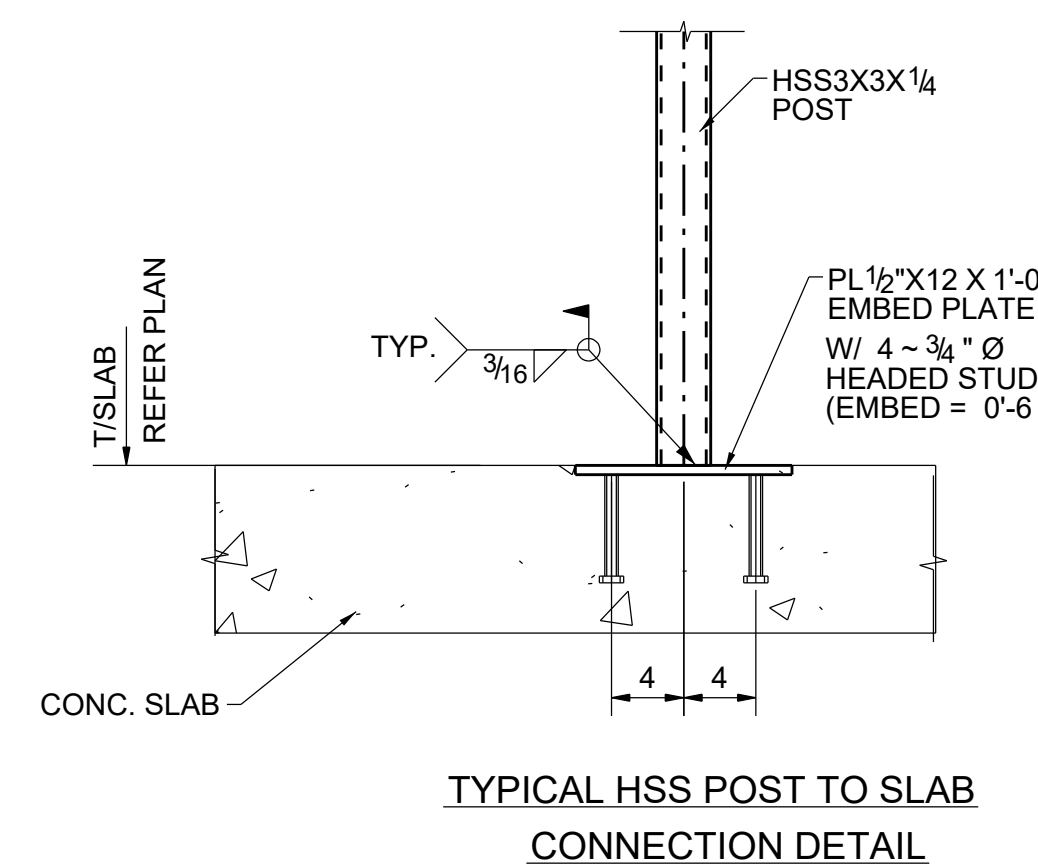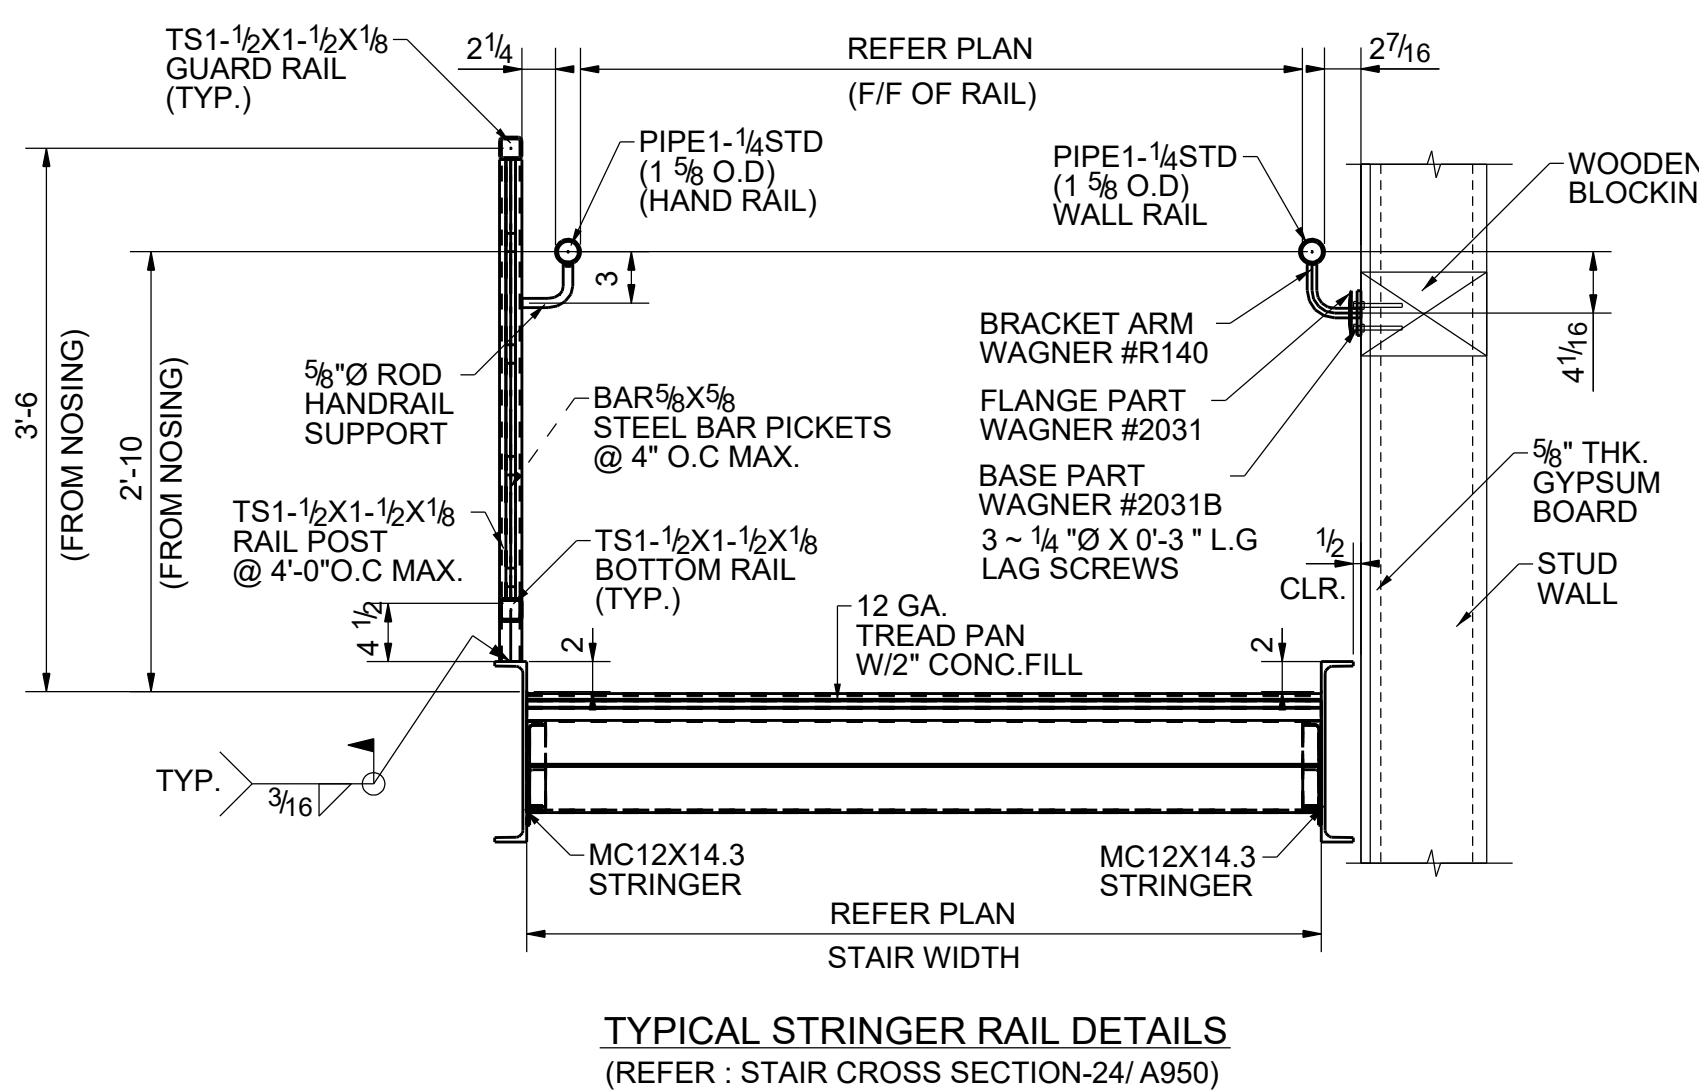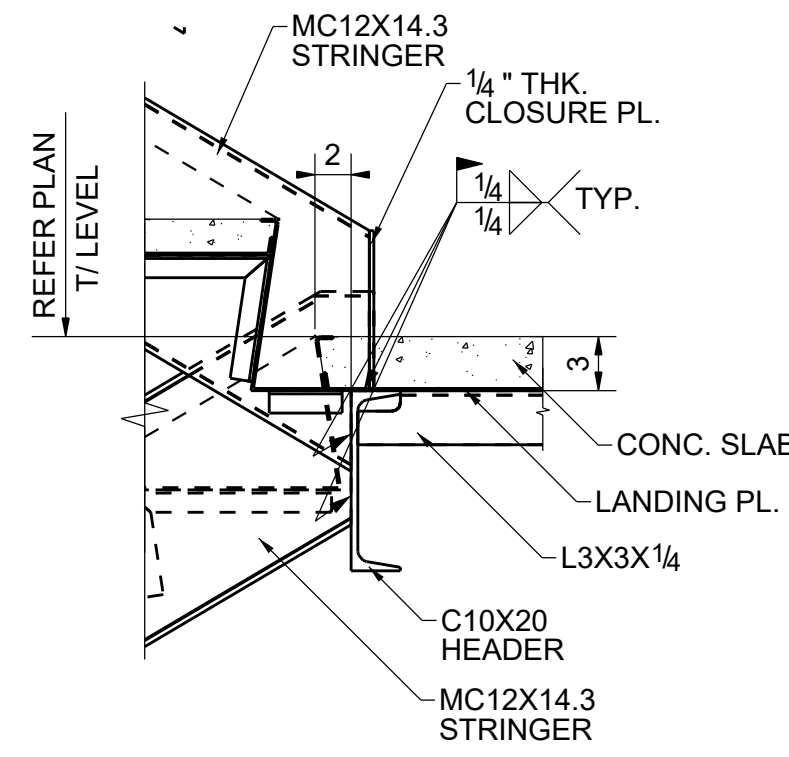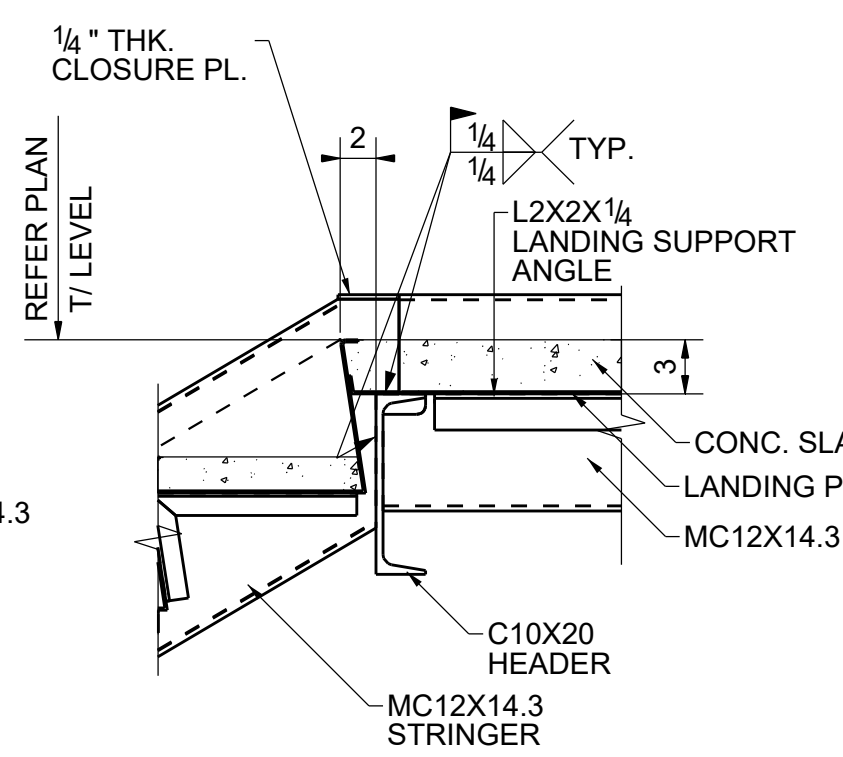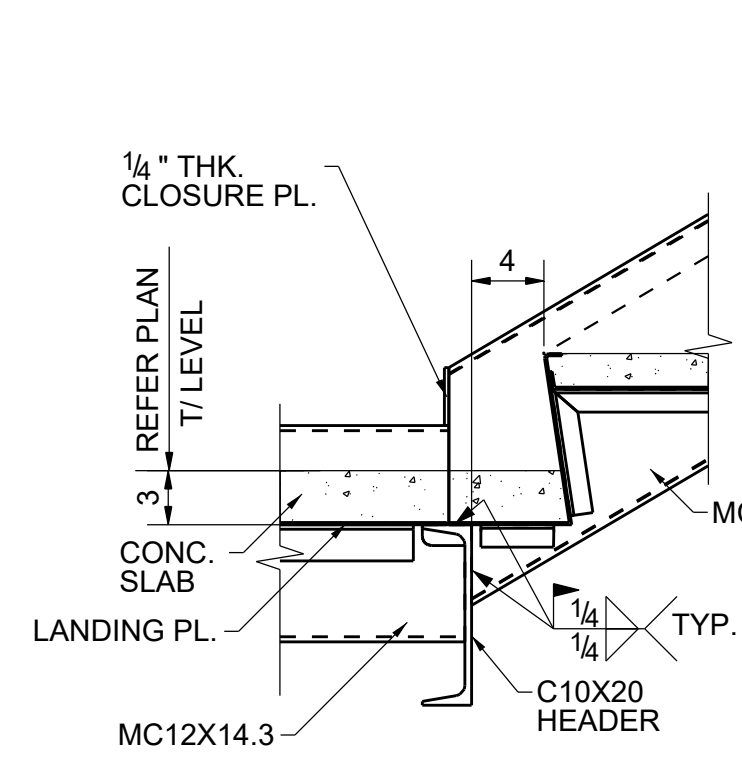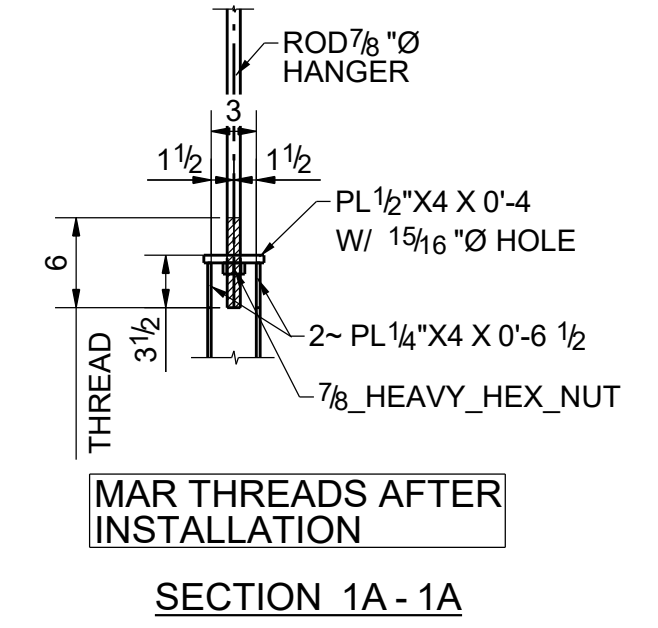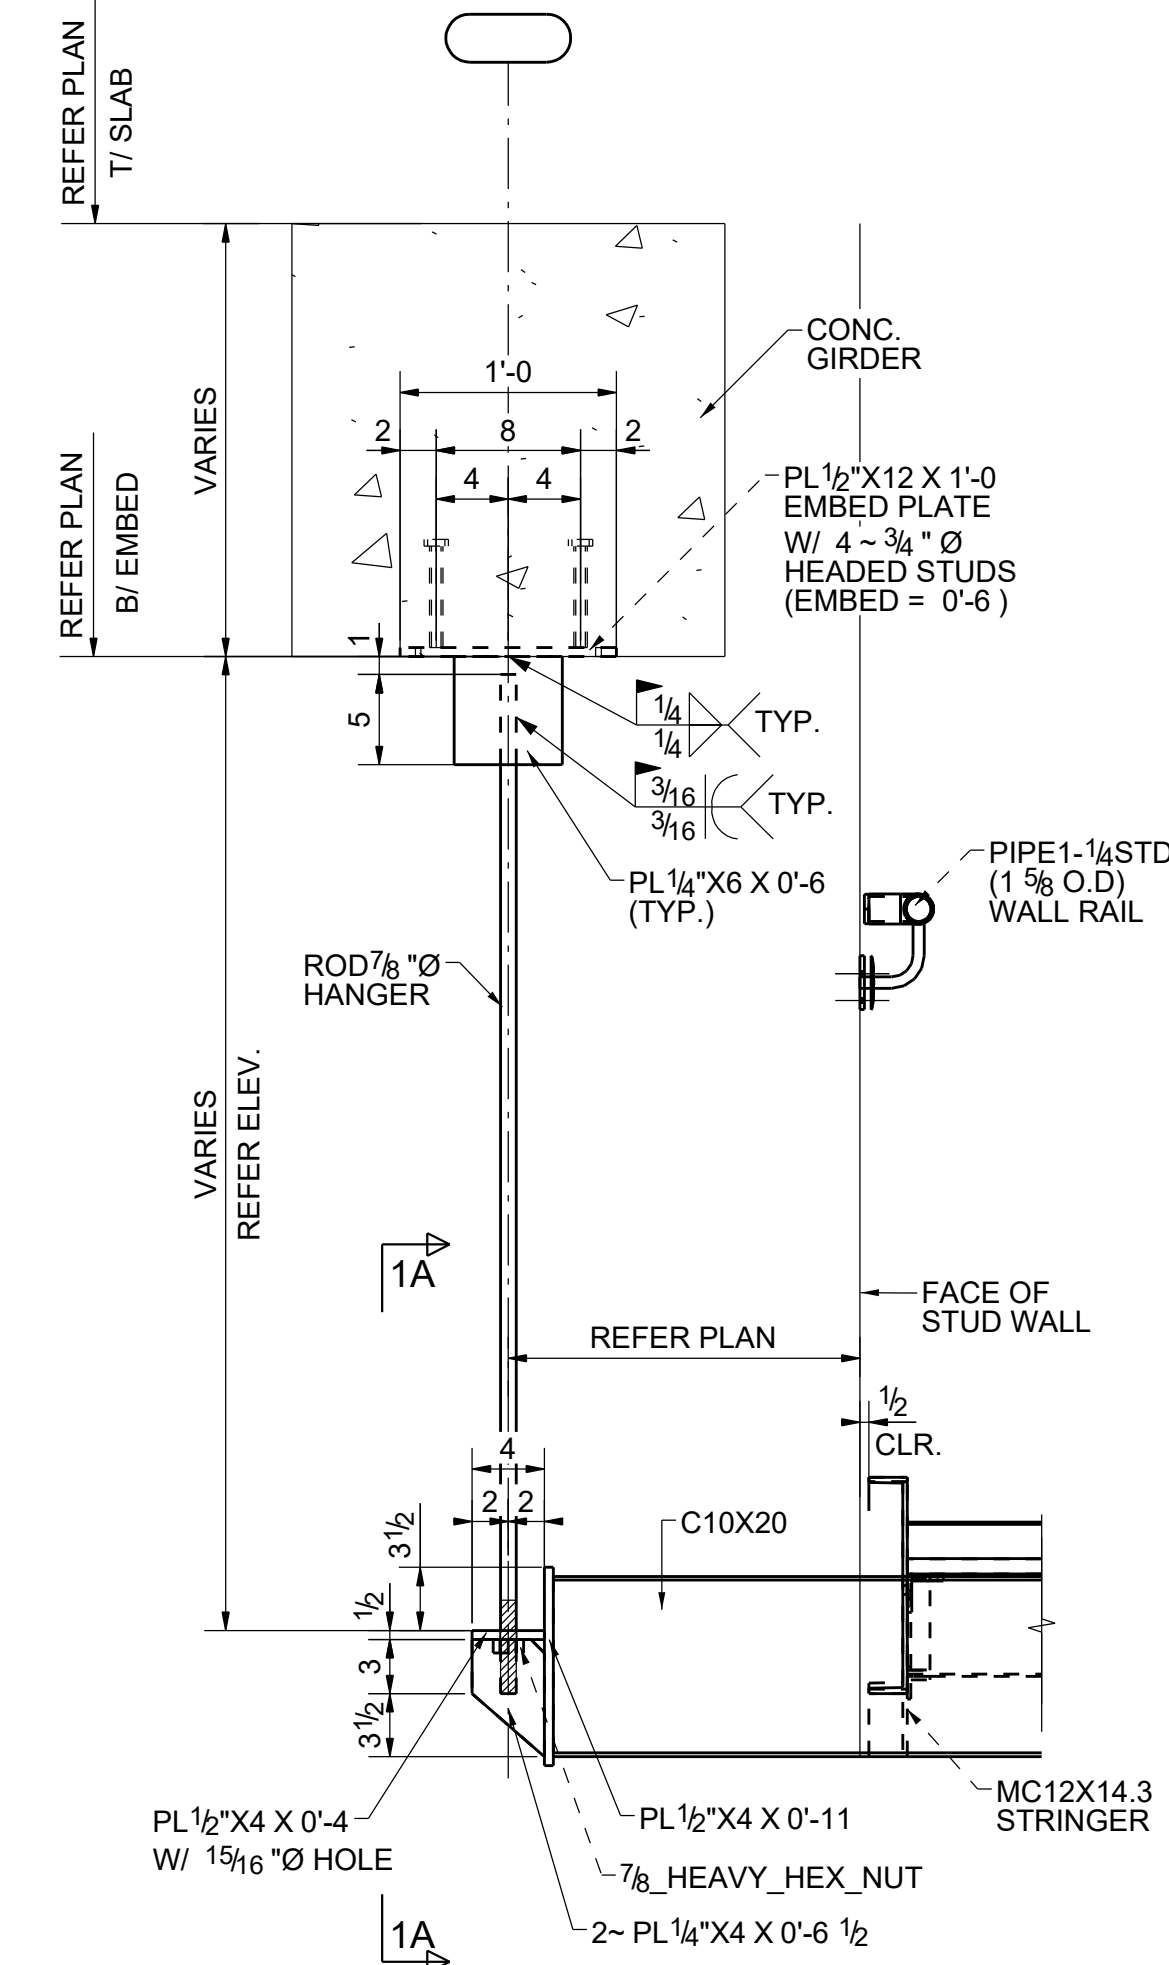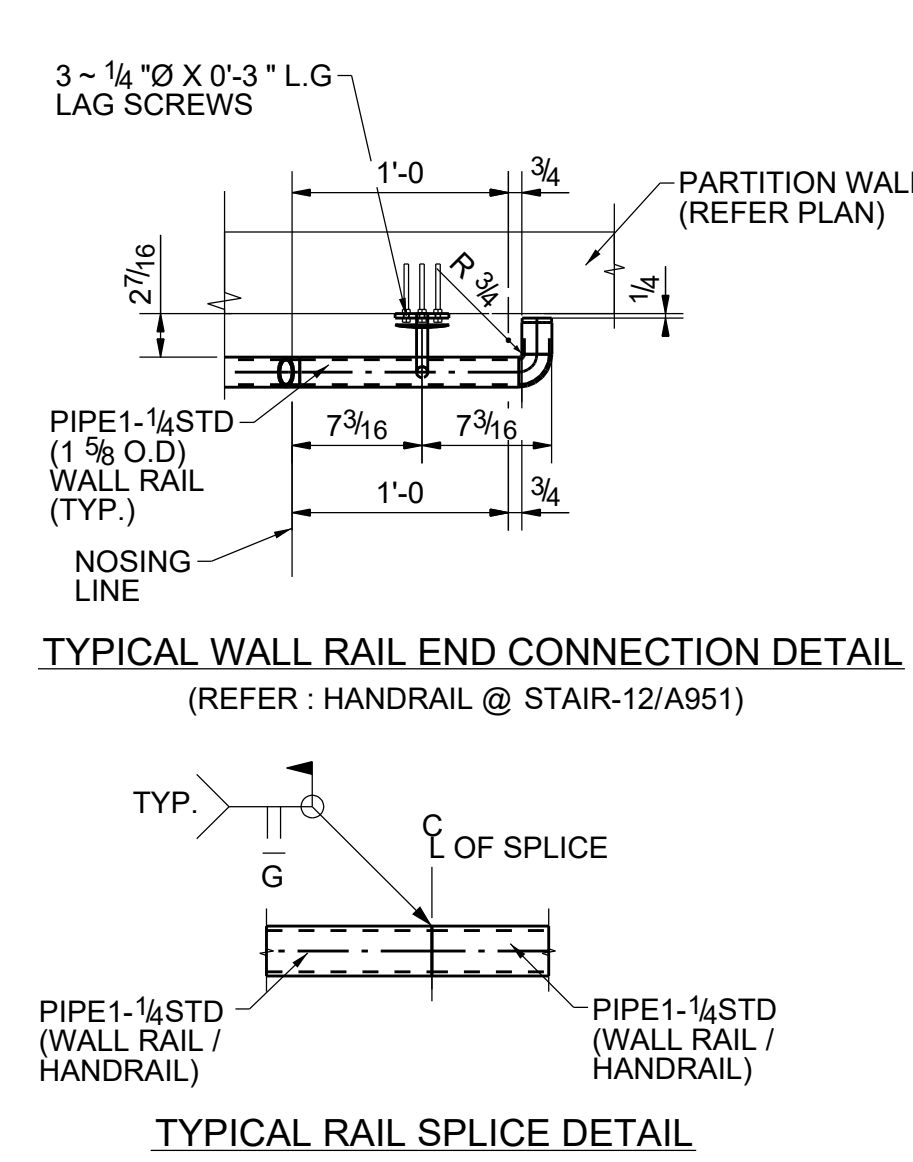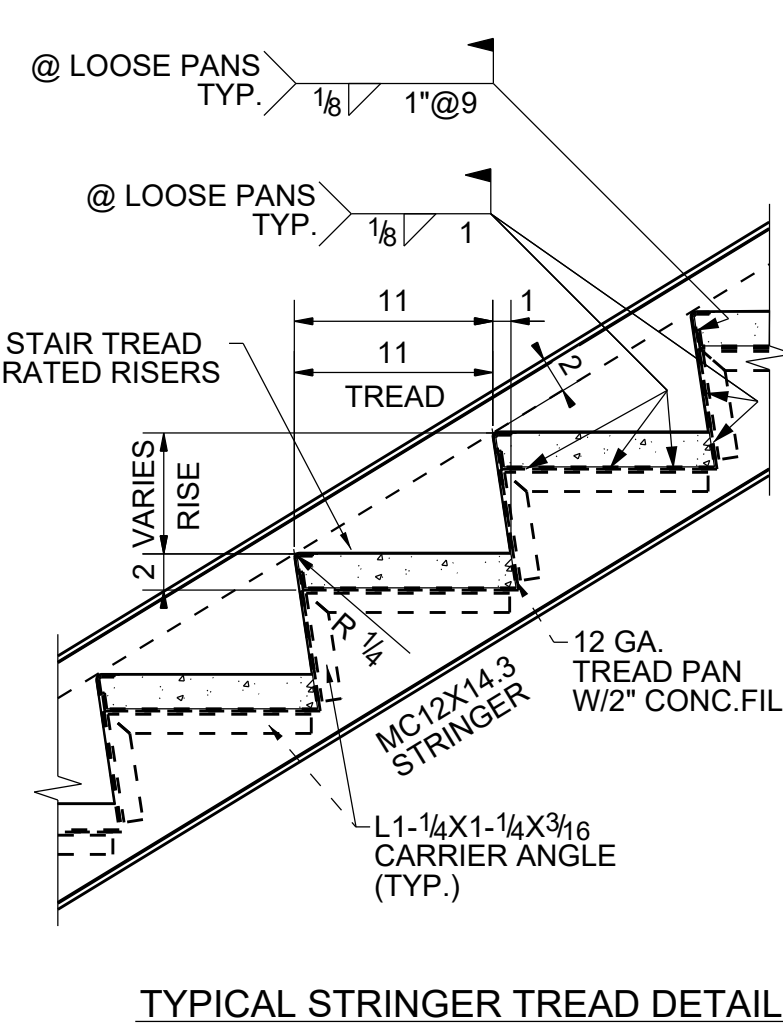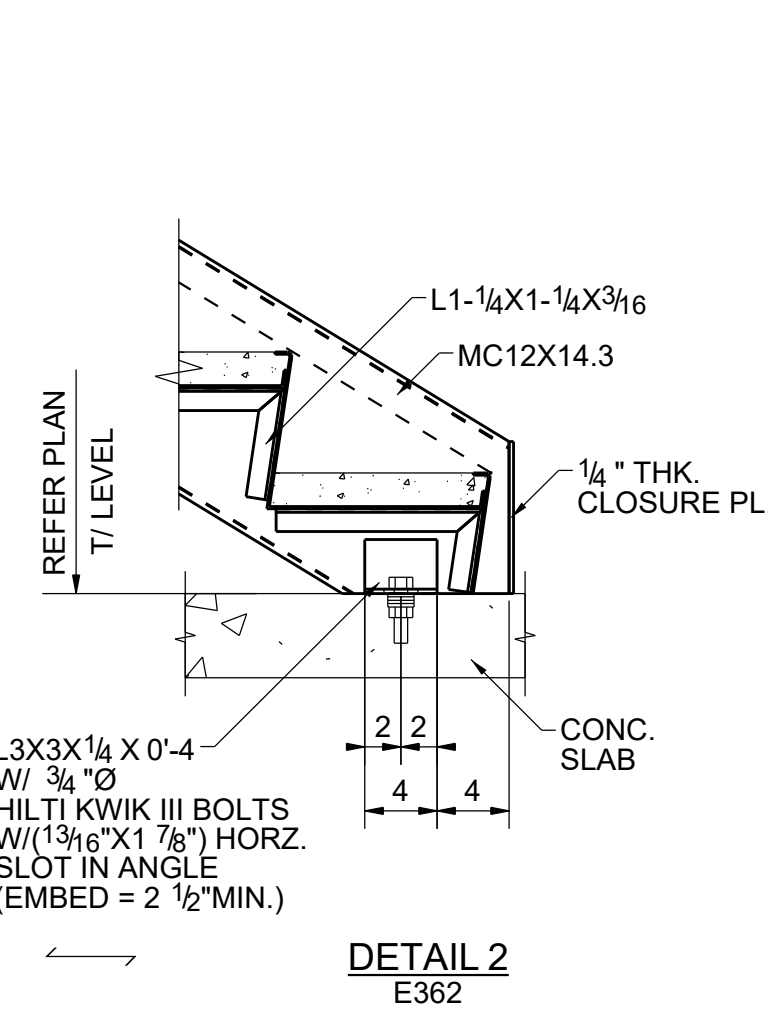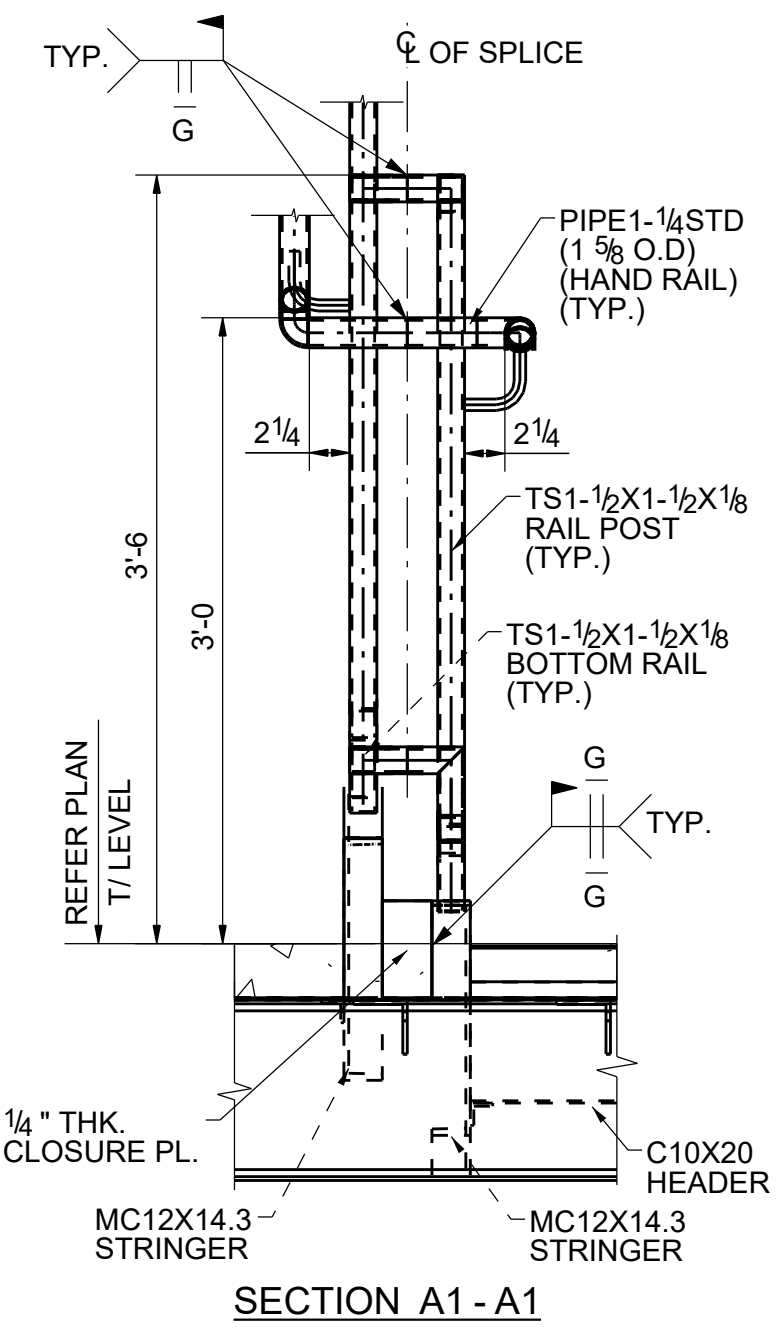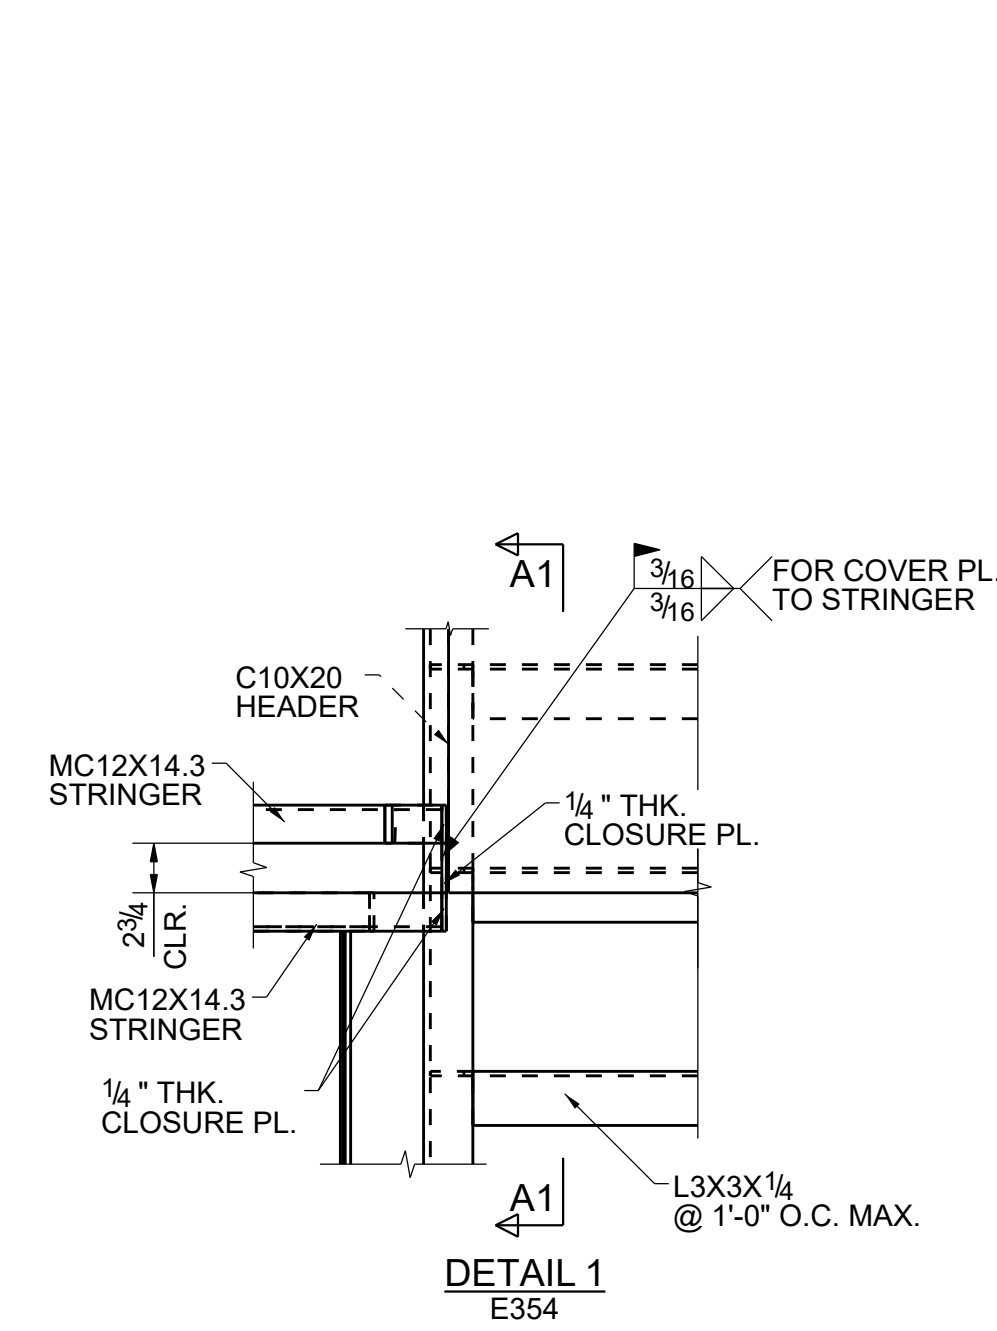

TYPICAL STRINGER TO EMBED CONNECTION DETAILS

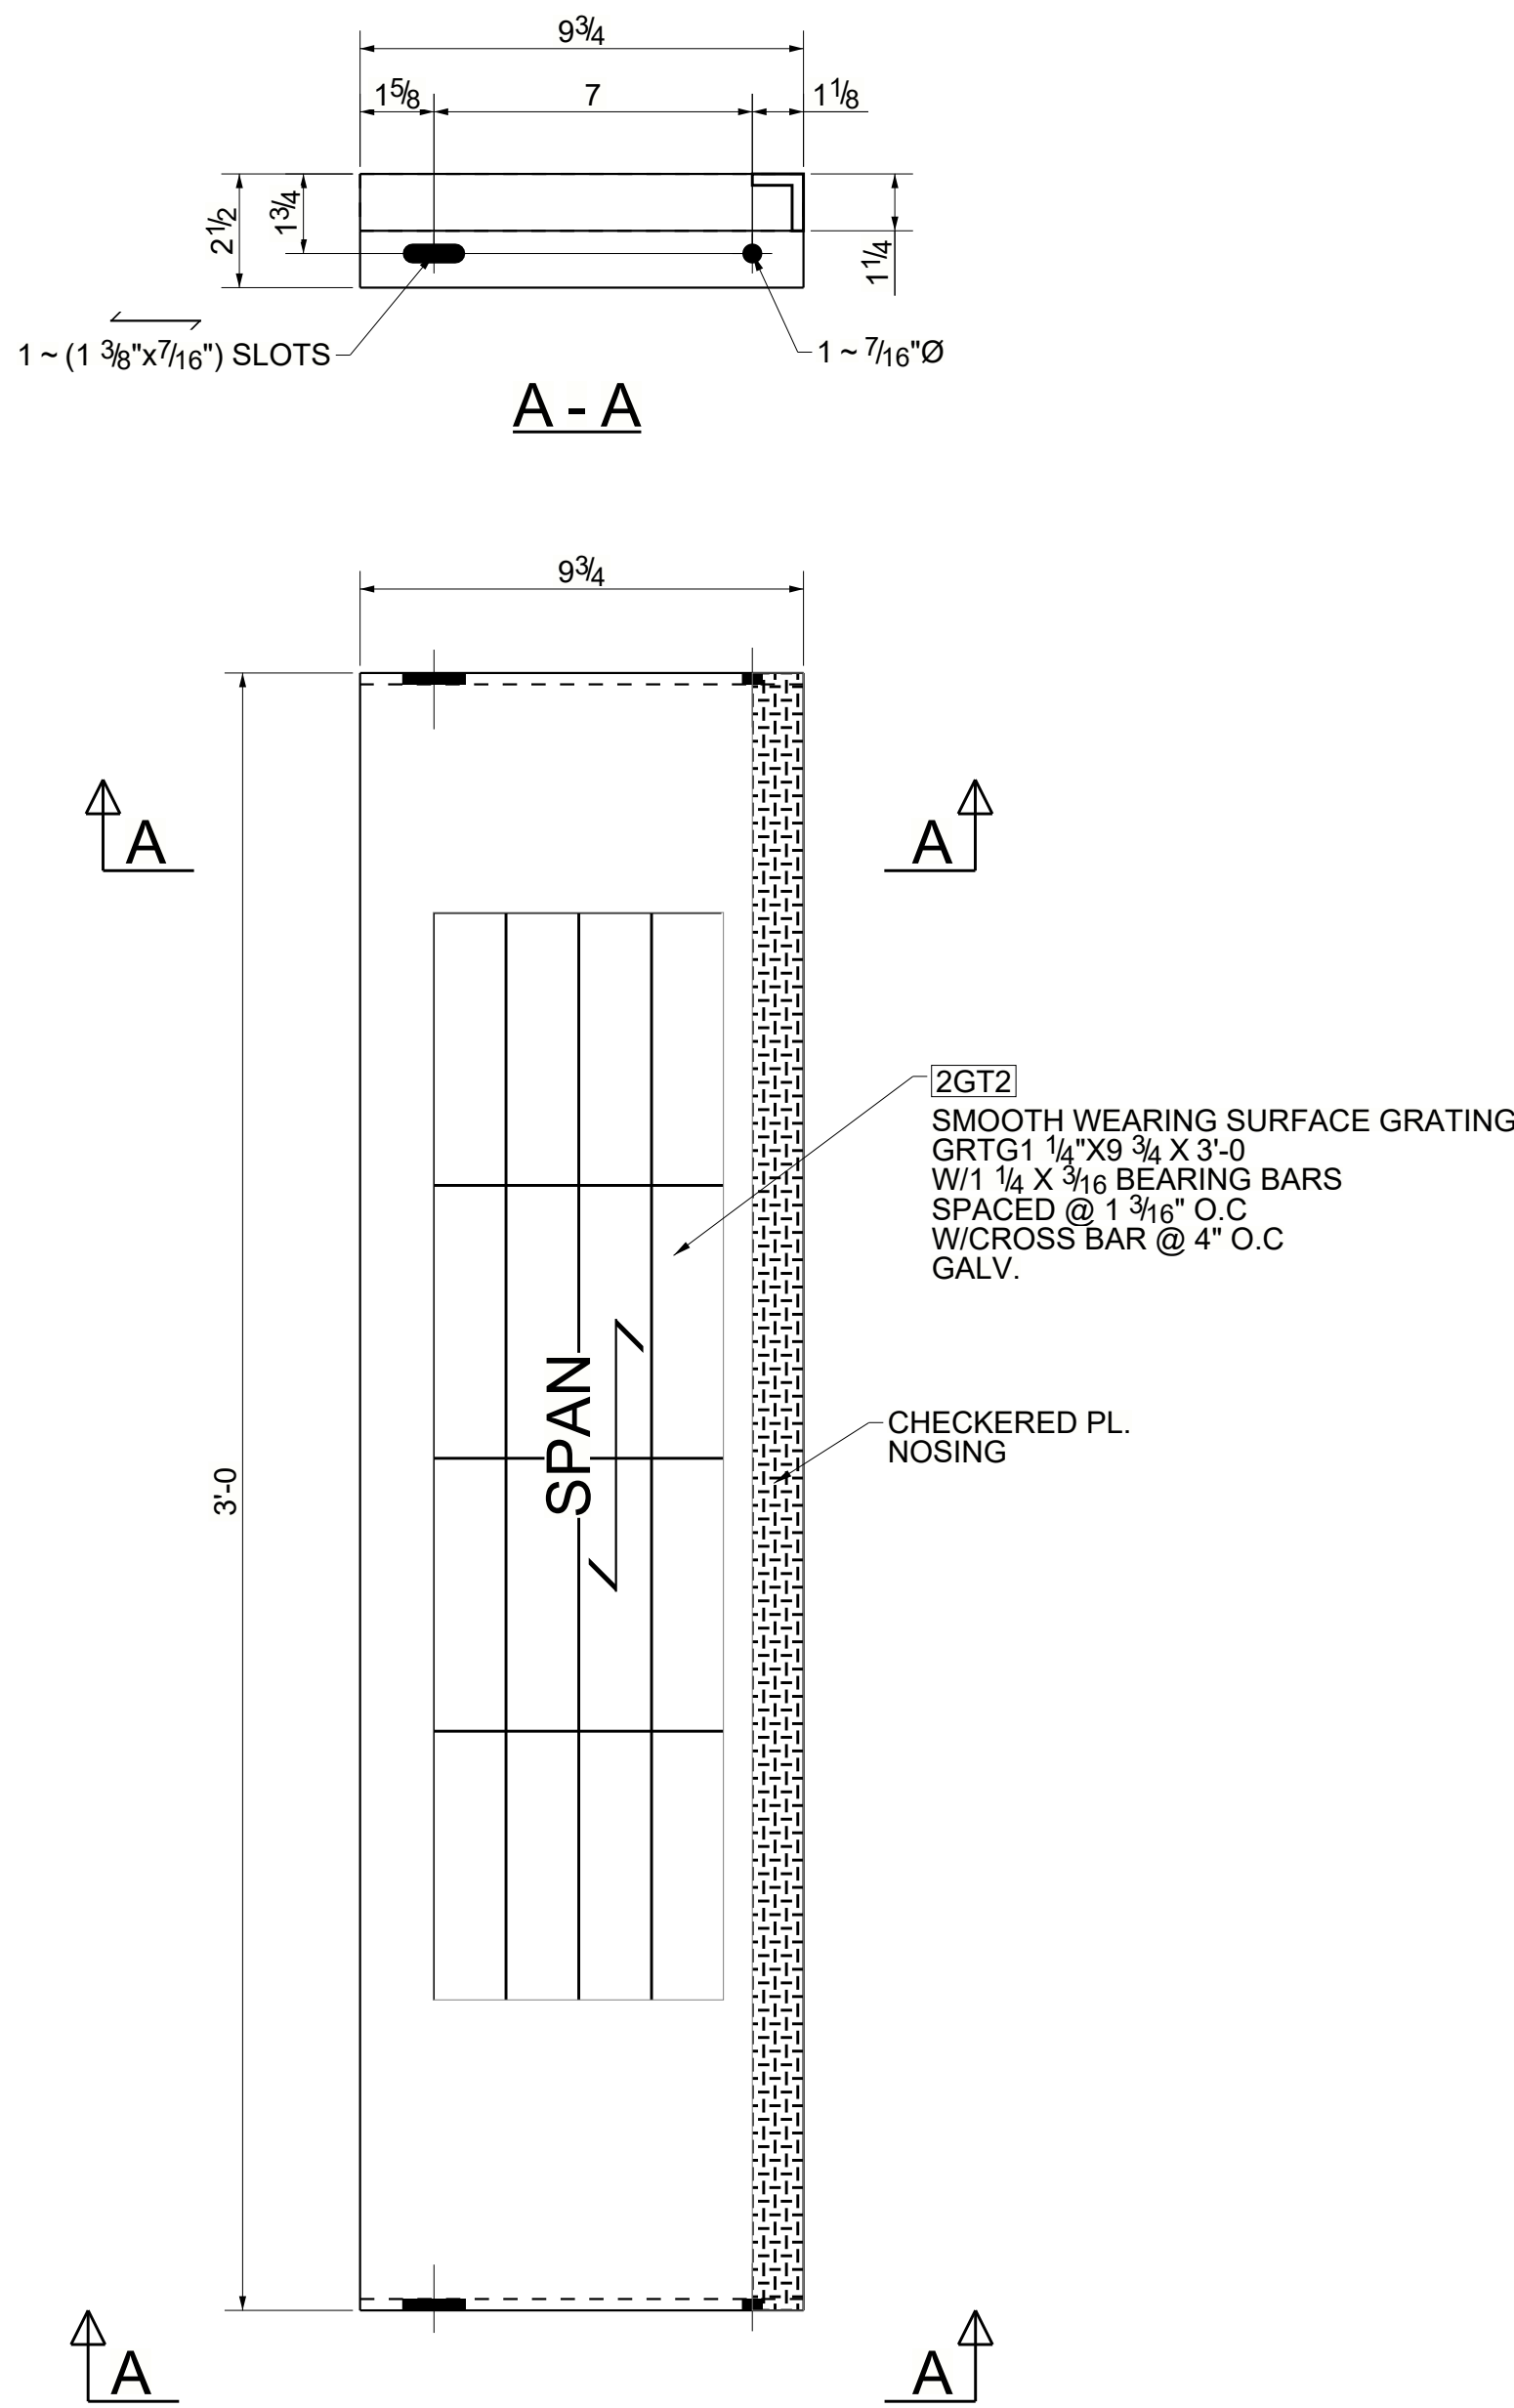

- SHOP NOTES:
1. ALL WELDS TO BE 3/16" ALL AROUND OR DOUBLE SIDED FILLET WELD UNLESS SHOWN OTHERWISE.
 2. TAG ALL MEMBERS IN A VERTICAL POSITION ON LEFT END AS DETAILED.
 3. ALL SHARP EDGES SHALL BE GROUND SMOOTH AND CORNERS ROUNDED OFF.
 4. ALL TAIL (RUNNING) DIMENSIONS SHALL BE MEASURED FROM END OF BEAM, COLUMN,...ETC.
 5. "RD" DENOTES RUNNING DIMENSION
 6. ALL COPES SHALL BE MEASURED FROM END OF BEAM.
 7. ALL BEAM COPES TO BE CUT WITH 1/2" RADIUS U.N.O.
 8. ALL ASSEMBLY PARTS ARE CENTERED UNLESS NOTED/SHOWN OTHERWISE.
 9. ALL CLIP ANGLES SHALL BE ATTACHED TO BEAM WITH 3/16" FILLET WELD ON THREE SIDES UNLESS SHOWN OTHERWISE.
 10. FOR INDIVIDUAL DETAILS OF PLATES, ANGLES, ETC., SEE GATHER SHEETS/ SINGLE PART SHEETS.
 11. B.T.S. DENOTES BOLT TO SHIP WITH A307 BOLTS. ASSEMBLE AFTER PAINTING/GALV.
 12. SHOP CLOSE ALL CAPS.
 13. ALL JOINTS TO BE SEAL WELDED WITH CONT. 1/8" FILLET OR BUTT WELD AS REQ'D
 14. PROVIDE VENT HOLES AS REQ'D FOR GALV.
 15. PLUG VENT HOLES AFTER GALV.

BILL OF MATERIAL

SHIP MARK	PIECE MARK	QTY	DESCRIPTION	LENGTH	REMARKS
2GT2		127	GRTG1 1/4"X9 3/4"	3'-0"	SQ-2 A572-50

127 - GRATING TREADS - 2GT2 REF.E202,E203




FOR FABRICATION : 07/20/2022

BILL OF MATERIAL					
MARK	QTY	DESCRIPTION	LENGTH	WEIGHT	REMARKS
11S2	1	STAIR			BEV-2
11S2	1	MC12X14.3	9'-8 1/8"	138	A36
11aa1	2	L1-1/4X1-1/4X3/16	0'-4 7/16"	1	A36
11aa2	14	L1-1/4X1-1/4X3/16	0'-3 1/2"	6	A36
11aa3	16	L1-1/4X1-1/4X3/16	0'-10"	20	A36
11aa4	2	L1-1/4X1-1/4X3/16	0'-2 1/2"	1	A36
11aa5	2	L1-1/4X1-1/4X3/16	0'-4 1/16"	1	A36
11aa16	2	L1-1/4X1-1/4X3/16	0'-6 13/16"	2	A36
11hh2	8	SHT14GAX21 5/8"	4'-3 1/2"	322	A36
11mm16	1	MC12X14.3	0'-8 3/16"	10	A36
11mm17	1	MC12X14.3	0'-8 7/16"	10	A36
11mm41	1	MC12X14.3	9'-8 1/8"	138	A36
11pp2	1	PL 1/4"X2 1/8"	0'-5"	1	A36
11pp4	1	PL 1/4"X2 1/8"	0'-6 15/16"	1	A36
11pp6	1	PL 1/4"X1 15/16"	0'-2 1/8"	0	A36
		TOTAL WEIGHT THIS DRAWING		649	


1. ALL WELDS TO BE 3/16" ALL AROUND OR DOUBLE SIDED FILLET WELD UNLESS SHOWN OTHERWISE.
2. TAG ALL MEMBERS IN A VERTICAL POSITION ON LEFT END AS DETAILED.
3. ALL SHARP EDGES SHALL BE GROUND SMOOTH AND CORNERS ROUNDED OFF.
4. ALL TAIL (RUNNING) DIMENSIONS SHALL BE MEASURED FROM END OF BEAM, COLUMN,...ETC.
5. "RD" DENOTES RUNNING DIMENSION
6. ALL COPES SHALL BE MEASURED FROM END OF BEAM.
7. ALL BEAM COPES TO BE CUT WITH 1/2" RADIUS U.O.
8. FOR INDIVIDUAL DETAILS OF PLATES, ANGLES, ETC., SEE SINGLE PARTS DETAIL SHEETS.
9. B.T.S.DENOTES BOLT TO SHIP"SNUG TIGHT" WITH NOTED BOLTS. ASSEMBLE AFTER PAINTING/GALV.



ONE - STAIR - 11S2

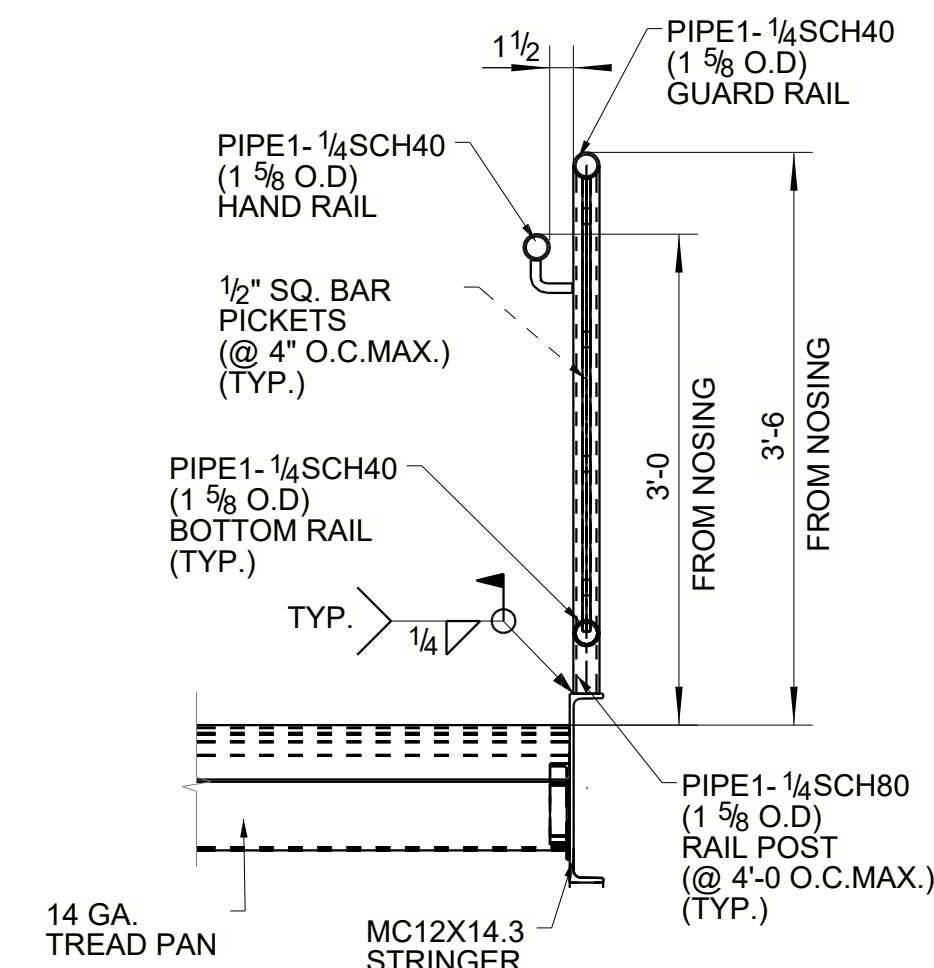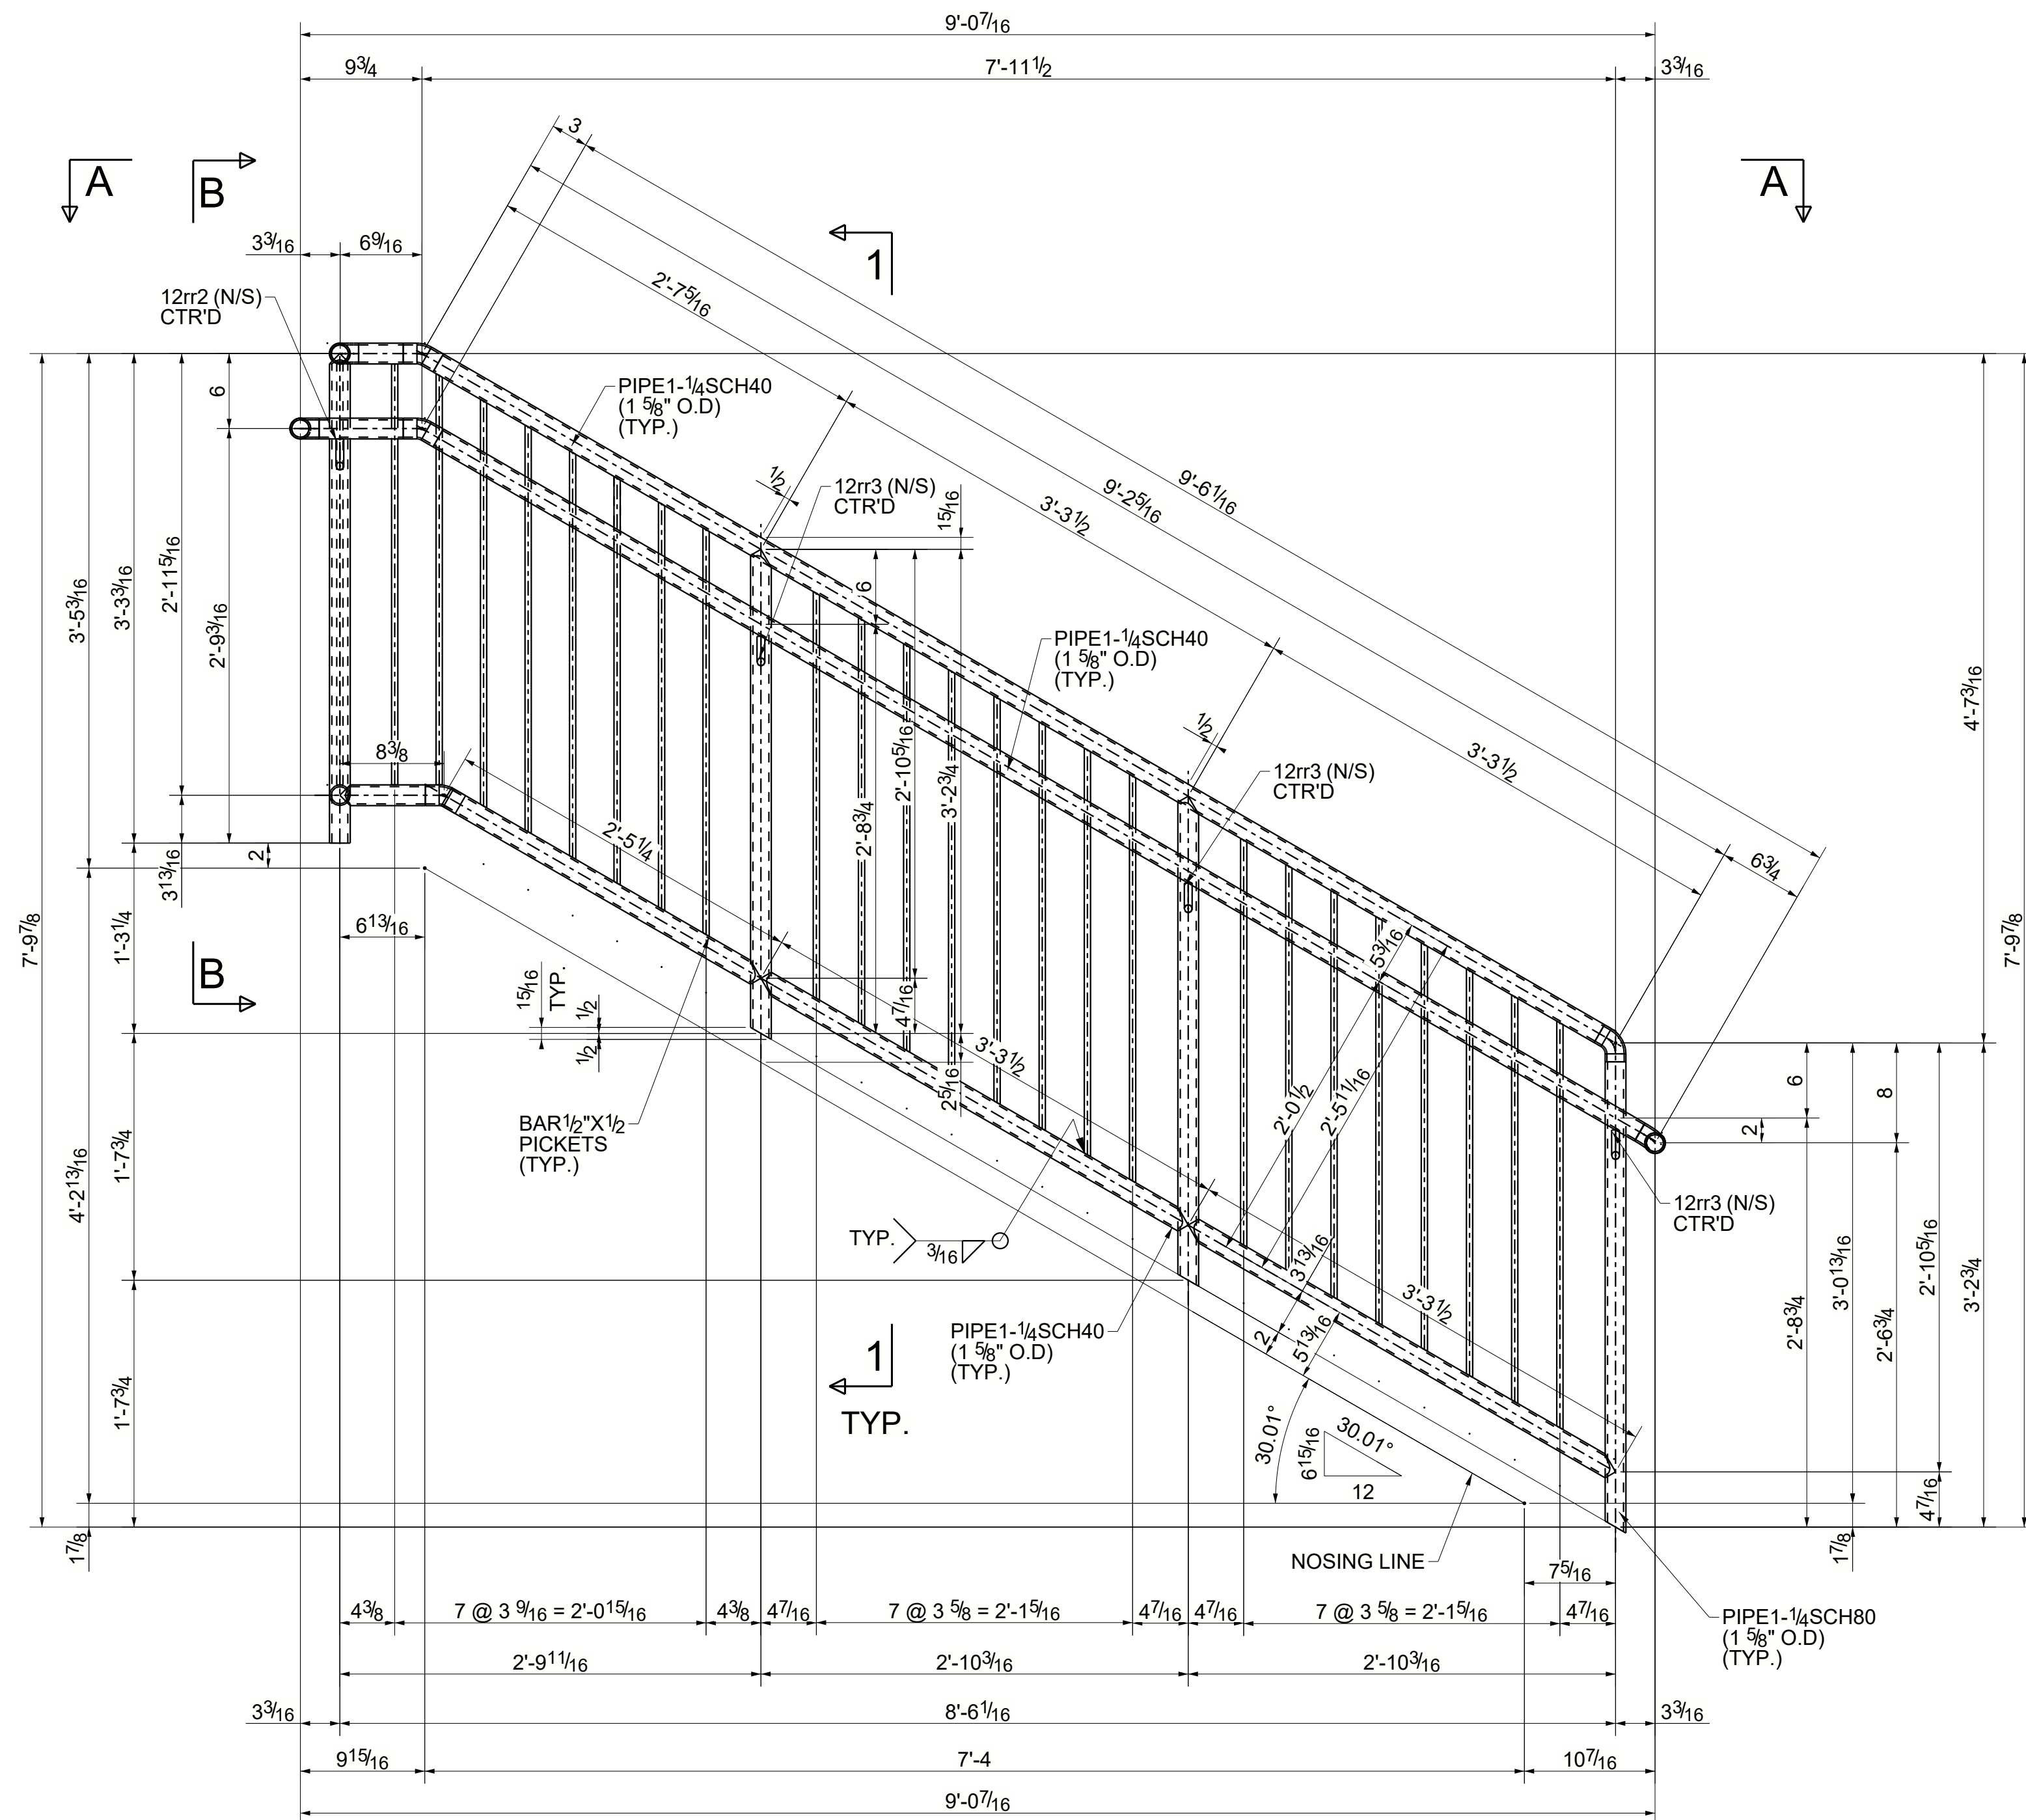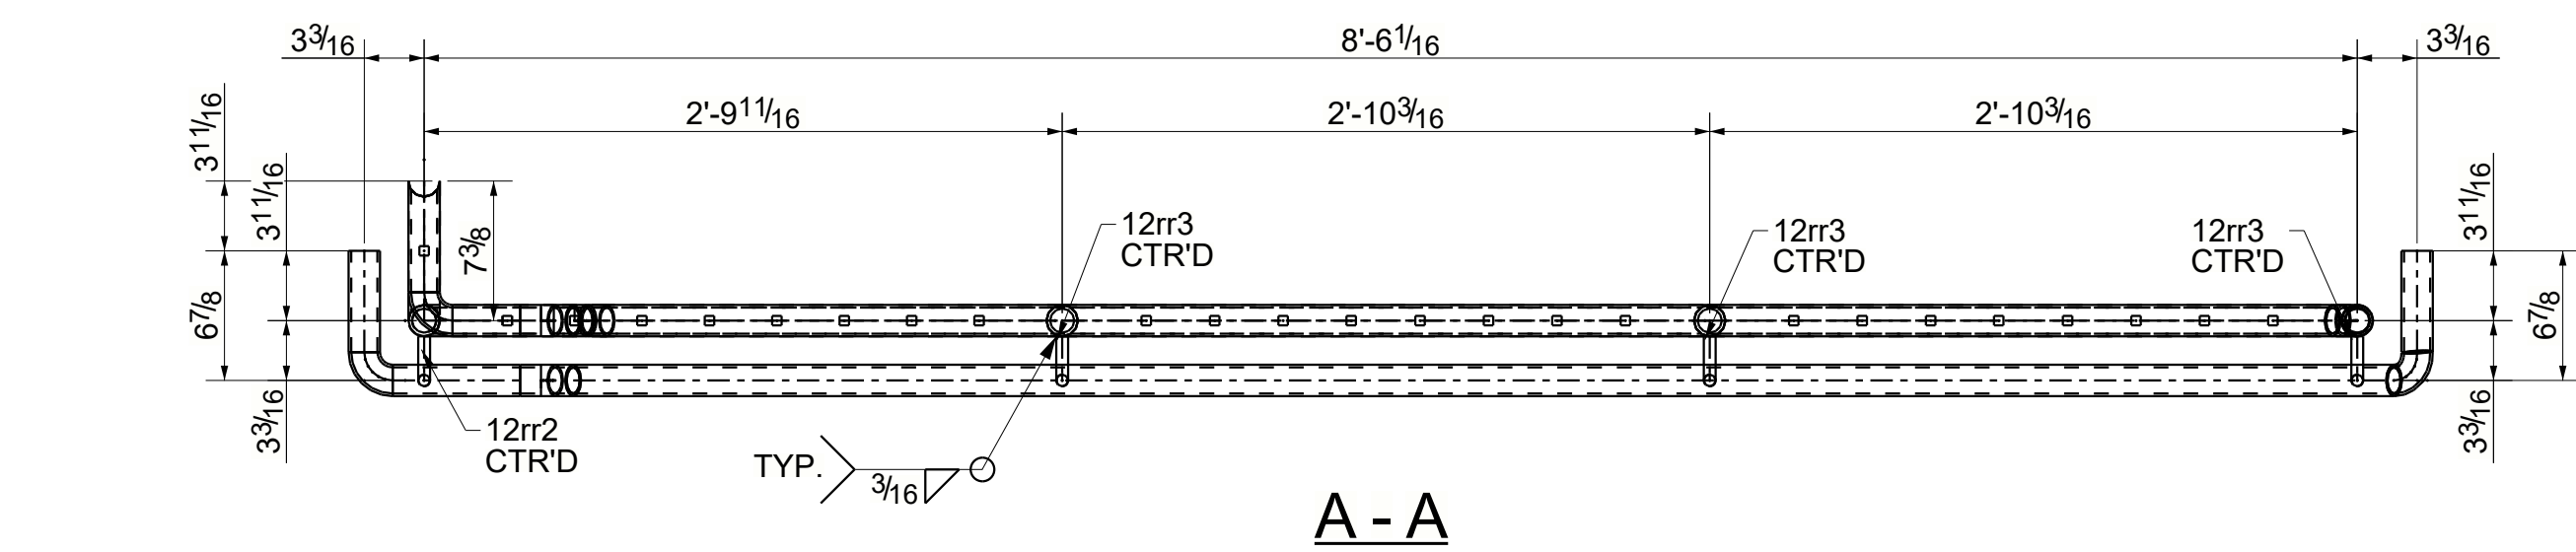

TYPICAL STRINGER RAIL DETAILS

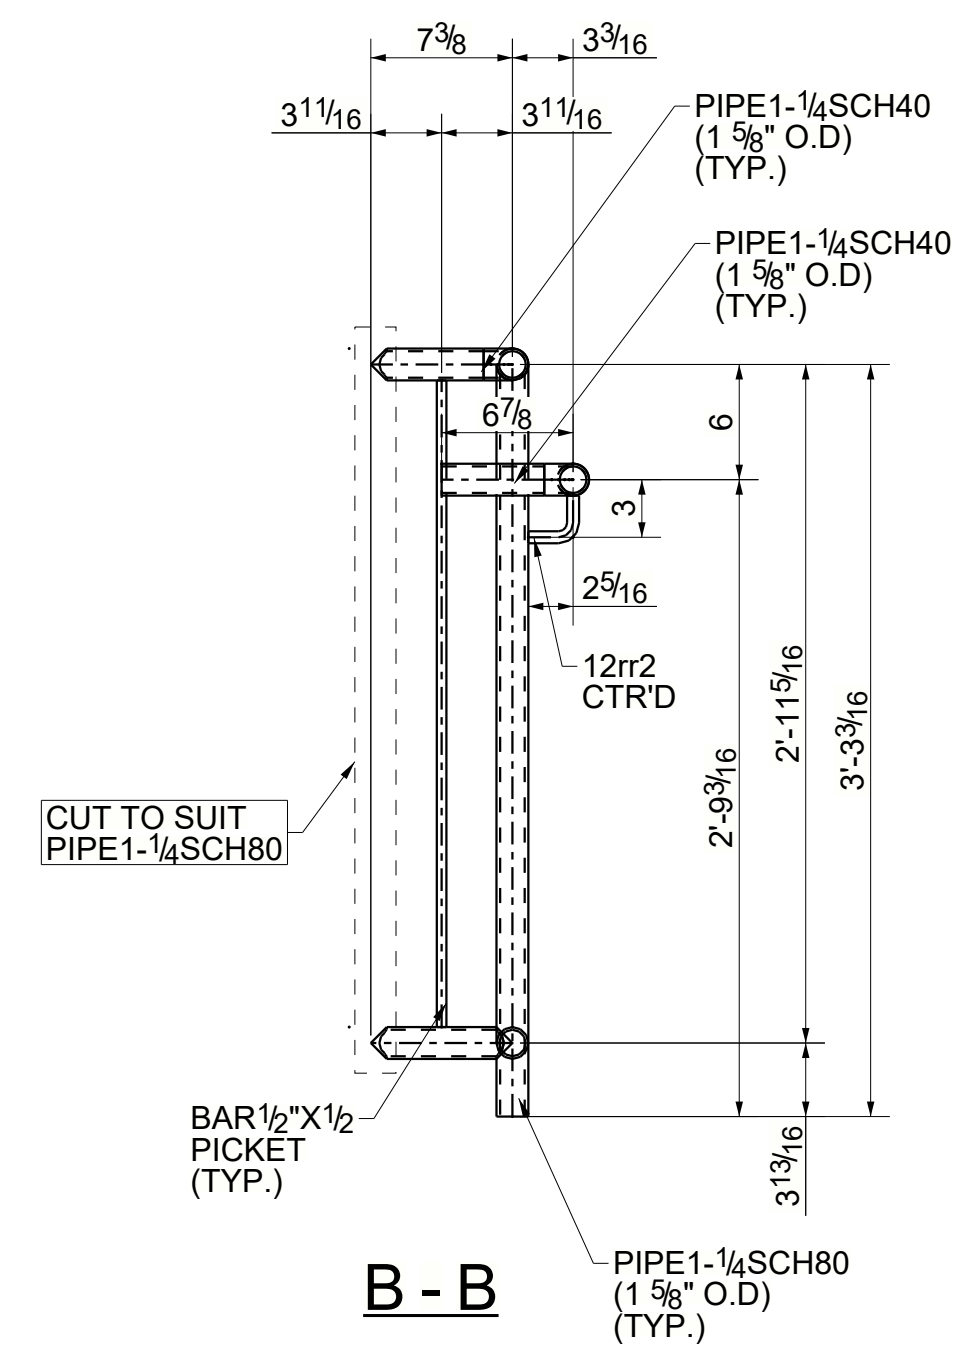

BILL OF MATERIAL					
MARK	QTY	DESCRIPTION	LENGTH	REMARKS	GRADE
12GR2	1	GUARD RAIL			A53
		PIPE1-1/4SCH40	32'-5 15/16"	Total Length	A53
		PIPE1-1/4SCH80	12'-11 5/16"	Total Length	A53
		BAR1/2"X1/2"	68'-3 3/8"	Total Length	A36
12r2	1	ROD5/8"	0'-4 3/16"		A36
12r3	3	ROD5/8"	0'-4 1/16"		A36

- SHOP NOTES:
- ALL WELDS TO BE 3/16" ALL AROUND OR DOUBLE SIDED FILLET WELD UNLESS SHOWN OTHERWISE.
 - TAG ALL MEMBERS IN A VERTICAL POSITION ON LEFT END AS DETAILED.
 - ALL SHARP EDGES SHALL BE GROUND SMOOTH AND CORNERS ROUNDED OFF.
 - ALL TAIL (RUNNING) DIMENSIONS SHALL BE MEASURED FROM END OF BEAM, COLUMN,...ETC.
 - "RD" DENOTES RUNNING DIMENSION
 - ALL COPES SHALL BE MEASURED FROM END OF BEAM.
 - ALL BEAM COPES TO BE CUT WITH 1/2" RADIUS U.N.O.
 - FOR INDIVIDUAL DETAILS OF PLATES, ANGLES, ETC., SEE SINGLE PARTS DETAIL SHEETS.
 - B.T.S.DENOTES BOLT TO SHIP"SNUG TIGHT" WITH NOTED BOLTS. ASSEMBLE AFTER PAINTING/GALV.

ONE - GUARD RAIL - 12GR2

