




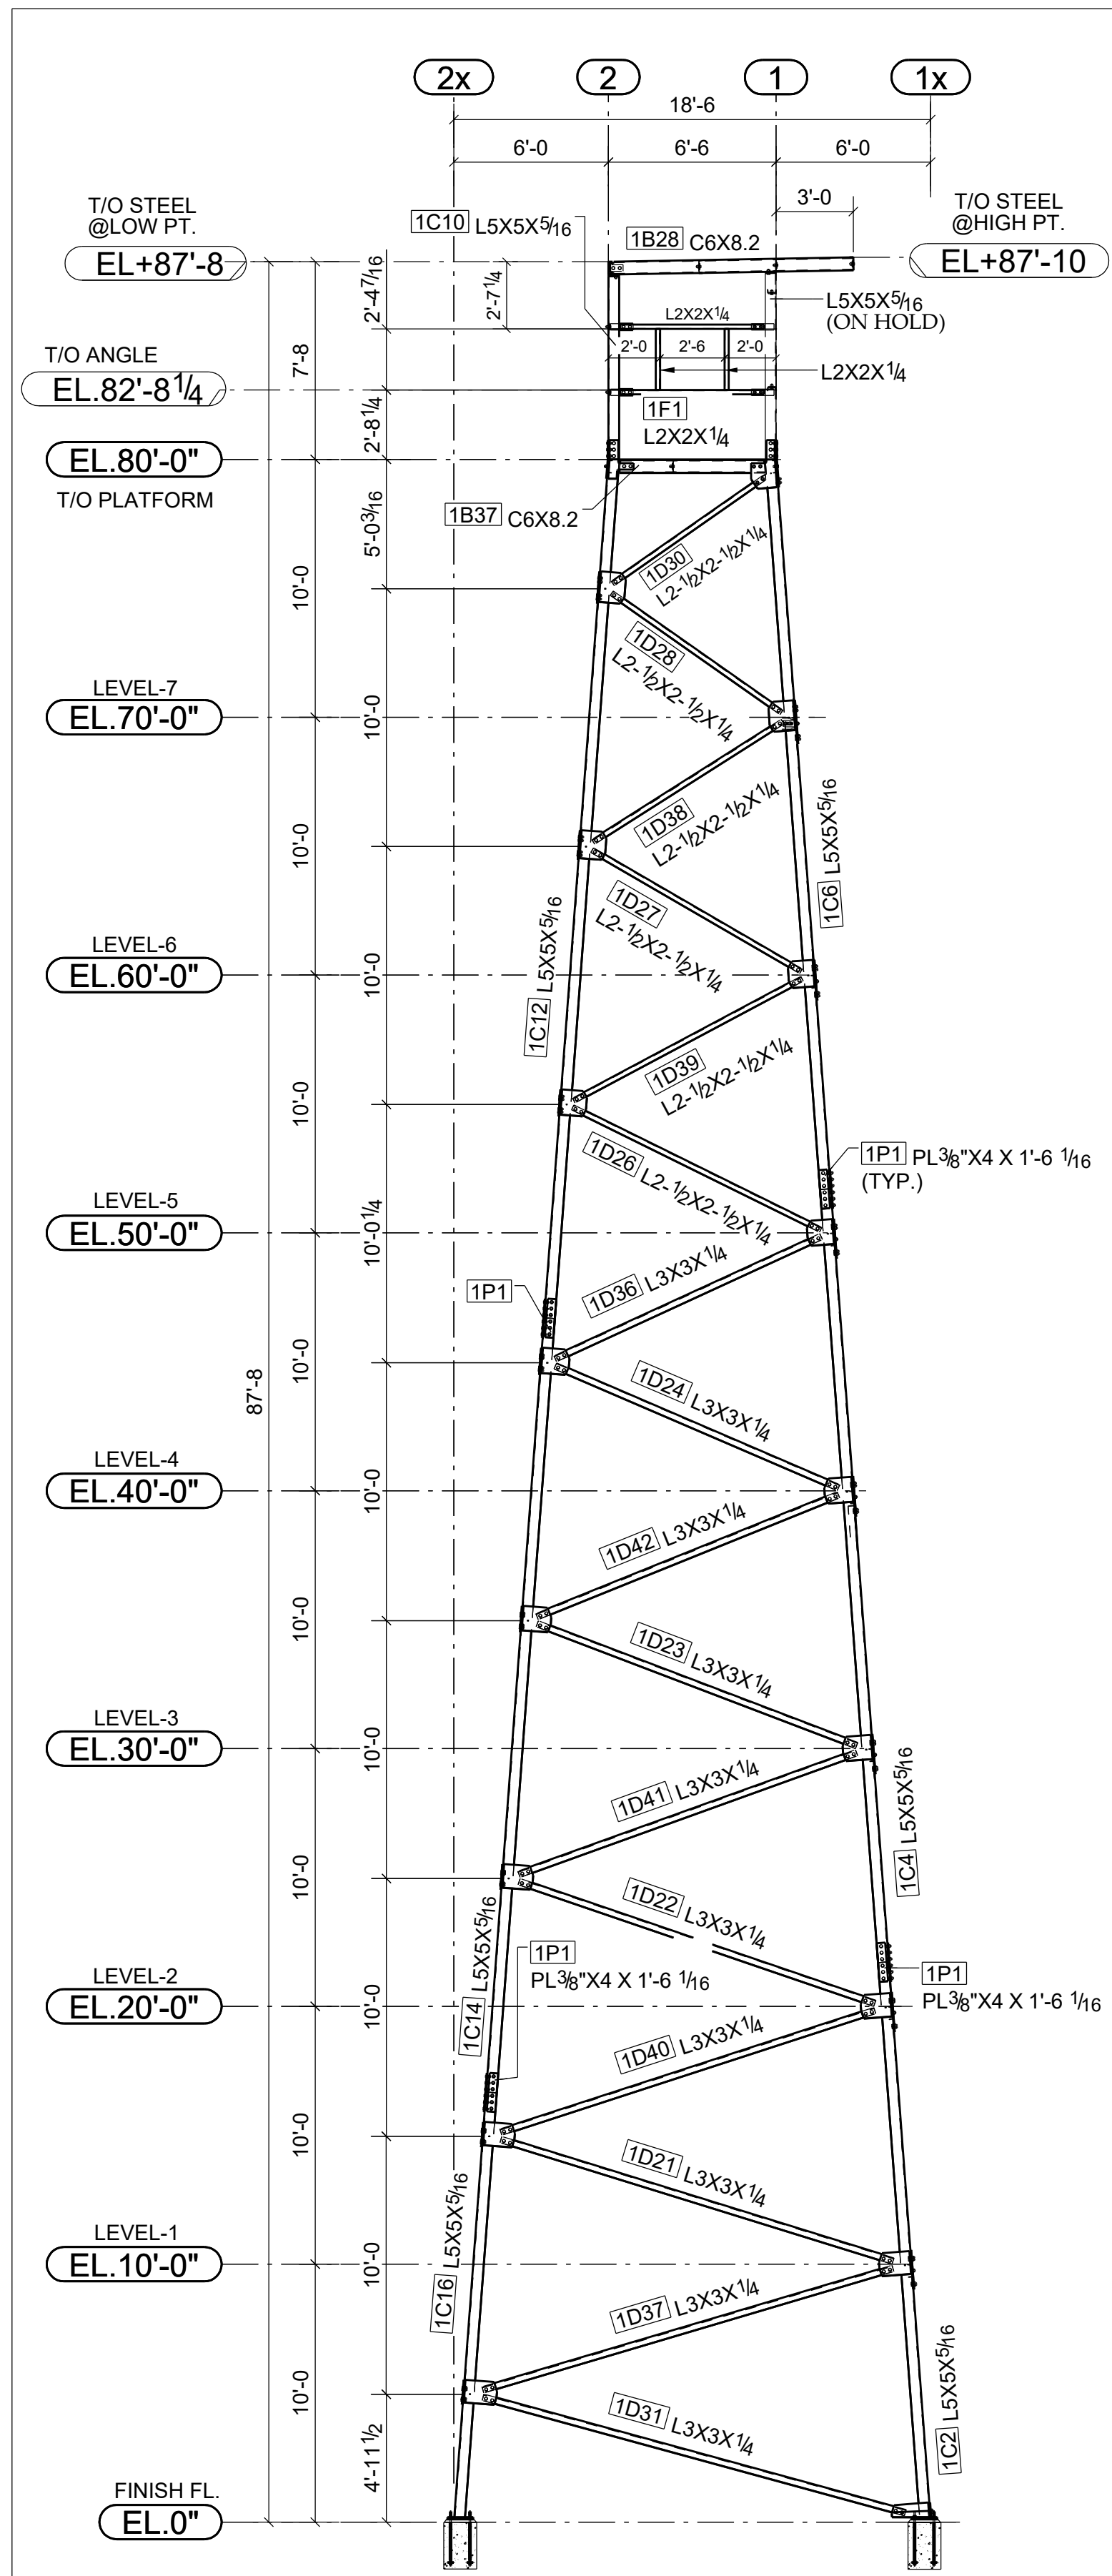


ELEVATION ALONG GRID LINE 'B'
REFER SHEET:4/S102

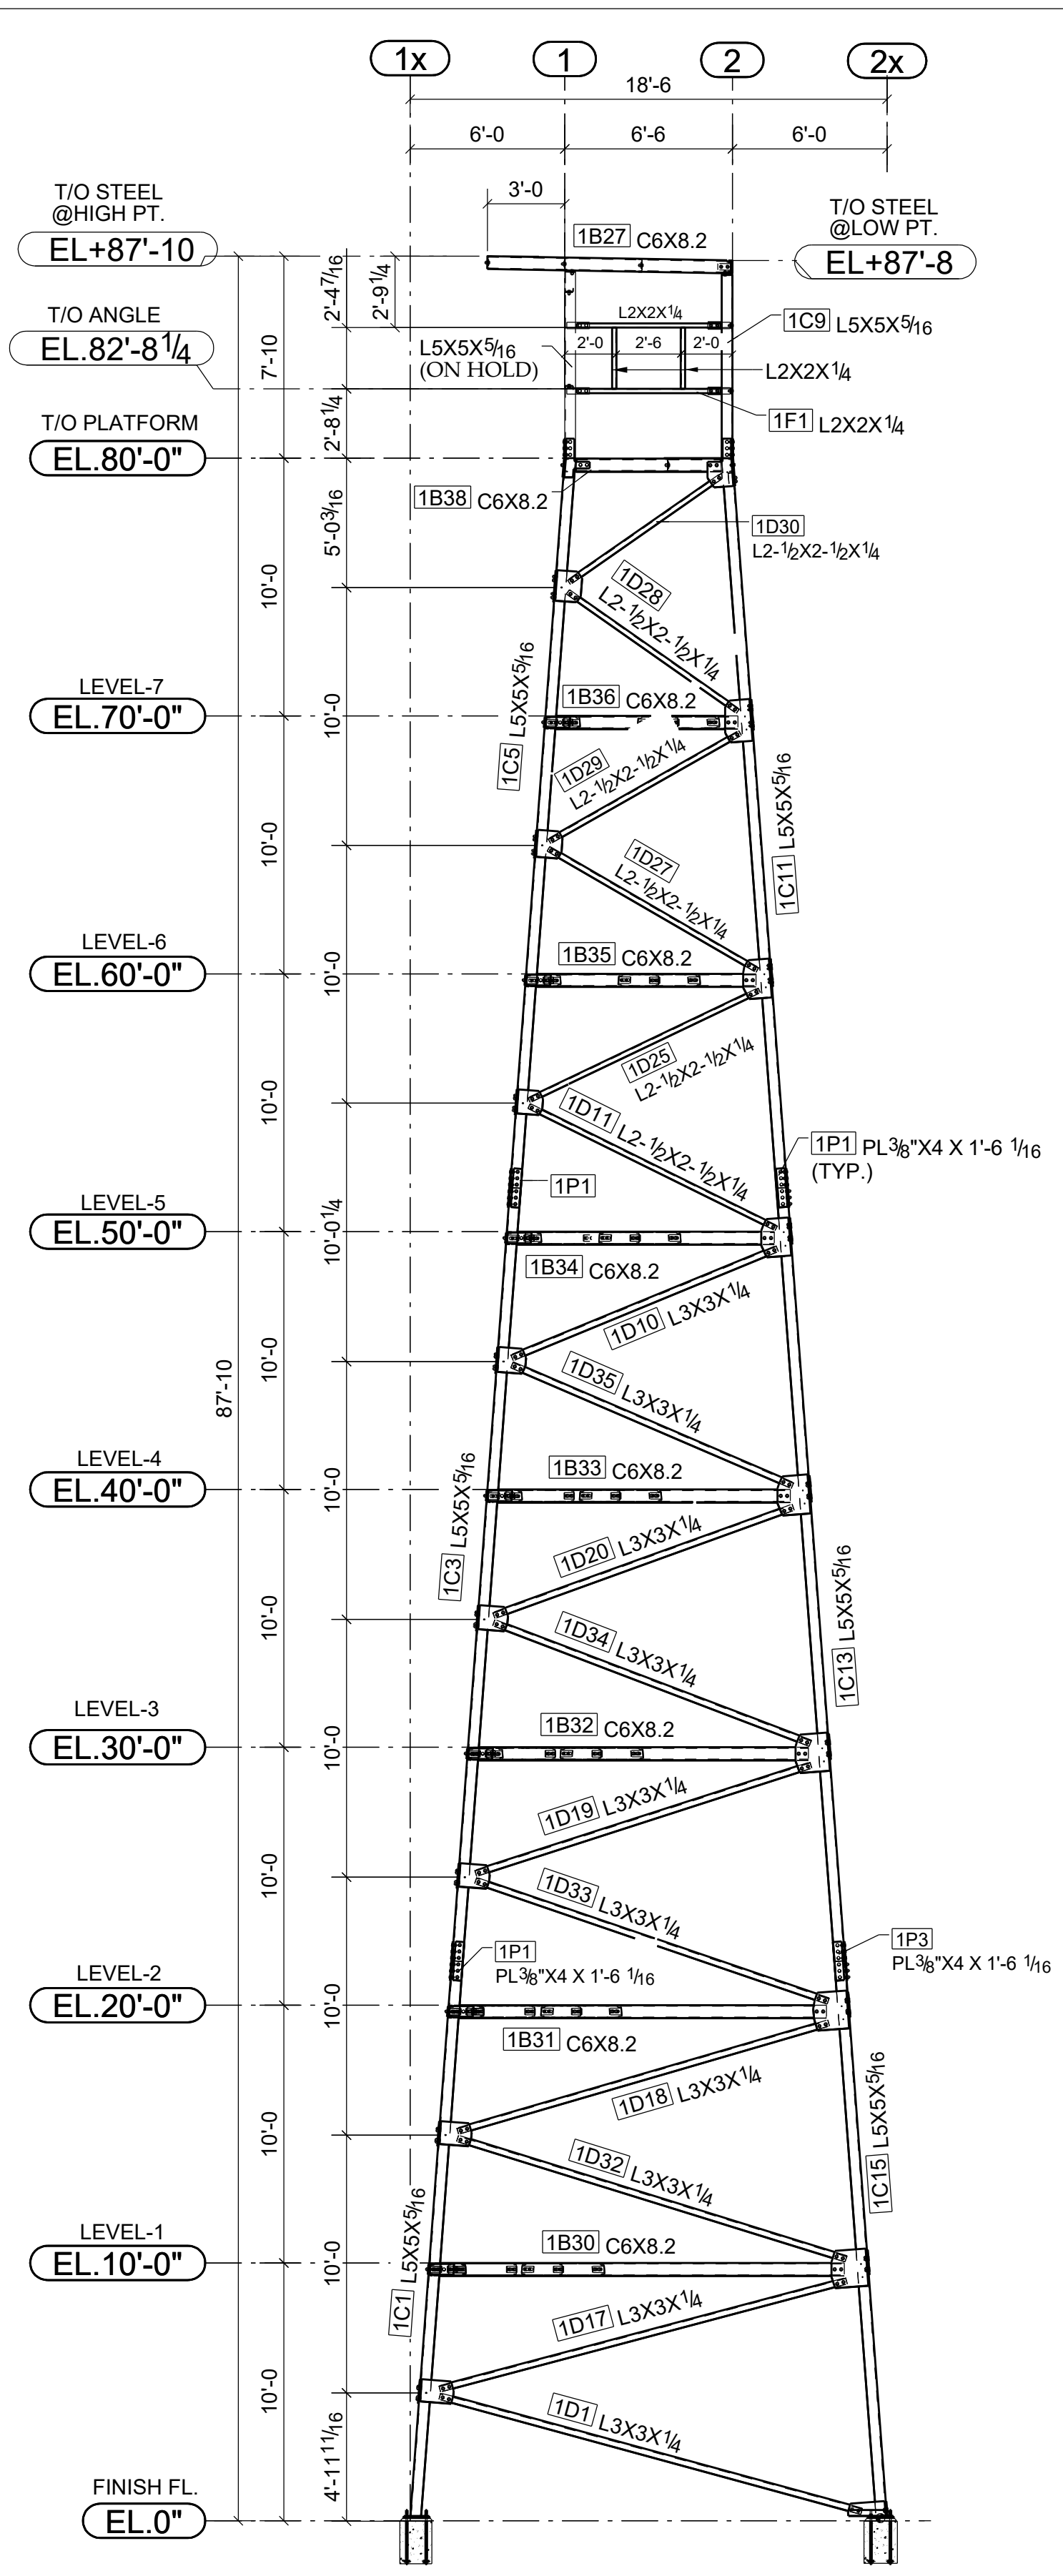

ELEVATION ALONG GRID LINE 'A'
REFER SHEET:3/S102

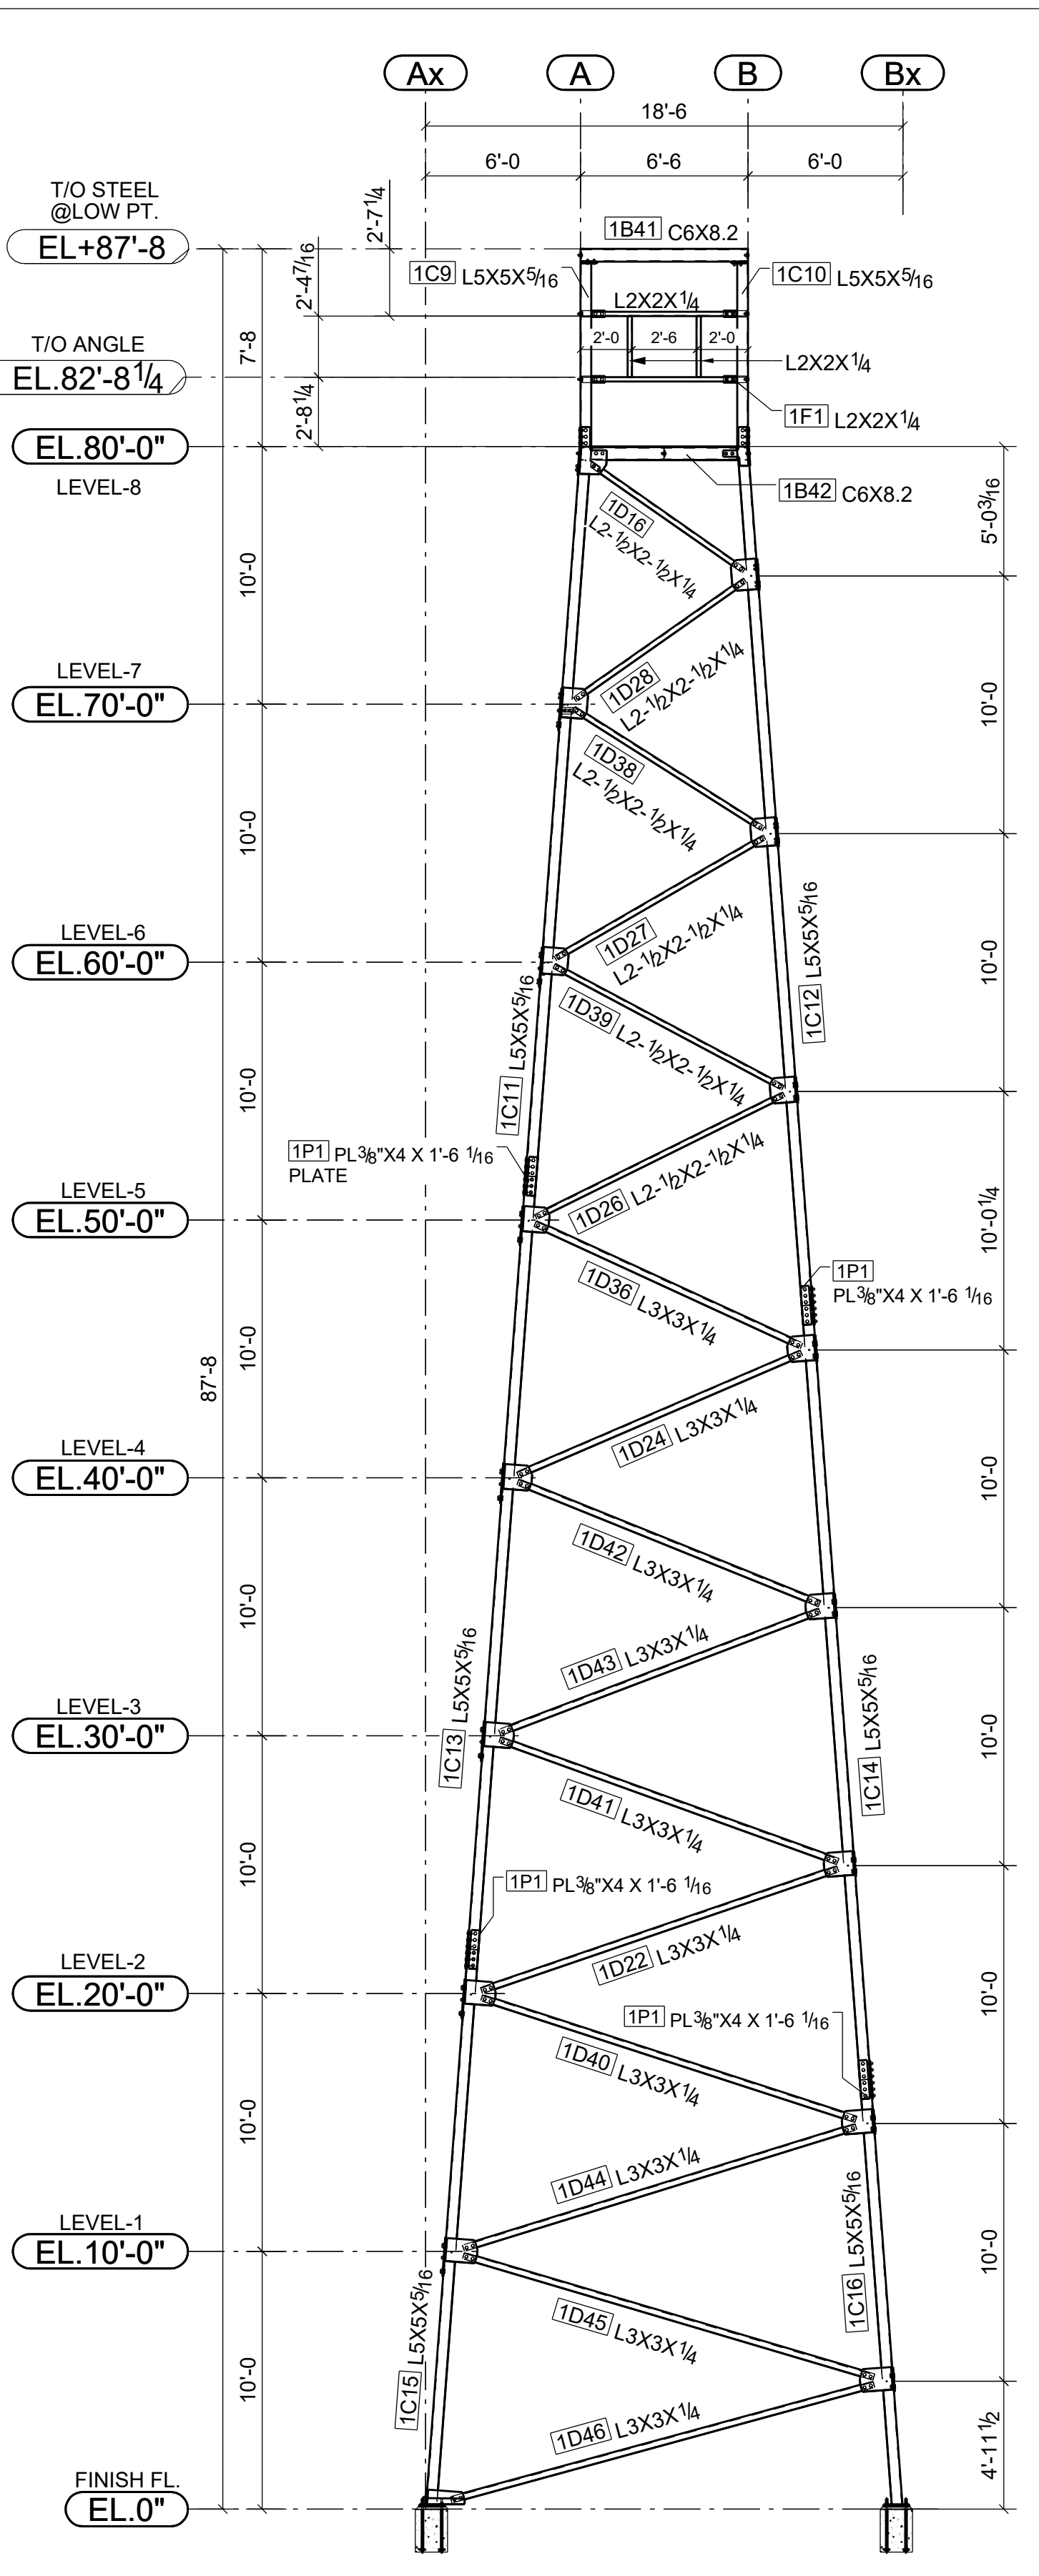


ELEVATION ALONG GRID LINE '2'
REFER SHEET:2/S102

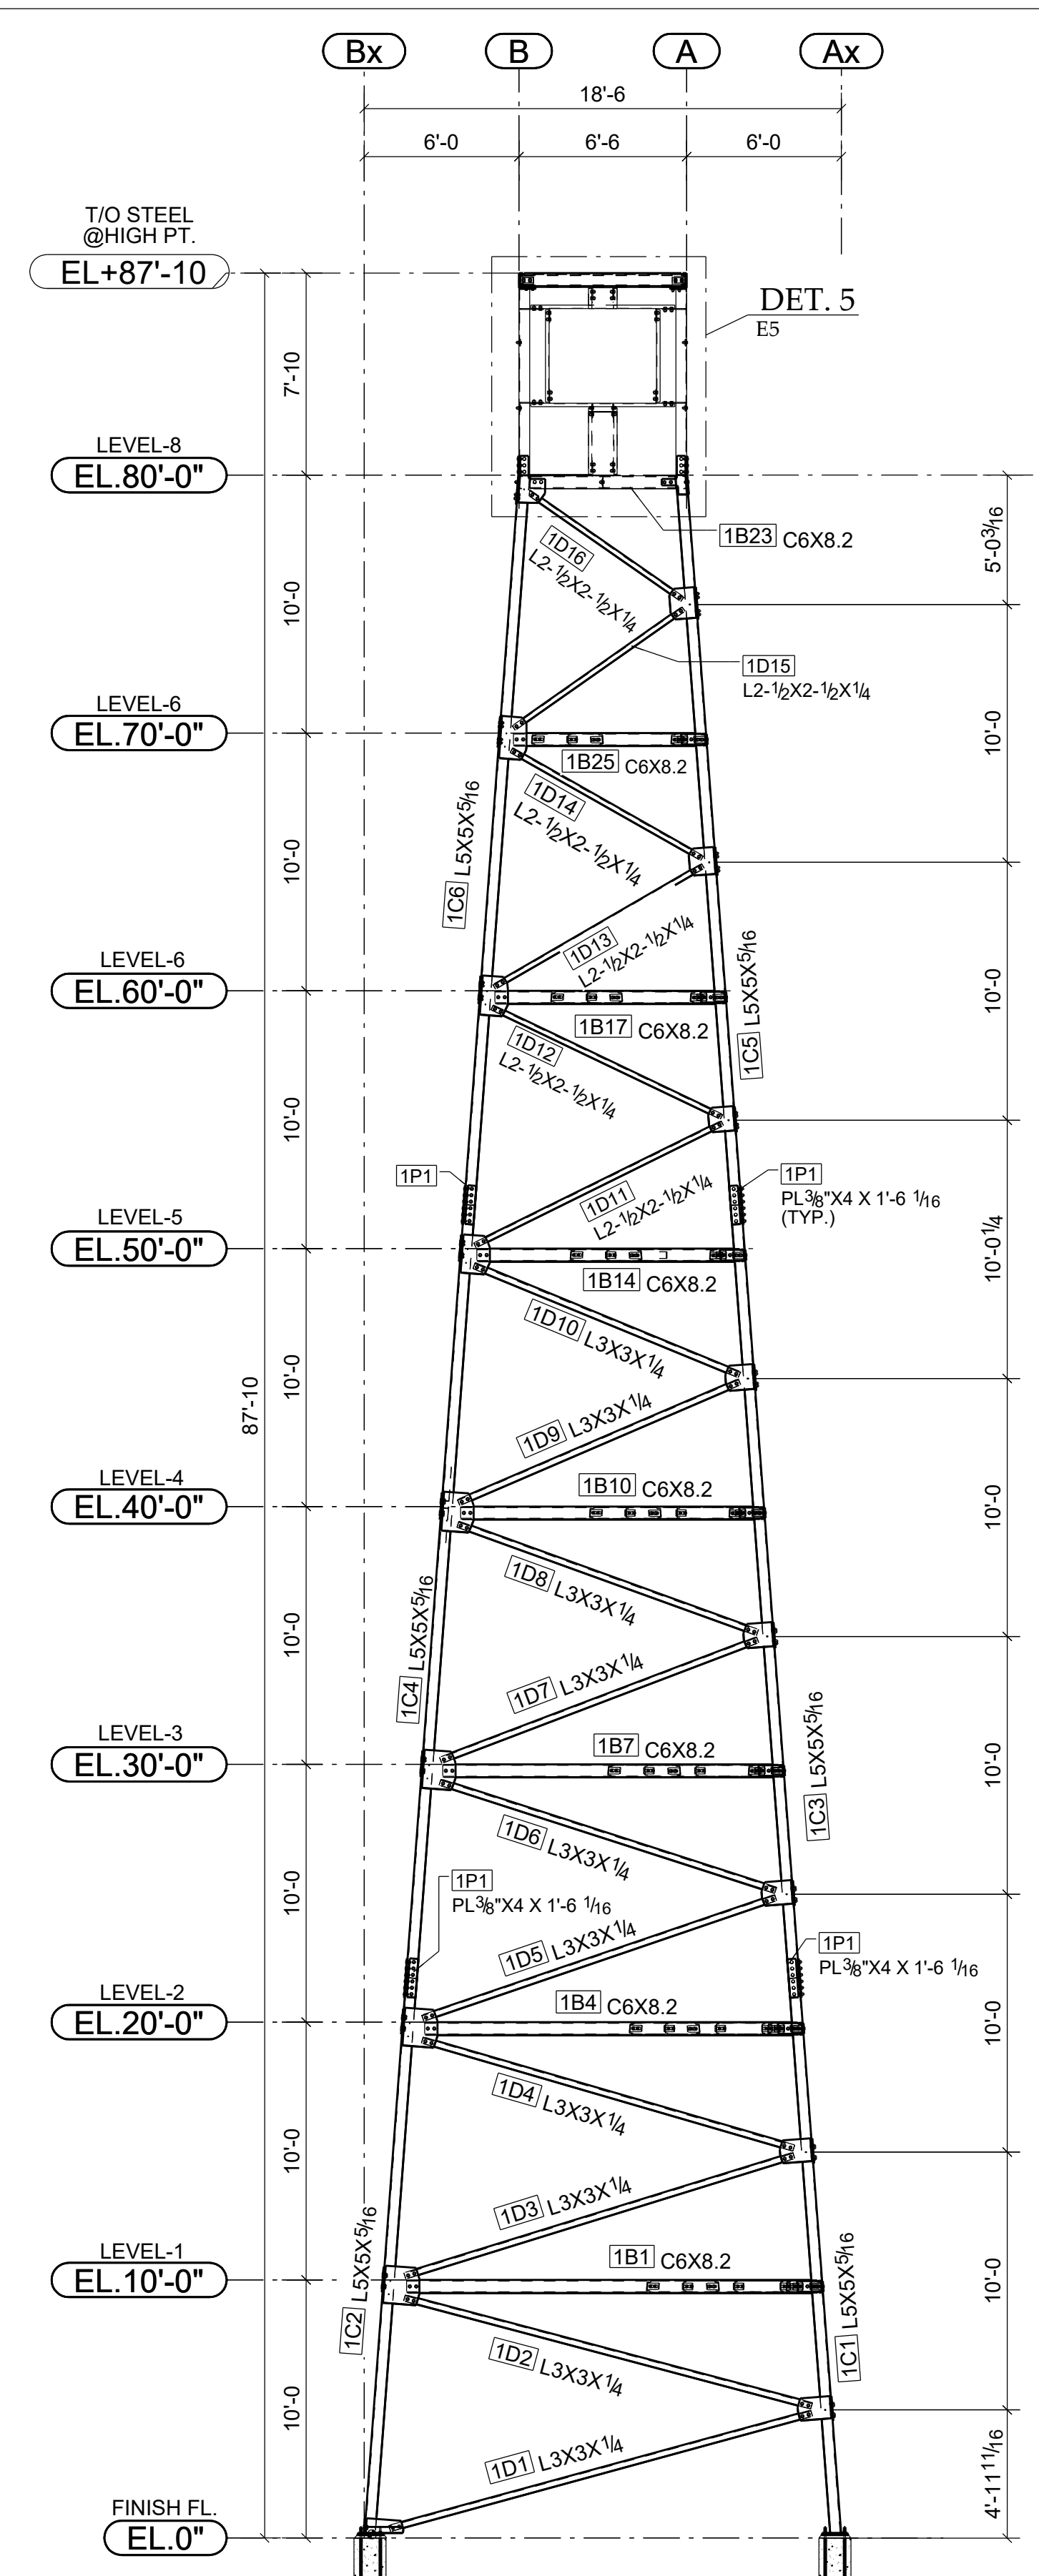

ELEVATION ALONG GRID LINE '1'
REFER SHEET:1/S102



ALL STEELS ARE GALVANIZED


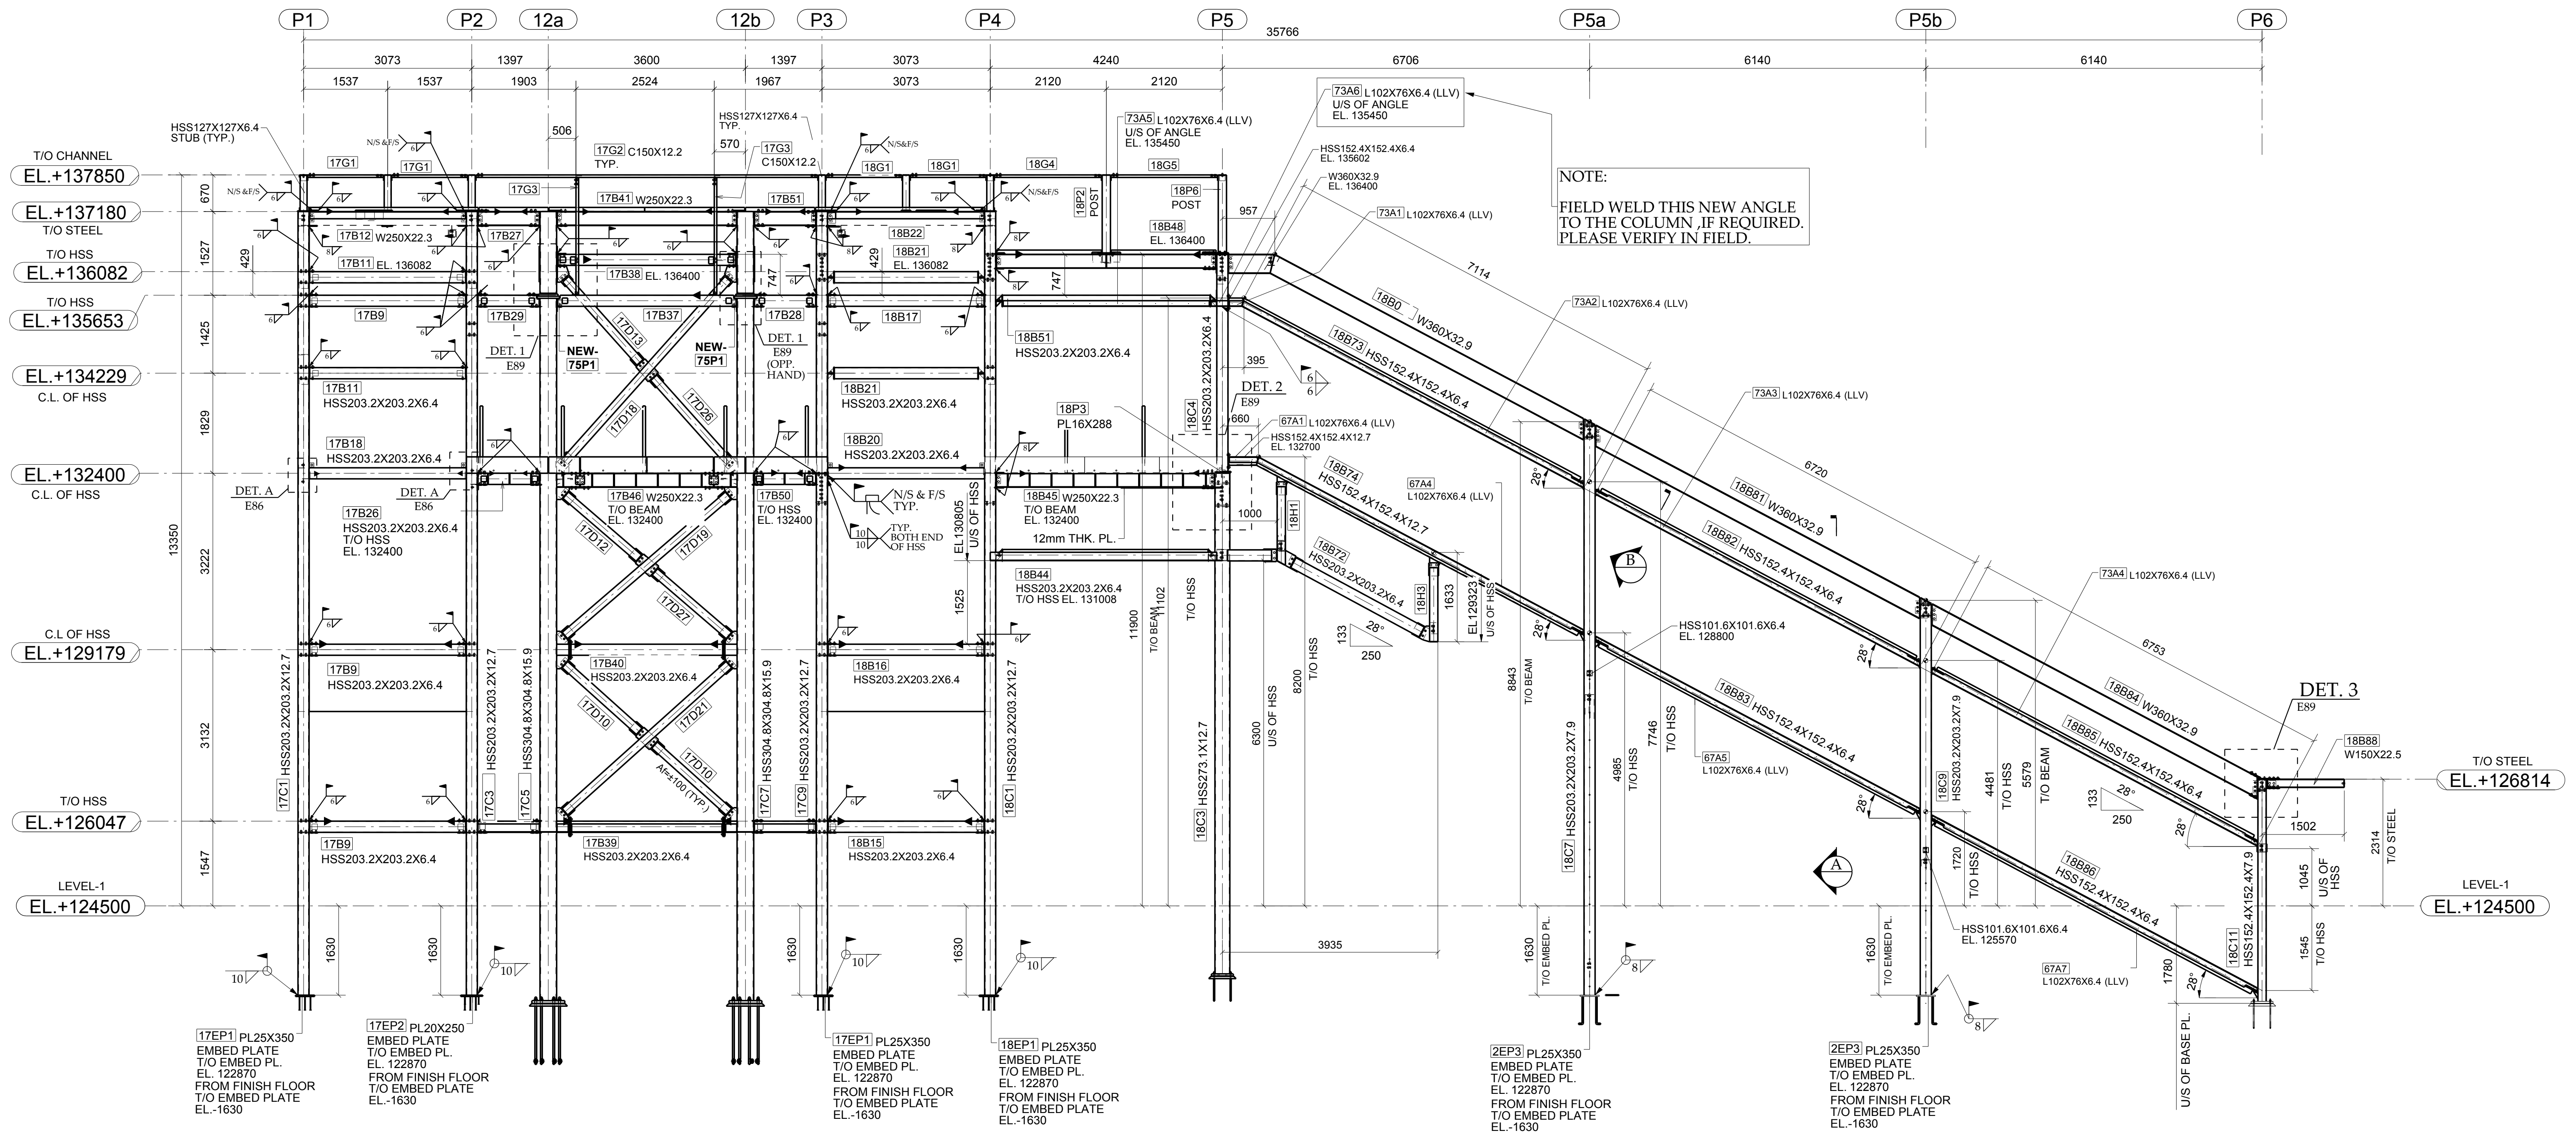


108 SECTION
E46 (REF. SEC 1/S410)



FINISH FLOOR = LEVEL -1 = EL.124500


ERECTOR NOTE:
PL6 TEMPORARY ERECTION TAB.
ERECTOR TO CUT AND
REMOVE UPON COMPLETION OF WORK

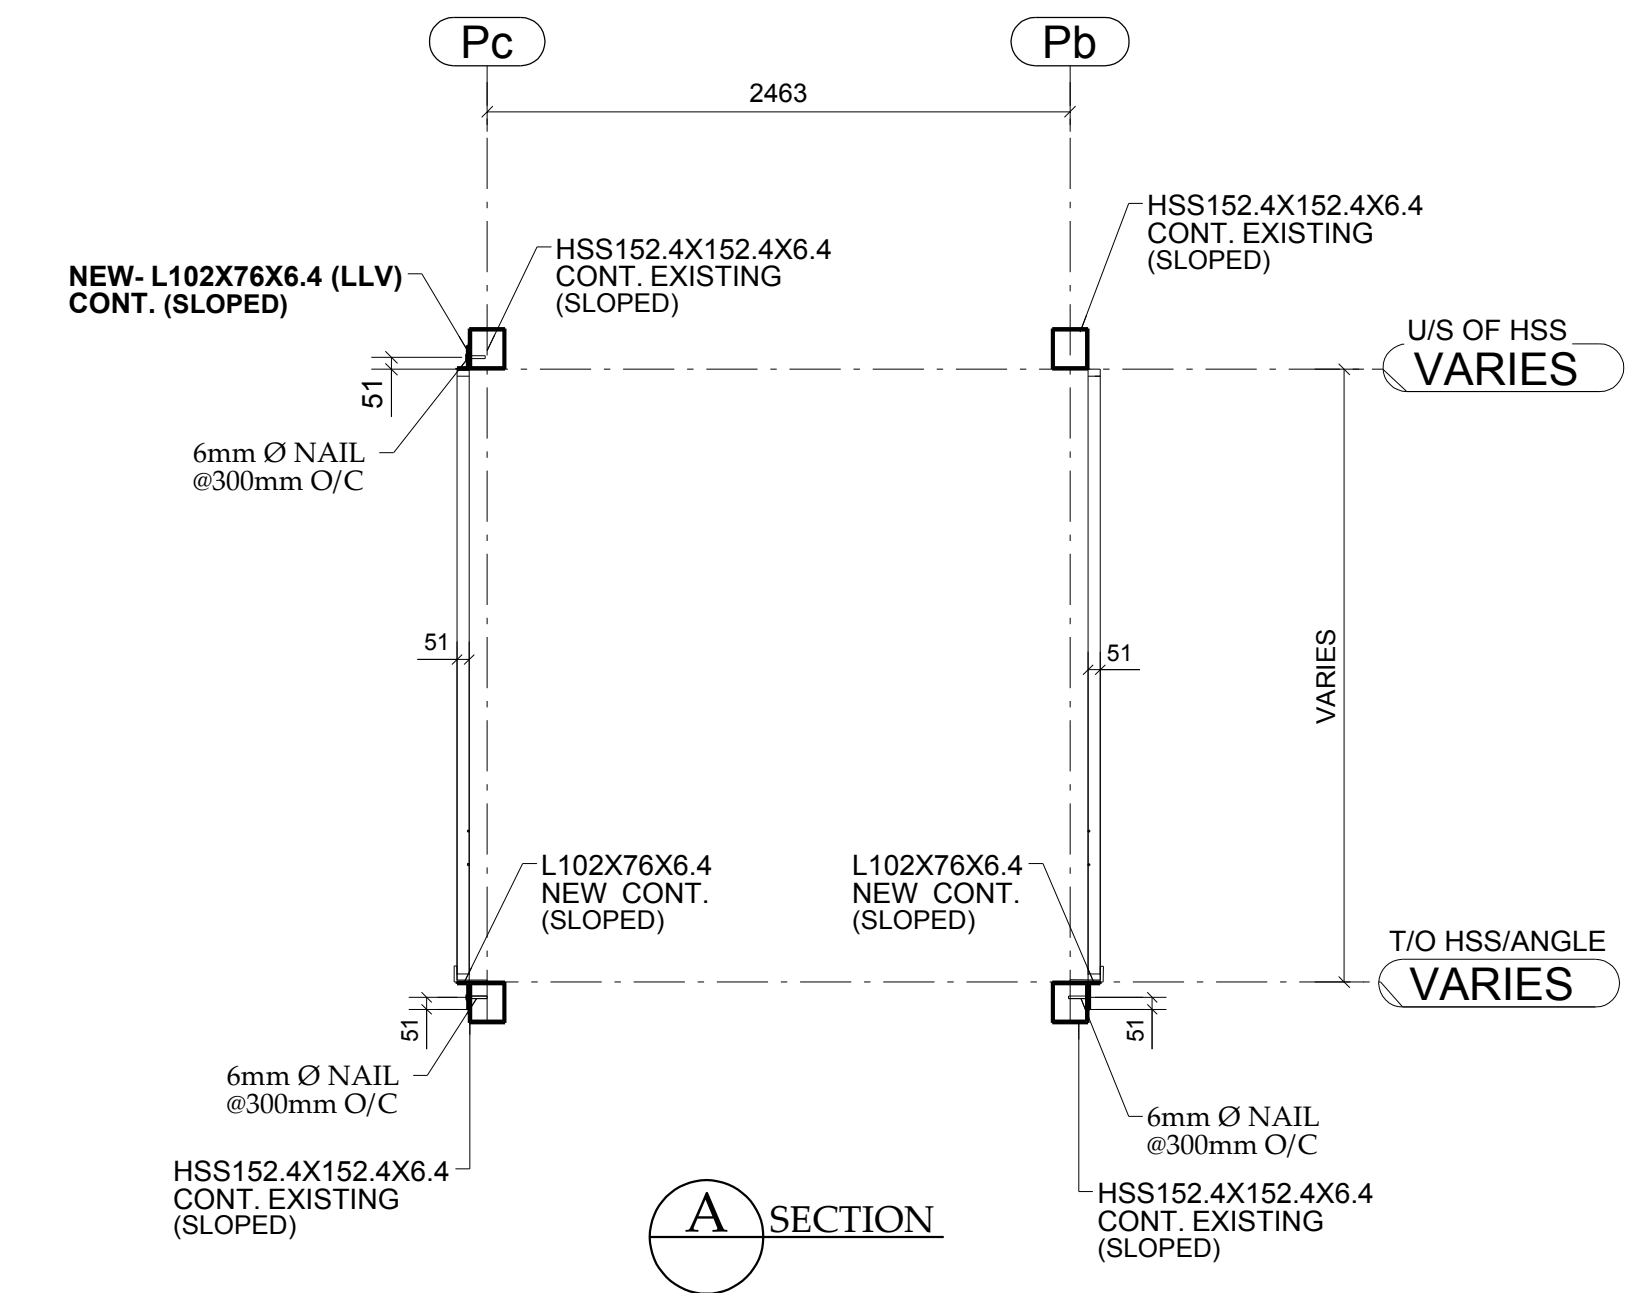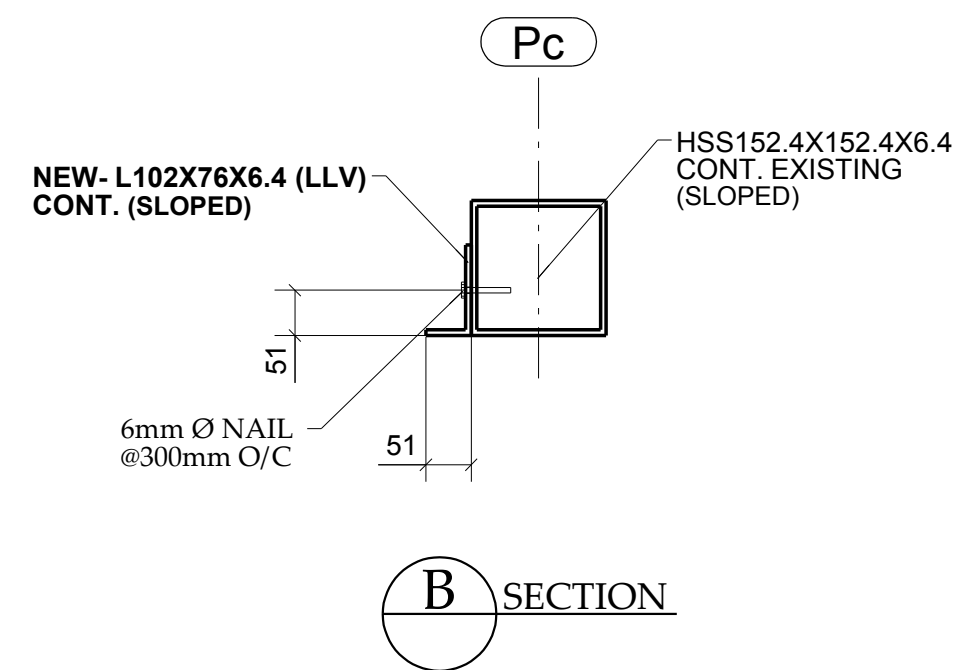

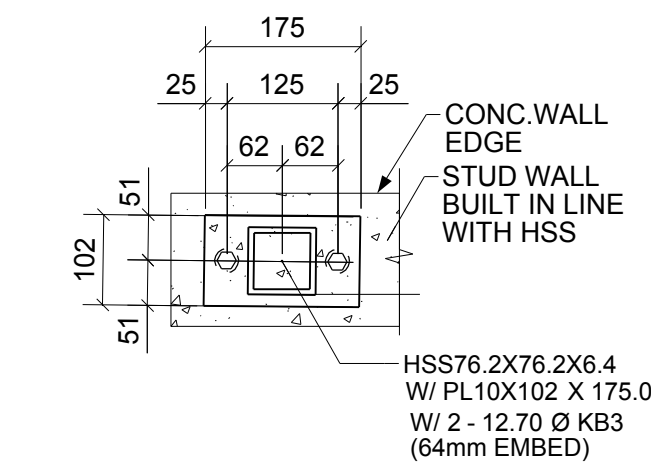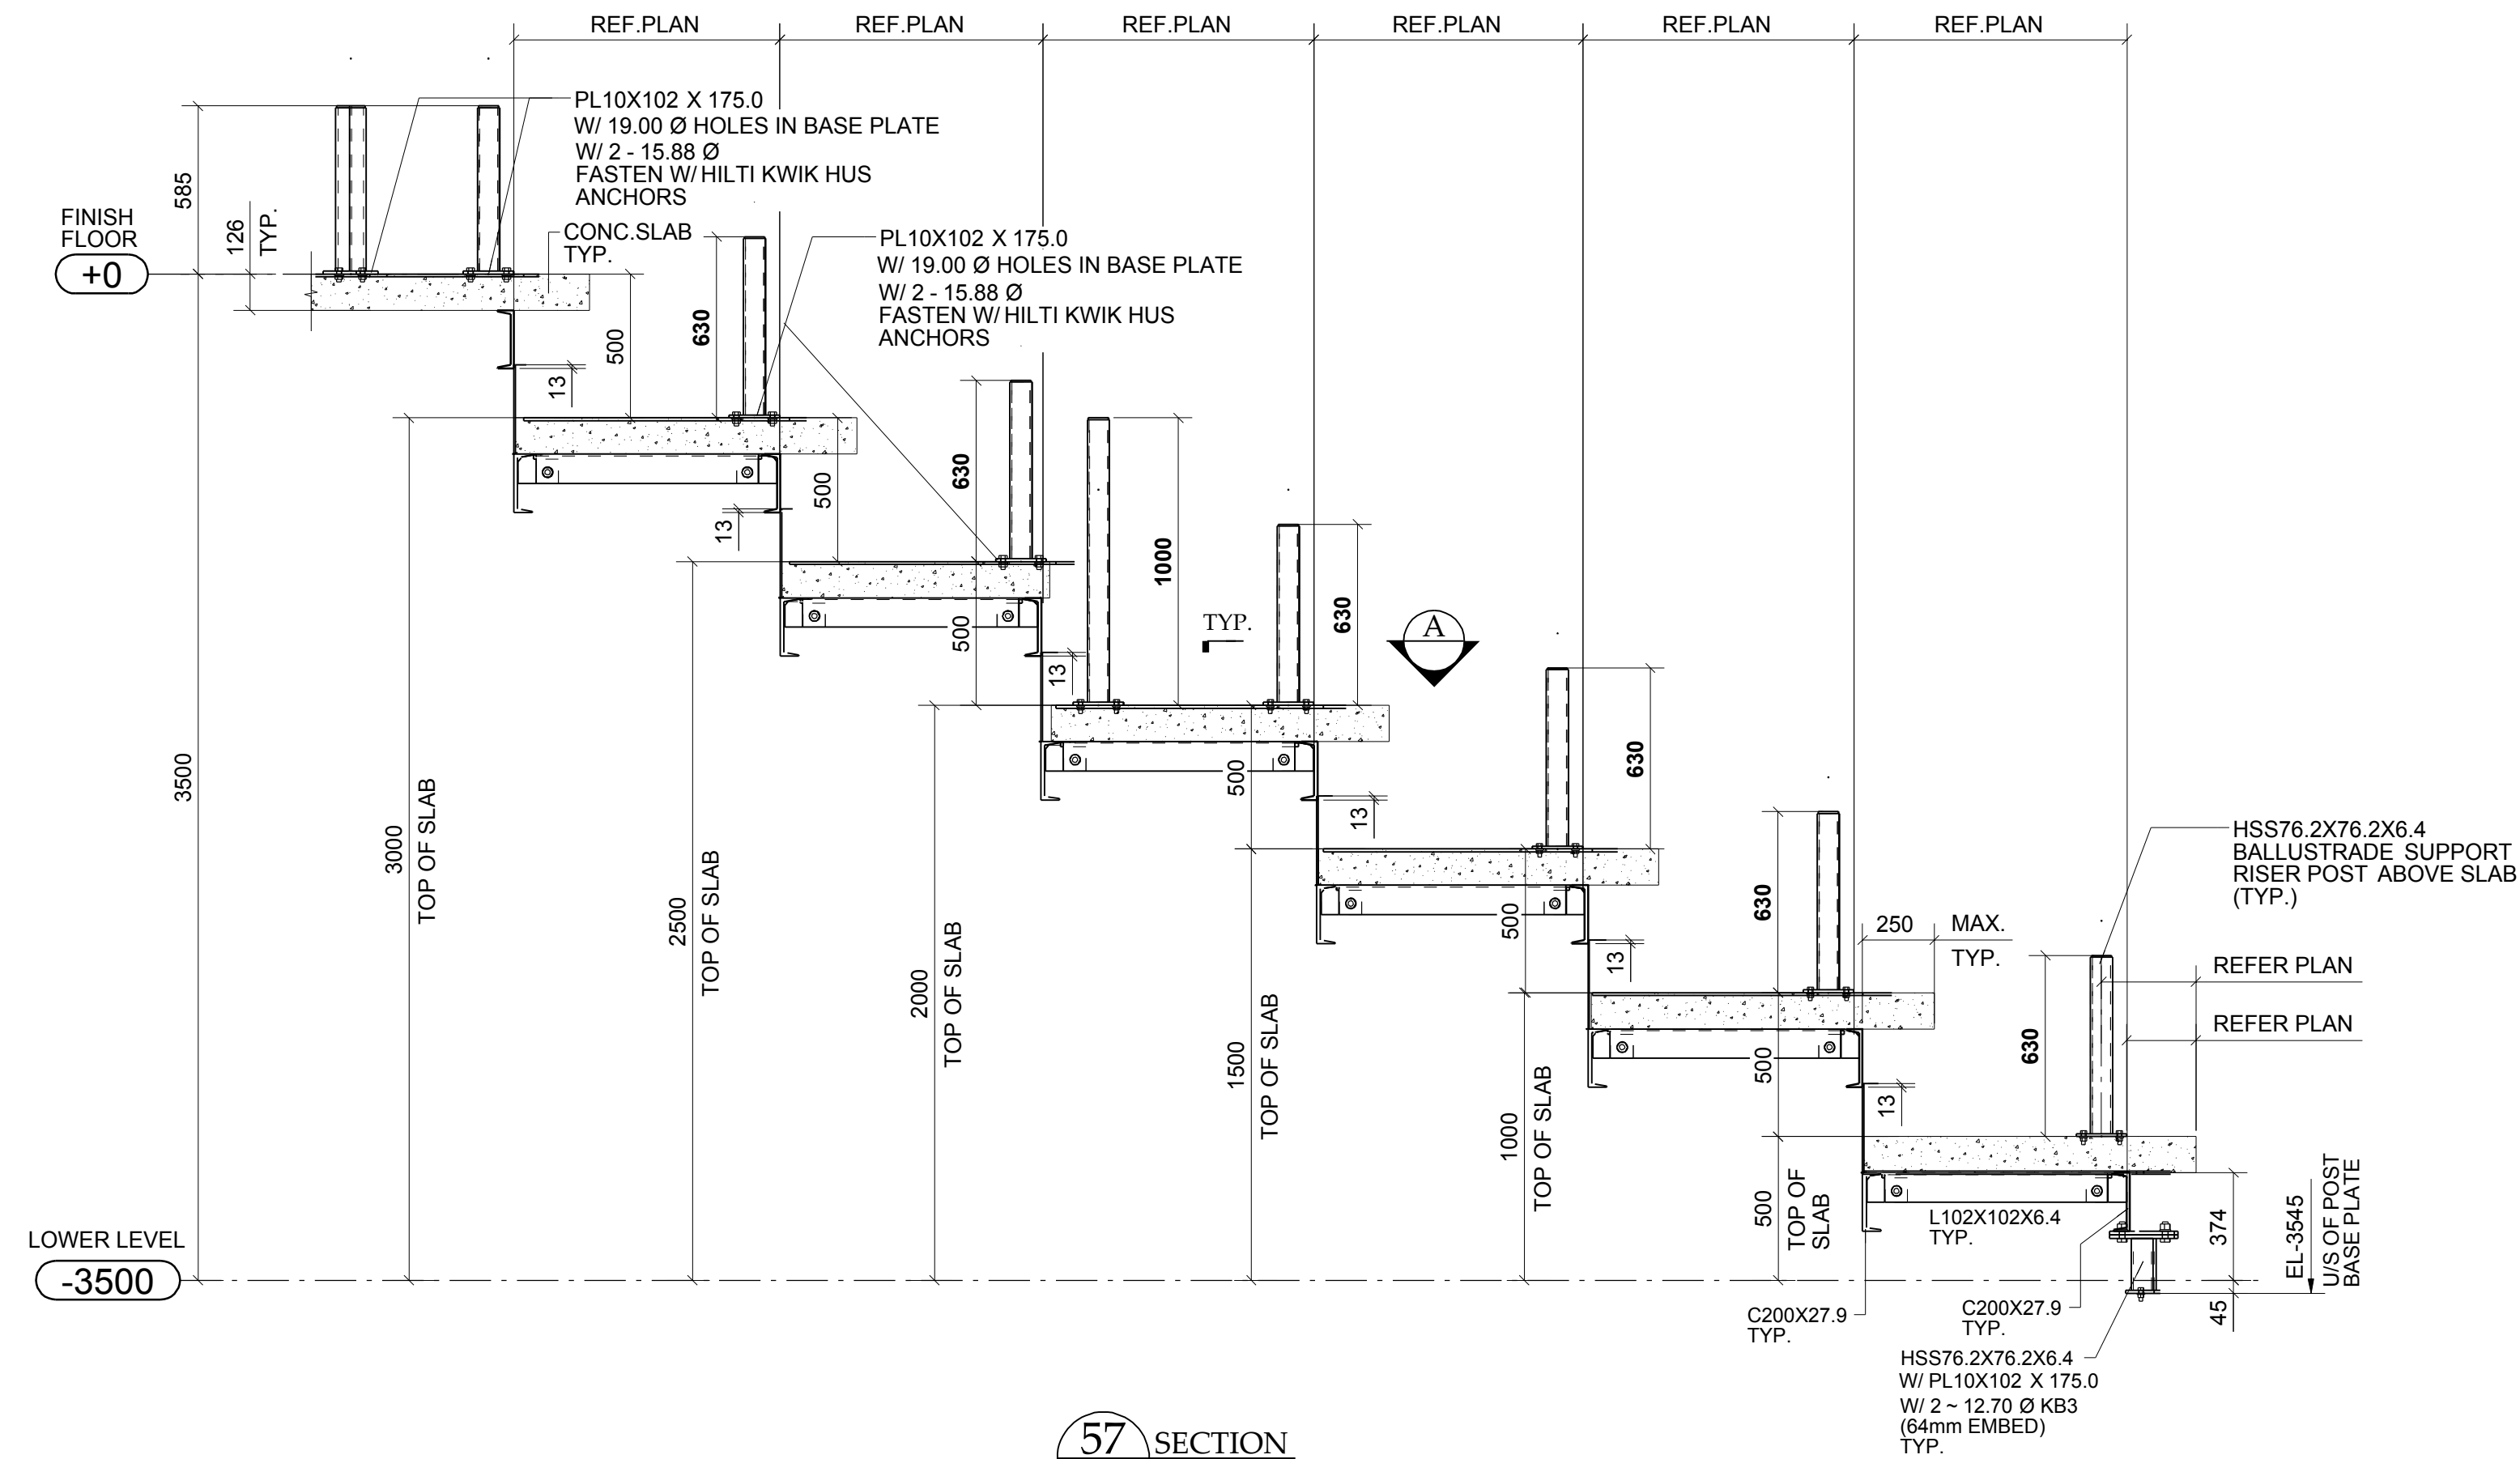



A SECTION

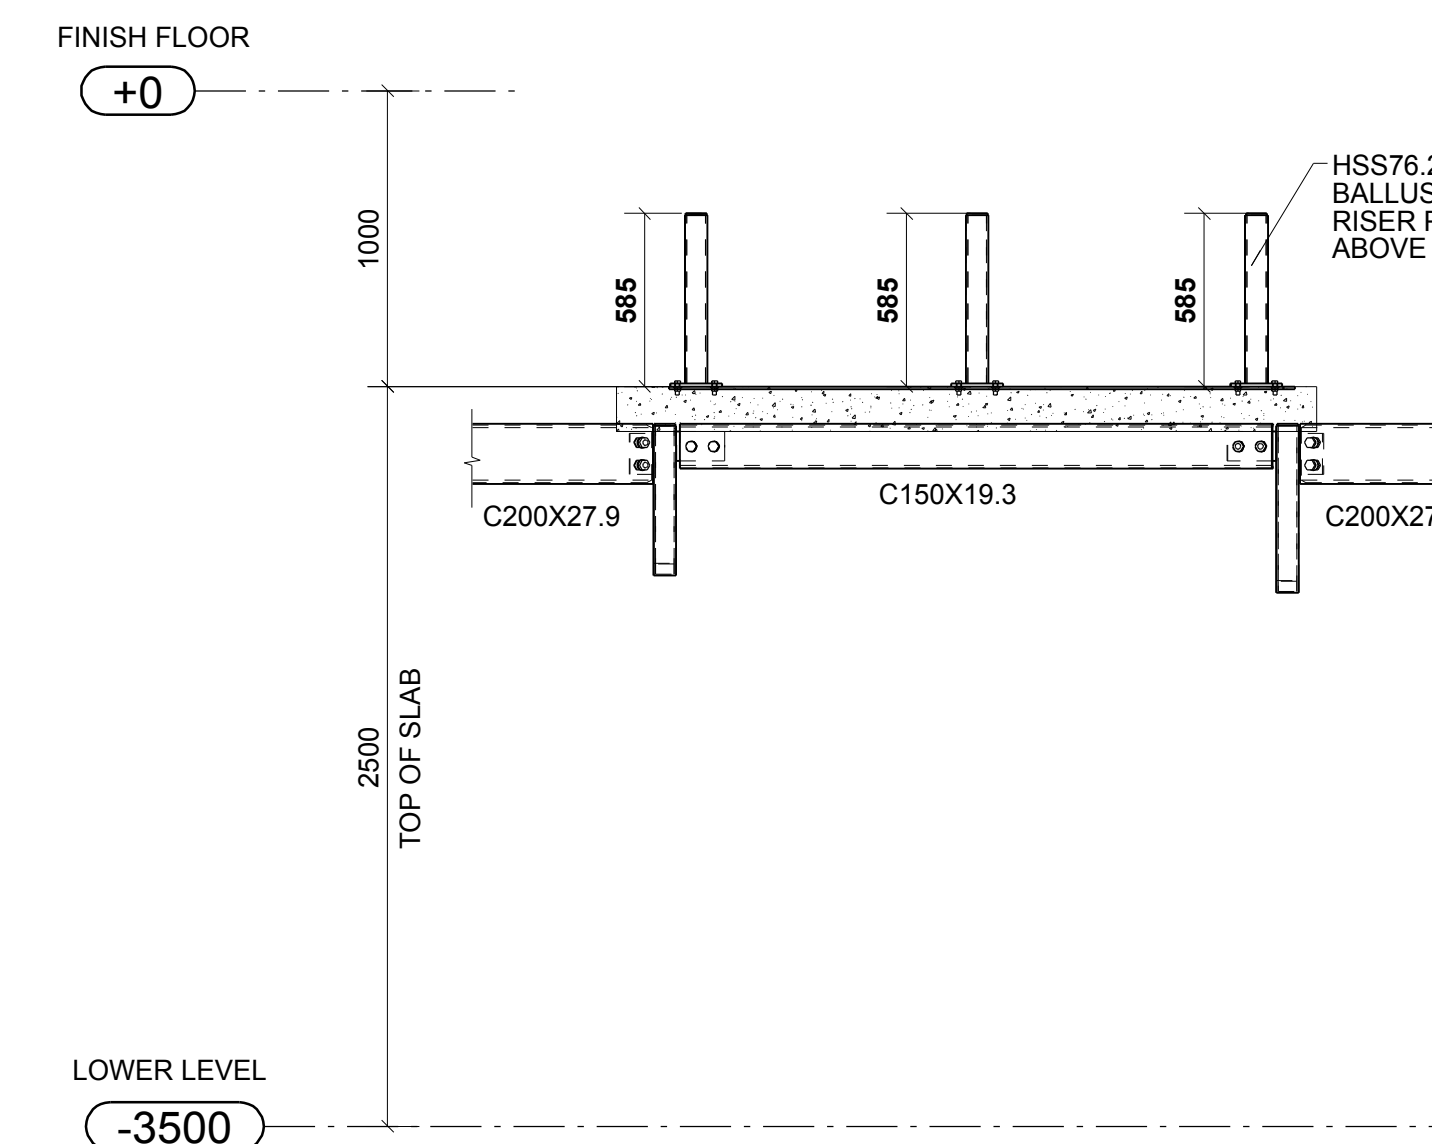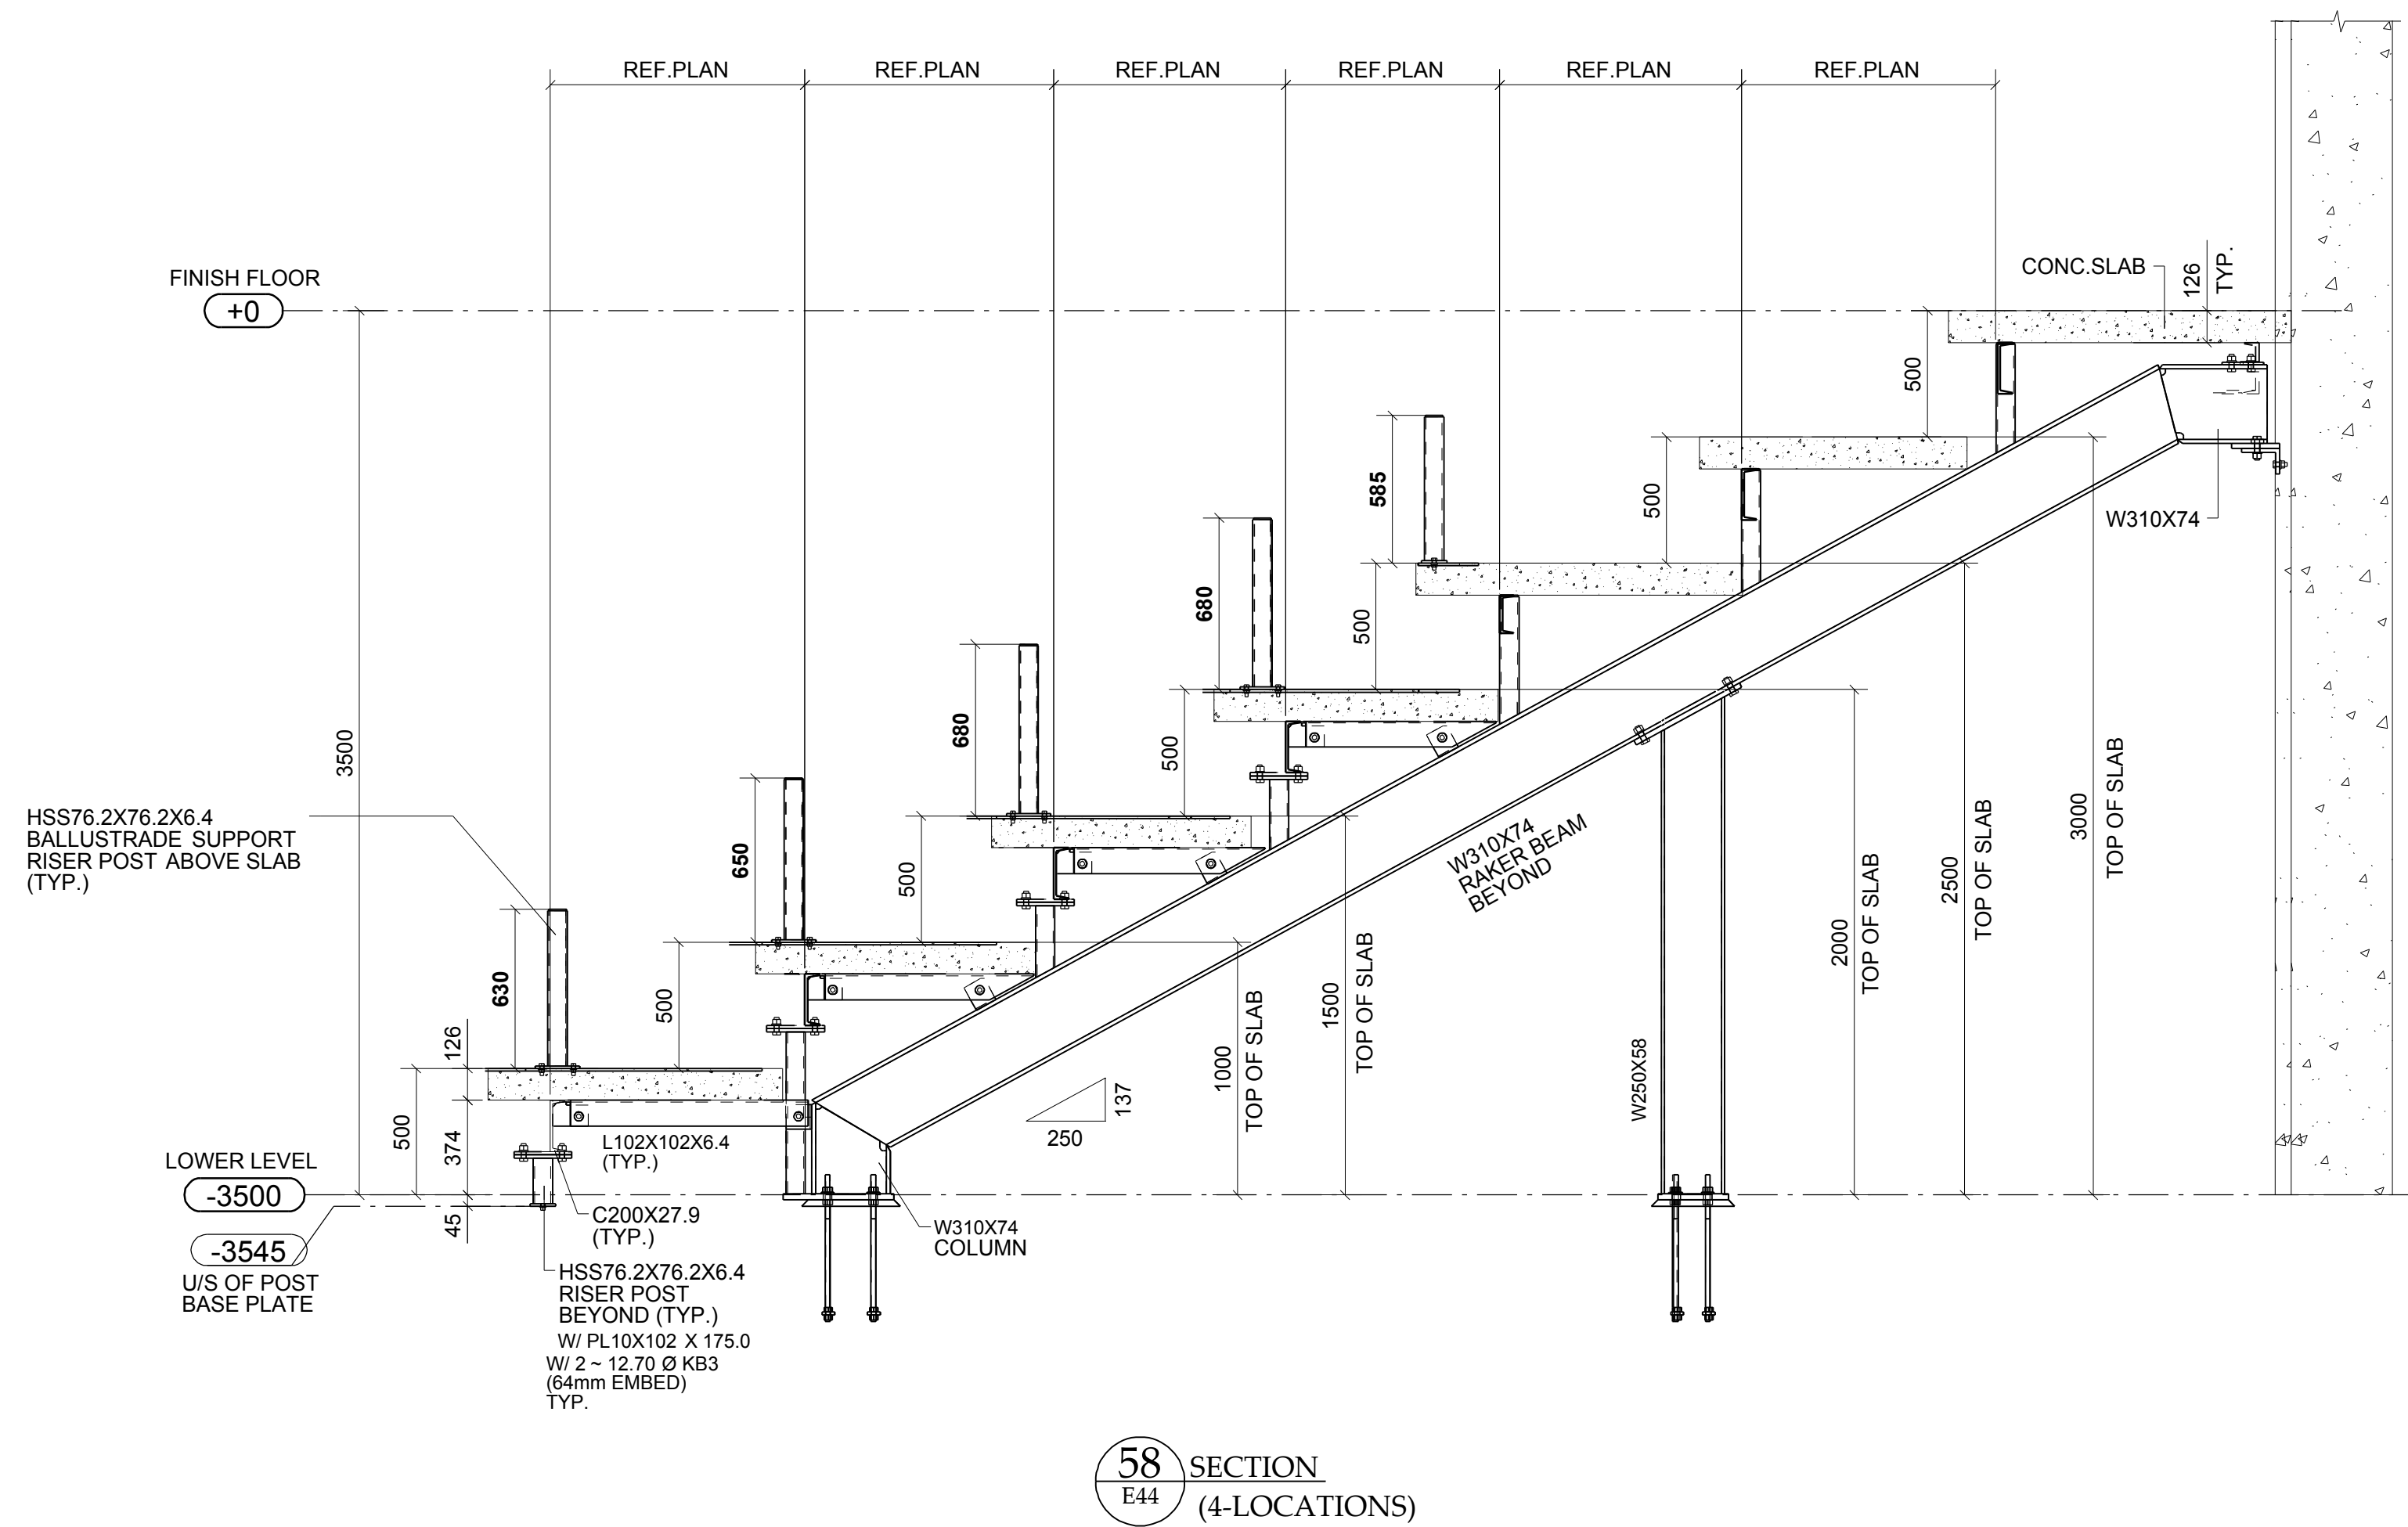





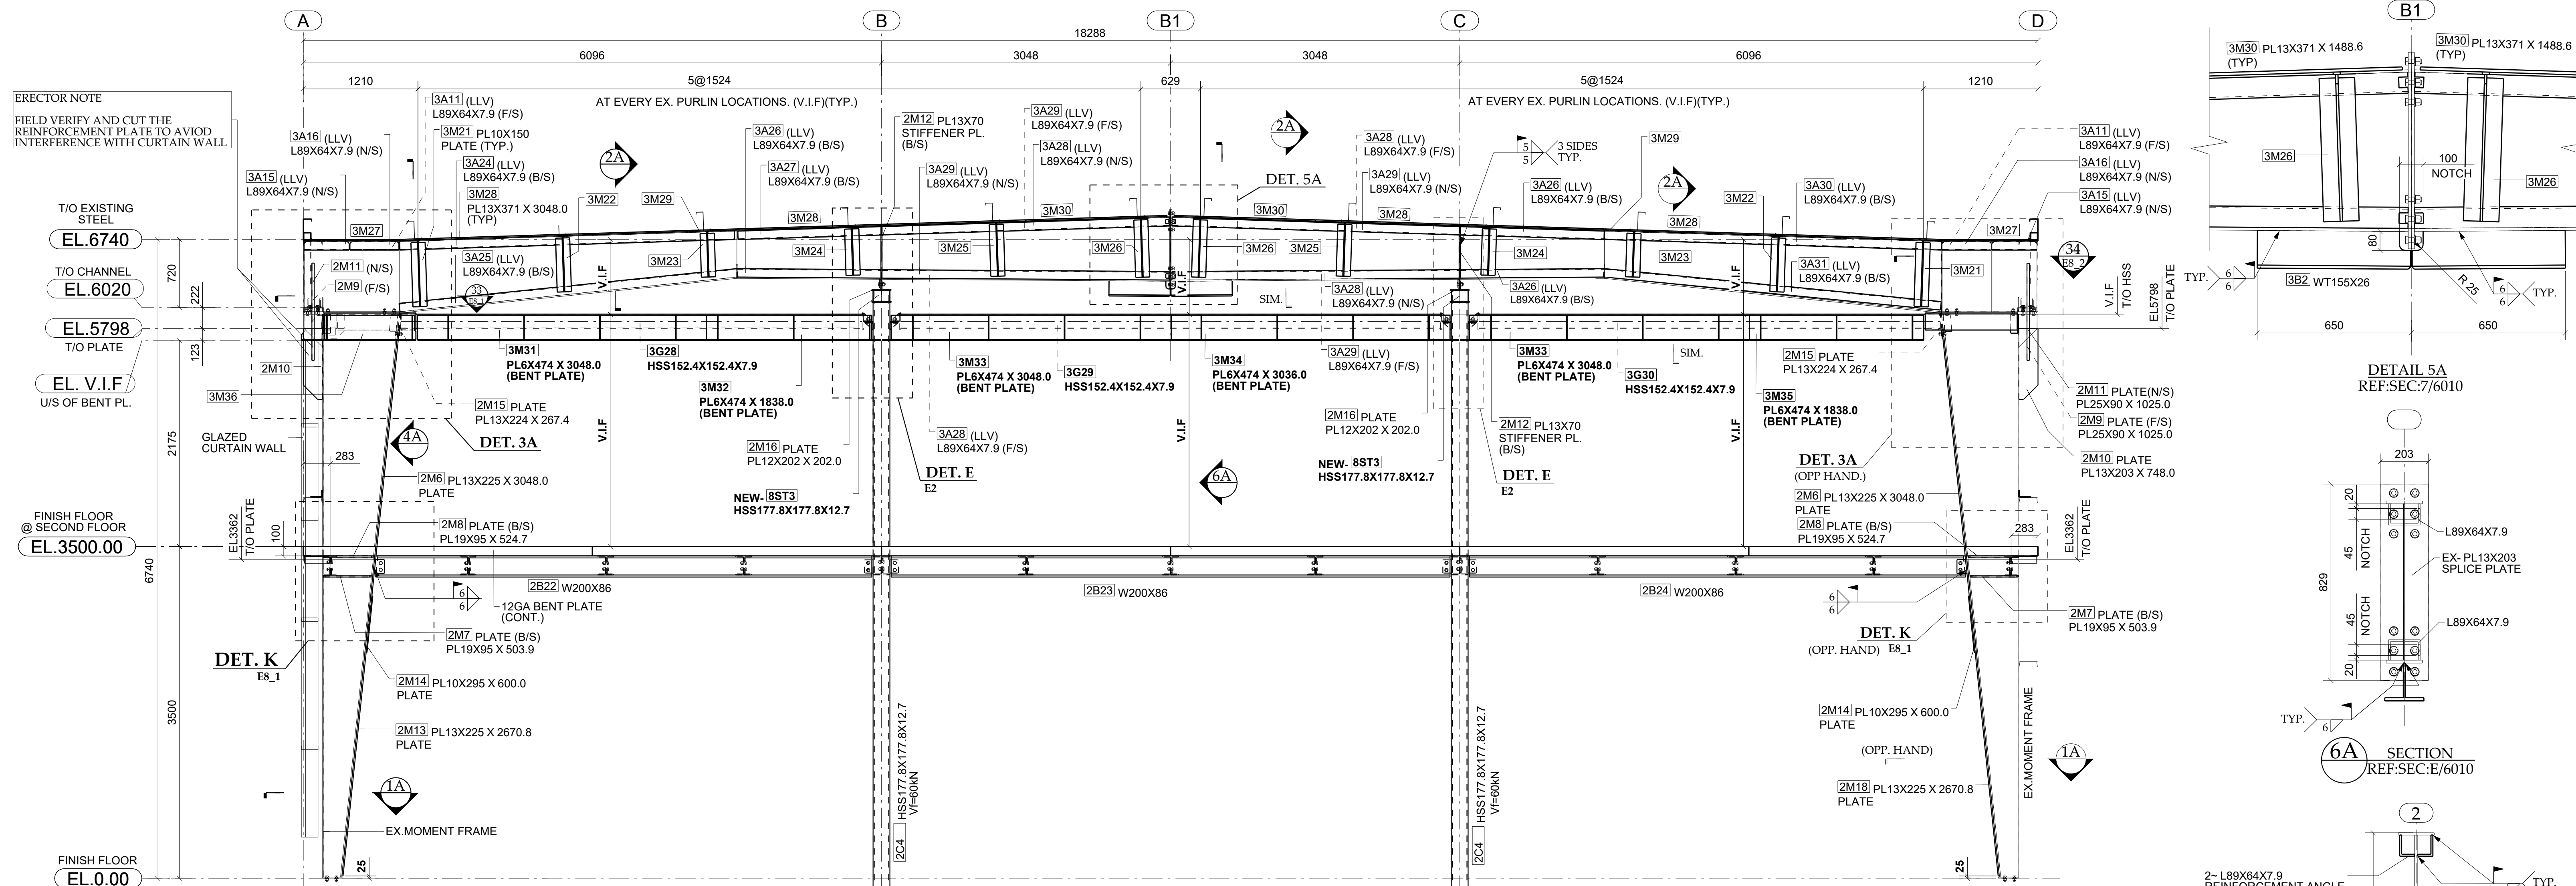



ELEVATION ALONG GRID "2"
REF:SEC.A/6009 & A/2001

ERECTOR NOTE:
CURTAIN WALL SUPPORT HSS (3G28,3G29,3G30)
AND BENT PLATE (3M31,3M32,3M33,3M34,3M35)
ELEVATIONS TO BE CO-ORDINATED WITH GLAZING
SUPPLIER BEFORE ERECTION.

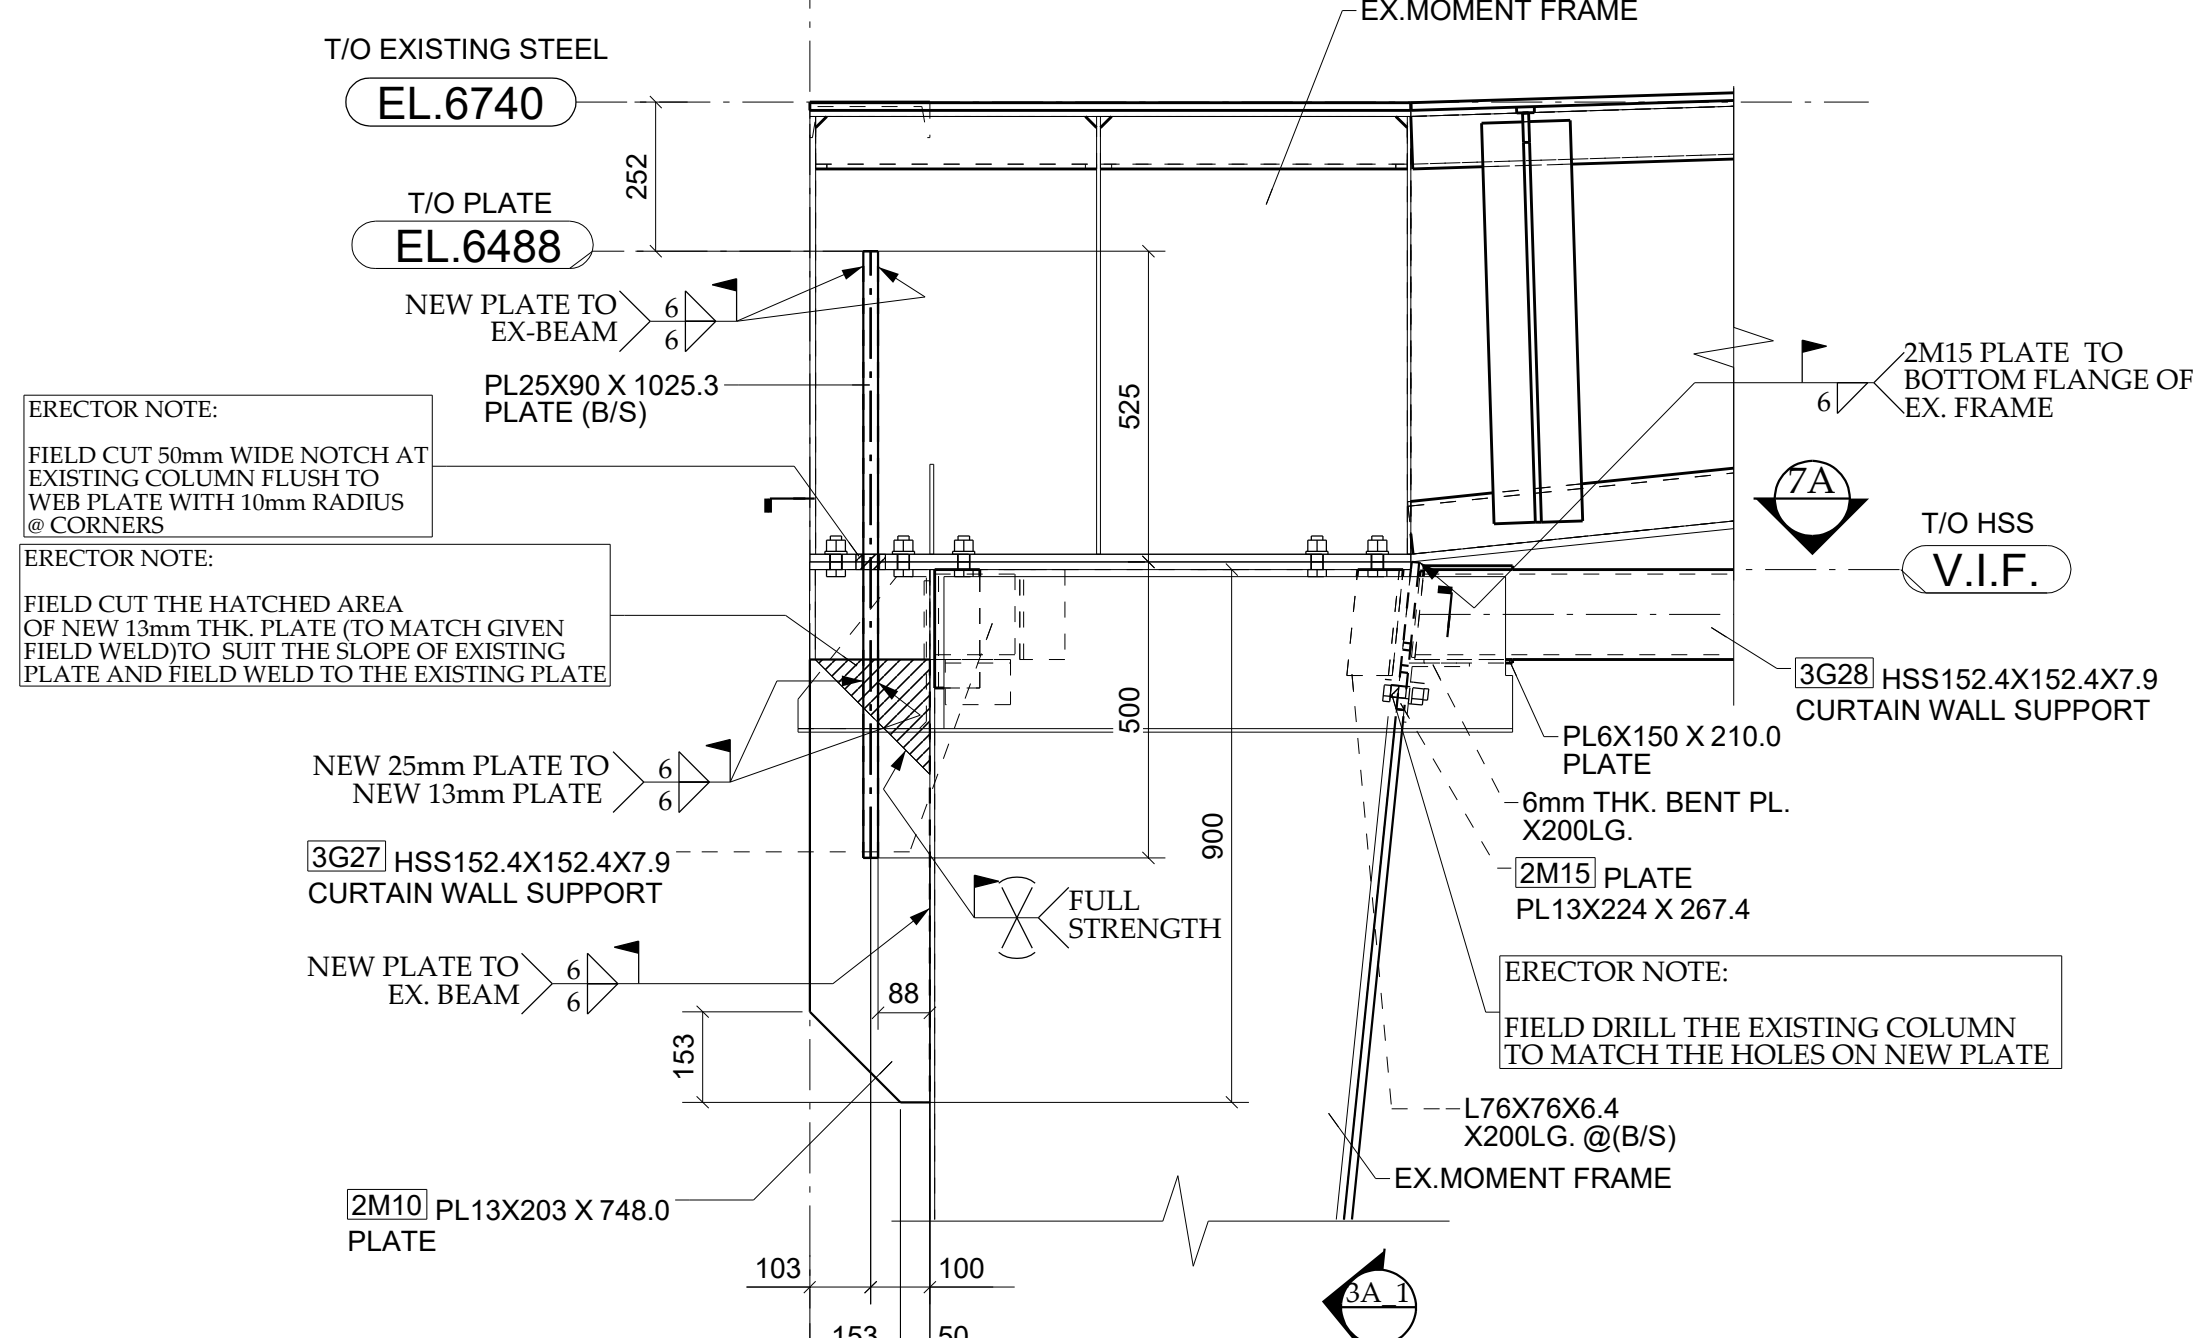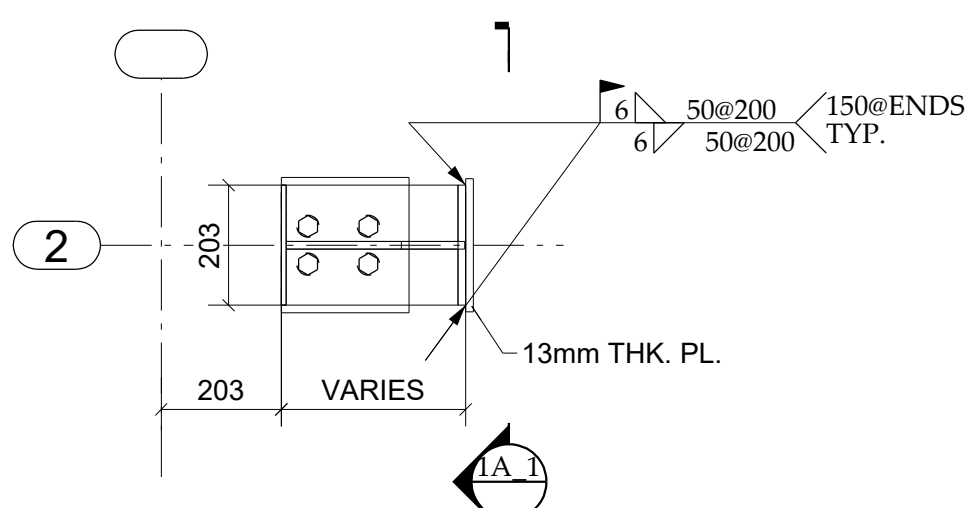


ERECTOR NOTE:
ALL EXISTING COLUMN AND BEAM
REINFORCEMENT TO BE COMPLETED
PRIOR TO INSTALLING NEW FRAMING MEMBERS

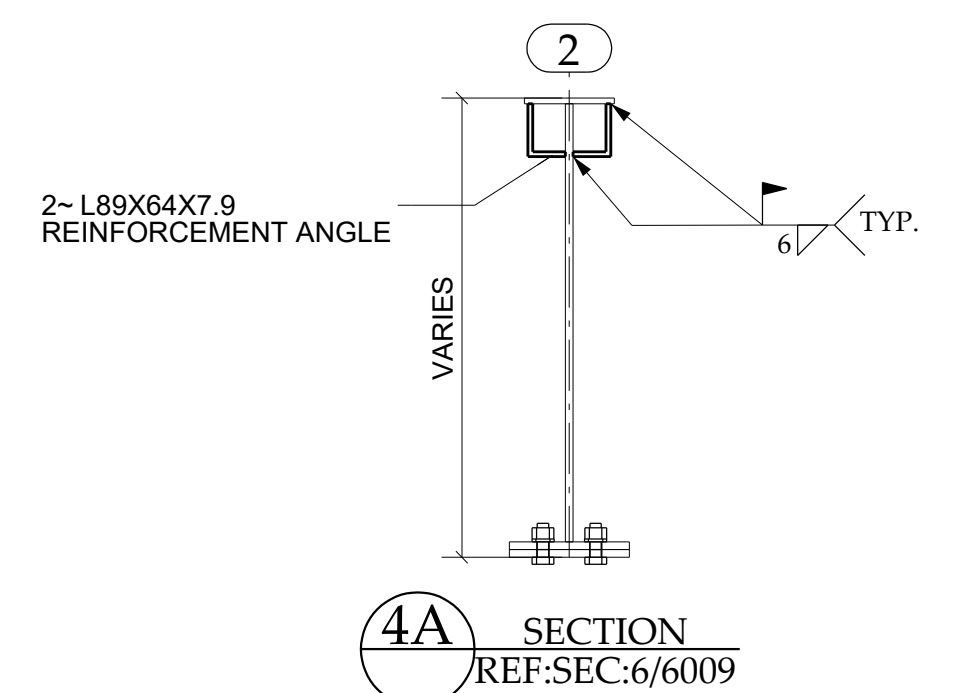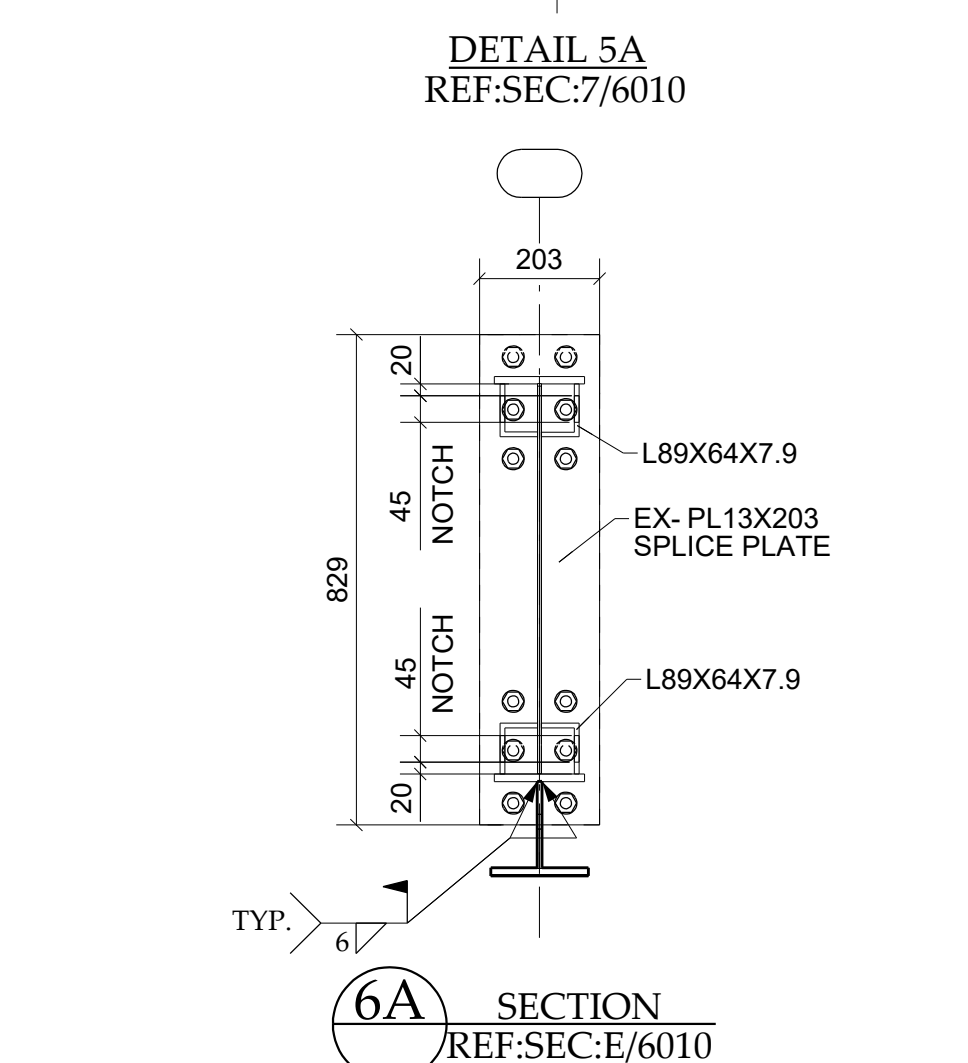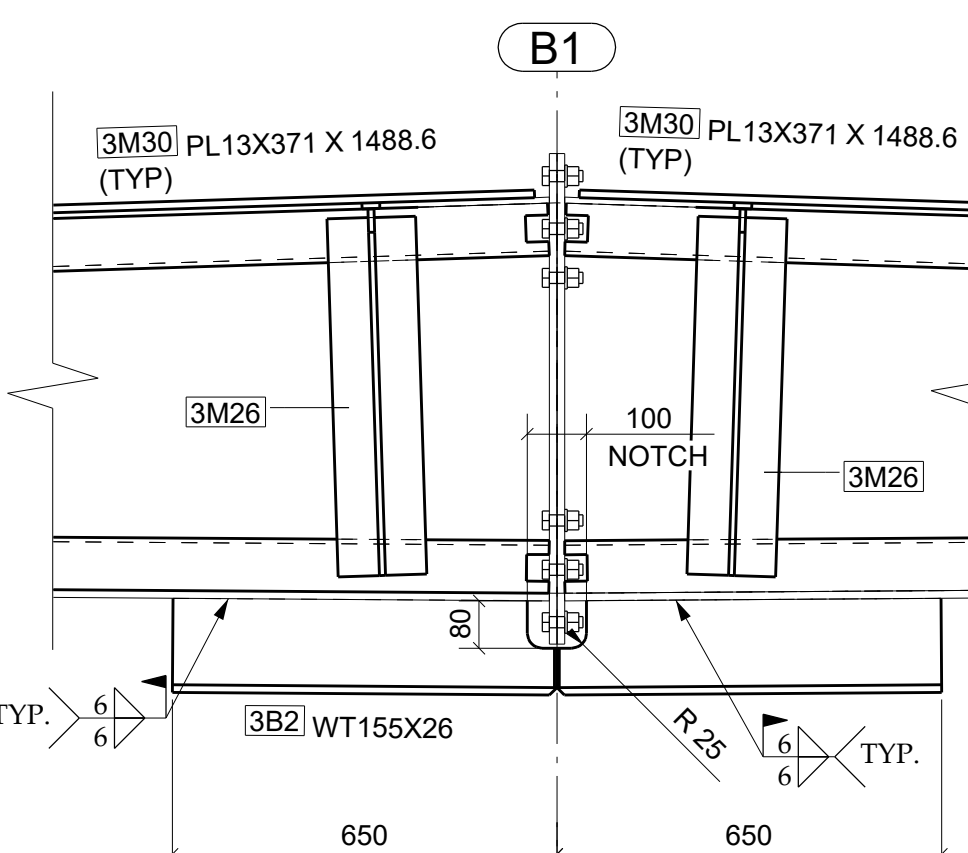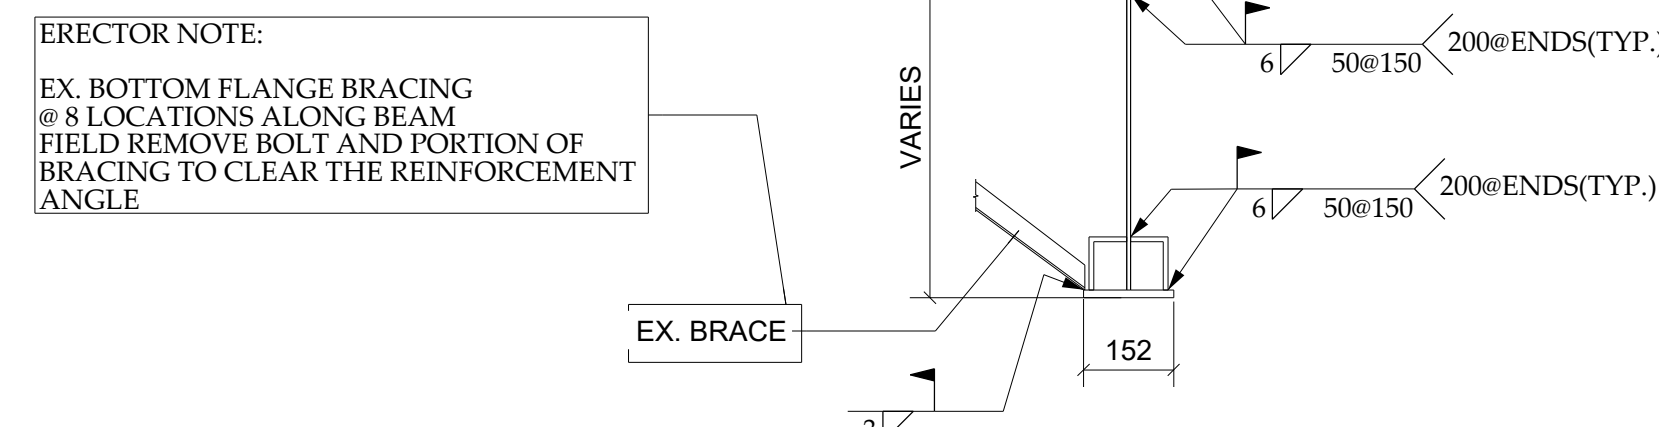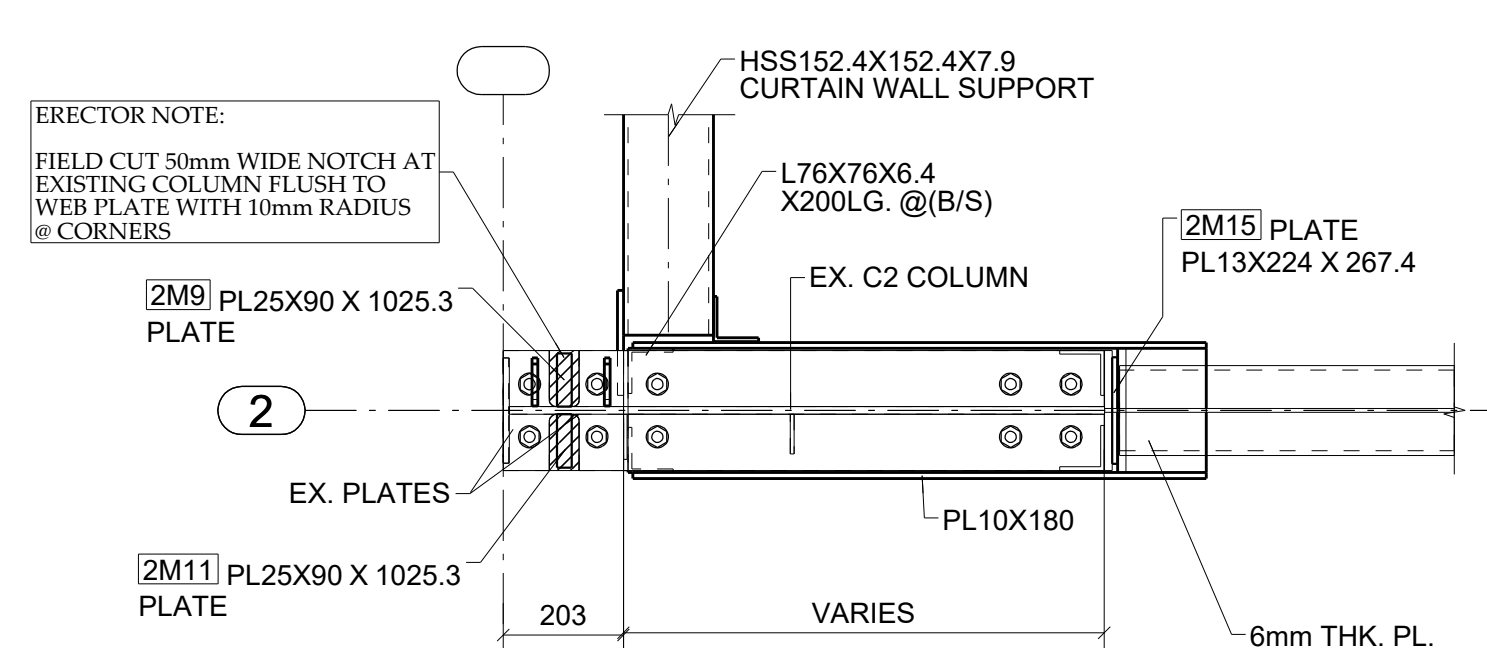

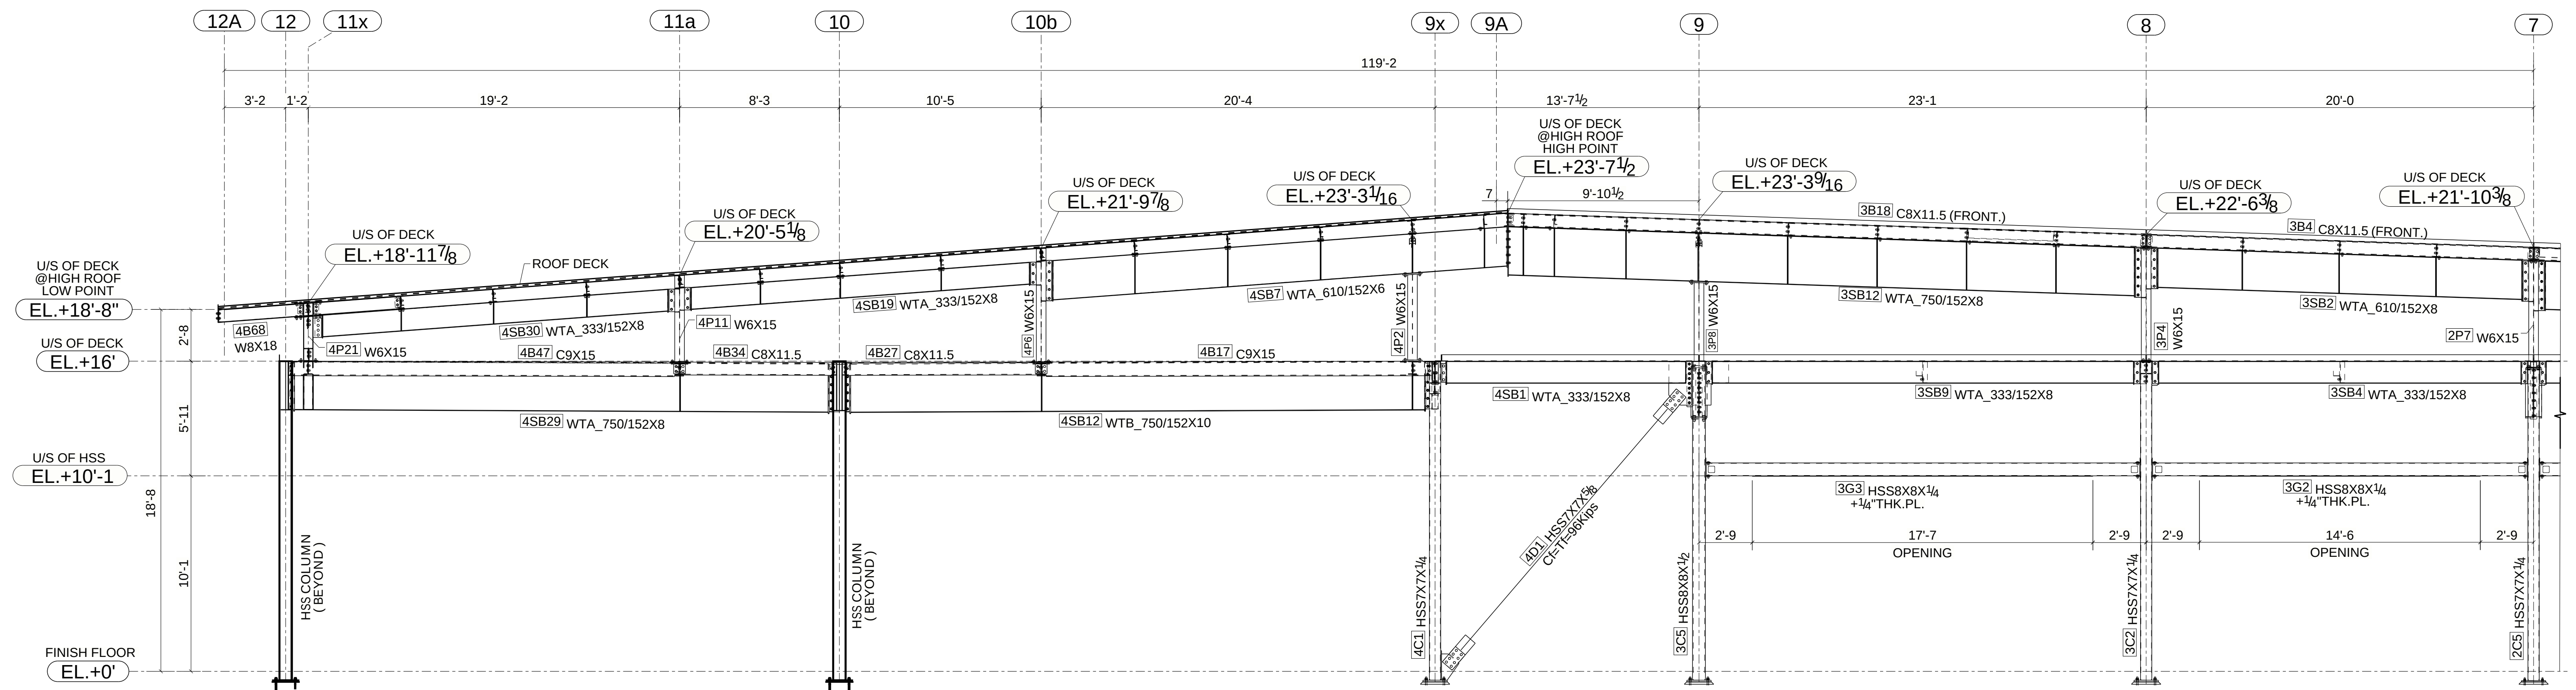

PARTIAL ELEVATION ALONG GRIDLINE 'E'
(REFER SHEET : S401)

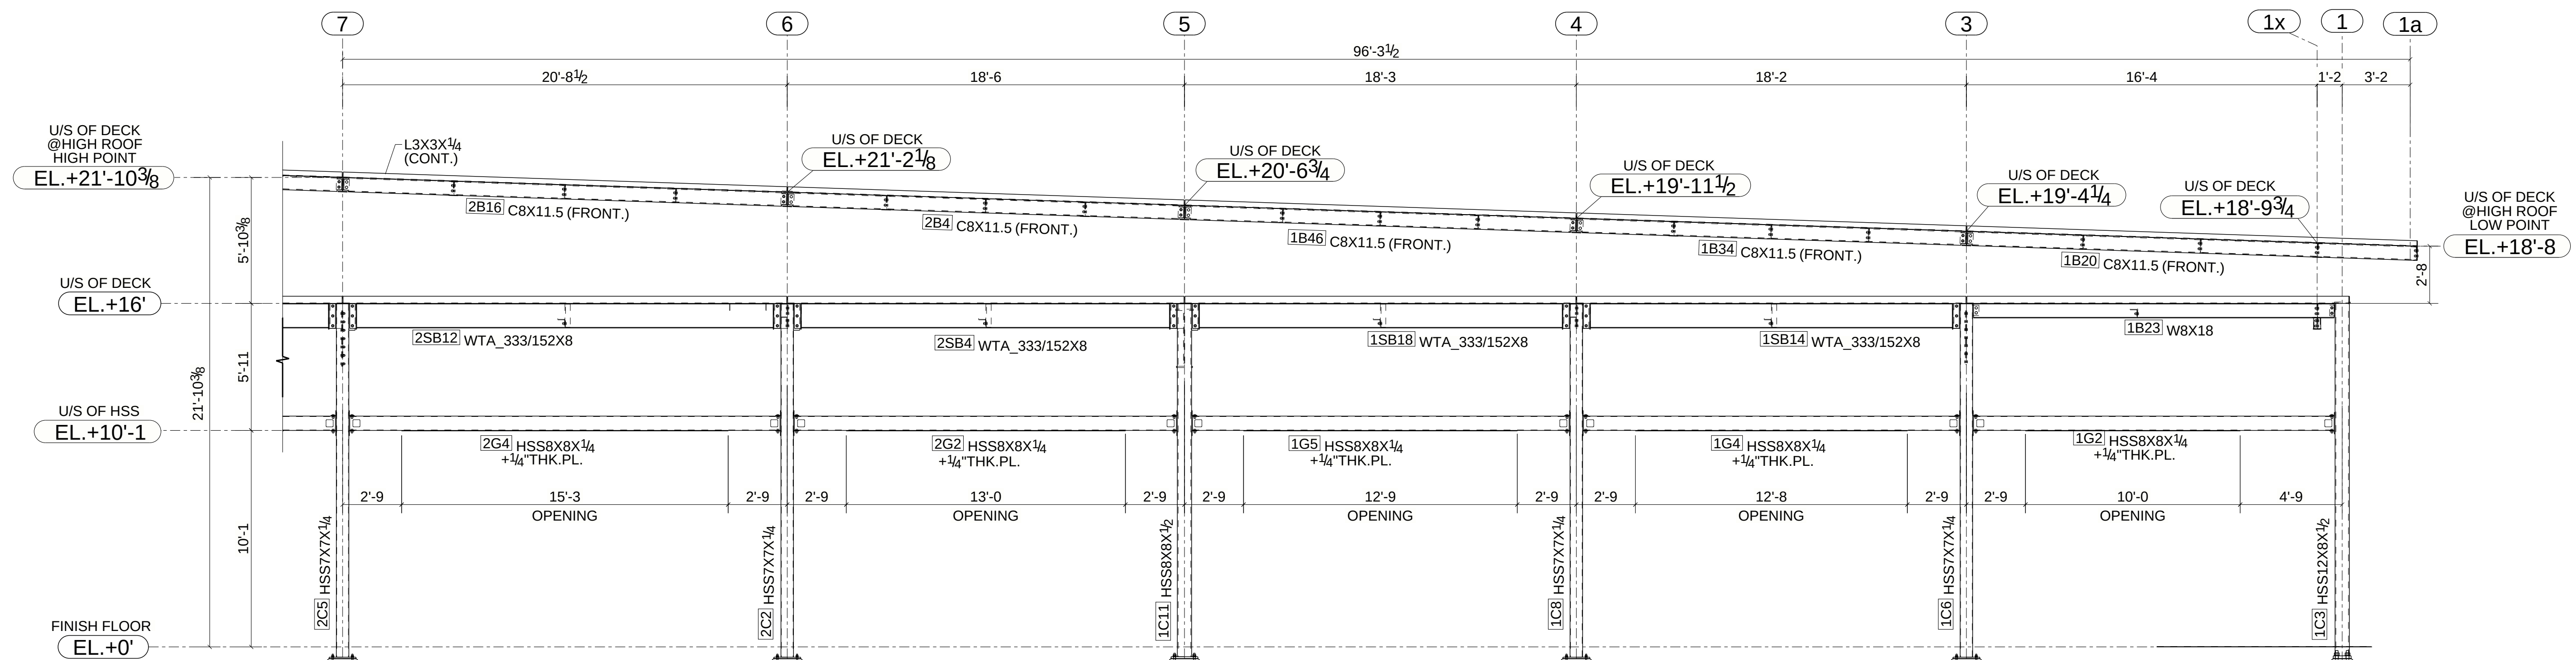

PARTIAL ELEVATION ALONG GRIDLINE 'E'
(REFER SHEET : S401)