




MATCH LINE
REFER SHEET E16


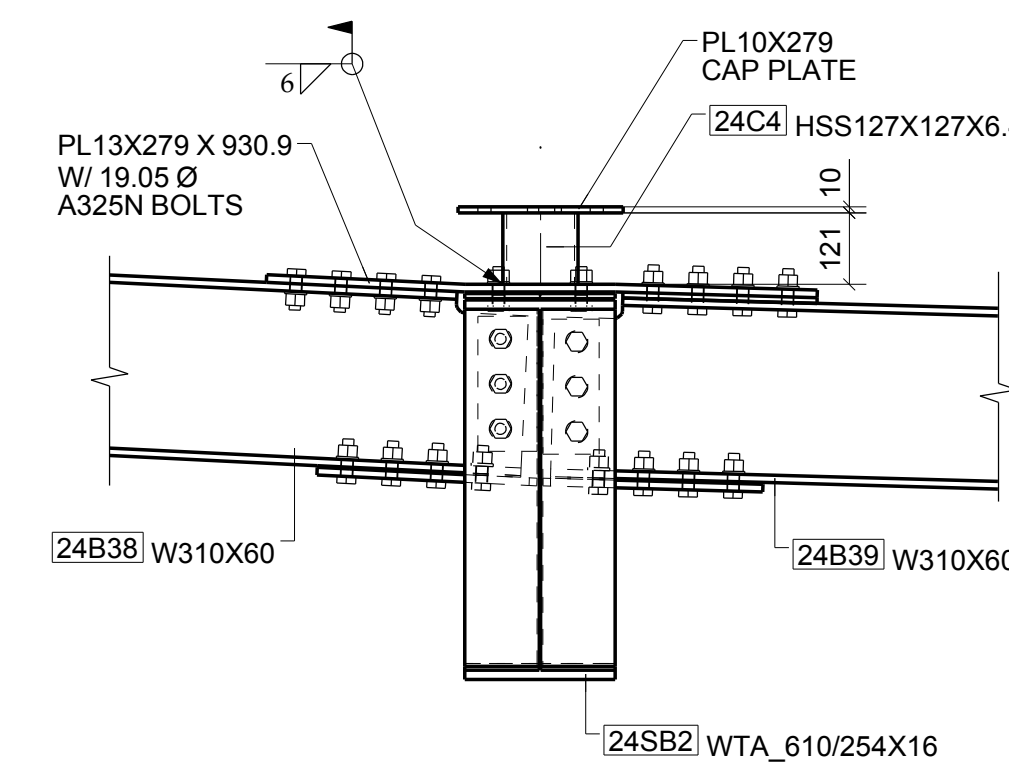


A SECTION

REFER 'DET. J/E18' FOR
LOW LEVEL FRAMING PLAN


- NOTES:-
- ROOF DATUM EL. = 131500 U.N.O.
 - +/- VALUES SHOWN IN PLAN ARE REFERRED FROM ROOF DATUM ELEVATION 131500
 - RA INDICATES ROOF ANCHORS (REF. TYPICAL SEC. @ SHEET E31)
 - E.O.A. INDICATES EDGE OF ANGLE
 - E.O.B.P.L. INDICATES EDGE OF BENT PL.
 - ⬤ INDICATES ORIENTATION OF MEMBER

PARTIAL TERMINAL BUILDING LEVEL-2 FRAMING PLAN
(REF. PLAN S221)

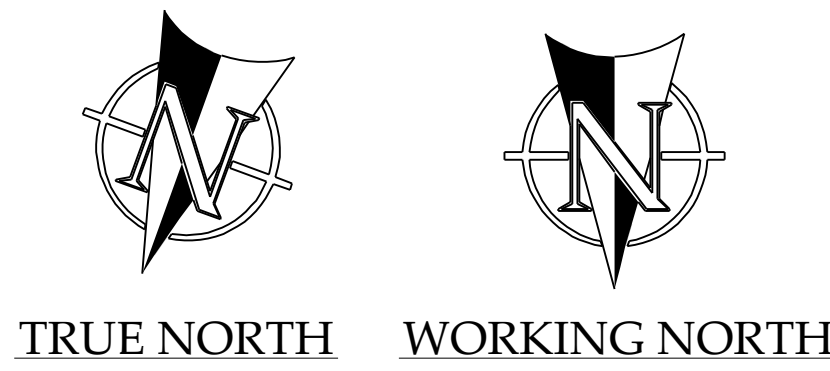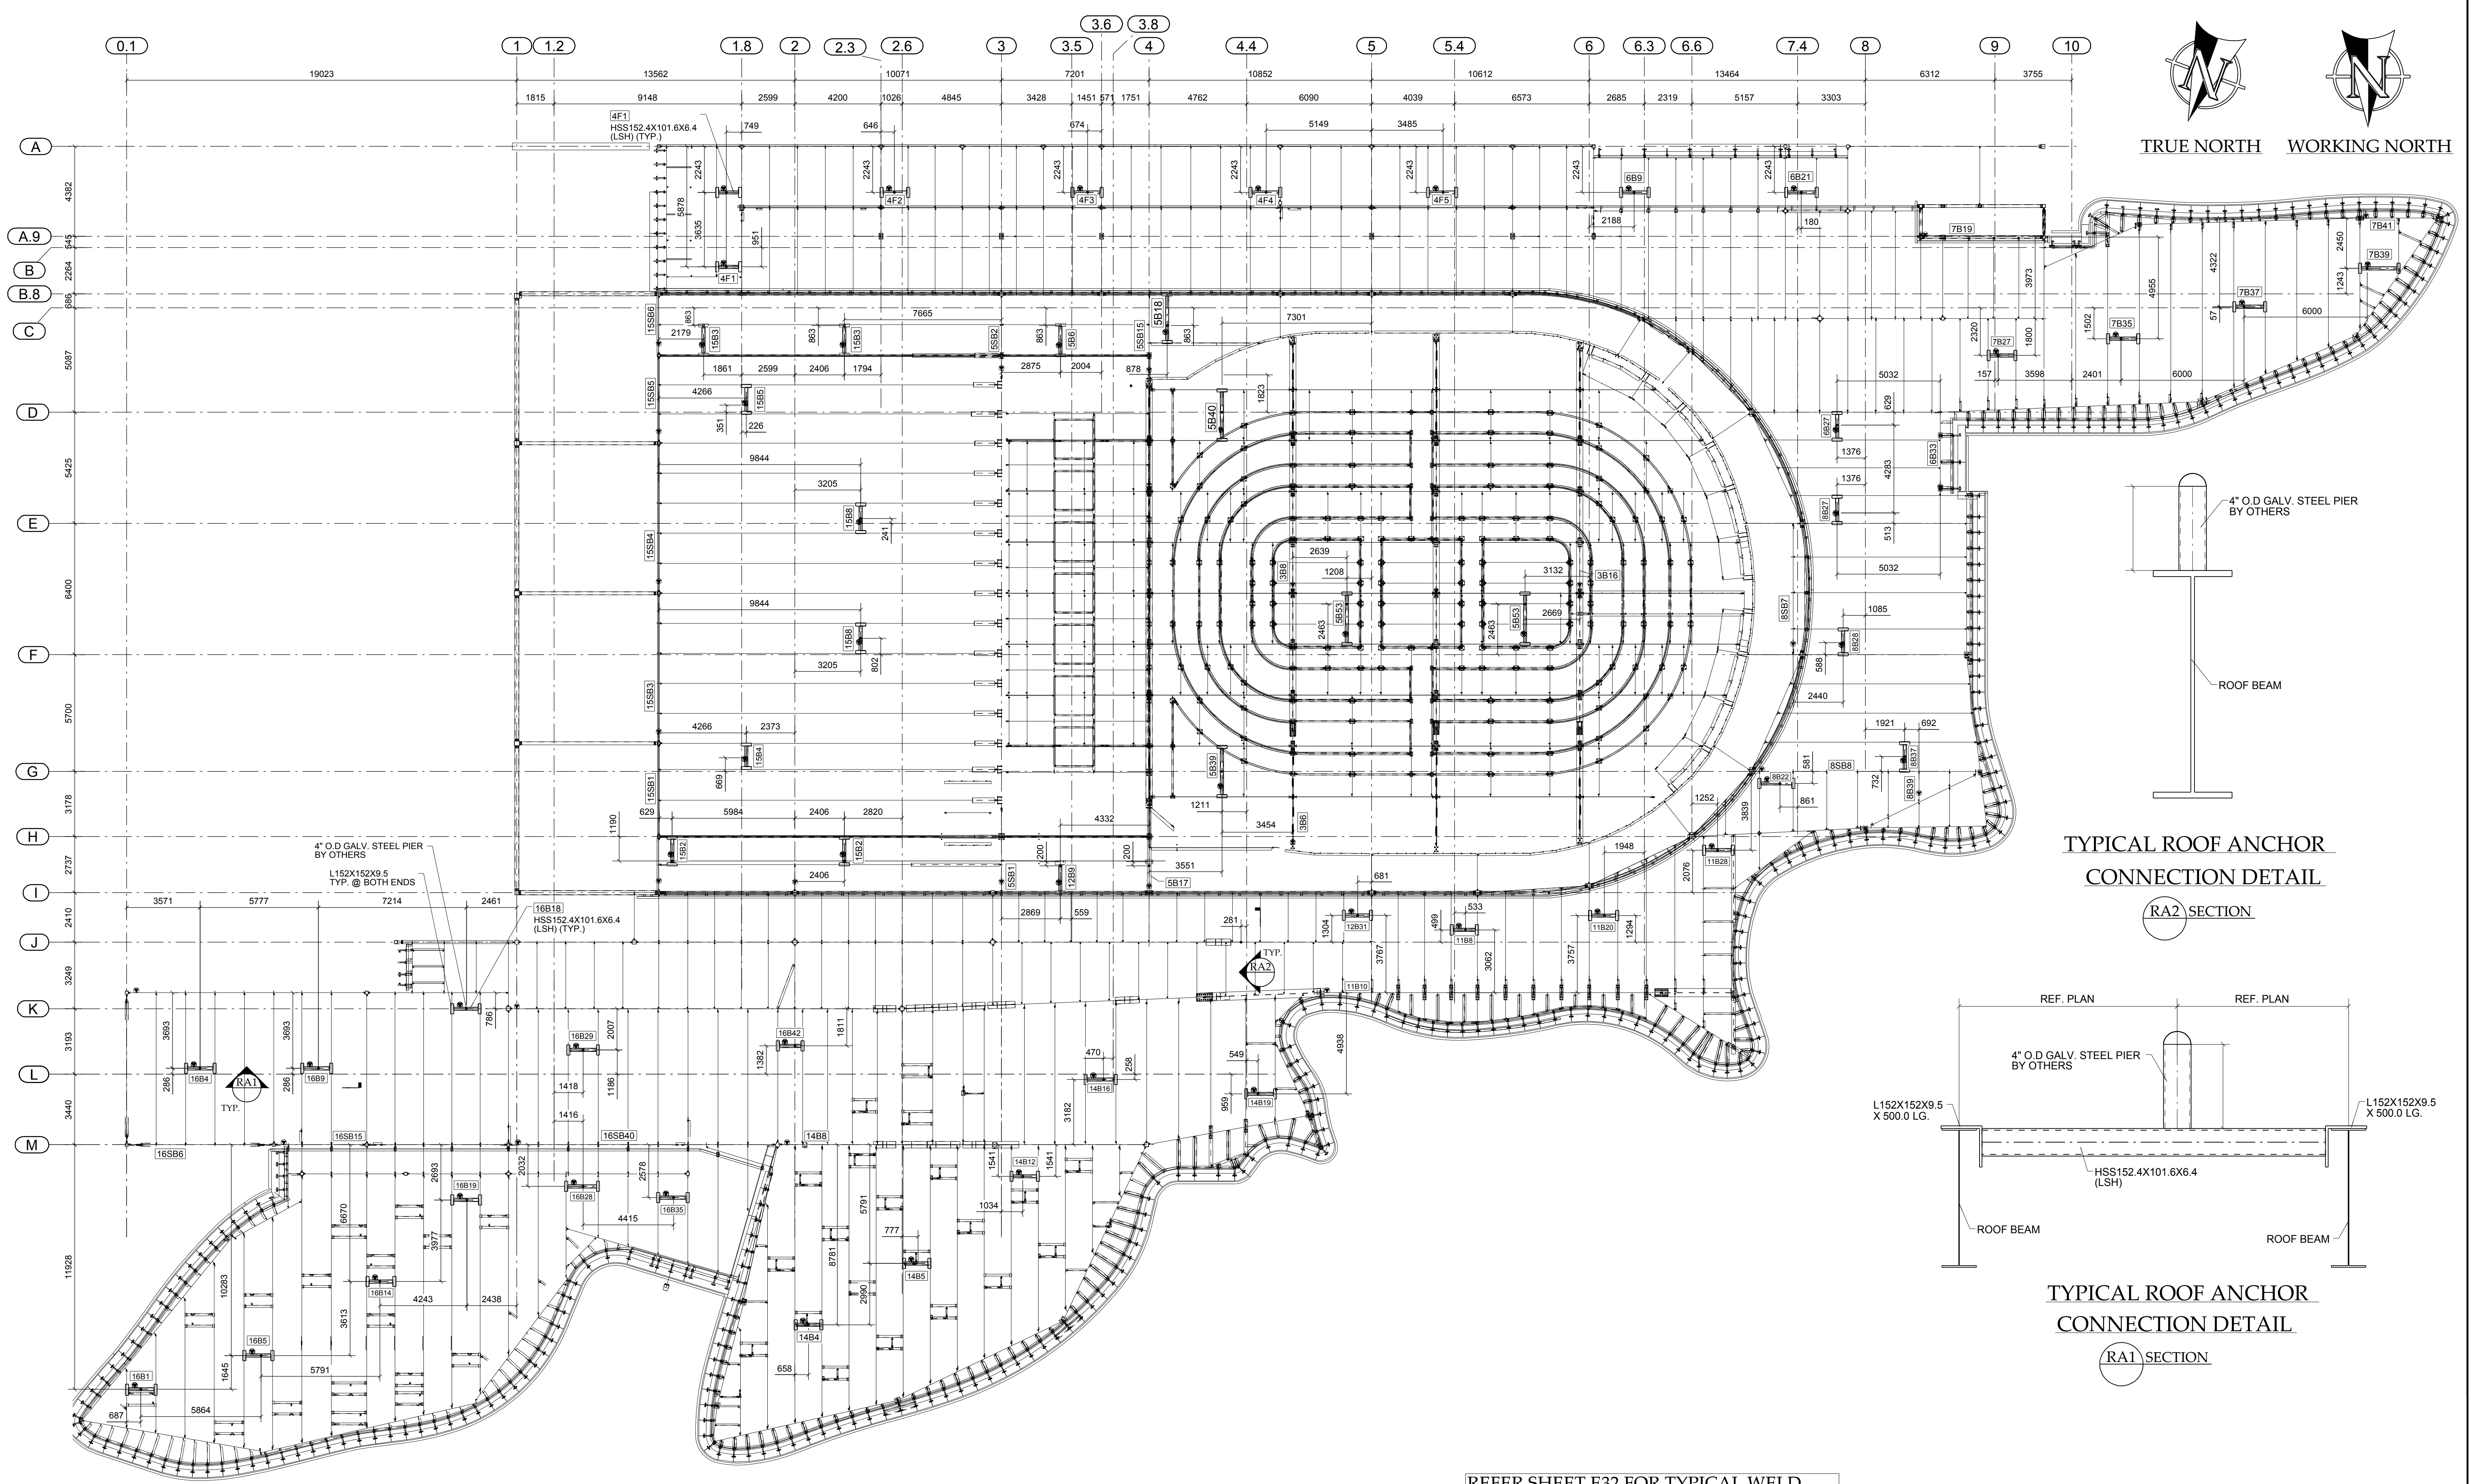

TYPICAL ROOF ANCHOR
CONNECTION DETAIL

RA2 SECTION

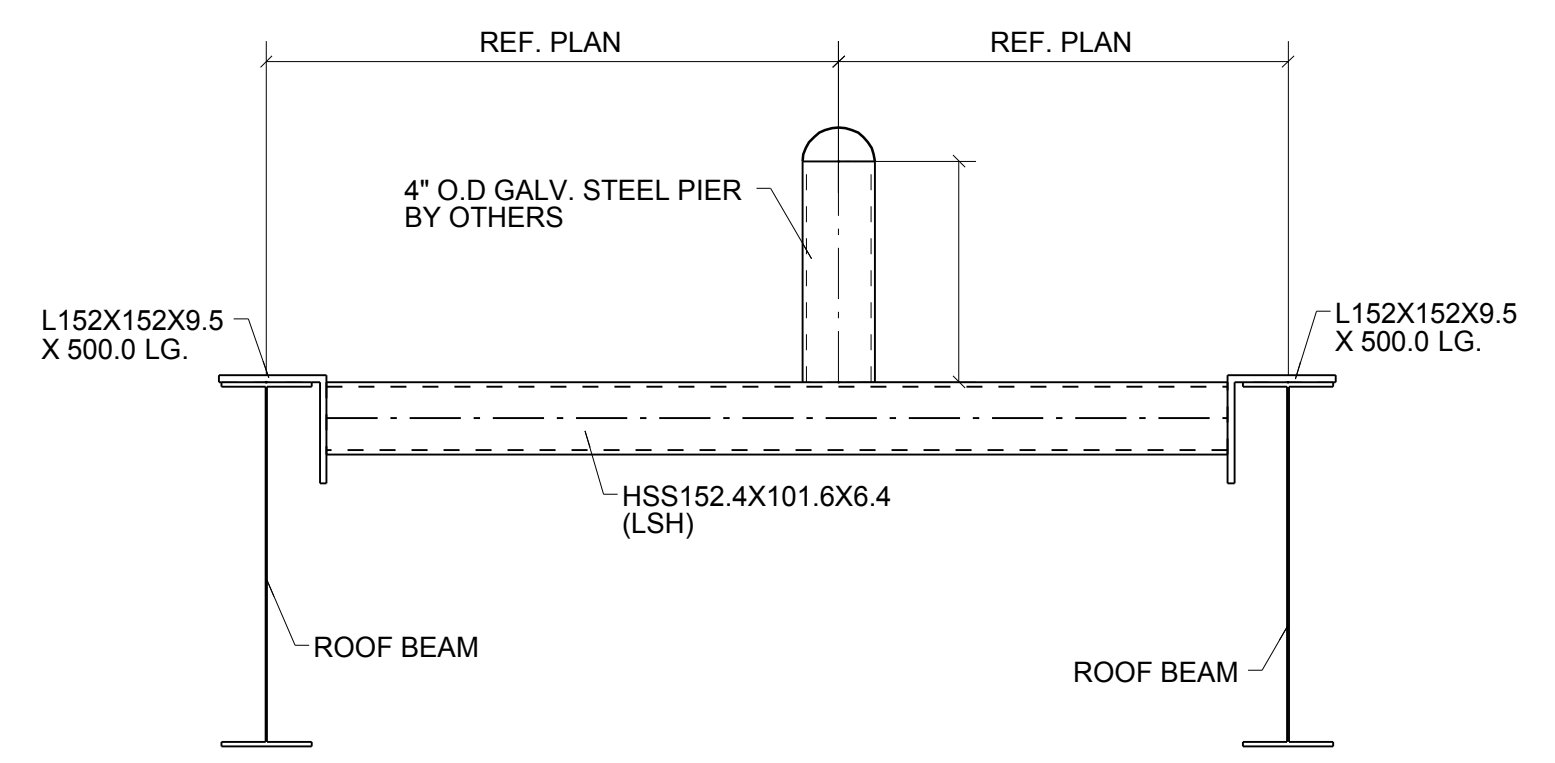

TYPICAL ROOF ANCHOR
CONNECTION DETAIL


RA1 SECTION

REFER SHEET E32 FOR TYPICAL WELD
DETAIL OF ROOF ANCHOR CONNECTION

ROOF ANCHOR LAYOUT

TRUE NORTH


PROJECT NORTH

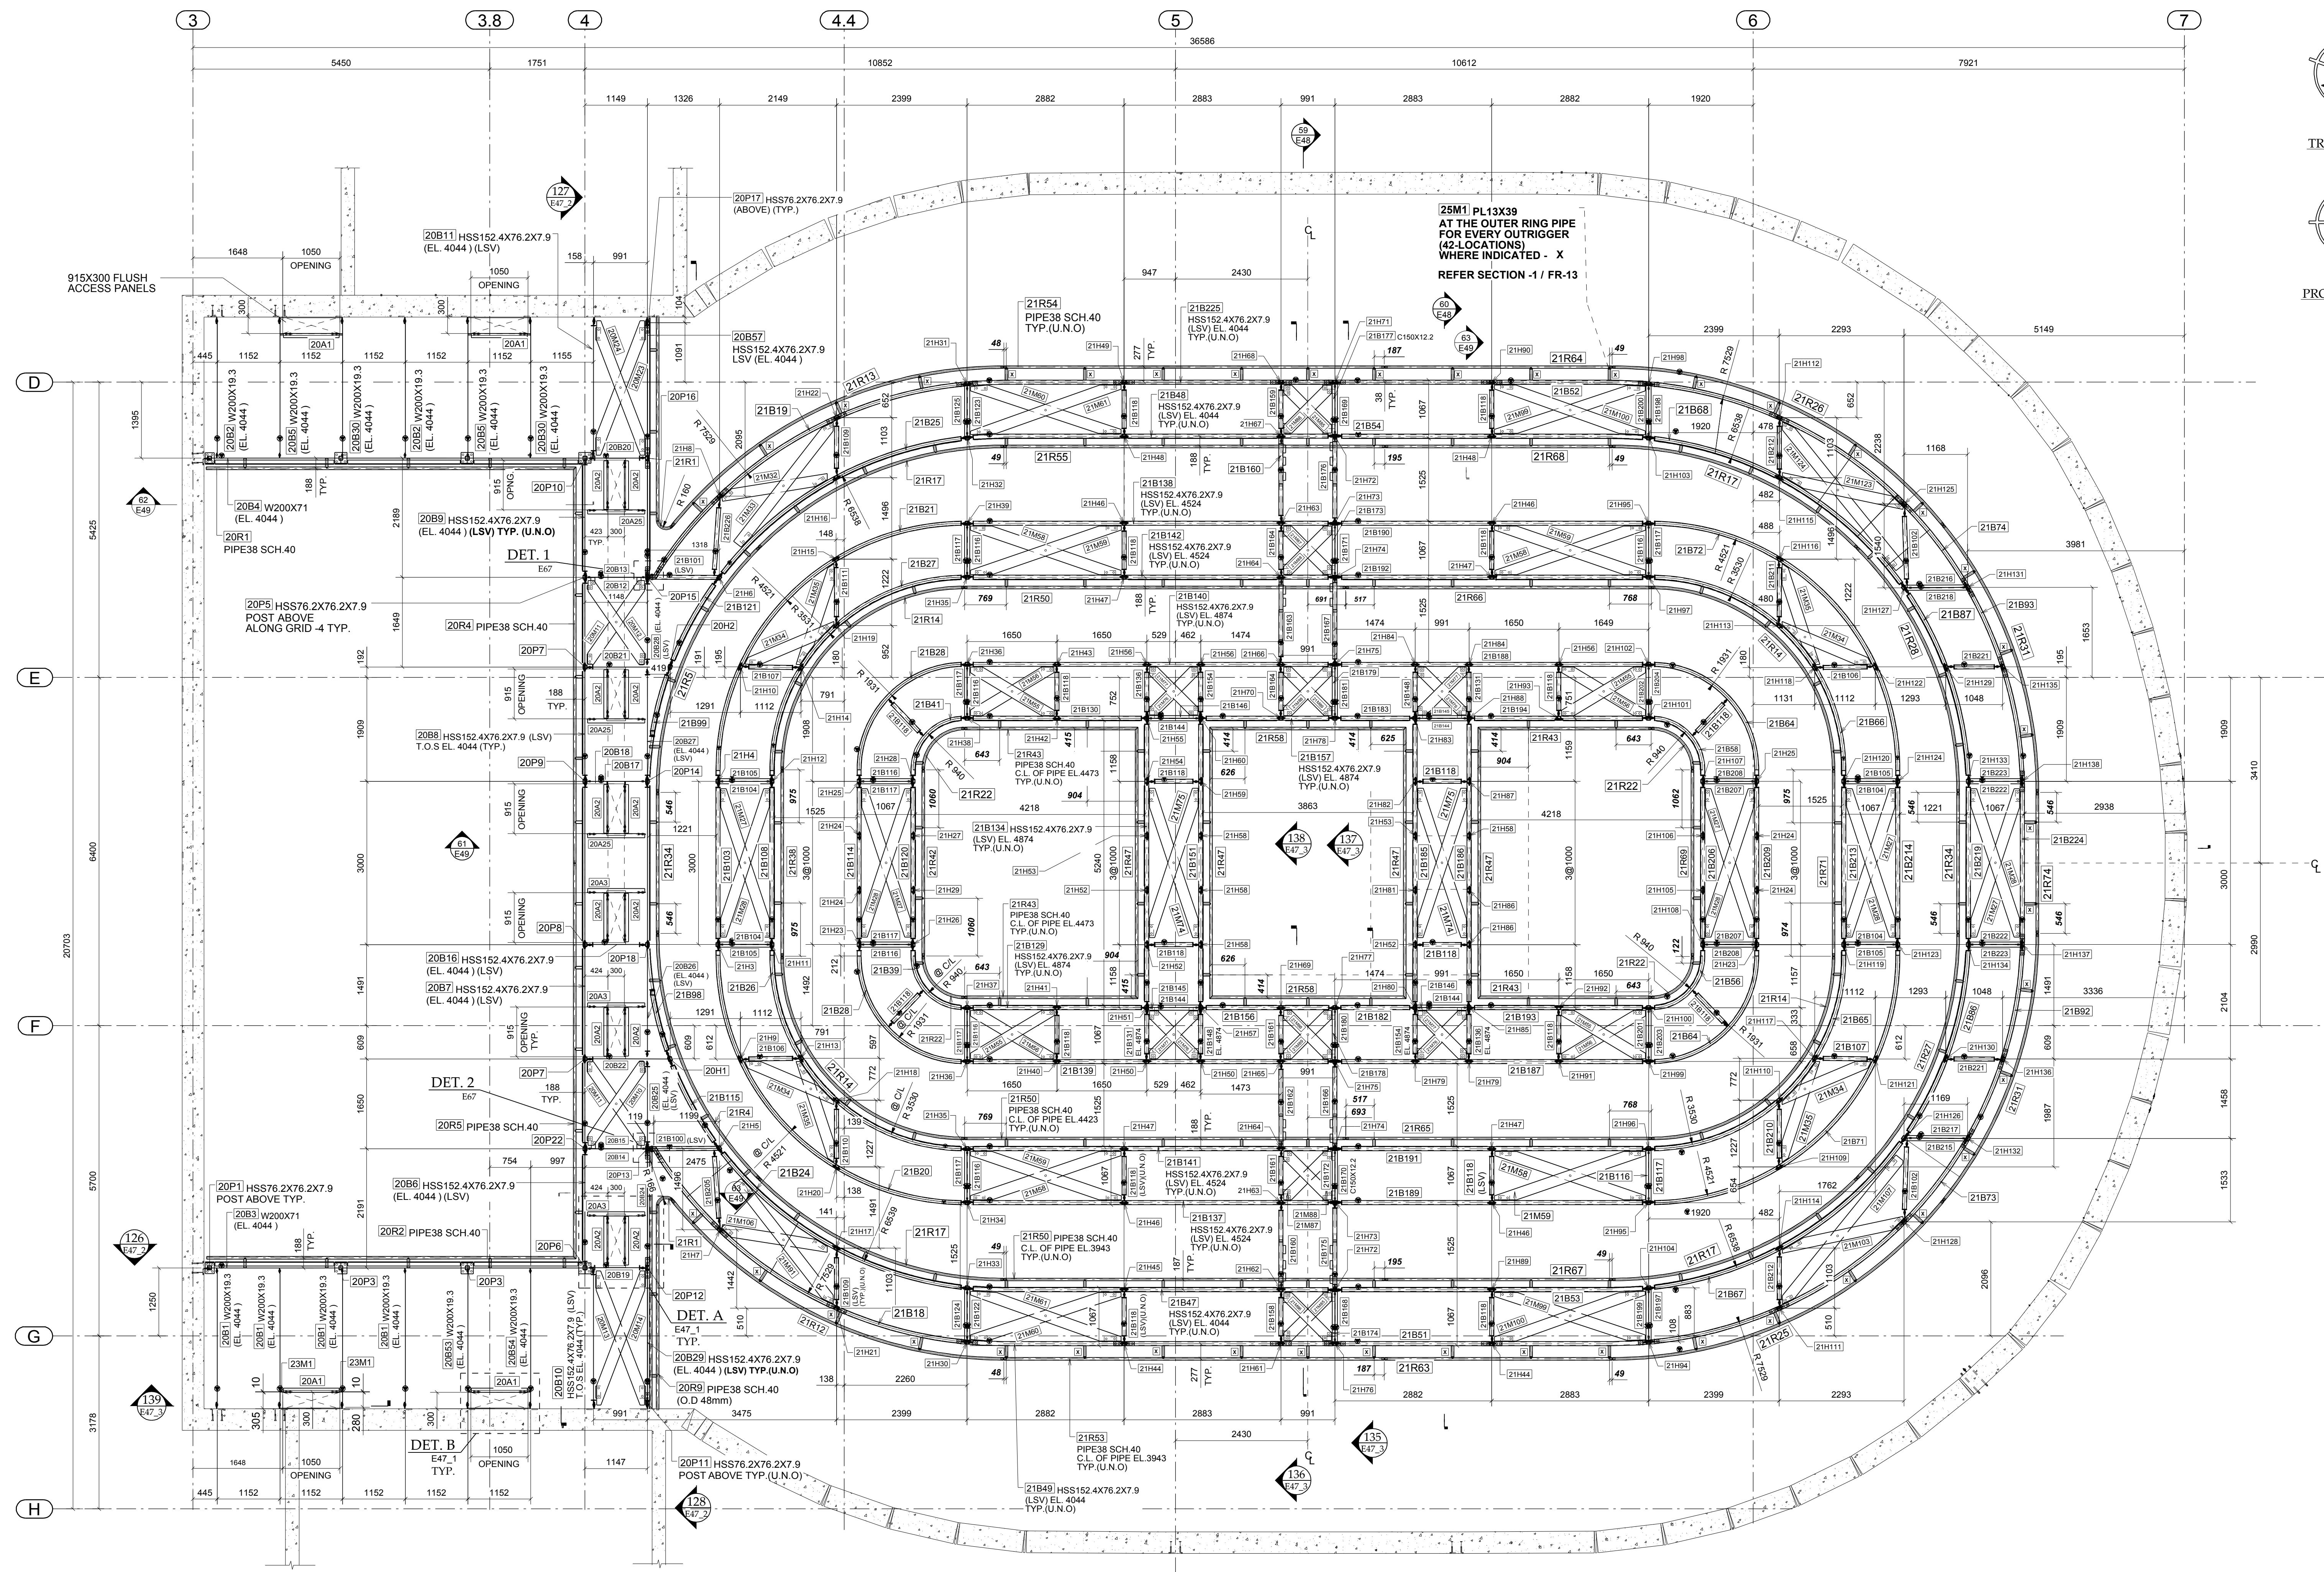


CATWALK PIPE FRAMING PLAN
REF.SHEET.A/8.02




TRUE NORTH PROJECT NORTH

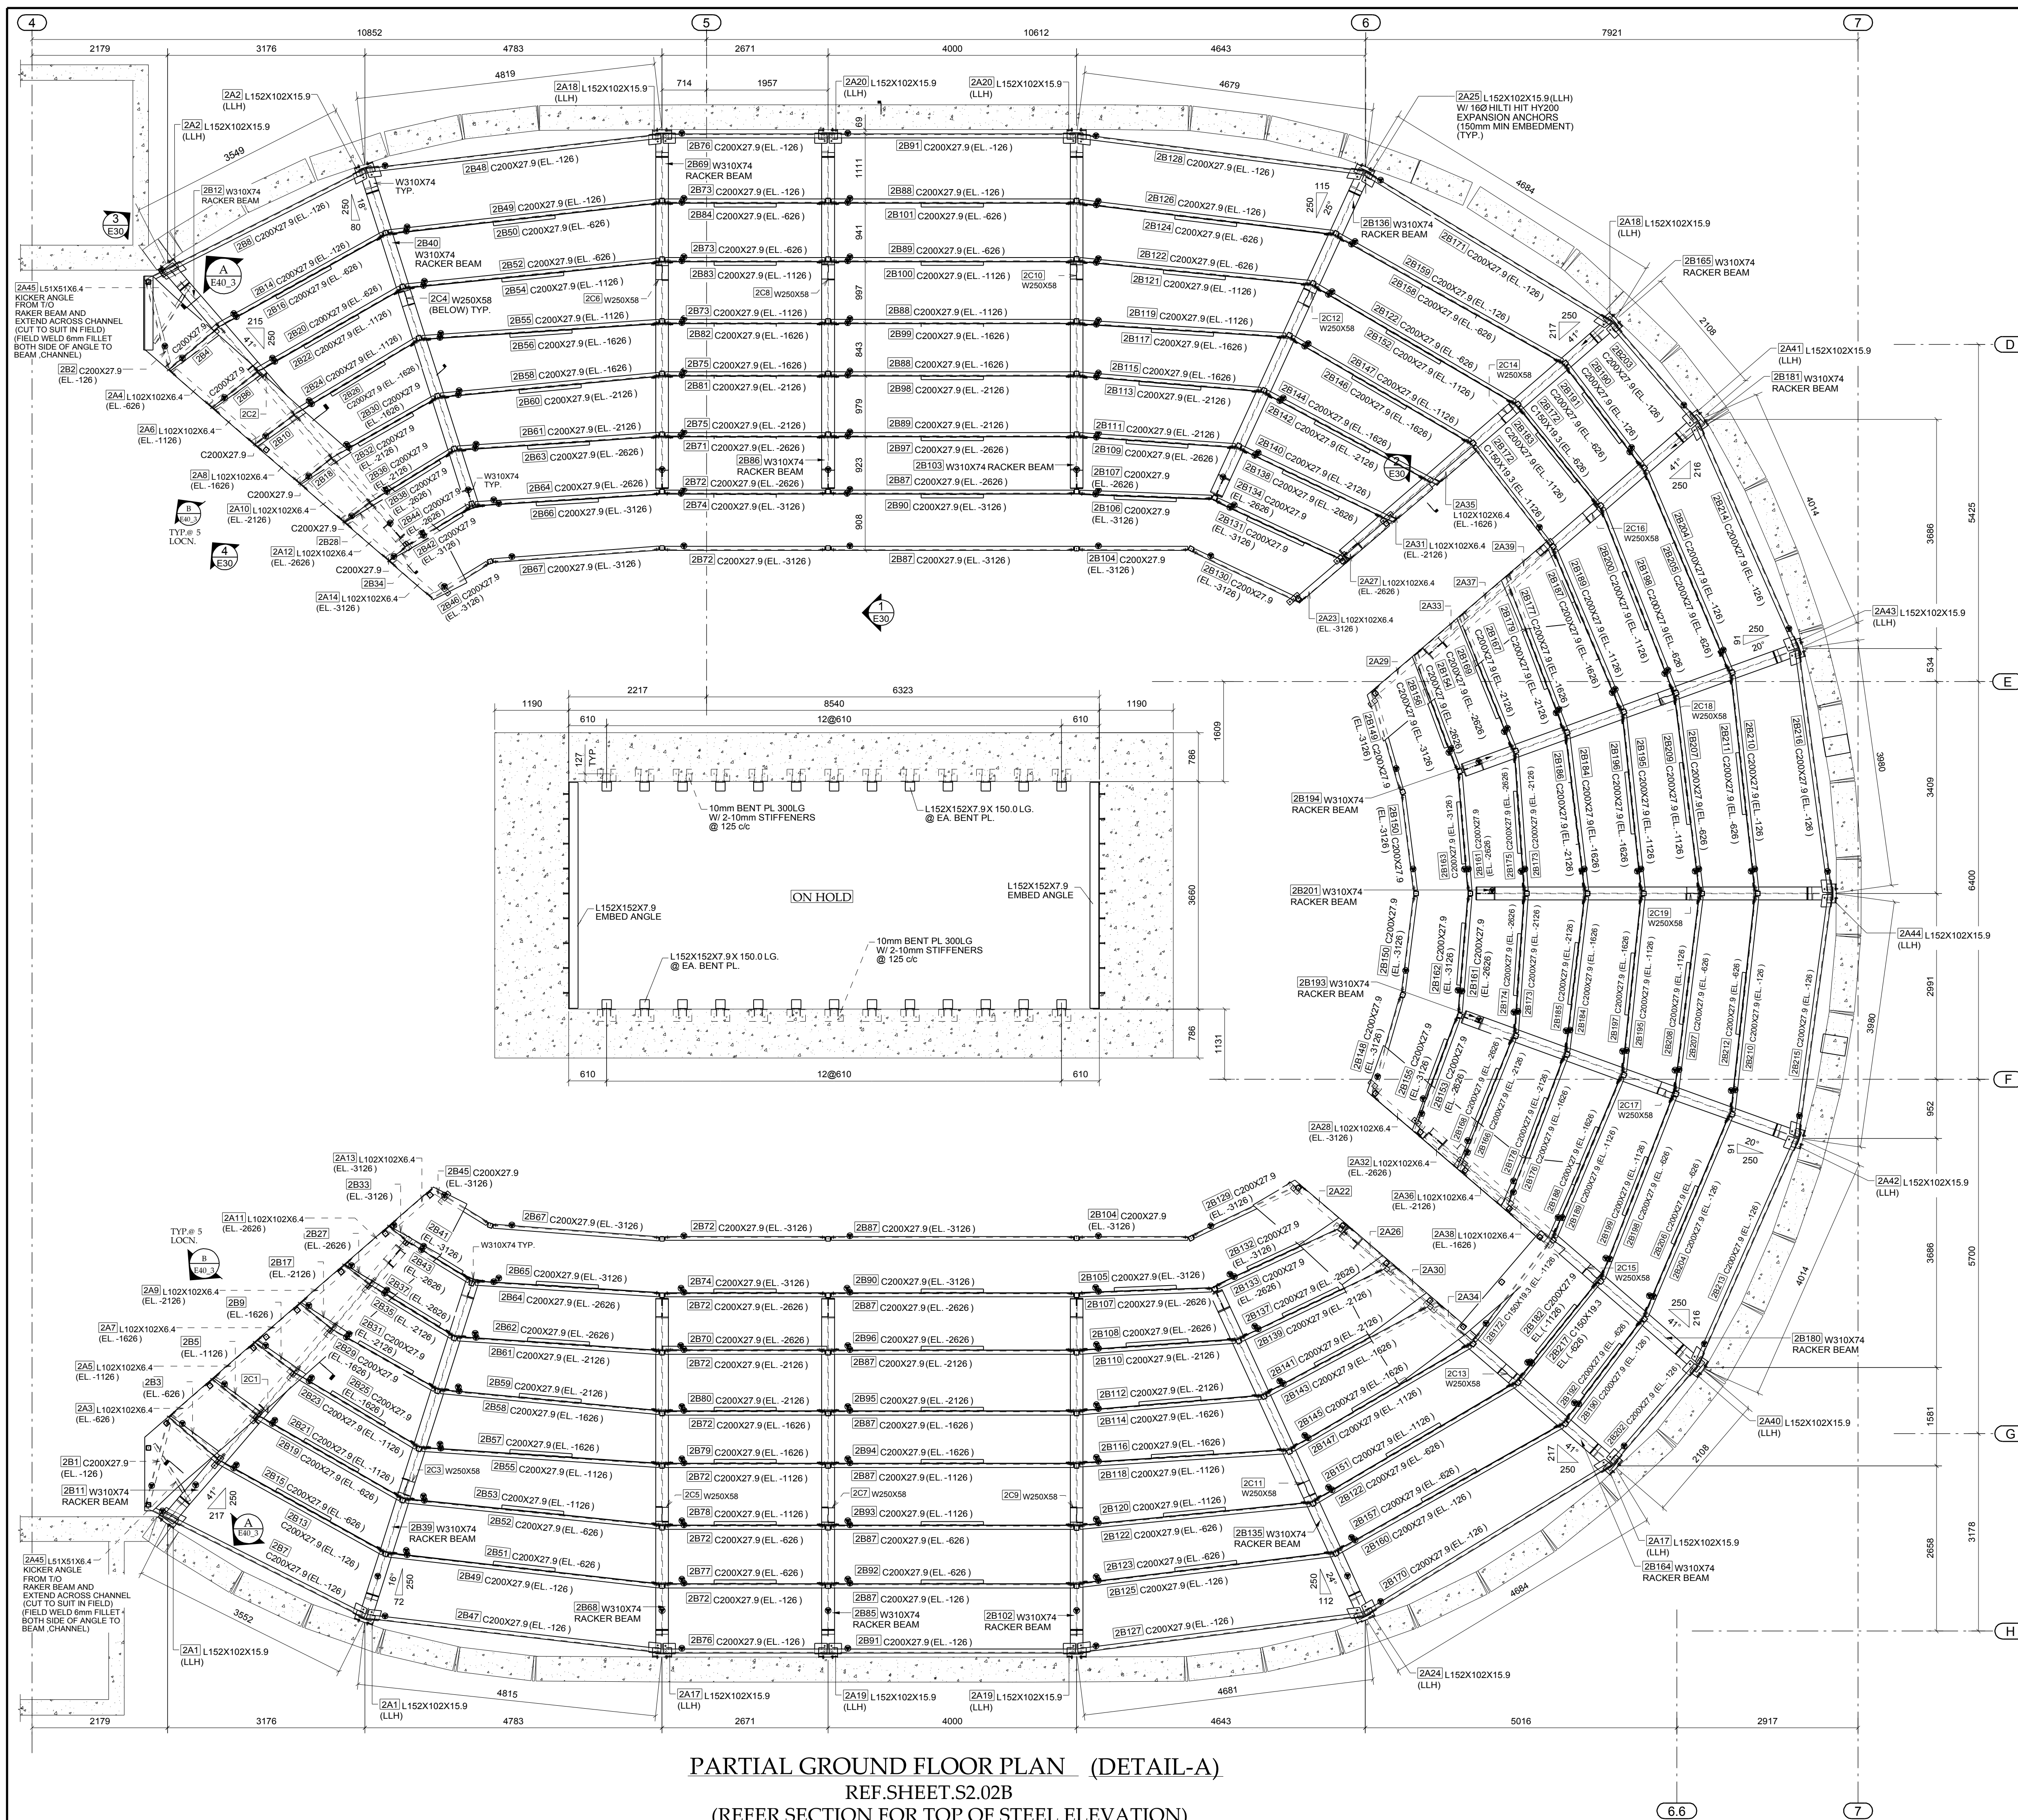

PARTIAL GROUND FLOOR PLAN (DETAIL-A)
REF.SHEET.S2.02B
(REFER SECTION FOR TOP OF STEEL ELEVATION)

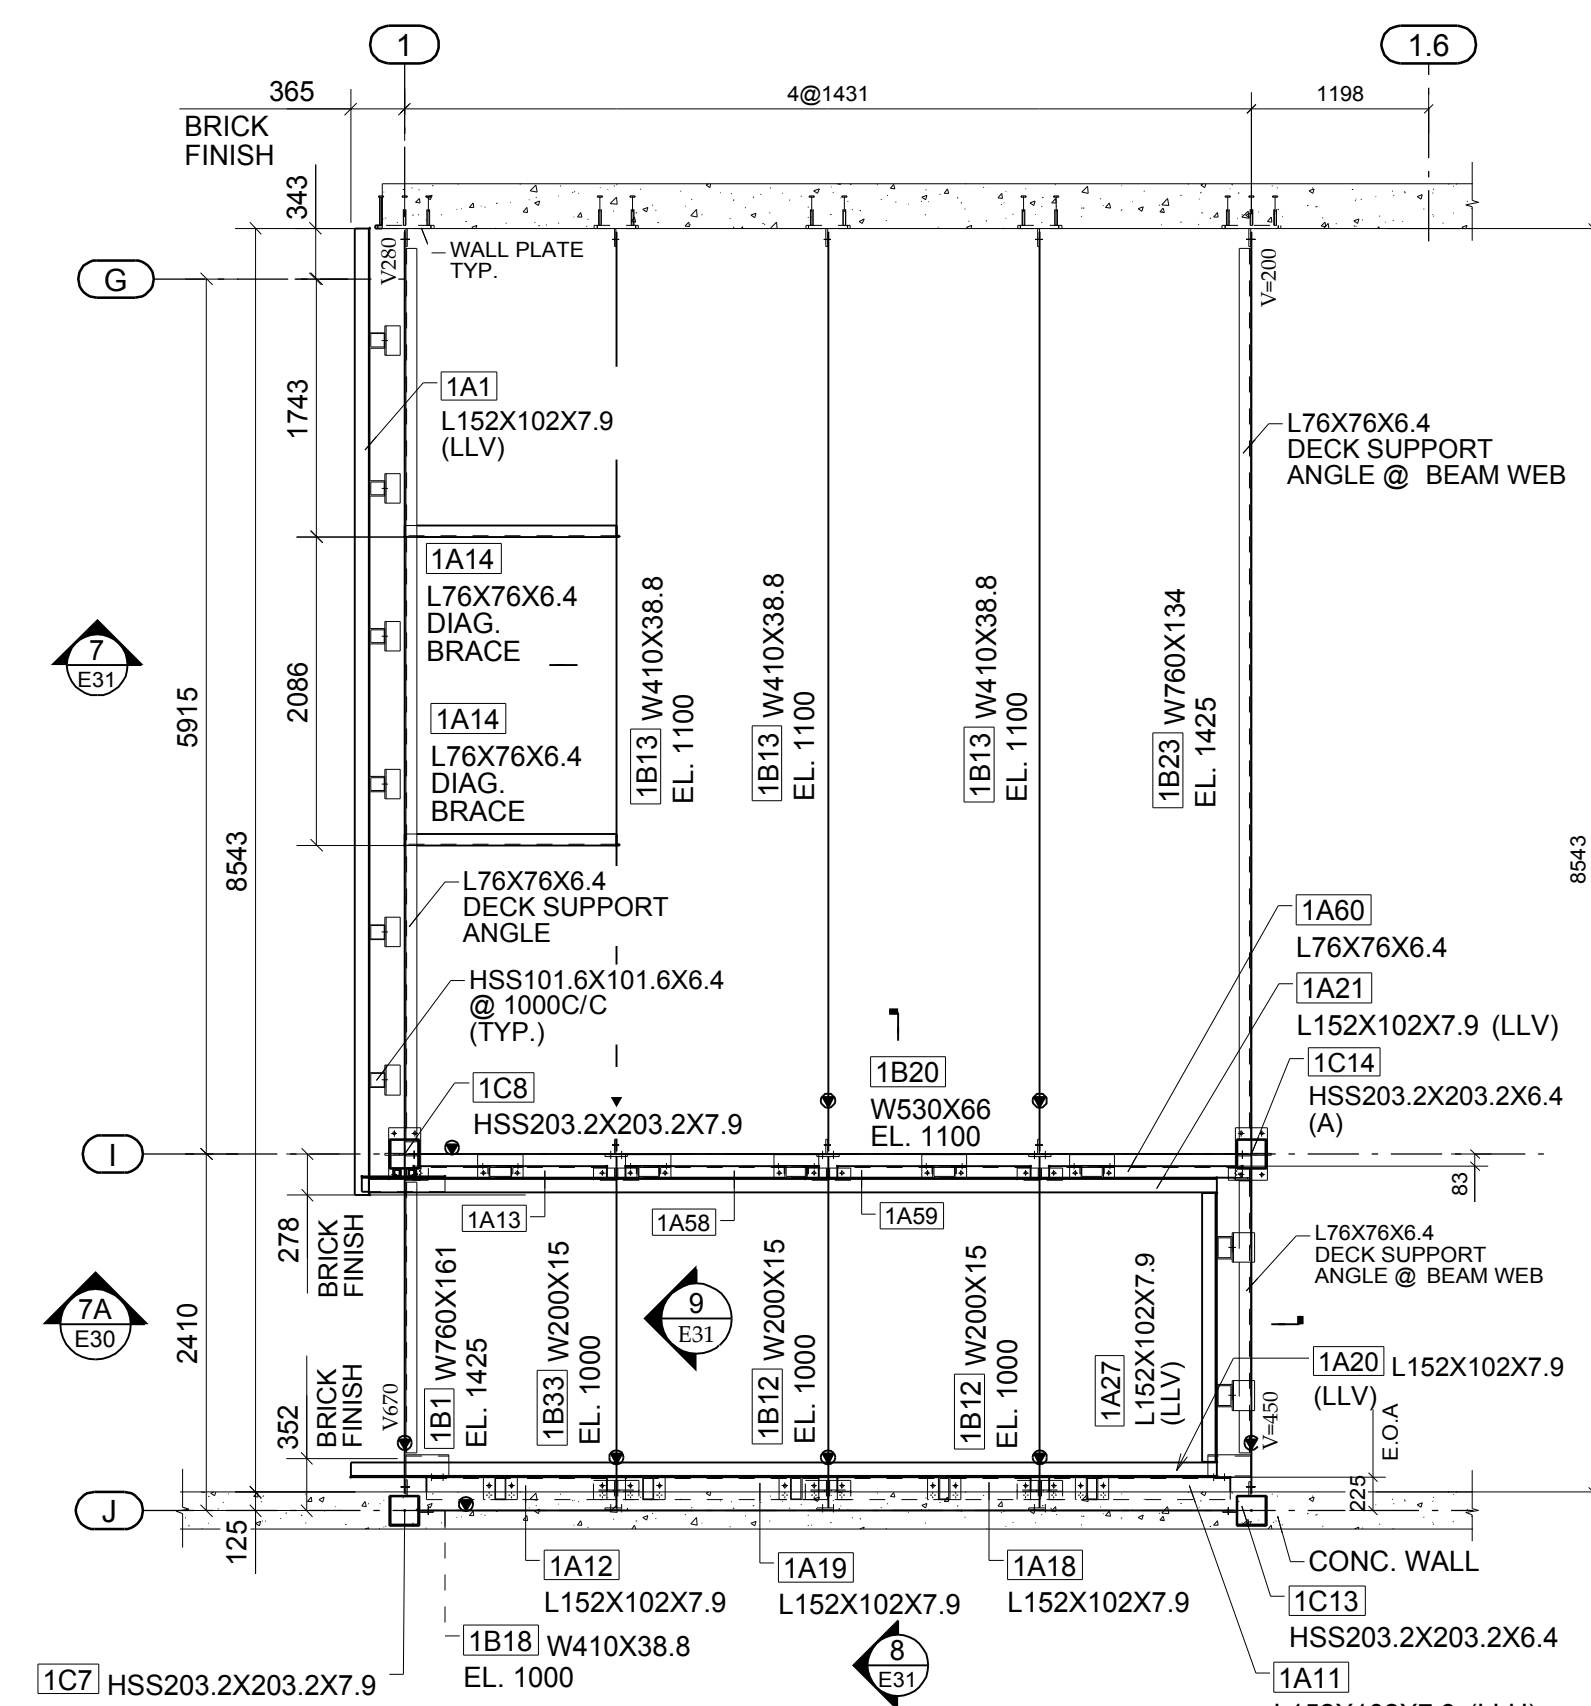


PARTIAL GROUND FLOOR PLAN - SECTOR 1
REF.SHEET.S2.02A

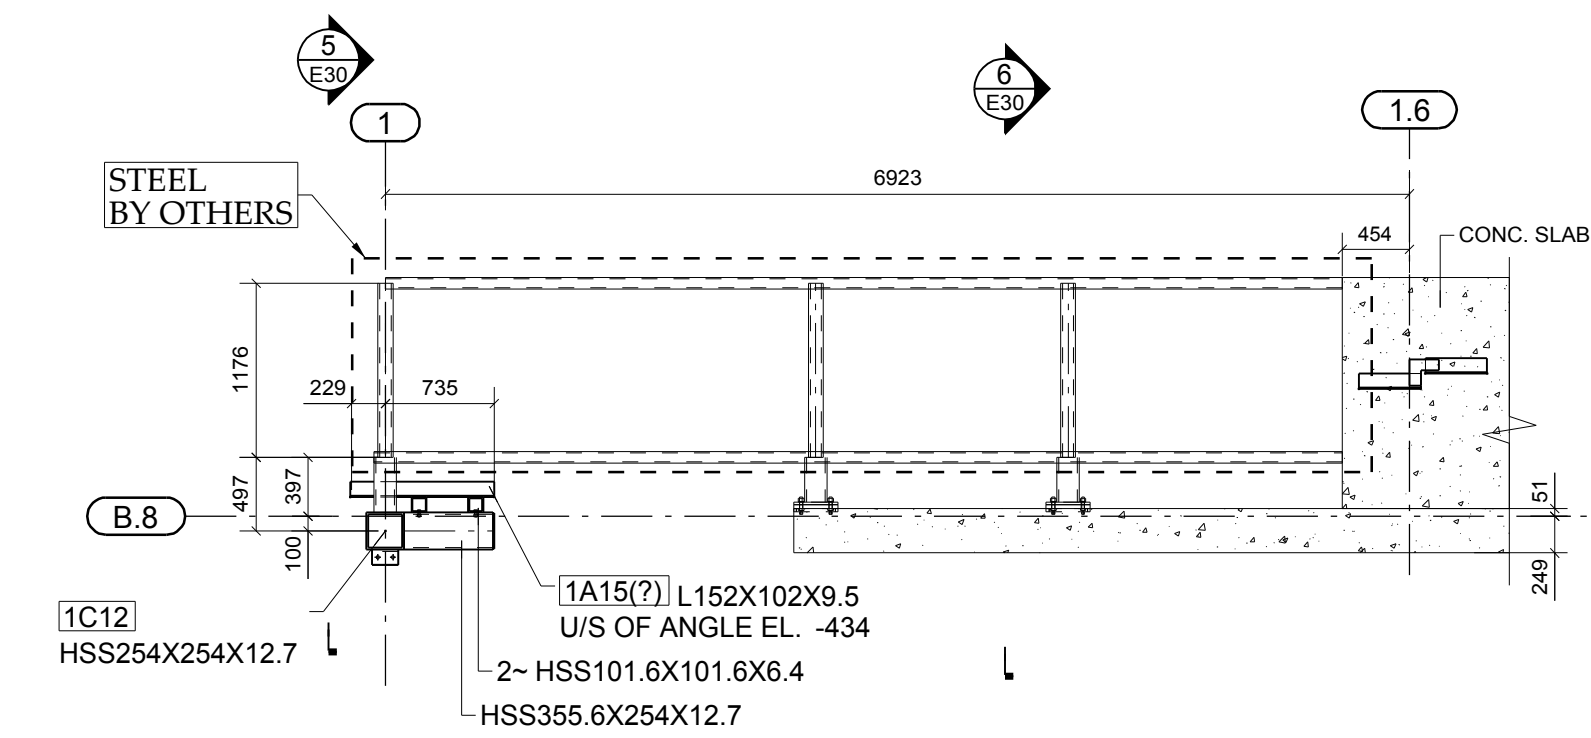

PARTIAL GROUND FLOOR PLAN - SECTOR 2
REF.SHEET.S2.02B


REFER SHEET E43
FOR BALLUSTRADE
DETAILS

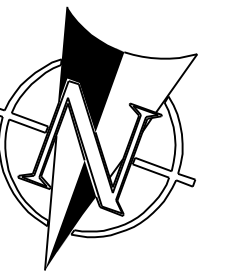

TRUE NORTH





PROJECT NORTH

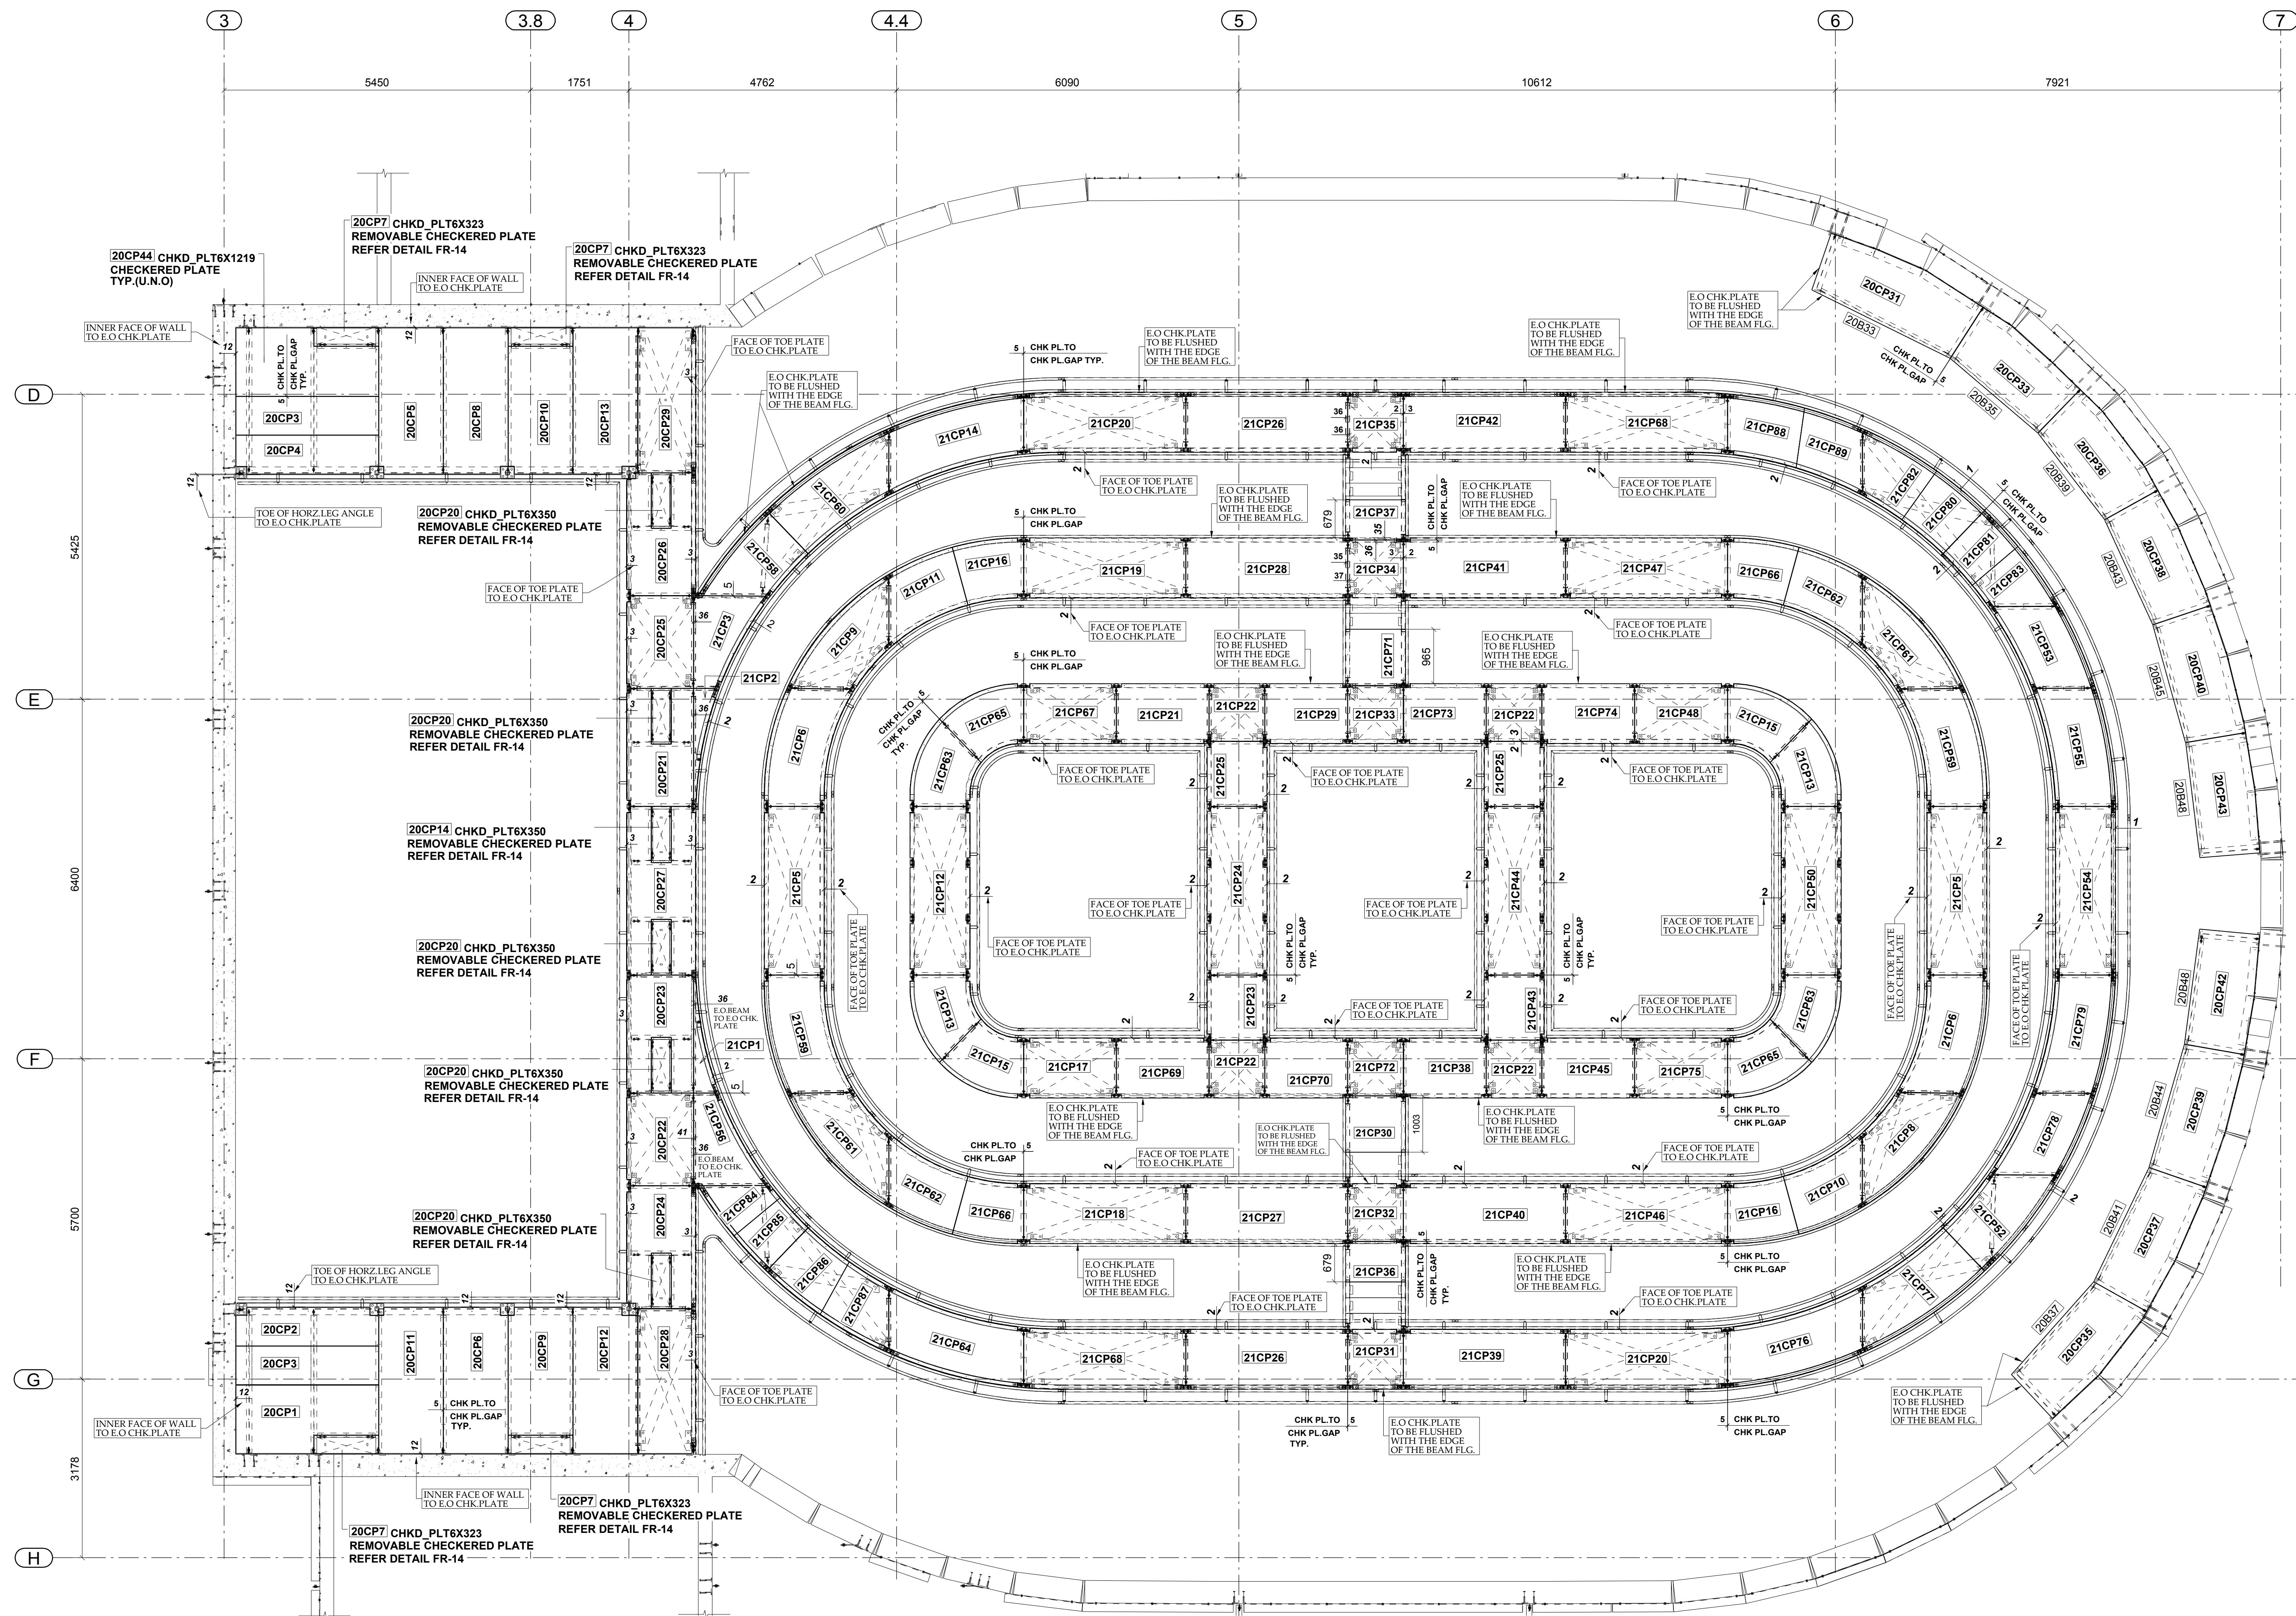


CATWALK - CHECKERED PLATE LOCATING PLAN

CHECKERED PLATE LOCATION & MARKS ONLY SHOWN IN THIS PLAN
FOR BEAM MARKS & LOCATIONS PLEASE REFER SHEET E47
PLEASE REFER SHEET E47.1 FOR CHECKERED PLATE FIELD WELD DETAILS

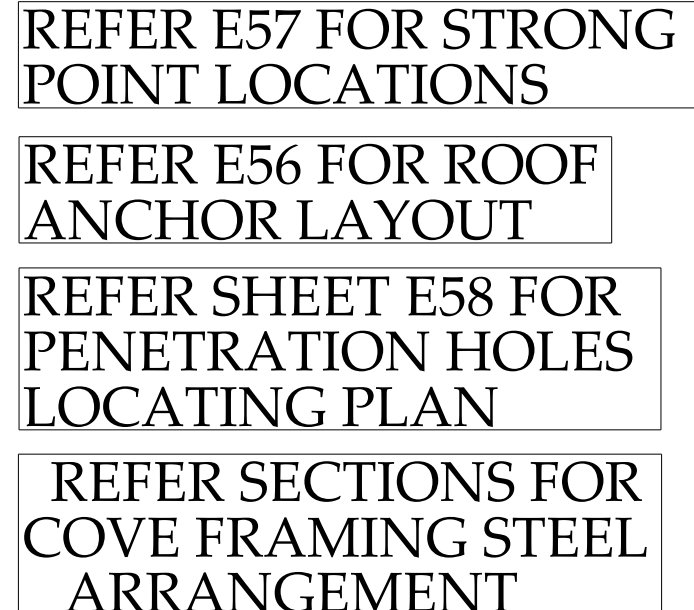


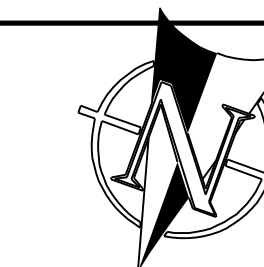

TRUE NORTH

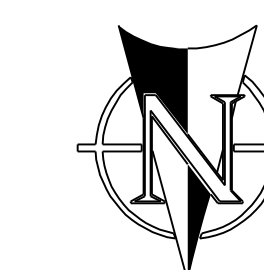

WORKING NORTH

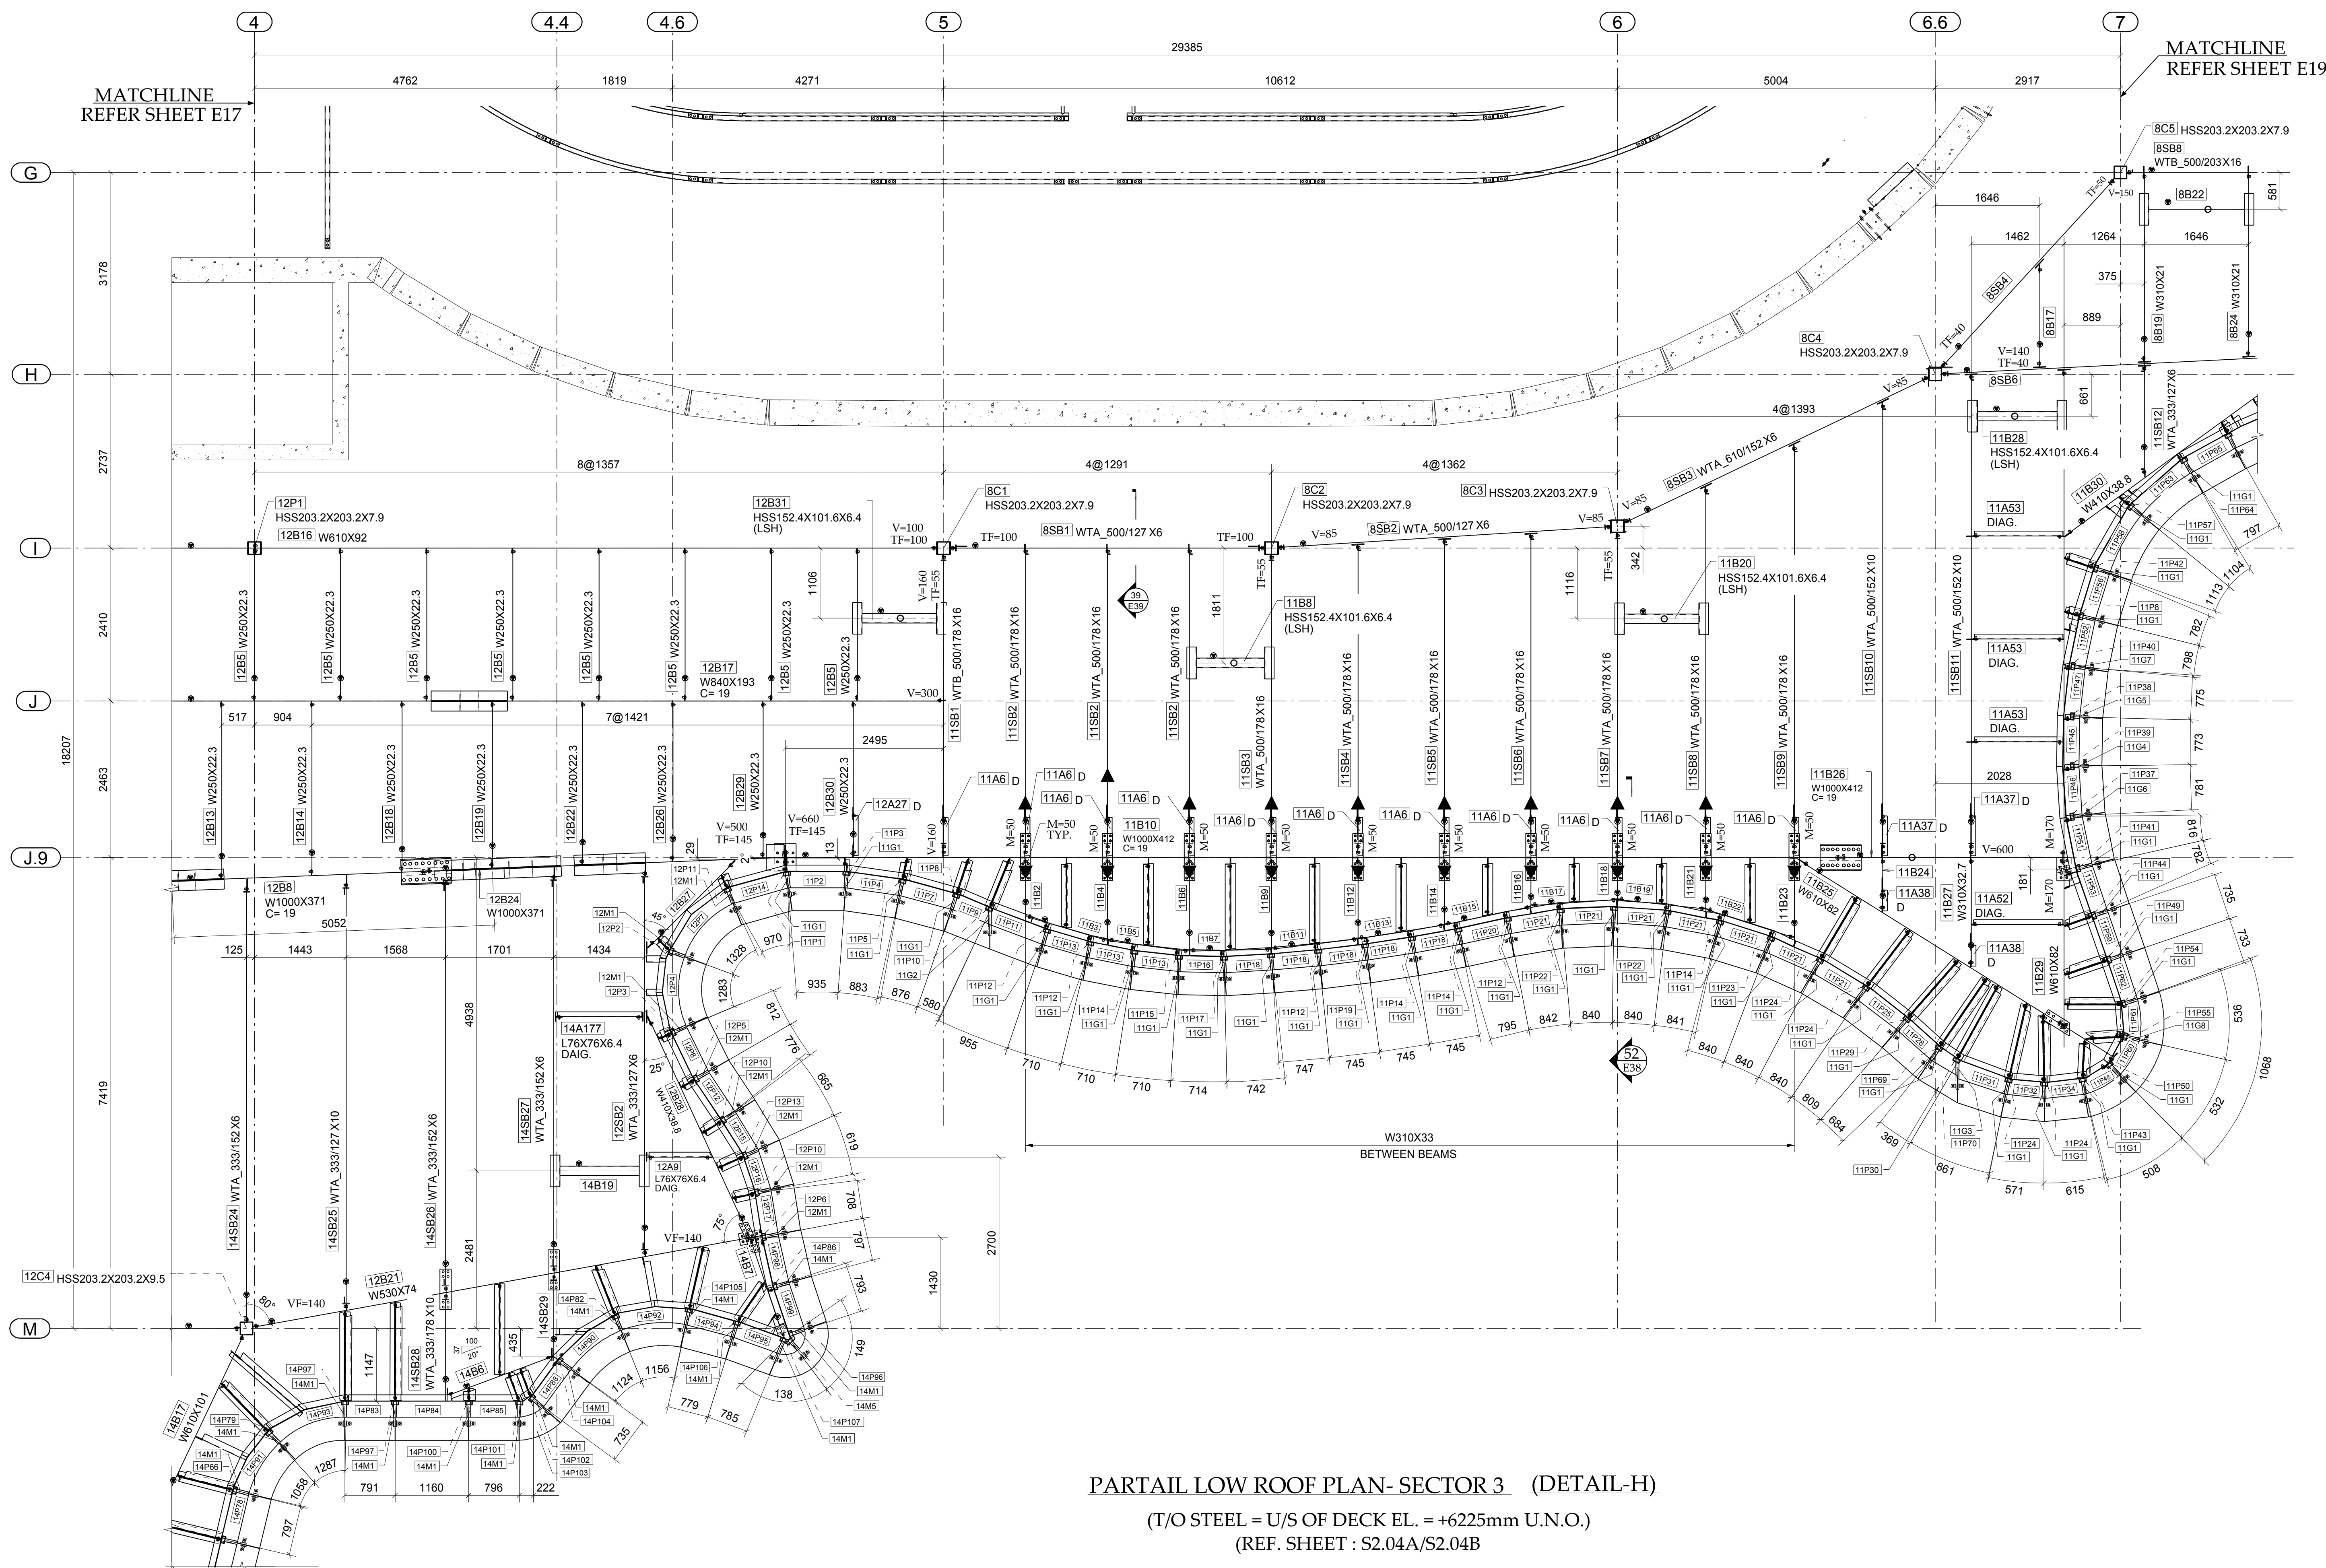

PARTIAL LOW ROOF PLAN- SECTOR 3 (DETAIL-H)

(T/O STEEL = U/S OF DECK EL. = +6225mm U.N.O.)

(REF. SHEET : S2.04A/S2.04B)


REFER E56 FOR ROOF
ANCHOR LAYOUT

REFER SHEET E53 FOR
KICKER ANGLE MARKS


REFER E60 FOR PENETRATION
HOLES LOCATING PLAN

D - INDICATES DIAGONAL
BRACE ANGLE

▼ - INDICATES MOMENT CONNECTION

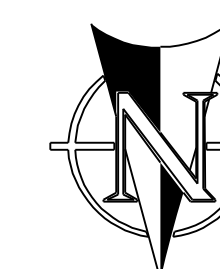

MATCHLINE
REFER SHEET E21

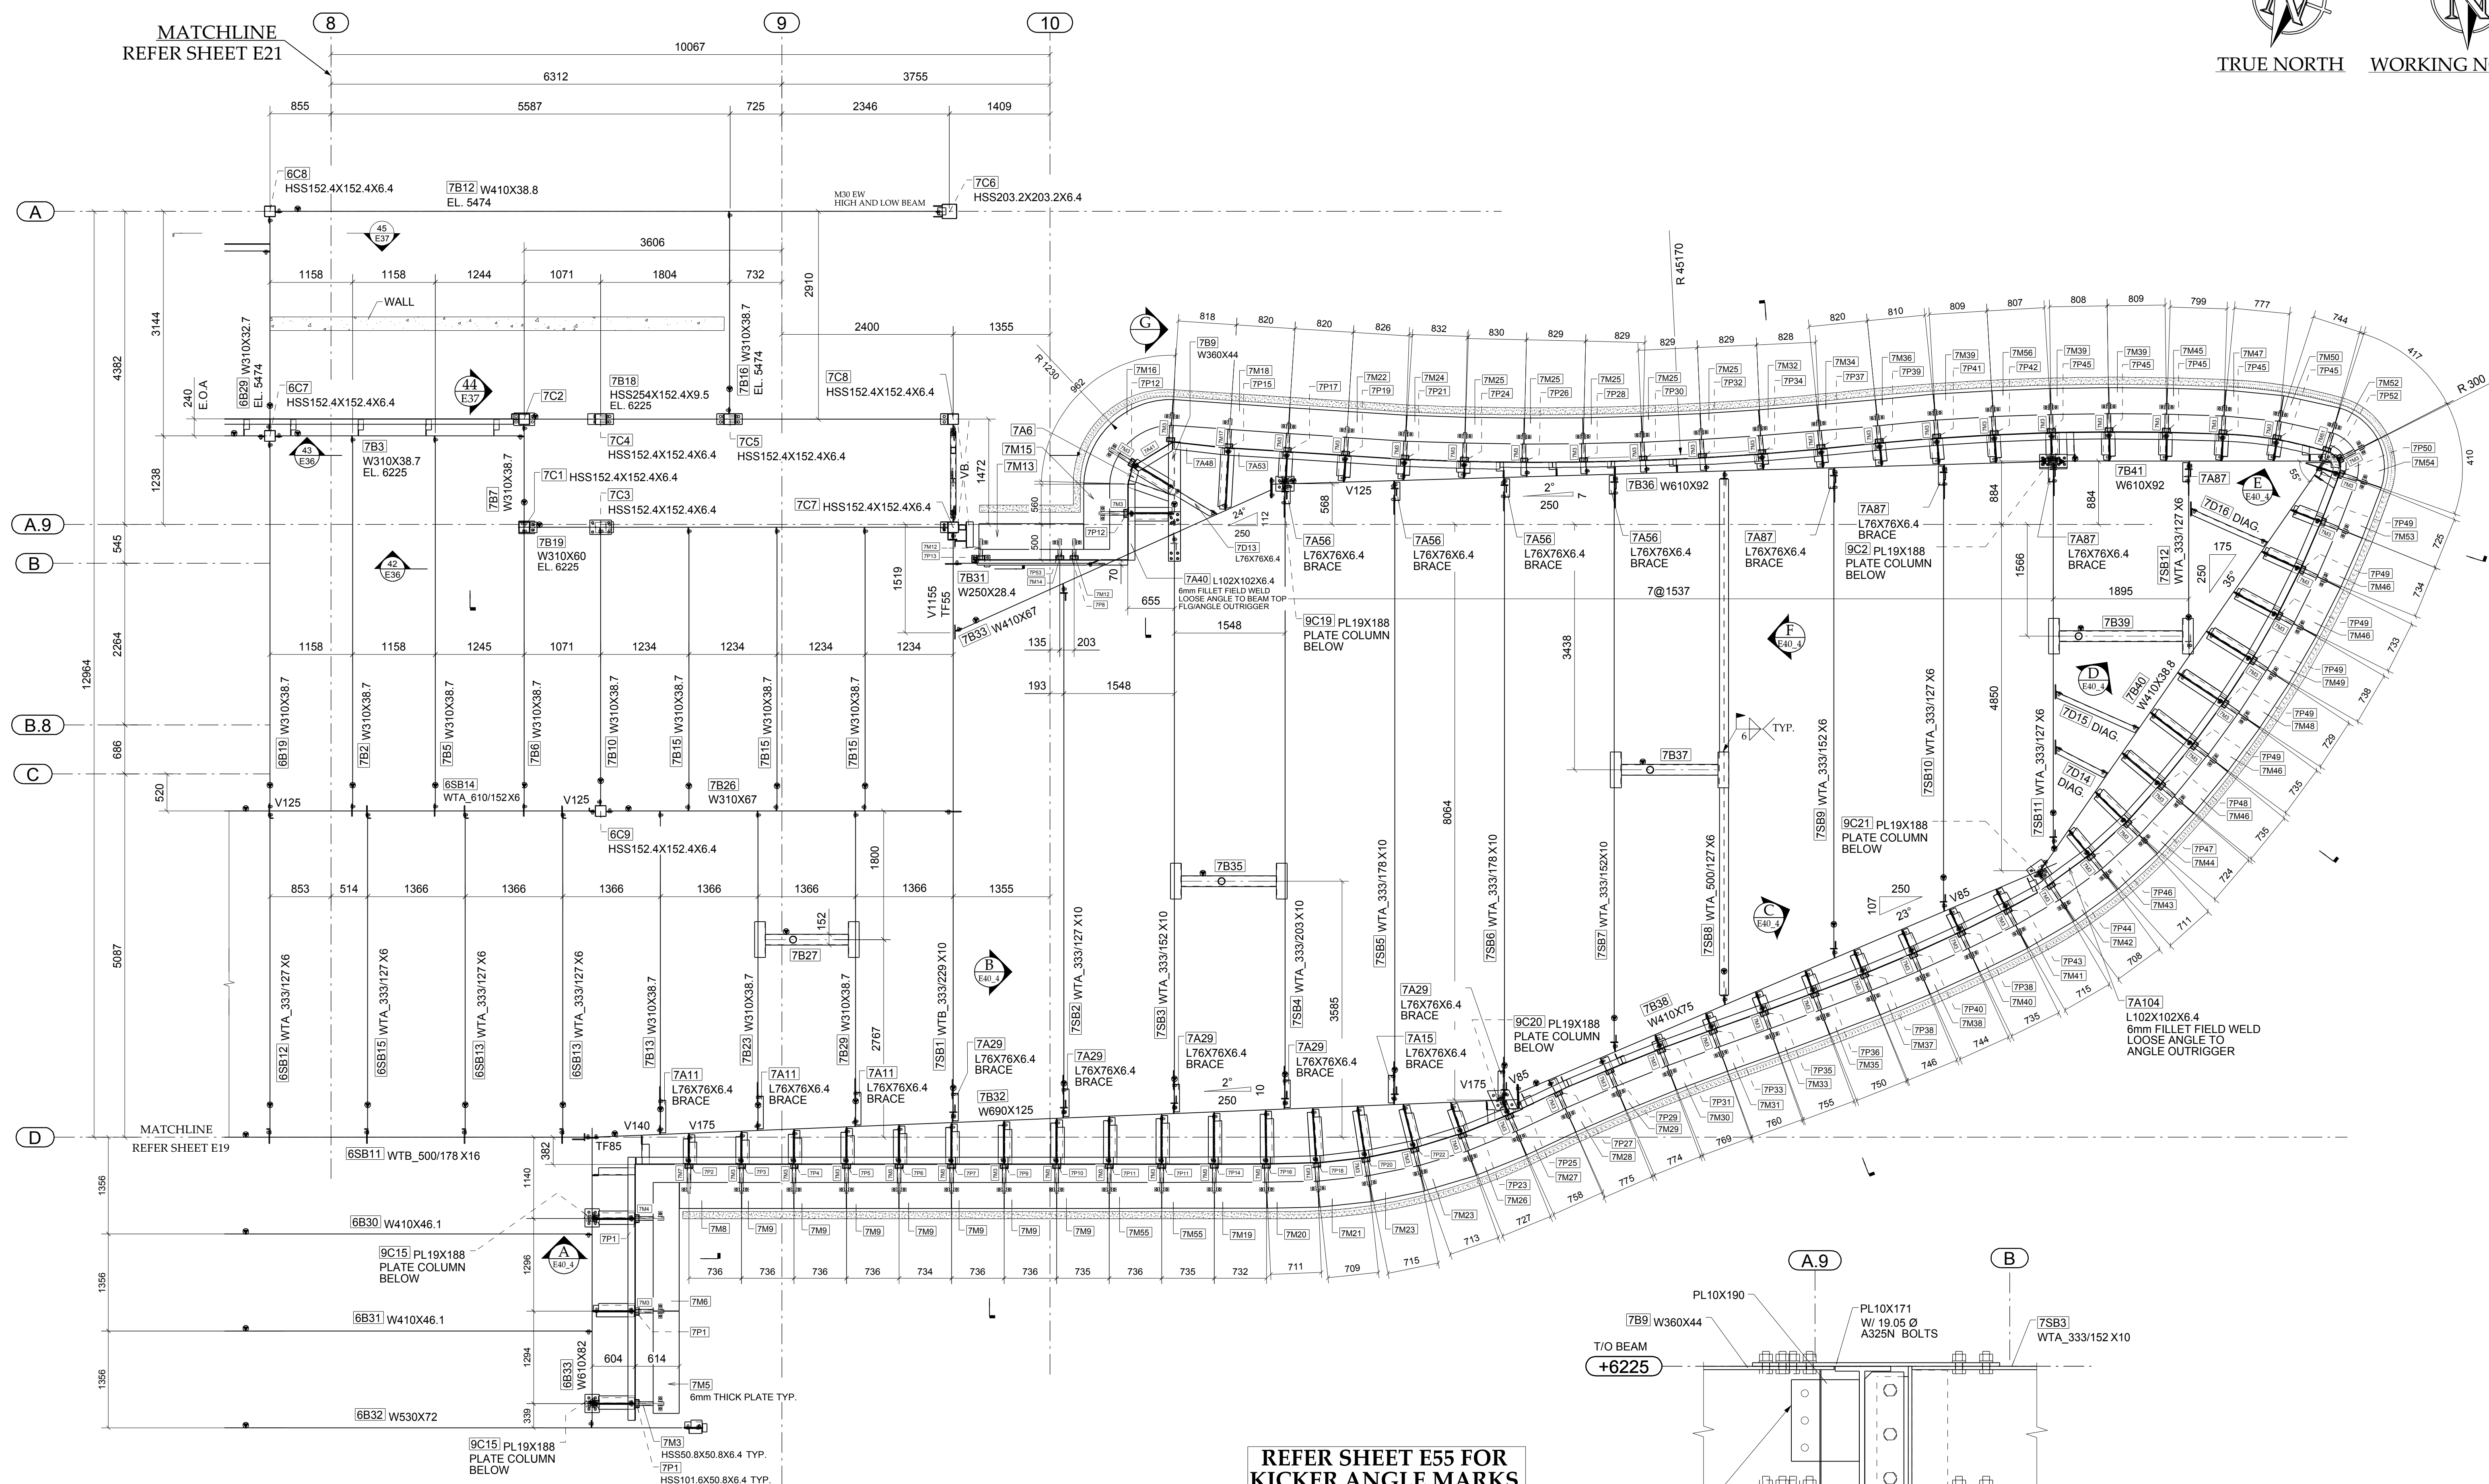

REFER E56 FOR ROOF
ANCHOR LAYOUT

REF:SHEET:S2.04C

MATCH LINE
REFER SHEET E16



TRUE NORTH



WORKING NORTH

REFER DETAIL-A/E34
TYP.

REFER DETAIL-A/E34
TYP.

REFER 'DET. K/E18' FOR
LOW LEVEL FRAMING PLAN


PARTIAL TERMINAL BUILDING LEVEL-2 FRAMING PLAN


(REF. PLAN S223 & S222)

NOTES:-


- ROOF DATUM EL. = 131500 U.N.O.
- +/- VALUES SHOWN IN PLAN ARE REFERRED FROM ROOF DATUM ELEVATION 131500
- RA INDICATES ROOF ANCHORS (REF. TYPICAL SEC. @ SHEET E31)
- E.O.A. INDICATES EDGE OF ANGLE
- E.O.B.P.L. INDICATES EDGE OF BENT PL.
- ◀ - INDICATES ORIENTATION OF MEMBER

FOR CLARITY THE EDGE OF BENT PLATE
DETAILS & MARKS ARE SHOWN IN SHEET E90








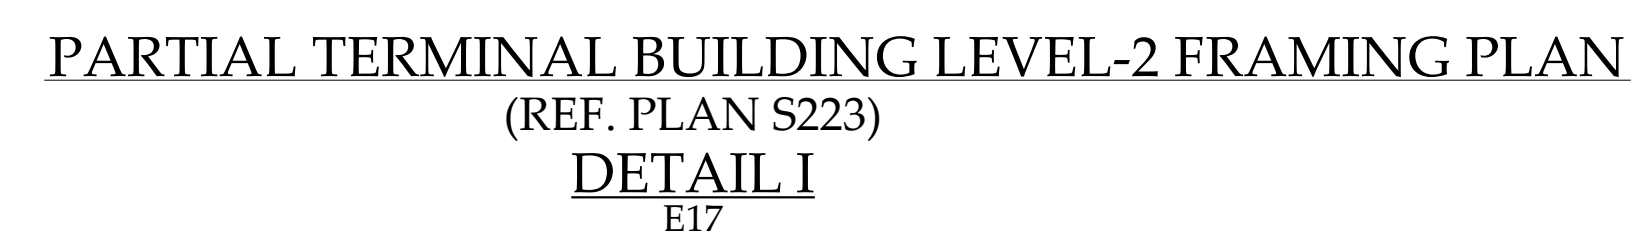


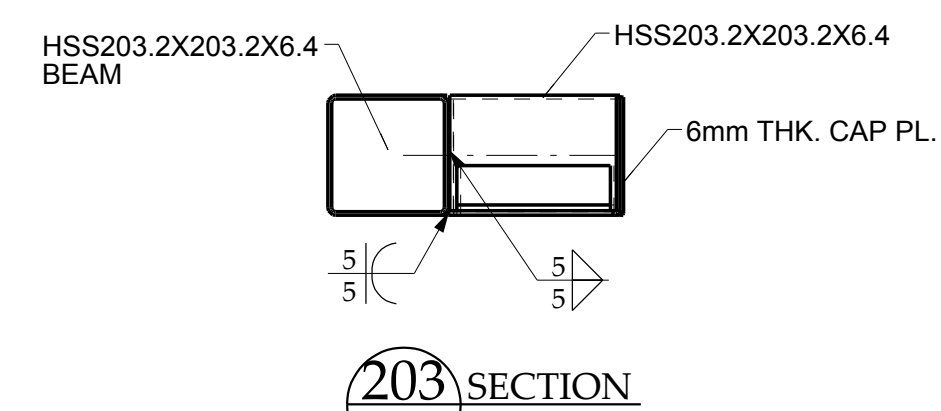


TYPICAL SECTION DETAIL FOR
HSS BEAM TO HSS OUTRIGGER CONNECTION

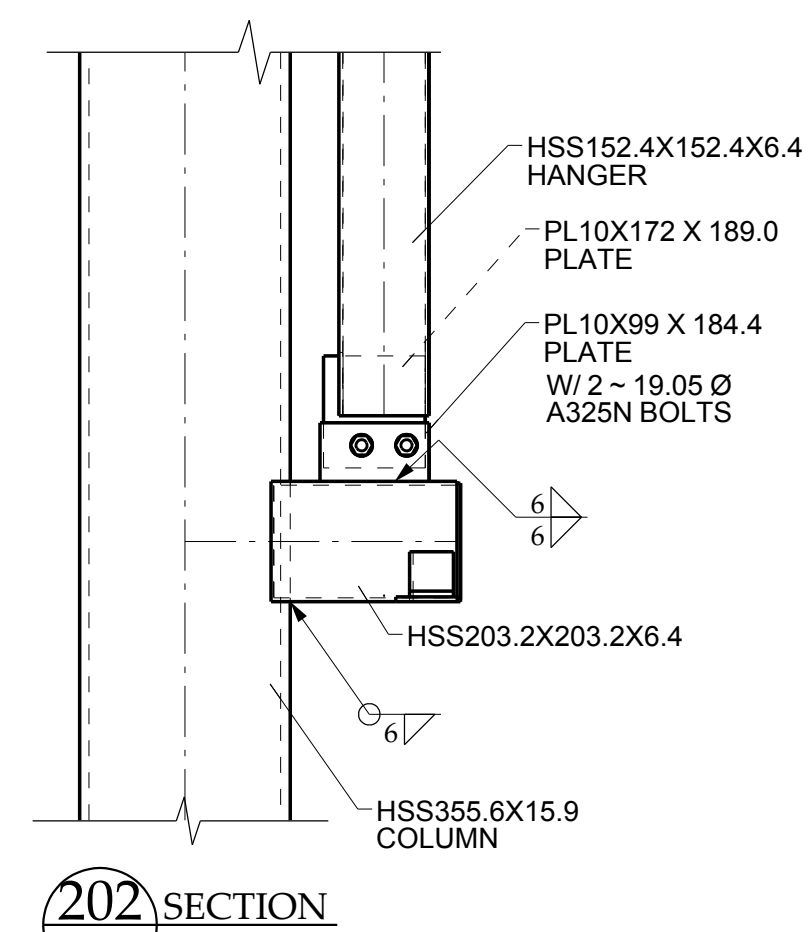


TYPICAL SECTION DETAIL FOR
HSS COLUMN TO HSS OUTRIGGER CONNECTION

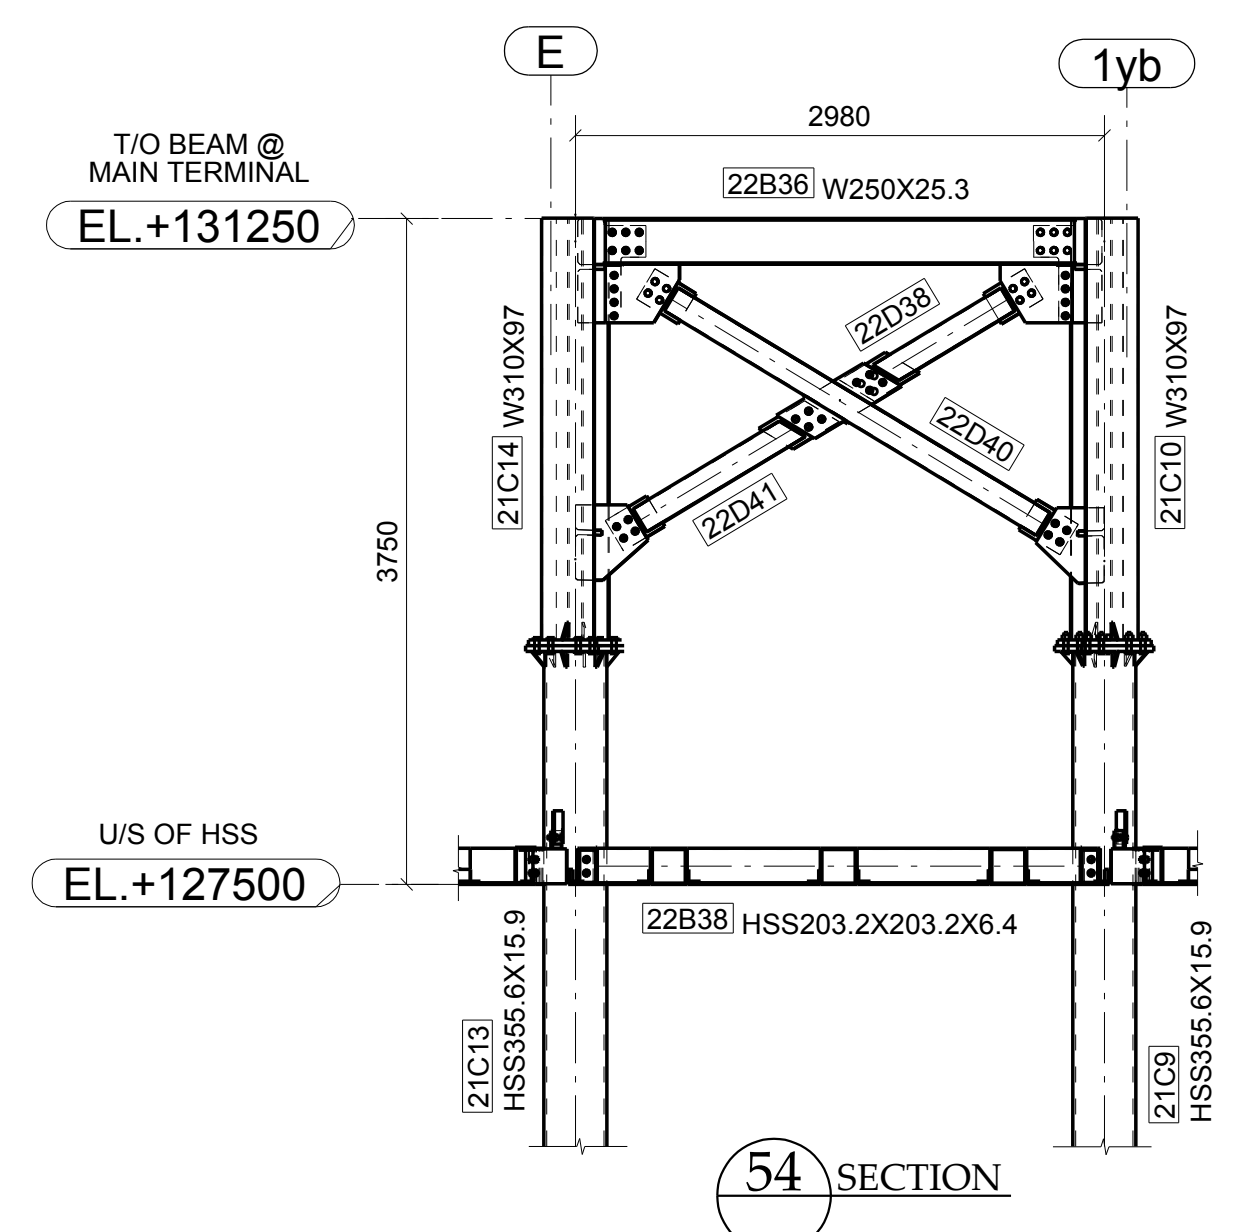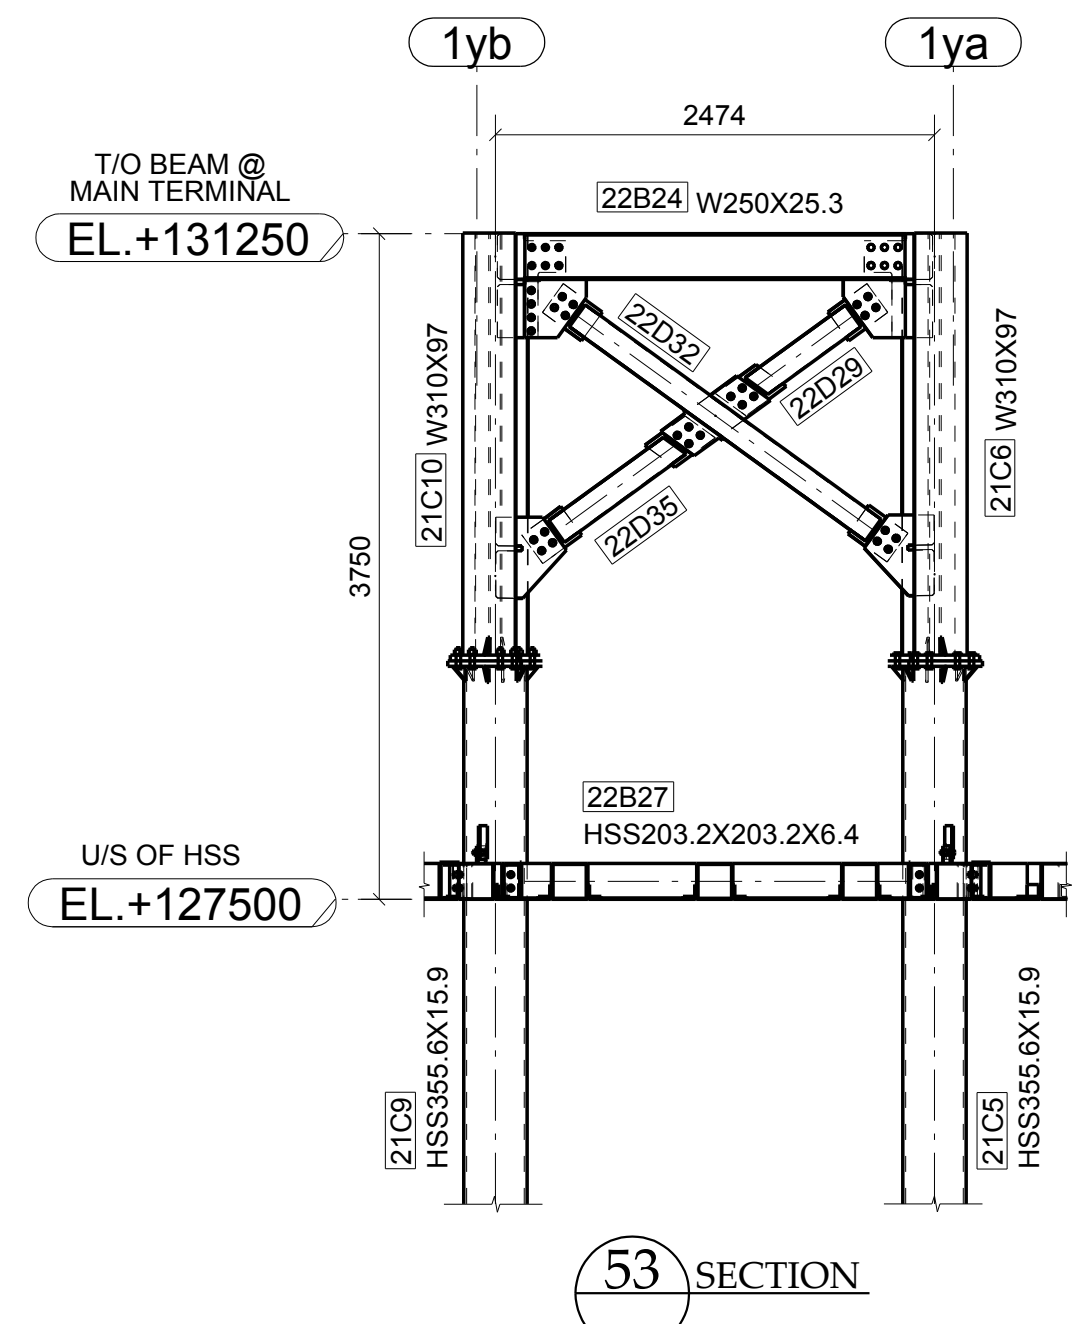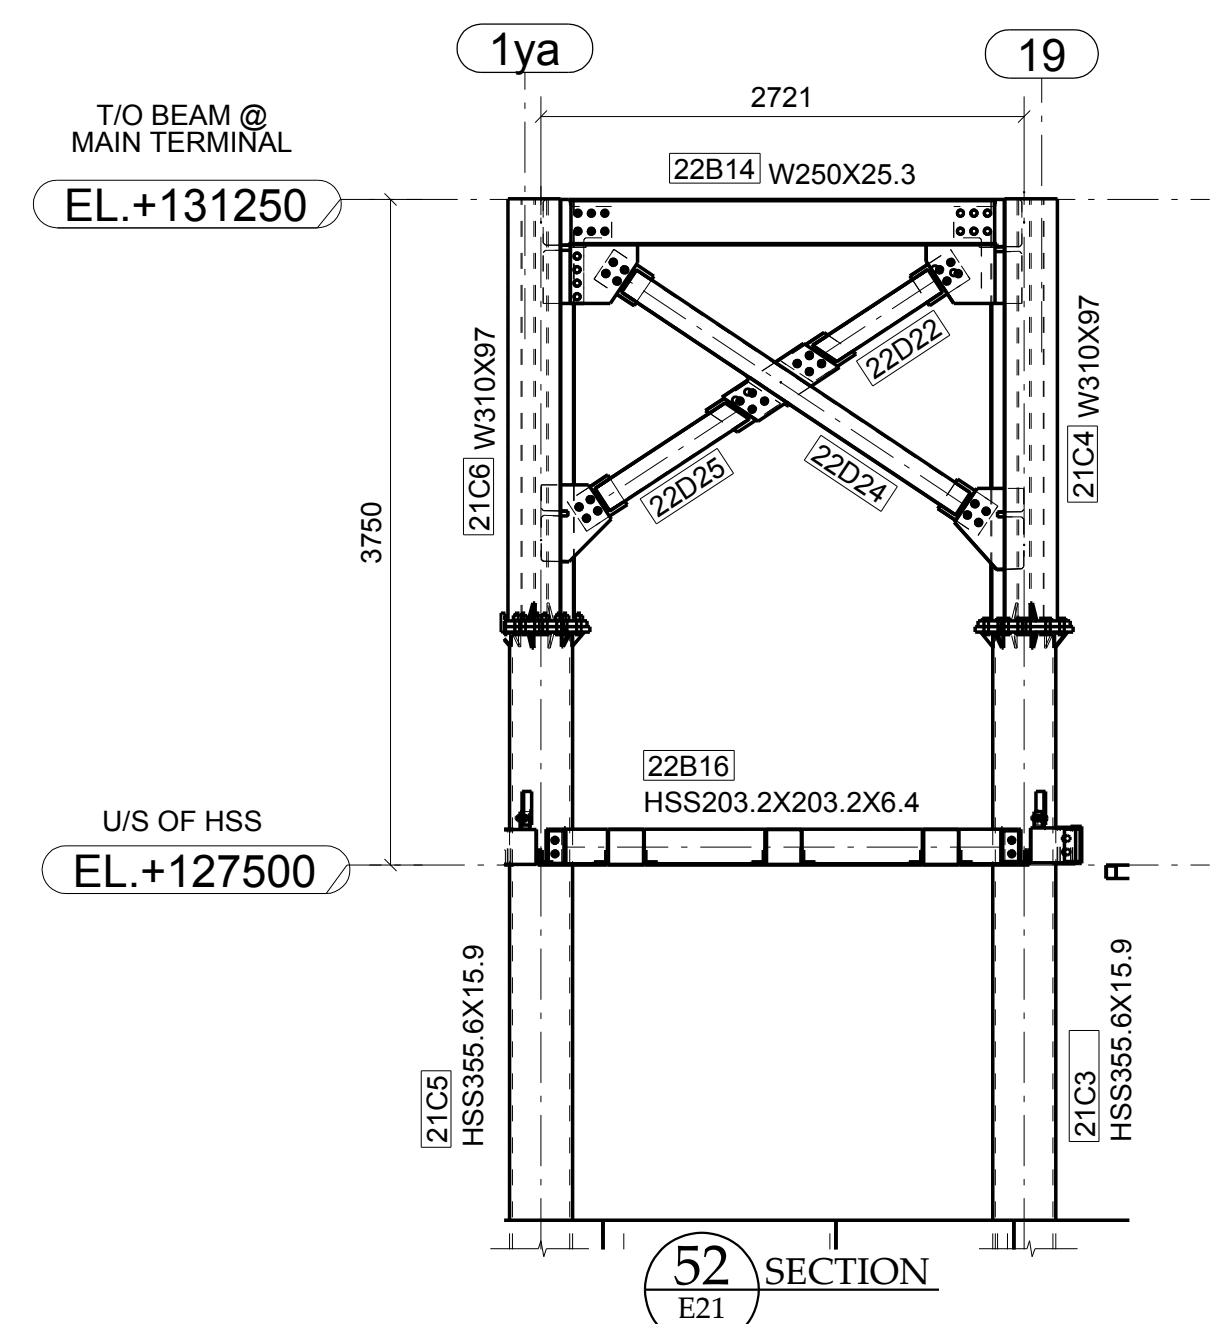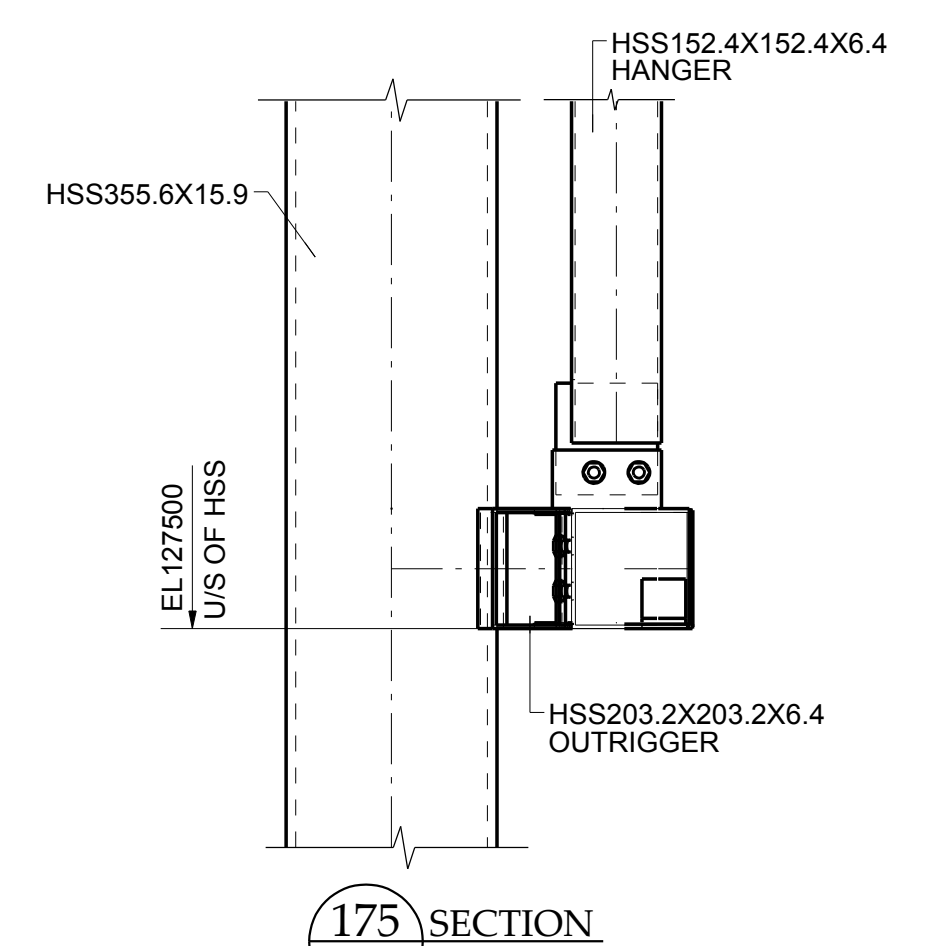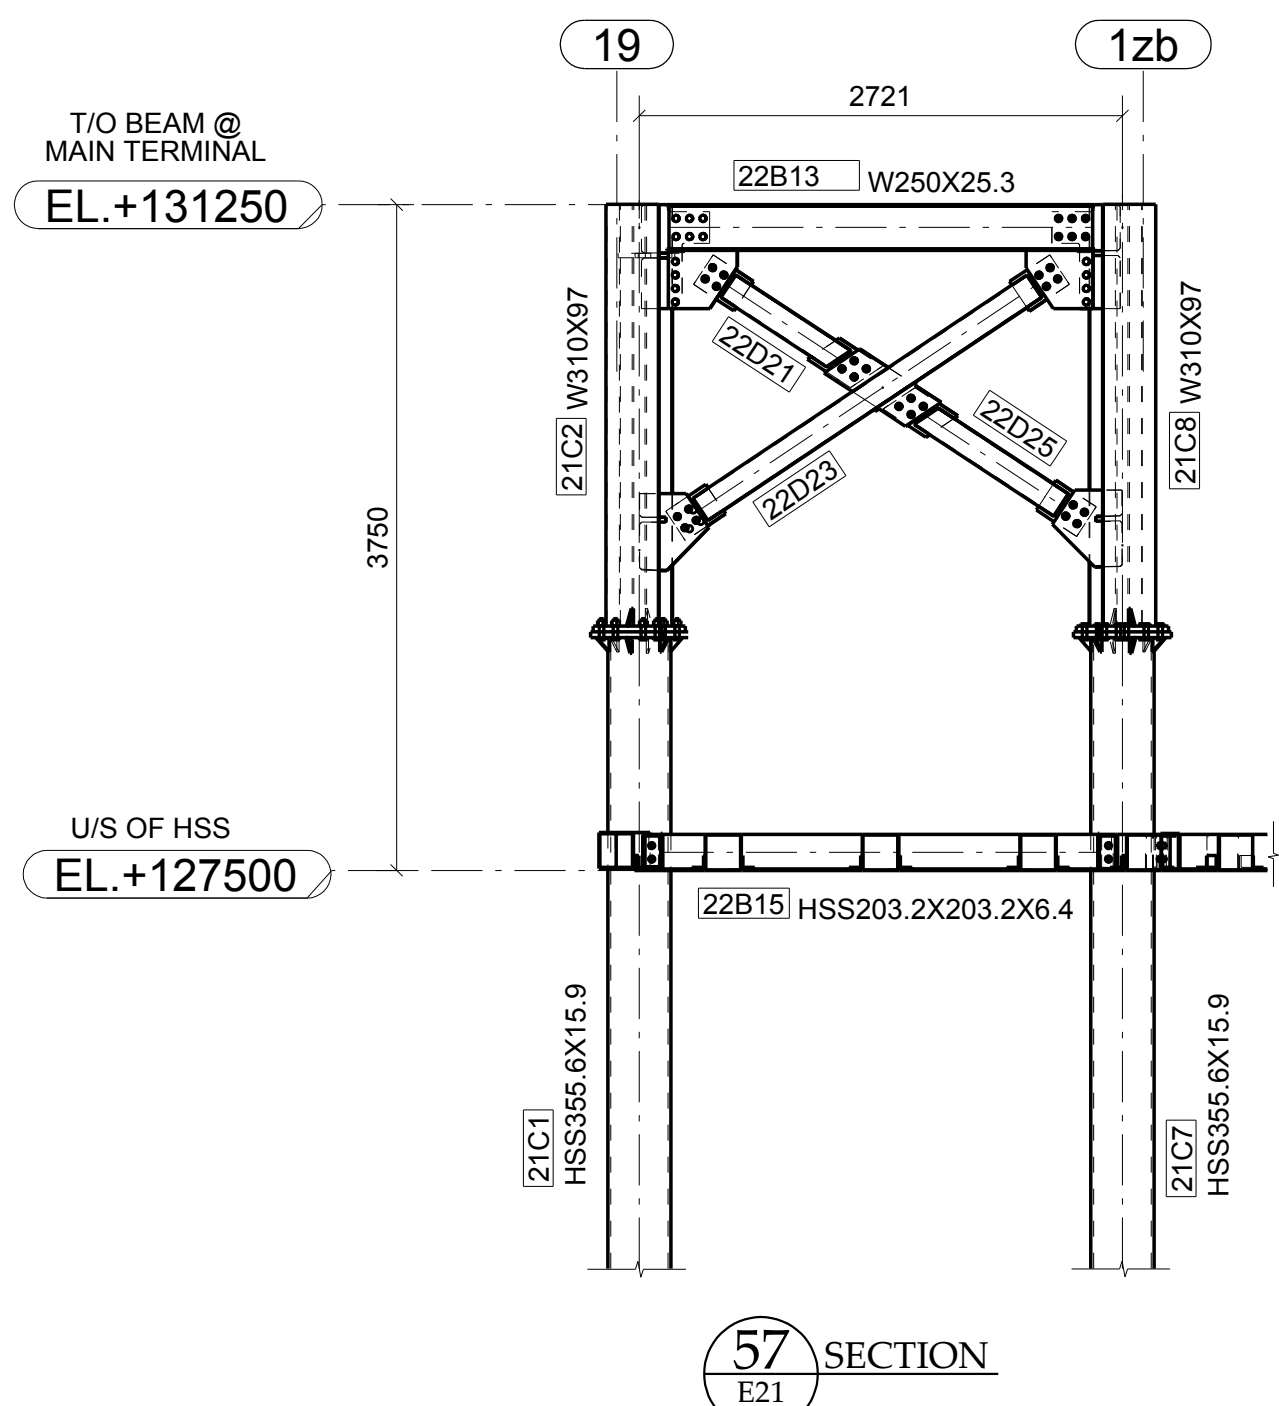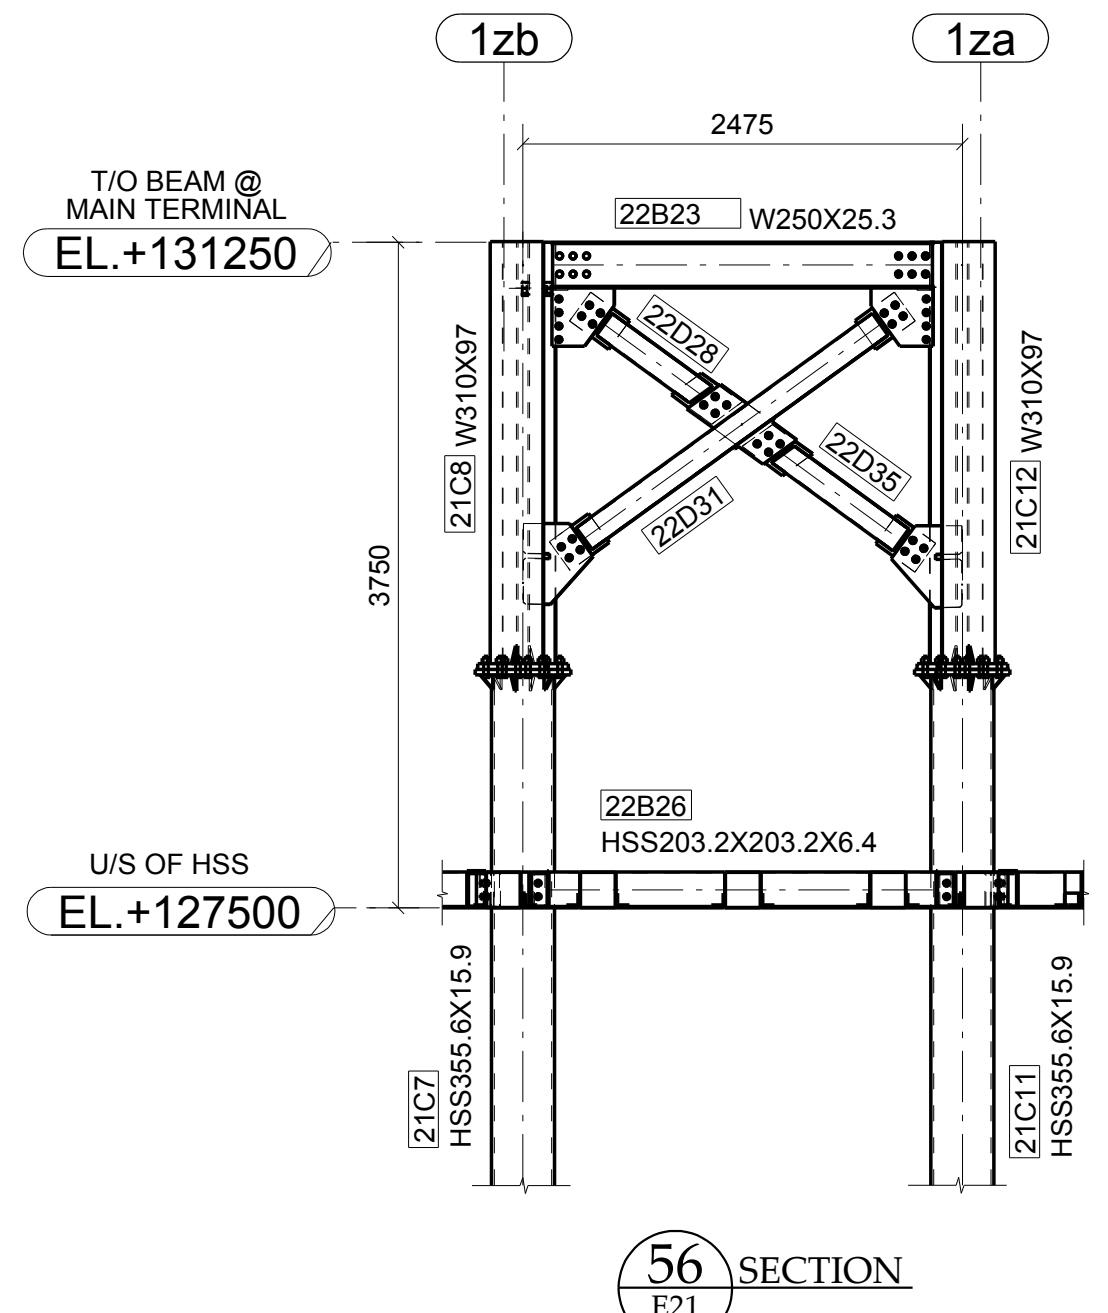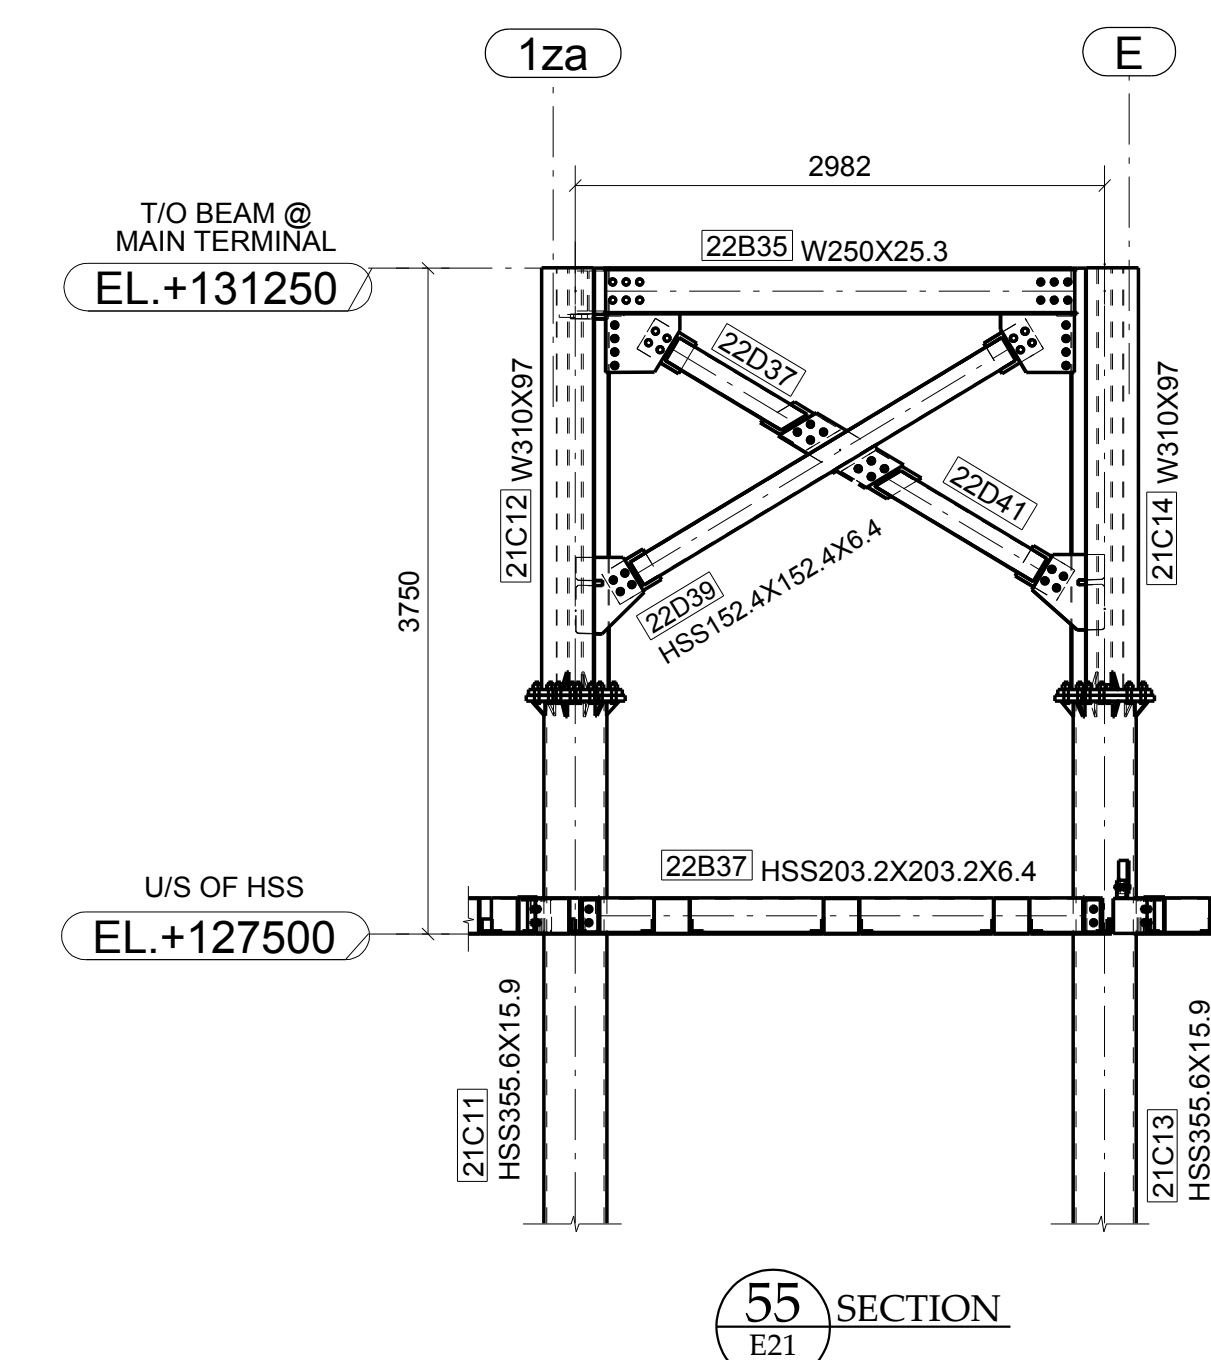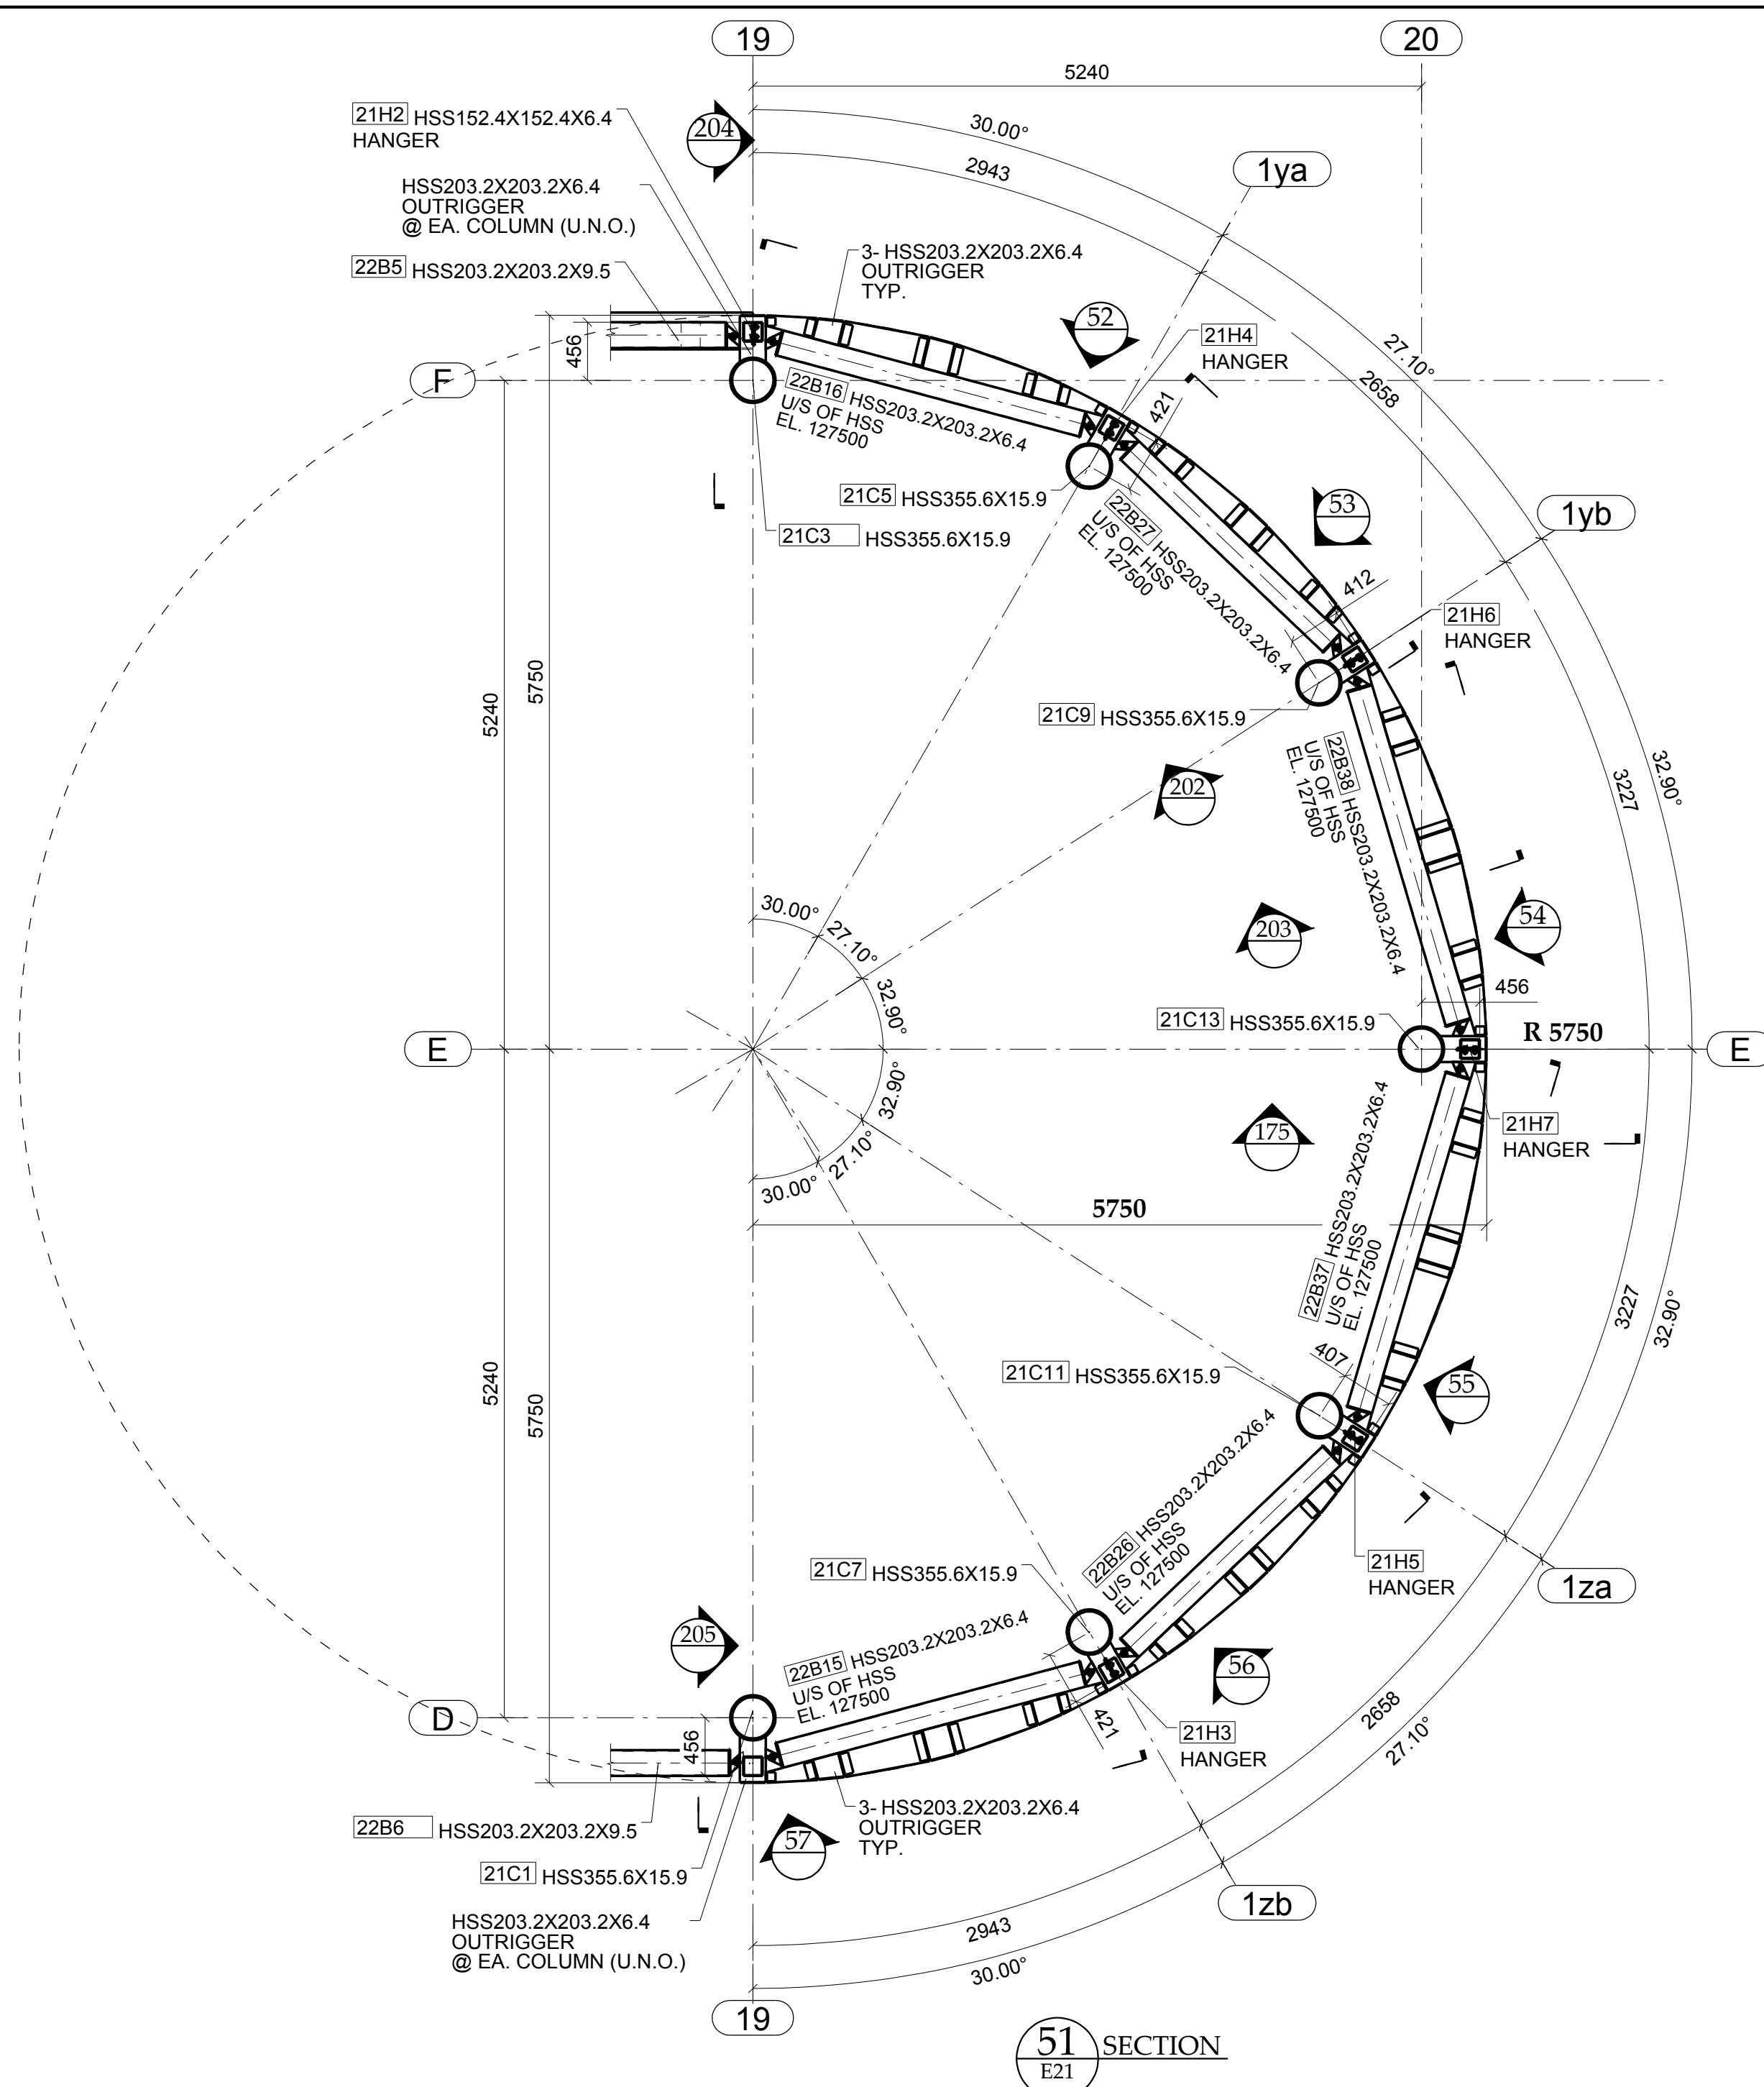

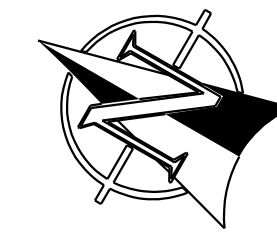

TRUE NORTH

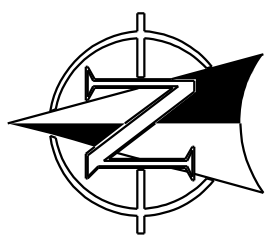


PROJECT NORTH

NOTES :


- FINISH FLOOR ELEVATION = 0.00 = DATUM.

▼ - INDICATES ORIENTATION MARK

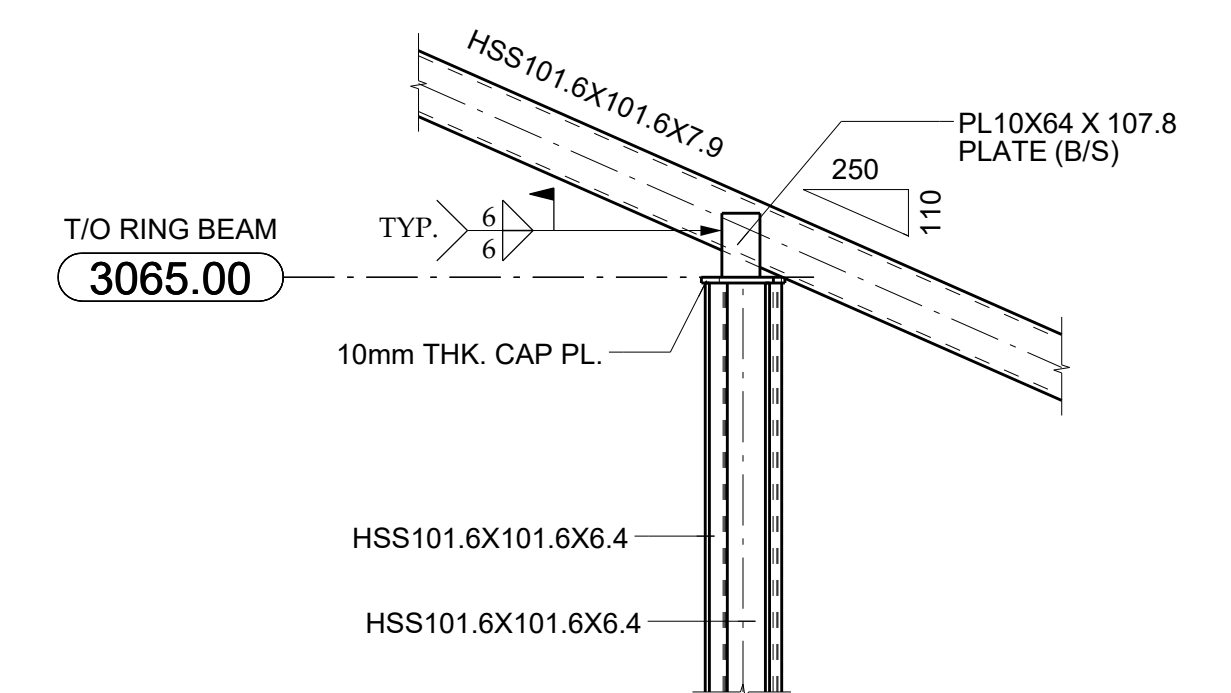

3 SECTION


TYPICAL CONNECTION DETAIL FOR
SLOPED HSS BEAM TO HSS COLUMN

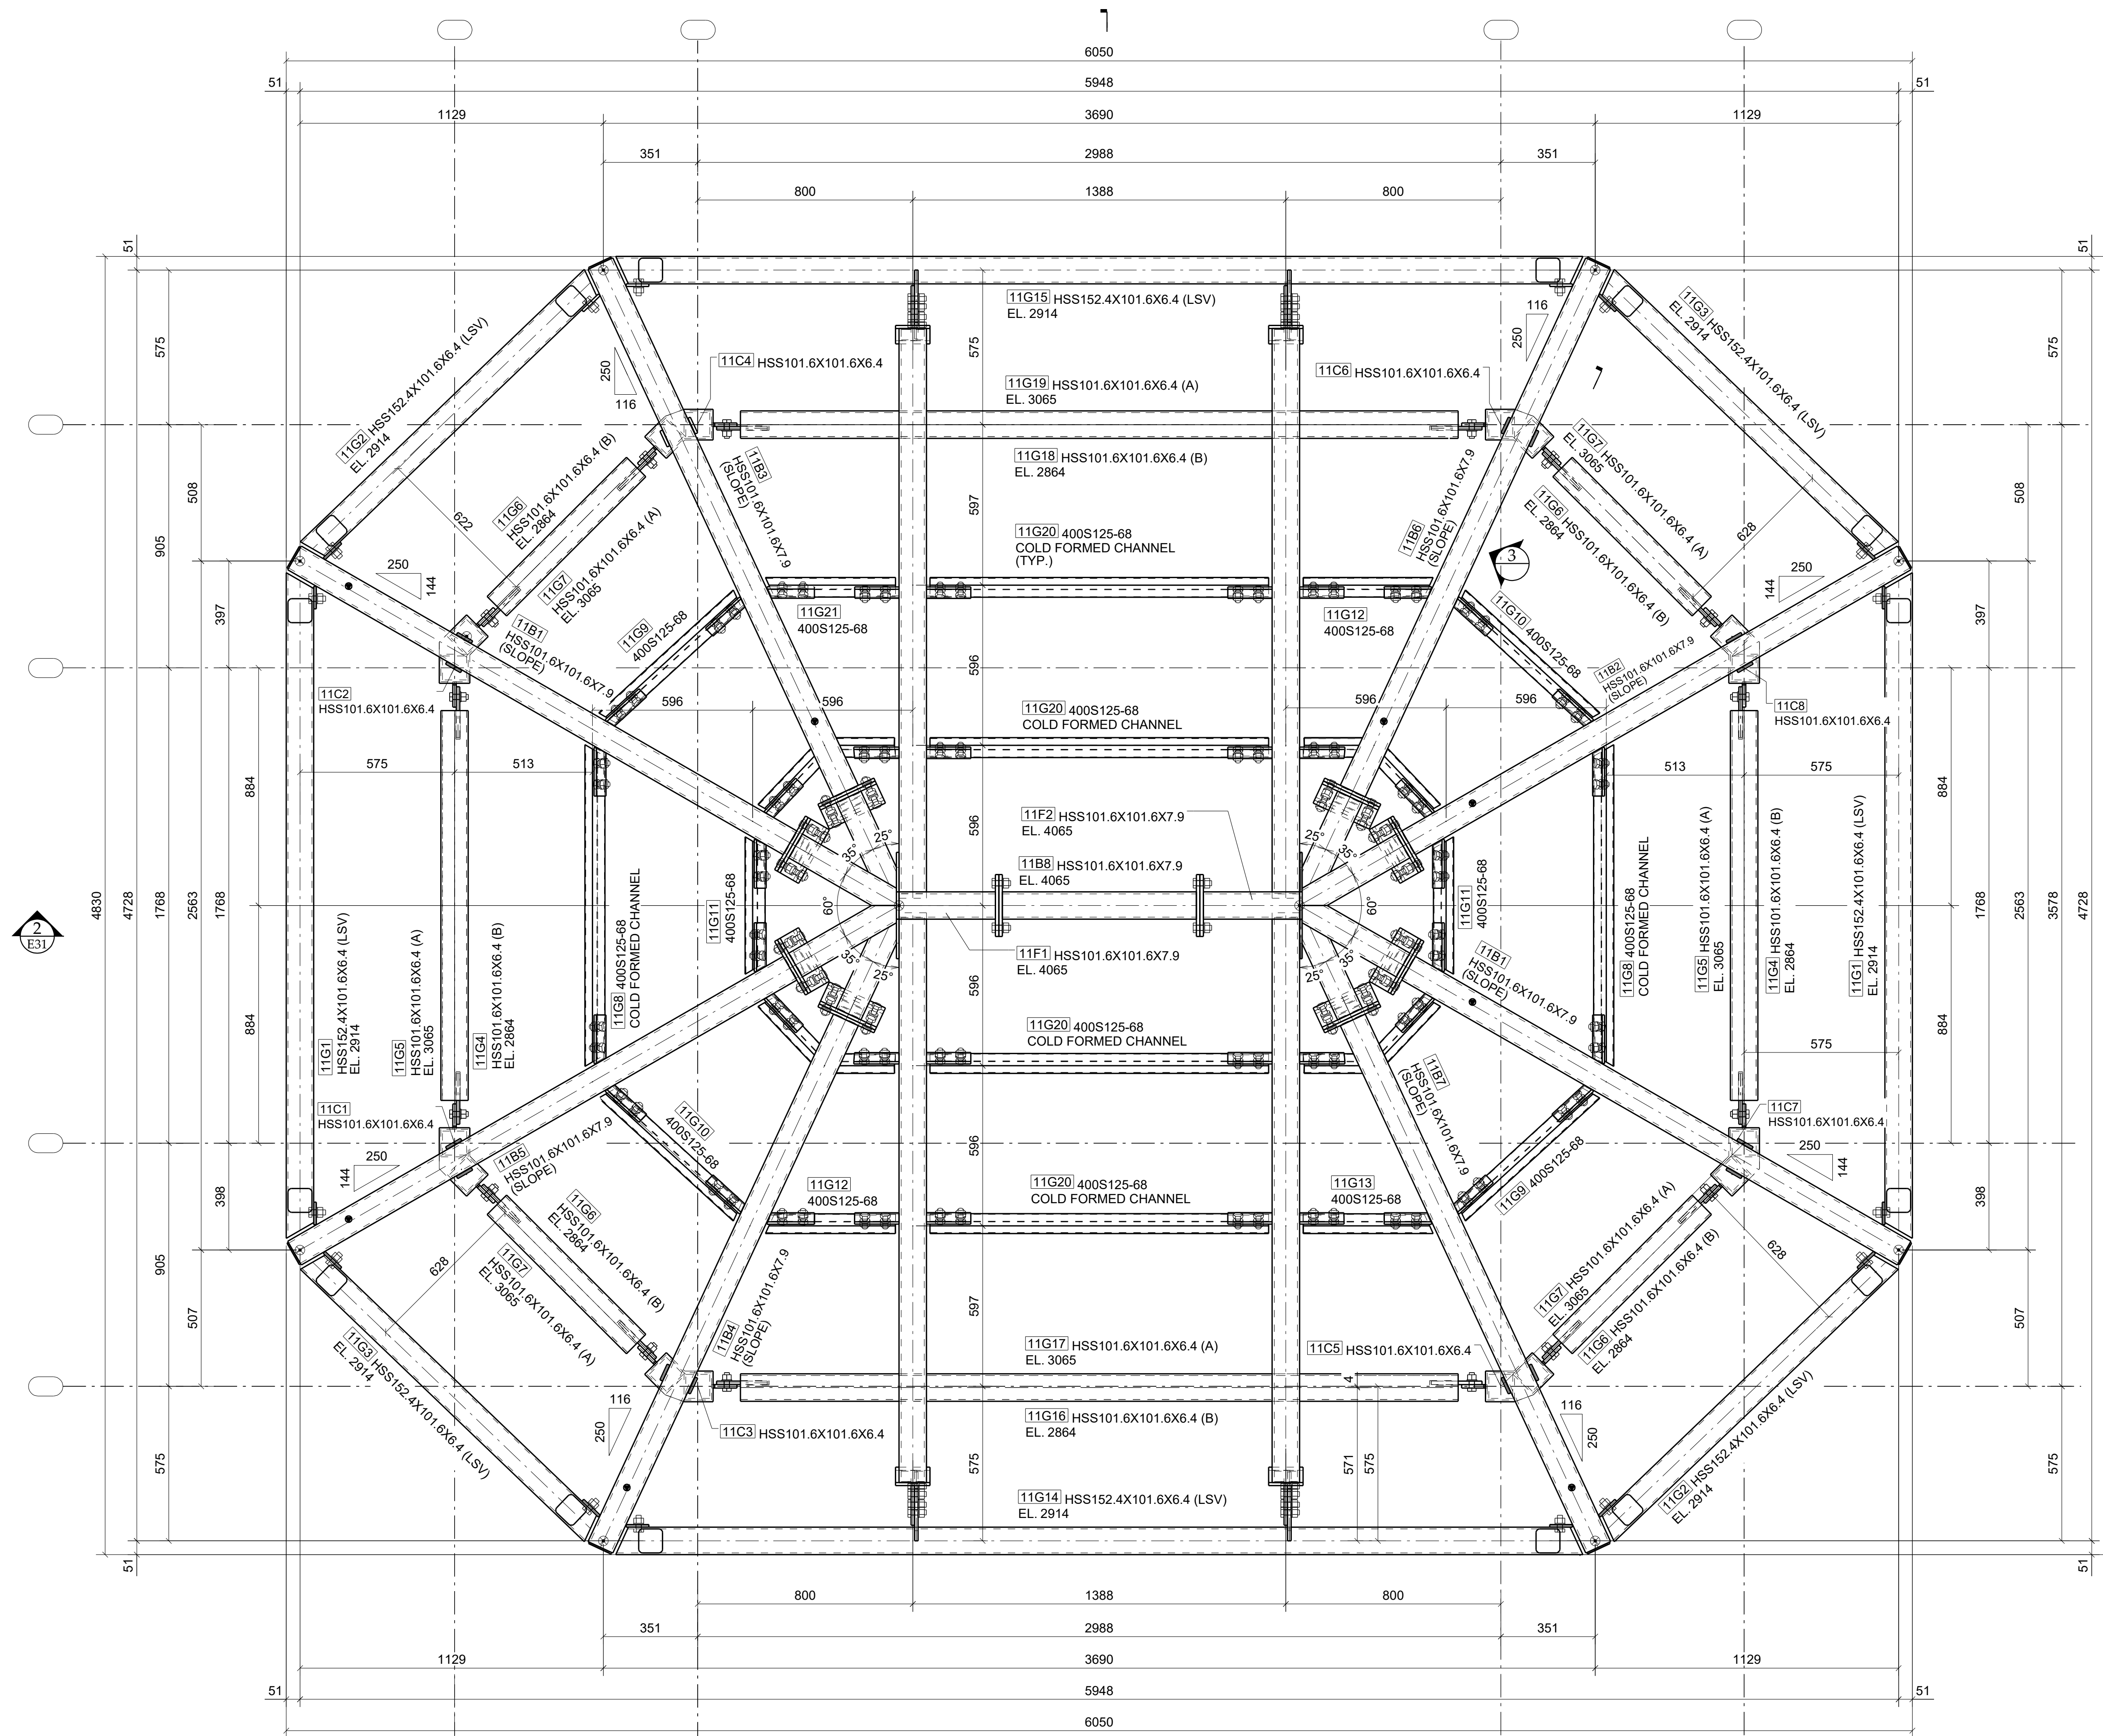


GAZEBO FRAMING PLAN



**DIMENSION ARE GIVEN
FROM THE REFERENCE OF
DEGREES (61° 151° 241° 331°)**


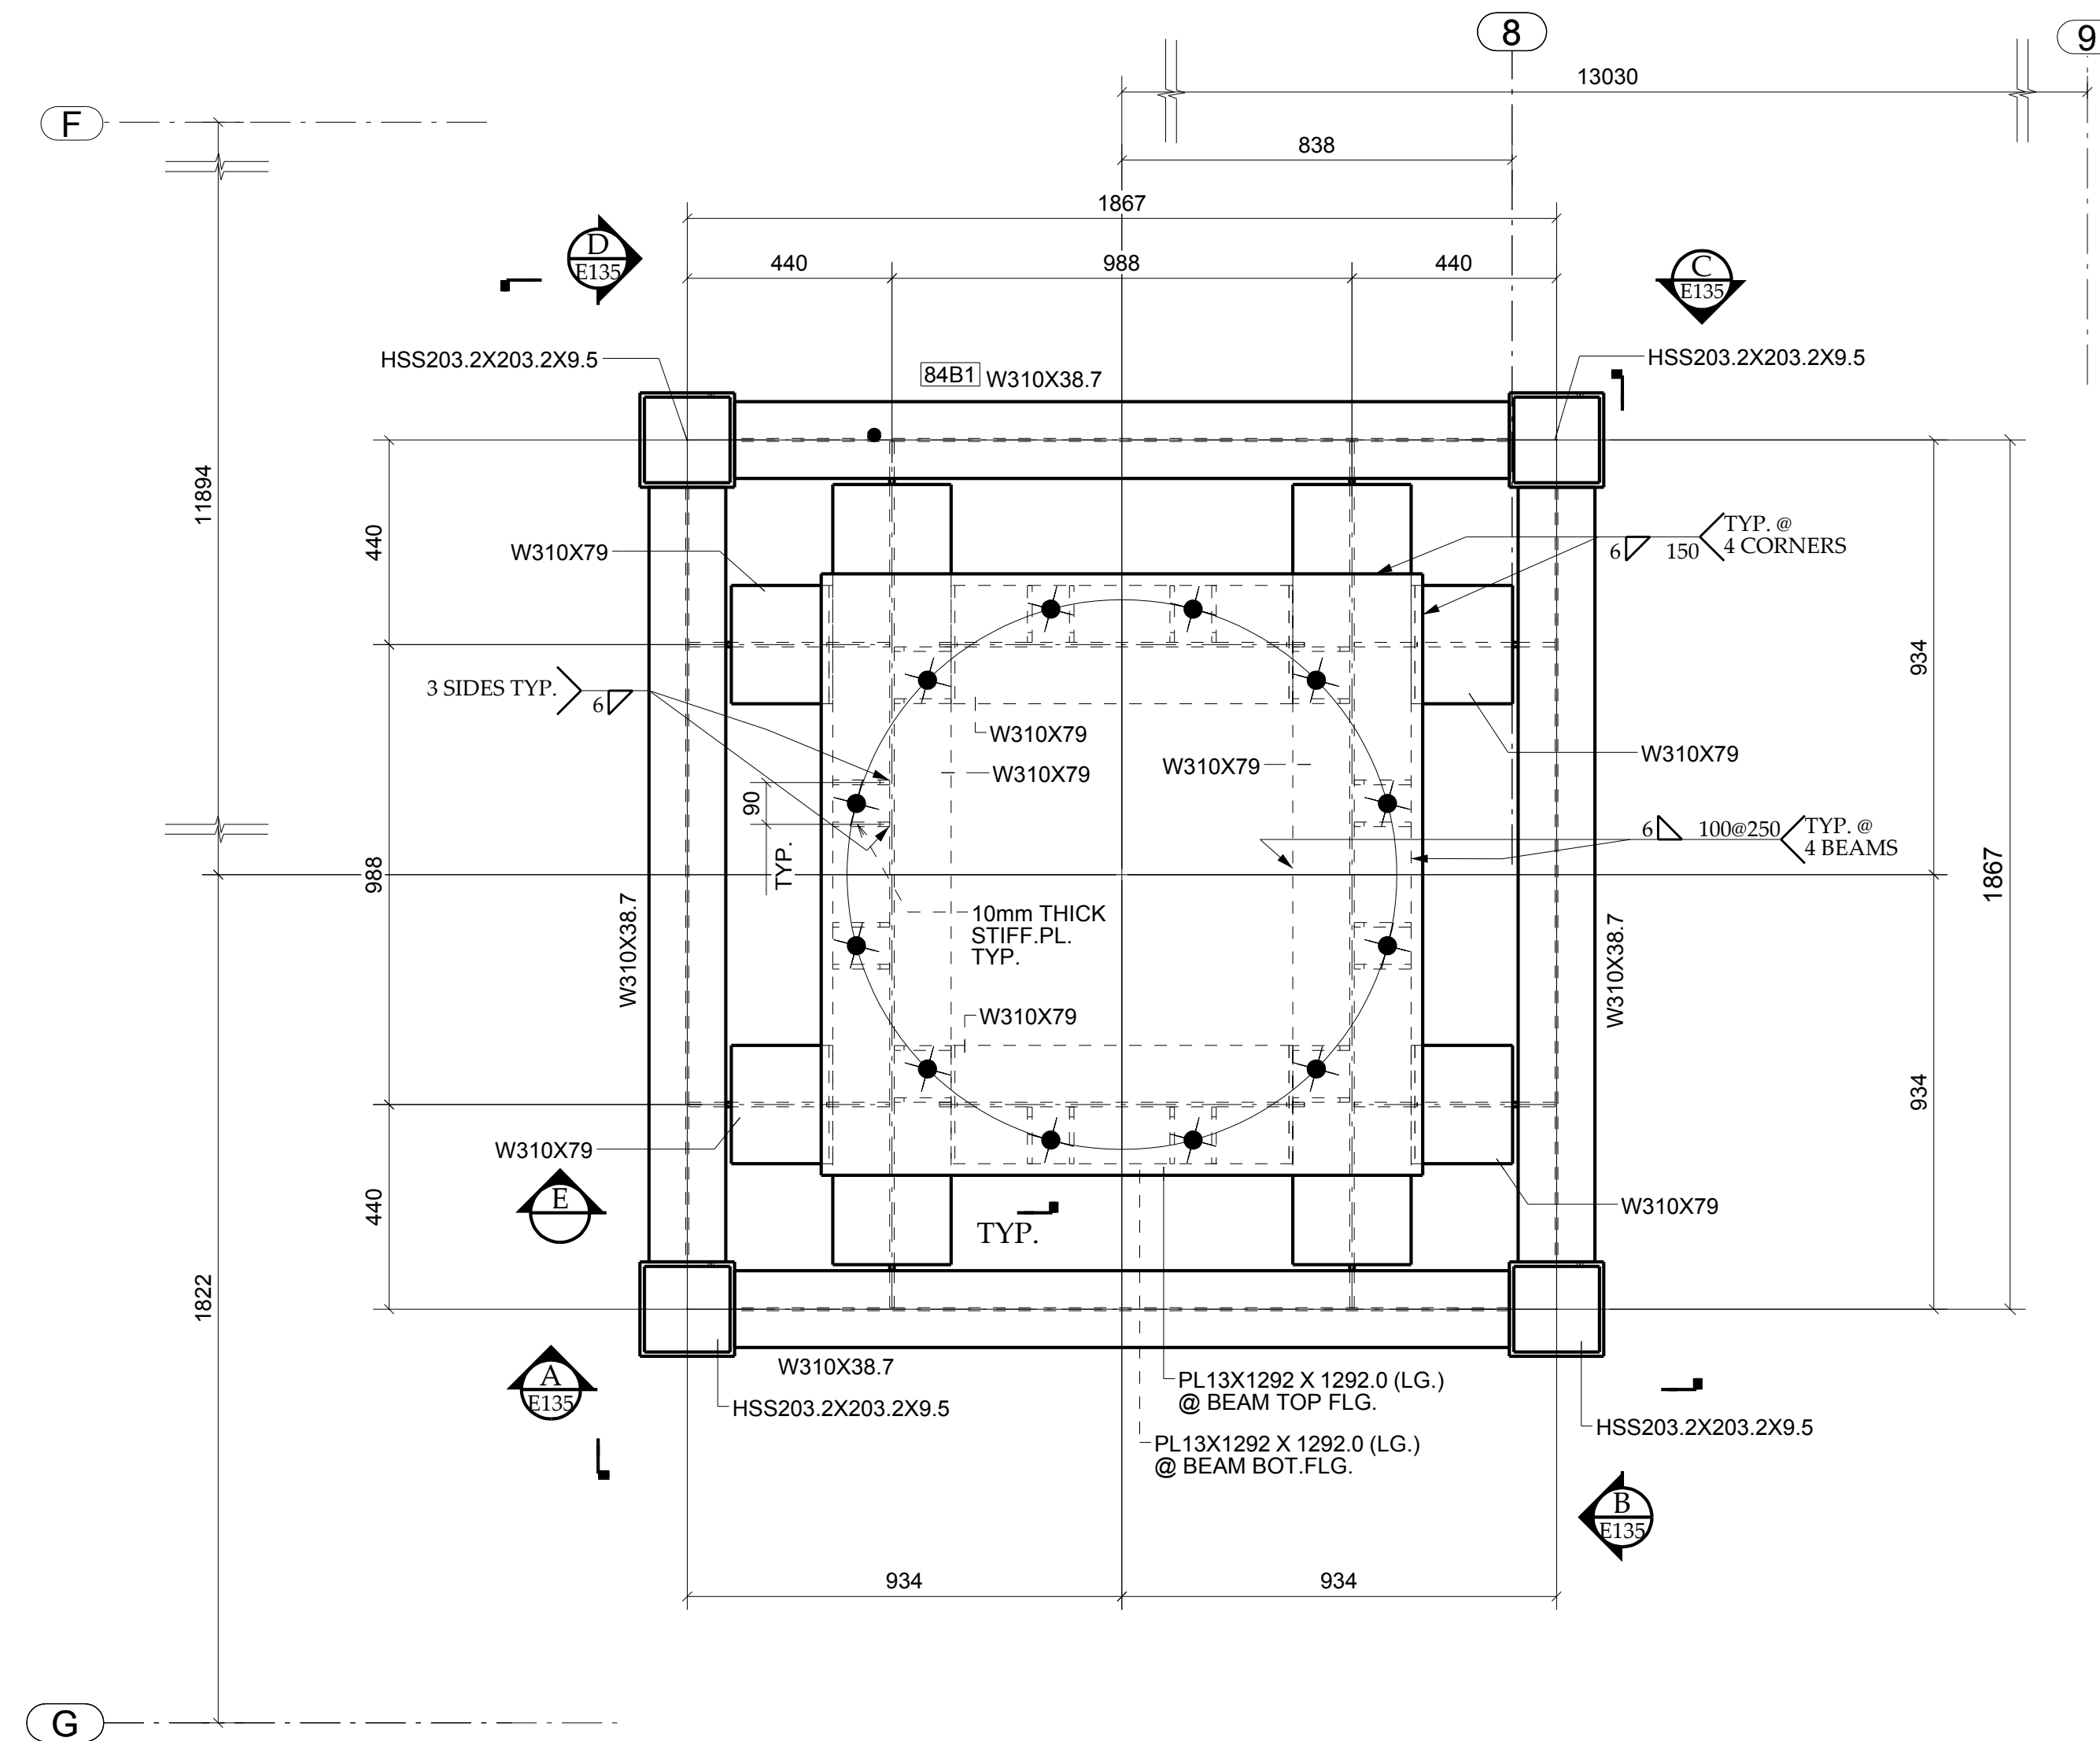


ALL STEELS ARE GALVANIZED

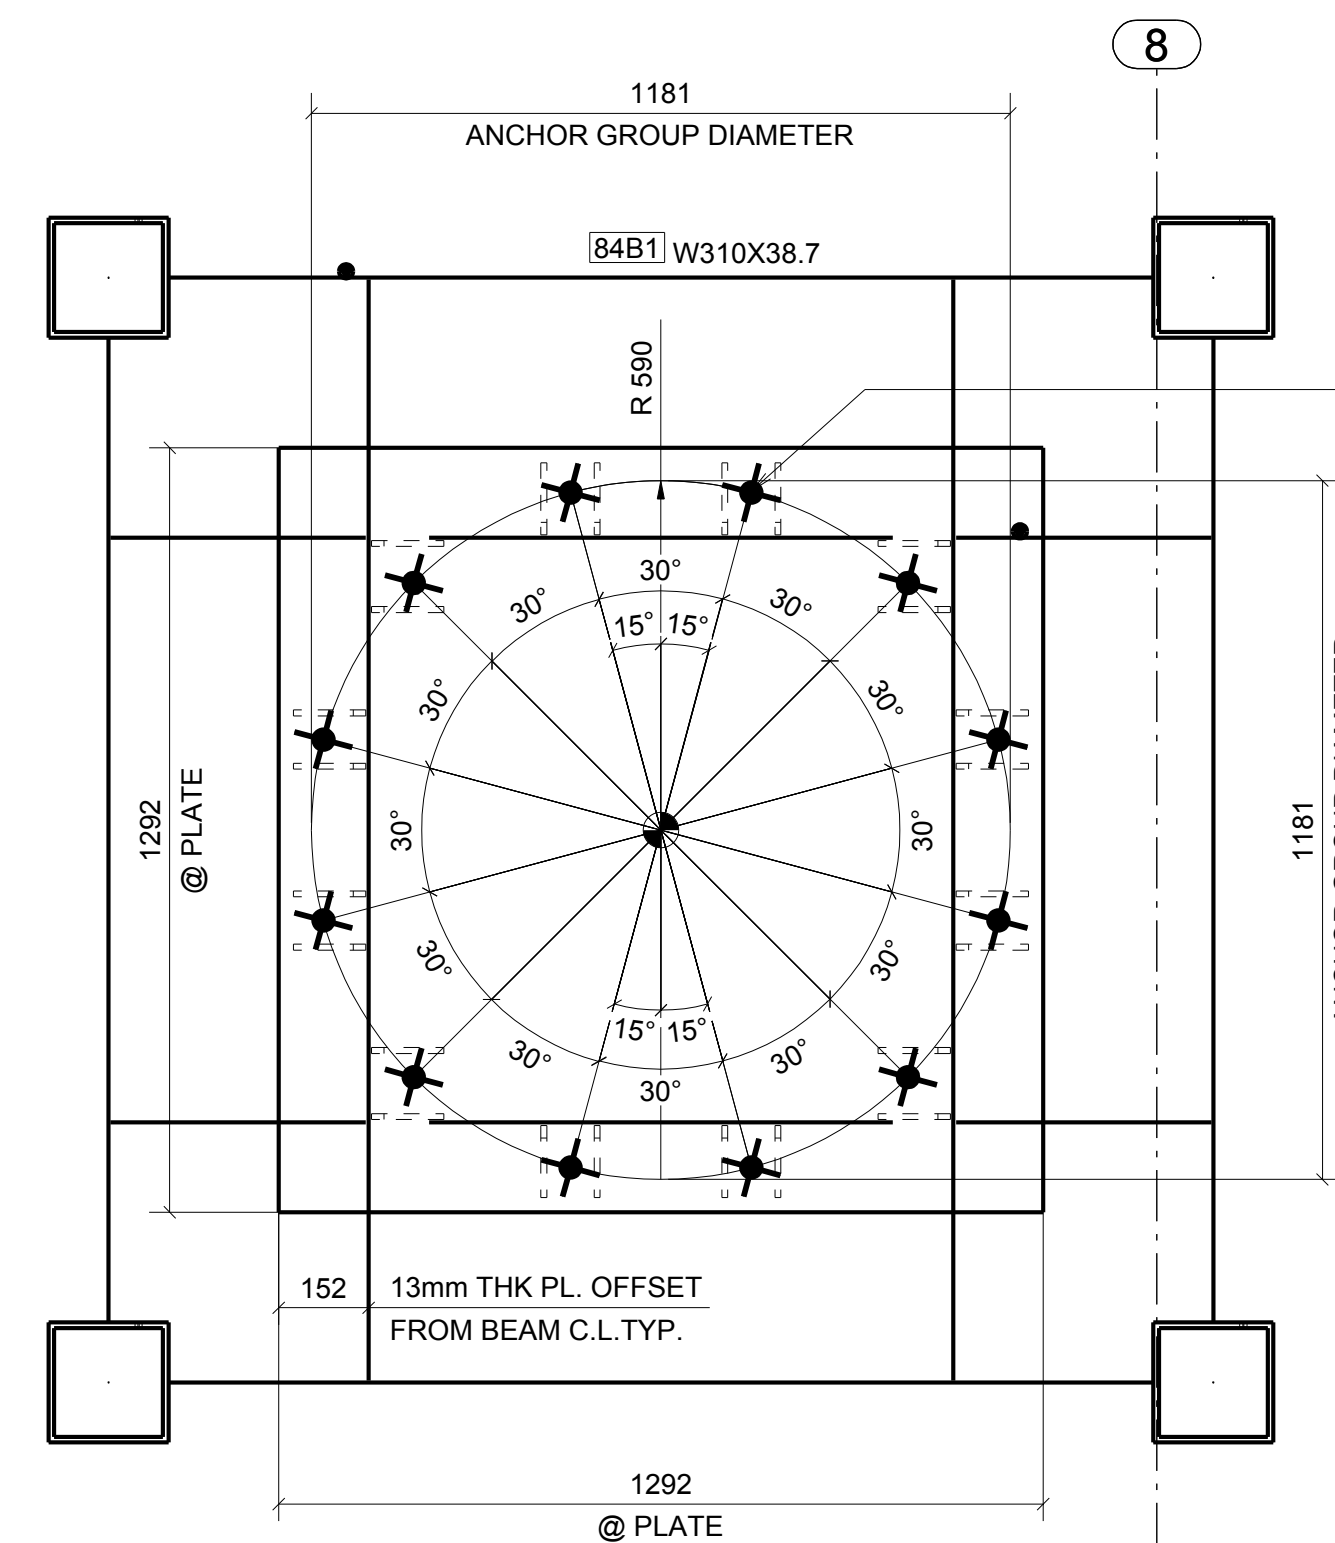


— 12- 1 ½" ANCHORS BY OTHERS
(41.3mm Ø HOLES IN BEAM TOP FLG. , BOT FLG.
& 13mm THK PLATE @ ABOVE BEAM TPP & BOT.FLG.)

DETAILED VIEW FOR ANCHOR ROD LOCATION

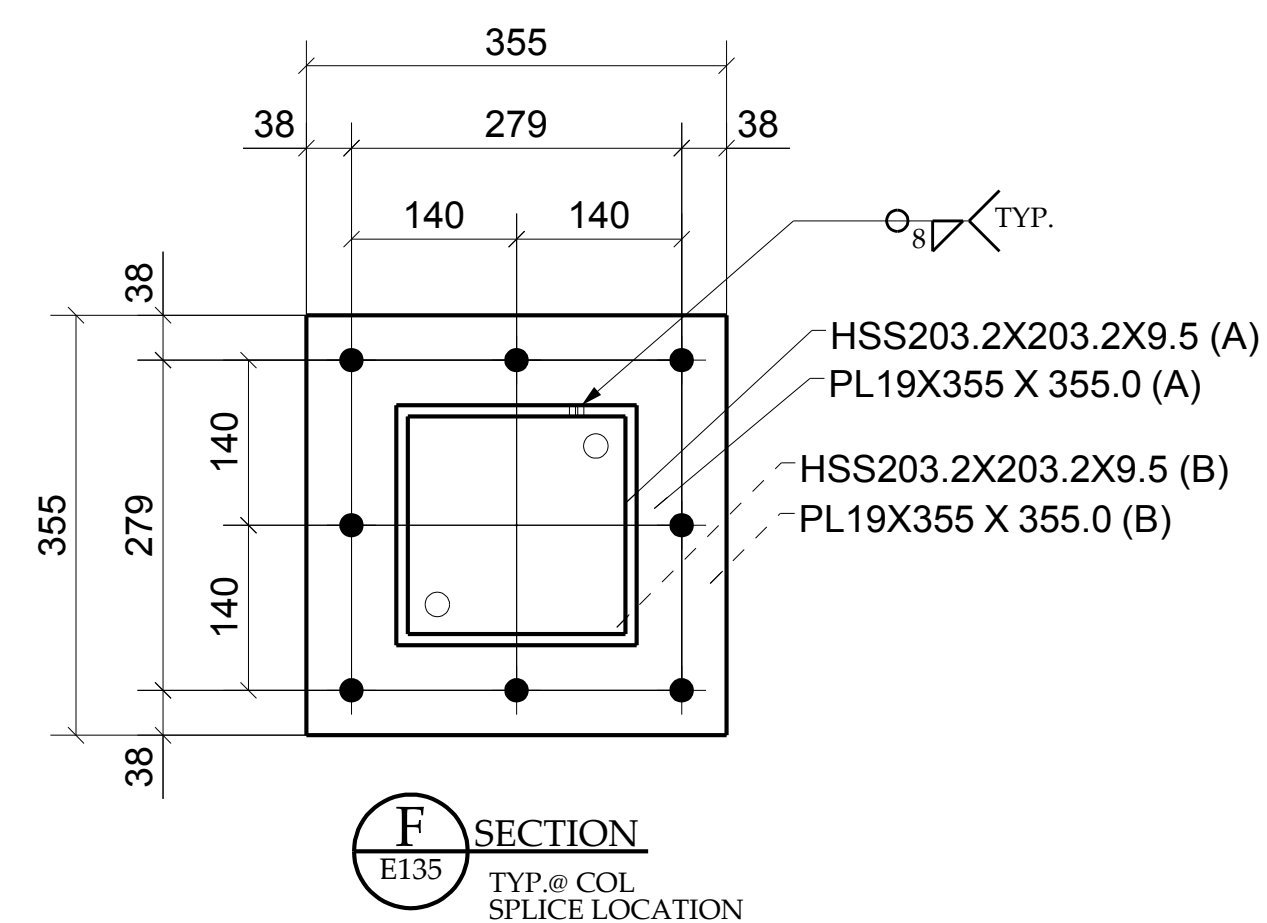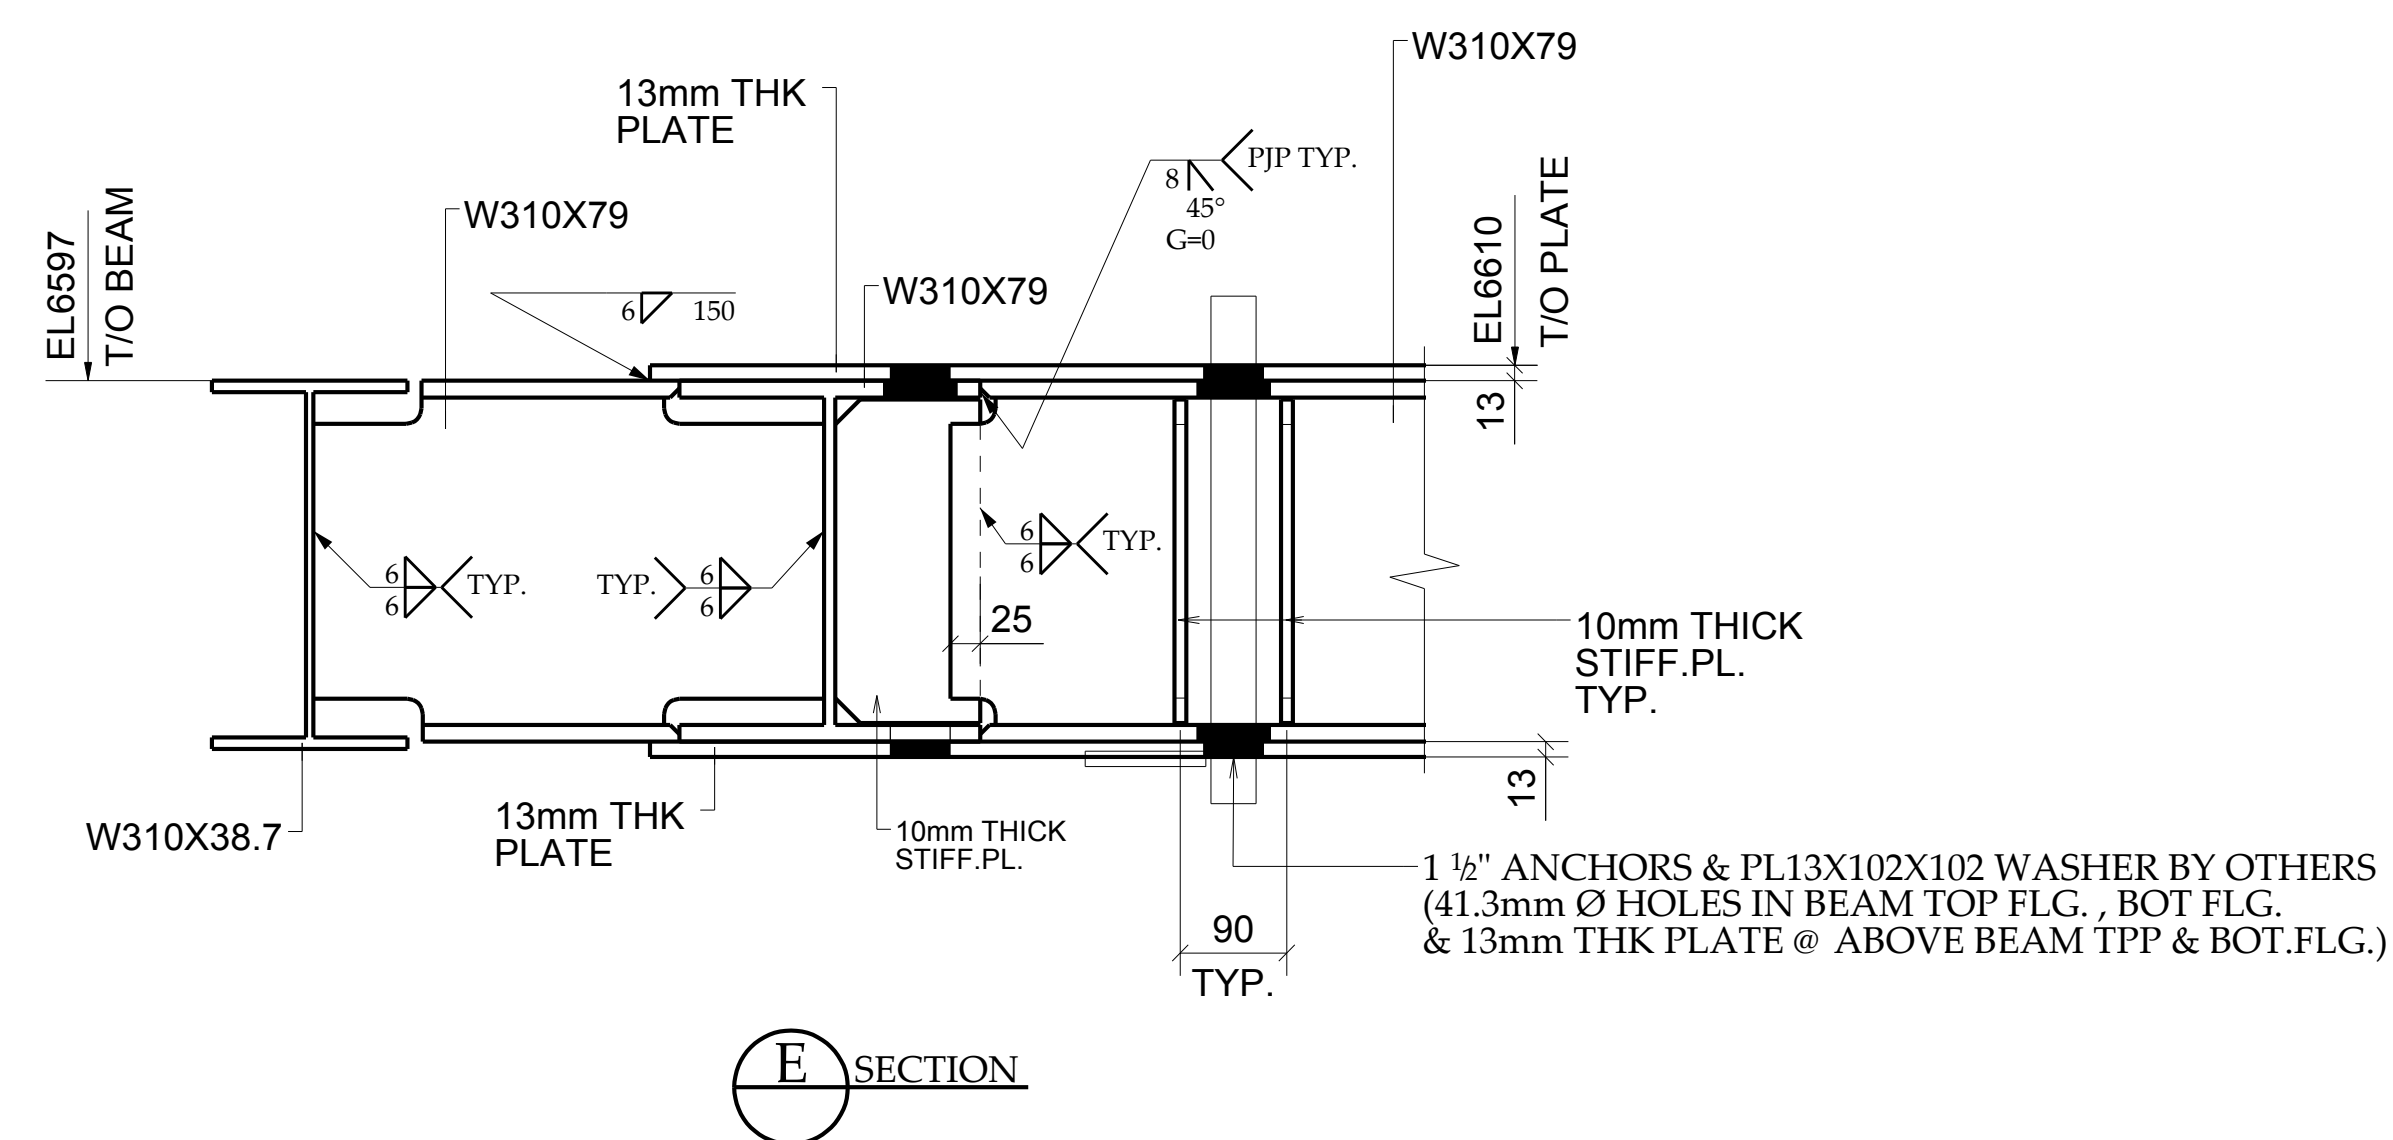




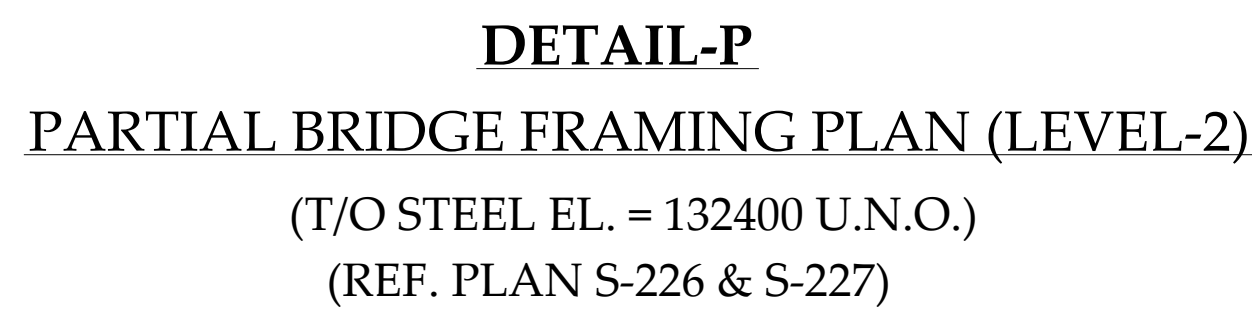



- T/O STEEL = U/S OF DECK = 132400 U.N.O.
- 'RA' INDICATES ROOF ANCHORS
- E.O.A. INDICATES EDGE OF ANGLE
- E.O.BPL. INDICATES EDGE OF BENT PL.
- ▼ - INDICATES ORIENTATIO OF THE MEMBER
- - INDICATES MOMENT CONNECTION


DETAIL-Q
PARTIAL BRIDGE FRAMING PLAN (LEVEL-2)
(T/O STEEL EL. = 132400 U.N.O.)
(REF. PLAN S-226 & S-227)

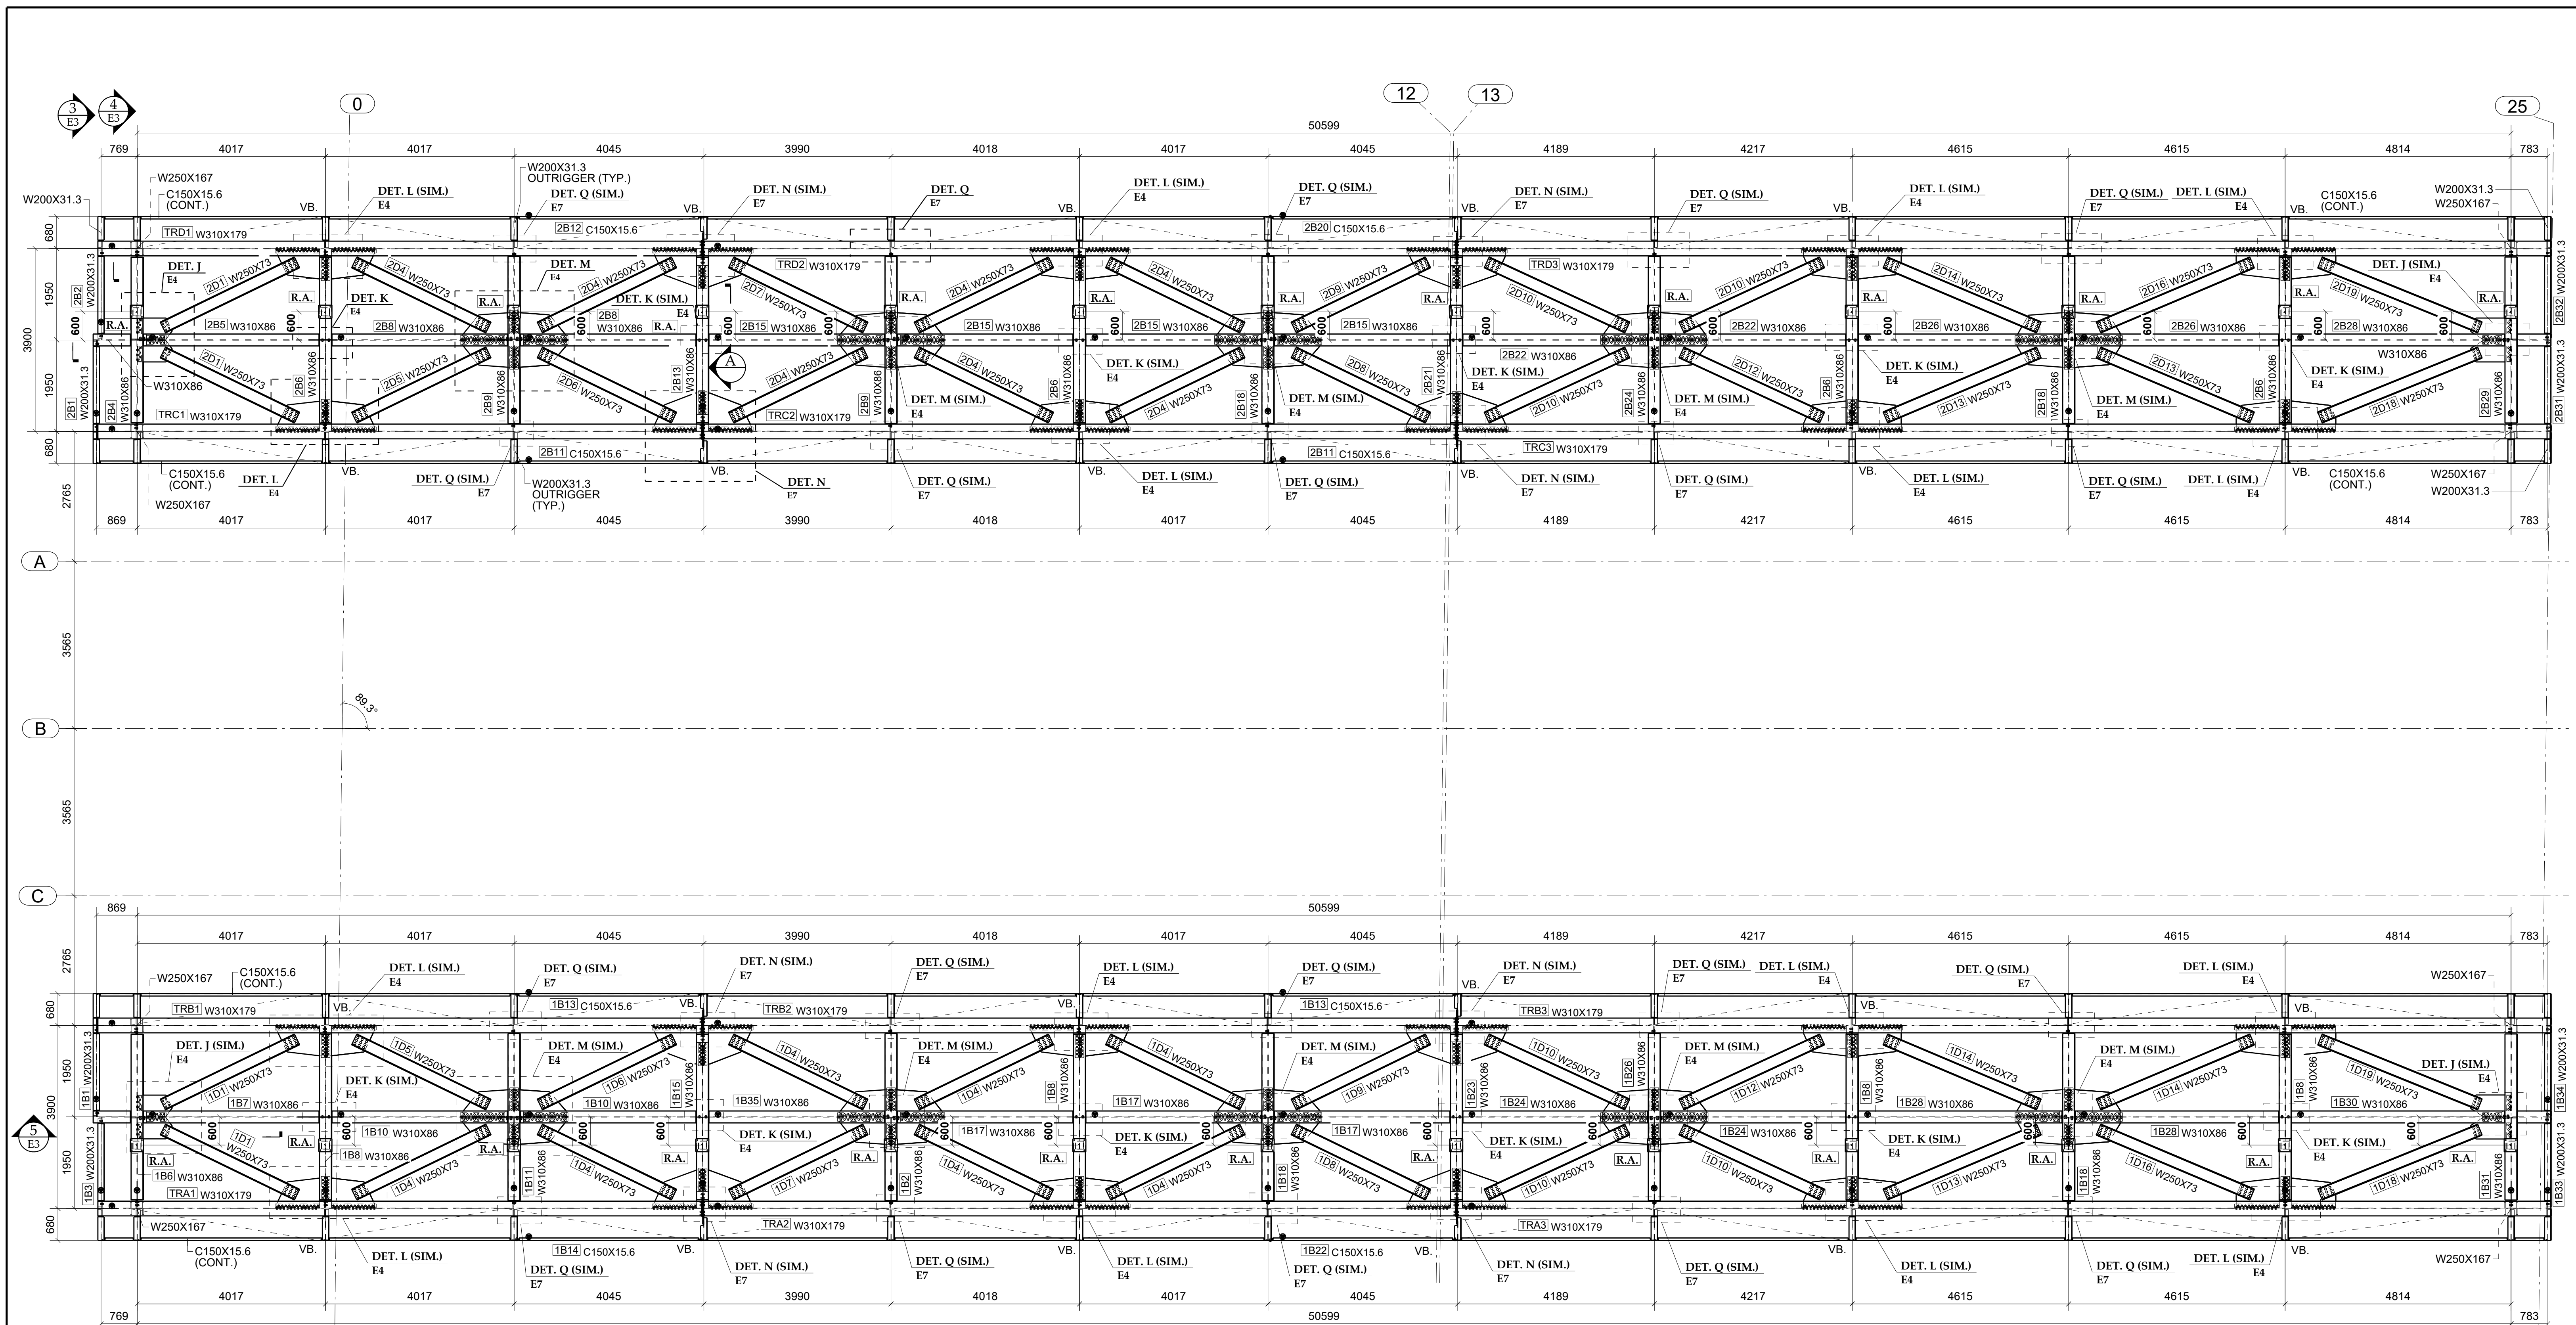

TOP CHORD FRAMING PLAN
REF:PLAN:S0024

GENERAL NOTES :
R.A. - INDICATES ROOF ANCHORS

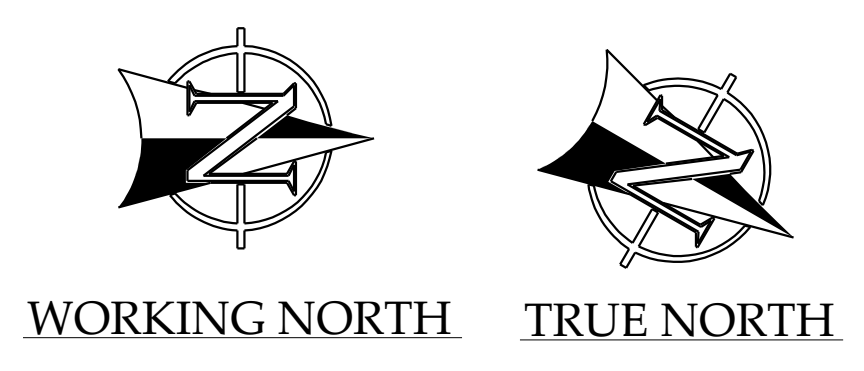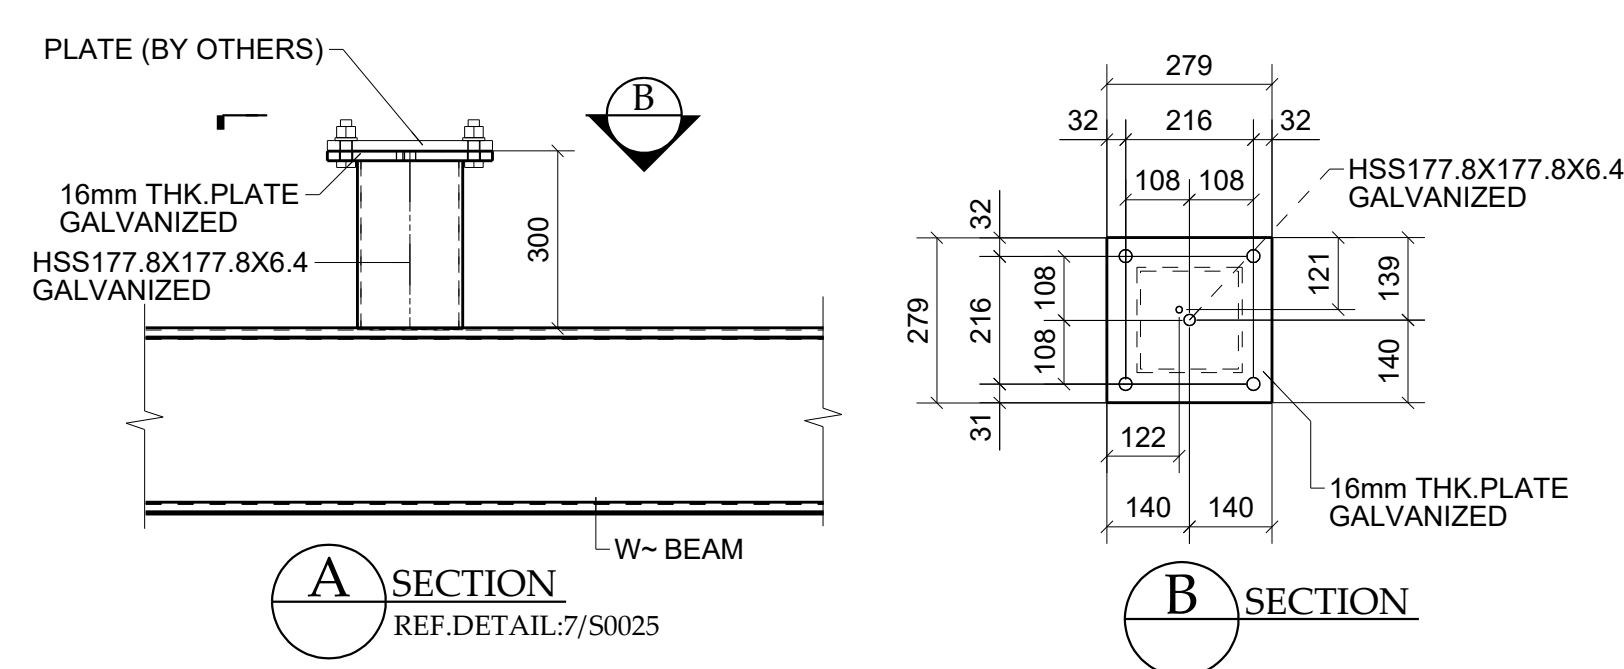


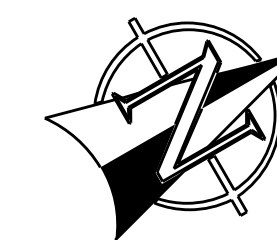

TRUE NORTH WORKING NORTH

NOTES:

- T/O STEEL = U/S OF DECK = EL.16'-5" (U.N.O.)
- E.O.A. - INDICATES EDGE OF ANGLE.
- VB DENOTES VERTICAL BRACE.
- -INDICATES ORIENTATION MARK.
- L.P. - INDICATES LOW POINT

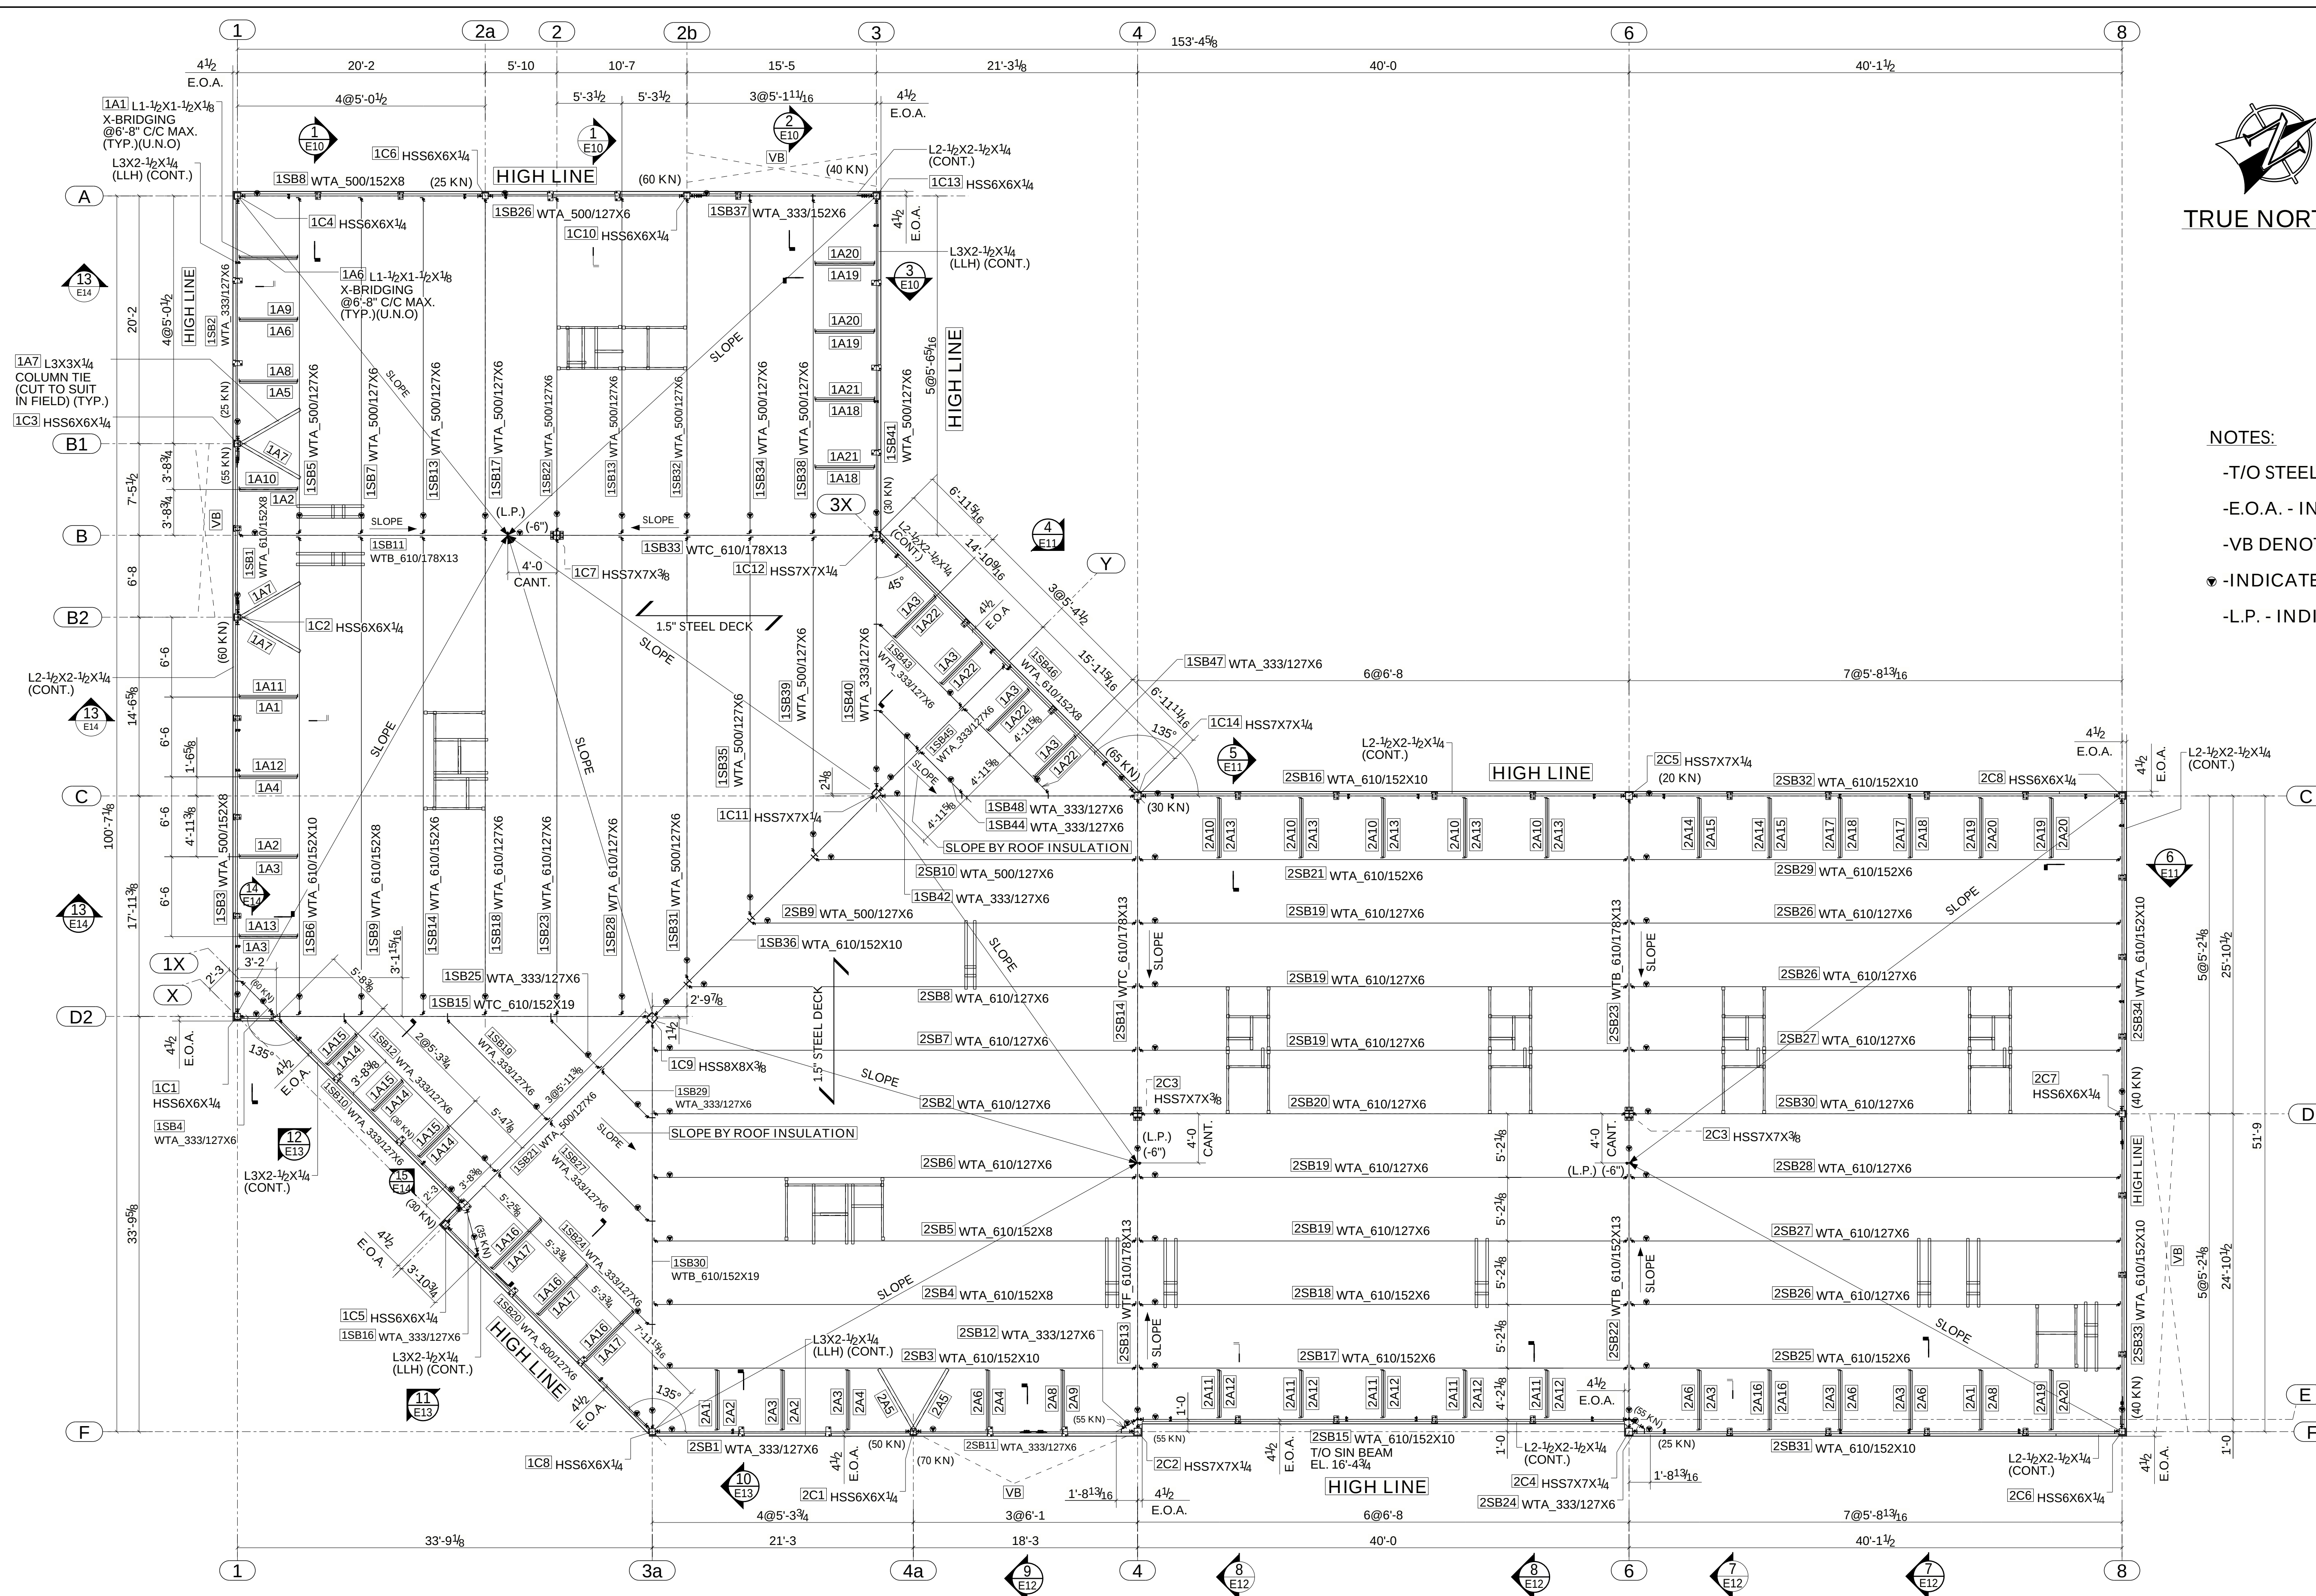

ROOF FRAMING PLAN

(T/O STEEL = U/S OF DECK = EL.16'-5" U.N.O.)

REFER SHEET E15 FOR RTU DETAILS