




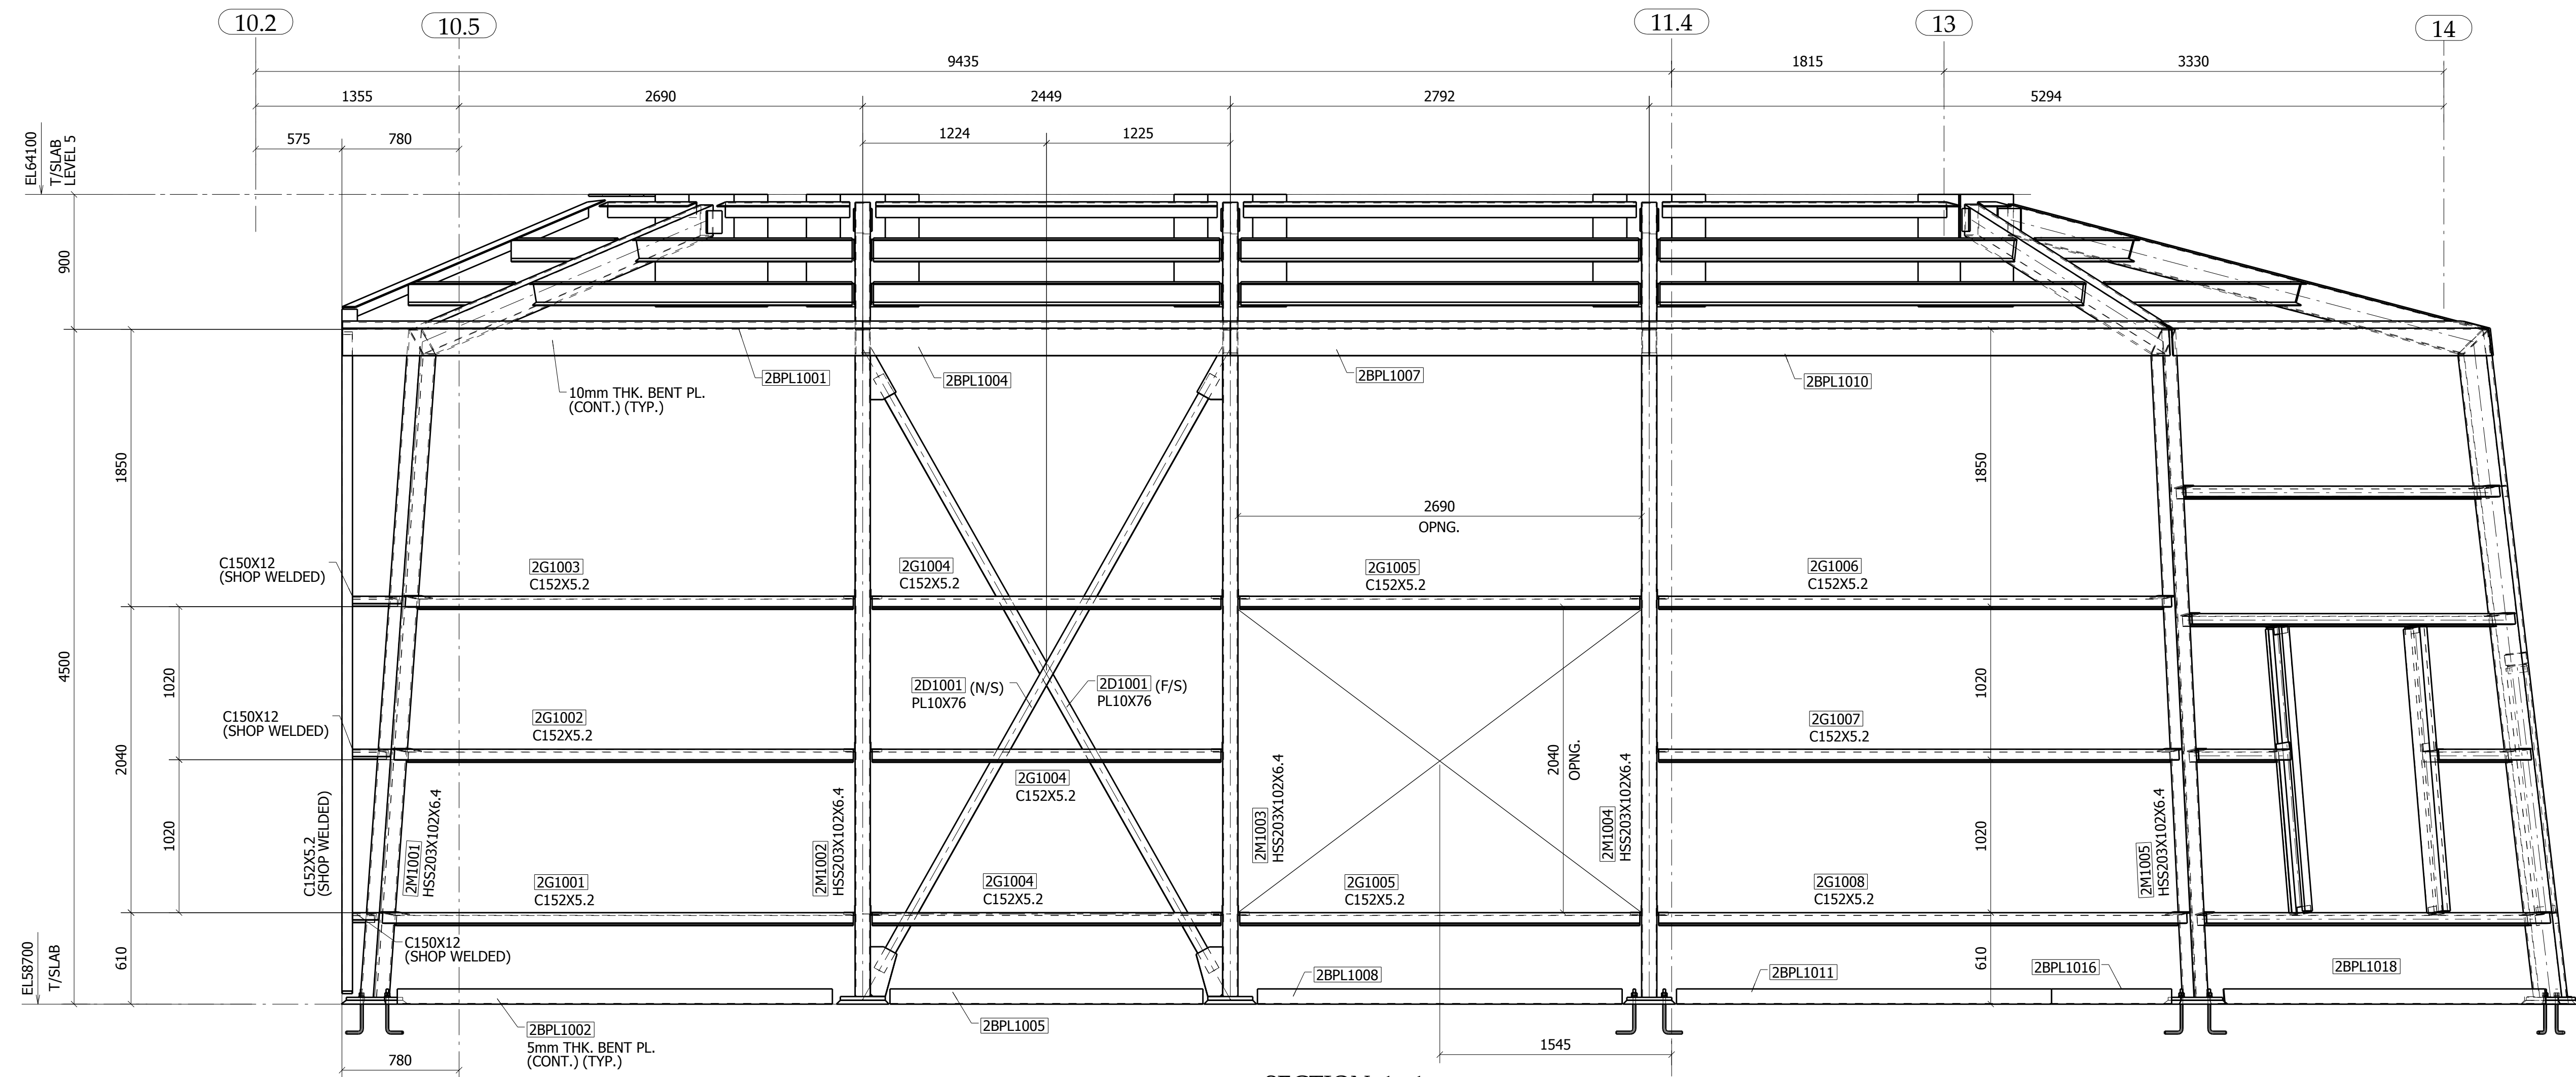


SECTION 1-1
E202
(REF.SEC: 3/S7.16)

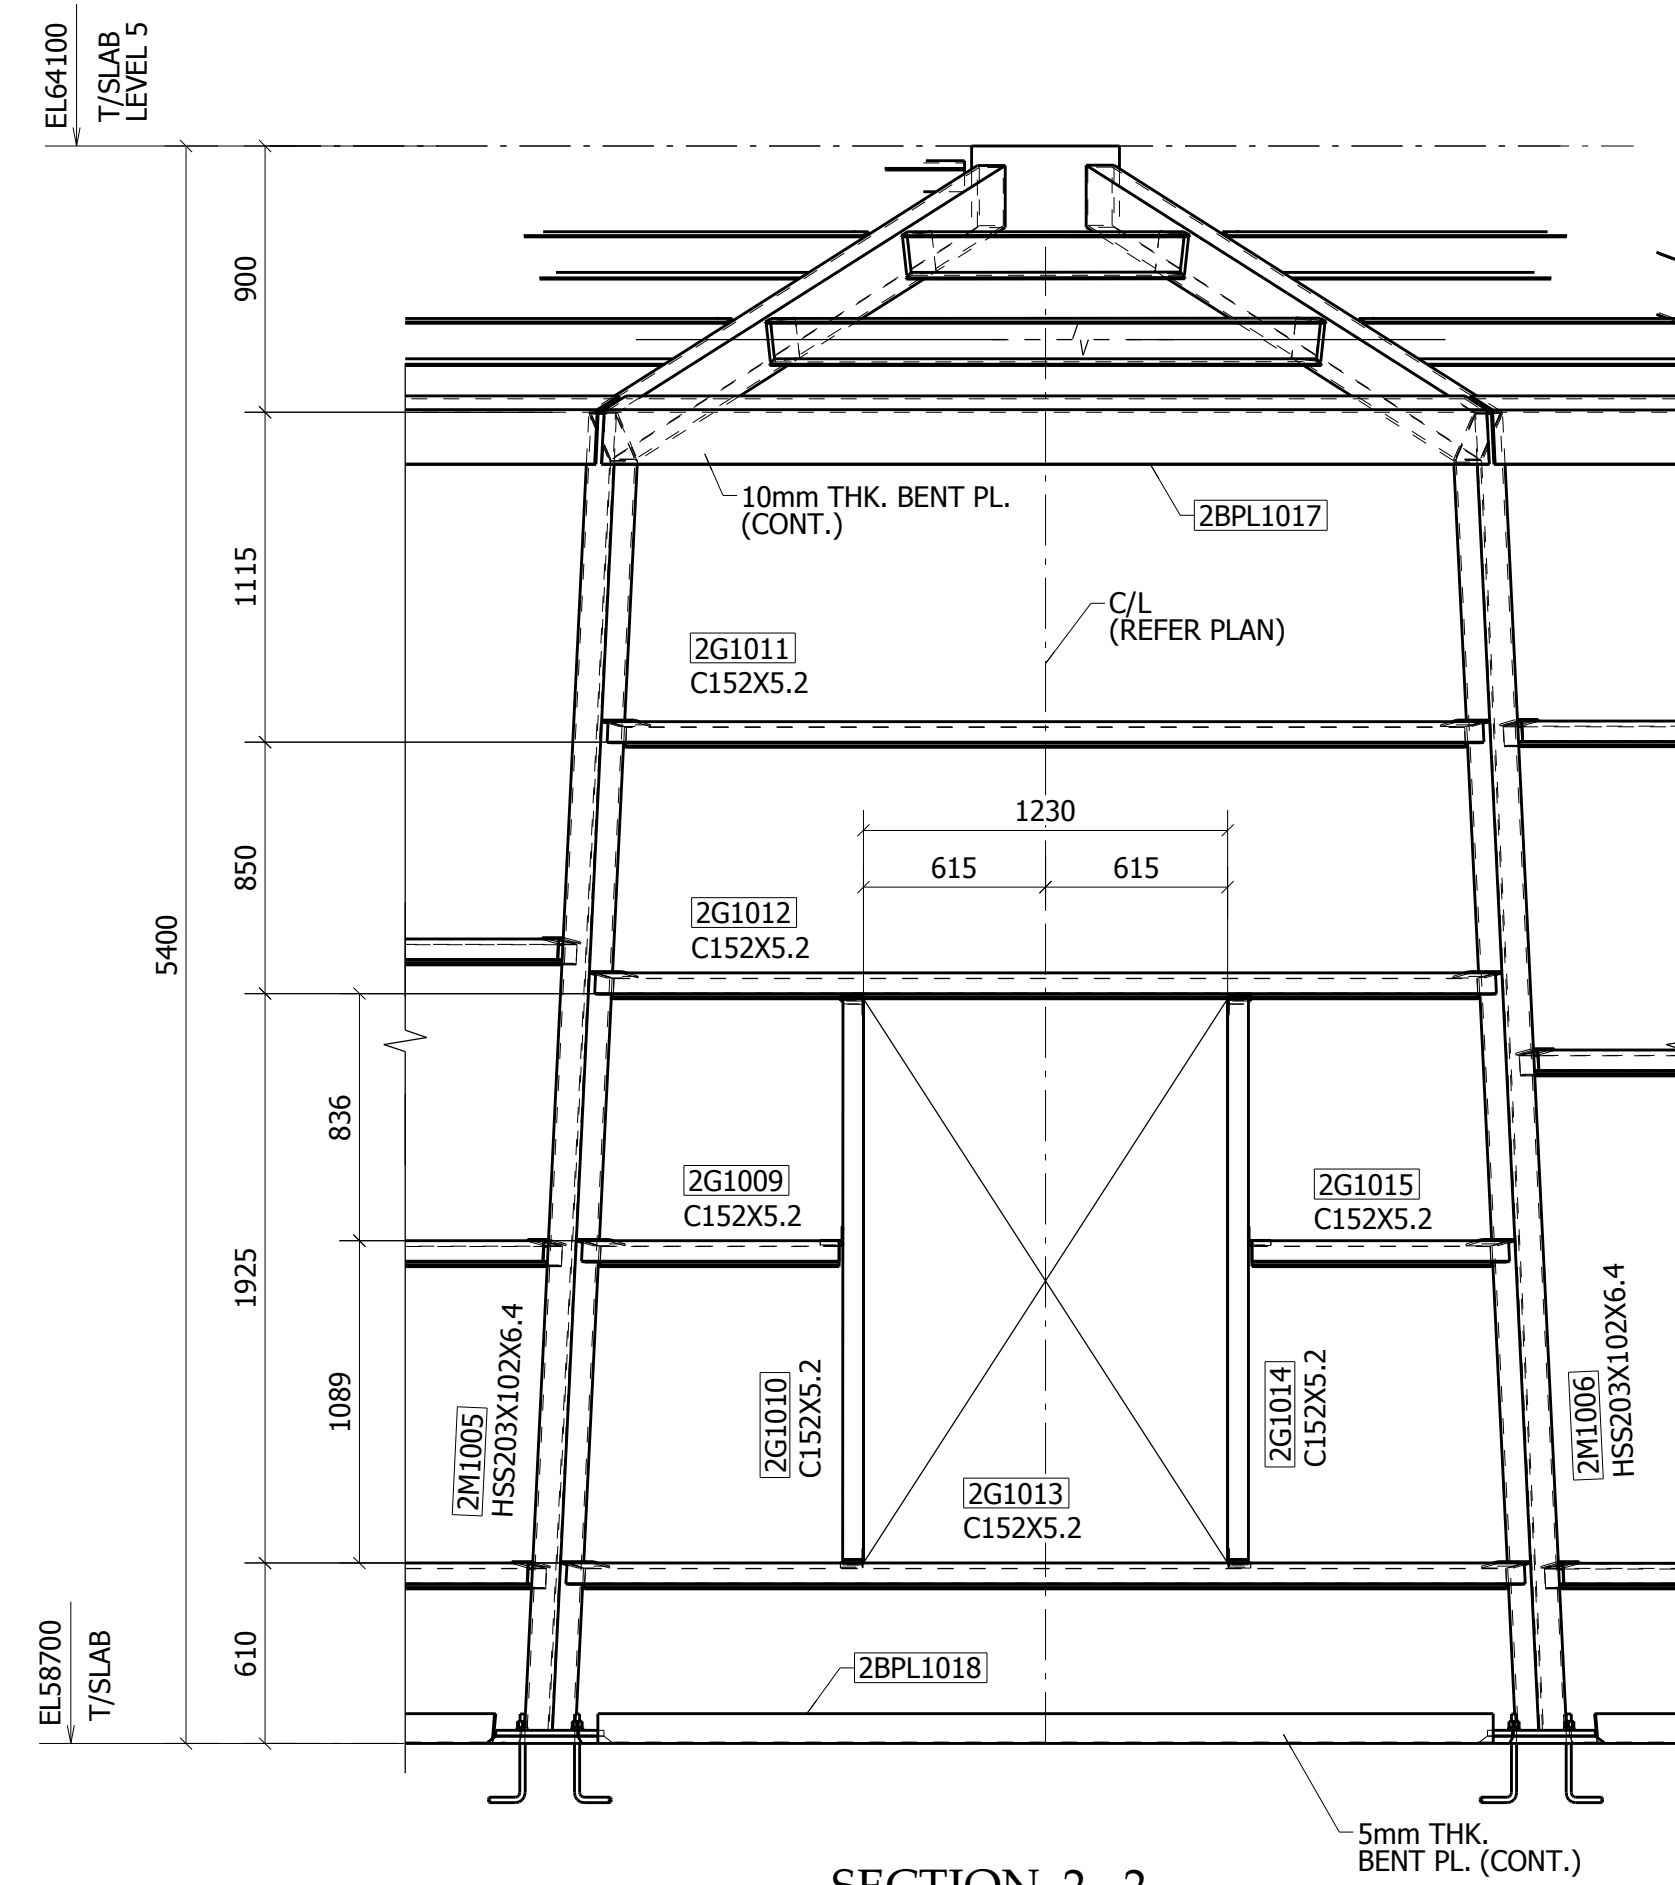

SECTION 2-2
E202
(REF.SEC: 2/S7.16)

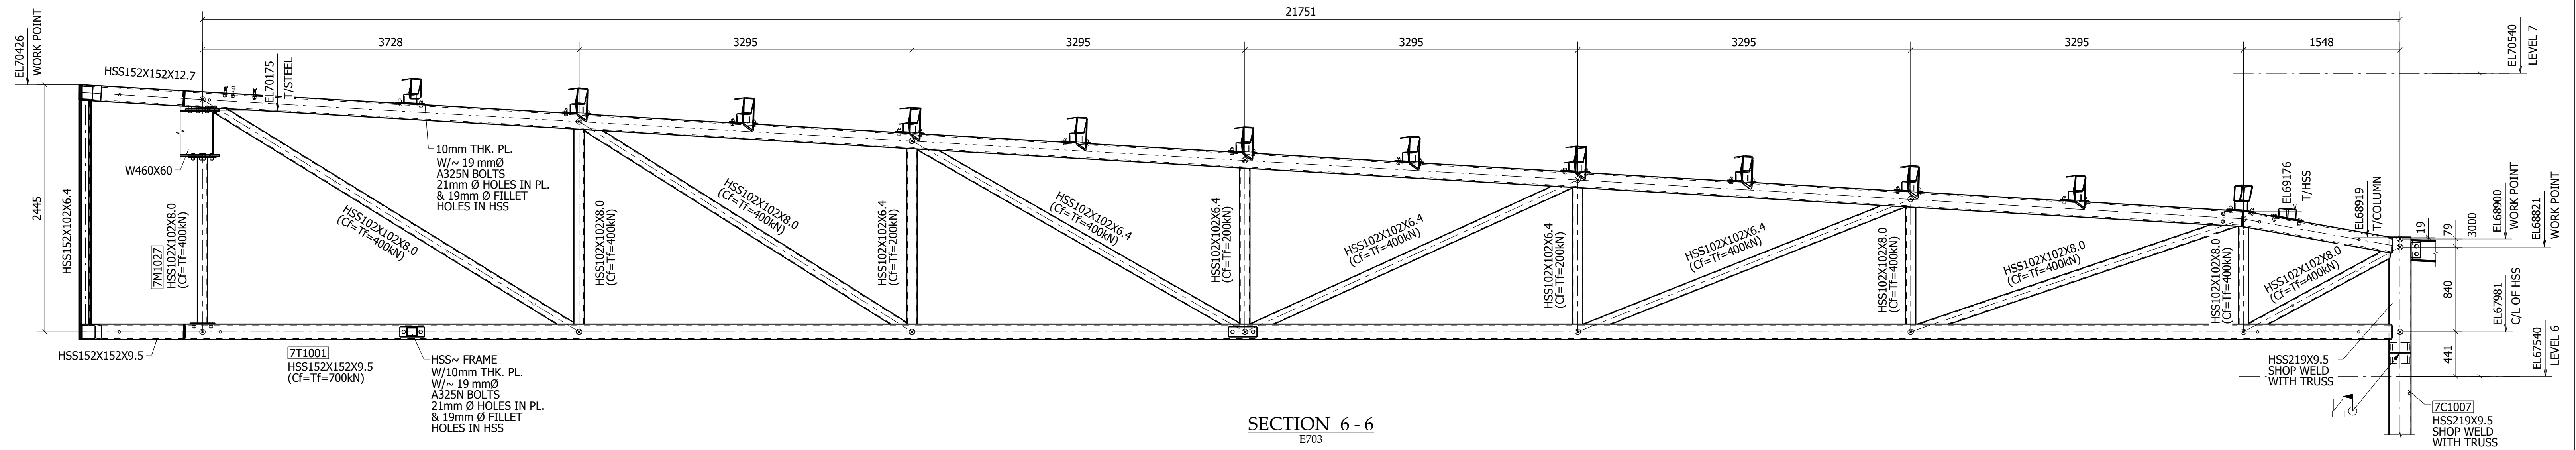


SECTION 6 - 6
E703
(REF.SEC: FRAME TYPE F-301/S7.31)
MEMBERS ARE HIDDEN FOR CLARITY

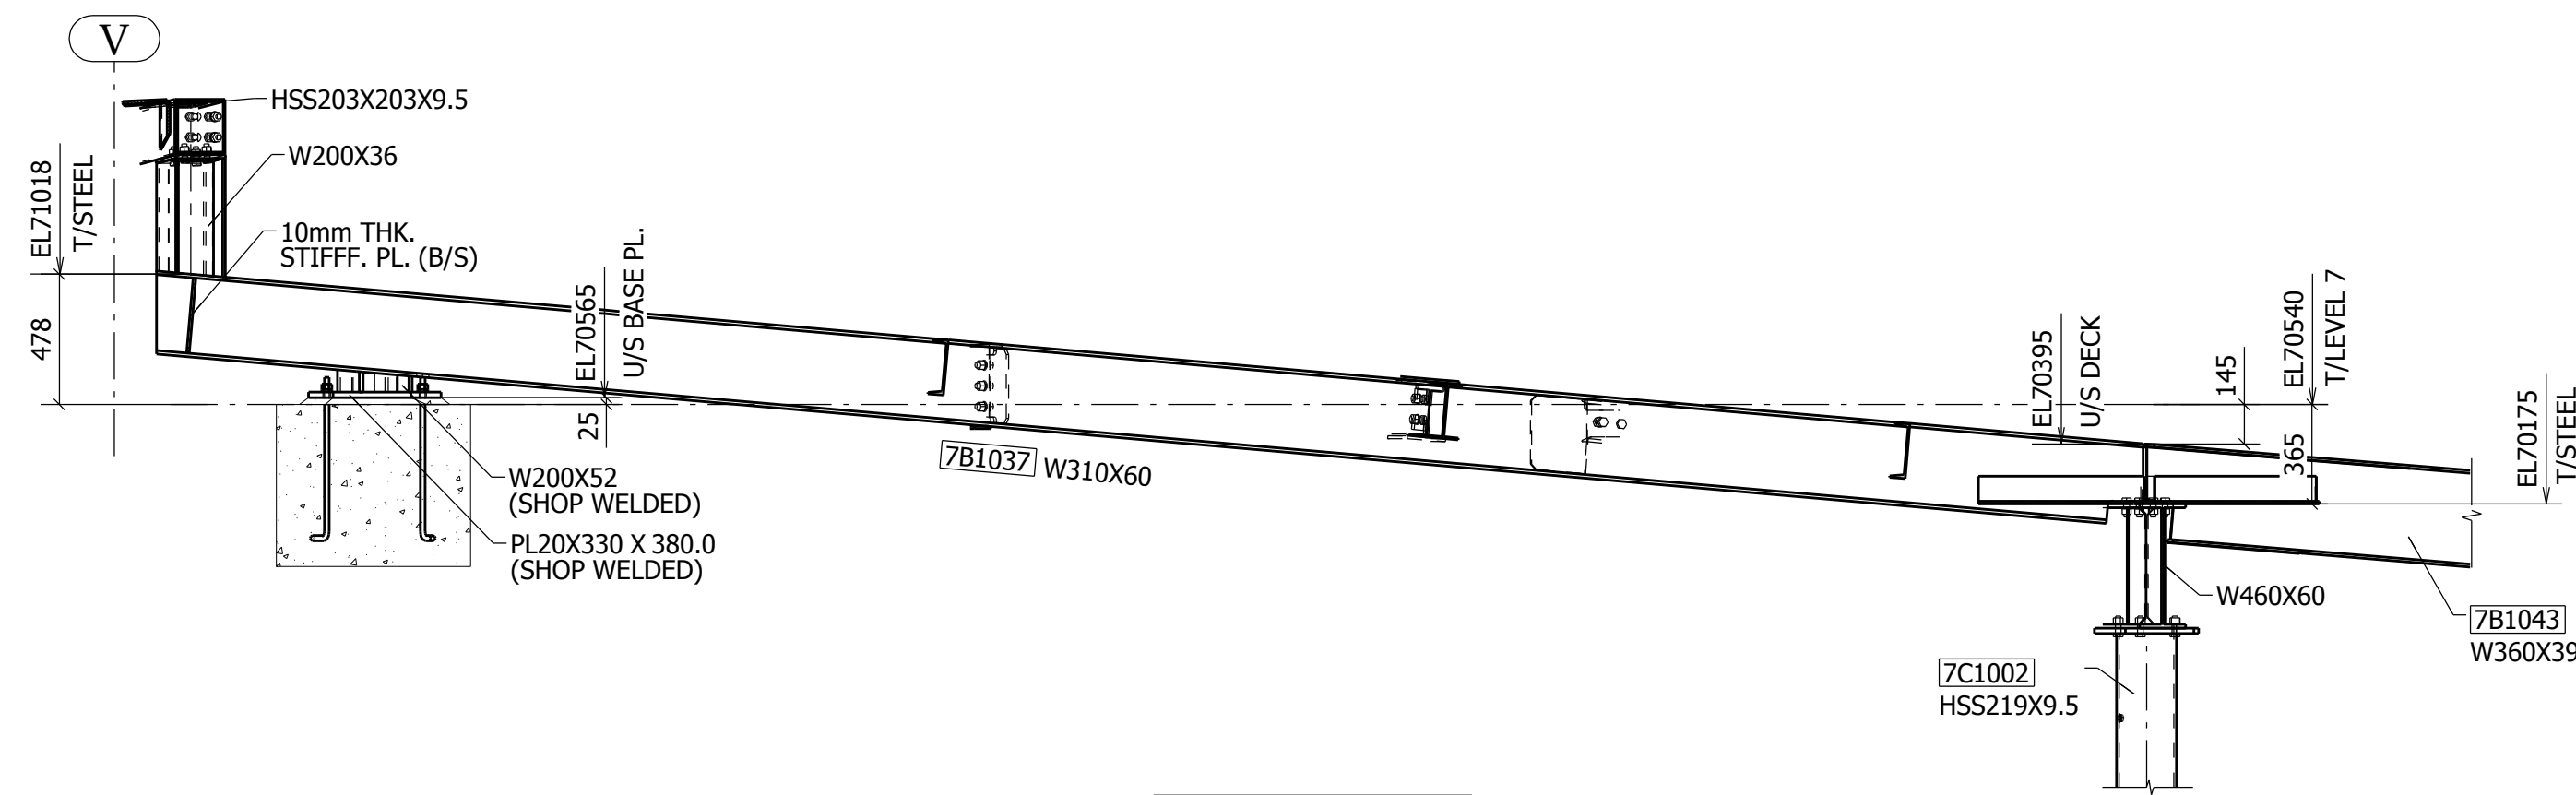


MEMBERS ARE HIDDEN FOR CLARITY


SECTION 7 - 7
E703

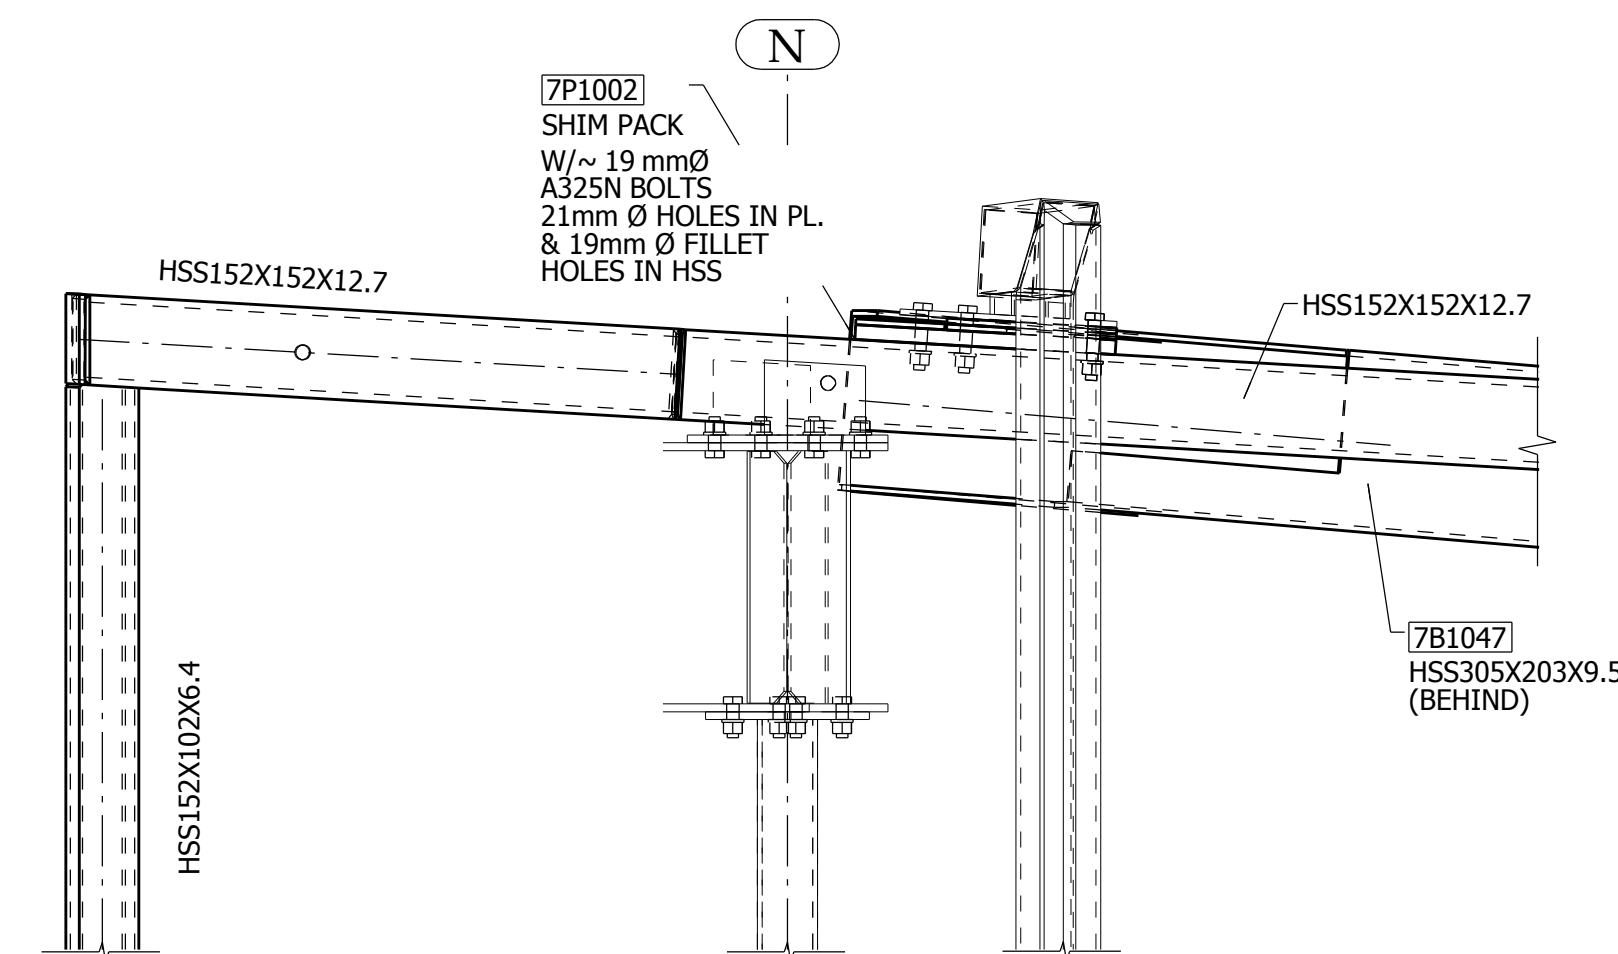


SECTION 8 - 8
E703

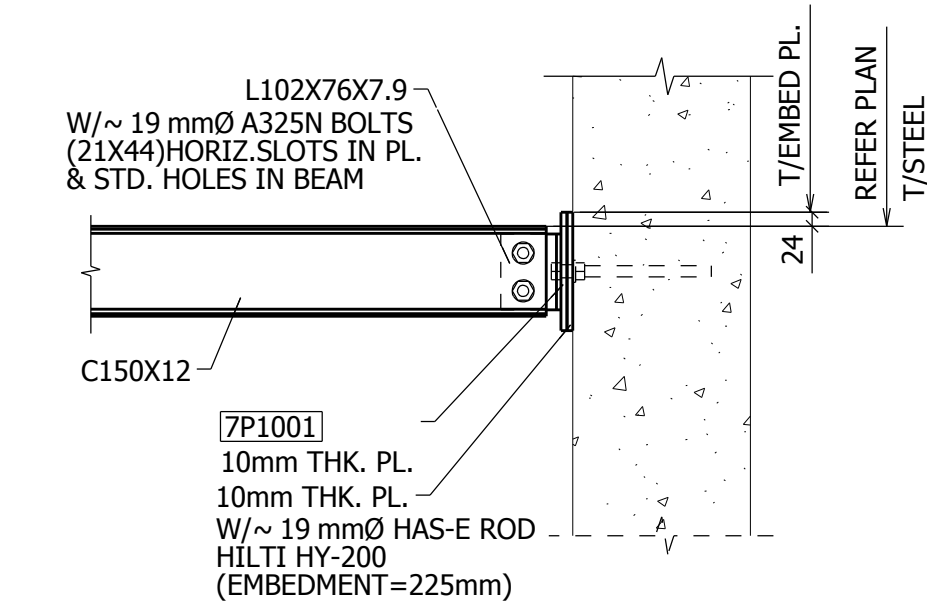


SECTION 9 - 9
E703

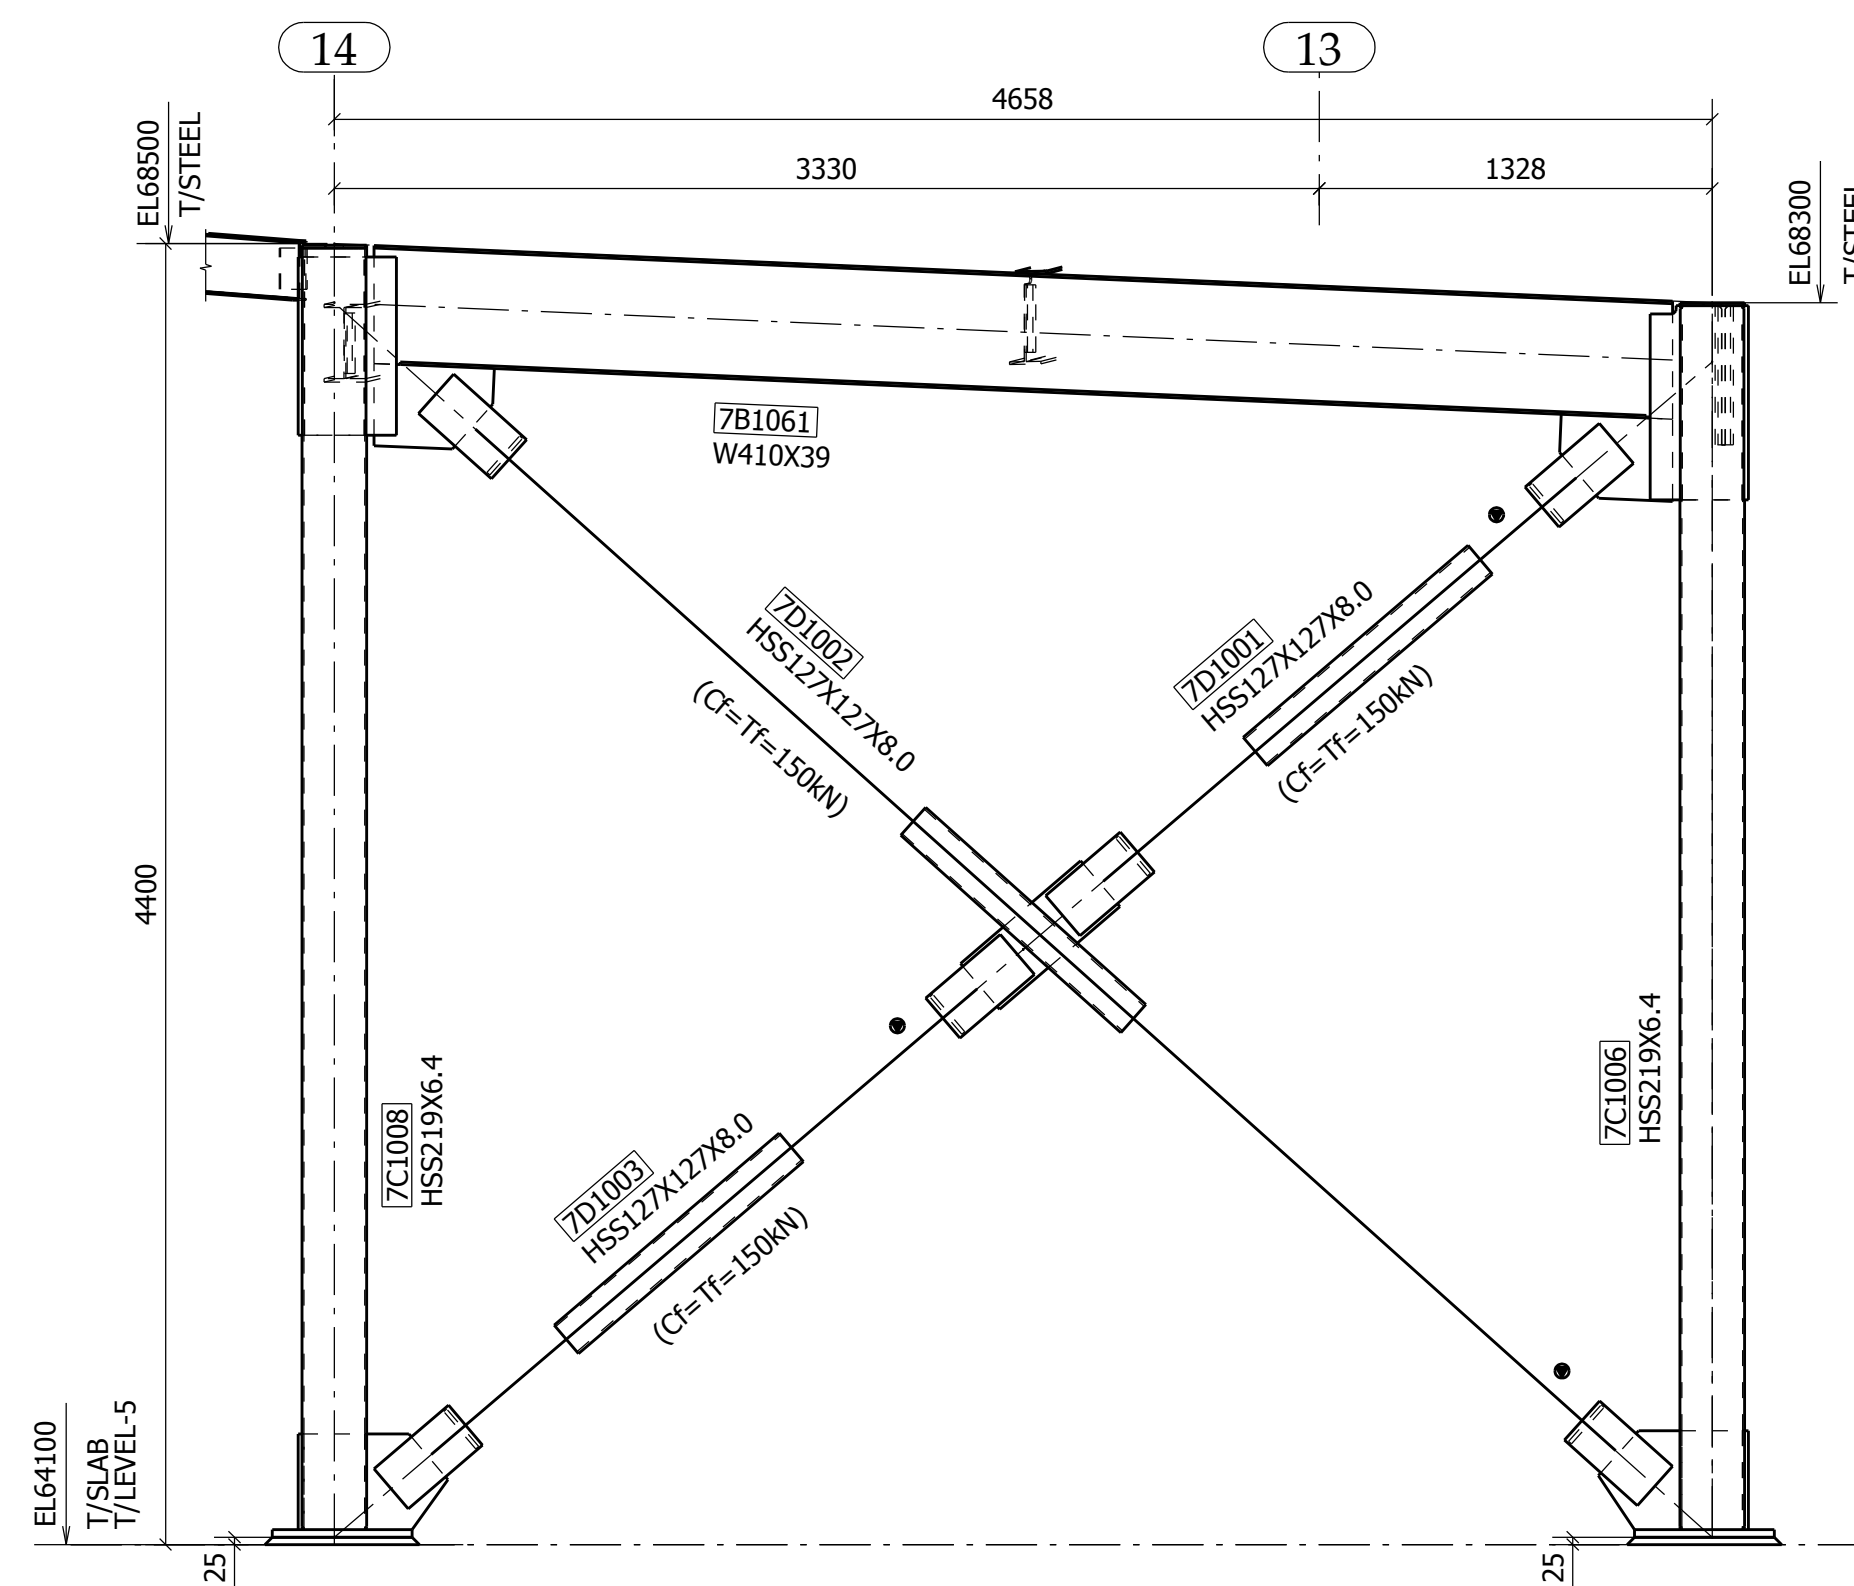


SECTION 10 - 10
E703
(REF.SEC: 5/S7.16)

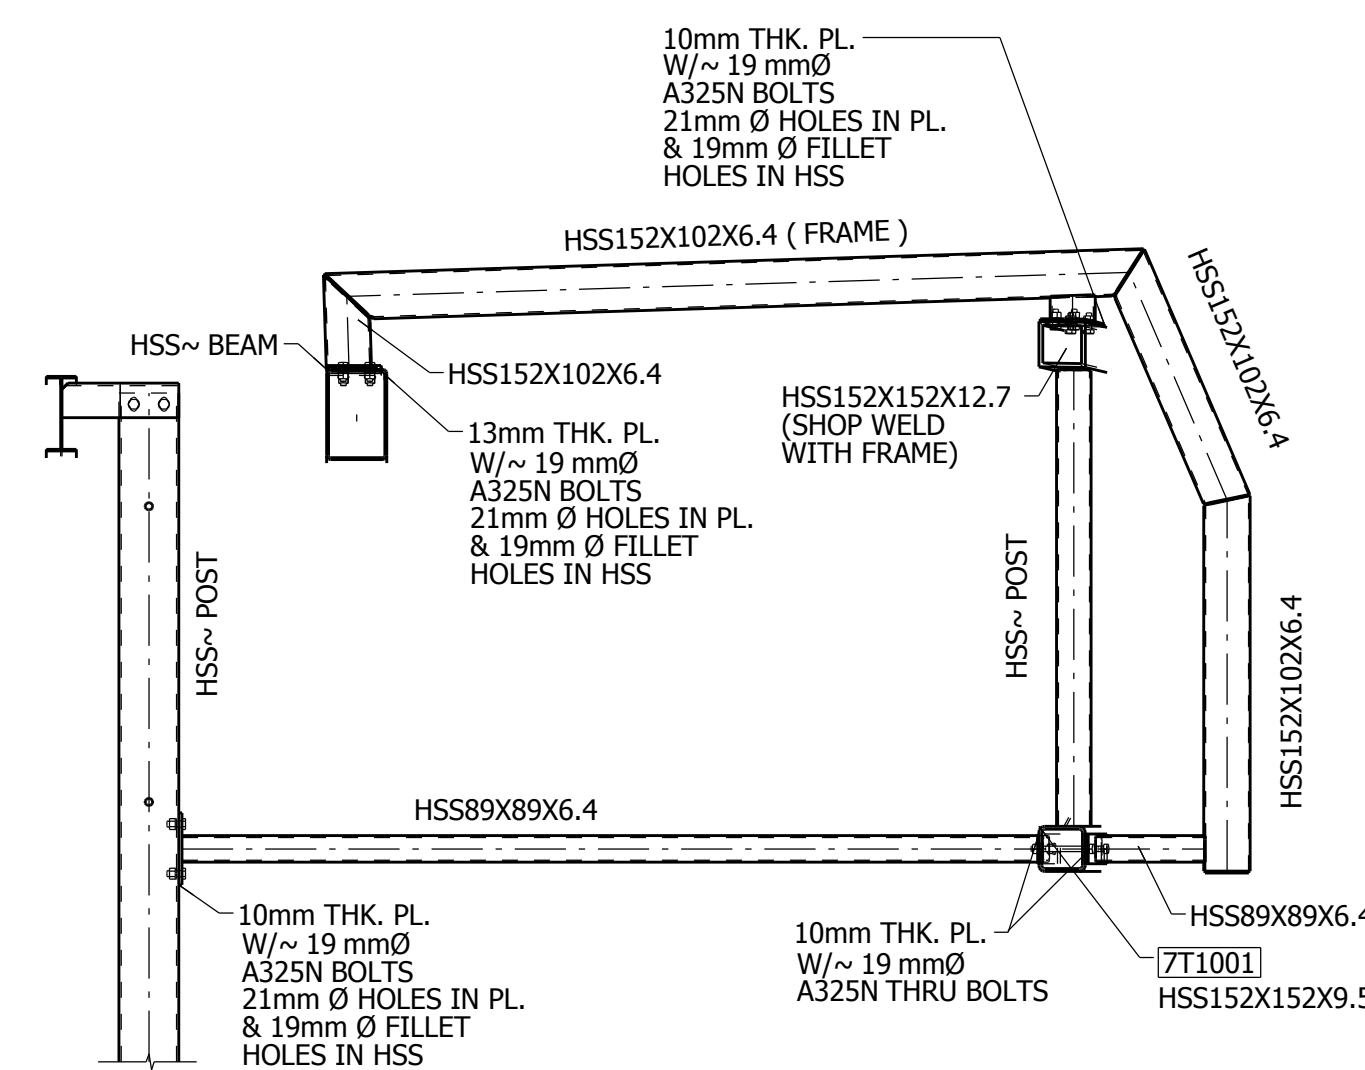

SECTION 11 - 11
E703
TYPICAL FRAME DETAIL
FRAMES ARE FIXED AS PER IFC MODEL

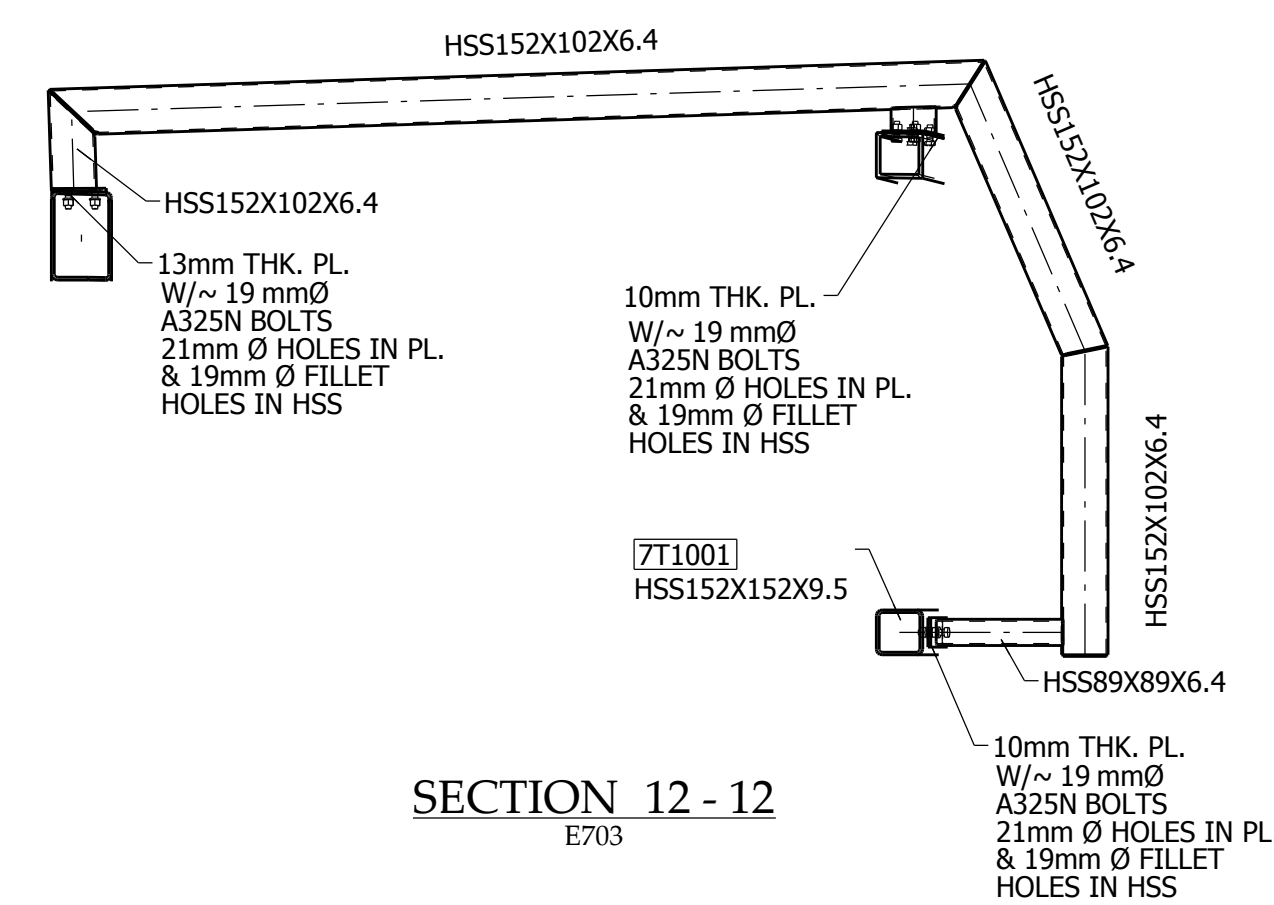

SECTION 12 - 12
E703
TYPICAL FRAME DETAIL
FRAMES ARE FIXED AS PER IFC MODEL

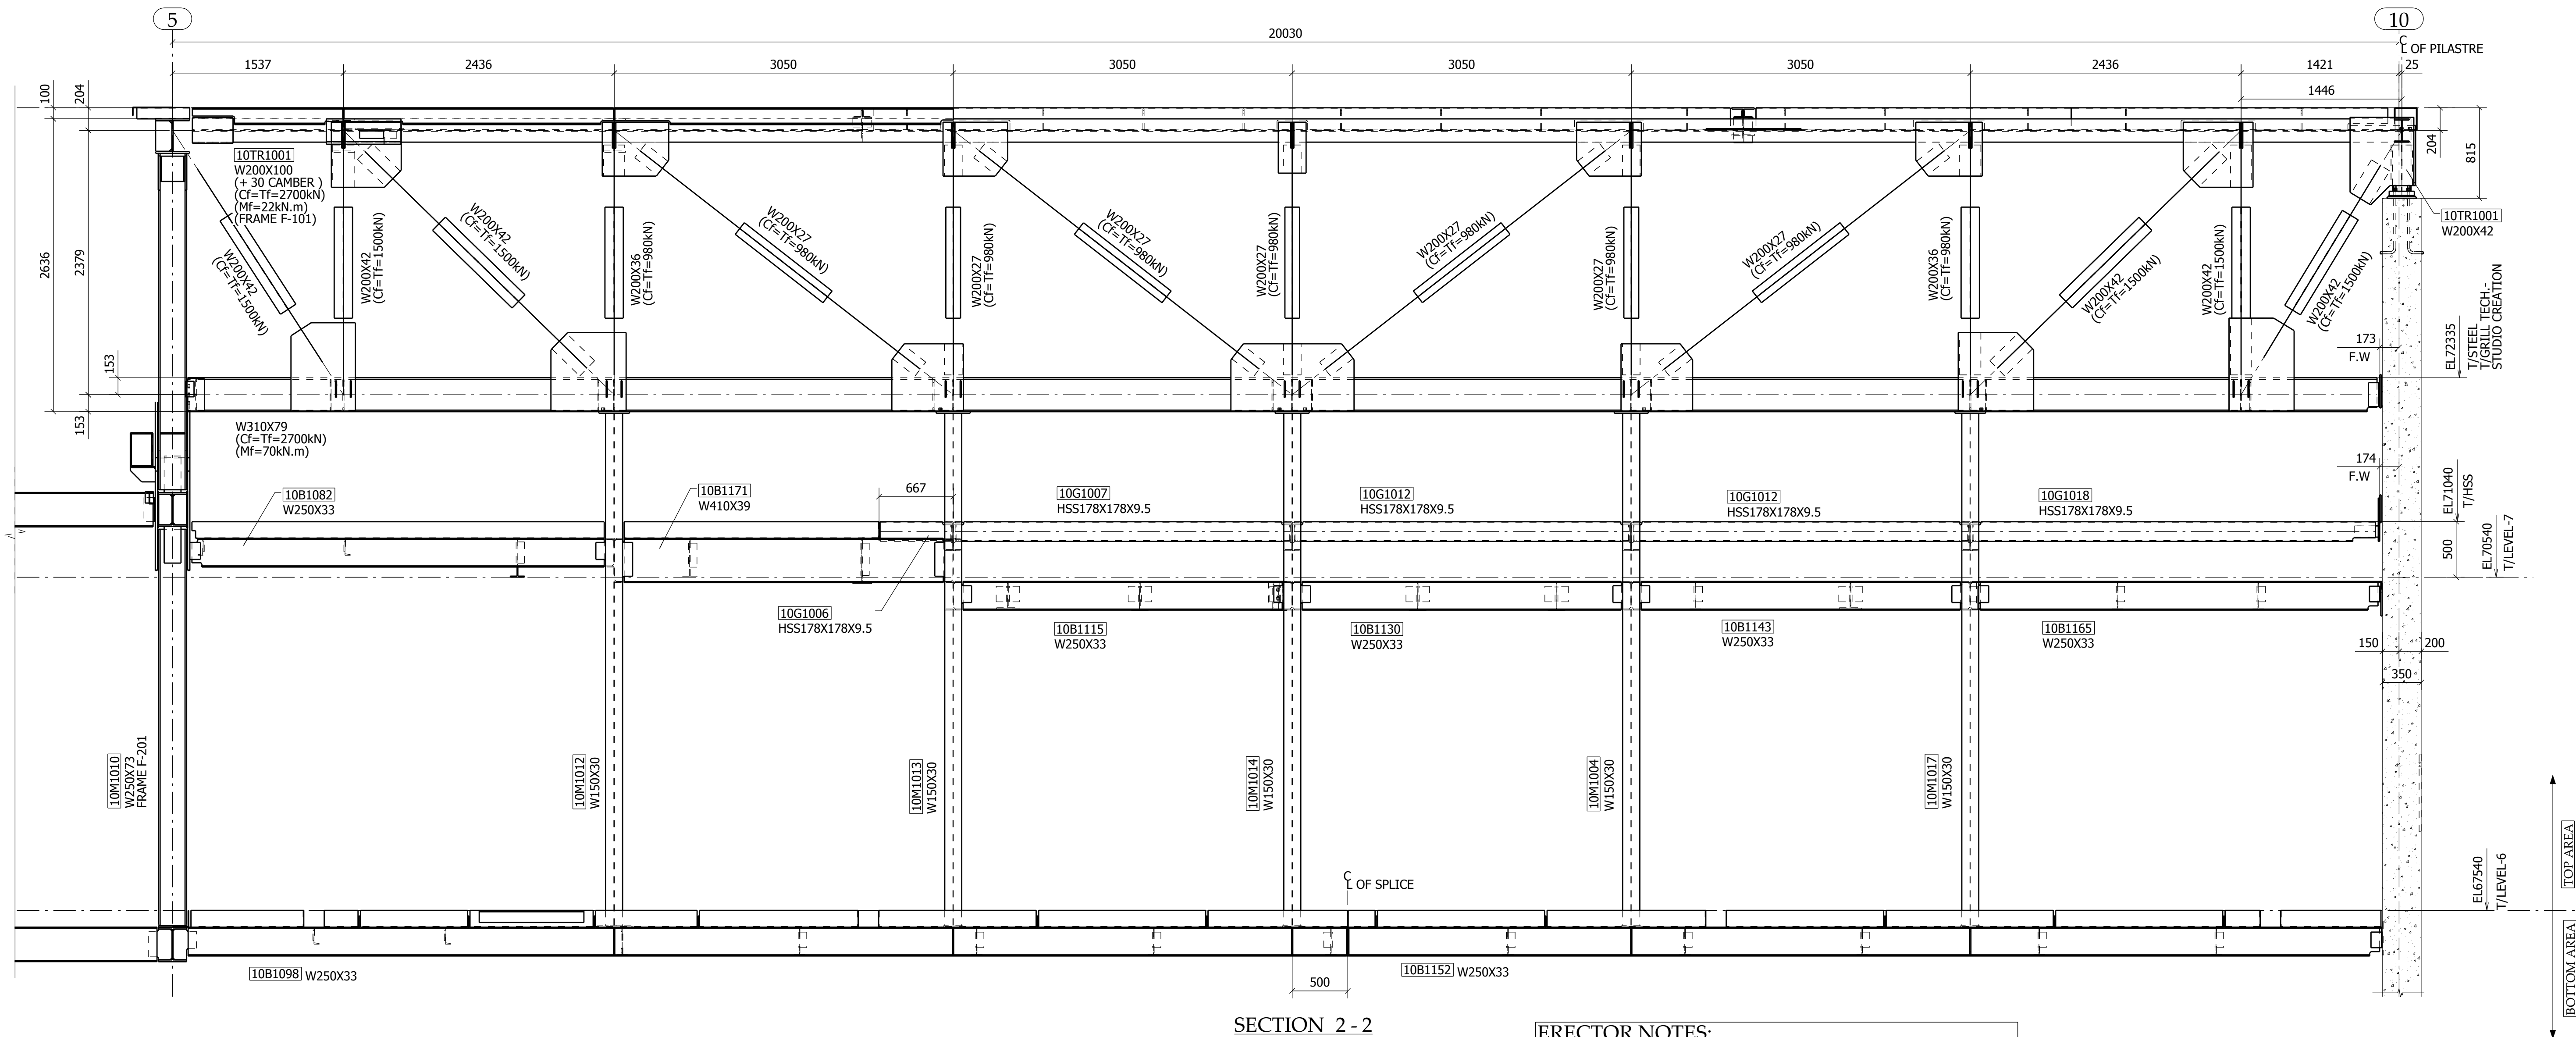


SECTION 2 - 2

E1002, E1003

(REF.SEC: 1/S7.12 & FRAME TYPE F-101/S7.31)

ERECTOR NOTES:


- PROVIDE LATERAL SUPPORT FOR TRUSSES F201 AND F101 DURING ERECTION.

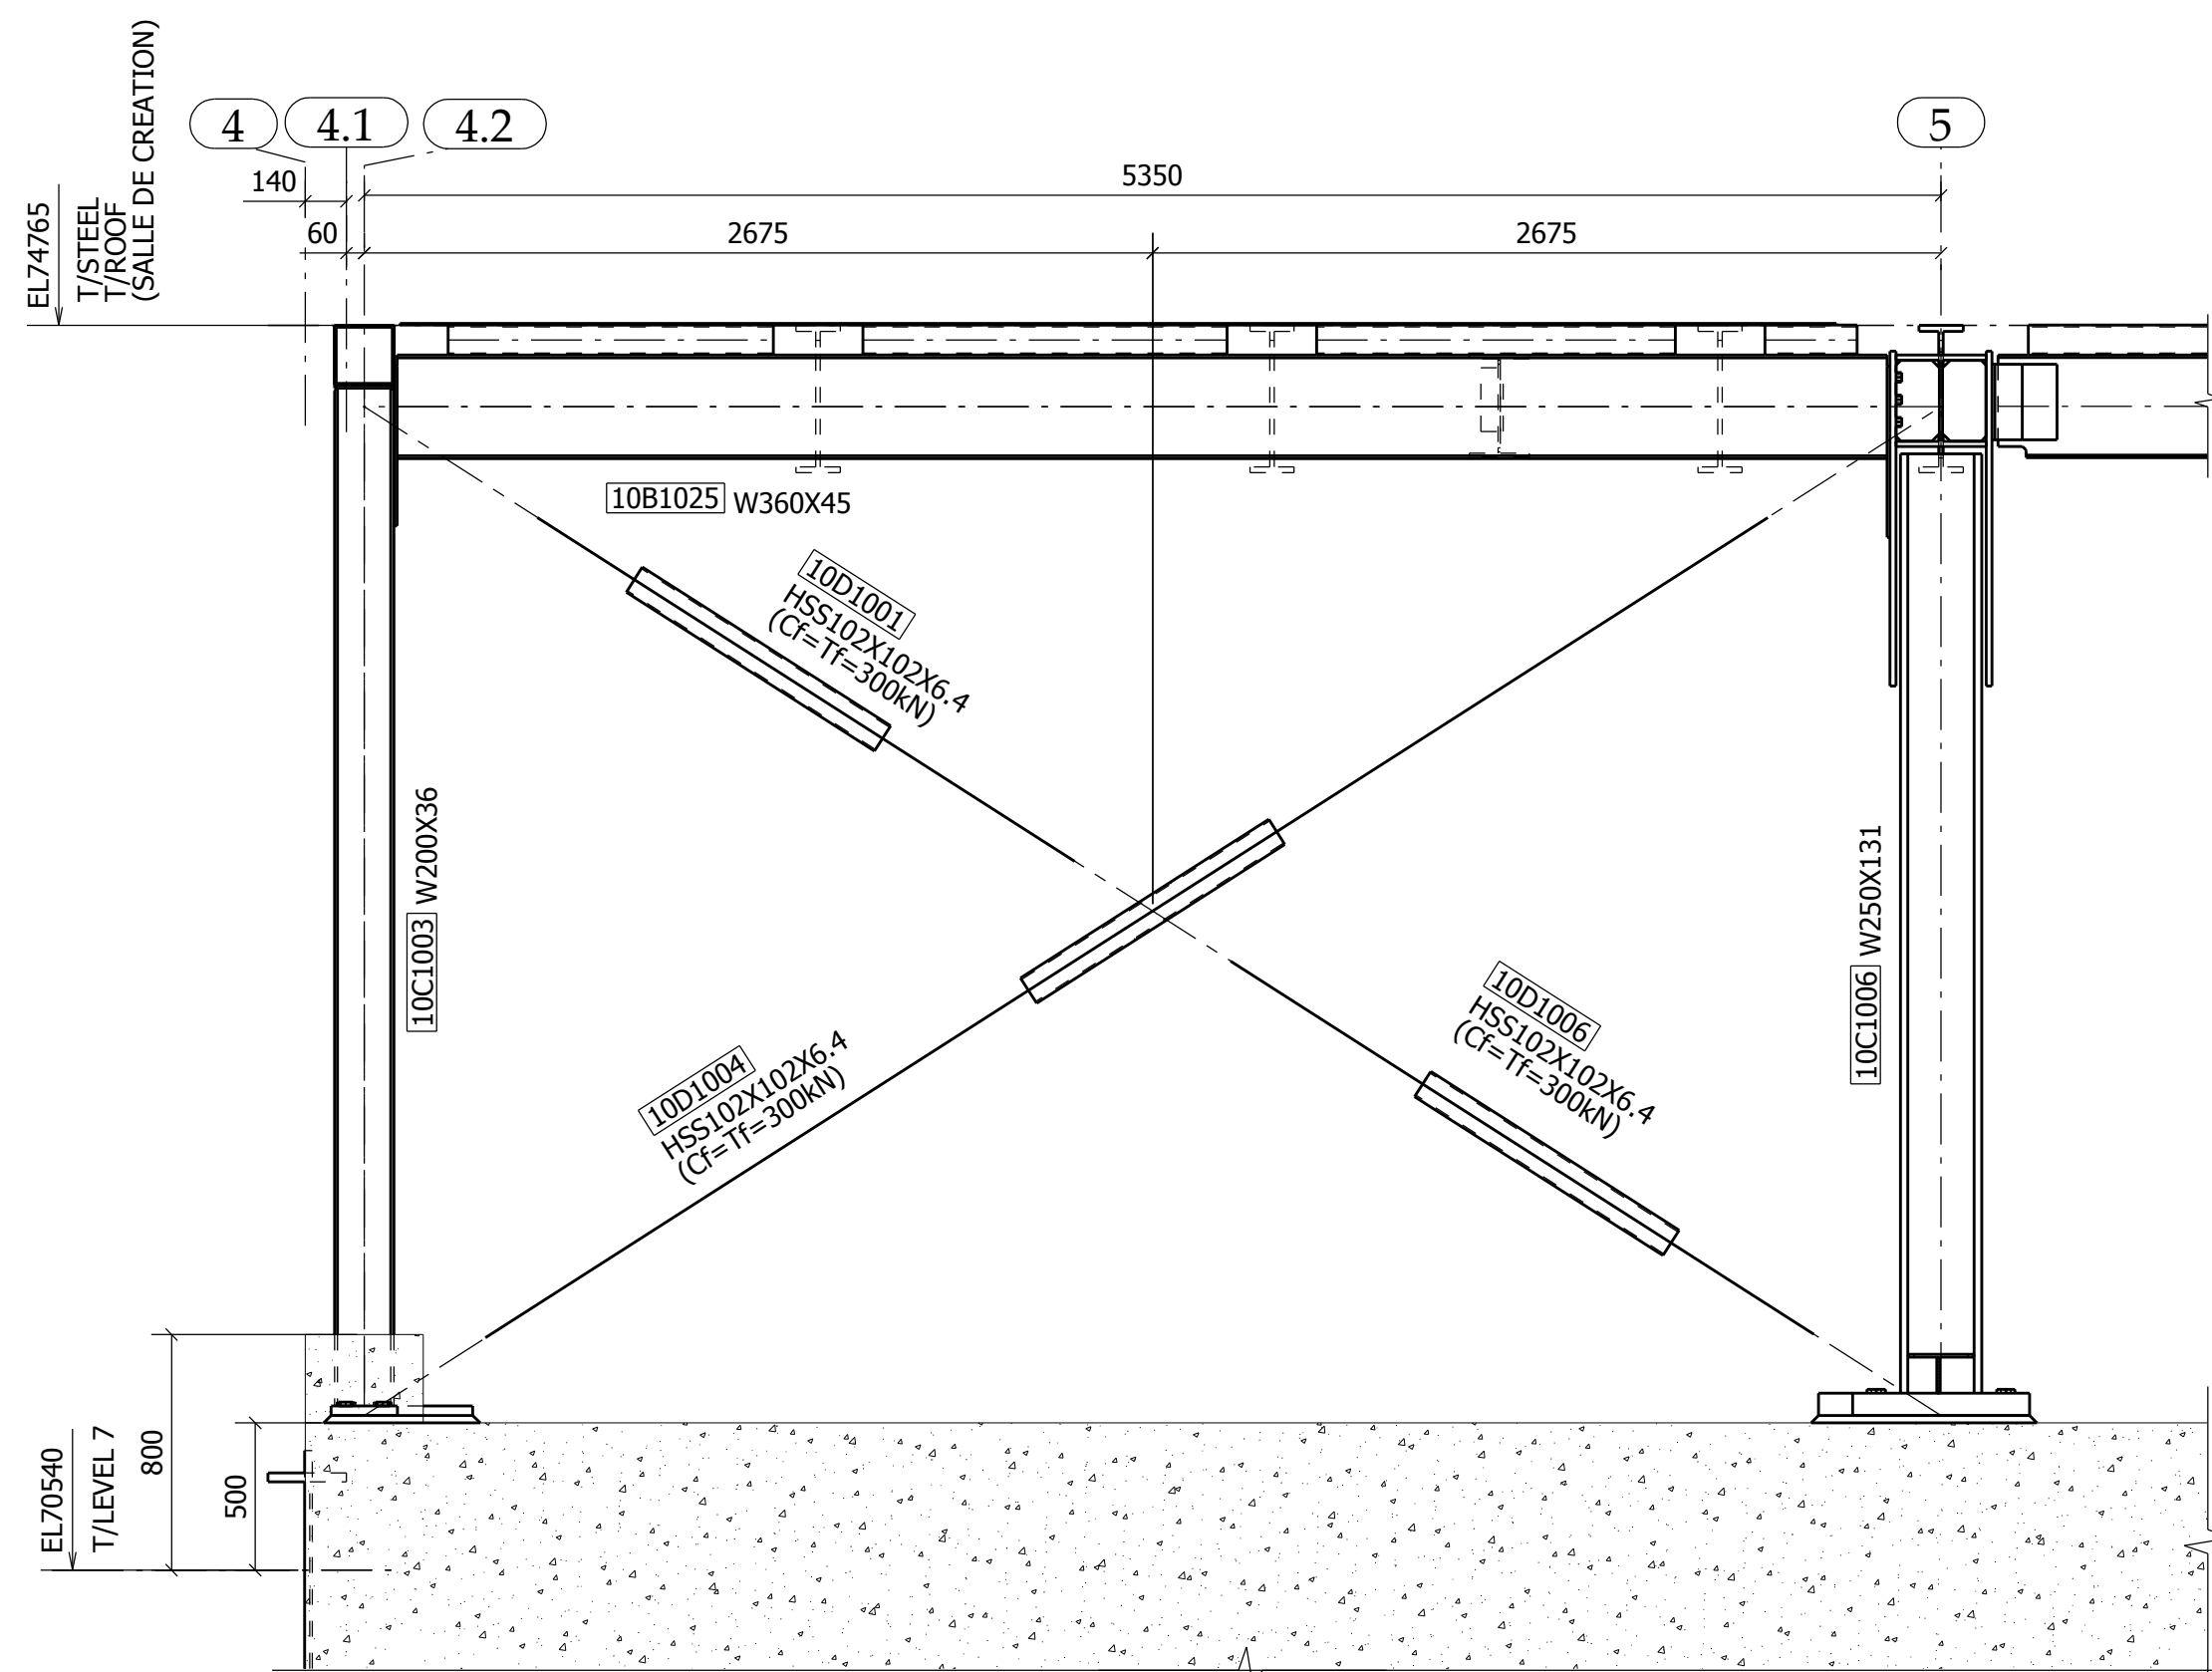

SECTION 3 - 3

E1003


(REF.SEC: 3/S7.12)

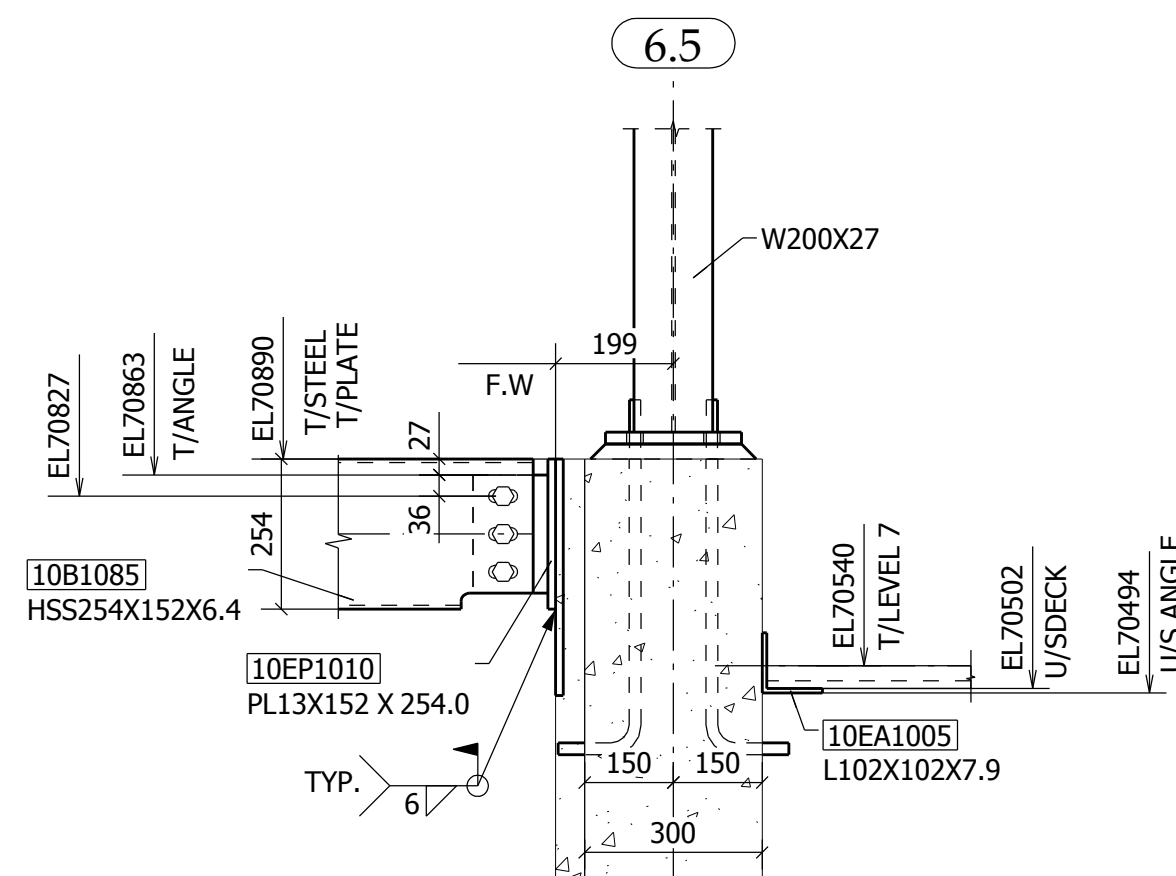

SECTION 4 - 4

E1003

(REF.SEC: 3/S6.34)

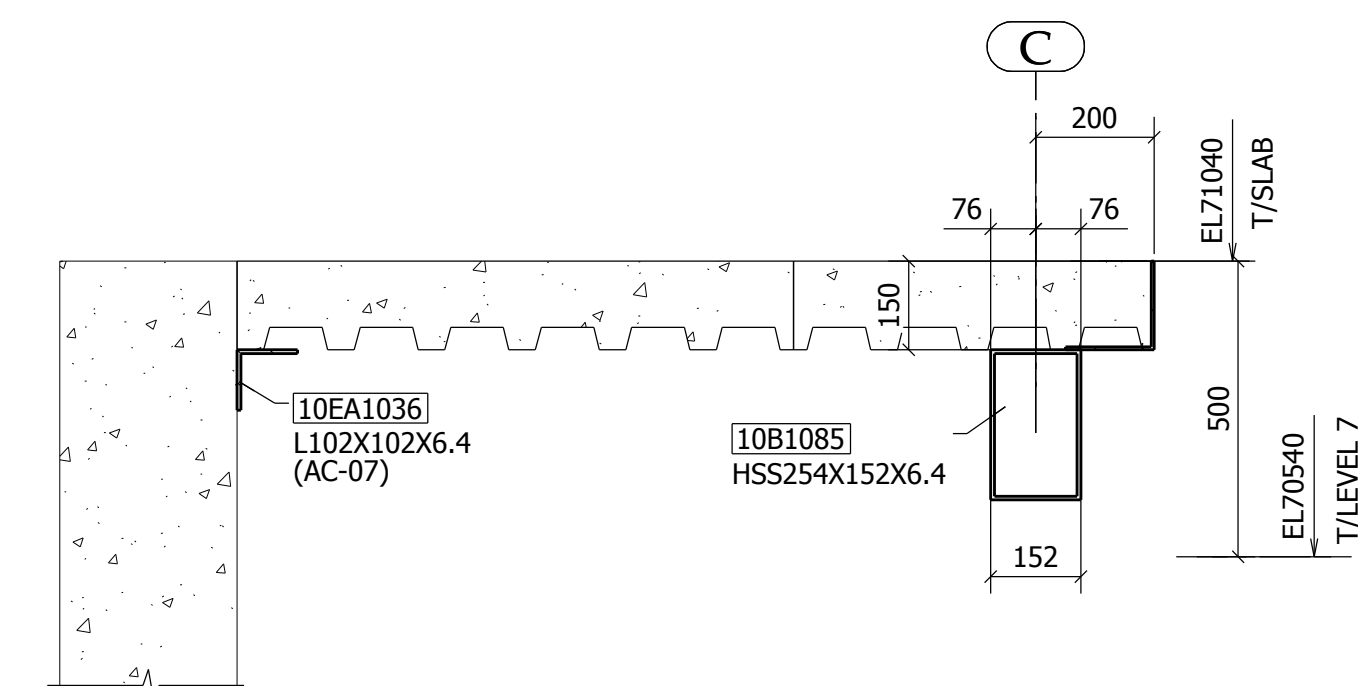

SECTION 5 - 5

E1003

(REF.SEC: 6/S6.34)

NOTES:

1. F.W - -INDICATES FACE OF WALL

SECTION 23 - 23
E1005
(REF.SEC: 6/S7.50)



FRAME TYPE F-104

SECTION 1 - 1

E1202

(REF.SEC: S7.31)

[illegible]

FRAME TYPE F-103



SECTION 2 - 2

E1202




(REF.SEC: S7.31)




ERECTOR NOTES:

- PROVIDE LATERAL SUPPORT FOR TRUSS
12TR1001 DURING ERECTION.

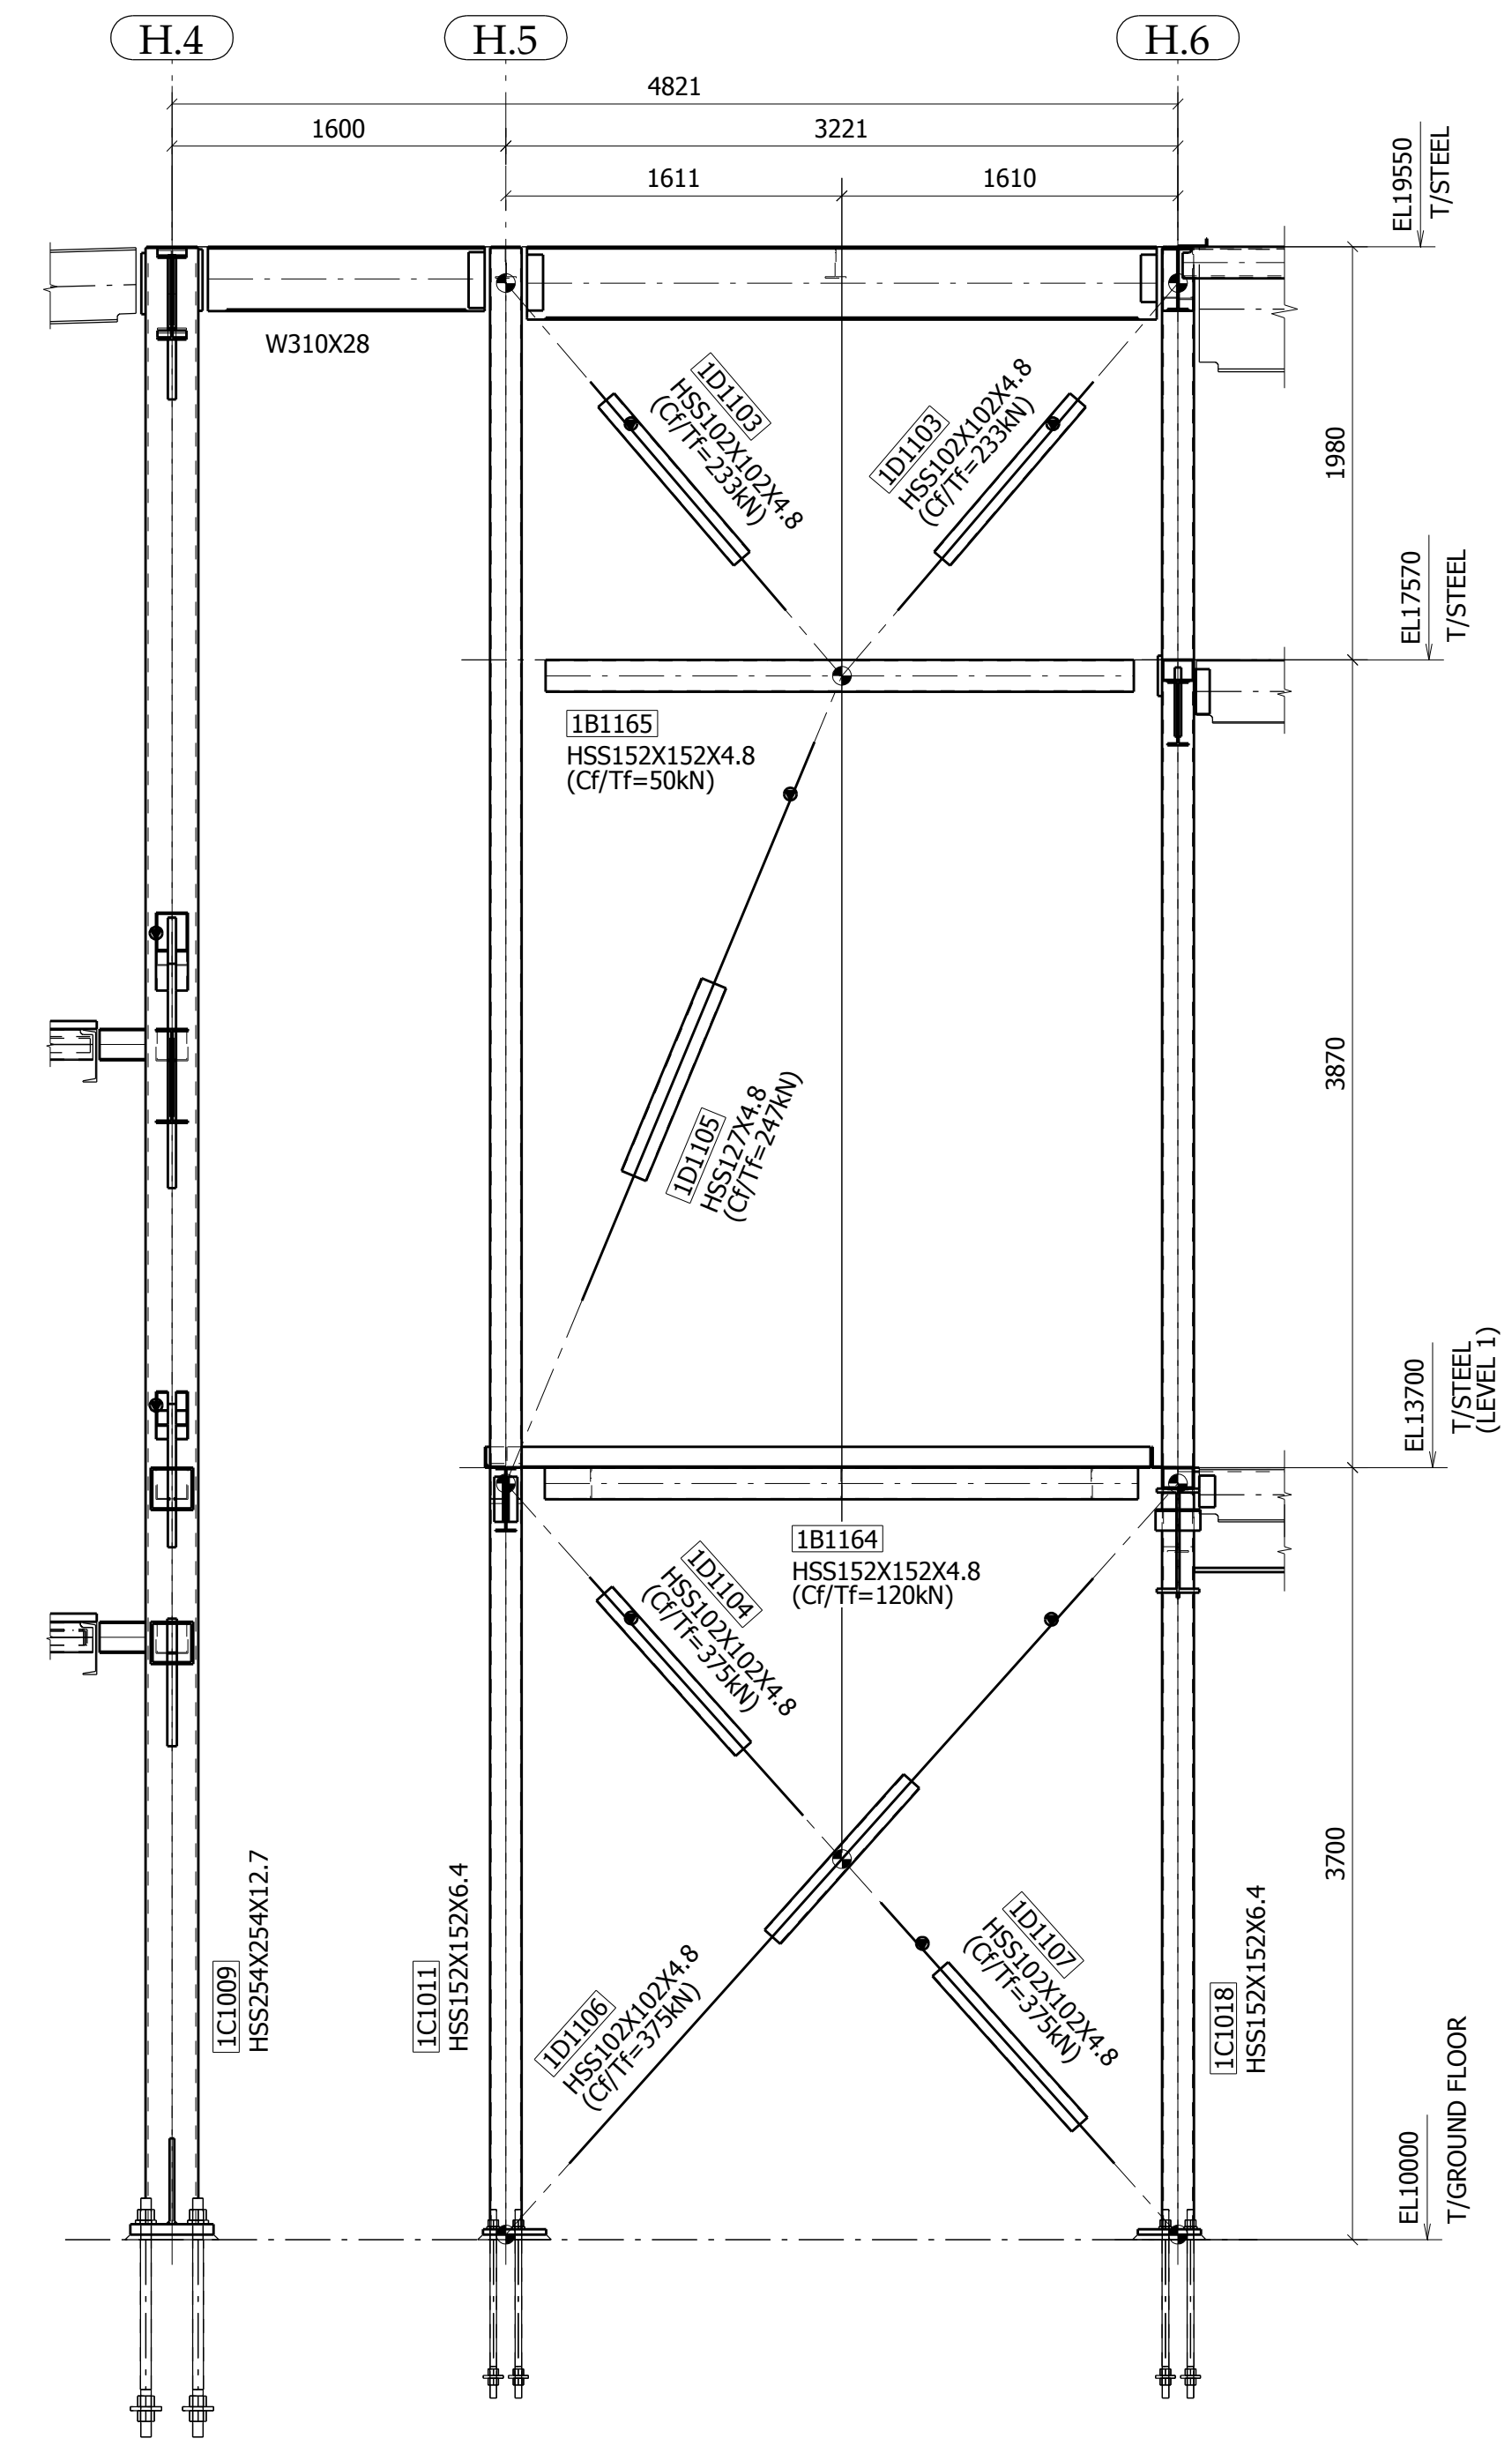
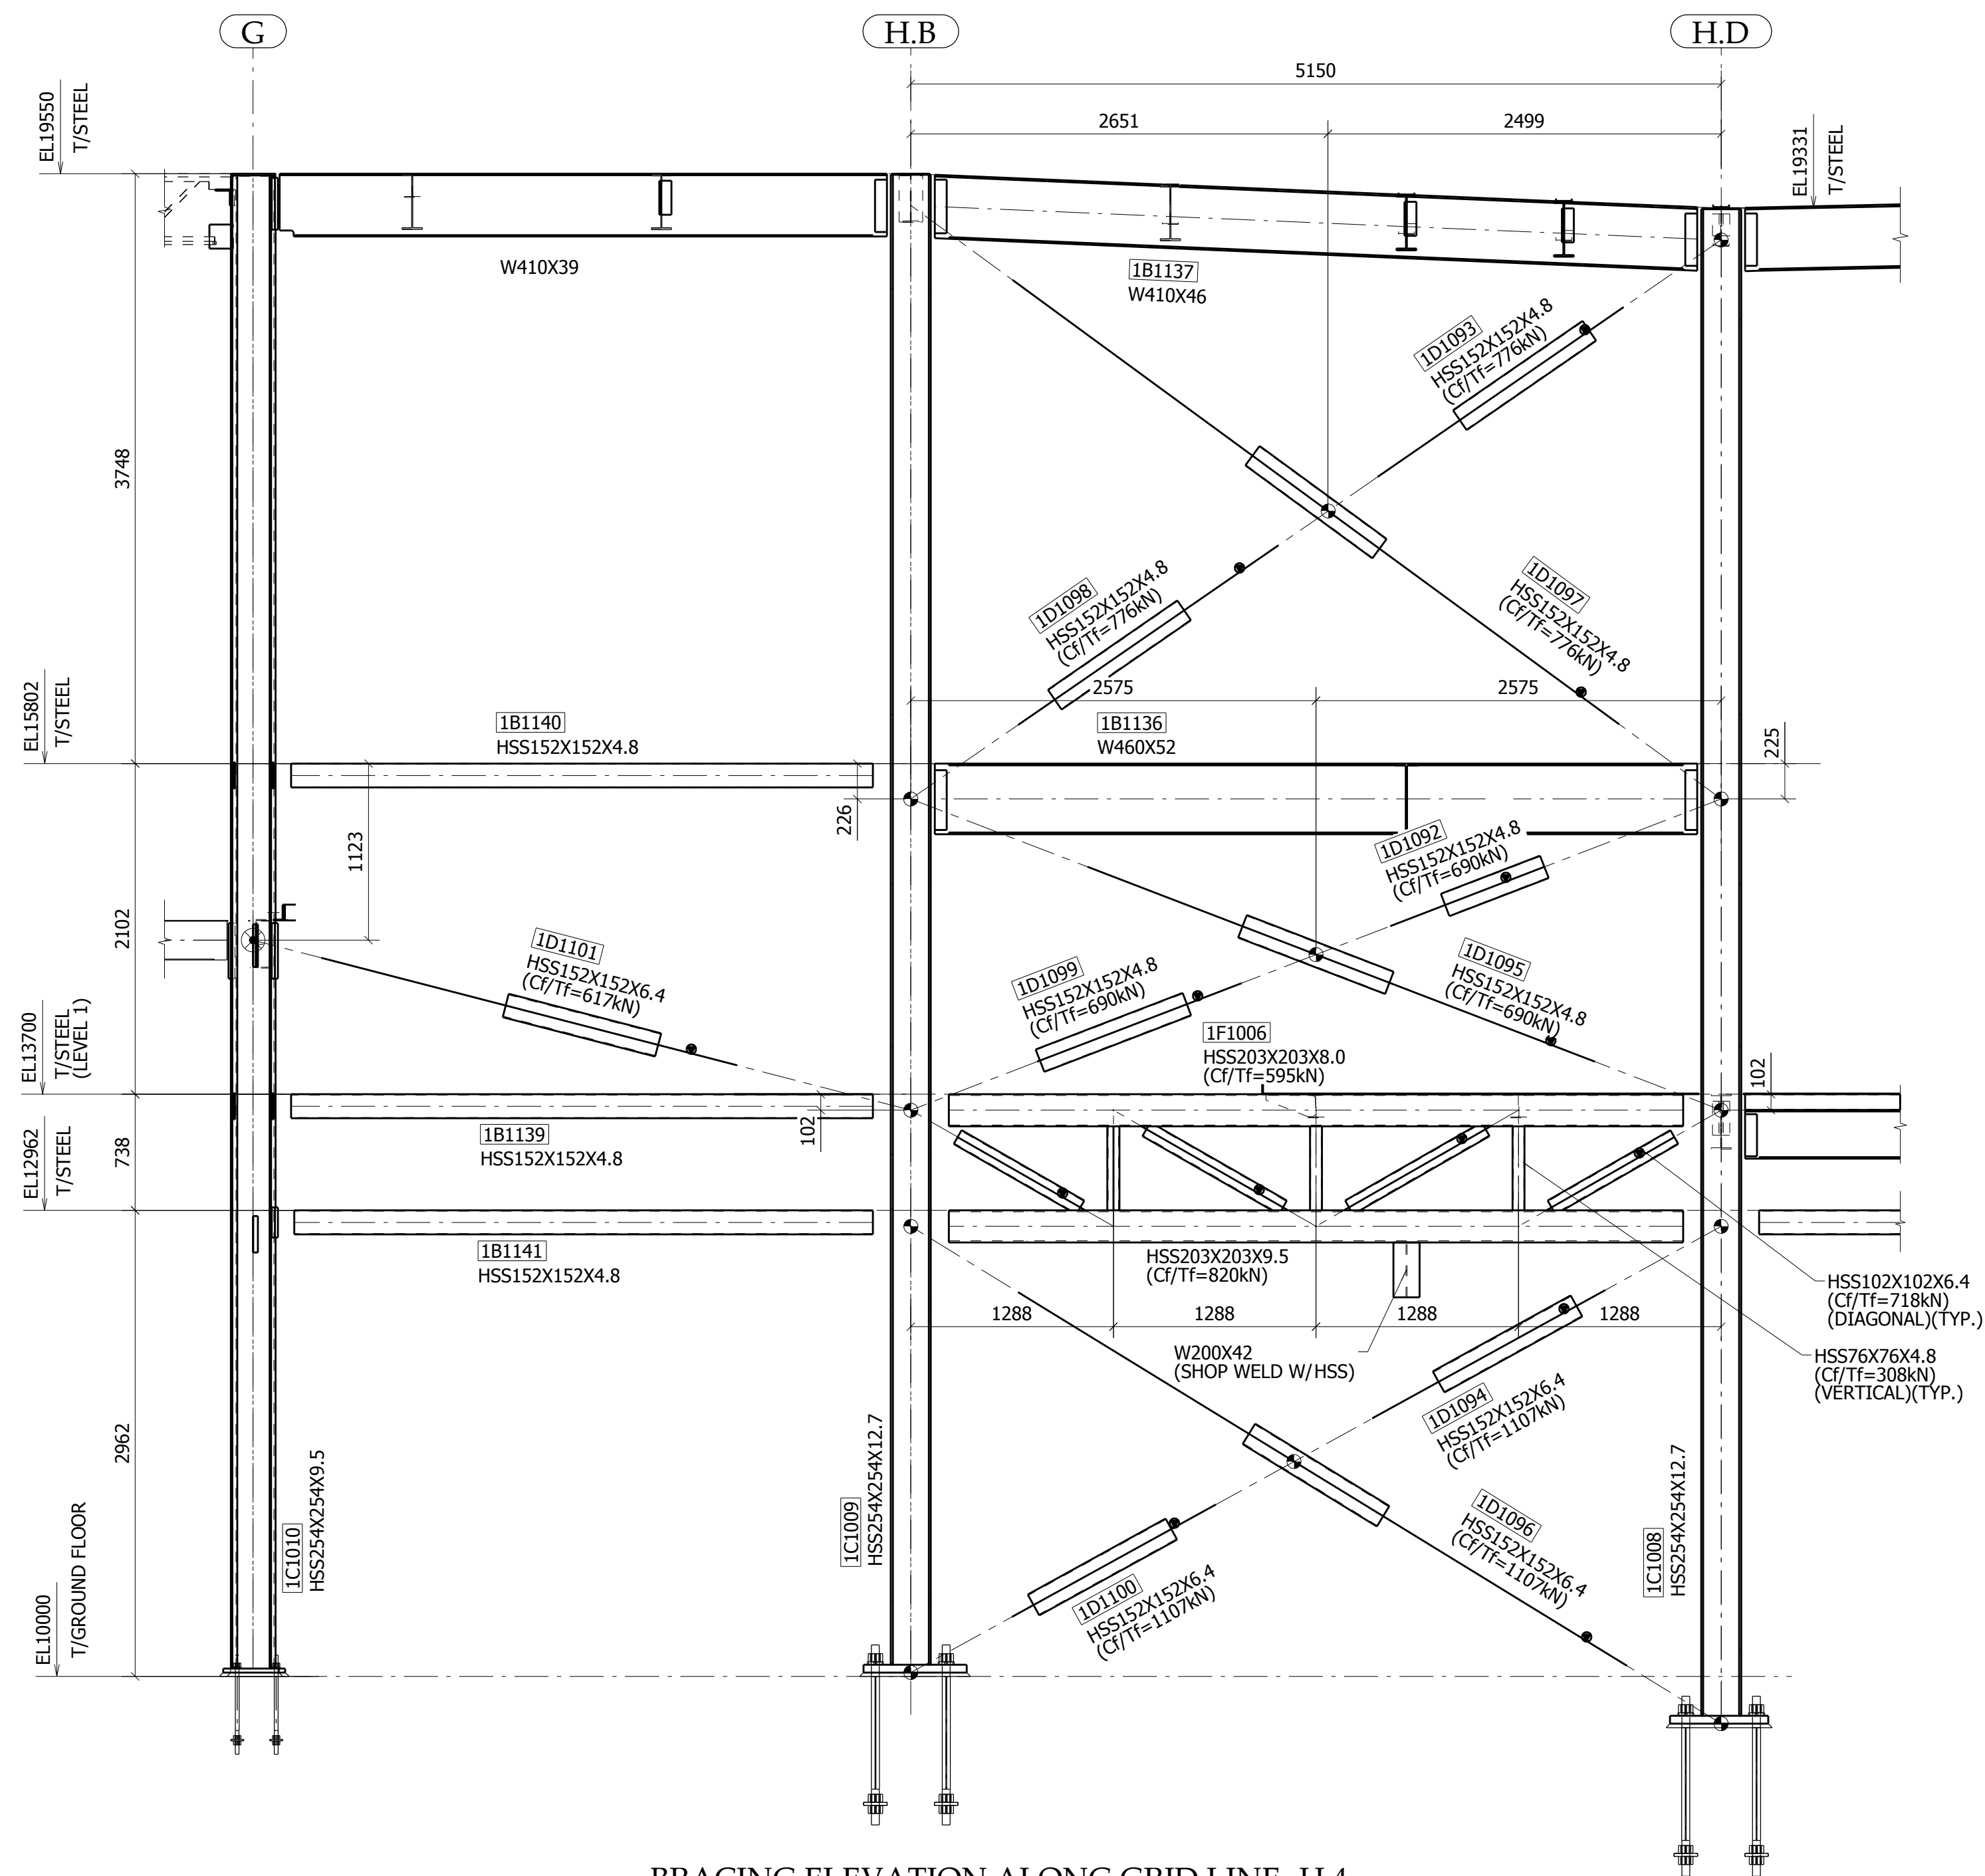





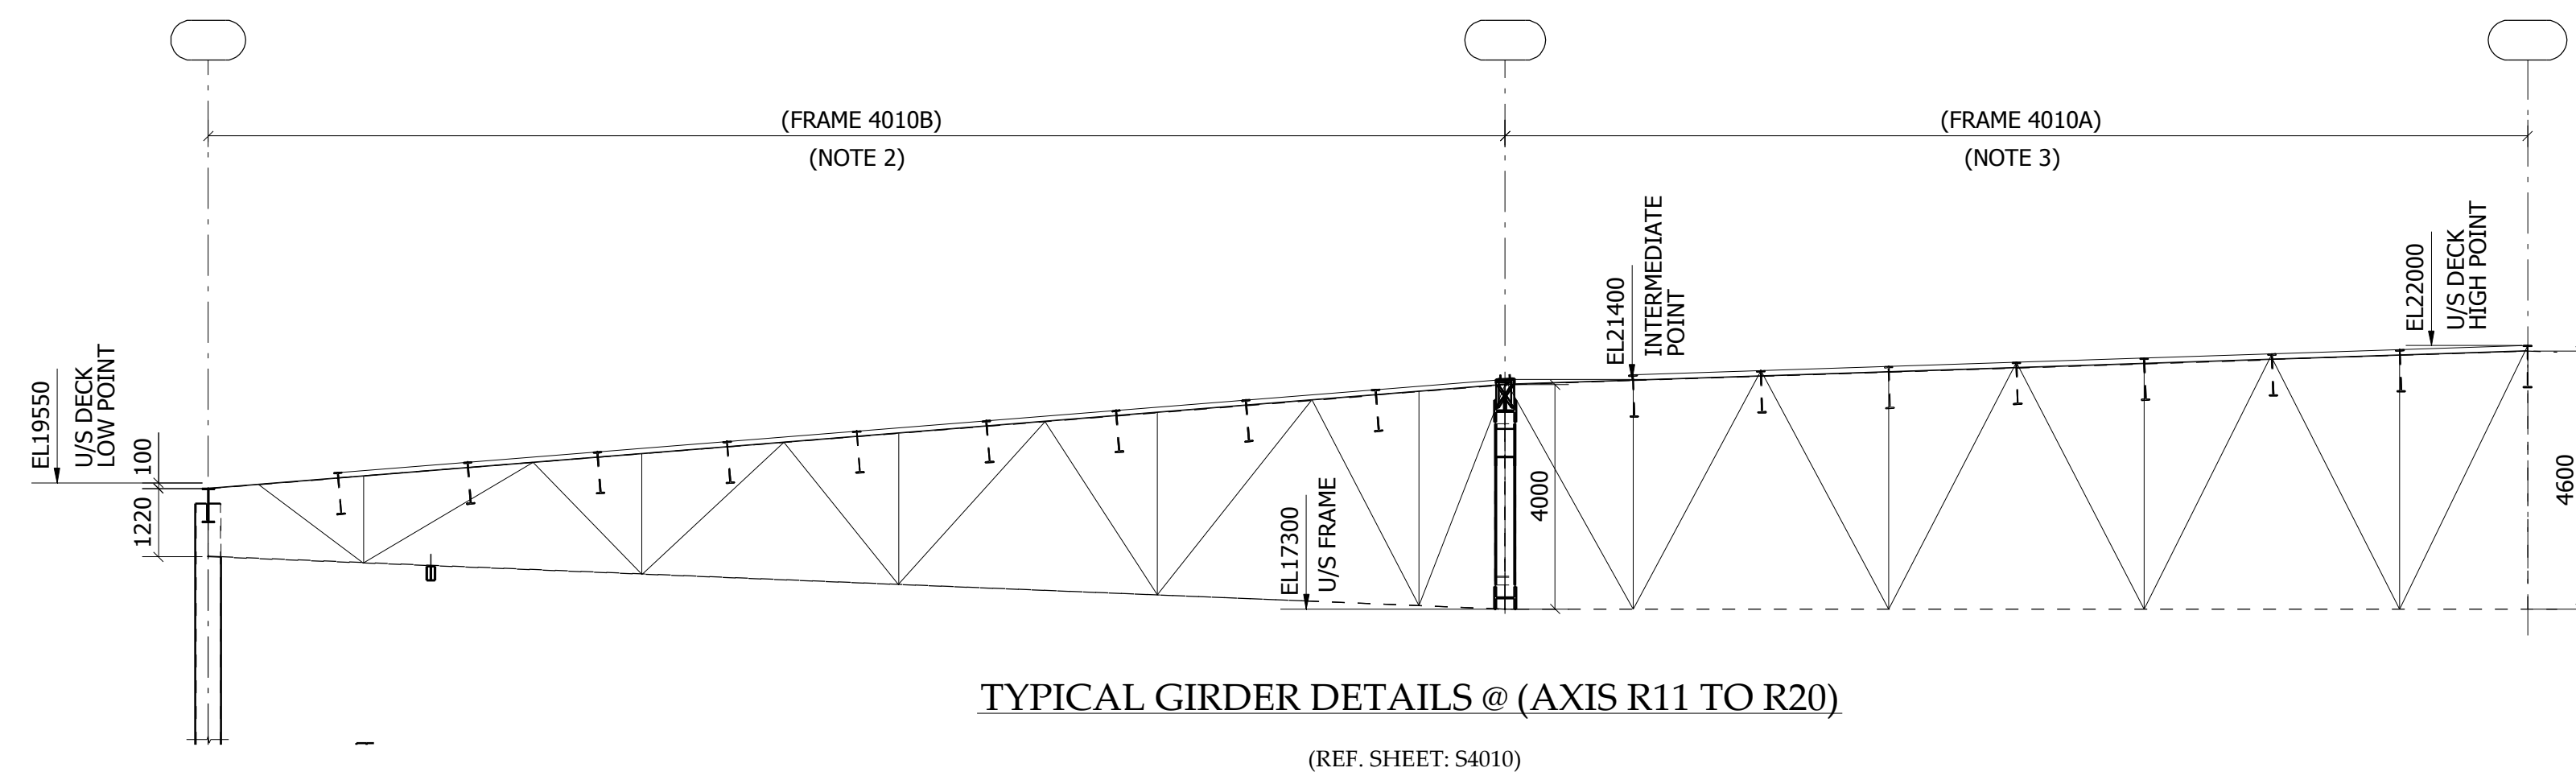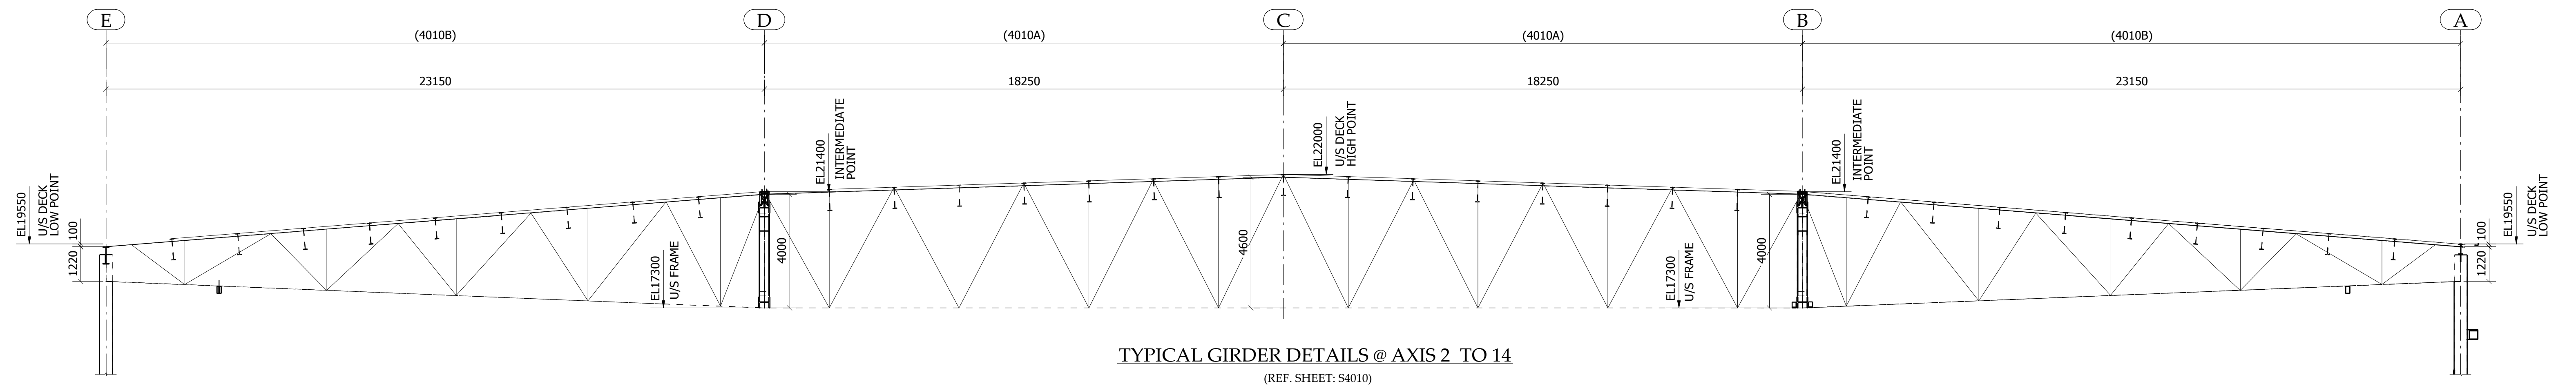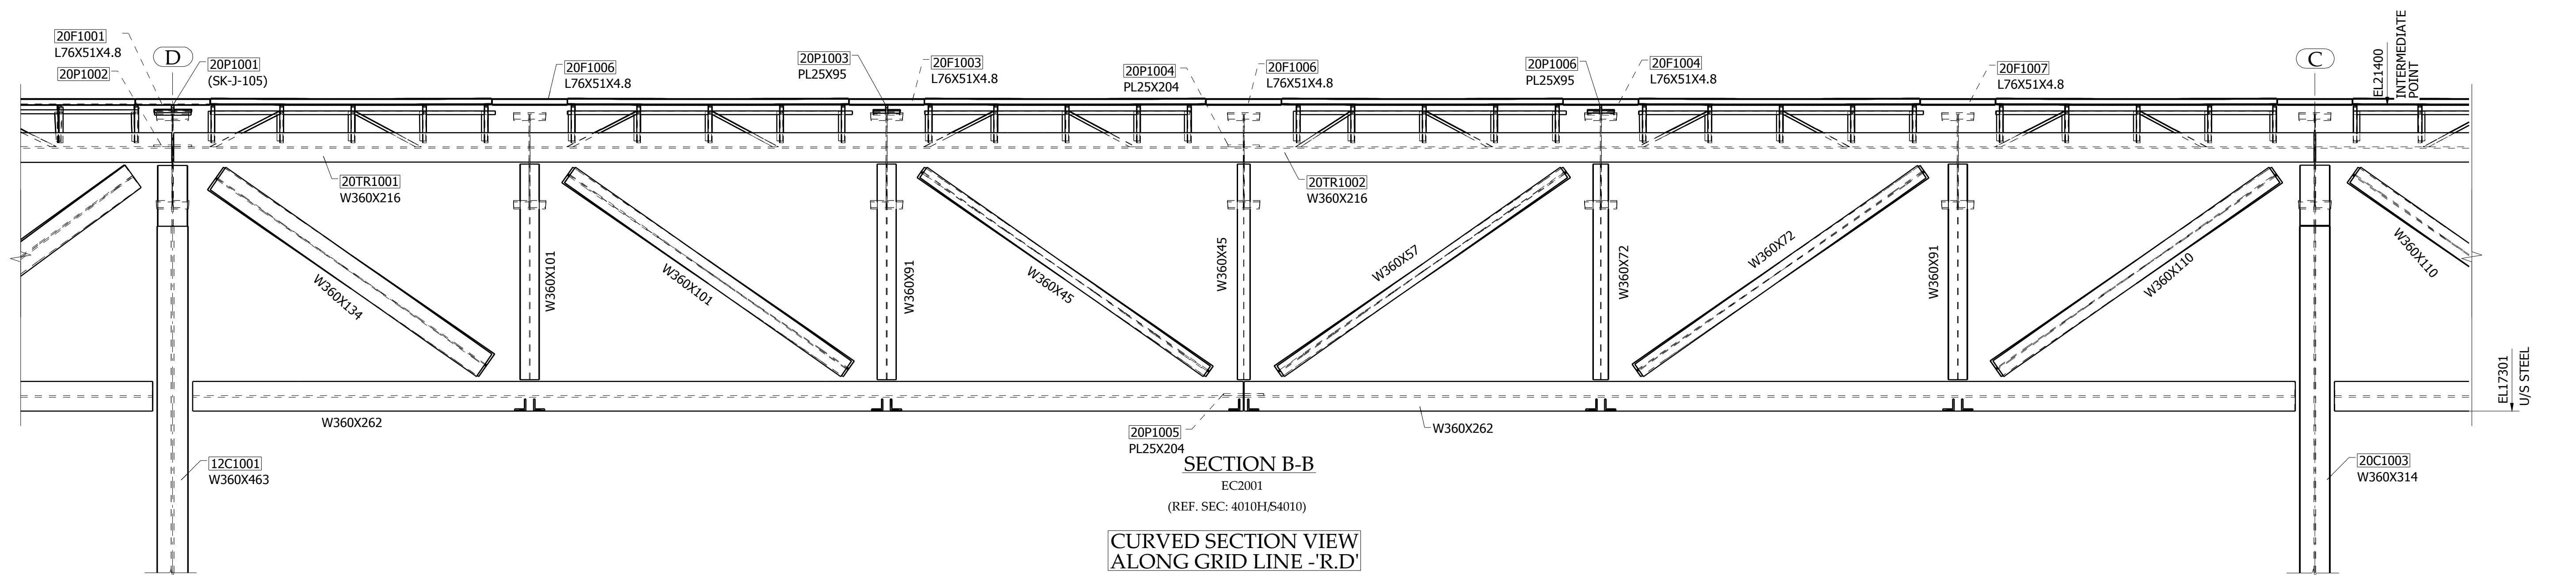

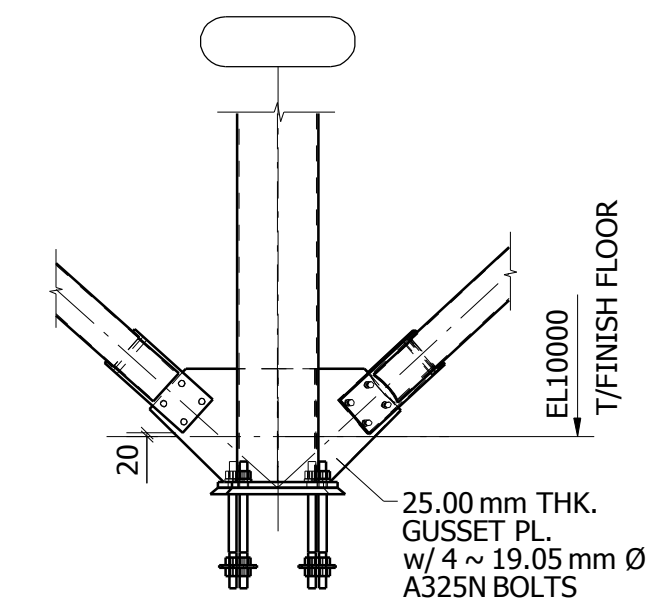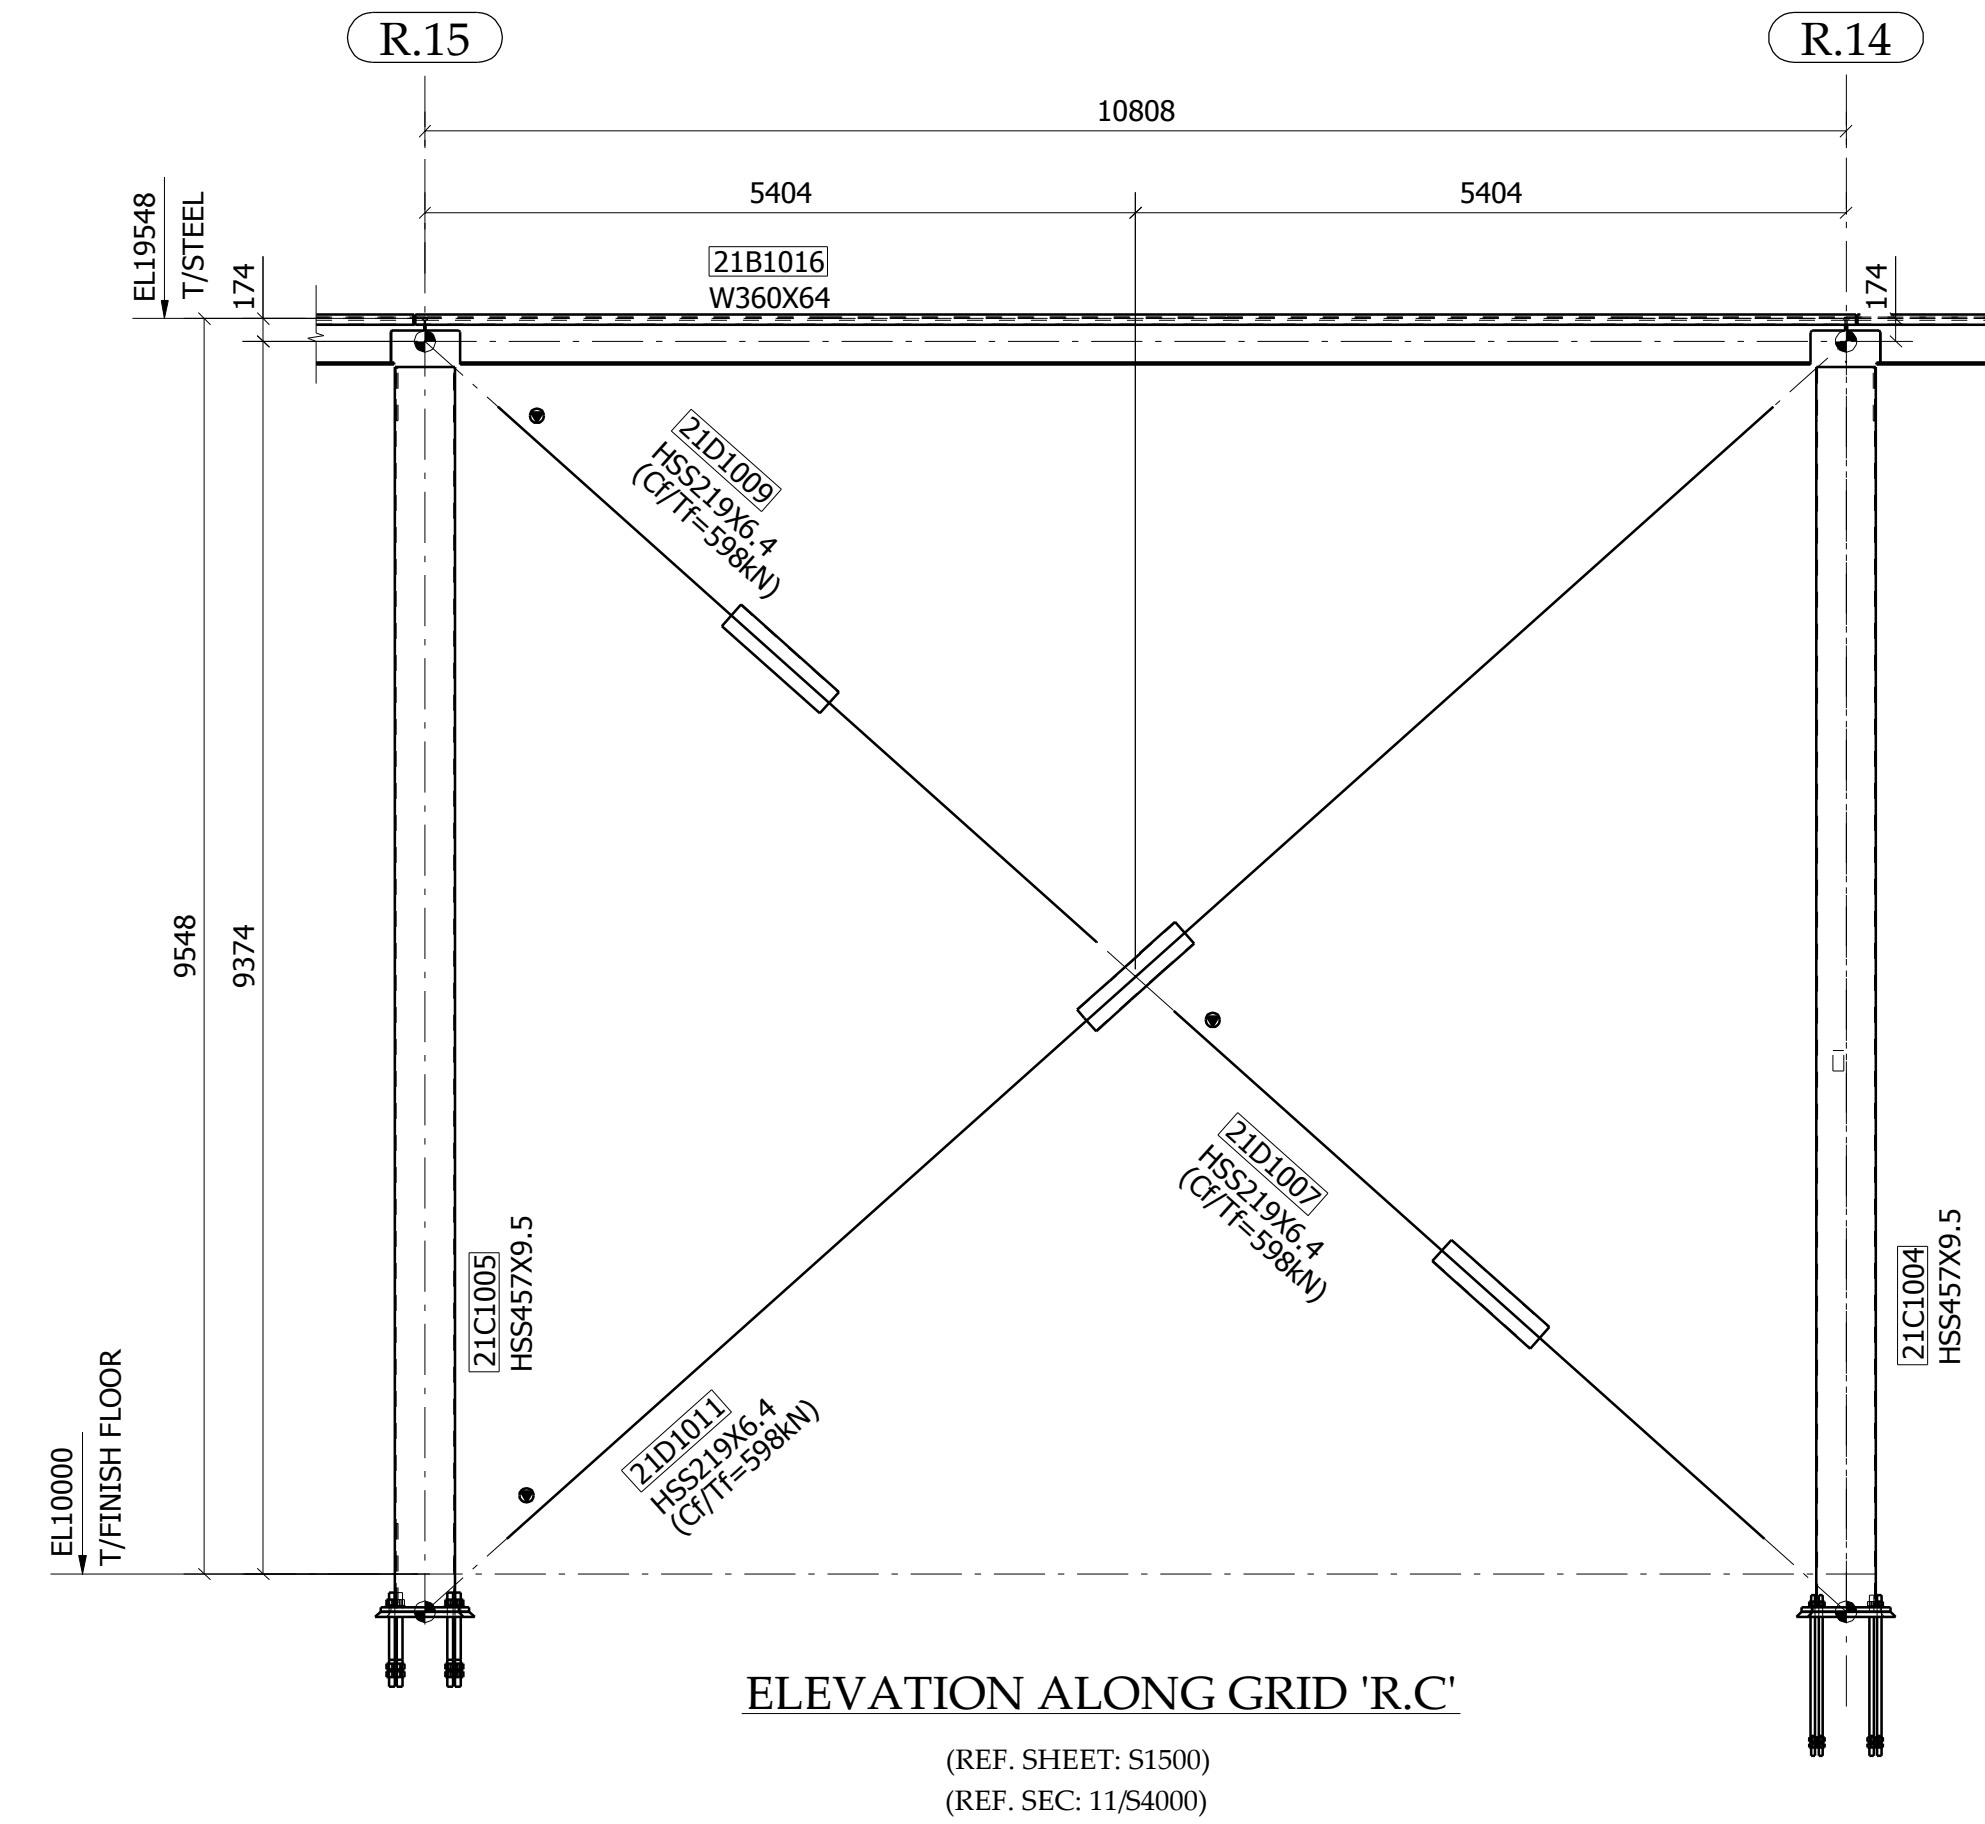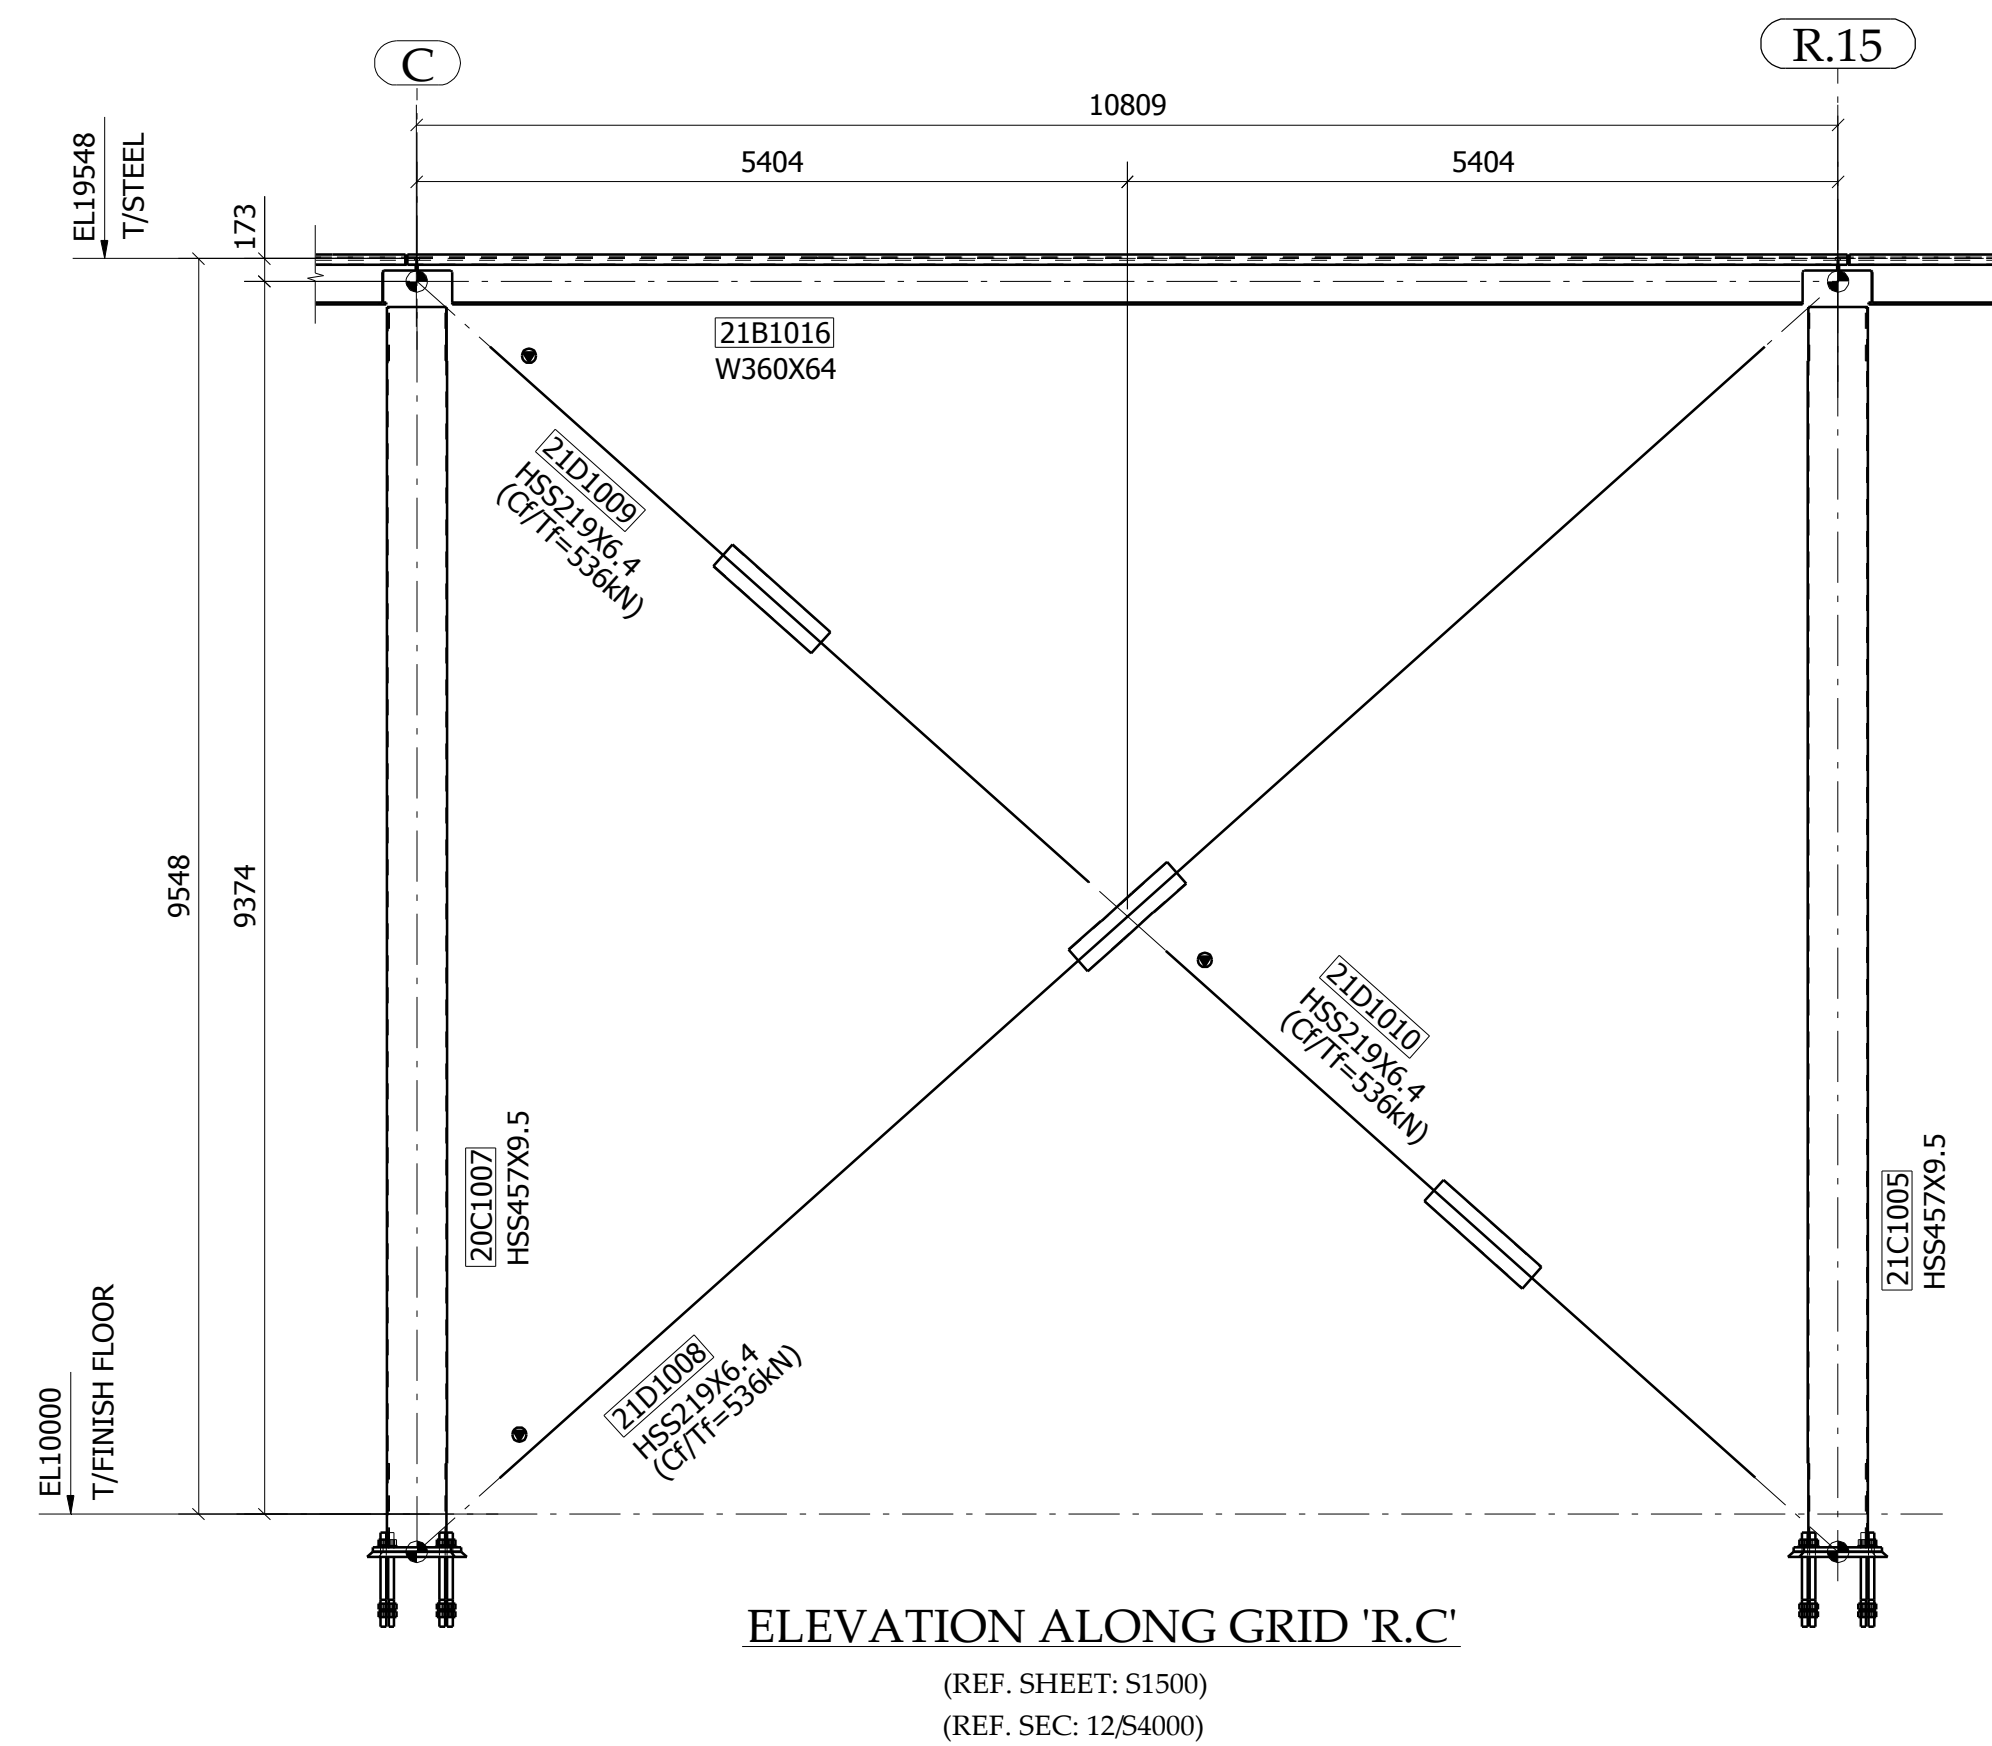


TYPICAL BRACE ARRANGEMENT

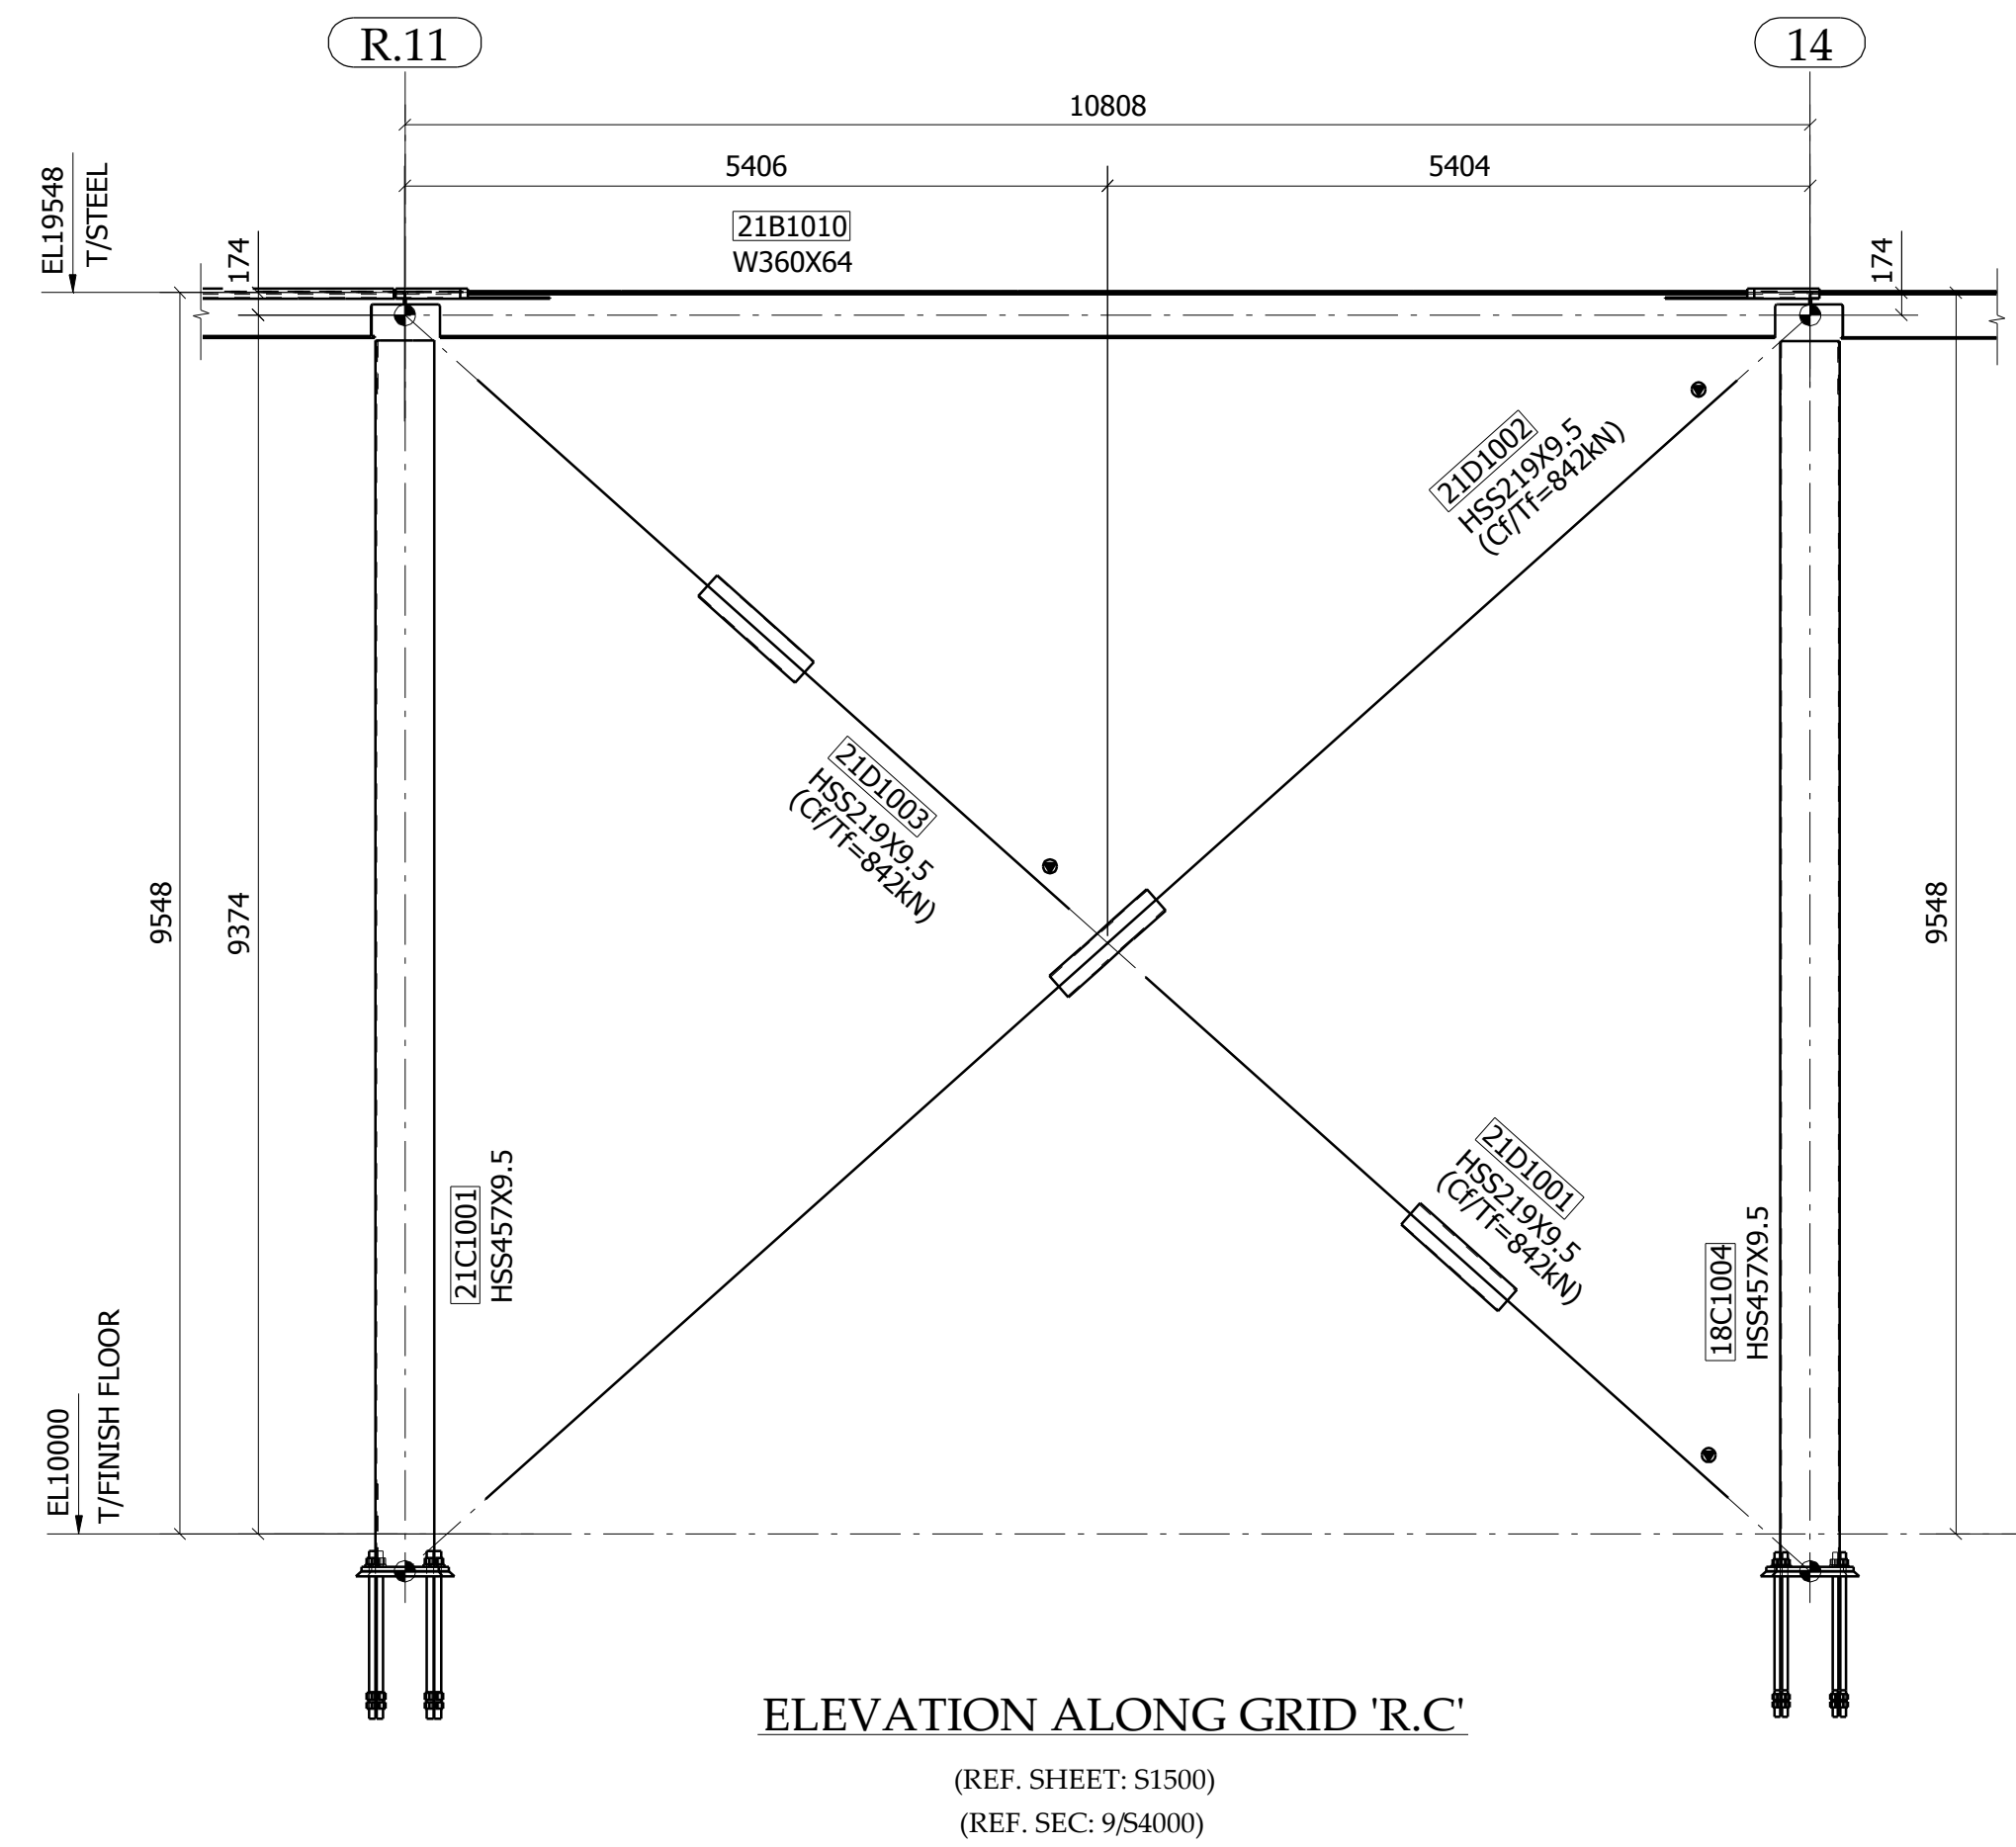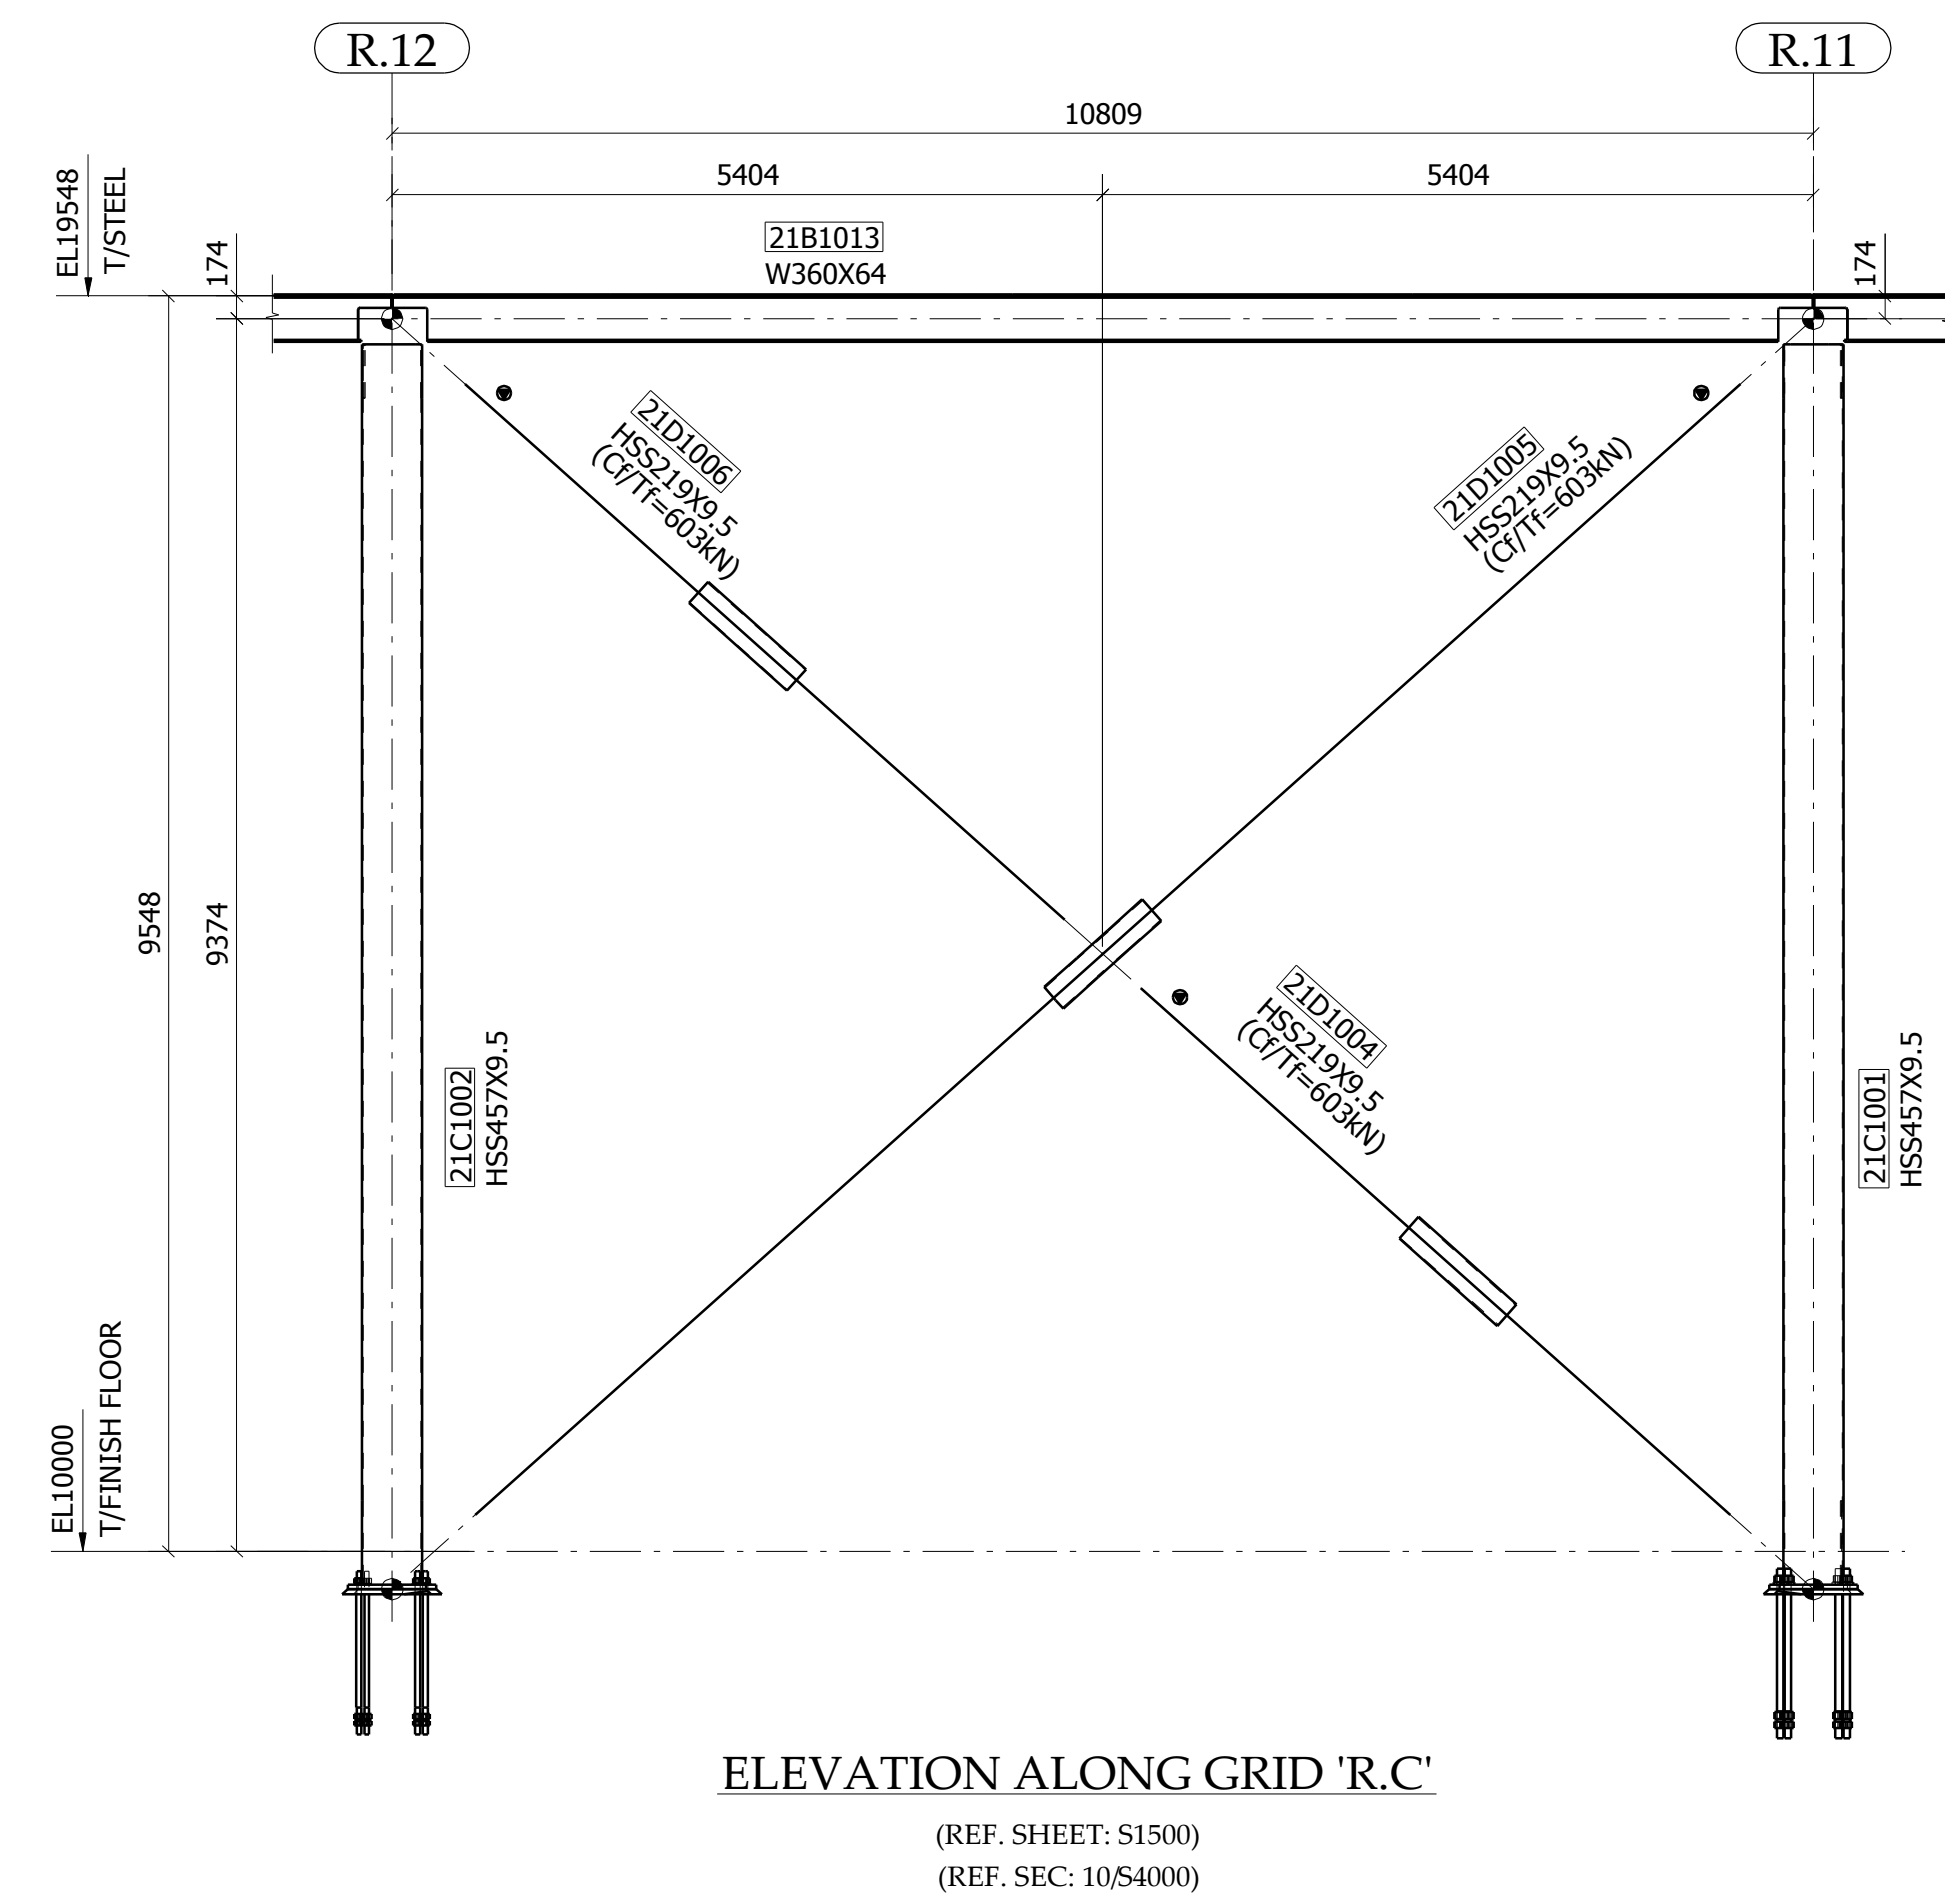


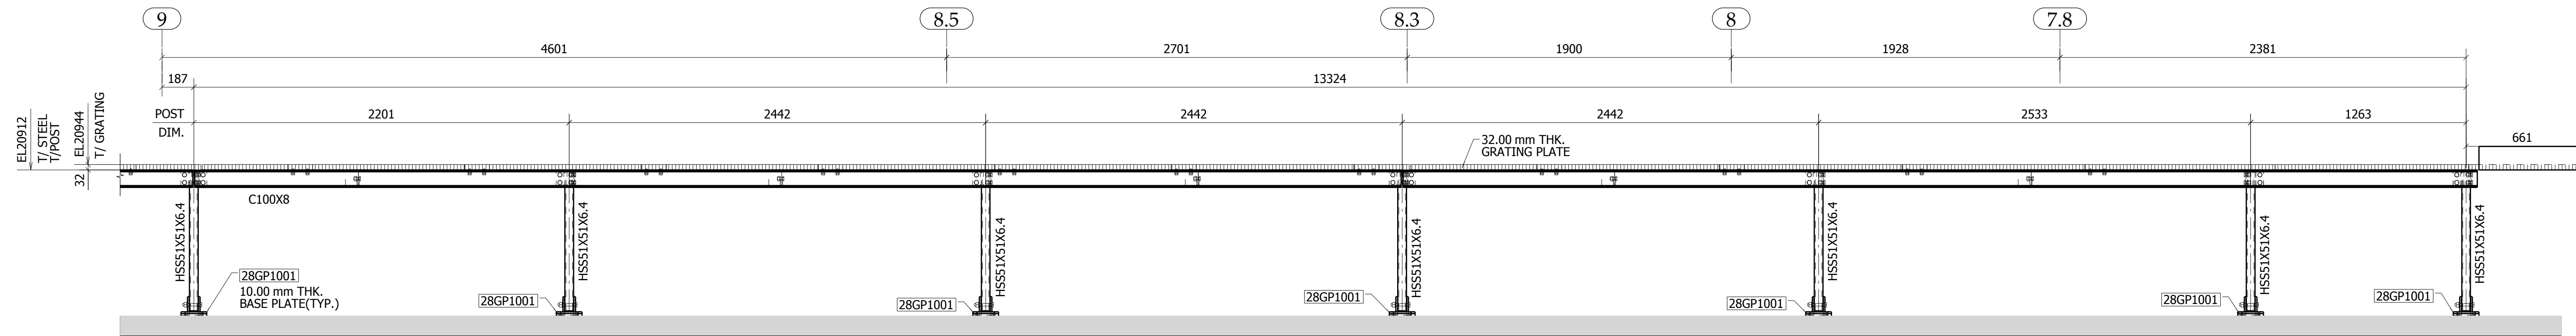


SECTION 1 - 1
EC2801

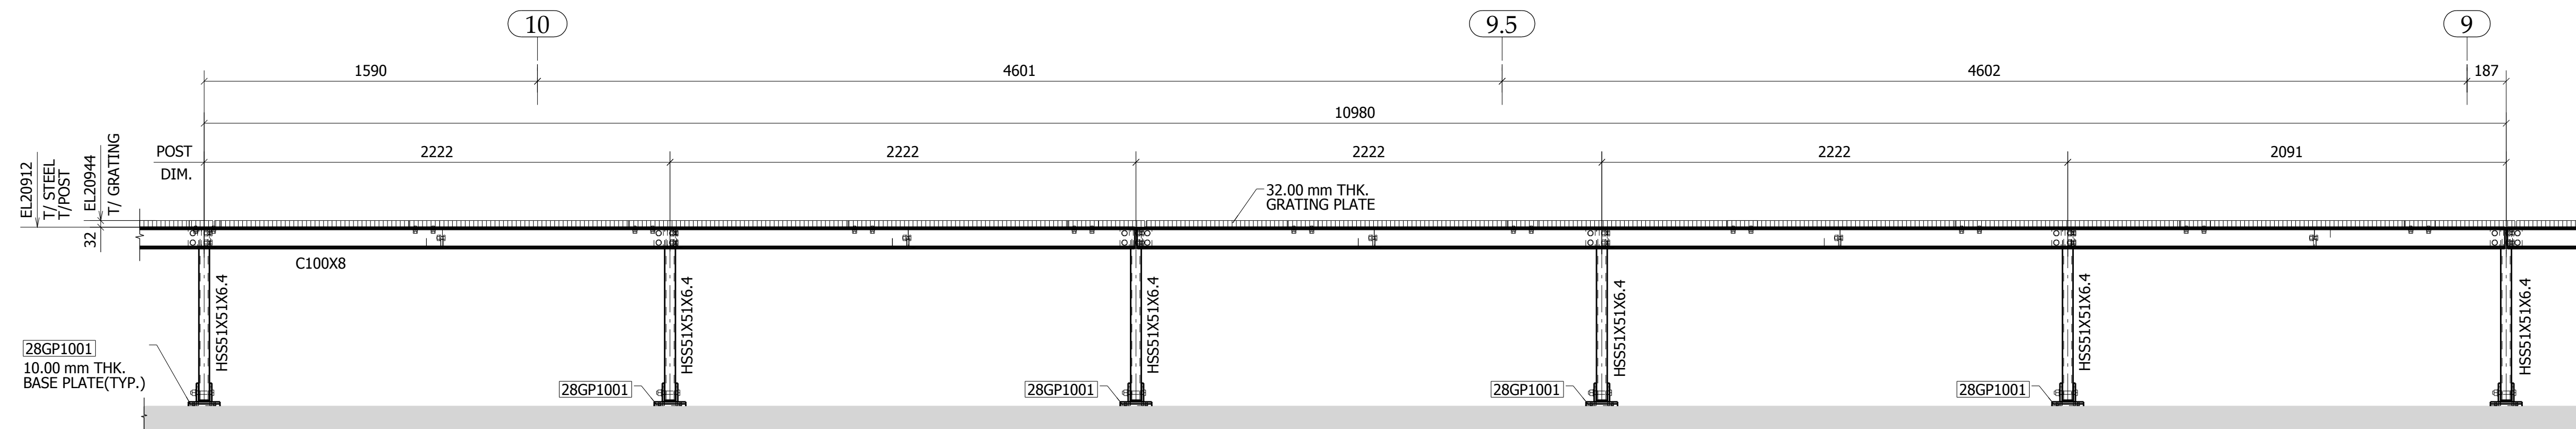


SECTION 2 - 2
EC2801

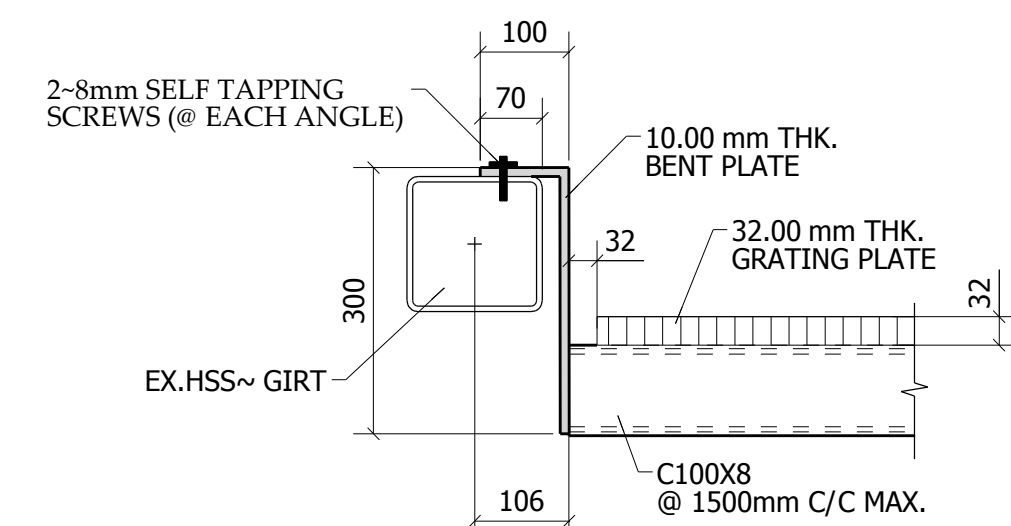


SECTION 6 - 6
EC2801
TYPICAL EX.GIRT TO ANGLE FIELD WELD DETAIL.

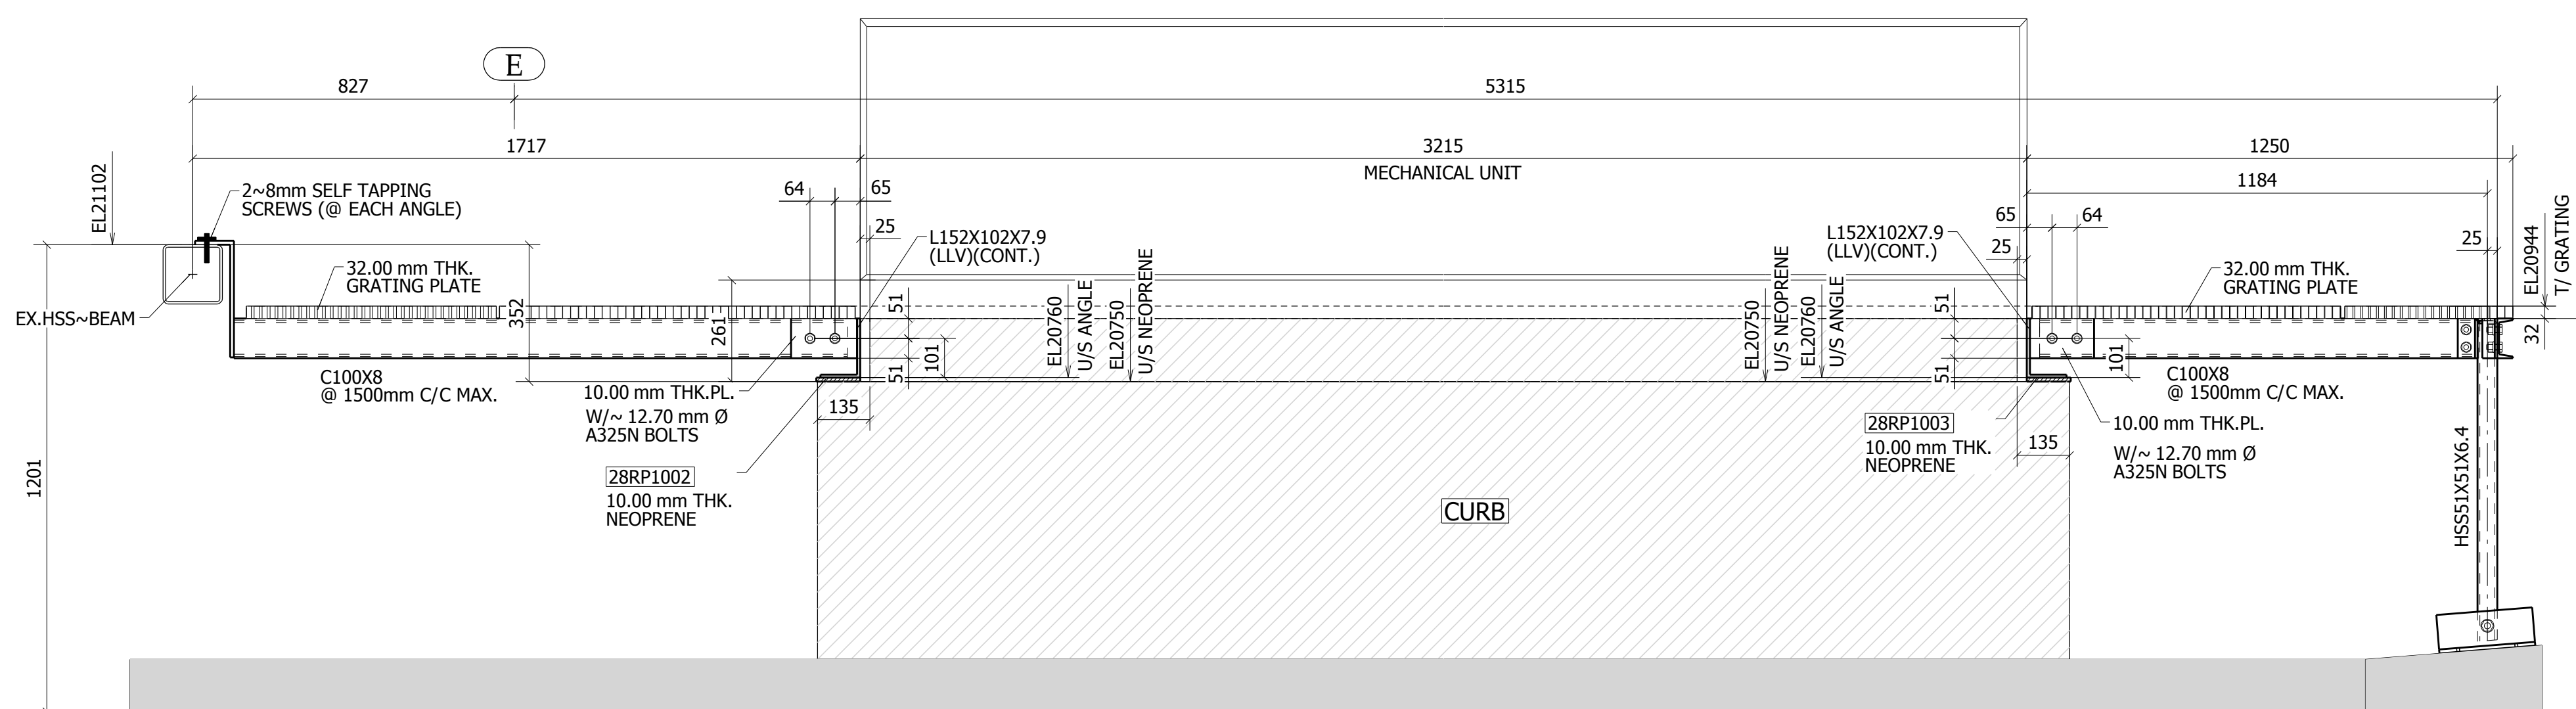


SECTION 5 - 5
EC2801

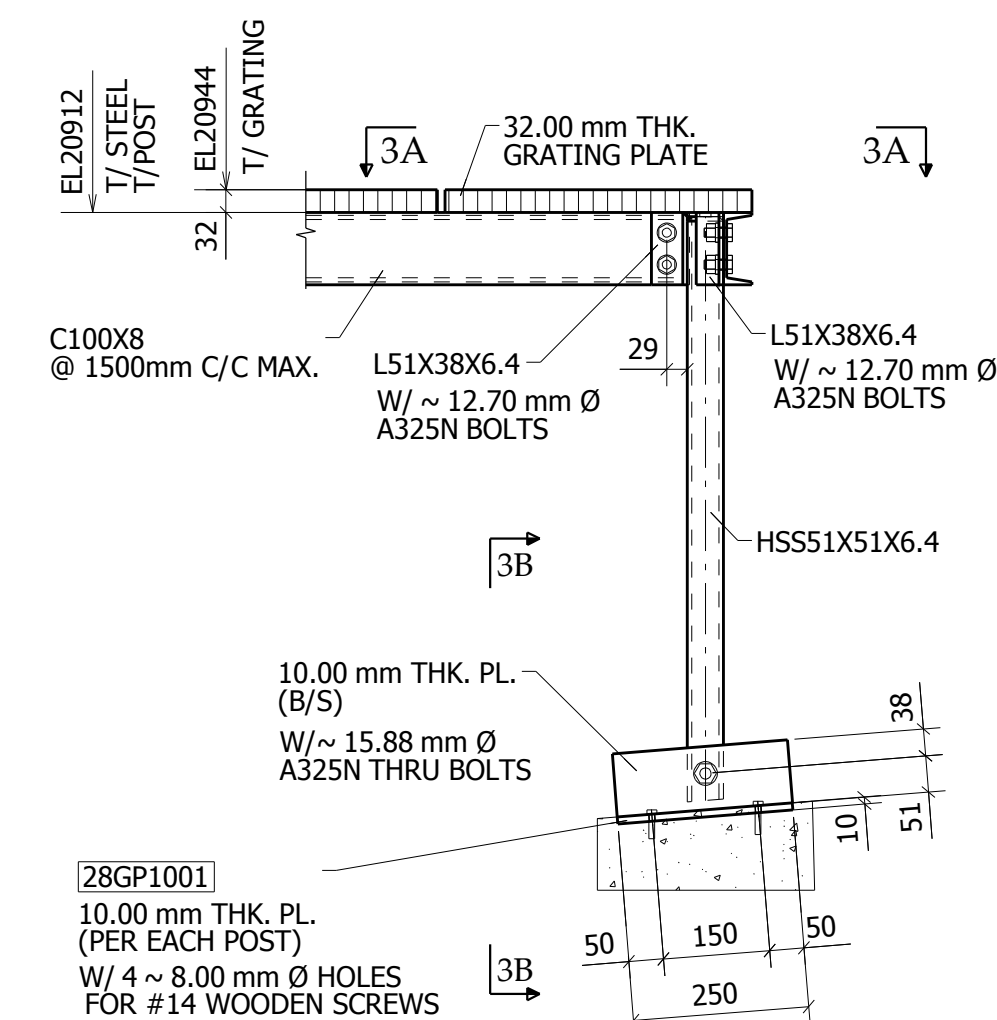


SECTION 3 - 3
EC2801

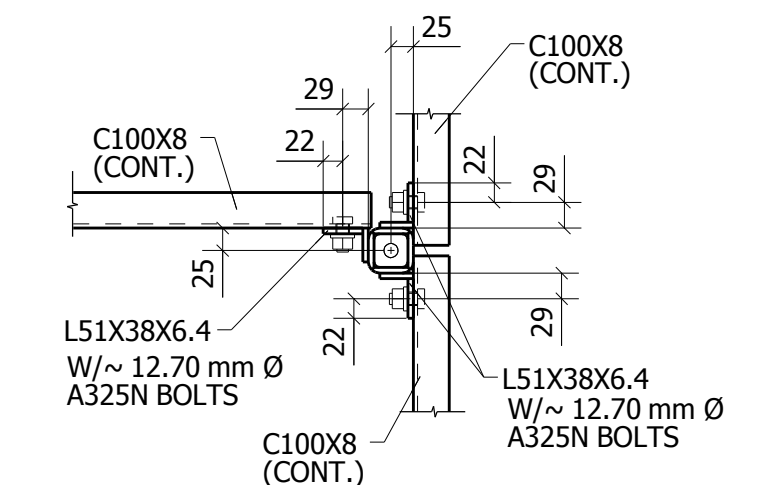

SECTION 3A - 3A

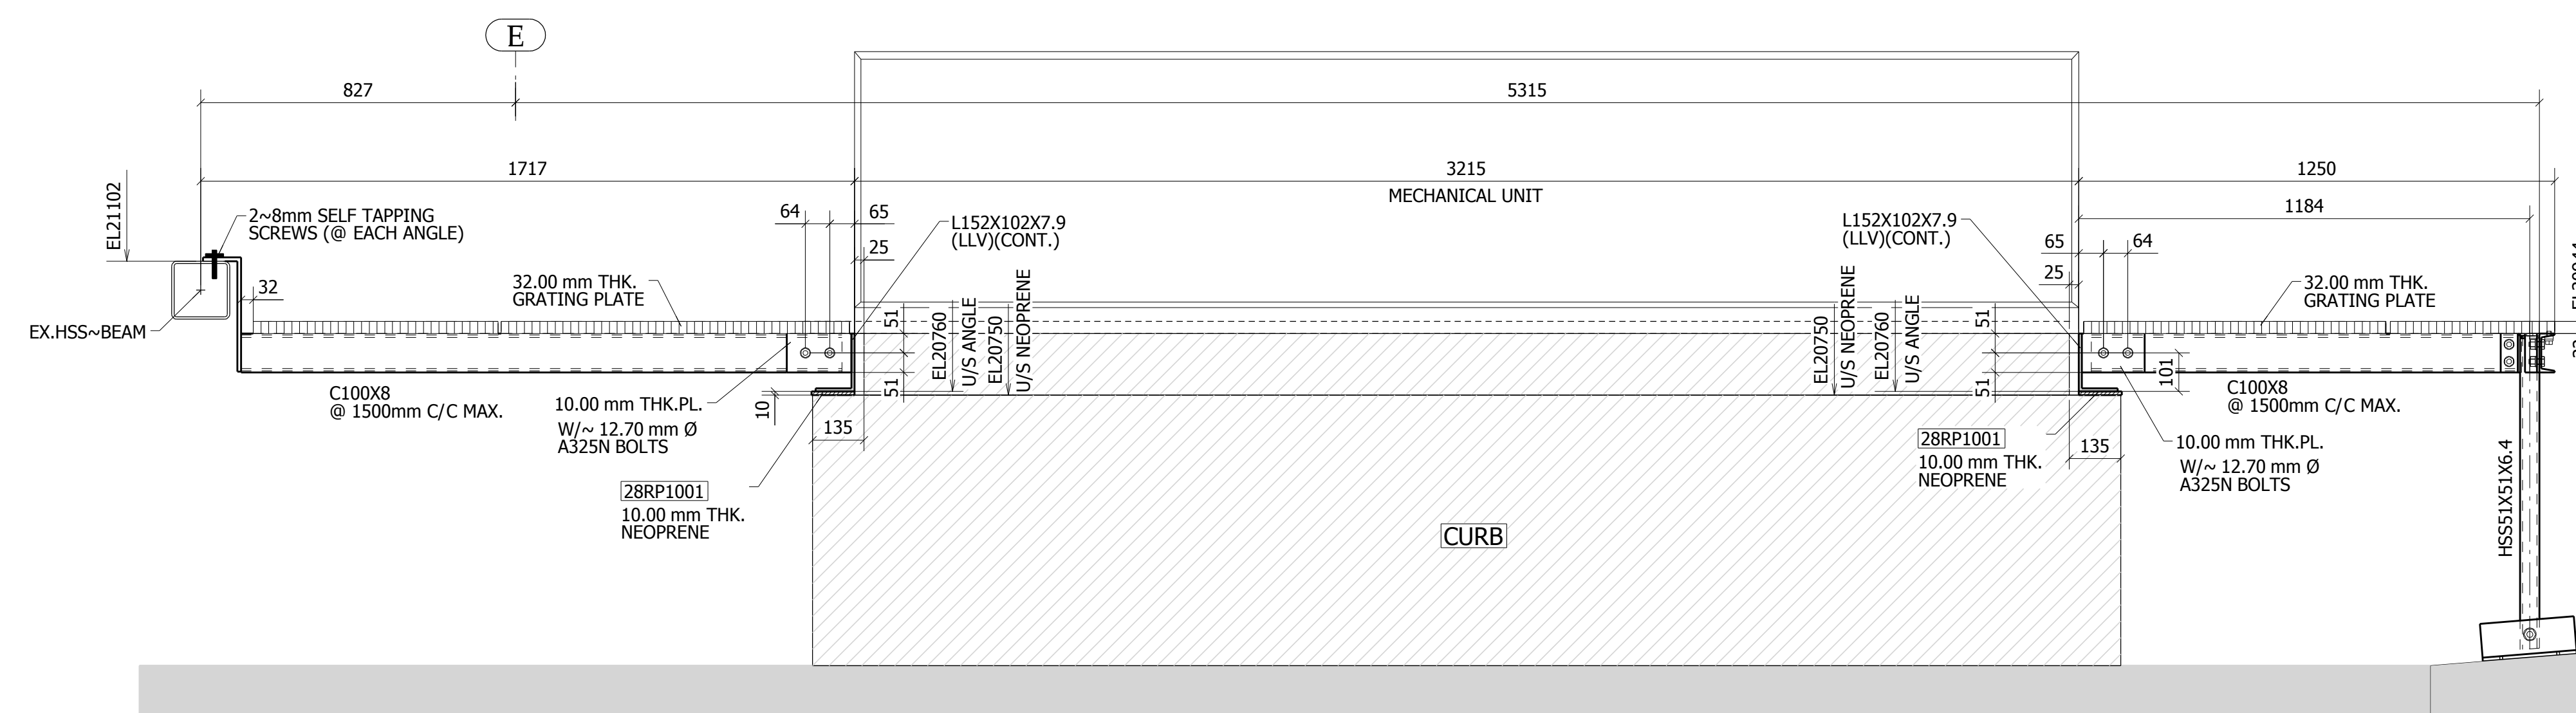


SECTION 4 - 4
EC2801

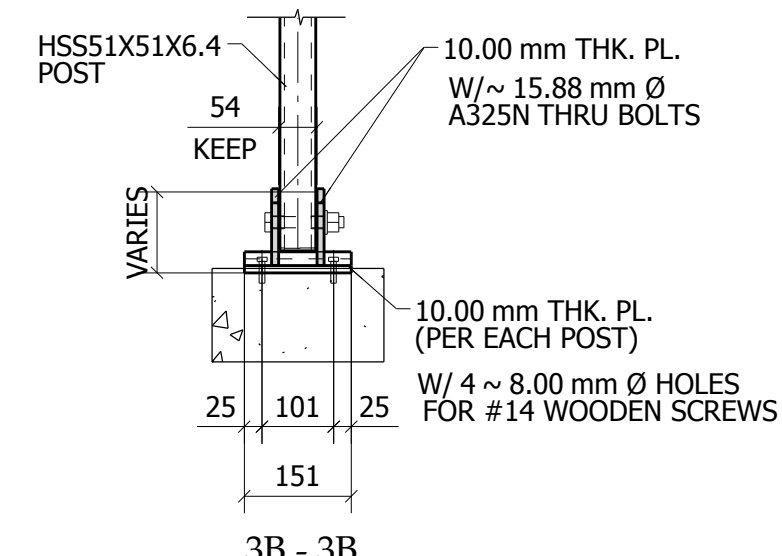


3B - 3B











30747

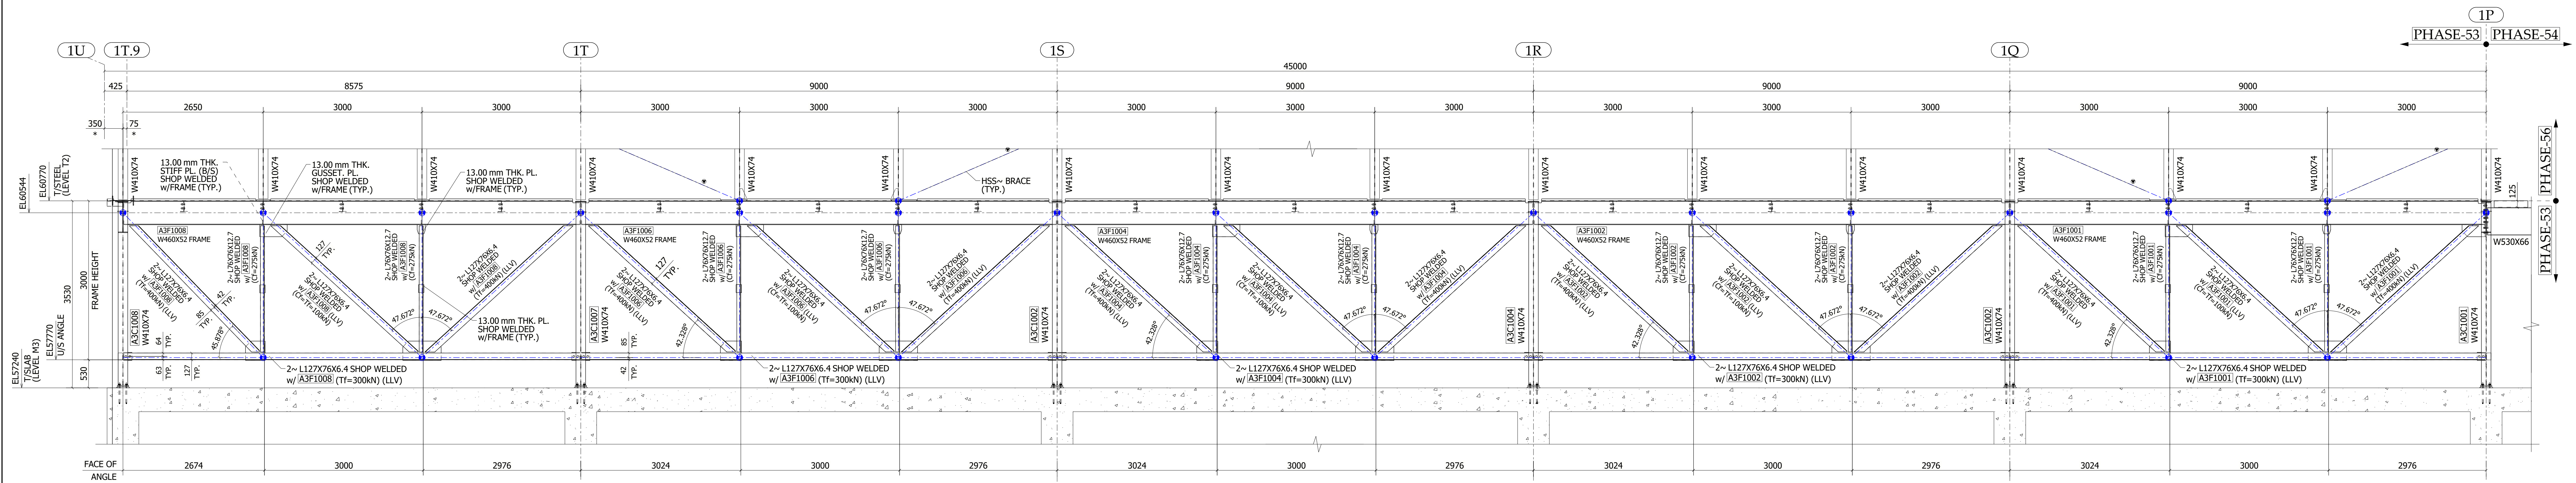

SECTION 7-7
ELEVATION ALONG AXIS "C3"
(REFER SHEET: S-A-7500)

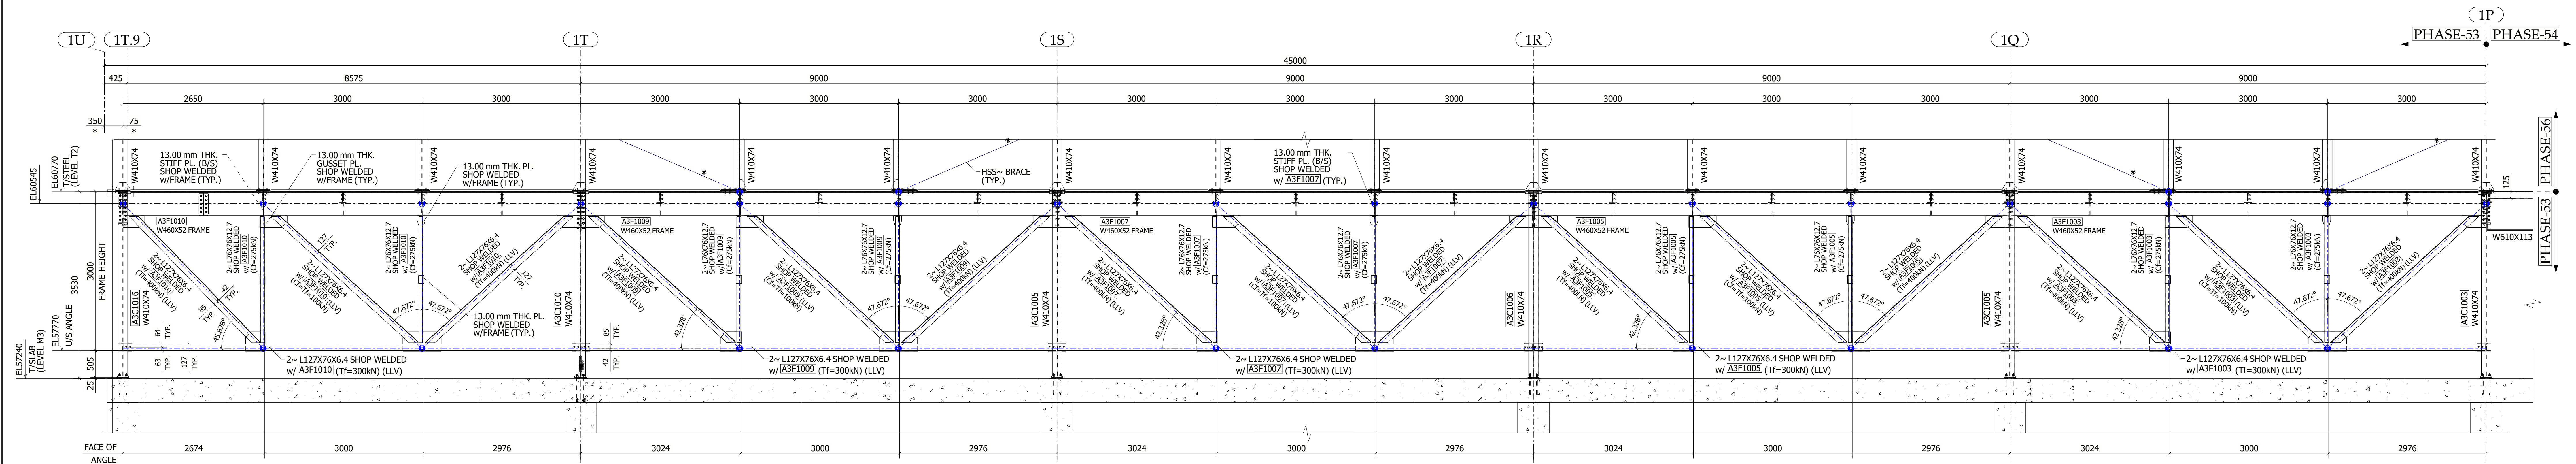


SECTION 8-8
ELEVATION ALONG AXIS "C5"
(REFER SHEET: S-A-7500)

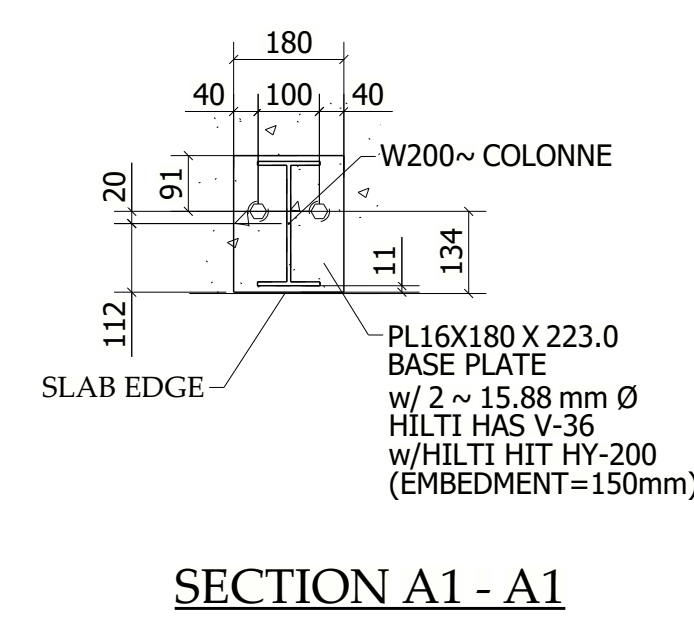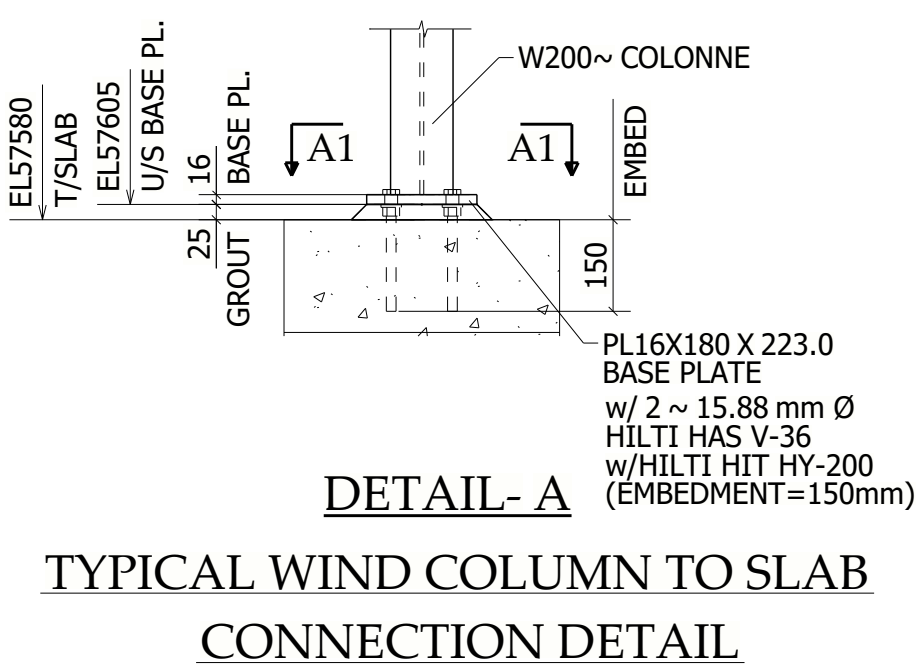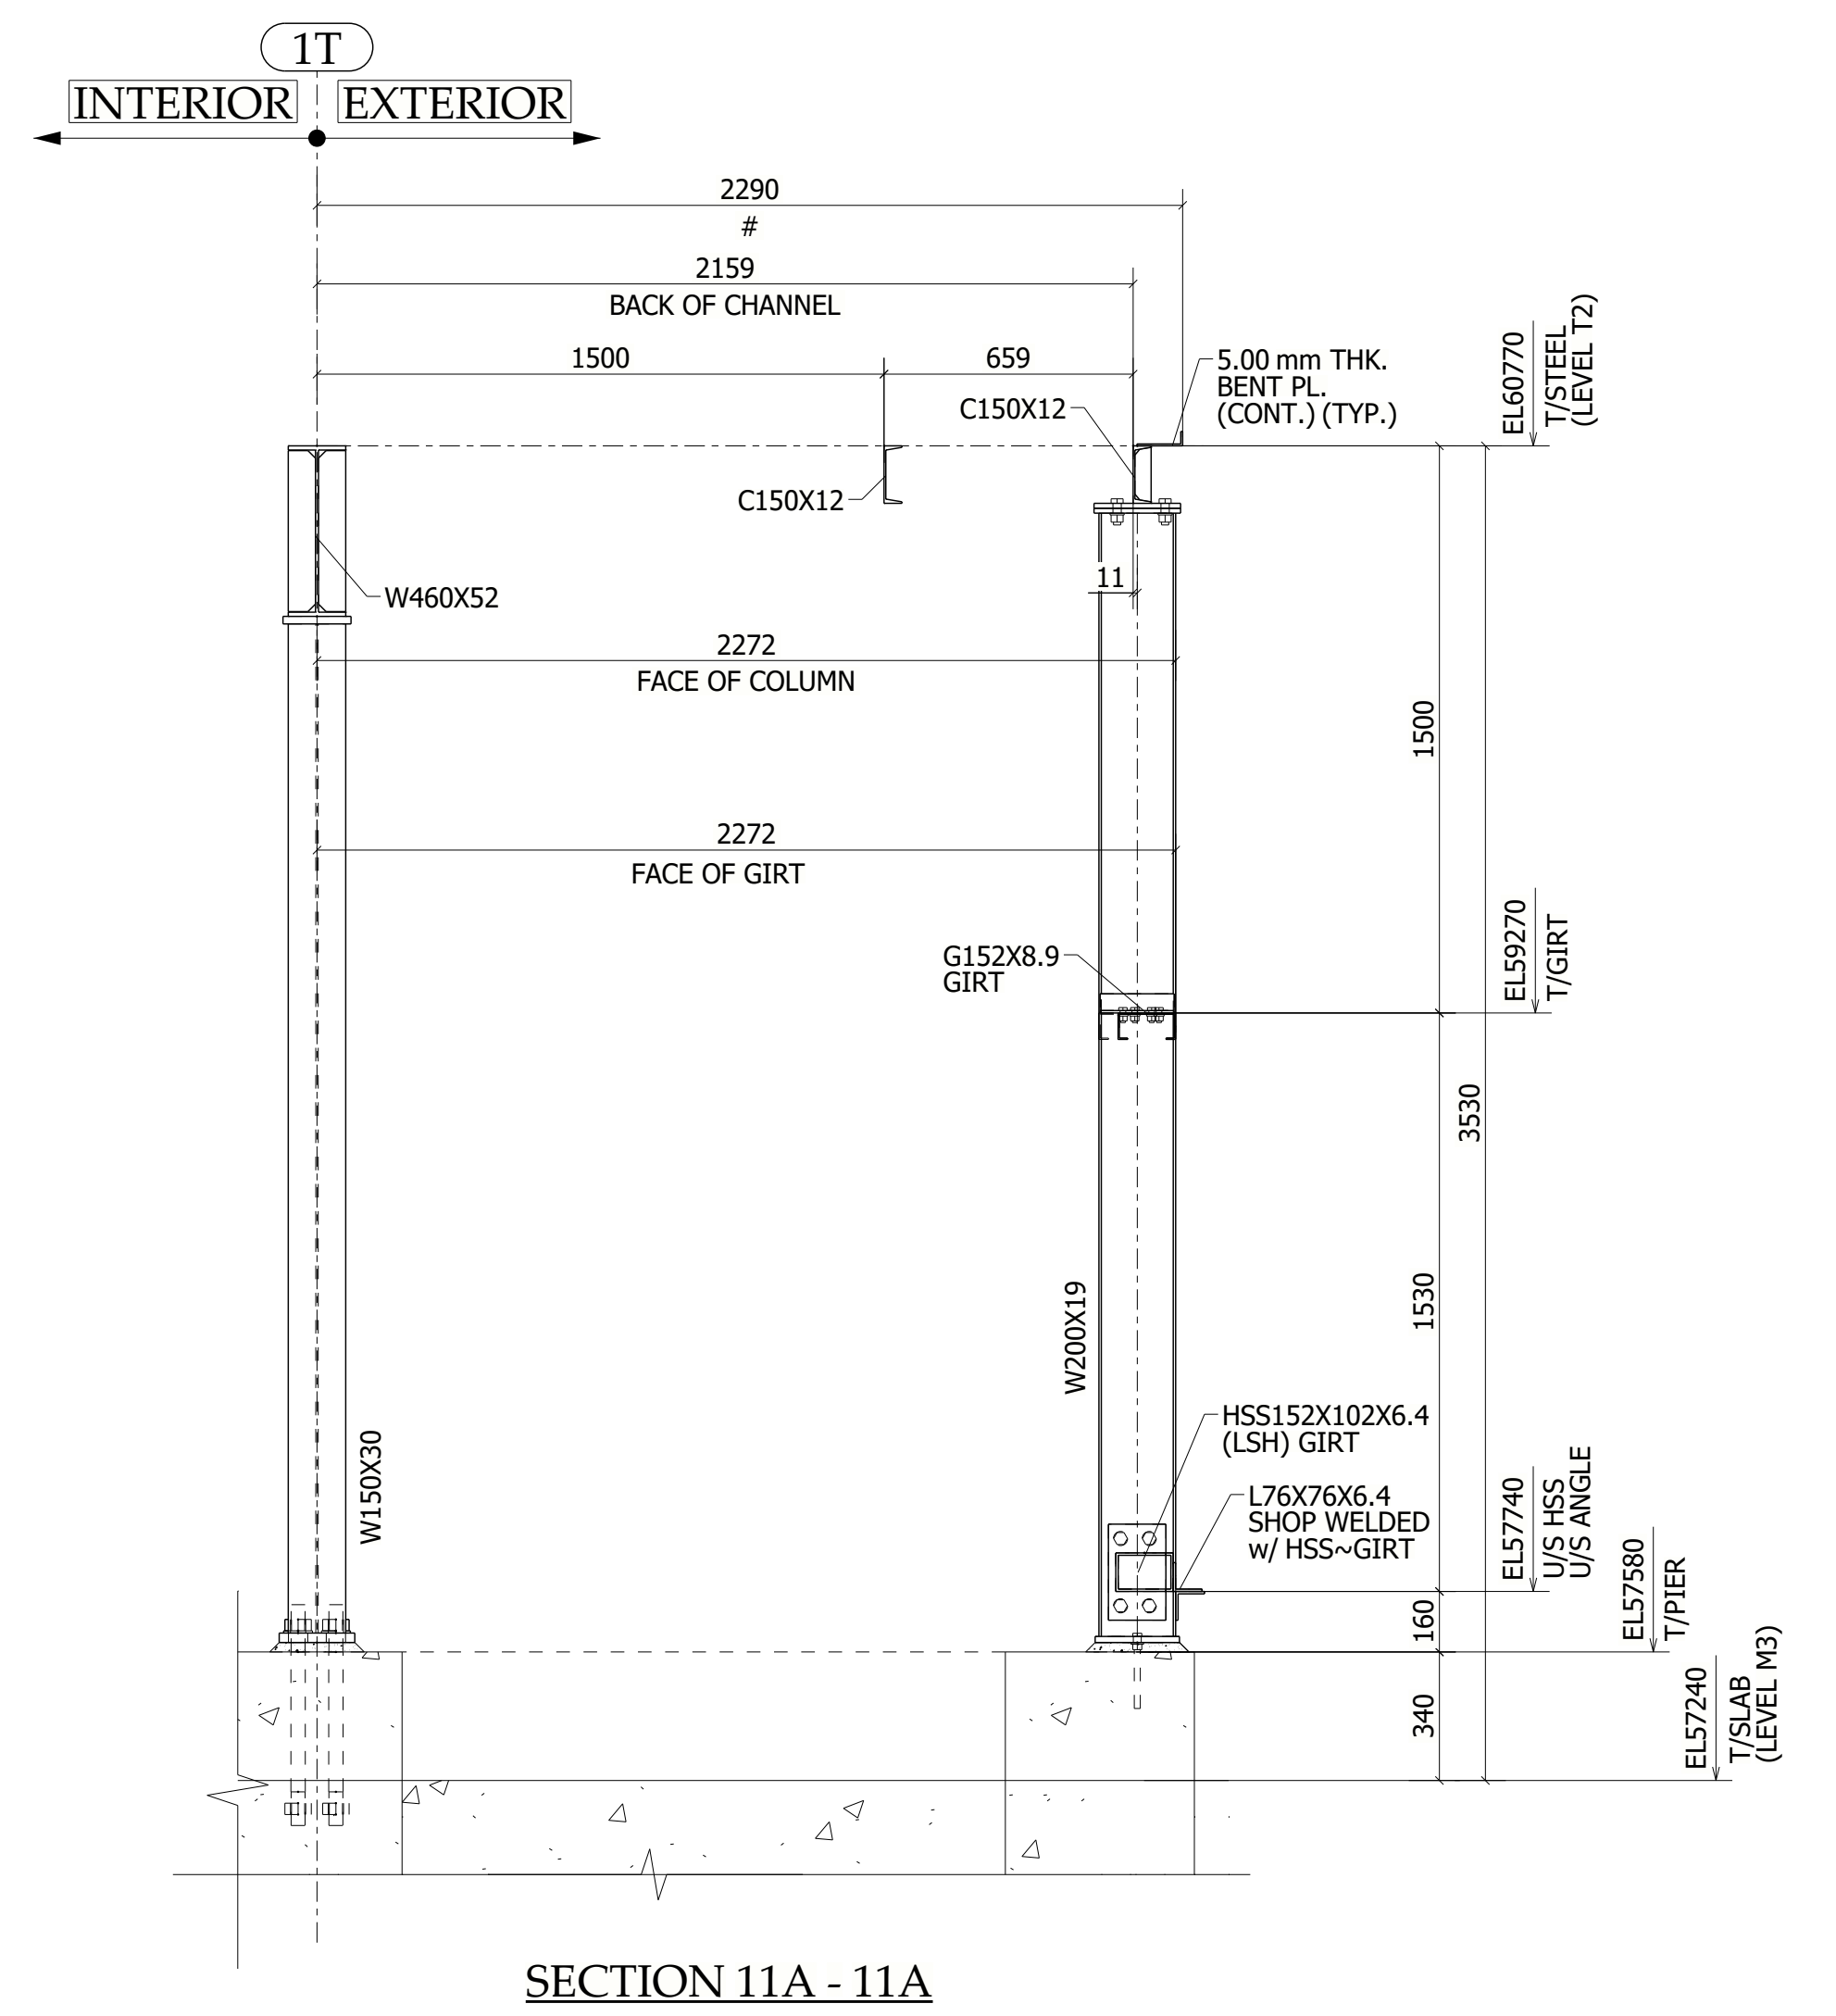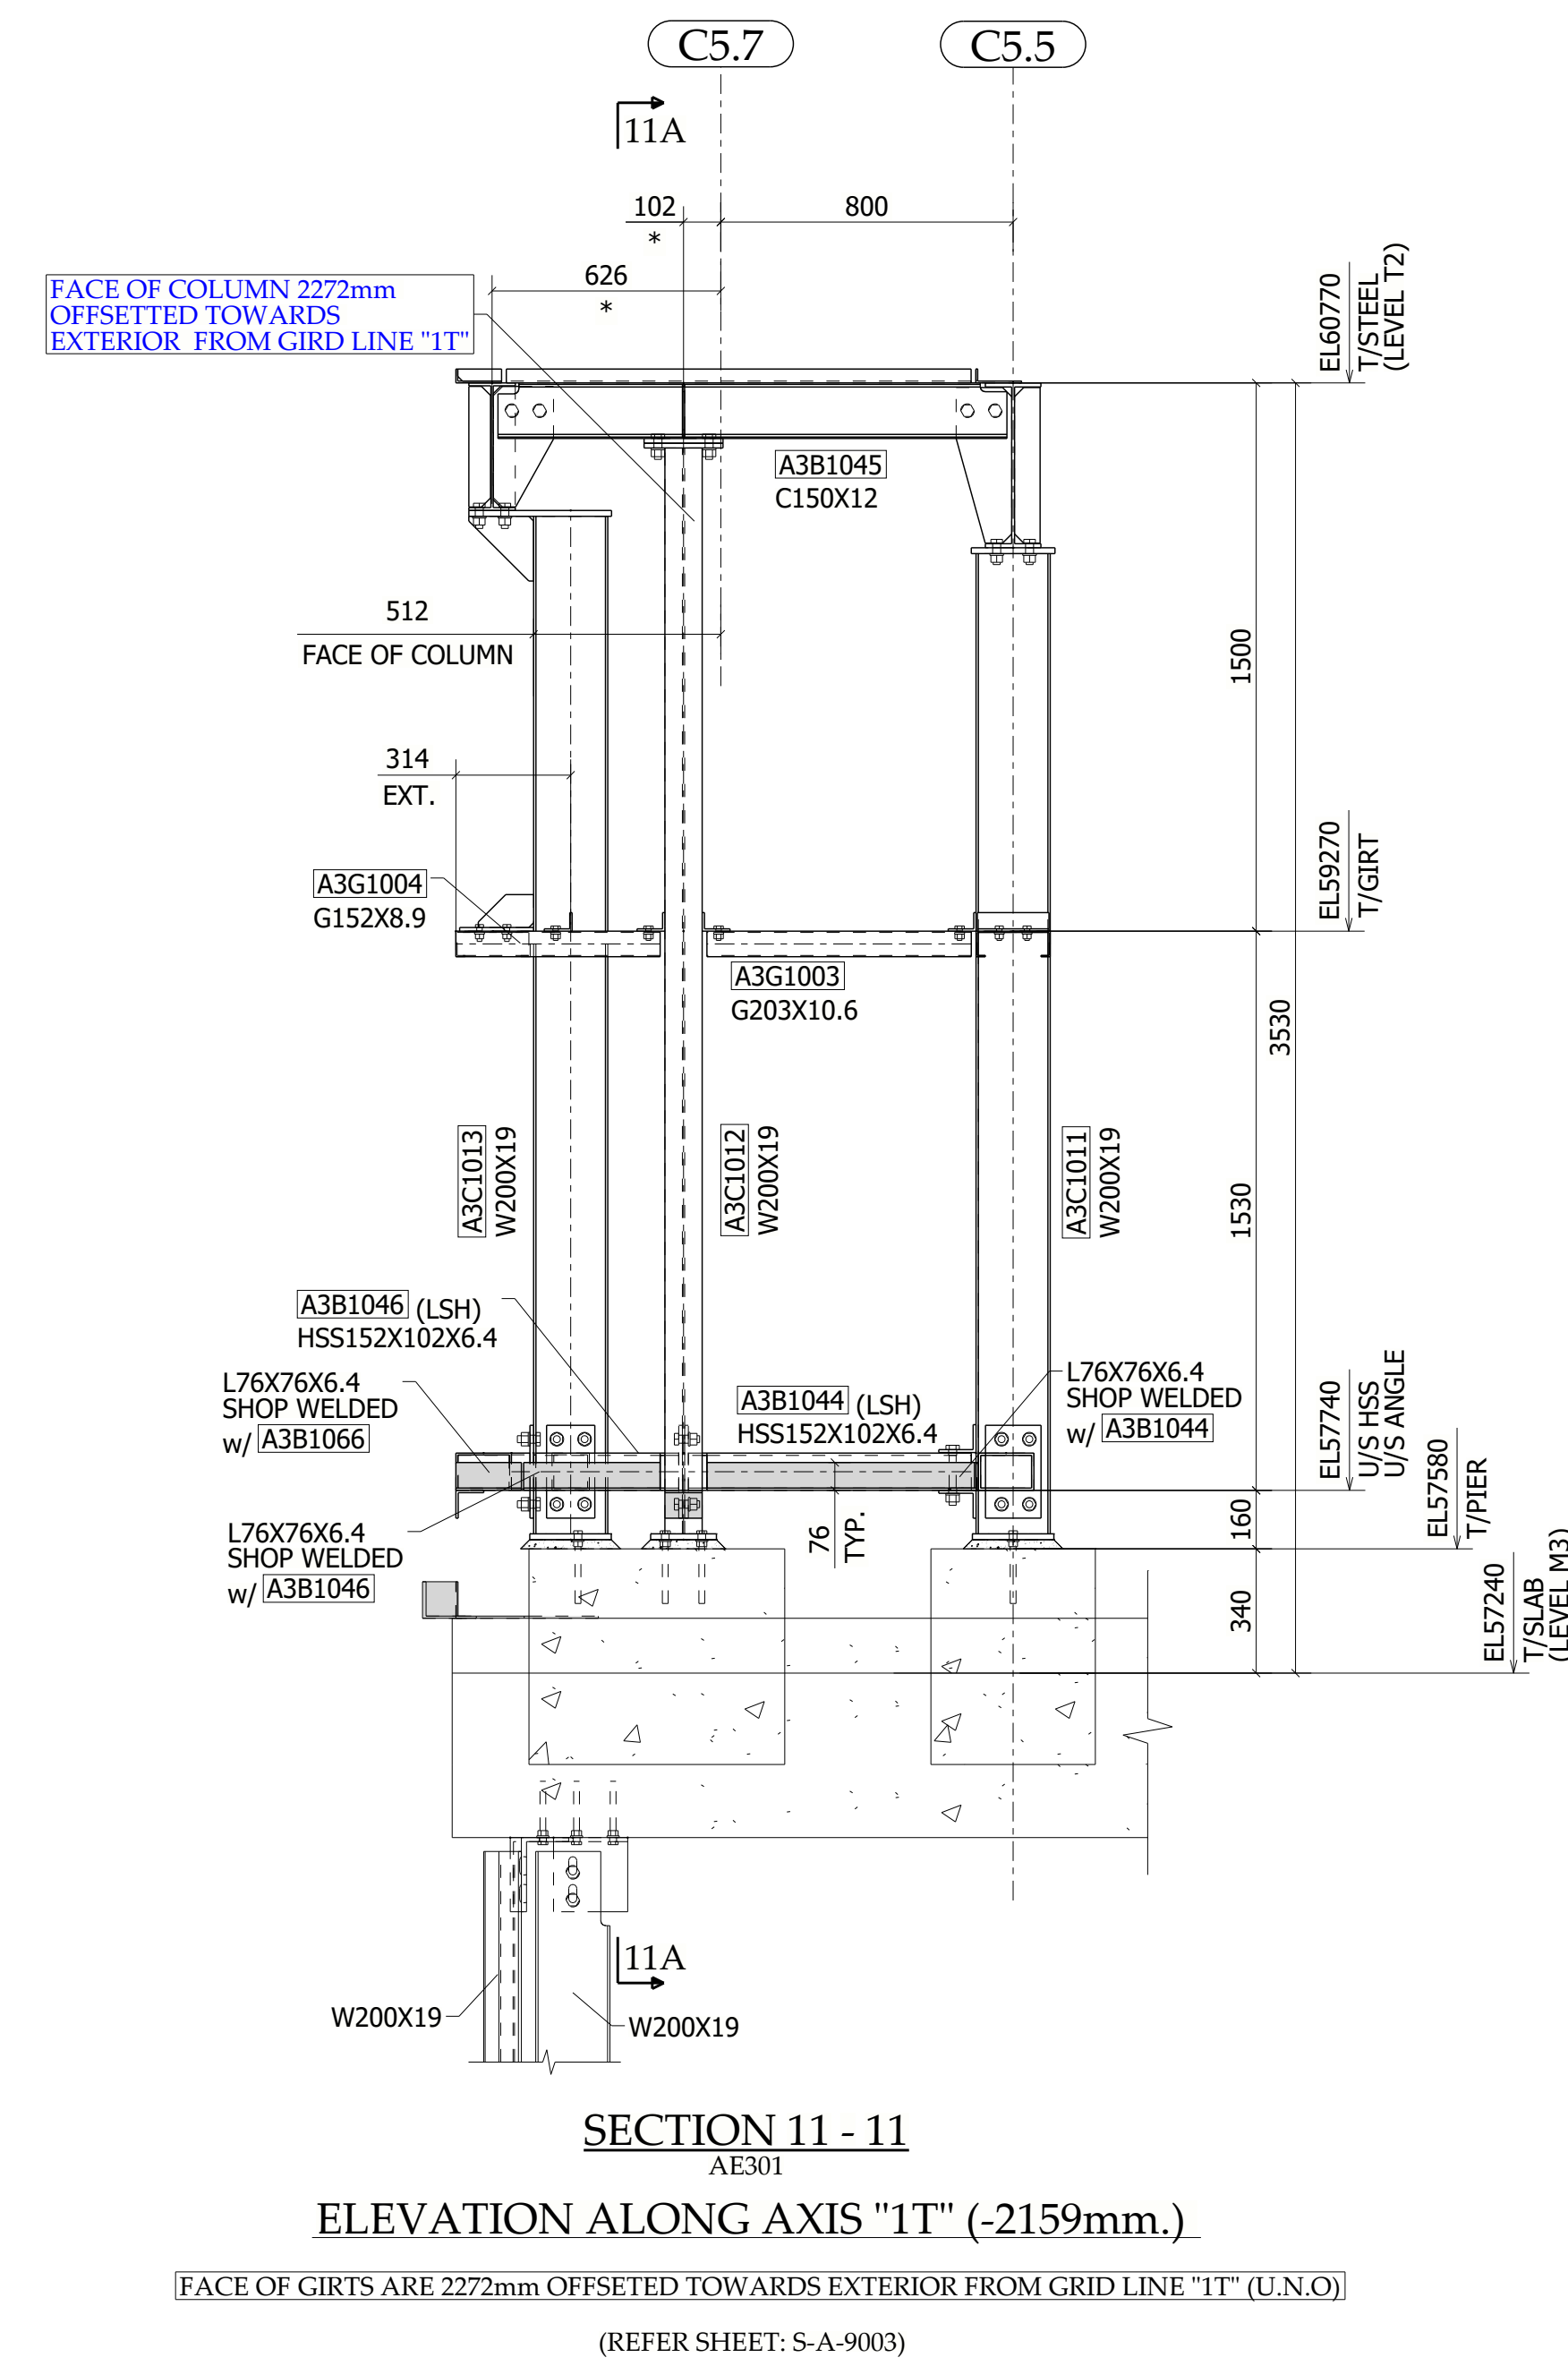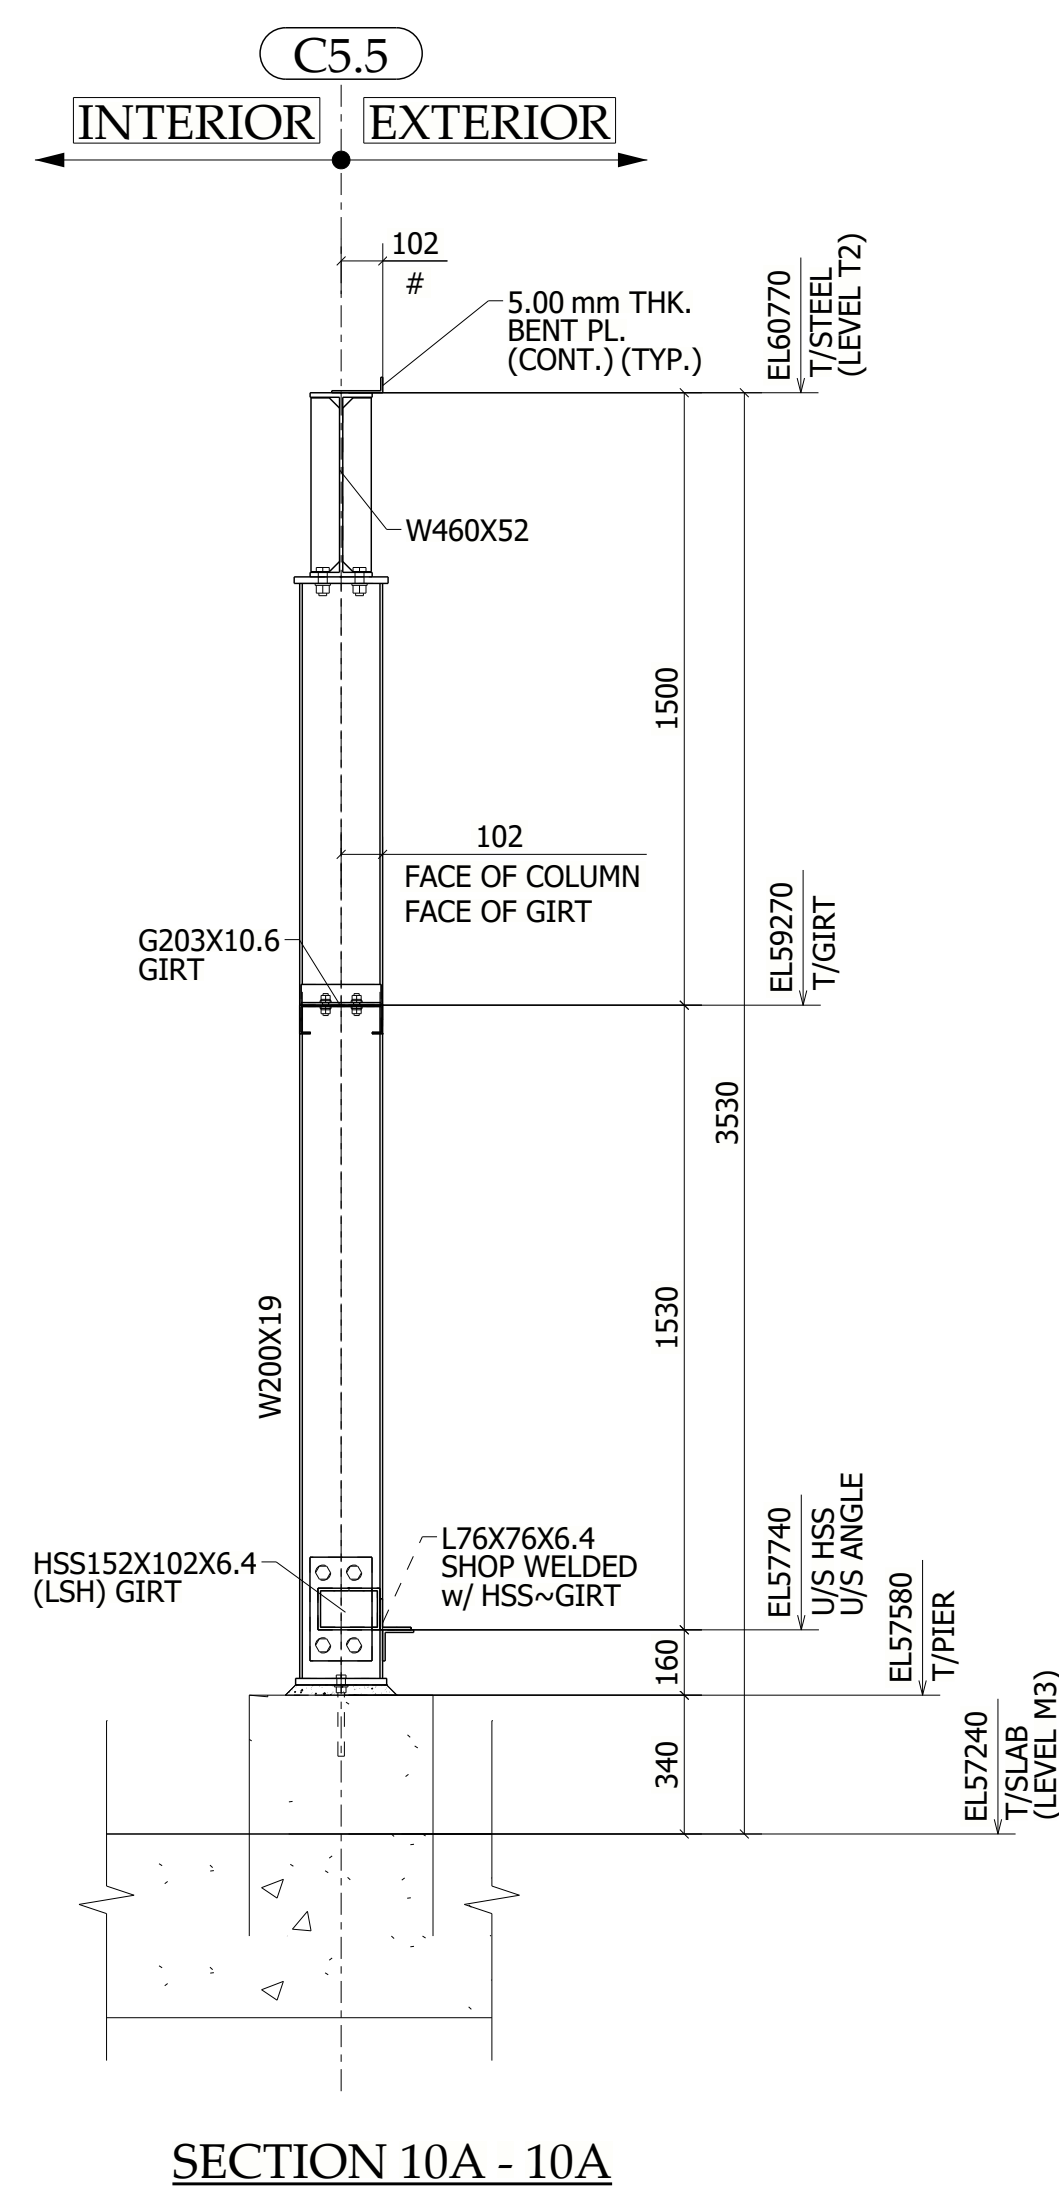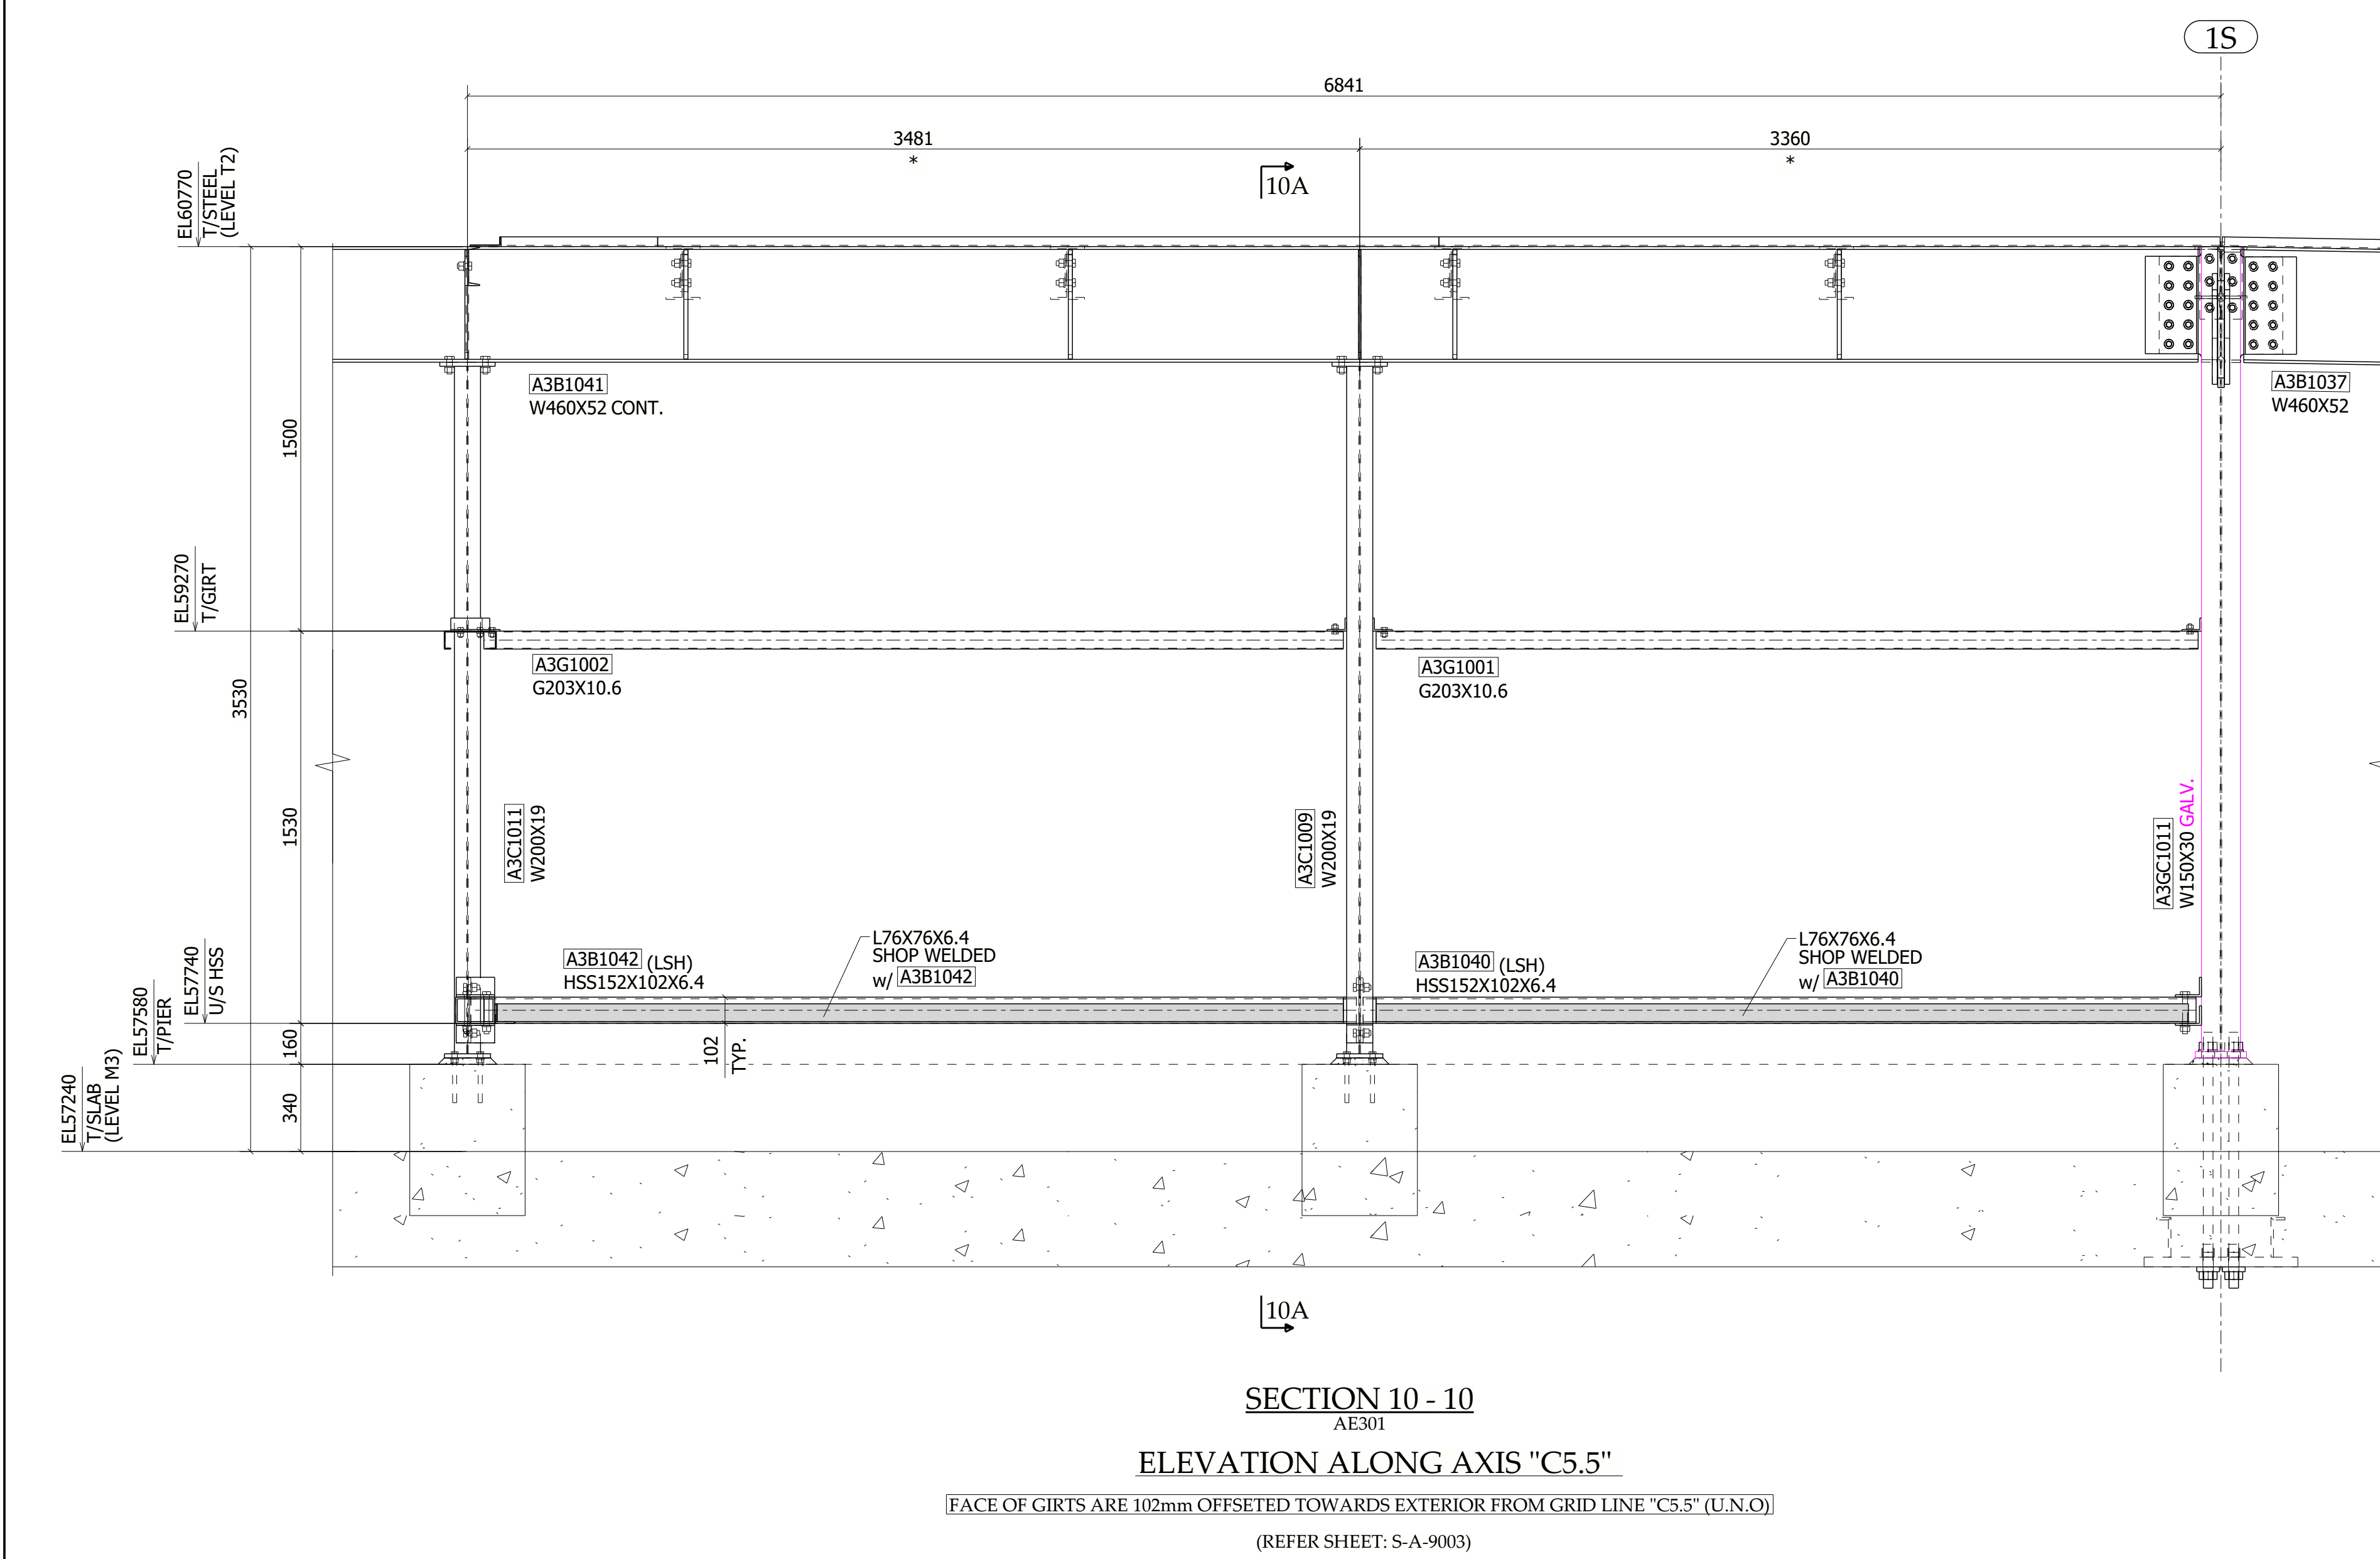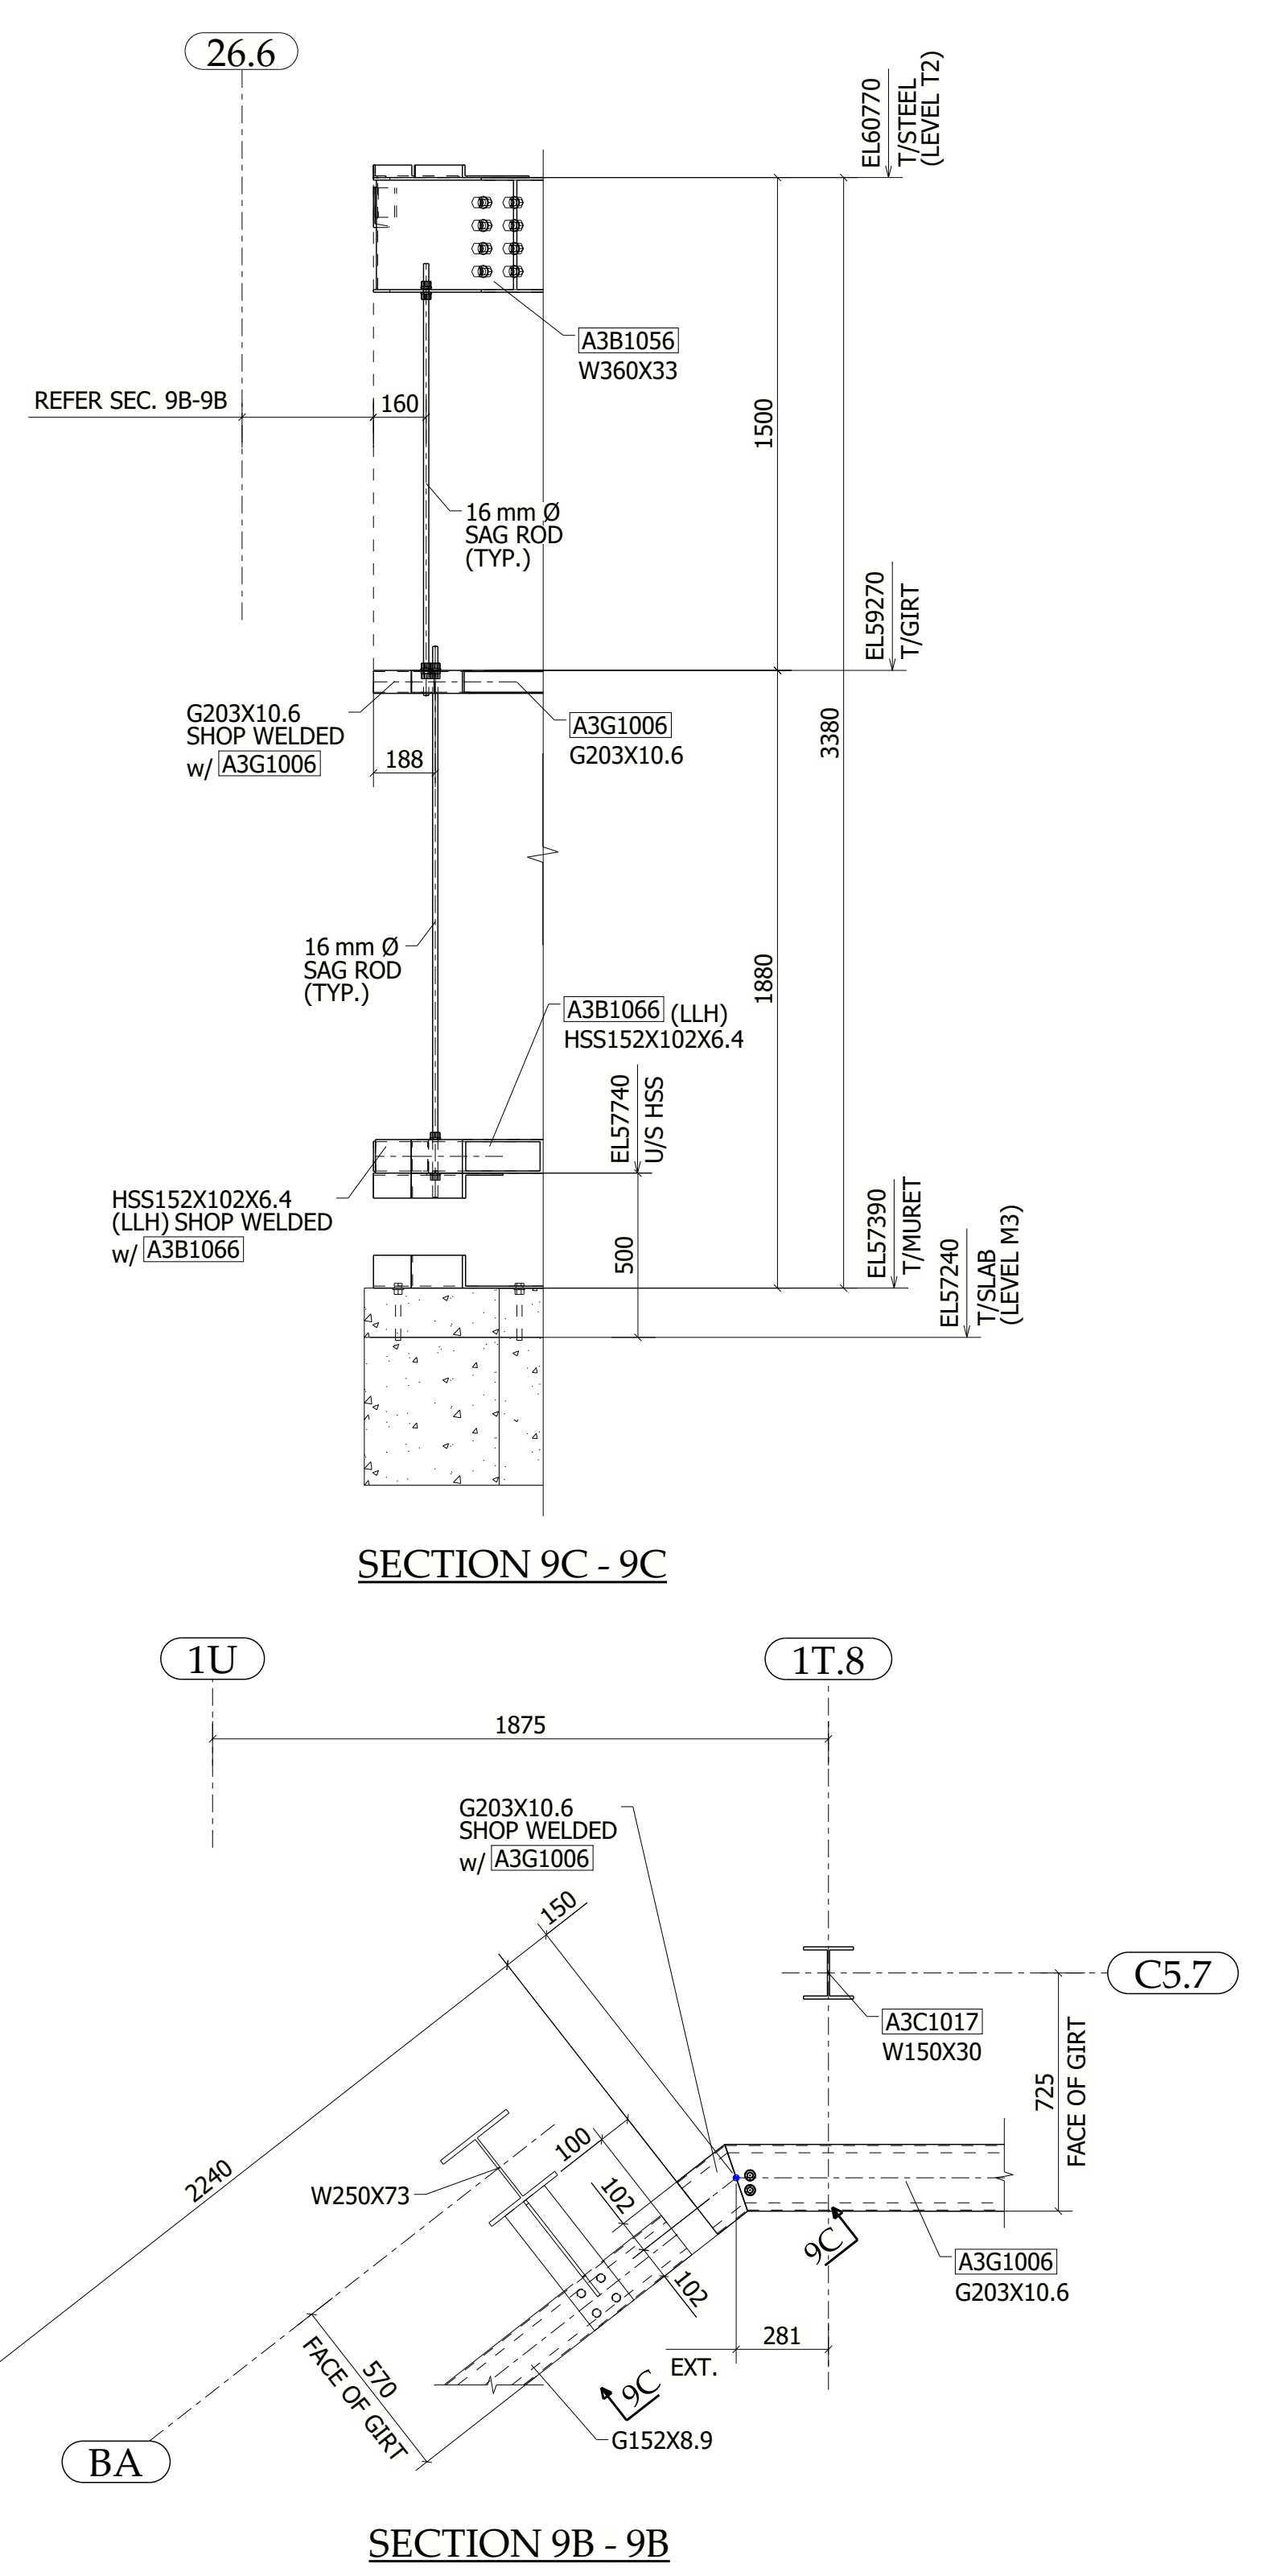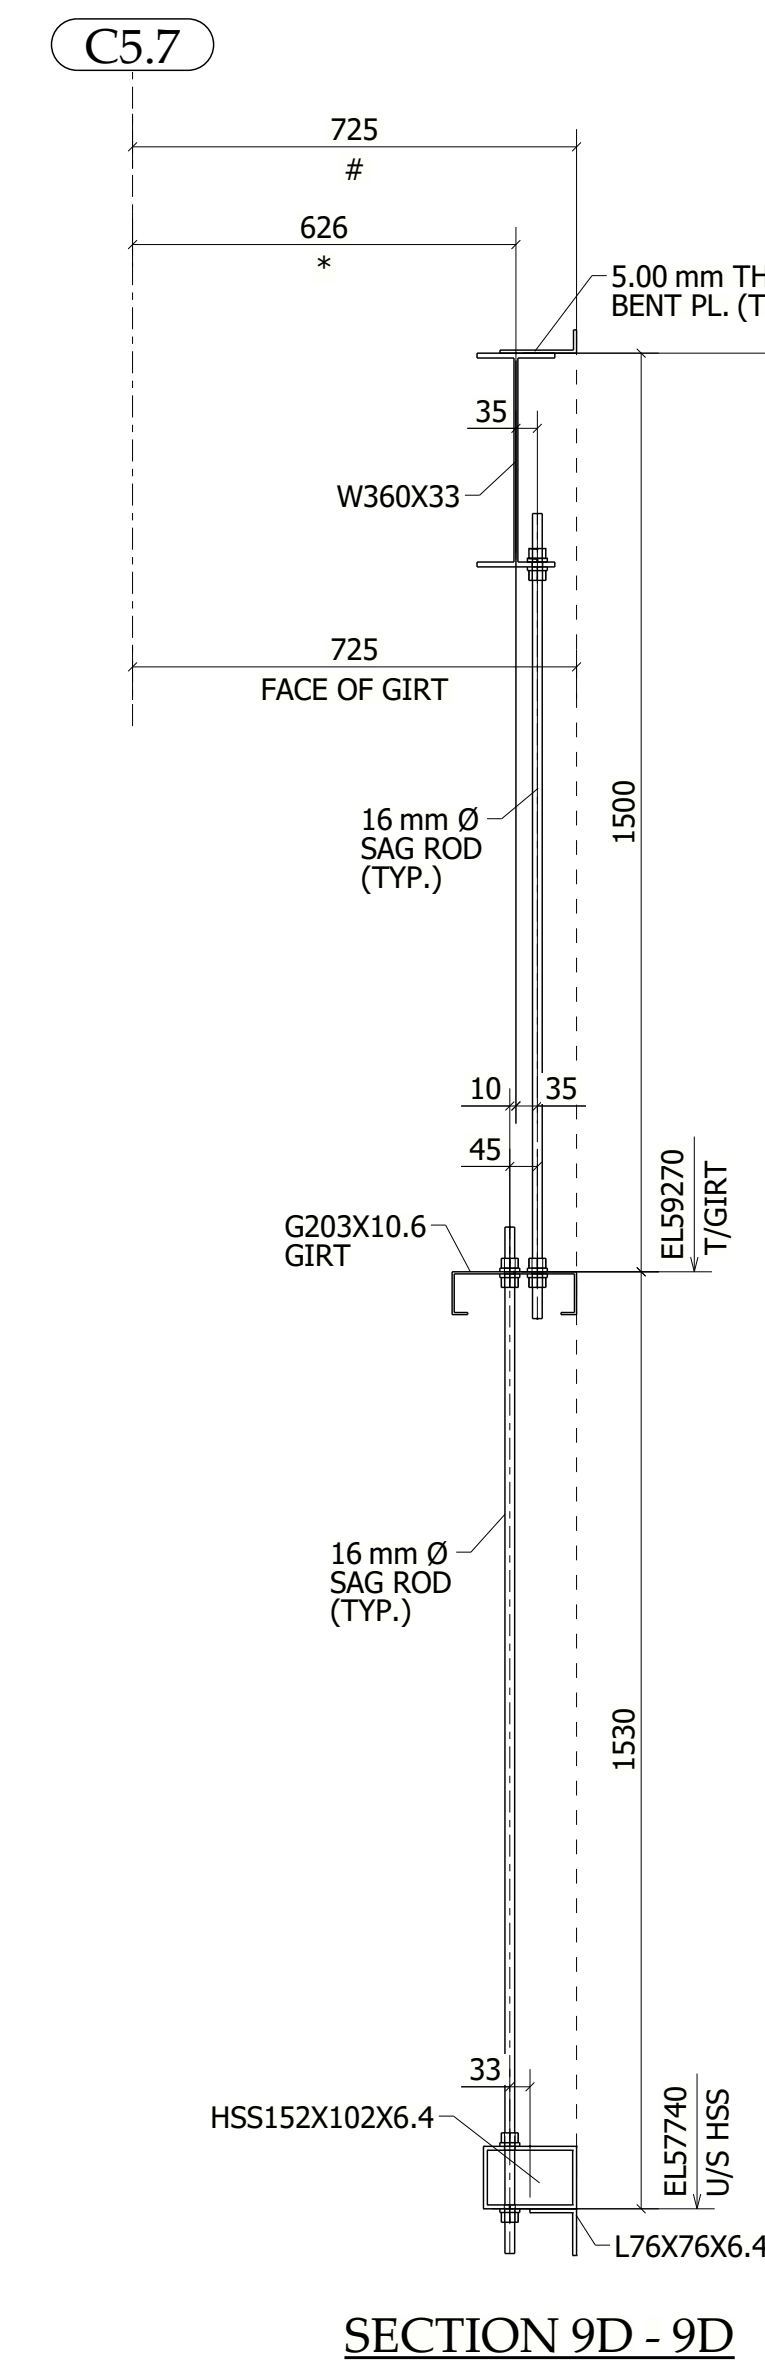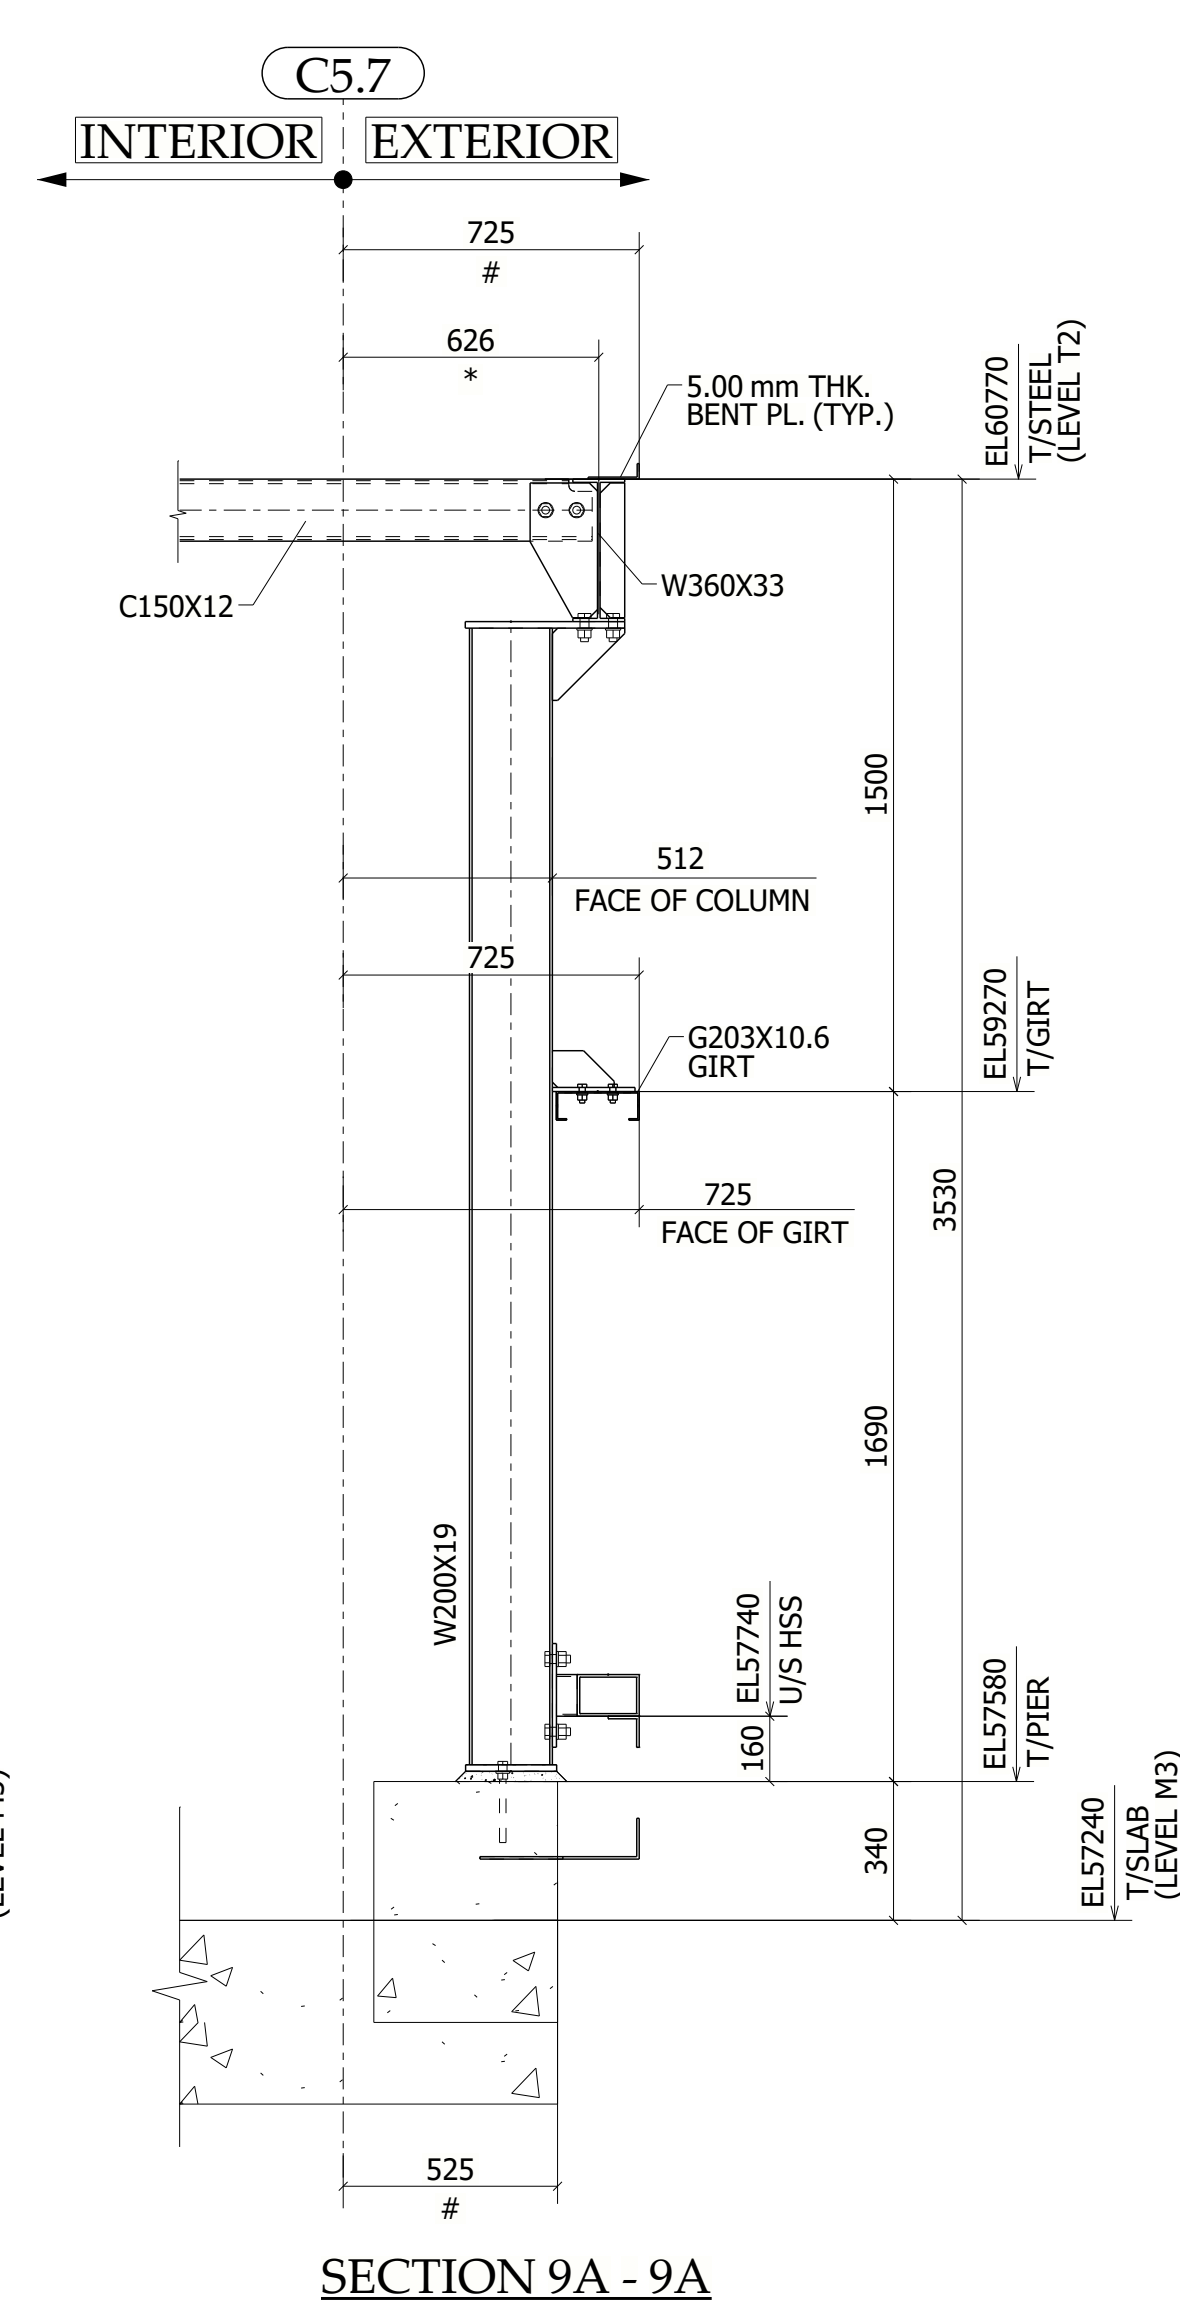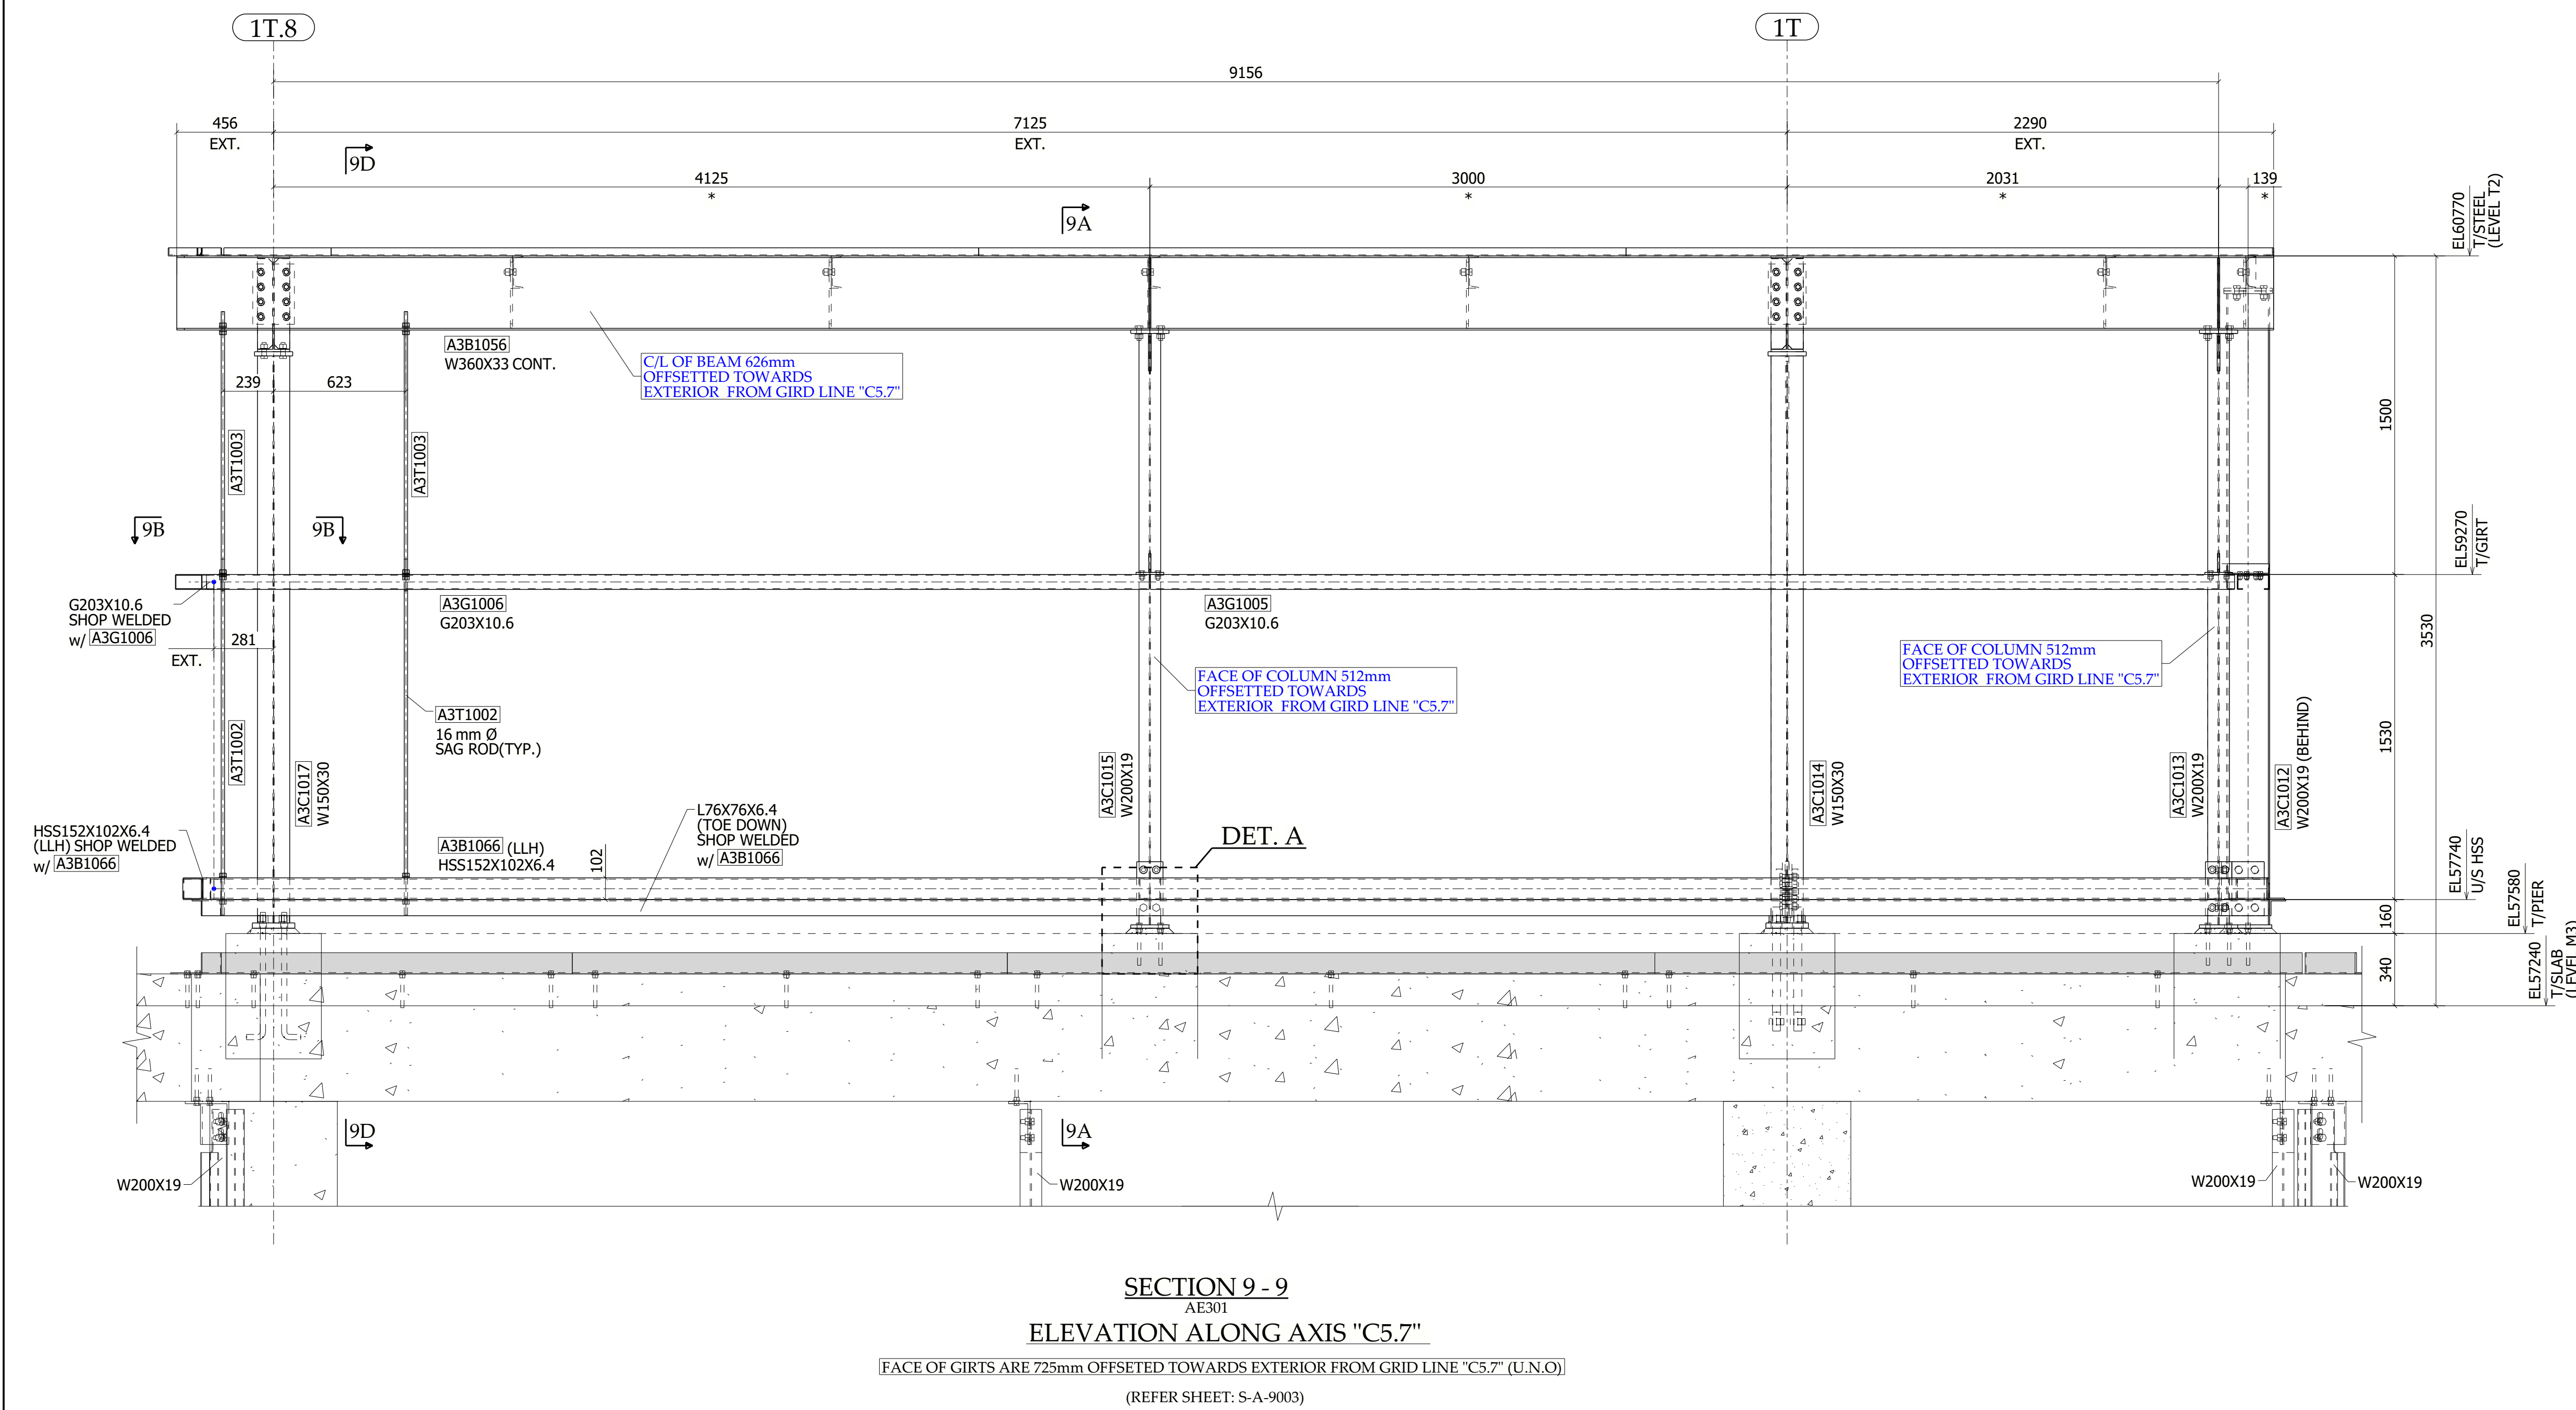


DATE	NO	DESCRIPTION	PAR
02/06/2003	1	FOR FIELD USE	PAR
10/31/2002	2	FOR APPROVAL	PERITURE

GRADE ACHER	350W	S.I.C.
ELECTRICALS	E48XX	S.I.C.
WOODCORE	6mm	S.I.C.
THICK	220	S.I.C.
BOULDER	A32N	S.I.C.
PRIMER	1-73A	S.I.C.

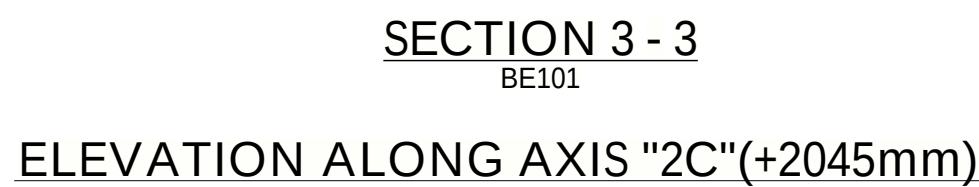


(REFER SHEET: S-B-9001)

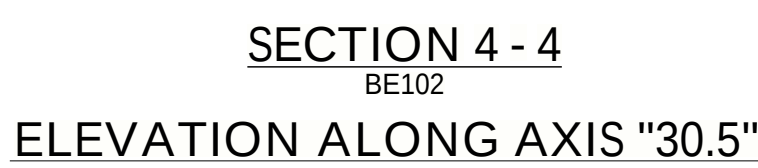


(REFER SHEET: S-B-9002)




DATE	NO.	DESCRIPTION	PAR	TRC05 220	S.I.C.
01/11/2023		FOR FIELD USE		BOULONS A325N	S.I.C.
12/21/2022		FOR FIELD USE		PEINTURE	
11/18/2022		FOR APPROVAL		1-73# SHOP PRIMER	S.I.C.

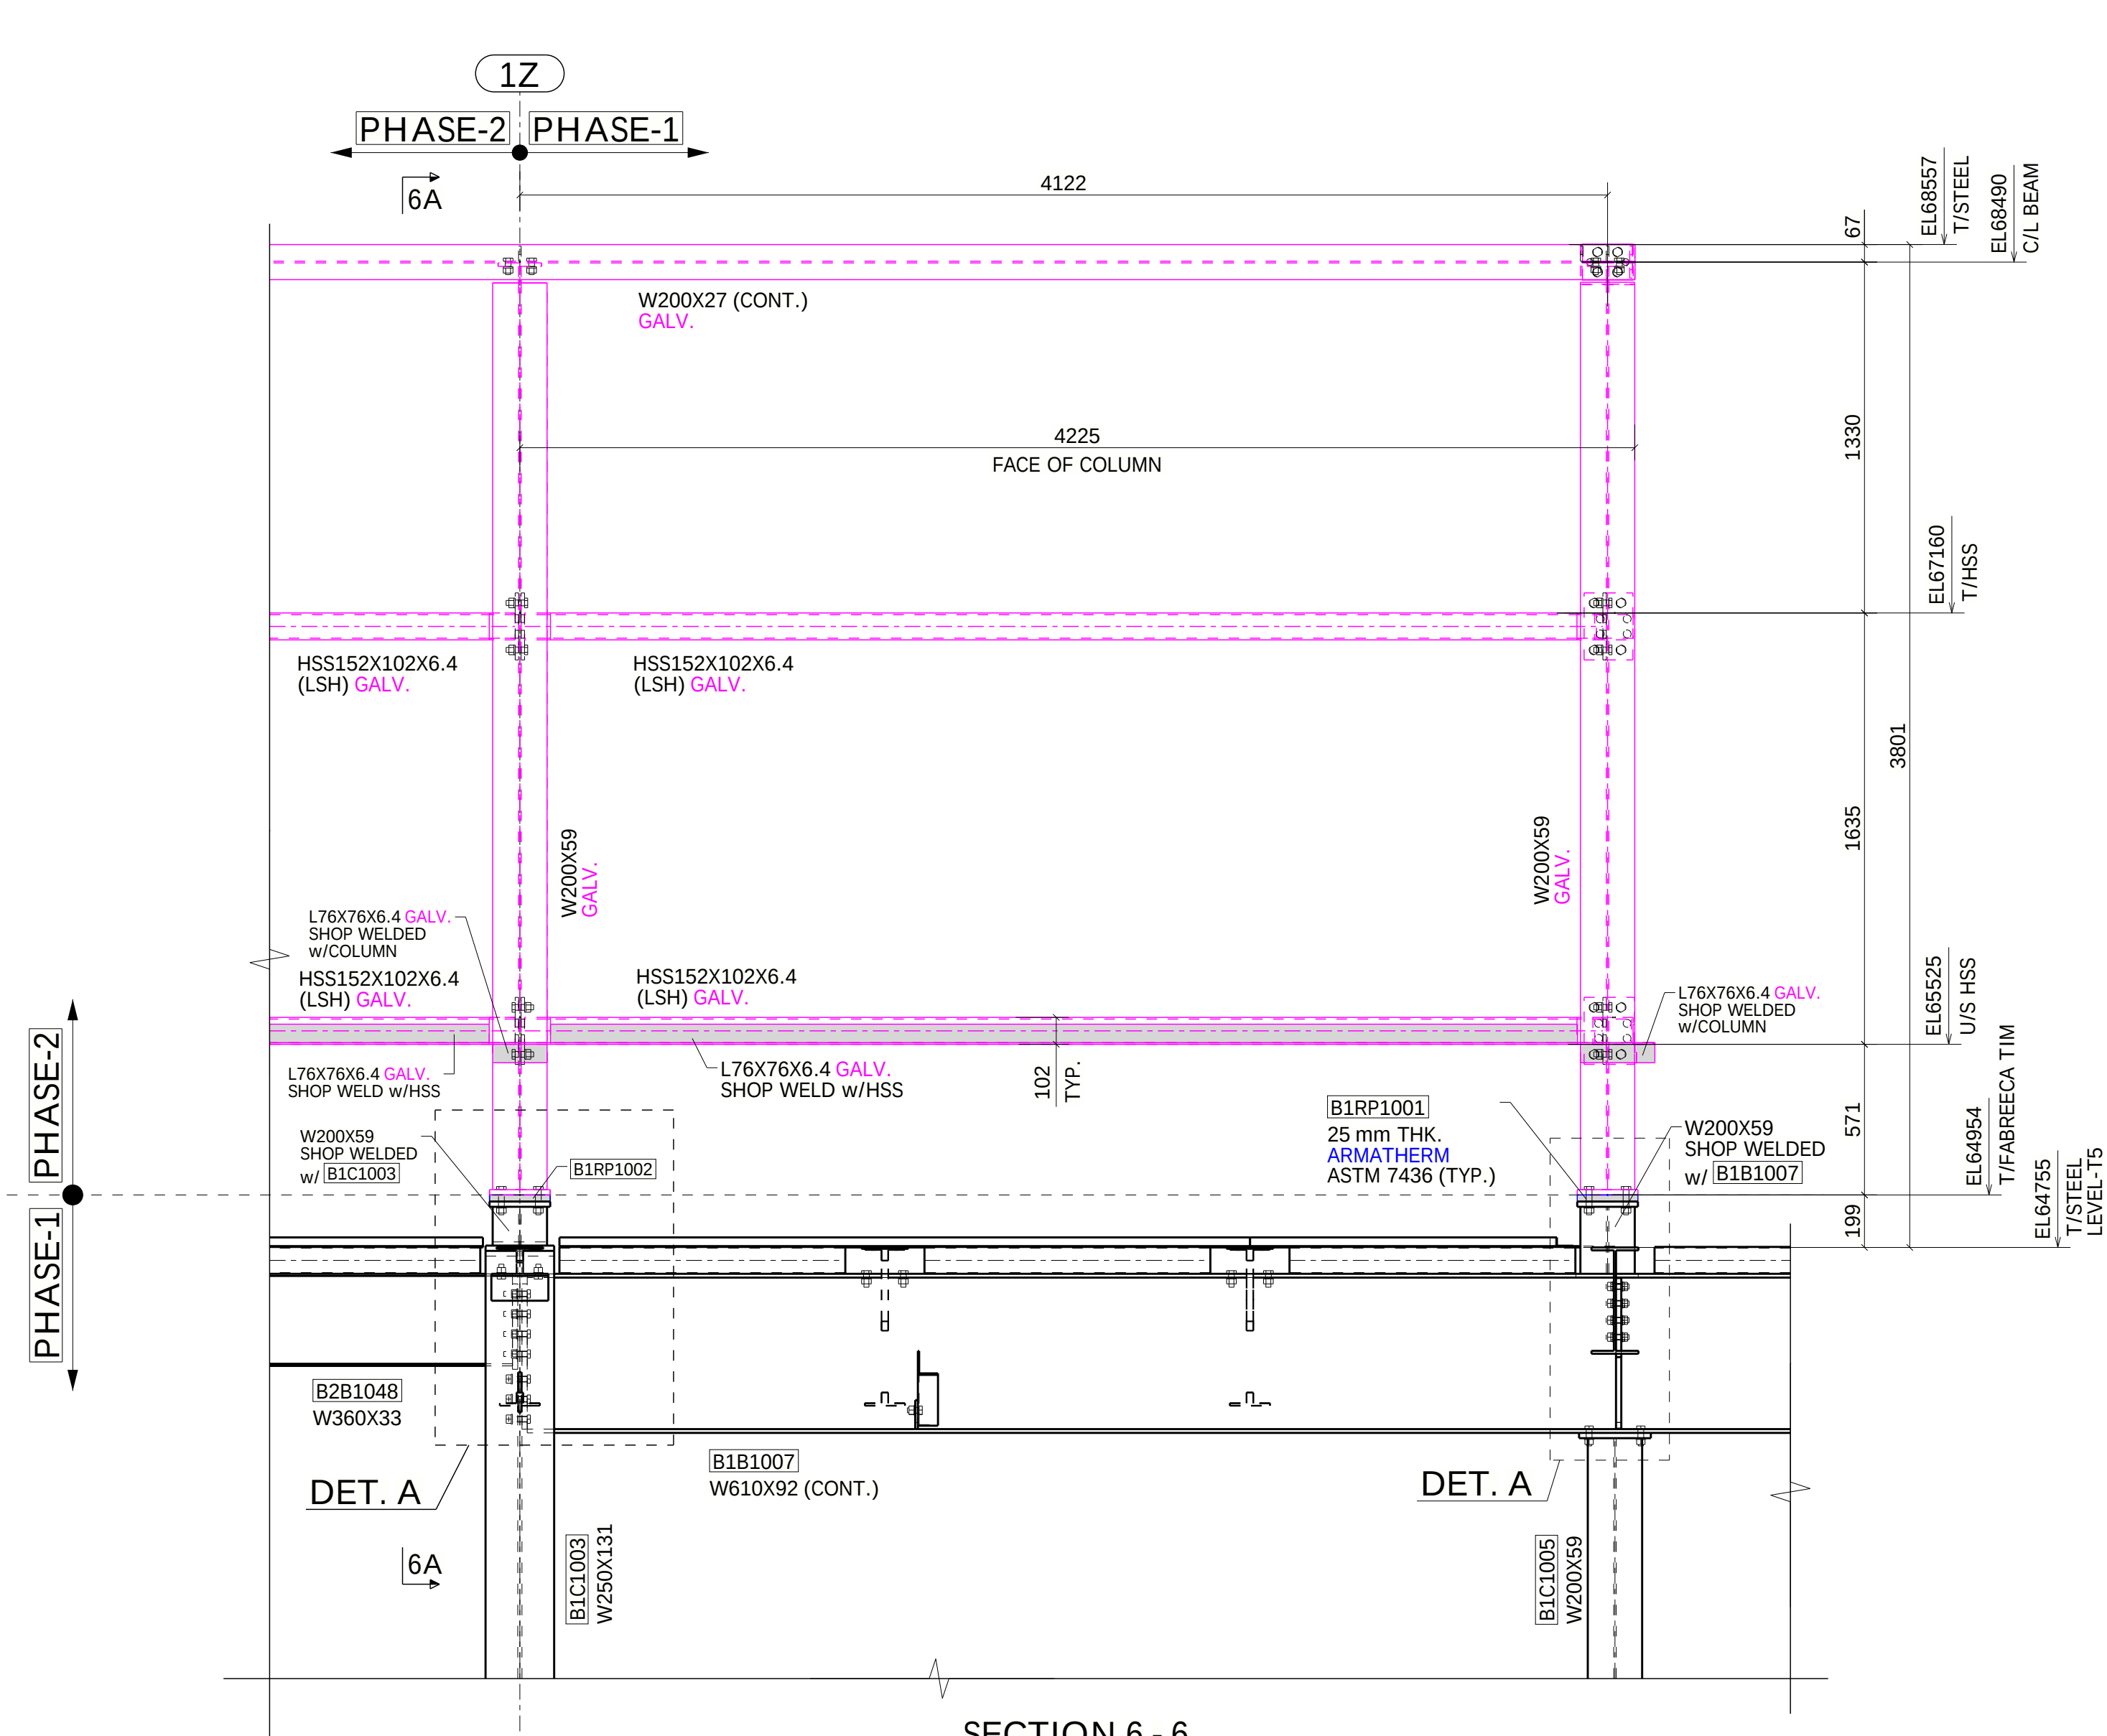


SECTION 6 - 6
ELEVATION ALONG AXIS "B9"
FACE OF GIRTS ARE 75mm OFFSETED TOWARDS EXTERIOR FROM GRID LINE "B9" (U.N.O)

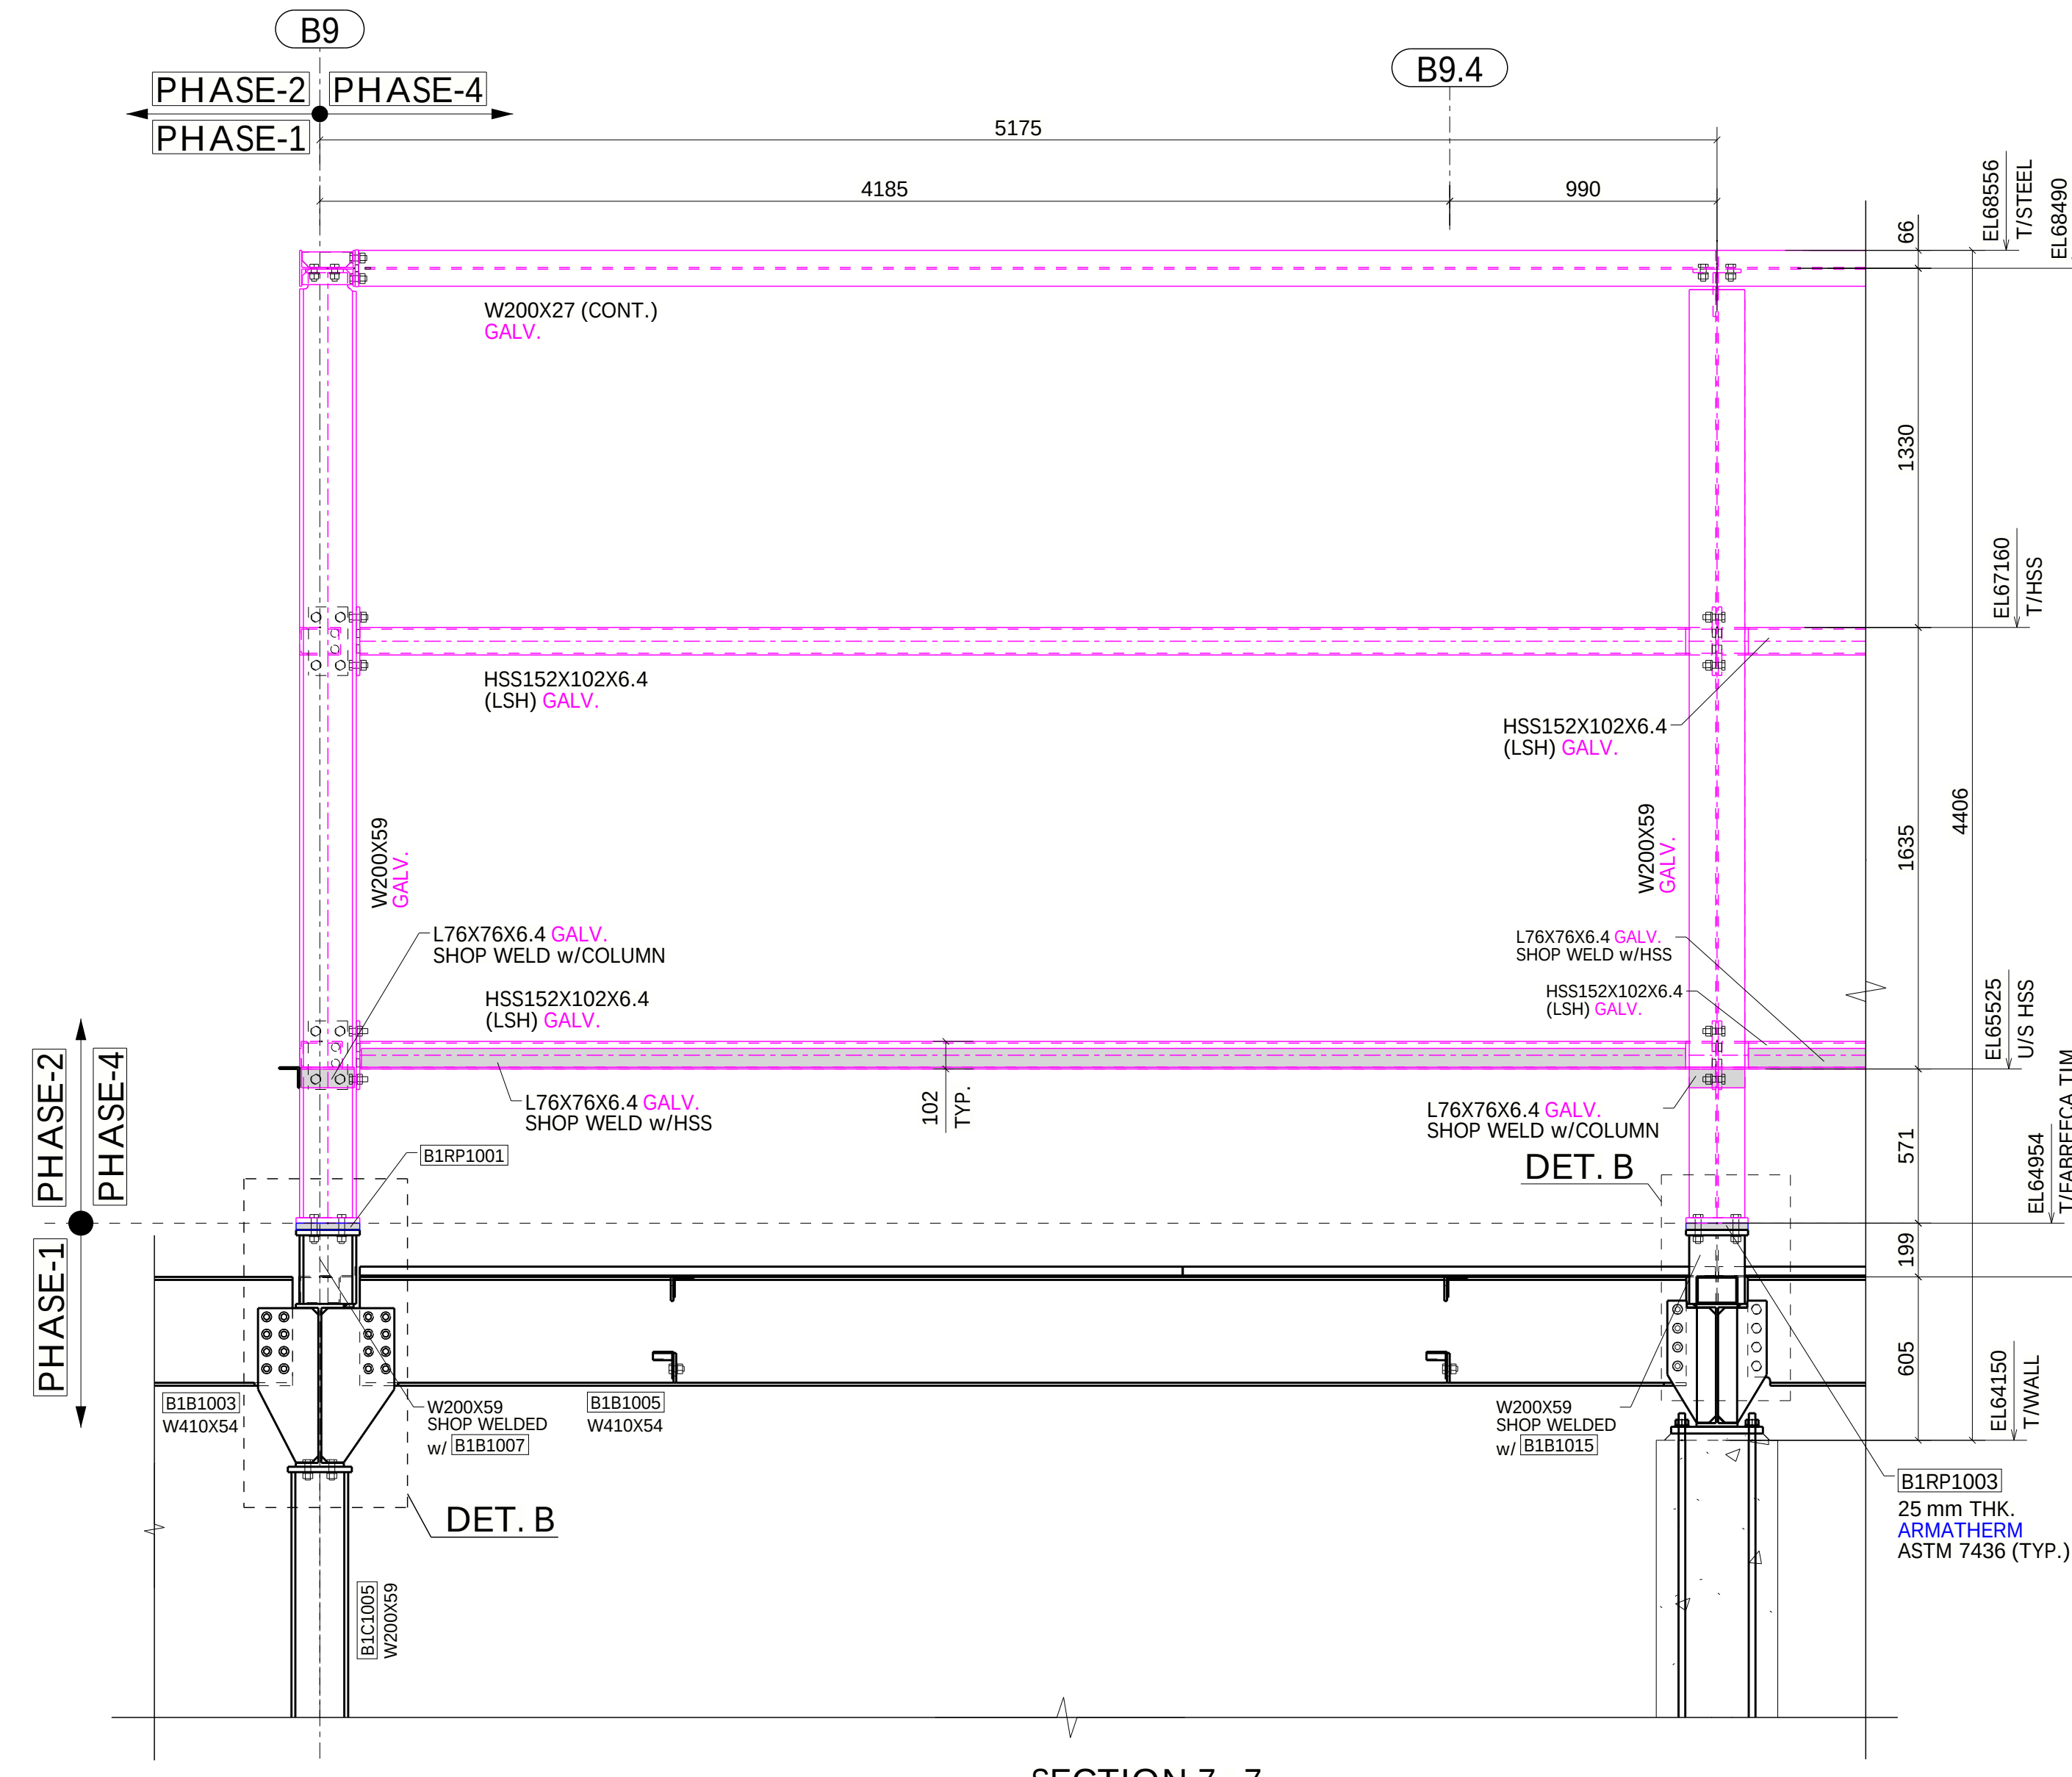


SECTION 7 - 7
ELEVATION ALONG AXIS "1Z" (+4150mm)
FACE OF GIRTS ARE 425mm OFFSETED TOWARDS EXTERIOR FROM GRID LINE "1Z" (U.N.O)
(REFER SHEET: S-B-9001)

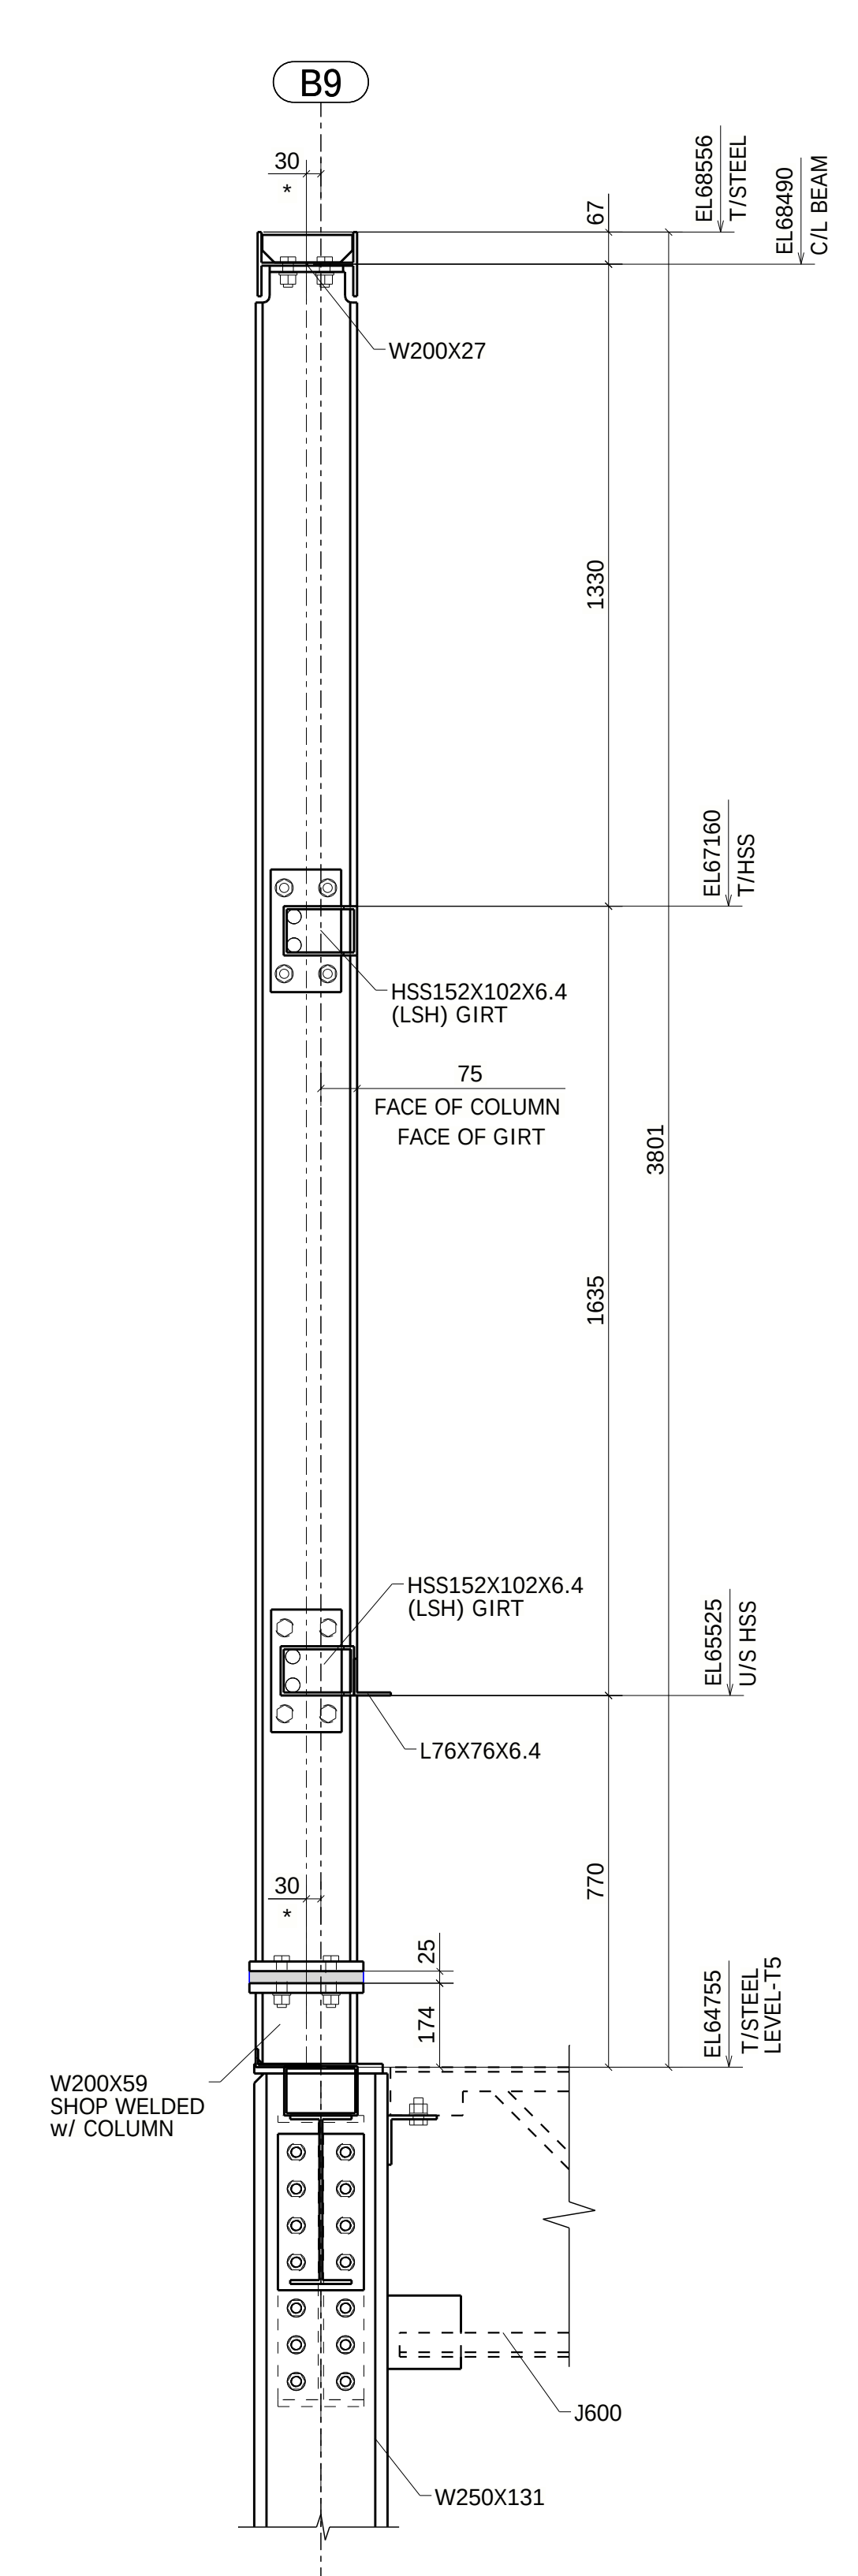

SECTION 6A - 6A

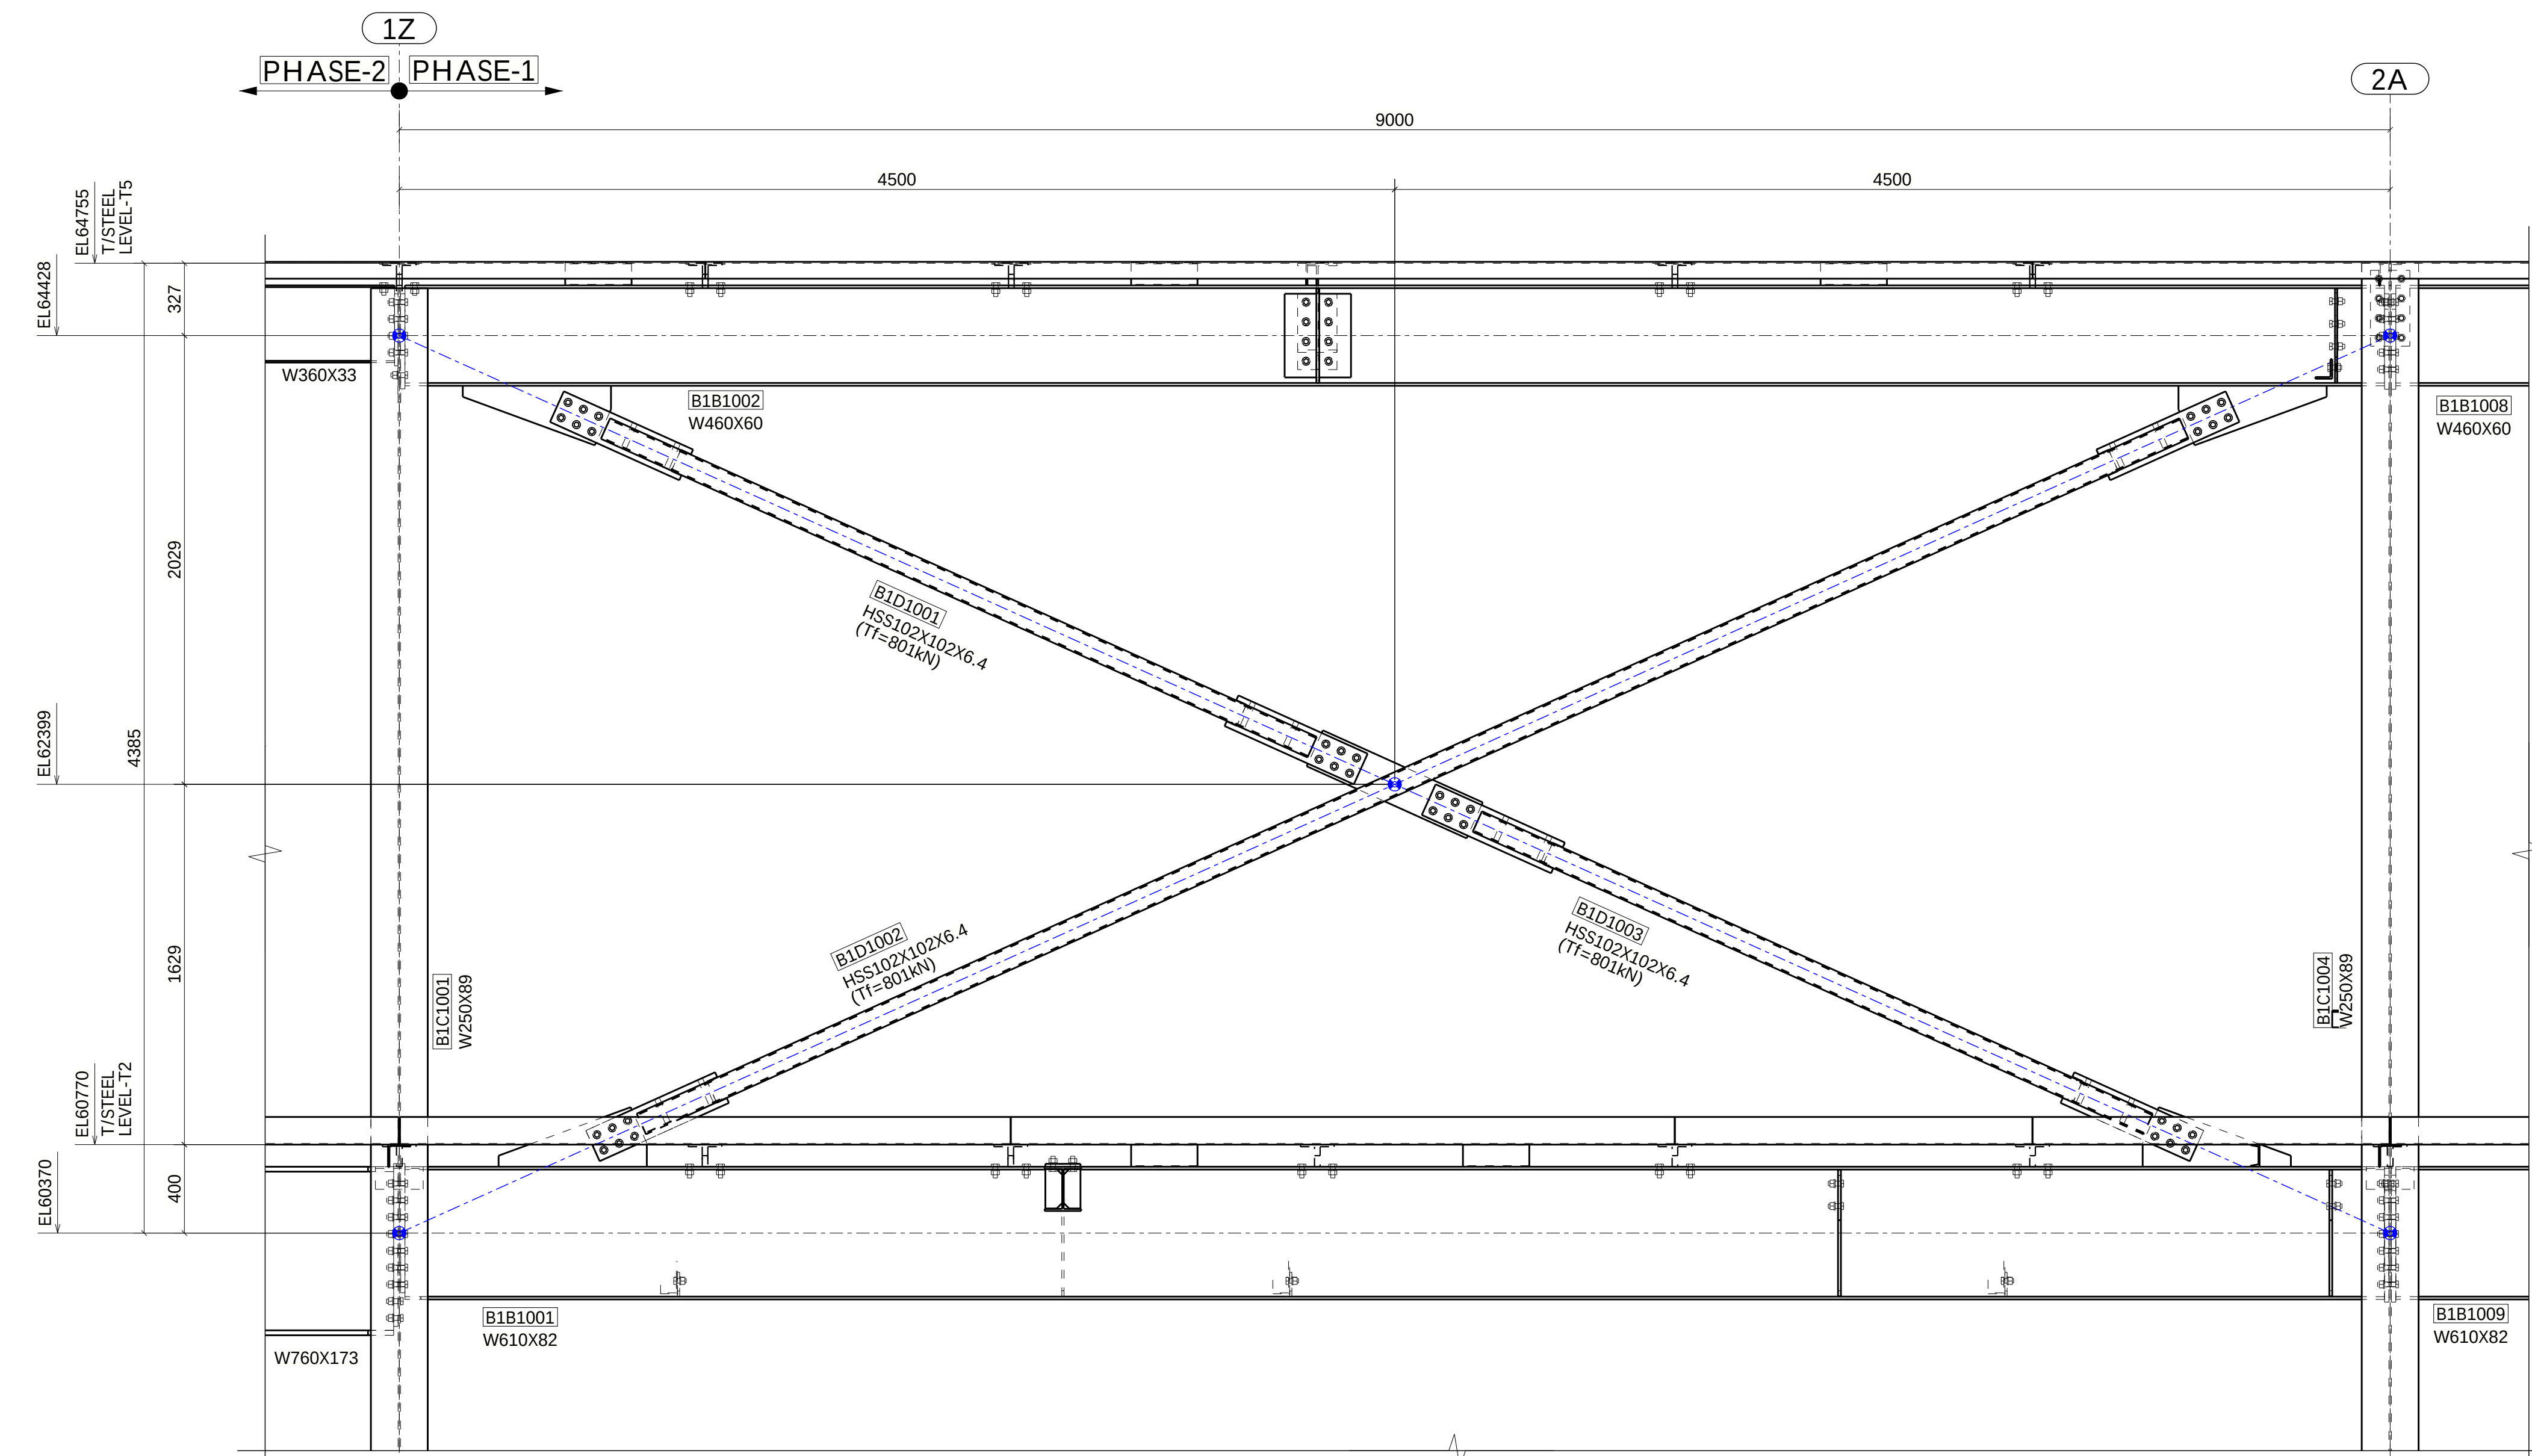


BRACING ELEVATION ALONG AXIS "B8.1"
(REFER SHEET: S-B-9001)
(MEMBERS ARE HIDDEN FOR CLARITY)

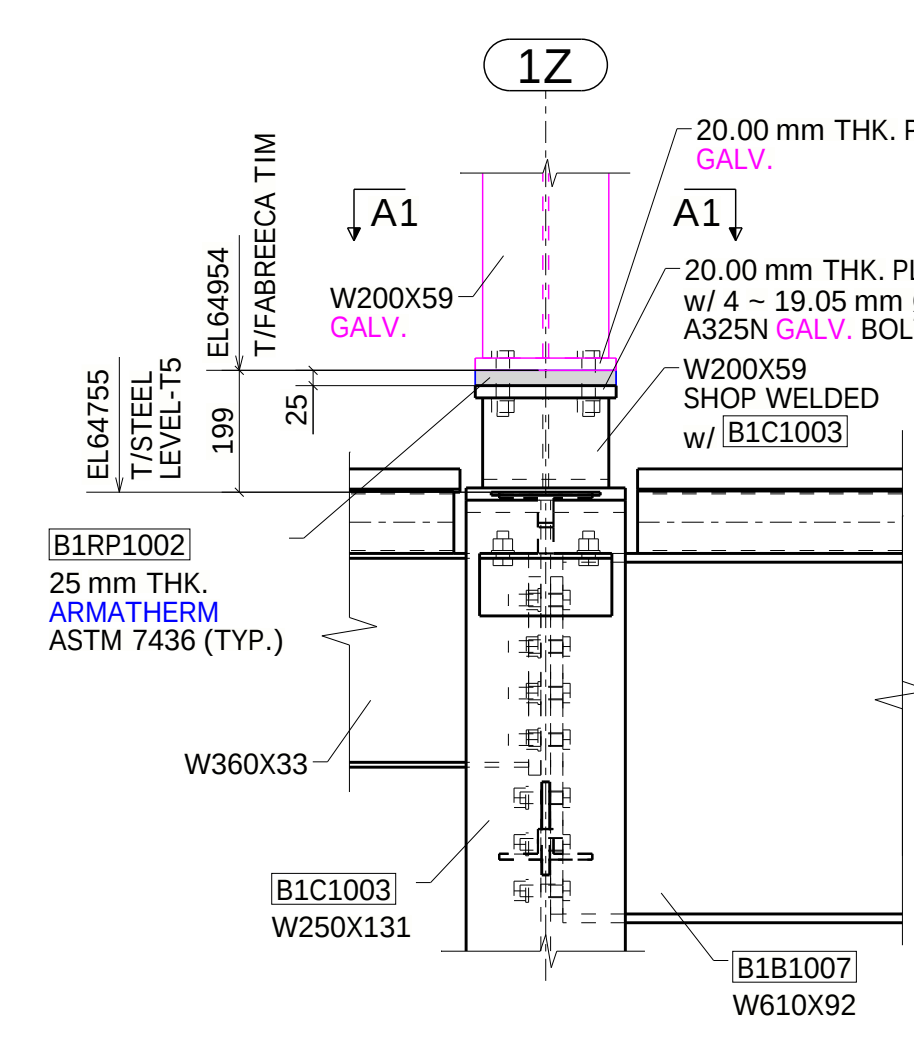

DETAIL - A

SECTION A1 - A1

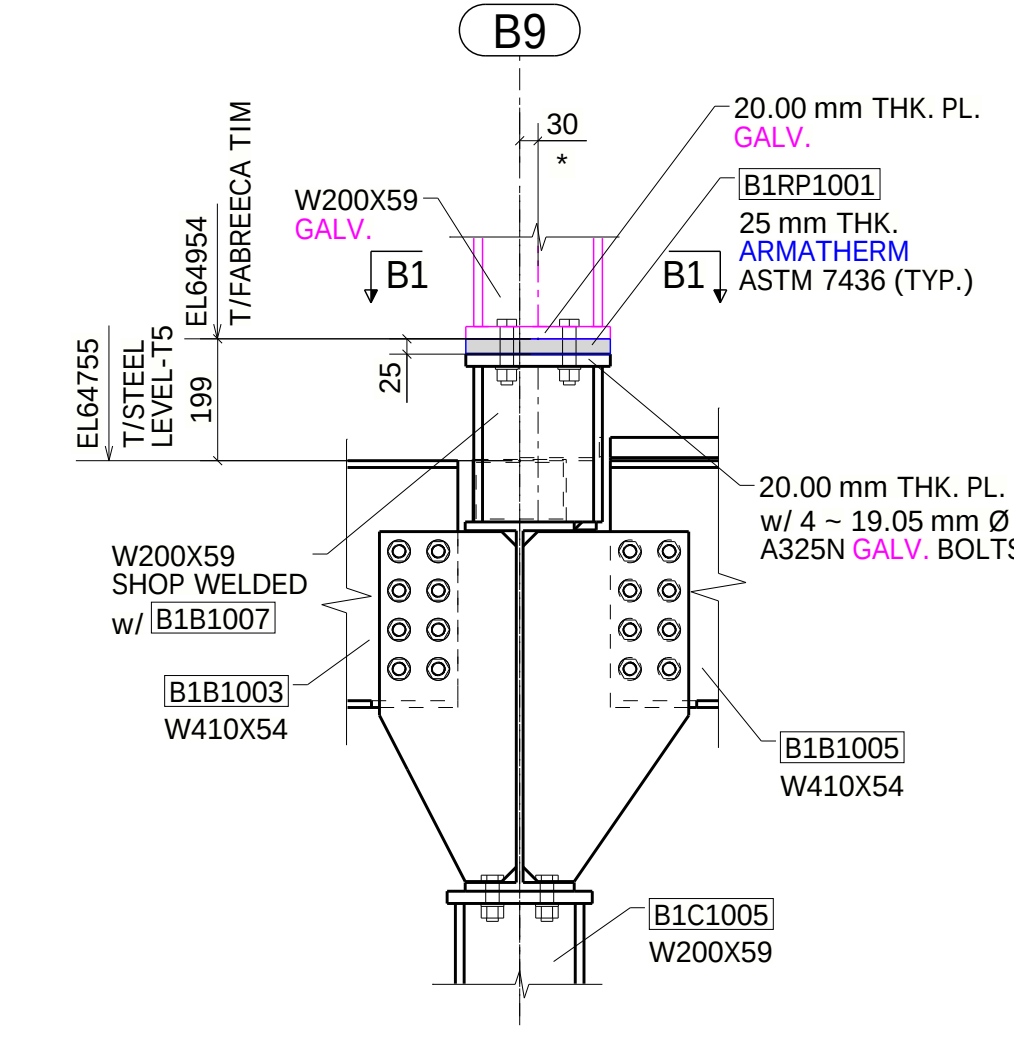


DETAIL - B

SECTION B1 - B1

DATE	NO.	DESCRIPTION	PAR.
01/11/2023	1	FOR FIELD USE	
02/11/2023	2	FOR FIELD USE	
11/18/2023	3	FOR APPROVAL	

GRADE ACHER	350W	S.I.C.
ELECTRICALS	E48XX	S.I.C.
WOODWORK	6mm	S.I.C.
TRUCK	220	S.I.C.
BOULDER	A32N	S.I.C.
PAINTURE	1-73A SHOP PRIMER	S.I.C.

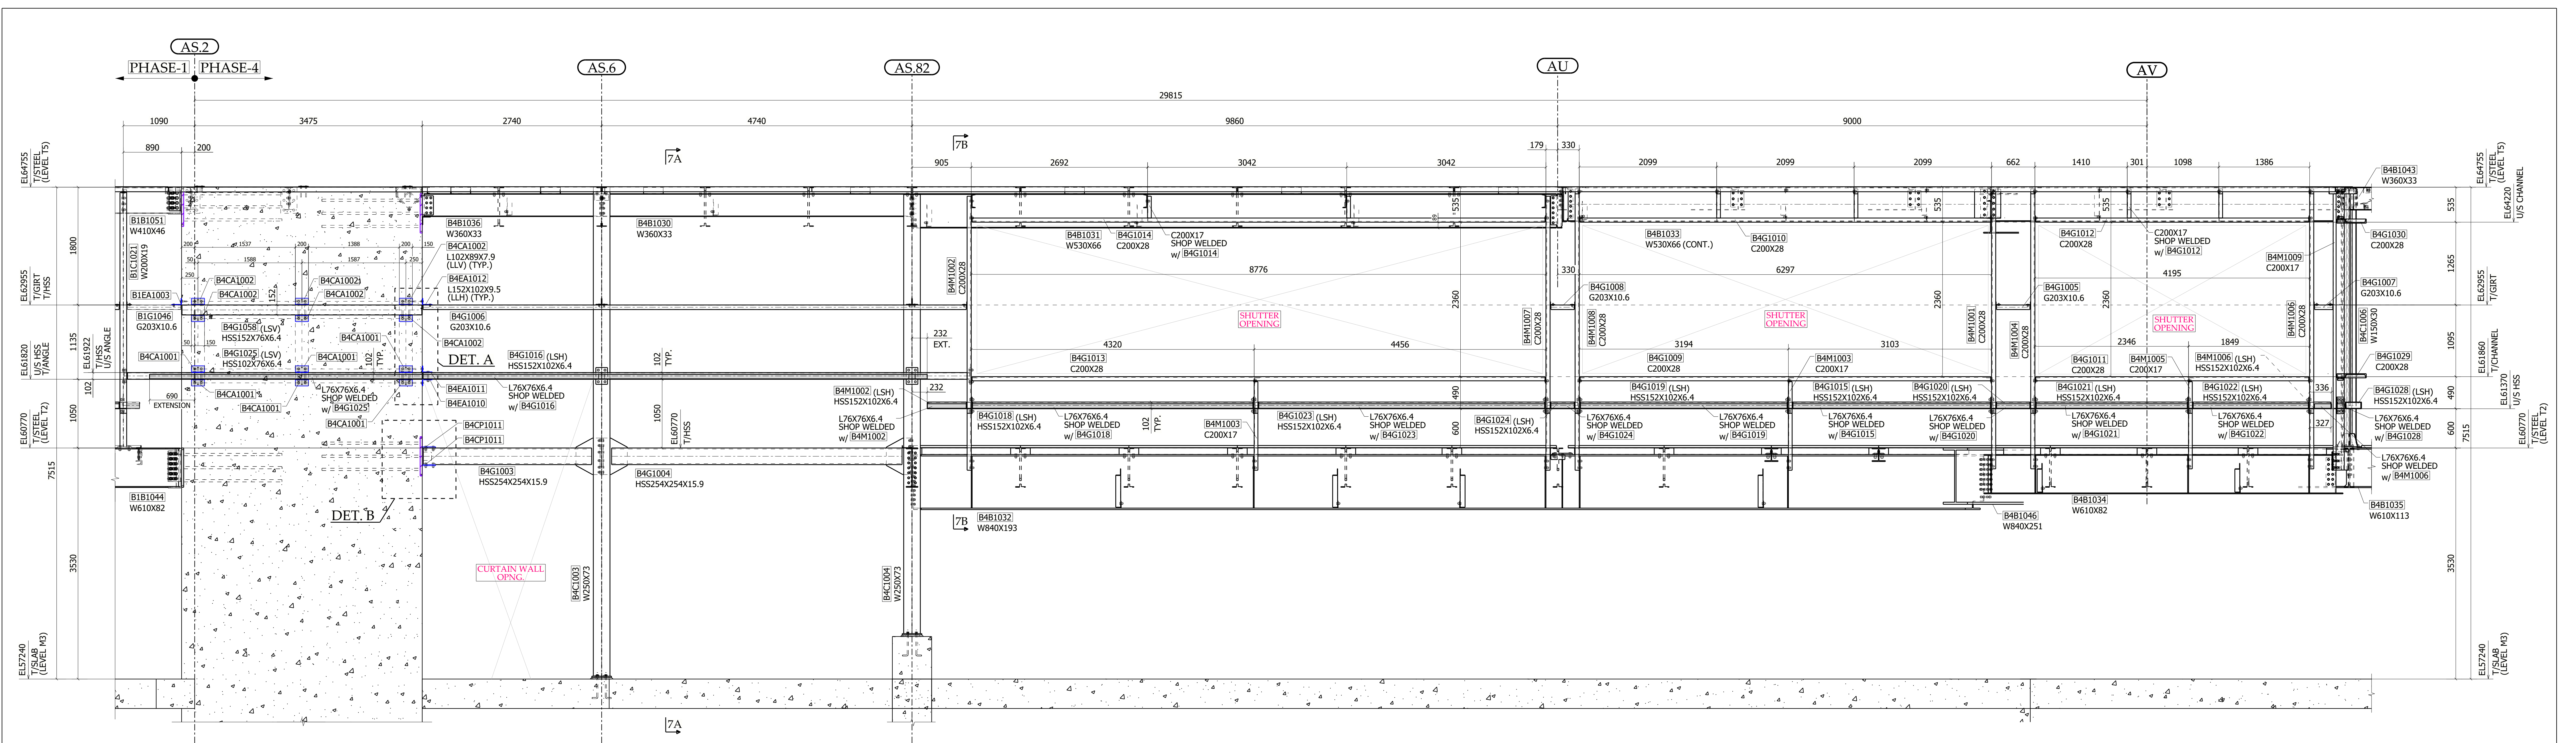


SECTION 7-7

GIRT ELEVATION ALONG AXIS "30.4"



[FACE OF GIRTS ARE 490mm OFFSETED TOWARDS EXTERIOR FROM GRID LINE "30.4" (U.N.O.)

(REFER SHEET: S-B-9002)

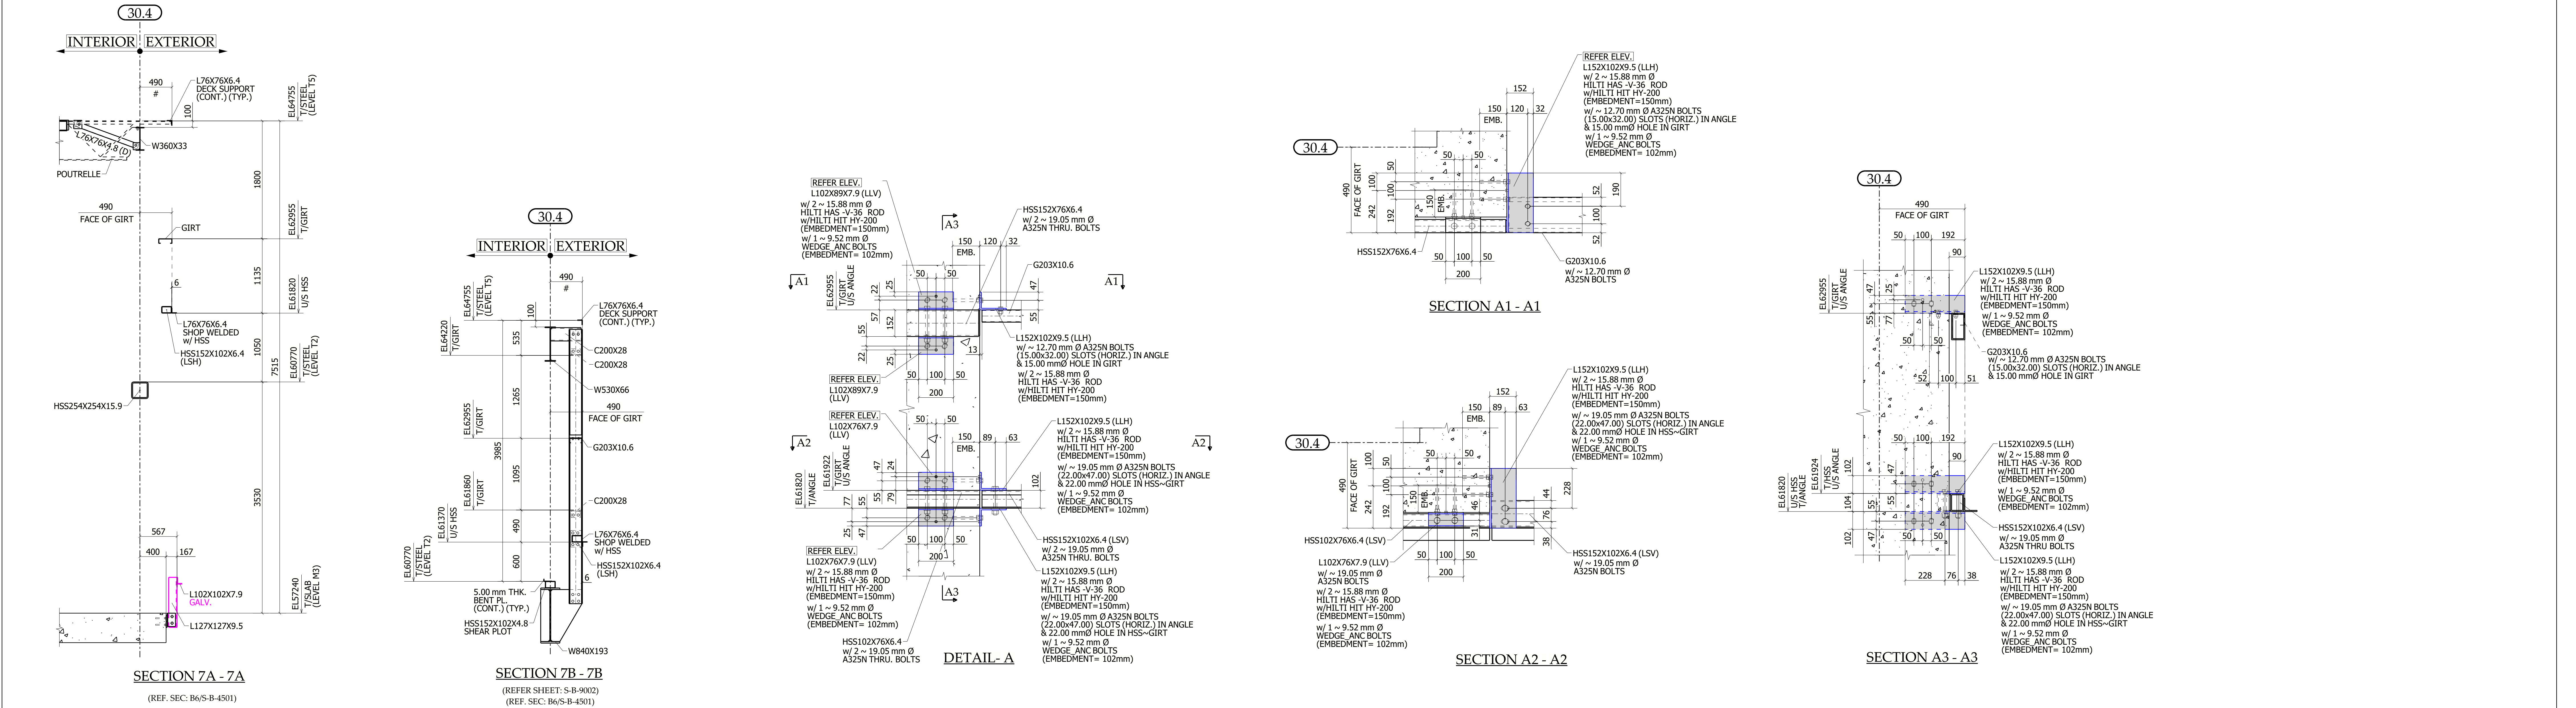

DATE	NO.	DESCRIPTION	PAR.
01/26/2023	1	FOR FIELD USE	
12/13/2022	2	FOR APPROVAL	


GRADE ACHIER	S.I.C.
350W	
ELECTRICALS	S.I.C.
E48XX	
BRICKS	S.I.C.
6mm	
THICK	S.I.C.
220	
BOULDER	S.I.C.
A32N	
PERITURE	S.I.C.
1-73A SHOP PRIMER	

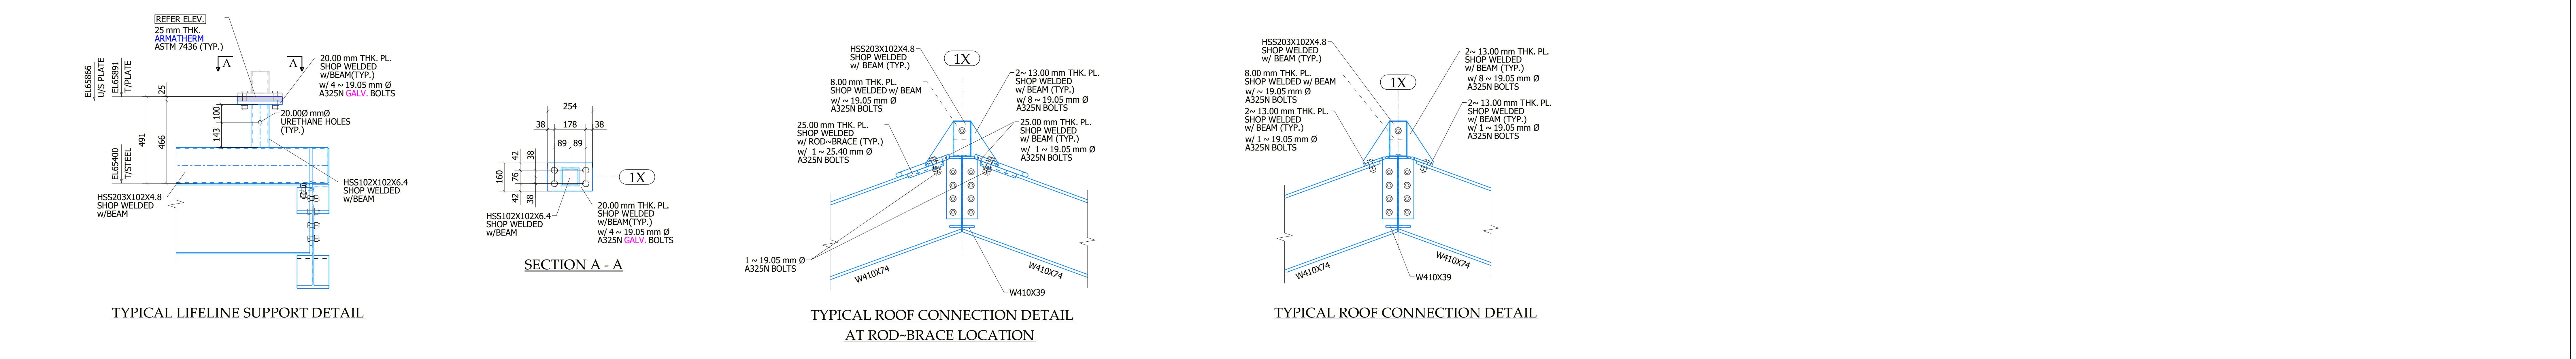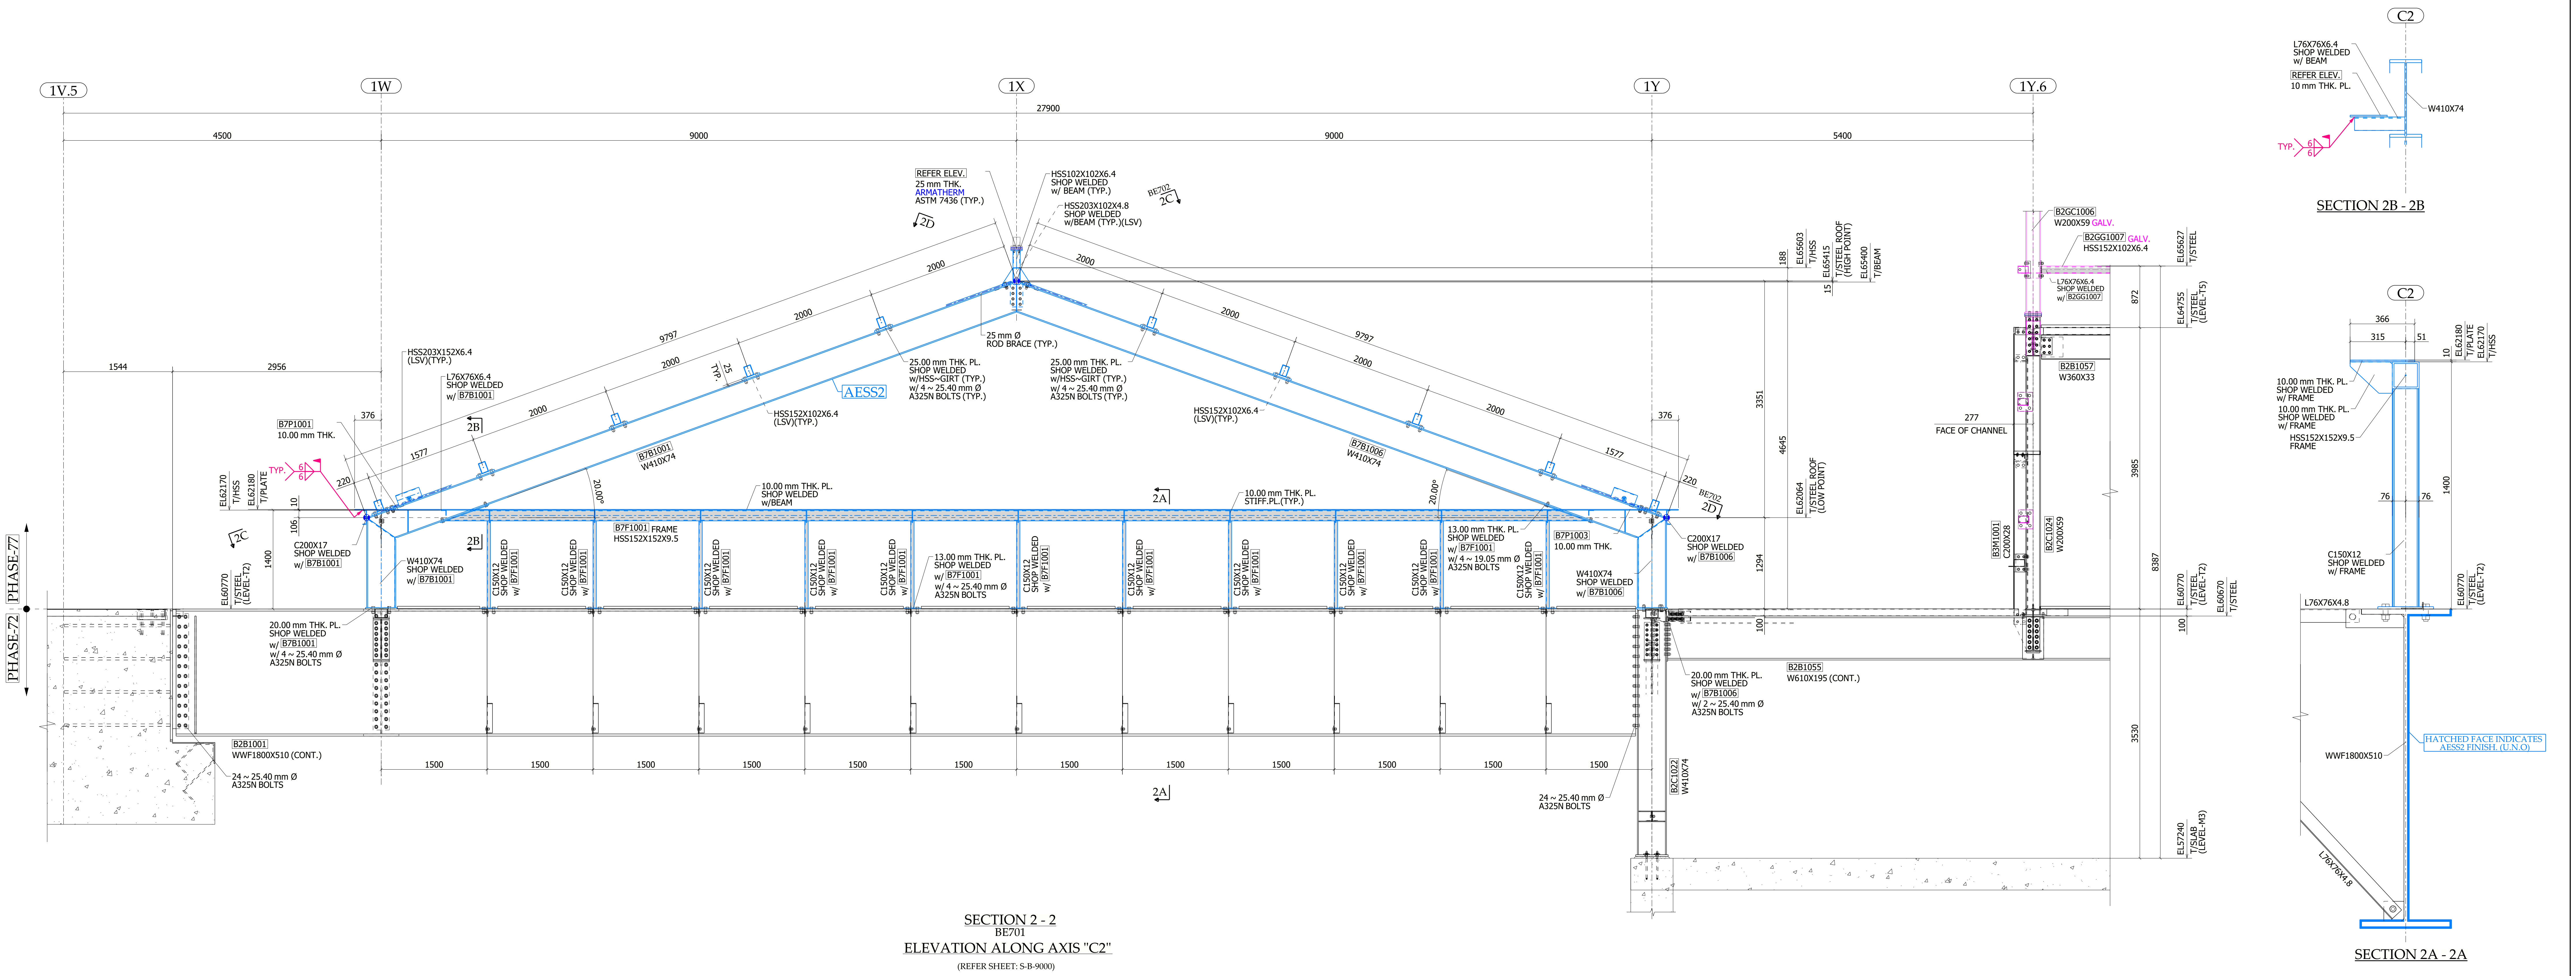


STEELS ABOVE ELEVATION 60770mm ARE RECEIVED AESS2

DATE	NO	DESCRIPTION	PAR	REVISION
01/28/2023	1	FOR FIELD USE		
01/05/2023	2	FOR APPROVAL		

GRADE AZHUR	350W	S.I.C.
ELECTRICAL	E48XX	S.I.C.
ROOFING	6mm	S.I.C.
TRUSS	220	S.I.C.
BOLTS	A325N	S.I.C.
PAINTURE	1-73A SHOP PRIMER	S.I.C.

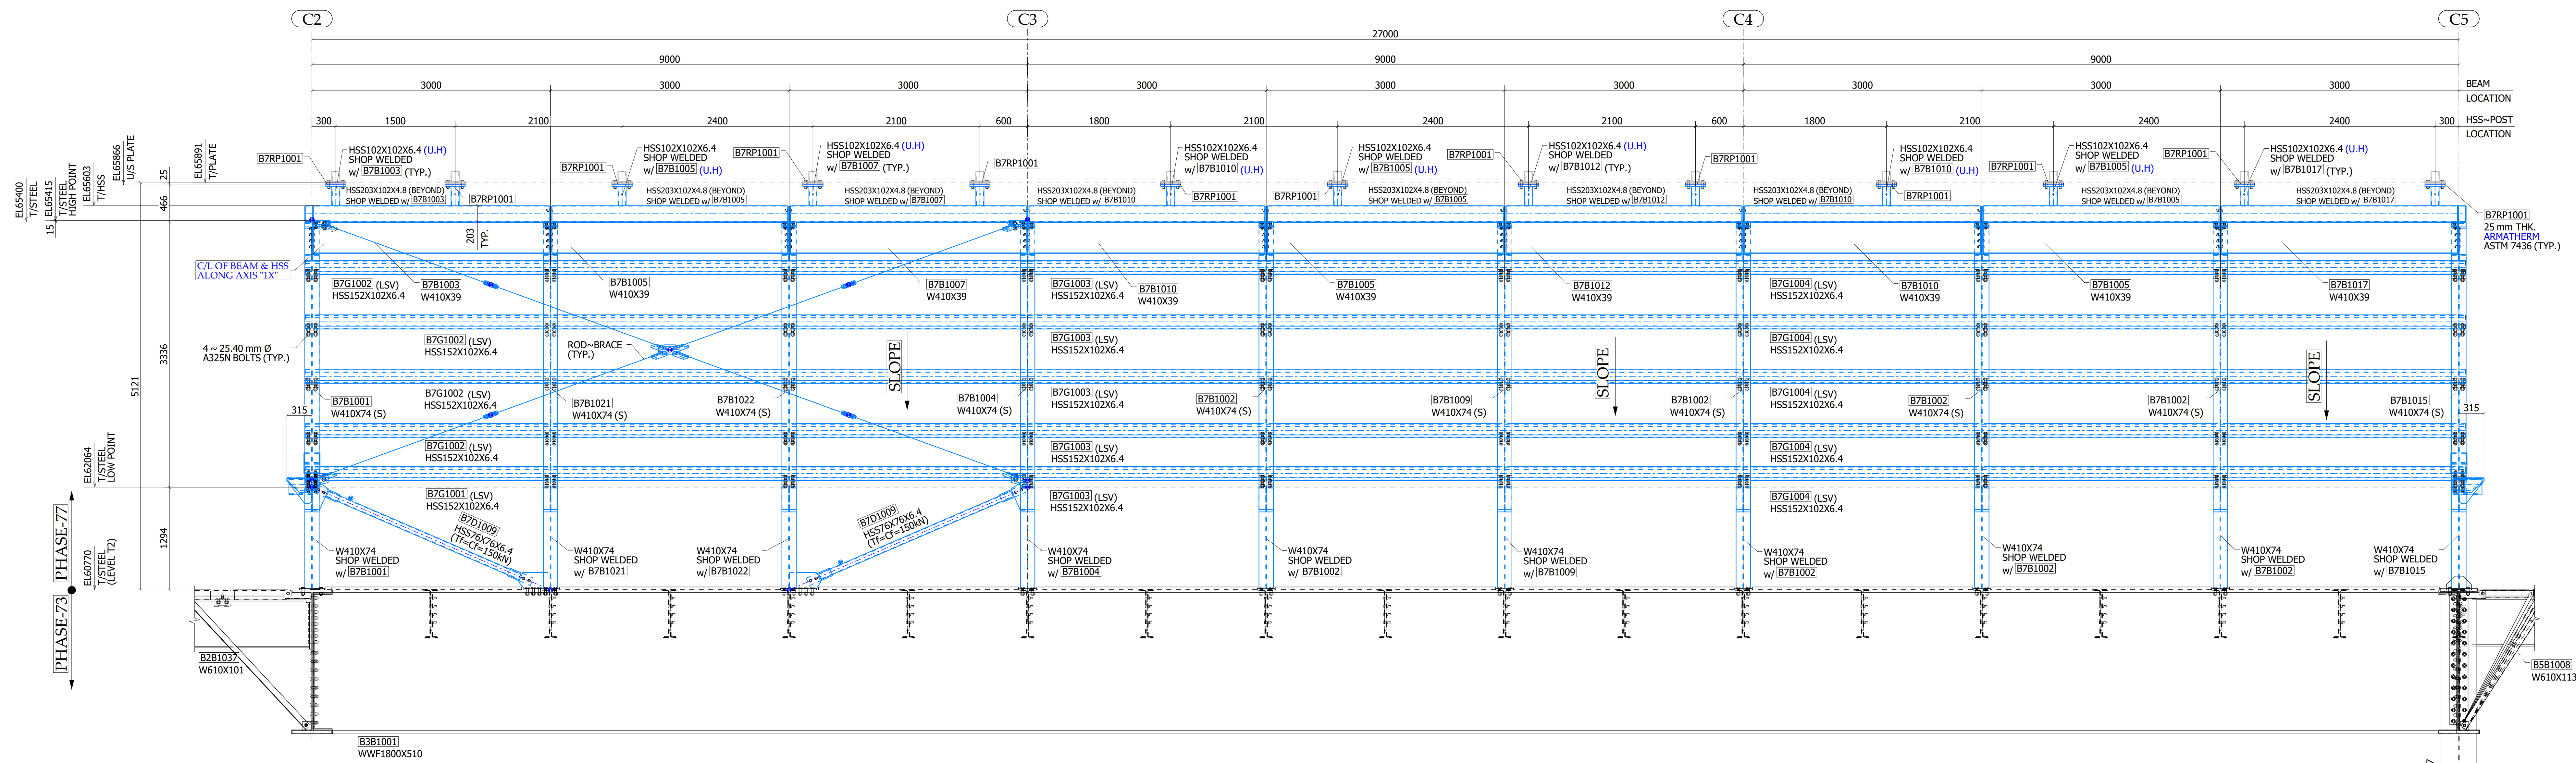

SECTION 3 - 3
ELEVATION ALONG AXIS "IW"
(REFER SHEET: S-B-9000)
U.H. INDICATES MEMBERS ARE HAVING URETHANE HOLES
BLUE INDICATES MEMBERS ARE RECEIVED AES2

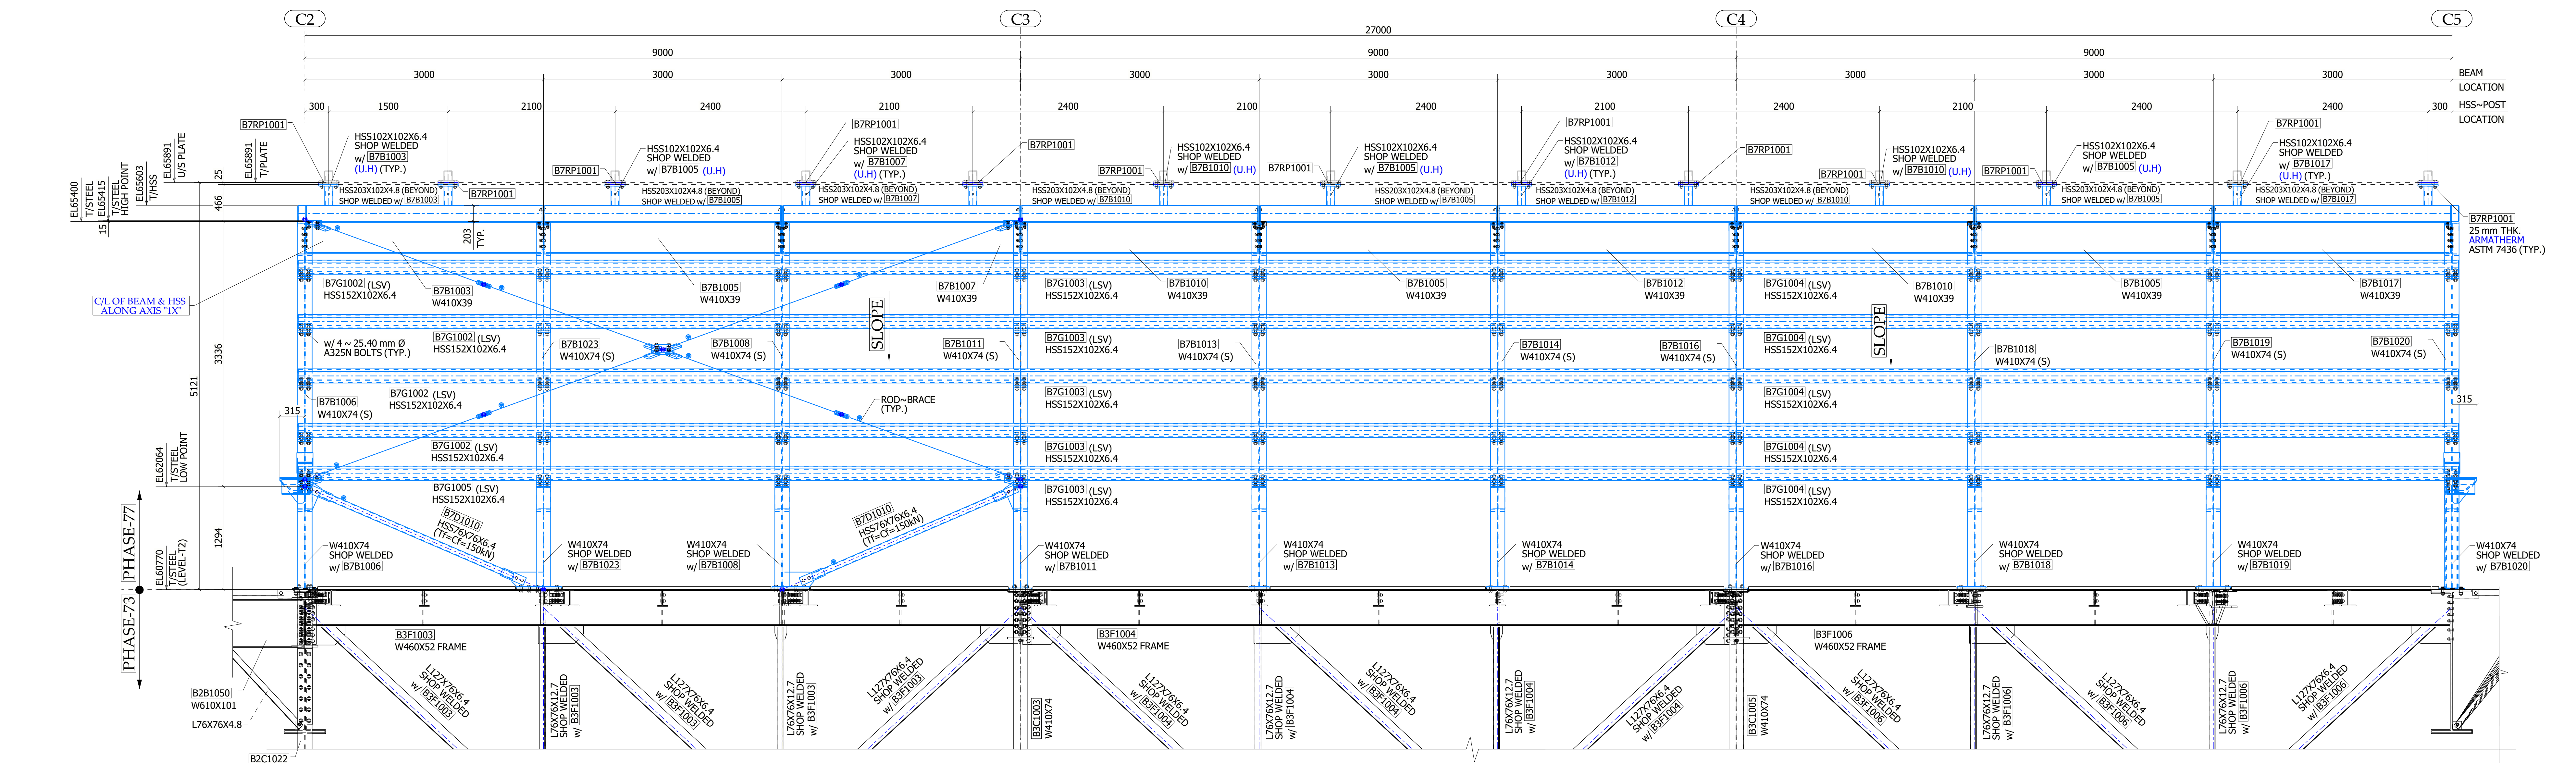


SECTION 4 - 4
ELEVATION ALONG AXIS "1Y"
(REFER SHEET: S-B-9000)
U.H. INDICATES MEMBERS ARE HAVING URETHANE HOLES
BLUE INDICATES MEMBERS ARE RECEIVED AES2


STEELS ABOVE ELEVATION 60770mm
ARE RECEIVED AES2

DATE	NO	DESCRIPTION	PAR	REVISION
01/28/2023	1	FOR FIELD USE		
01/25/2023	2	FOR APPROVAL		


GRADE ASHER	S.I.C.
FLYER PRODS	S.I.C.
E48XX	S.I.C.
WOODLINE	S.I.C.
6mm	S.I.C.
TRUCK	S.I.C.
220	S.I.C.
BOULDER	S.I.C.
AS2N	S.I.C.
PERITURE	S.I.C.
1-23A SHOP PRIMER	S.I.C.

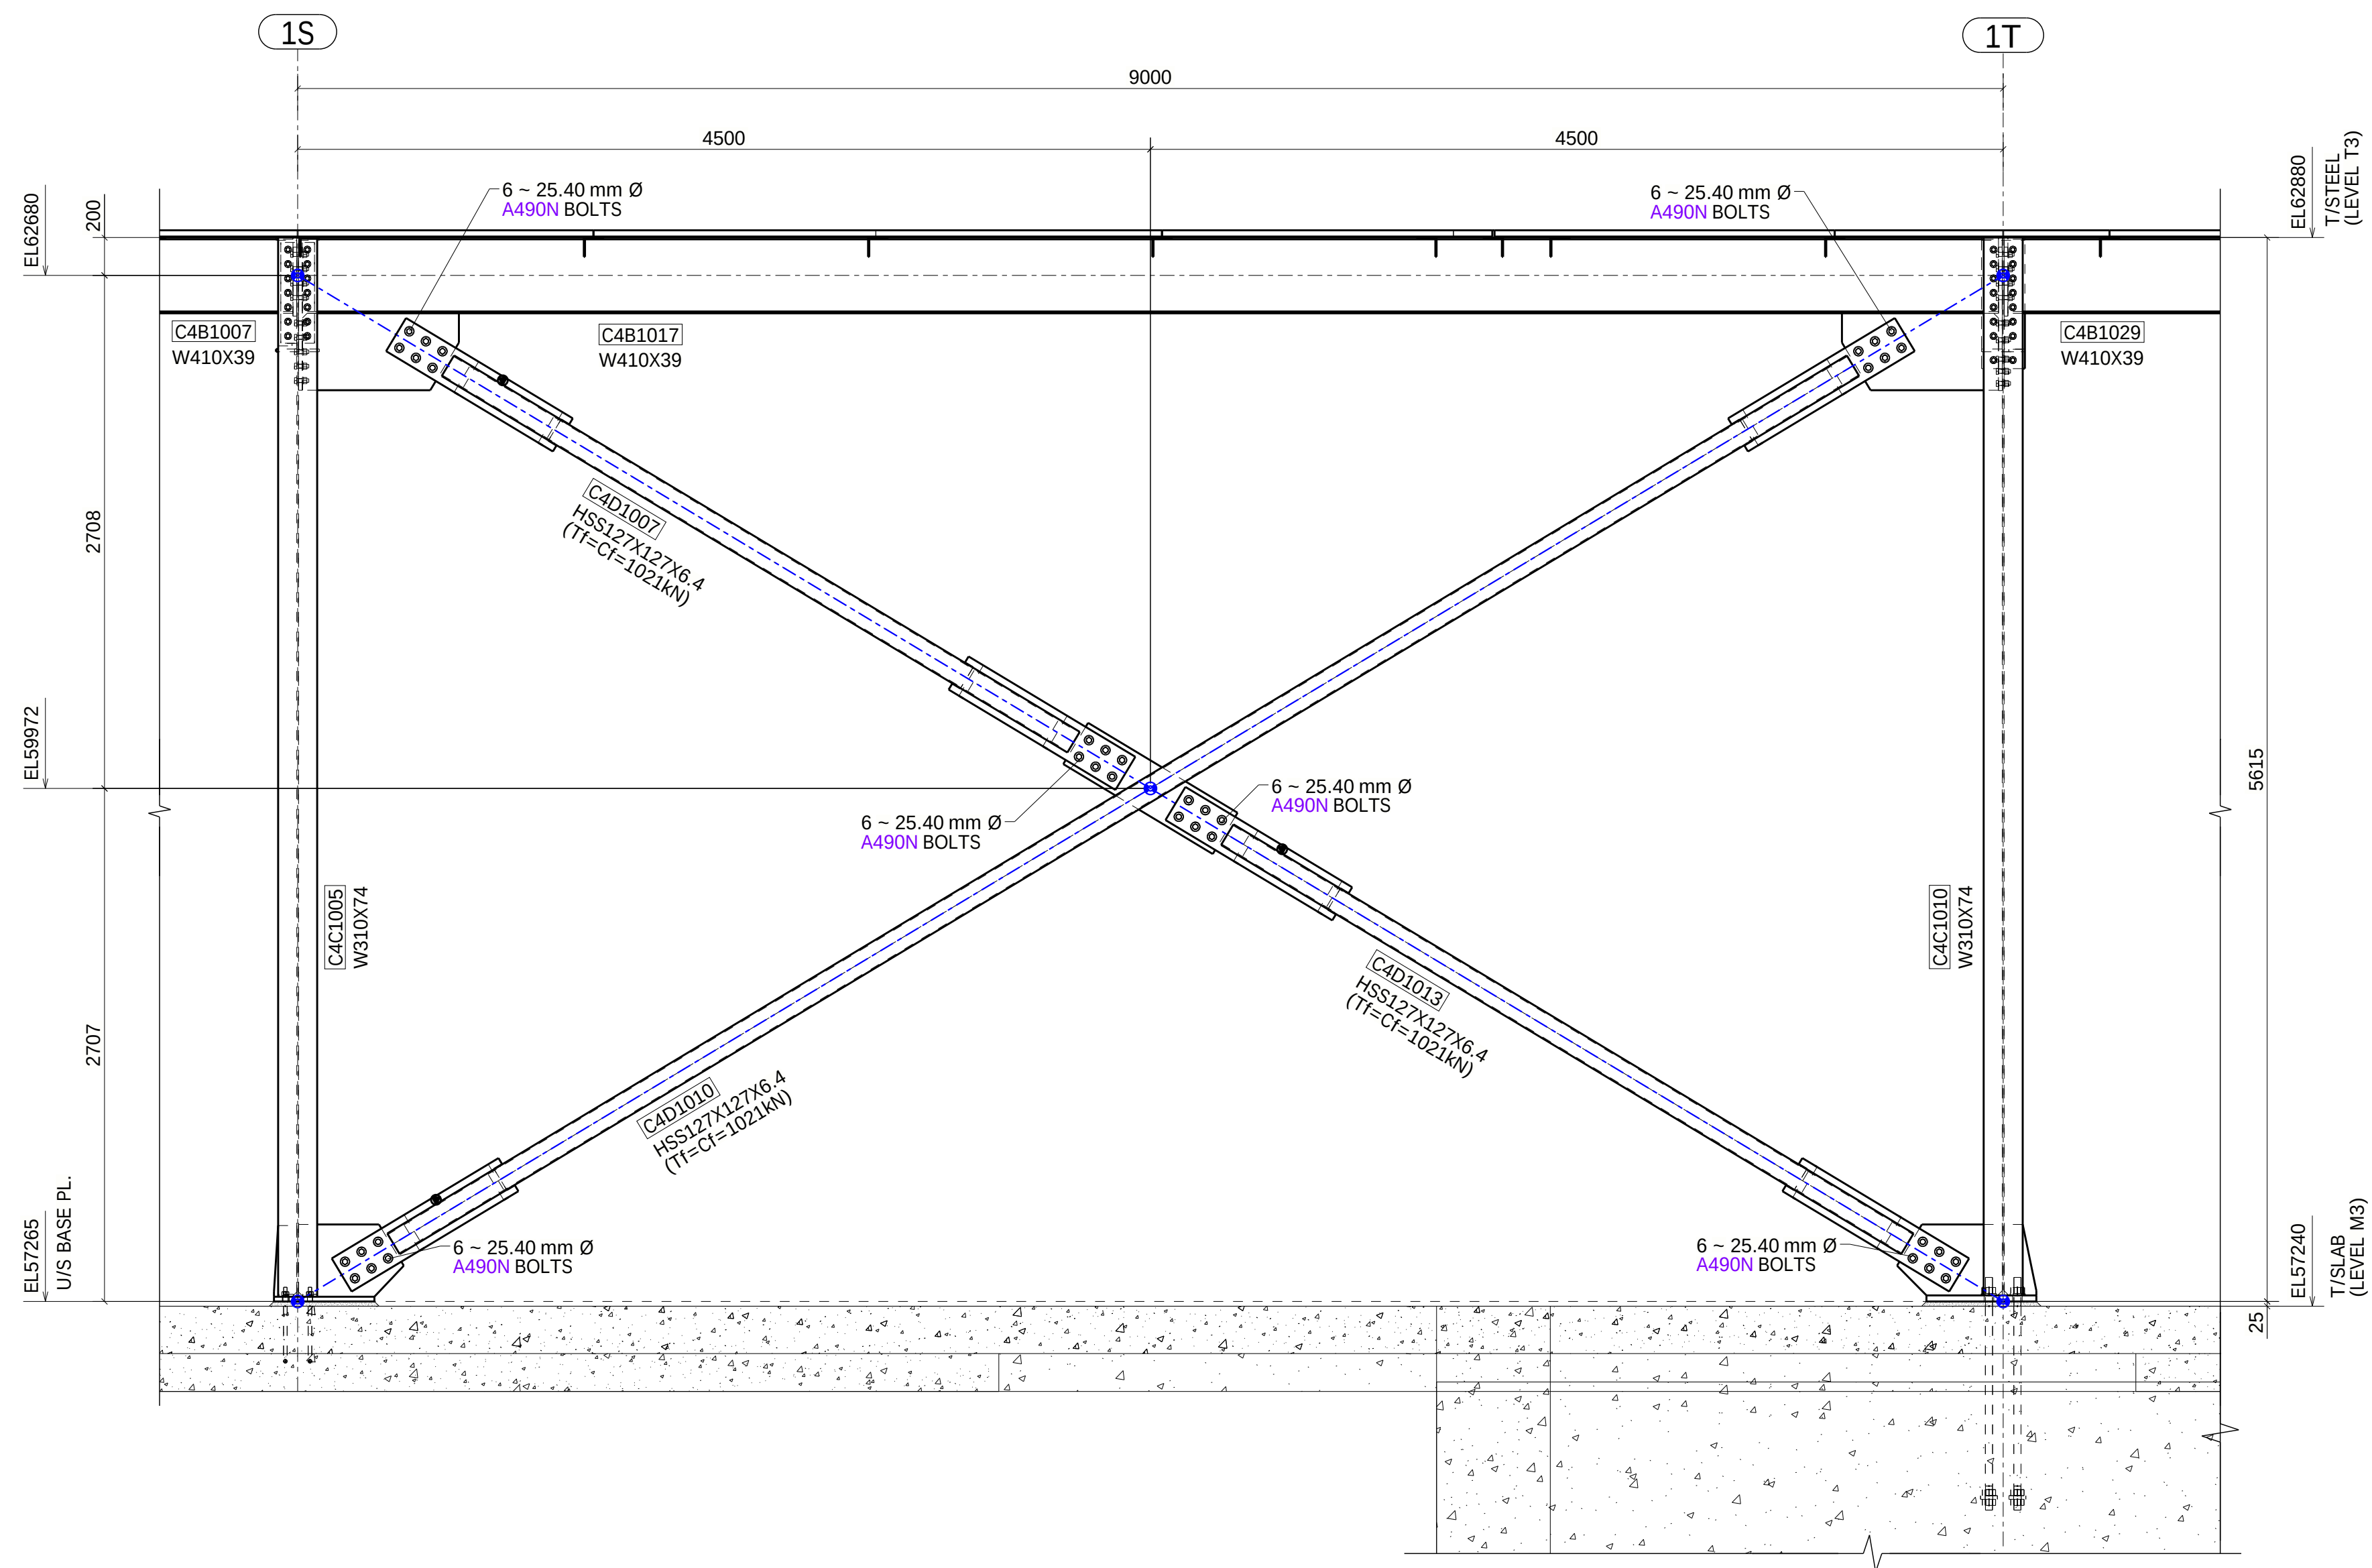


BRACE ELEVATION ALONG AXIS "A8.1" (-225)
(REFER SHEET: S-C-9002)

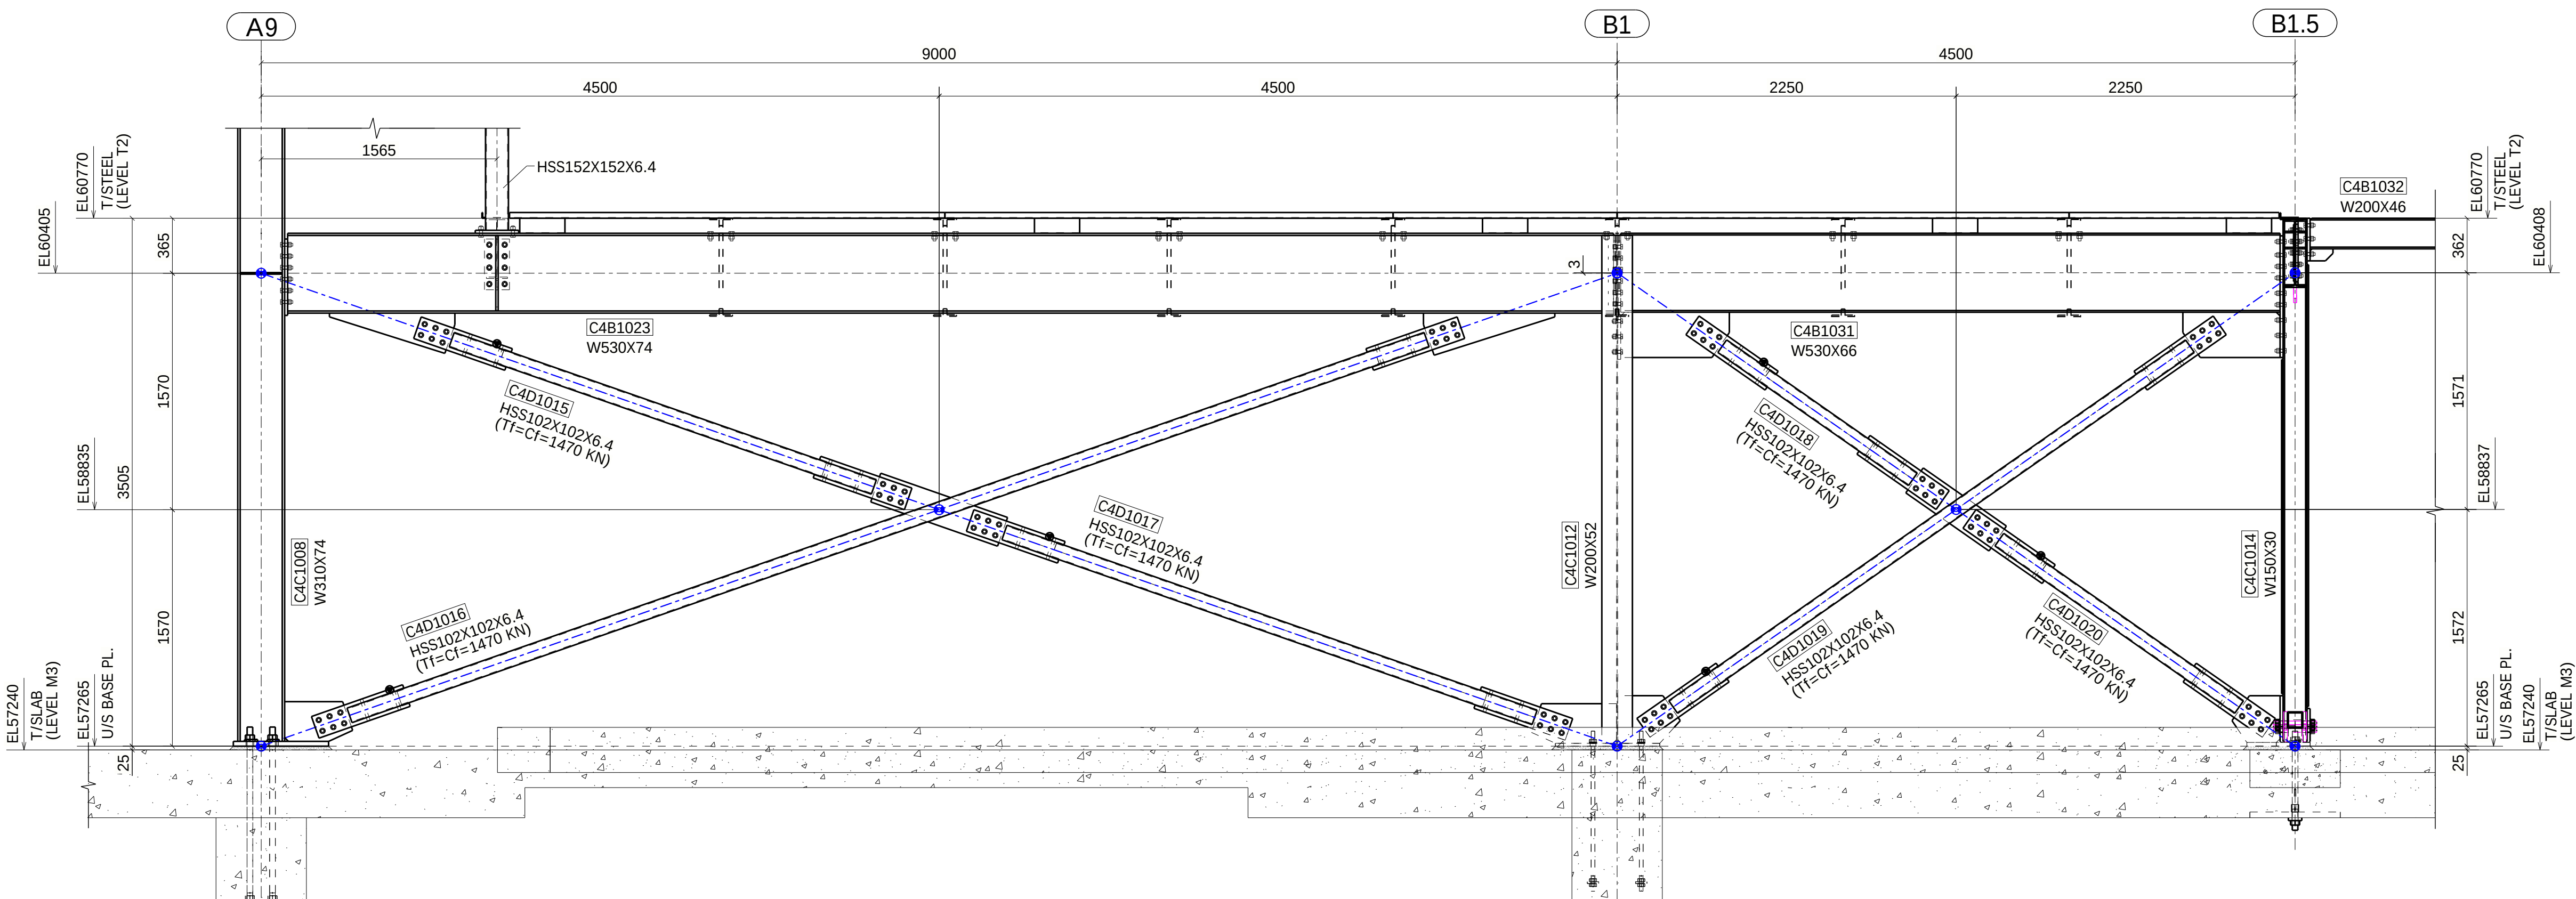

BRACE ELEVATION ALONG AXIS "1S"
(REFER SHEET: S-C-9002)

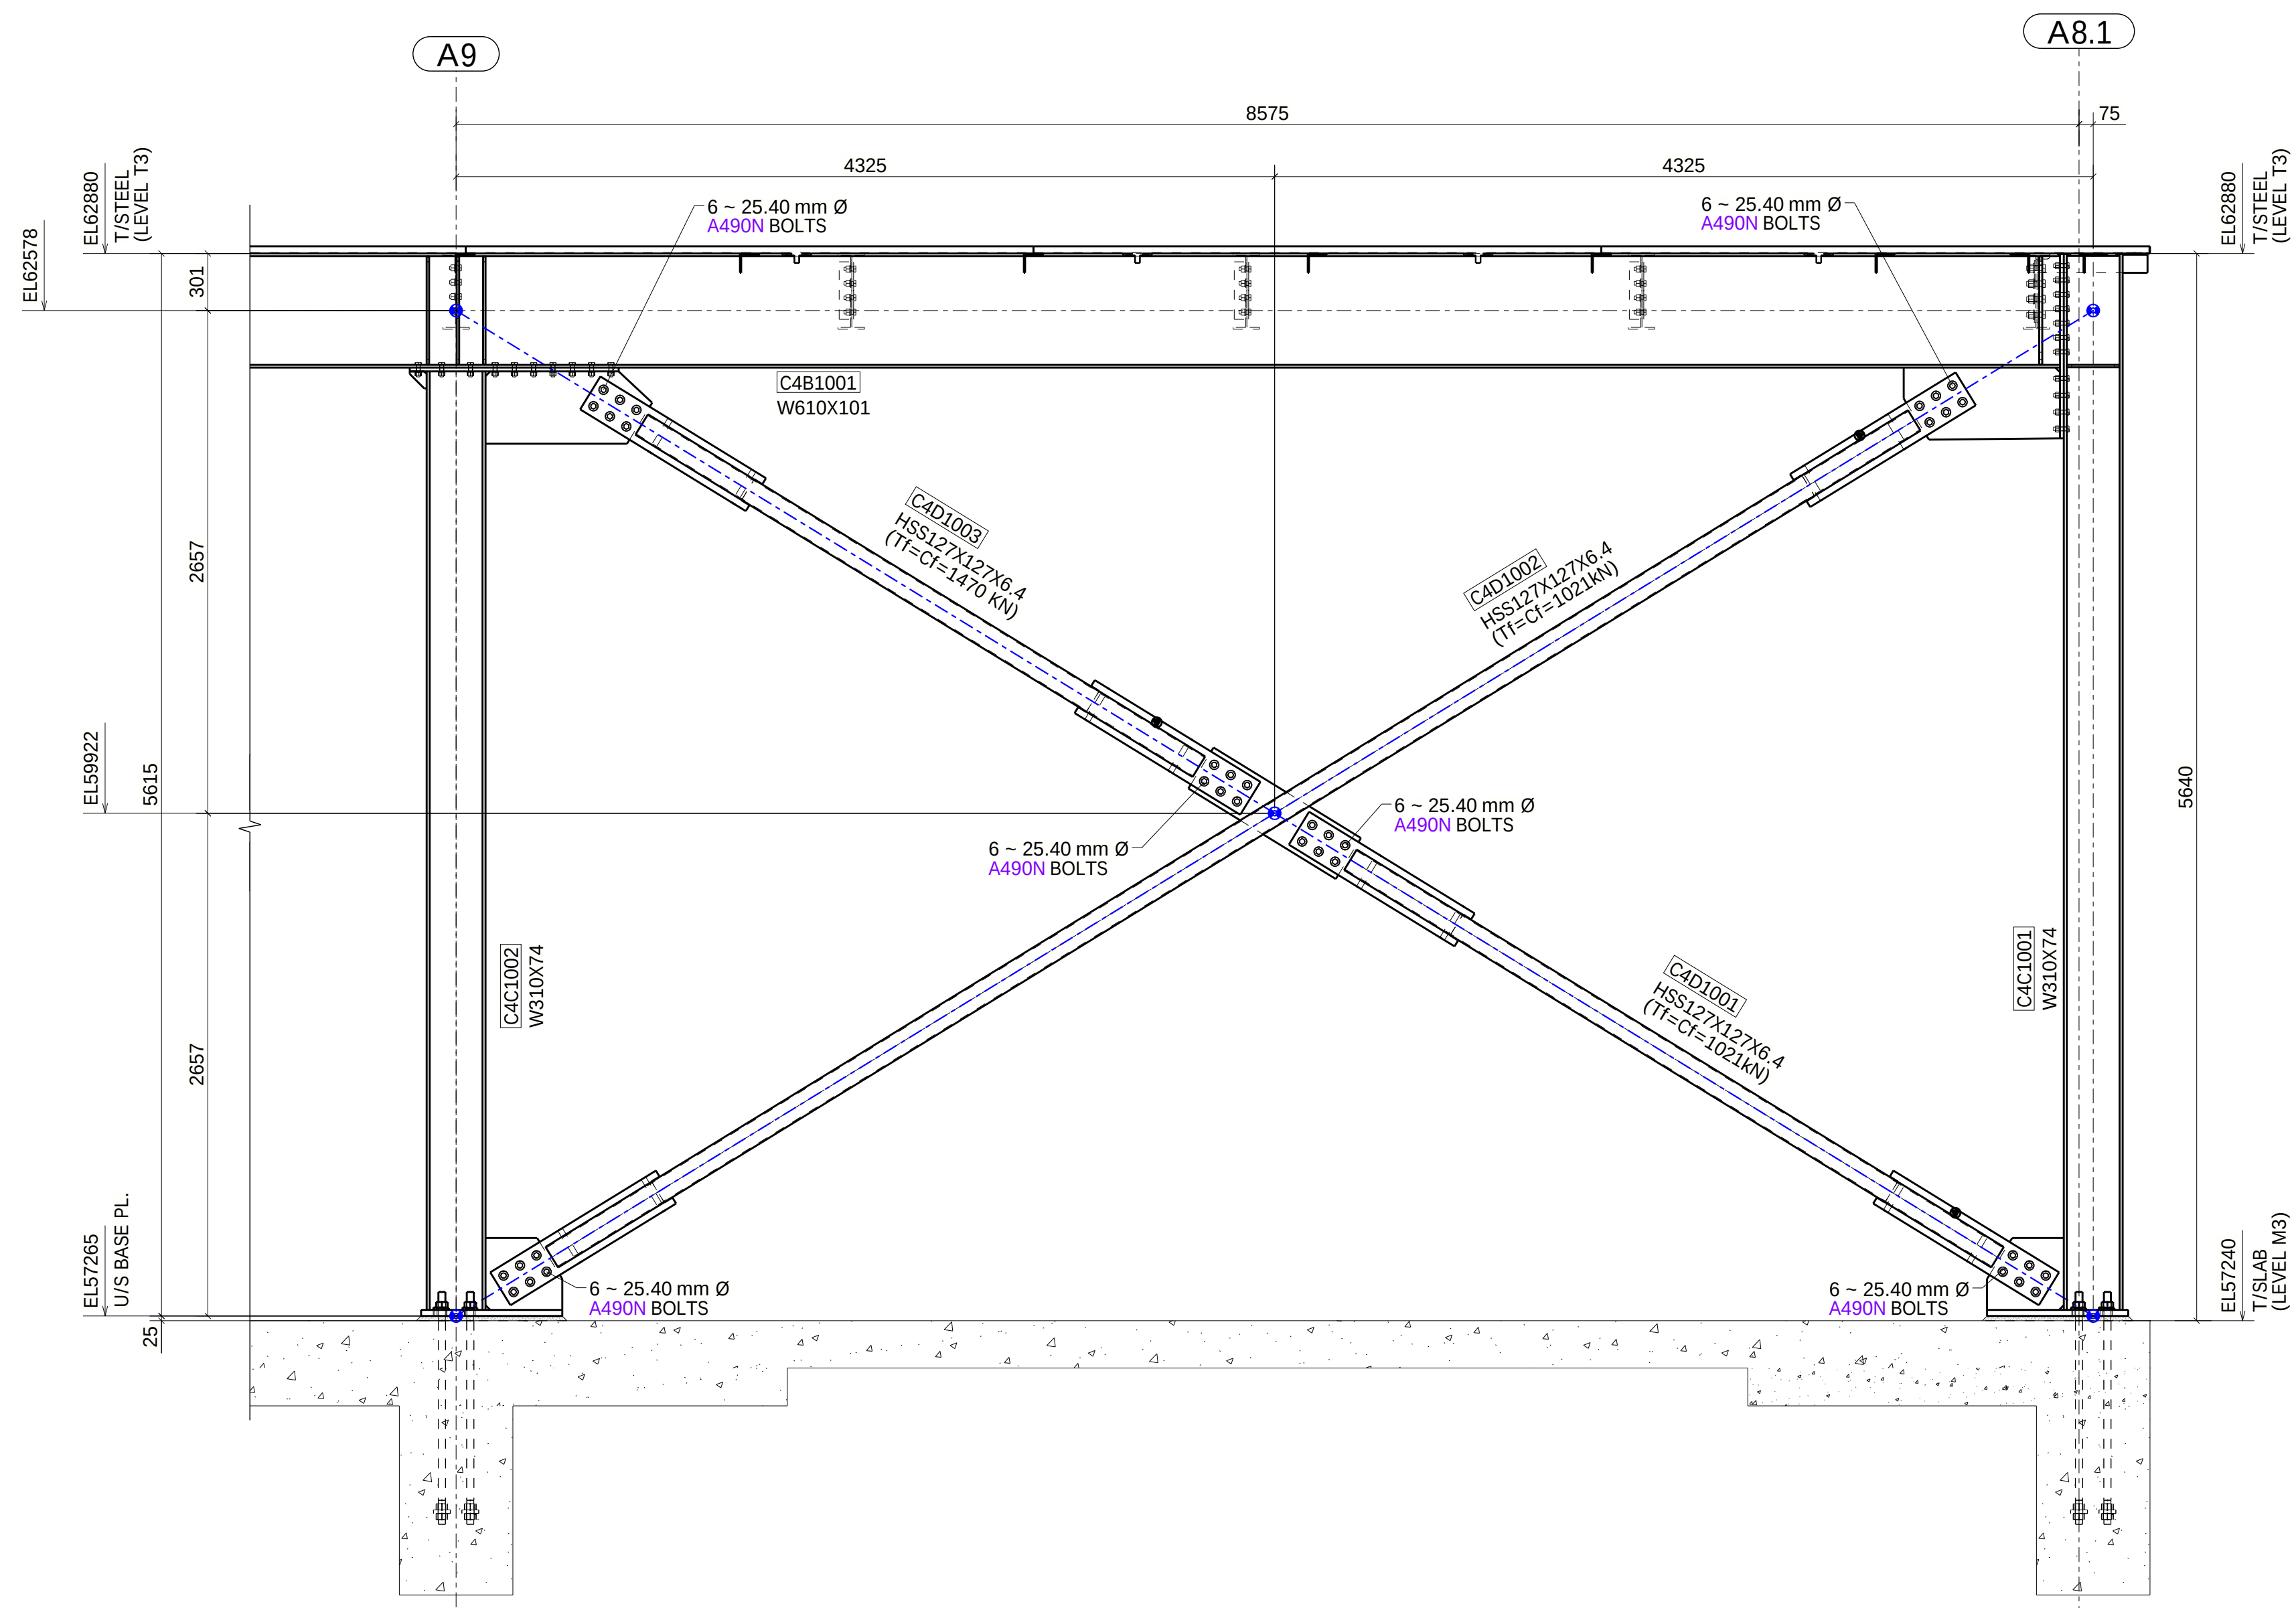

BRACE ELEVATION ALONG AXIS "1Q.1" (-75mm)
(REFER SHEET: S-C-9002)

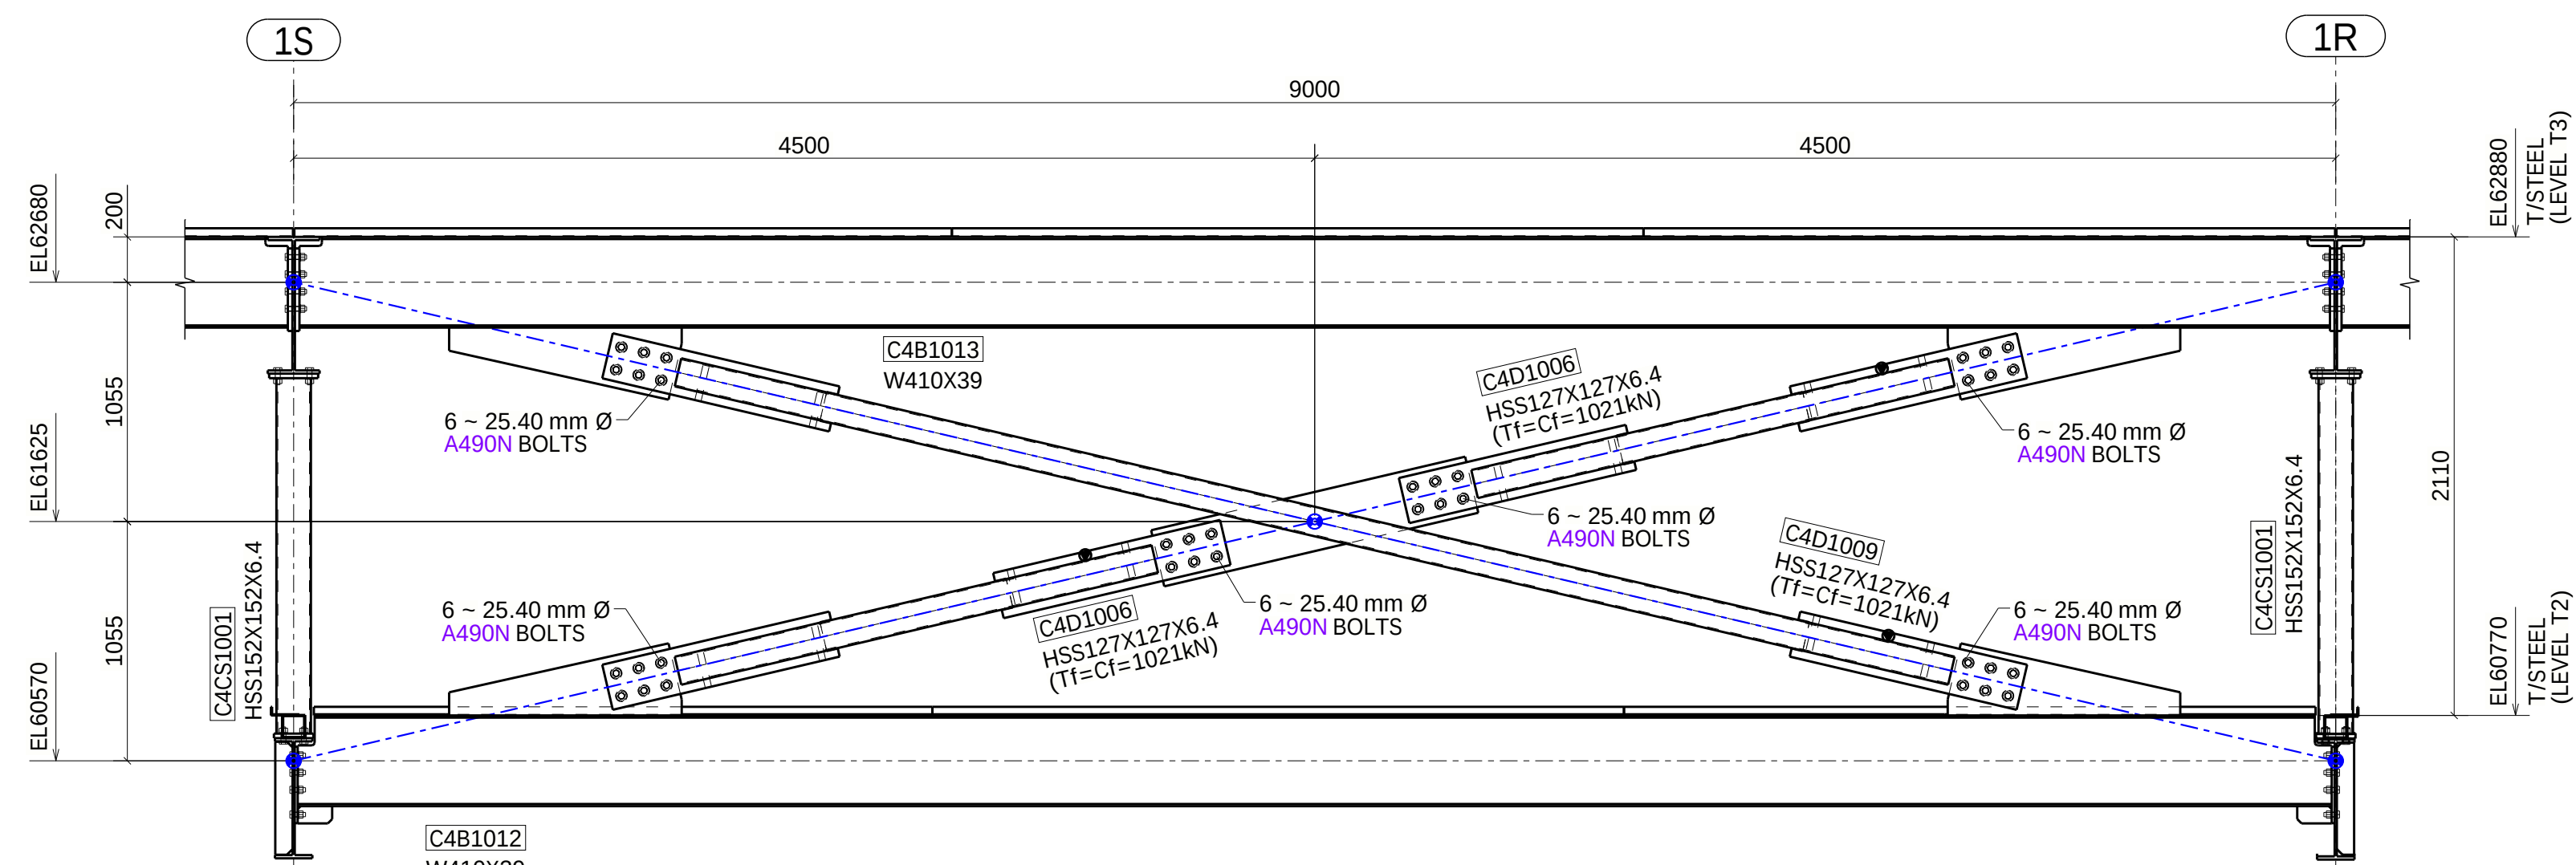

BRACING ELEVATION ALONG AXIS "A9.2" (+127mm)
(REFER SHEET: S-C-9002)

				GRADE ACER	S.I.C.
				350W	S.I.C.
				ELECTRICALS	S.I.C.
				E48XX	S.I.C.
				WOODWORK	S.I.C.
				6mm	S.I.C.
				TRUCK	S.I.C.
				220	S.I.C.
				BOLTS	S.I.C.
				A325	S.I.C.
				PAINTURE	S.I.C.
				1-32A SHOP PRIMER	S.I.C.
DATE	NO	DESCRIPTION		PAR	
11/15/2022	1	FOR FIELD USE			
08/26/2022	2	FOR APPROVAL			