





WORKING NORTH

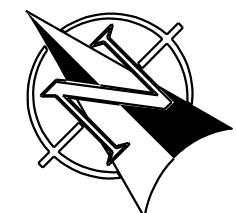

PROJECT NORTH

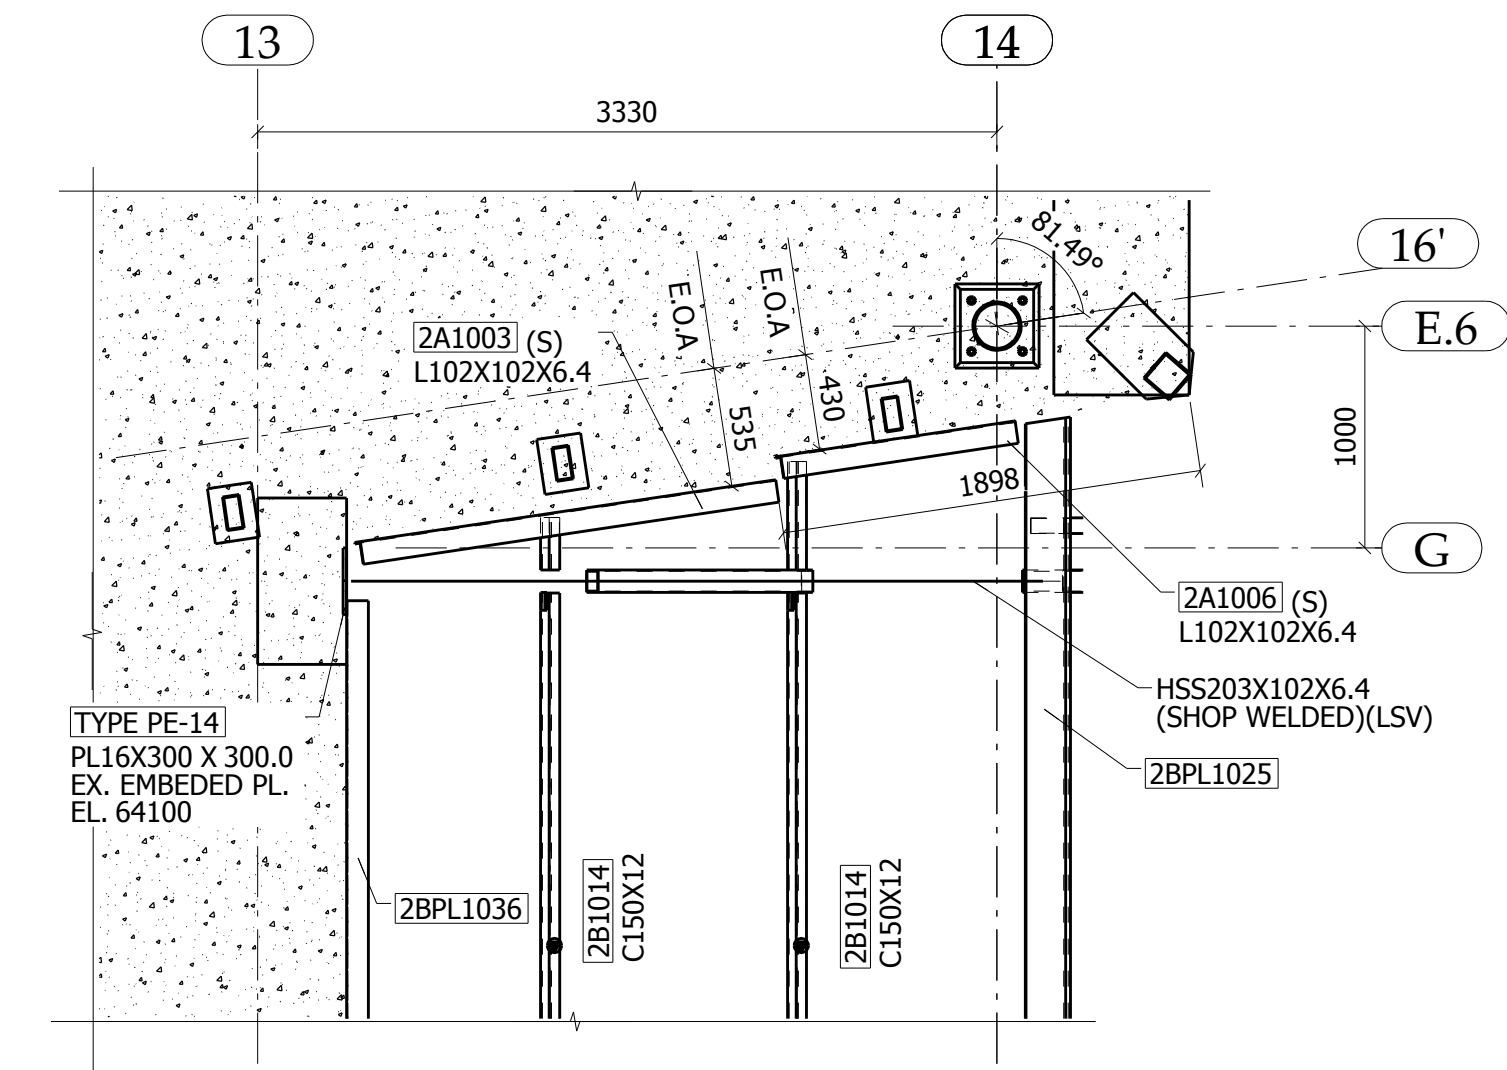


DETAIL 1

ROOF FRAMING PLAN (MANSARD AREA) -PHASE 2

(REF.SEC: ENLARGED PLAN VIEW 1/ S7.05)

NOTES:


1. TOP OF LEVEL 5 EL.64100mm (U.N.O)
2. ▼ -INDICATES ORIENTATION OF MEMBER
3. ◀ -INDICATES MOMENT CONNECTION.
4. (A)-INDICATES ABOVE,(B)-INDICATES BELOW
(S)-INDICATES SLOPES
5. (LSV)- INDICATES LONG SIDE VERTICAL
(LSH)- INDICATES LONG SIDE HORIZONTAL
6. <X> -INDICATES 10mm THK. PLATE BRACES.

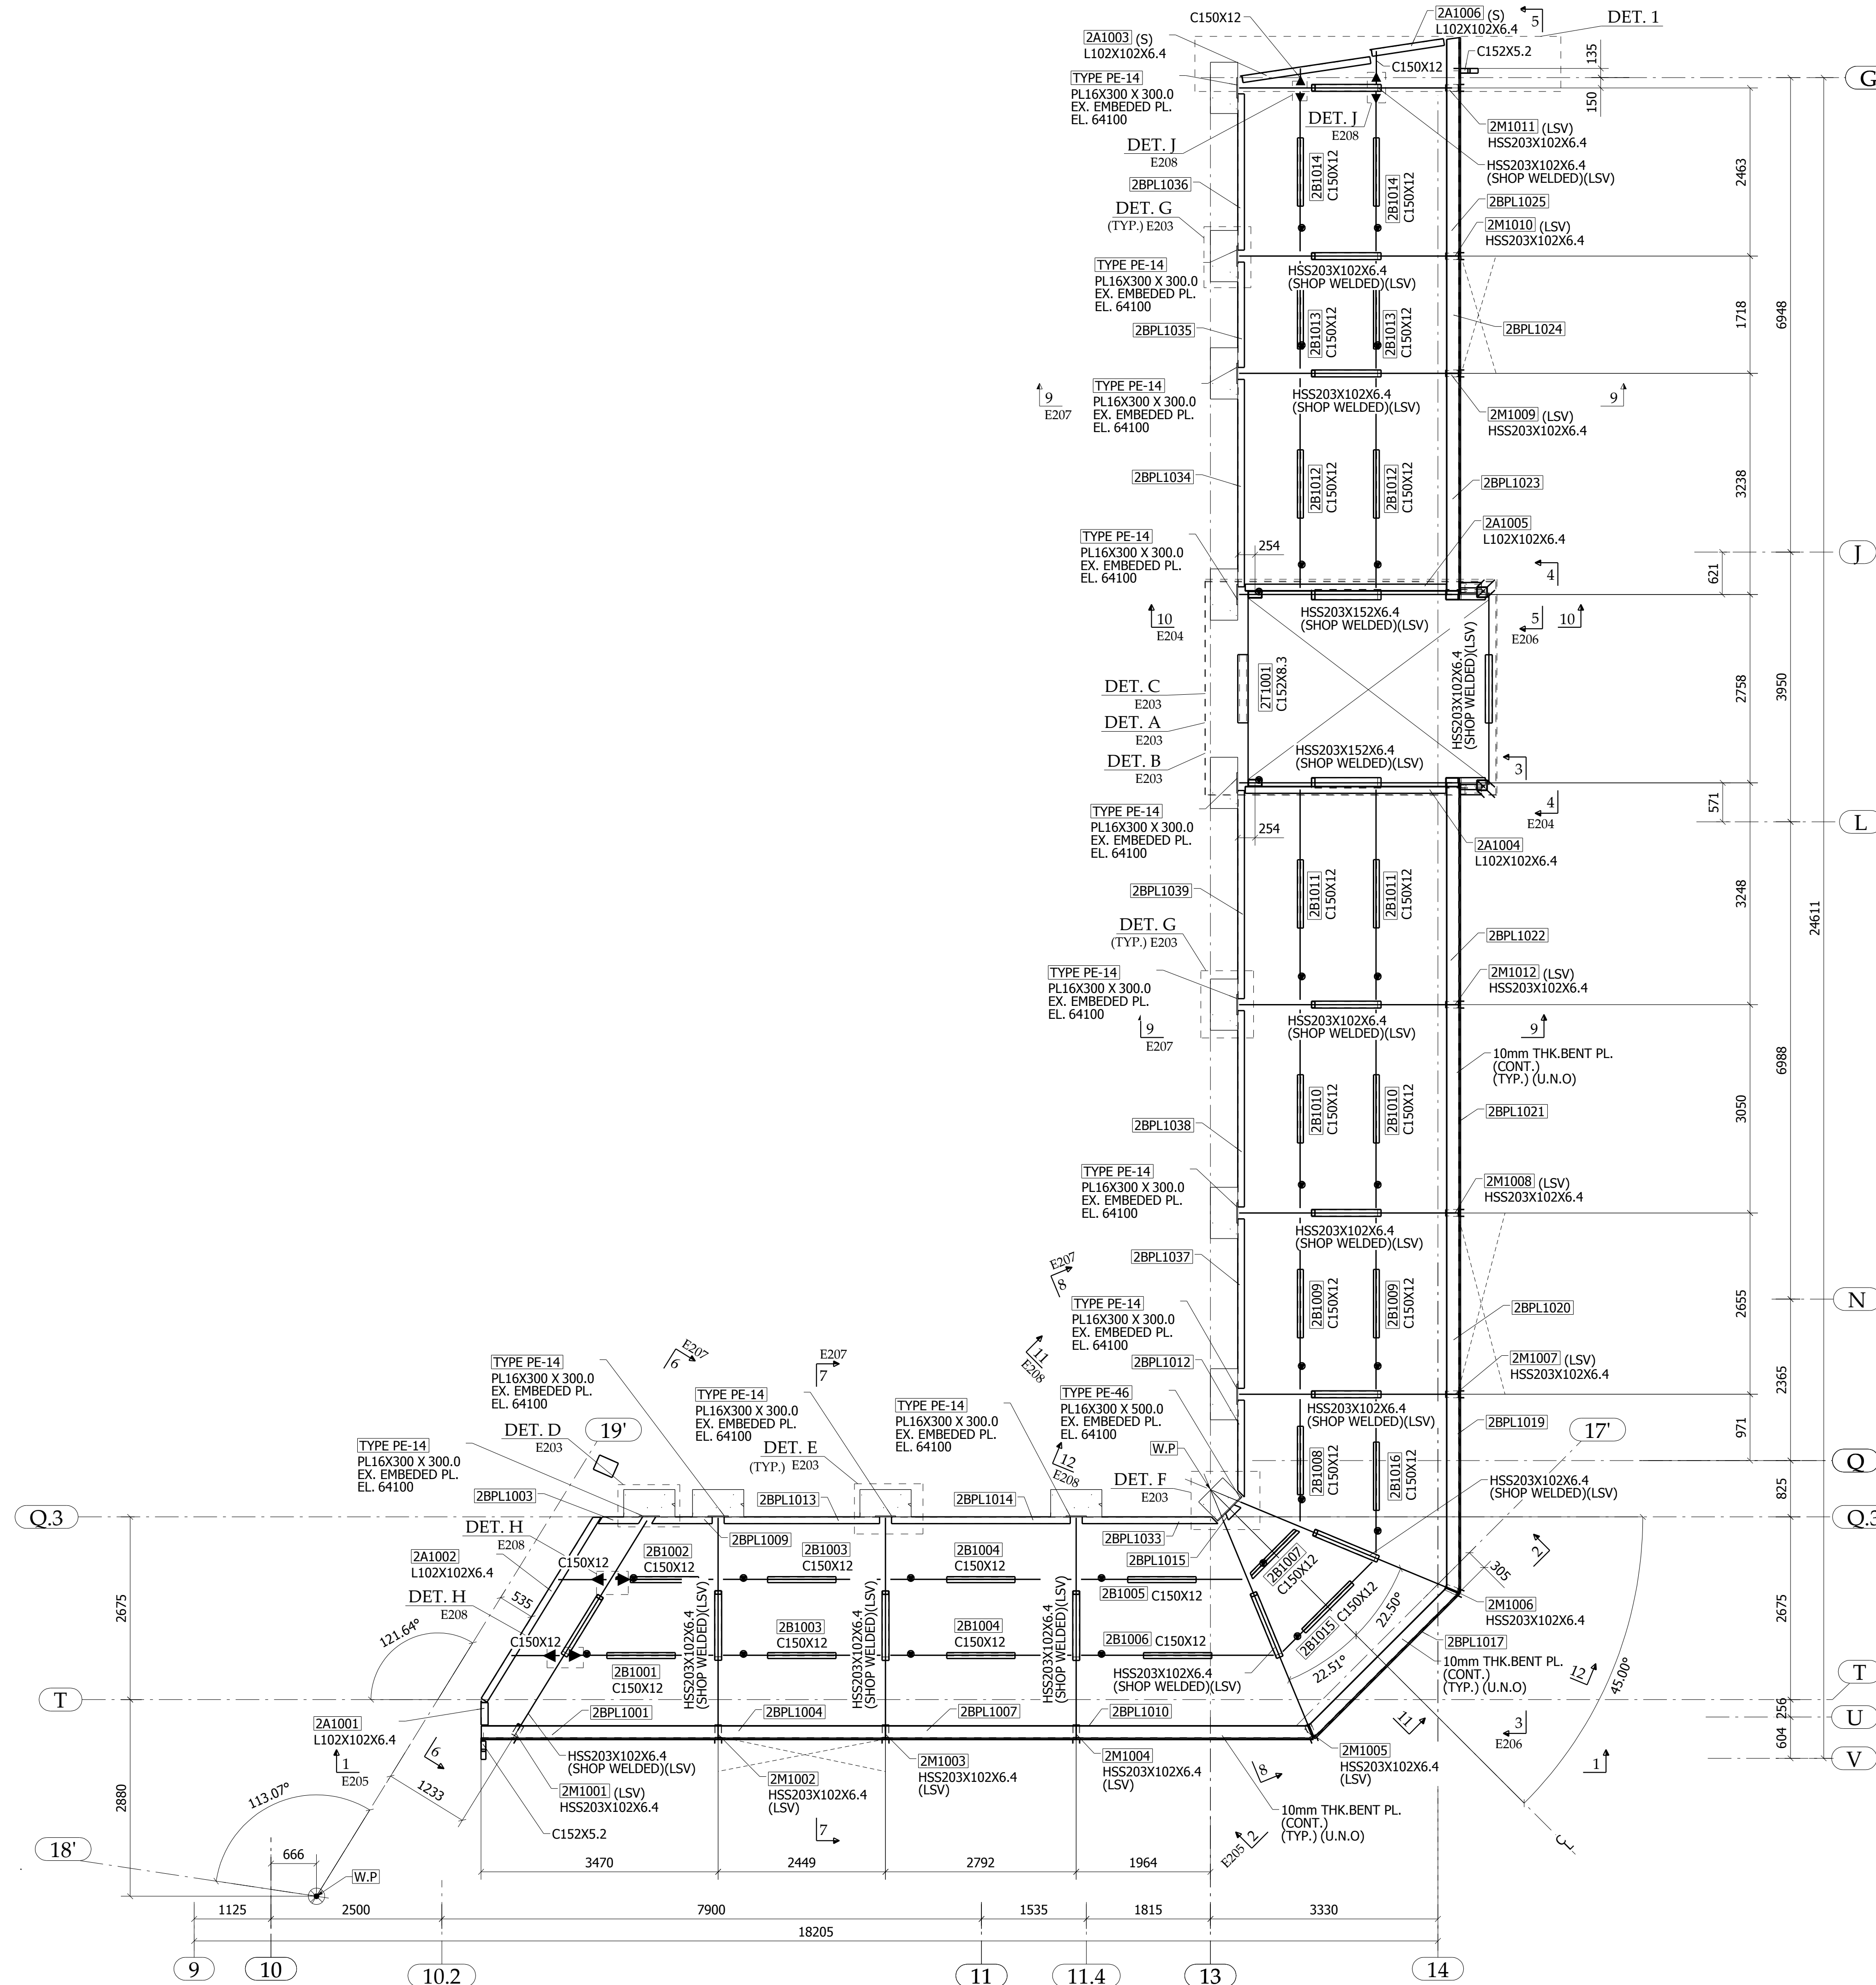



NOTES:


1. TOP OF SLAB EL.64100mm (U.N.O)
2. (A)-INDICATES ABOVE,(B)-INDICATES BELOW
(S)-INDICATES SLOPES
3. ▼ -INDICATES ORIENTATION OF MEMBER

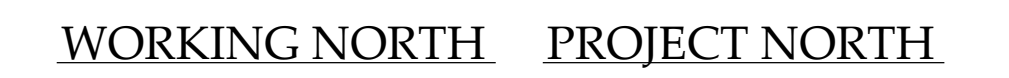

(REF.SEC: S7.06)

1. (A)-INDICATES ABOVE,(B)-INDICATES BELOW
(S)-INDICATES SLOPES


2. -INDICATES ORIENTATION OF MEMBER

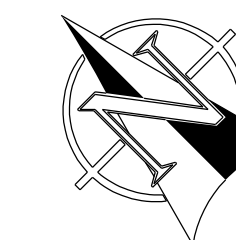

PROJECT NORTH



WORKING NORTH

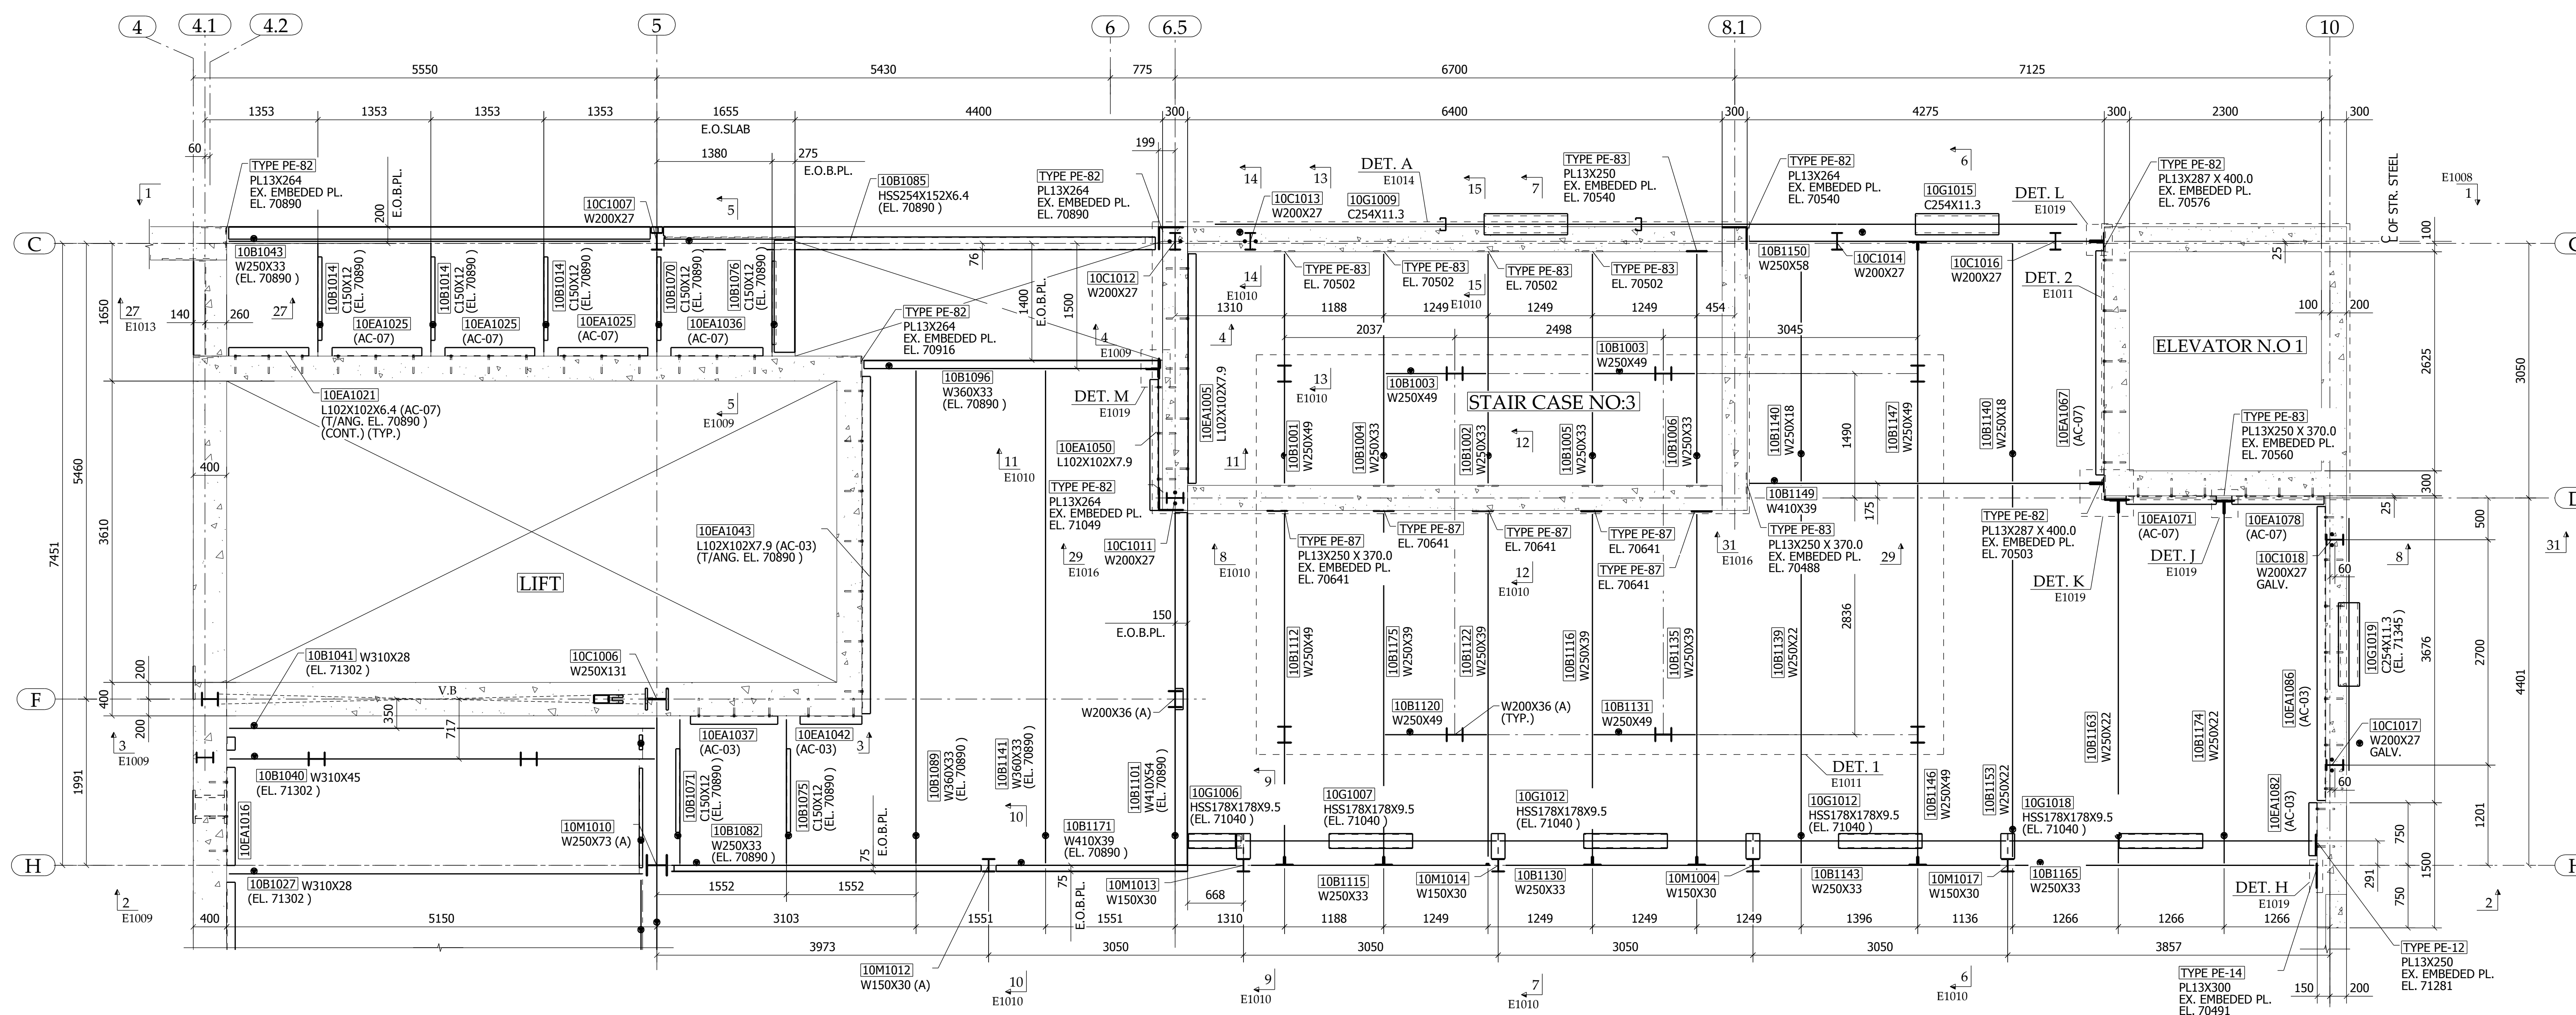



PARTIAL LEVEL 7 FLOOR FRAMING PLAN
TOP OF STEEL EL.70502mm (U.N.O.)

(REF.SEC: 1/56.34)

NOTES:


- 1.ELEVATION SHOWN IN PLAN ARE REFERRED TO TOP OF STEEL ELEVATION
2. TOP OF SLAB EL.71400.00 mm (SLAB THICKNESS=150mm U.N.O).
3.  - INDICATES ORIENTATION OF MEMBER.
4. (A)-INDICATES ABOVE,(B)-INDICATES BELOW
5. E.O.BPL - INDICATES EDGE OF BENT PLATE.

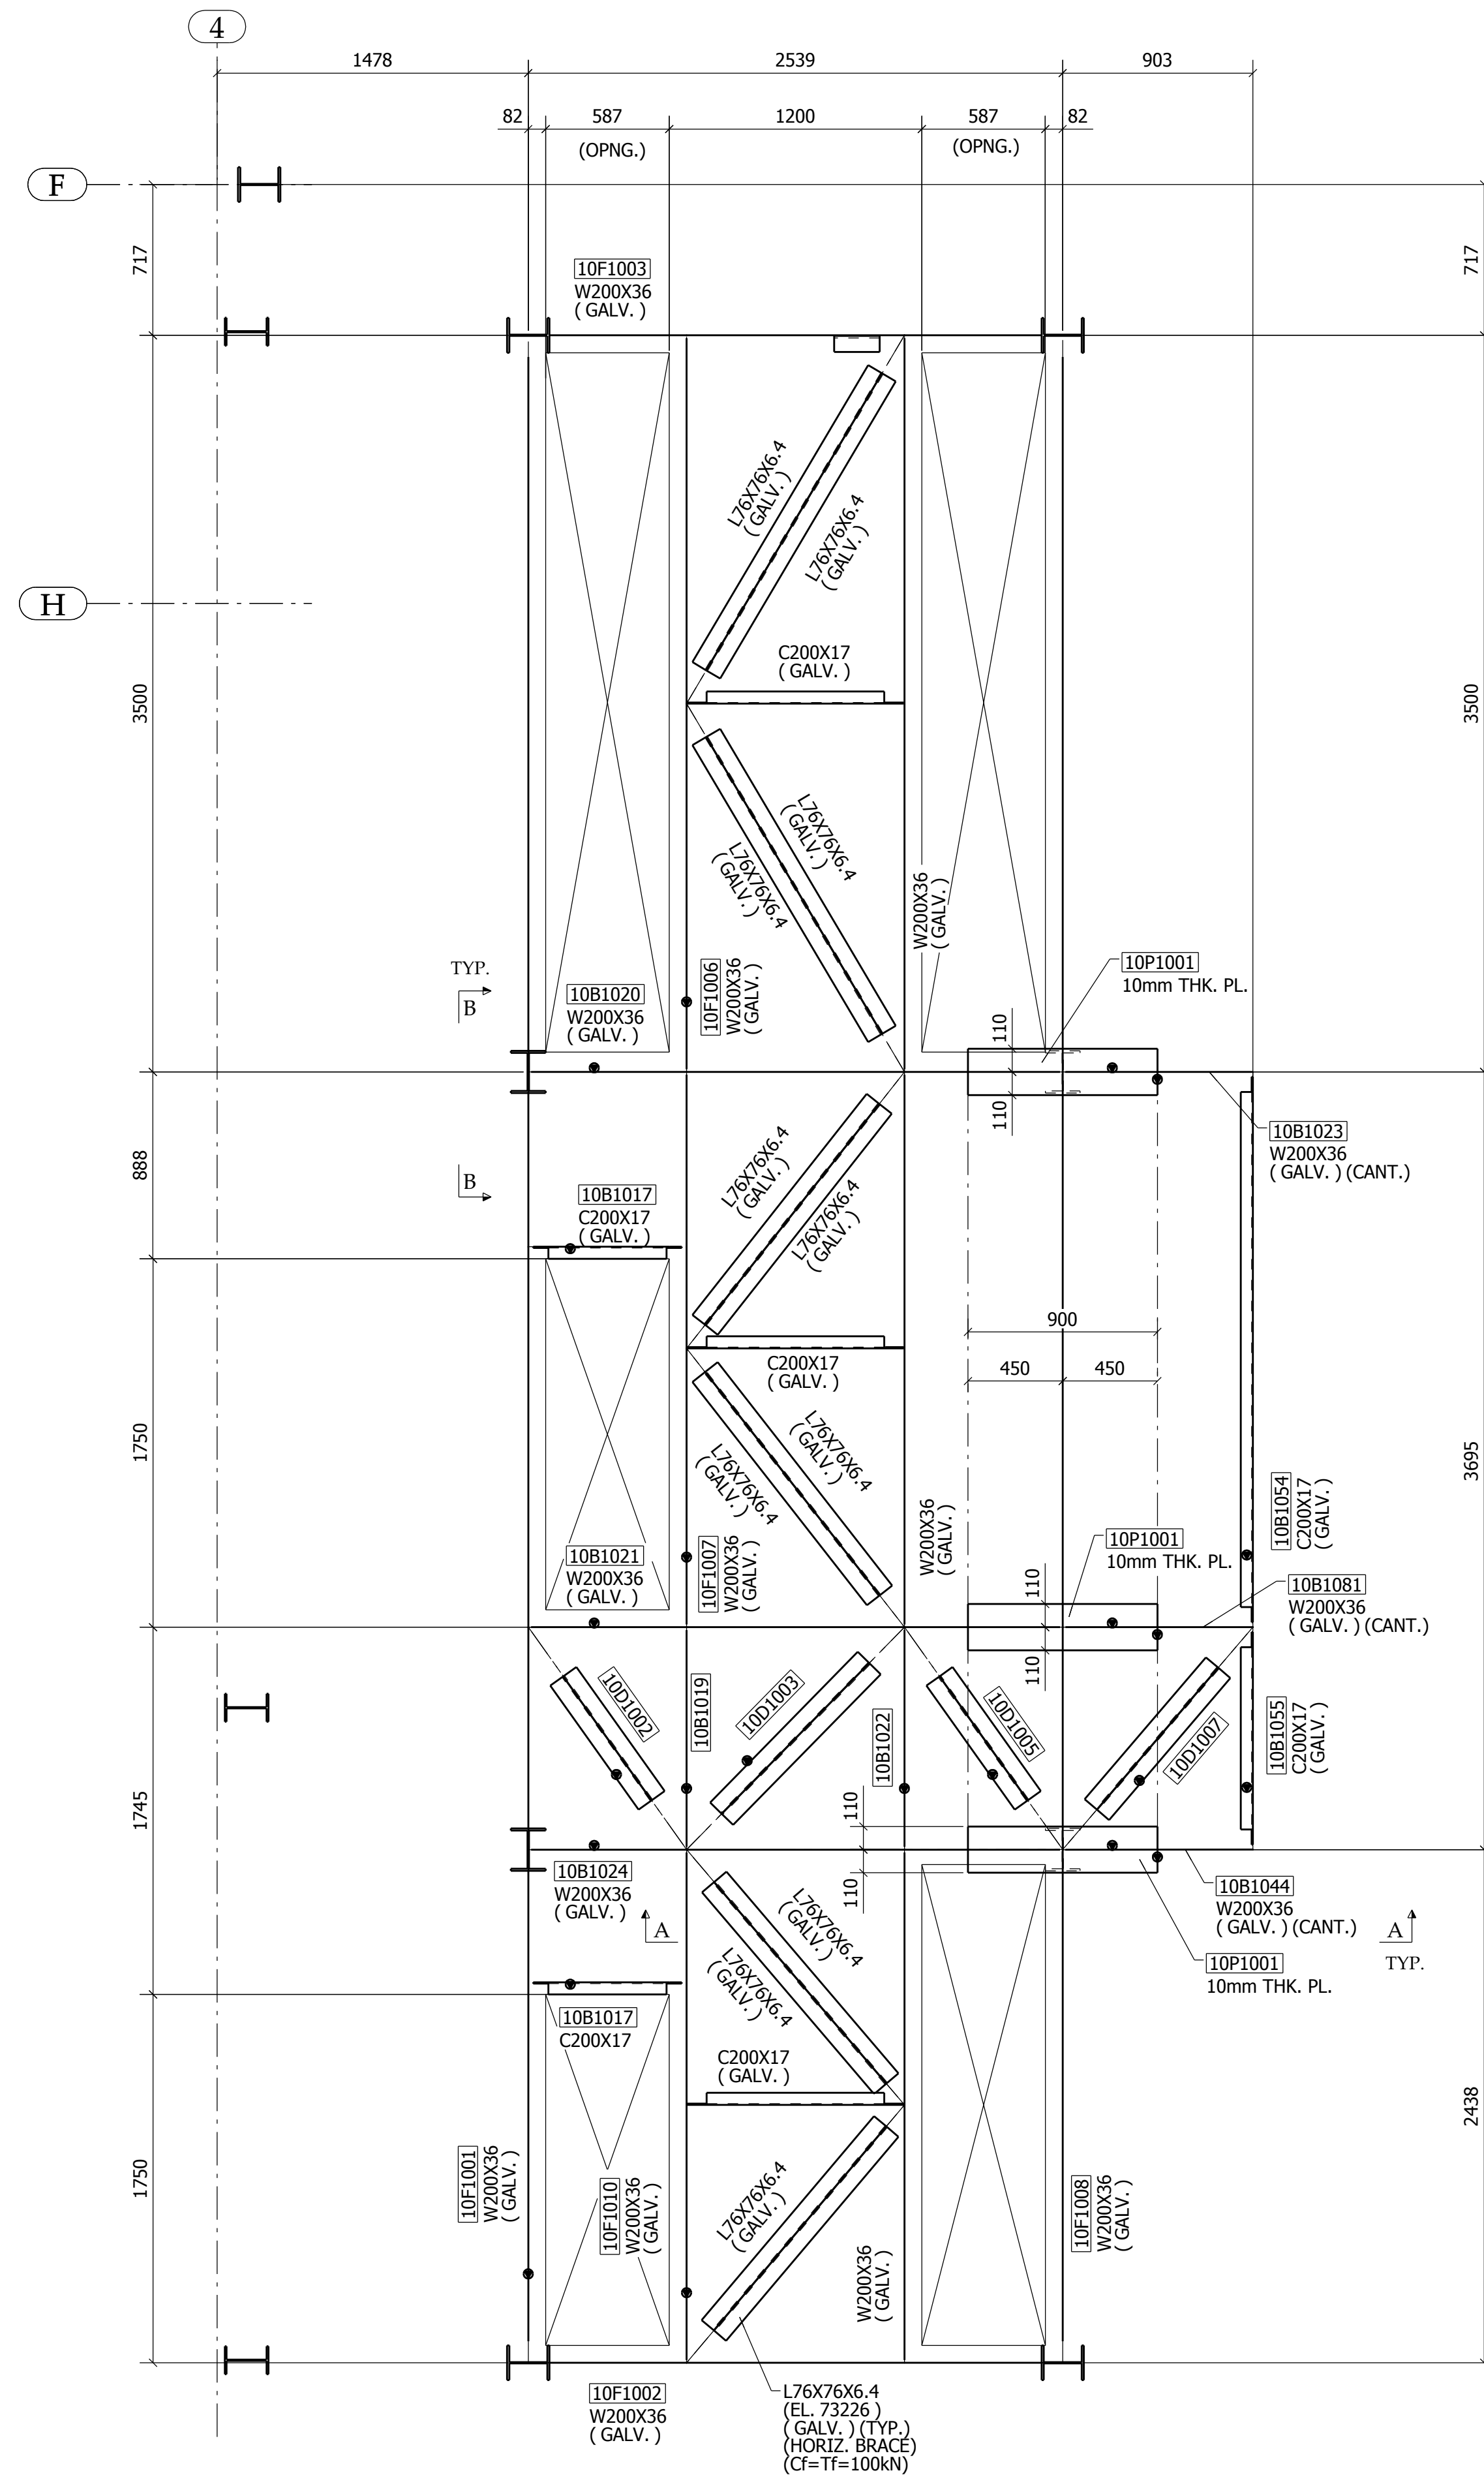

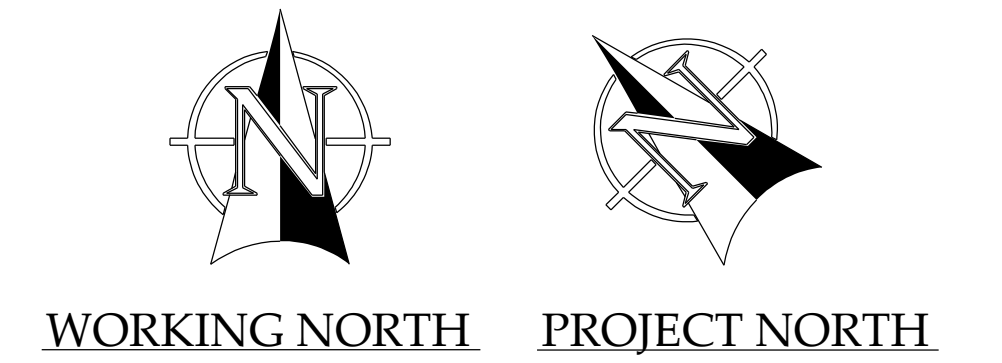

1. TOP OF STEEL EL.74765.00mm (U.N.O)
2. (A)-INDICATES ABOVE,(B)-INDICATES BELOW
(S)-INDICATES SLOPES
3.  -INDICATES ORIENTATION OF MEMBER
4. ALL HORIZONTAL BRACE MEMBES 2-127X89 (LLV)
TOP OF STEEL EL.74565mm TYP.(U.N.O)
LOAD:
L127X89X13 : Cf = Tf = 450 kN
L127X89X9.5 : Cf = Tf = 350 kN
- 5.(INV.)-INDICATES INVERTED BEAM TOE UP



SECTION 1A - 1A

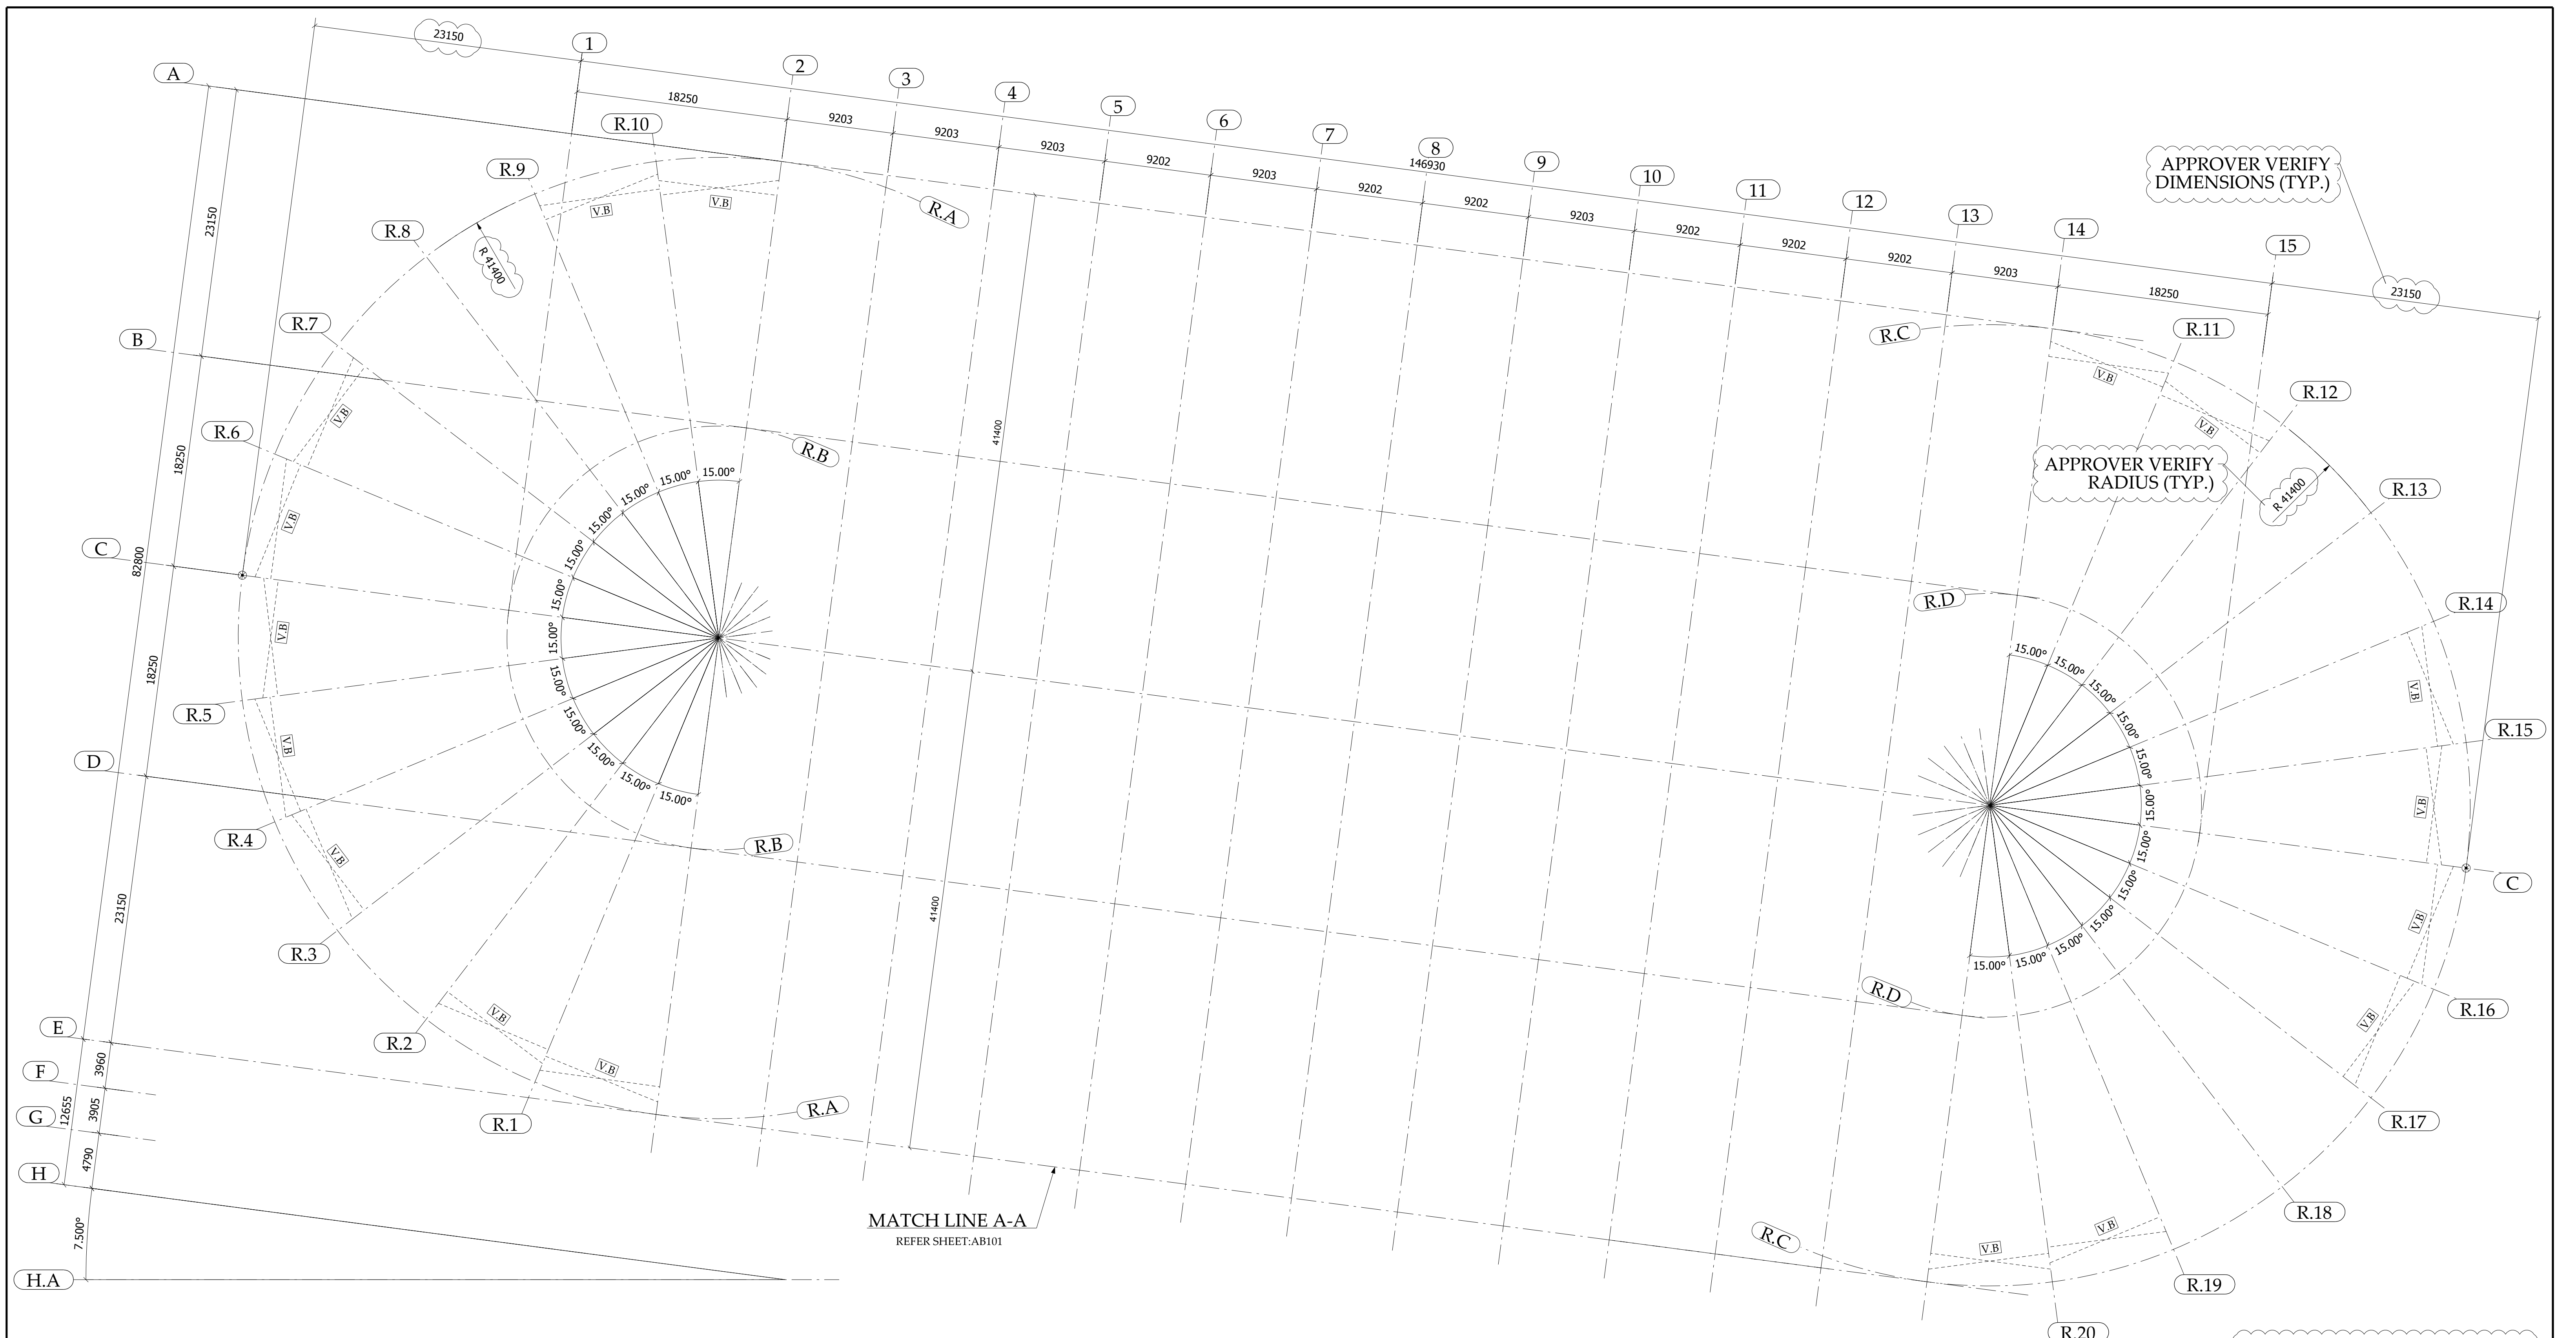

PARTIAL GRID LAYOUT PLAN AREA 'A' & 'B'
(REF. SHEET: S1100)


NOTES:

1. TOP OF GROUND FLOOR EL.10,000 mm = DATUM ELEVATION.
2. ALL UNDER SIDE OF BASE PLATE ELEVATIONS SHOWN AT COLUMN LOCATIONS ARE REFERRED FROM DATUM ELEVATION.
3.  -INDICATES VERTICAL BRACING
4. REFER AB114 & AB115 FOR BASE PLATE & ANCHOR ROD DETAILS.

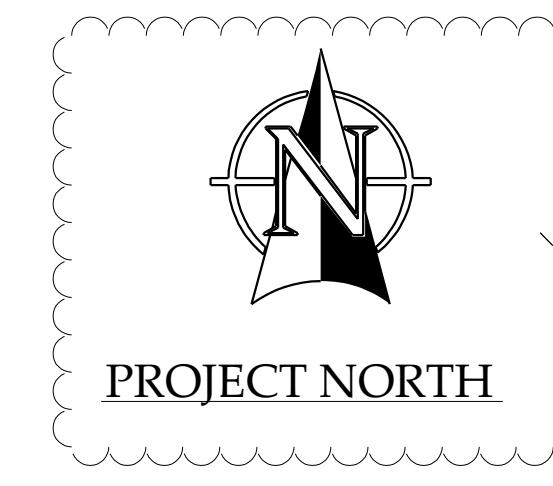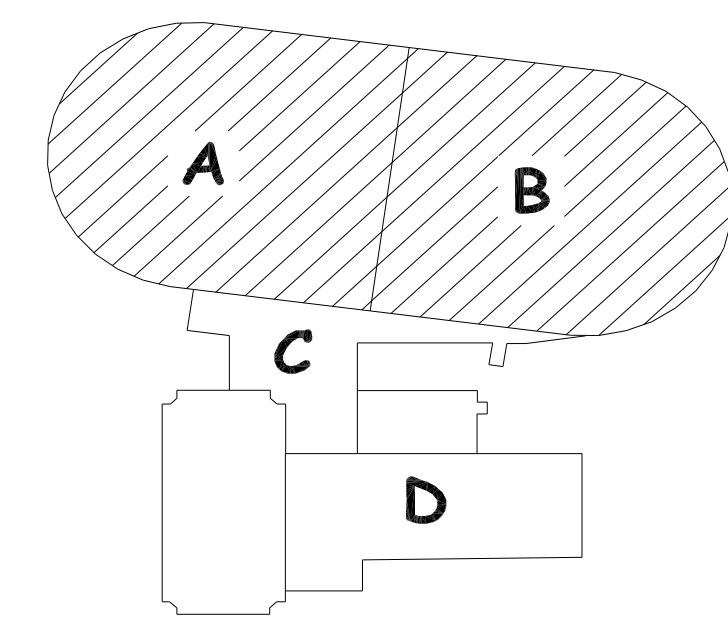

APPROVER VERIFY
NORTH DIRECTION


APPROVER VERIFY/FURNISH
ALL CLOUDED INFORMATIONS

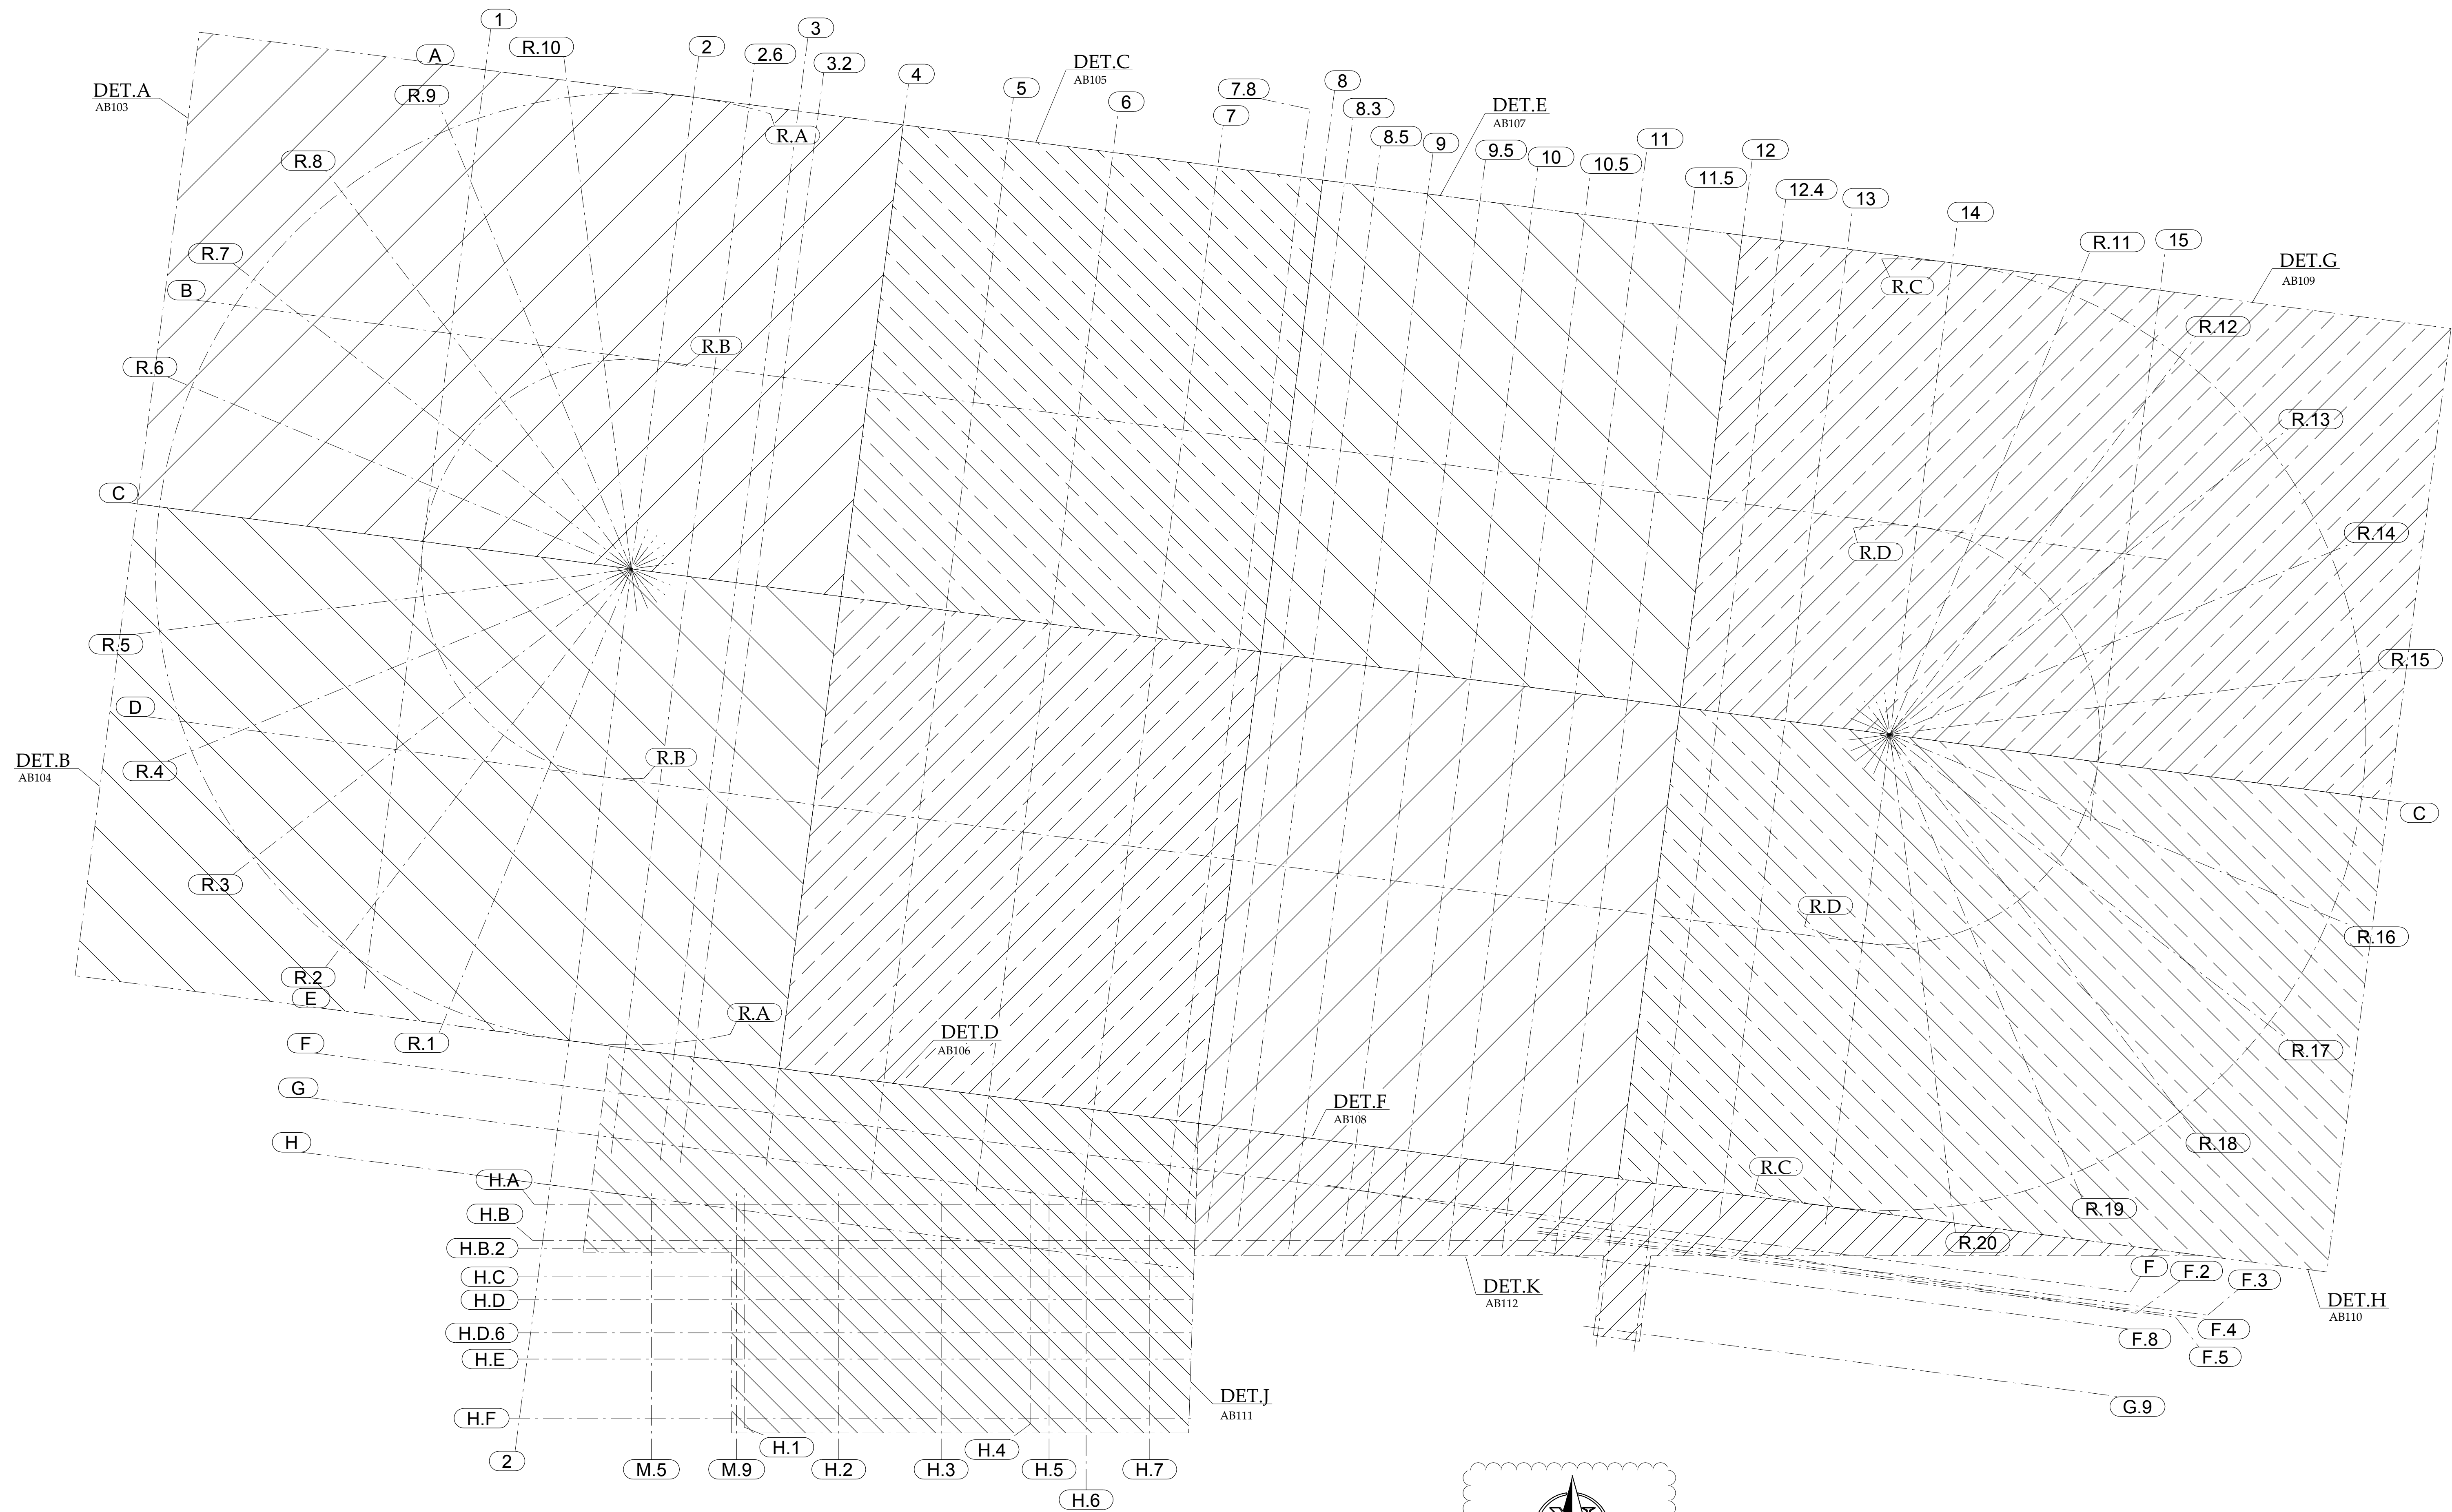


ANCHOR BOLT KEY PLAN
(REF. SHEET: S1100)




APPROVER VERIFY
NORTH DIRECTION

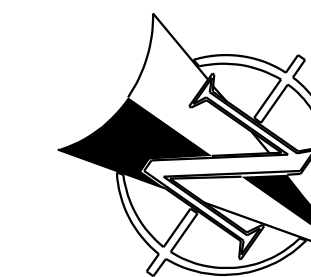

PROJECT NORTH

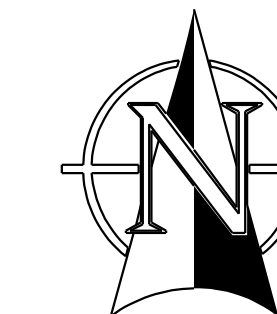

WORKING NORTH

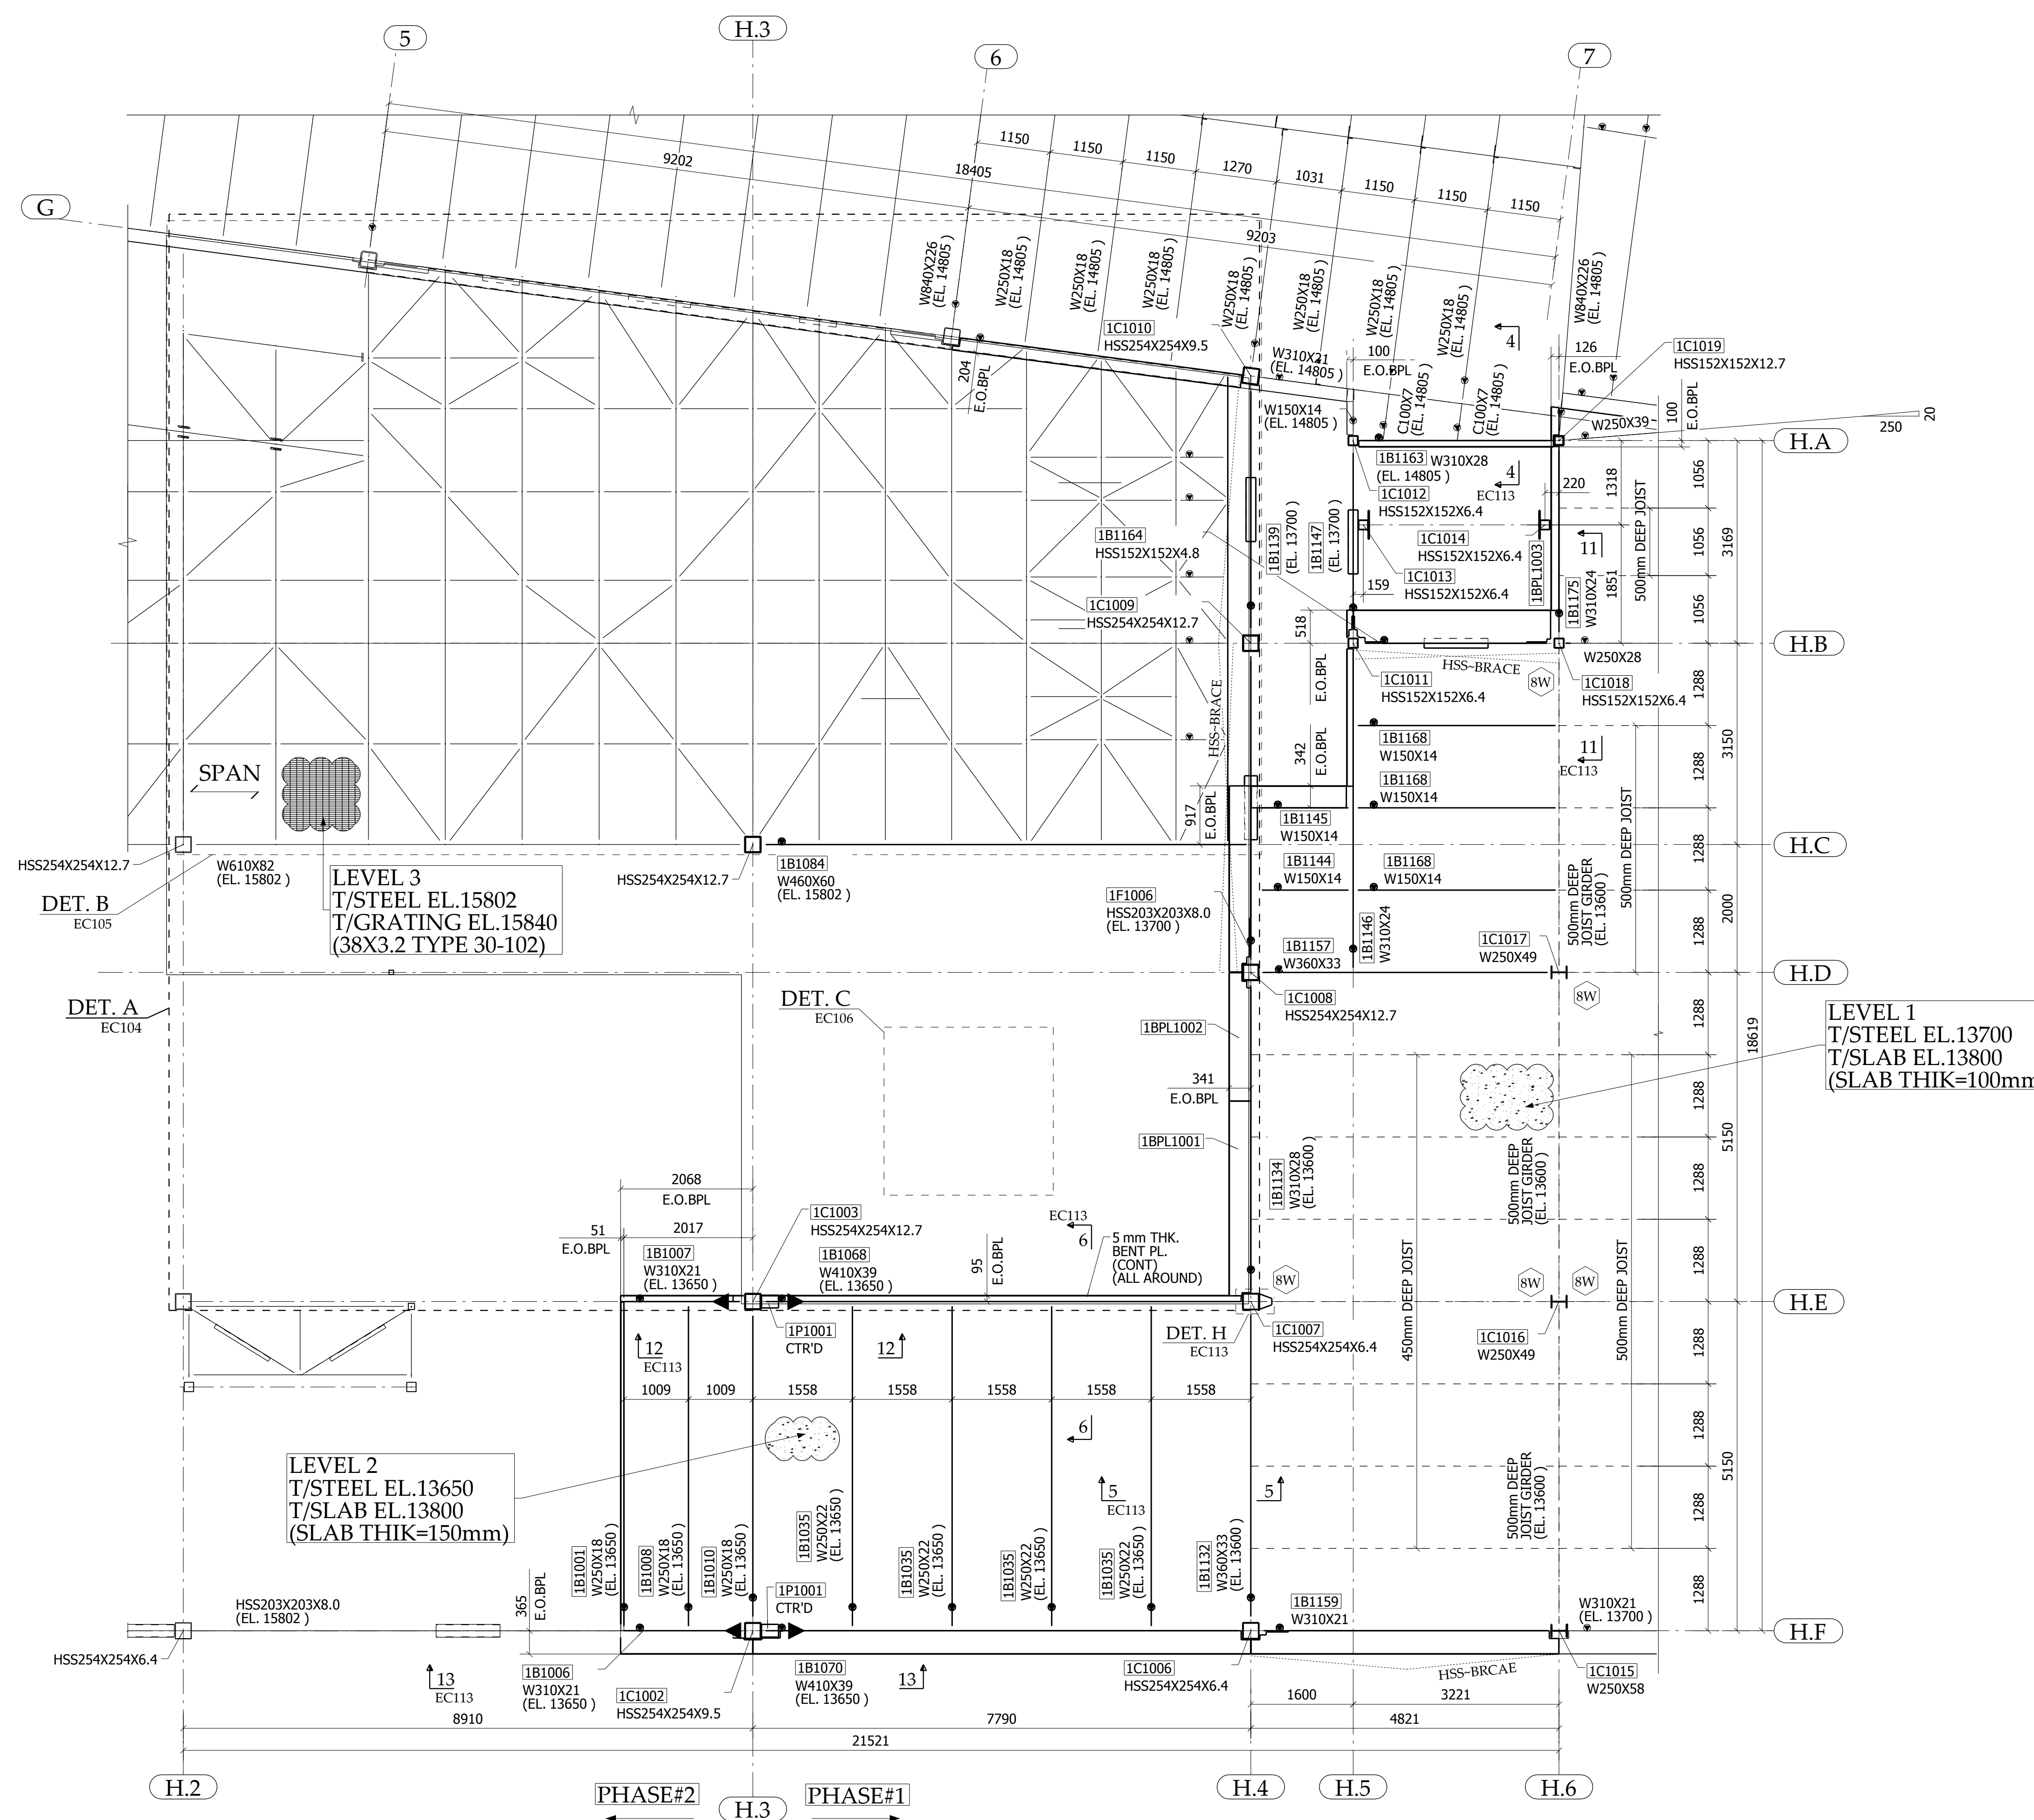

NOTES:



1. -INDICATES ORIENTATION OF MEMBER.
2. -INDICATES MOMENT CONNECTION
3. -INDICATES HSS-BRACING
4. E.O.BPL - INDICATES EDGE OF BENT PLATE
E.O.A - INDICATED EDGE OF ANGLE
E.O.G - INDICATED EDGE OF GRATING
5. (A)-INDICATES ABOVE,(B)-INDICATES BELOW
(S)-INDICATES SLOPES.
6. (LSV)-LONG SIDE VERTICAL,(LSH)-LONG SIDE HORIZONTAL

LEVEL 1 & LEVEL 2 FRAMING PLAN-PHASE#1


(REF. SHEET: S1300)



PROJECT NORTH

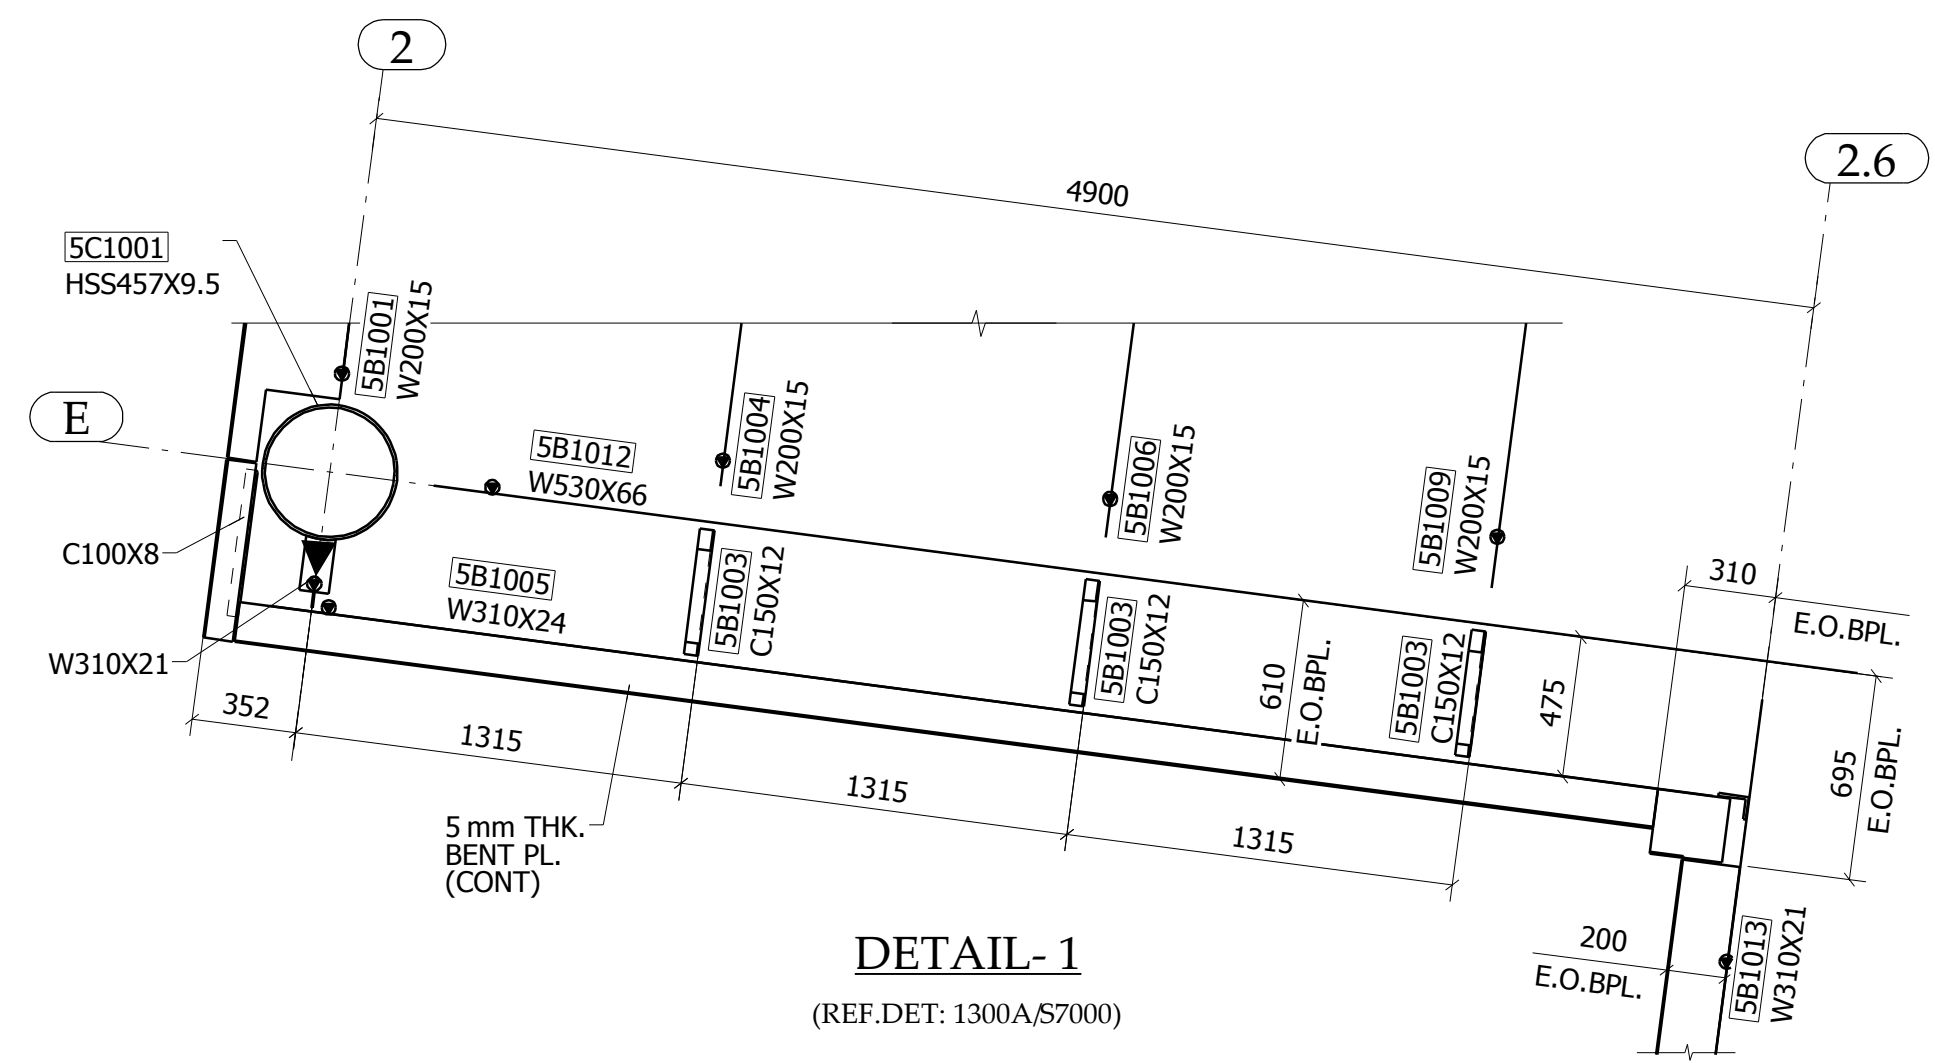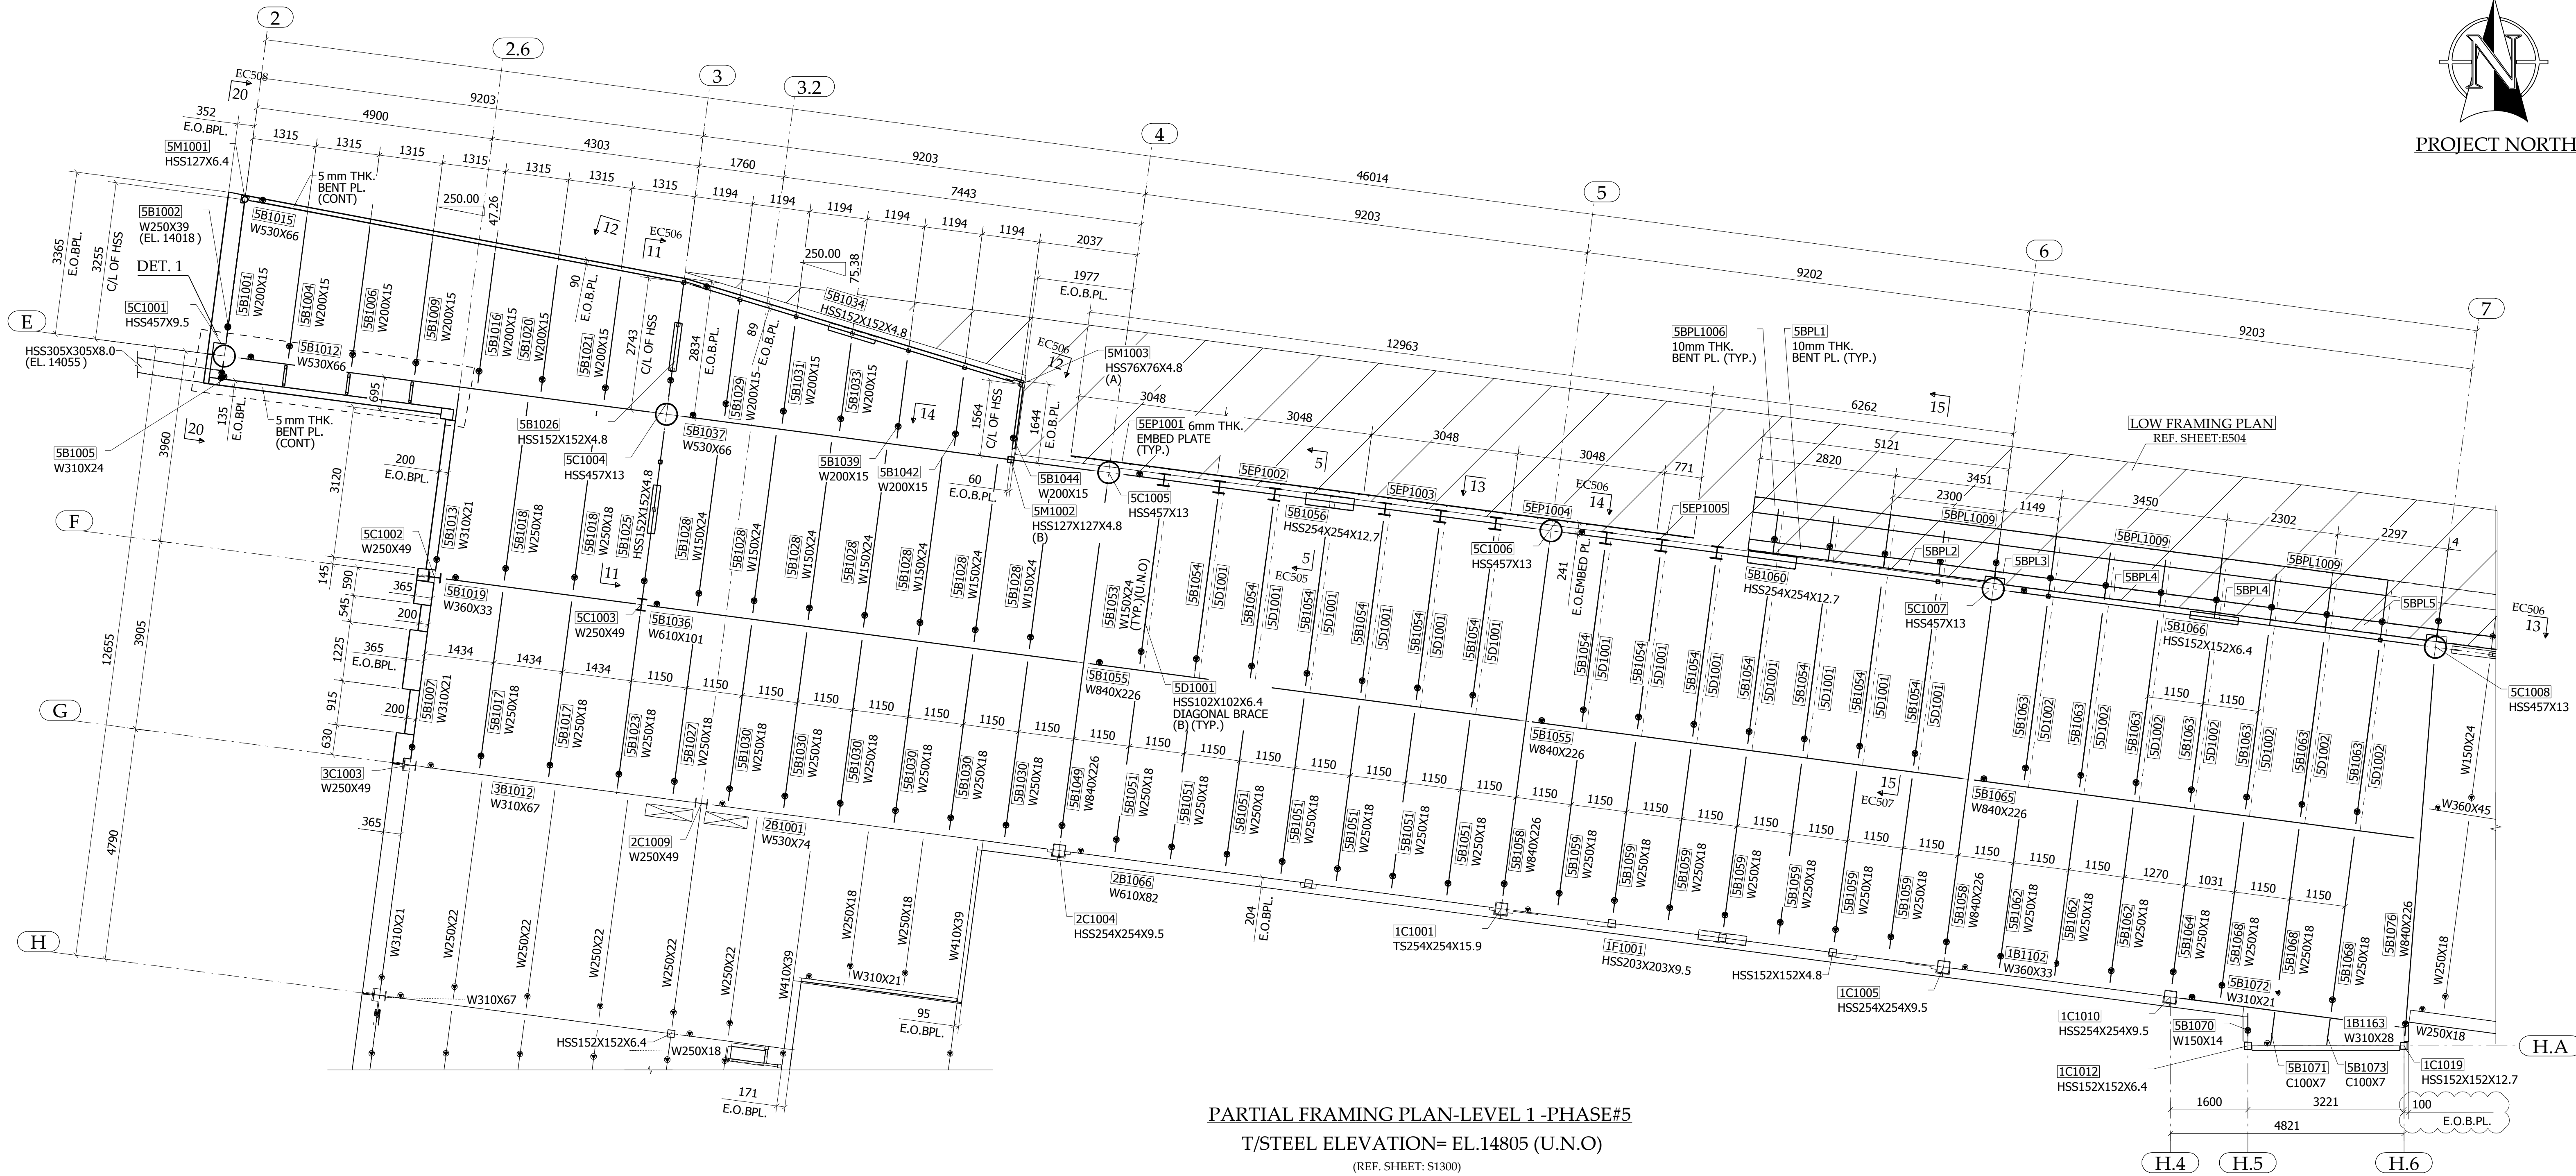

- NOTES:
1. ELEVATIONS SHOWN IN PLAN ARE REFERRED TO TOP OF STEEL ELEVATIONS TYP. (U.N.O).
 2. ▼ - INDICATES ORIENTATION OF THE MEMBER.
 3. ◀ - INDICATES MOMENTS CONNECTION.
 4. (A) - INDICATES ABOVE, (B) - INDICATES BELOW
(S) - INDICATES SLOPES.

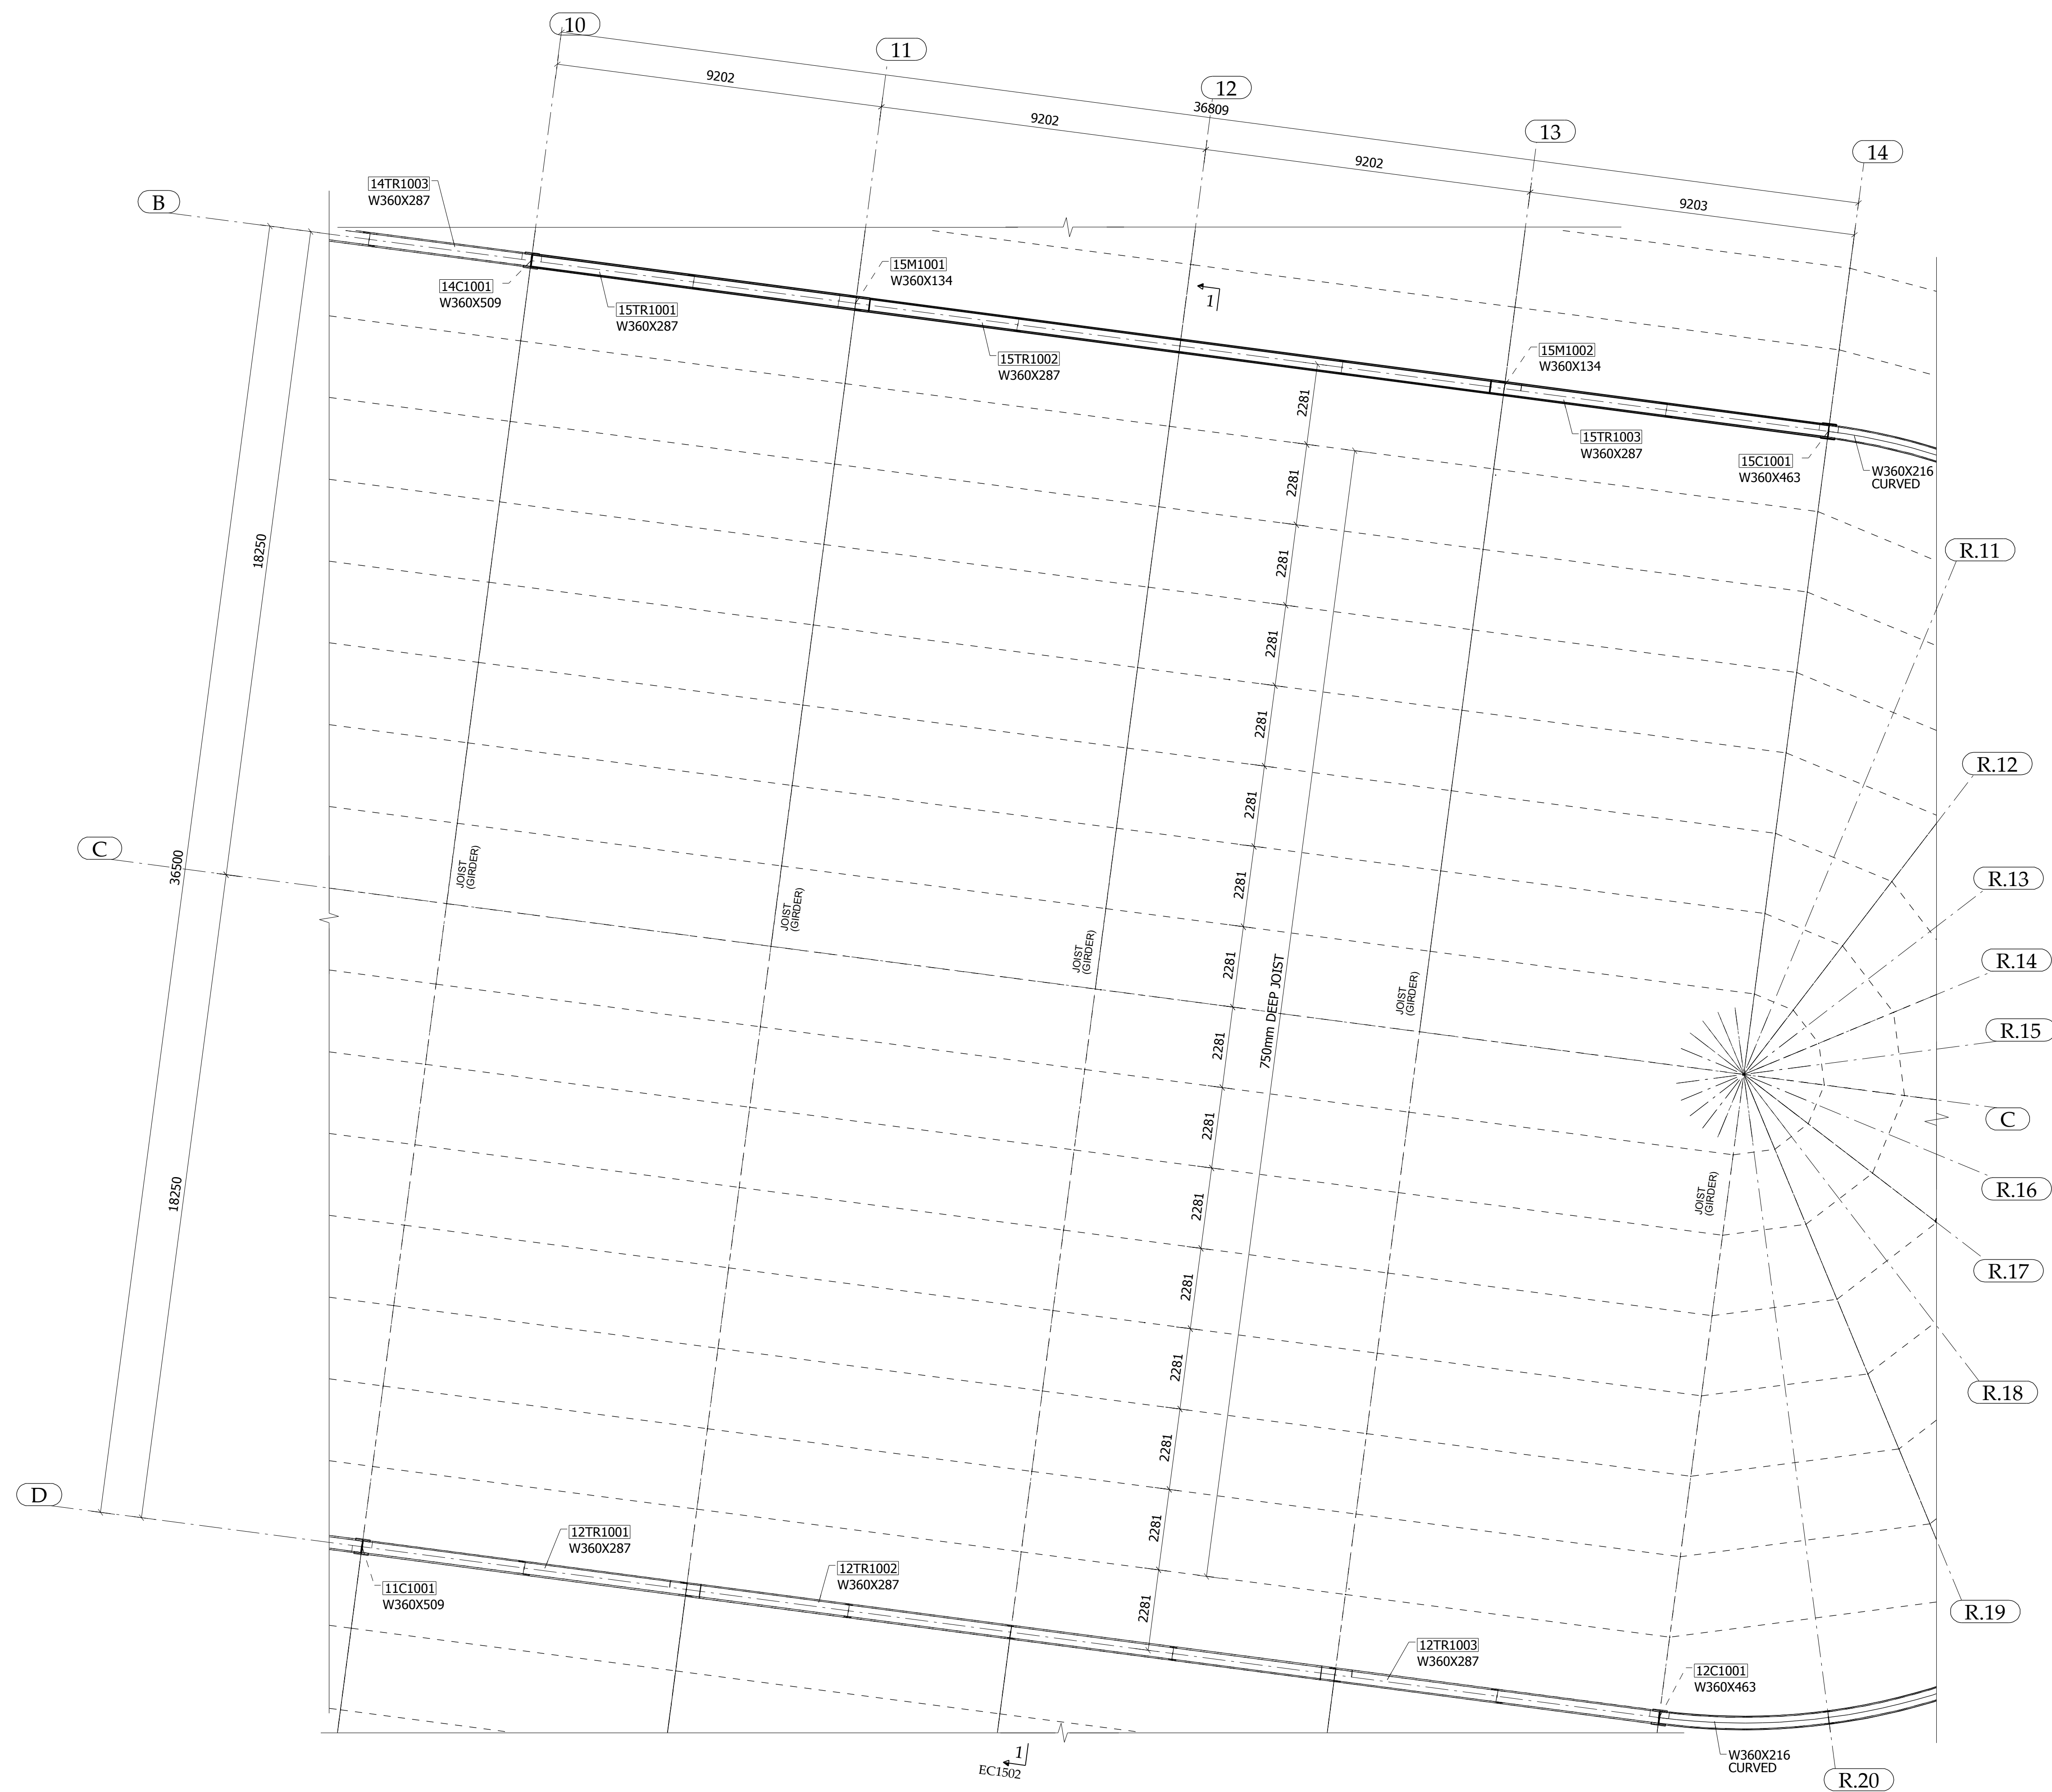

ROOF FRAMING PLAN (PHASE-15)
(SECTOR A&B)
(REF. SHEET: S1420)



ALL GRATINGS ARE
SHOP WELDED WITH FRAME


1. $\longleftarrow$ - INDICATES DIRECTION OF GRATING SPAN
2. E.O.G. - INDICATES EDGE OF GRATING



(REF. SHEET: 1420)




-
- 3 mm THK. BENT PL. (CONT.)
- W~ BEAM
- 5.00 mm THK. STIFF. PL.
- L76X76X6.4 (CONT.)
- SECTION A - A**

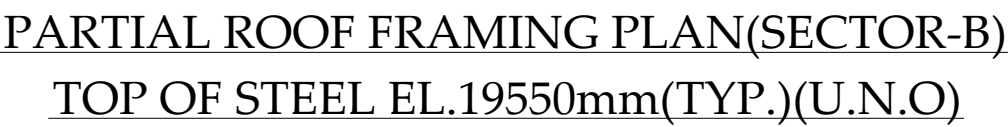

(REF. SHEET: 1420)




PROJECT NORTH

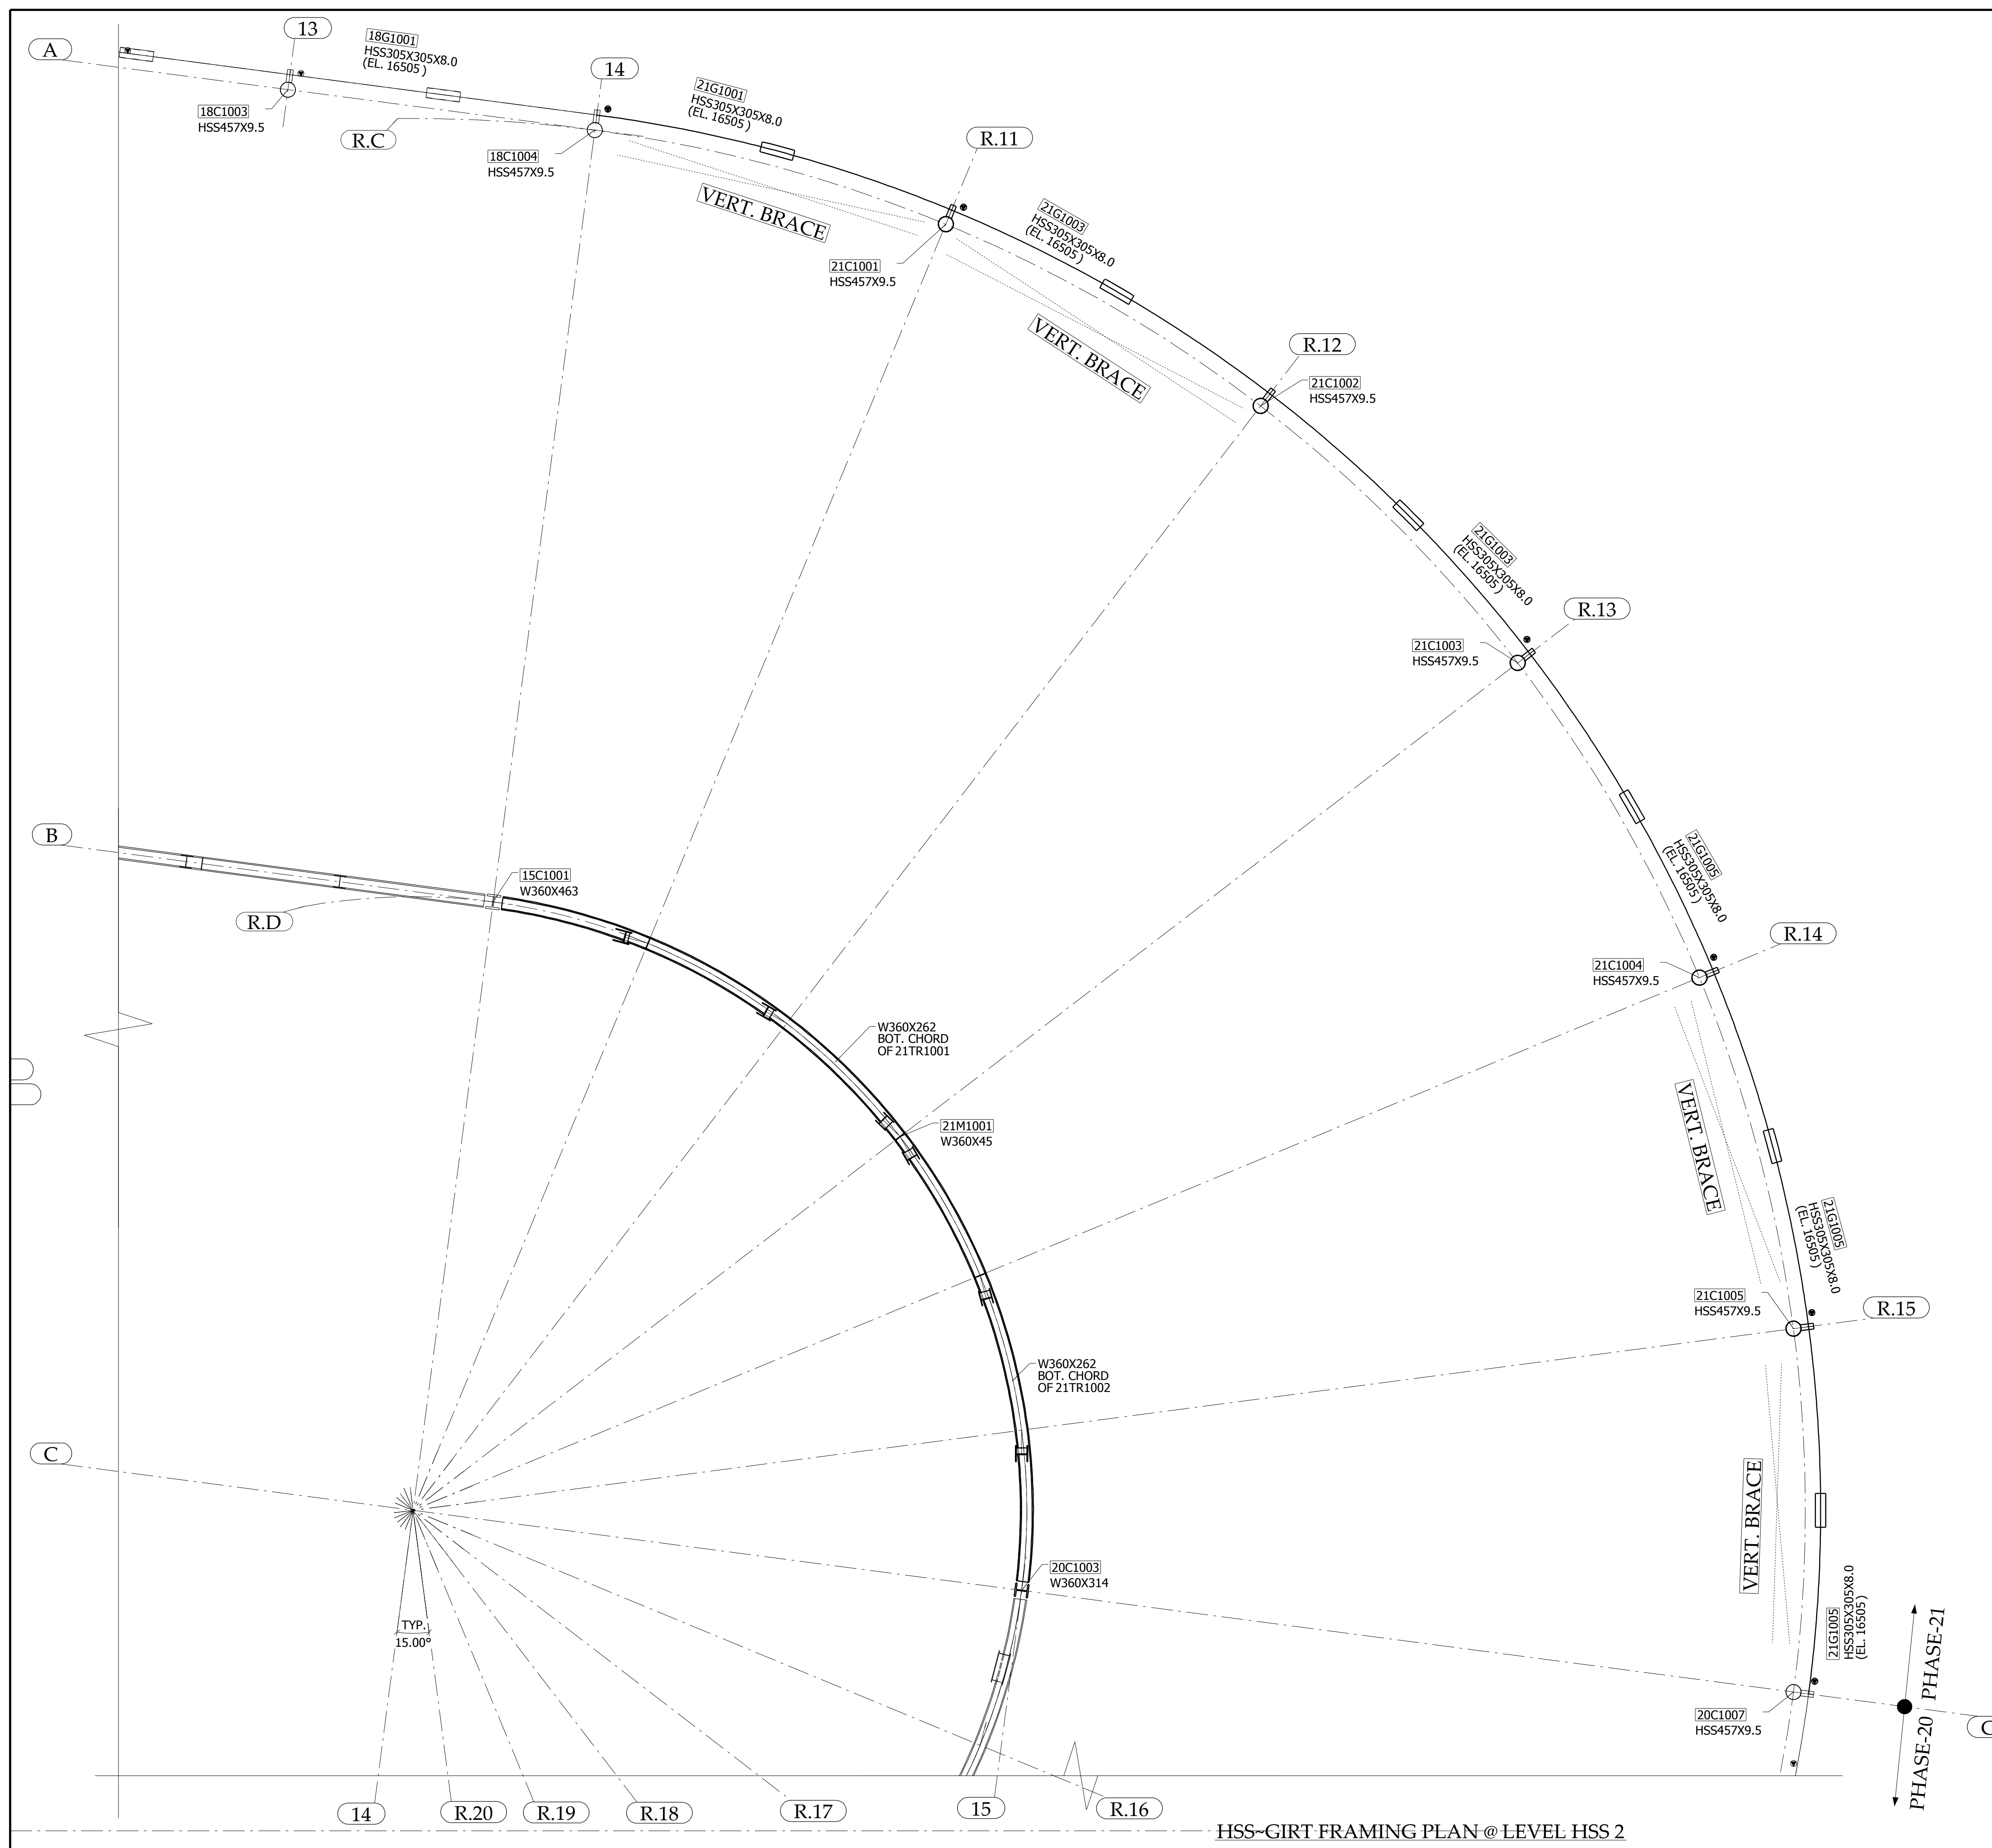


- NOTES:
- 1.ELEVATION SHOWN IN PLAN ARE REFERED TO TOP OF STEEL ELEVATION
 2. ▼ -INDICATES ORIENTATION OF THE MEMBER




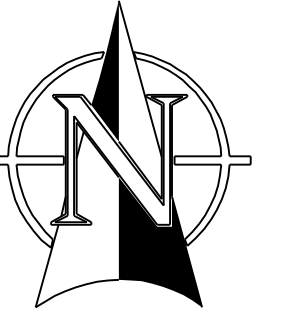


PROJECT NORTH

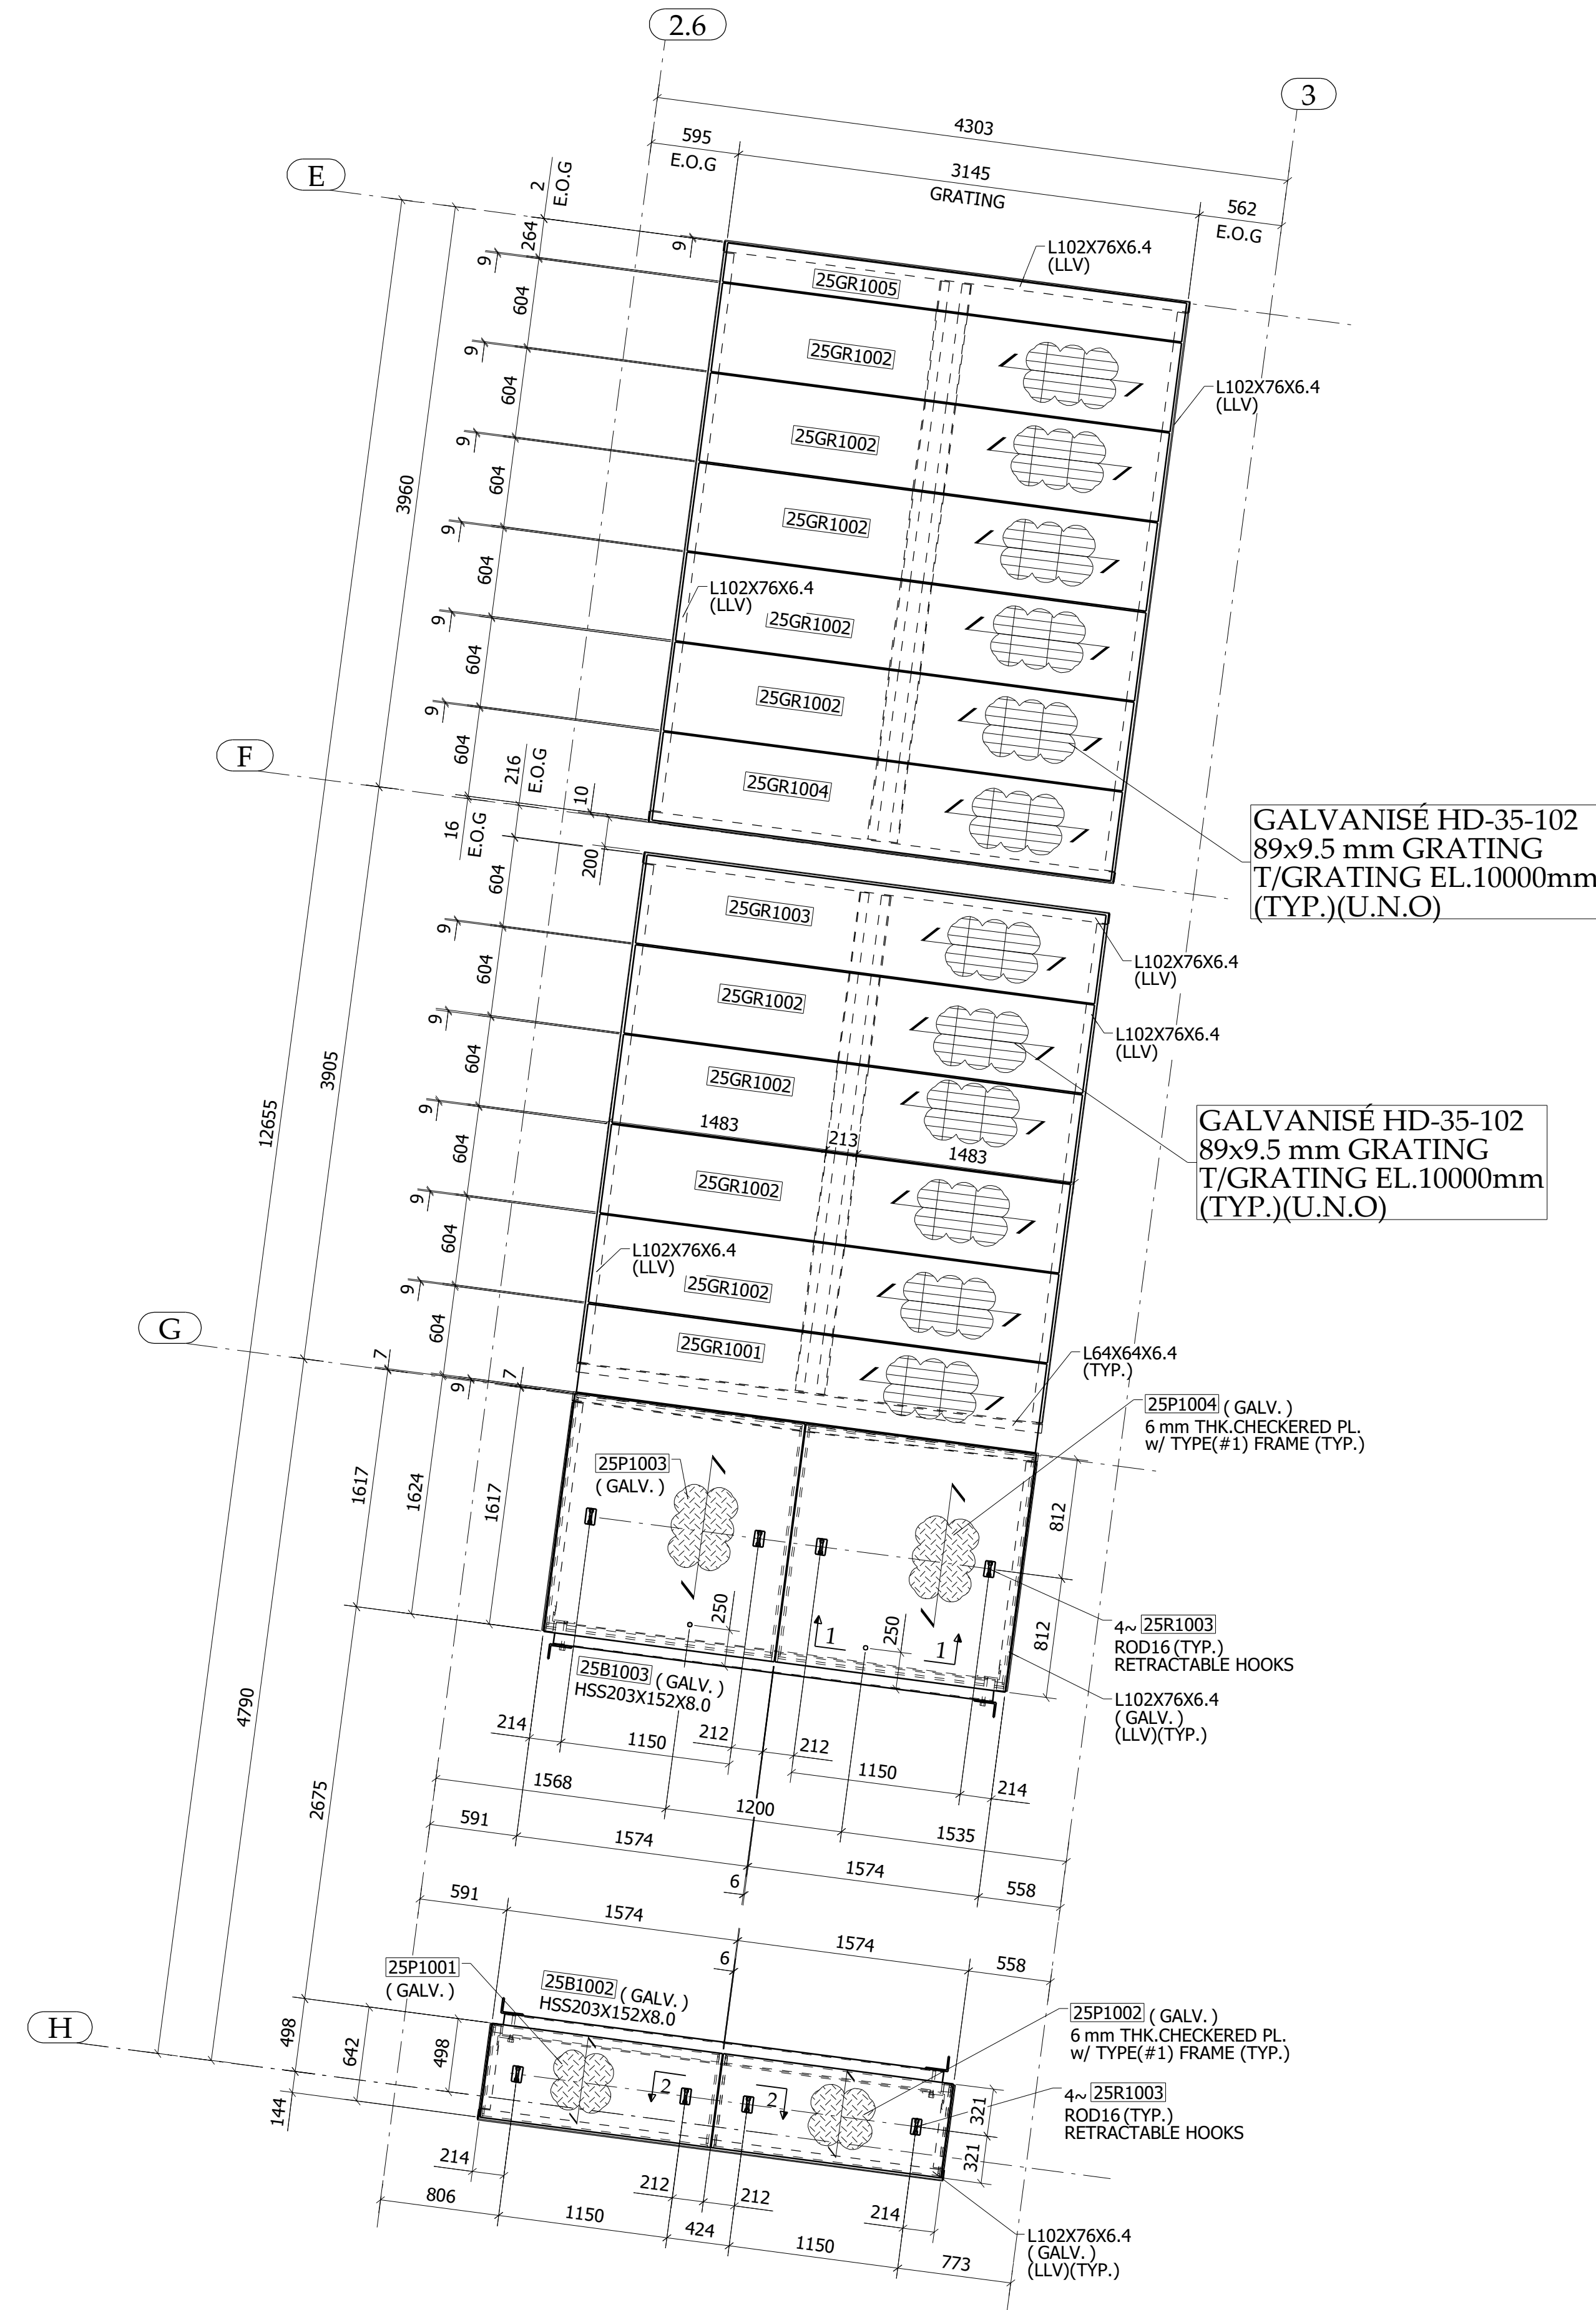


SNOW PIT SUPPORT GRATING FRAMING PLAN (SECTOR C)
T/GRATING EL.10000mm TYP. (U.N.O.)
(REF. SHEET: 5003A/5003)

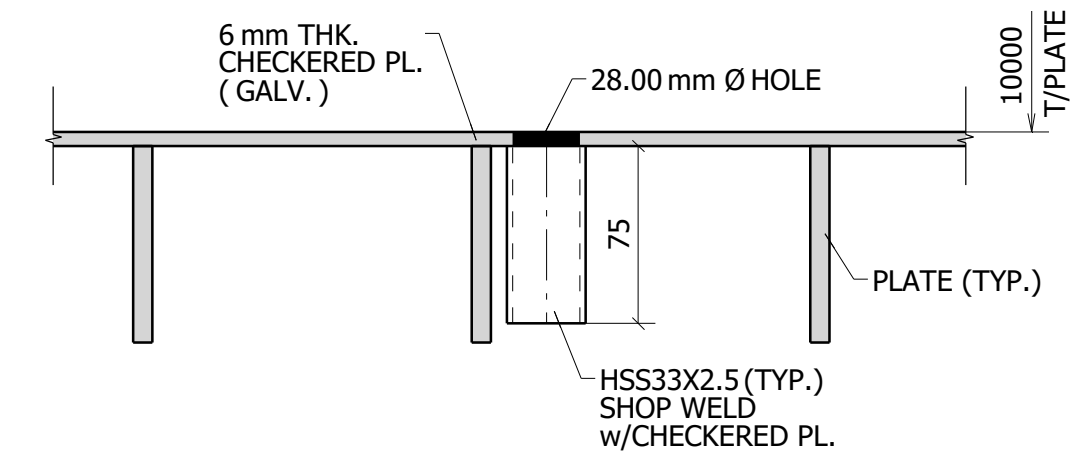

SECTION 1 - 1
TUBULAR TUBE TYPICAL DETAIL
(REF. SEC: 5003P/5003)

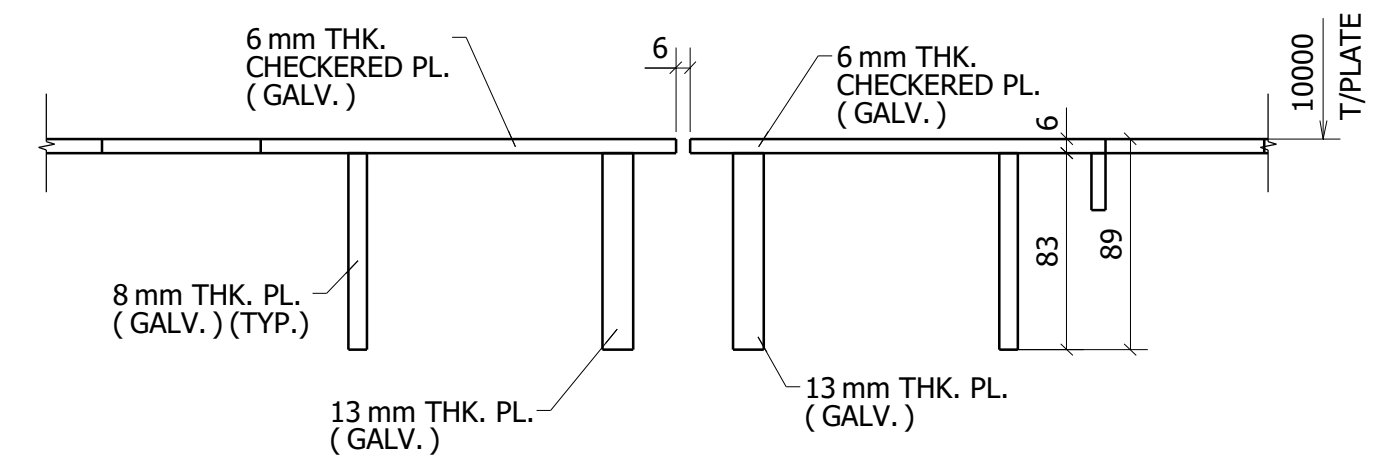


SECTION 2 - 2
TYPICAL PLATE ARRANGEMENT DETAIL
(REF. SEC: 5003D/5003)


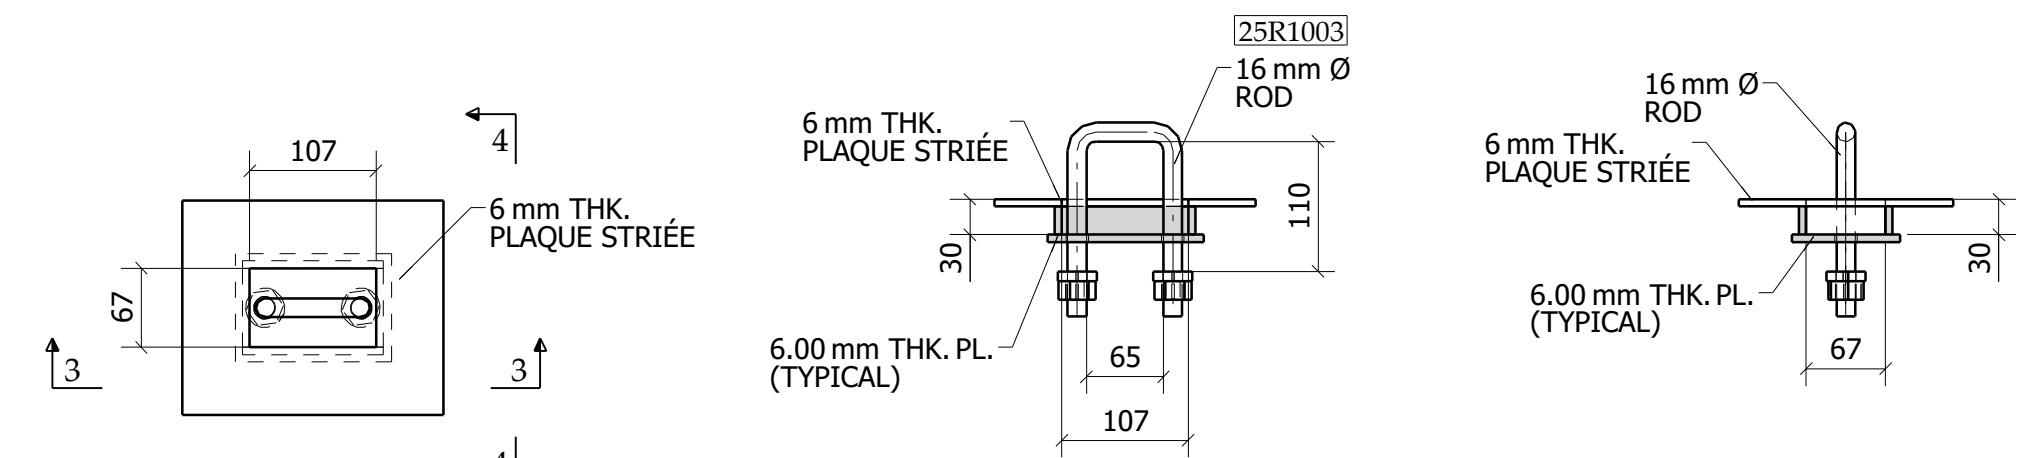


SECTION 3 - 3
RETRACTABLE HOOK DETAIL
(REF. SEC: 5003Q/5003)

SECTION 4 - 4

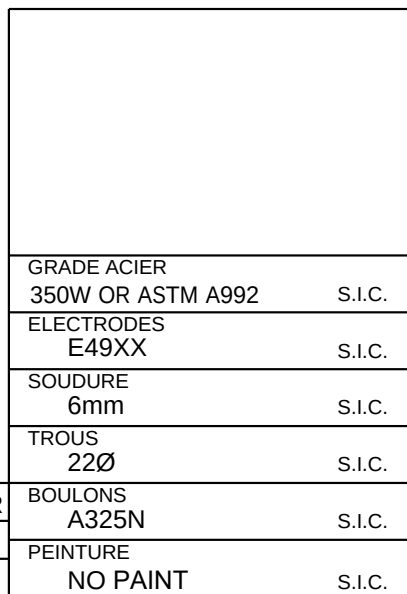

DATE	NO.	DESCRIPTION	PAR	BOULONS A325N S.I.C.	
08/24/2022	0	FOR FIELD USE		PEINTURE NO PAINT	S.I.C.
05/05/2022	1	FOR APPROVAL			

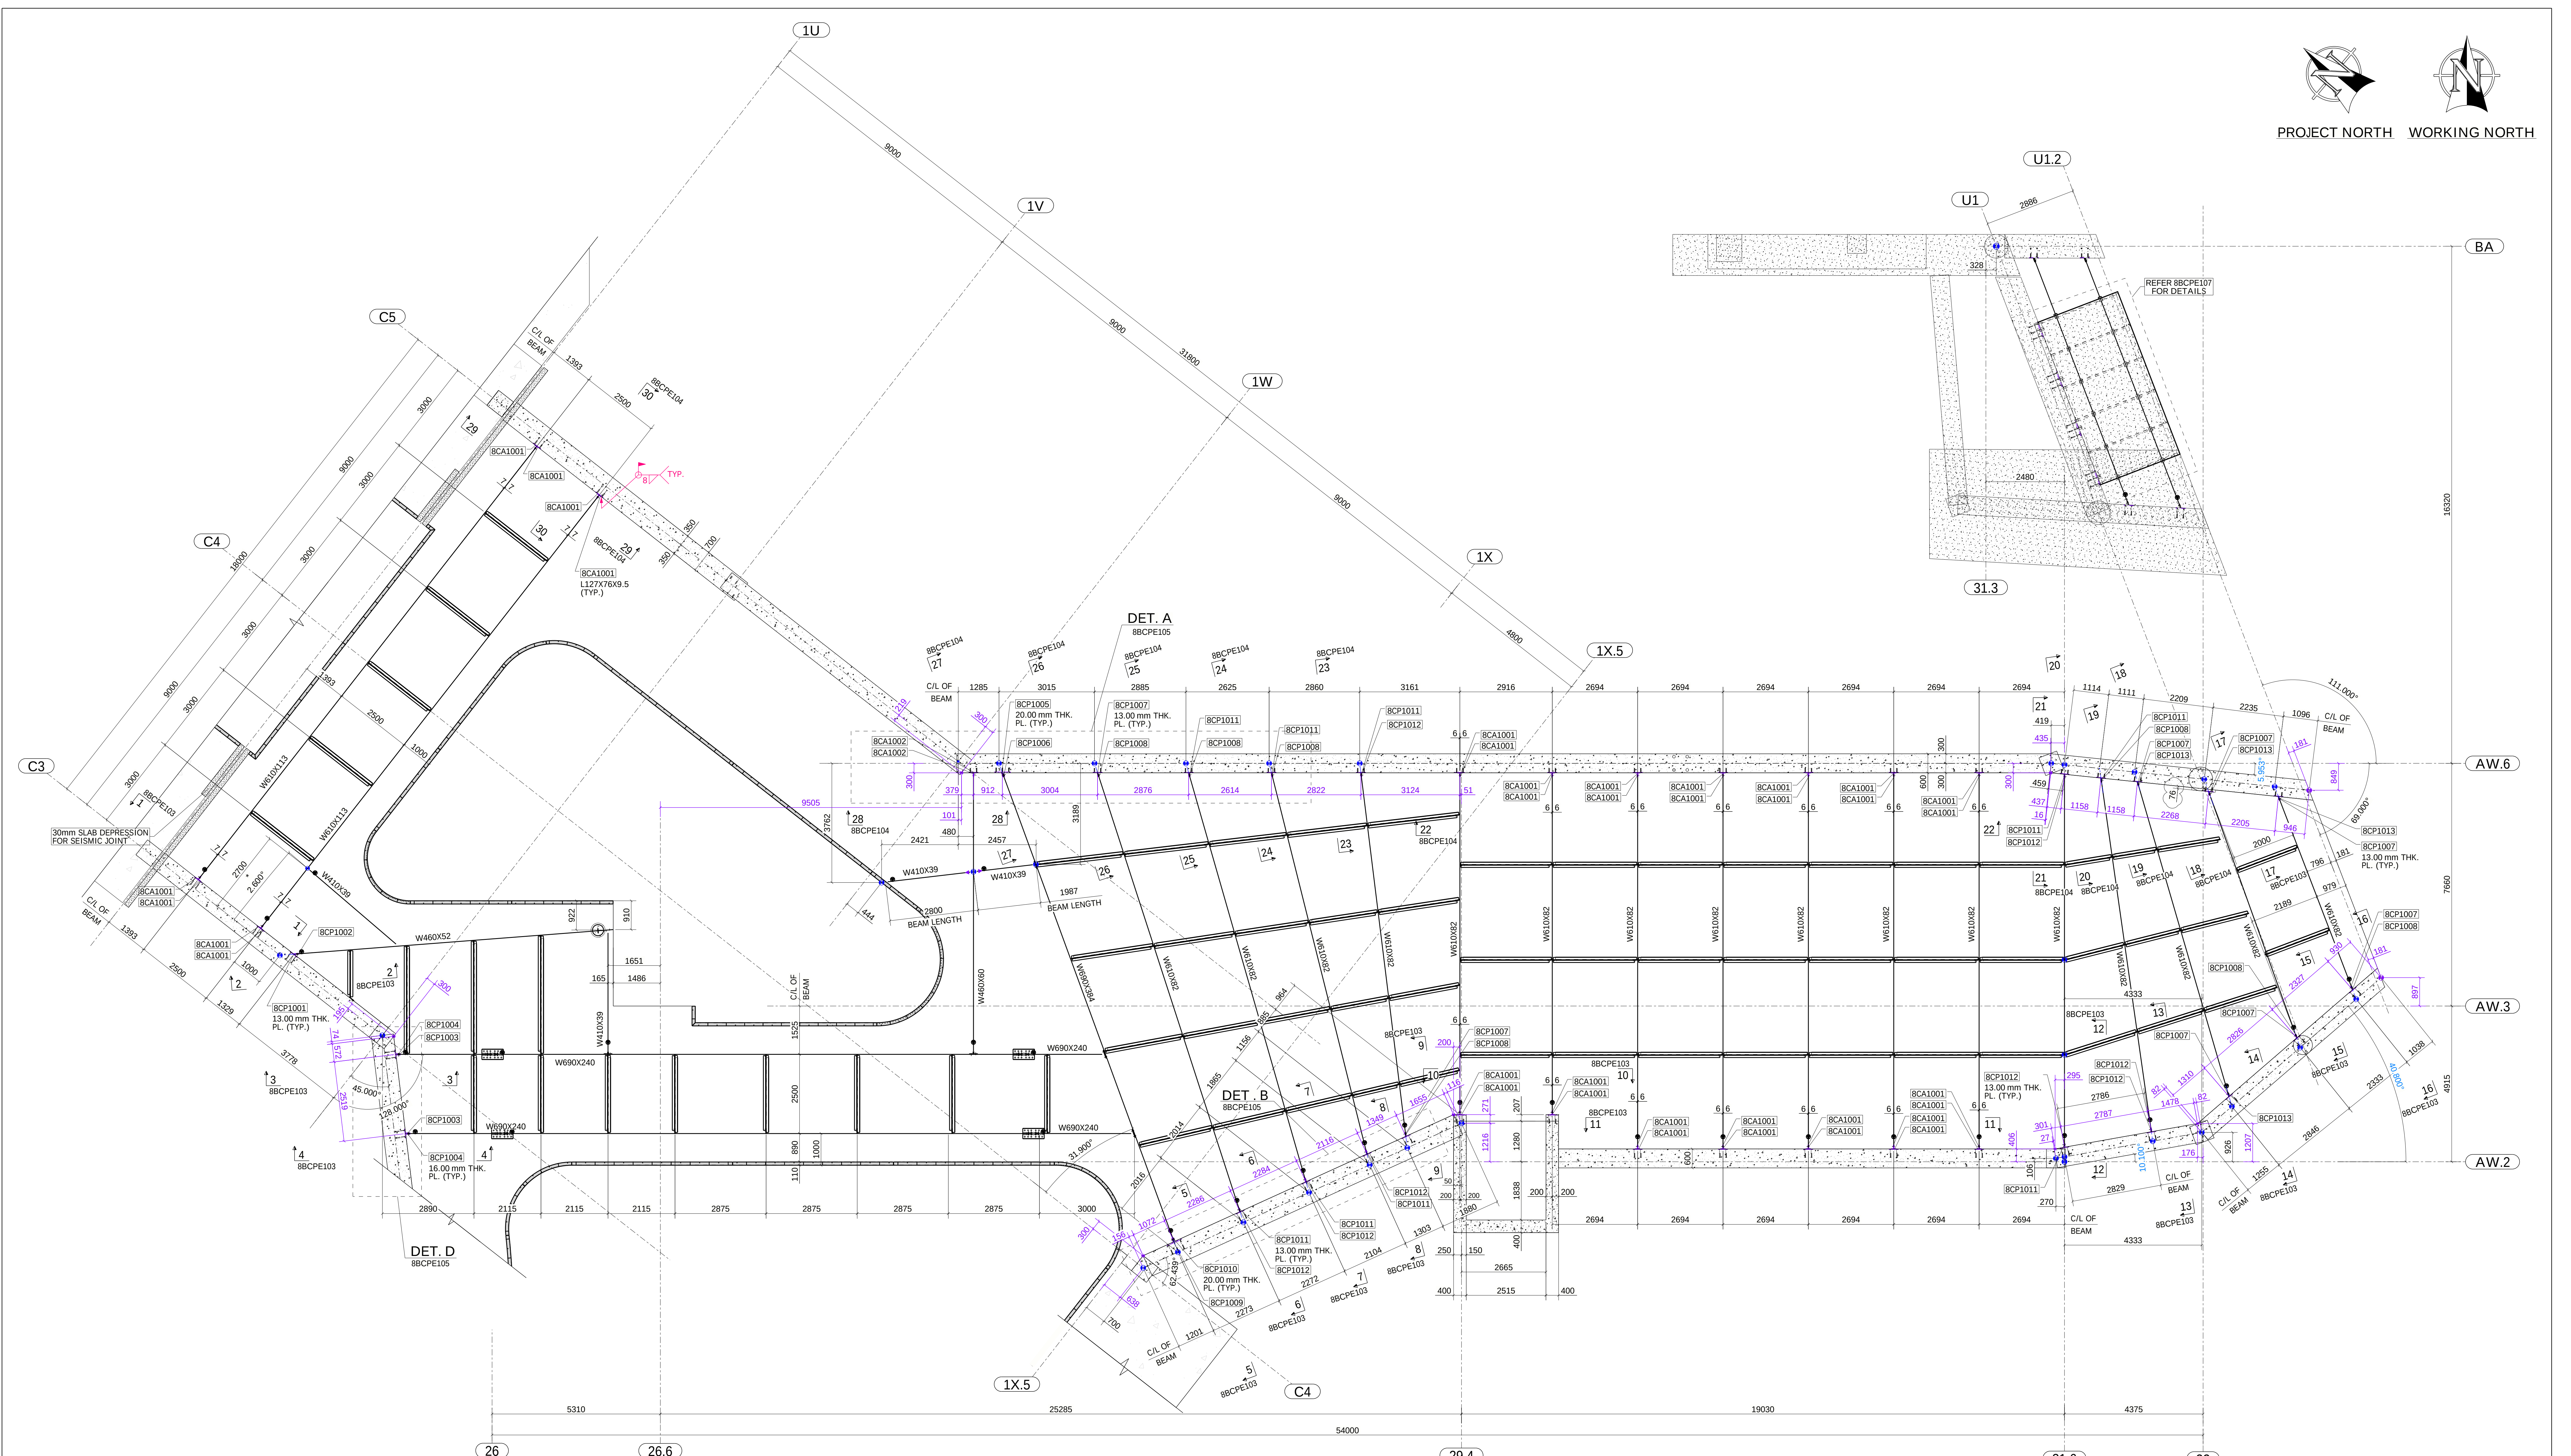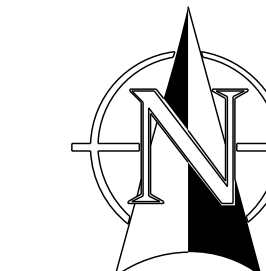

PARTIAL CONNECTION ANGLE LOCATING PLAN @ LEVEL-M2 (SECTOR B)

T/STEEL = U/S DECK ELEVATION =52310mm (U.N.O)

(REFER SHEET: S-B-1424)

	GRADE ACIER	
	350W	S.I.C
	ELECTRODES	
	E49XX	S.I.C
	SOUDURE	
	6mm	S.I.C
PAR	TROUS	
	22Ø	S.I.C
	BOULONS	
	A325N	S.I.C
	PEINTURE	
	NO. PAINT	S.I.C

DATE	NO.	DESCRIPTION	PAR
01/10/2023	1	FOR FINAL FIELD USE	
12/12/2022	0	FOR FIELD USE	
09/11/2022	4	FOR APPROVAL	



PROJECT NORTH WORKING NORTH



PARTIAL EMBED LOCATING PLAN @ LEVEL-M2 (SECTOR-F)
T/STEEL = U/S DECK ELEVATION =52310mm (U.N.O)
T/SLAB ELEVATION = 52530mm (U.N.O)
 (REFER SHEET: S-F-1432)

				220	S.I.C.
DATE	NO.	DESCRIPTION	PAR	BOULONS A325N	S.I.C.
07/06/2022	0	FOR FIELD USE			
06/13/2022	1	FOR APPROVAL		PEINTURE 1-73/A PRIMER	S.I.C.

	GRADE ACIER 300W	S.I.C
	ELECTRODES E49XX	S.I.C
	SOUDURE 6mm	S.I.C
	TROUS 22Ø	S.I.C
PAR	BOULONS A325N	S.I.C
	PEINTURE 1-73/A PRIMER	S.I.C



PARTIAL LIFELINE LOCATING PLAN @ ROOF LEVEL (SECTOR-A)(PHASE#2)

T/STEEL = H.P = U/S DECK ELEVATION = 62880mm (U.N.O)

T/STEEL = L.P = U/S DECK ELEVATION = 62730mm (U.N.O)


(REFER SHEET: S-A-1623)

ONLY FOR SHOWING LIFELINE SUPPORTS LOCATING DIMENSIONS.

				GRADE ACHR	S.I.C.
				350W	S.I.C.
				ELECTRICALS	S.I.C.
				E48XX	S.I.C.
				WOODWORK	S.I.C.
				6mm	S.I.C.
				TRUCK	S.I.C.
				220	S.I.C.
				BOULDER	S.I.C.
				A32N	S.I.C.
				PERITURE	S.I.C.
				1-23A PRIMER	S.I.C.
DATE	NO	DESCRIPTION		PAR	
02/22/2023	1	FOR FIELD USE			
02/07/2023	2	FOR APPROVAL			




WORKING NORTH

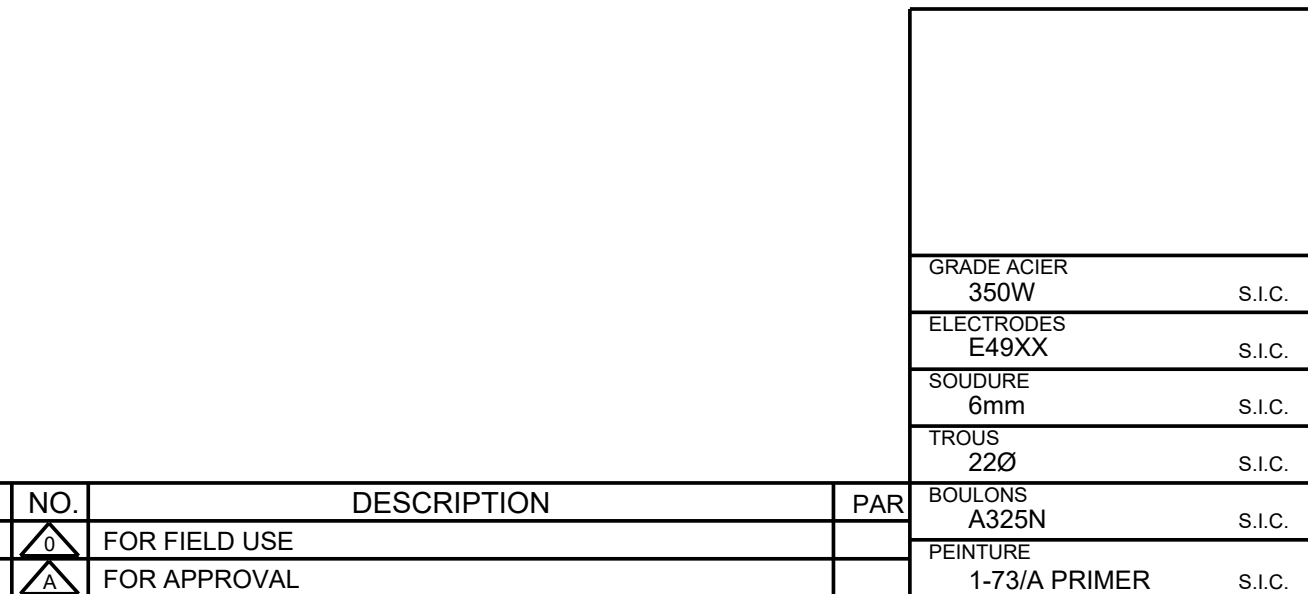

(REFER SHEET: S-A-1612 & S-A-1623)

DATE	NO.	DESCRIPTION	PAR	220	S.I.C.
02/06/2023		FOR FIELD USE		BOULONS A325N	S.I.C.
10/31/2022		FOR APPROVAL		PEINTURE 1-73/A PRIMER	S.I.C.

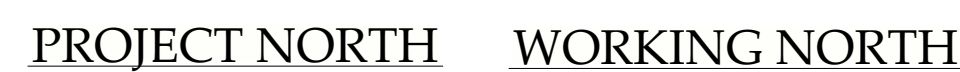

DATE	NO.	DESCRIPTION	PAR
01/10/2023	1	FOR APPROVAL	



WORKING NORTH



ERECTOR NOTE:
1.ERECTOR USE BOTH BE101 AND BE102 FOR ALL DETAILS @ LEVEL T2

#1 -INDICATES MEMBERS ARE INSTALLED WITH
25.40mm Ø BOLTS

NOTES-1:
WE ARE SENDING THEORITICAL ANCHOR LOCATIONS FOR THIS INDICATED COLUMNS.
NEW ANCHORS TO BE PLACED AT THIS THEORITICAL ANCHOR LOCATIONS.


GRADE ACIER	
350W	S.I.C.
ELECTRODES	
E49XX	S.I.C.
SOUDEURE	
6mm	S.I.C.
TROUS	
22Ø	S.I.C.
BOULONS	
A325N	S.I.C.
PEINTURE	
1-73A SHOP PRIMER	S.I.C.

DATE	NO.	DESCRIPTION	PAR	220	S.I.C.
01/11/2023		FOR FIELD USE		BOULONS	
12/21/2022		FOR FIELD USE		A325N	S.I.C.
11/18/2022		FOR APPROVAL		PEINTURE	
				1-73A SHOP PRIMER	S.I.C.



	GRADE ACHIER 350W	S.I.C.
	ELECTRODES E49XX	S.I.C.
	SOUDEURE 6mm	S.I.C.
	TROUS 22Ø	S.I.C.
PAR	BOULONS A325N	S.I.C.
	PERFURE	
	4 73/4 SHOP PRIMER	S.I.C.

DATE	NO.	DESCRIPTION	PAR	BOULONS A325N	S.I.C.
01/26/2023	0	FOR FIELD USE			
12/13/2023	1	FOR APPROVAL		PEINTURE 1.731A SHOP PRIMER S.I.C.	

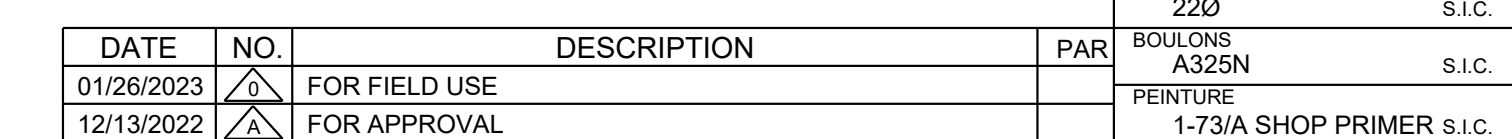




PROJECT NORTH WORKING NORTH




(REFER SHEET: S-B-1624)

	GRADE ACTIER	
	350W	S.I.C
	ELECTRODES	
	E49XX	S.I.C
	SOUDEURE	
	6mm	S.I.C
	TROUS	
	22Ø	S.I.C
PAR	BOULONS	
	A325N	S.I.C
	PEINTURE	
	1.73/A SHOP PRIMER	S.I.C


DATE	NO.	DESCRIPTION	PAR
01/26/2023	0	FOR FIELD USE	
01/06/2023	1	FOR APPROVAL	

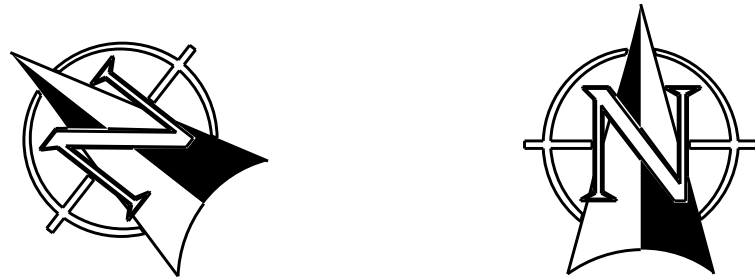


PROJECT NORTH WORKING NORTH

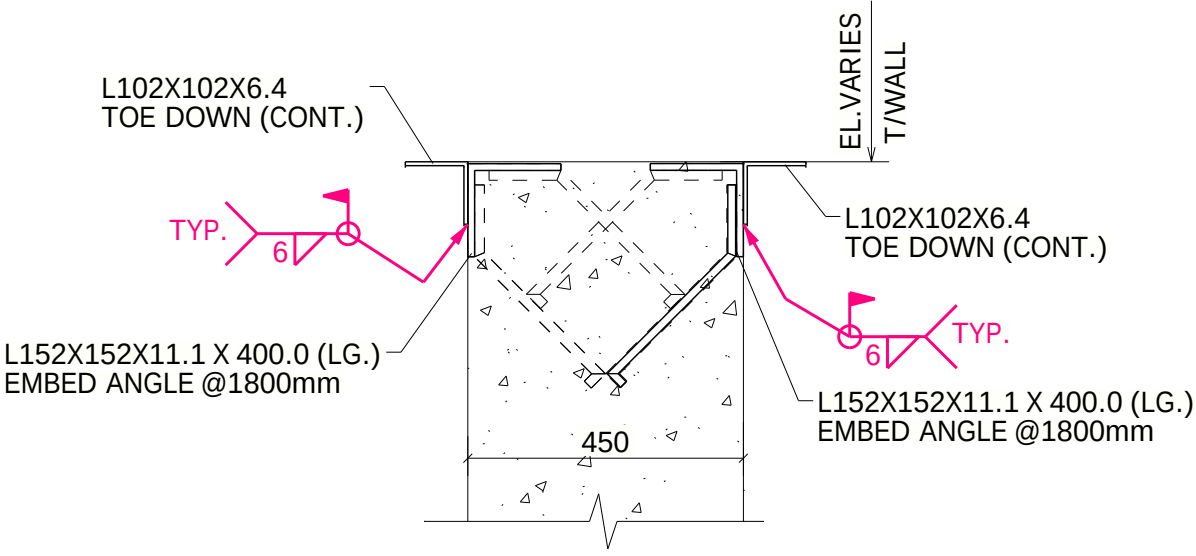

SECTION A - A

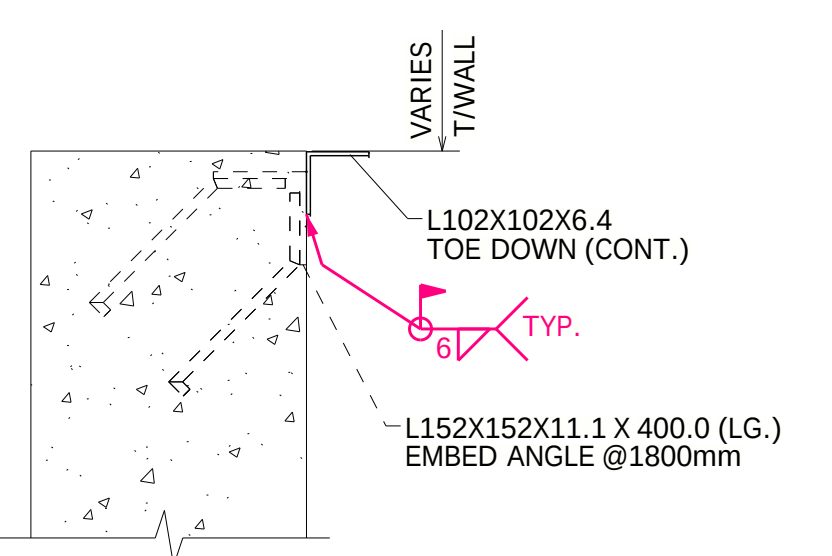

SECTION B - B

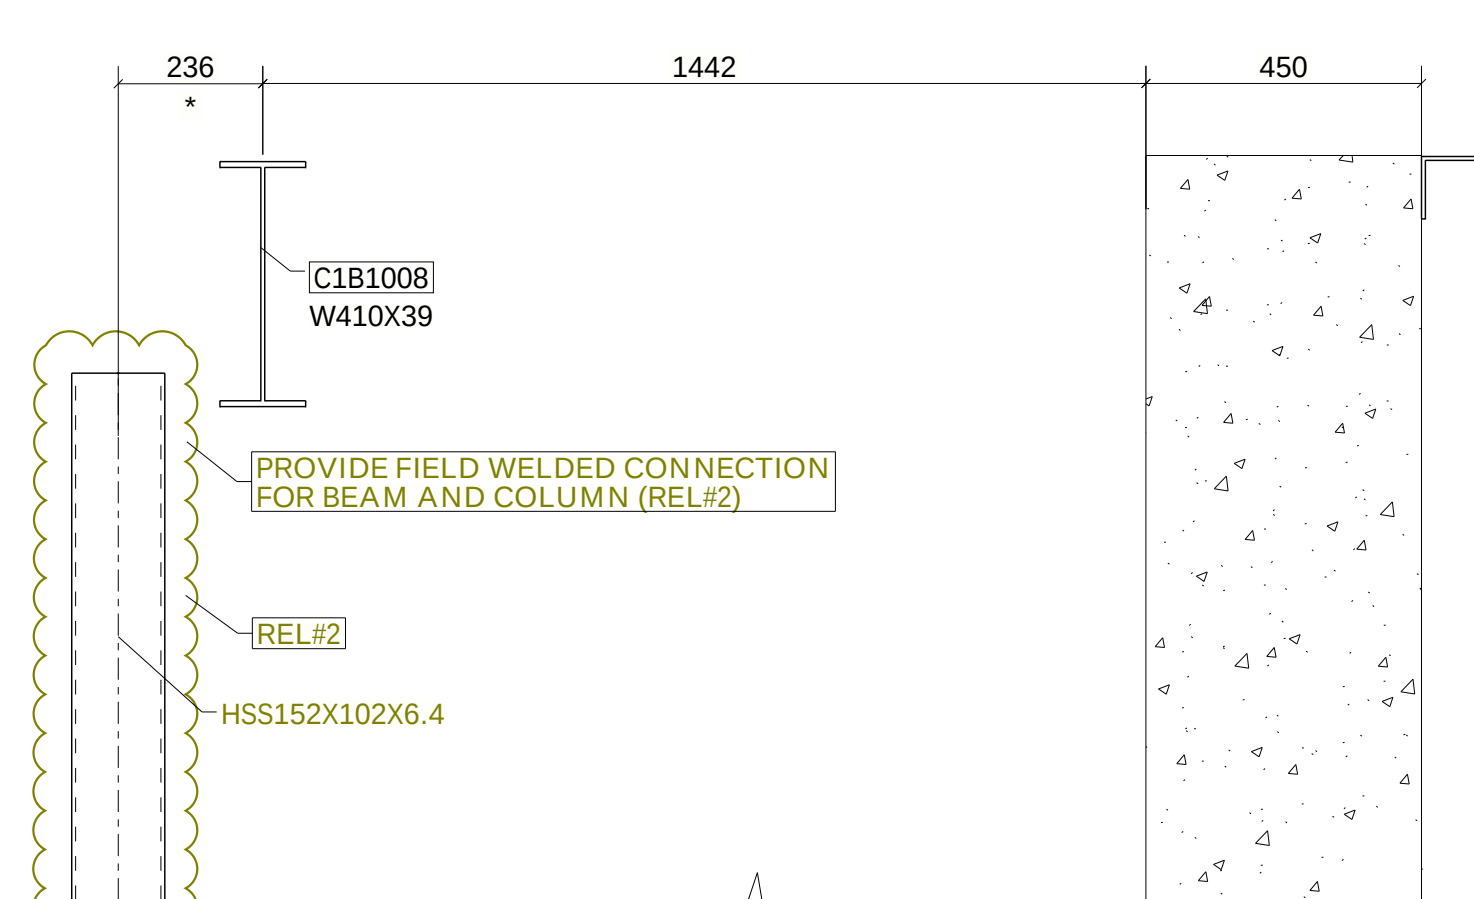

SECTION C - C

FRAMING PLAN @ ROOF LEVEL (SECTOR-C) (PHASE#1)
T/STEEL = U/S DECK HIGH POINT ELEVATION = H.P. = 60770mm (U.N.O.)
T/STEEL = U/S DECK HIGH POINT ELEVATION = L.P. = 60620mm (U.N.O.)
(REFER SHEET: S-C-163A)

DATE	NO.	DESCRIPTION	PAR.
11/07/2022	1	REVISED AS NOTED	
11/01/2022	2	FOR FIELD USE	
08/16/2022	3	FOR APPROVAL	

#2 - INDICATES MEMBERS ARE INSTALLED WITH 25.4mmØ BOLTS

GRADE	ACER
350W	S.I.C.
E48XX	S.I.C.
6mm	S.I.C.
220	S.I.C.
BOLDS	S.I.C.
3-324	SHOP PRIMER S.I.C.