

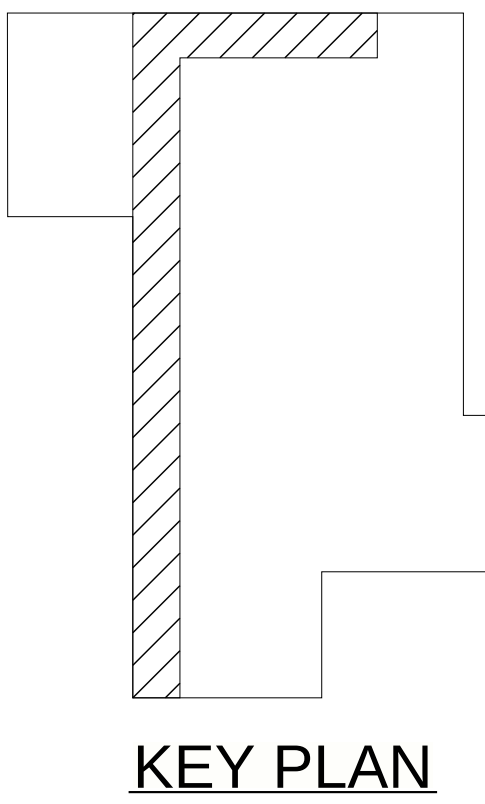
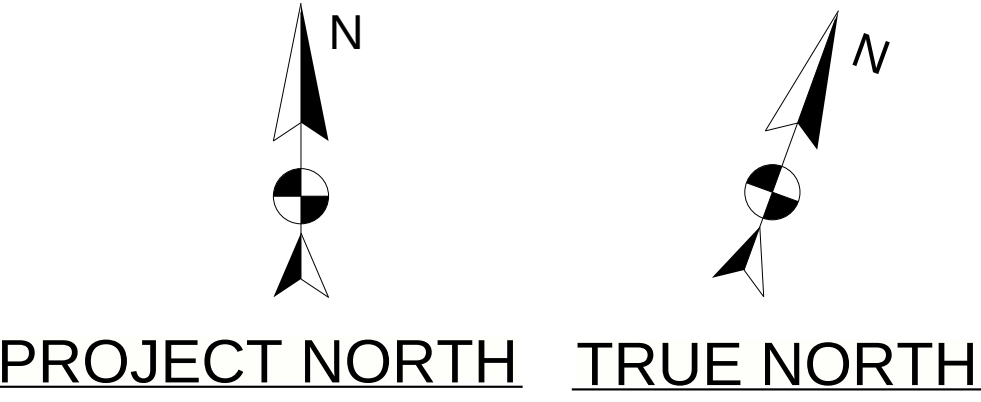


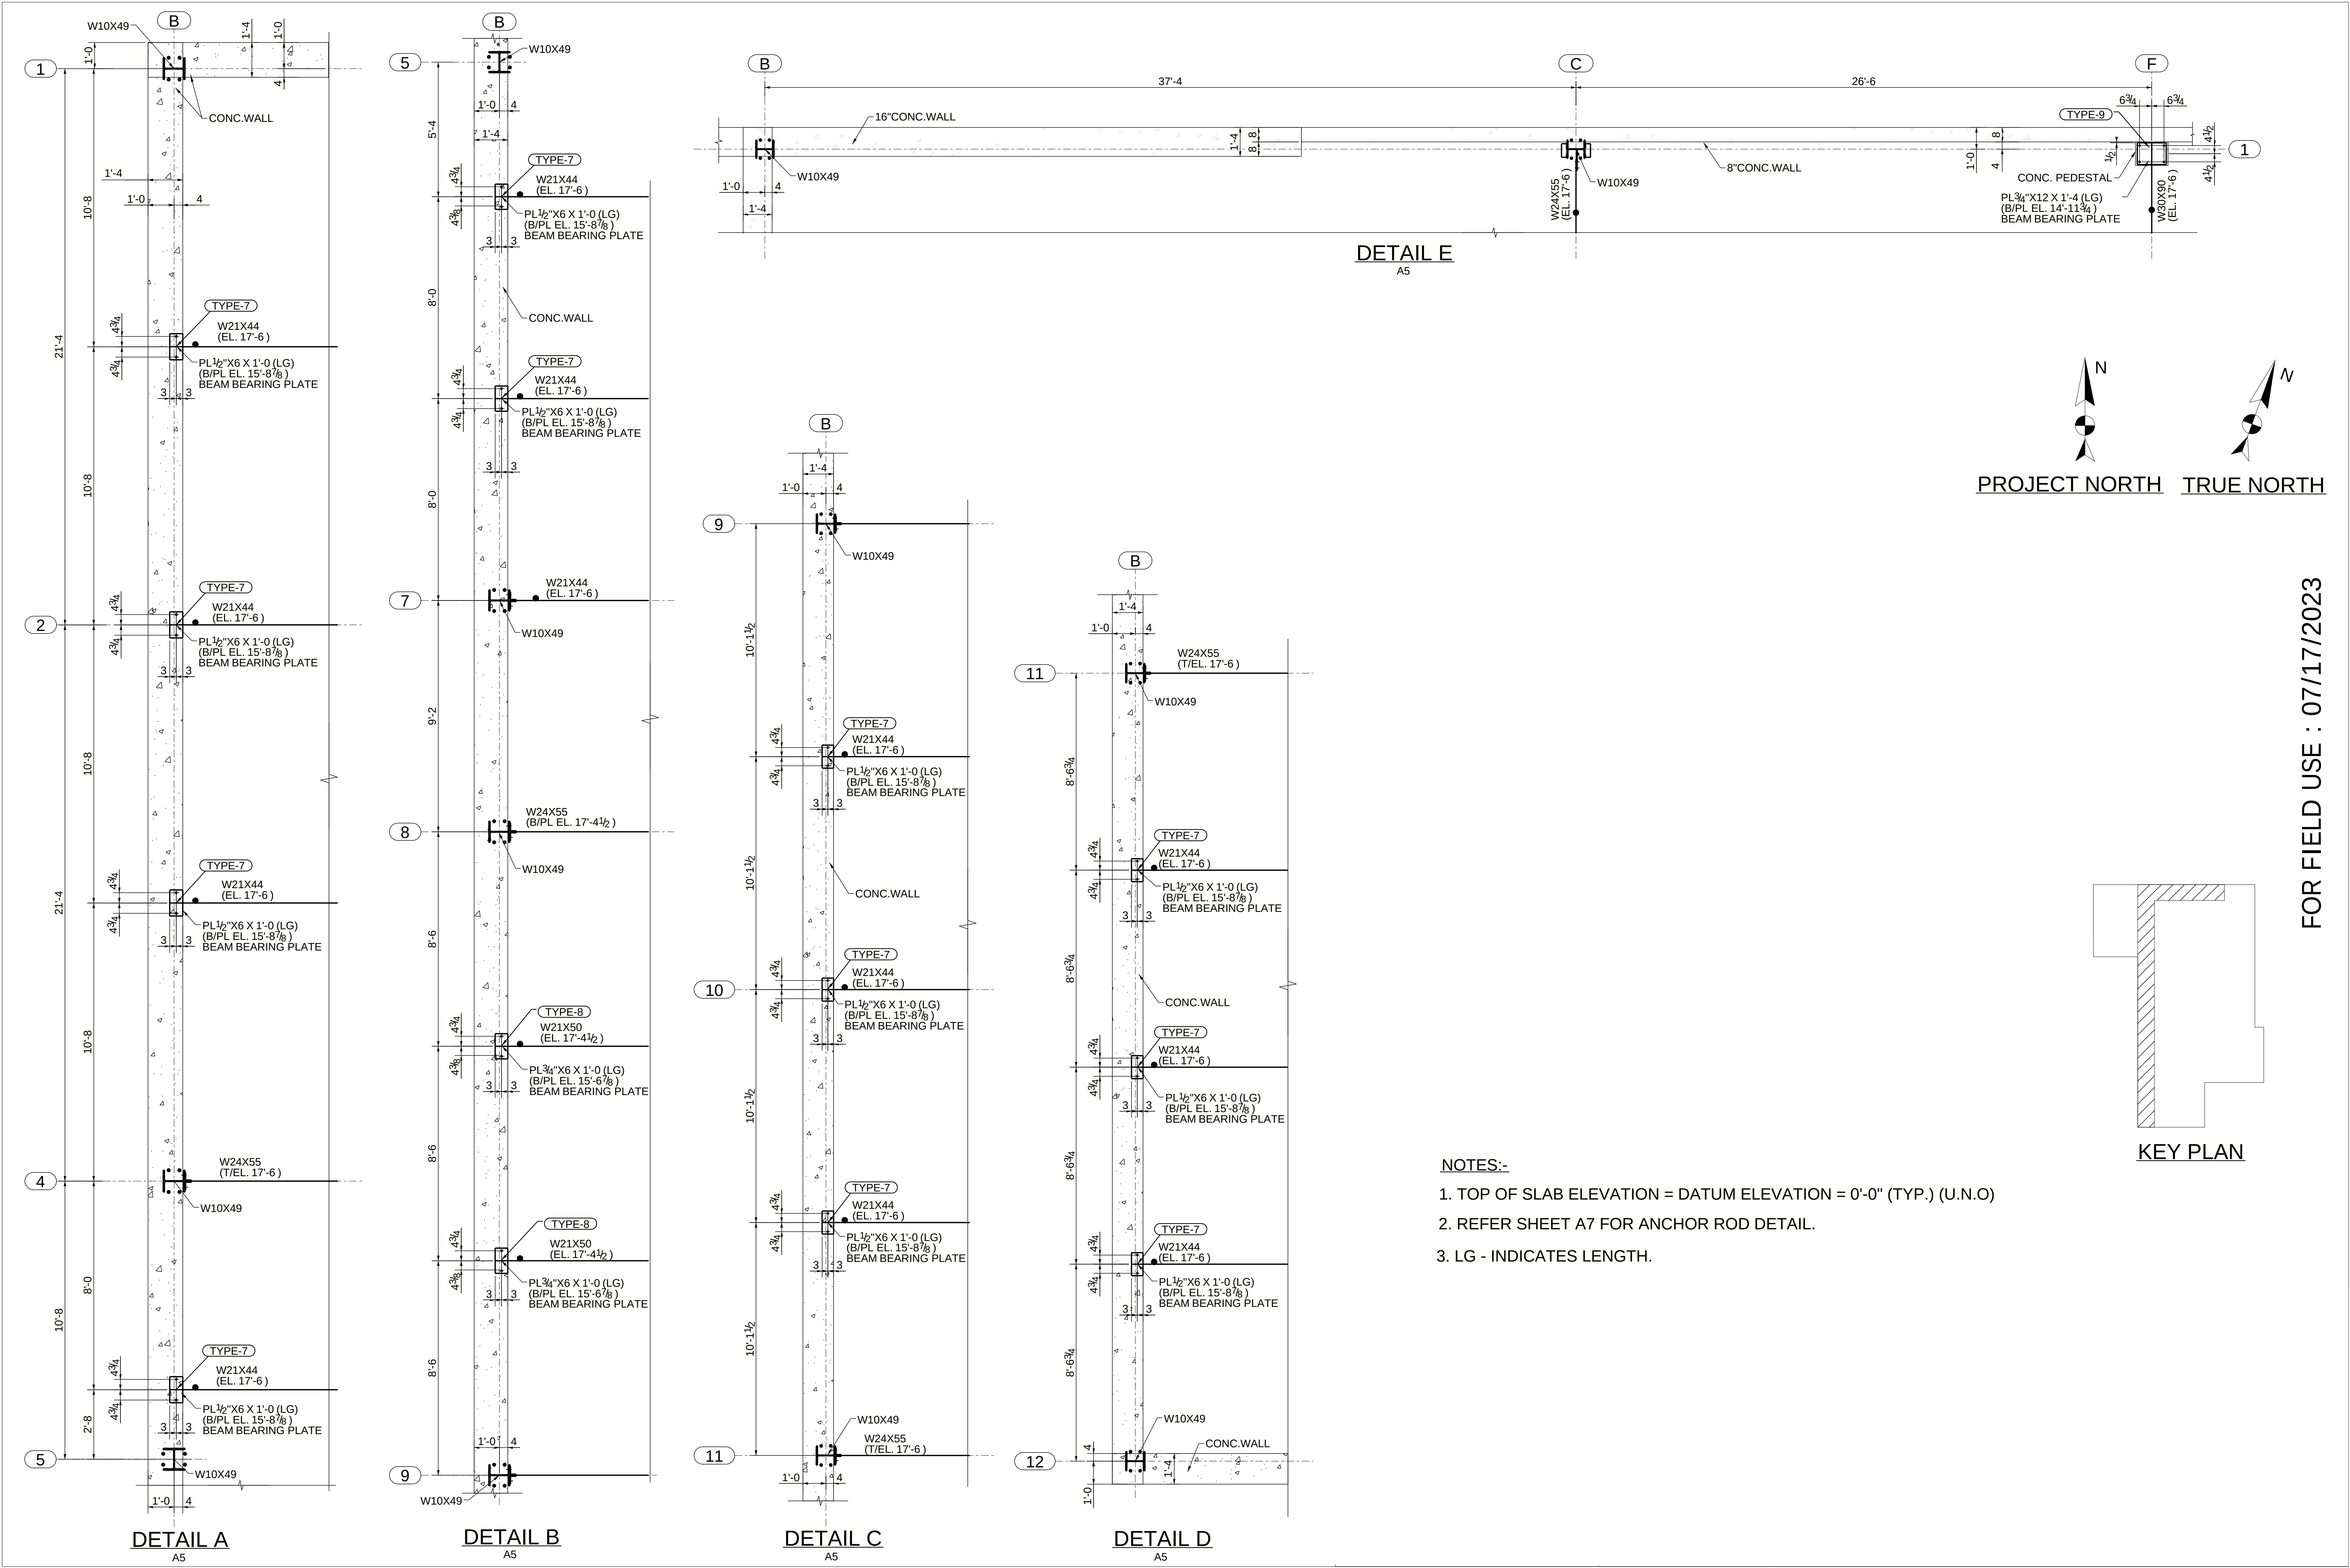


- NOTES:-
1. TOP OF SLAB ELEVATION = DATUM ELEVATION = 0'-0" (TYP.) (U.N.O)
 2. REFER SHEET A7 FOR ANCHOR ROD DETAIL.
 3. LG - INDICATES LENGTH.

FOR FIELD USE : 07/17/2023

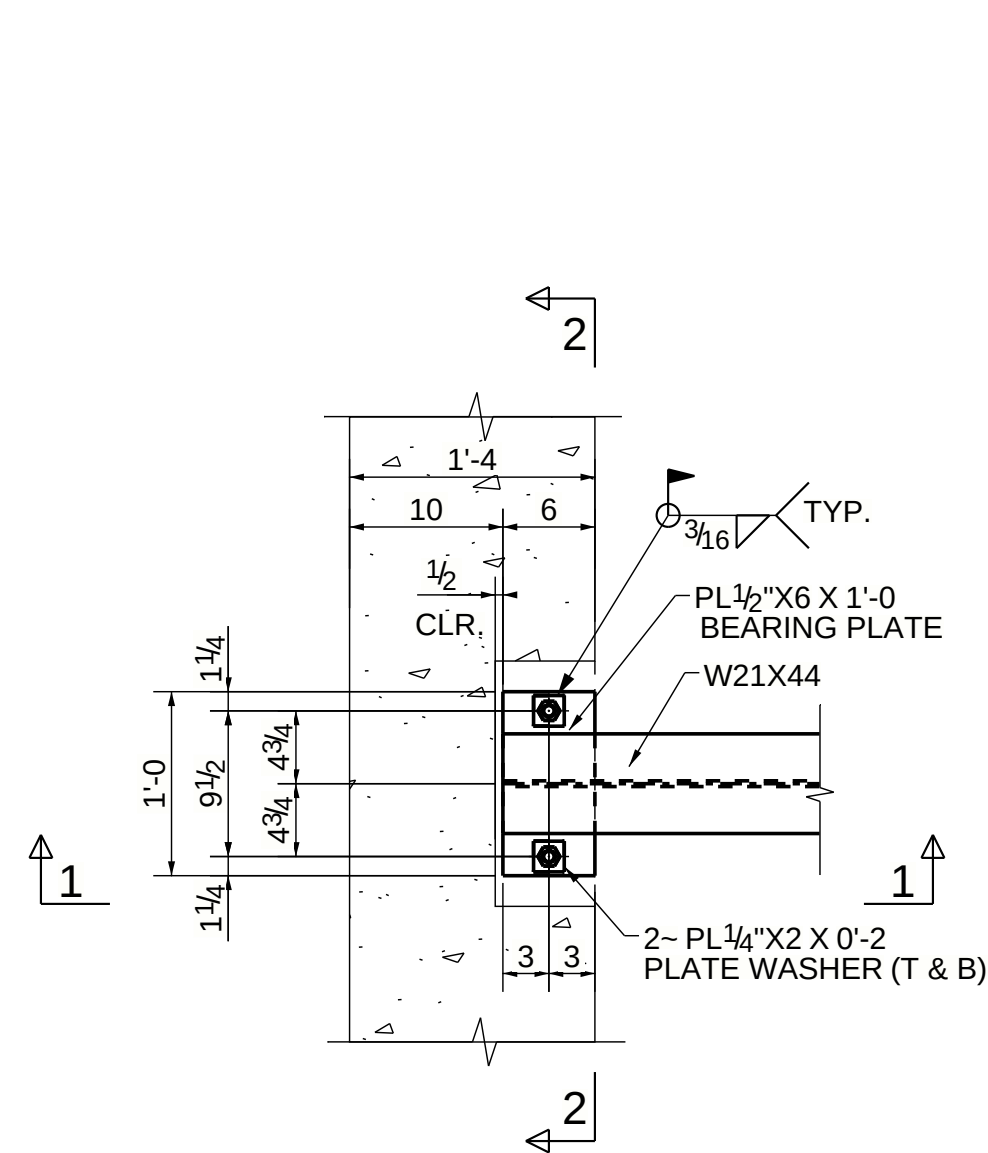


TYPE-7

(12- LOCATIONS)

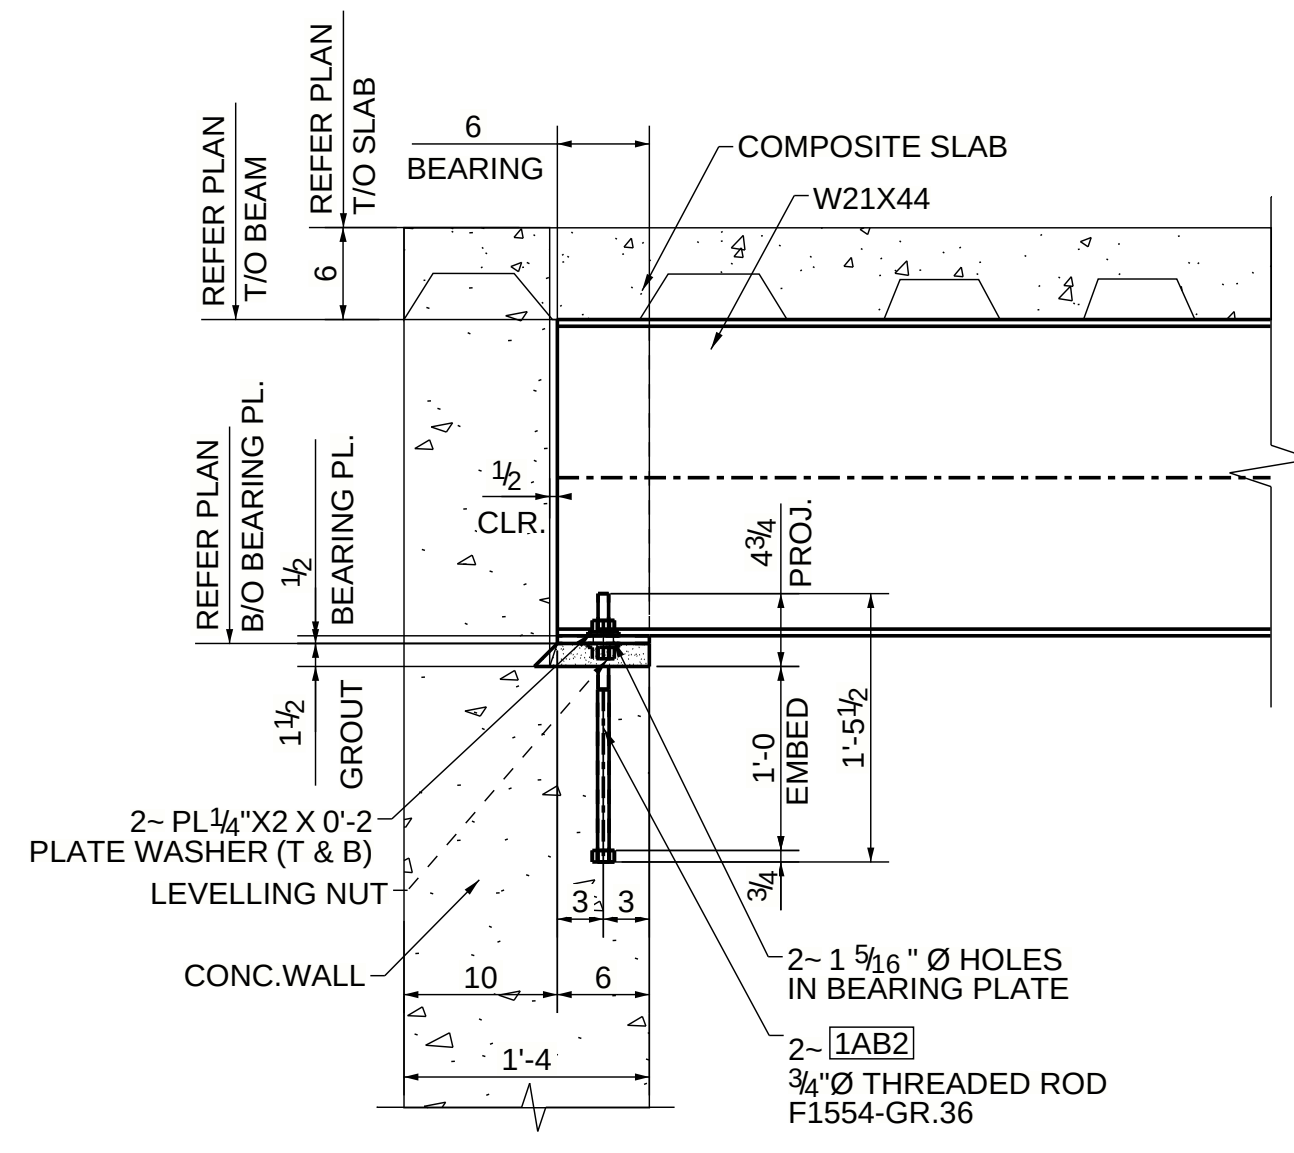


SECTION 1 - 1

(REFER:SECTION 2/S4.1)

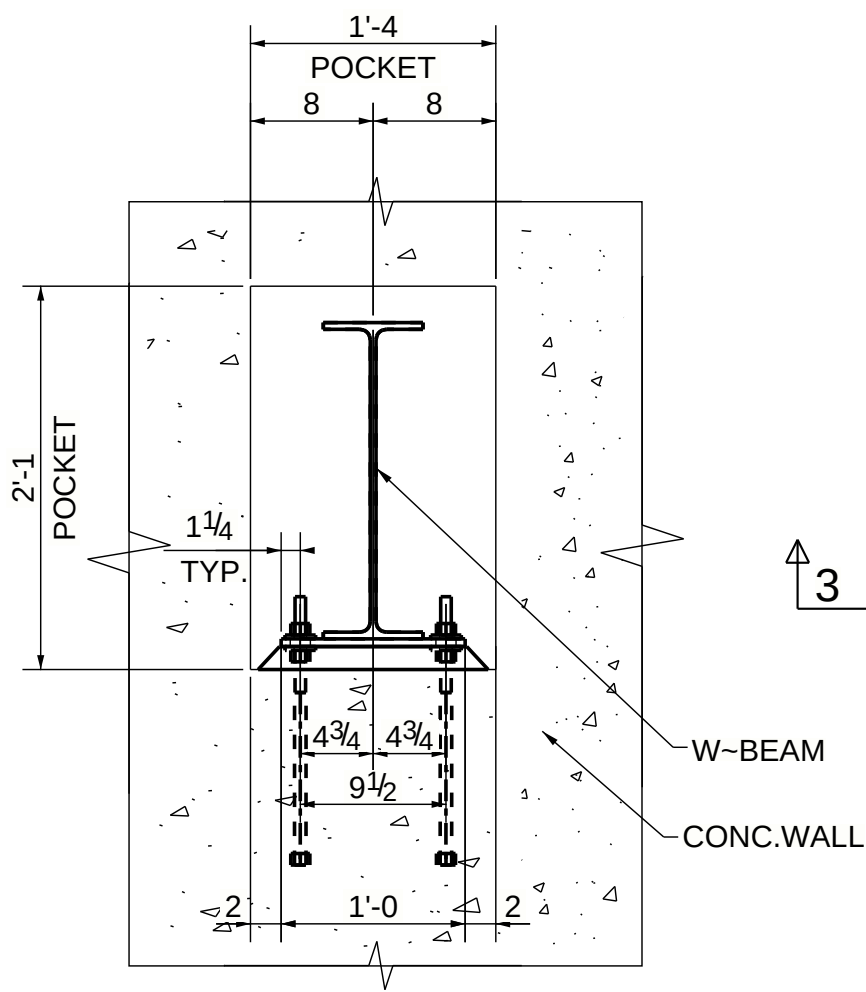


SECTION 2 - 2

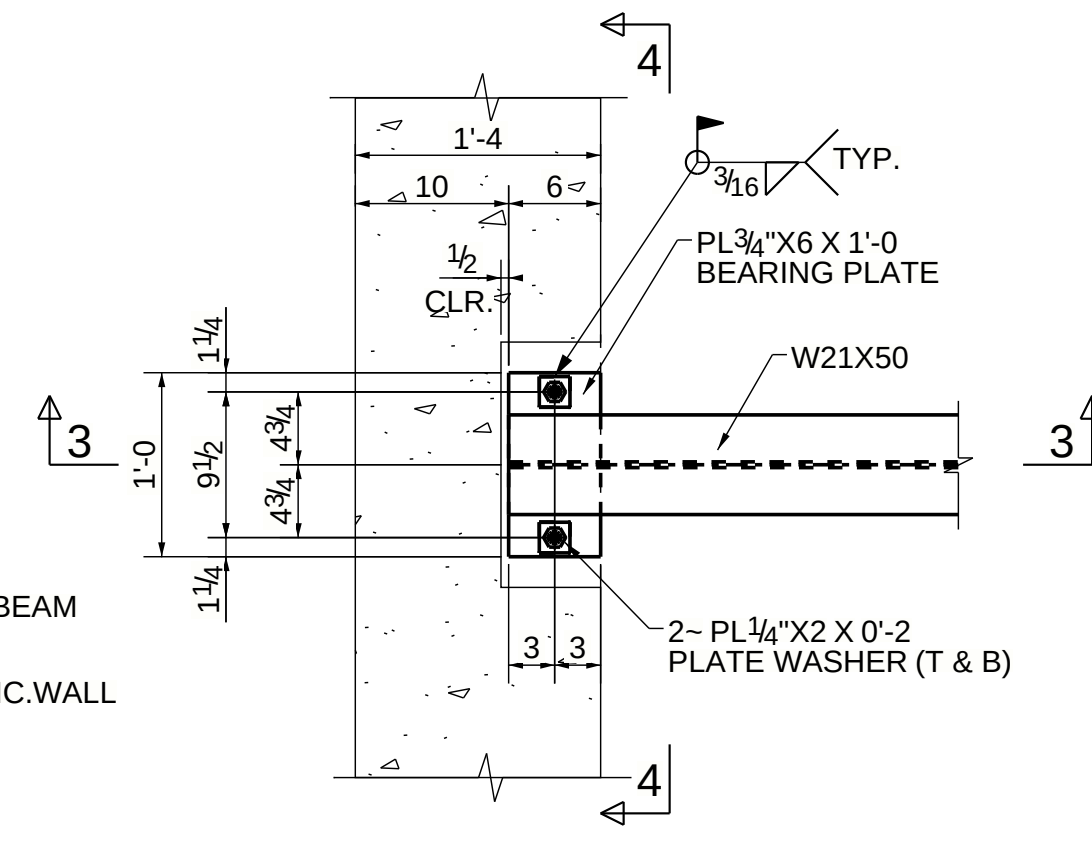


TYPE-8


(02- LOCATIONS)

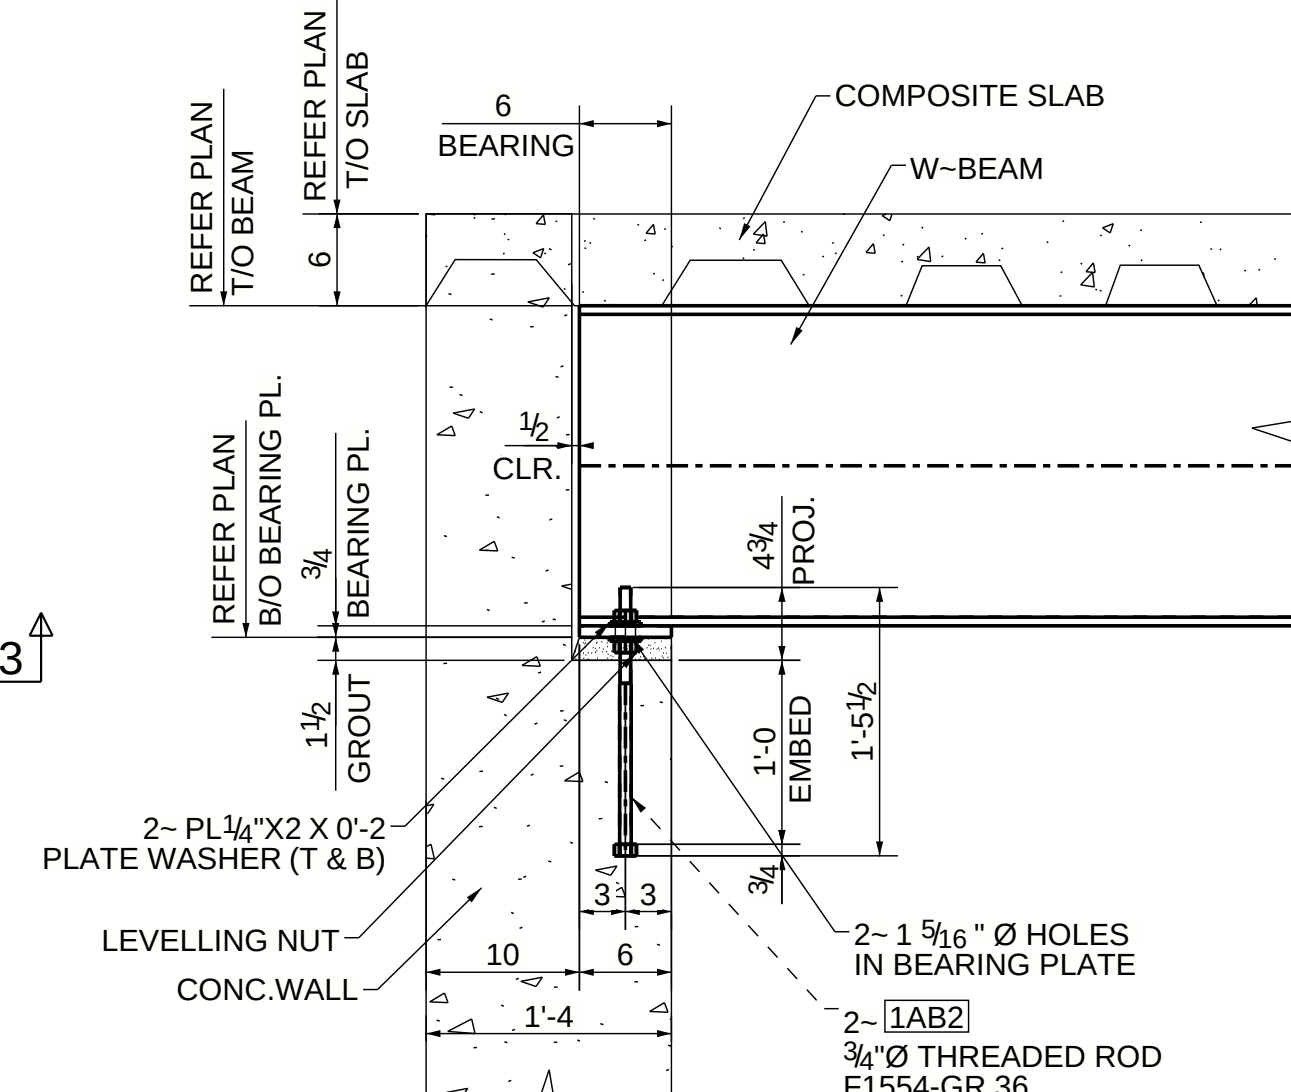

SECTION 3 - 3

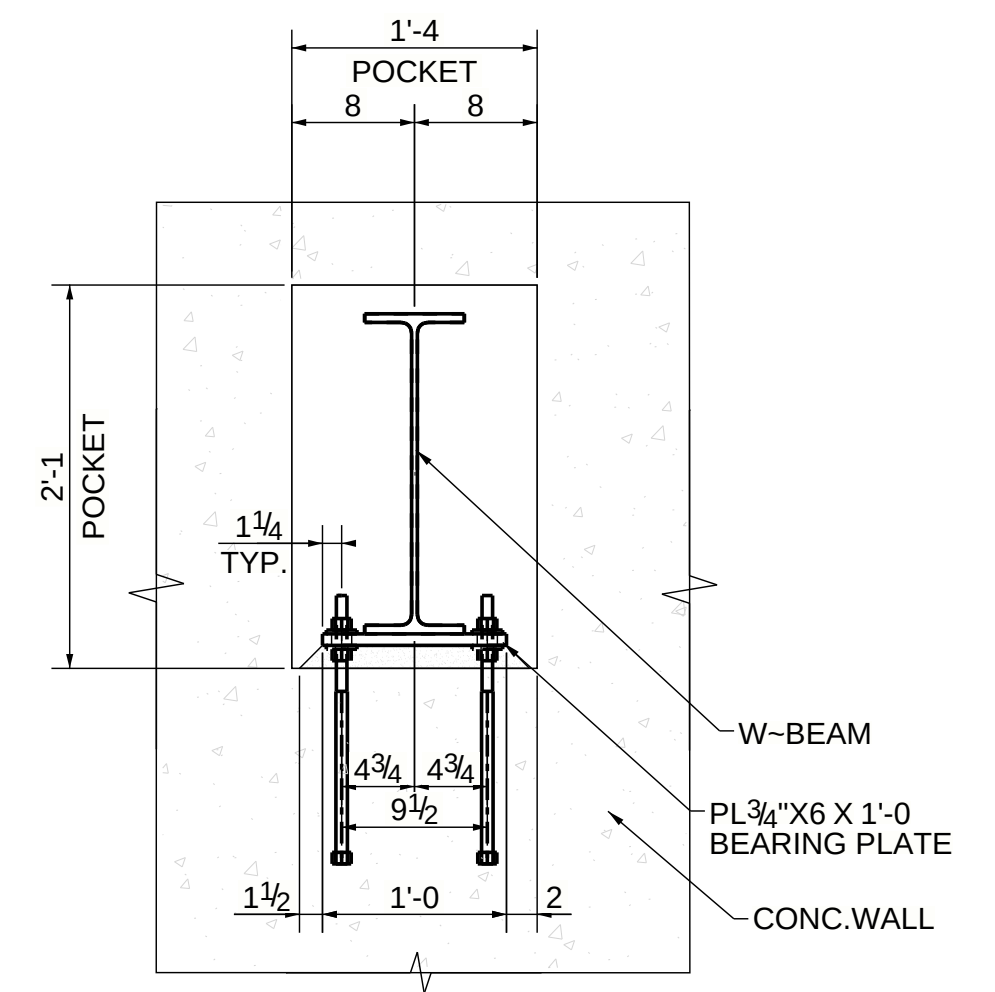


SECTION 4 - 4

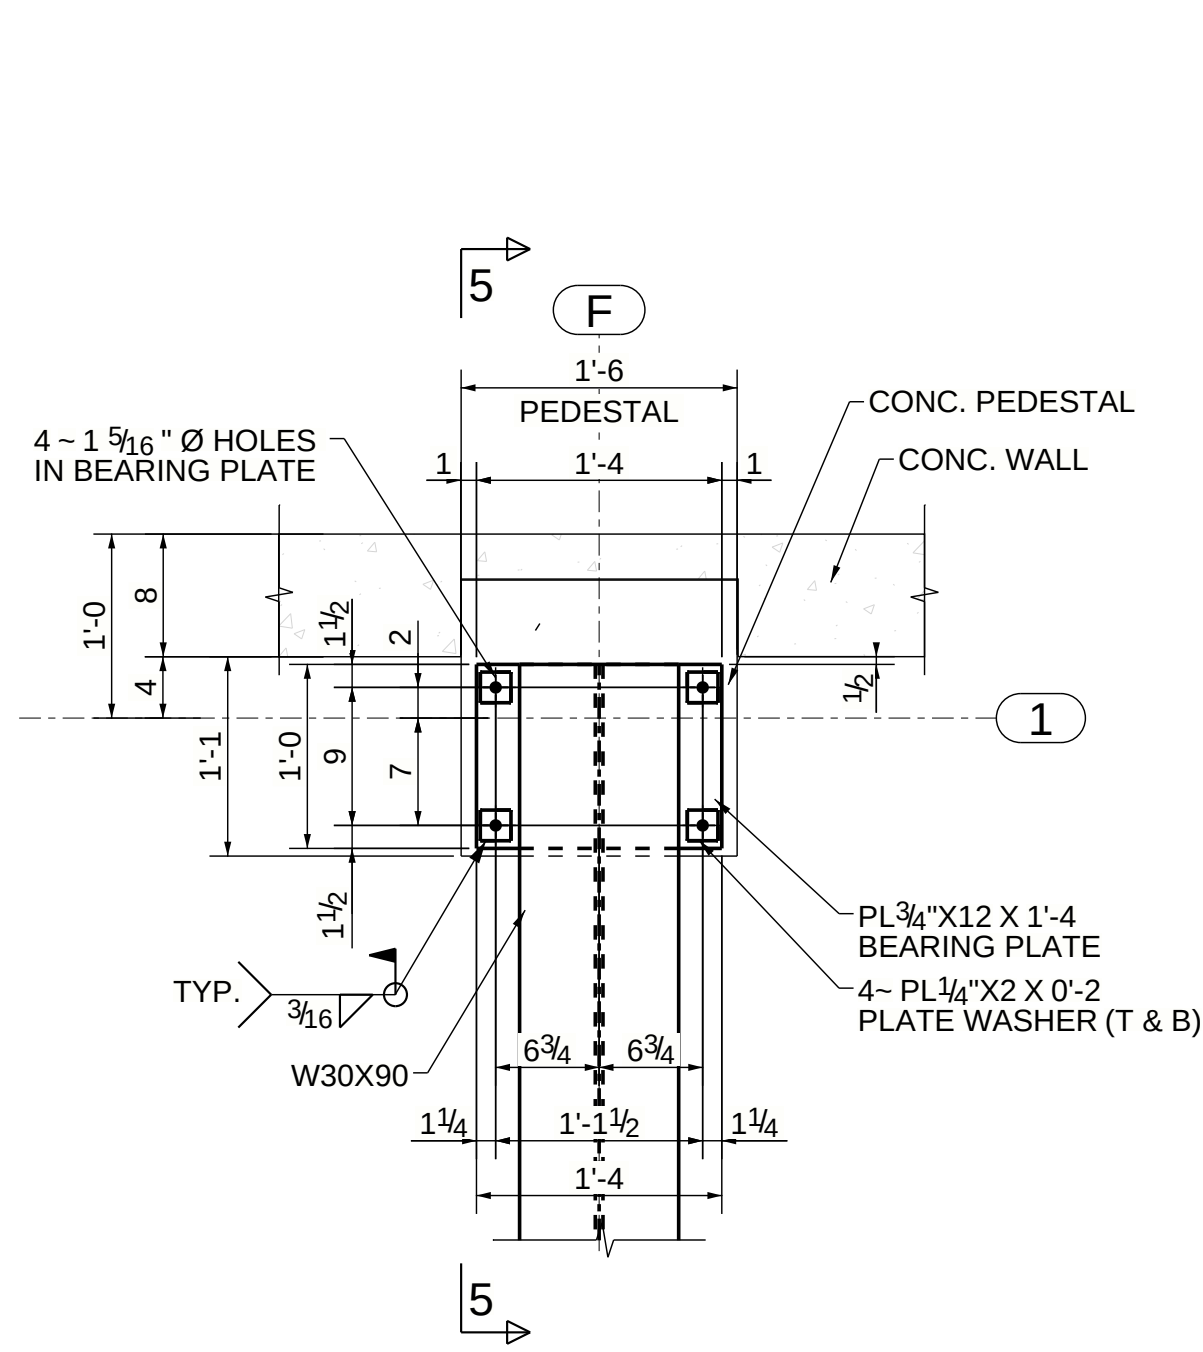


TYPE-9

(01- LOCATION)

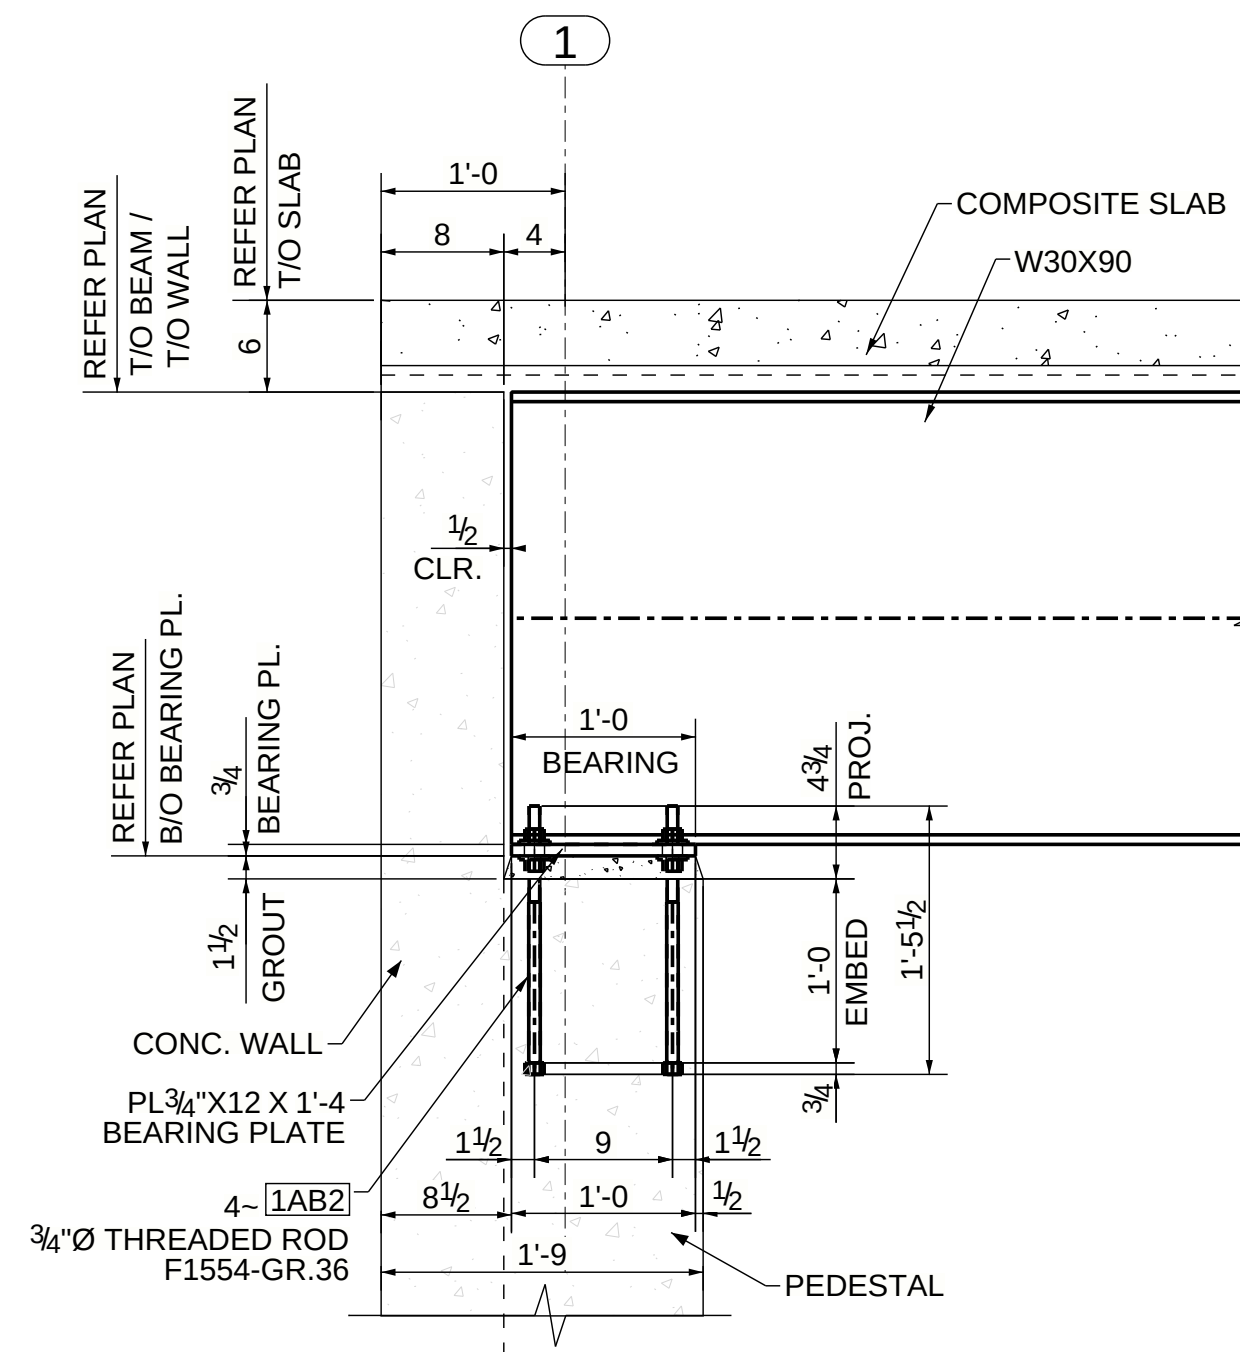


SECTION 5 - 5


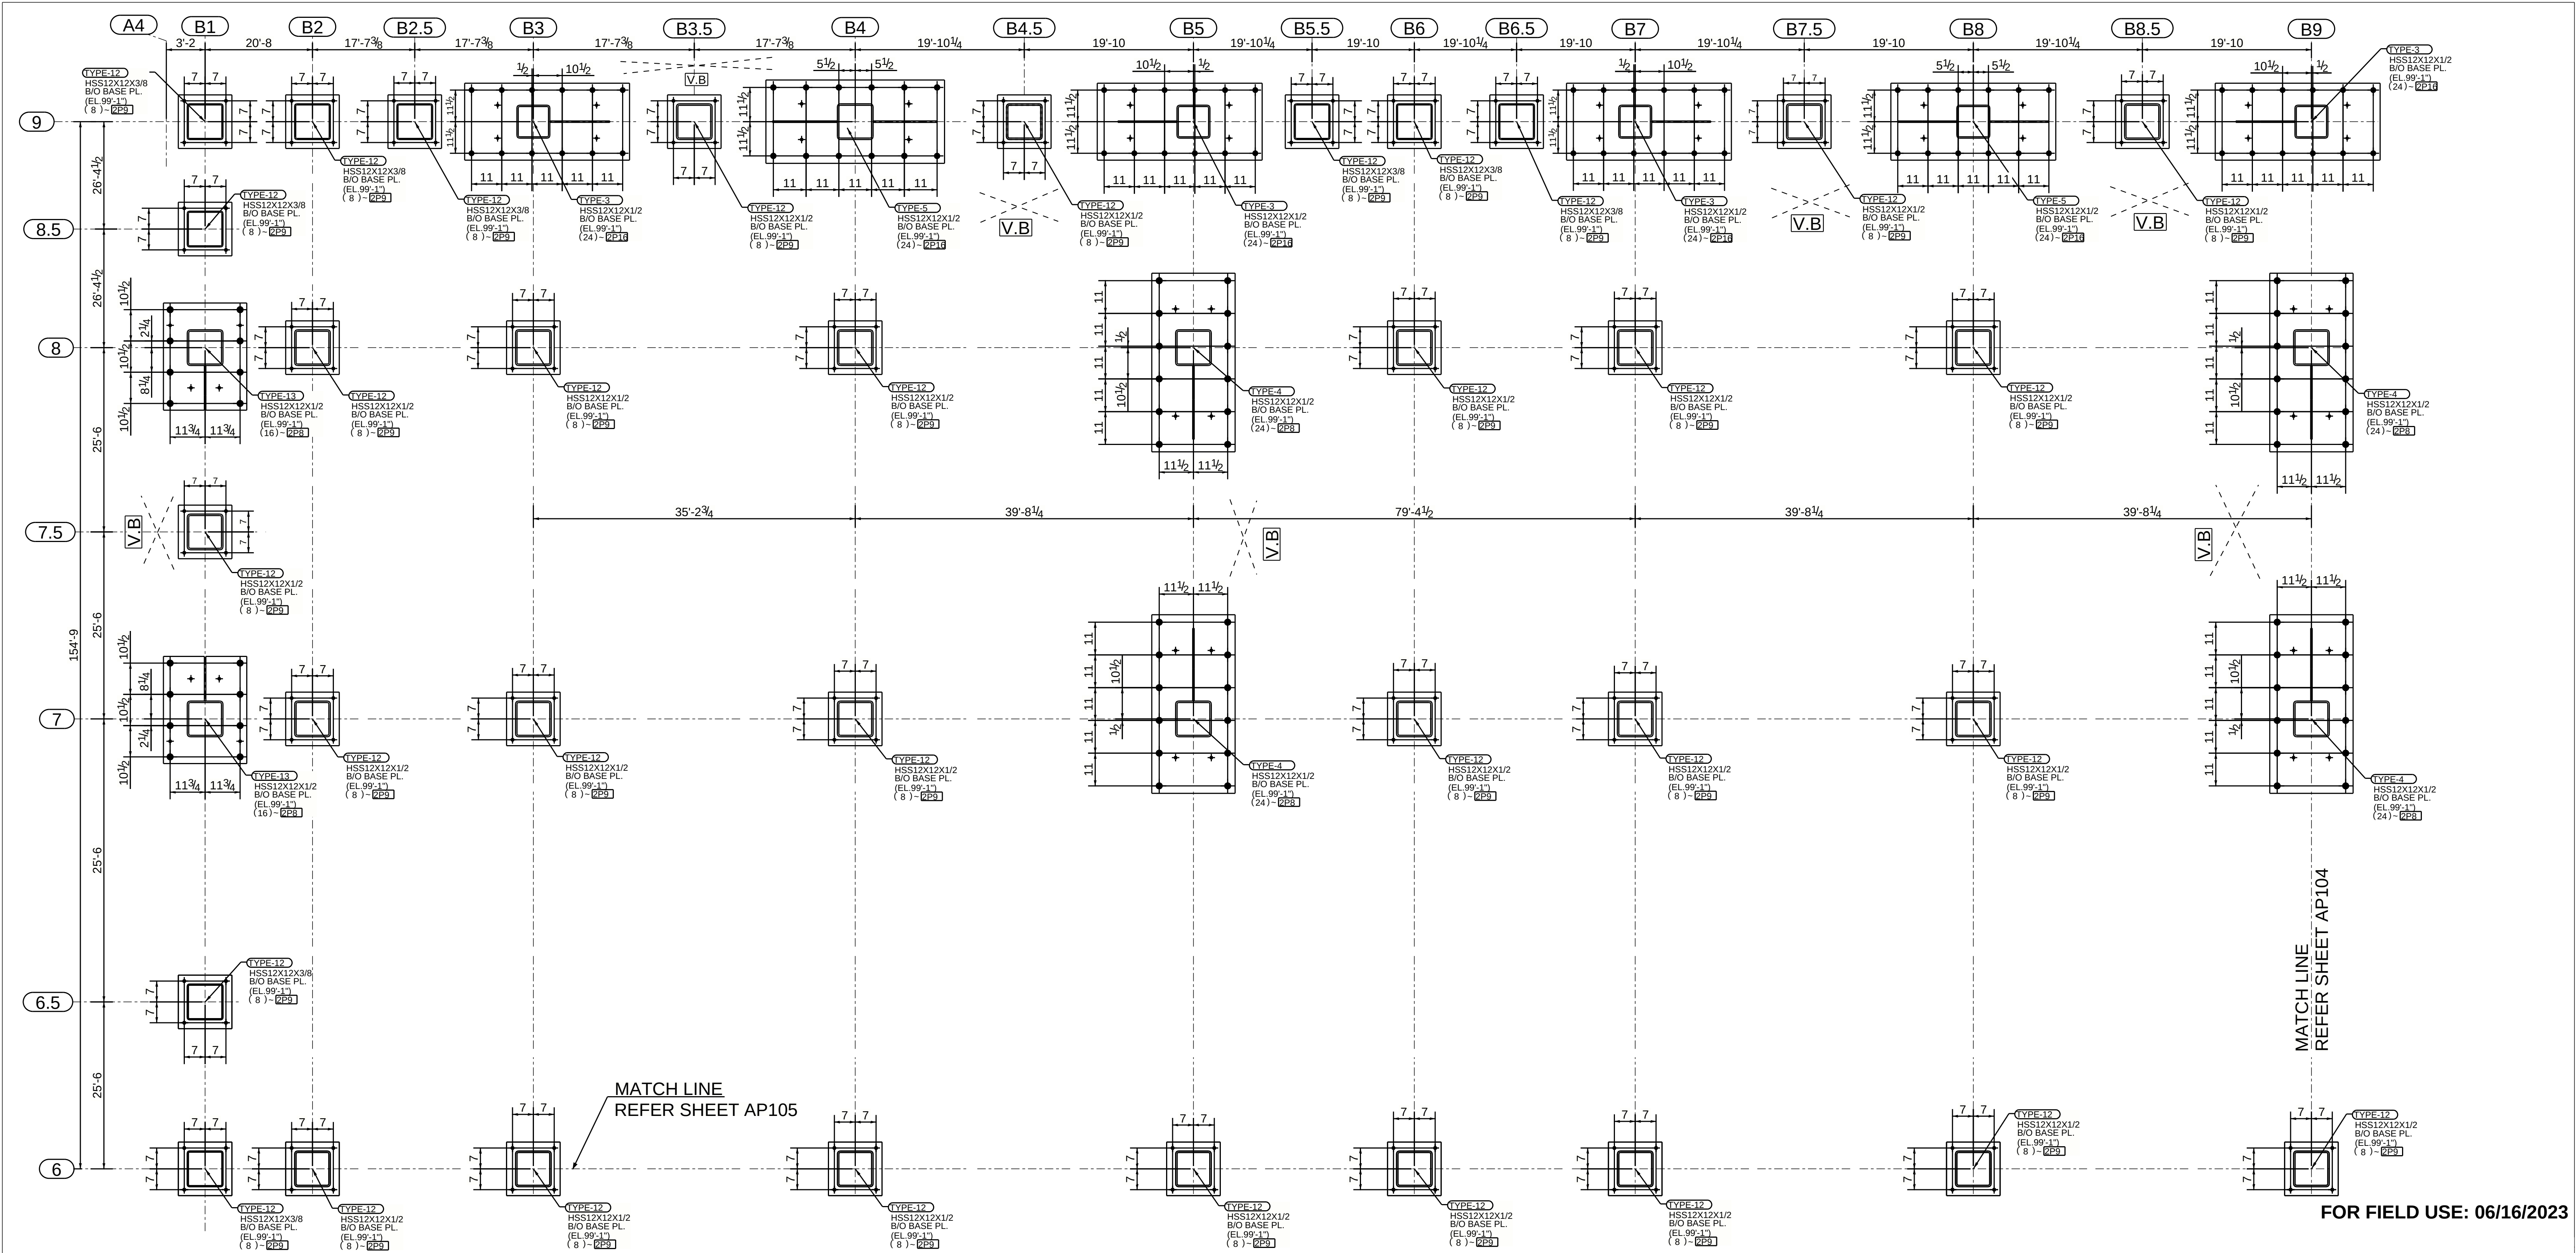


DETAIL B
AP101
PARTIAL ANCHOR BOLT SETTING PLAN
(REFER: FOUNDATION PLAN-(AREA 11-1) 11.S.01.01)

- NOTES:-
1. REFER AP100 SHEET FOR GENERAL NOTES.
 2. REFER AP111 & AP112 SHEET FOR ANCHOR BOLT DETAILS.
 3. - INDICATES VERTICAL BRACING.

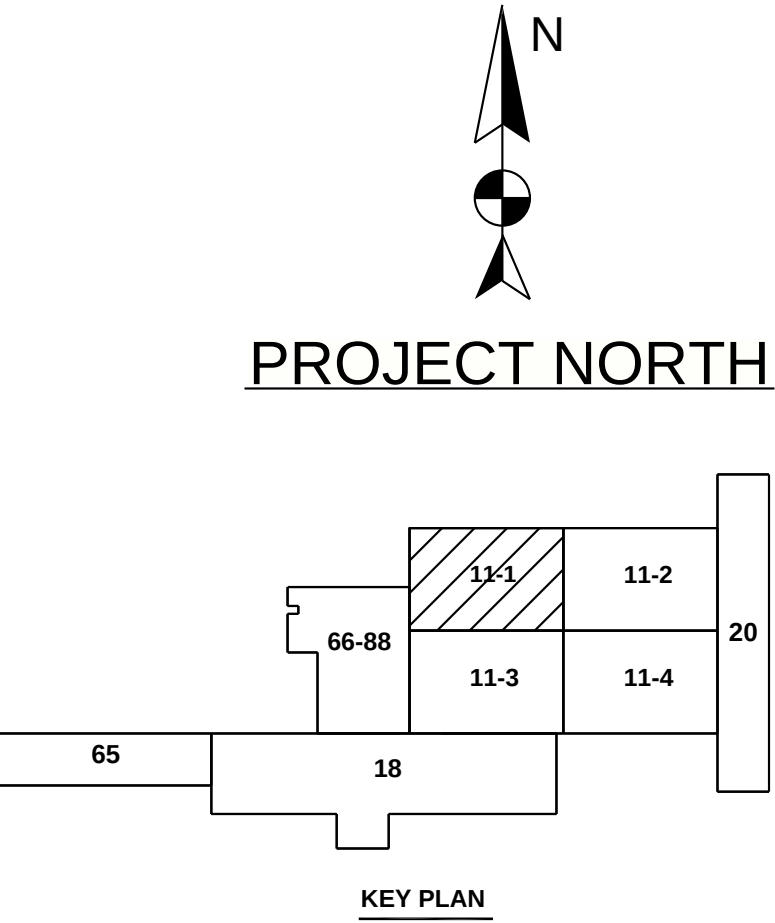

FOR FIELD USE: 06/16/2023

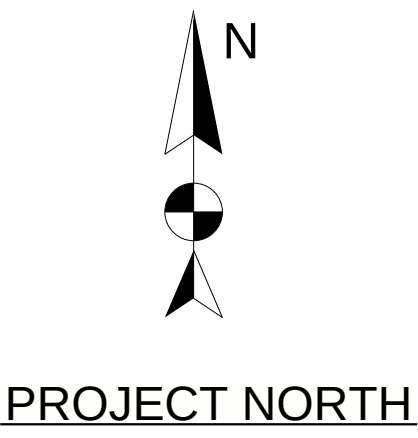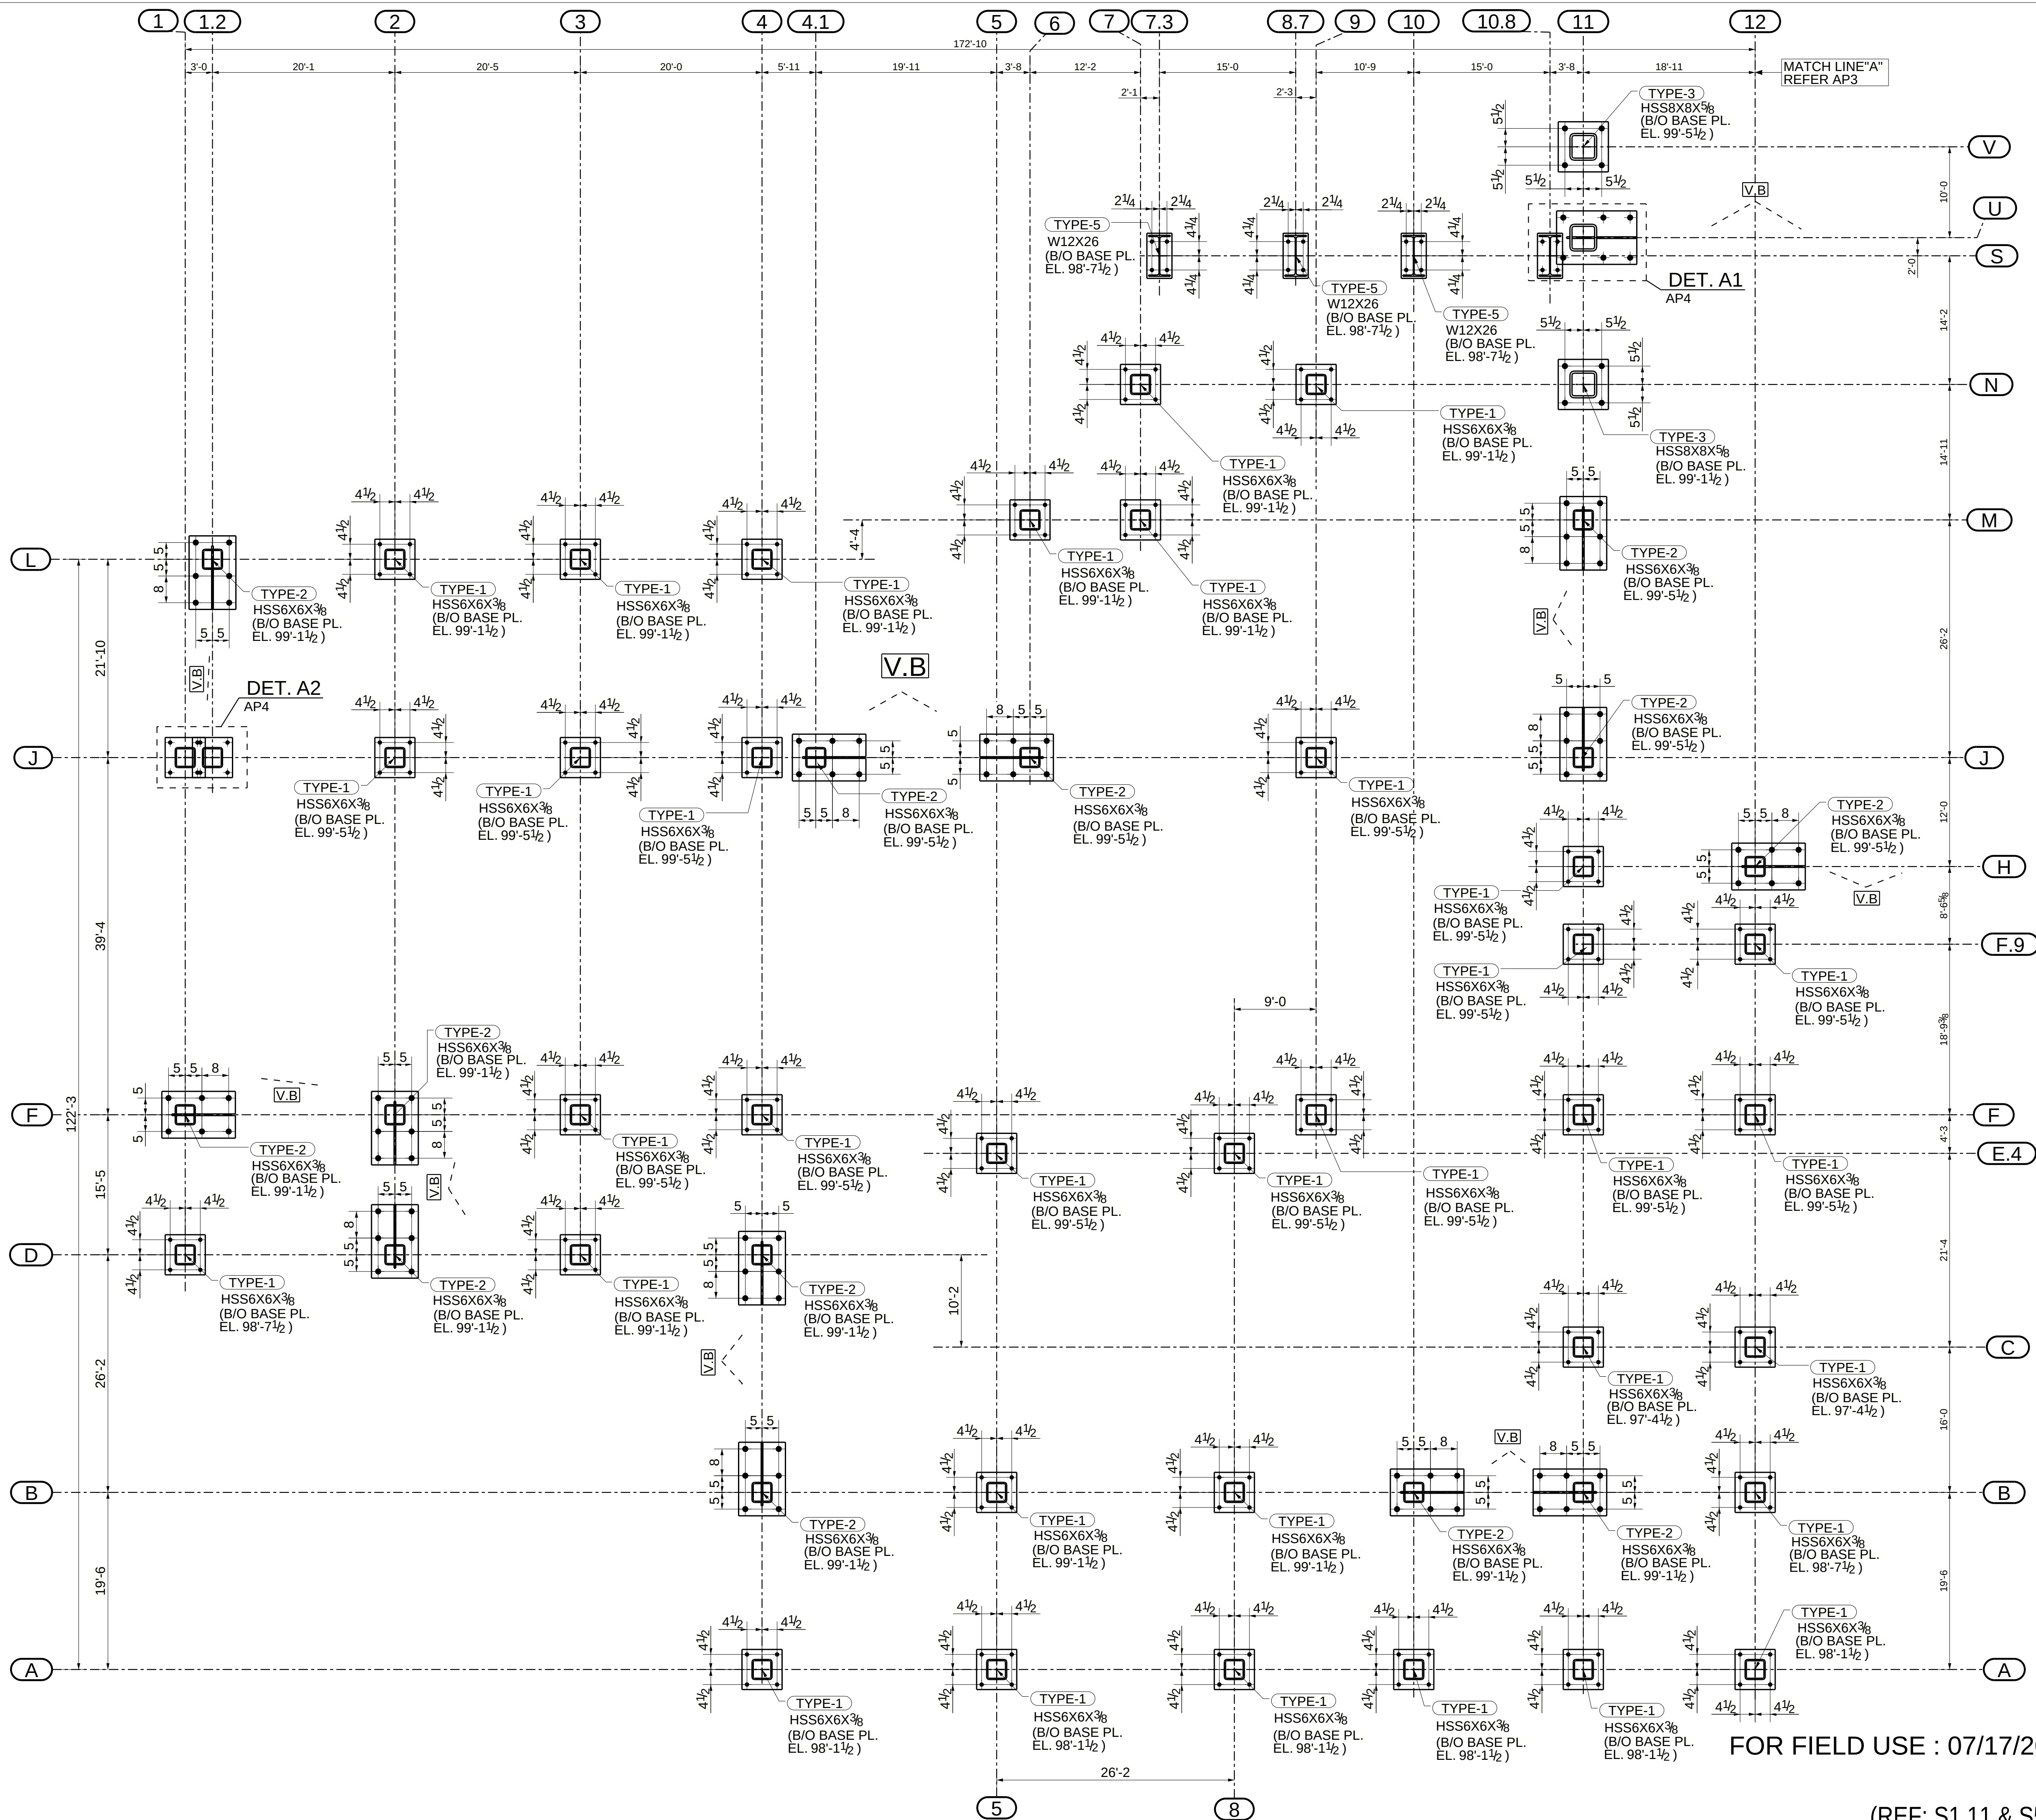




DETAIL-A
AP1
PARTIAL ANCHOR BOLT SETTING PLAN
(REFER : FOUNDATION PLAN 1-S1.11)

- NOTES:-
1. REFER AP1 SHEET FOR GENERAL NOTES.
 2. REFER AP4 SHEET FOR ANCHOR BOLT DETAILS.

FOR FIELD USE : 07/17/2023


(REF: S1.11 & S5.01)

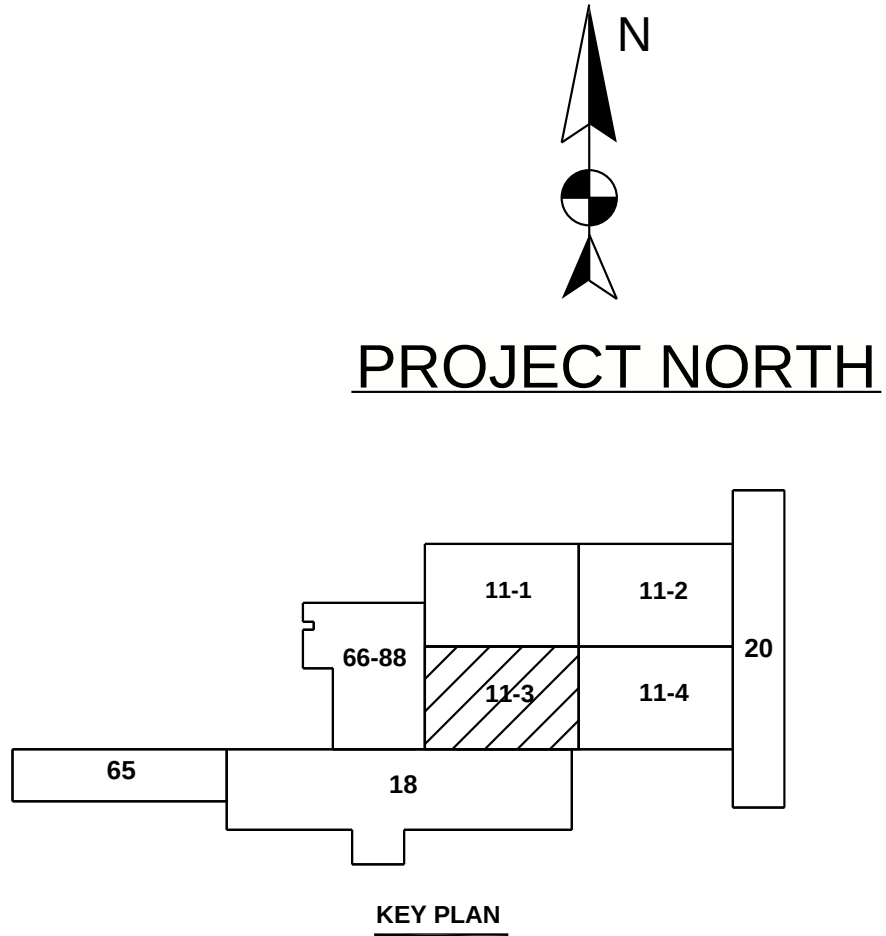

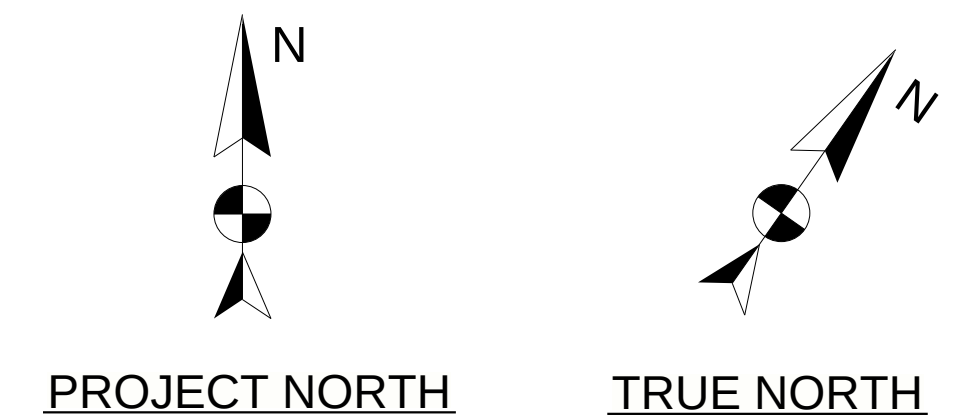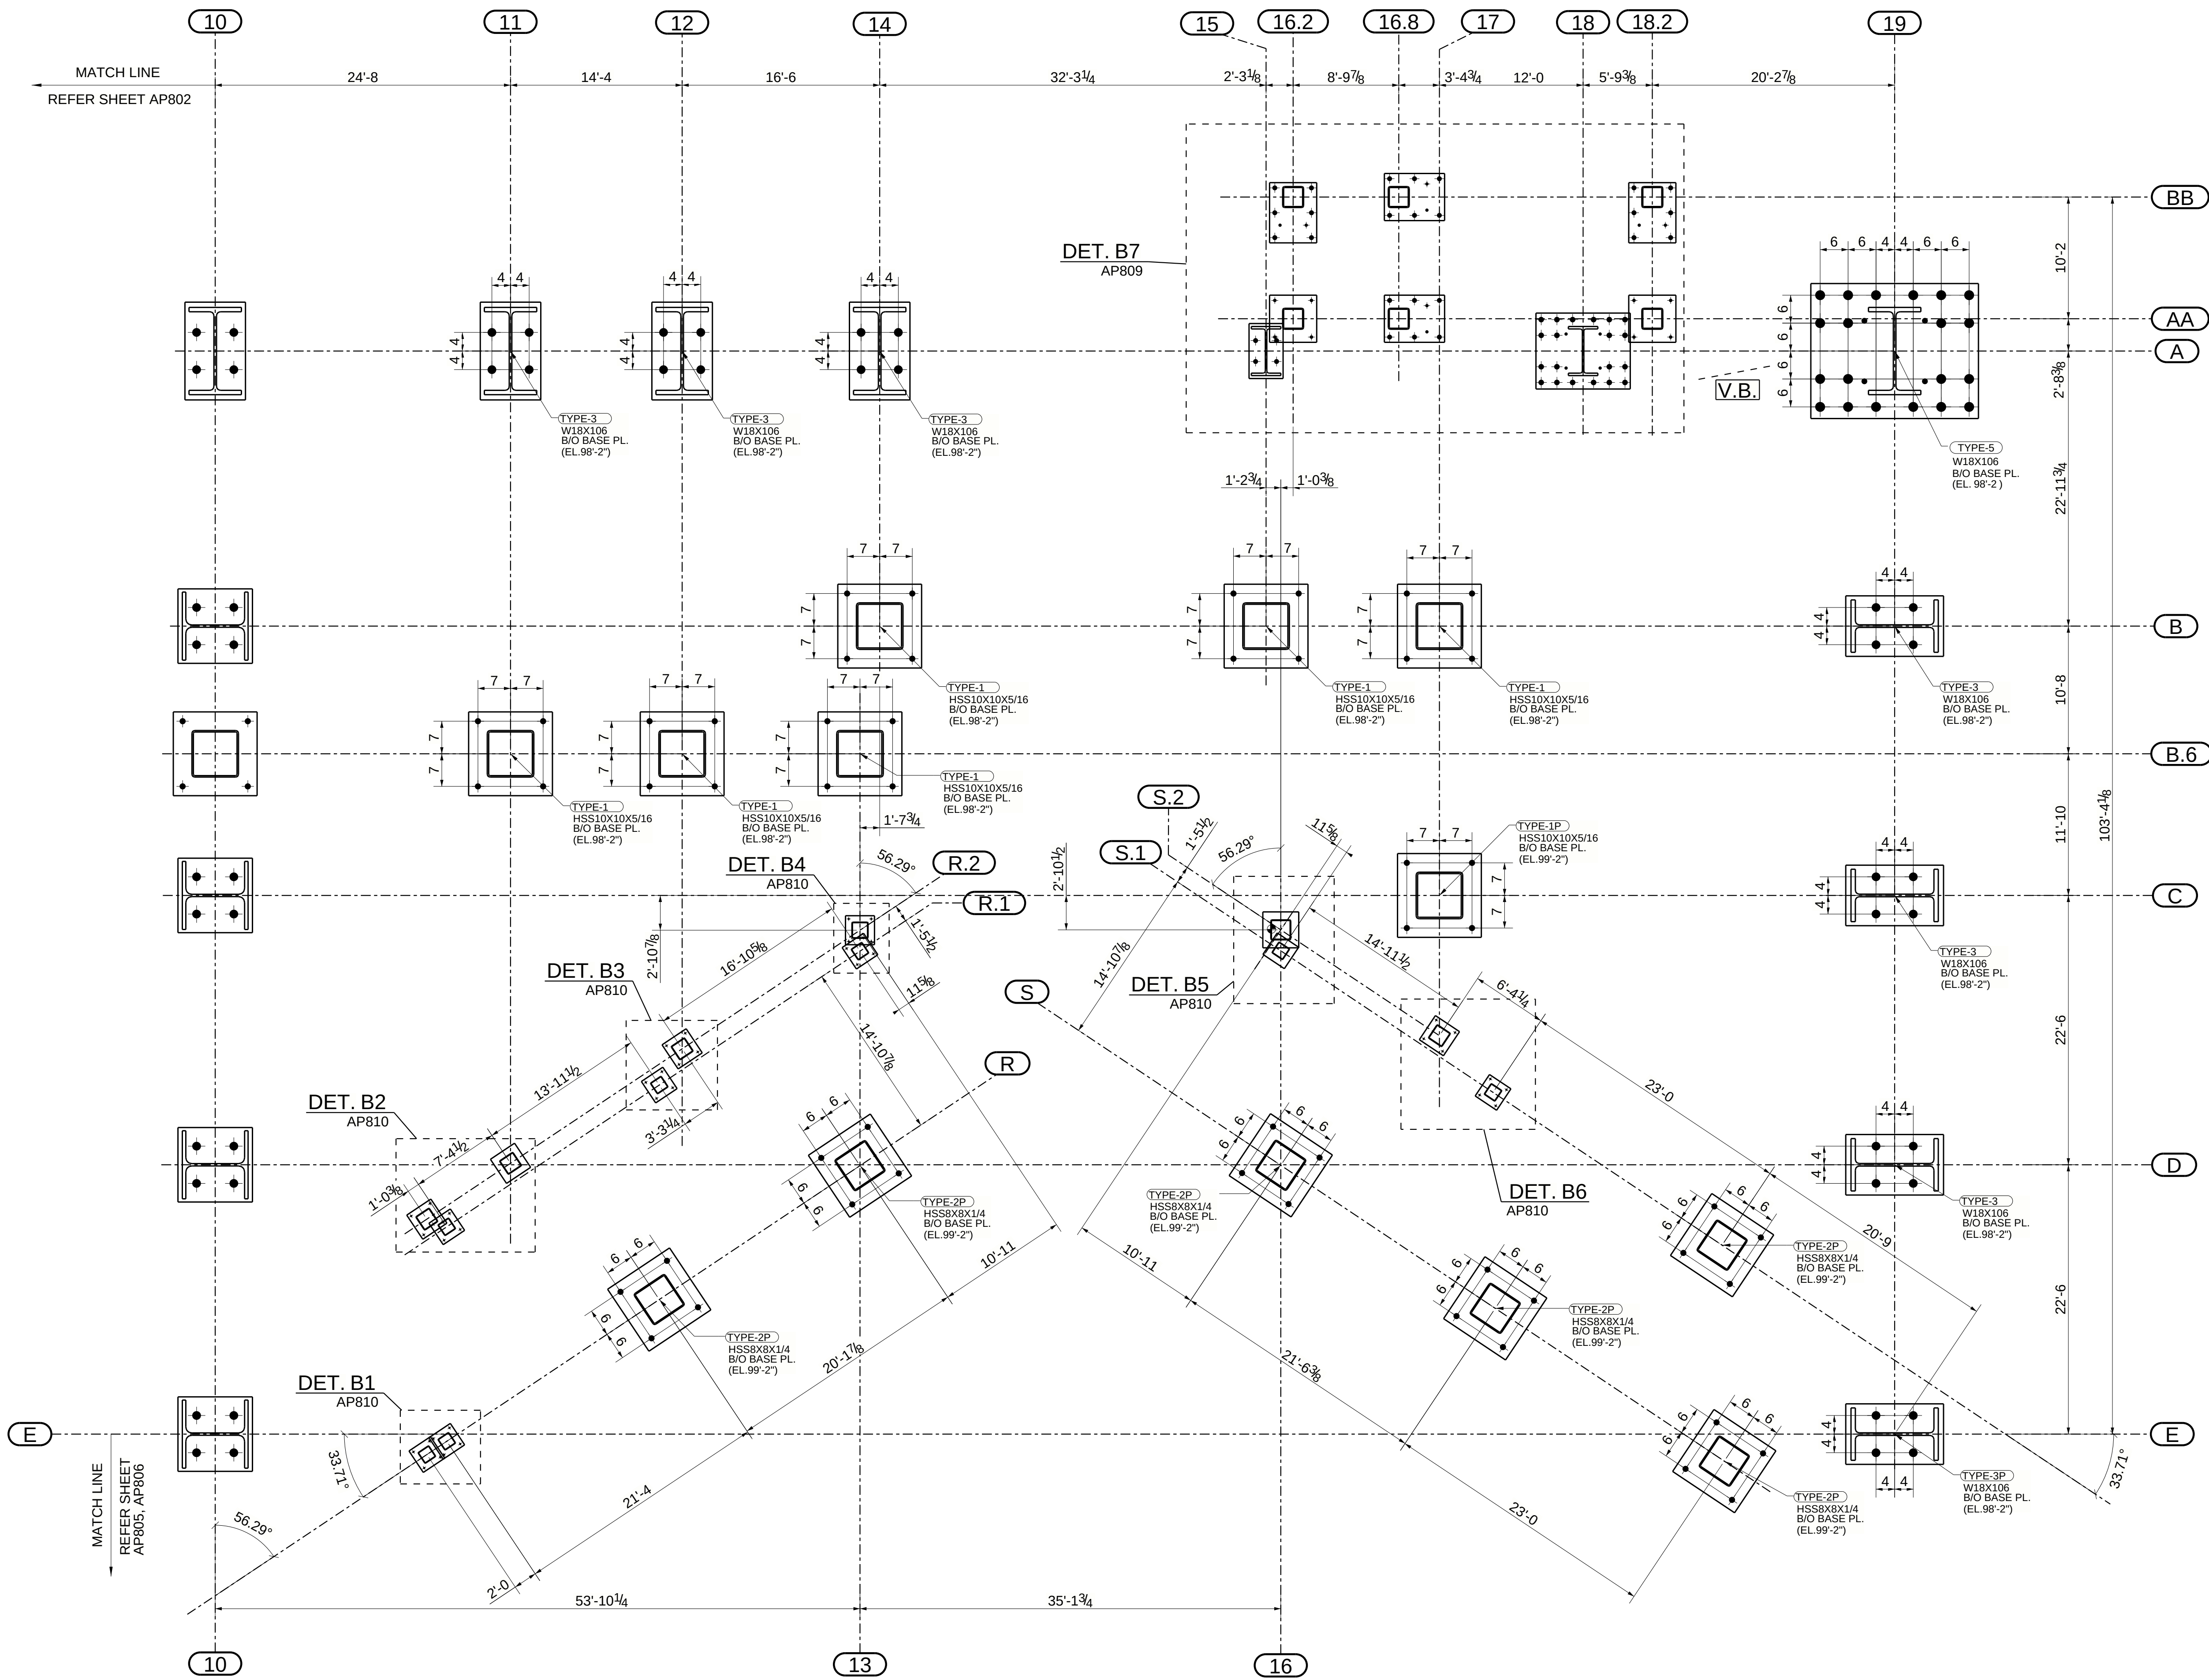


- NOTES:-
1. REFER AP801 SHEET FOR GENERAL NOTES.
 2. REFER AP811 & AP812 SHEETS FOR ANCHOR BOLT DETAILS.

DETAIL B
AP801
PARTIAL ANCHOR BOLT SETTING PLAN
(REFER : OVERALL FOUNDATION AND SLAB PLAN 1/S - 100 & & PARTIAL FOUNDATION AND SLAB PLAN 1/ S-101& S-102)

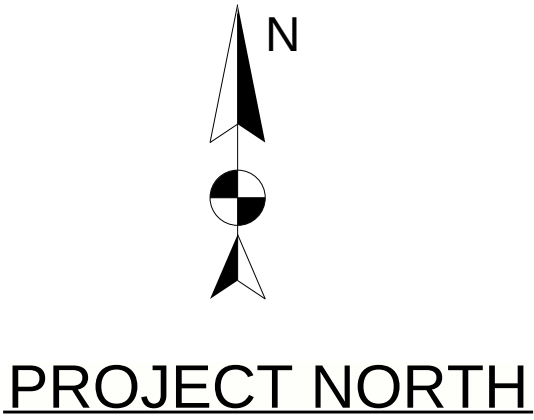


(REFER : FOUNDATION PLAN 1/ S-201)



1. REFER A101 SHEET FOR GENERAL NOTES.
2. REFER A104 & A105 SHEET FOR ANCHOR BOLT AND BASE PLATE DETAILS.


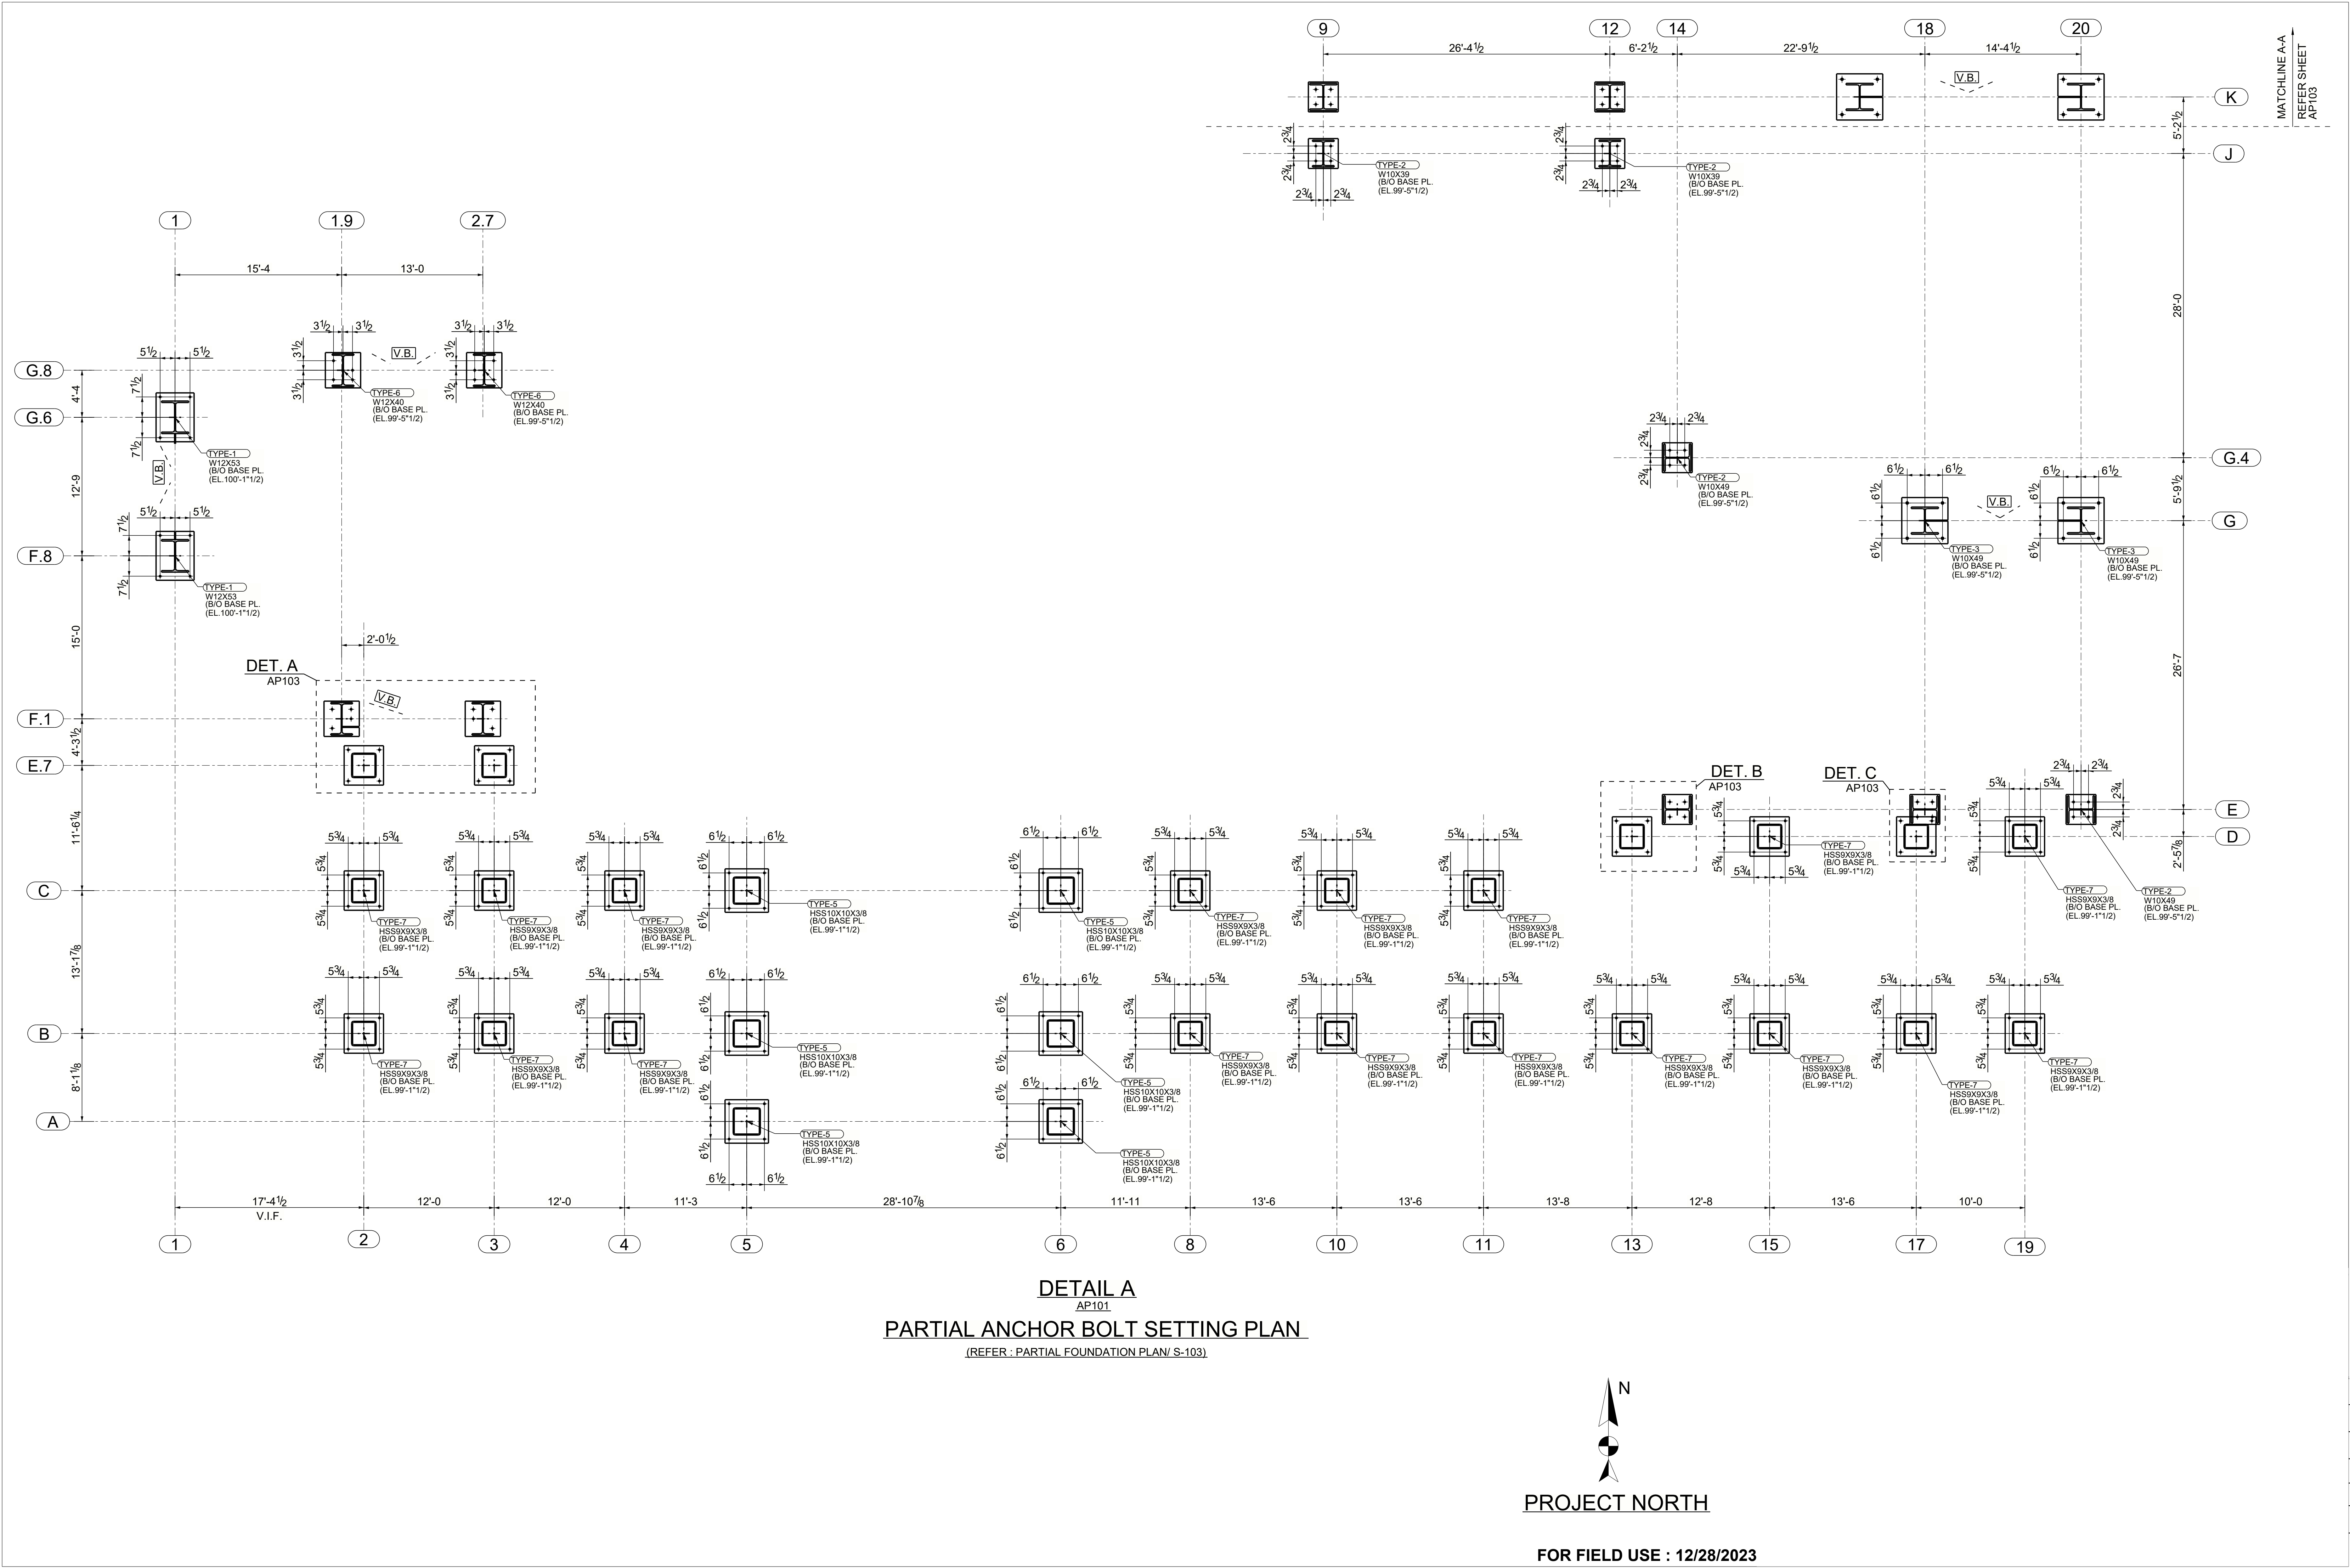


DETAIL A
AP101
PARTIAL ANCHOR BOLT SETTING PLAN
(REFER : PARTIAL FOUNDATION PLAN/ S-103)

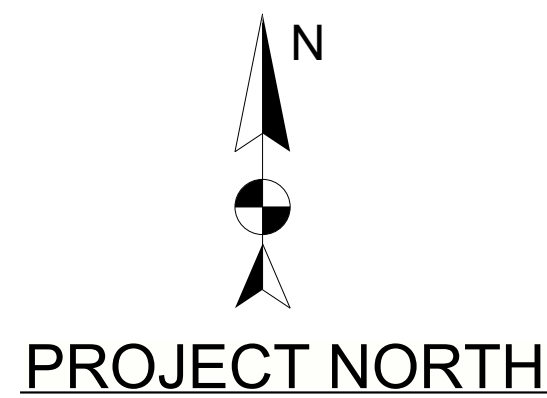



FOR FIELD USE : 12/28/2023

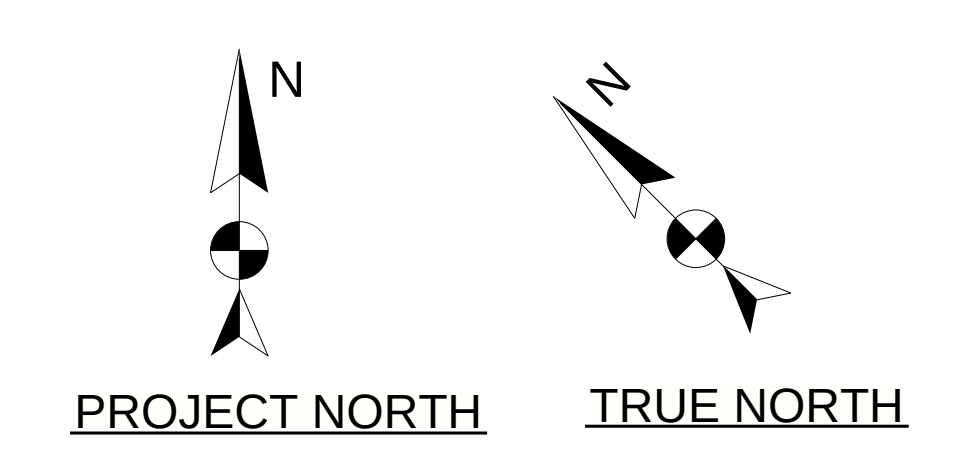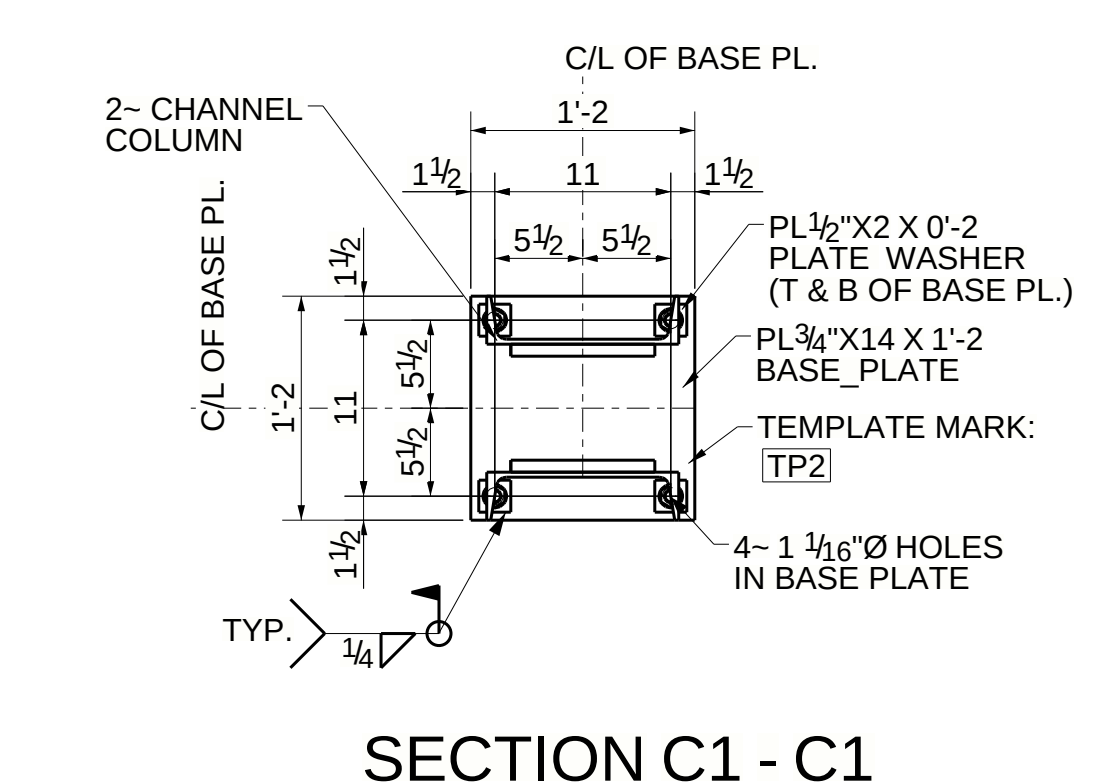

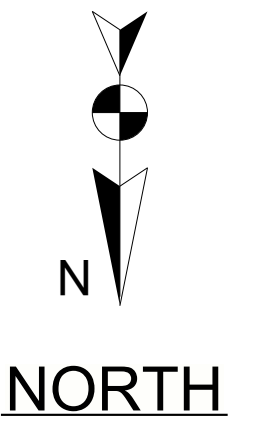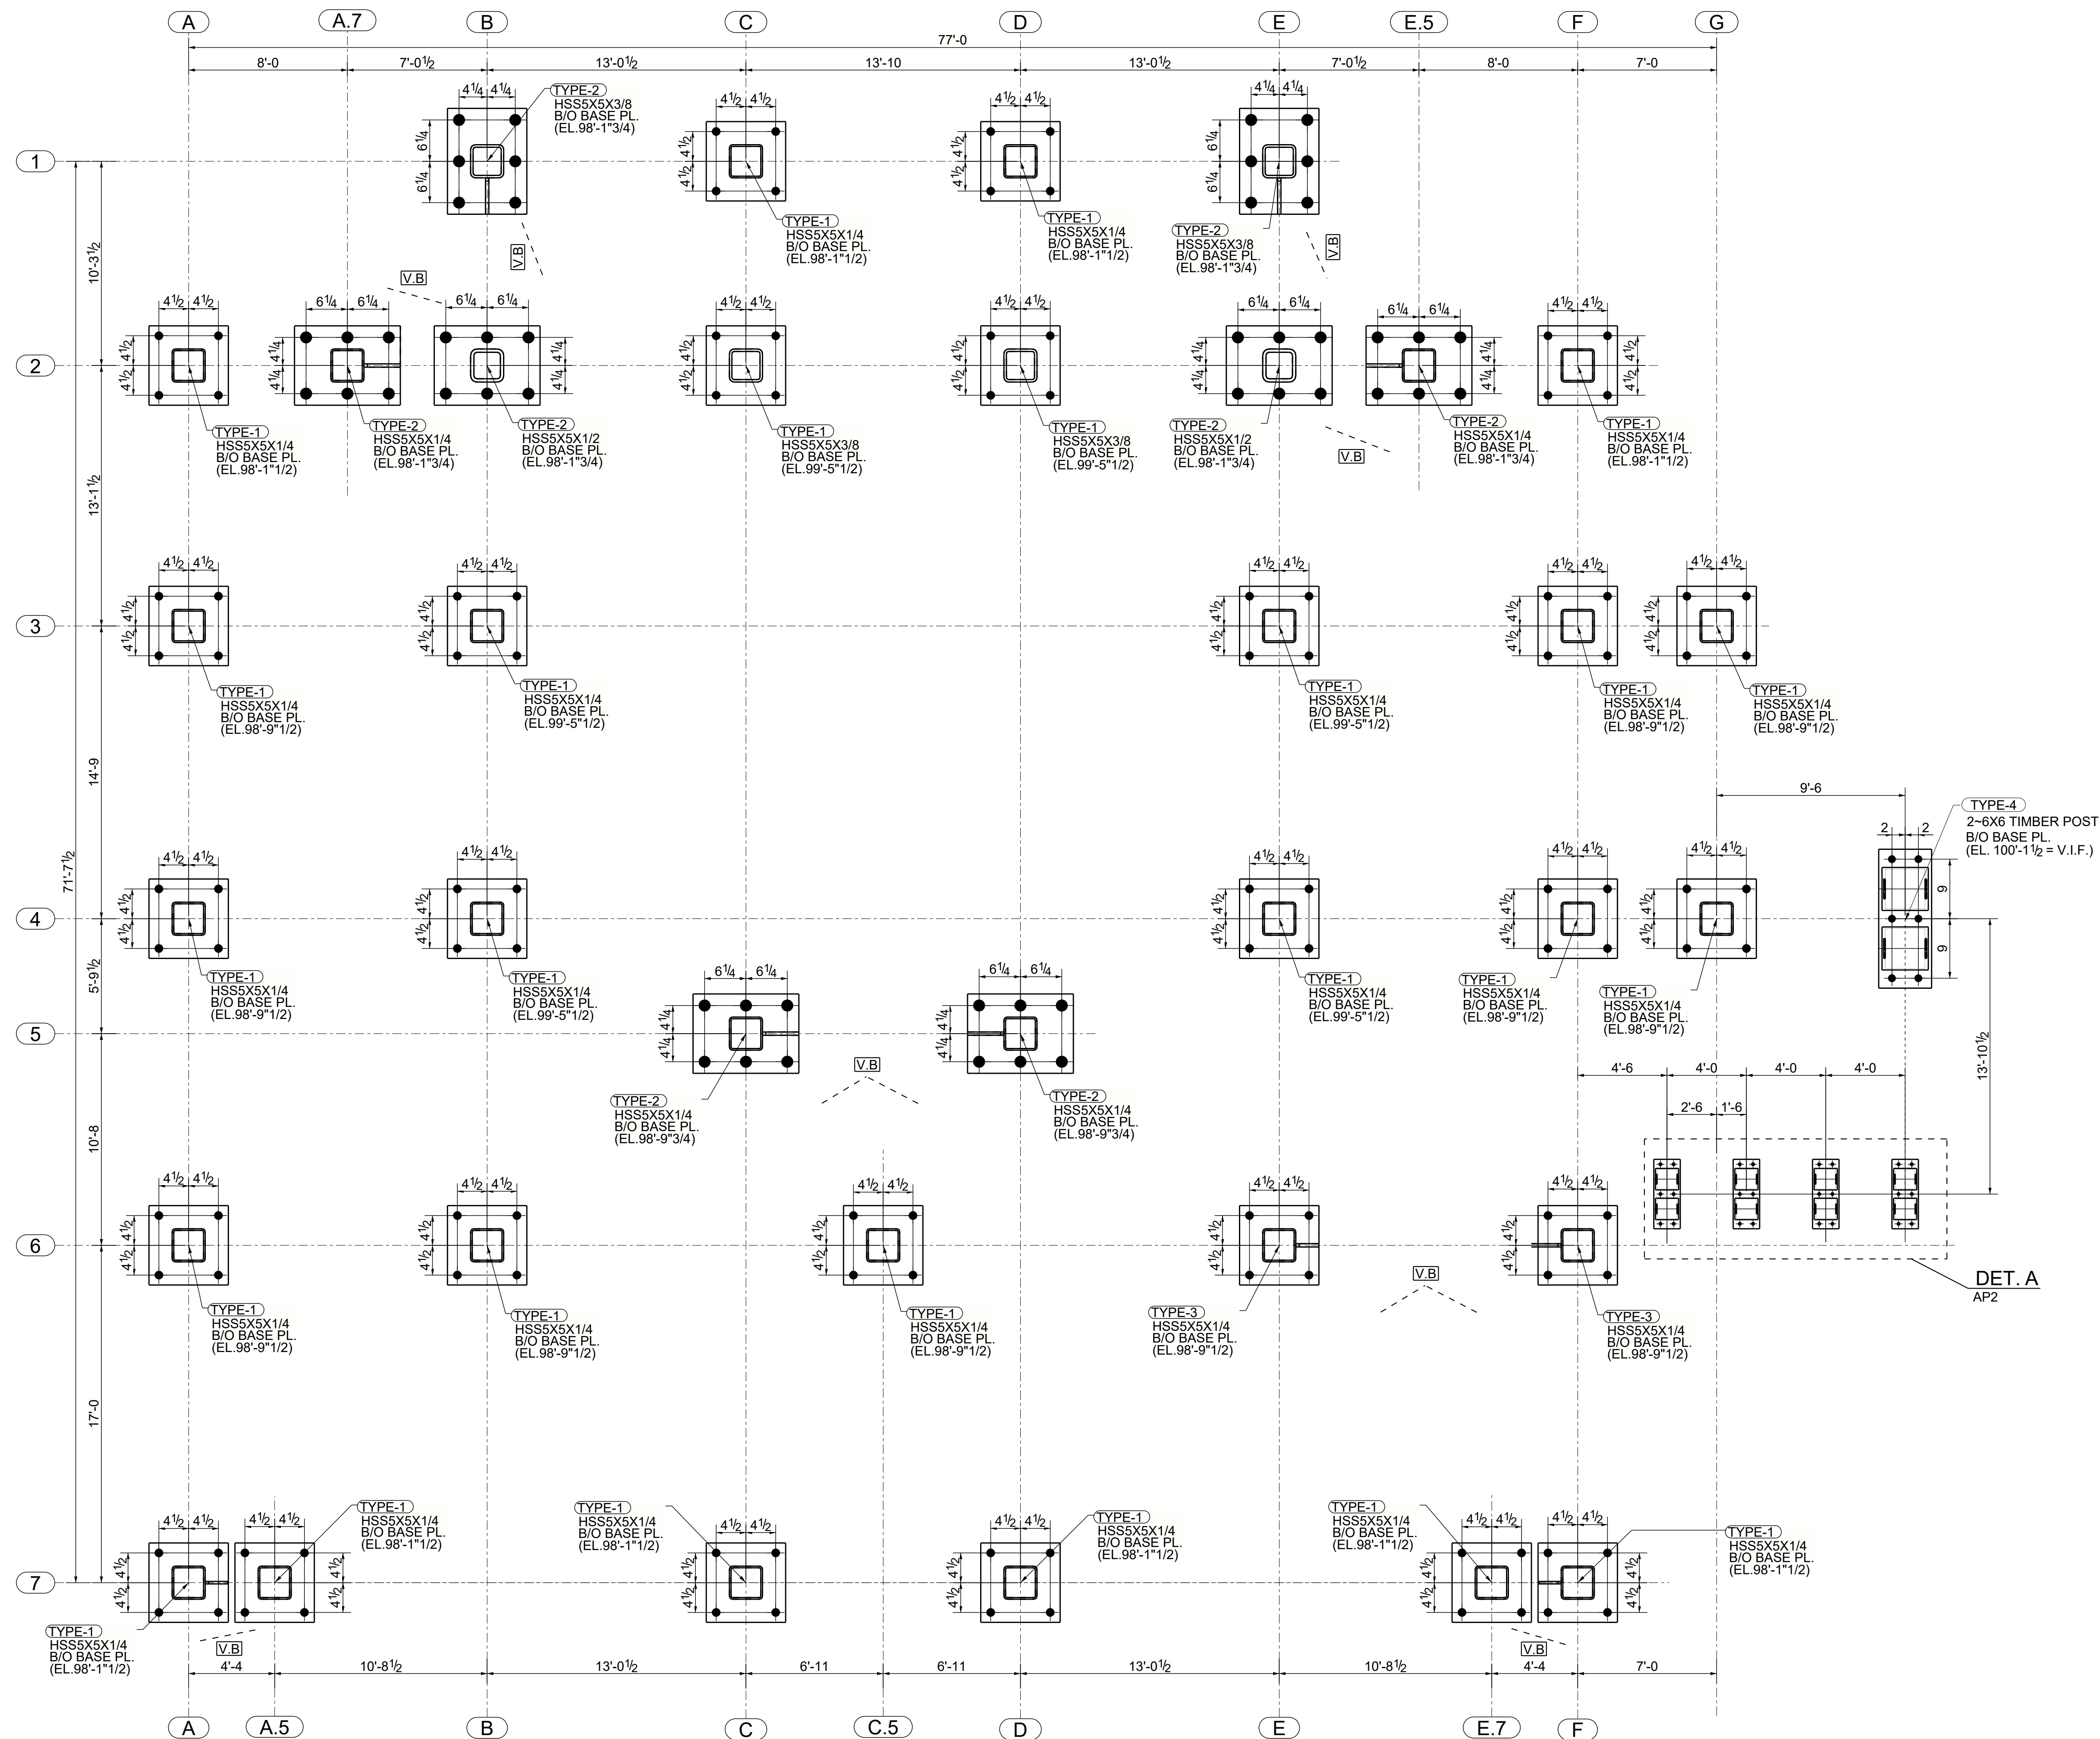

ANCHOR BOLT SETTING PLAN
(REFER : FOUNDATION PLAN 1/S.1.1)


FOR FIELD USE :01/19/2024

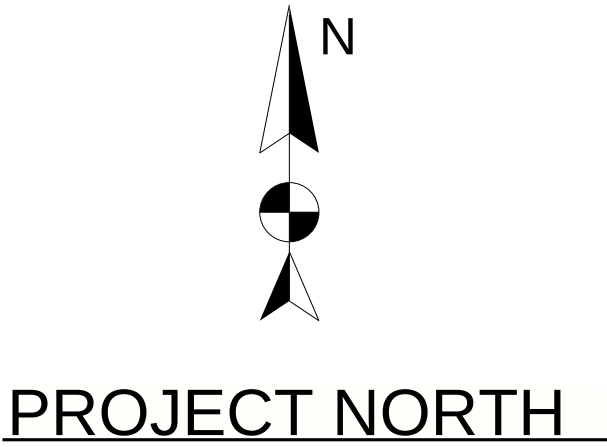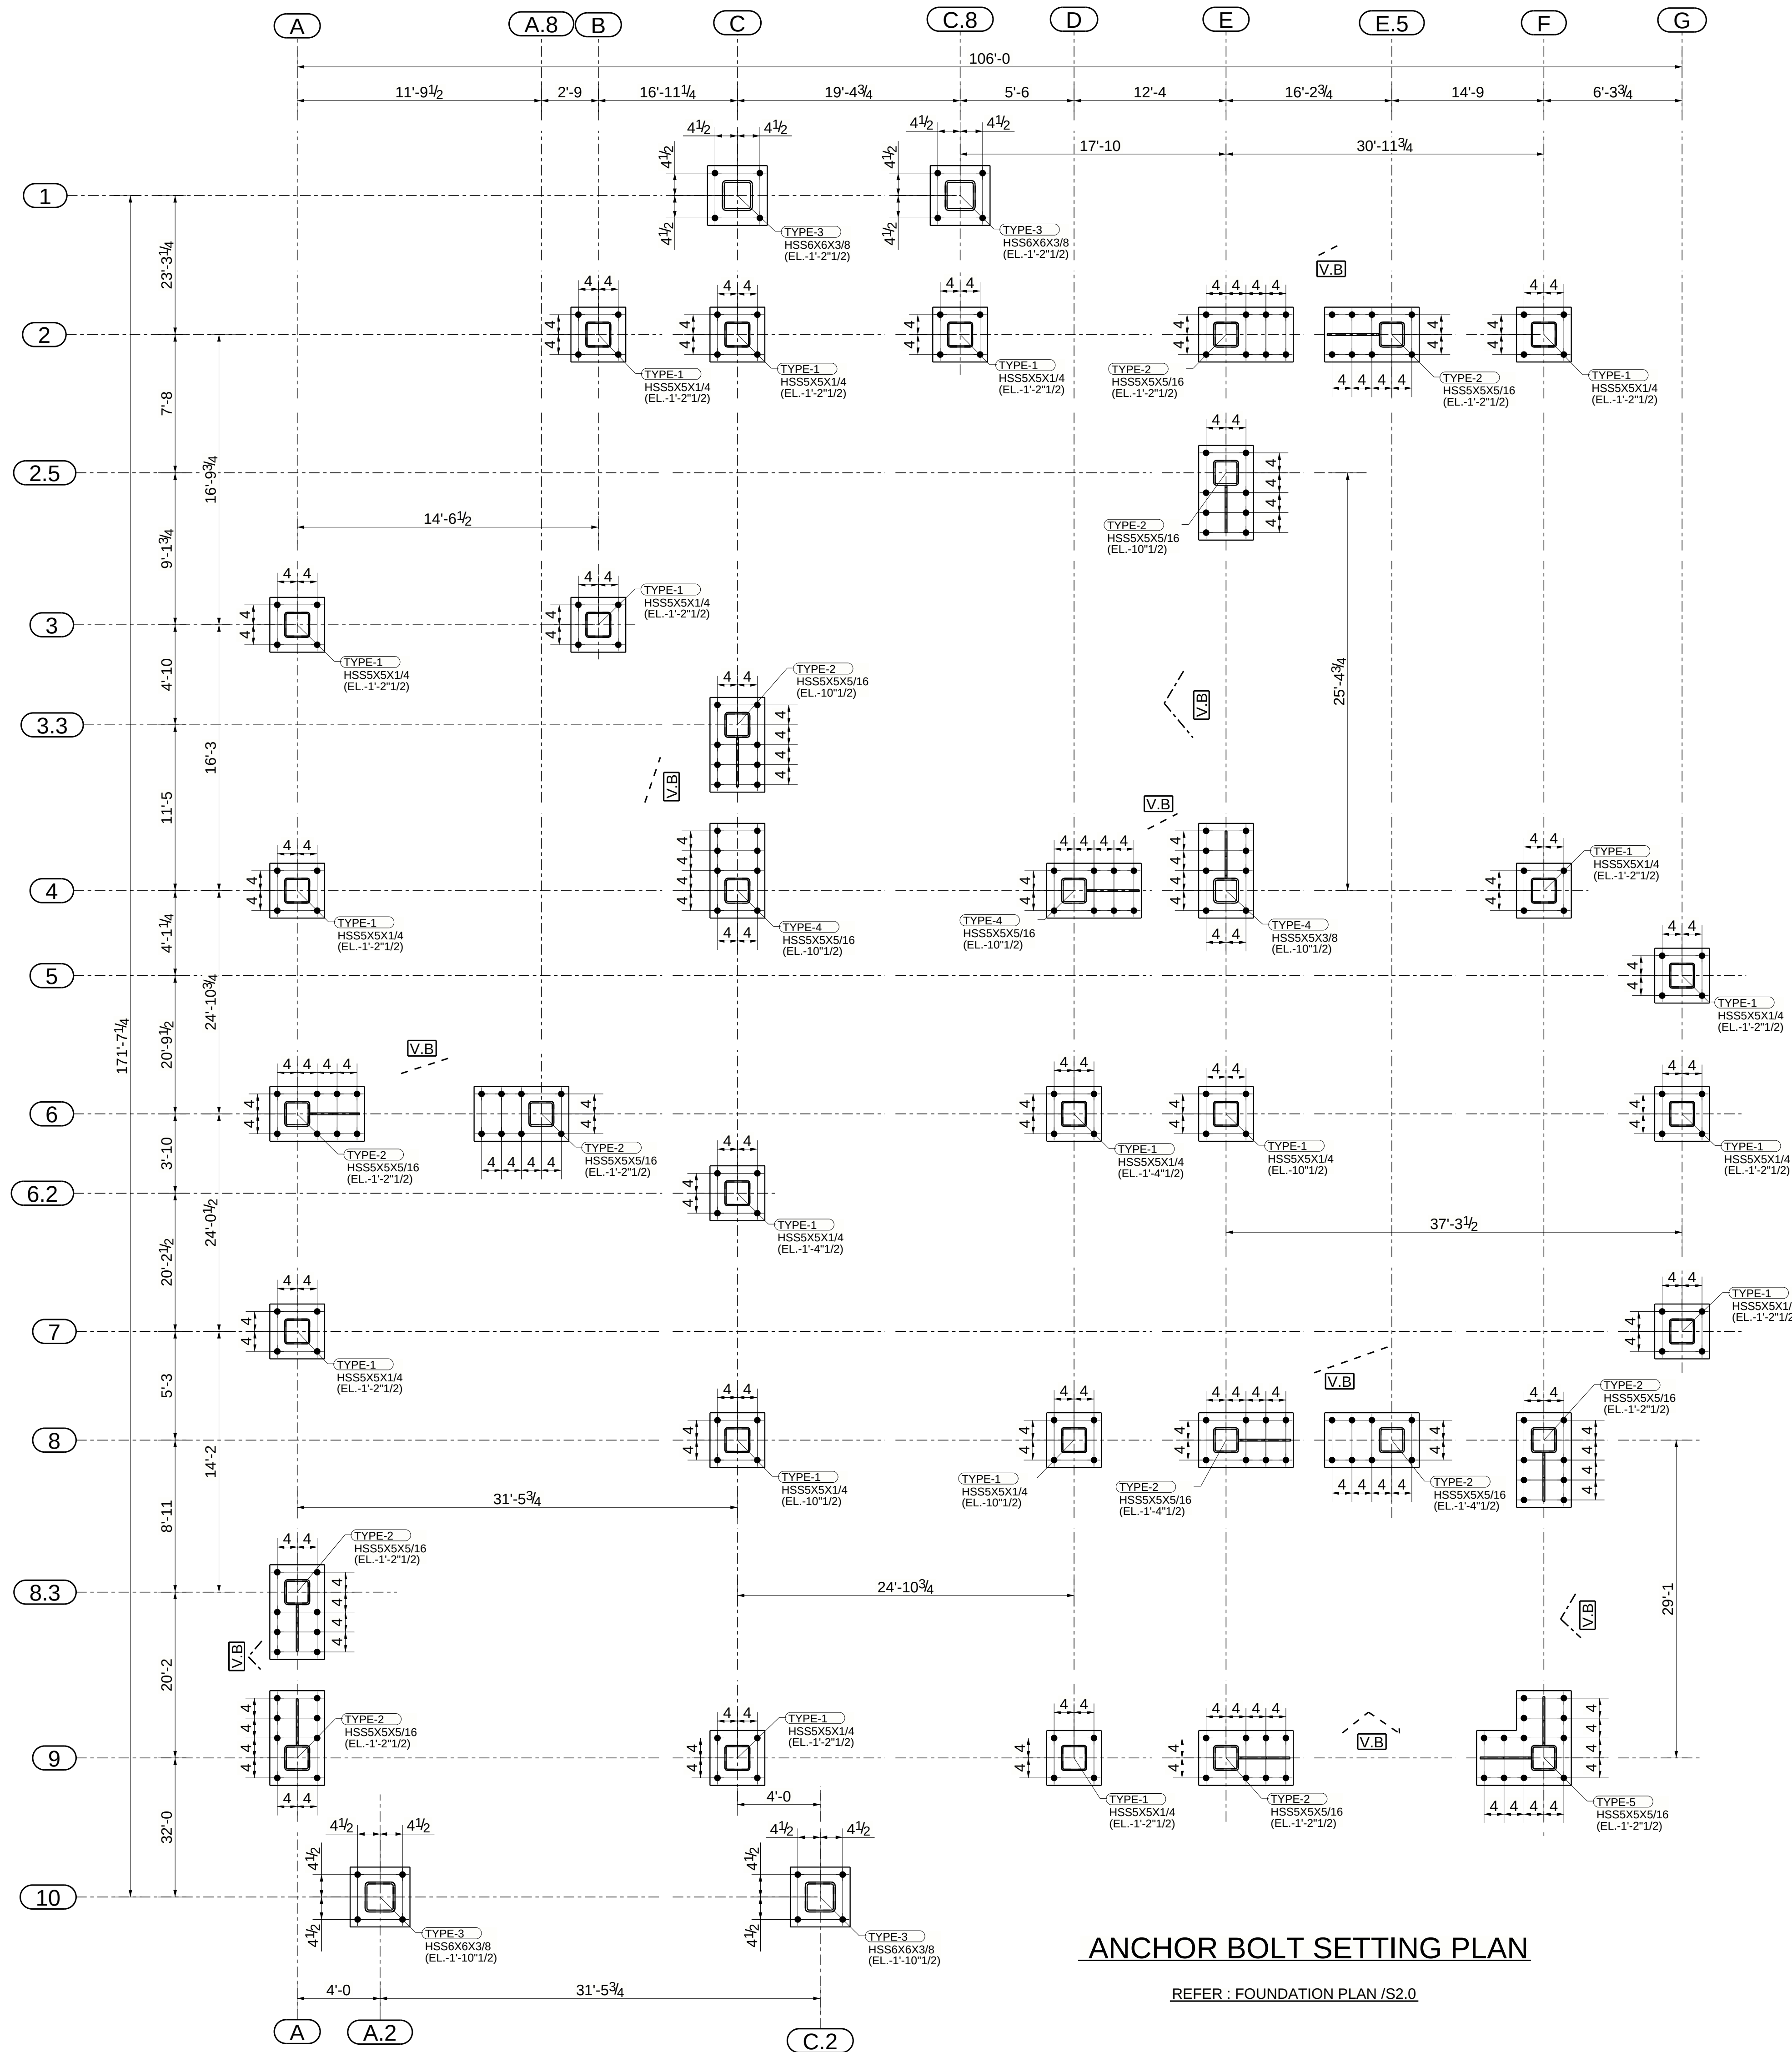

ANCHOR BOLT SETTING PLAN



REFER : FOUNDATION PLAN /S2.0



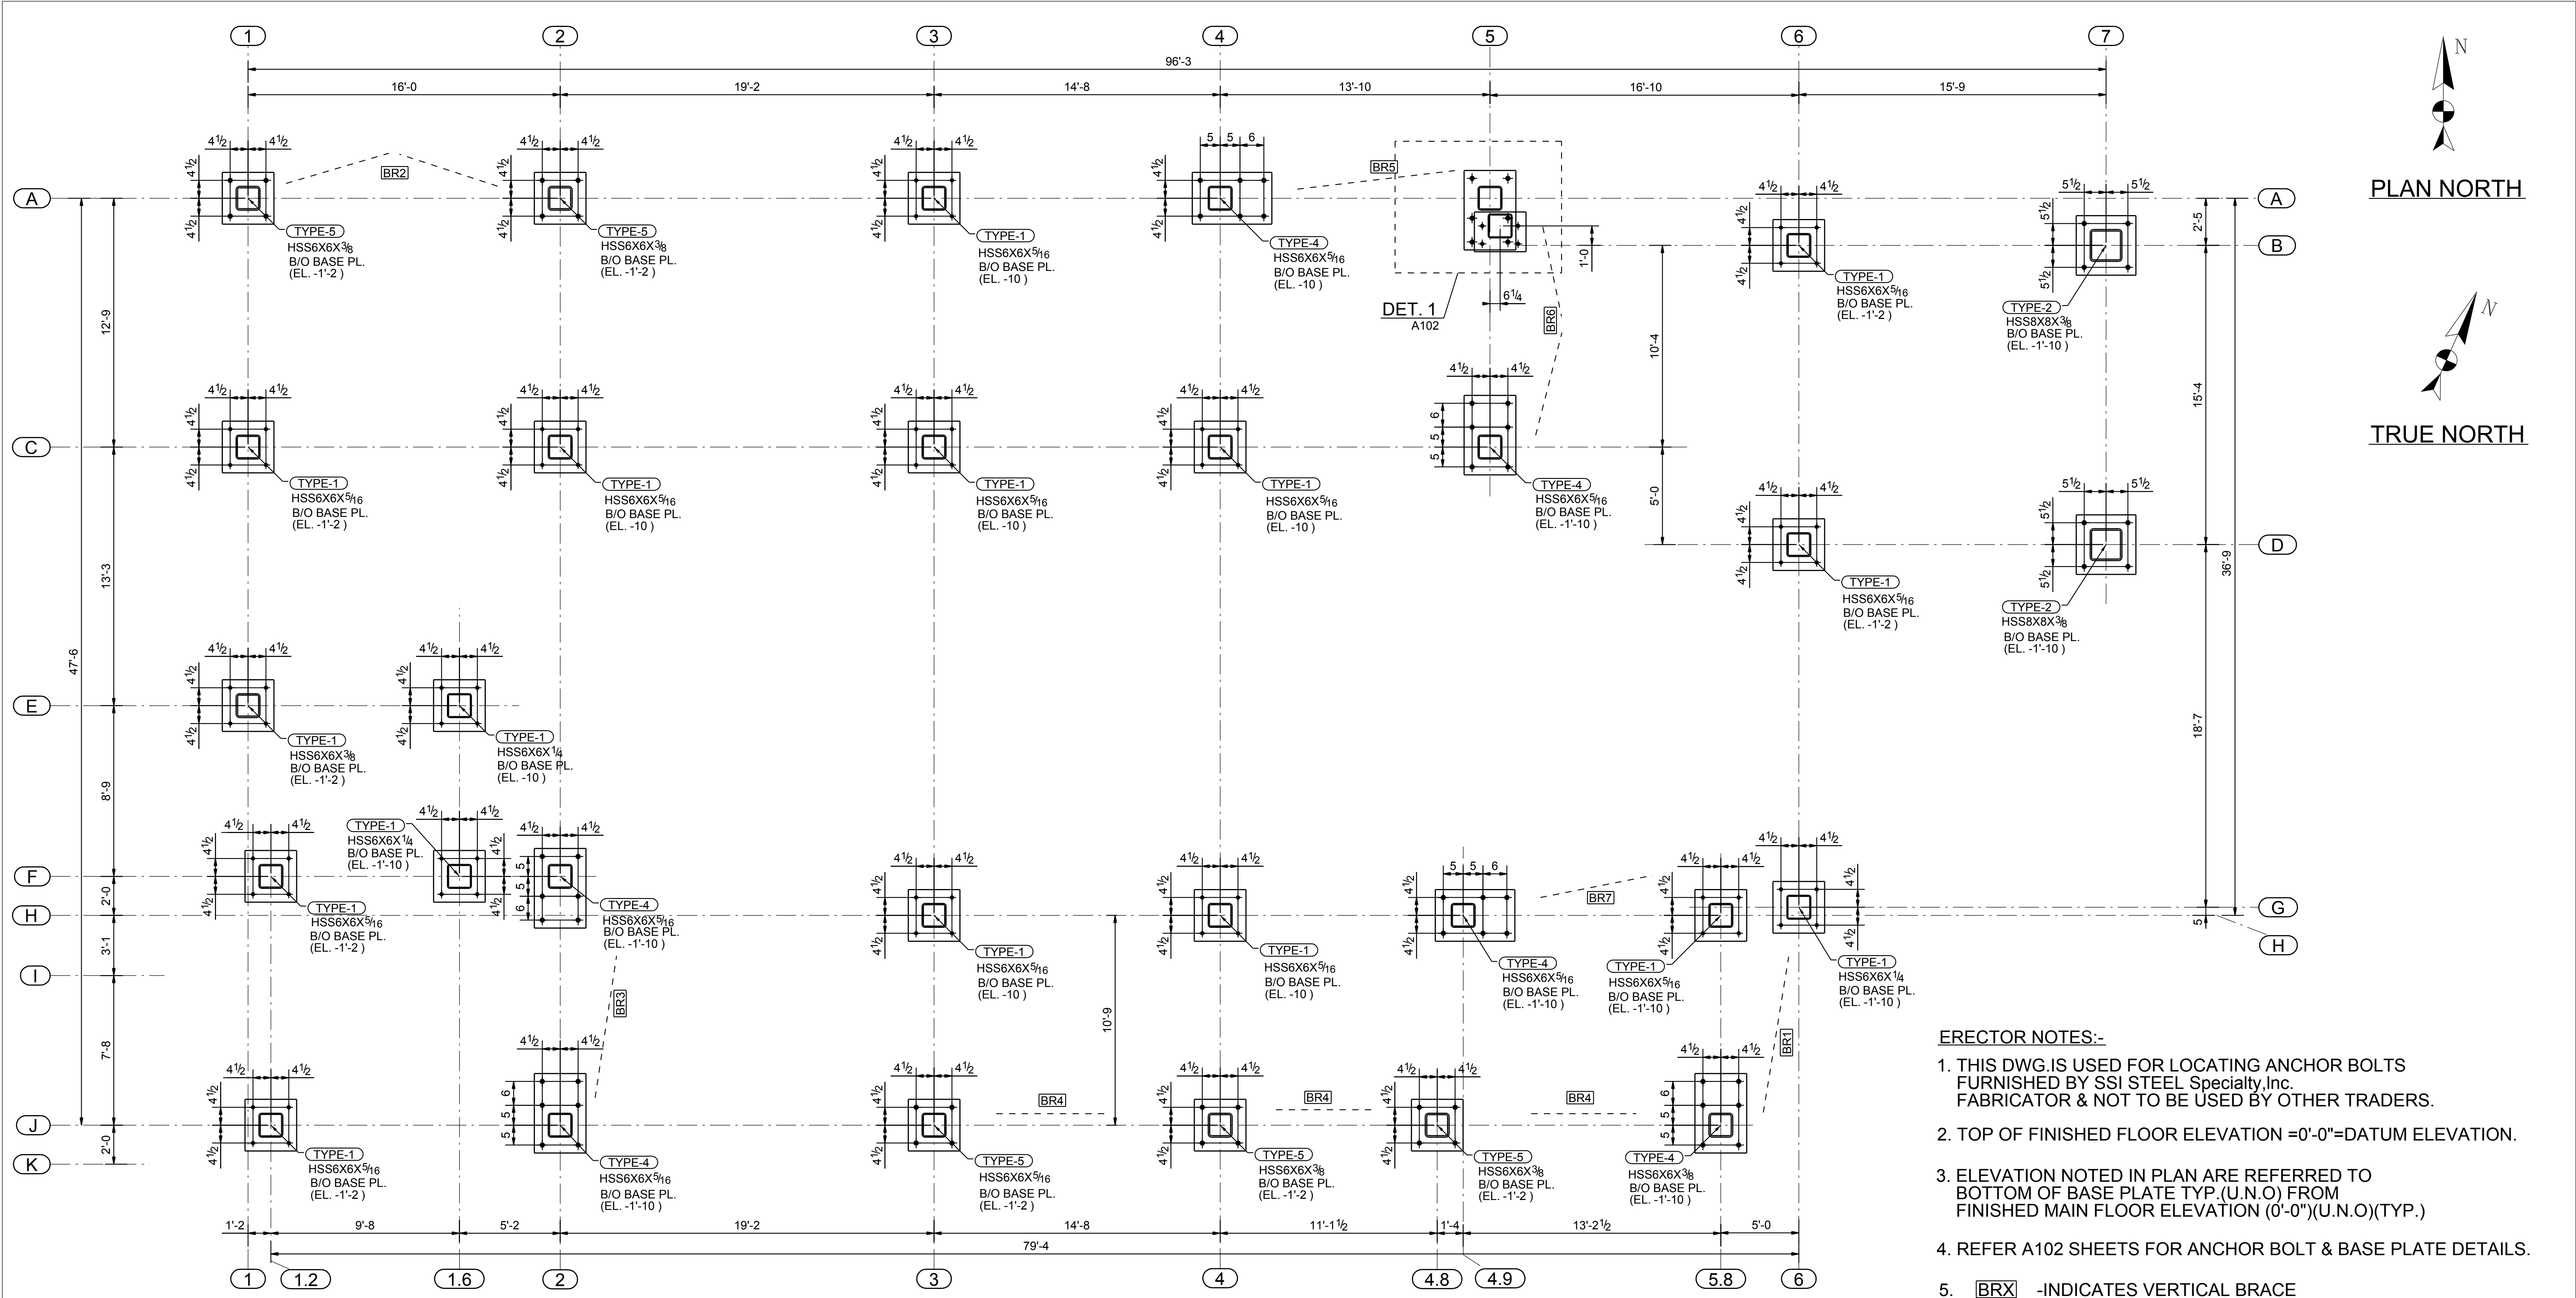


ANCHOR BOLT SETTING PLAN & GRID LOCATION PLAN
(REFER : FOUNDATION + FLOOR SLAB PLAN 1/S1.01)

- ERECTOR NOTES:-
1. THIS DWG.IS USED FOR LOCATING ANCHOR BOLTS FURNISHED BY SSI STEEL Specialty,Inc. FABRICATOR & NOT TO BE USED BY OTHER TRADERS.
 2. TOP OF FINISHED FLOOR ELEVATION =0'-0"=DATUM ELEVATION.
 3. ELEVATION NOTED IN PLAN ARE REFERRED TO BOTTOM OF BASE PLATE TYP.(U.N.O) FROM FINISHED MAIN FLOOR ELEVATION (0'-0") (U.N.O) (TYP.)
 4. REFER A102 SHEETS FOR ANCHOR BOLT & BASE PLATE DETAILS.
 5. BR -INDICATES VERTICAL BRACE

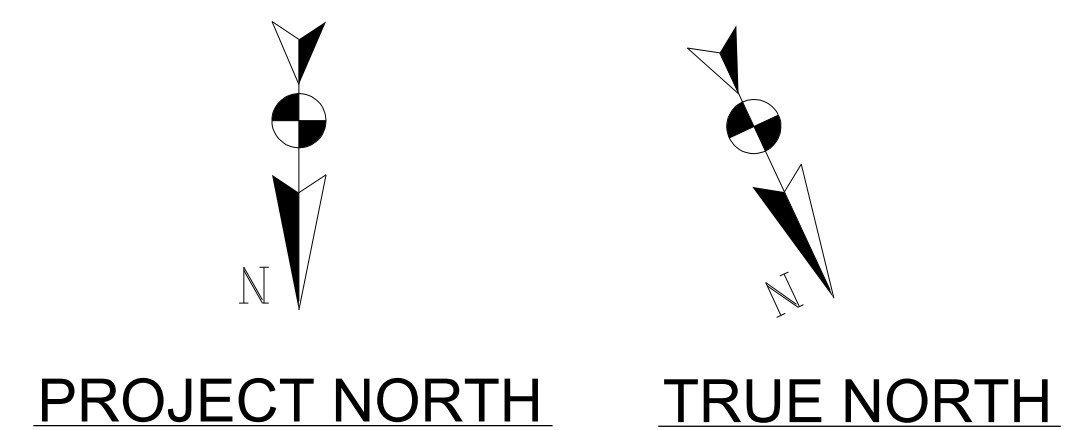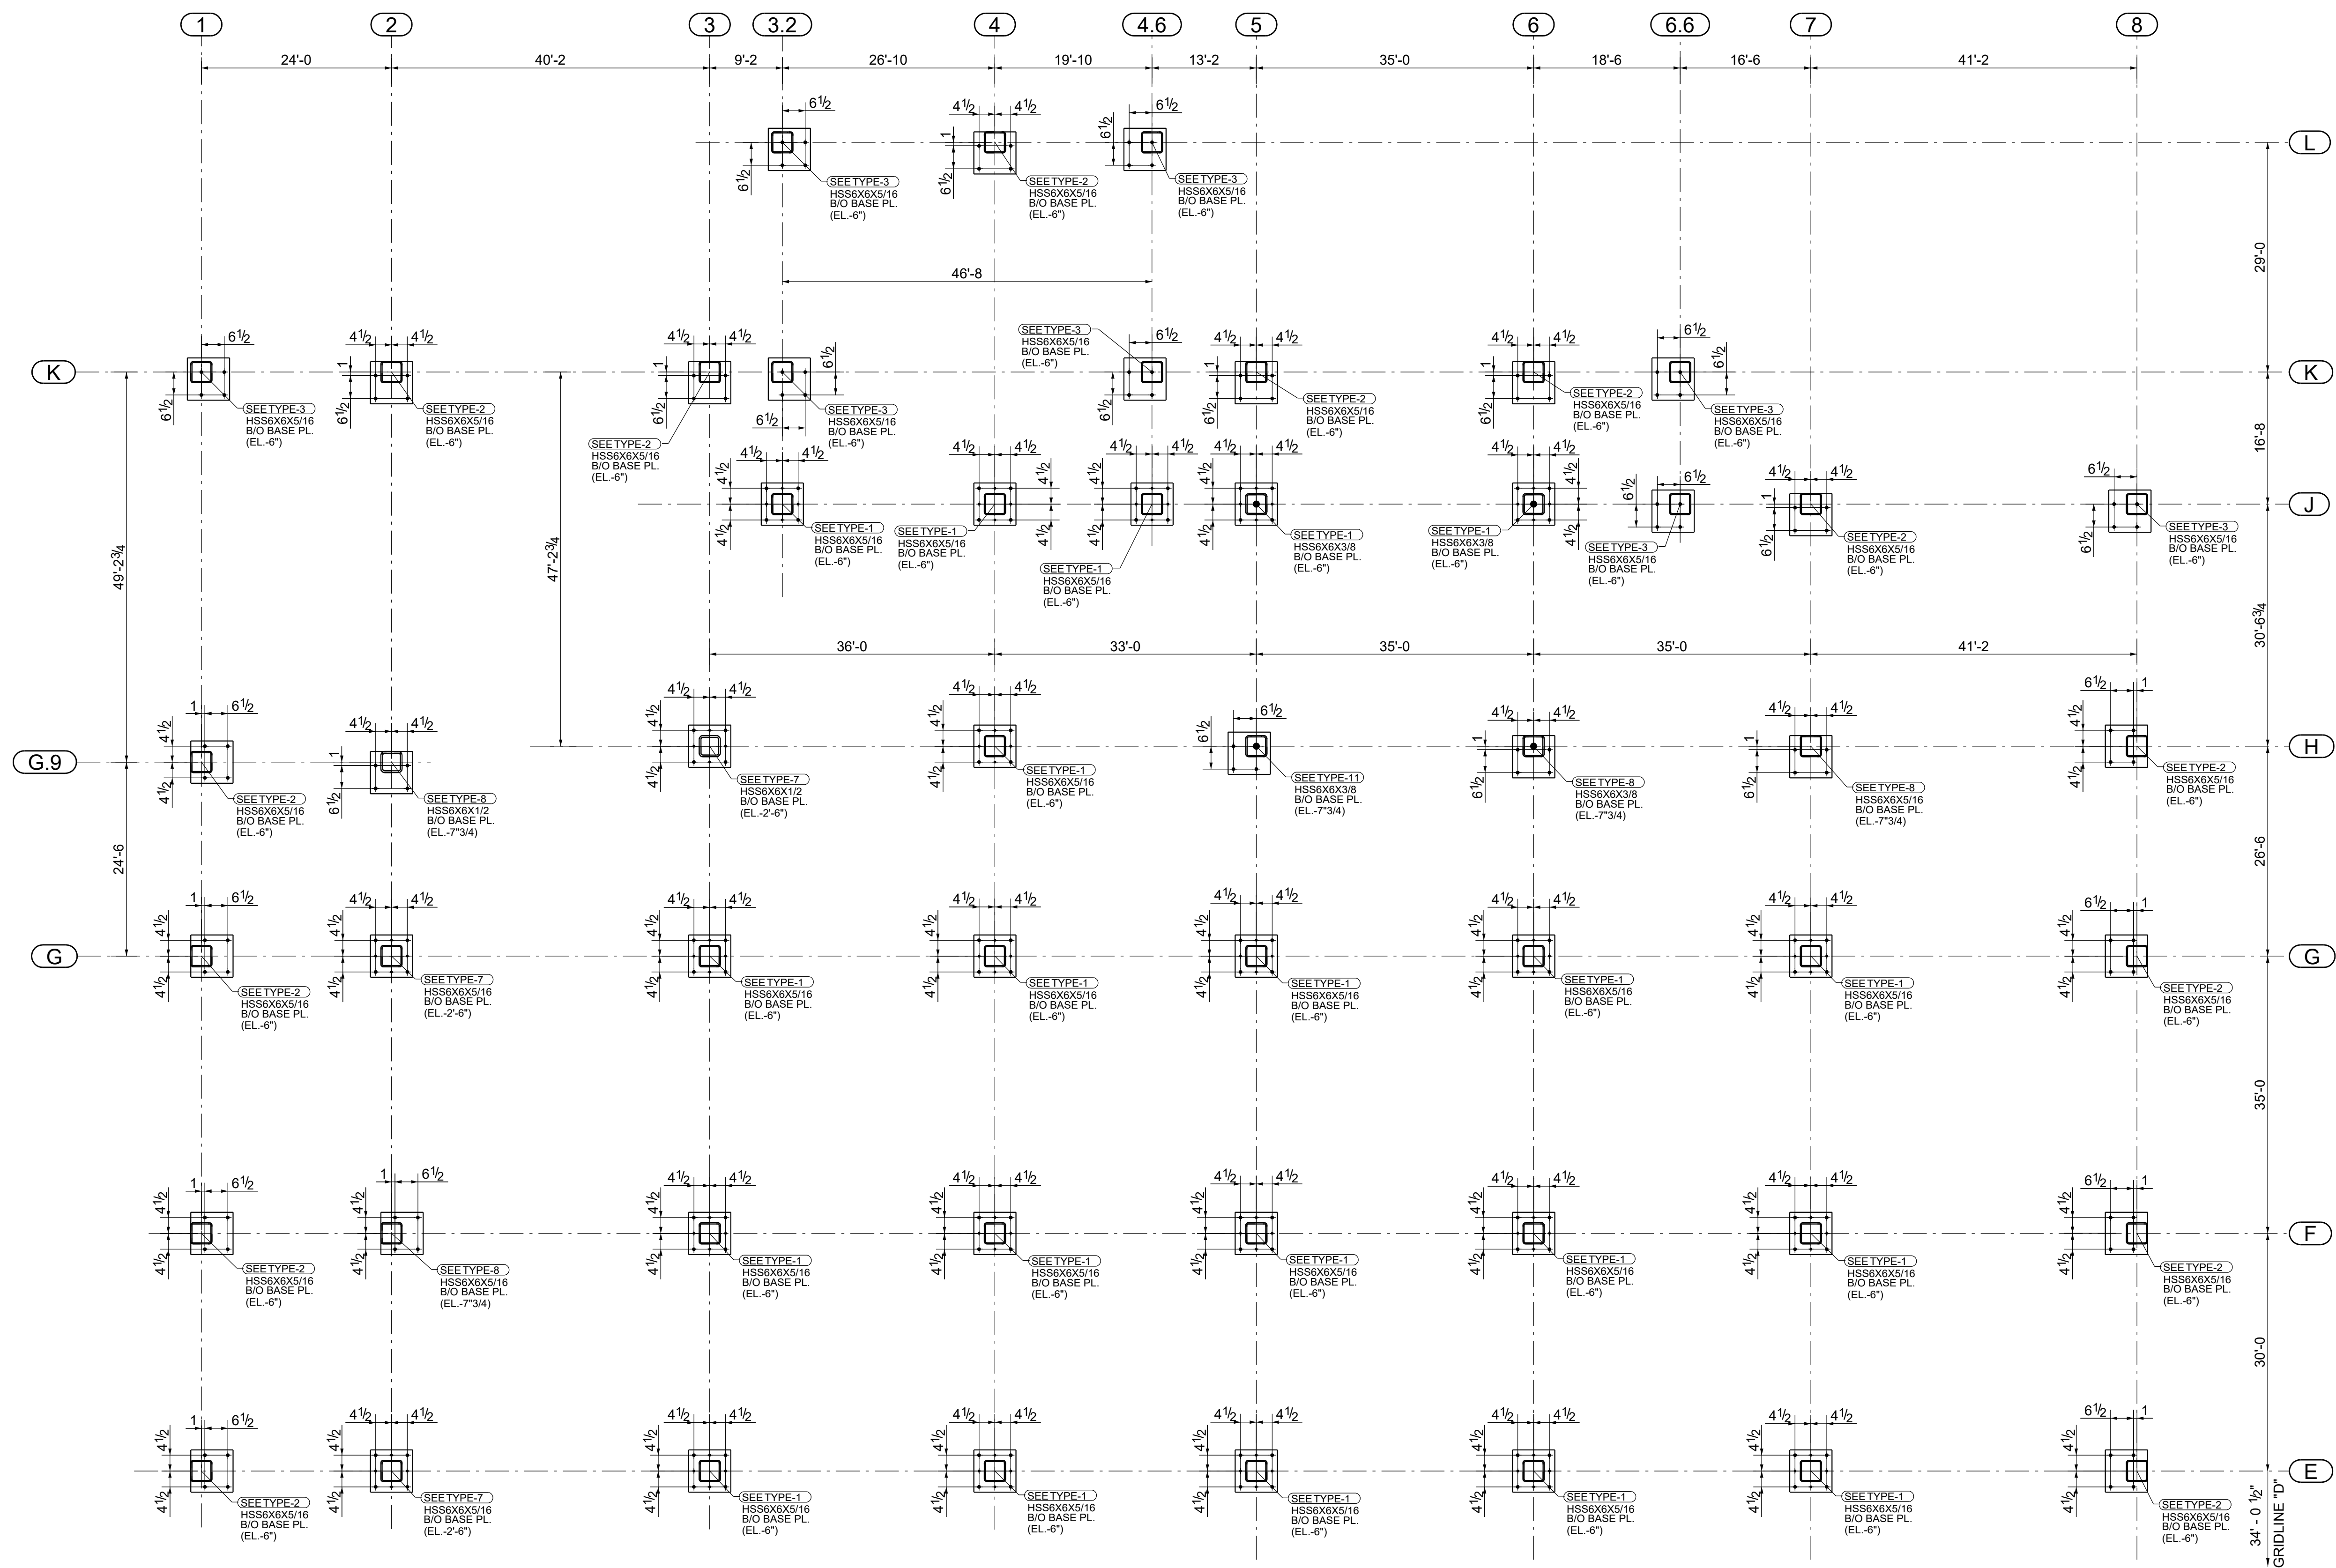

NOTES:-

1. REFER A101 SHEET FOR ANCHOR BOLT NOTES.
2. REFER A105 SHEET FOR ANCHOR BOLT DETAILS.

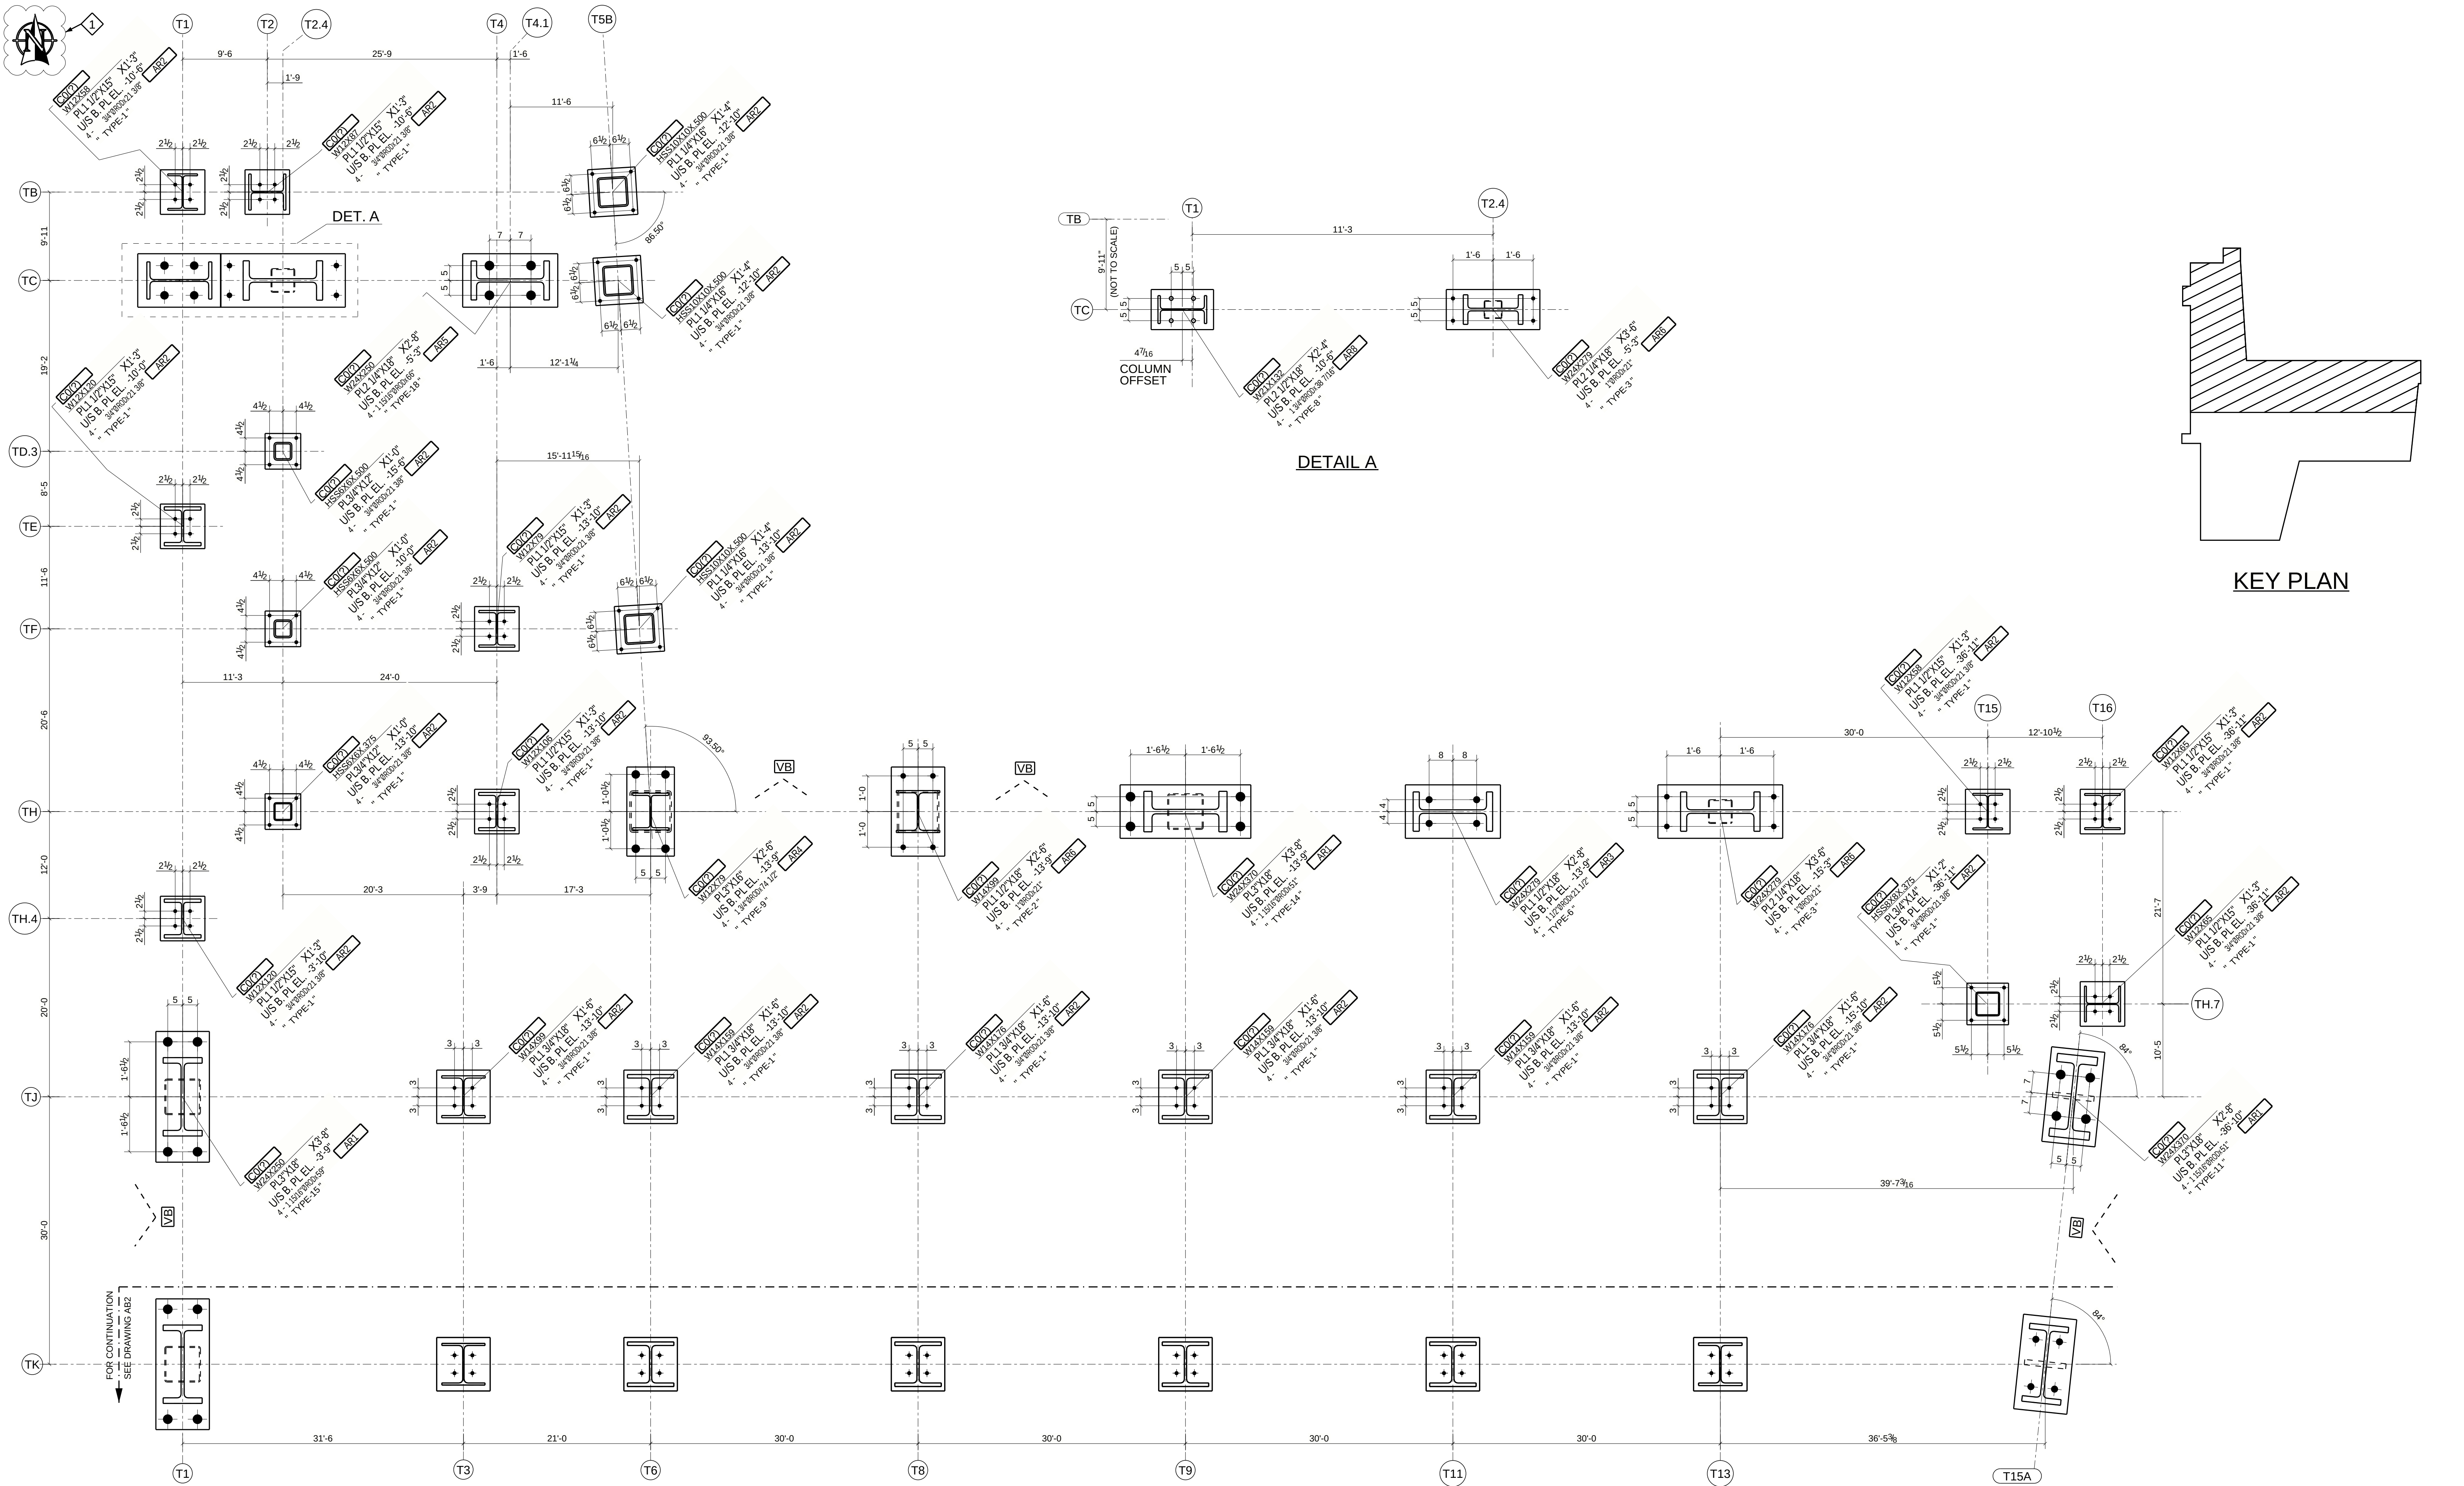

PARTIAL ANCHOR BOLT PLAN


- ALL U/S BASE ELEVATIONS ARE AS NOTED ON PLAN.
- SEE AB3,AB4 & AB5 SHEET FOR BASE PLATE DETAILS.
- VB INDICATES VERTICAL BRACING.

APPROVER VERIFY AND CONFIRM THE NORTH DIRECTION.


APPROVER VERIFY ALL BOTTOM OF BASE PLATE ELEVATION.

APPROVER NOTE!


PLEASE SUPPLY/VERIFY CLOUDED INFORMATION

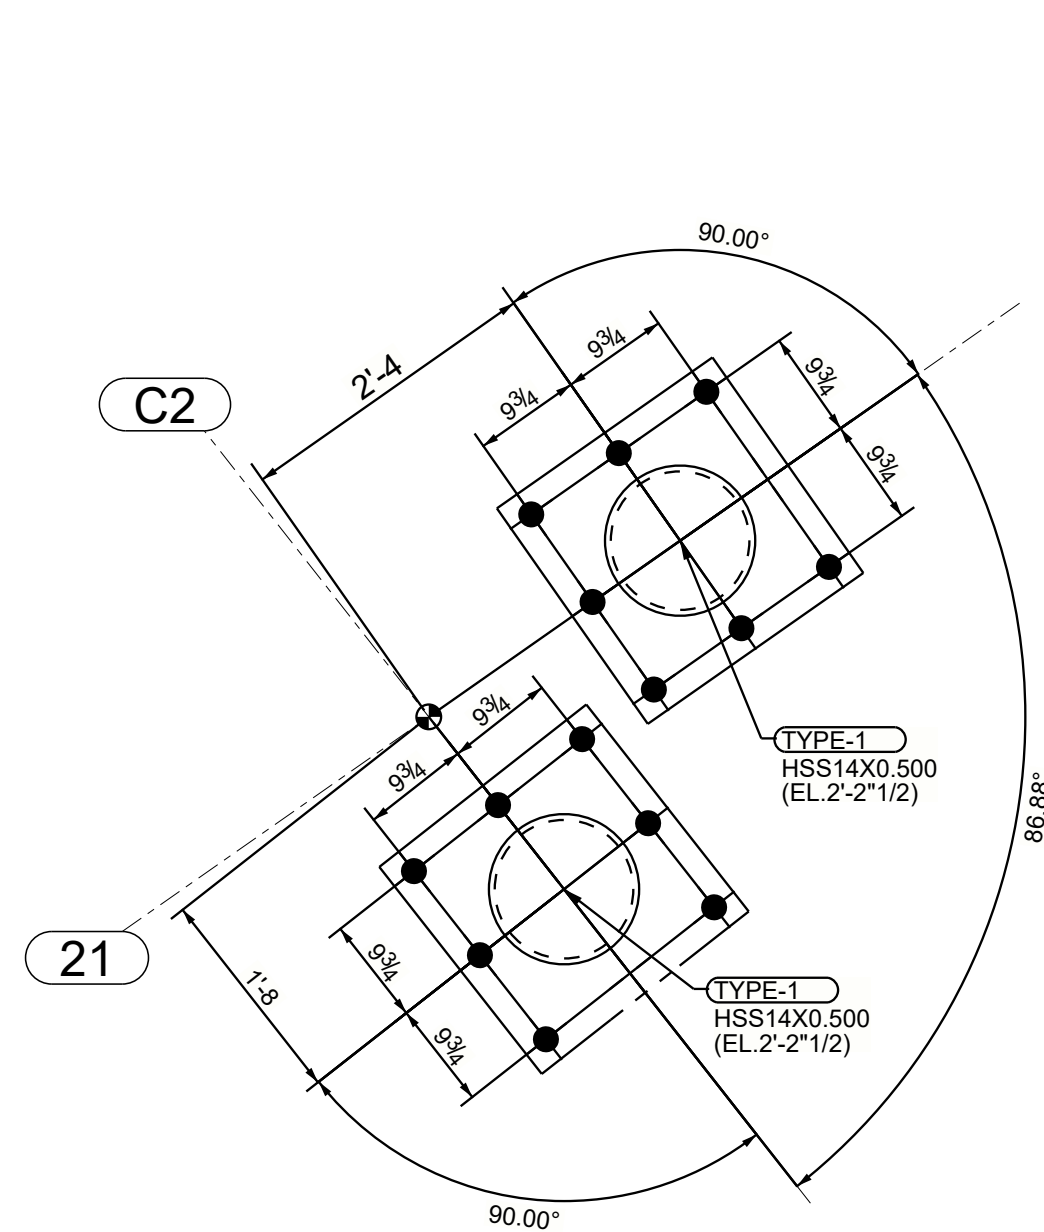


DETAIL A
1-A102

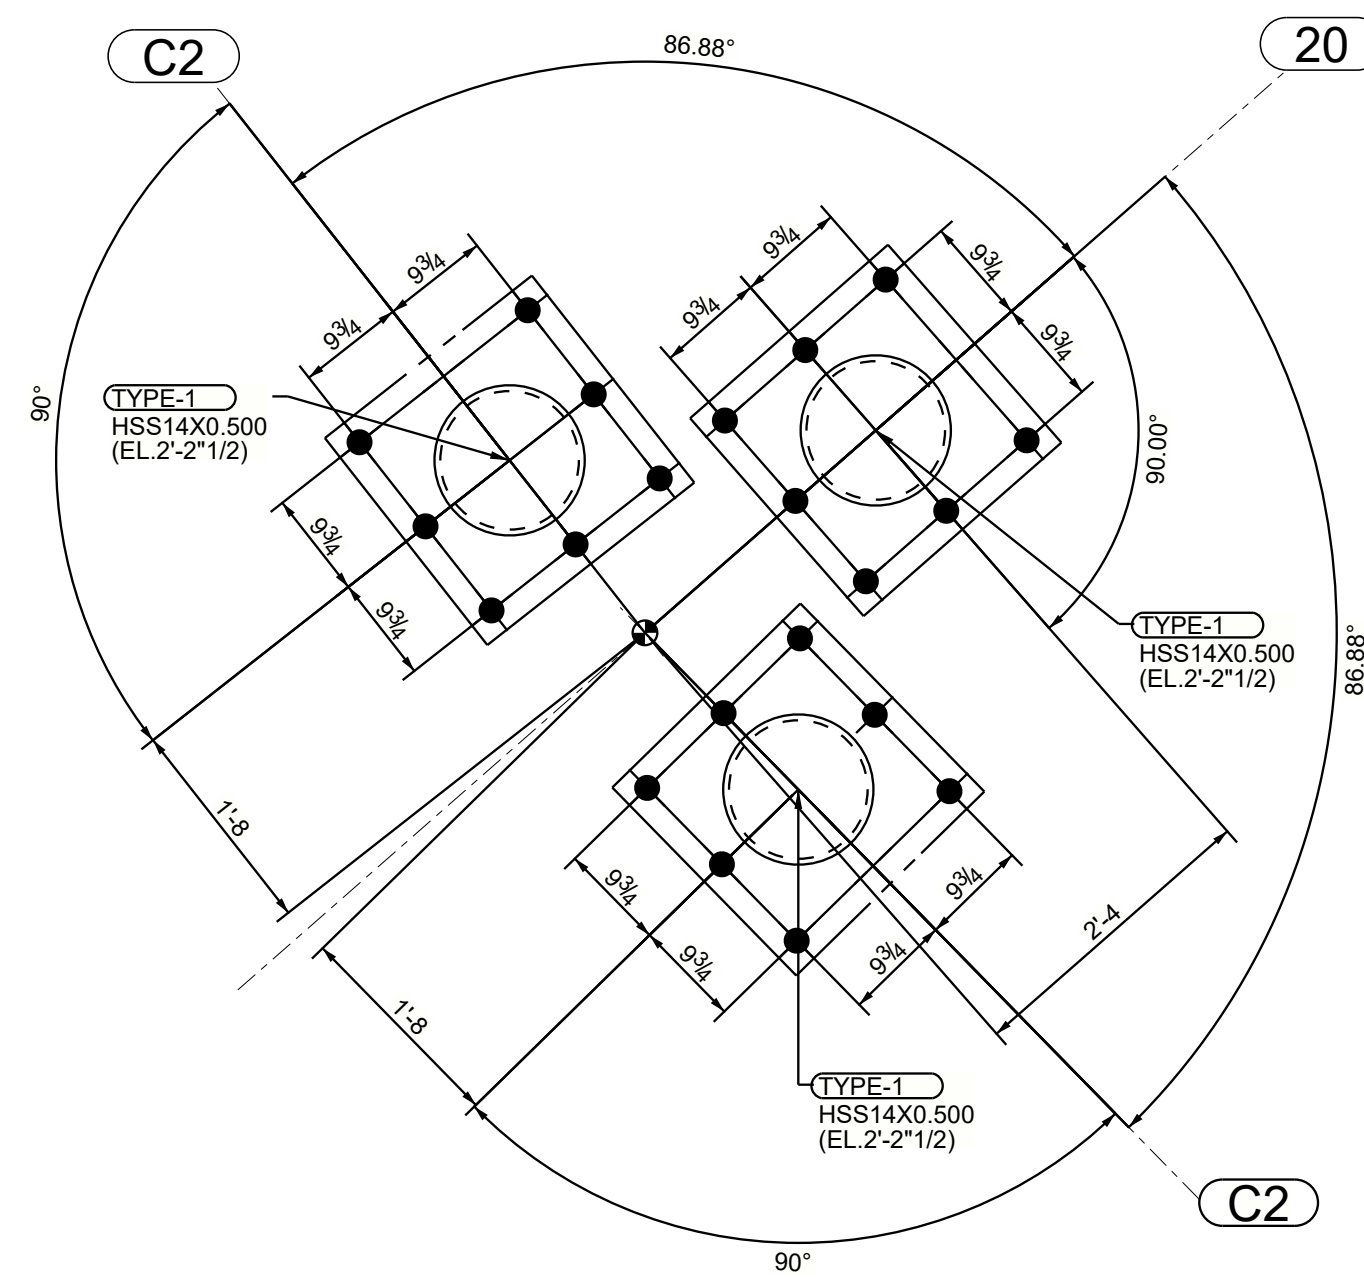




DETAIL B
1-A102

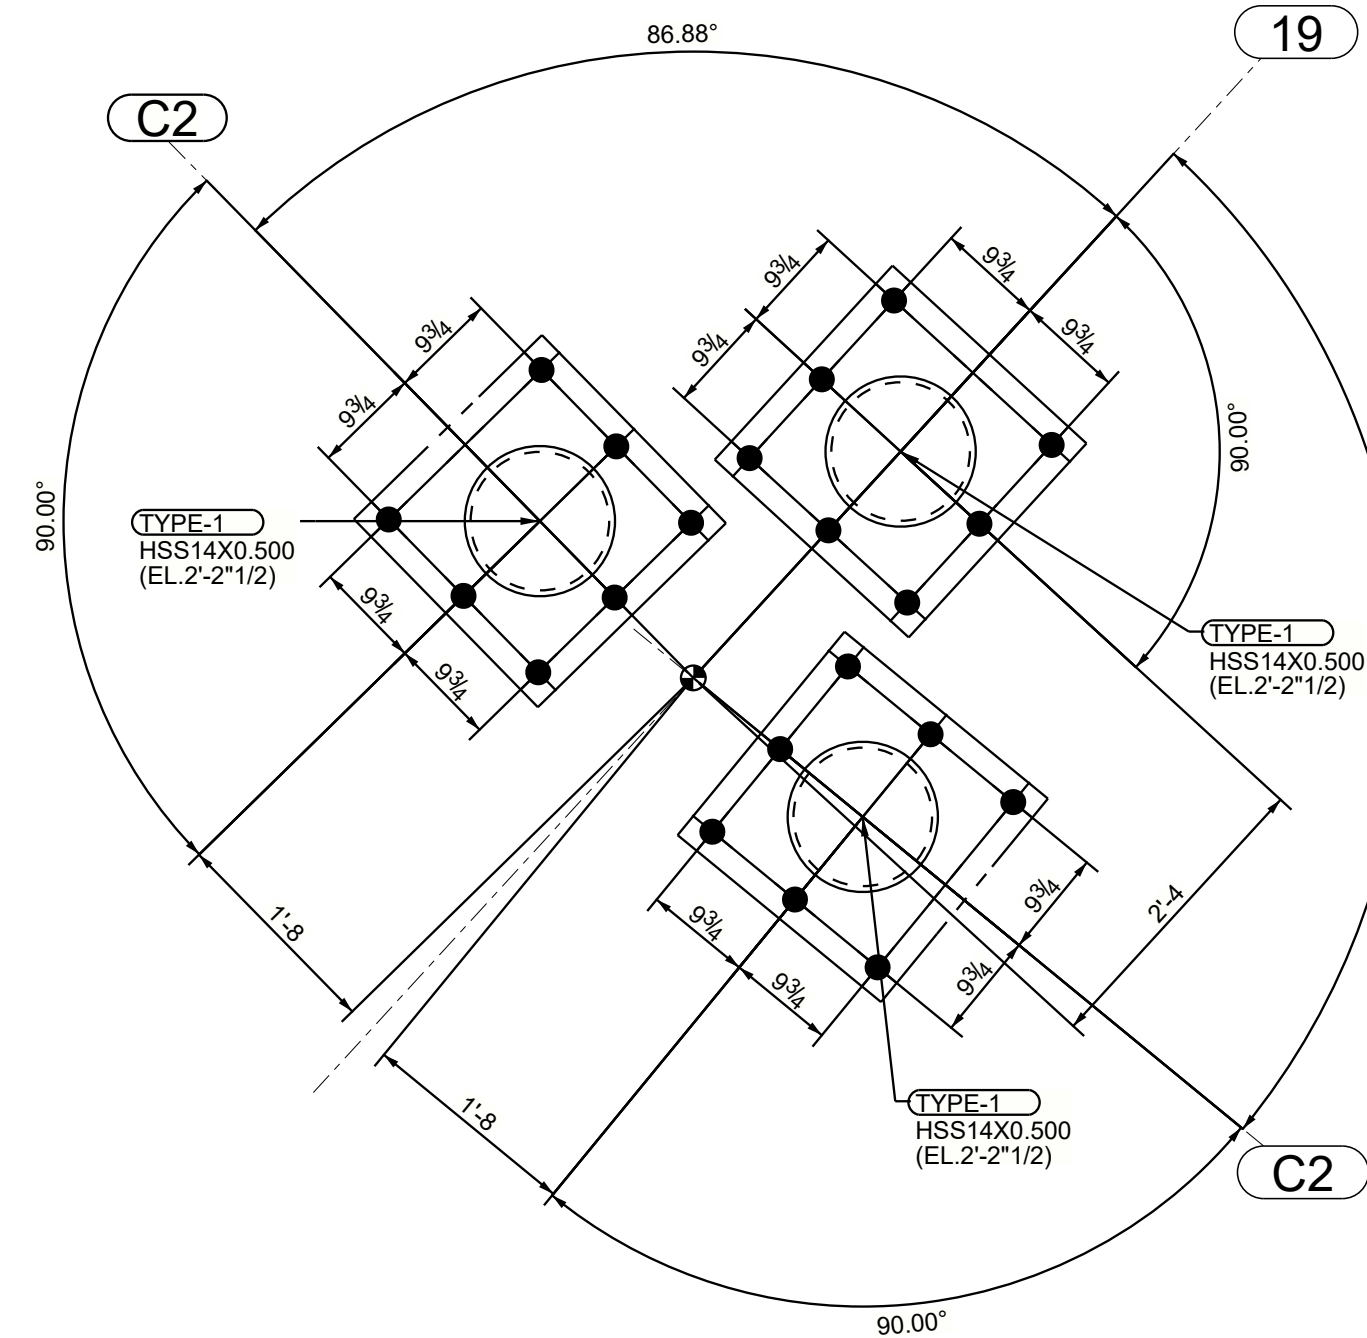


DETAIL C
1-A102

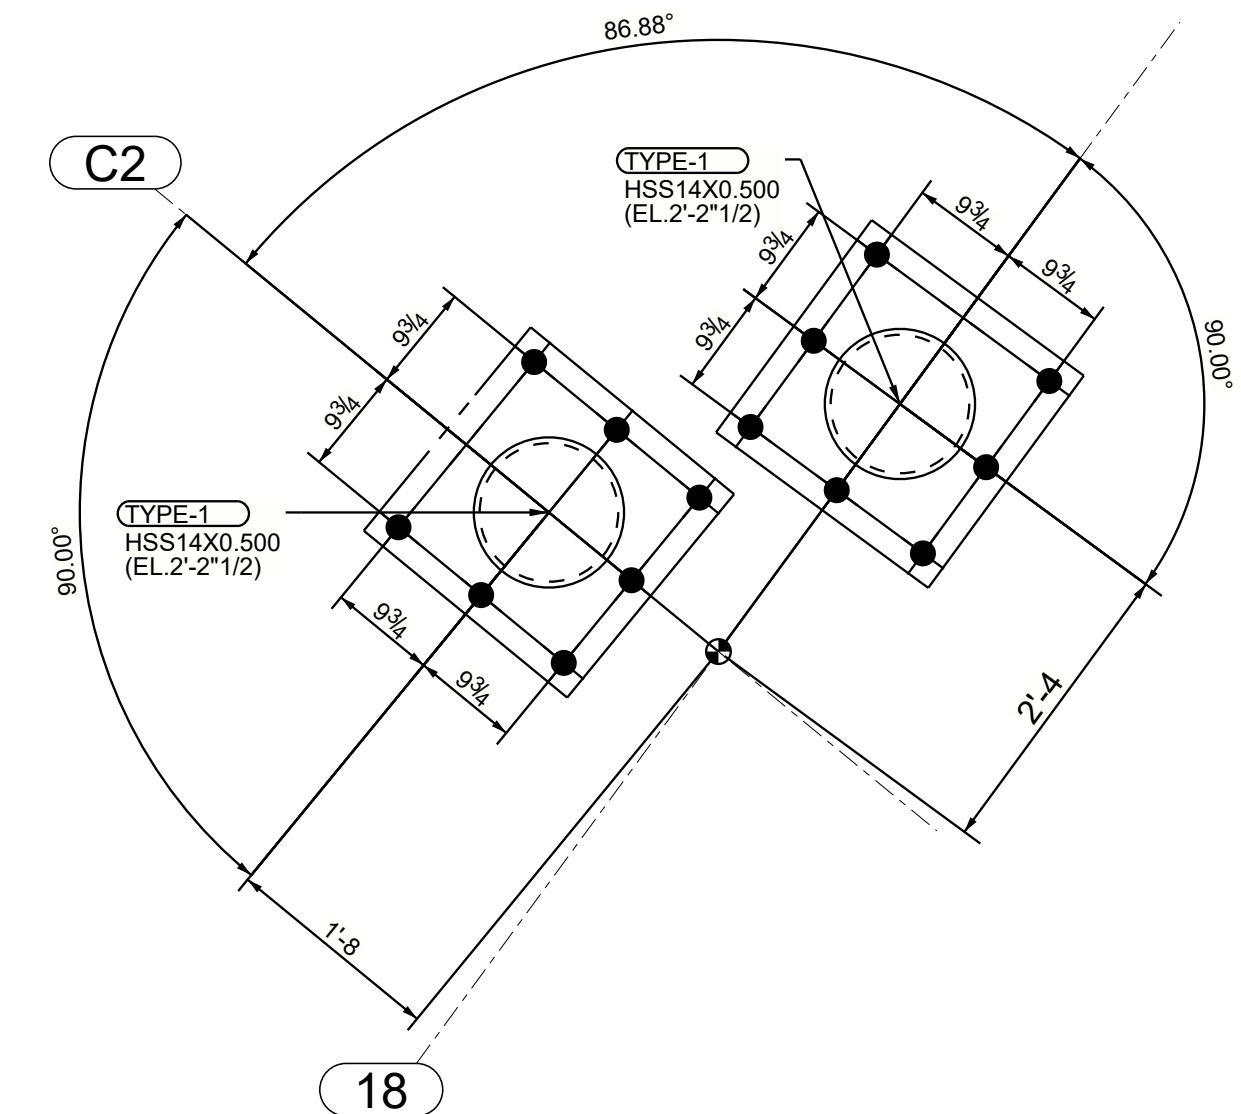









DETAIL D
1-A102

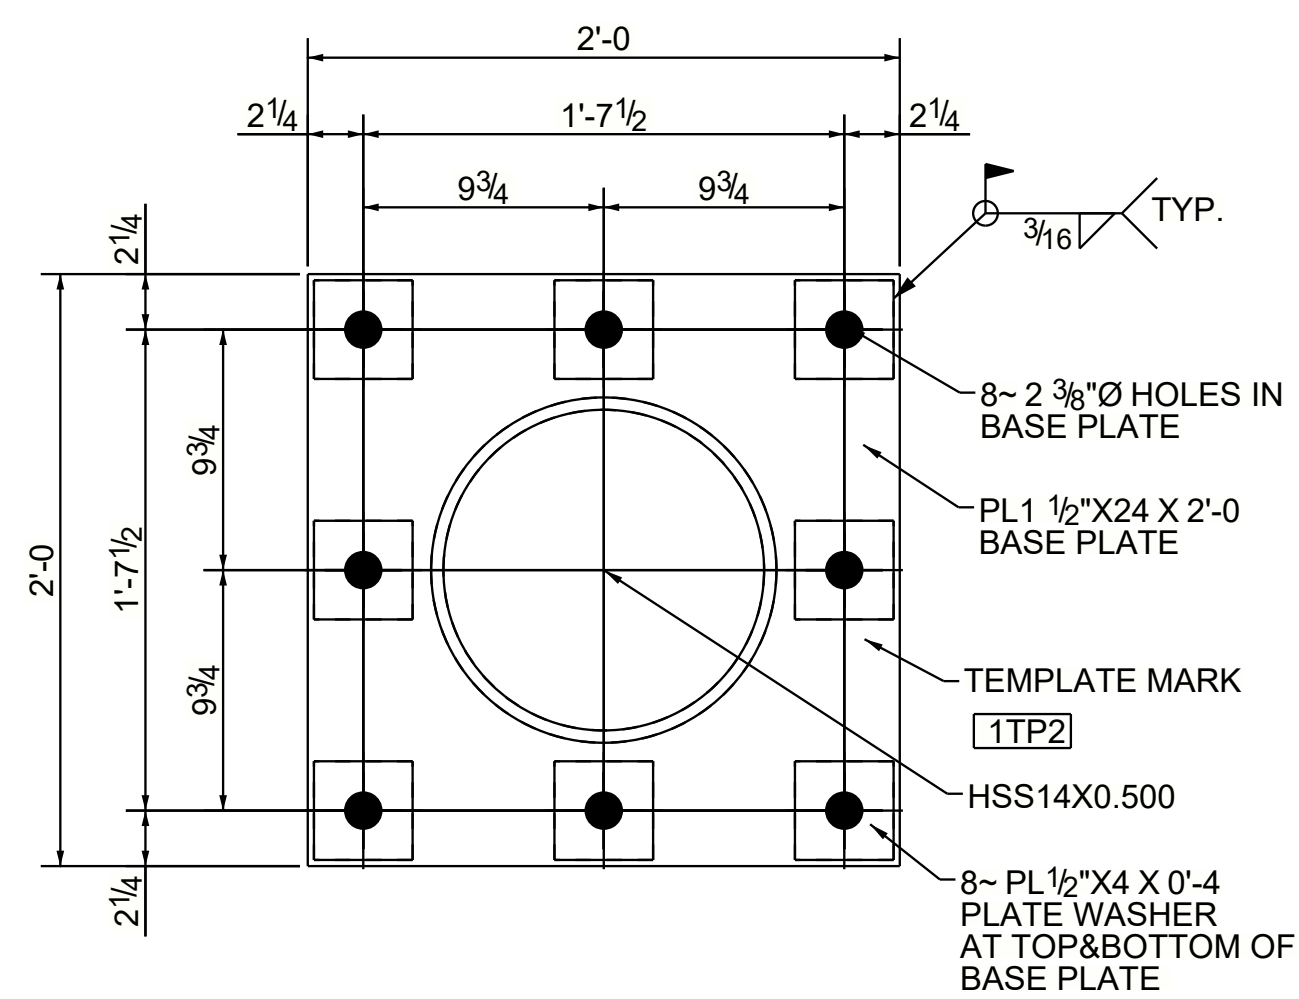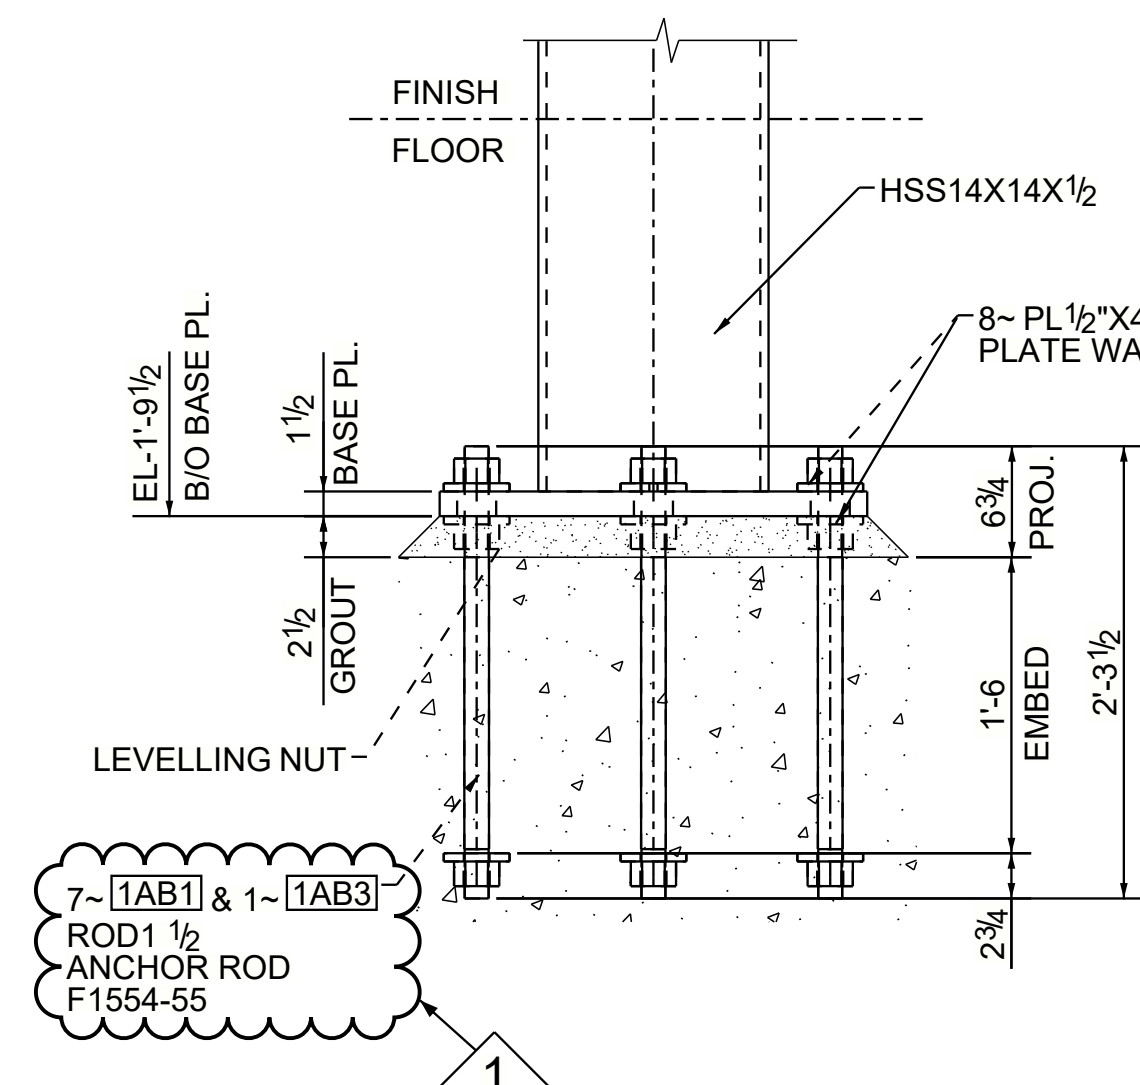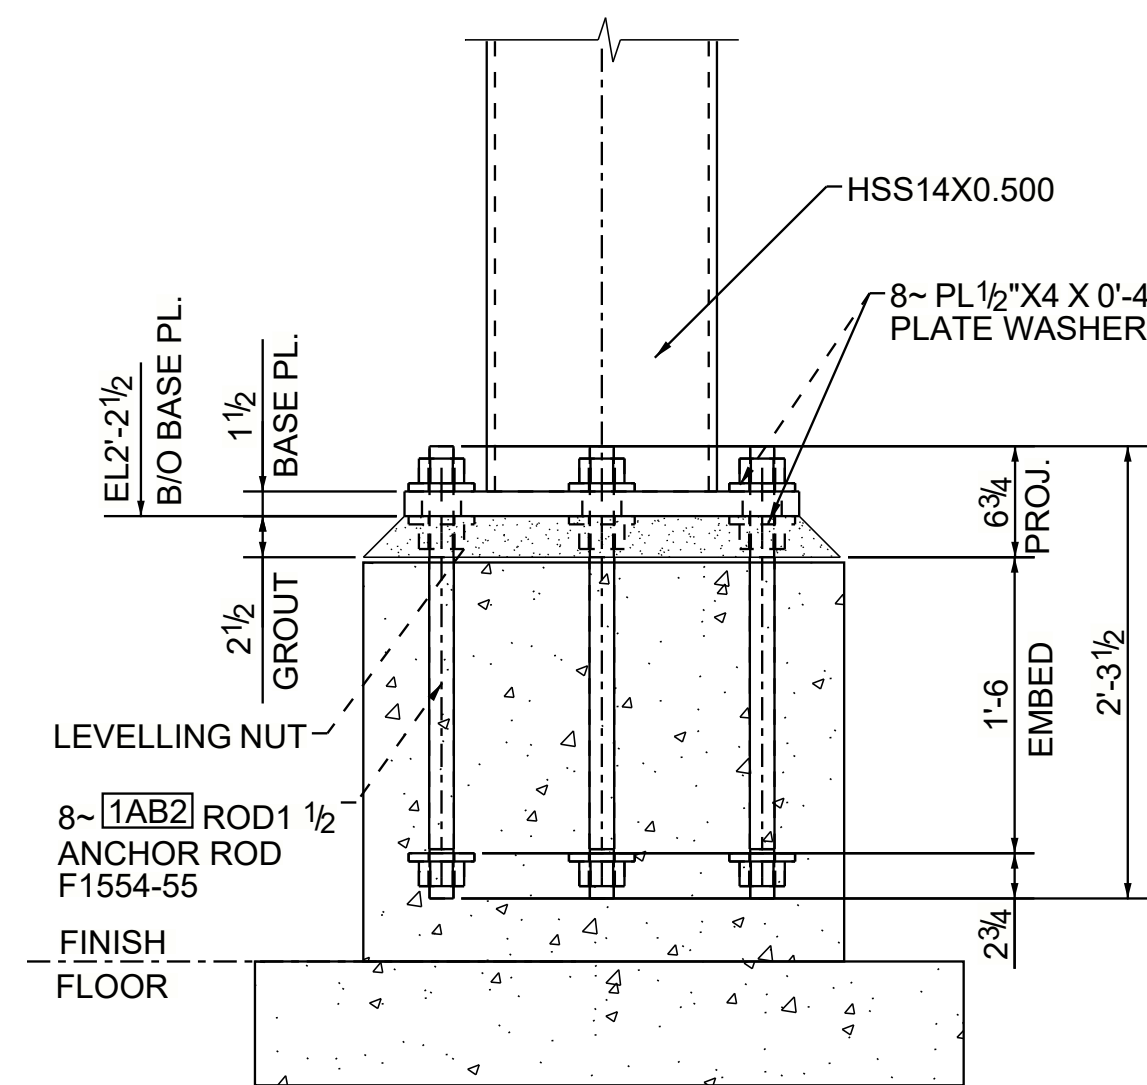

TYPE-1
(14-LOCATIONS)

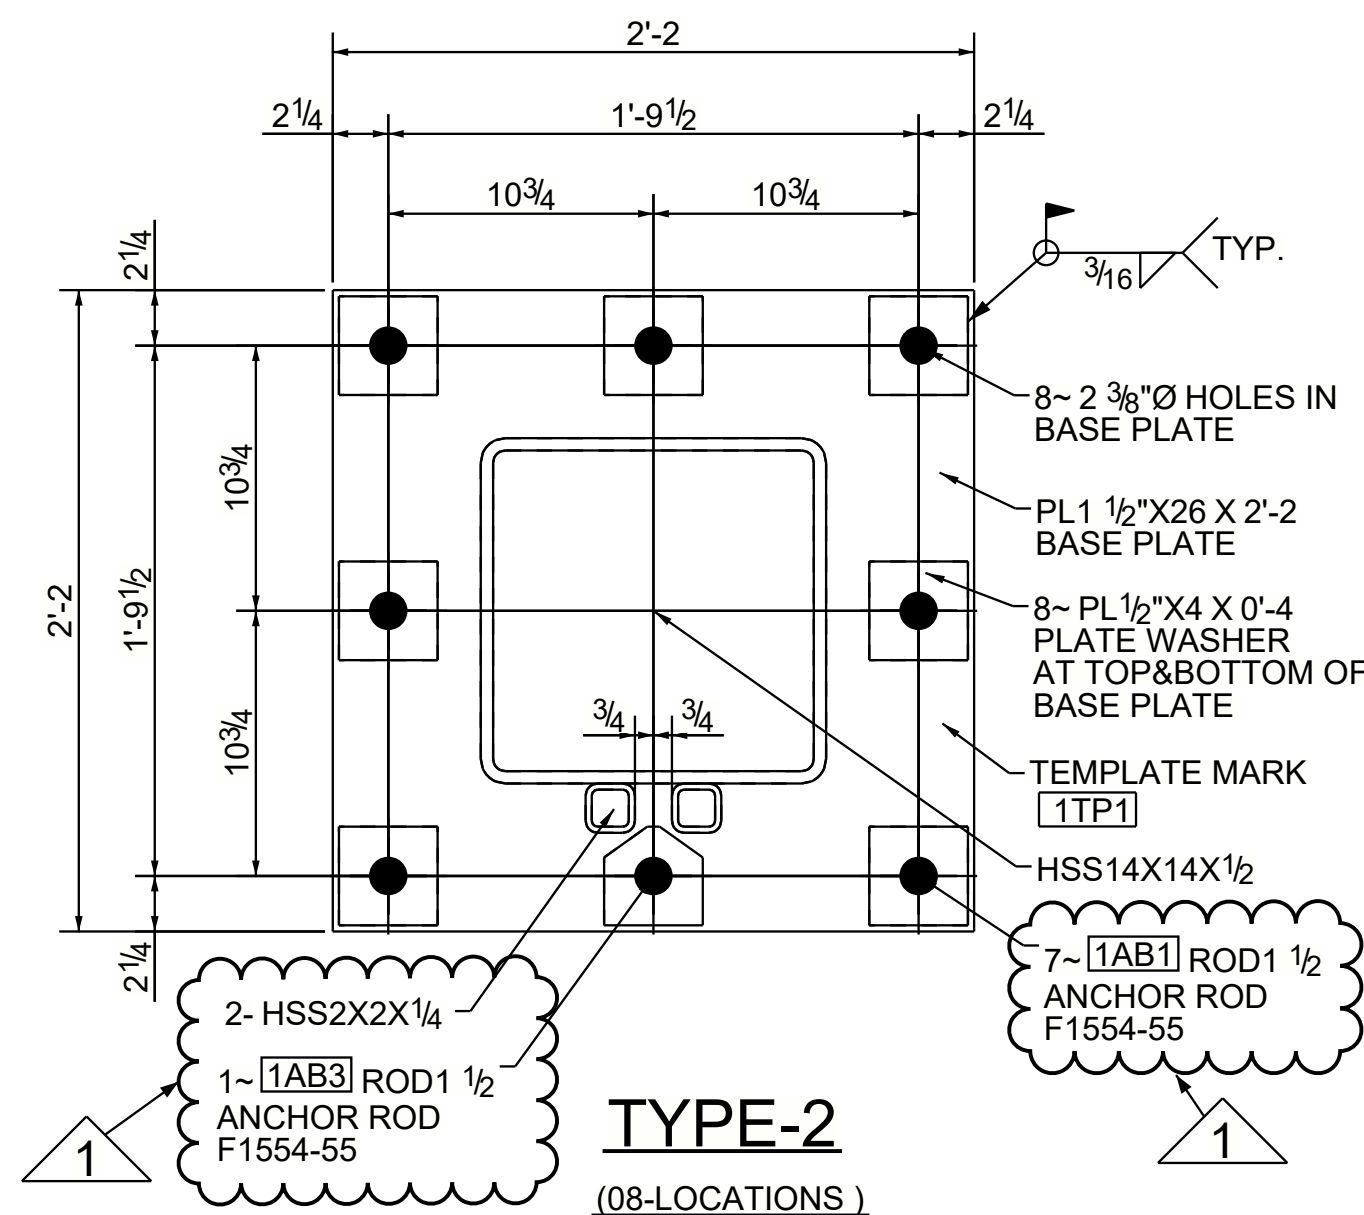

TYPE-2
(08-LOCATIONS)

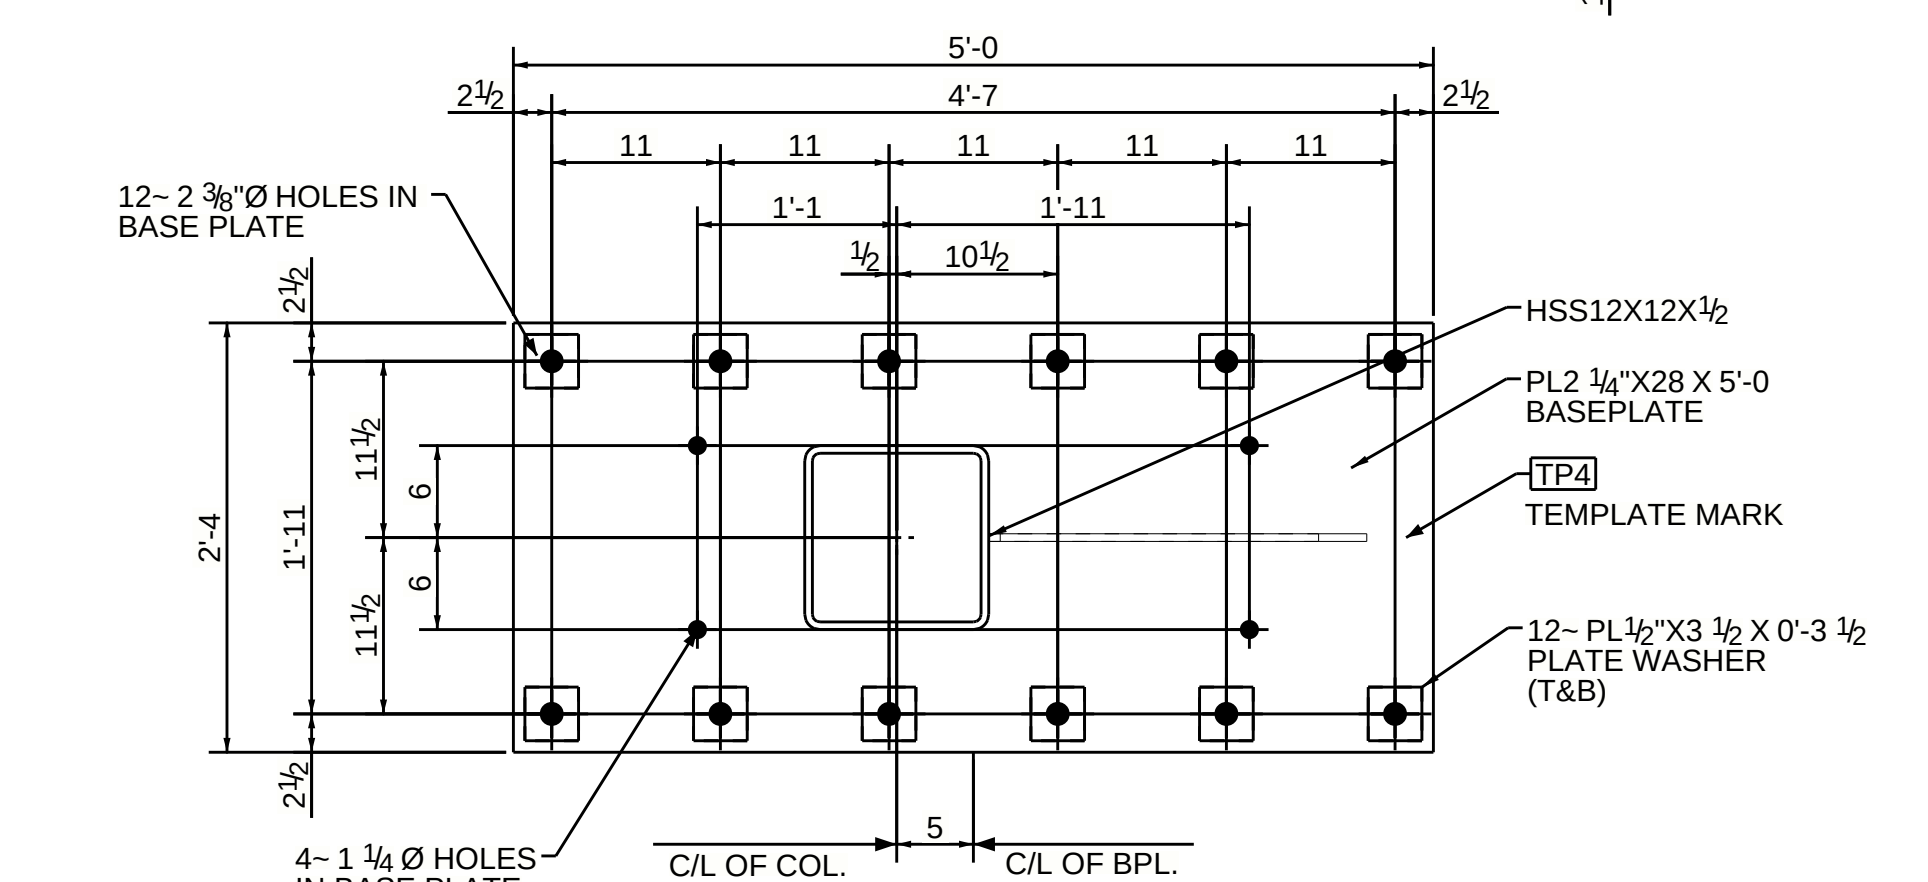
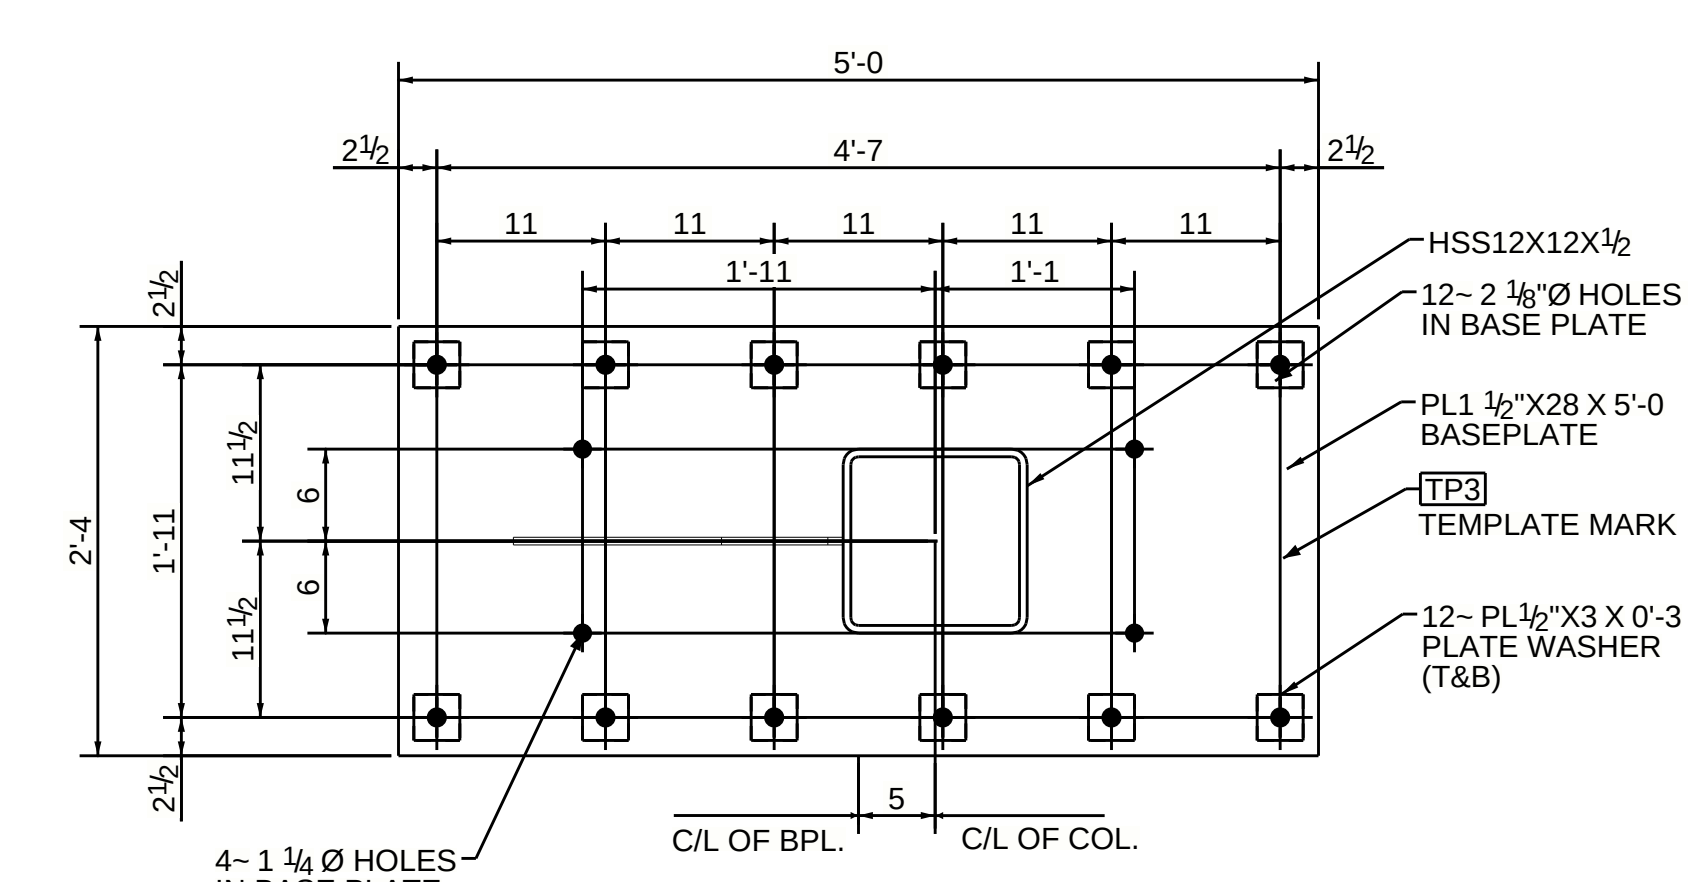
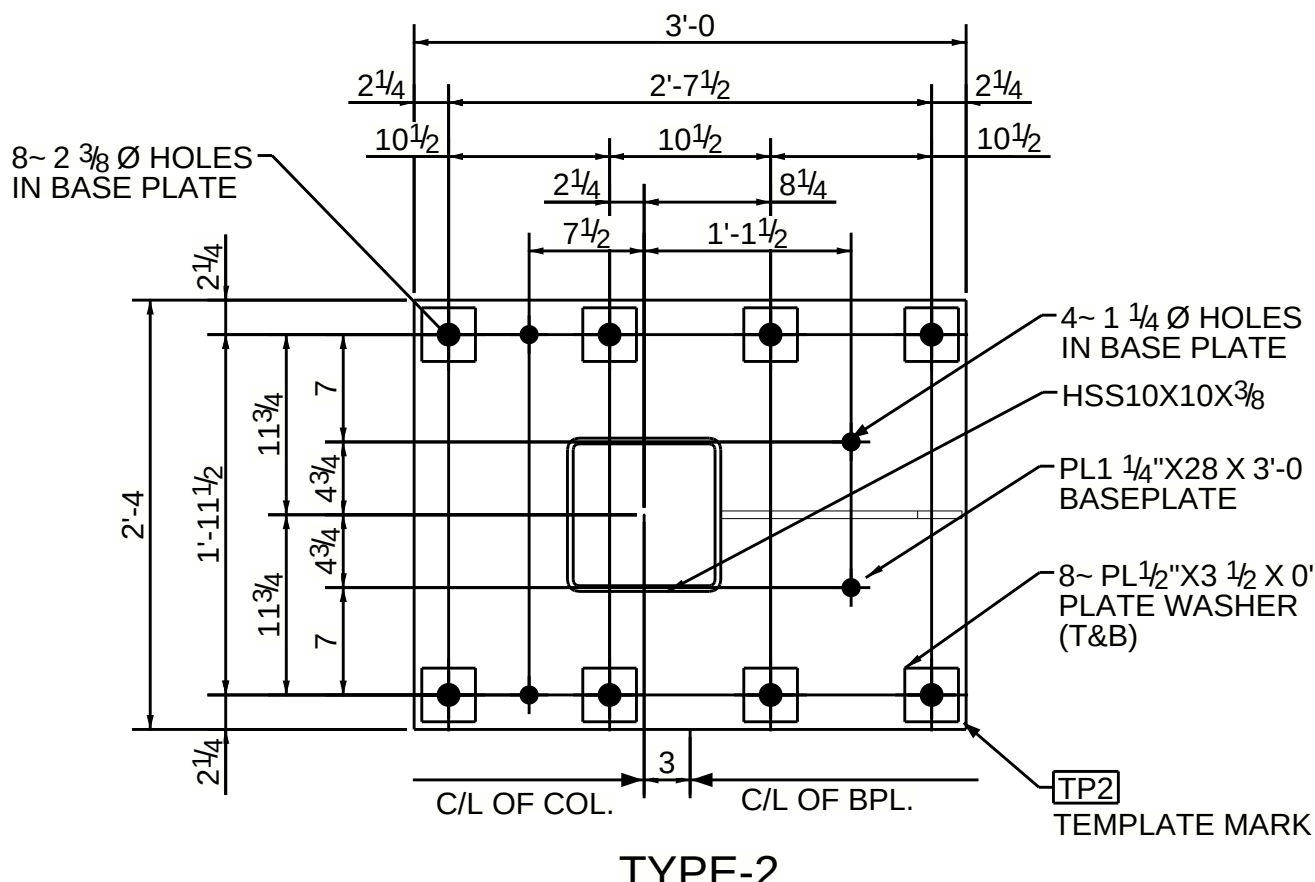
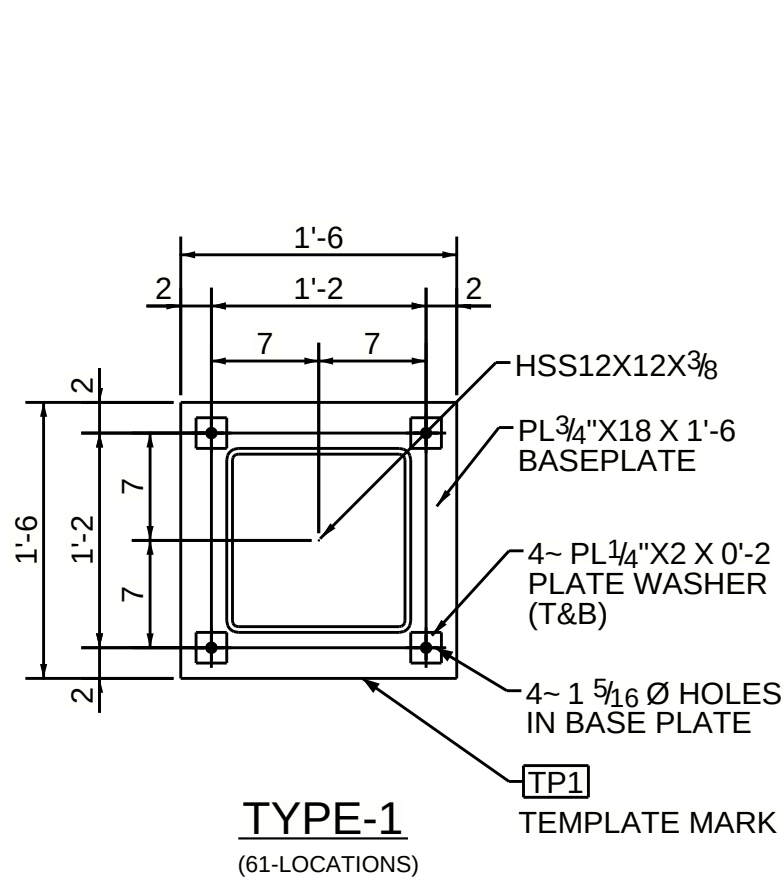
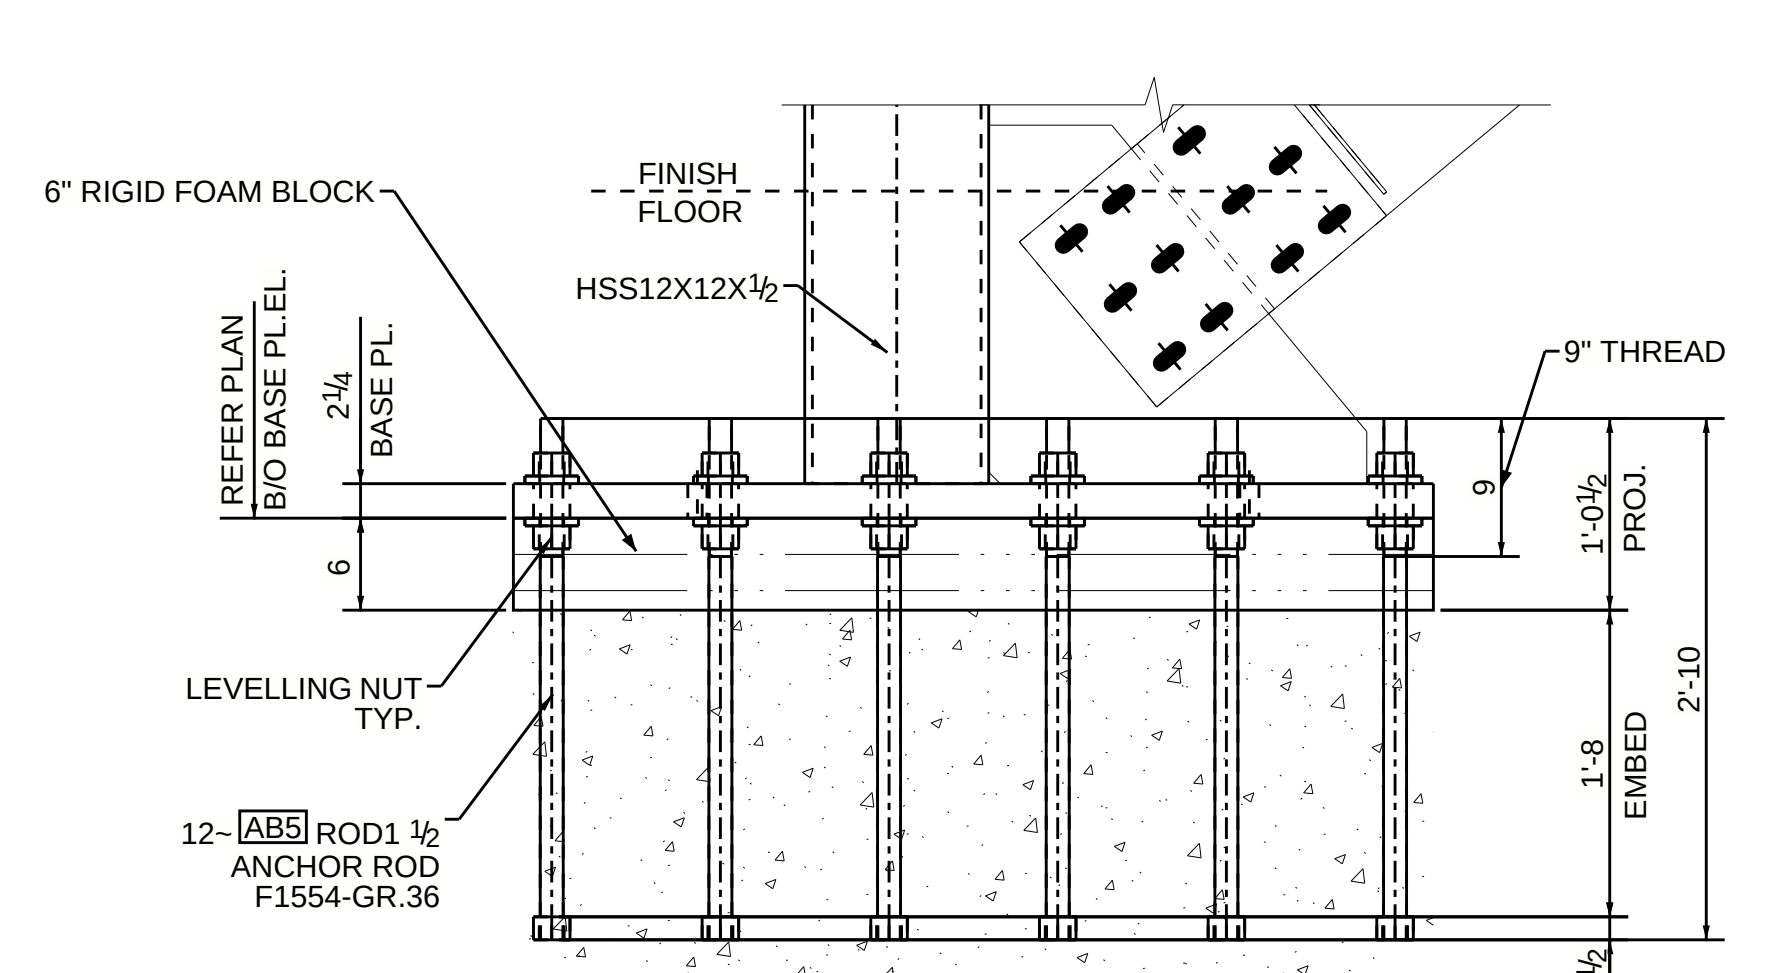
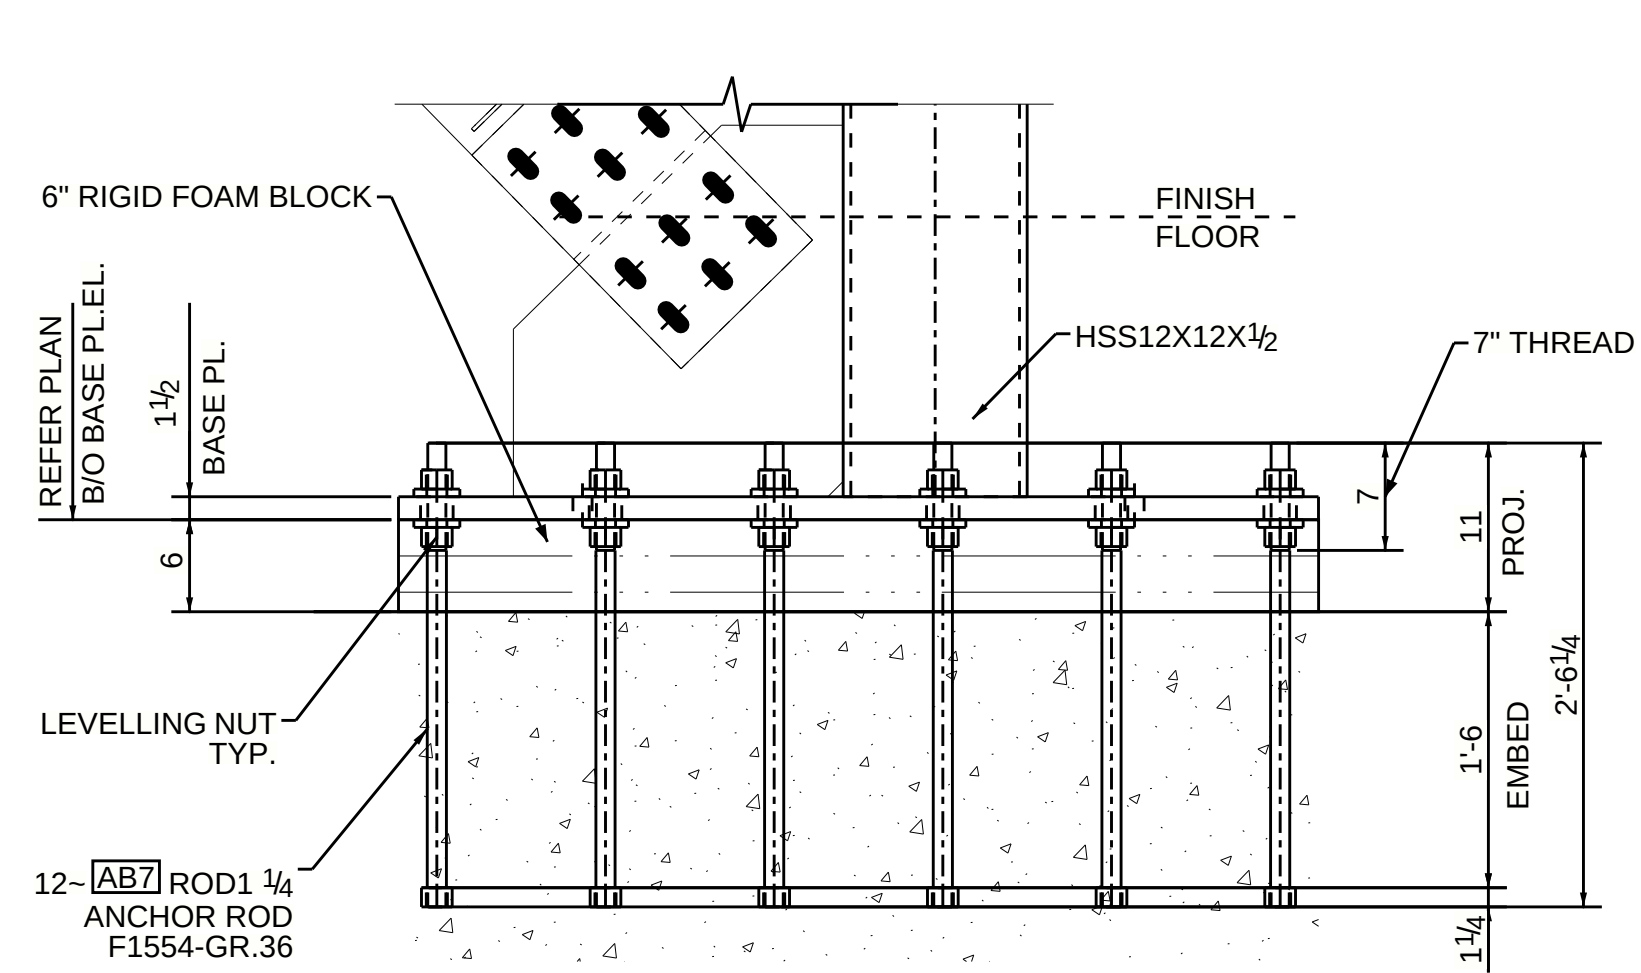
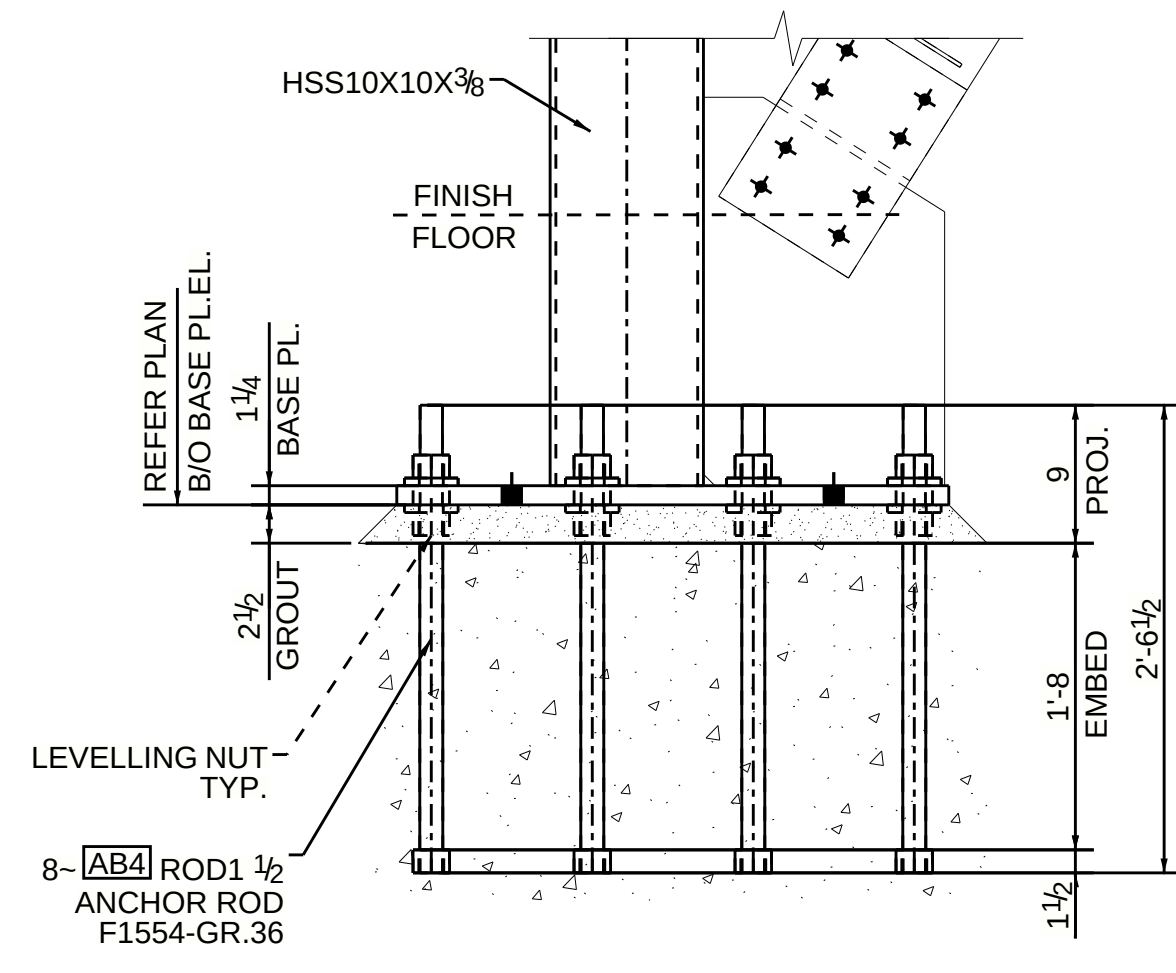
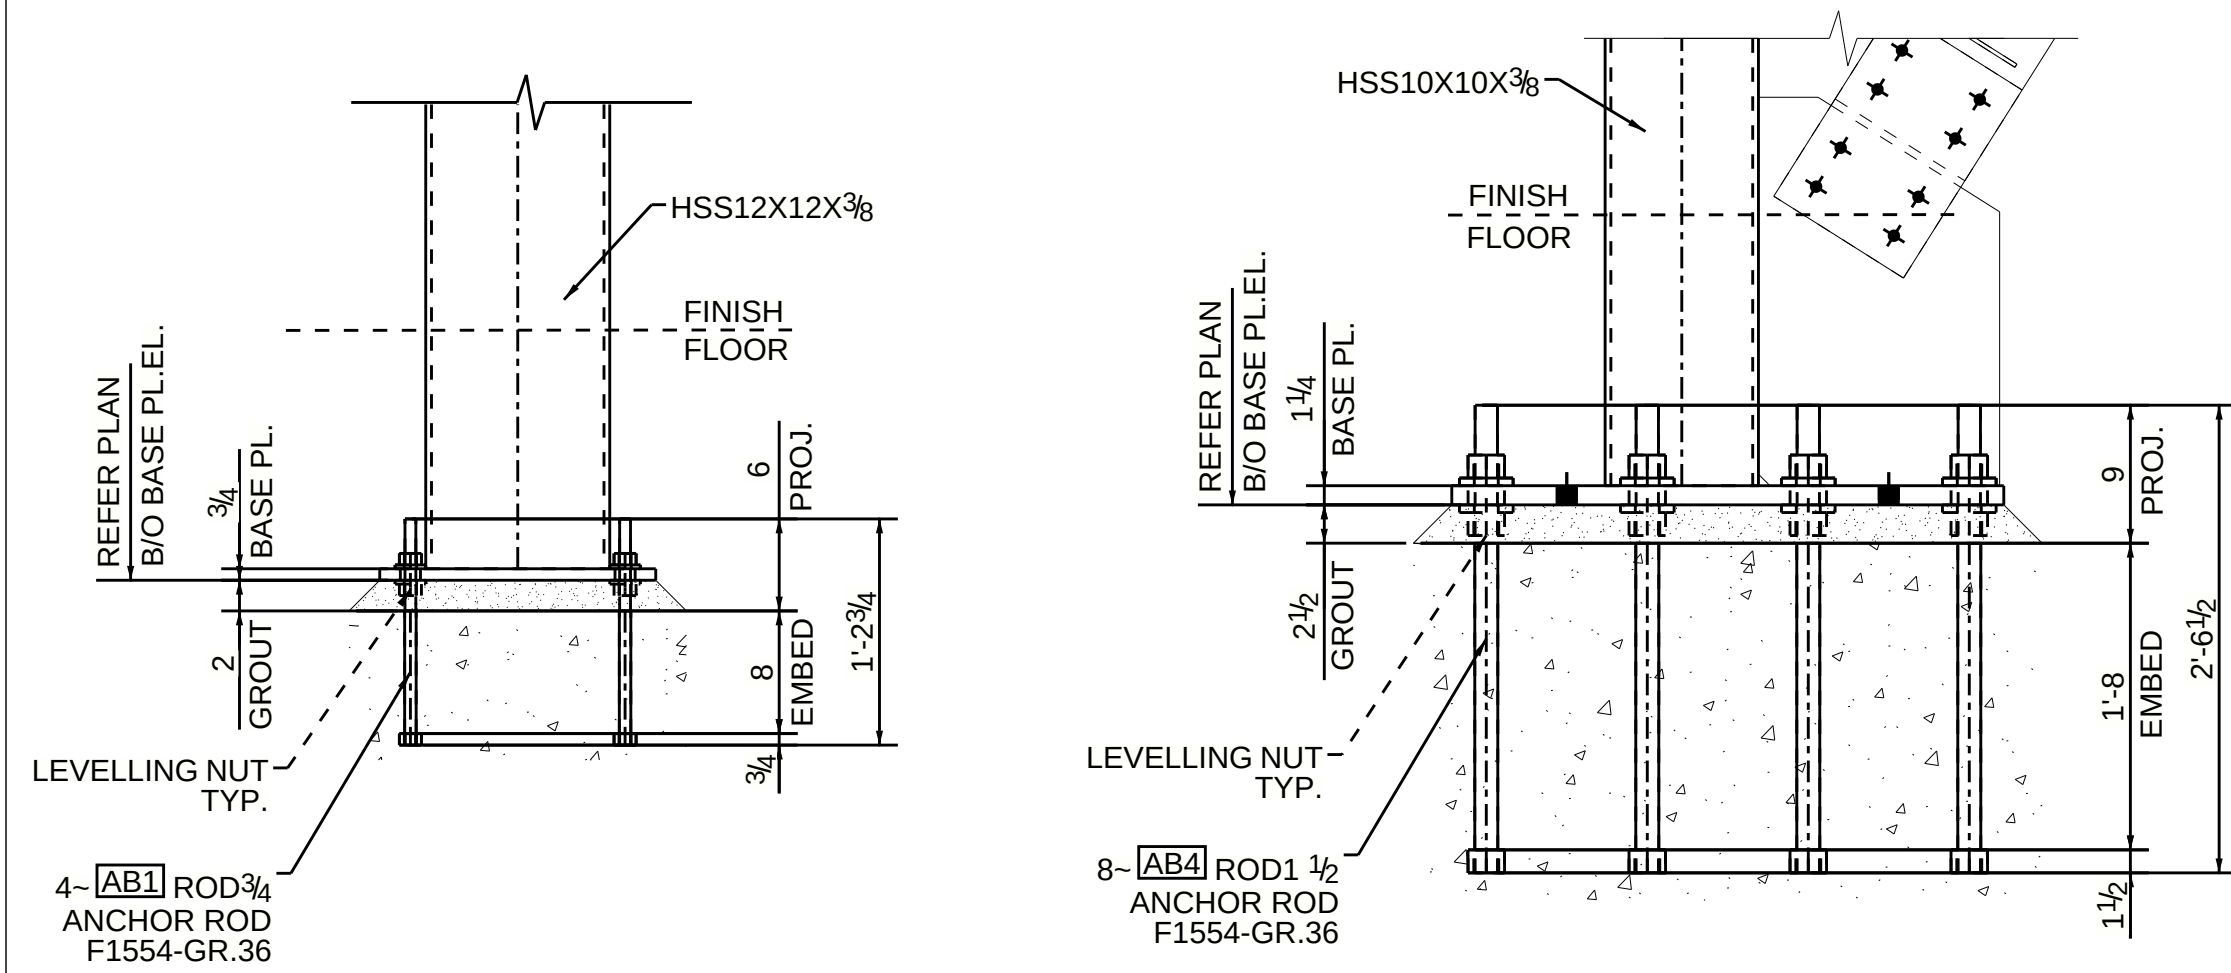


TYPE-1
 (61-LOCATIONS)
 REFER PLAN FOR
 BASE PLATE ORIENTATION

TYPE-2
 (10-LOCATIONS)
 REFER PLAN FOR
 BASE PLATE ORIENTATION

TYPE-3
 (16-LOCATIONS)
 REFER PLAN FOR
 BASE PLATE ORIENTATION

TYPE-4
 (12-LOCATIONS)
 REFER PLAN FOR
 BASE PLATE ORIENTATION

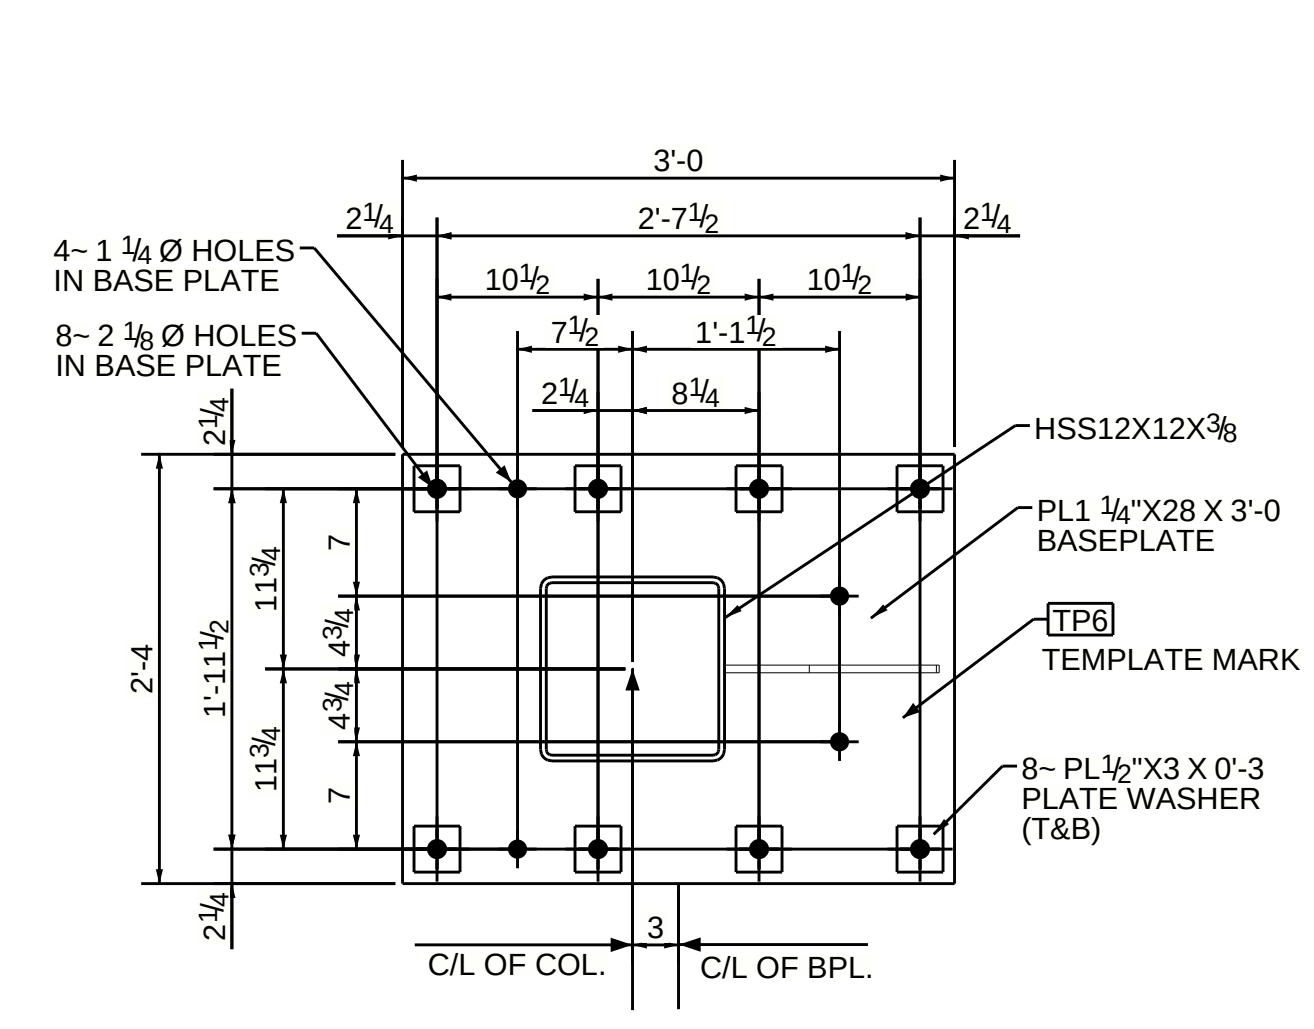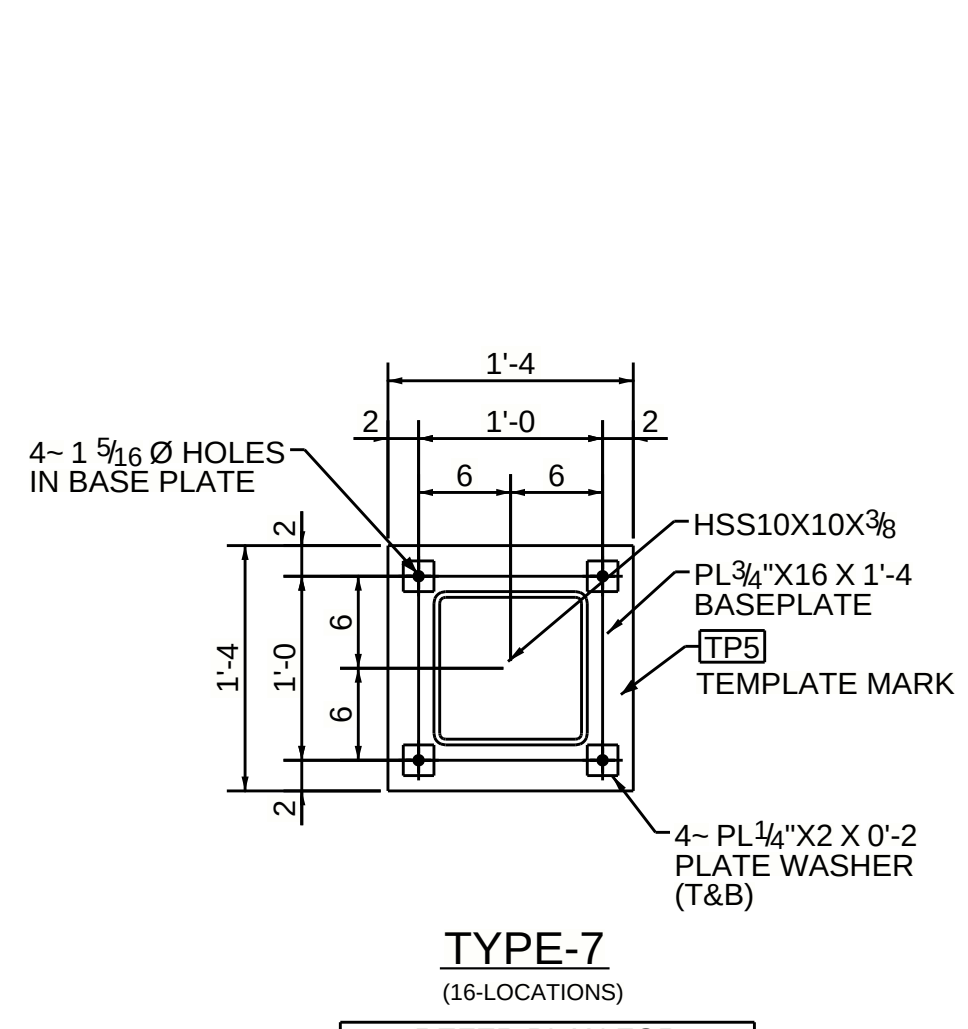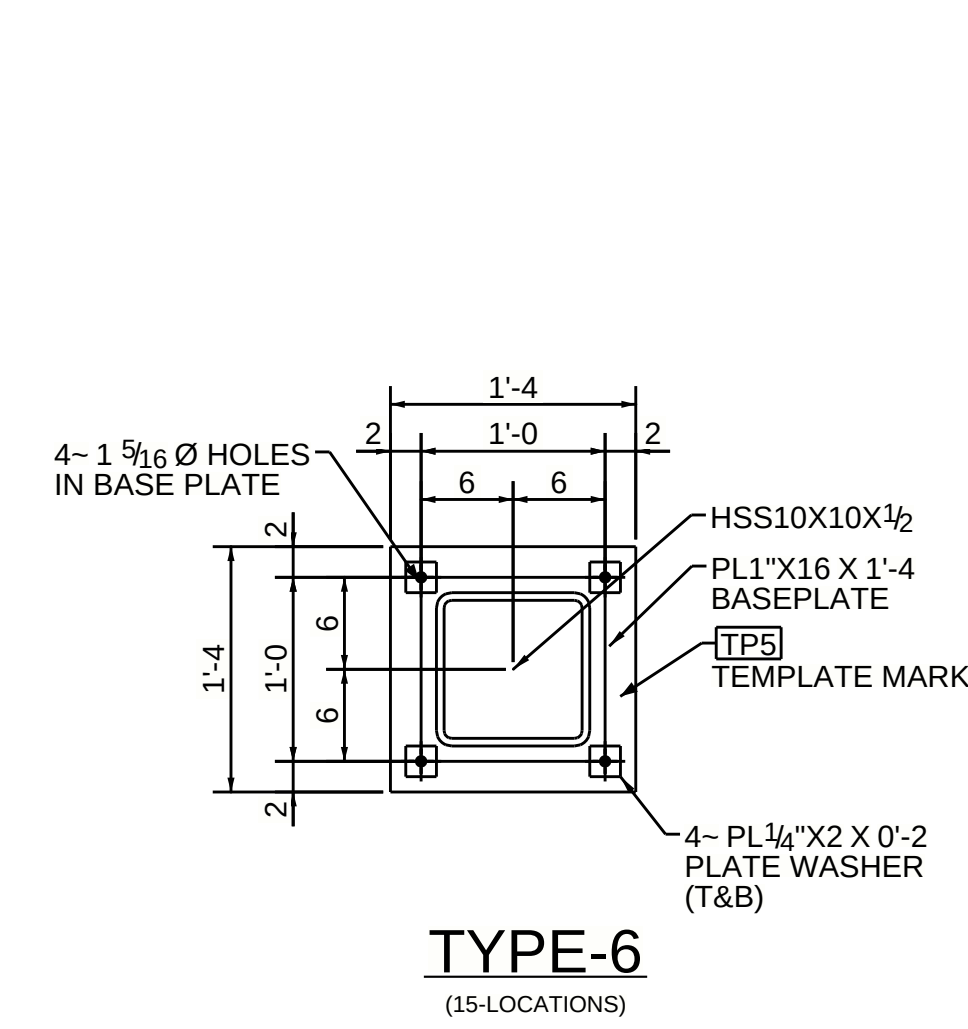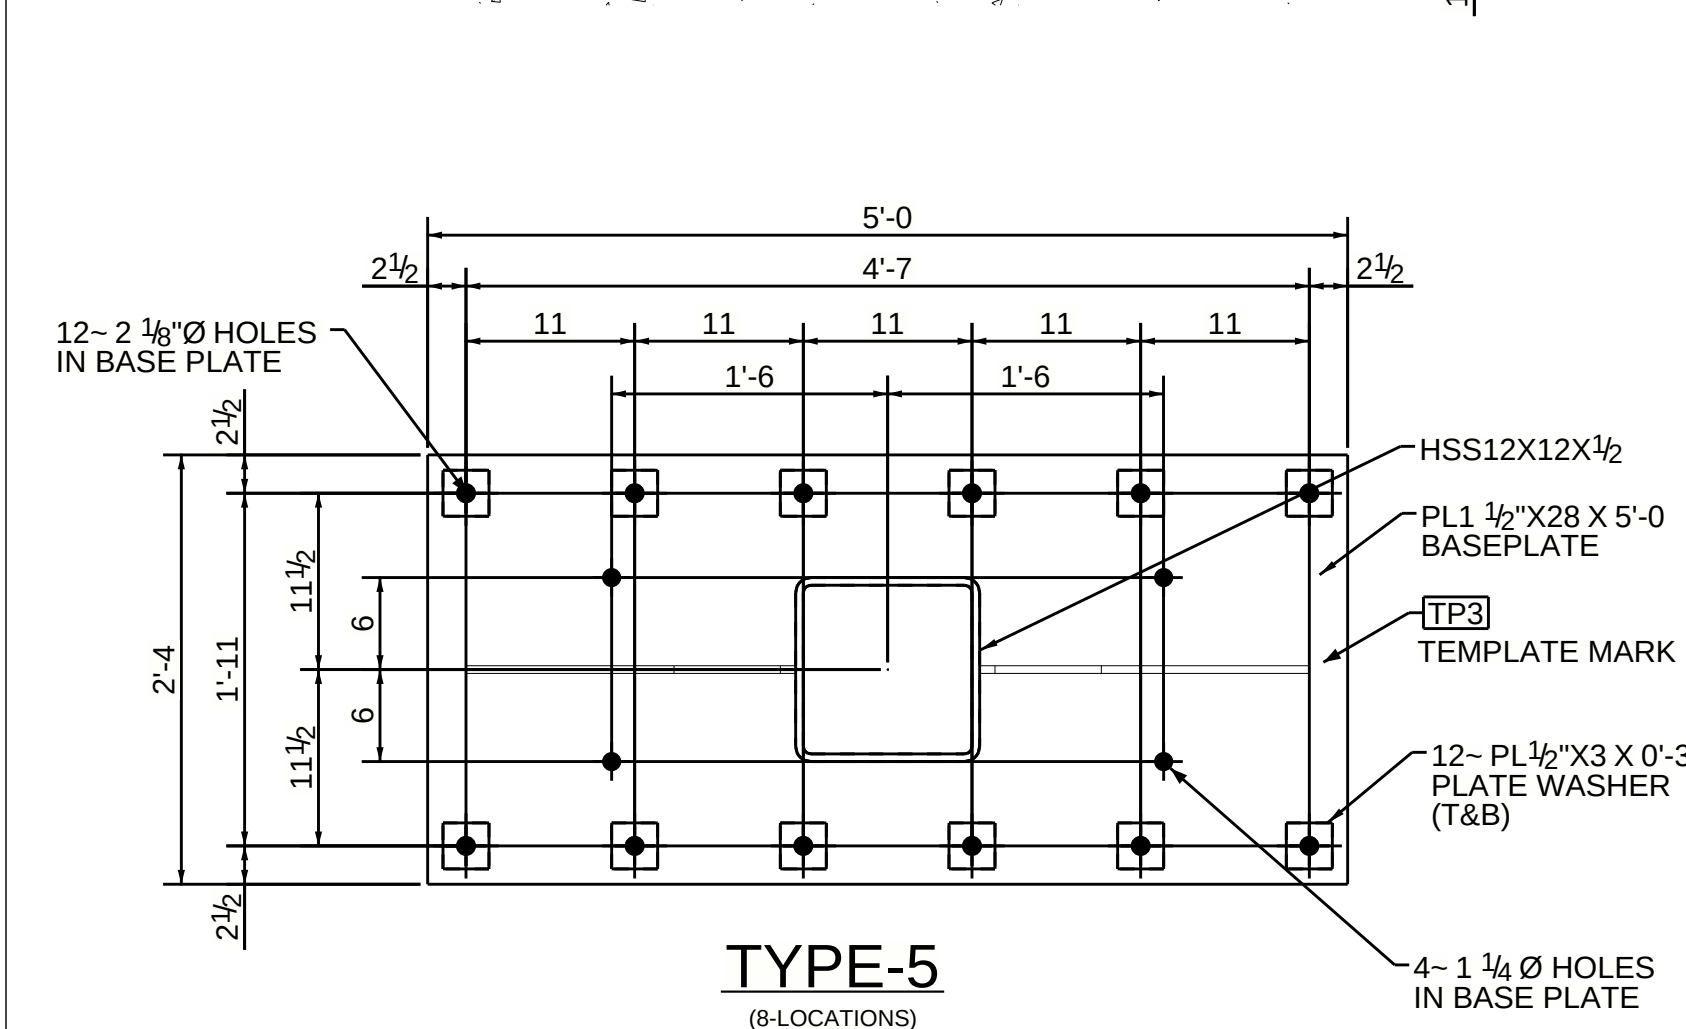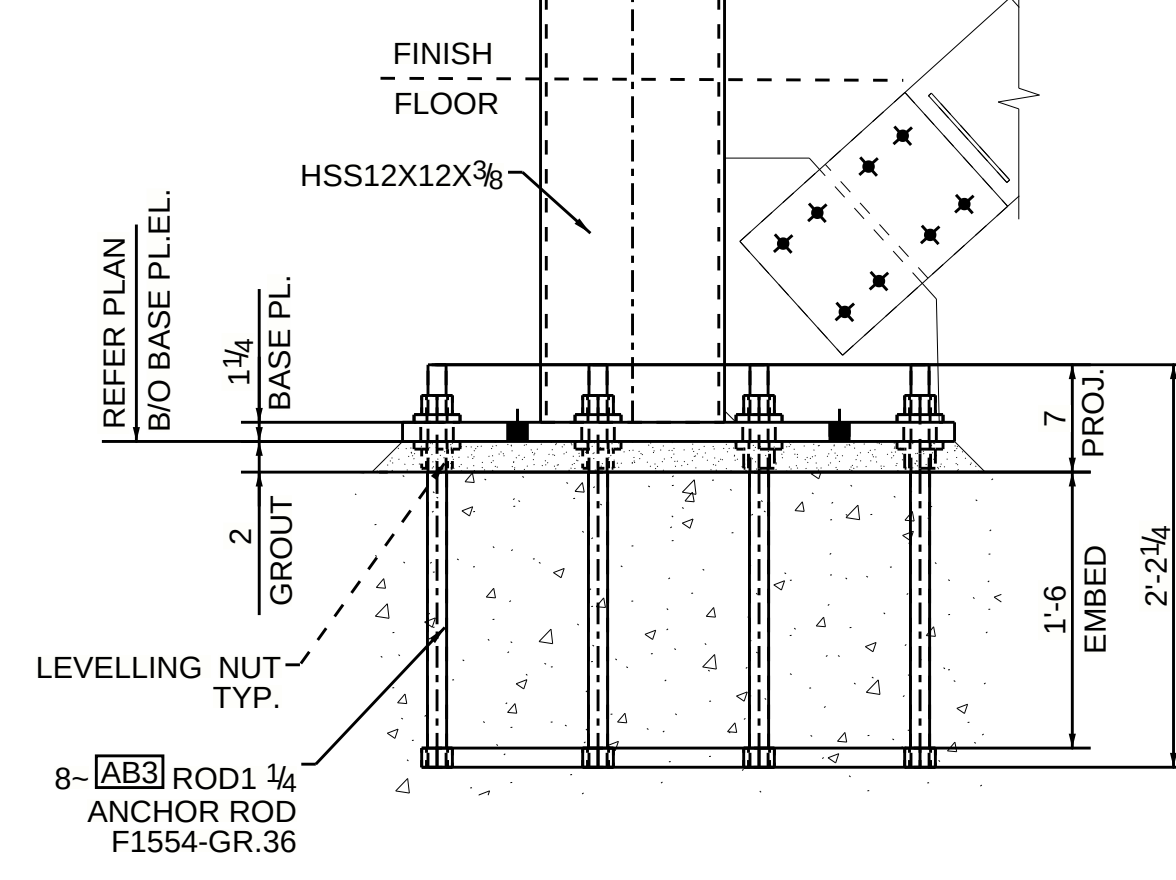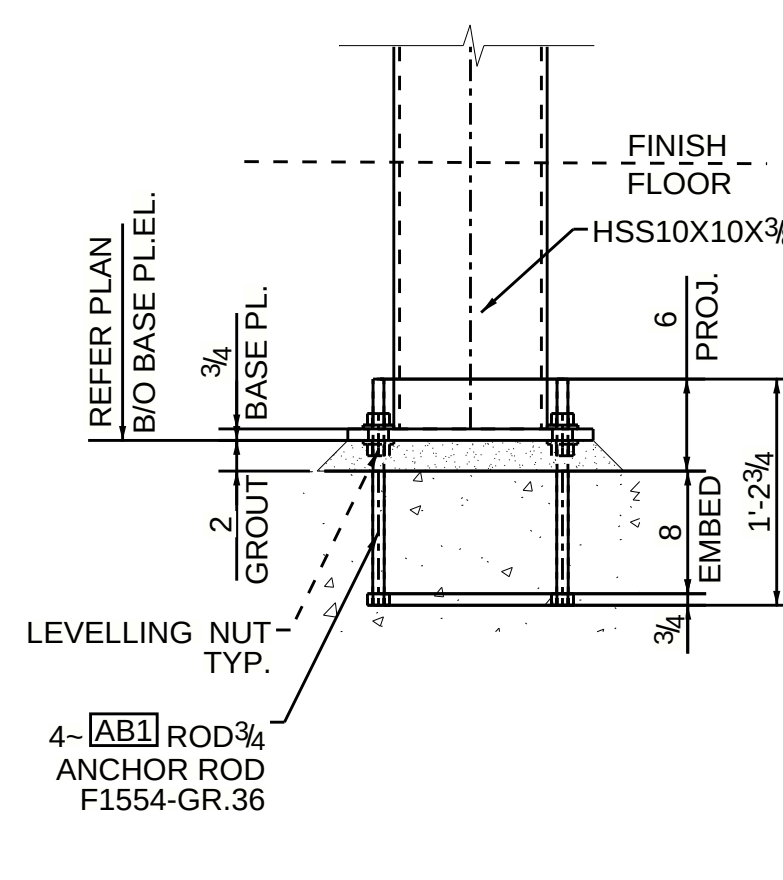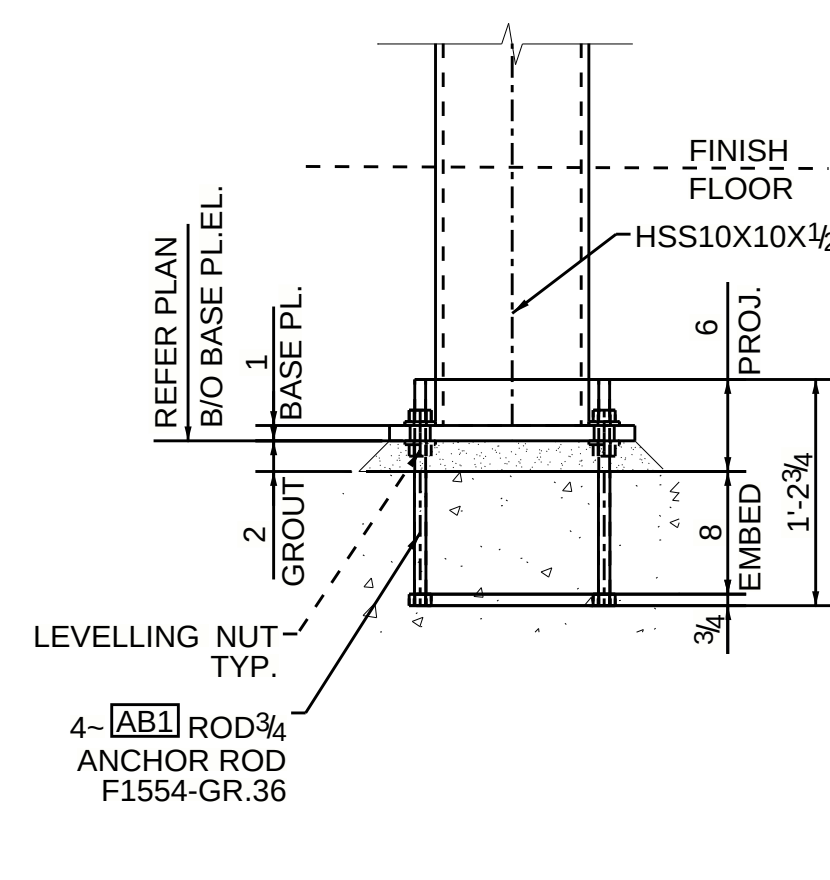
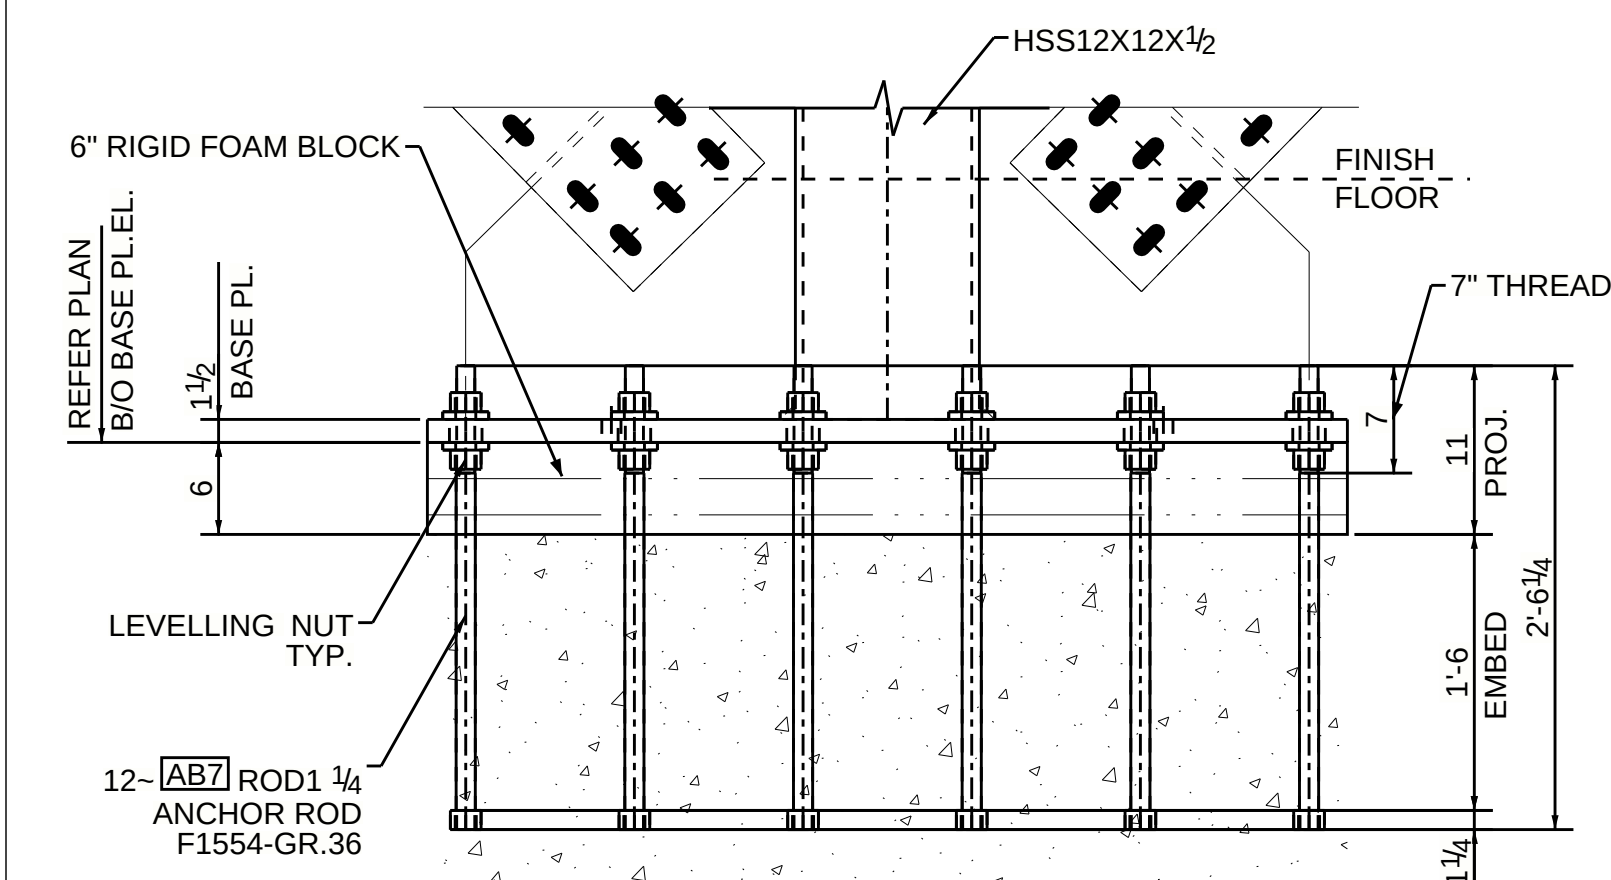


TYPE-5
 (8-LOCATIONS)
 REFER PLAN FOR
 BASE PLATE ORIENTATION



TYPE-6
 (15-LOCATIONS)
 REFER PLAN FOR
 BASE PLATE ORIENTATION

TYPE-7
 (16-LOCATIONS)
 REFER PLAN FOR
 BASE PLATE ORIENTATION



TYPE-8
 (12-LOCATIONS)
 REFER PLAN FOR
 BASE PLATE ORIENTATION

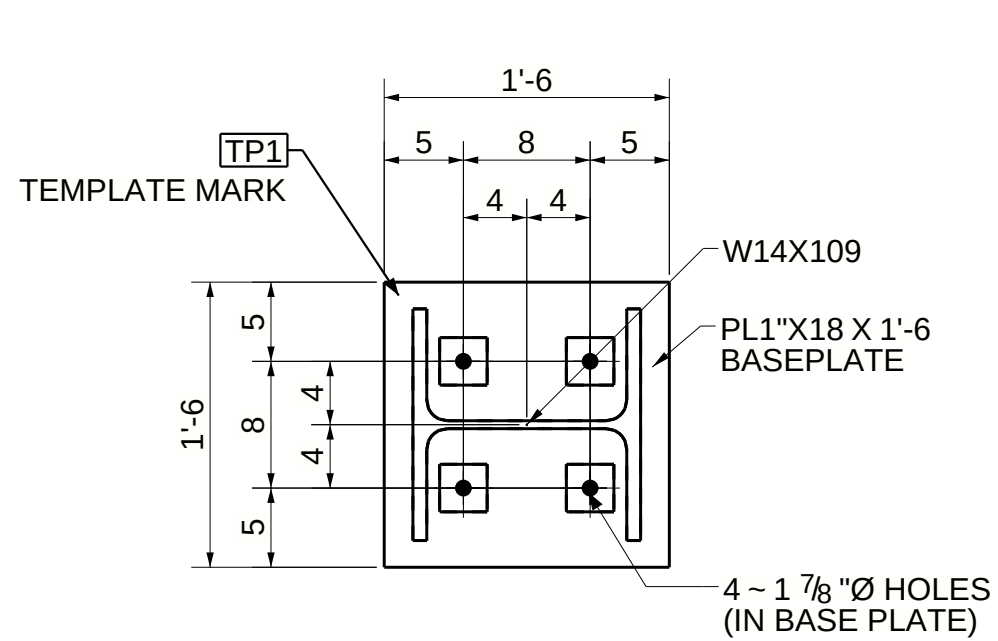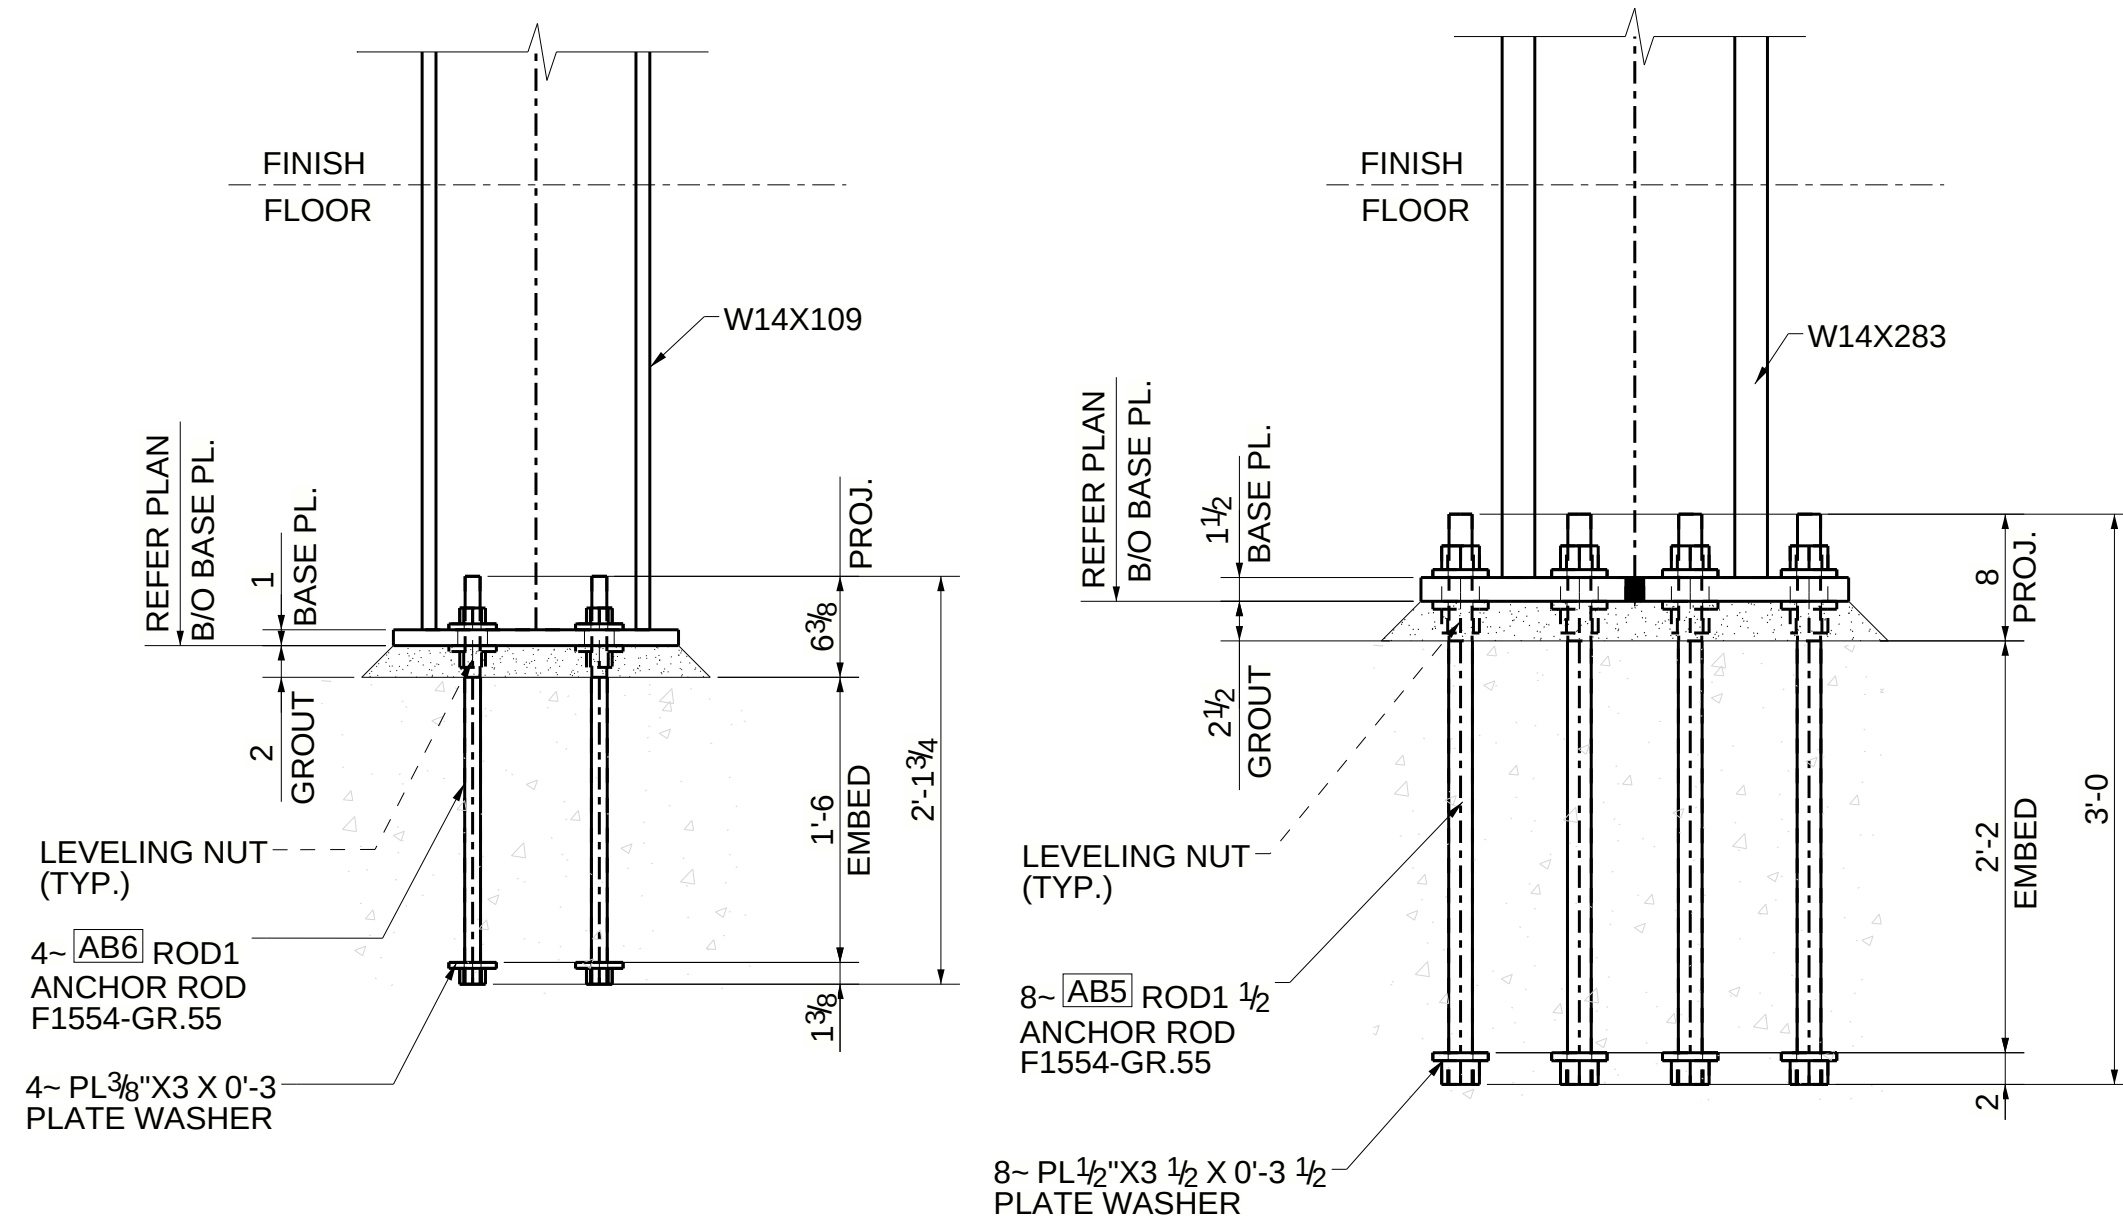

TYPE-1
(18 LOCATIONS)

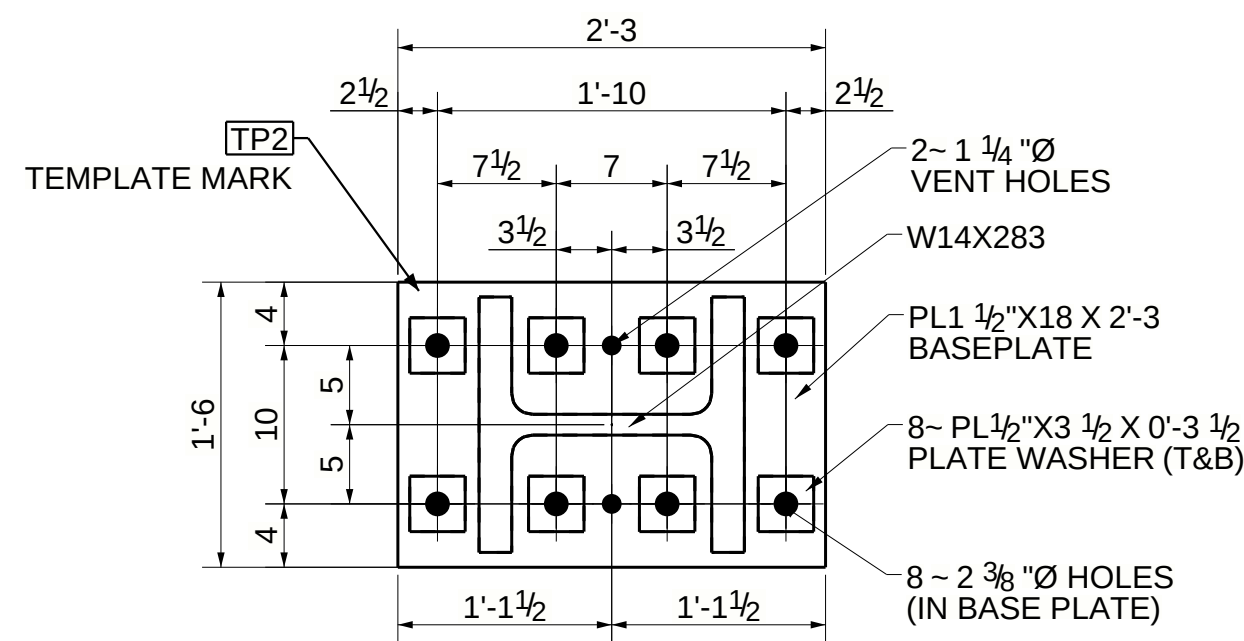
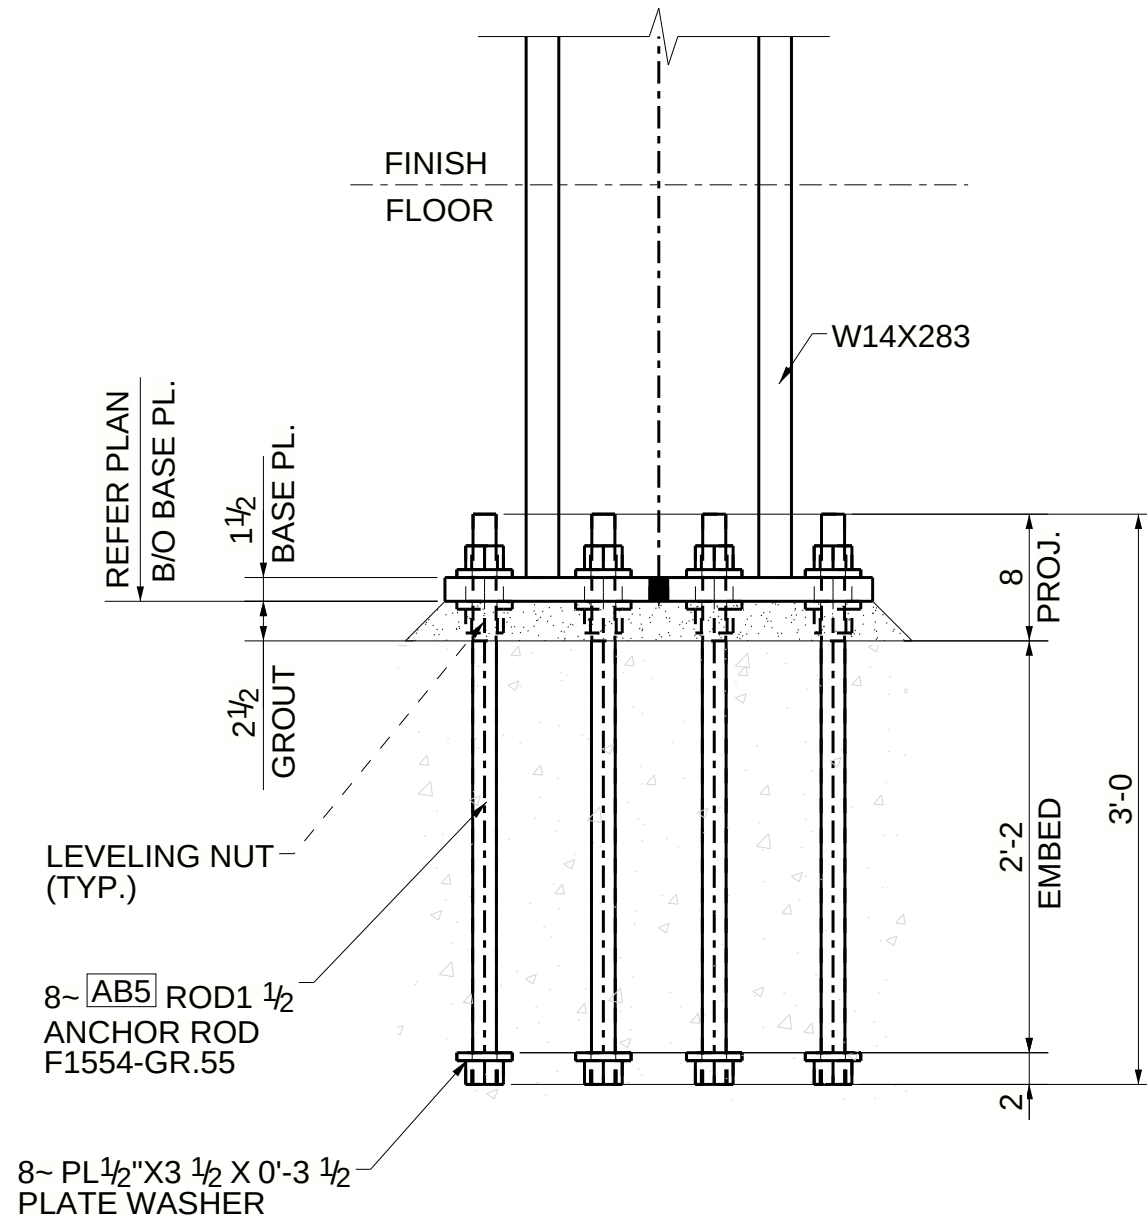


TYPE-2
(04 LOCATIONS)

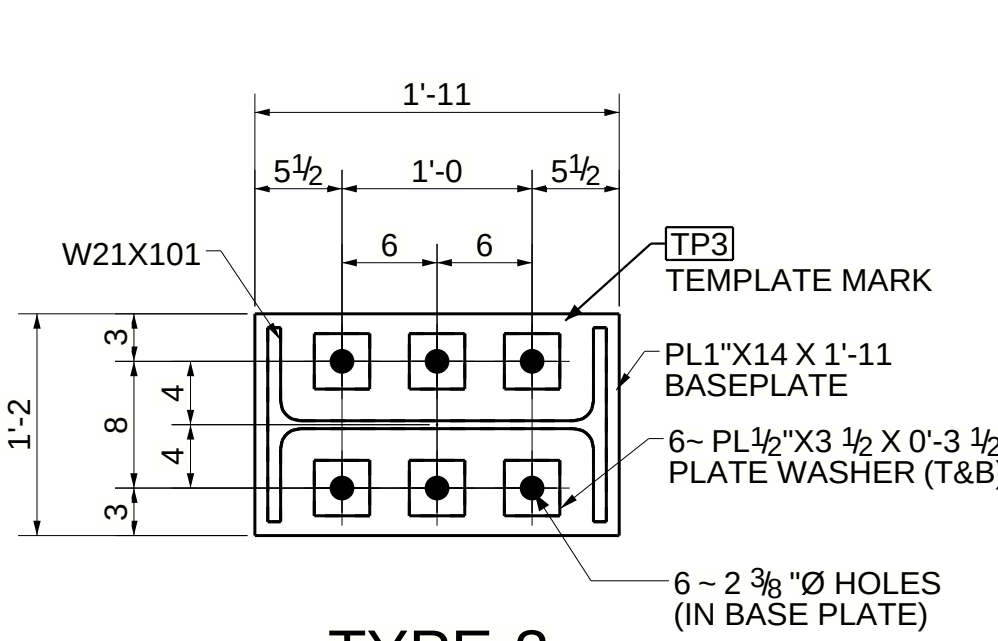
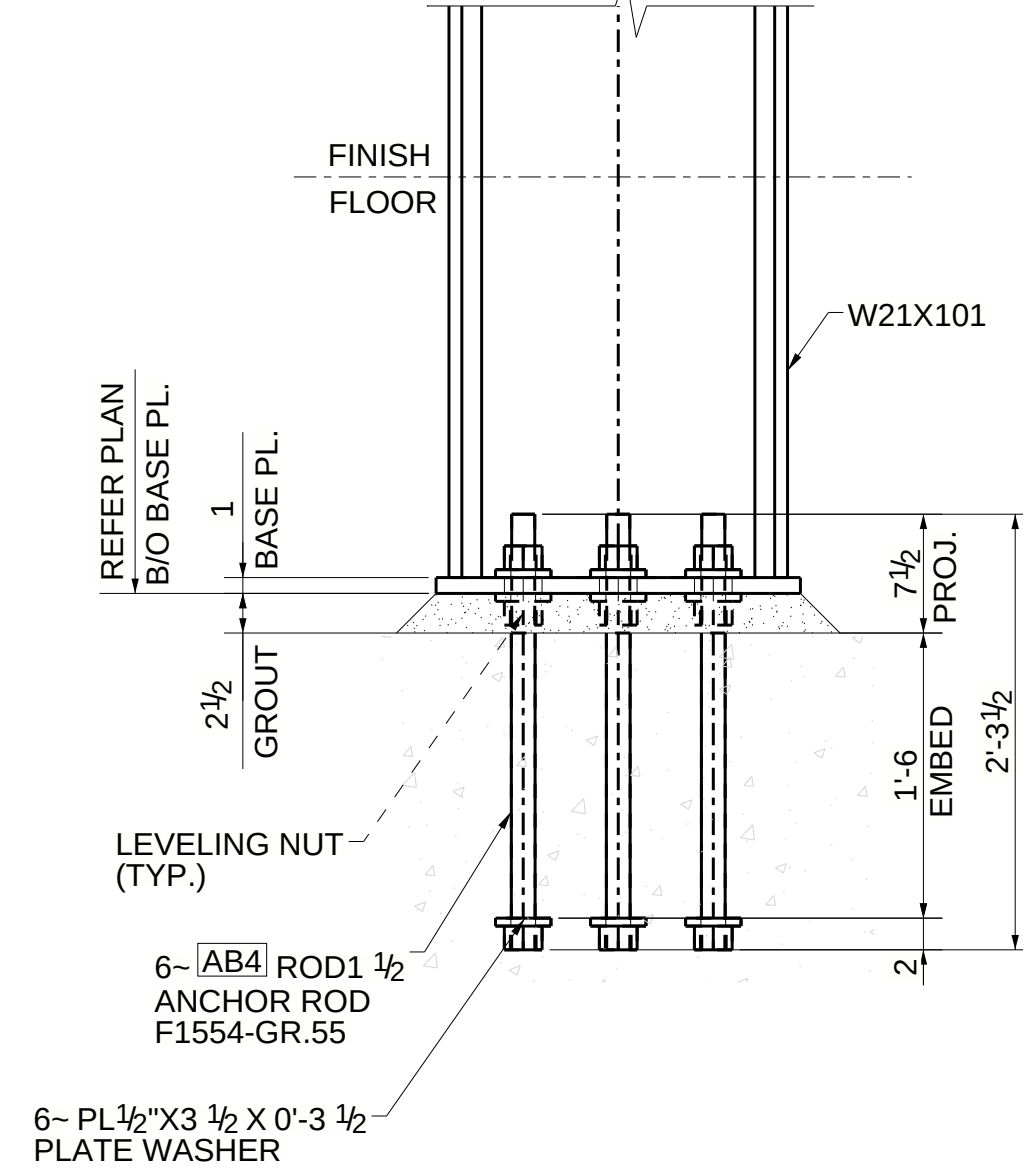


TYPE-3
(14 LOCATIONS)



REFER PLAN FOR BASE
PLATE ORIENTATION
TYPICAL FOR ALL DETAIL

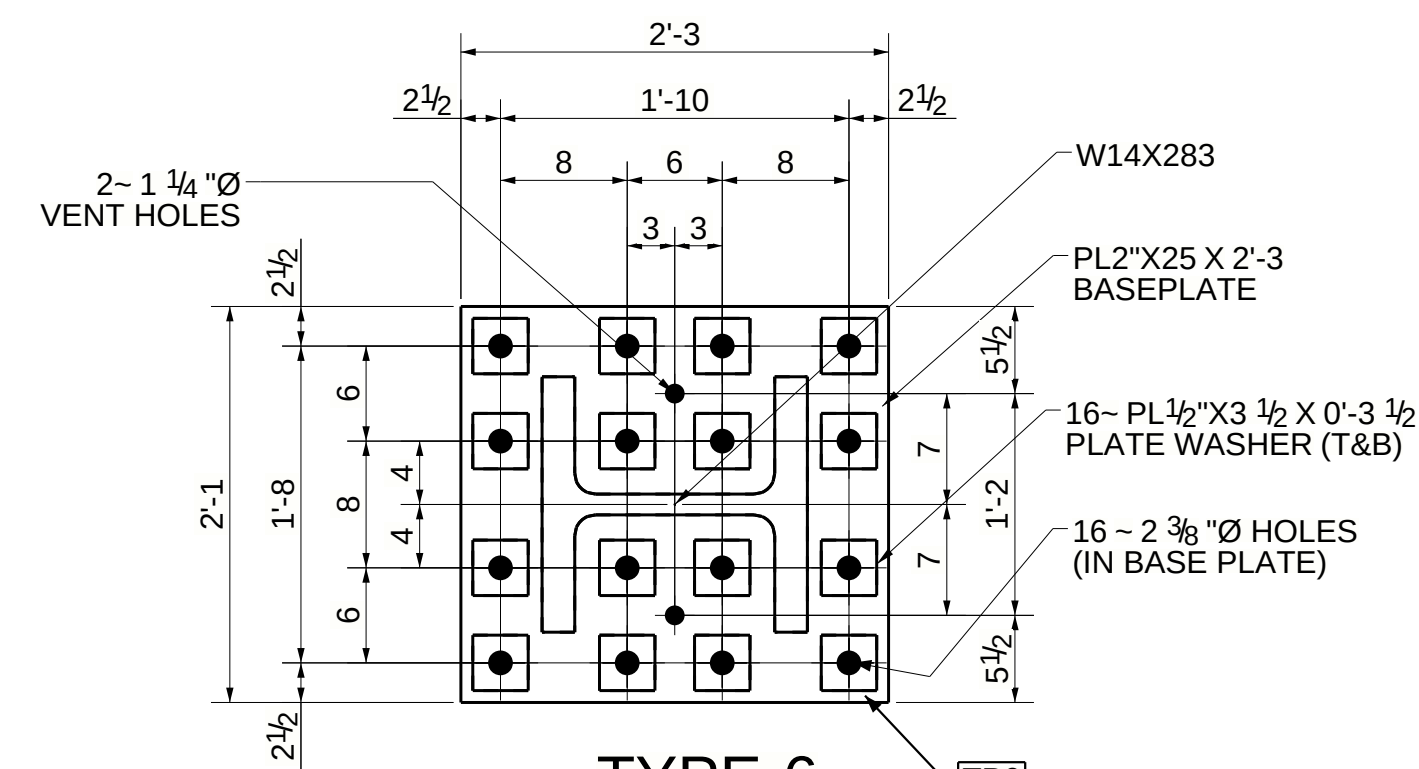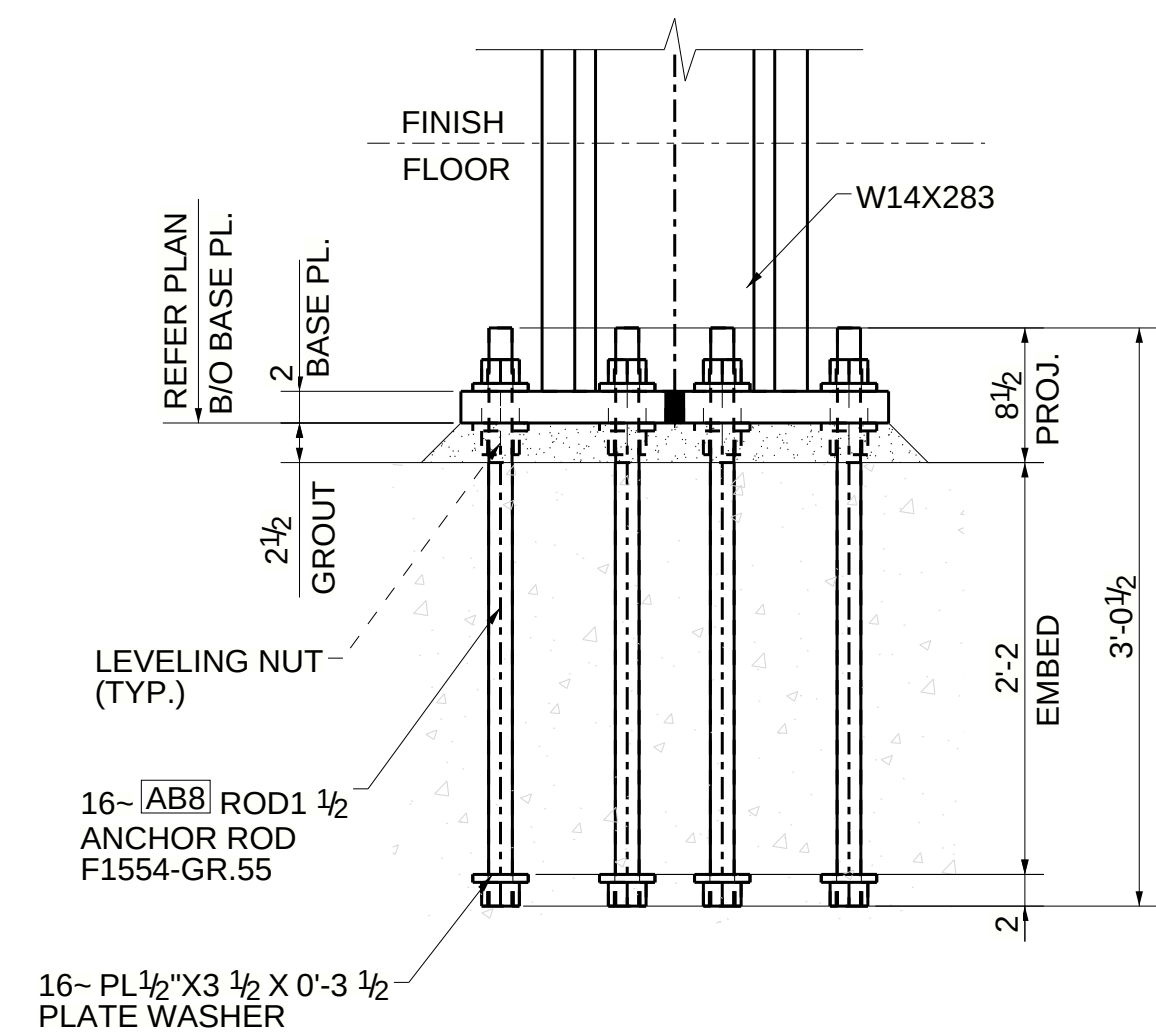



TYPE-6
(04 LOCATIONS)

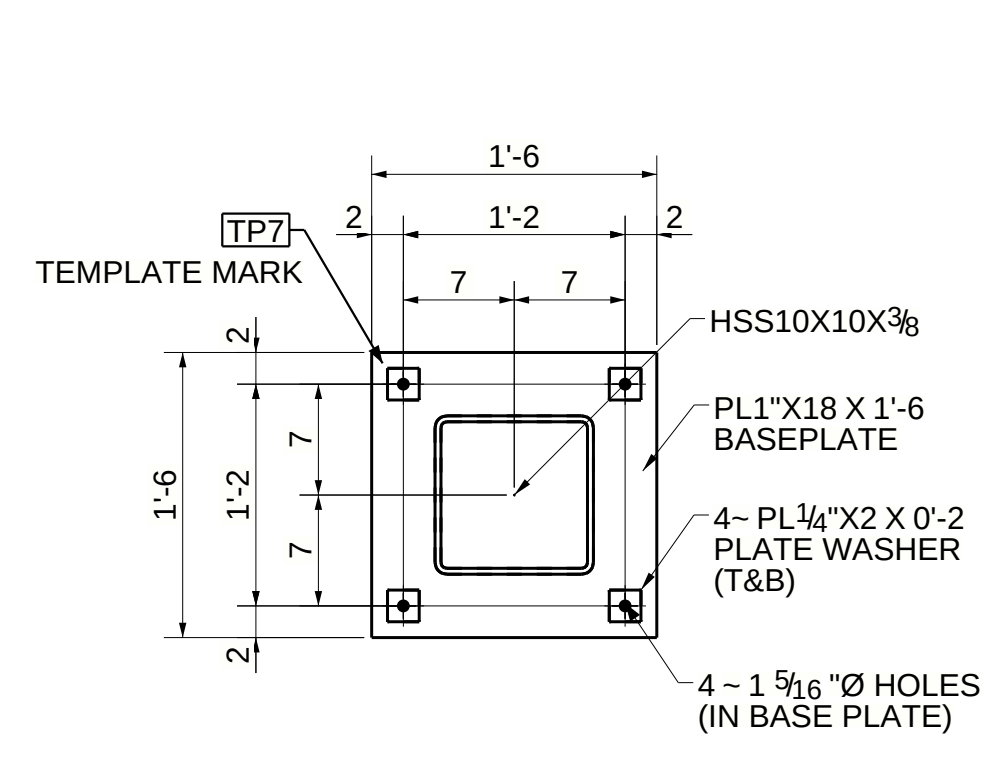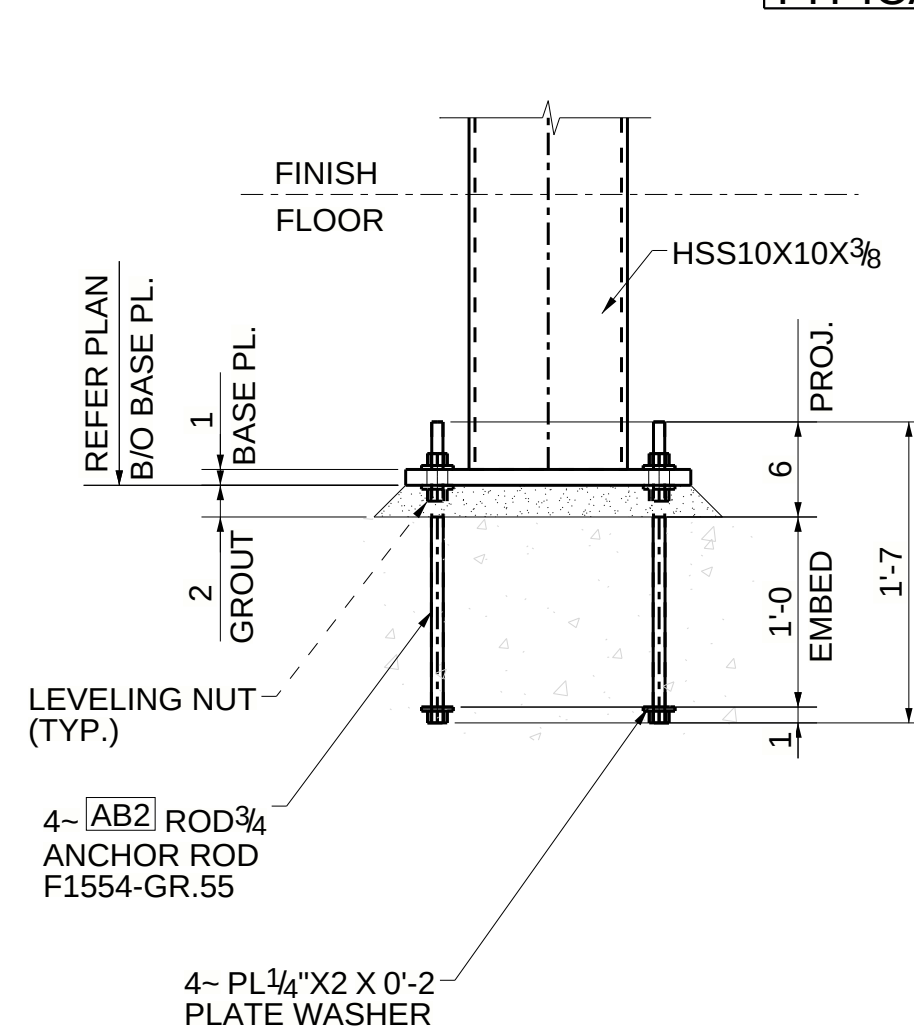


TYPE-7
(17 LOCATIONS)

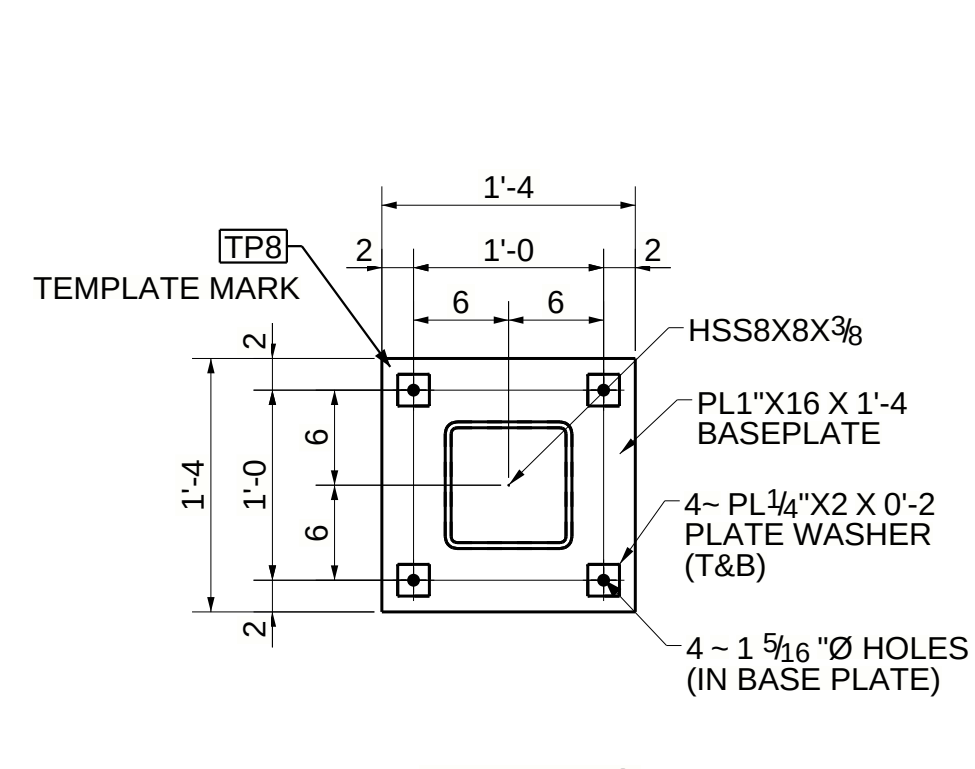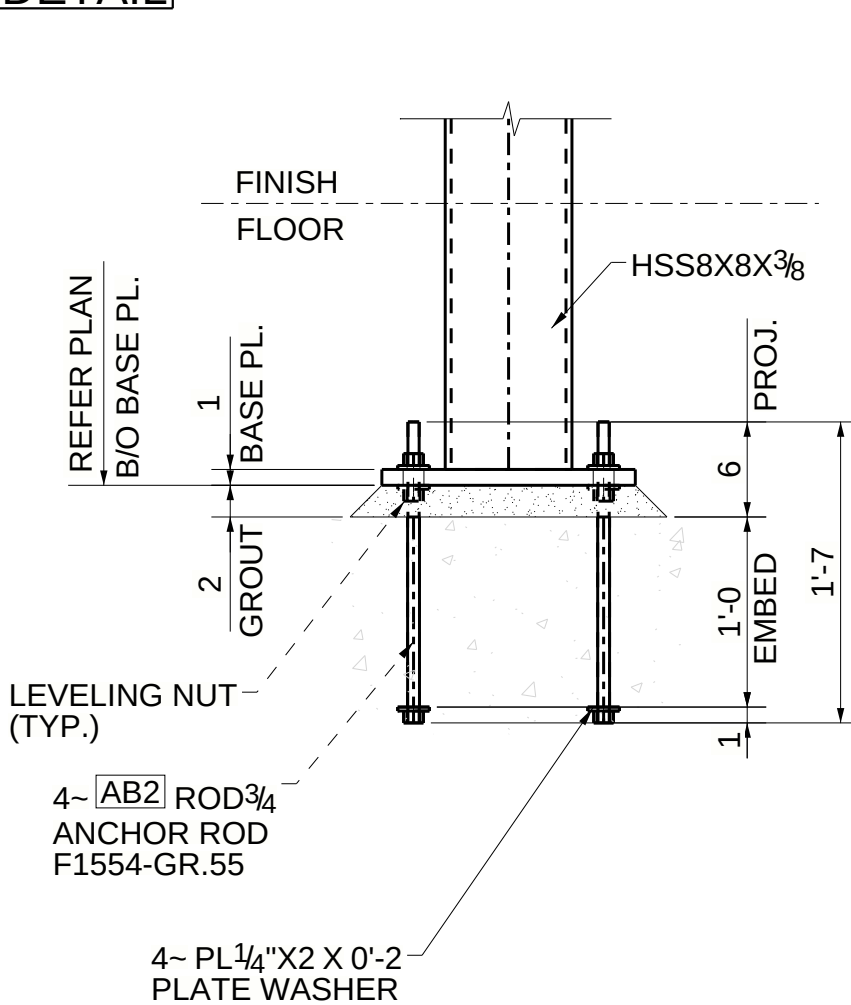


TYPE-8
(02 LOCATIONS)

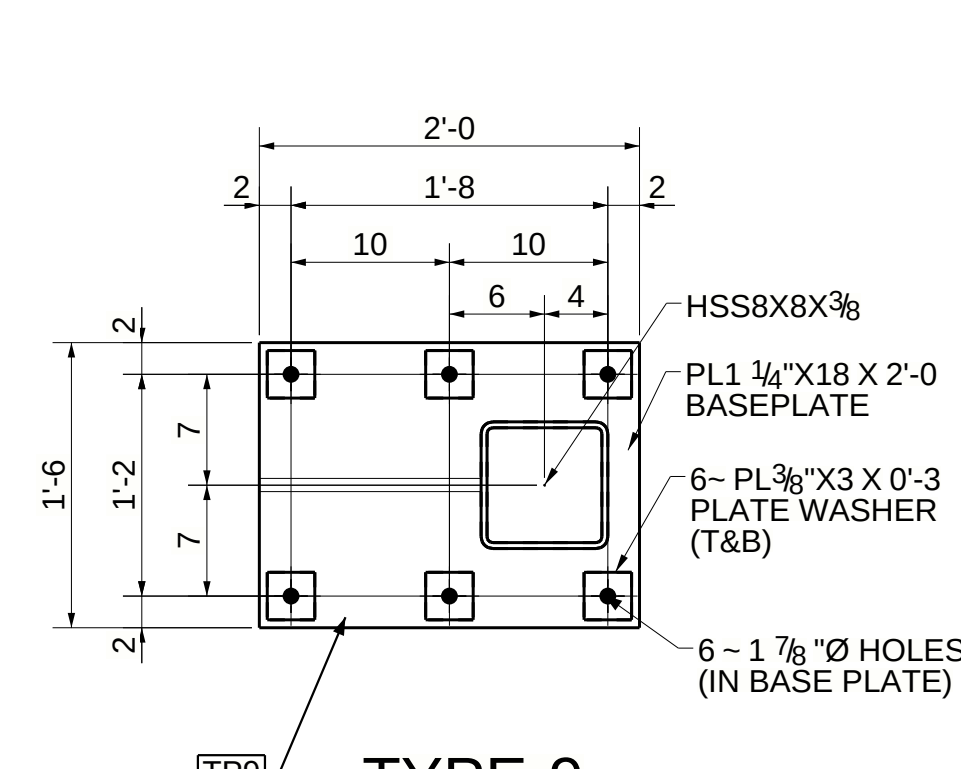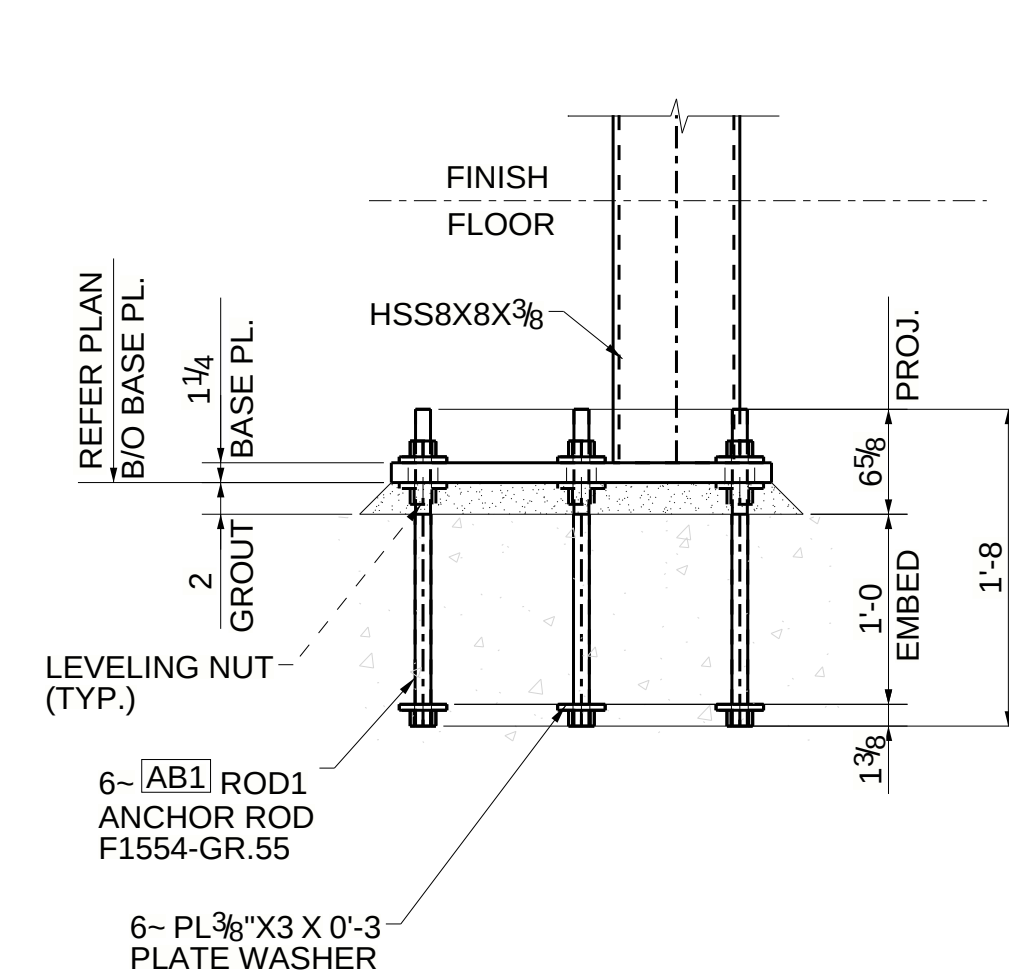

TYPE-9
(04 LOCATIONS)

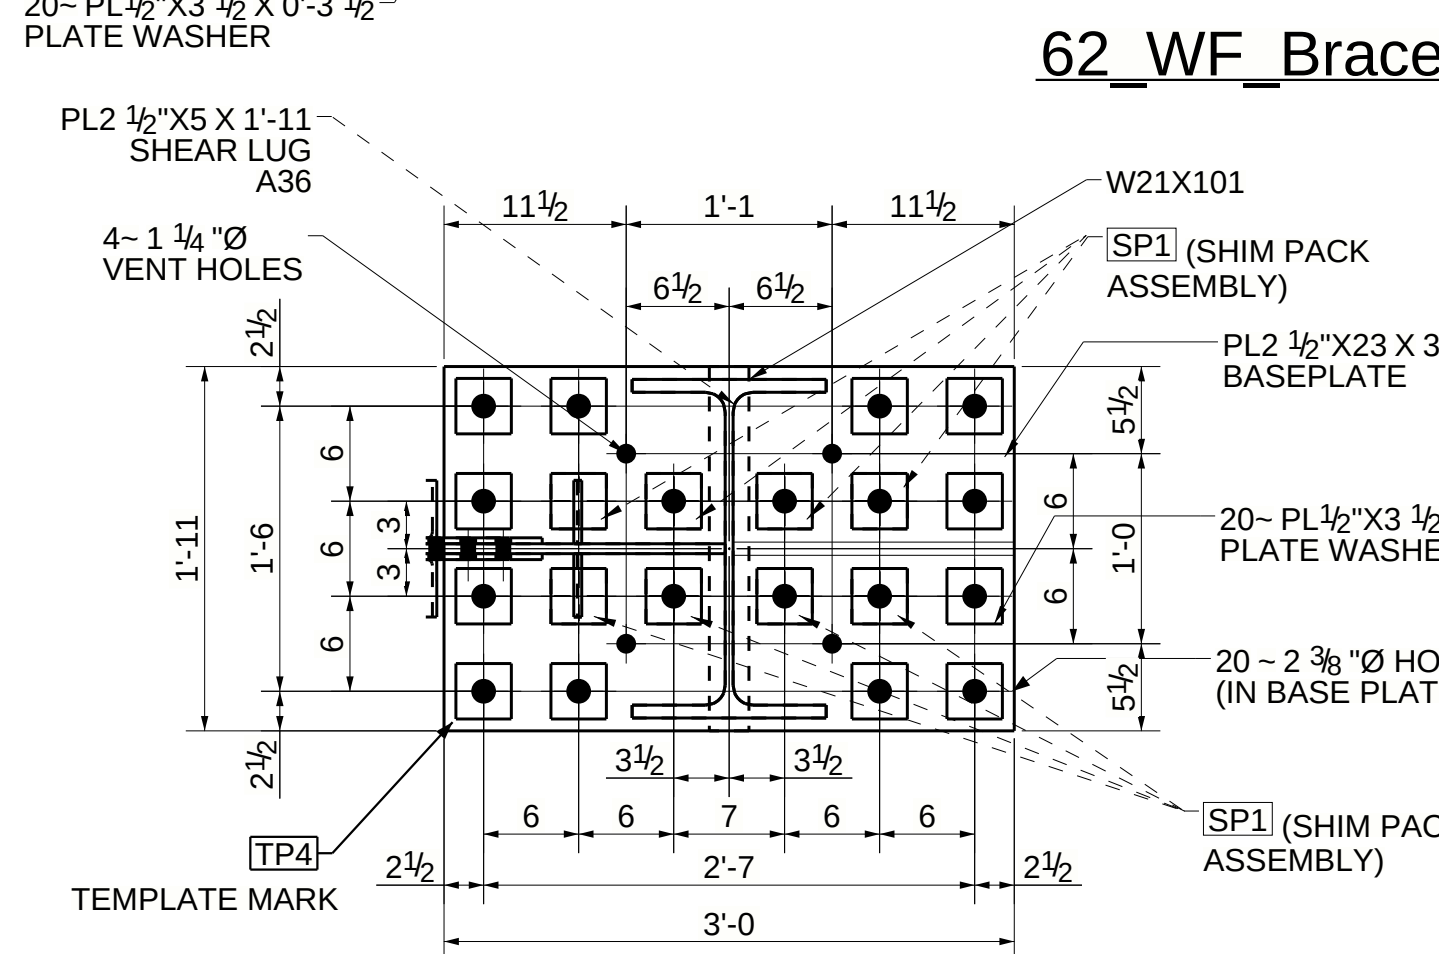

TYPE-4
(08 LOCATIONS)

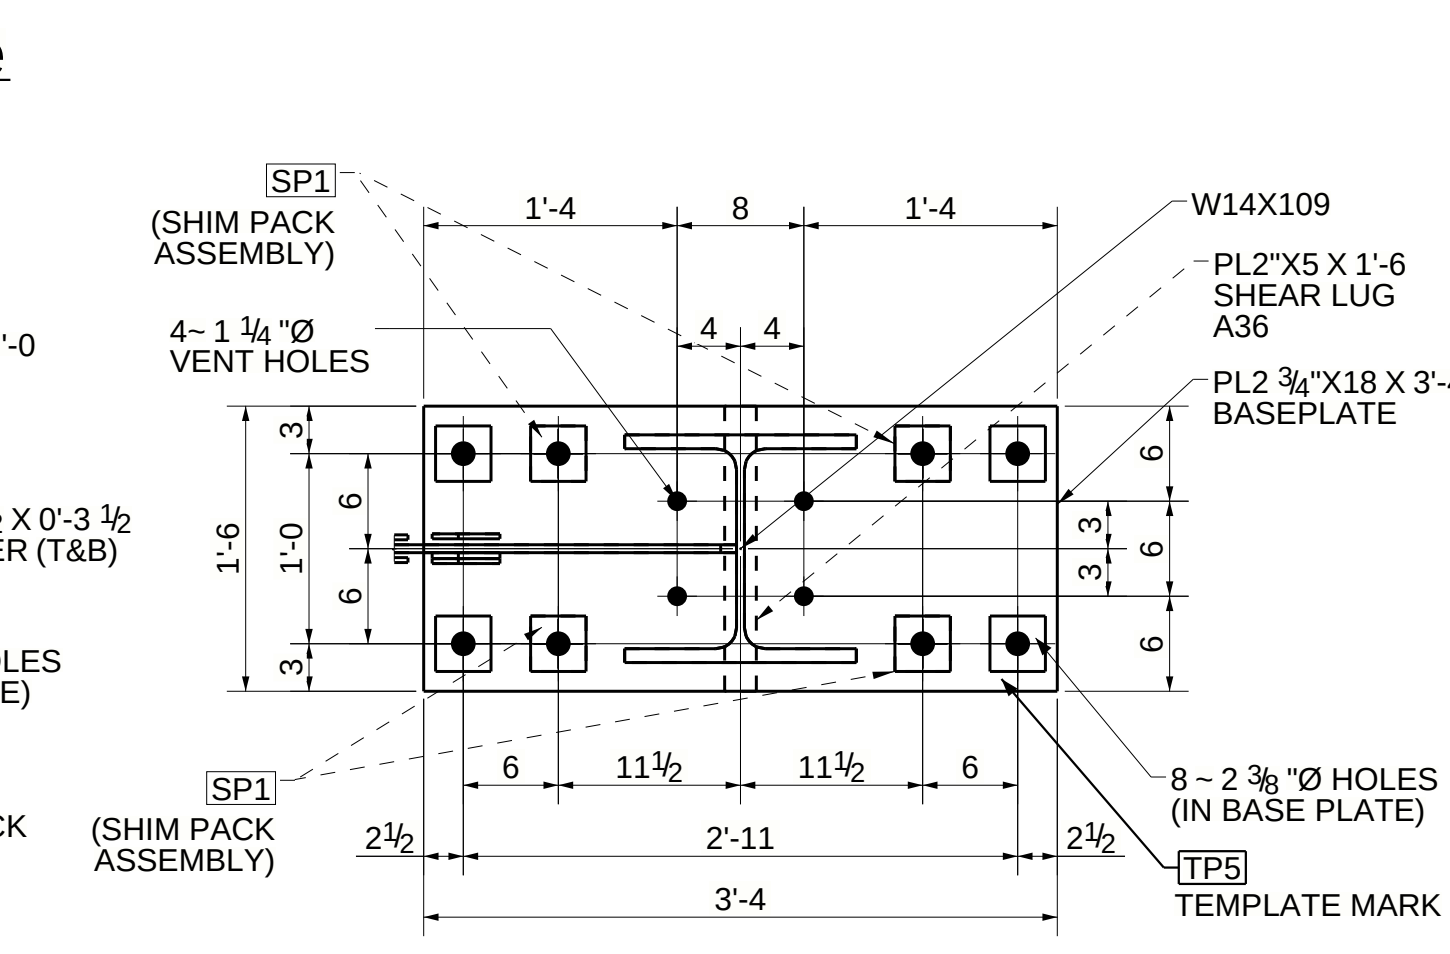

TYPE-5
(08 LOCATIONS)

62_WF_Brace

62_WF_Brace

62_WF_Brace

62_WF_Brace

62_WF_Brace

62_WF_Brace

62_WF_Brace

62_WF_Brace

62_WF_Brace

62_WF_Brace

62_WF_Brace

62_WF_Brace

62_WF_Brace

62_WF_Brace

62_WF_Brace

62_WF_Brace

62_WF_Brace

62_WF_Brace

62_WF_Brace

62_WF_Brace

62_WF_Brace


62_WF_Brace

62_WF_Brace

62_WF_Brace



62_WF_Brace

62_WF_Brace

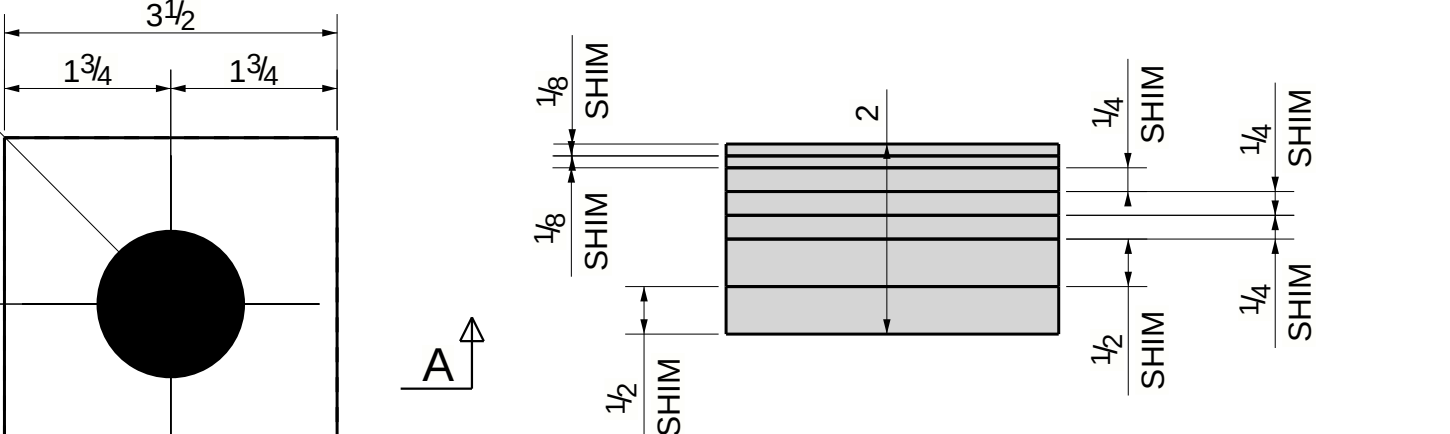

SECTION A - A

FOR FIELD USE : 09/21/2023

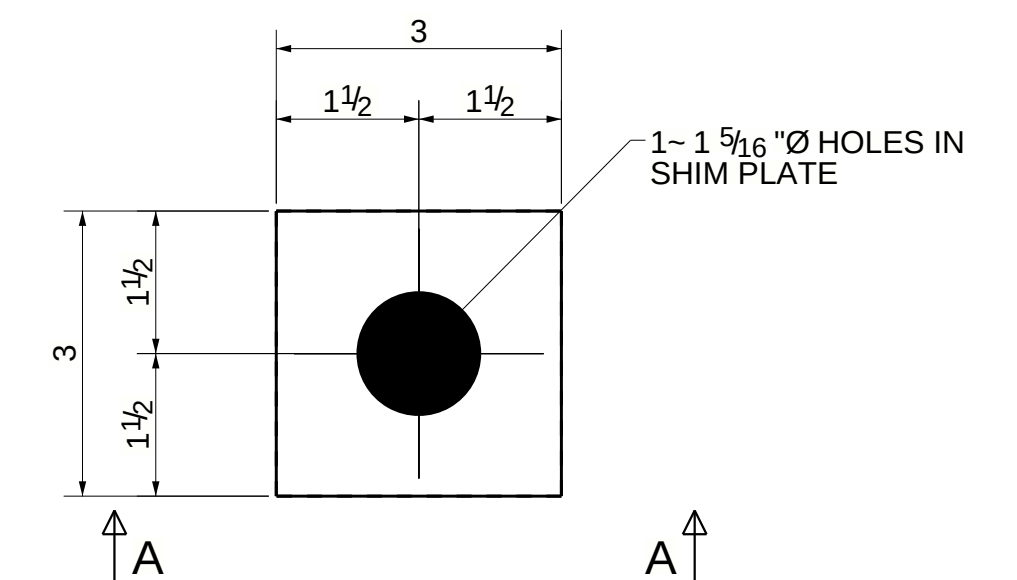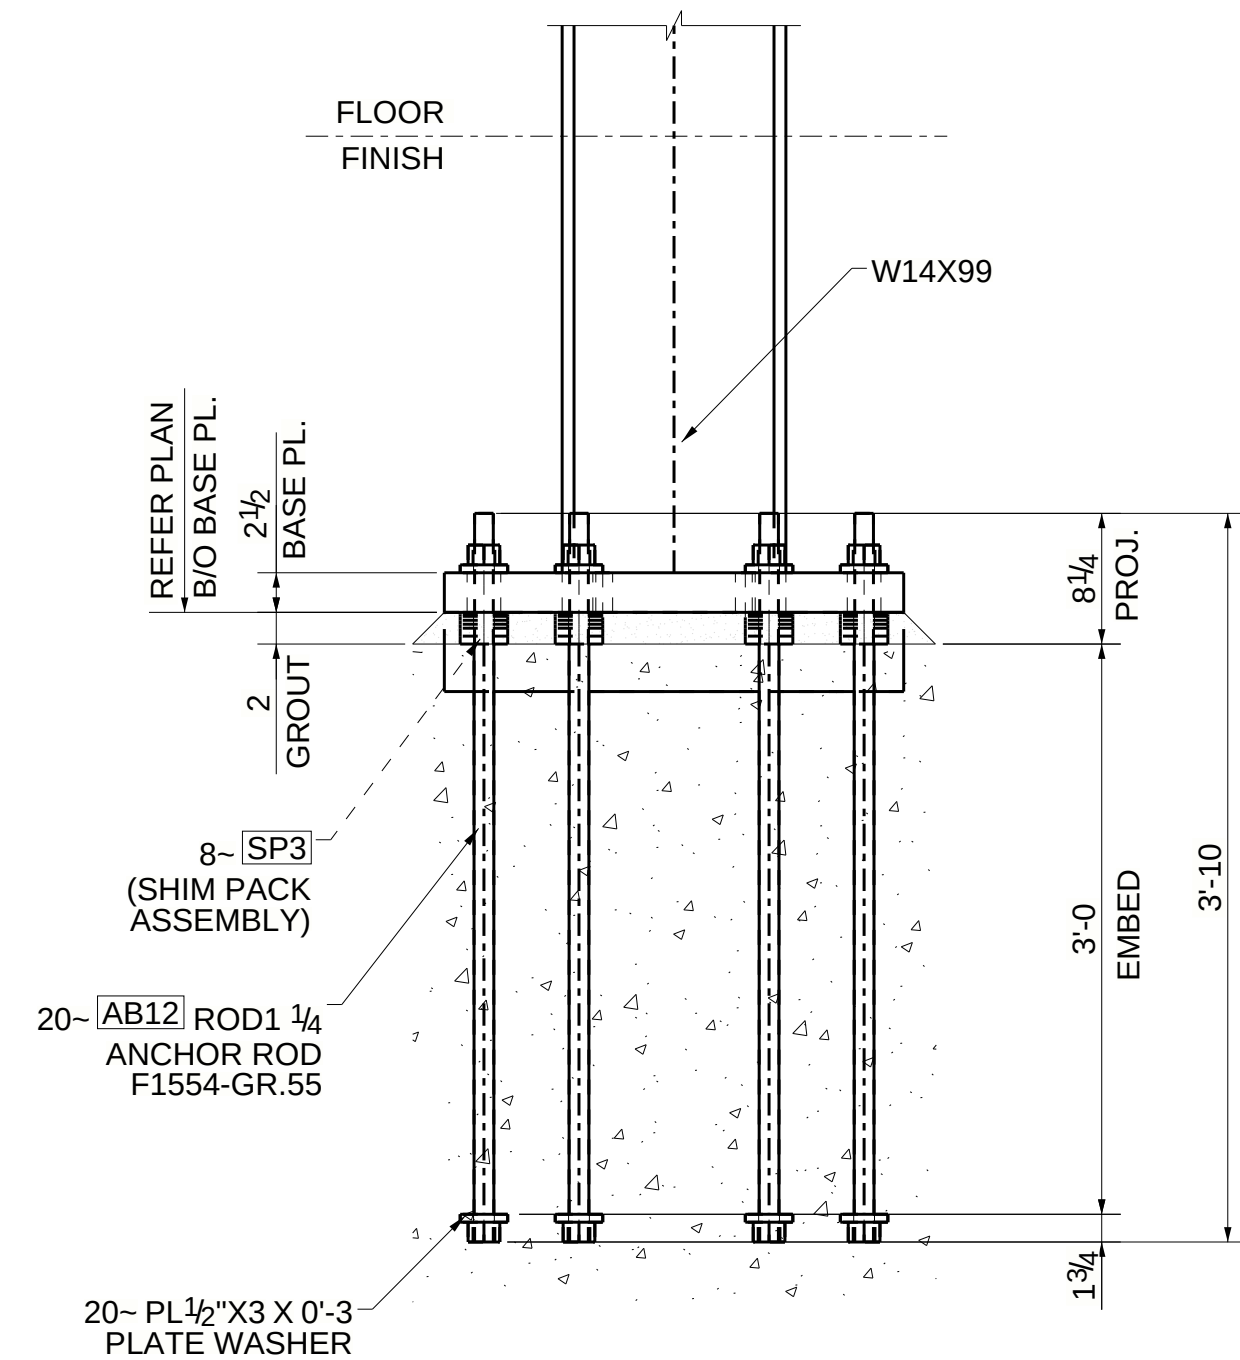[illegible]

1'-6"

1'-2"

7"

7"

2"

1'-11"

1'-7"

2"

9 1/2"

9 1/2"

3 1/2"

6"

TP11
TEMPLATE MARK

PL1 1/4" X18 X 1'-11"
BASEPLATE

6- PL 3/8" X3 X 0'-3"
PLATE WASHER (T&B)

6- 1/8" Ø HOLES
IN BASE PLATE

HSS8X8X3/8"

5 1/2"

10 3/4"

6 3/4"

4"

5"

4"

Technical drawing of a base plate assembly. The drawing shows a cross-section of a base plate (BASE PL.) mounted on a concrete foundation (POCKET). The base plate is secured with four bolts. Dimensions are provided in inches:

- Overall width of the base plate: $2\frac{1}{2}$
- Distance from the left edge of the base plate to the center of the first bolt: 2
- Distance between the centers of the two left bolts: 1
- Distance between the centers of the two right bolts: 1
- Distance from the center of the rightmost bolt to the right edge of the base plate: 4
- Thickness of the base plate: 3
- Distance from the bottom edge of the base plate to the top of the concrete pocket: 4
- Distance from the bottom edge of the base plate to the bottom of the concrete pocket: 1









The concrete pocket is labeled "POCKET" at the bottom. The base plate is labeled "BASE PL." on the left. The bolts are shown in cross-section.

The diagram illustrates a cross-section of a base plate assembly. A central vertical rod passes through a horizontal base plate. The base plate is secured by four bolts, two on each side of the rod. Below the base plate is a thick layer labeled "GROUT". At the bottom are two rectangular cavities labeled "POCKET". Dimensions are indicated as follows:



- Vertical Dimensions:**
 - Total height from the top of the base plate to the bottom of the grout: $2\frac{1}{2}$
 - Height of the base plate: 2
 - Thickness of the grout layer: 1
- Horizontal Dimensions:**
 - Distance from the centerline of the rod to the inner edge of the left pocket: 1
 - Width of the left pocket: 2
 - Distance between the inner edges of the two pockets: 4
 - Distance from the centerline of the rod to the outer edge of the right pocket: 5
 - Width of the right pocket: 4

SECTION 6PA - 6PA

REFER PLAN FOR BASE PLATE &
COLUMN ORIENTATION
TYPICAL FOR ALL DETAILS

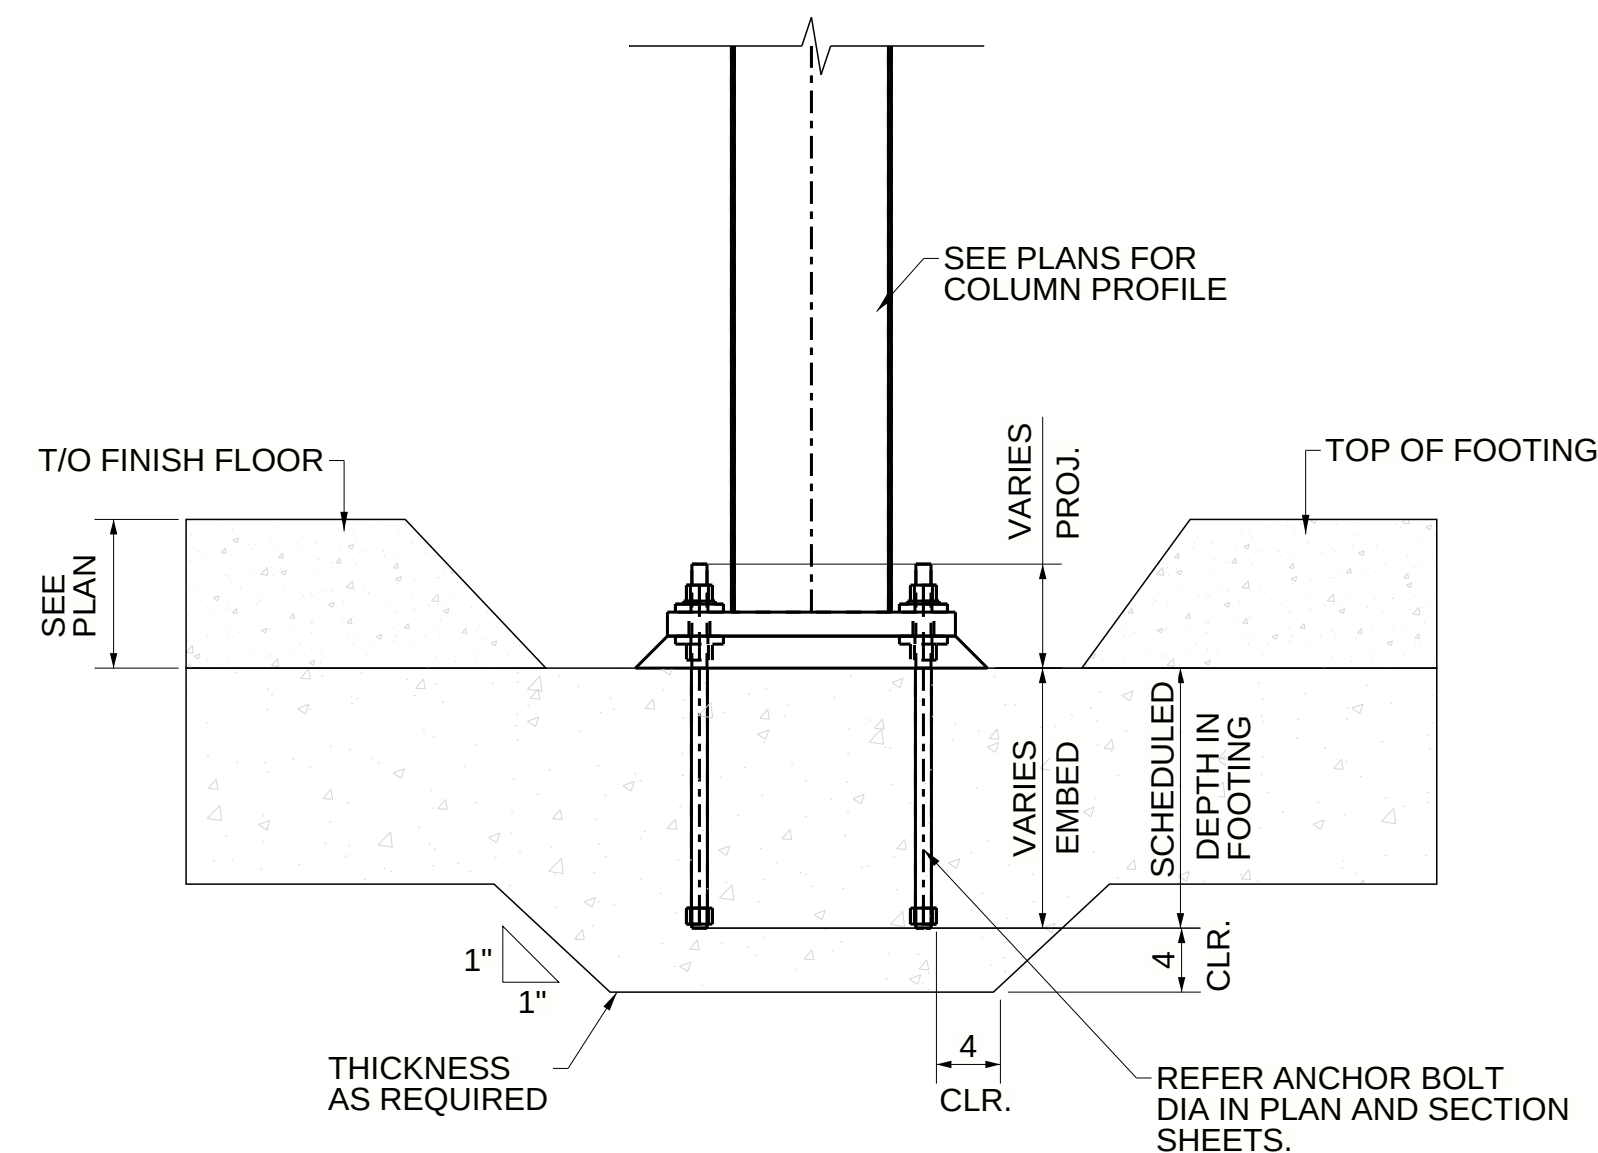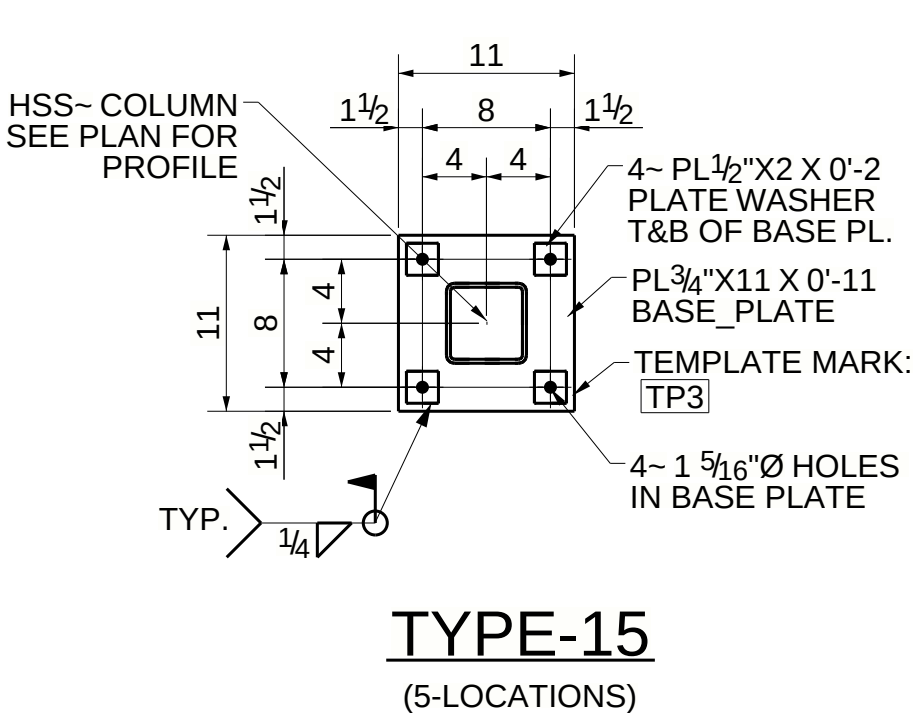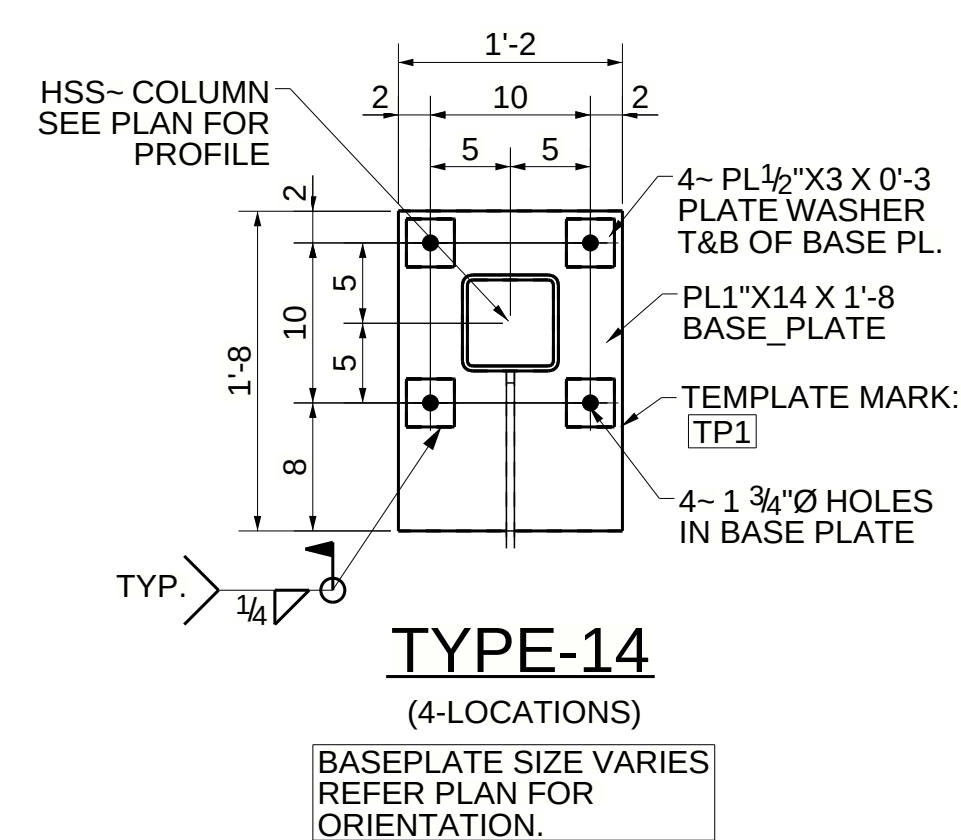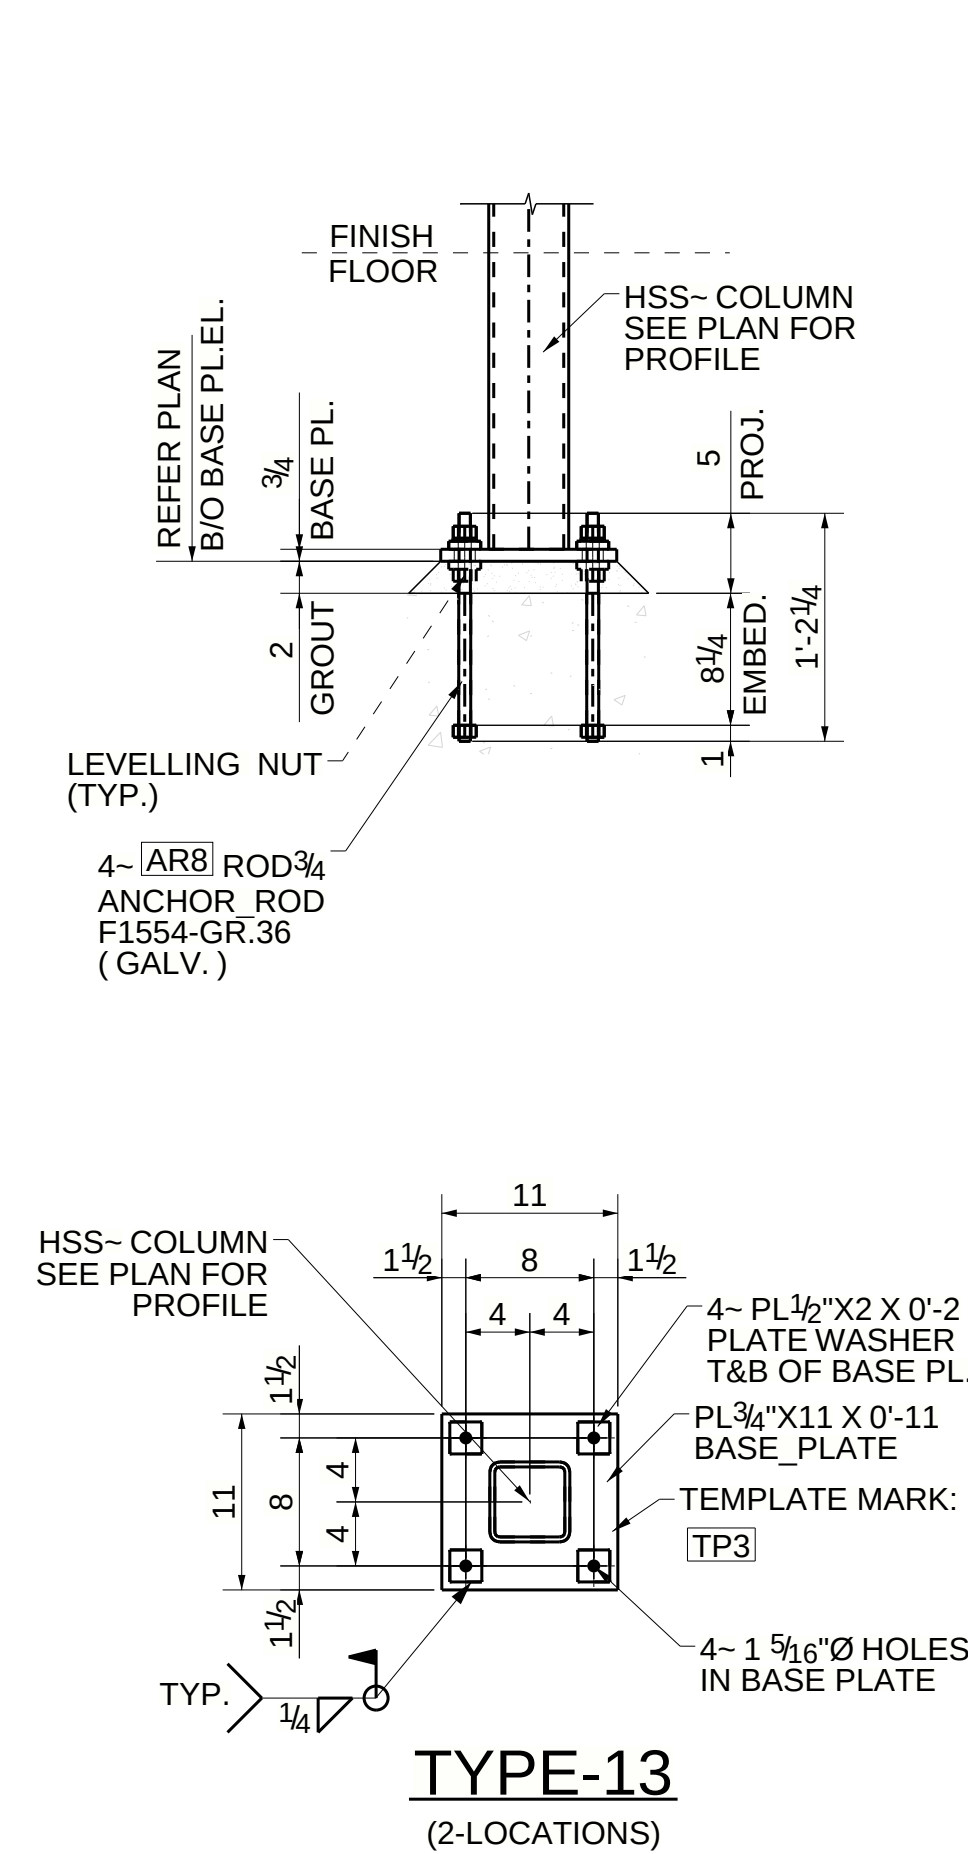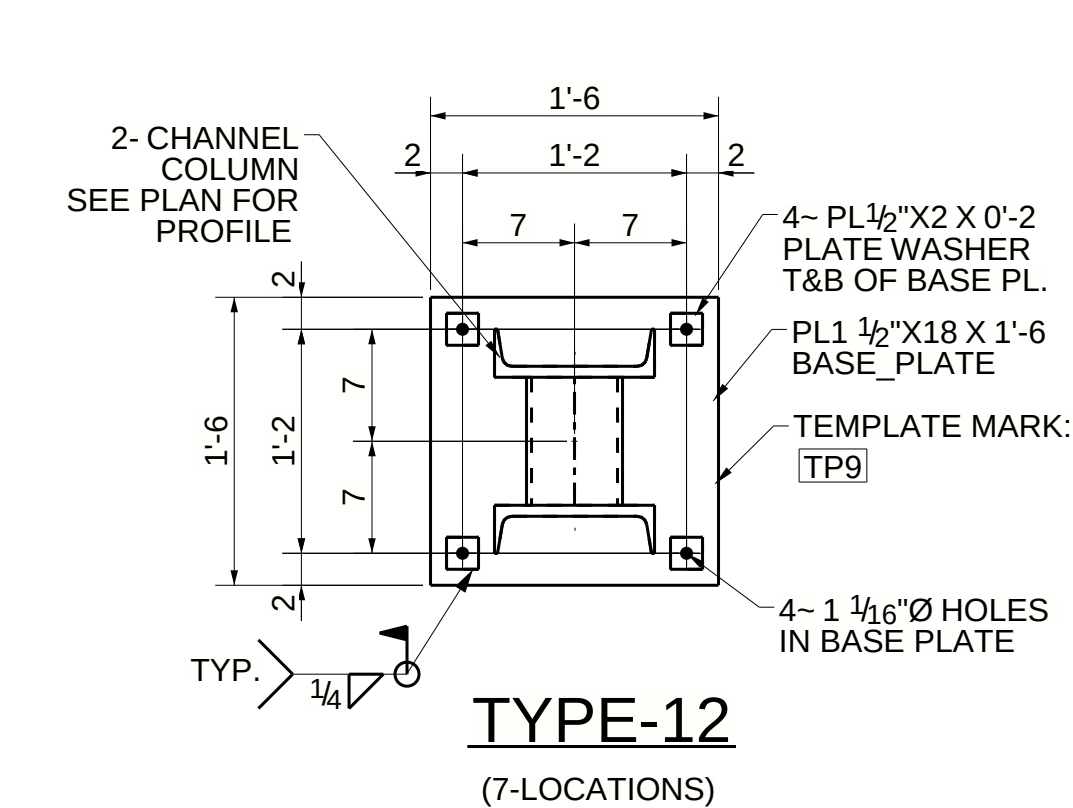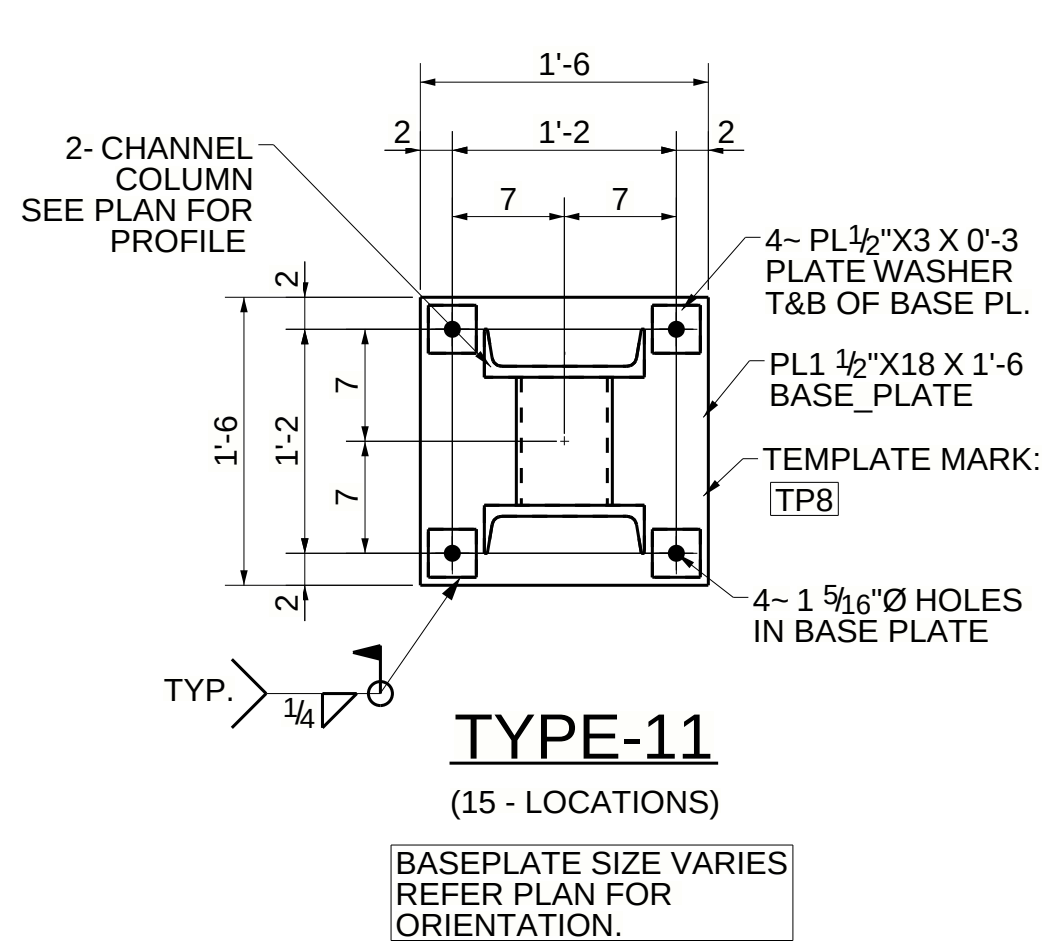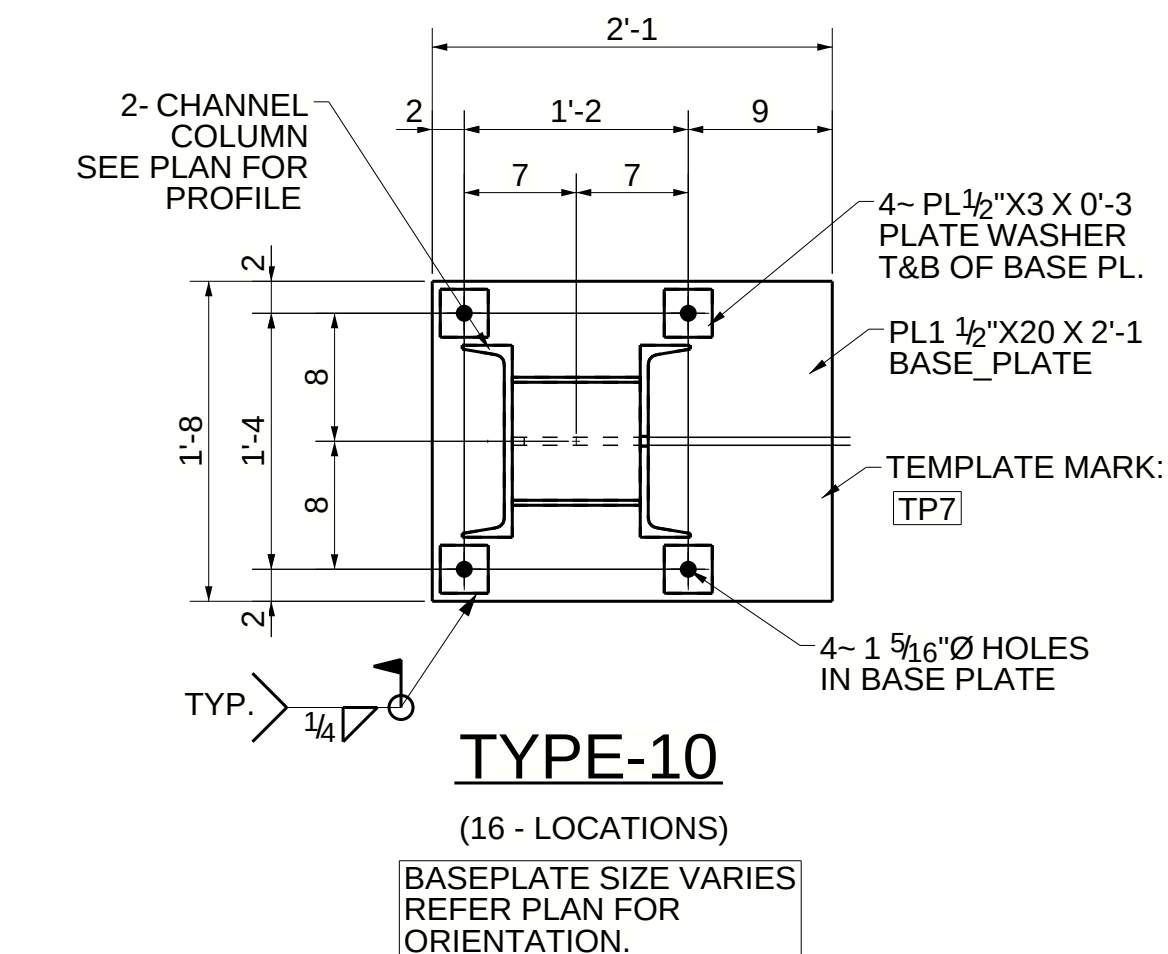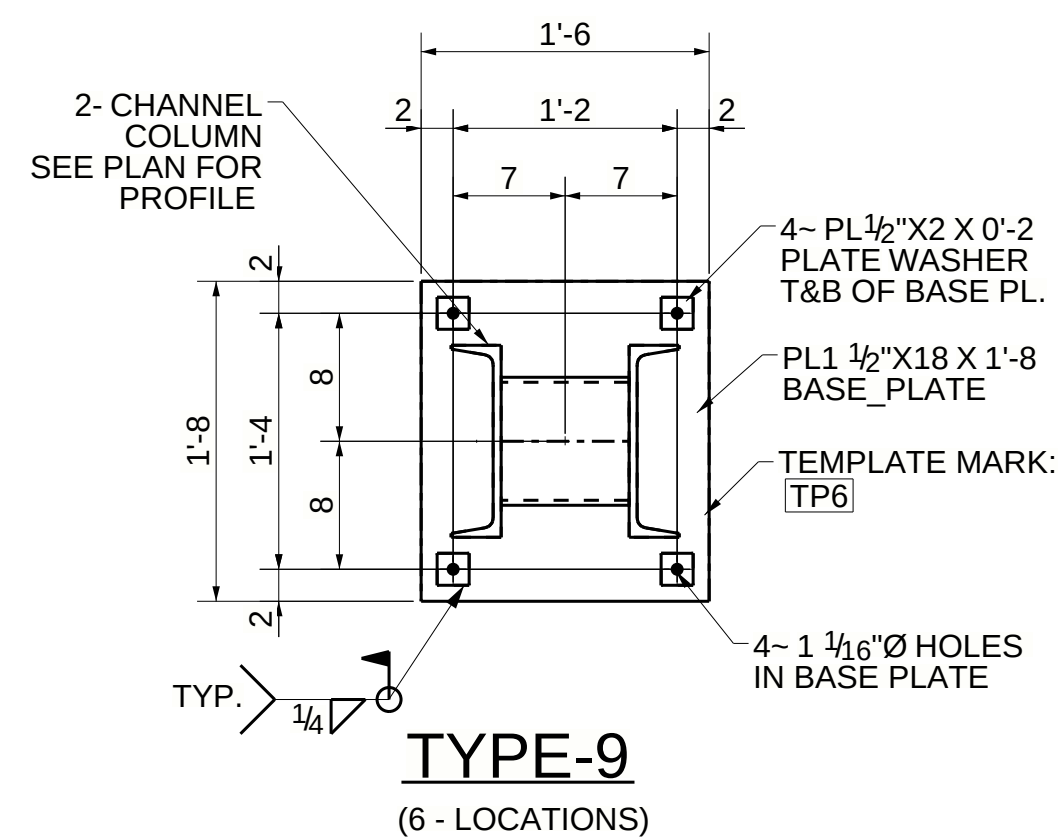



TYPICAL FOOTING DETAIL FOR DEPTH FOR EXCEEDING EMBEDS
(REFER : TYPICAL THICKEN FOOTING AT ANCHOR BOLTS 9 / S0.4)

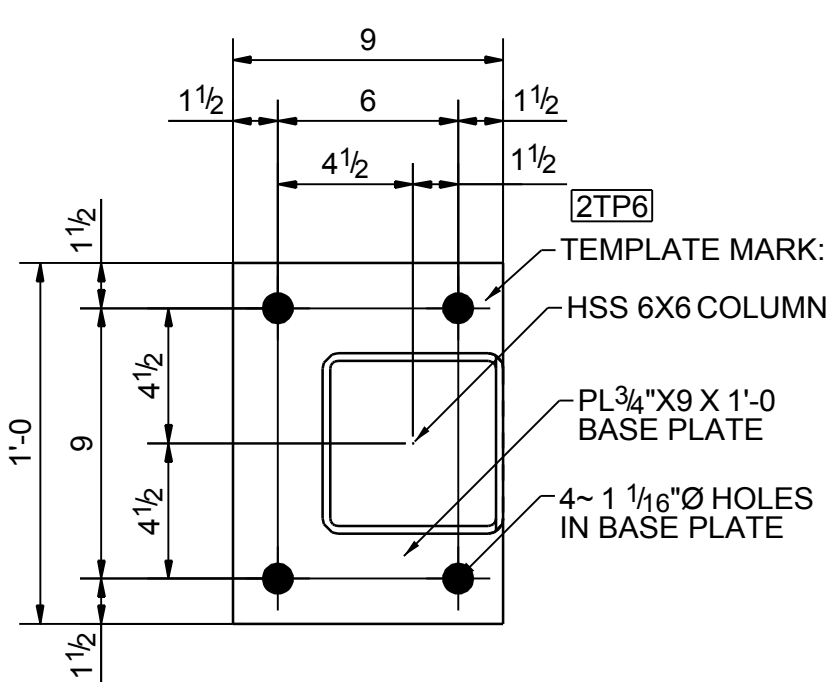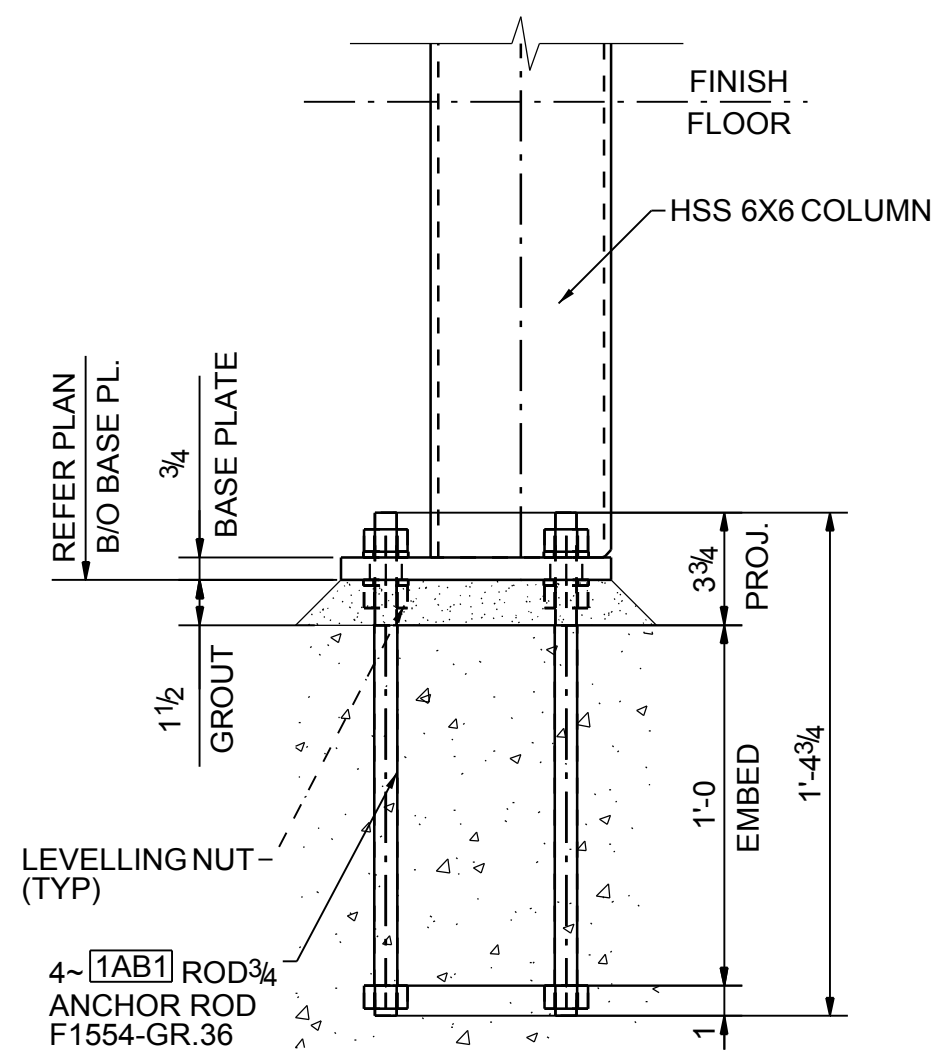

TYPE-8

(04-LOCATIONS)



REFER PLAN FOR COLUMN & BASEPLATE ORIENTATION

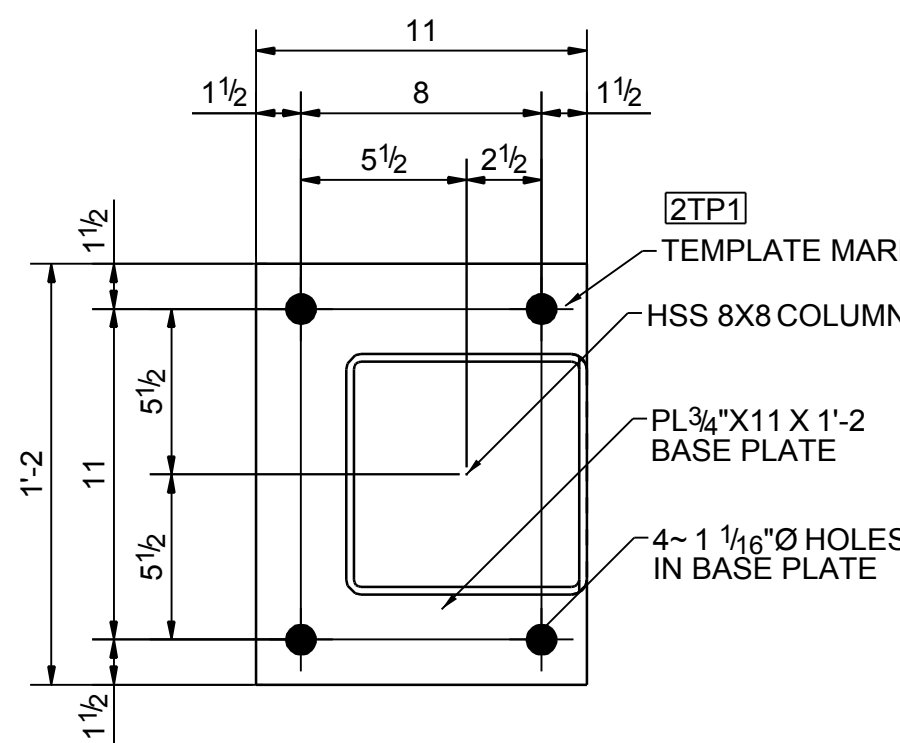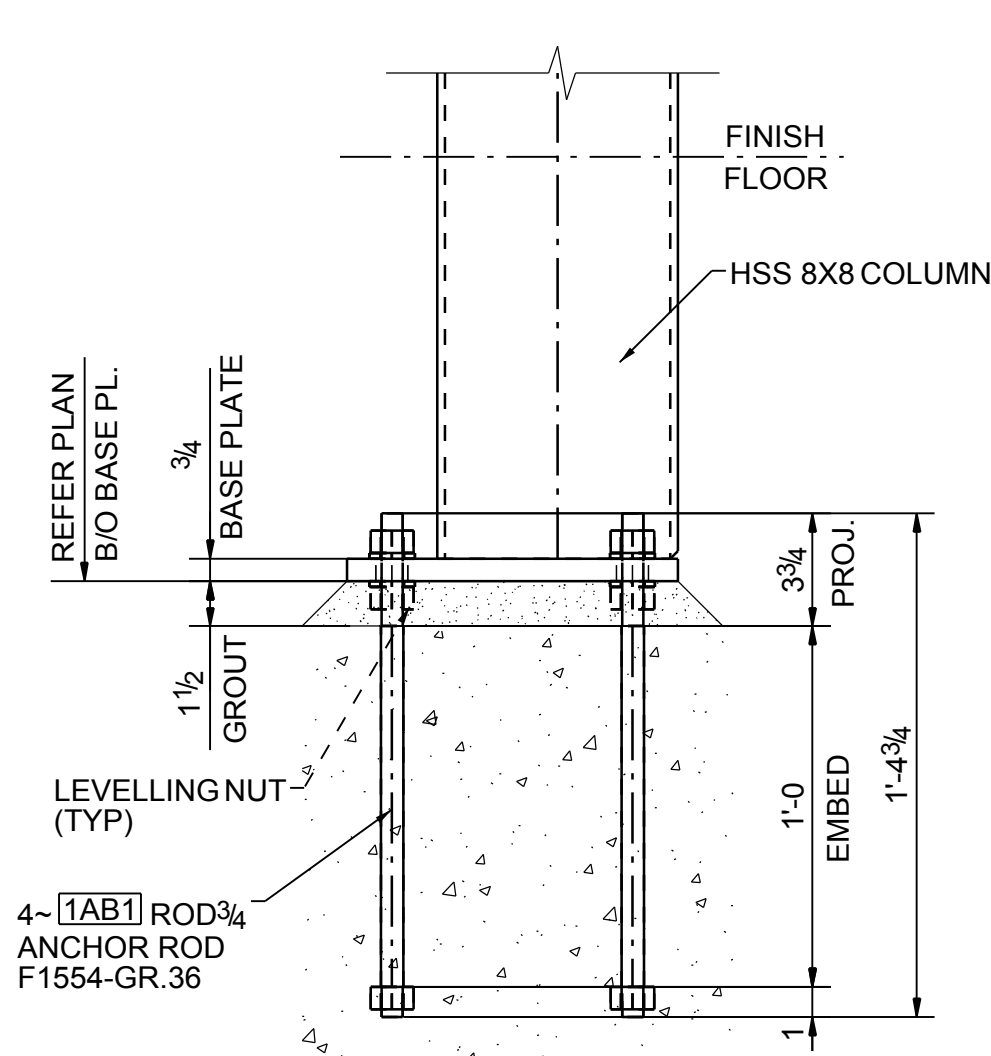

TYPE-9

(01-LOCATION)



REFER PLAN FOR COLUMN & BASEPLATE ORIENTATION

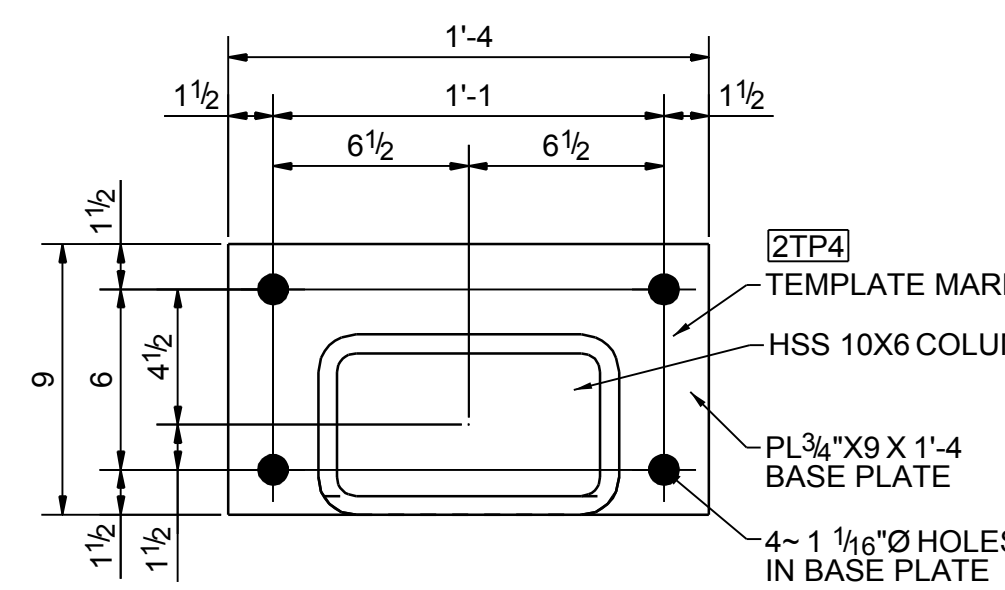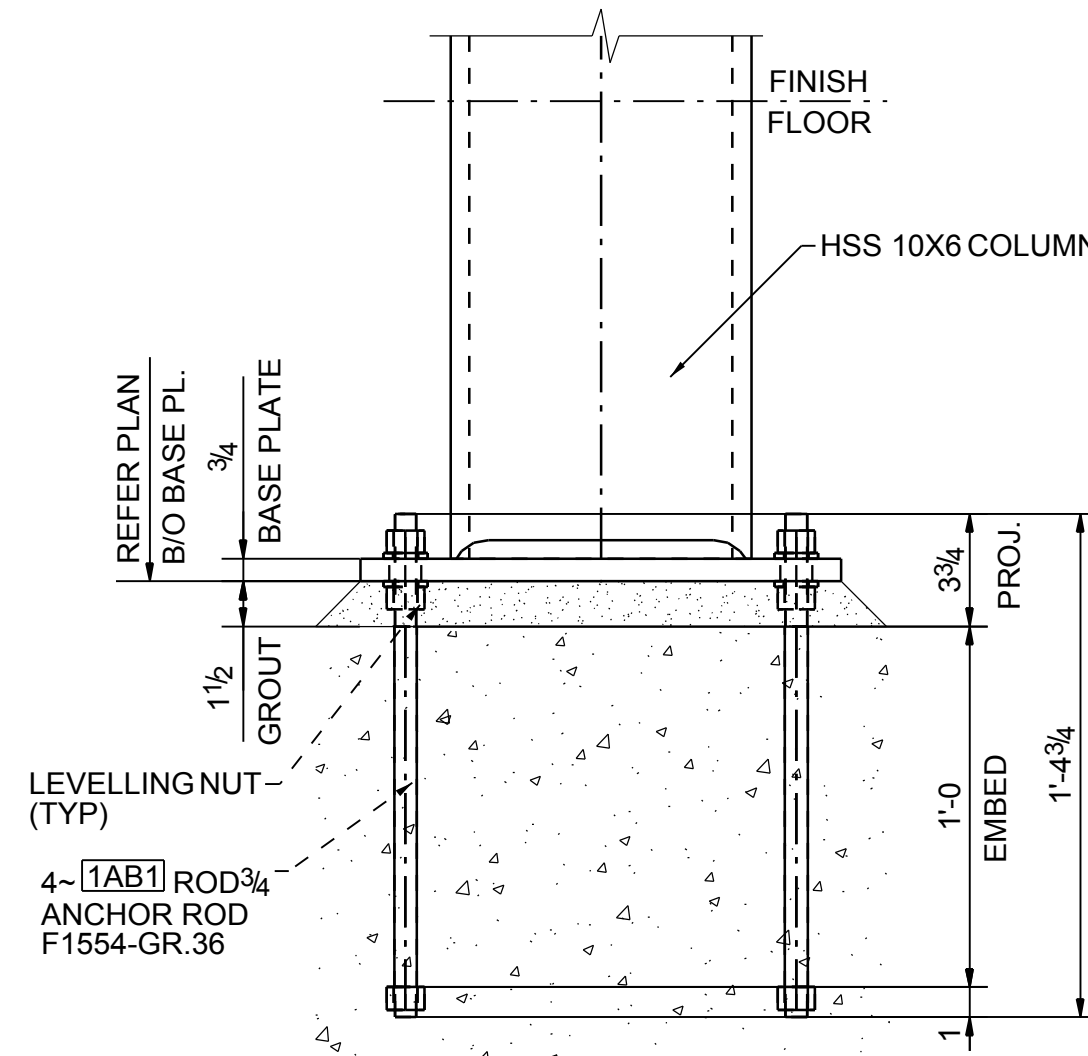

TYPE-10

(01-LOCATION)



REFER PLAN FOR COLUMN & BASEPLATE ORIENTATION

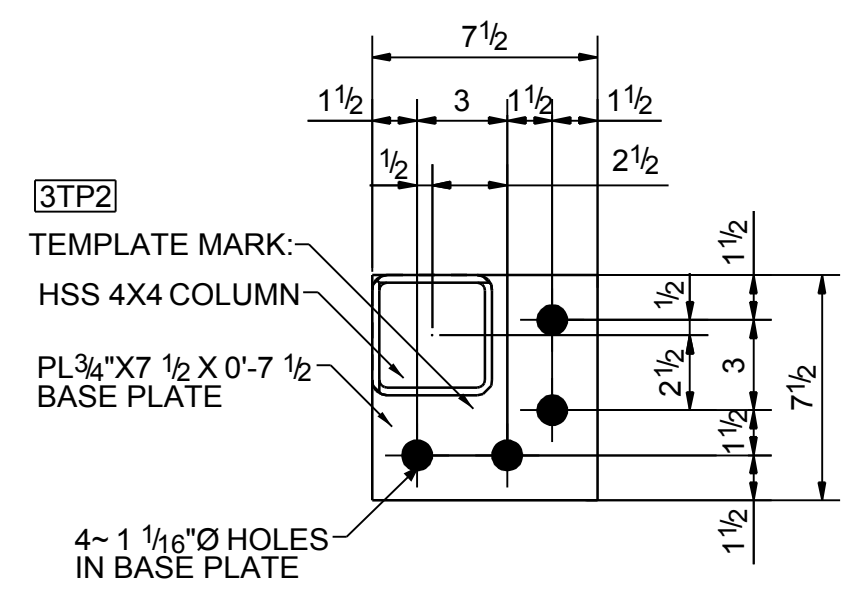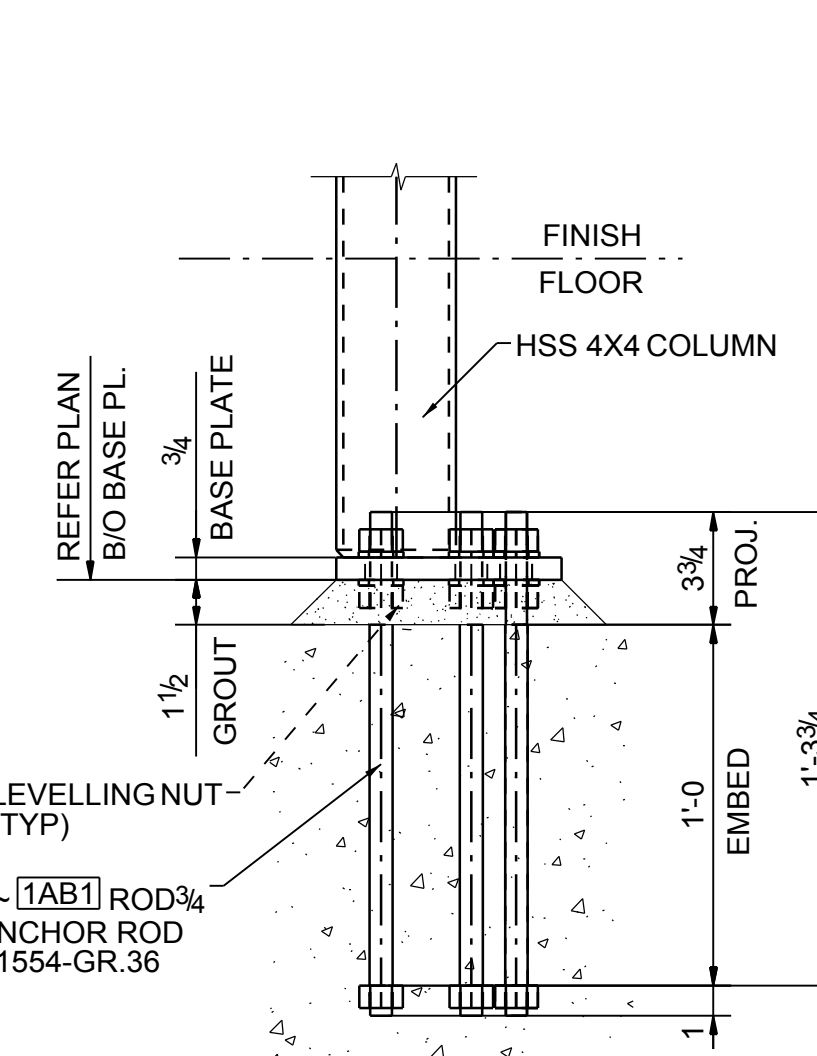

TYPE-11

(02-LOCATIONS)



REFER PLAN FOR COLUMN & BASEPLATE ORIENTATION

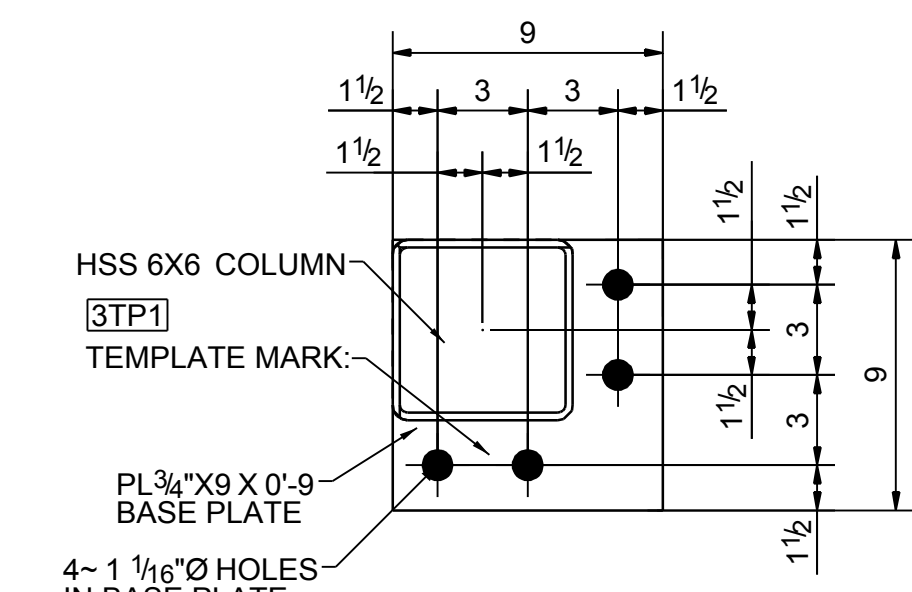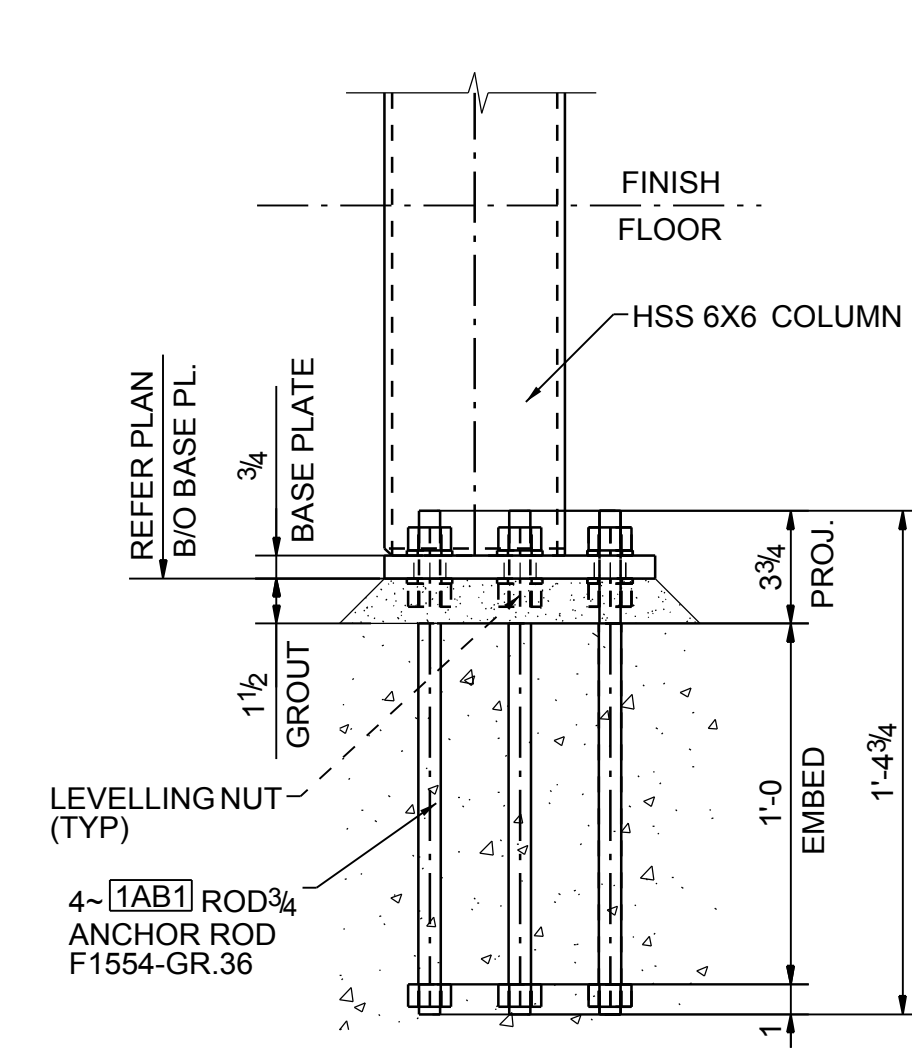

TYPE-12

(10-LOCATIONS)



REFER PLAN FOR COLUMN & BASEPLATE ORIENTATION

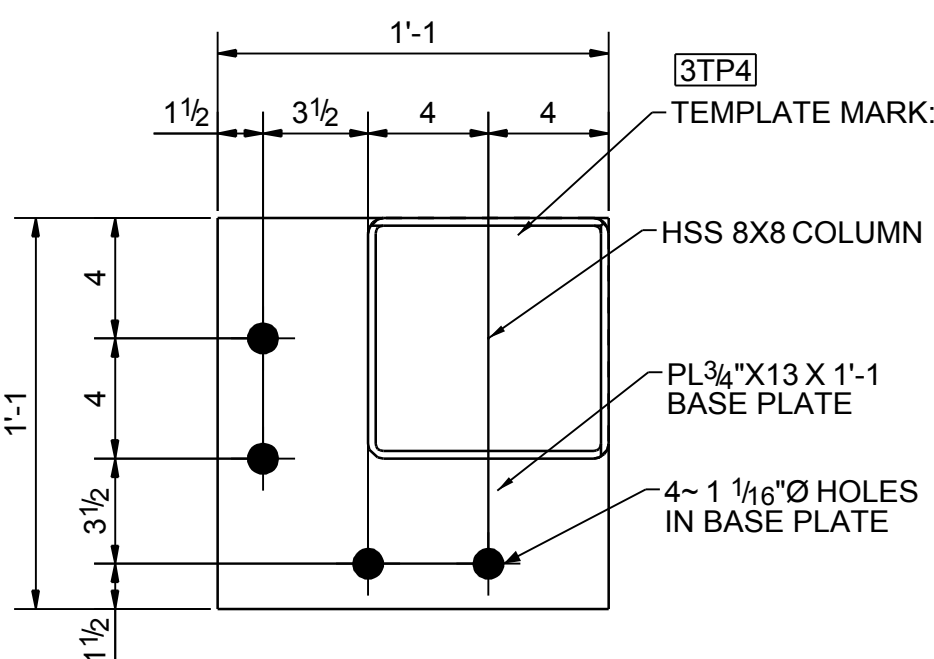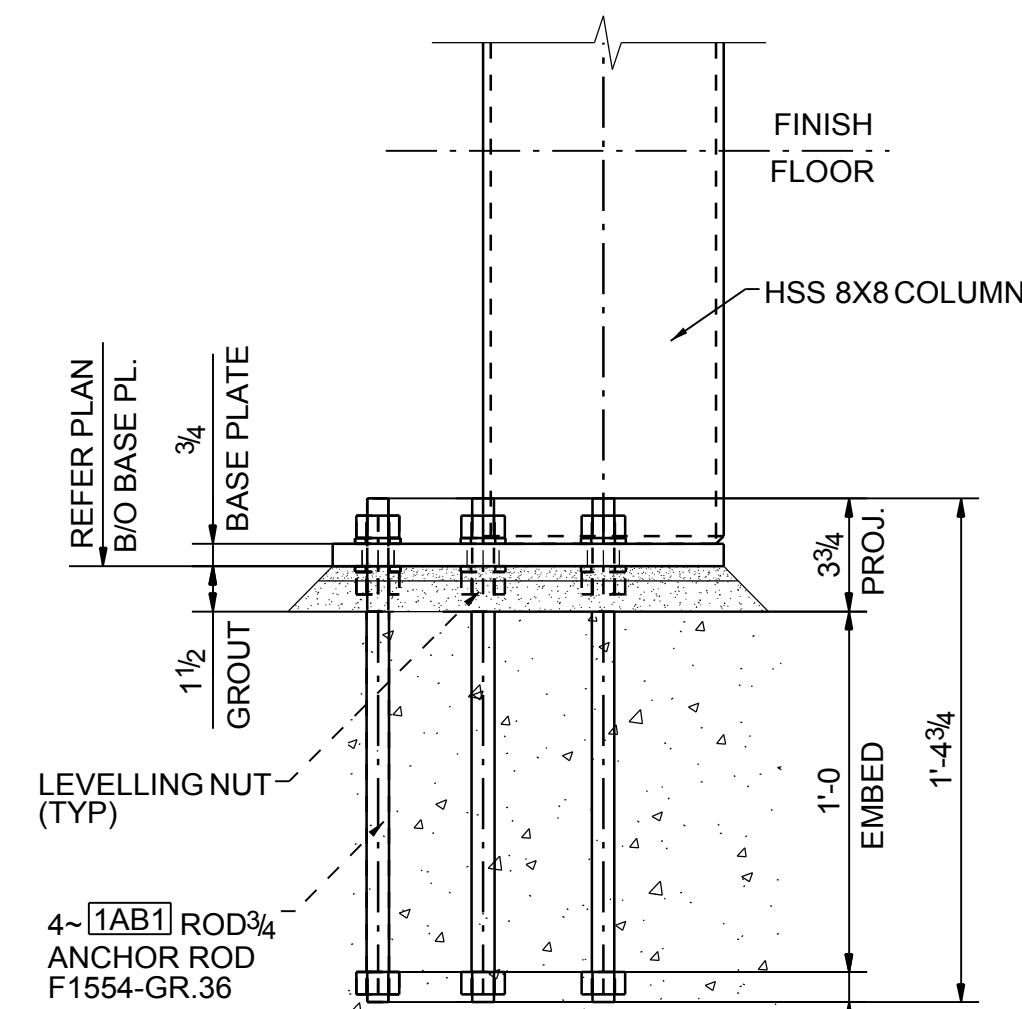

TYPE-13

(01-LOCATIONS)



REFER PLAN FOR COLUMN & BASEPLATE ORIENTATION

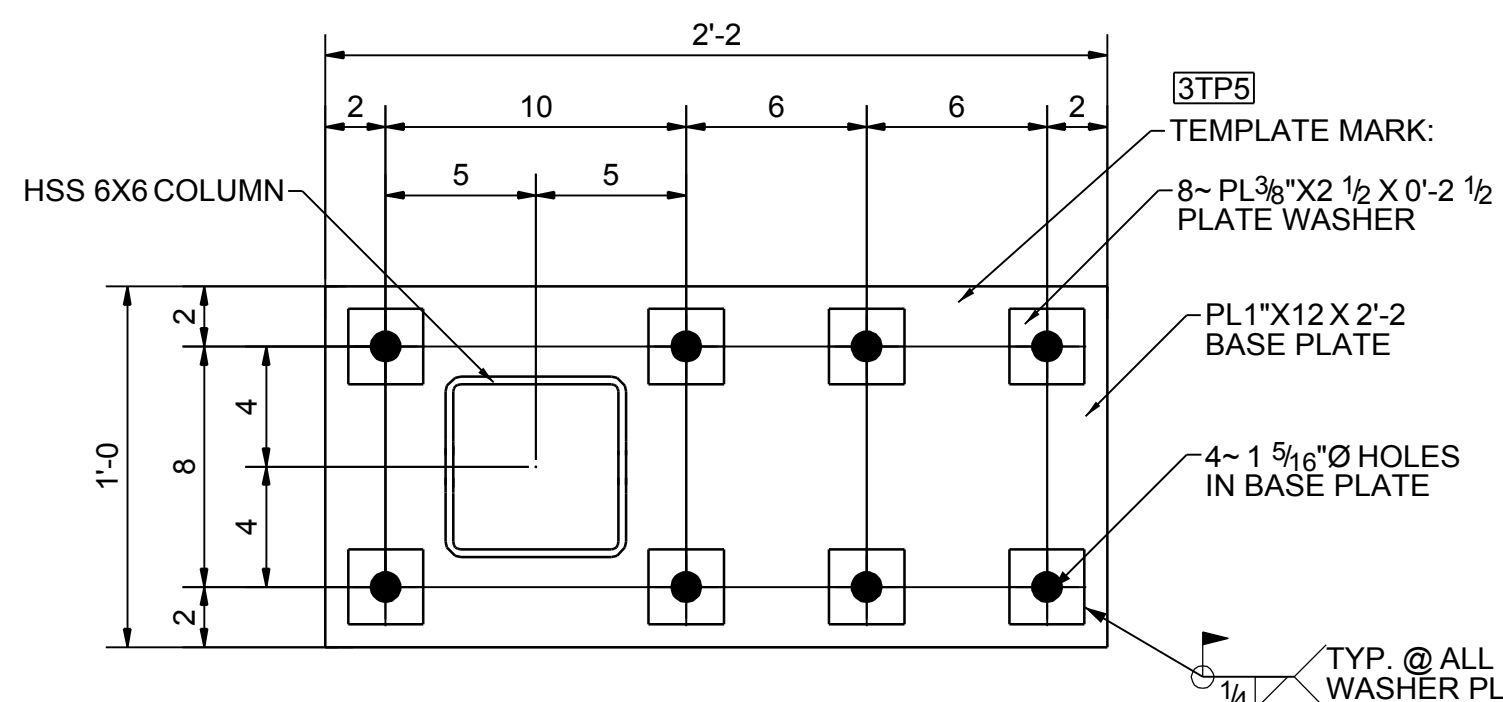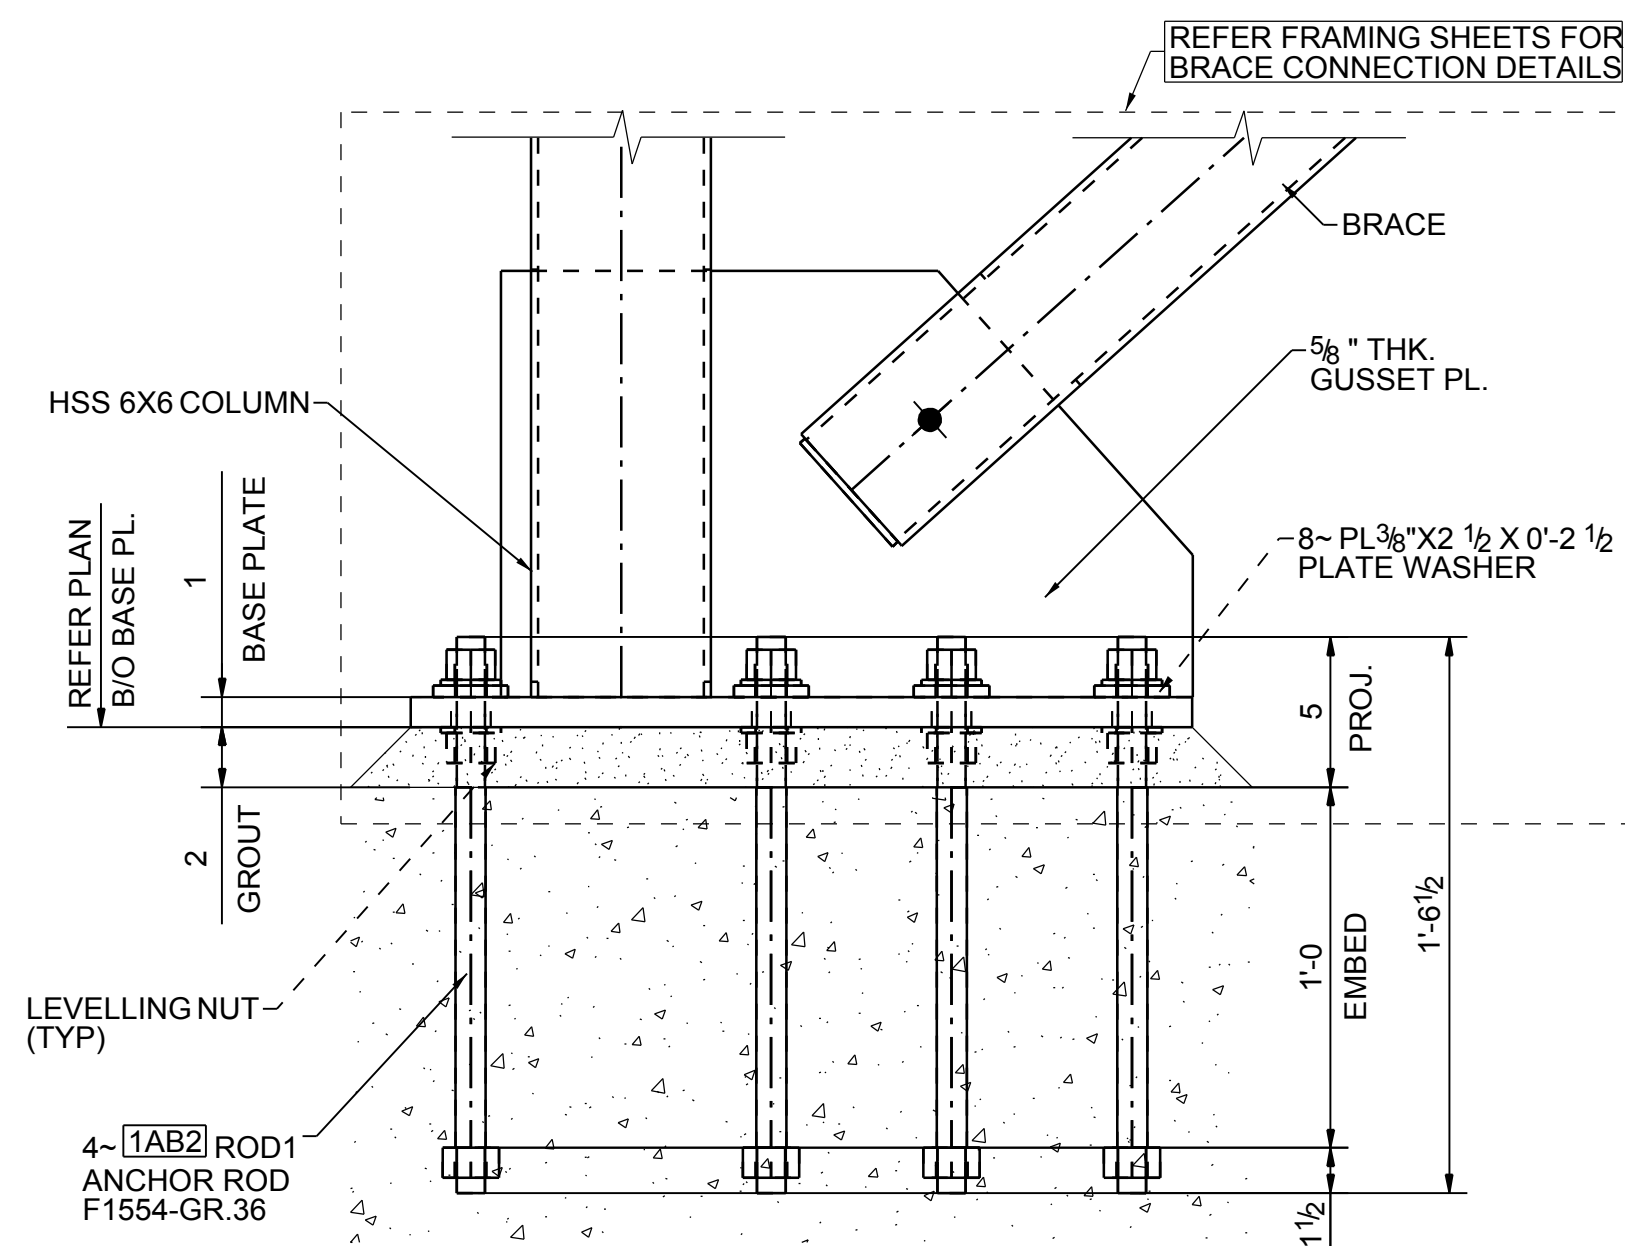

TYPE-14

(03-LOCATIONS)




REFER PLAN FOR COLUMN & BASEPLATE ORIENTATION

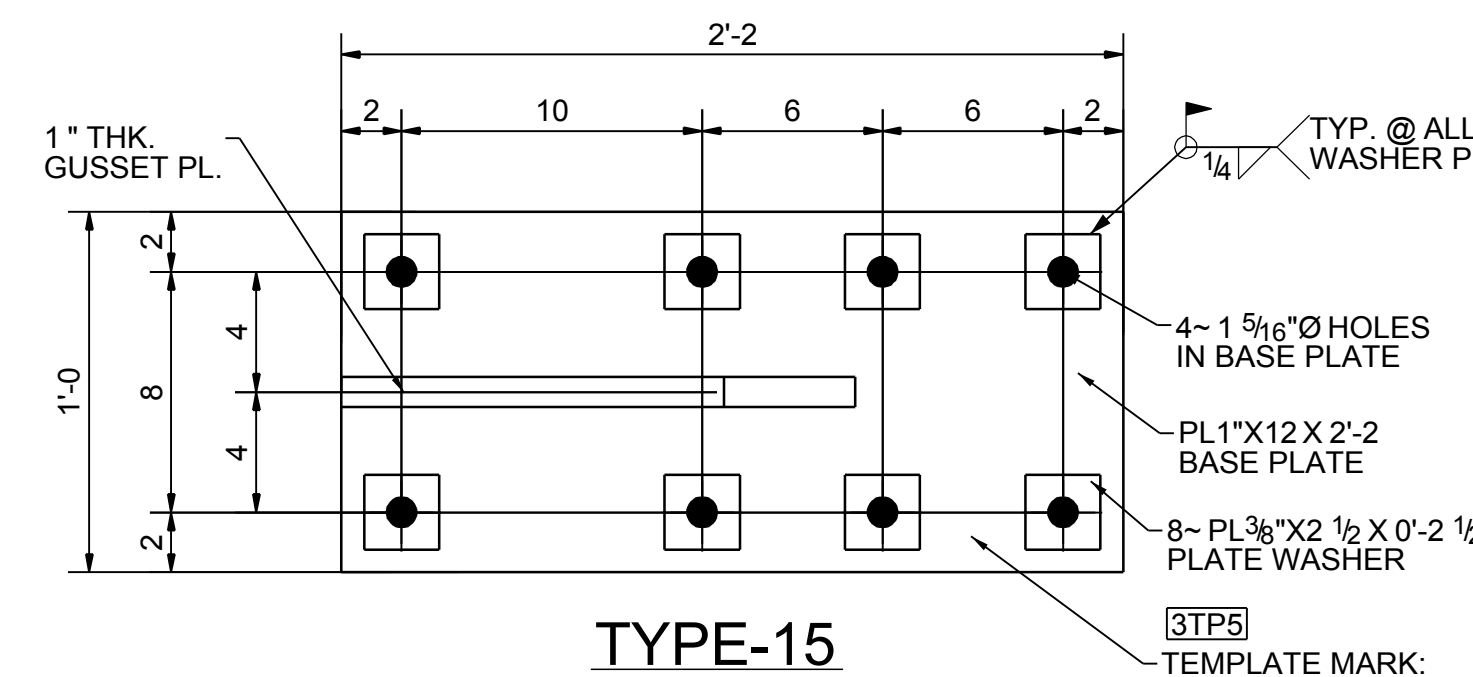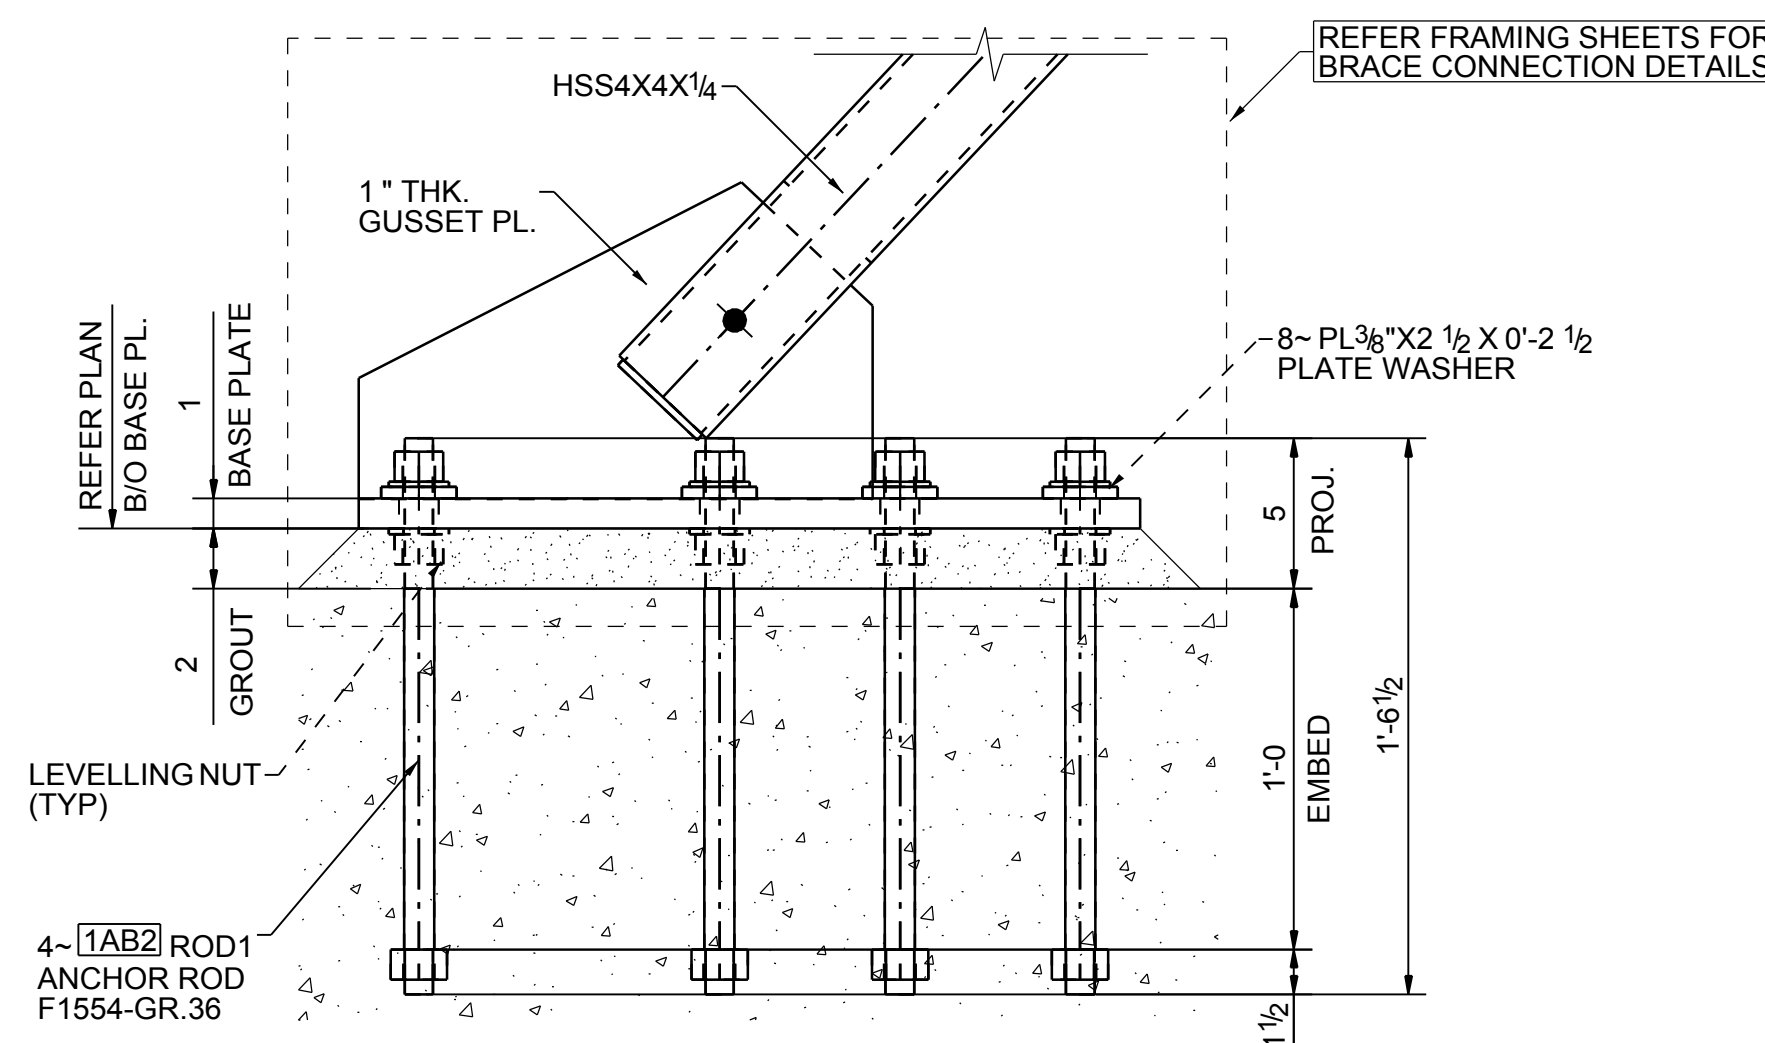












TYPE-15


(01-LOCATION)

REFER PLAN FOR COLUMN & BASEPLATE ORIENTATION

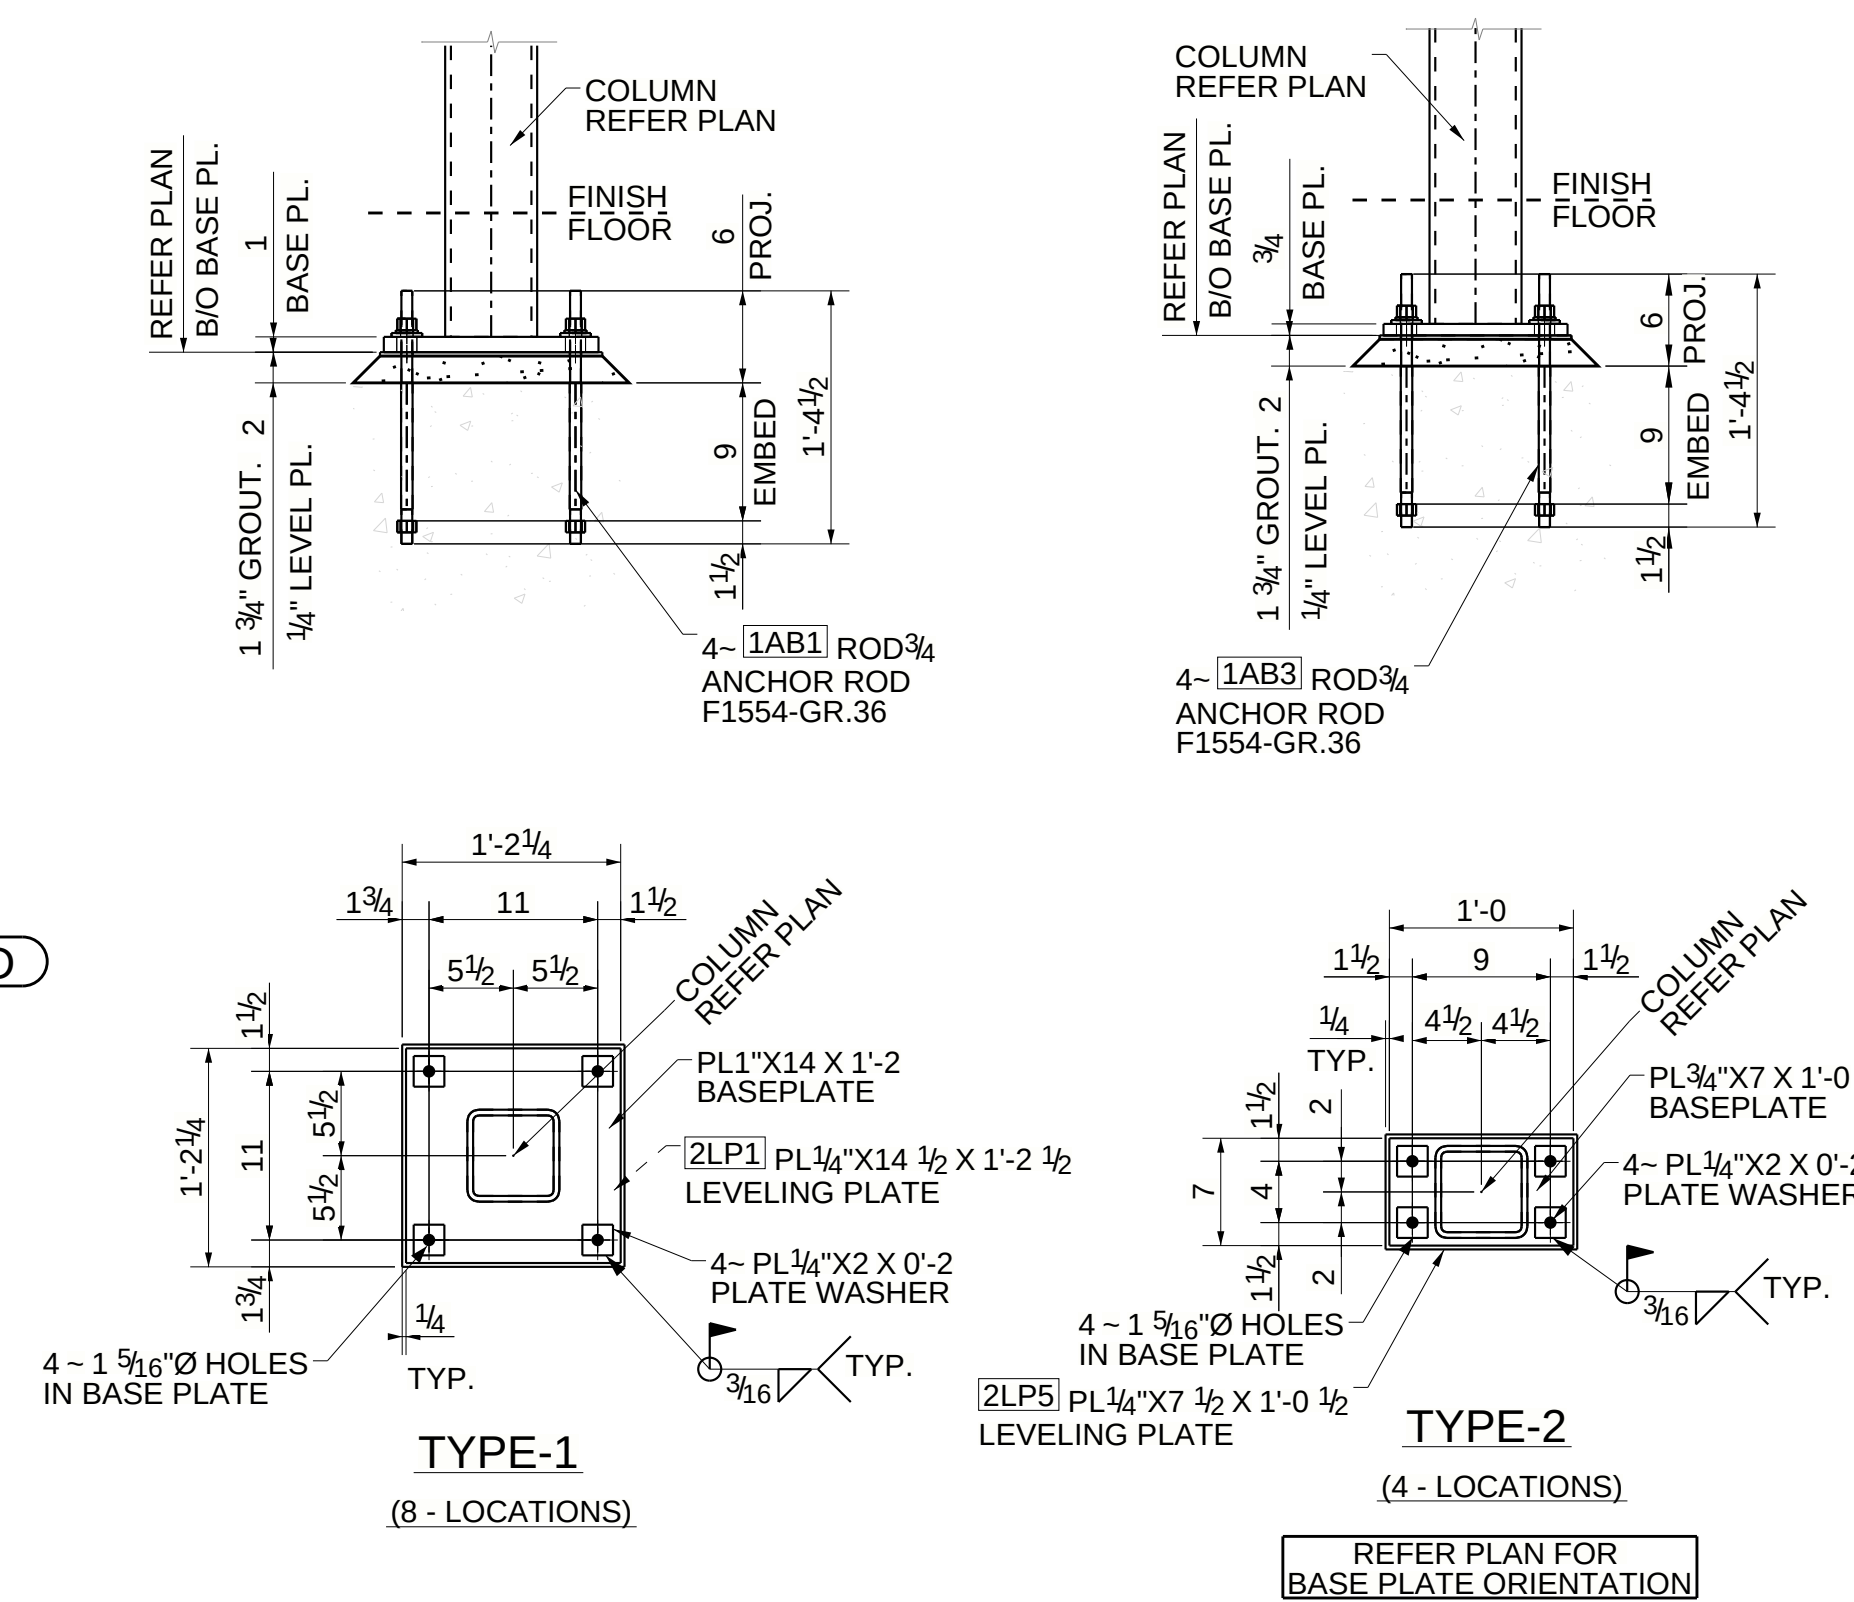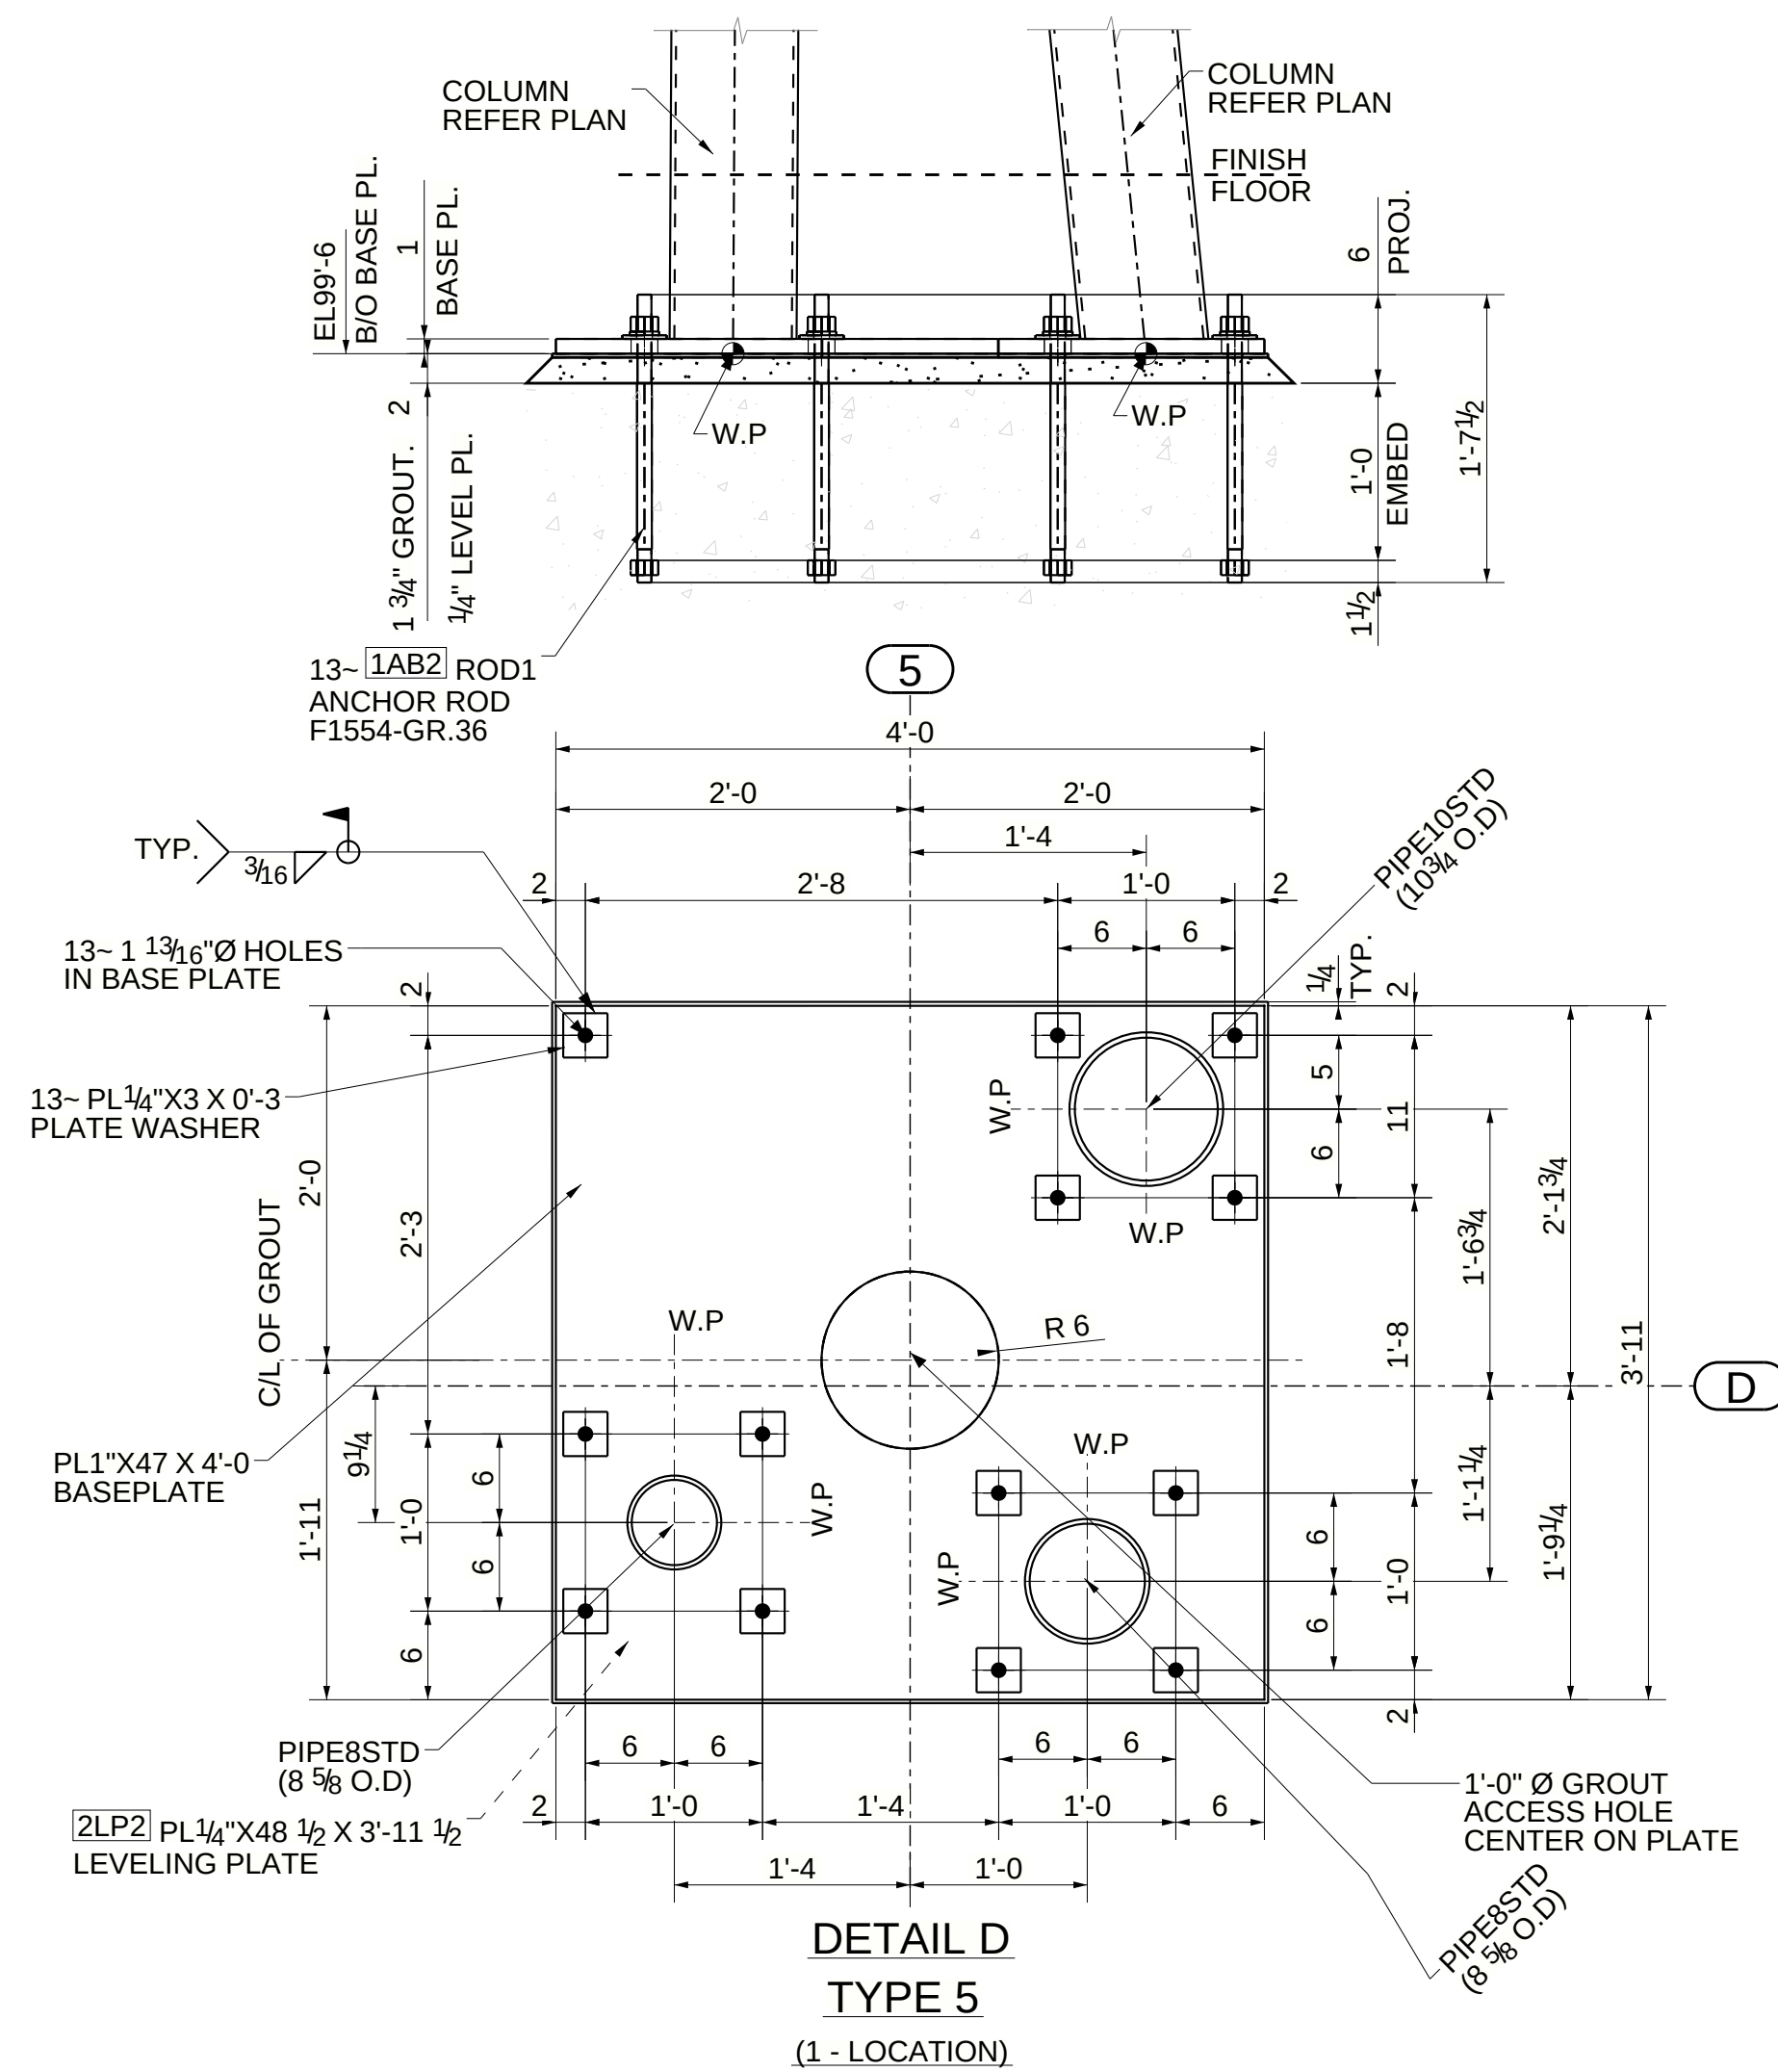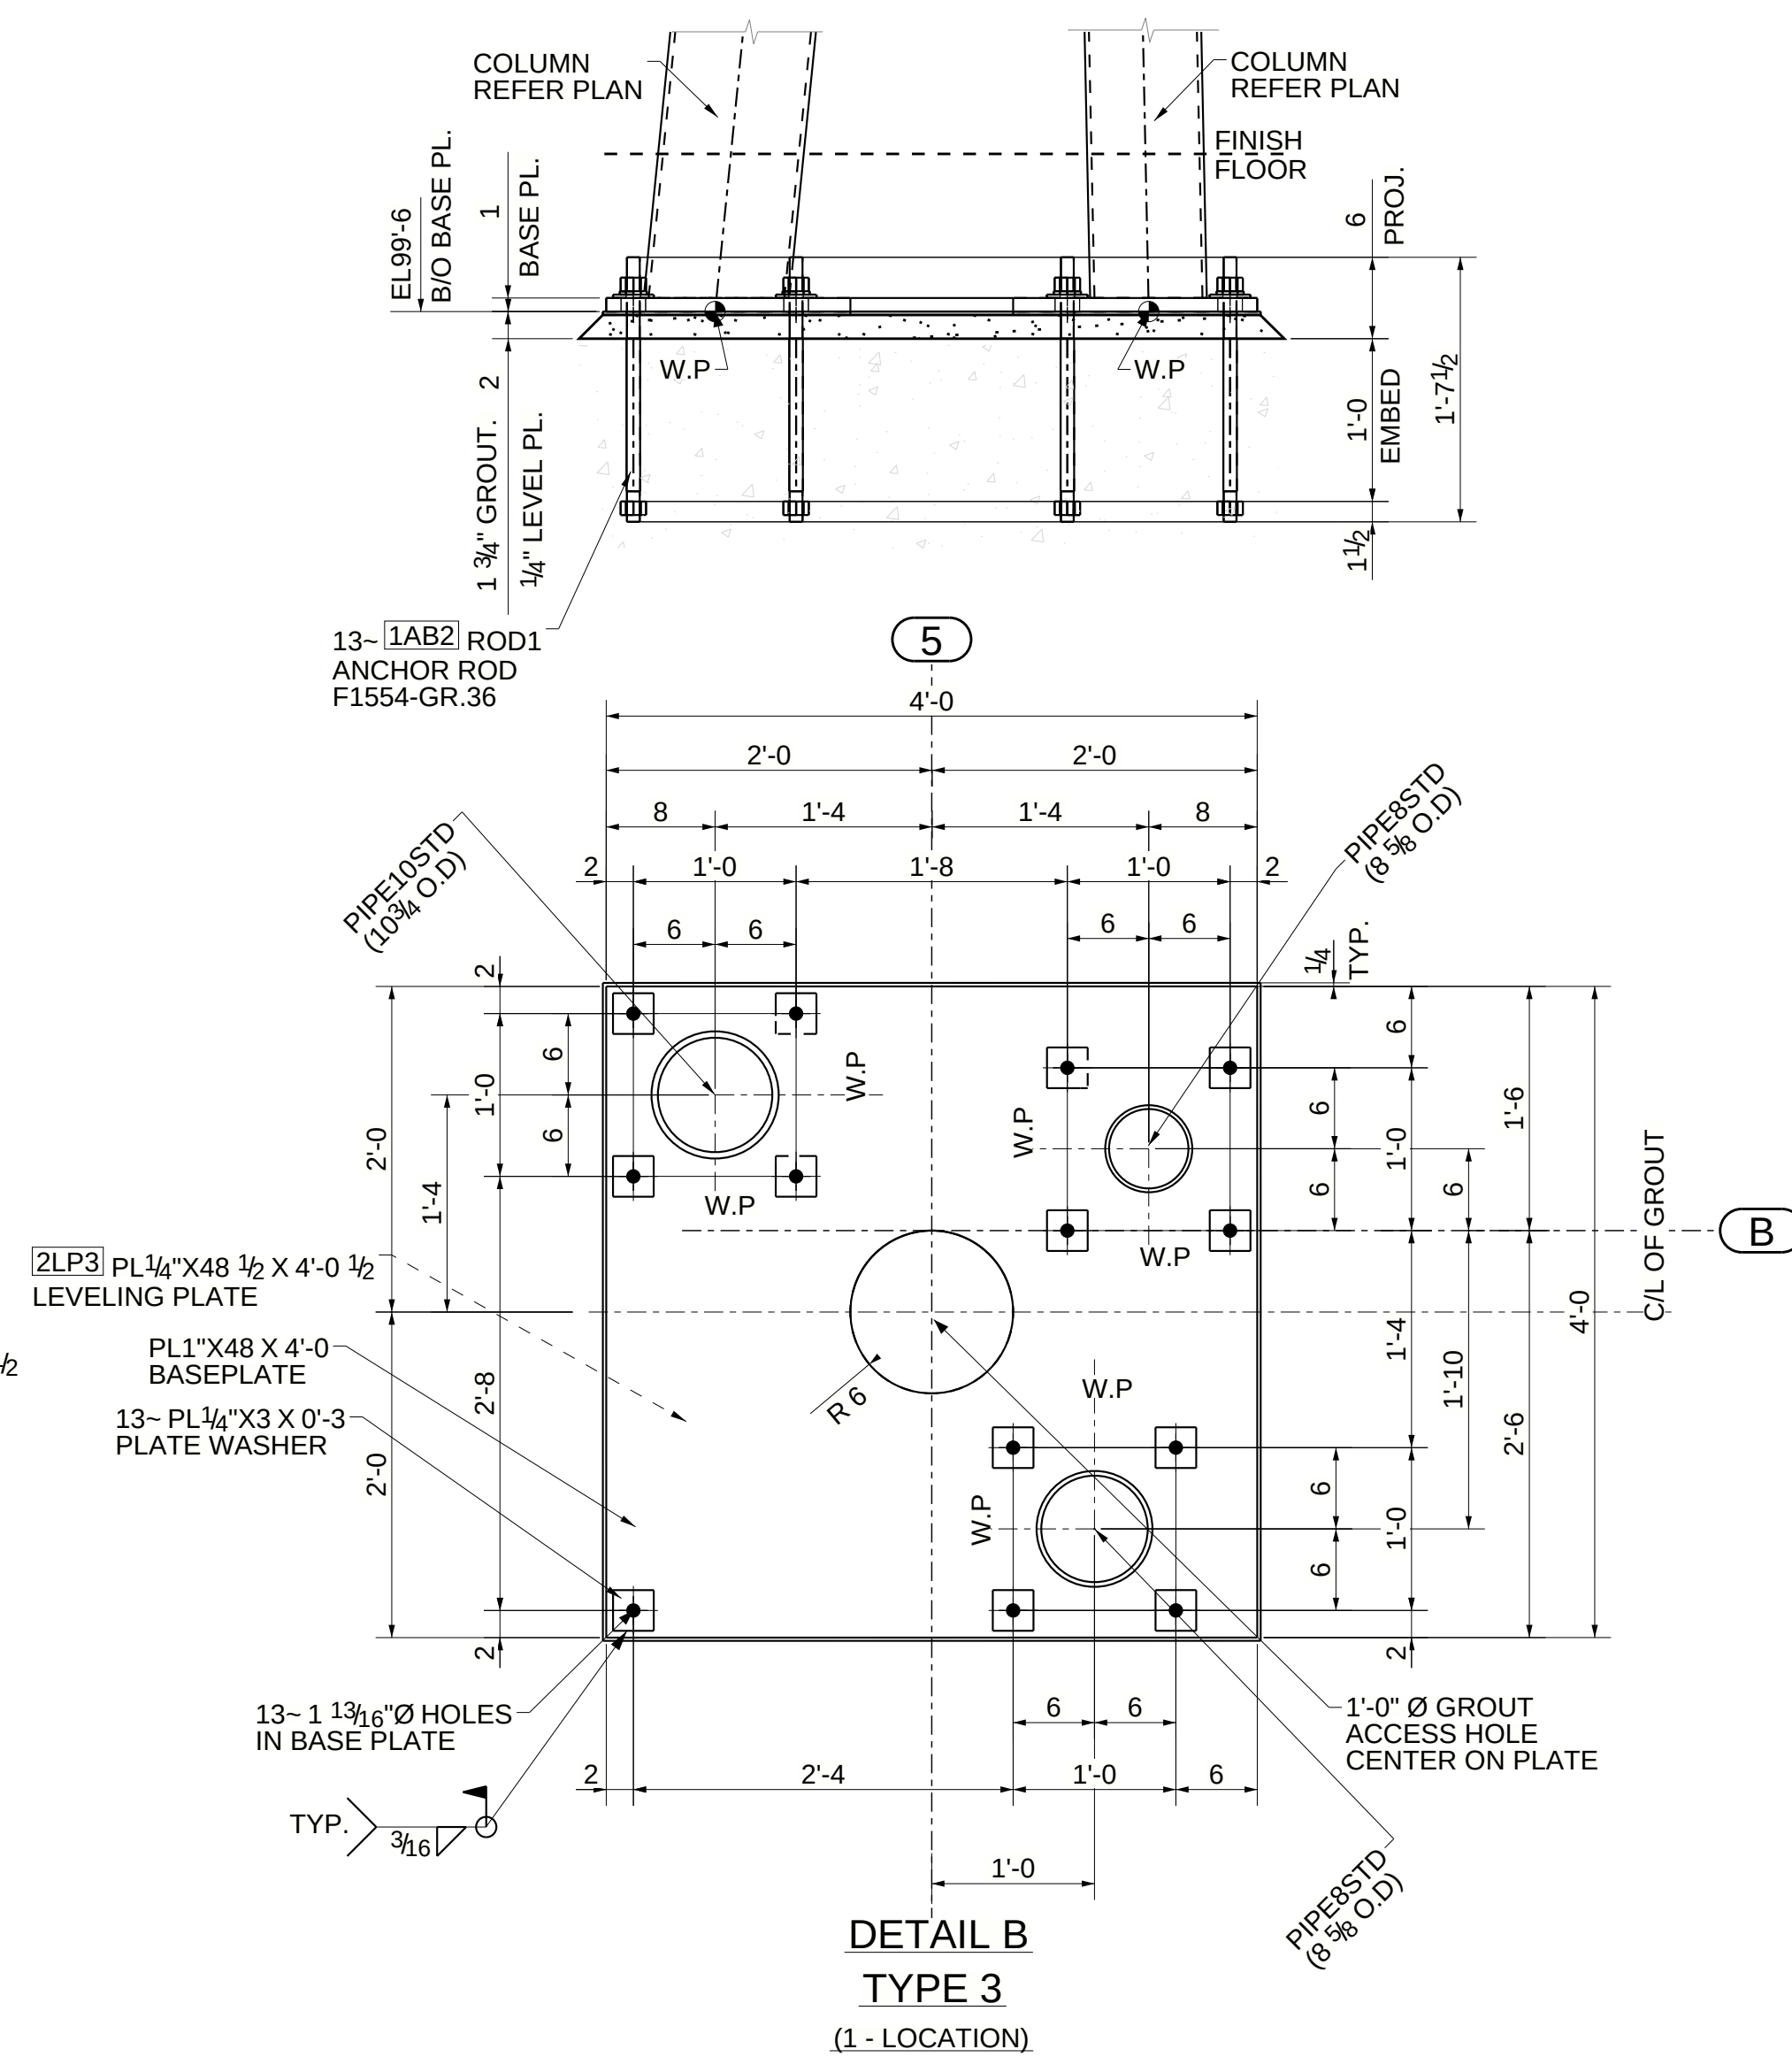

ALL ANCHOR RODS ARE "NO PAINT" AND LEVELLING
PLATES ARE " ONE SHOP COAT PRIMER" TYPICAL.

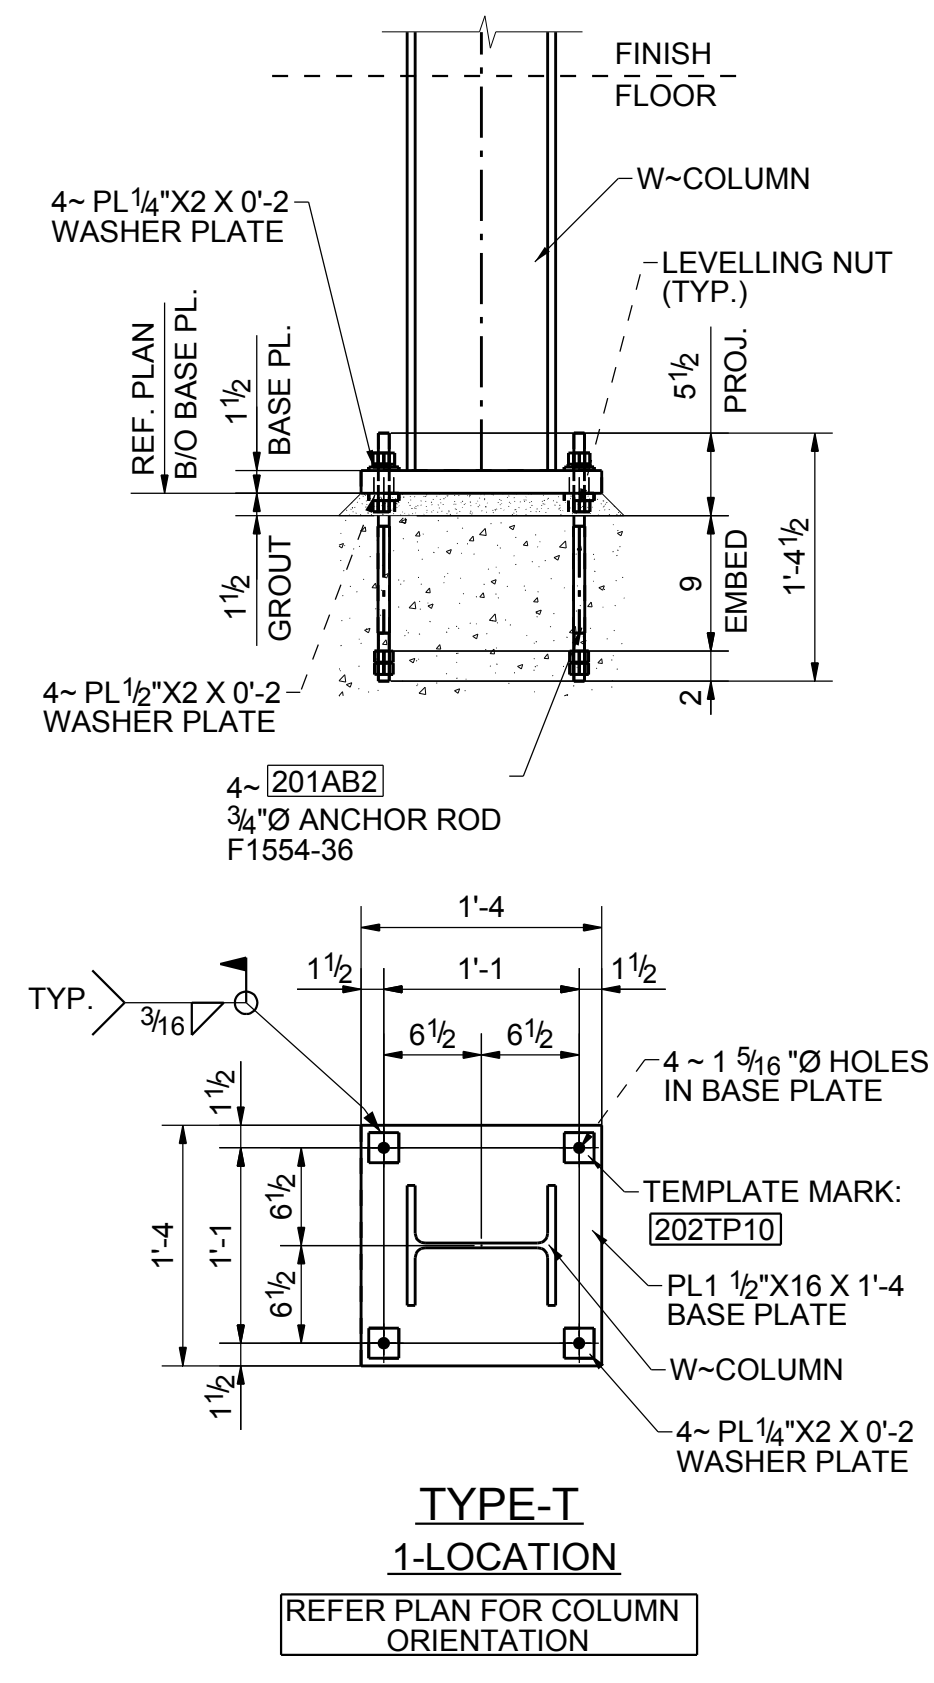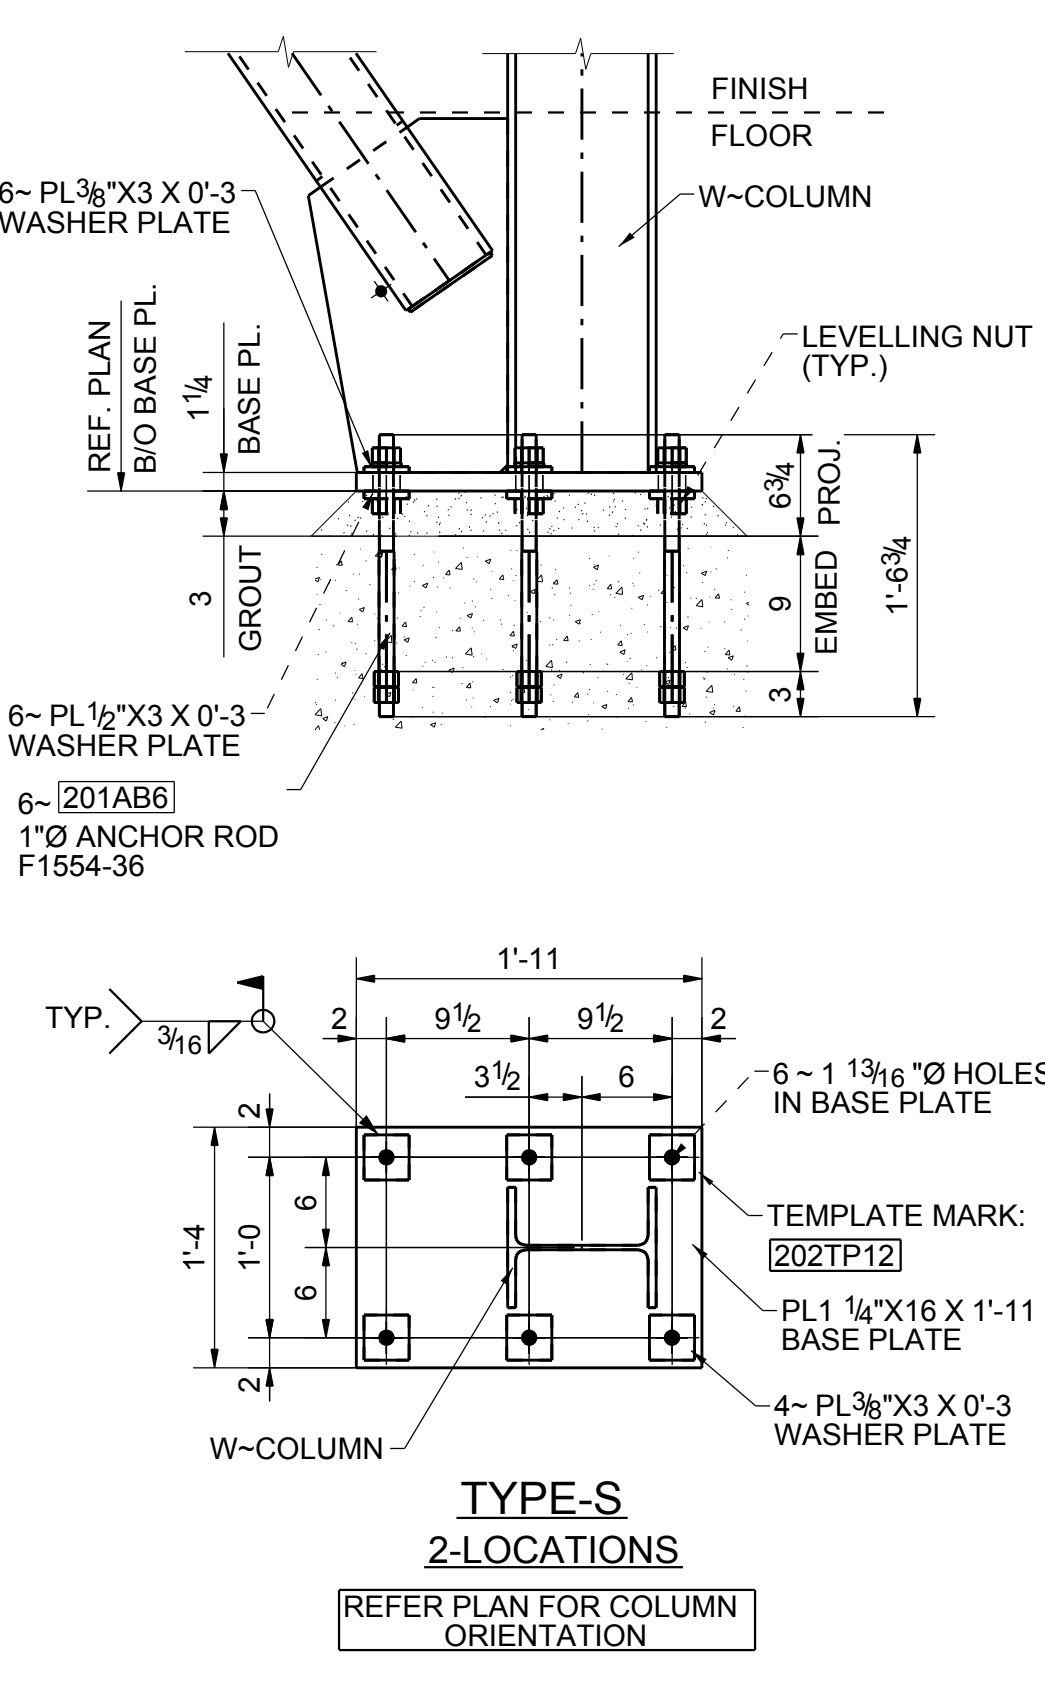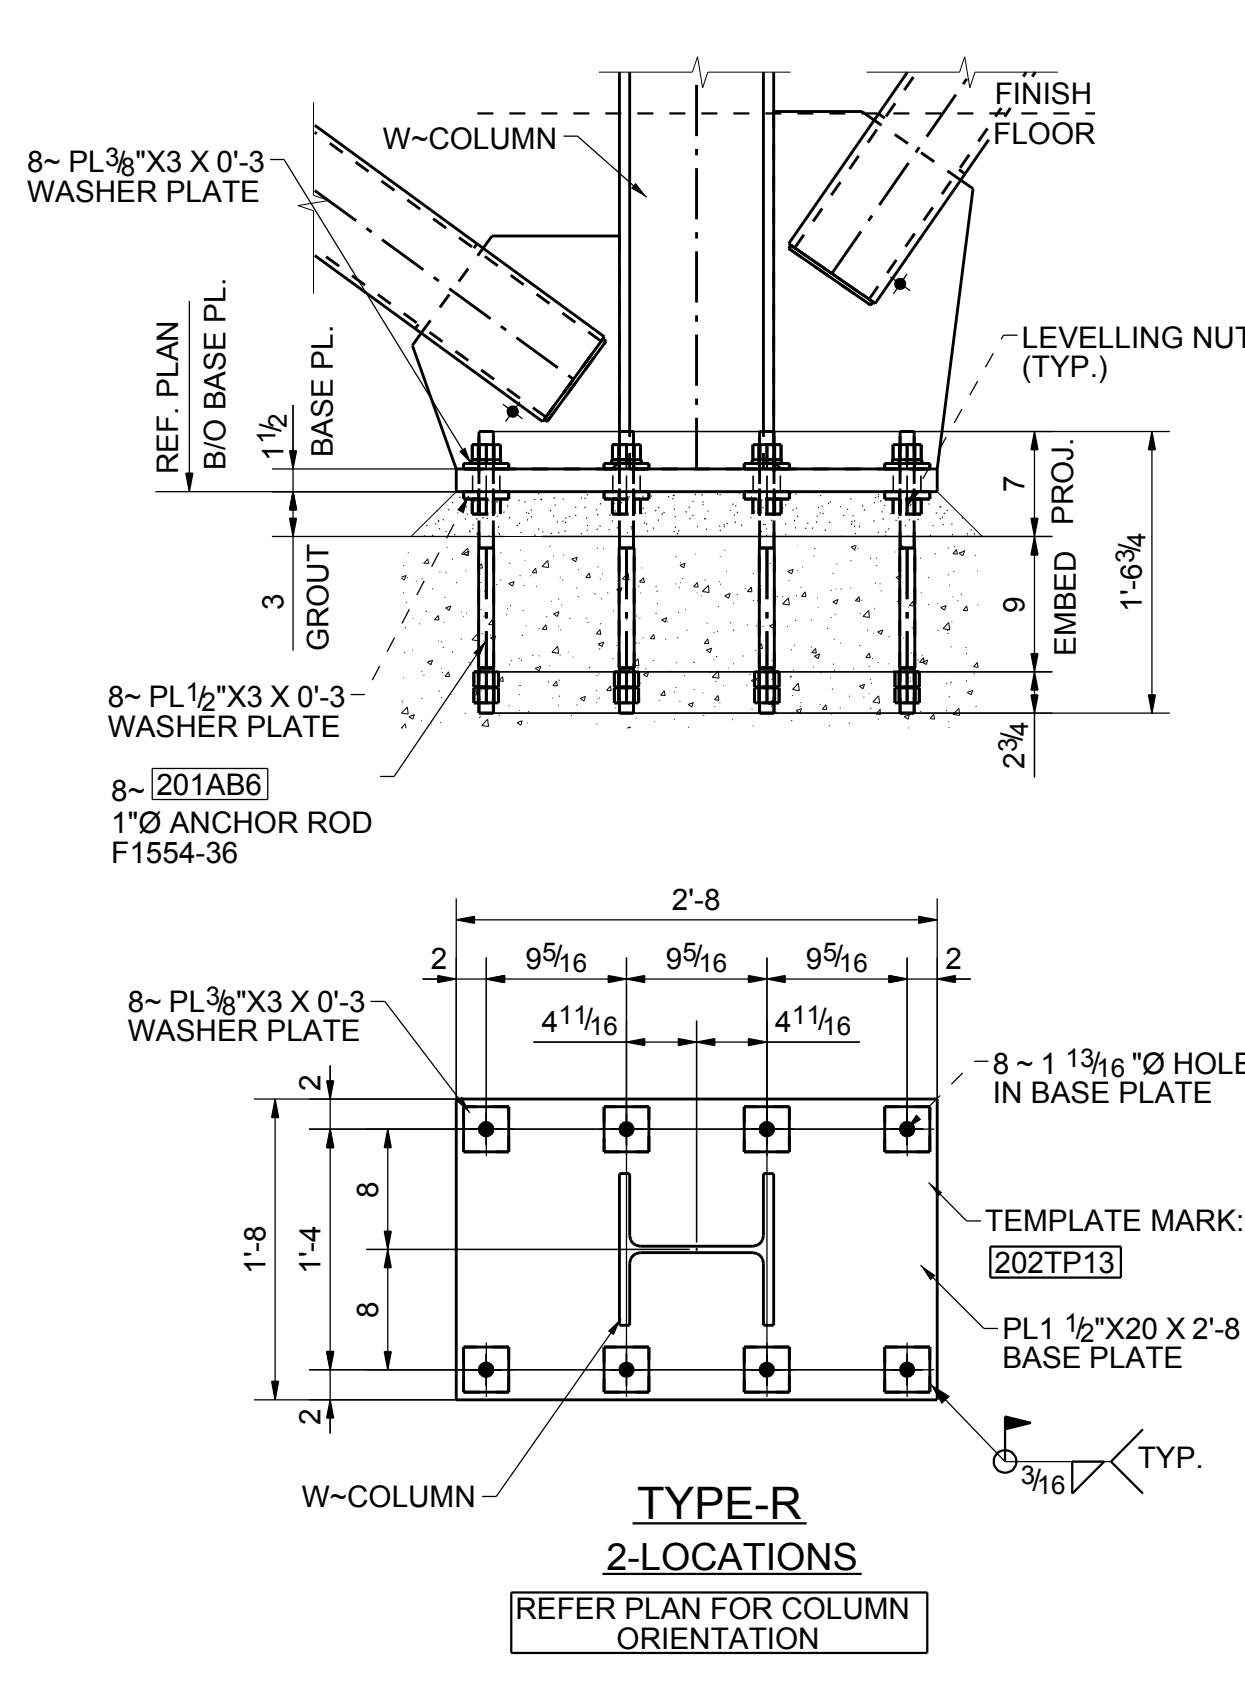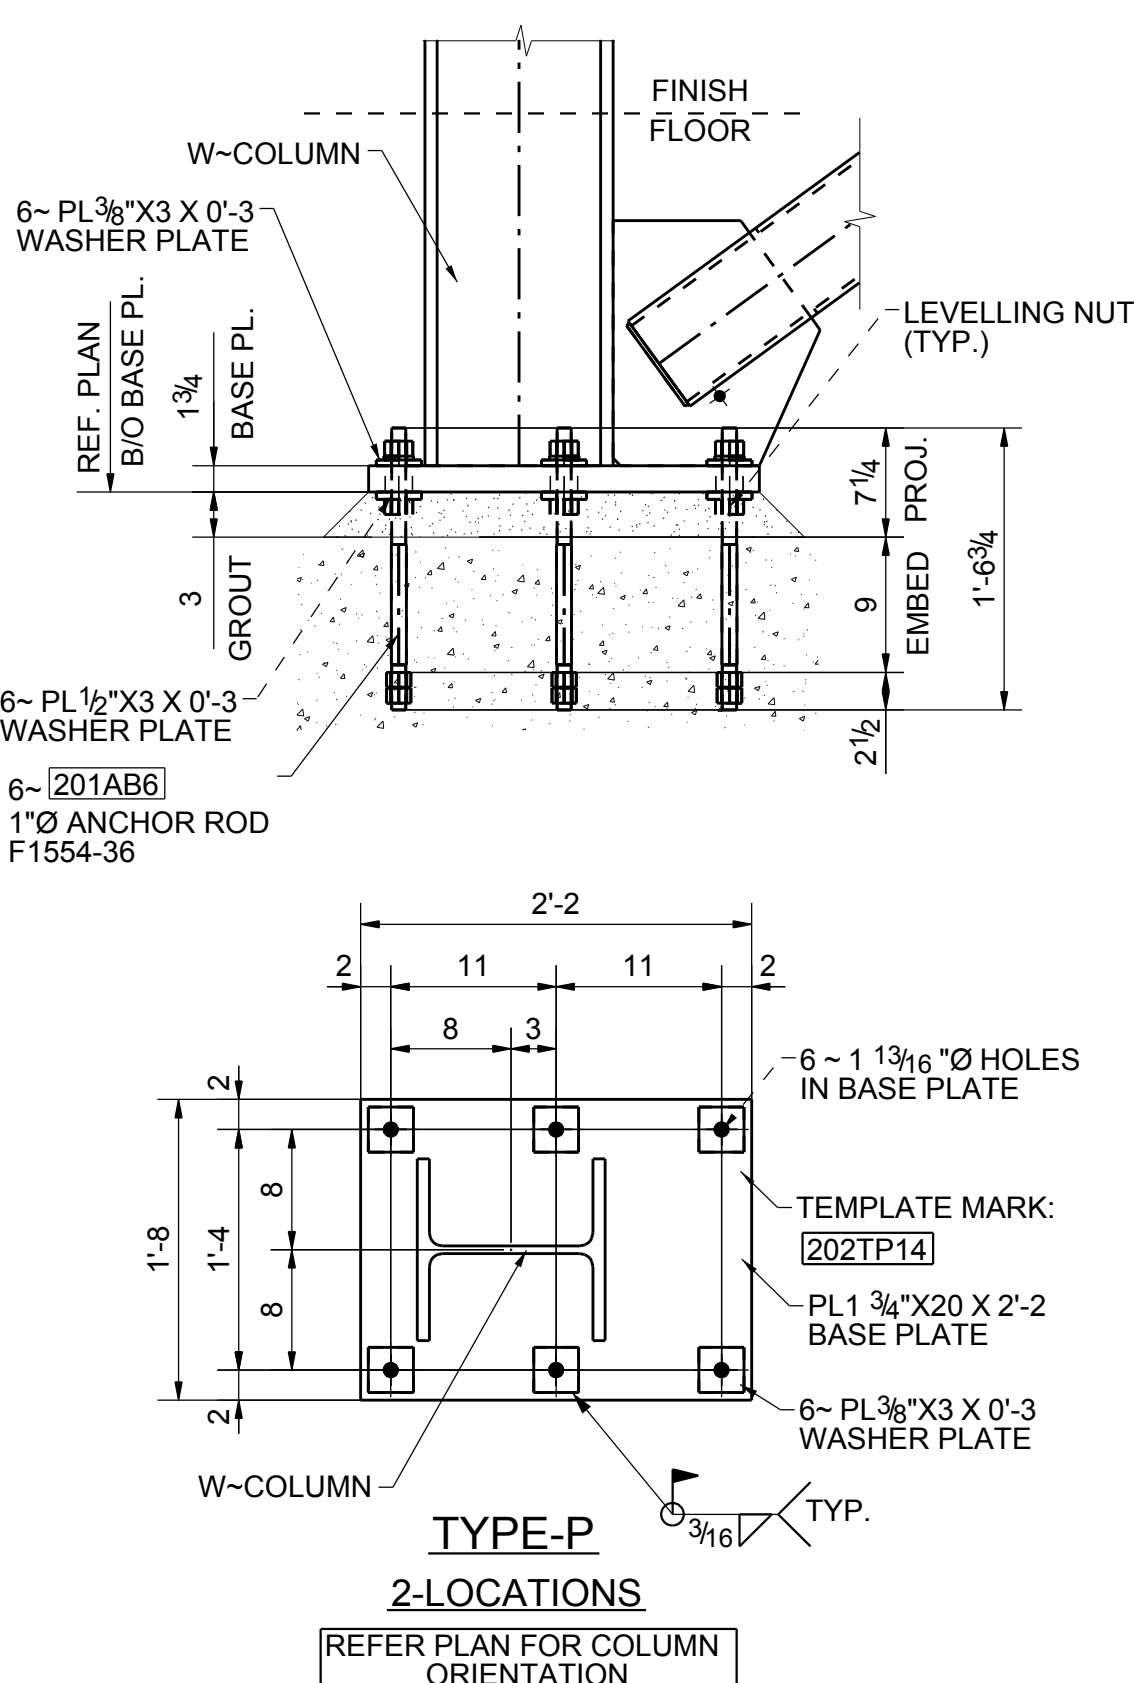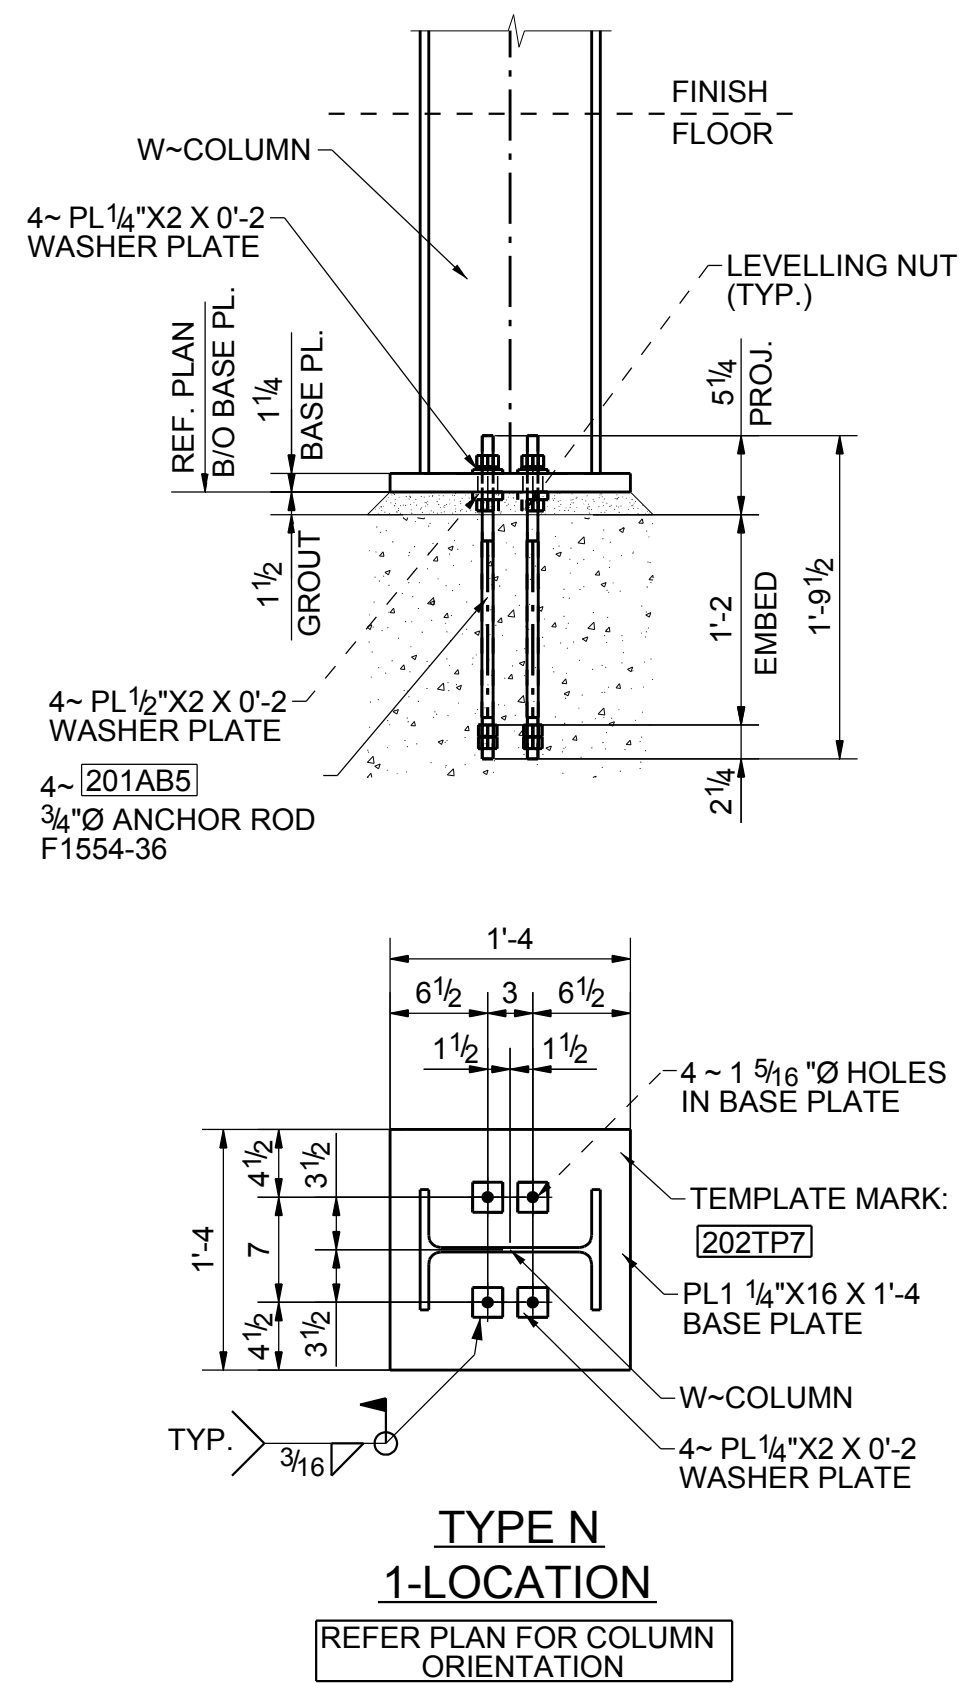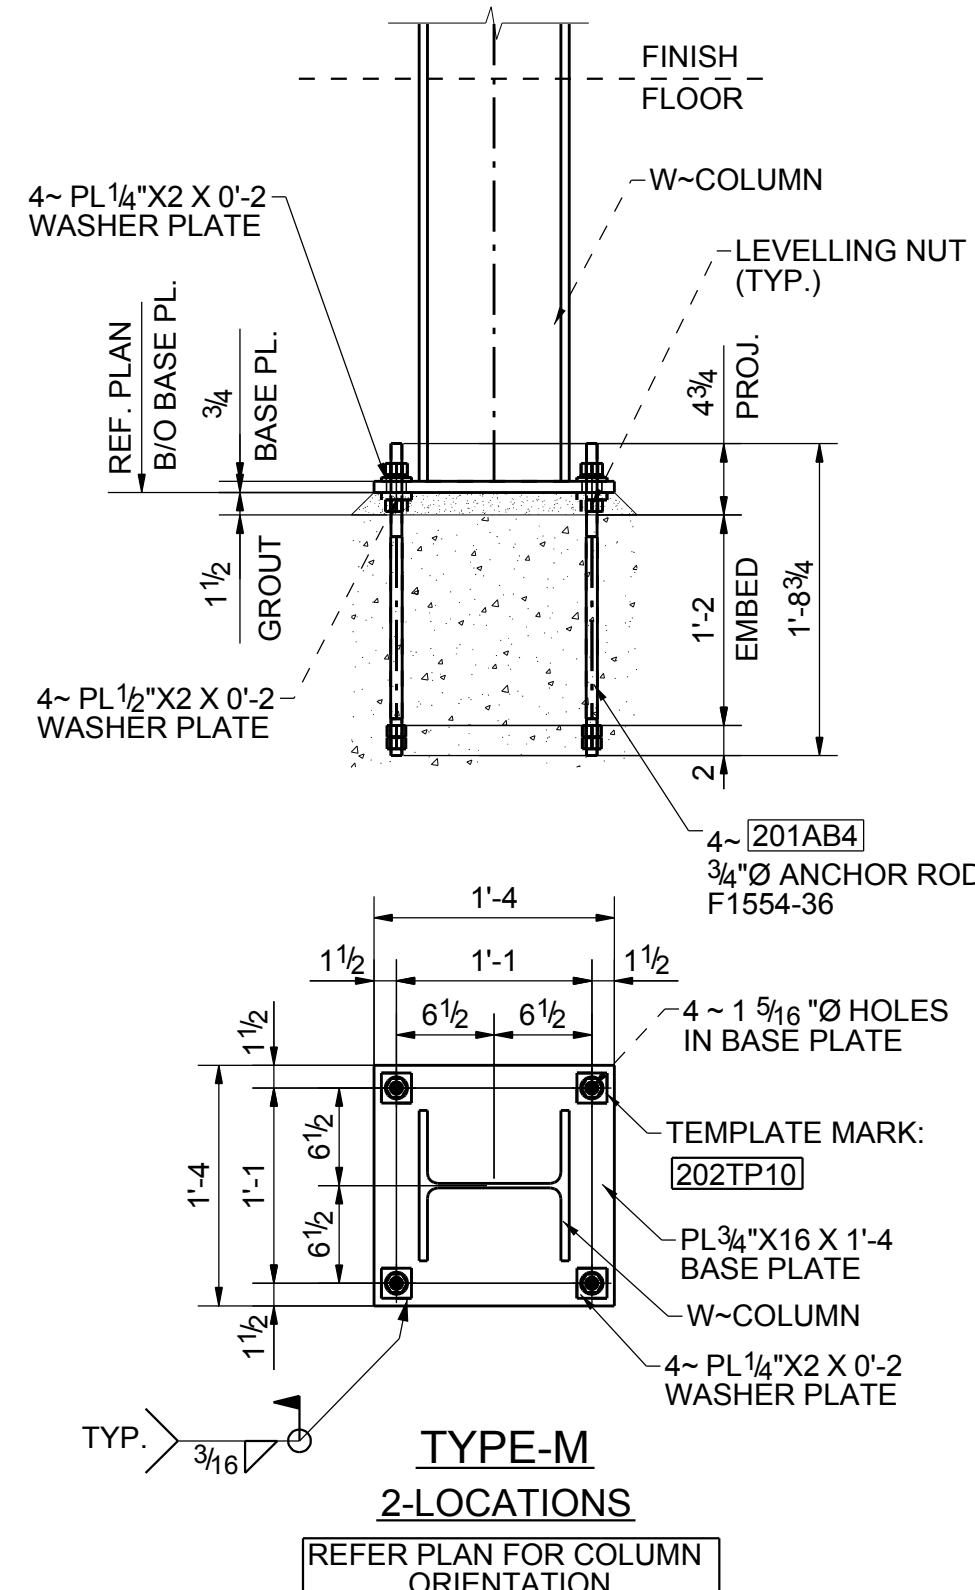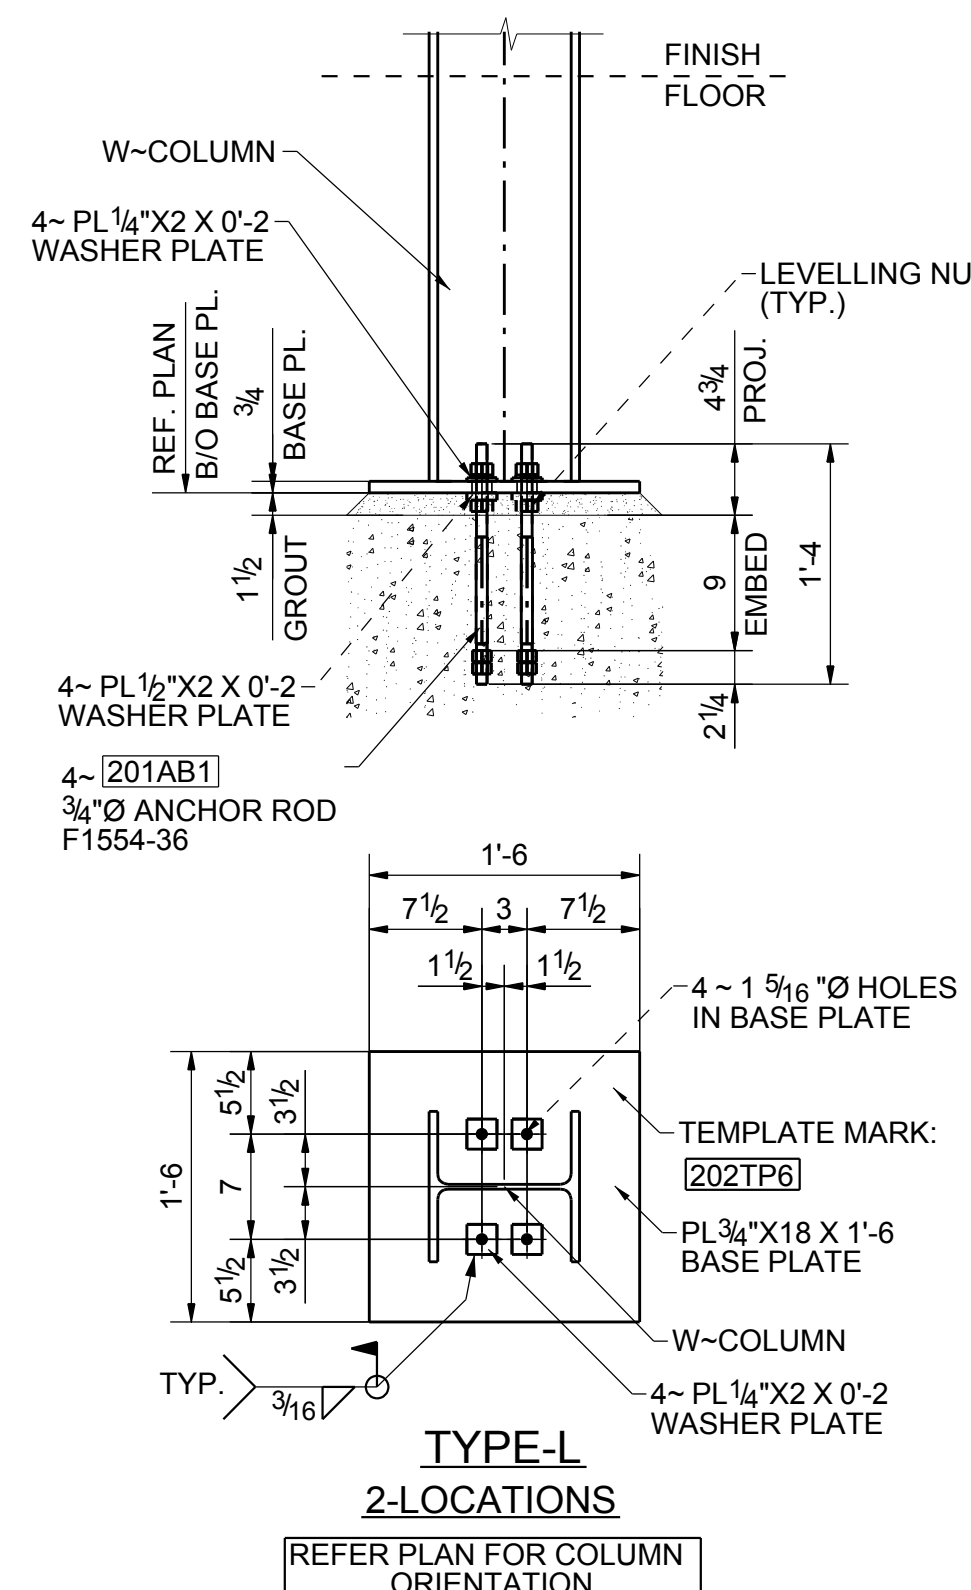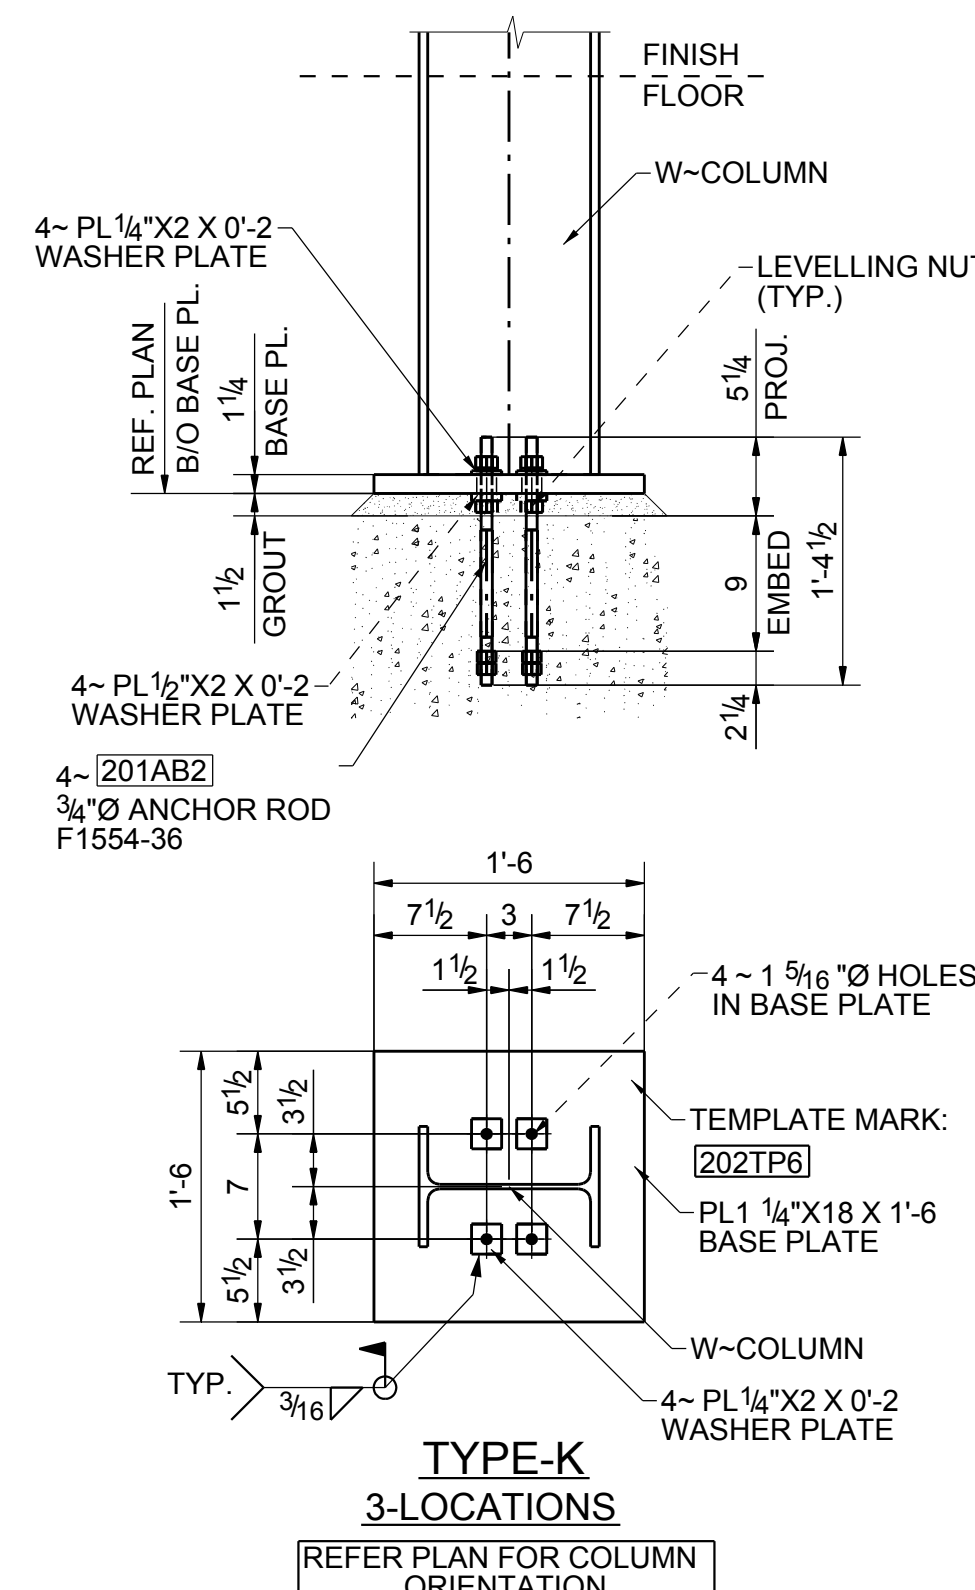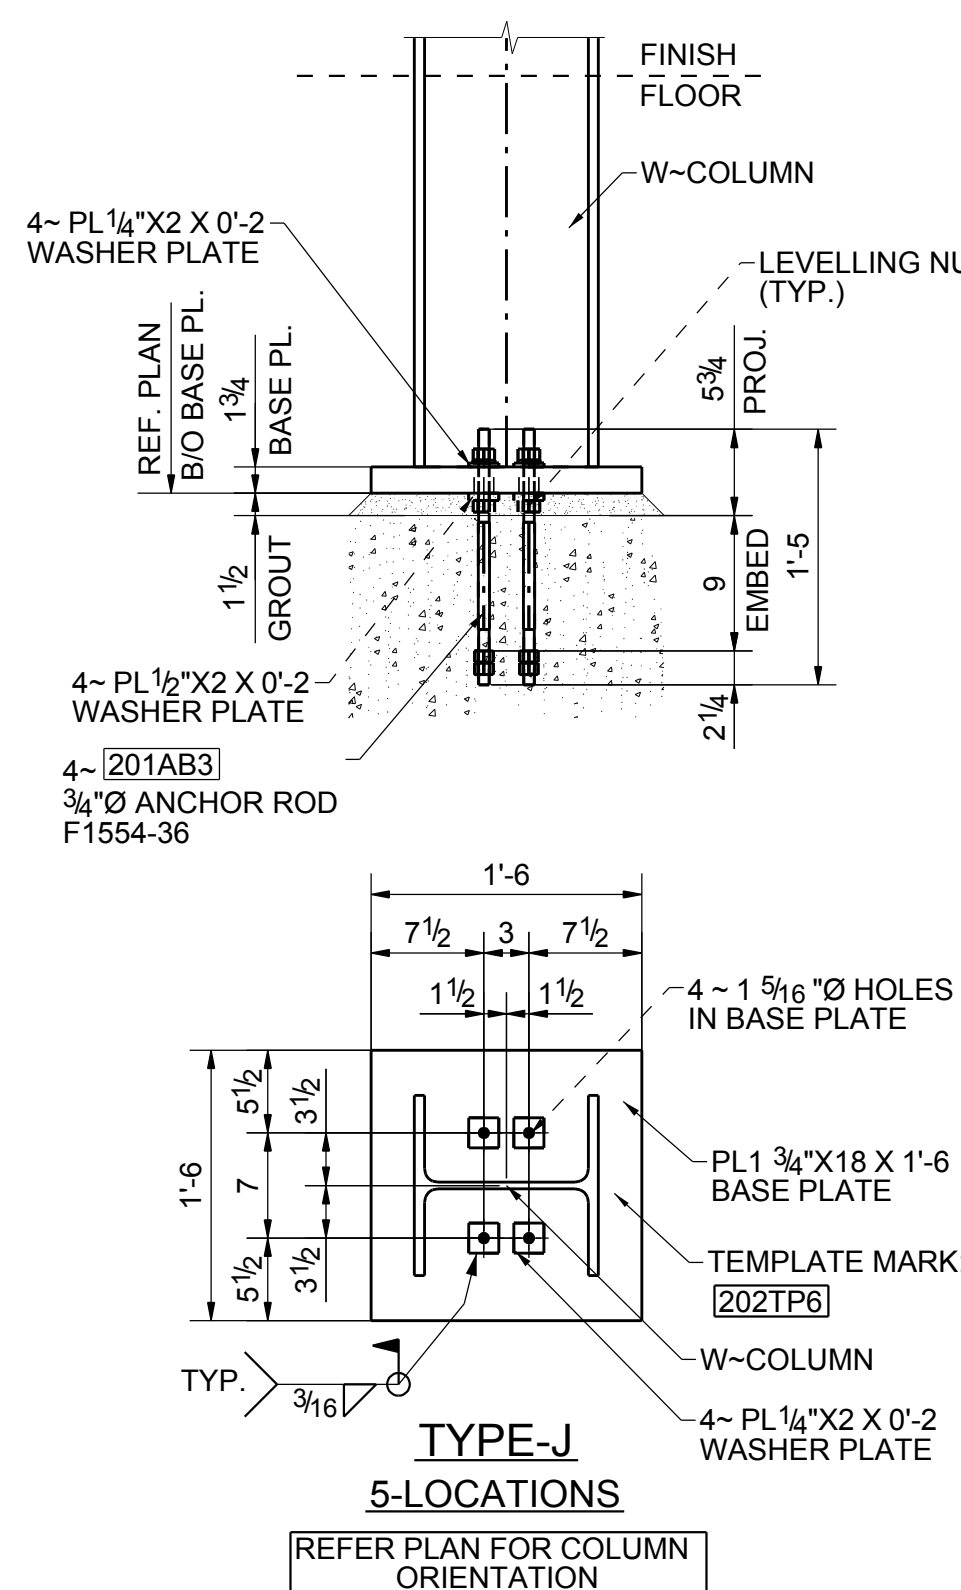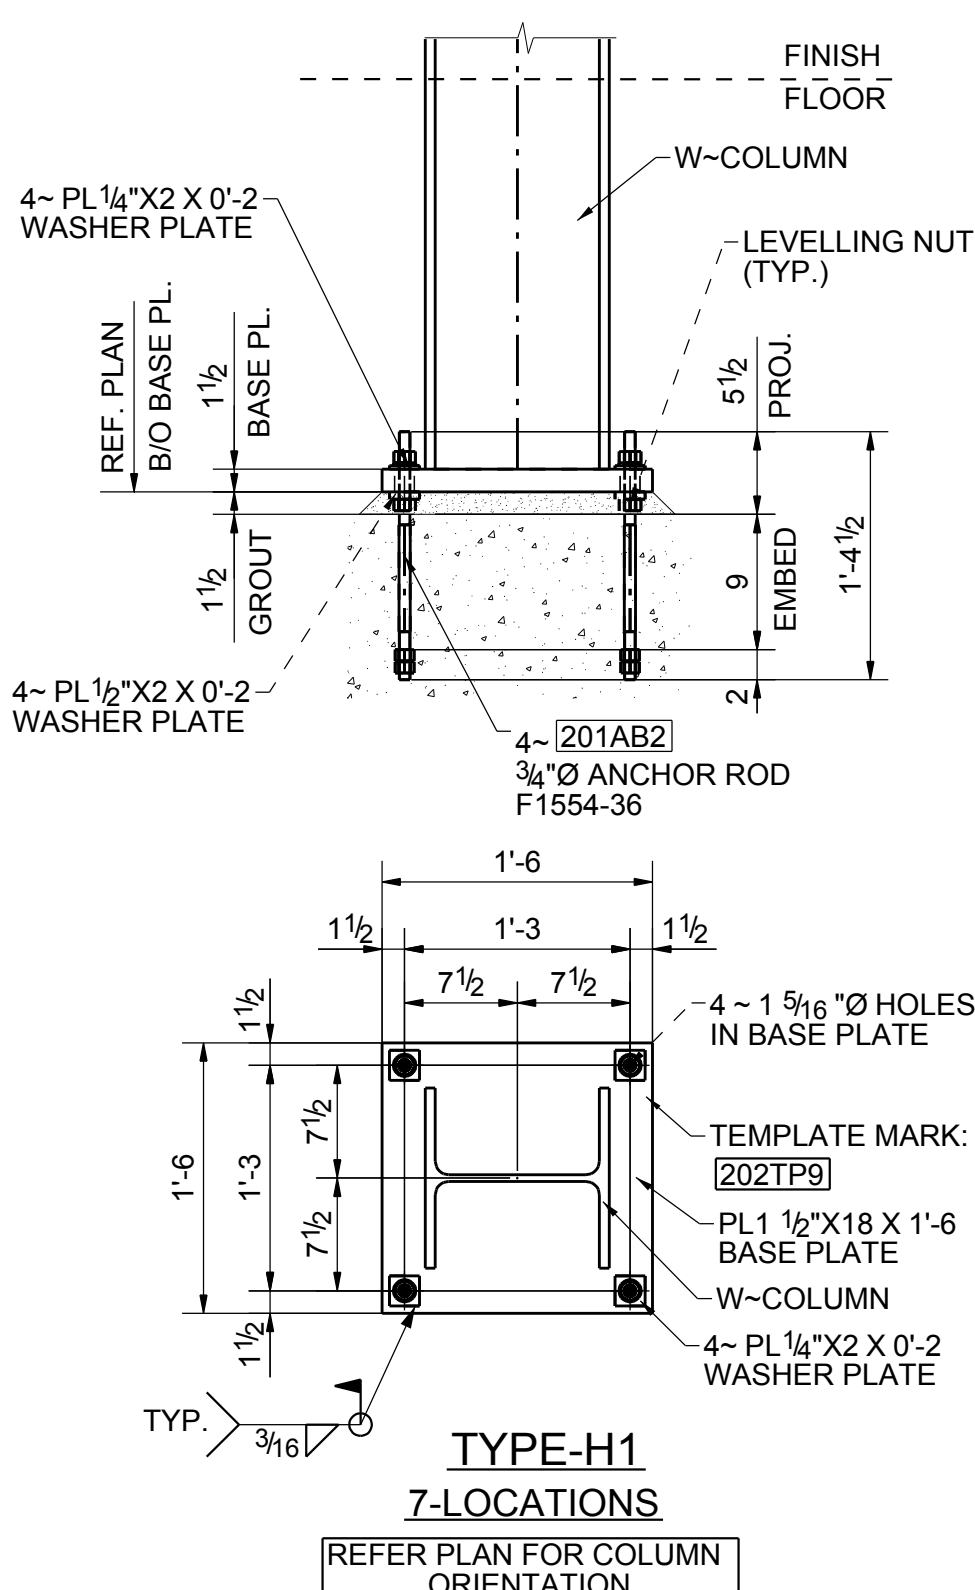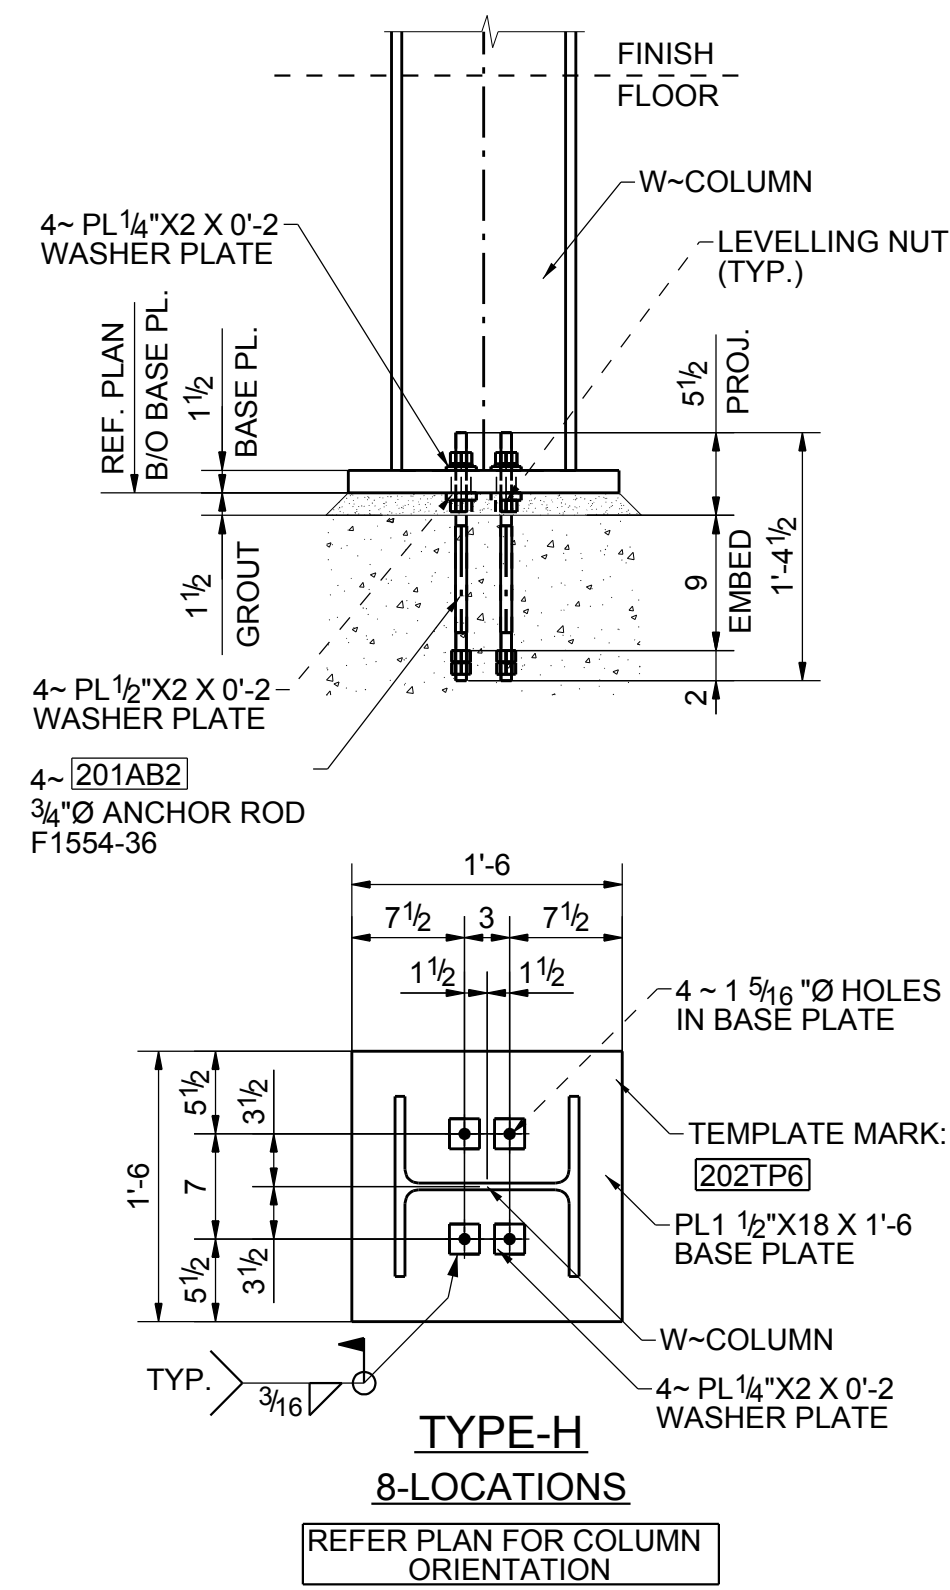

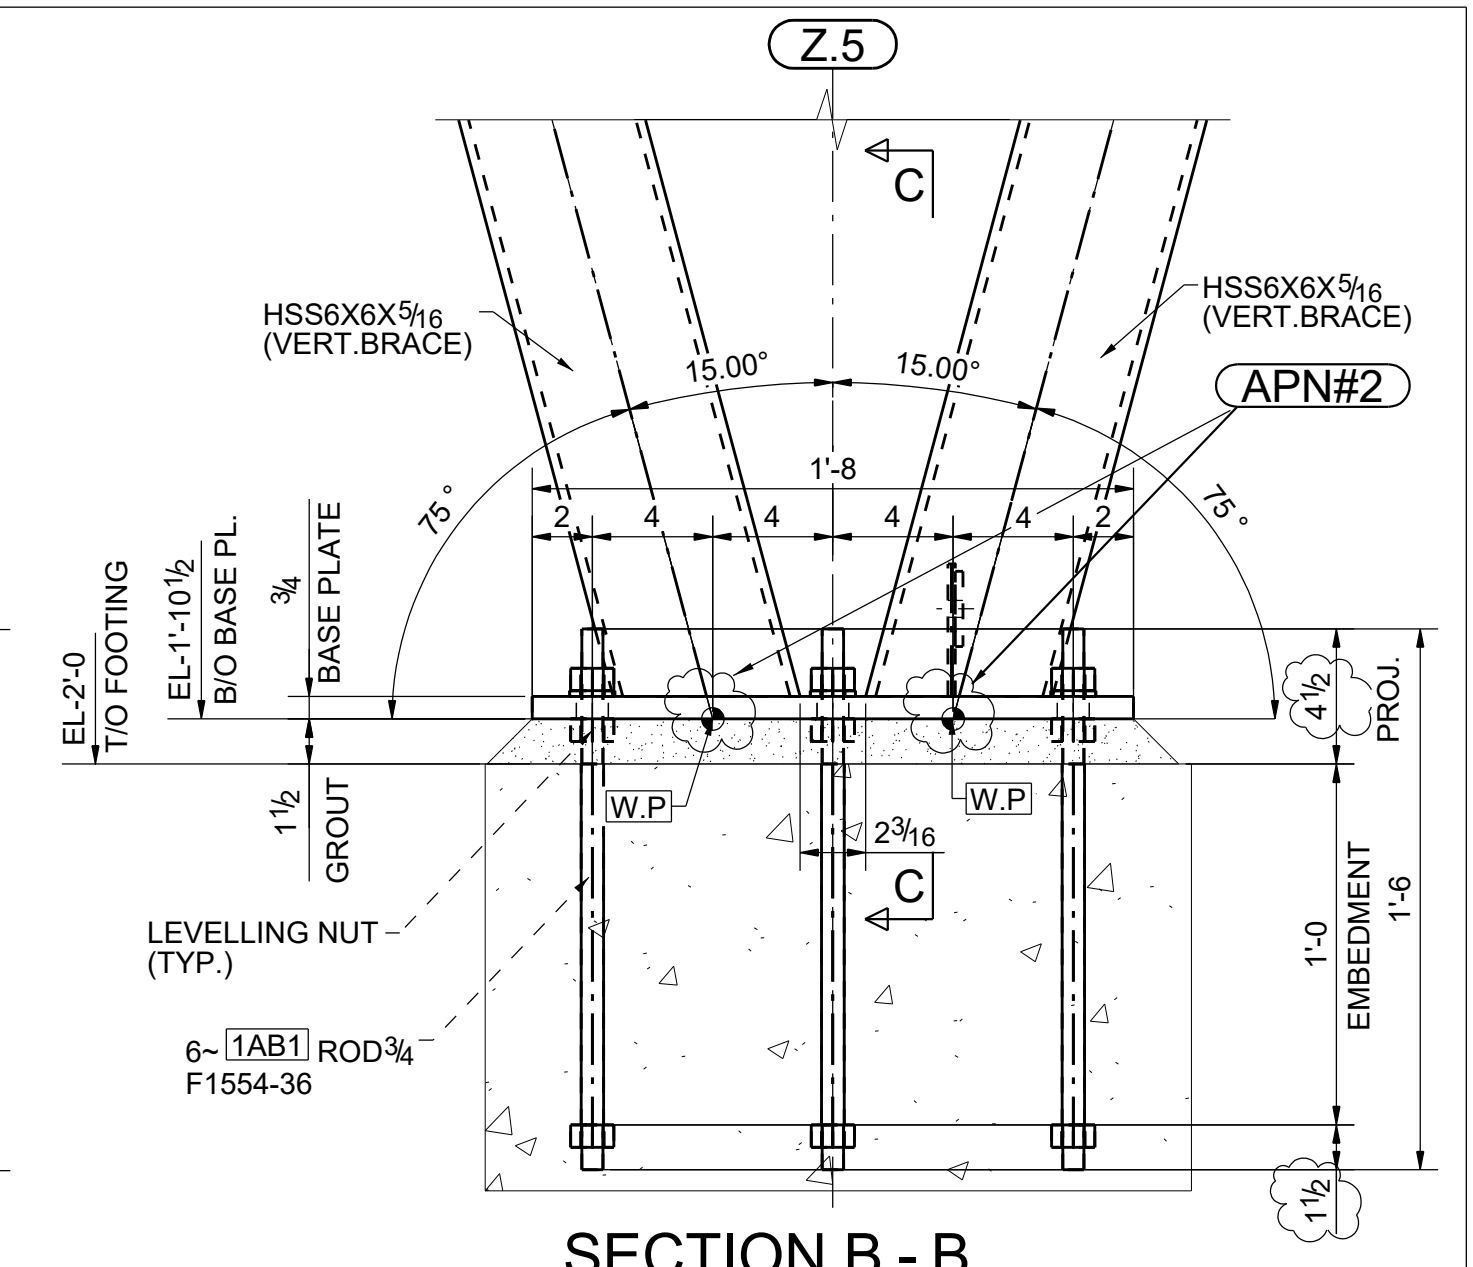

TYPE-5
(02-LOCATIONS)

REFER PLAN FOR COLUMN & BASEPLATE ORIENTATION.

Technical drawing of a base plate assembly for a vertical brace. The drawing shows a rectangular base plate with dimensions 1'-8" by 1'-0". It features two rectangular cutouts, each 10" by 8", and four circular holes with a diameter of 6-1 1/16". The plate is labeled "Z.5" and "APN#1". A vertical brace is attached to the plate, labeled "W" and "B". The brace has a 67.46° angle. The plate is made of PL 3/4" X 12 X 1'-8" and is labeled "BASE PLATE". The holes are labeled "HSS6X6X5/16 (VERT. BRACE)" and "6 ~ 1 1/16" Ø HOLE IN BASE PLATE". The plate is labeled "TEMPLATE MARK [1TP5]".

E.L.O.
FINISH FLOOR
T/O EMBED

1'-0"

1 1/2"

1 1/2"

C6X13
JAMB

L3X3X3/8" X 0'-3"

1/2"

4"

4"

8"

3EP1
EMBED 1"
PL 1/2" X 8"
W/ 2 - 3/4"
HEADED

CONCRETE
BLOCK

Technical drawing of a Type - 6 wall bracket. The drawing shows a side view of the bracket with dimensions in inches. The overall width is 8 inches, divided into two 4-inch sections. The overall height is 8 inches, divided into two 4-inch sections. The bracket is made of 3/16 inch thick plate. The mounting holes are 3/16 inch in diameter. The bracket is labeled with dimensions and components: 3, 5, 1 1/2, 5, 3, 1 1/2, 4, 4, 8, 1 1/2, 2 1/2, 2 1/2, 5, 3, 8, 3/16, 3 SIDES TYP., C6X13 JAMB, 3EP1, EMBED PLATE PL 1/2"X8 X 0'-8 W/ 2 - 3/8" Ø X 0'-4 HEADED STUDS.

APN#2 APPROVER VERIFY WORKPOINT OF HSS-BRACE PROVIDED TO BOTTOM OF BASEPLATE, IS THAT REQUIRED TO CHANGE THE WORKPOINT TO TOP OF BASEPLATE TYPICAL.