




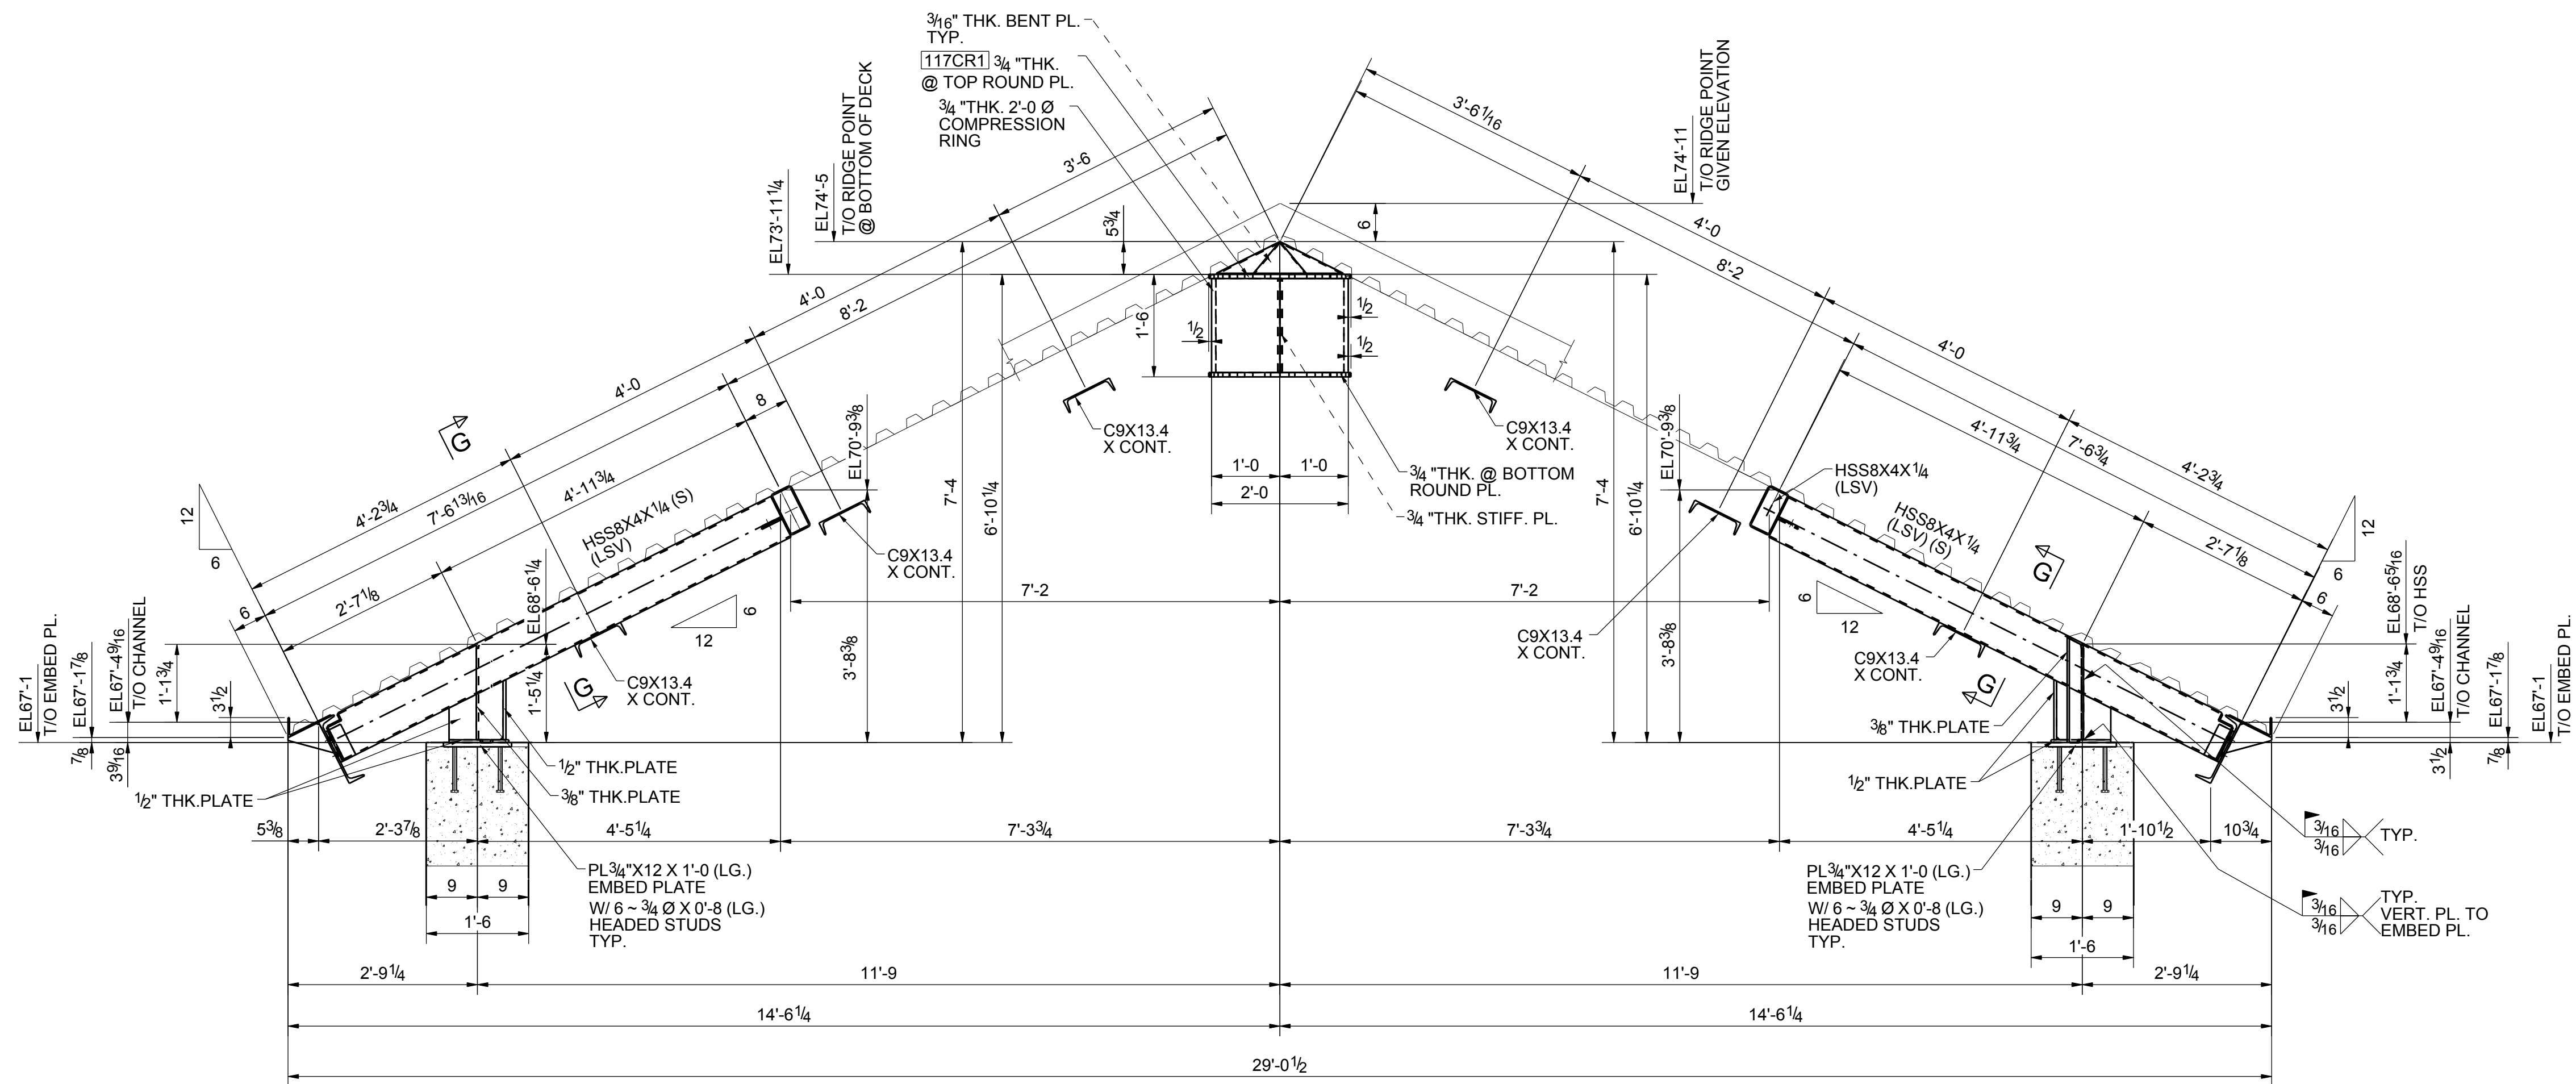


SECTION 7 - 7
1-E103

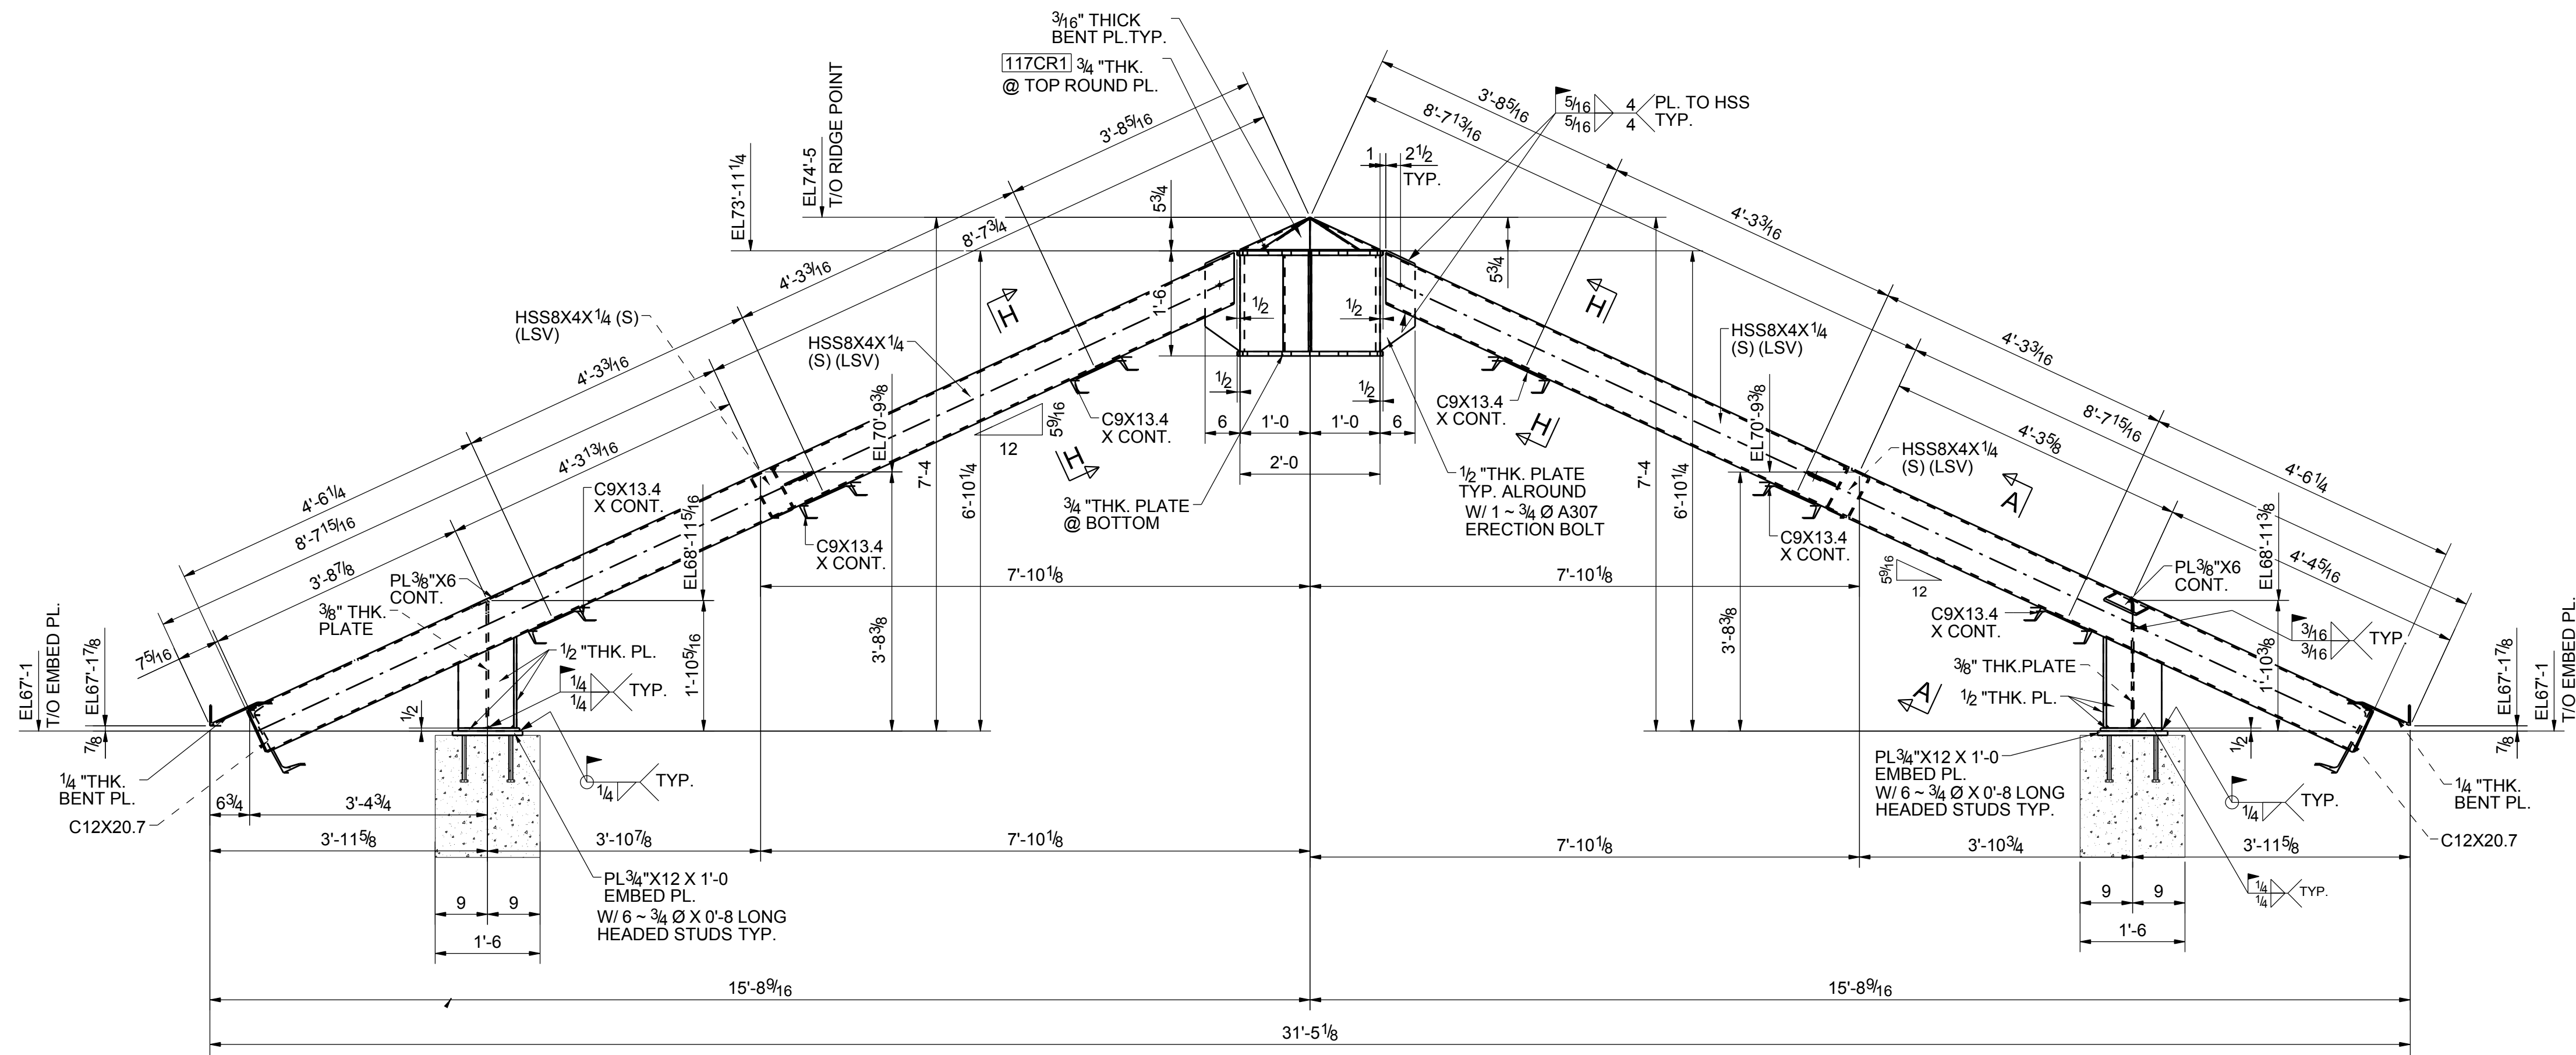


SECTION 8 - 8
1-E103

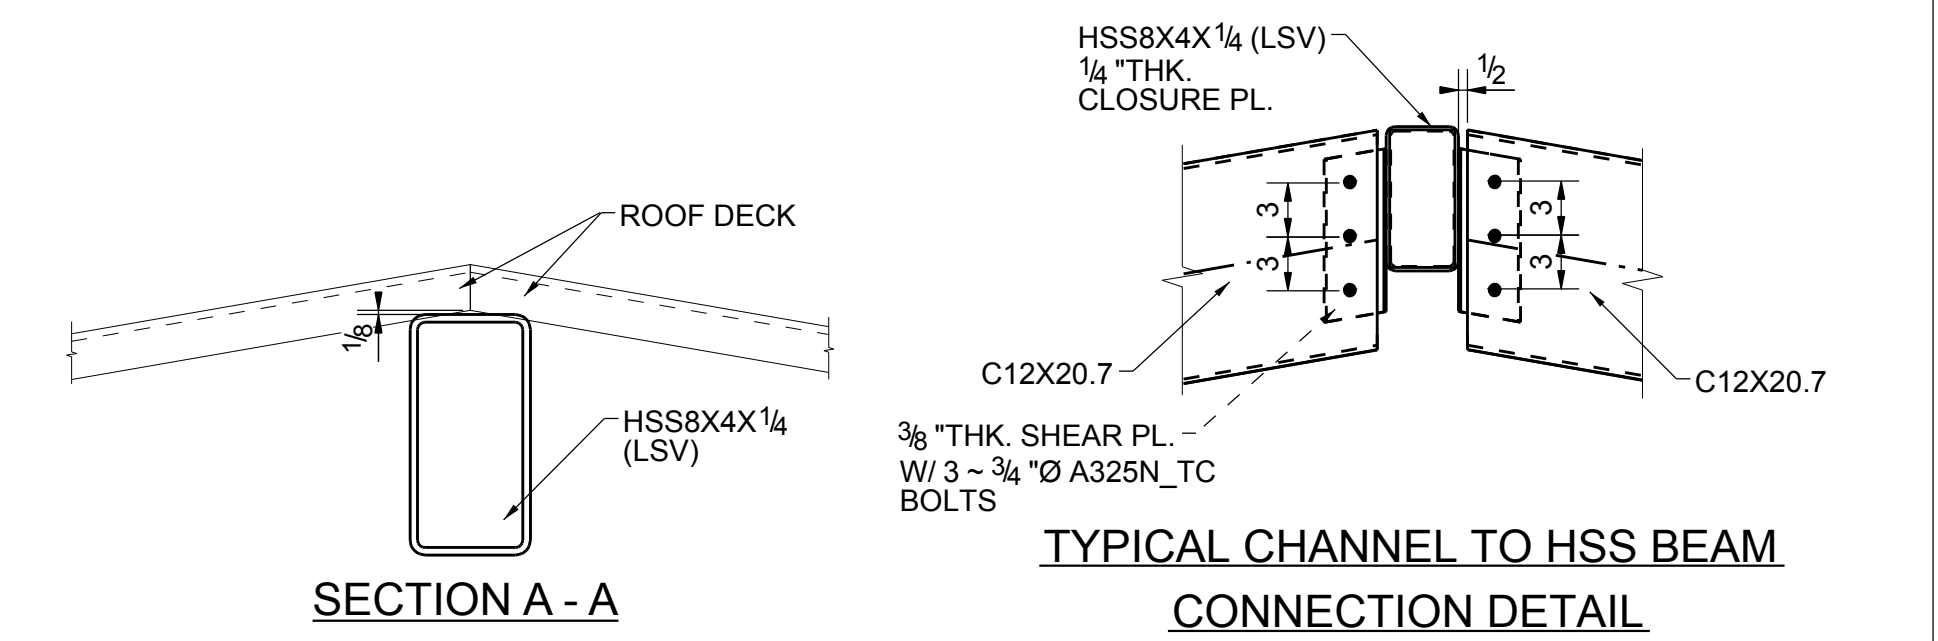


SECTION A - A

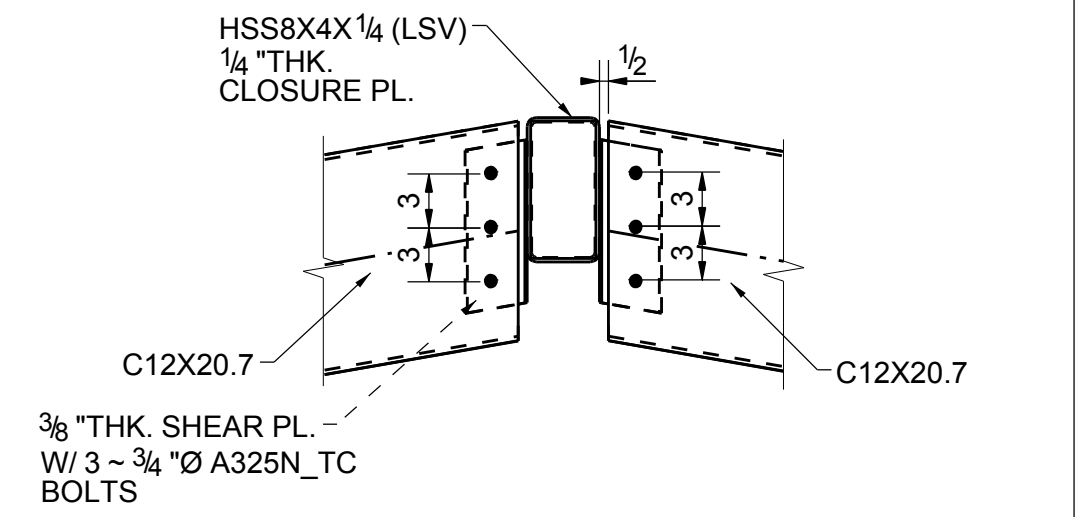


TYPICAL CHANNEL TO HSS BEAM
CONNECTION DETAIL

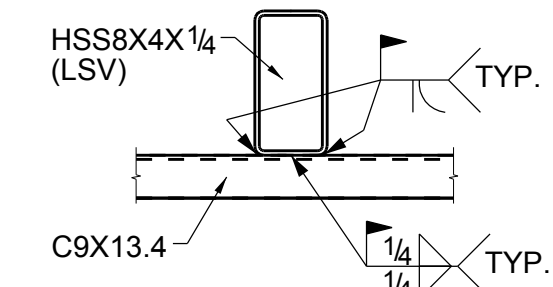


SECTION G - G

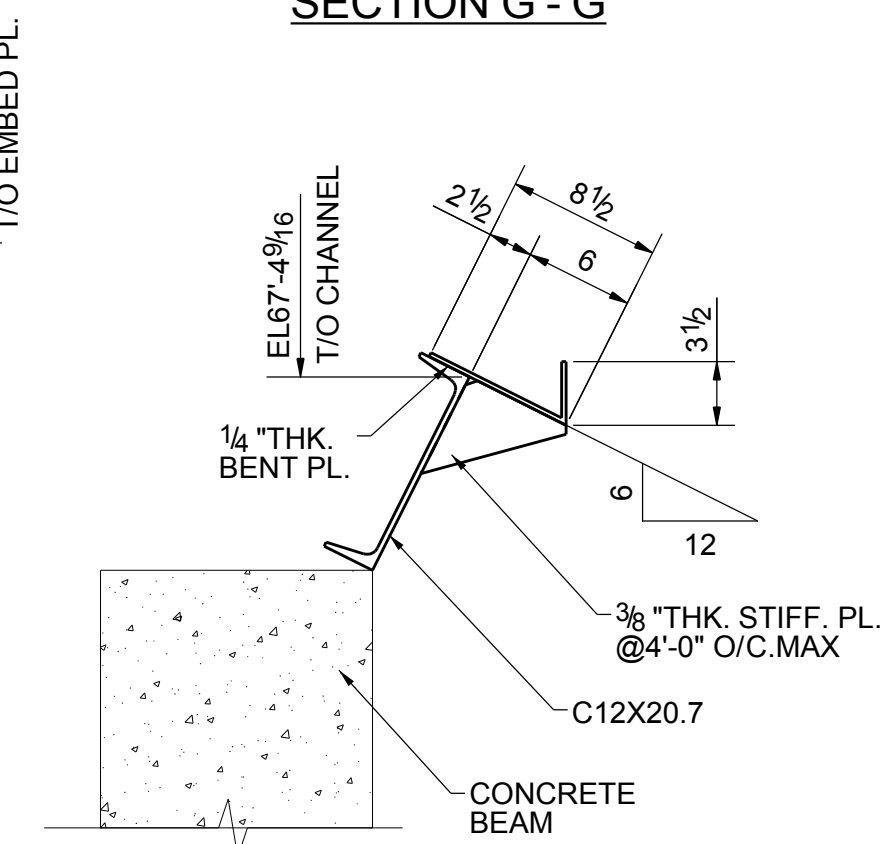

SECTION 9 - 9
1-E103

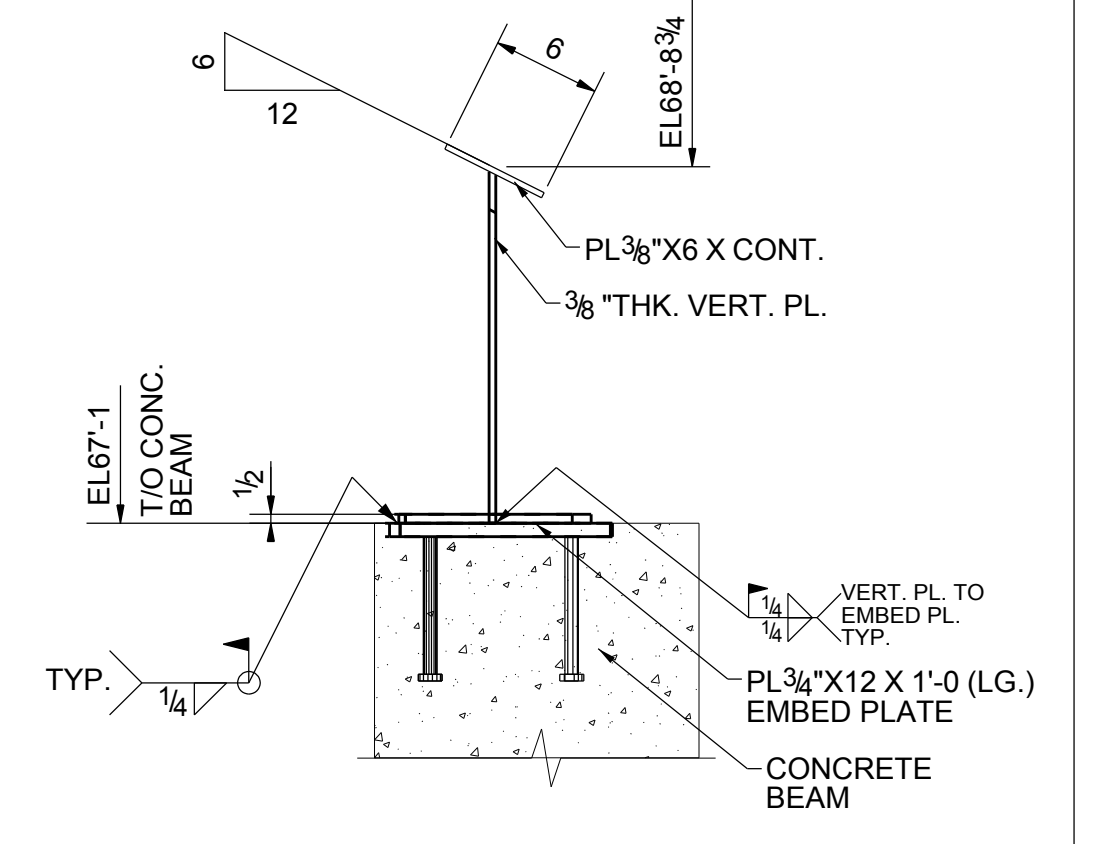



SECTION 10 - 10
1-E103

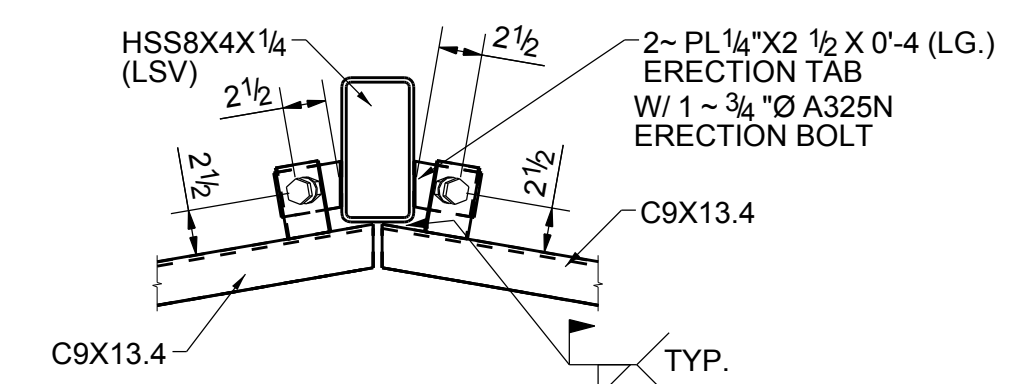




SECTION H - H

NOTES:-


1. REFER 1-E100 SHEET FOR ALL GENERAL NOTES.

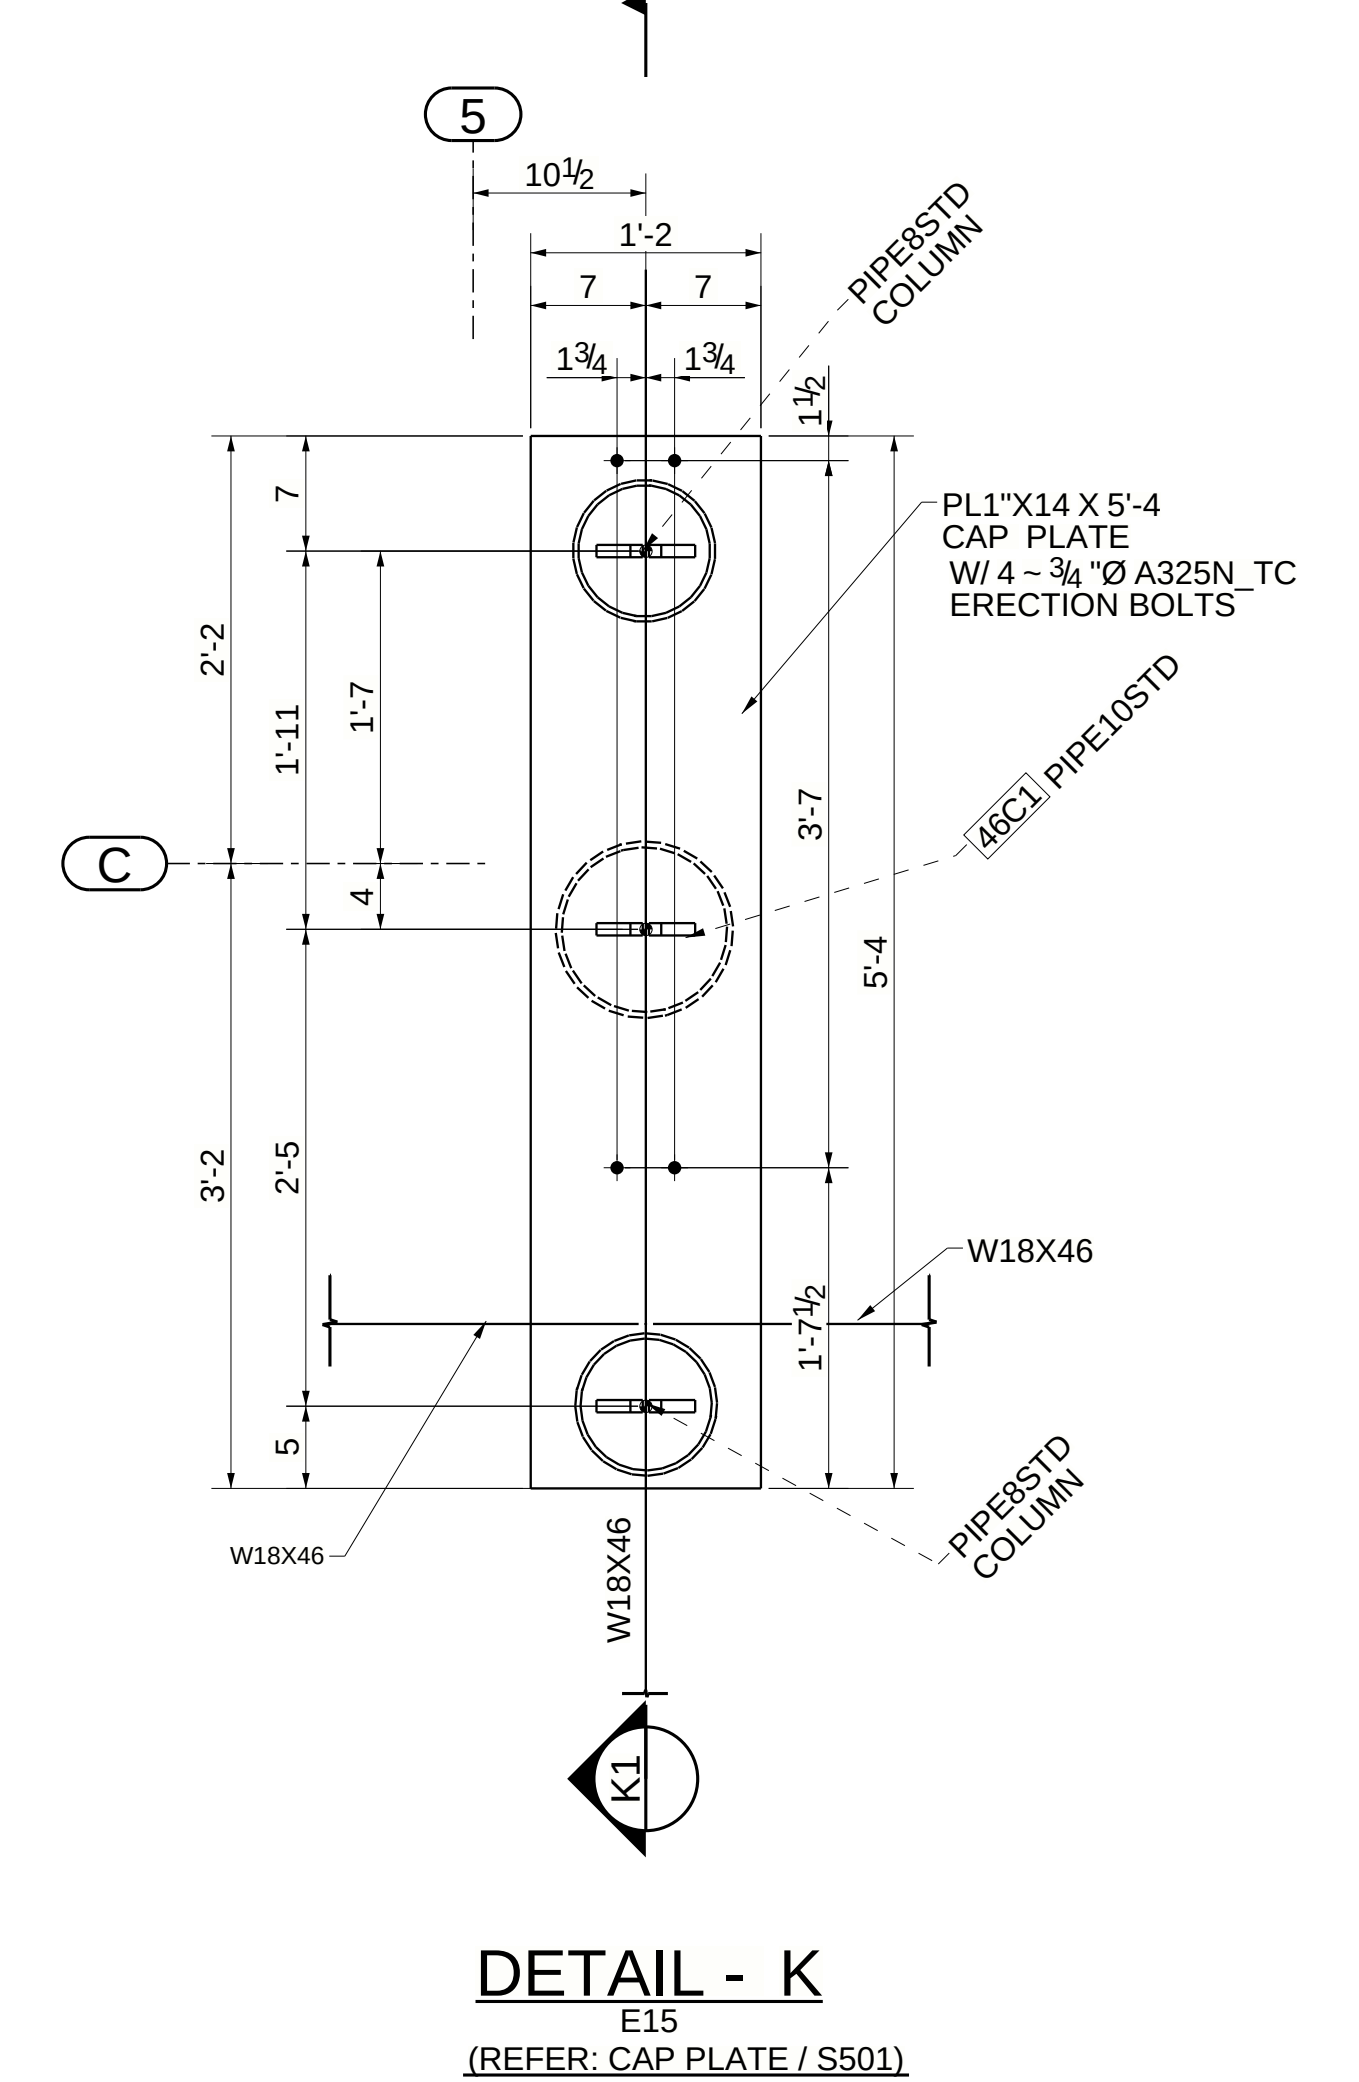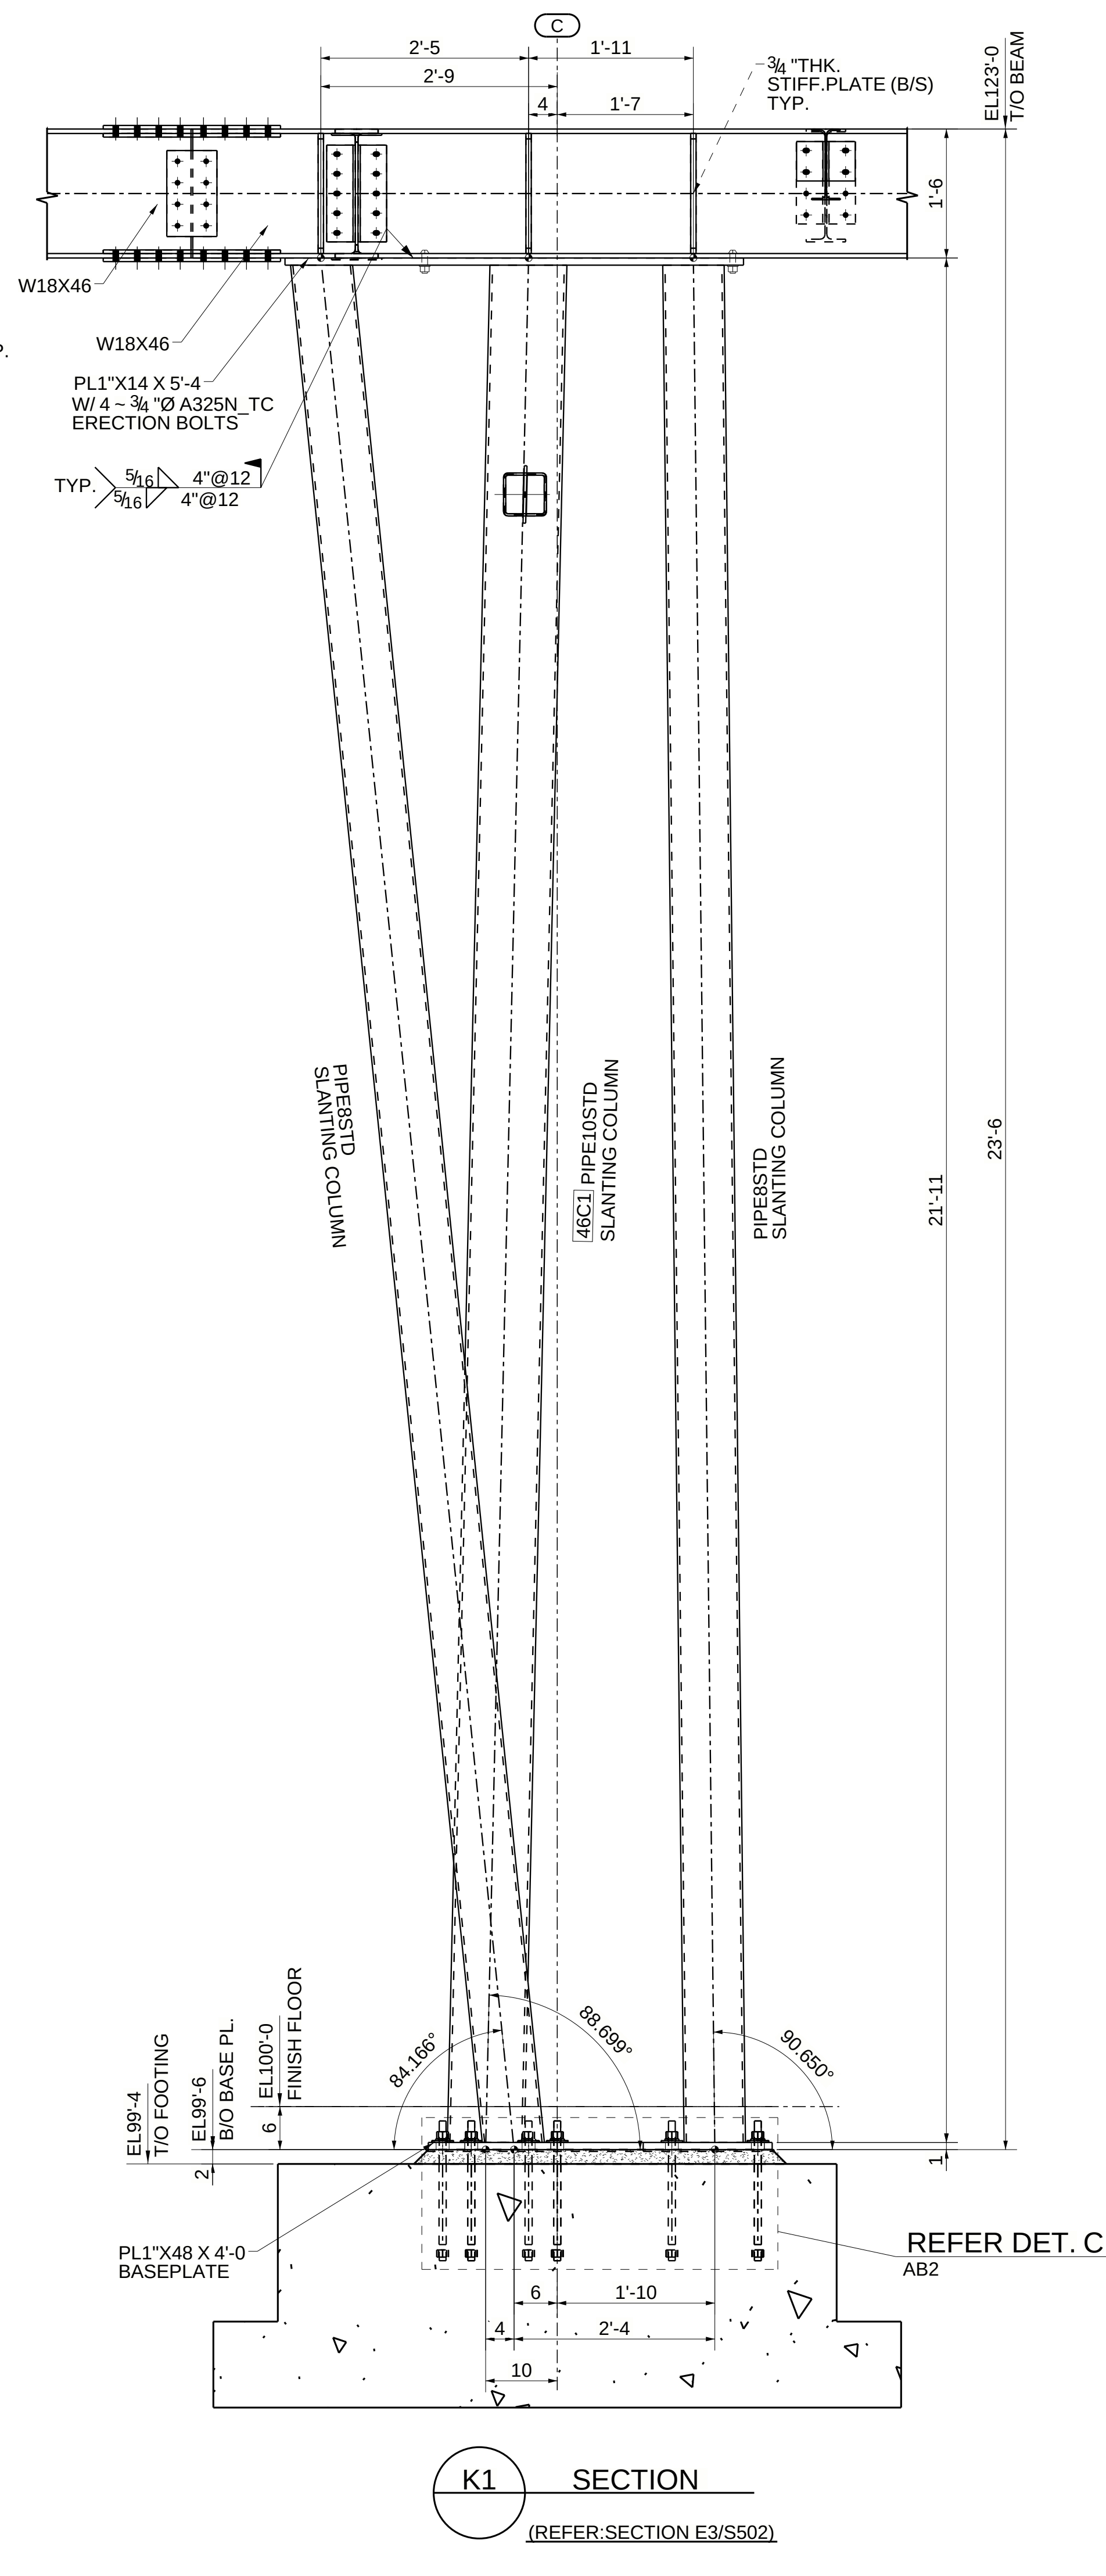


1. REFER E1 SHEET FOR GENERAL NOTES.

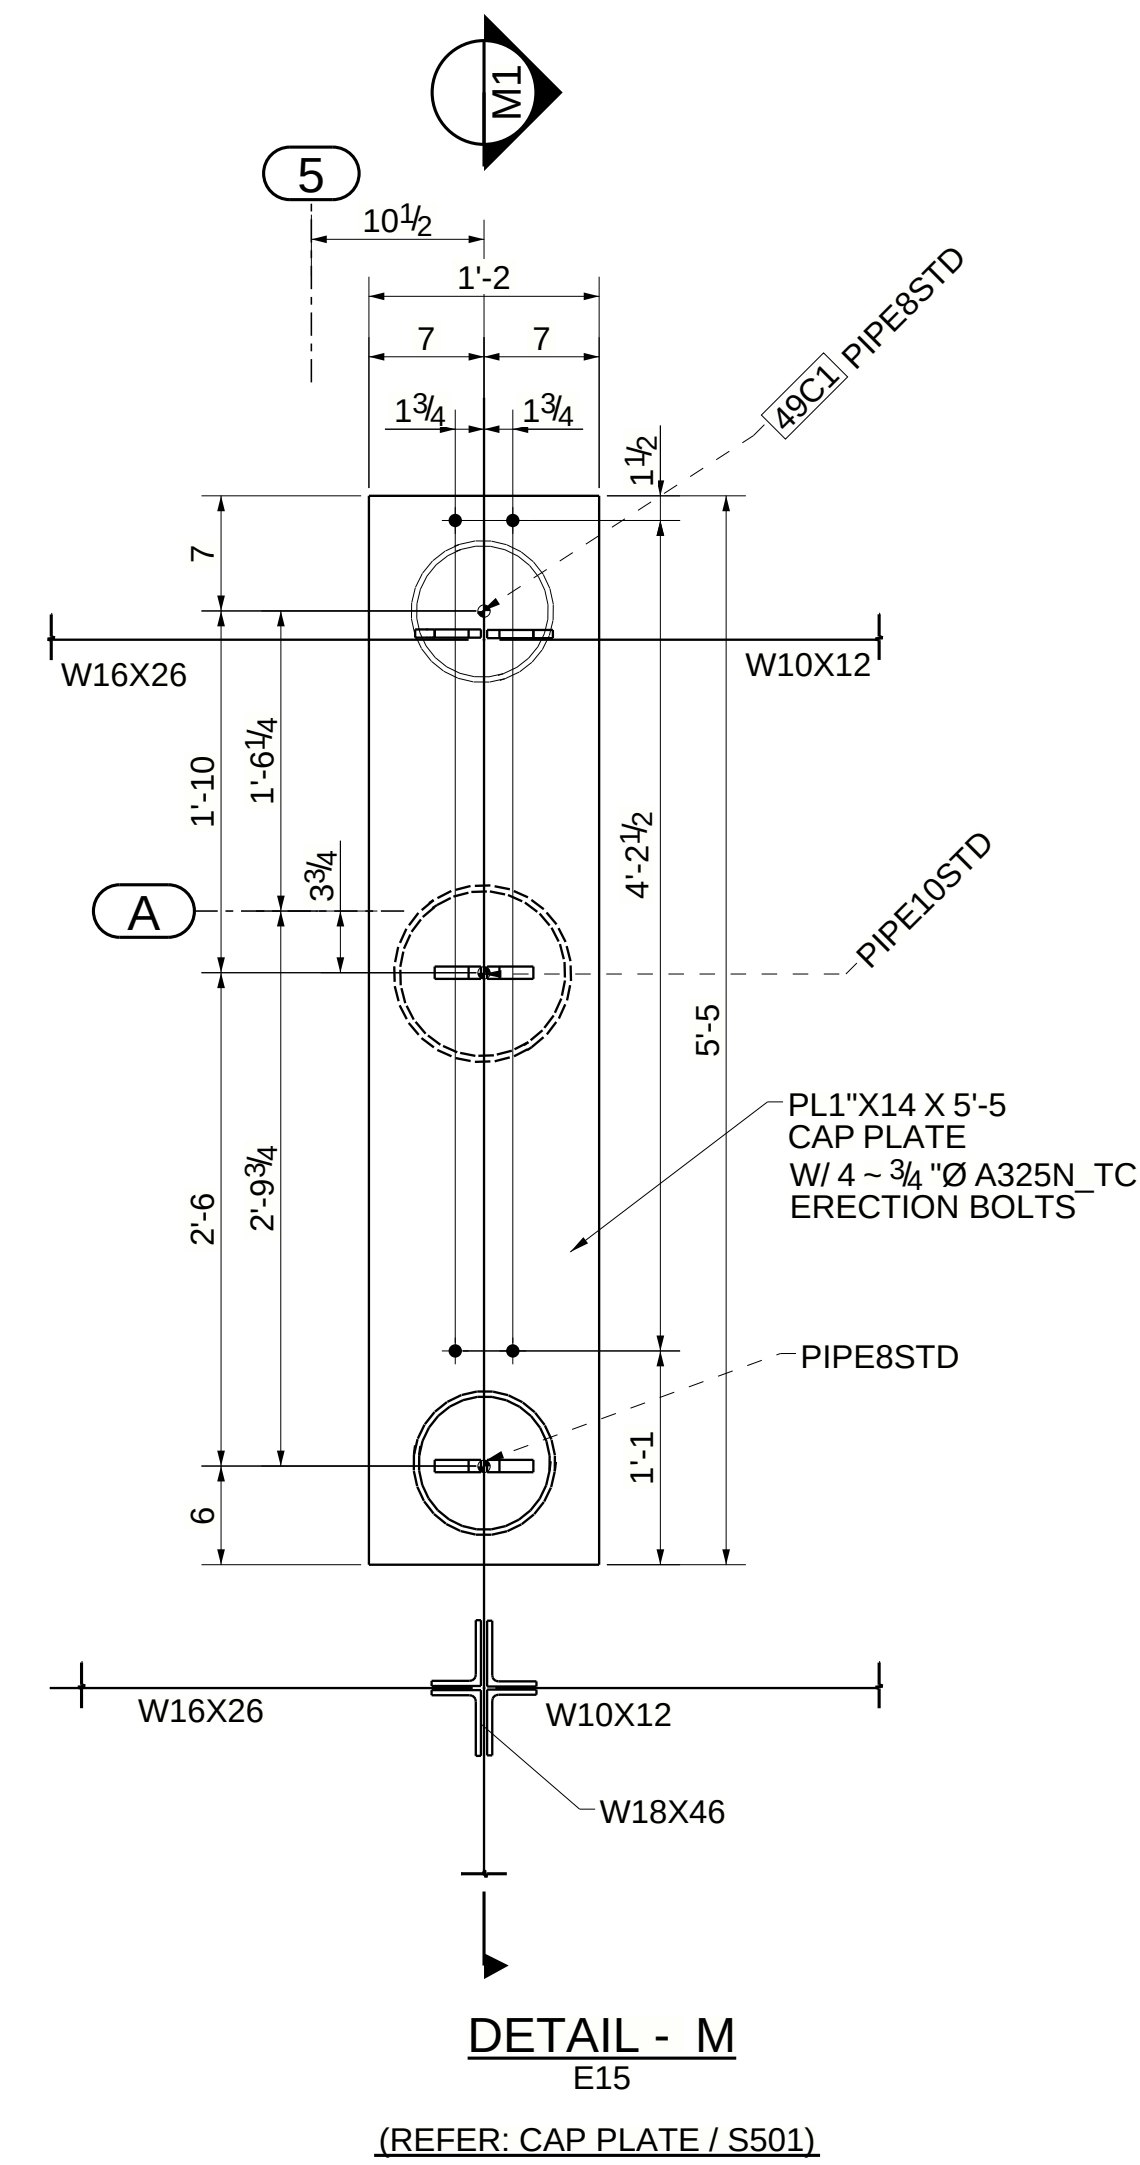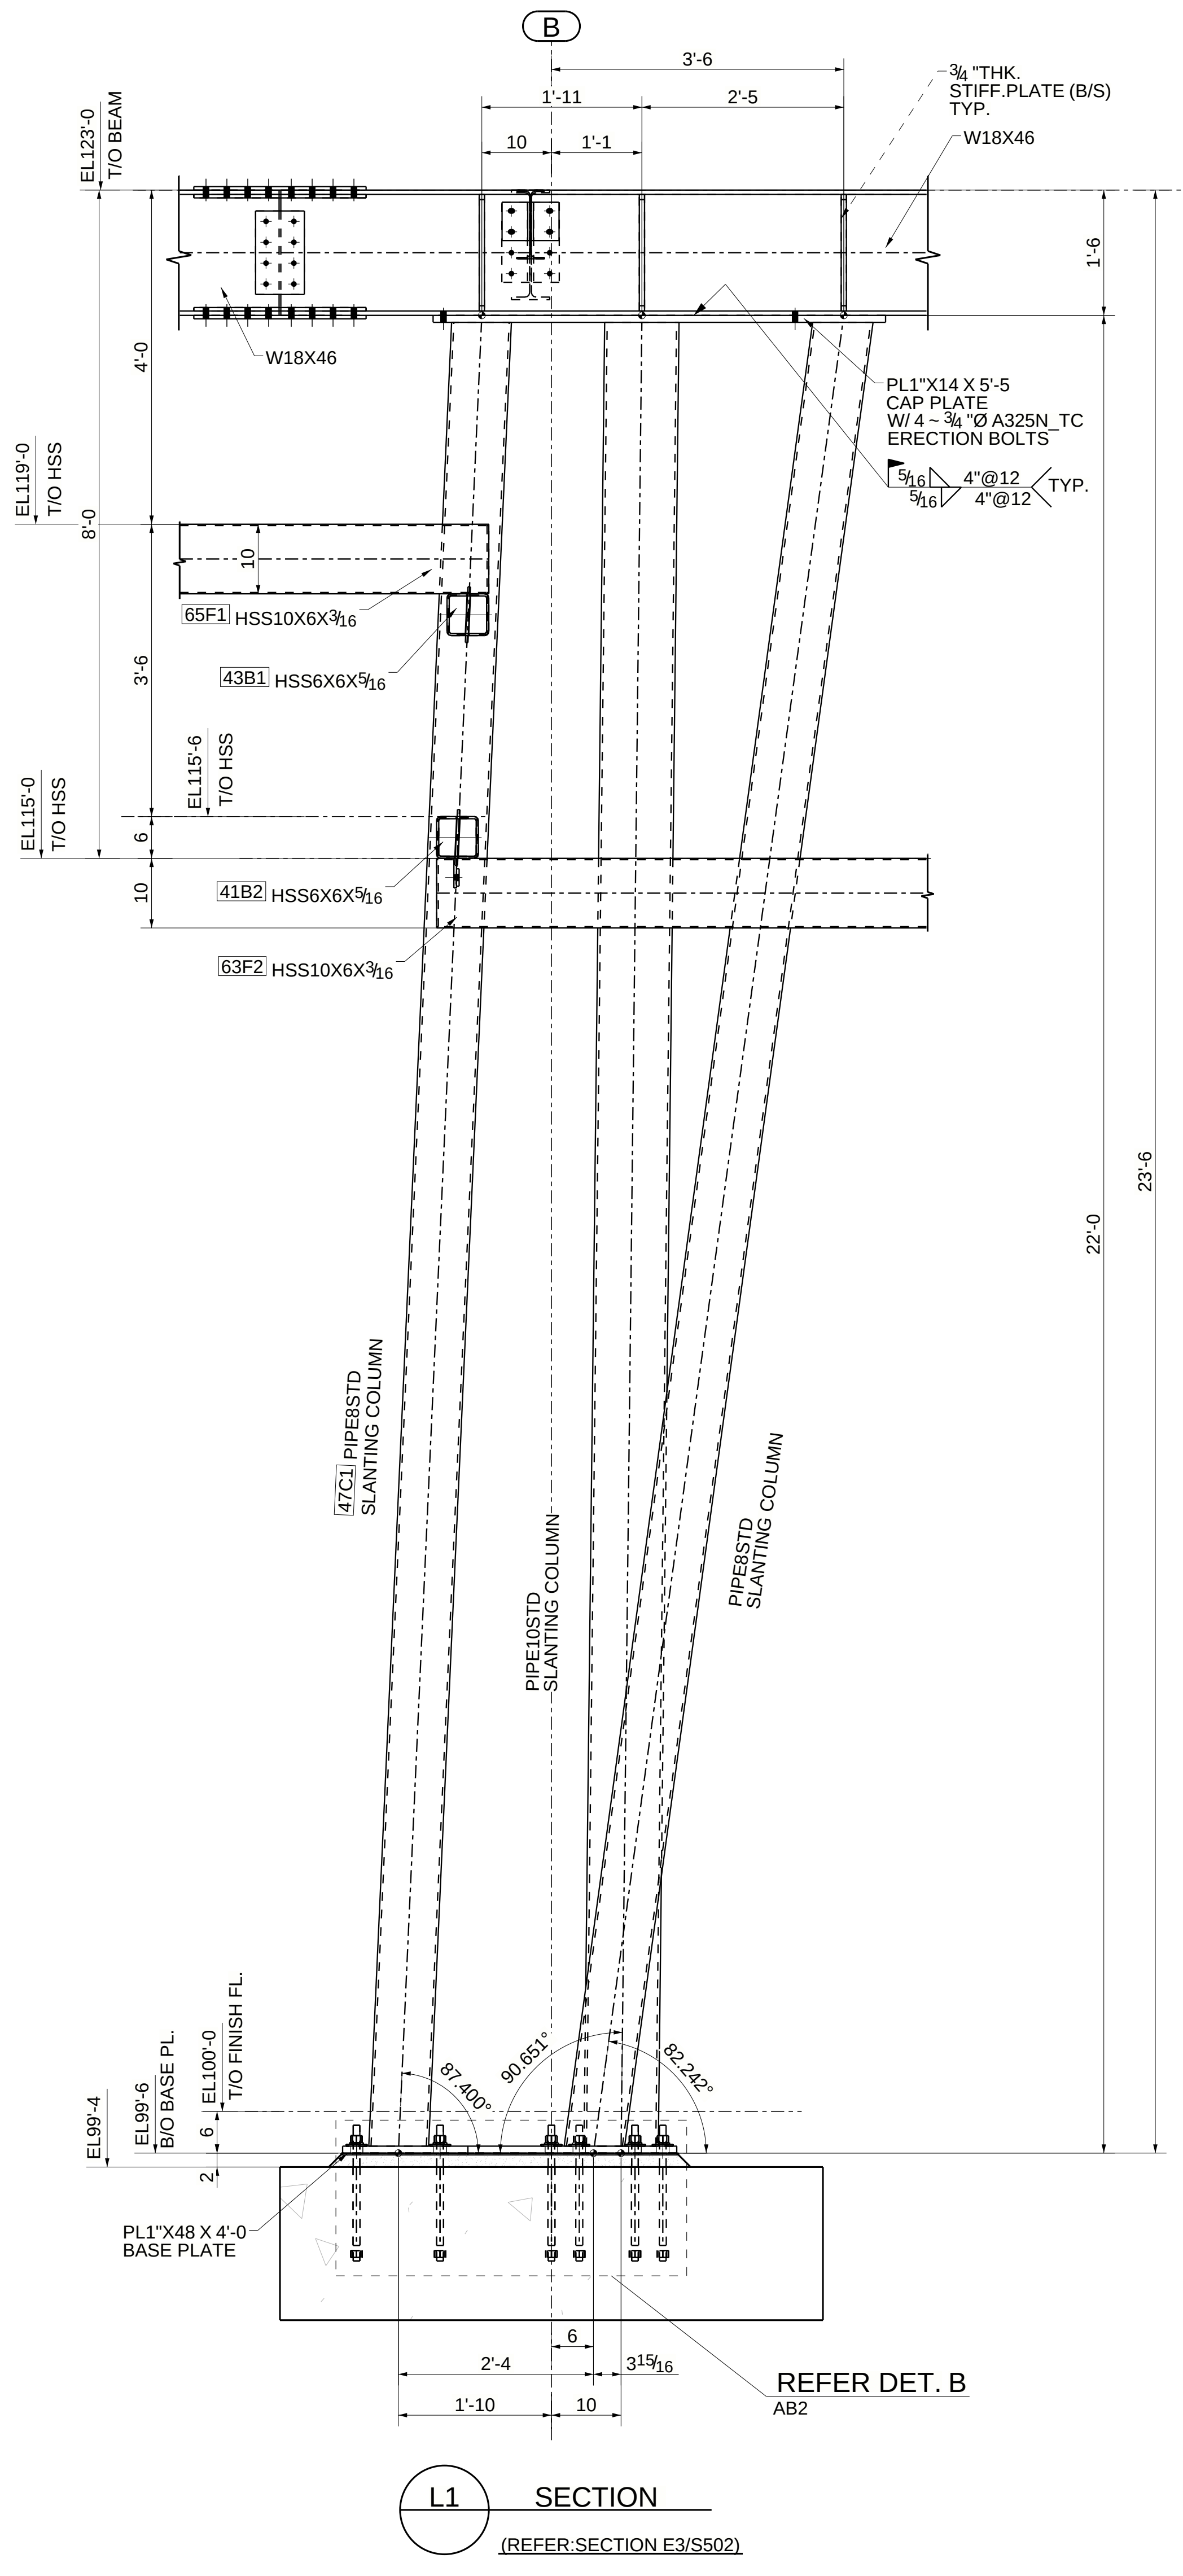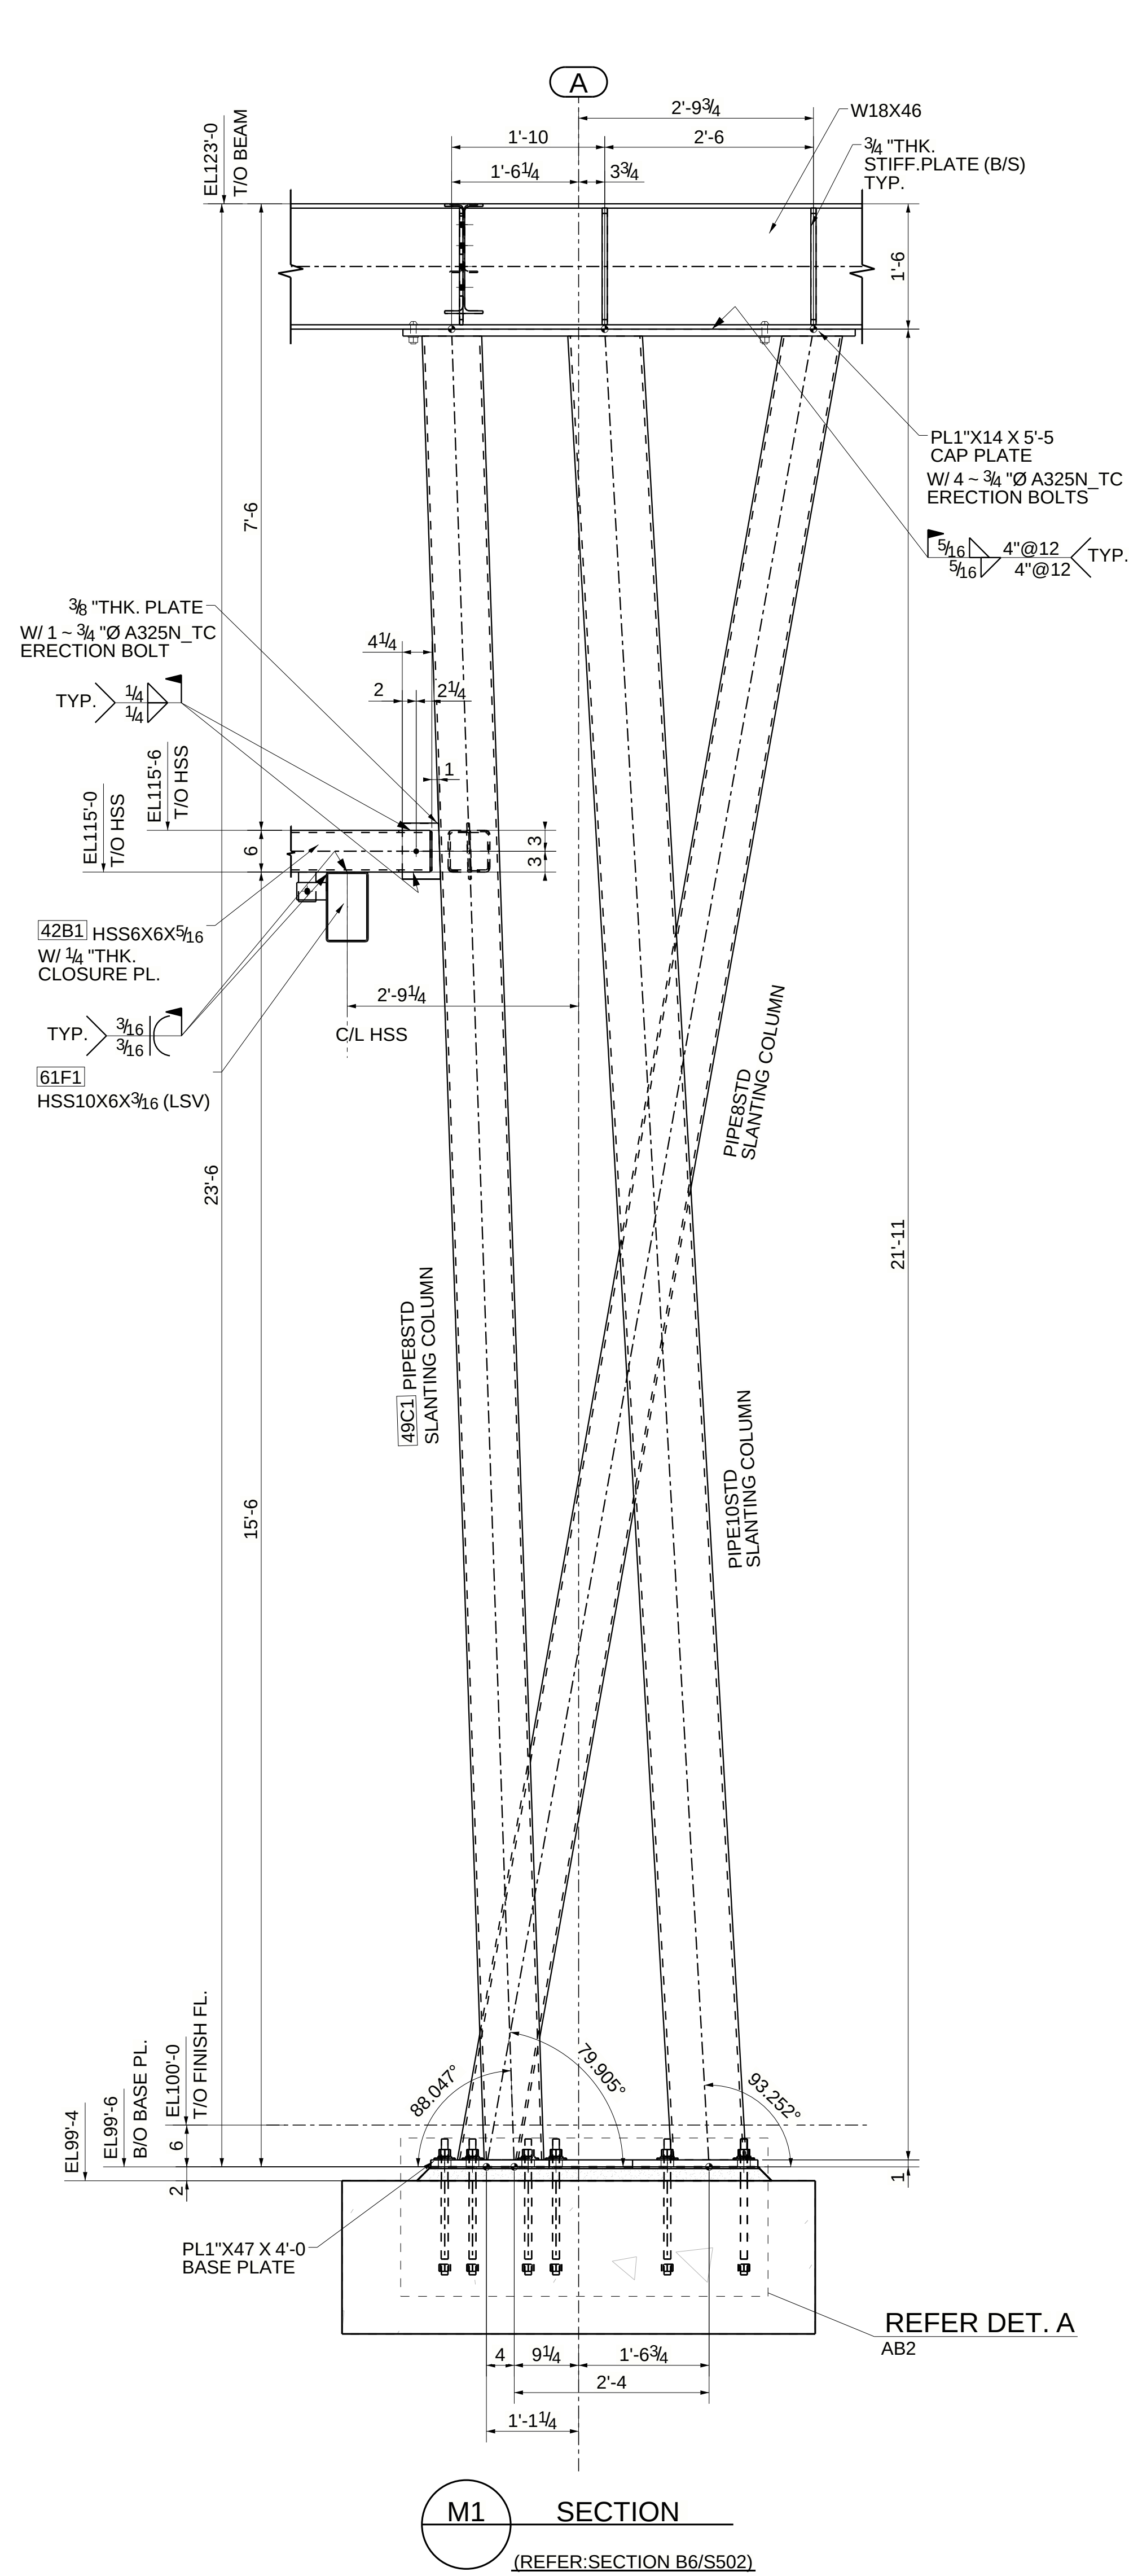


- NOTES:-**
1. REFER E1 SHEET FOR GENERAL NOTES.

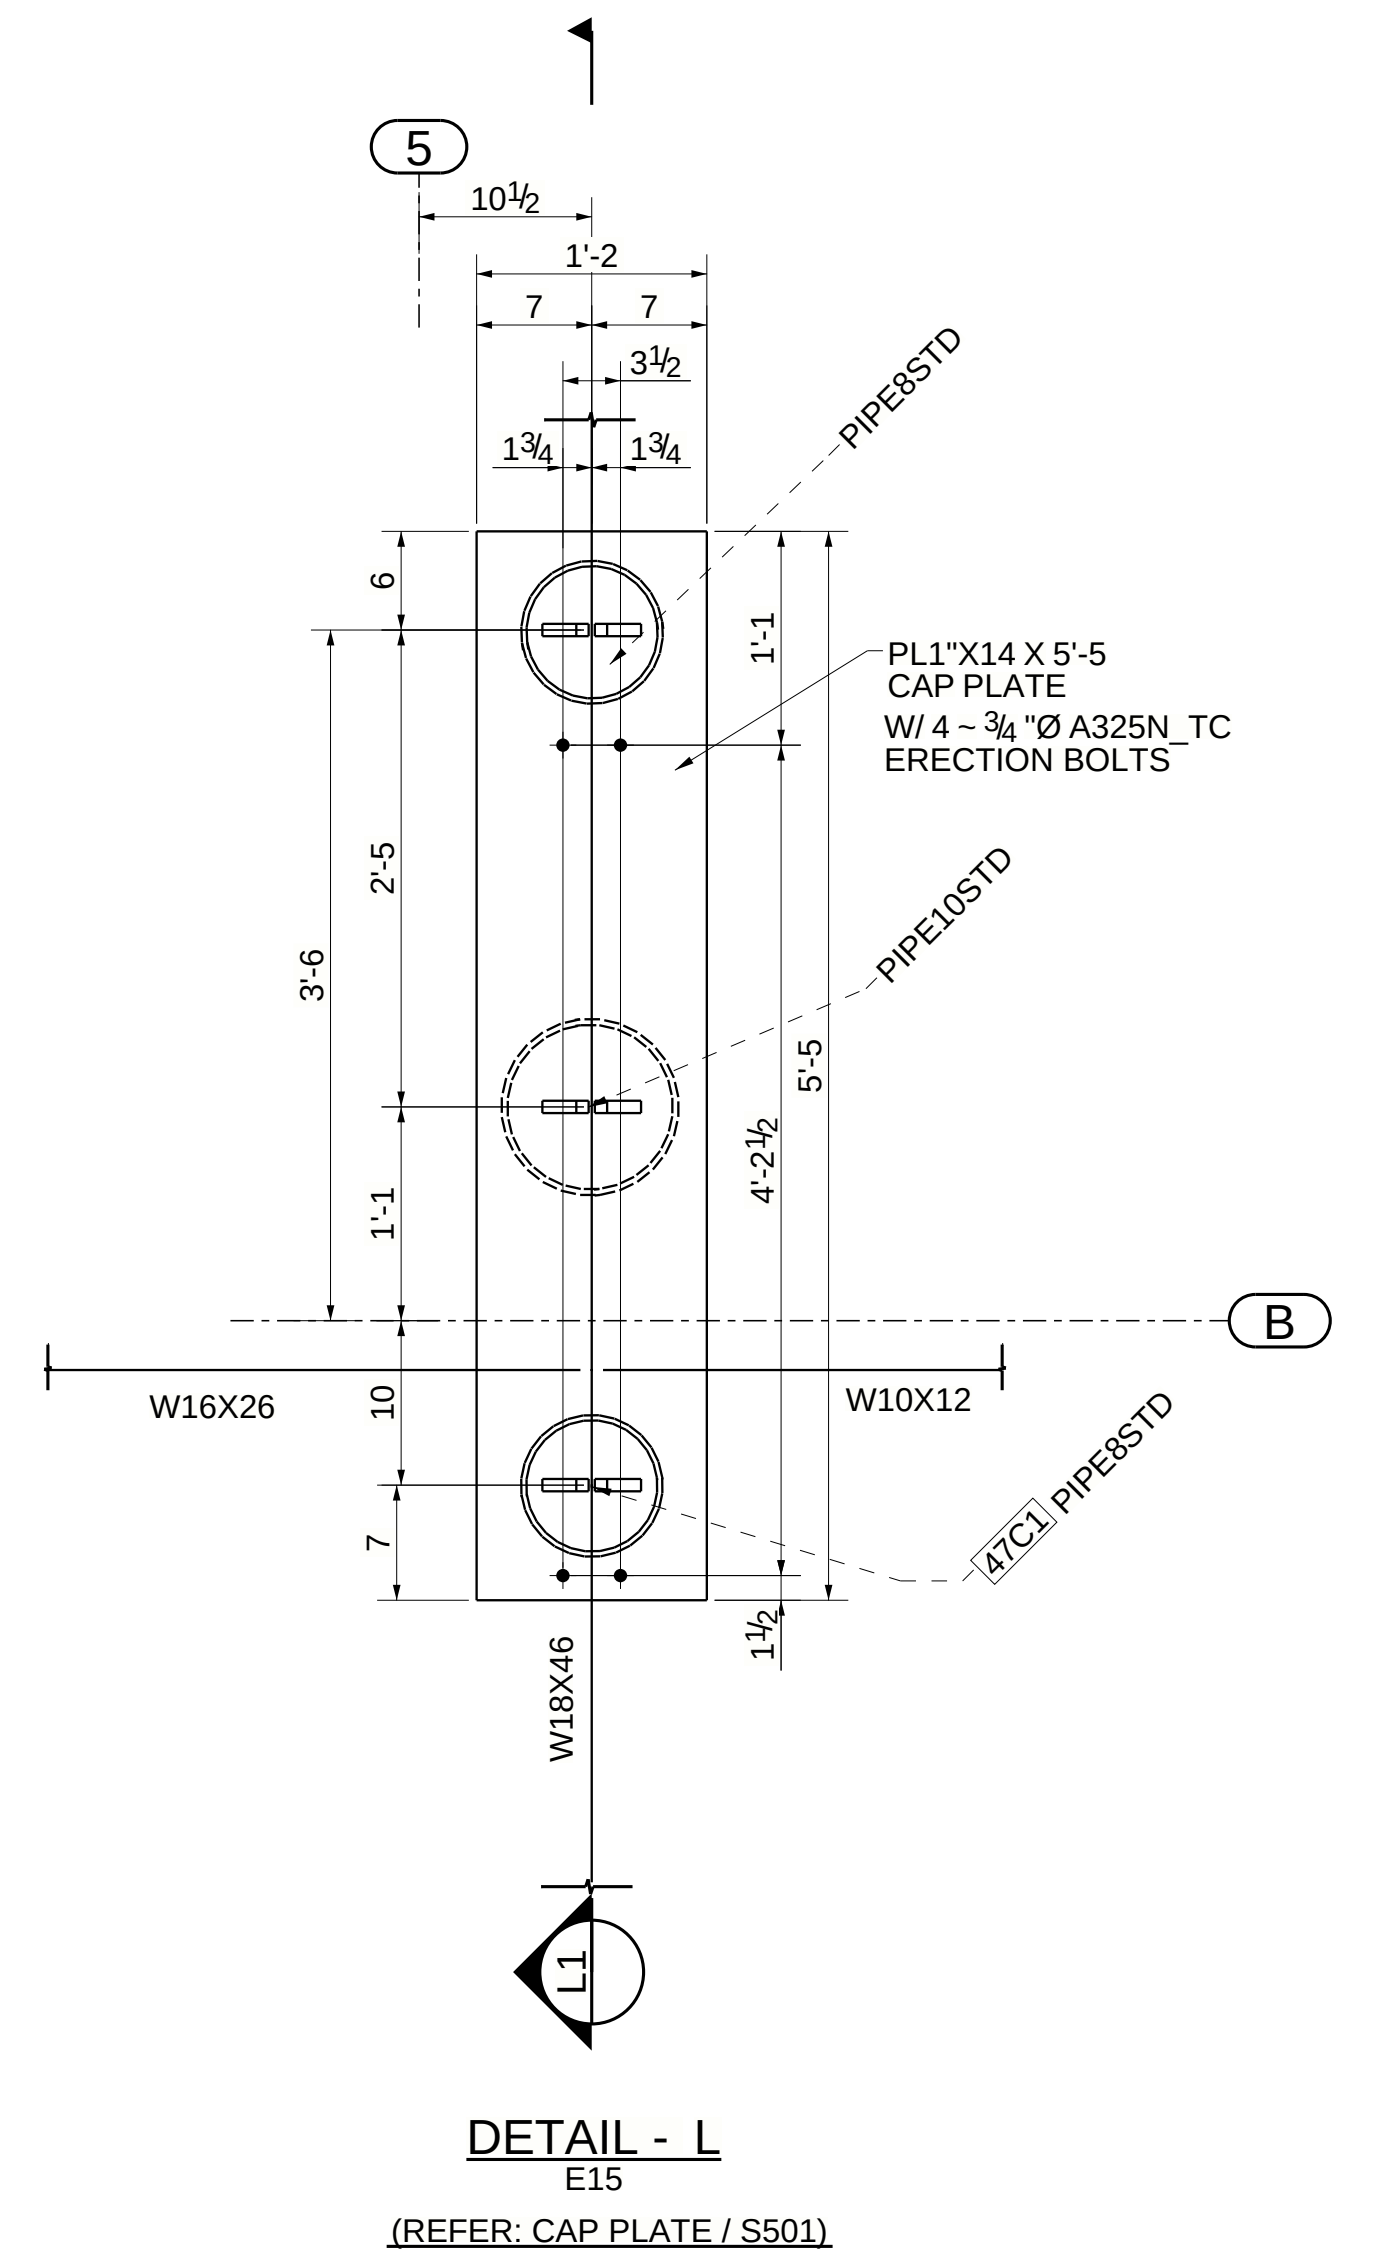

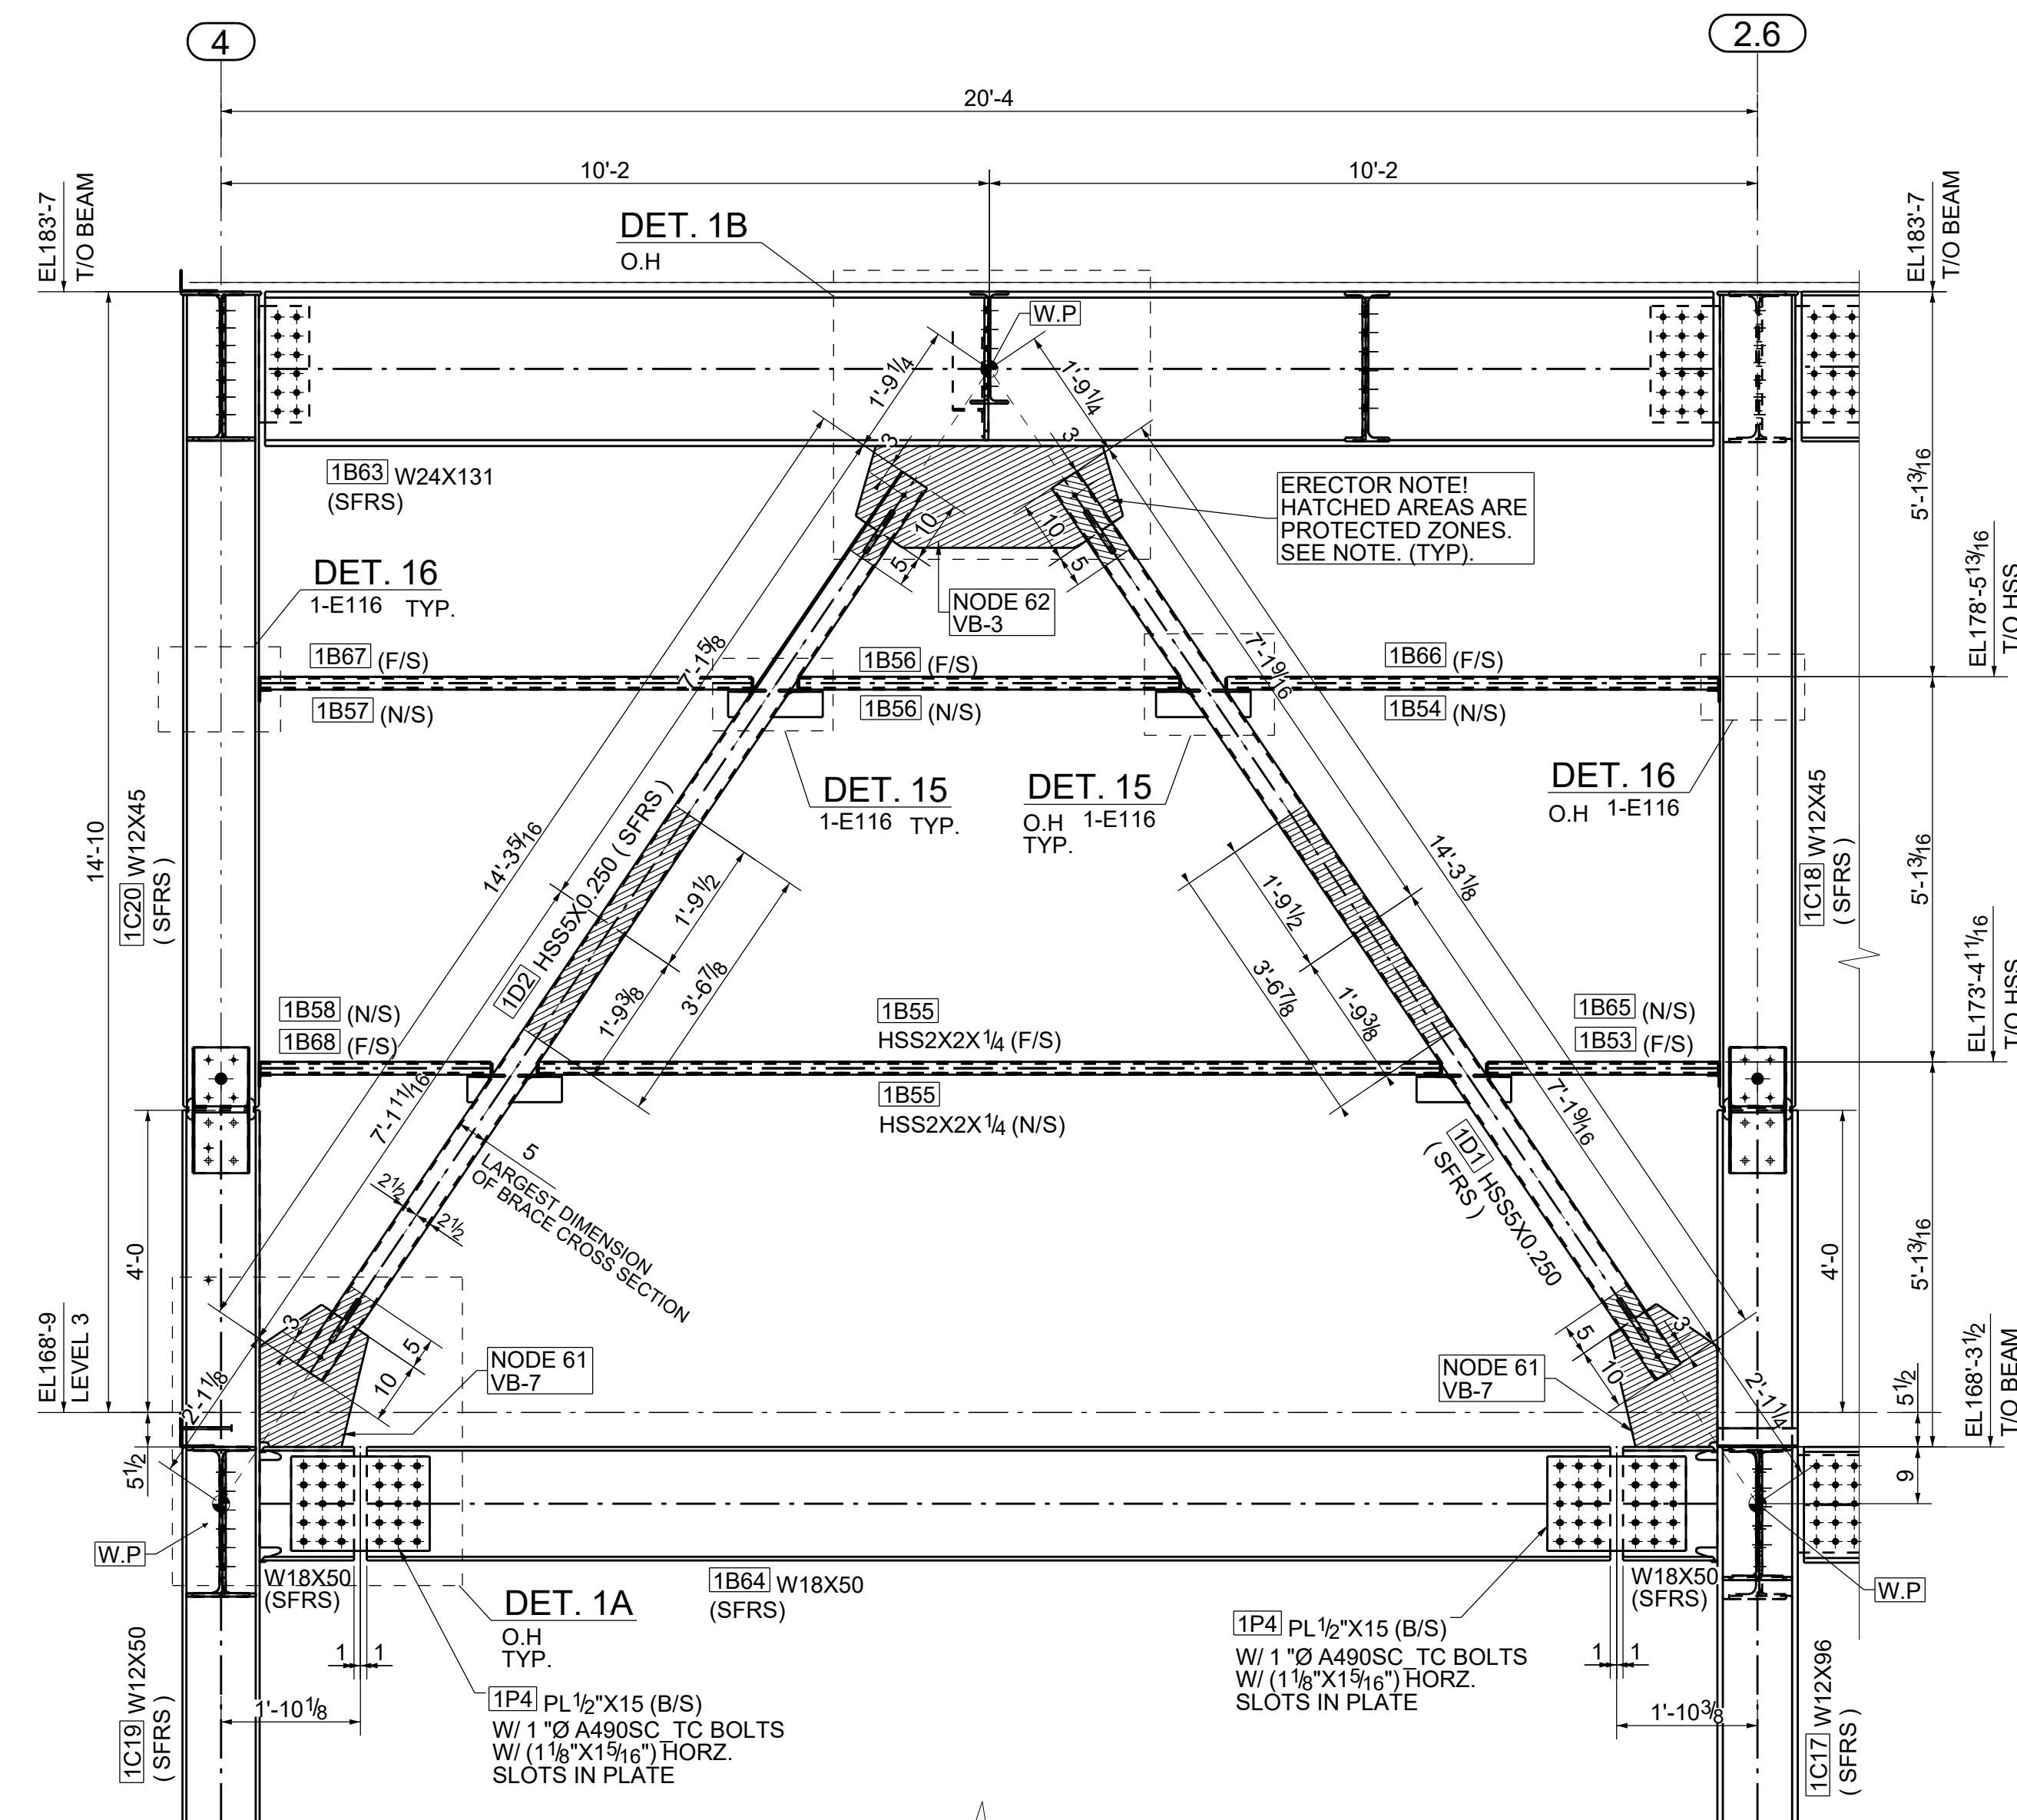

SECTION 2-2


(REFER: BRACE FRAME ELEVATION - GRID B 4/ S5.2)

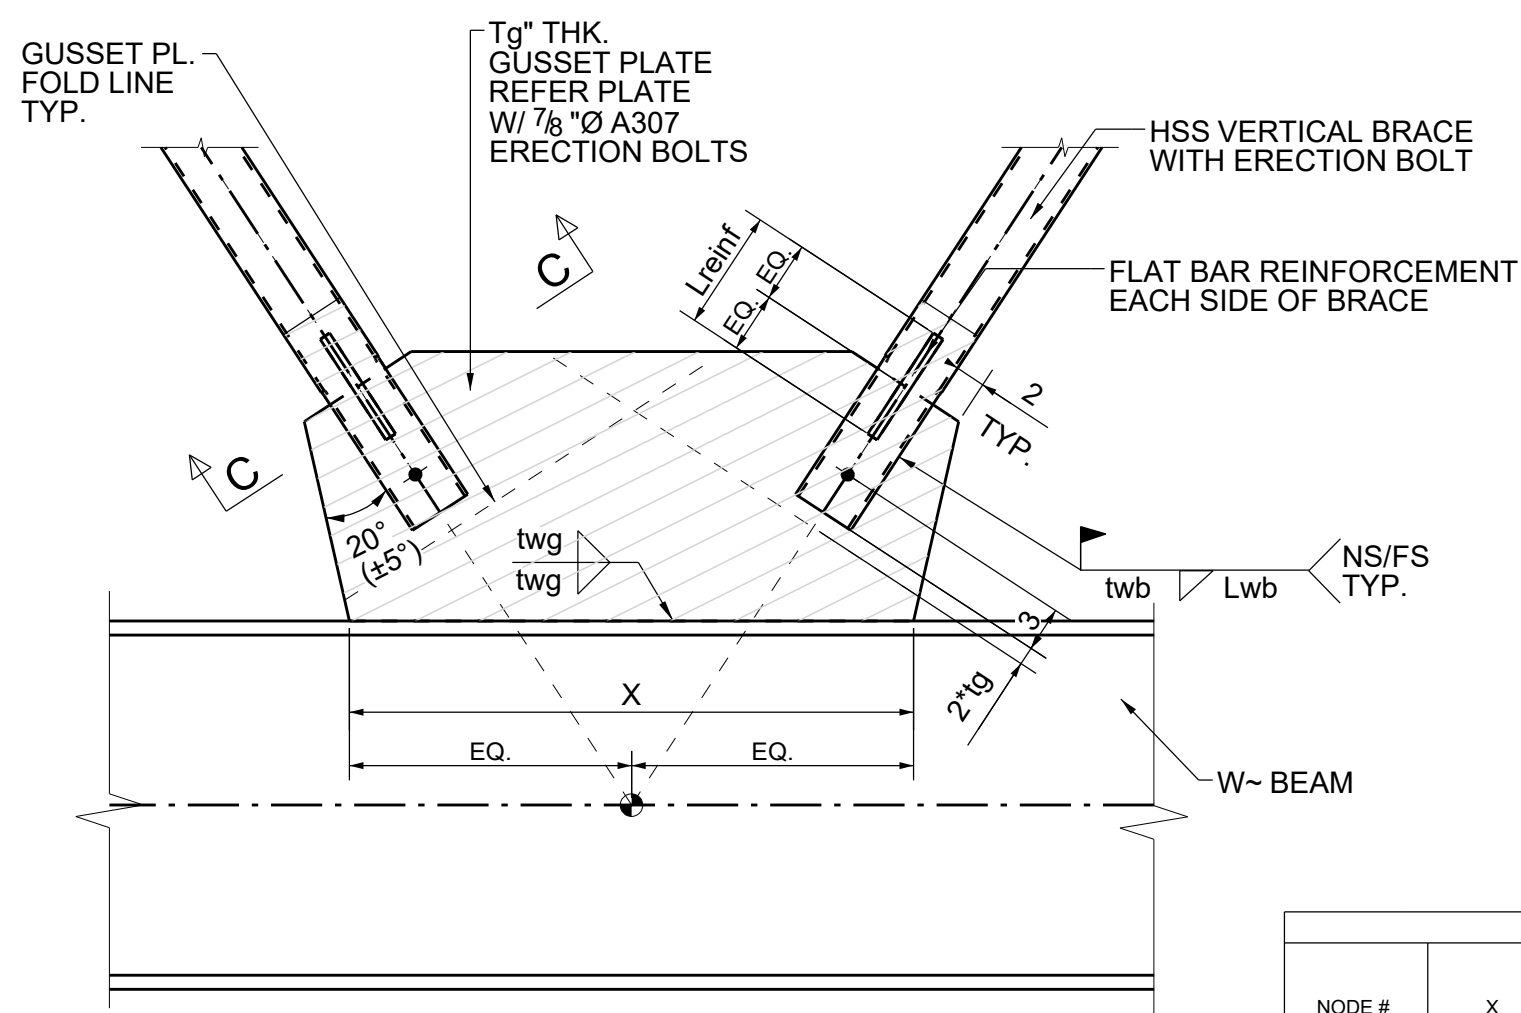

DETAIL 1B


1-E110
(REFER: DETAIL VB-3)

NODE #	X	GUSSET THICKNESS (Tg)	GUSSET WELD SIZE (twg)	BRACE WELD LENGTH (Lwb)	BRACE WELD SIZE (twb)	REINF. PLATE THICKNESS (Tr)	REINF. PLATE DEPTH (Dr)	REINF. PLATE LENGTH (Lreinf)	REINF. PLATE WELD SIZE (twr)
NODE 9	40"	5/8"	1/2"	16"	5/16"	1"	1"	12"	1/4"
NODE 11	36"	1/2"	3/8"	10"	1/4"	3/4"	3/4"	8"	1/4"
NODE 62	36"	1/2"	3/8"	10"	1/4"	3/4"	3/4"	8"	1/4"

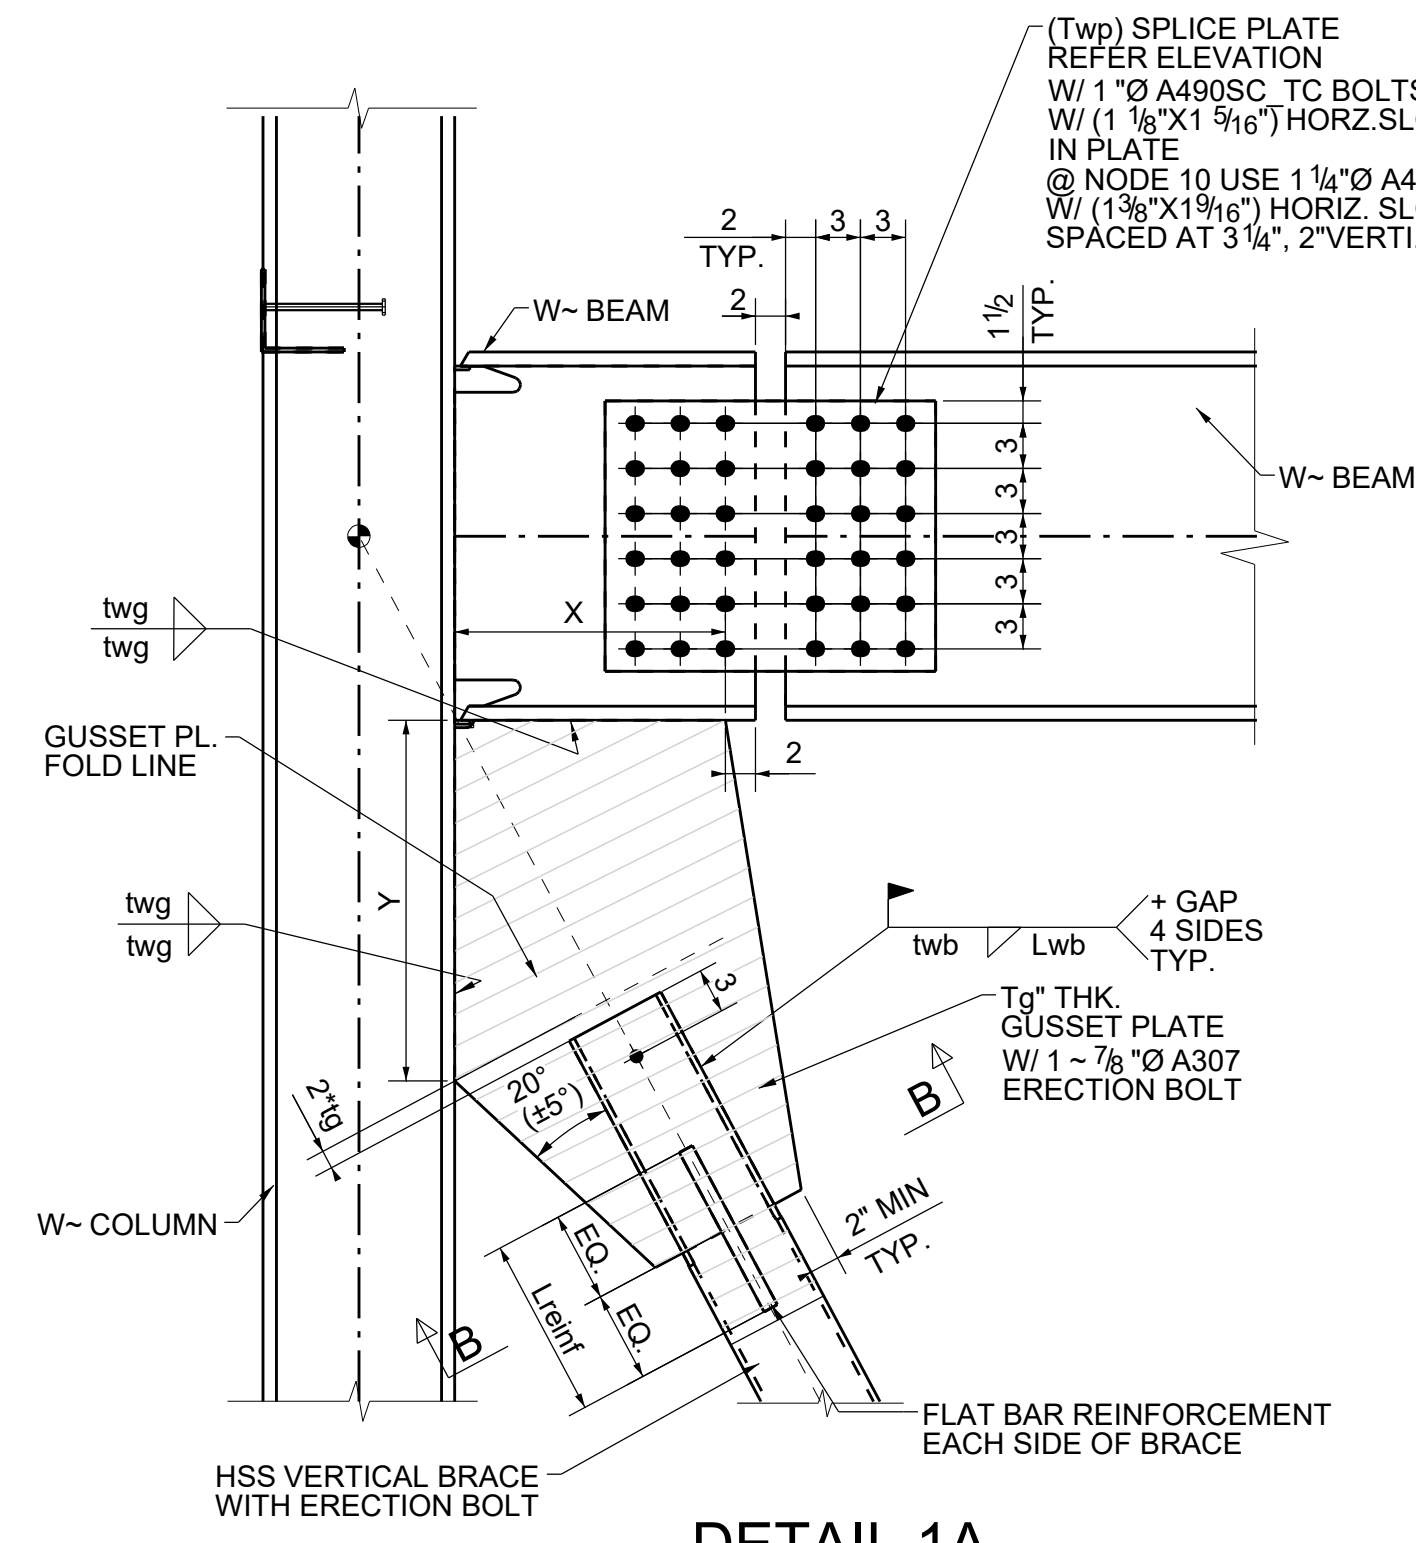


DETAIL 1A

1-E110
(REFER: DETAIL VB-7)

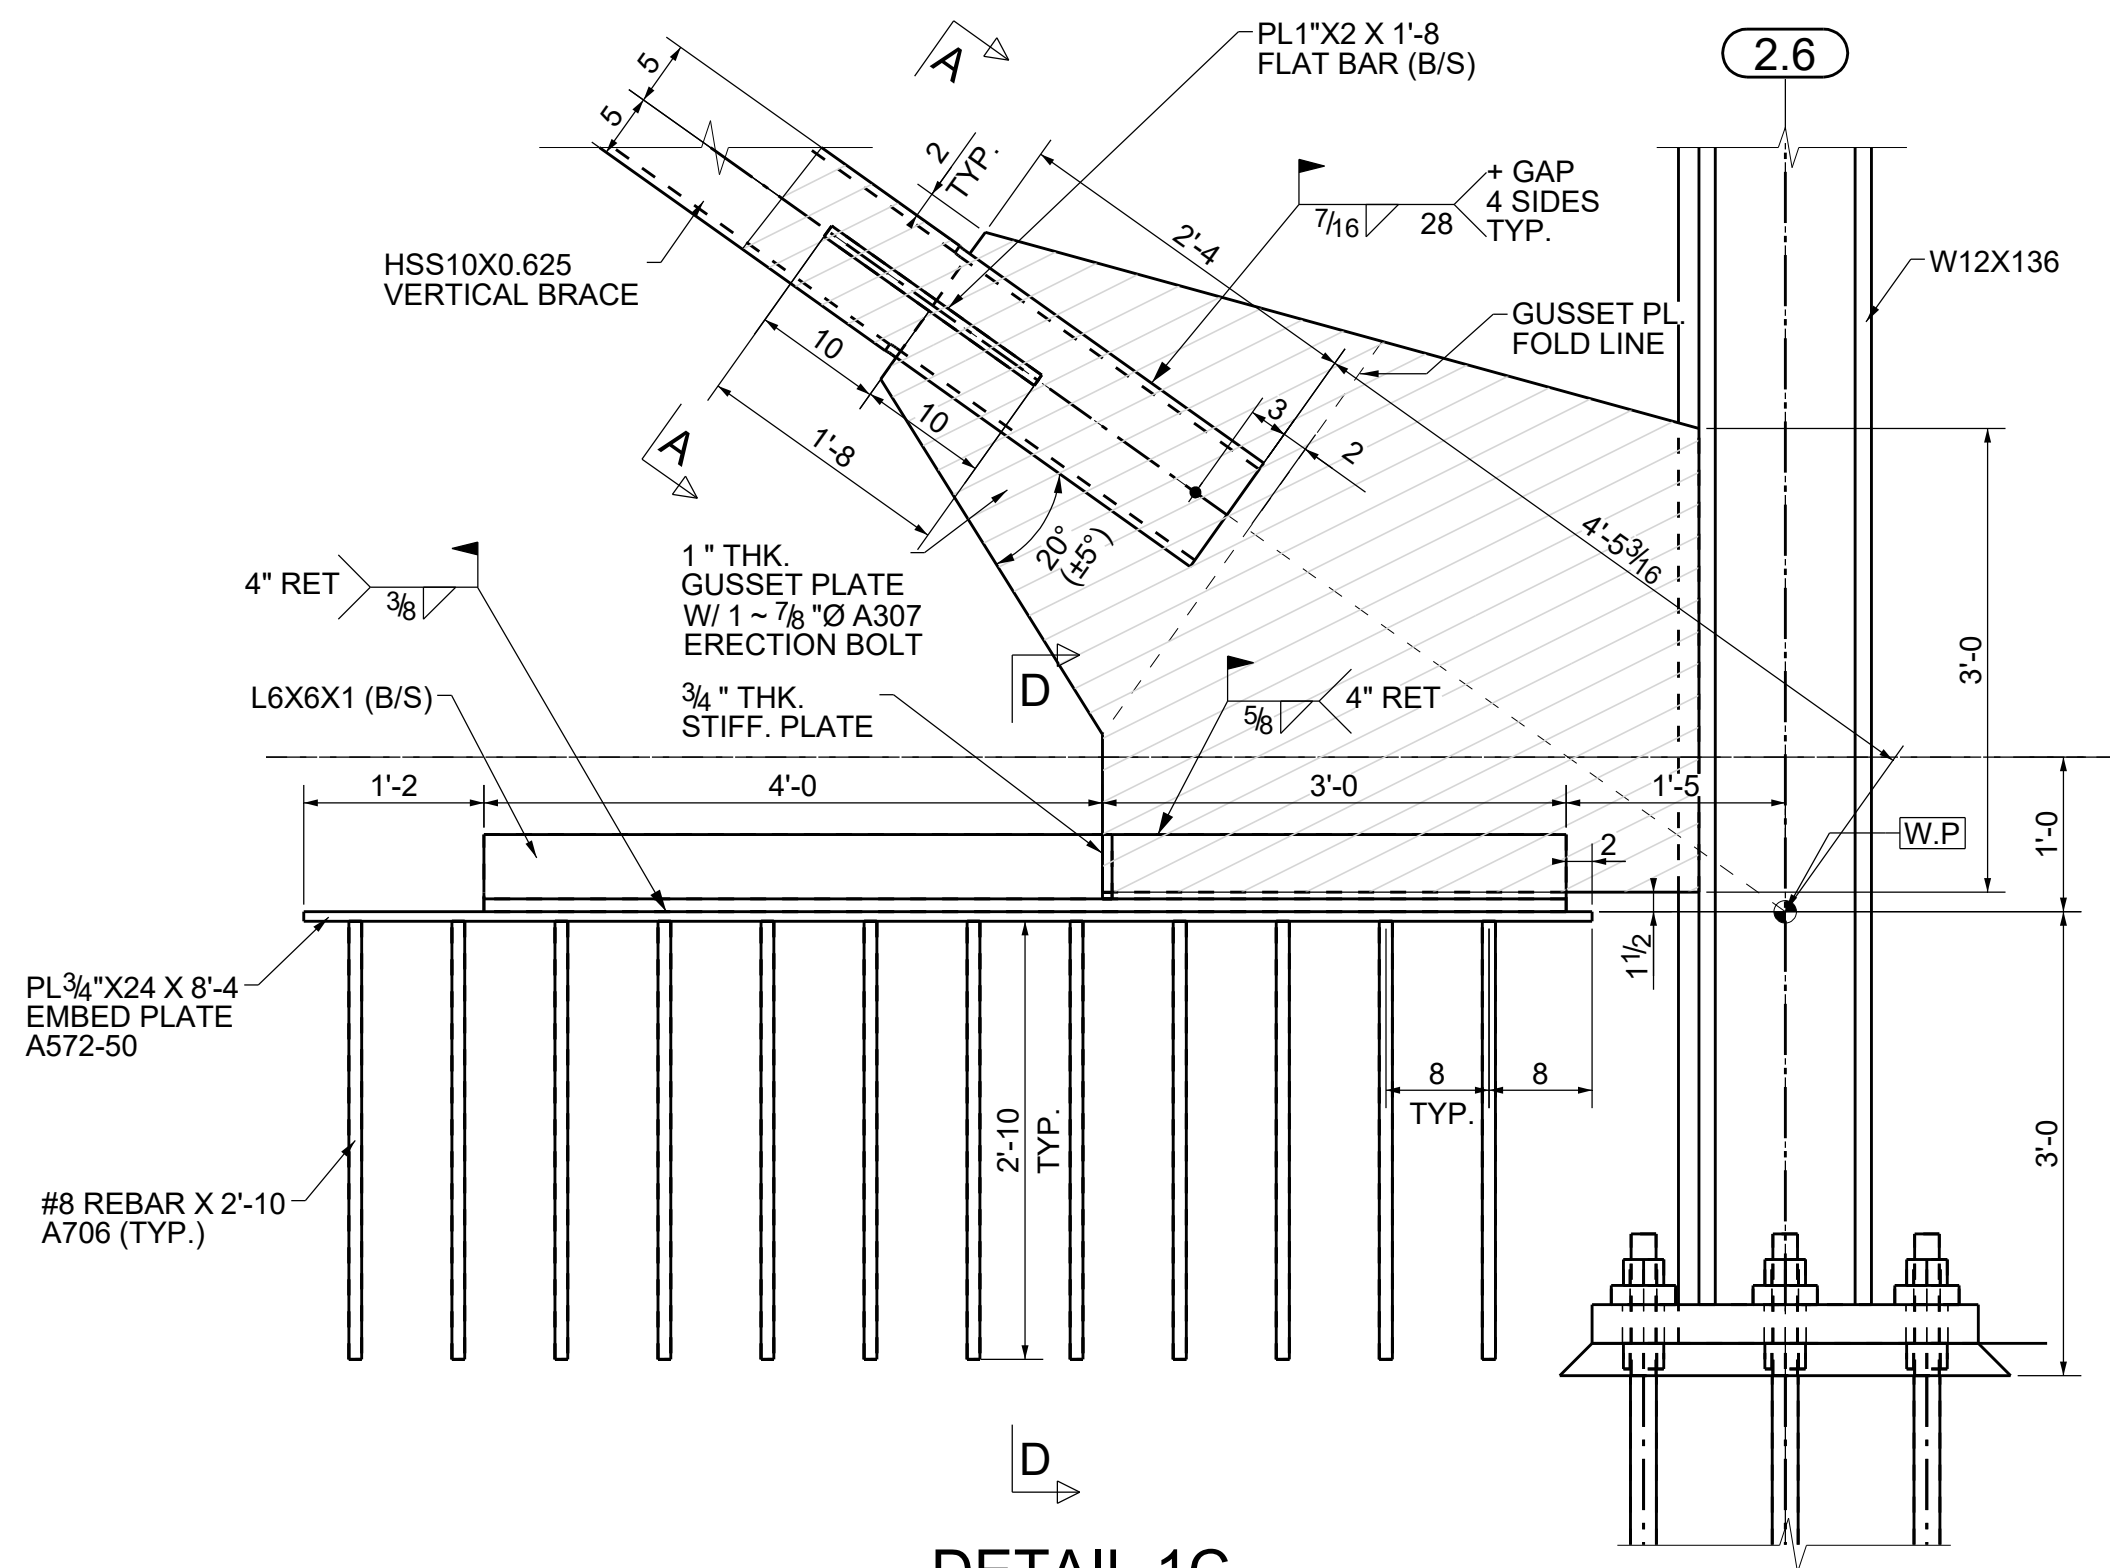

DETAIL 1C

1-E110
(REFER: DETAIL 10/S5.5)
(REFER: DETAIL VB-6, NODE 7)

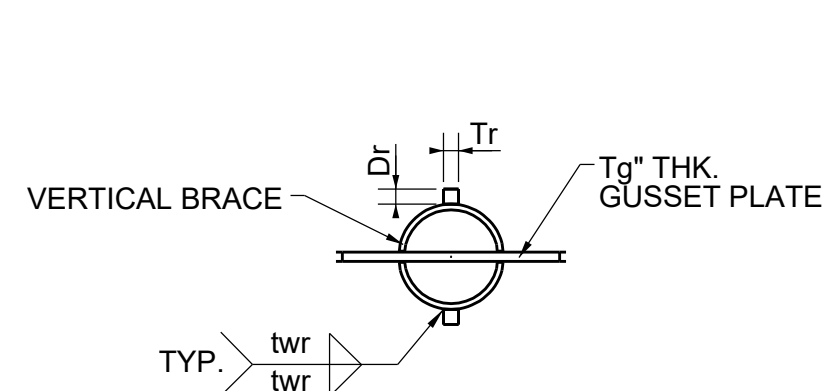


SECTION B - B


NODE #	X	Y	GUSSET THICKNESS (Tg)	GUSSET WELD SIZE (twg)	BRACE WELD LENGTH (Lwb)	BRACE WELD SIZE (twb)	REINF. PLATE THICKNESS (Tr)	REINF. PLATE DEPTH (Dr)	REINF. PLATE LENGTH (Lreinf)	REINF. PLATE WELD SIZE (twr)	WEB SPLICE PLATE THICKNESS (Twp)
NODE 10	40"	24"	1"	9/16"	28"	7/16"	1"	2"	20"	5/16"	3/4"
NODE 12	18"	24"	5/8"	1/2"	16"	5/16"	1"	1"	12"	1/4"	1/2"
NODE 13	13"	15"	1/2"	3/8"	10"	1/4"	3/4"	3/4"	8"	1/4"	1/2"
NODE 61	13"	16"	1/2"	3/8"	10"	1/4"	3/4"	3/4"	8"	1/4"	1/2"

ERECTOR NOTES :


1. SEE 1-E105 FOR GENERAL NOTES.
2. SEE 1-E110 FOR SEISMIC PROTECTED ZONE AND DEMAND CRITICAL WELD NOTES
3. ALL PROTECTED ZONES SHALL BE YELLOW PAINT.

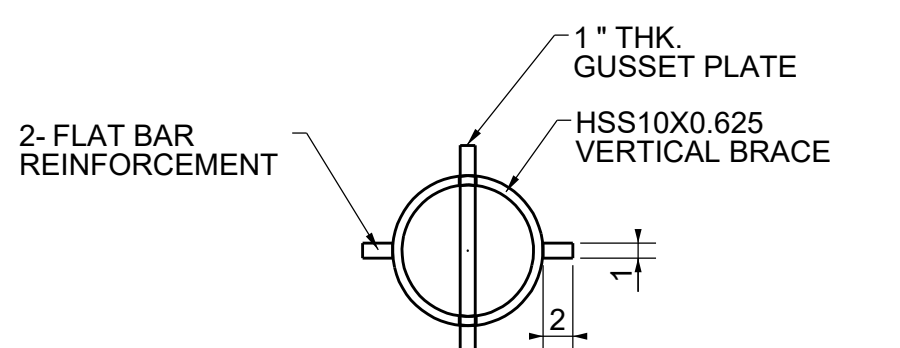


SECTION A - A

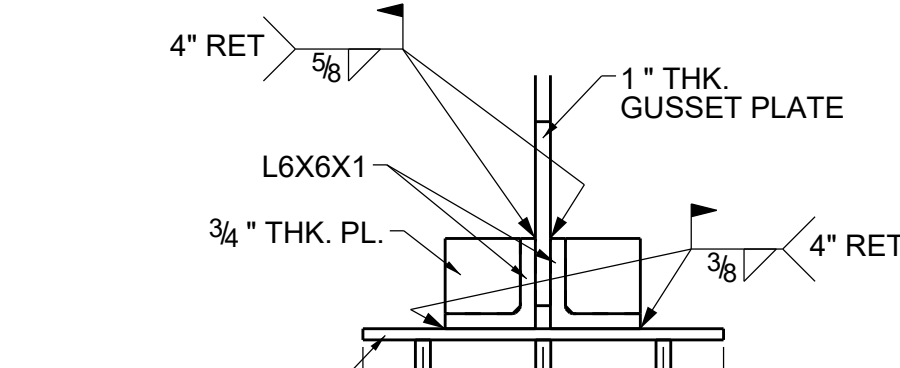


SECTION D - D

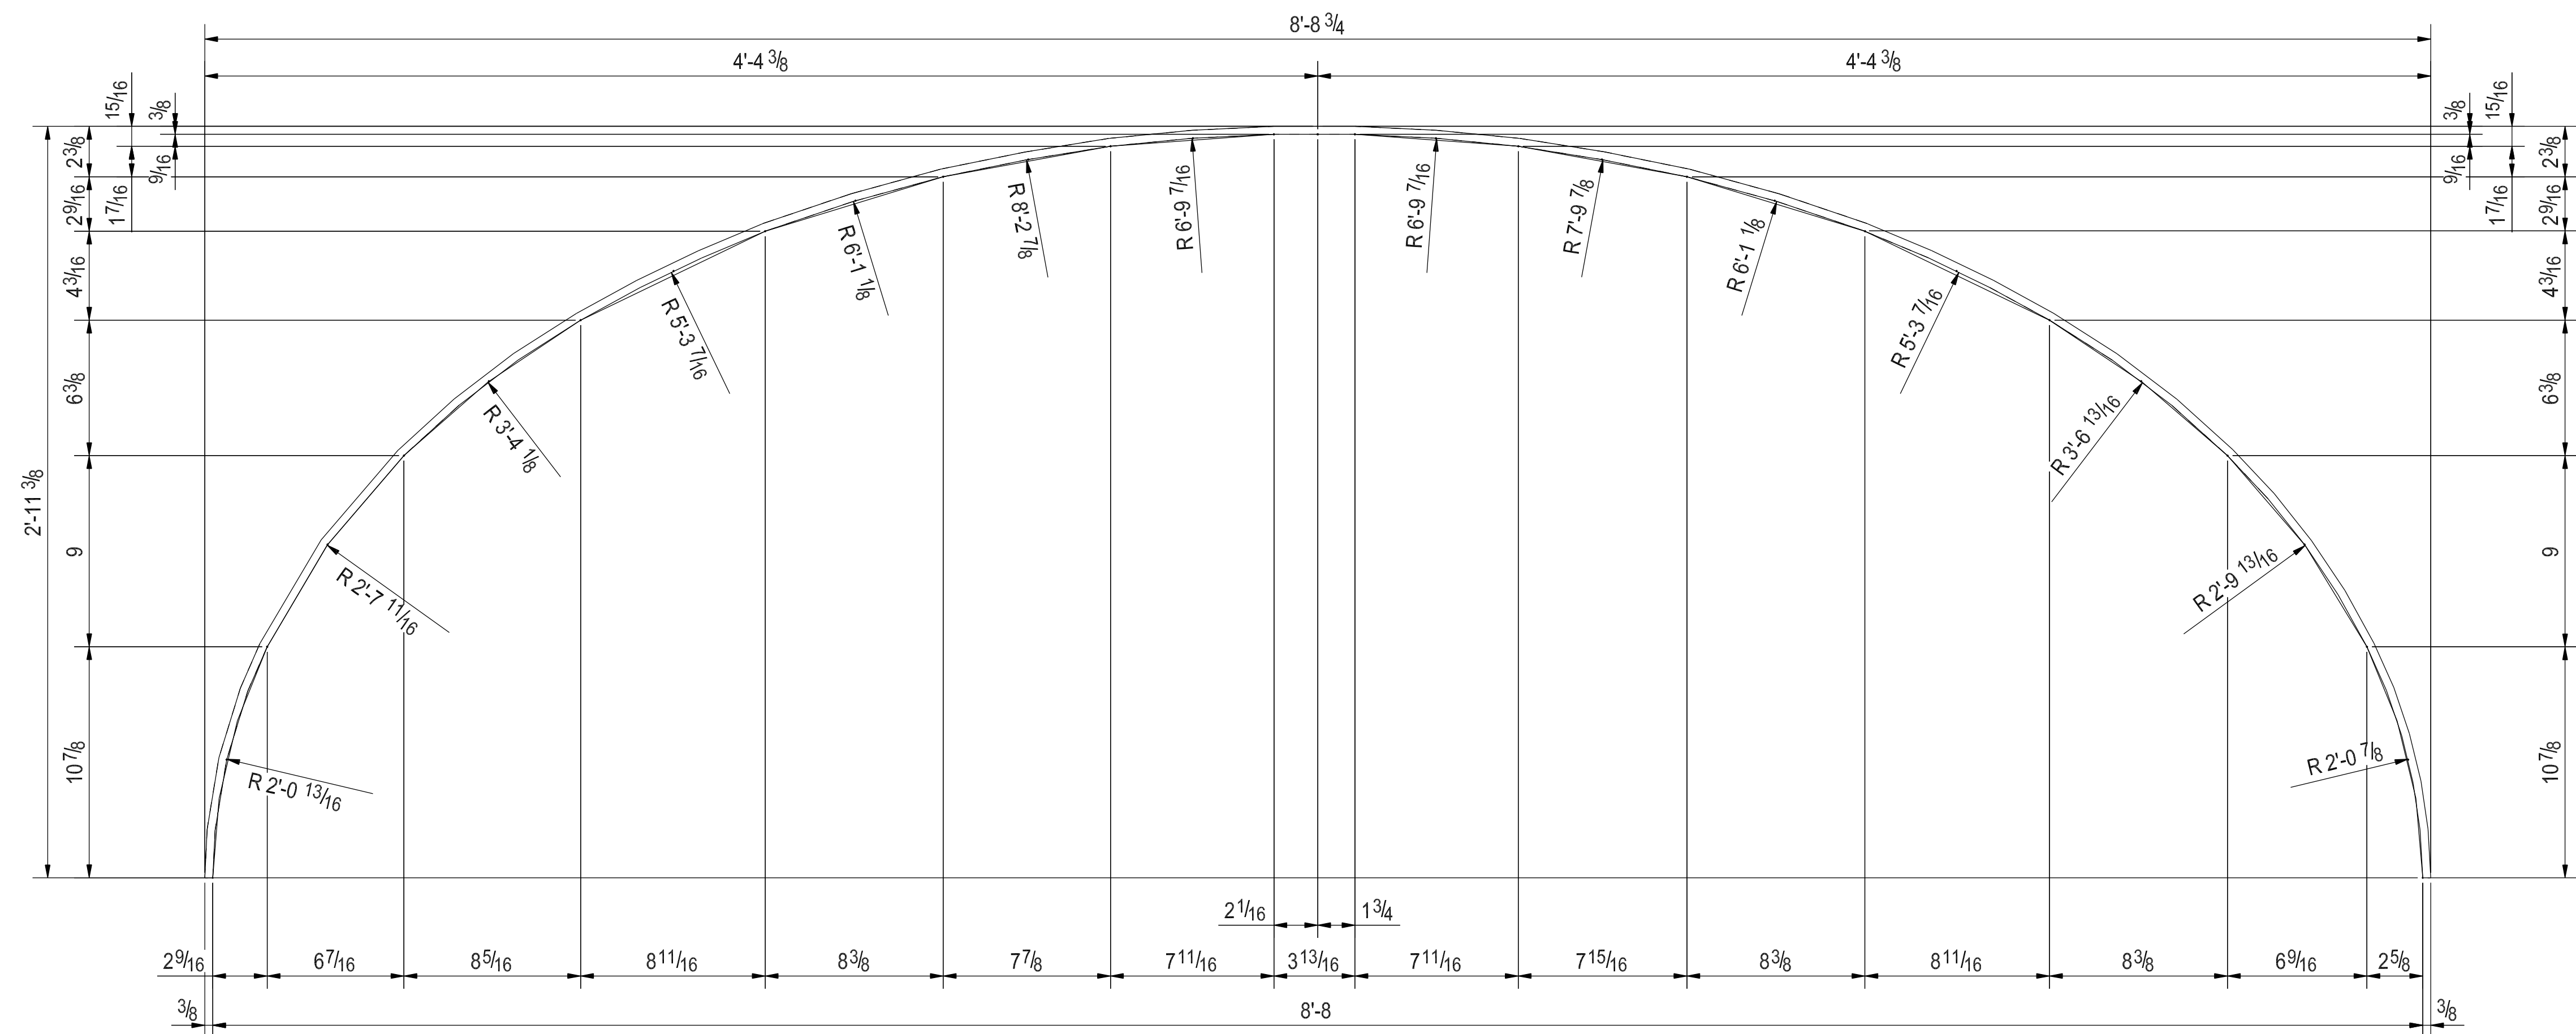

TYPICAL CURVED BRICK SUPPORT PLATE
@ 8'-8" OPENING LOCATION

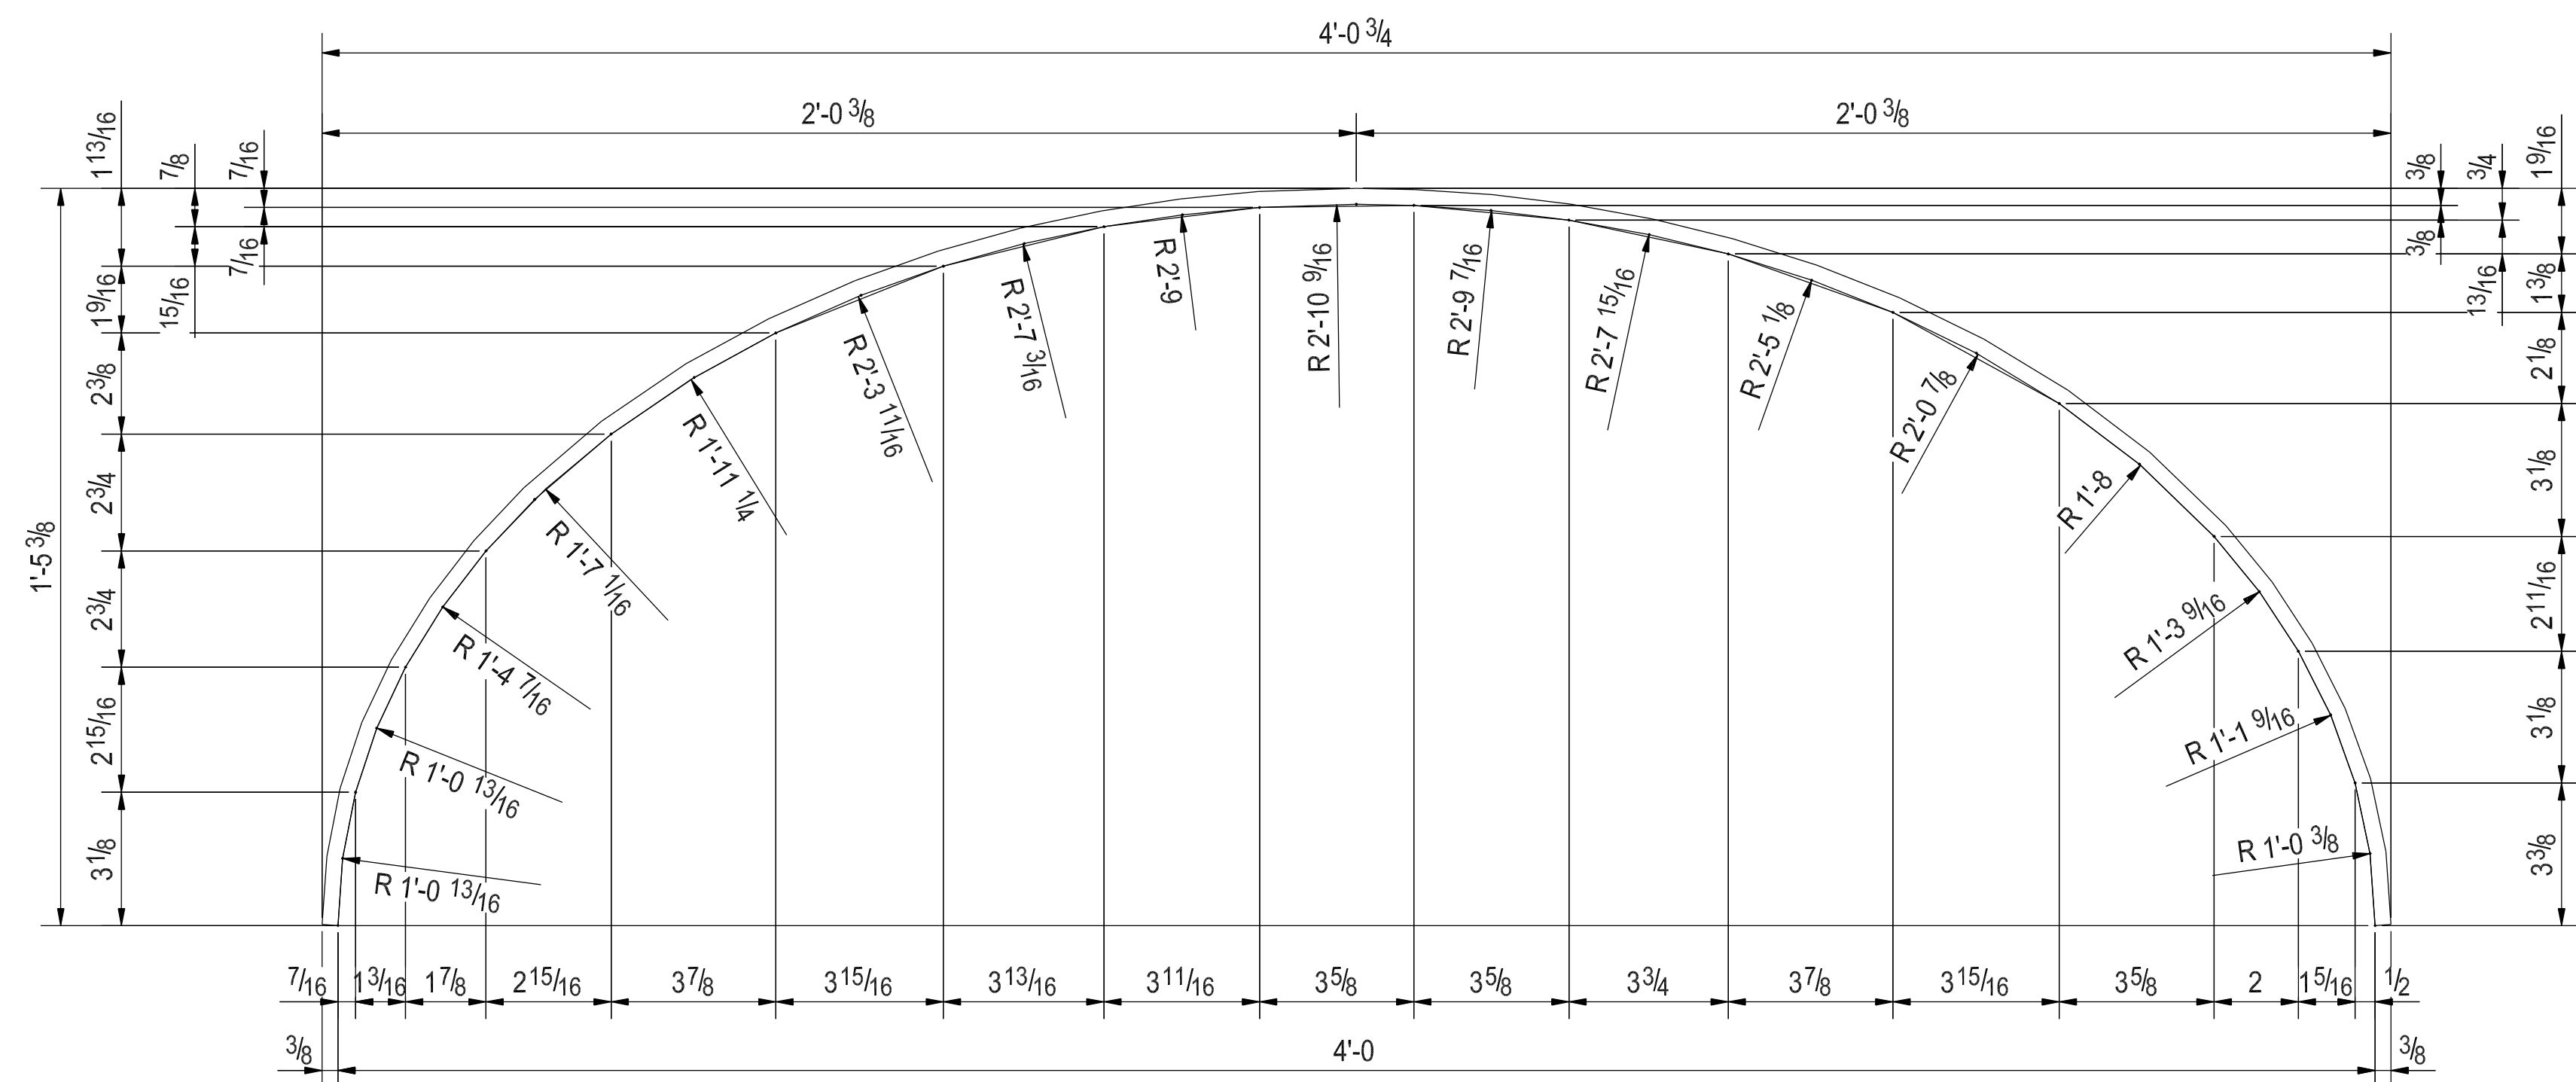


TYPICAL CURVED BRICK SUPPORT PLATE
@ 4'-0" OPENING LOCATION

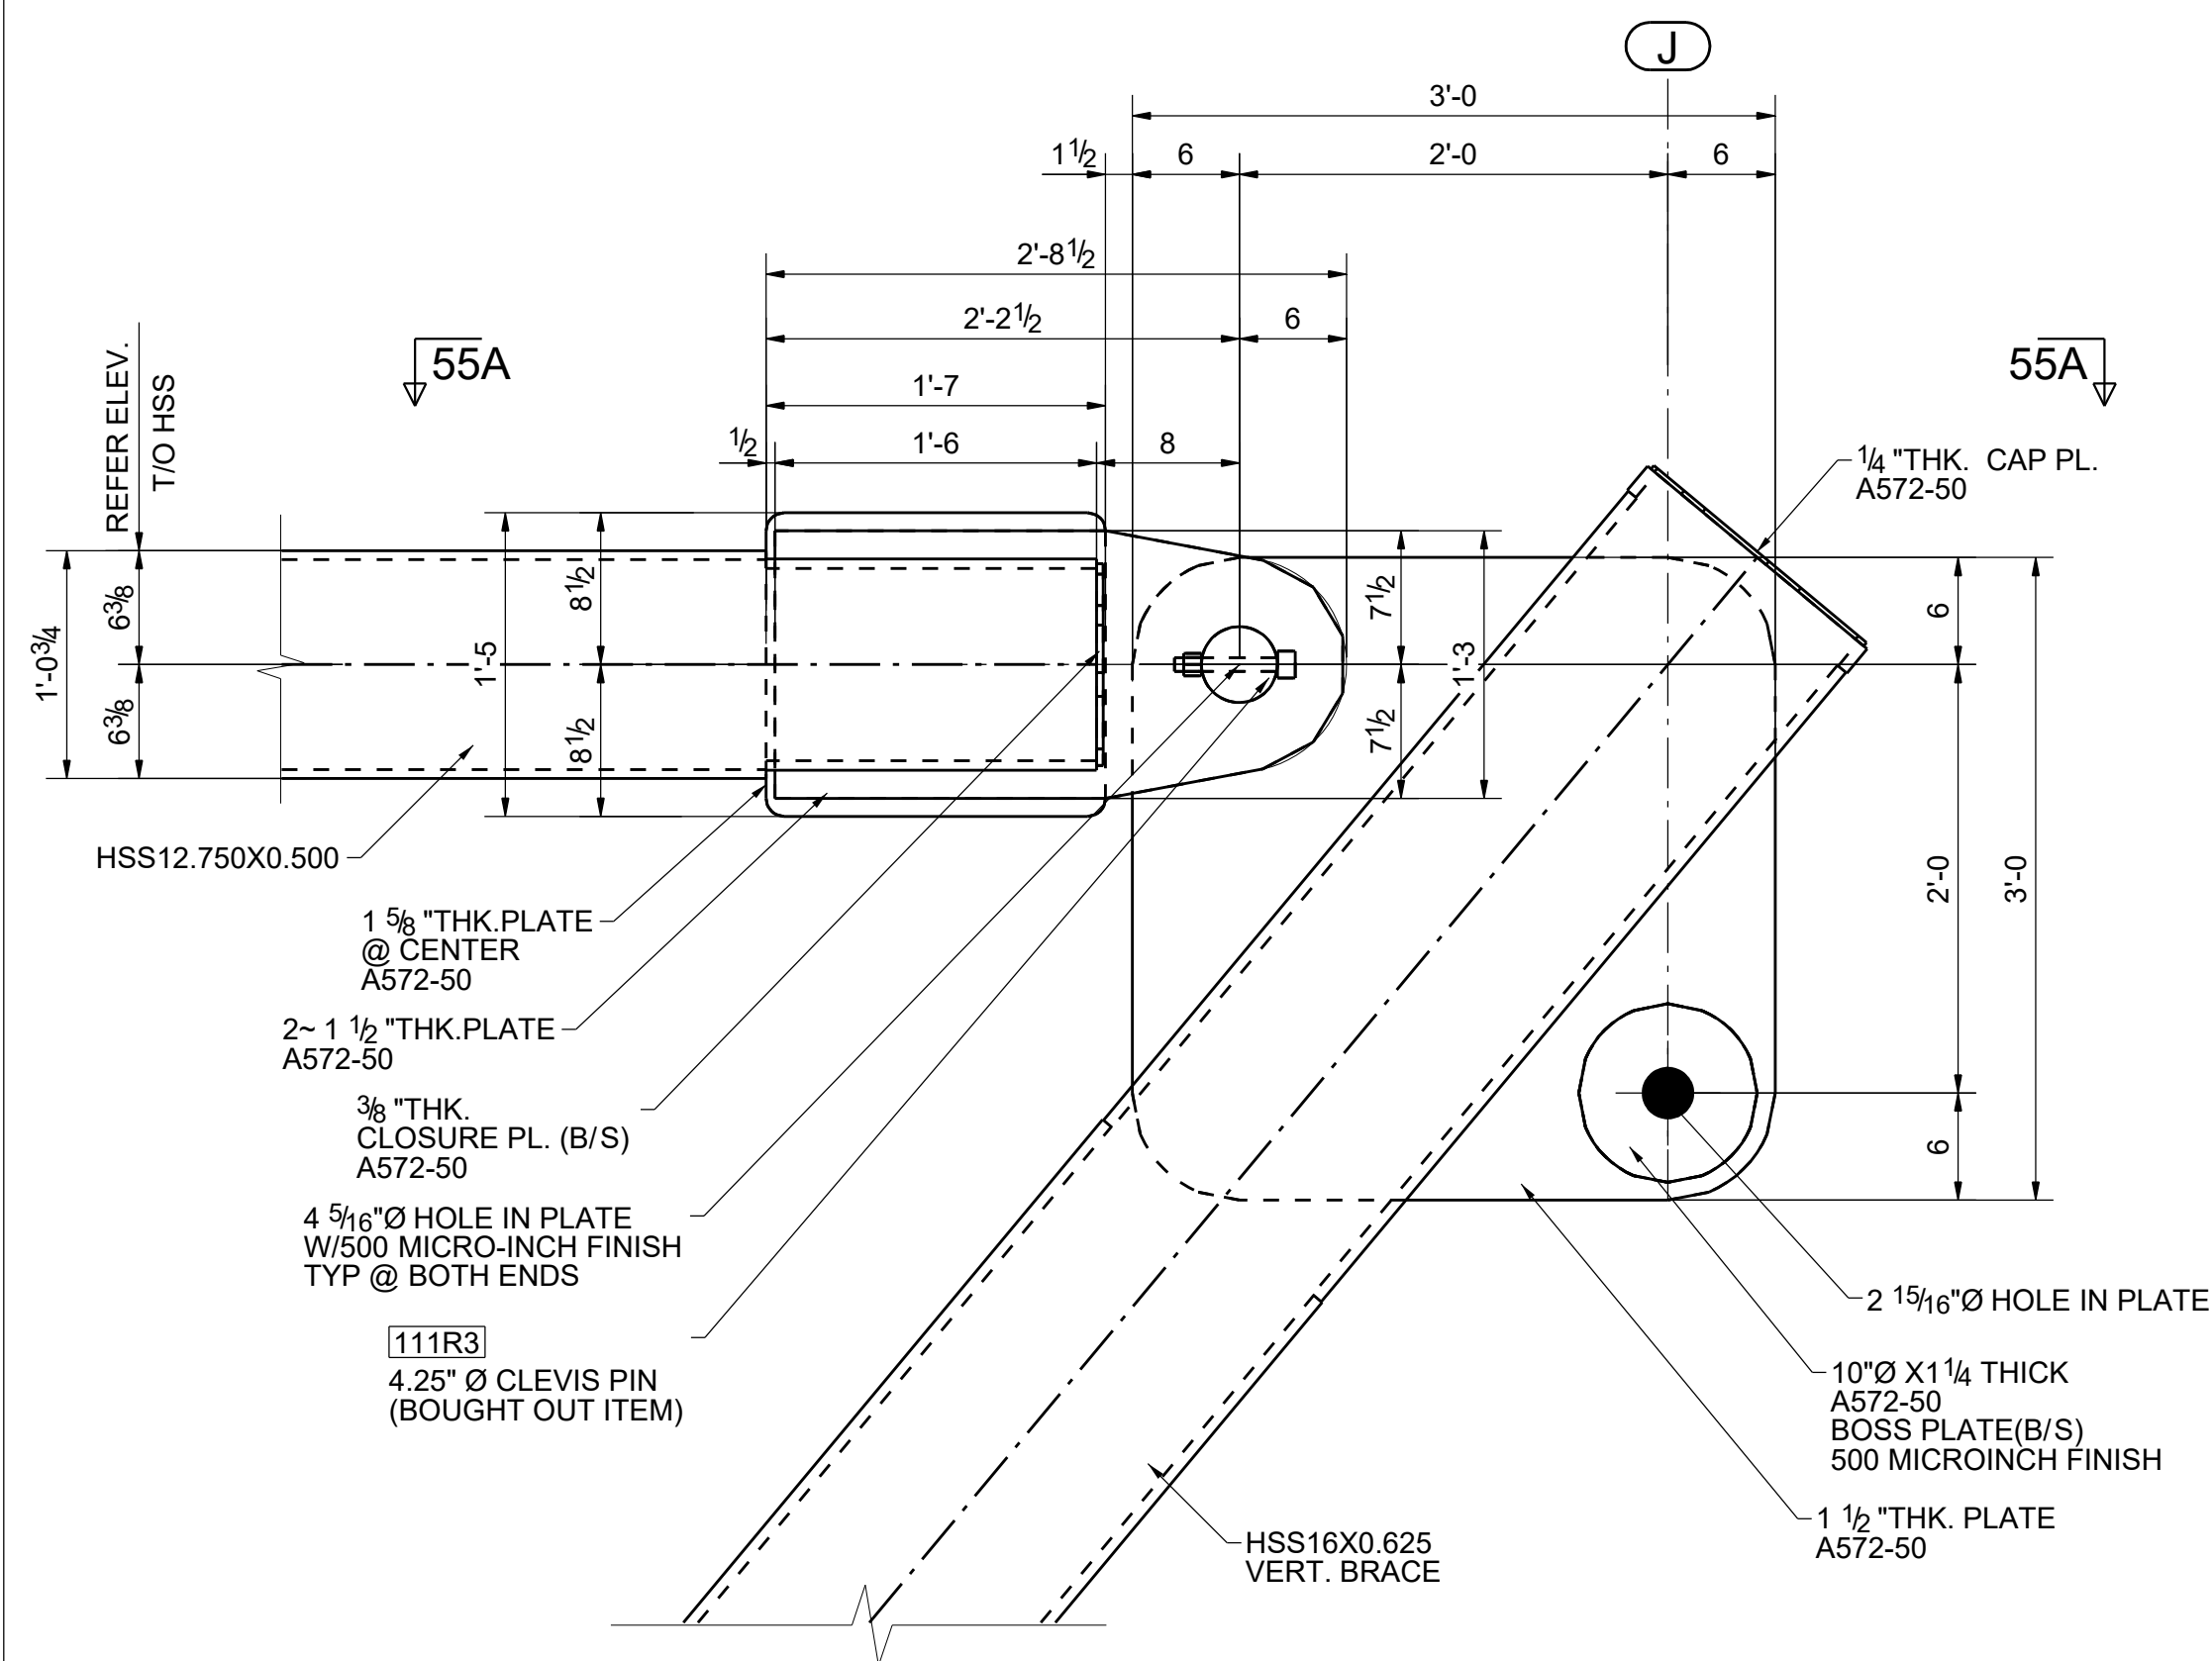


DETAIL 55
E117

(REFER: CANTRY CONNECTION 82B/ S2.07)

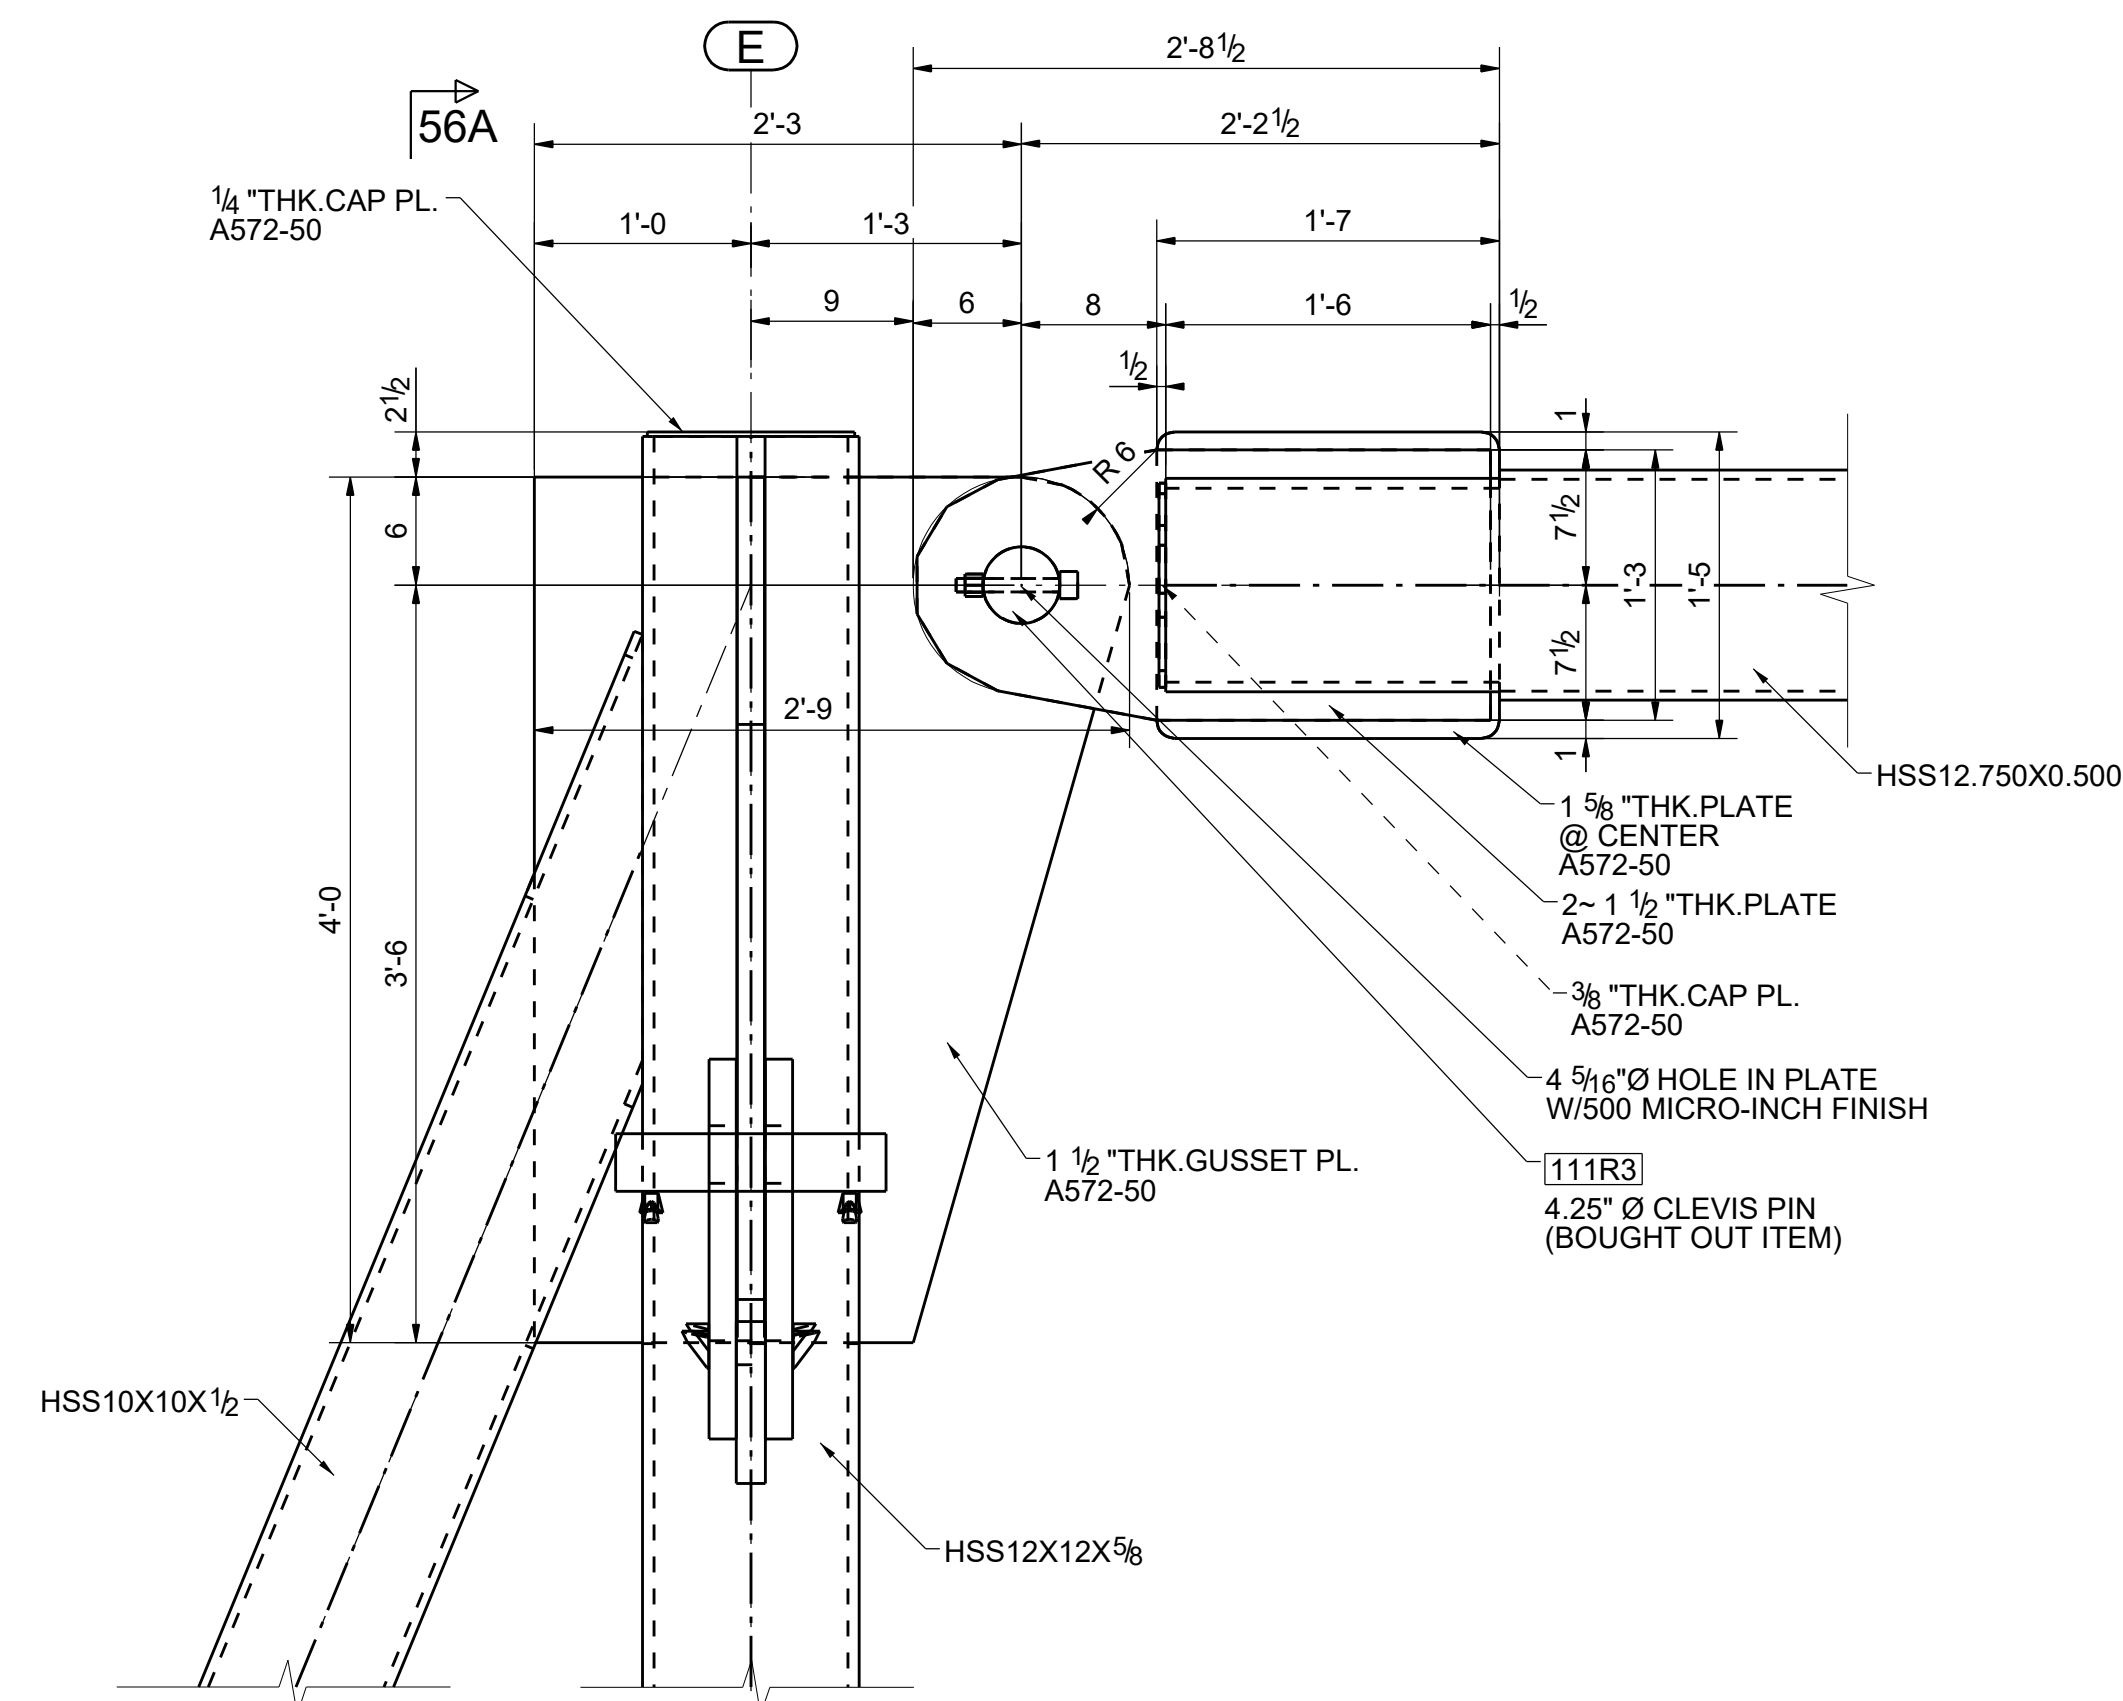


DETAIL 56 - 56
E117

(REFER: SECTION 81A / S2.07)

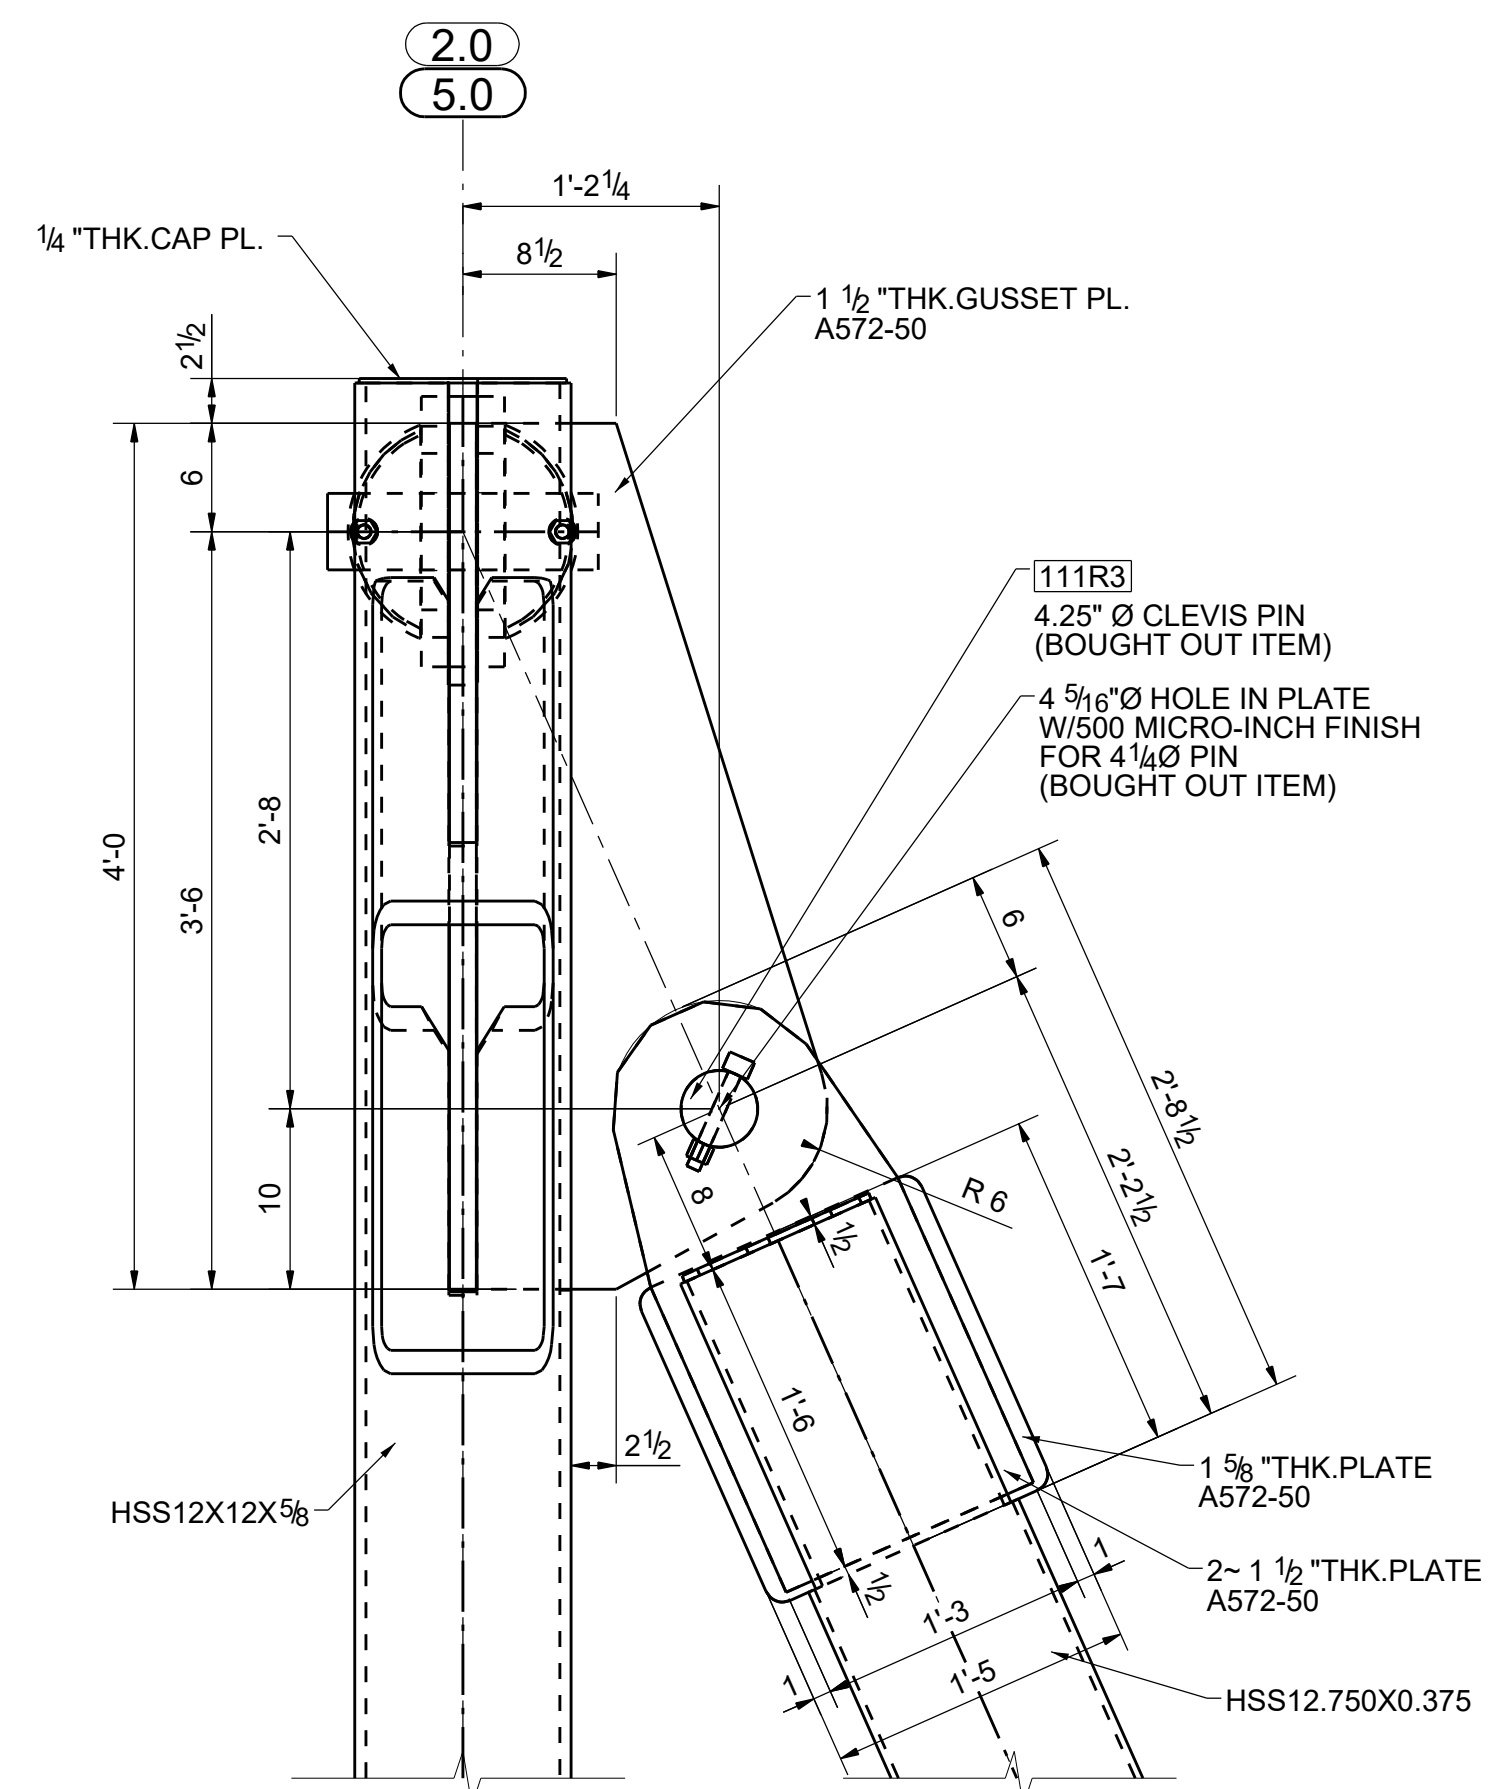


SECTION 56A - 56A

(REFER: SECTION Y / S2.07)

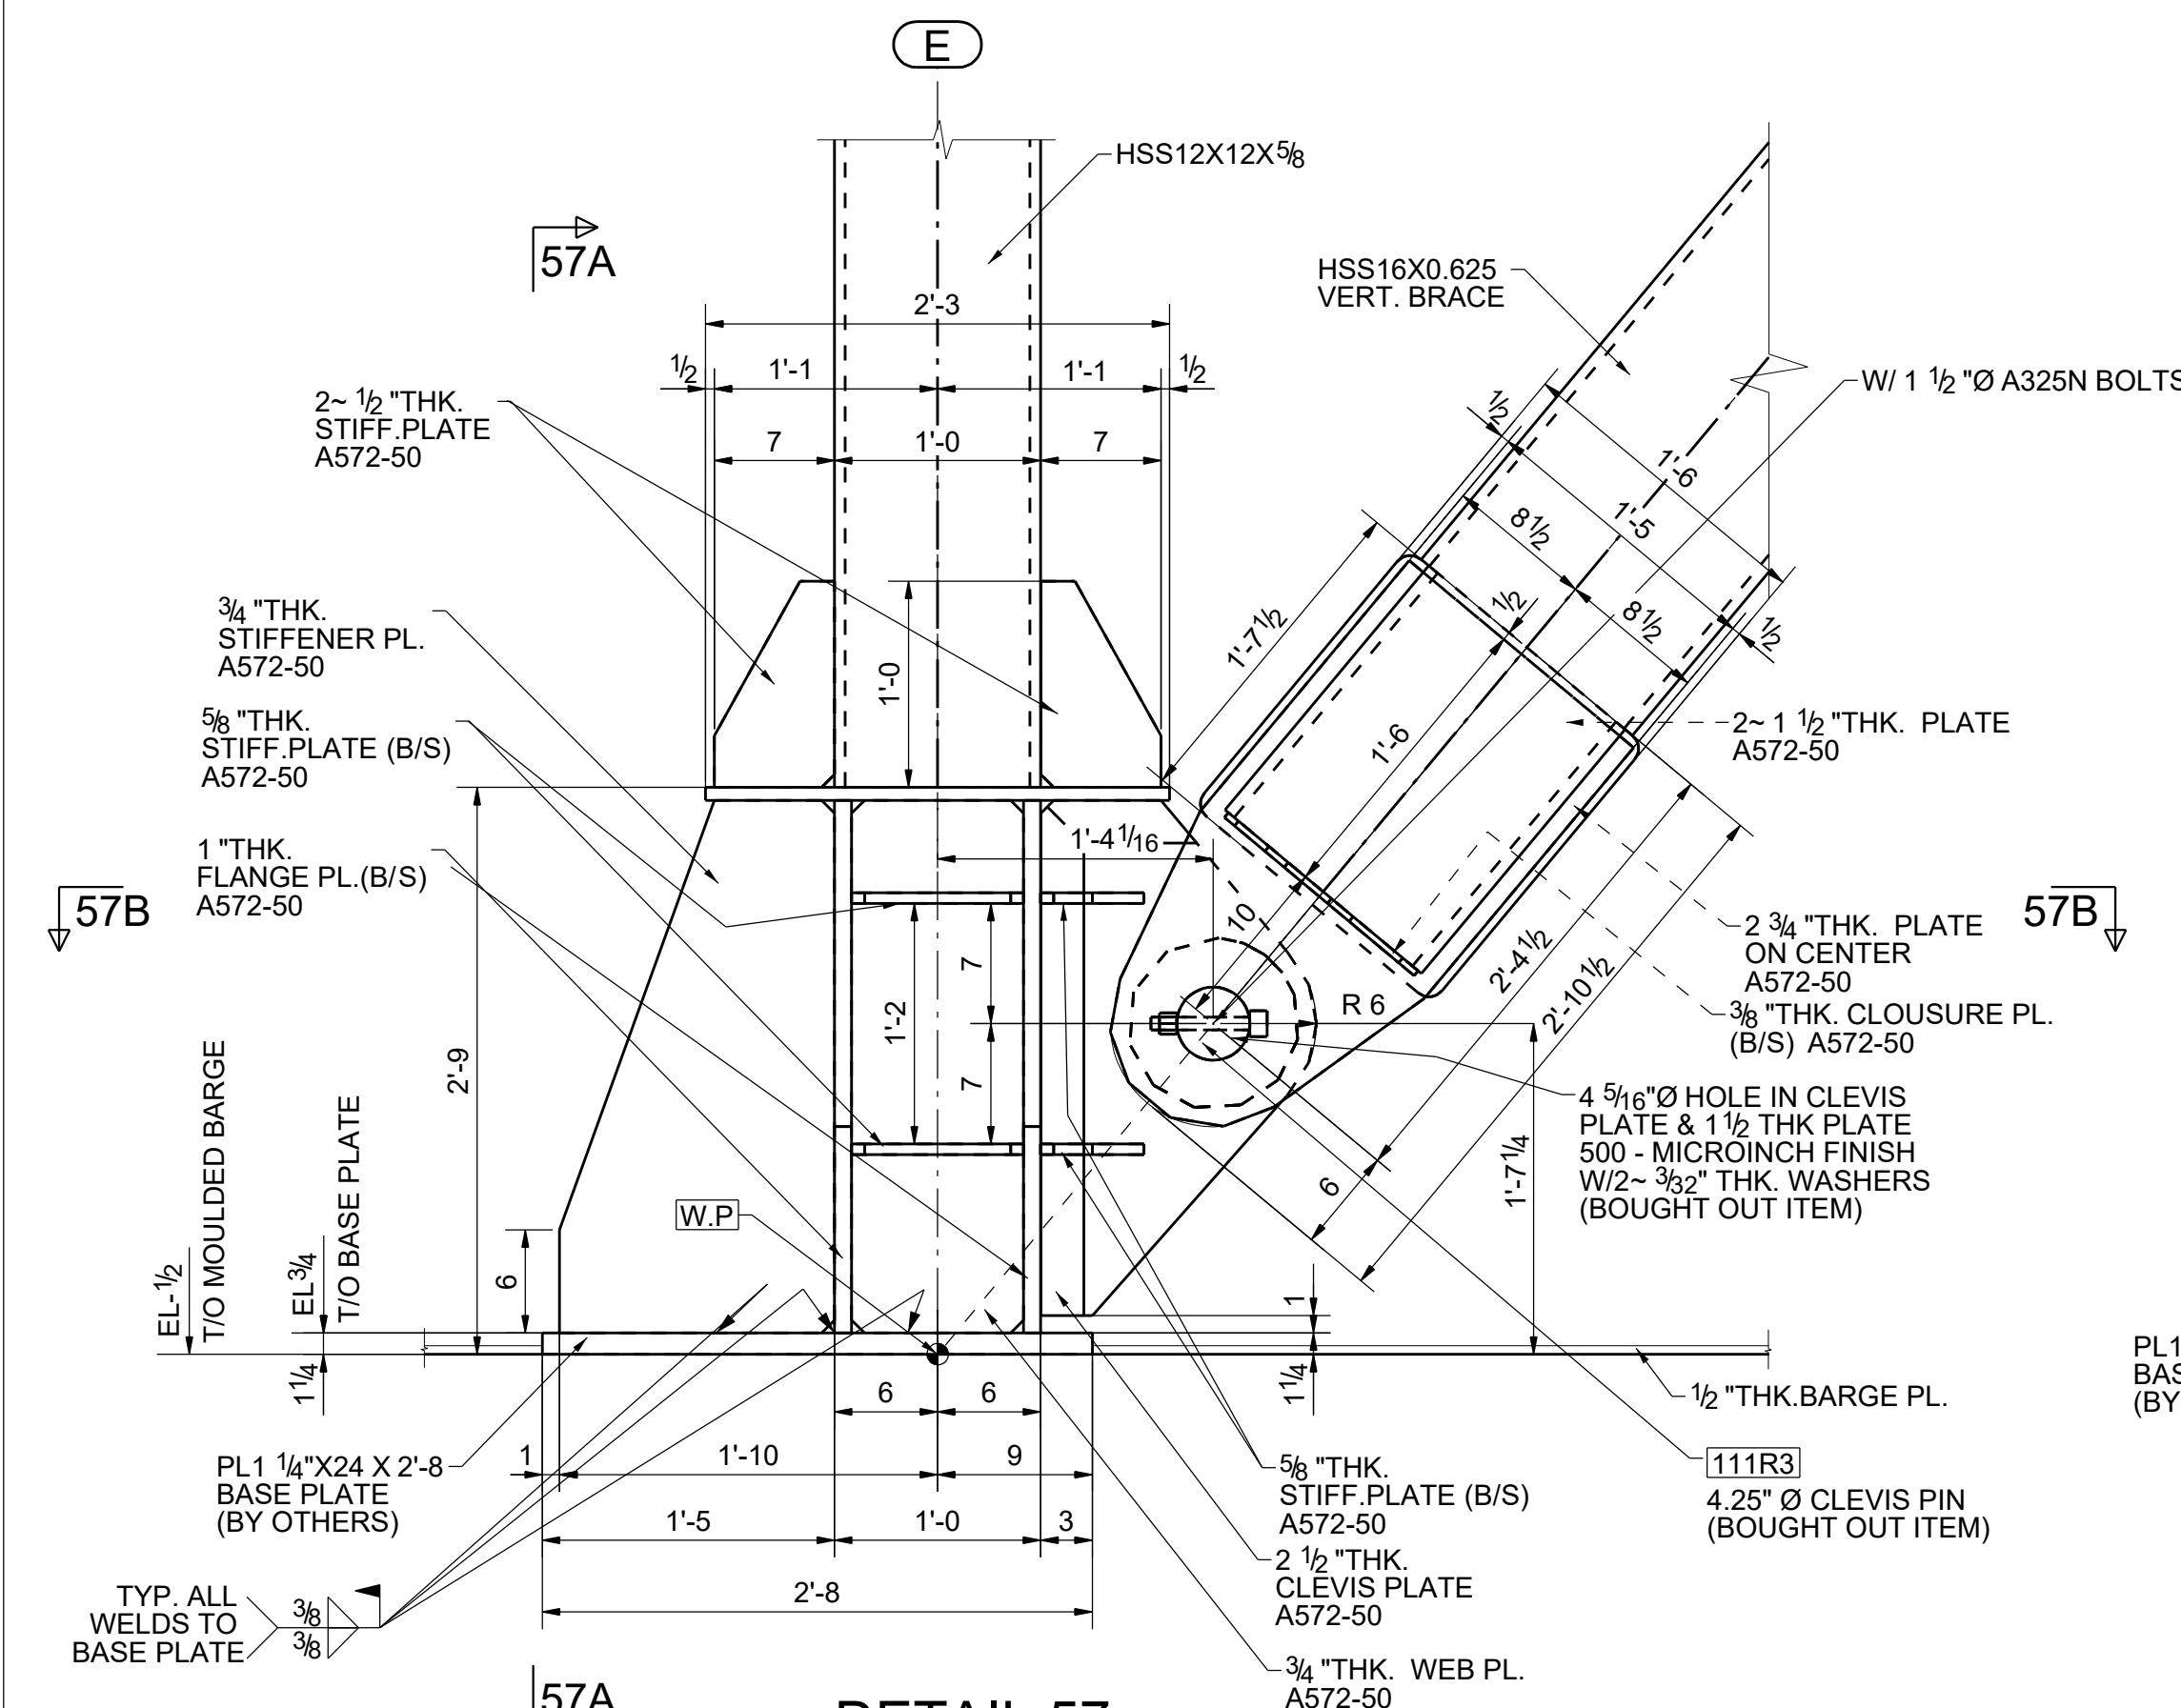


DETAIL 57
E117

(REFER: TRUSS CONNECTION @ BRAGE DECK 83/ S2.09)

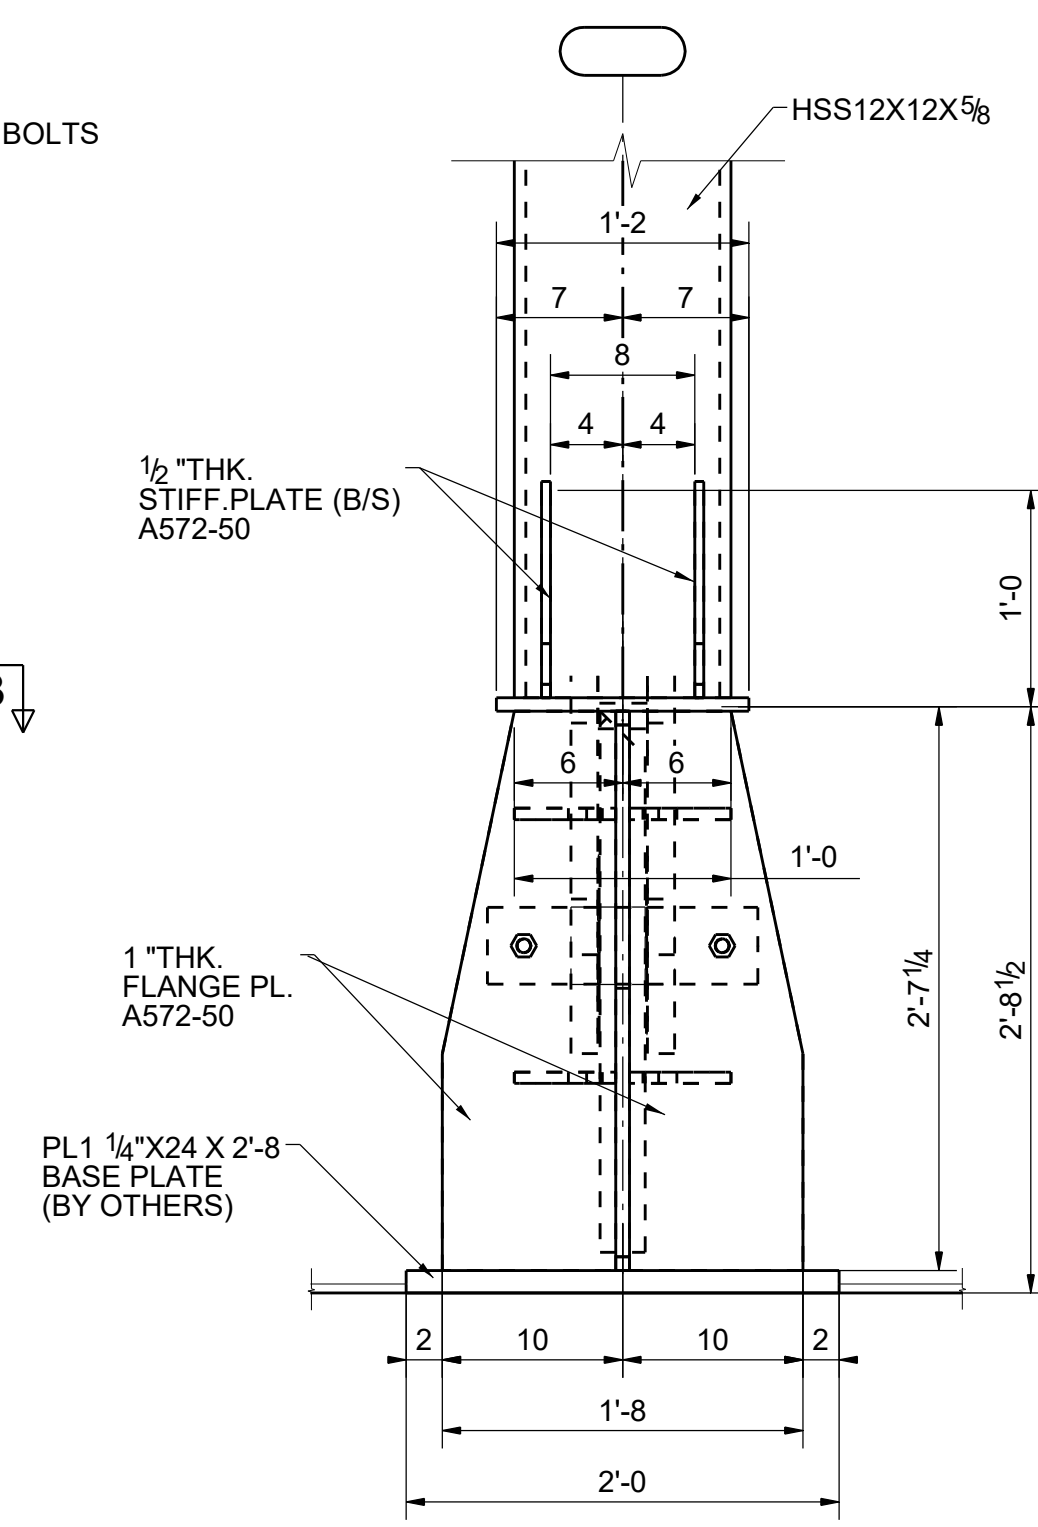


SECTION 57A - 57A

(REFER: SECTION W / S2.09)

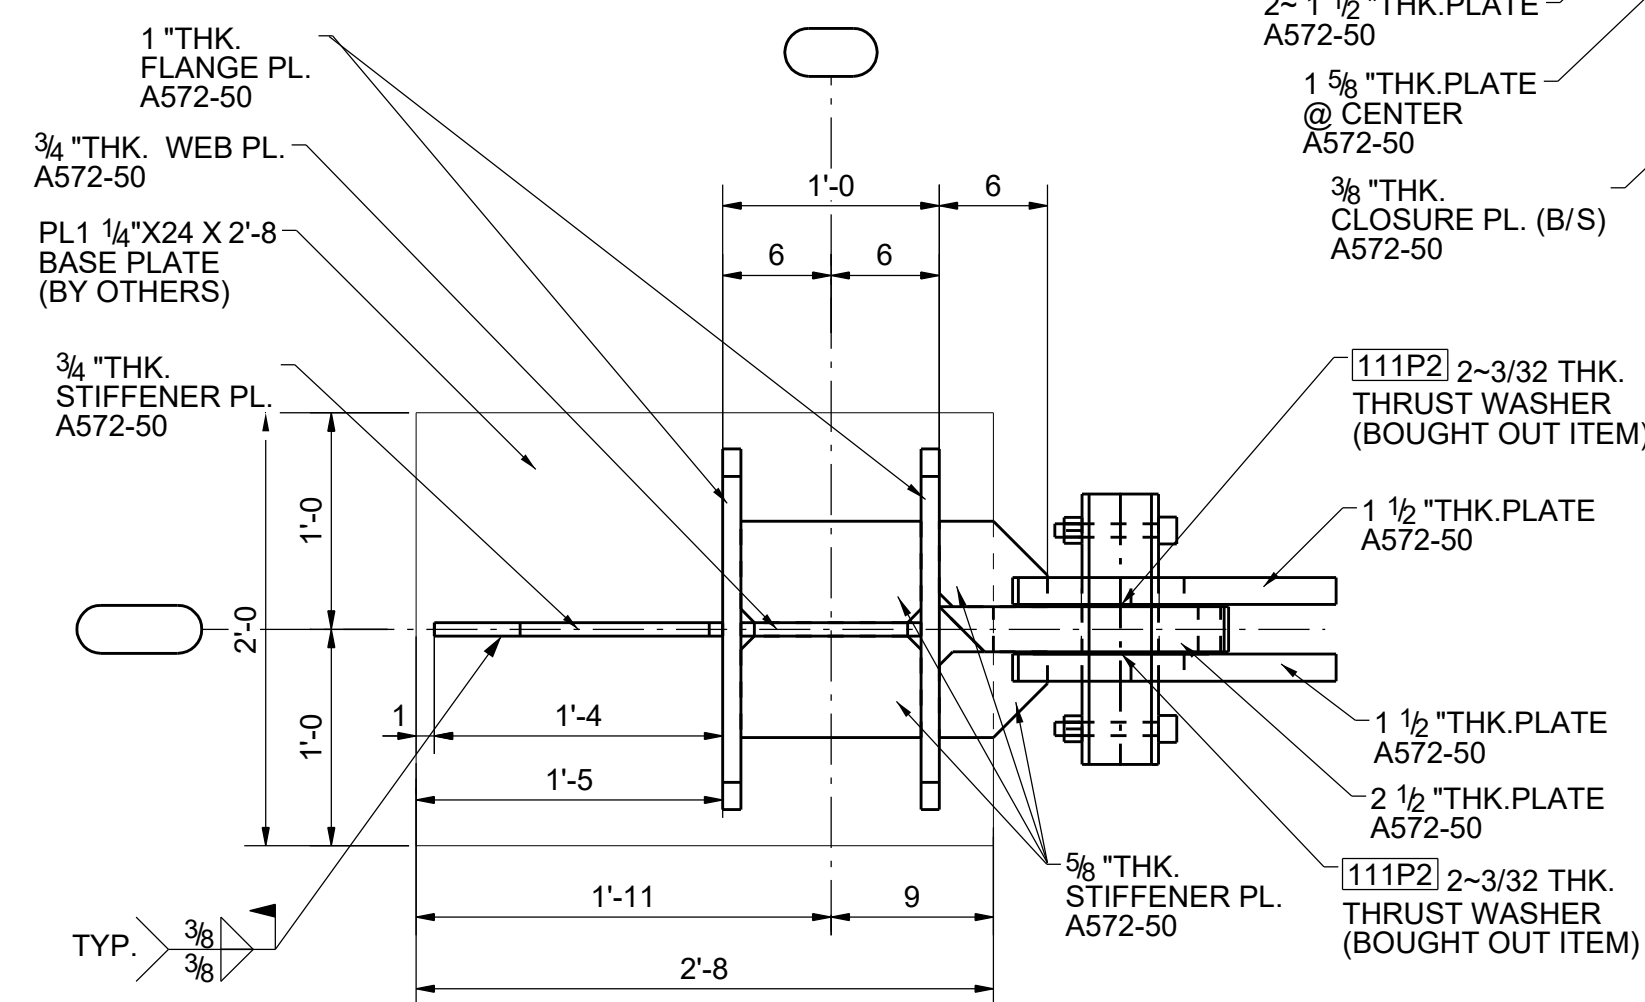





SECTION 57B - 57B

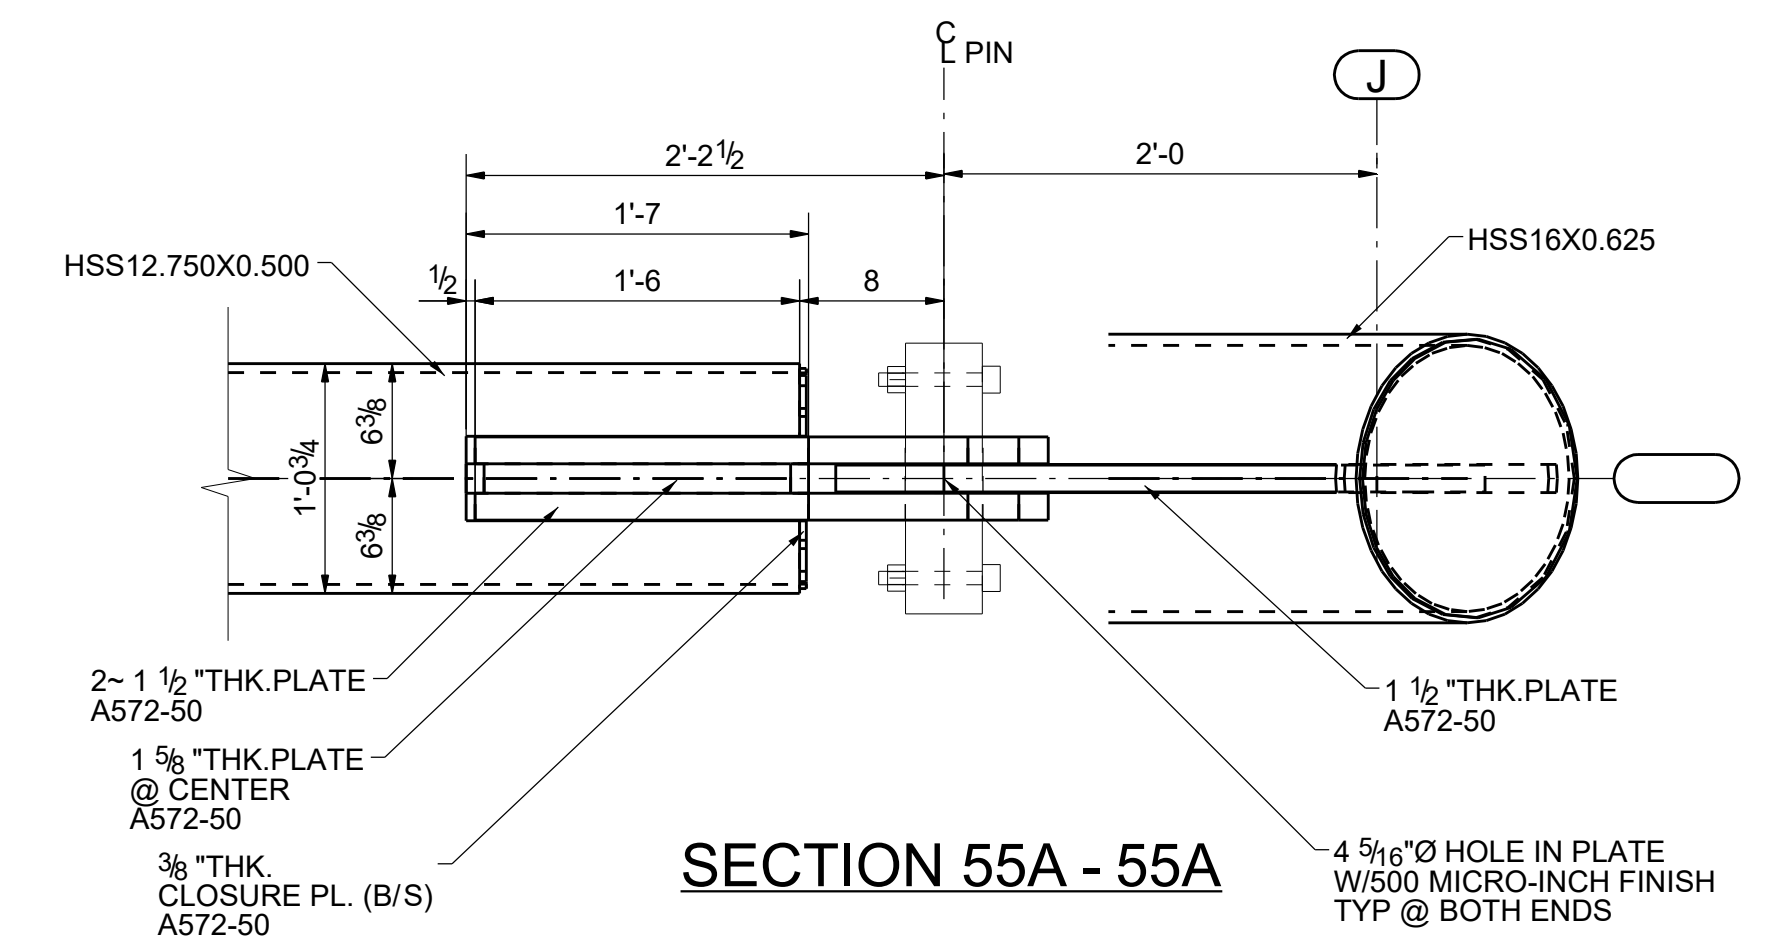

SECTION 55A - 55A


NOTES:-

1. REFER E100 SHEET FOR GENERAL NOTES.

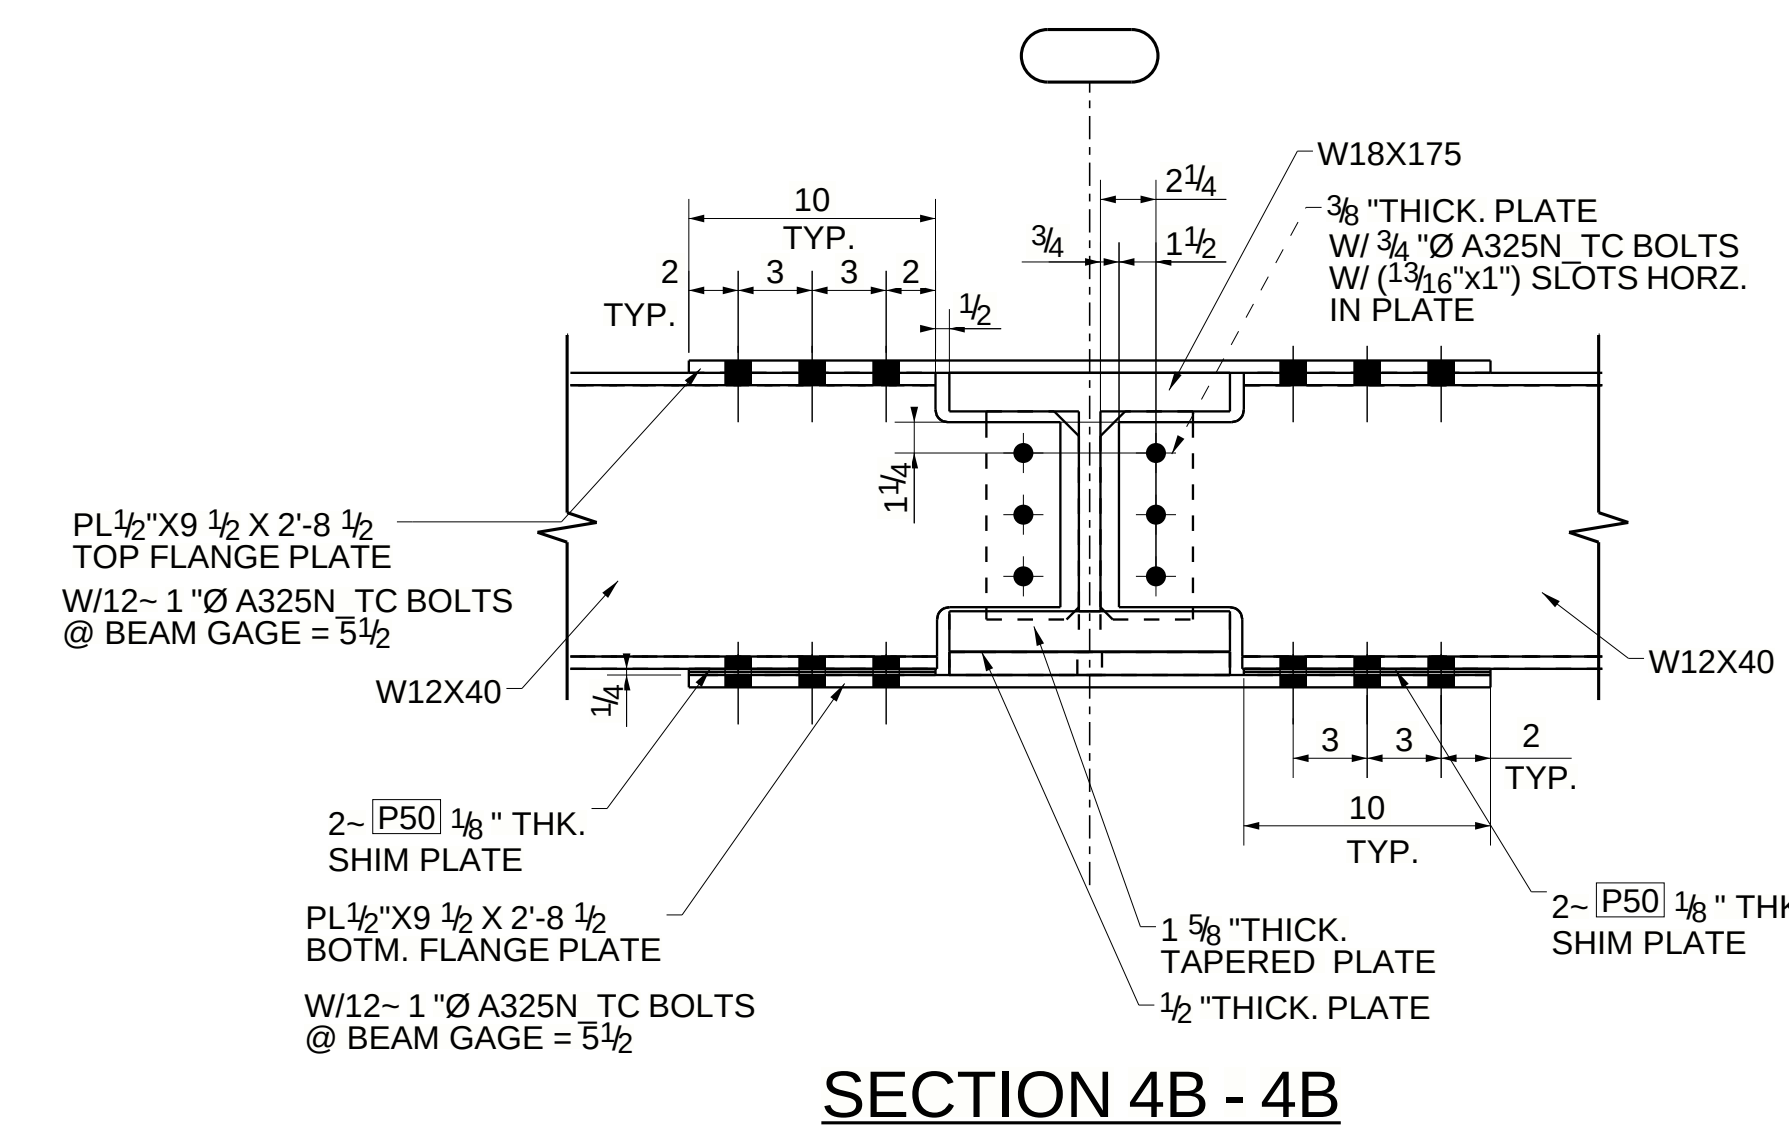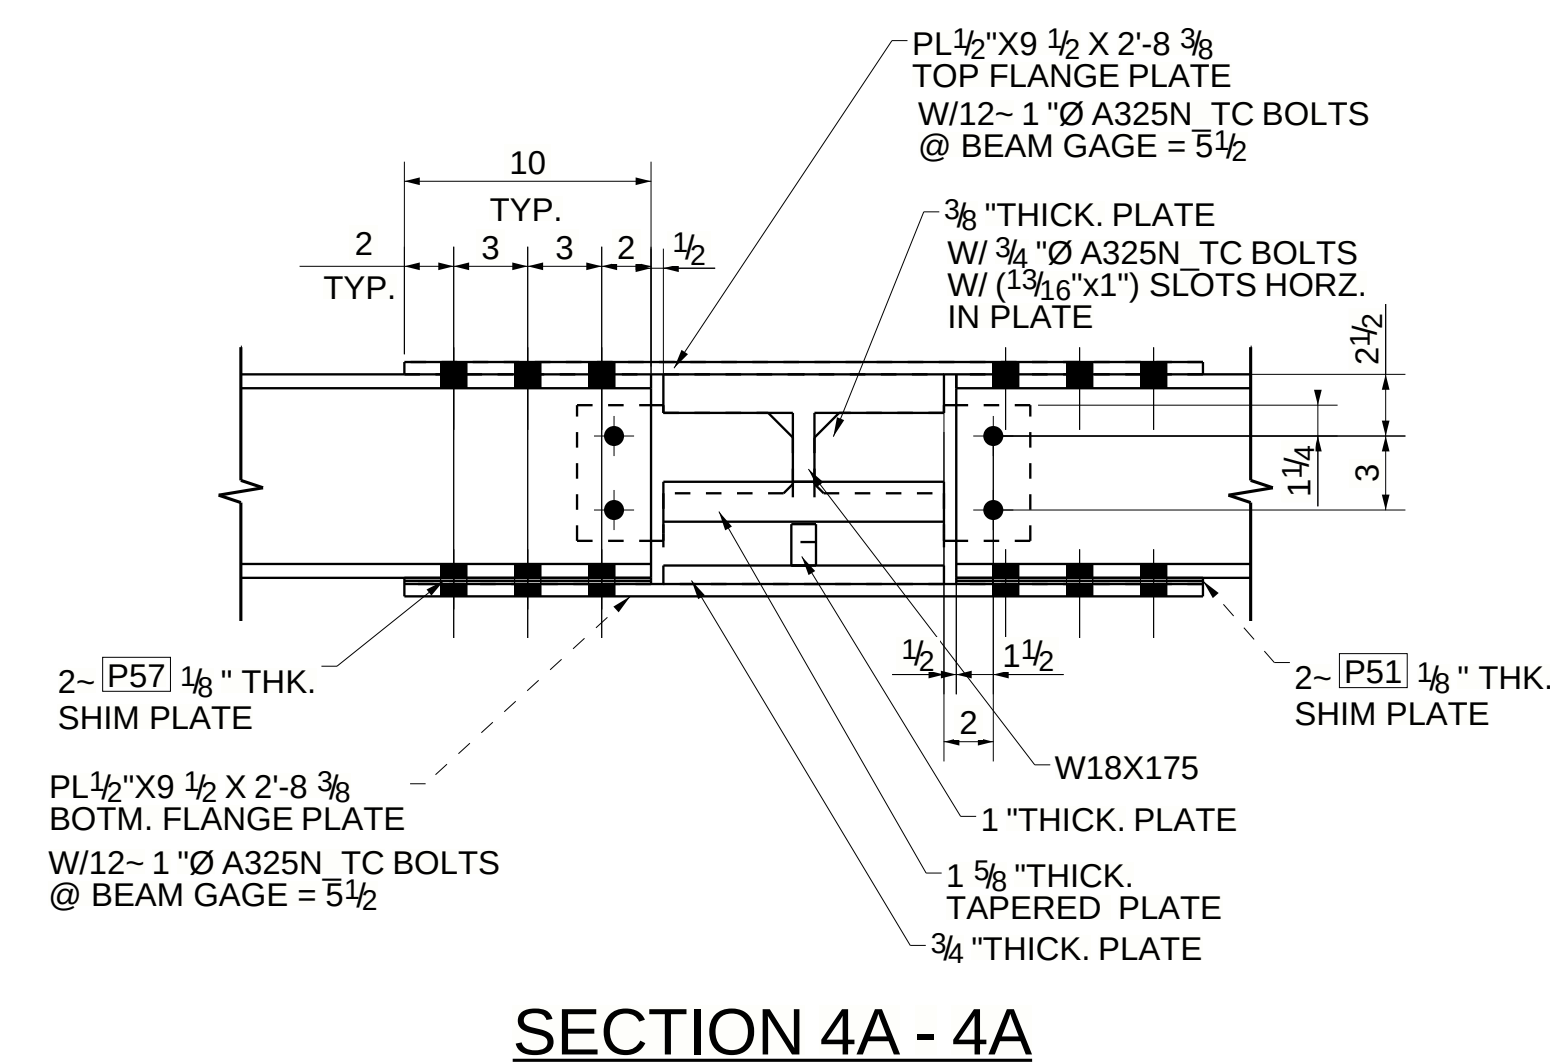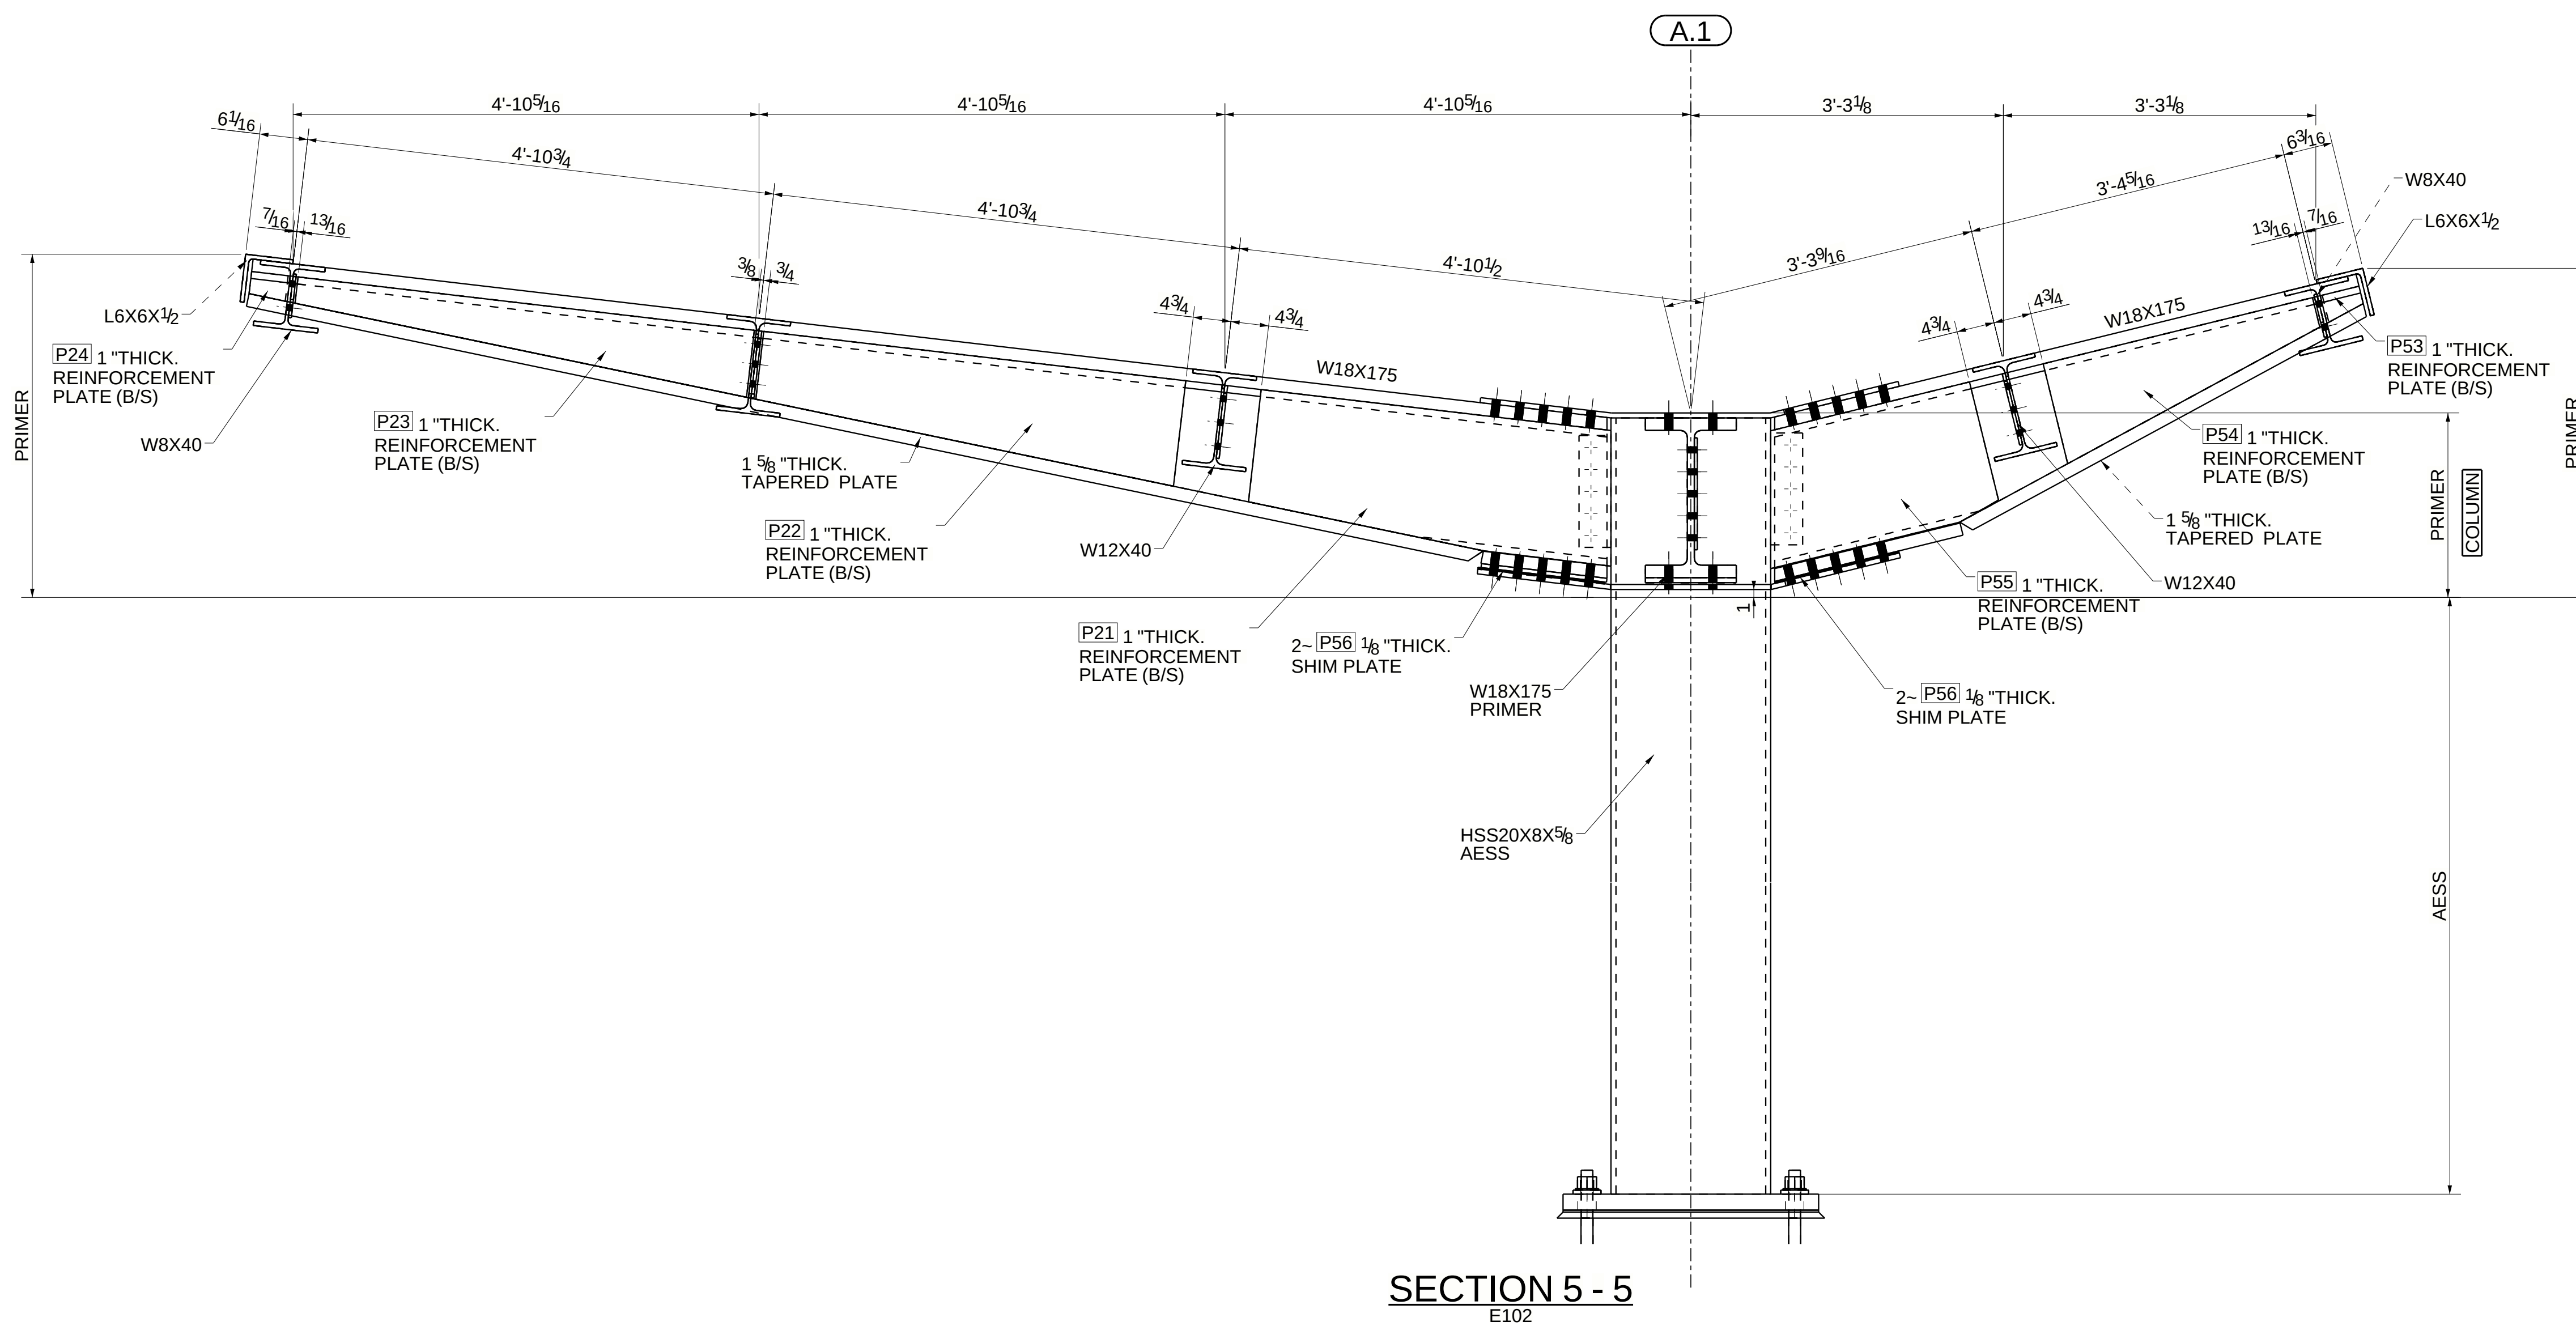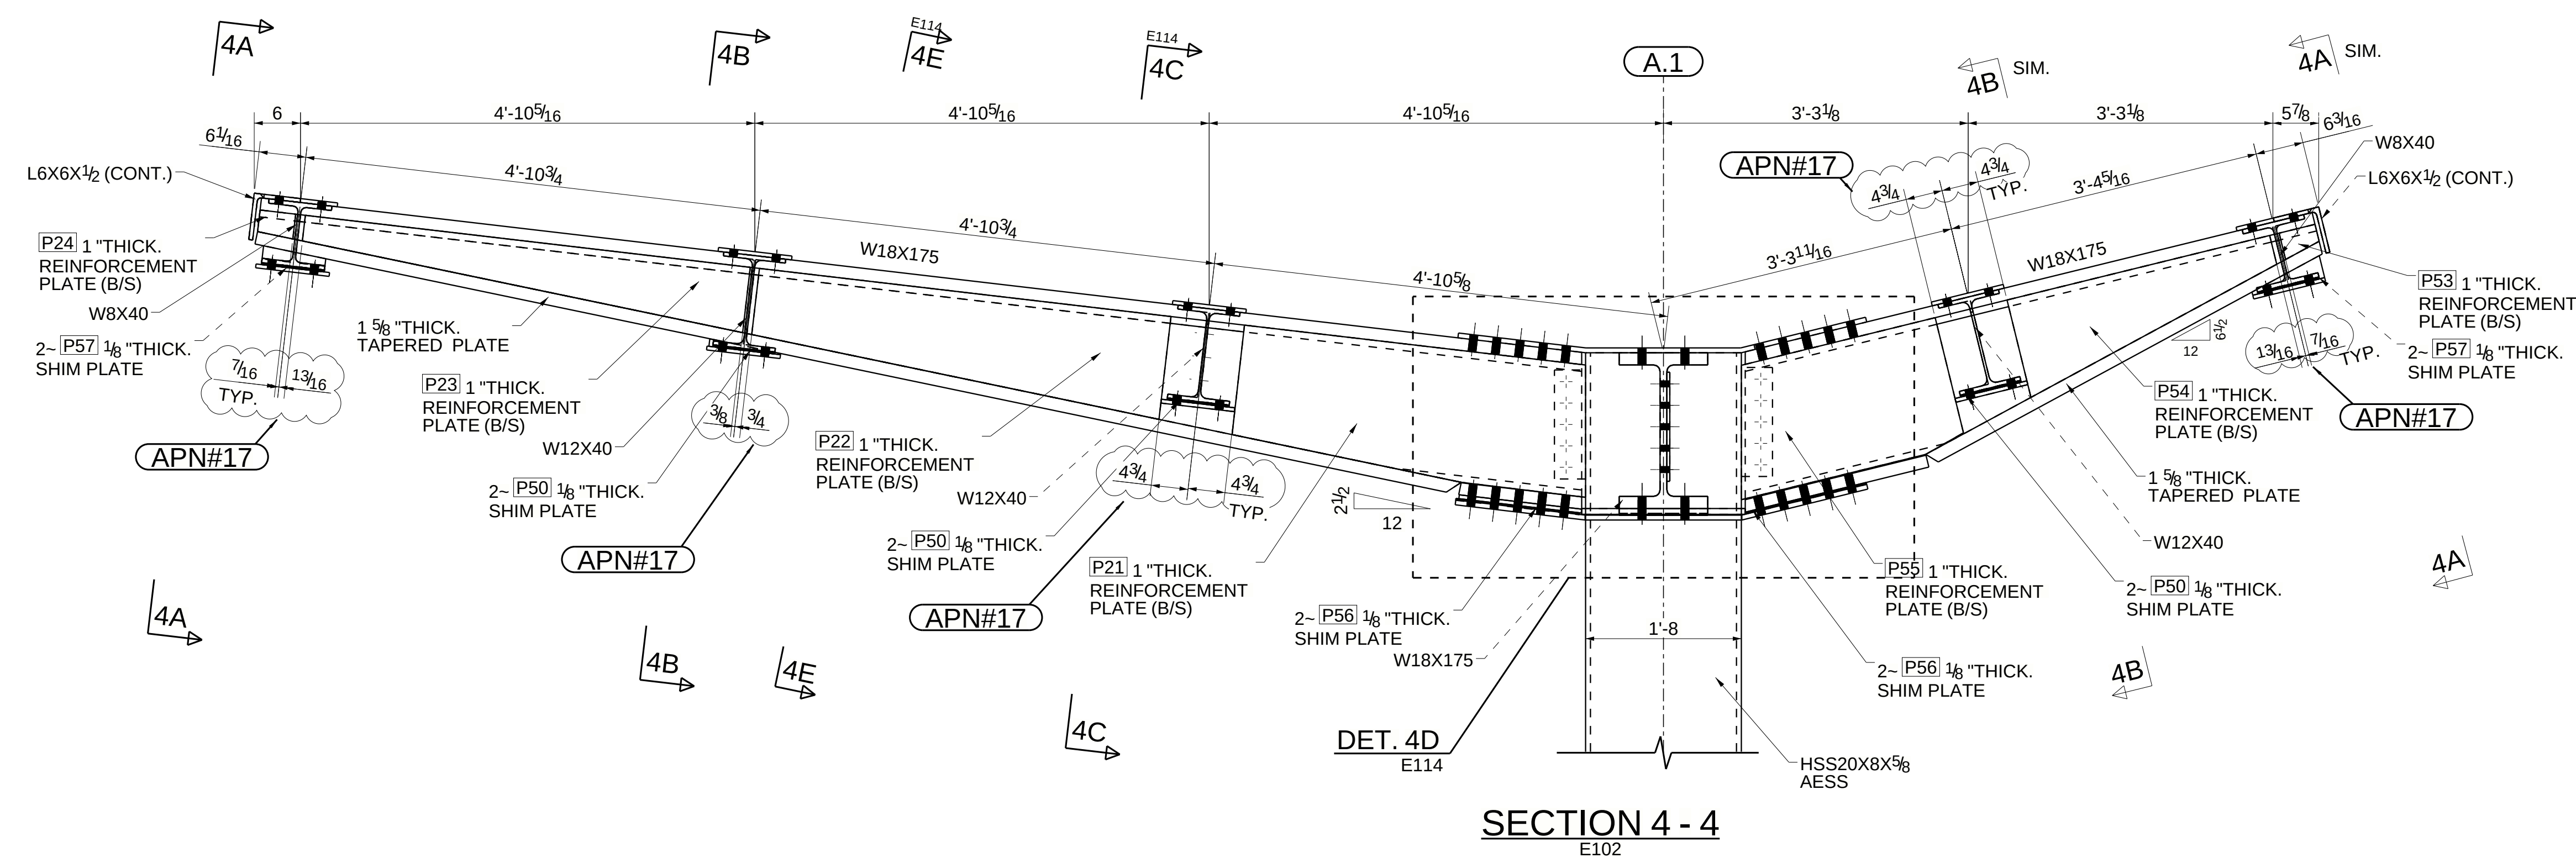


APPROVER VERIFY REINFORCEMENT PLATE
ARRANGEMENT AND LOCATING DIMENSION.


APPROVER VERIFY ALL CLOUDED INFORMATION TYPICAL.
THRU E113 TO E127 SHEETS.

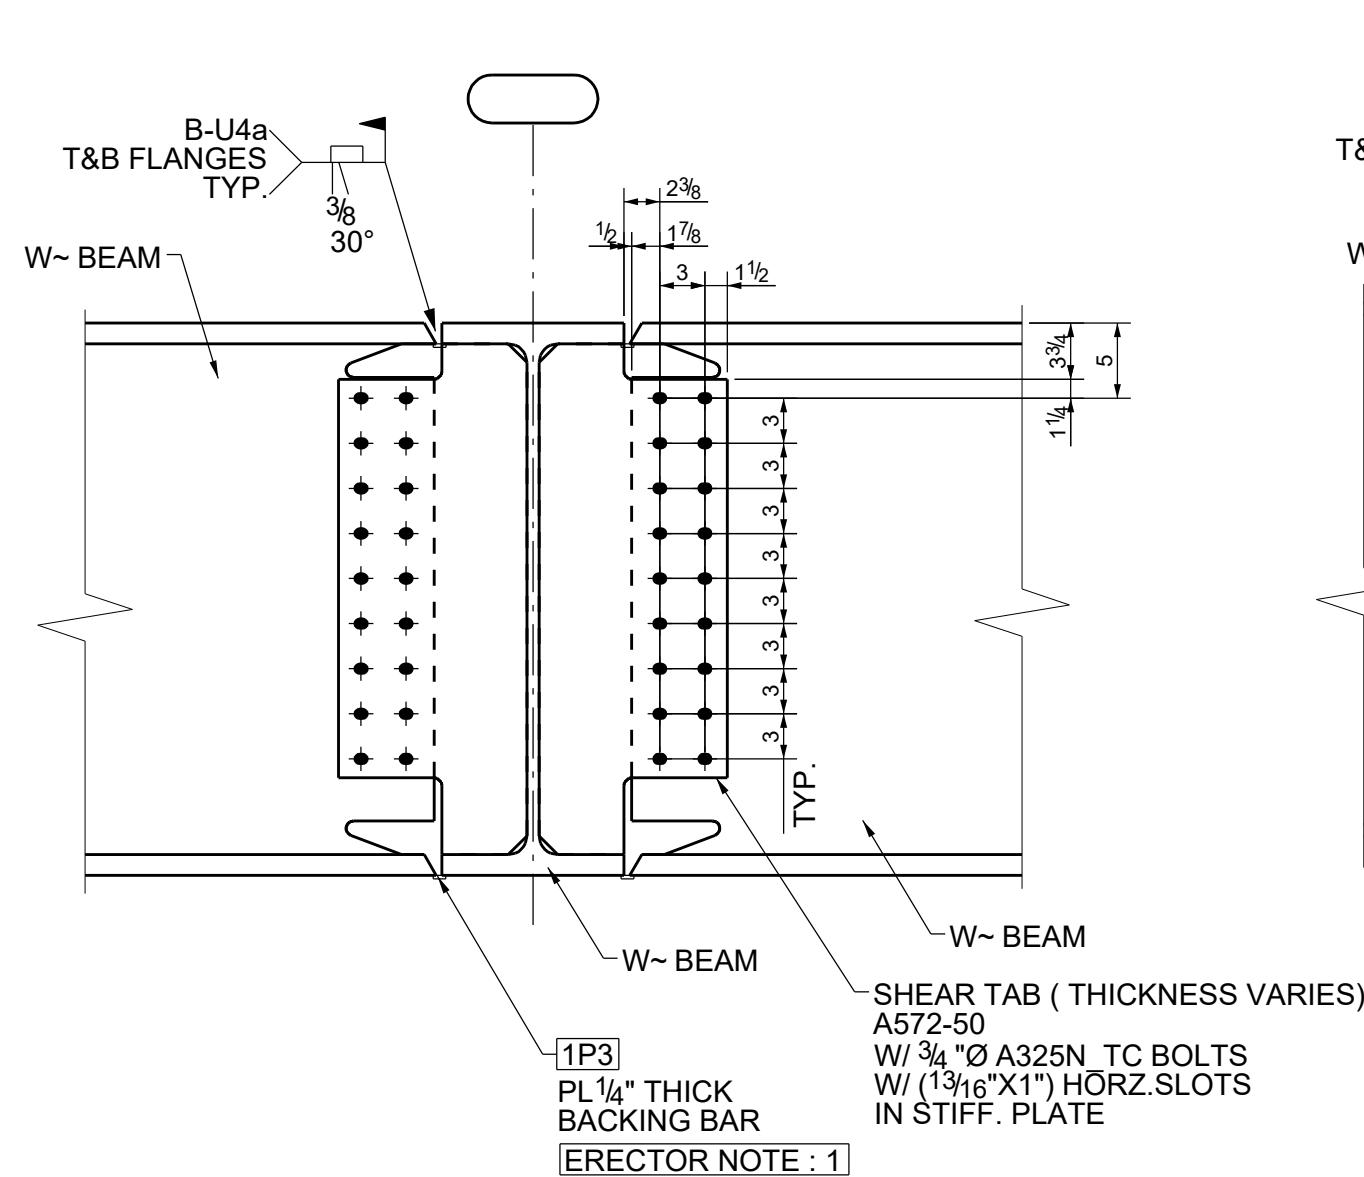


**TYPICAL BEAM TO BEAM
MOMENT CONNECTION DETAIL**

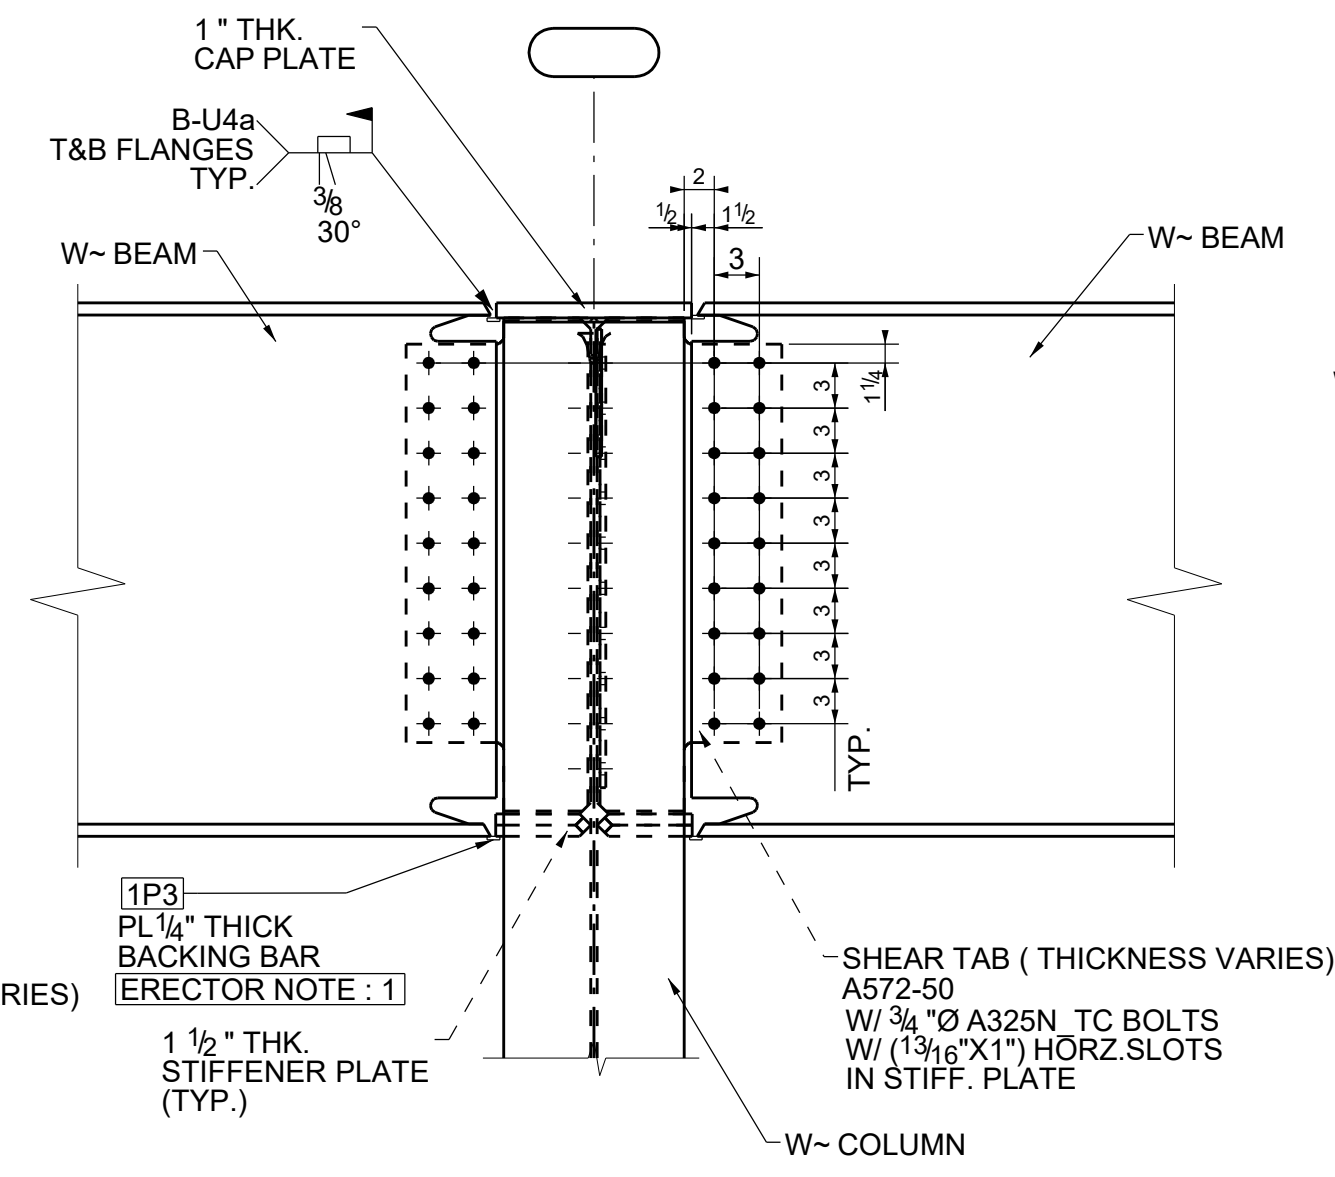


**W~ BEAM TO W~COLUMN WEB
MOMENT CONNECTION**

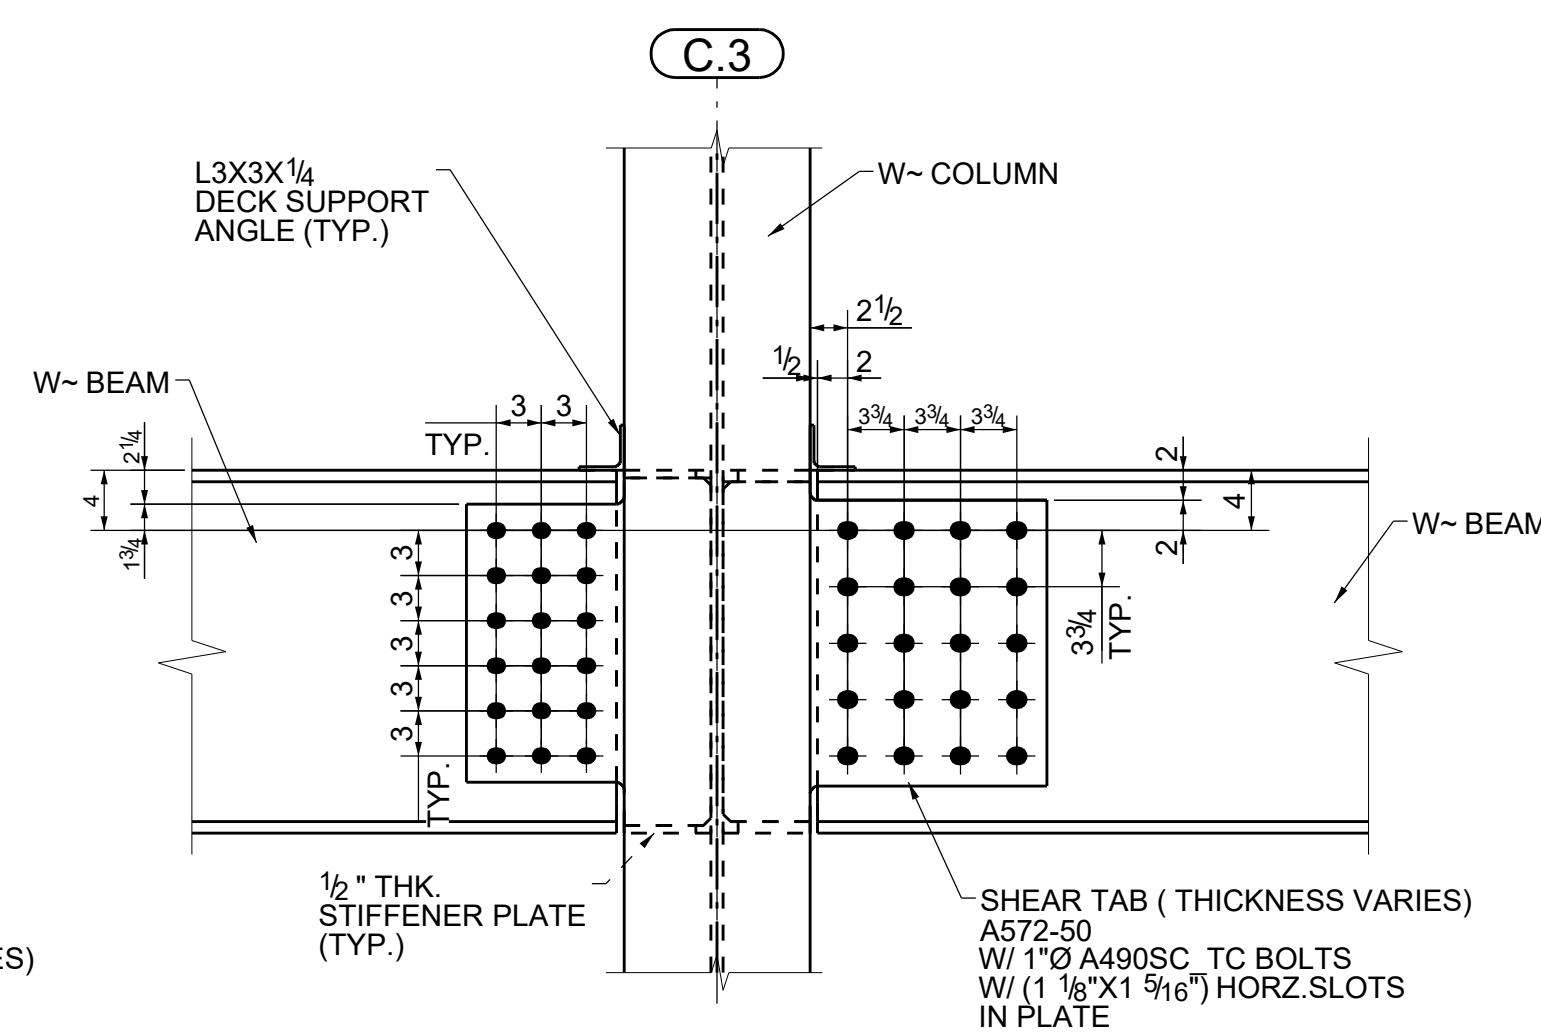

**W~ BEAM TO W~COLUMN WEB
SHEAR TAB CONNECTION**

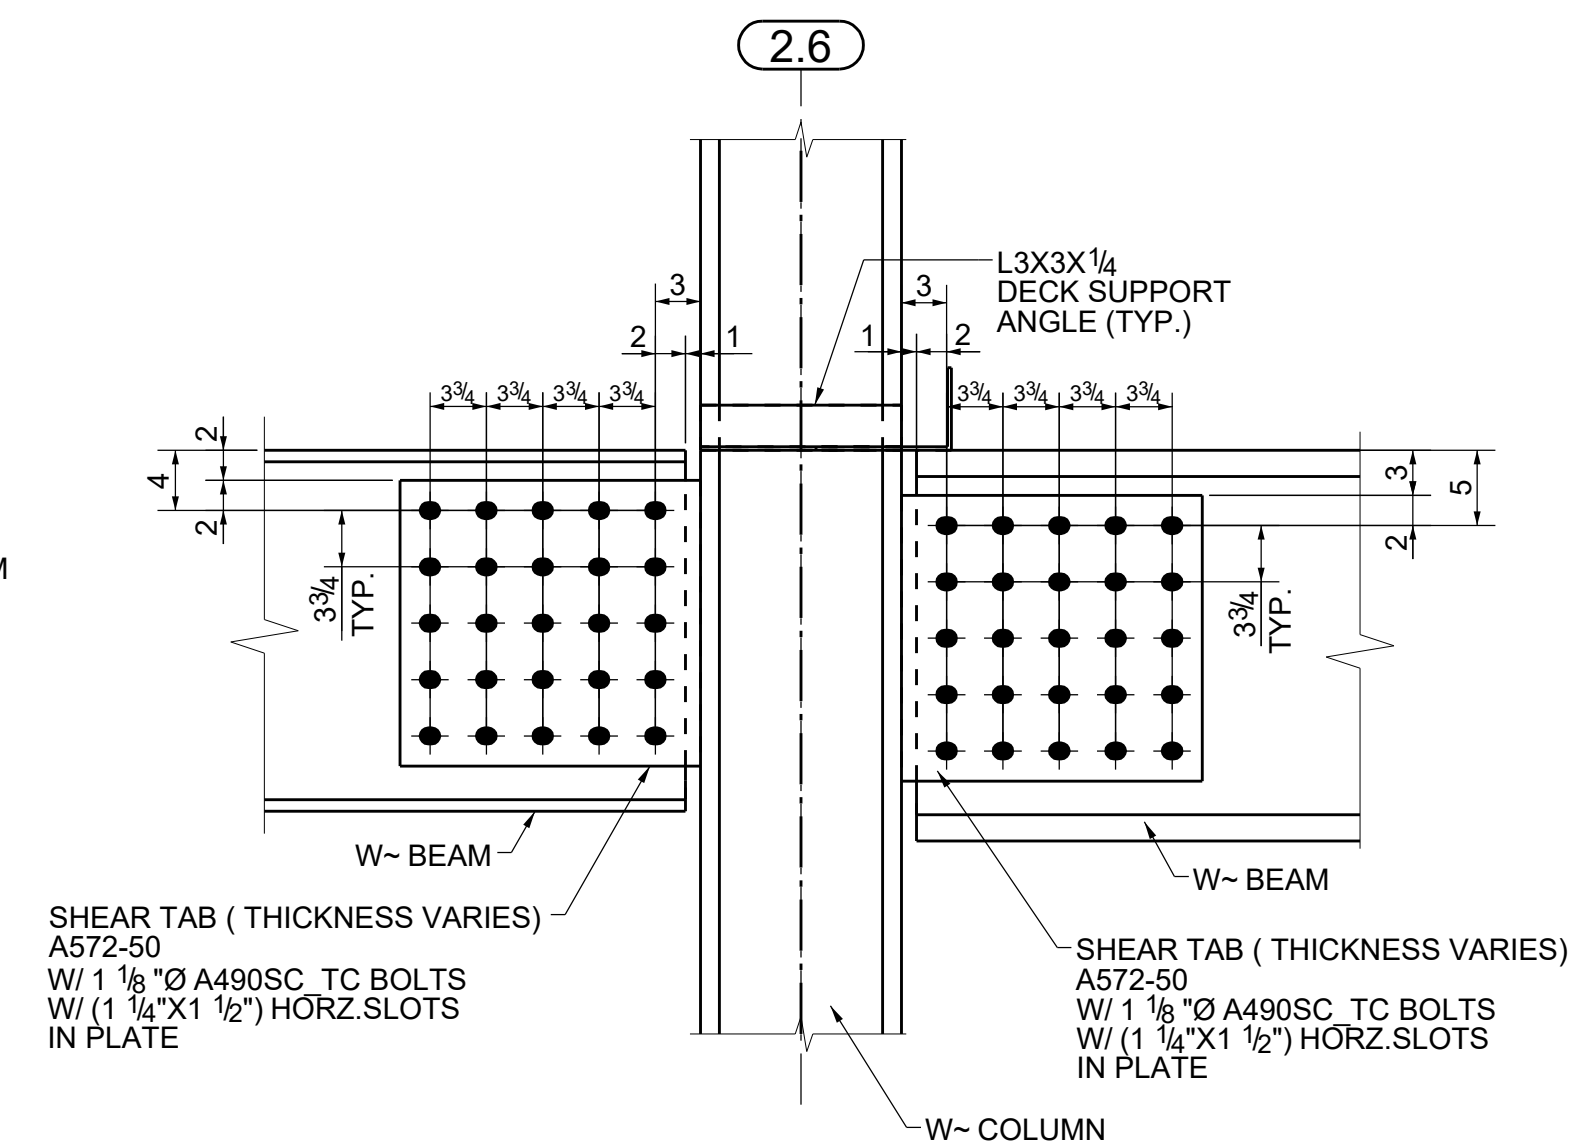


**W~ BEAM TO W~COLUMN FLANGE
SHEAR TAB CONNECTION**

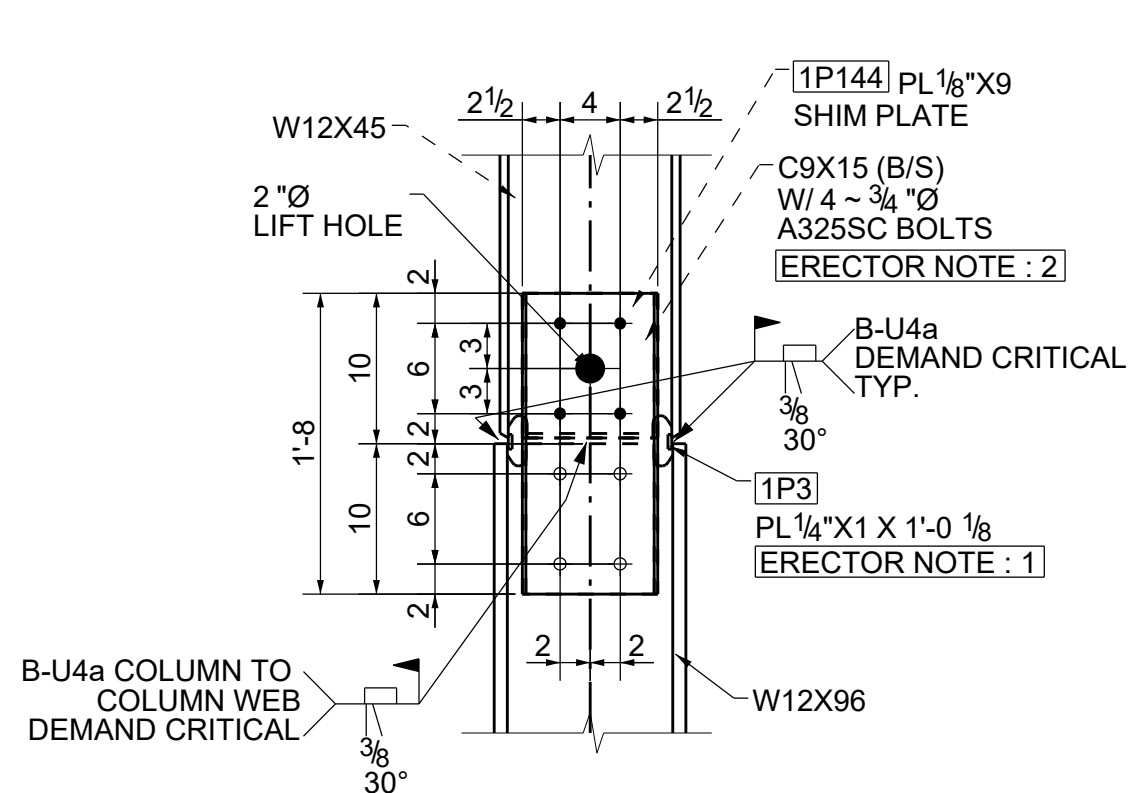


**TYPICAL W12X96 COLUMN TO W12X45 COLUMN
SPLICE CONNECTION DETAILS
@ BRACE LOCATION**

SEE 1-E110 FOR DEMAND
CRITICAL WELD NOTE.

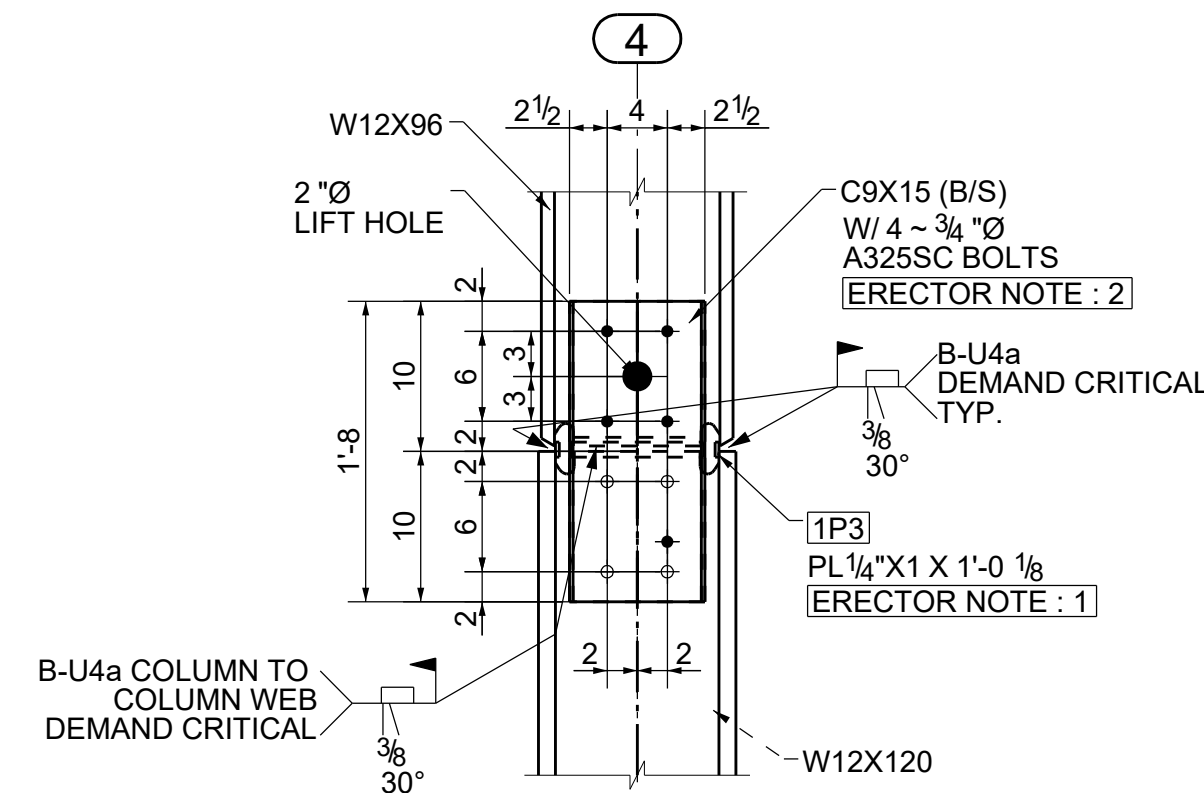


**TYPICAL W12X120 COLUMN TO W12X96 COLUMN
SPLICE CONNECTION DETAILS
@ BRACE LOCATION**

SEE 1-E110 FOR DEMAND
CRITICAL WELD NOTE.

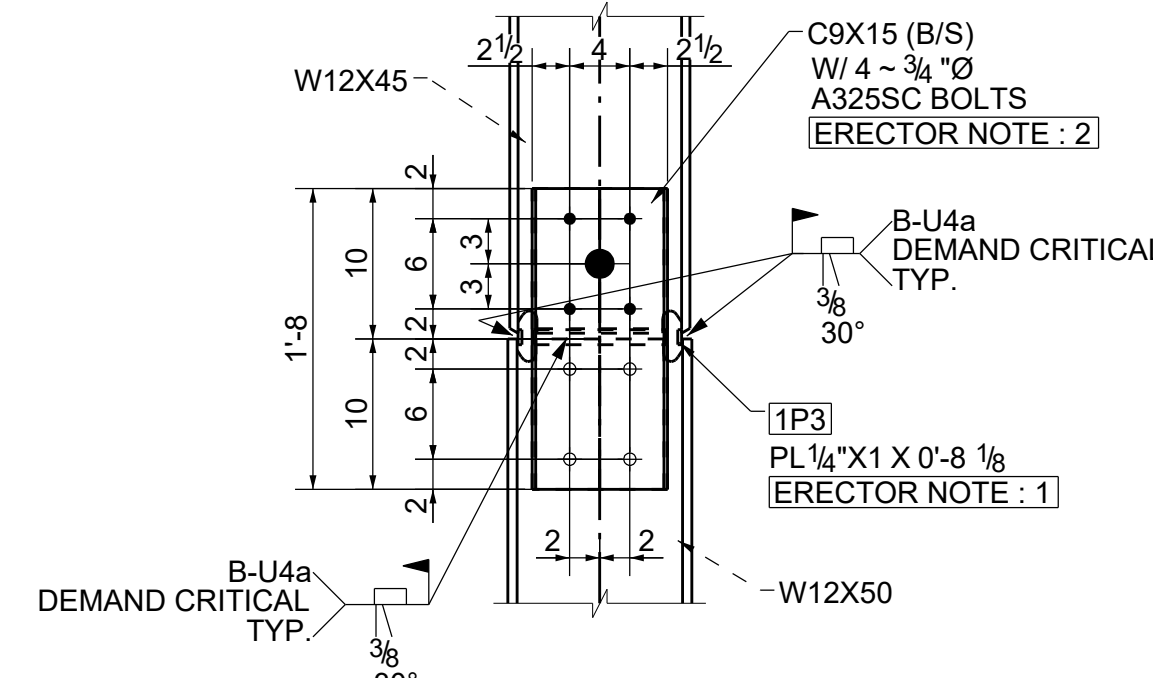


**TYPICAL W12X50 COLUMN TO W12X45 COLUMN
SPLICE CONNECTION DETAILS
@ BRACE LOCATION**

SEE 1-E110 FOR DEMAND
CRITICAL WELD NOTE.

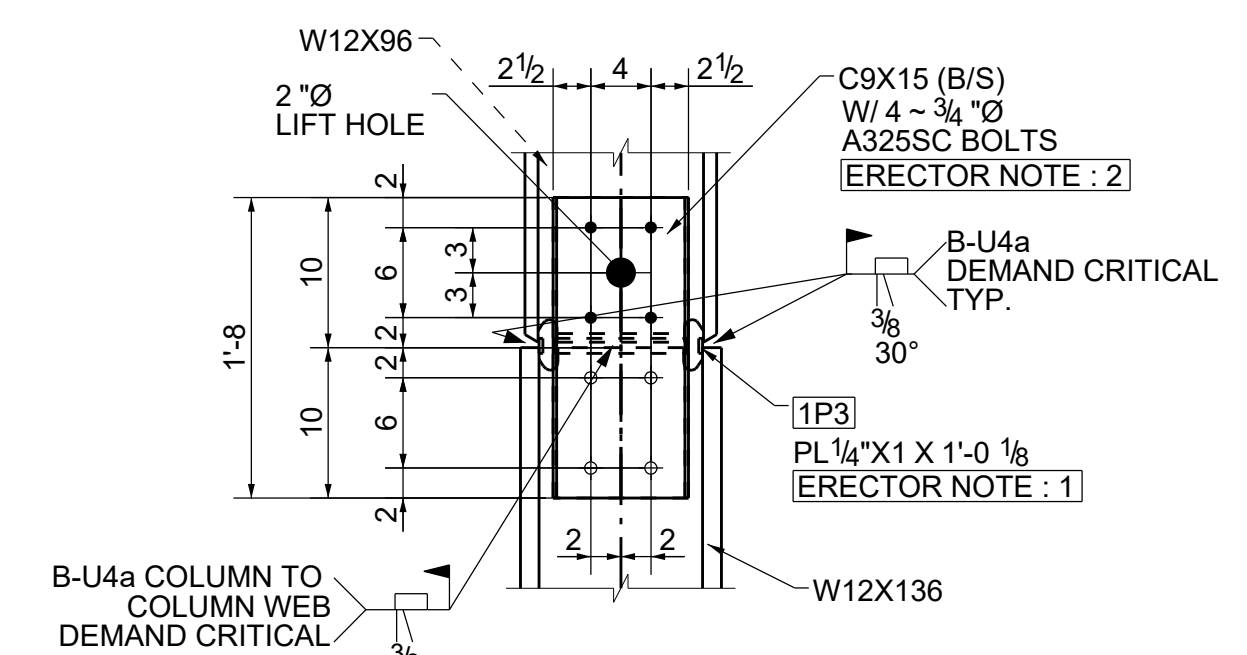

**TYPICAL W12X136 COLUMN TO W12X96 COLUMN
SPLICE CONNECTION DETAILS
@ BRACE LOCATION**


SEE 1-E110 FOR DEMAND
CRITICAL WELD NOTE.

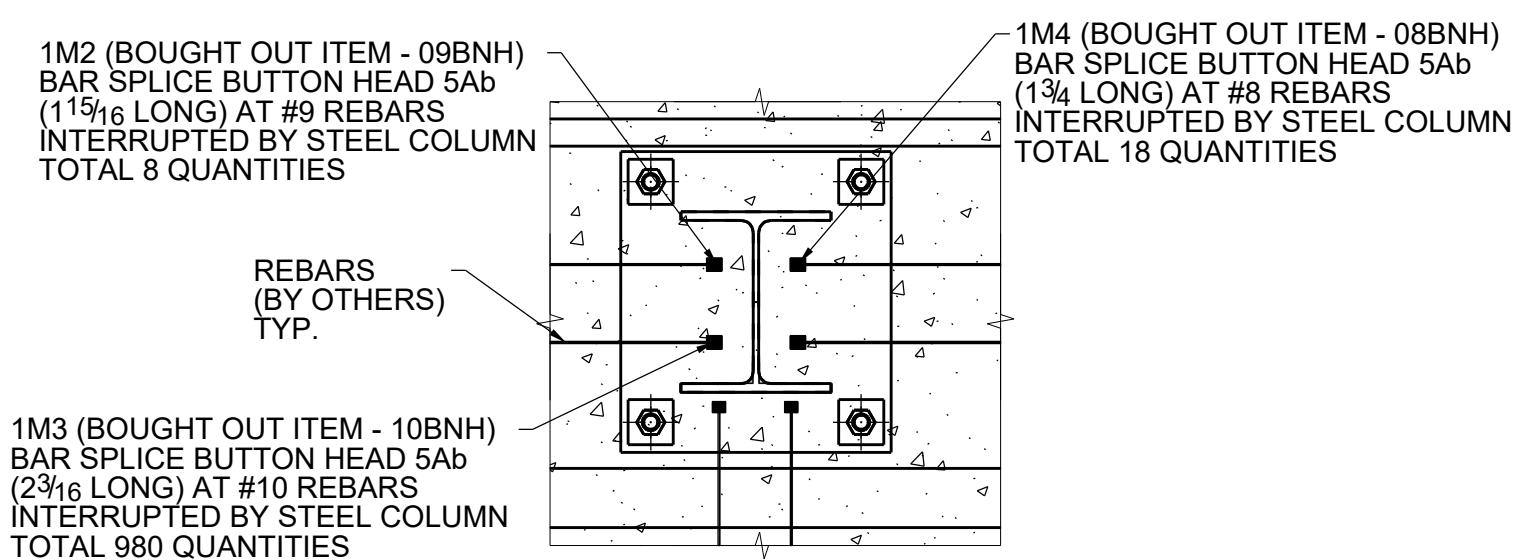


**TYPICAL BAR SPLICE BUTTON HEAD 5Ab
DETAIL**

REFER SECTION 12/S3.10

COORDINATE REBAR SIZES & LOCATIONS
WITH REBAR SUPPLIER.

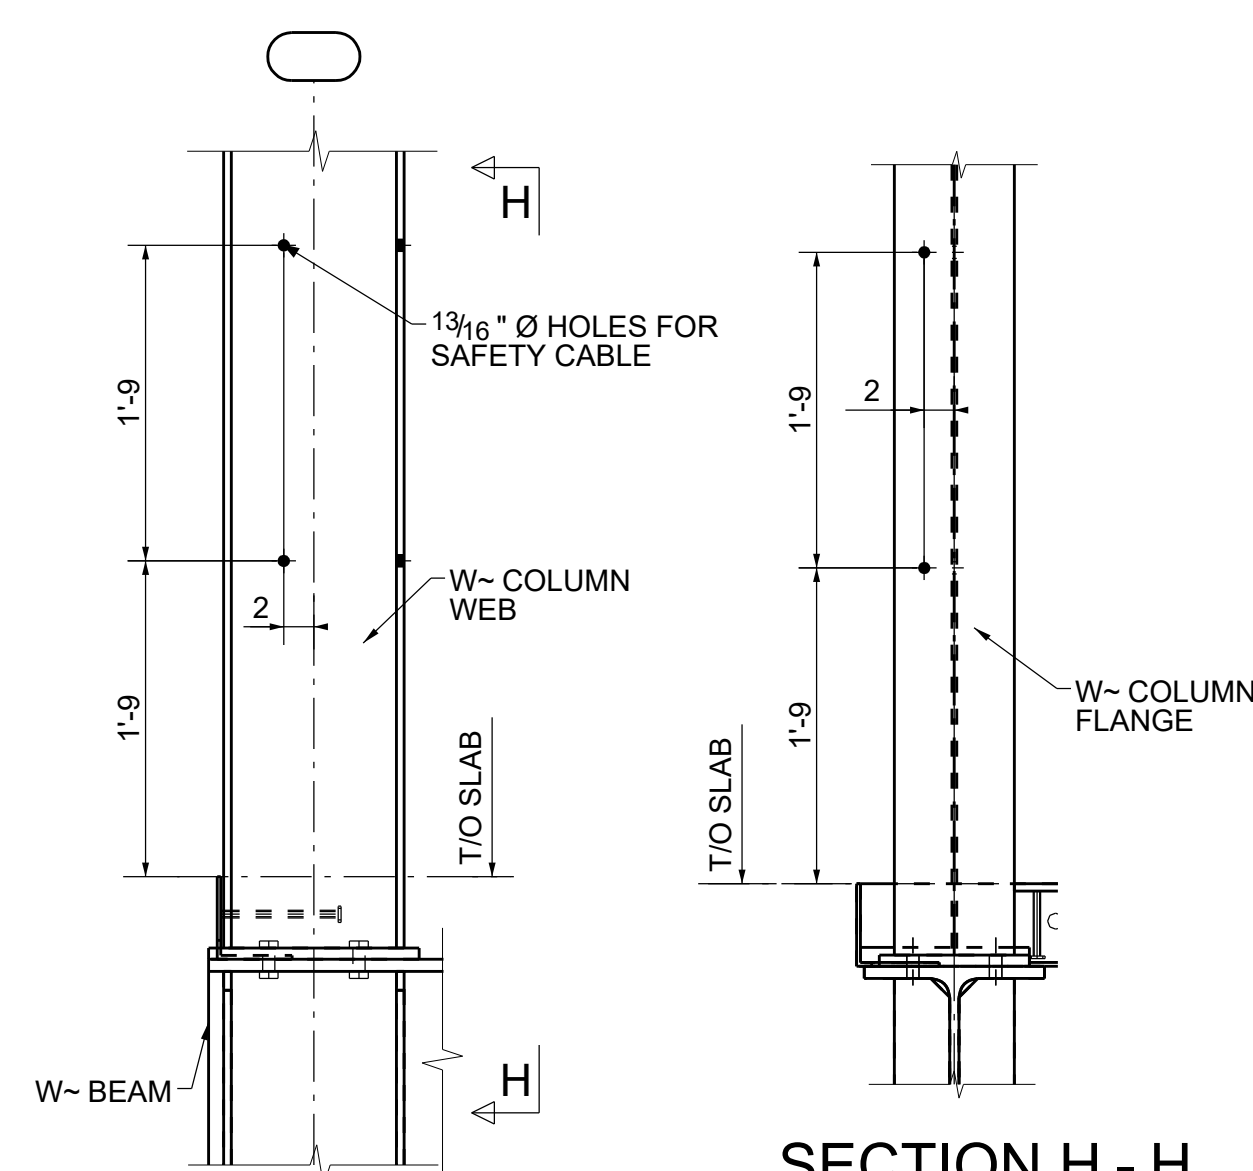


TYPICAL SAFETY CABLE HOLE DETAIL

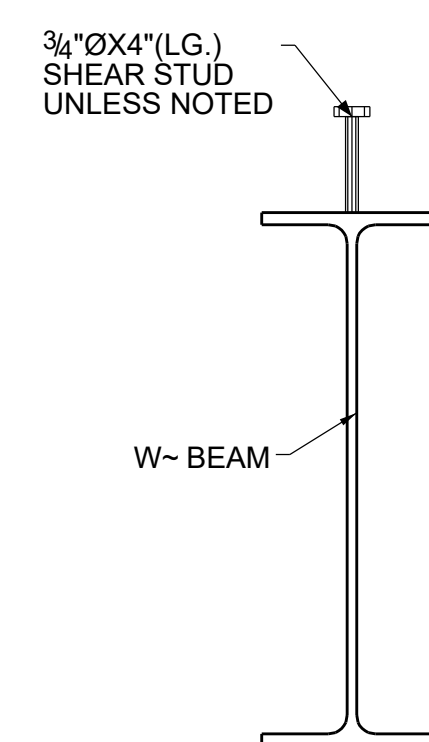

**TYPICAL SHEAR STUD
DETAIL**













NOTE: SEE DECK MFG.
DRAWINGS FOR
COMPLETE INFORMATION.

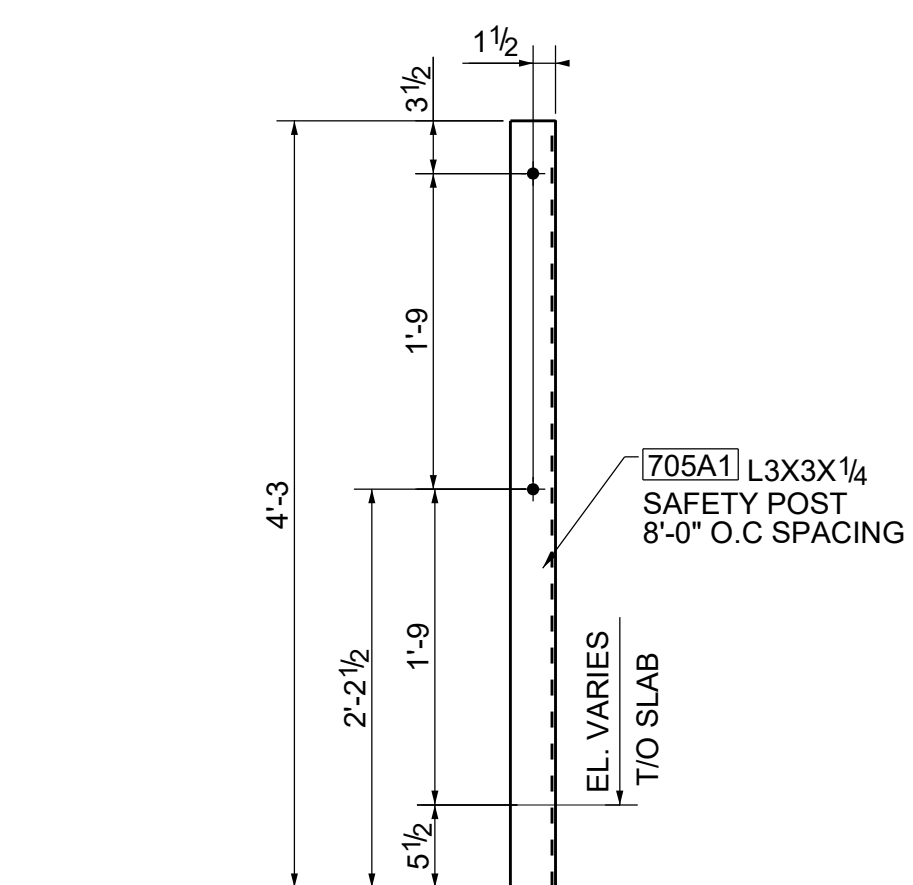

**TYPICAL TEMPORARY ANGLE
SAFETY CABLE POST DETAIL**

ERECTOR NOTE : 01
1) REMOVE BACKING BAR AT ALL COLUMN SPLICE IN
SFRS AND ANY WELD IN THE PROTECTED ZONE.


ERECTOR NOTE : 02
1. ERECT UPPER COLUMN AND BOLT CHANNEL AS SHOWN.
2. REMOVE THE CHANNEL AFTER THE FLANGES ARE FIELD WELDED.
3. AFTER THE CHANNELS IS REMOVED FIELD WELD THE COLUMN WEB AS SHOWN.
4. COLUMN SPLICE WELDS ARE DEMAND CRITICAL.

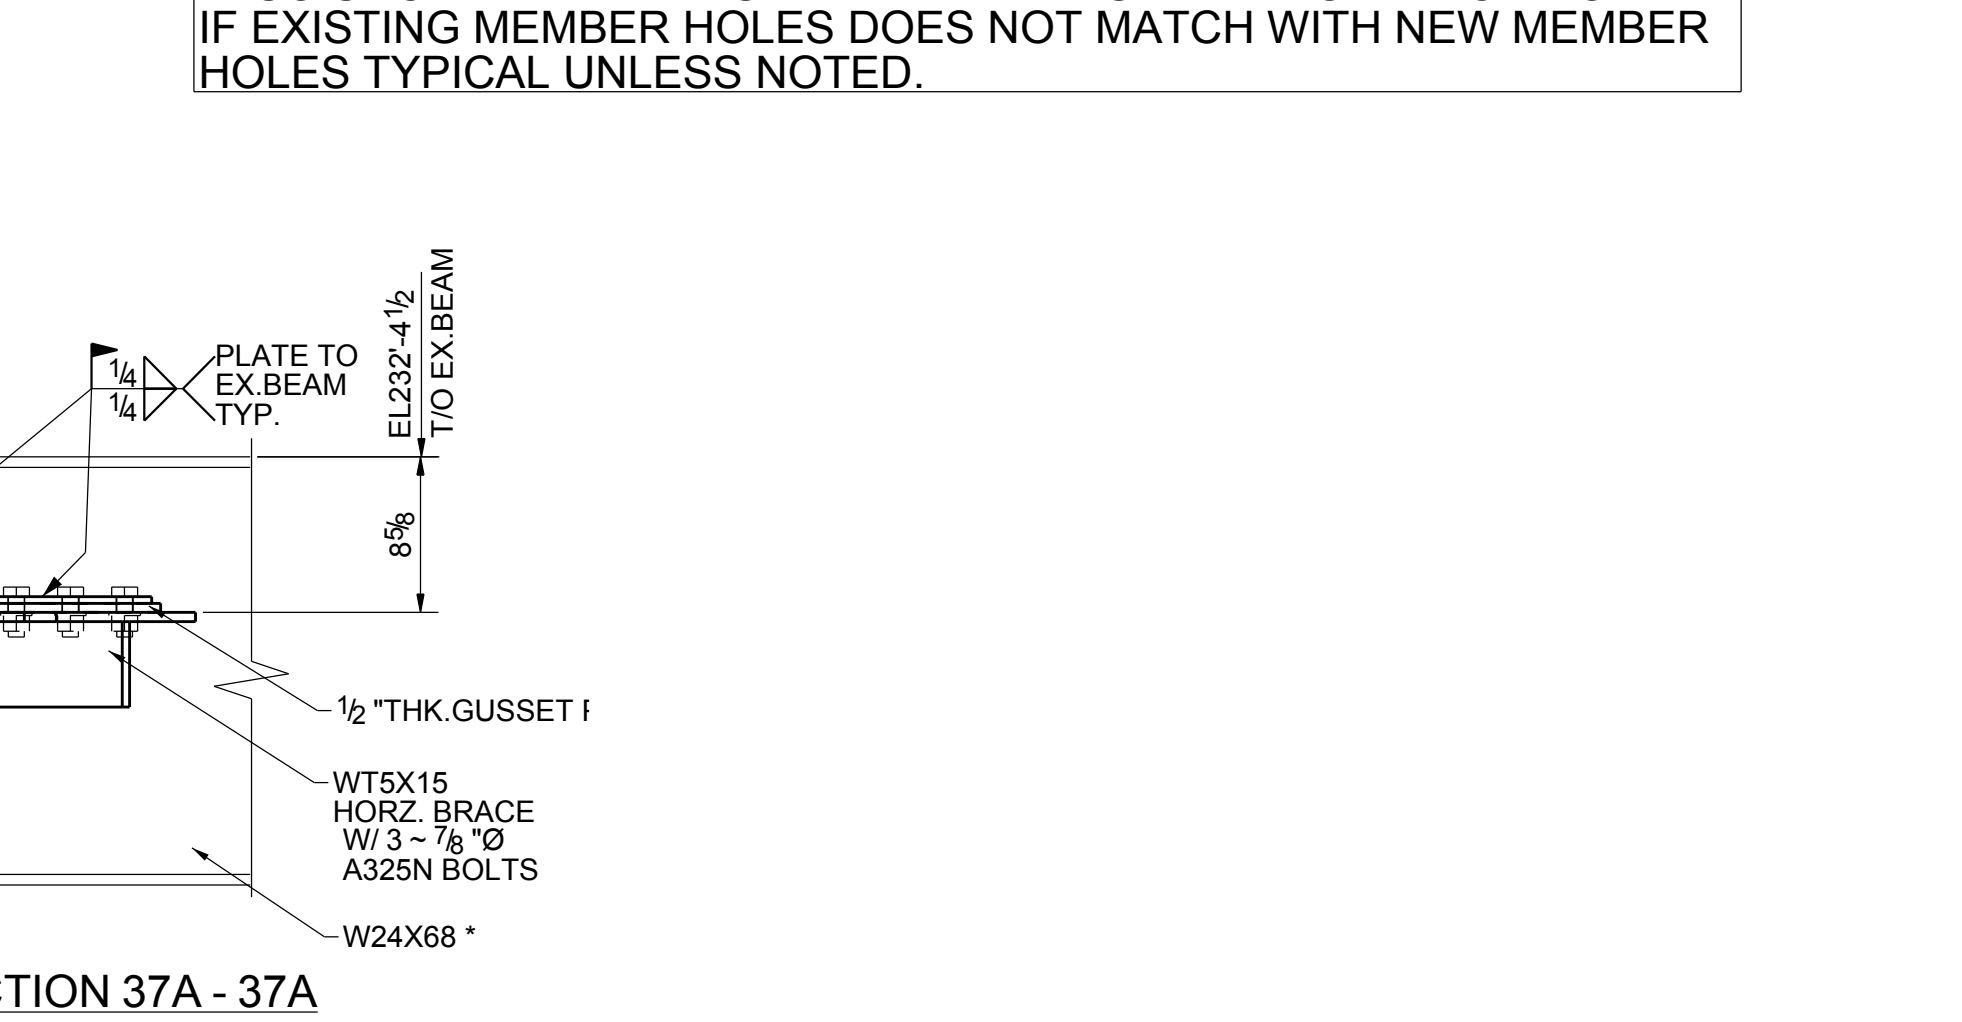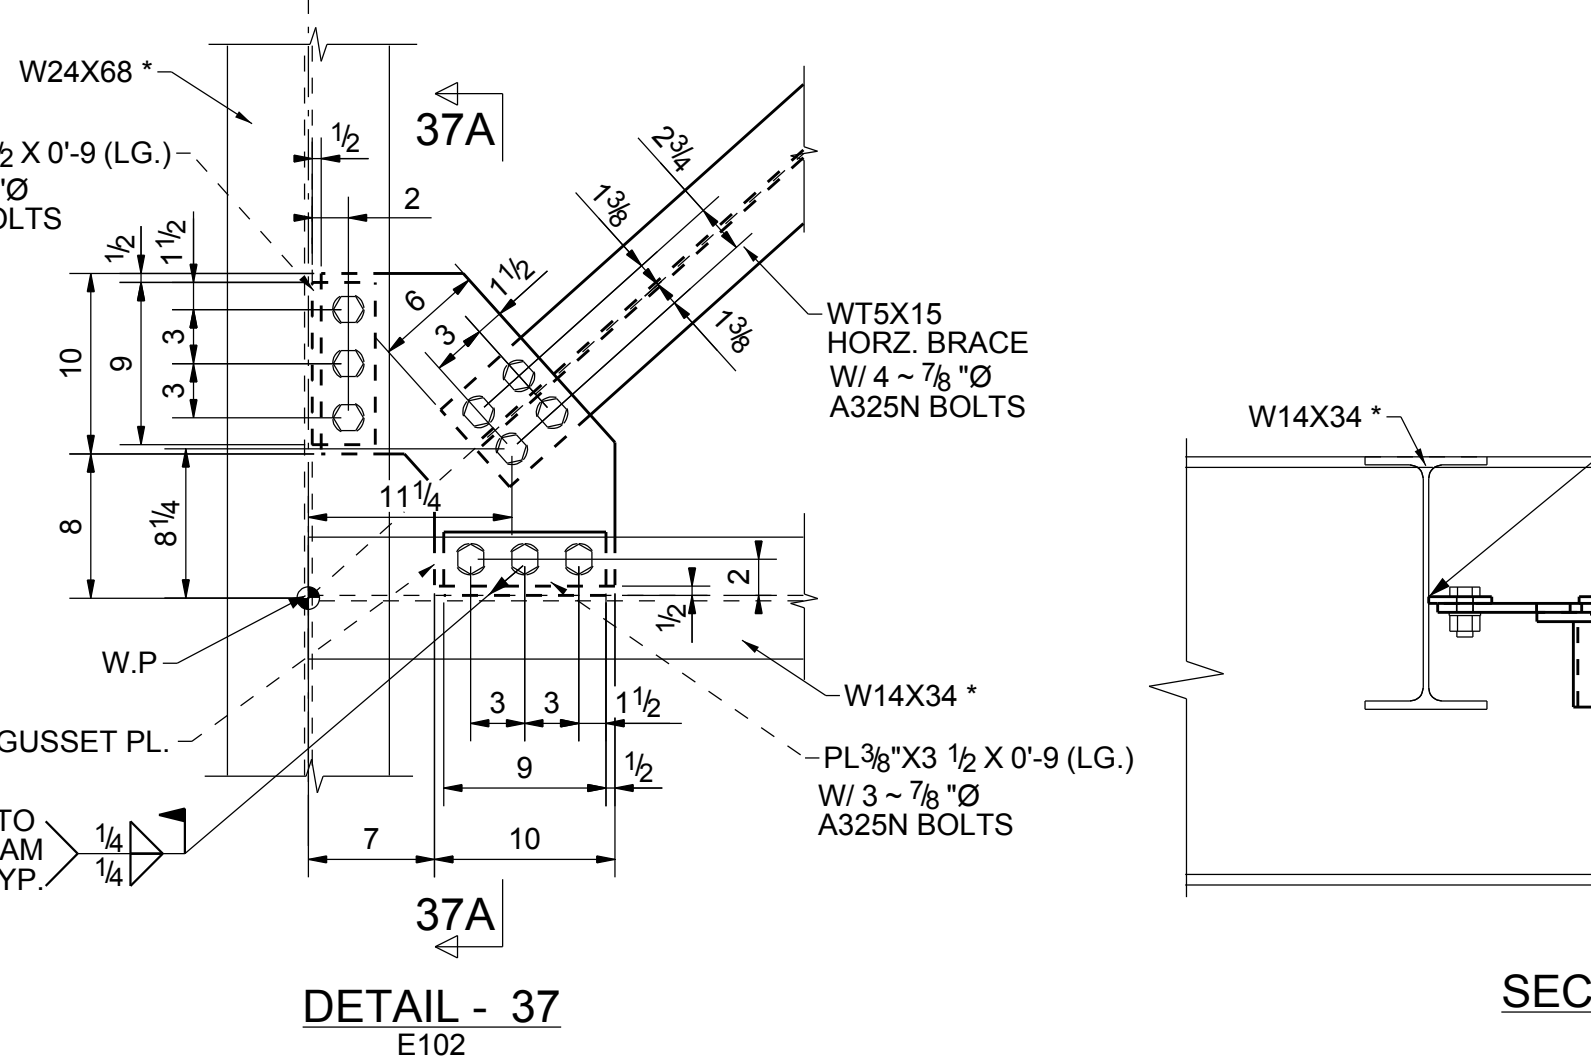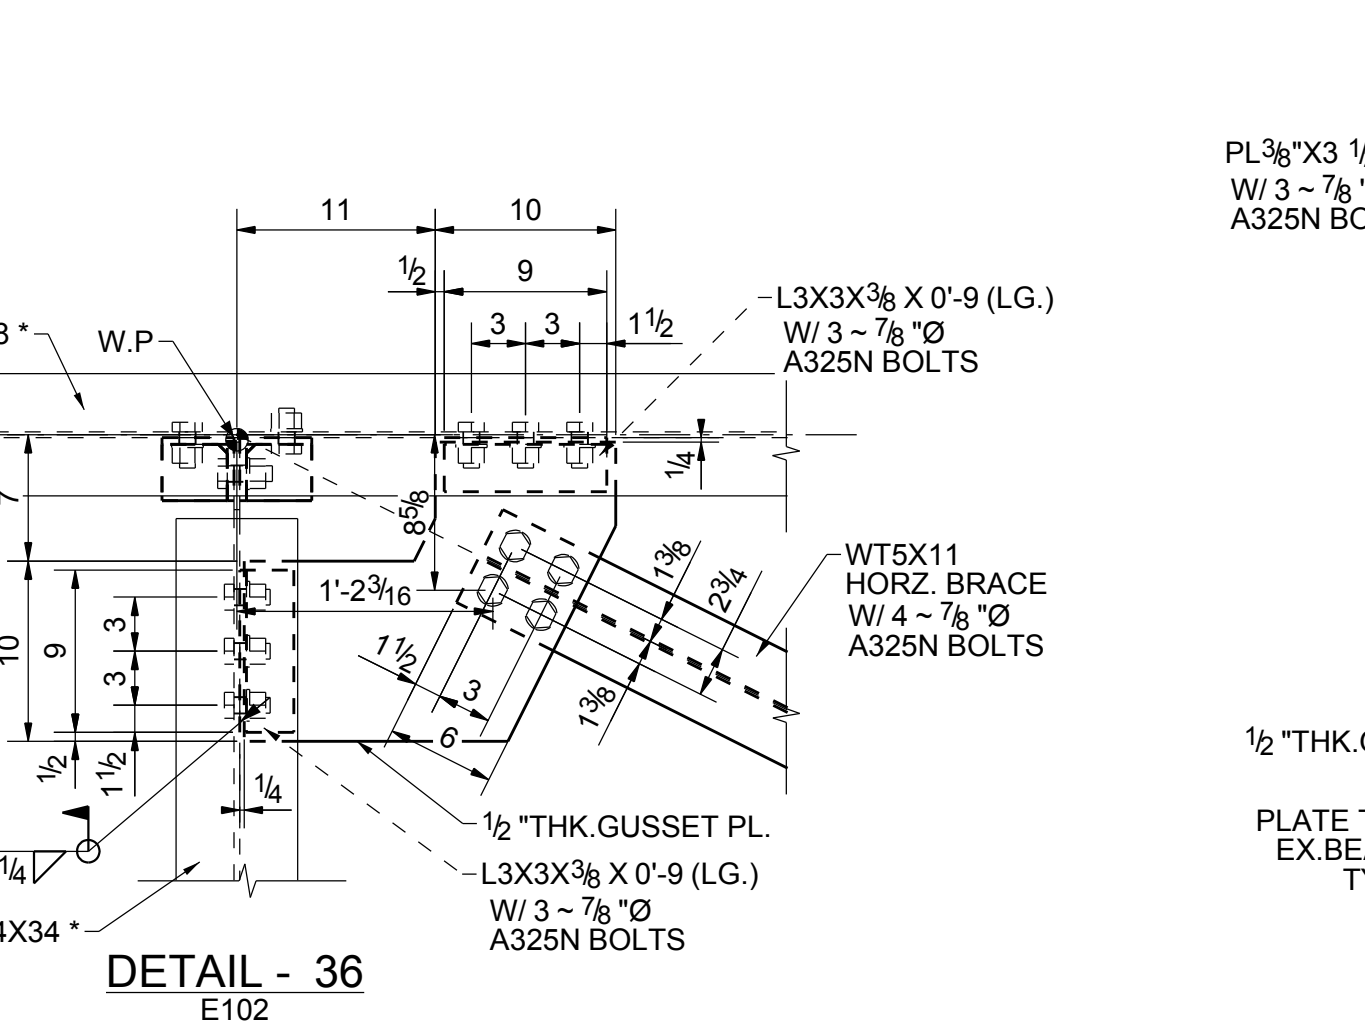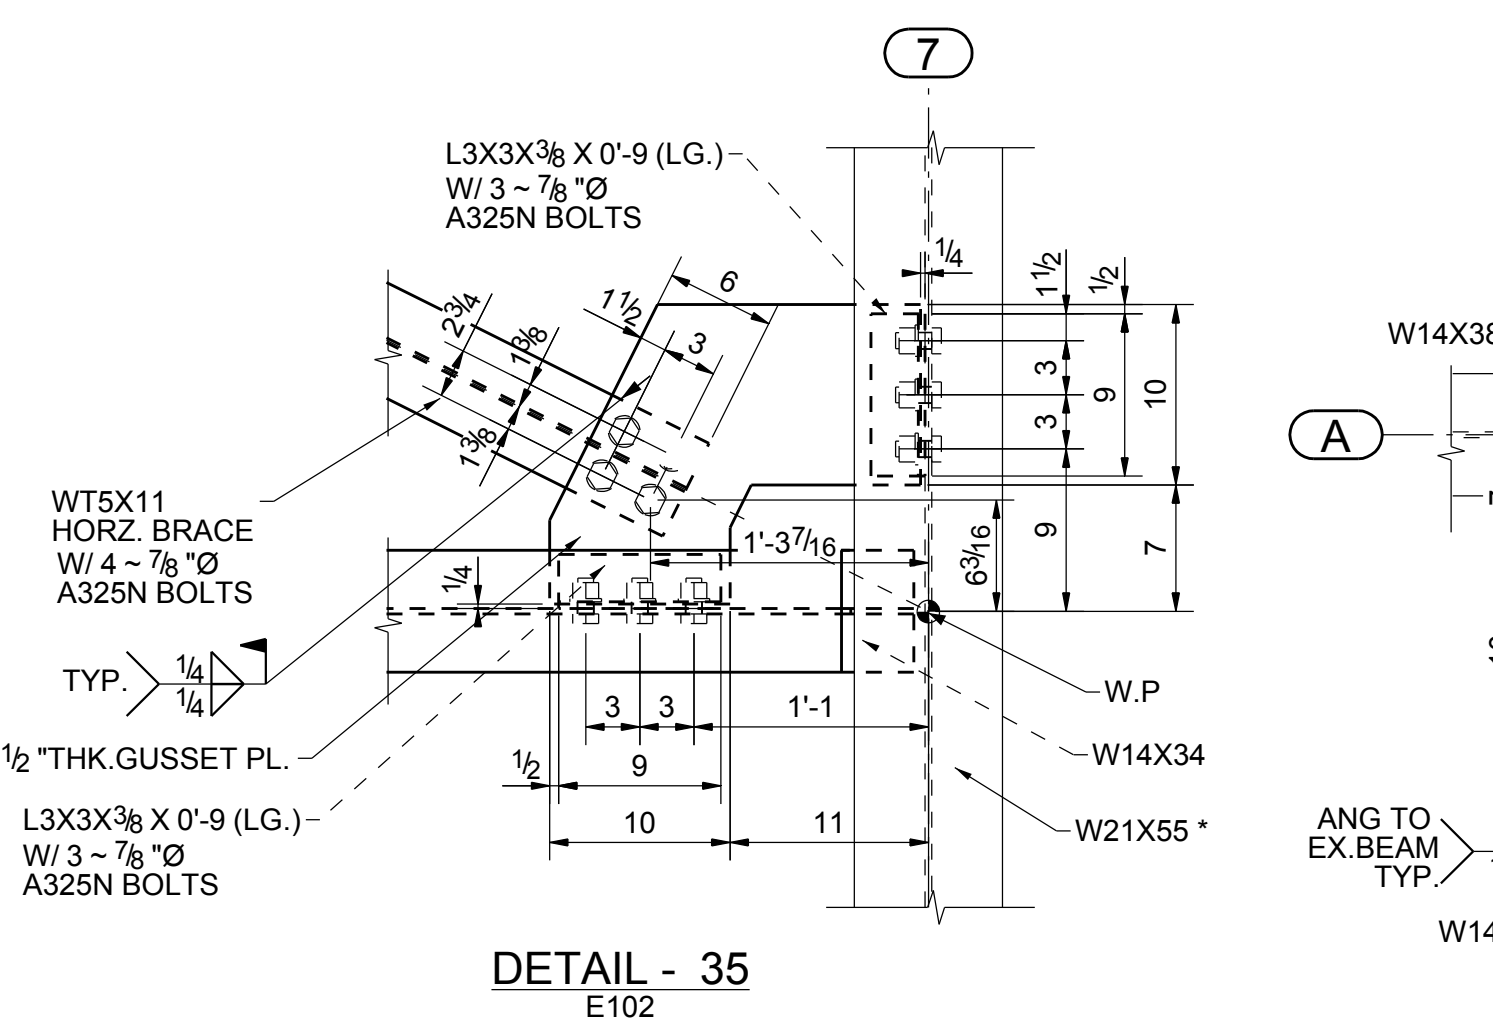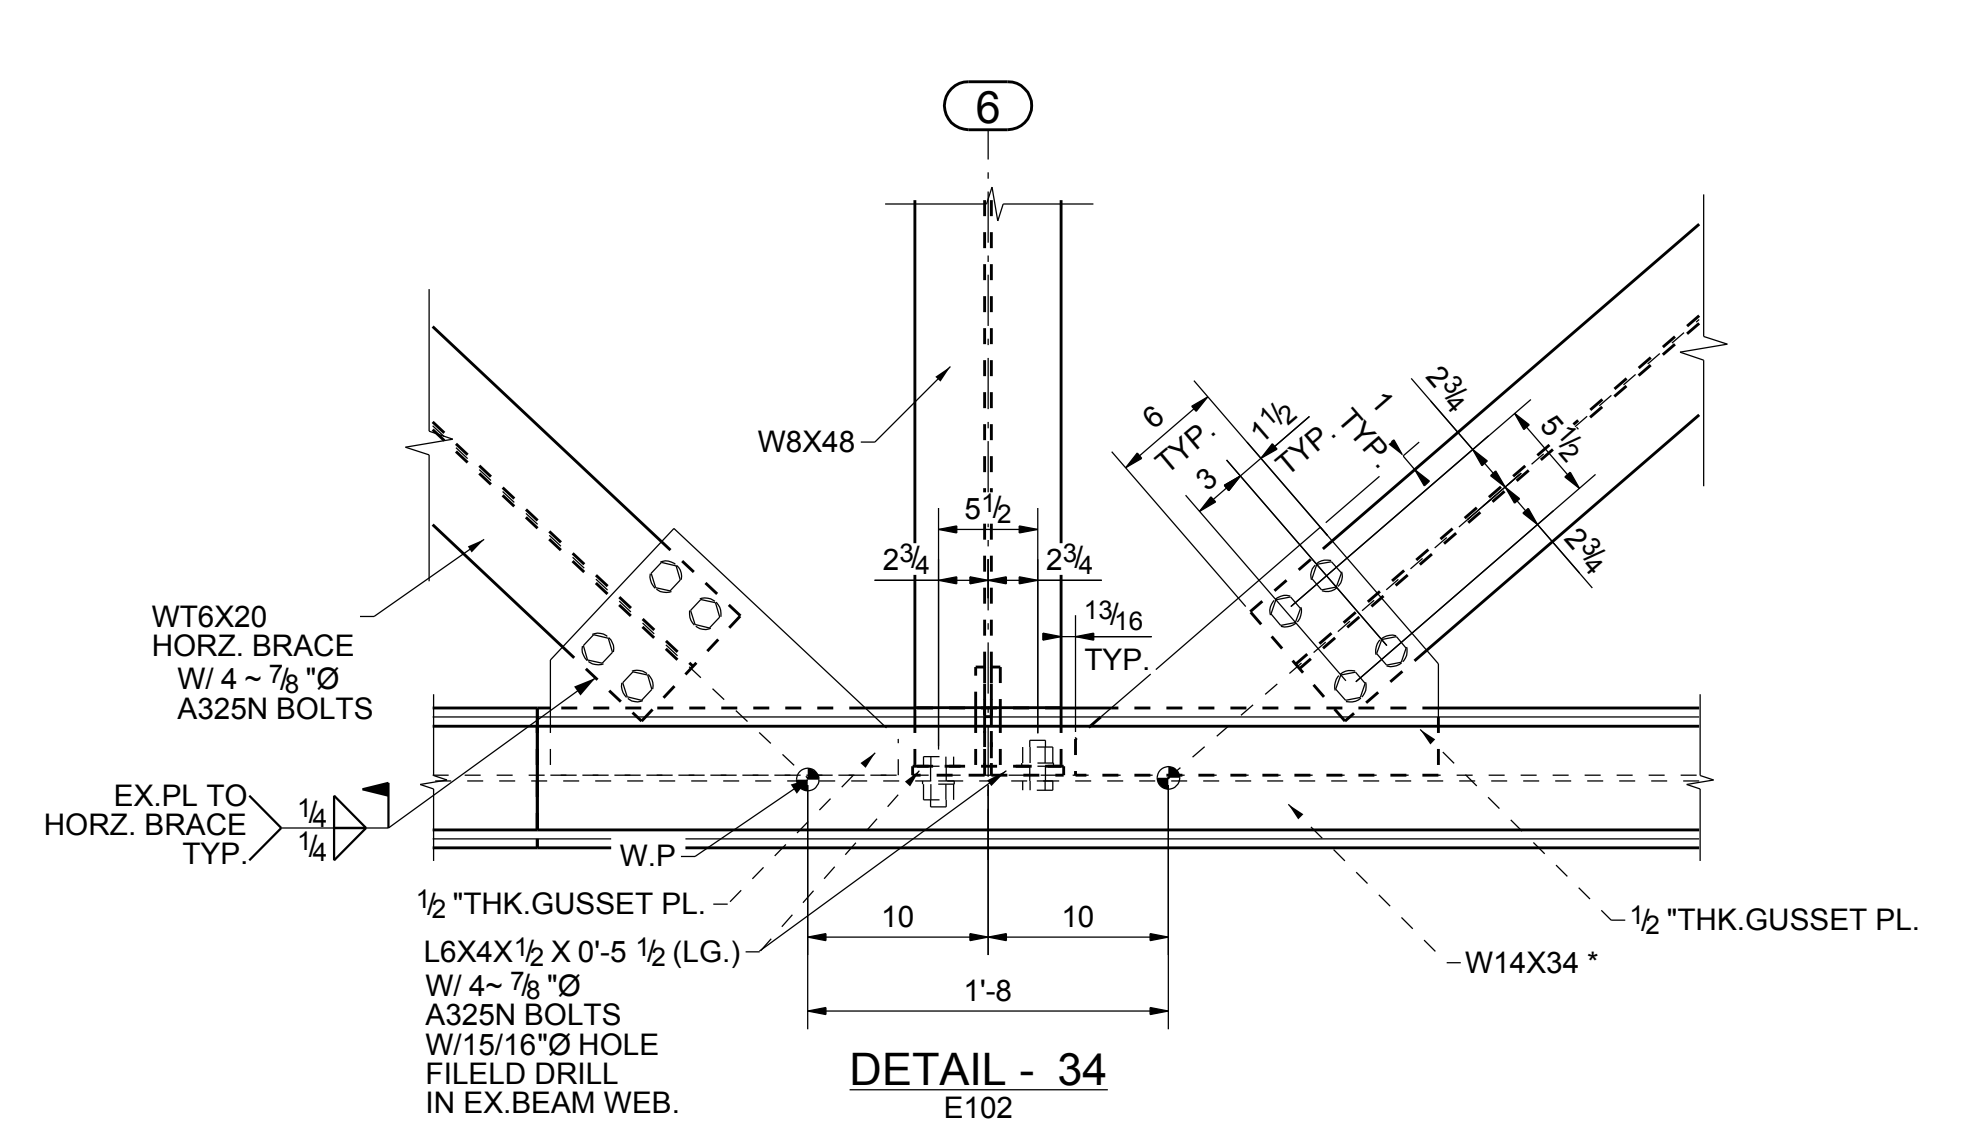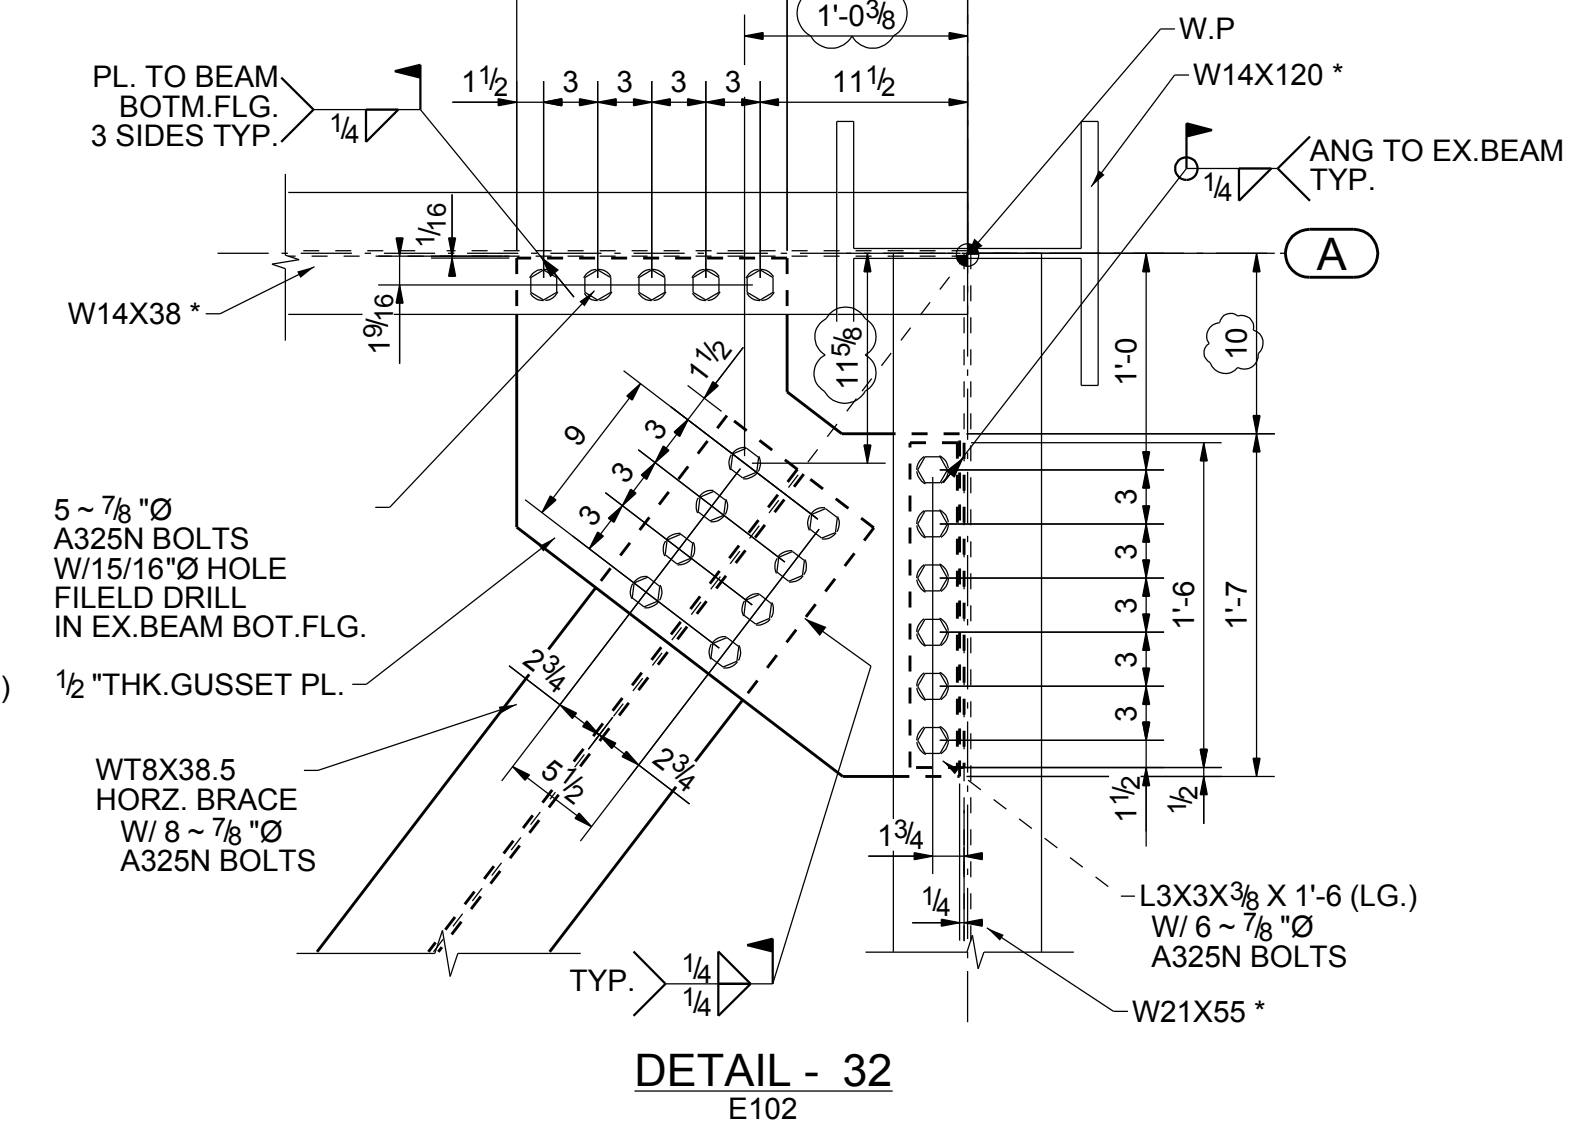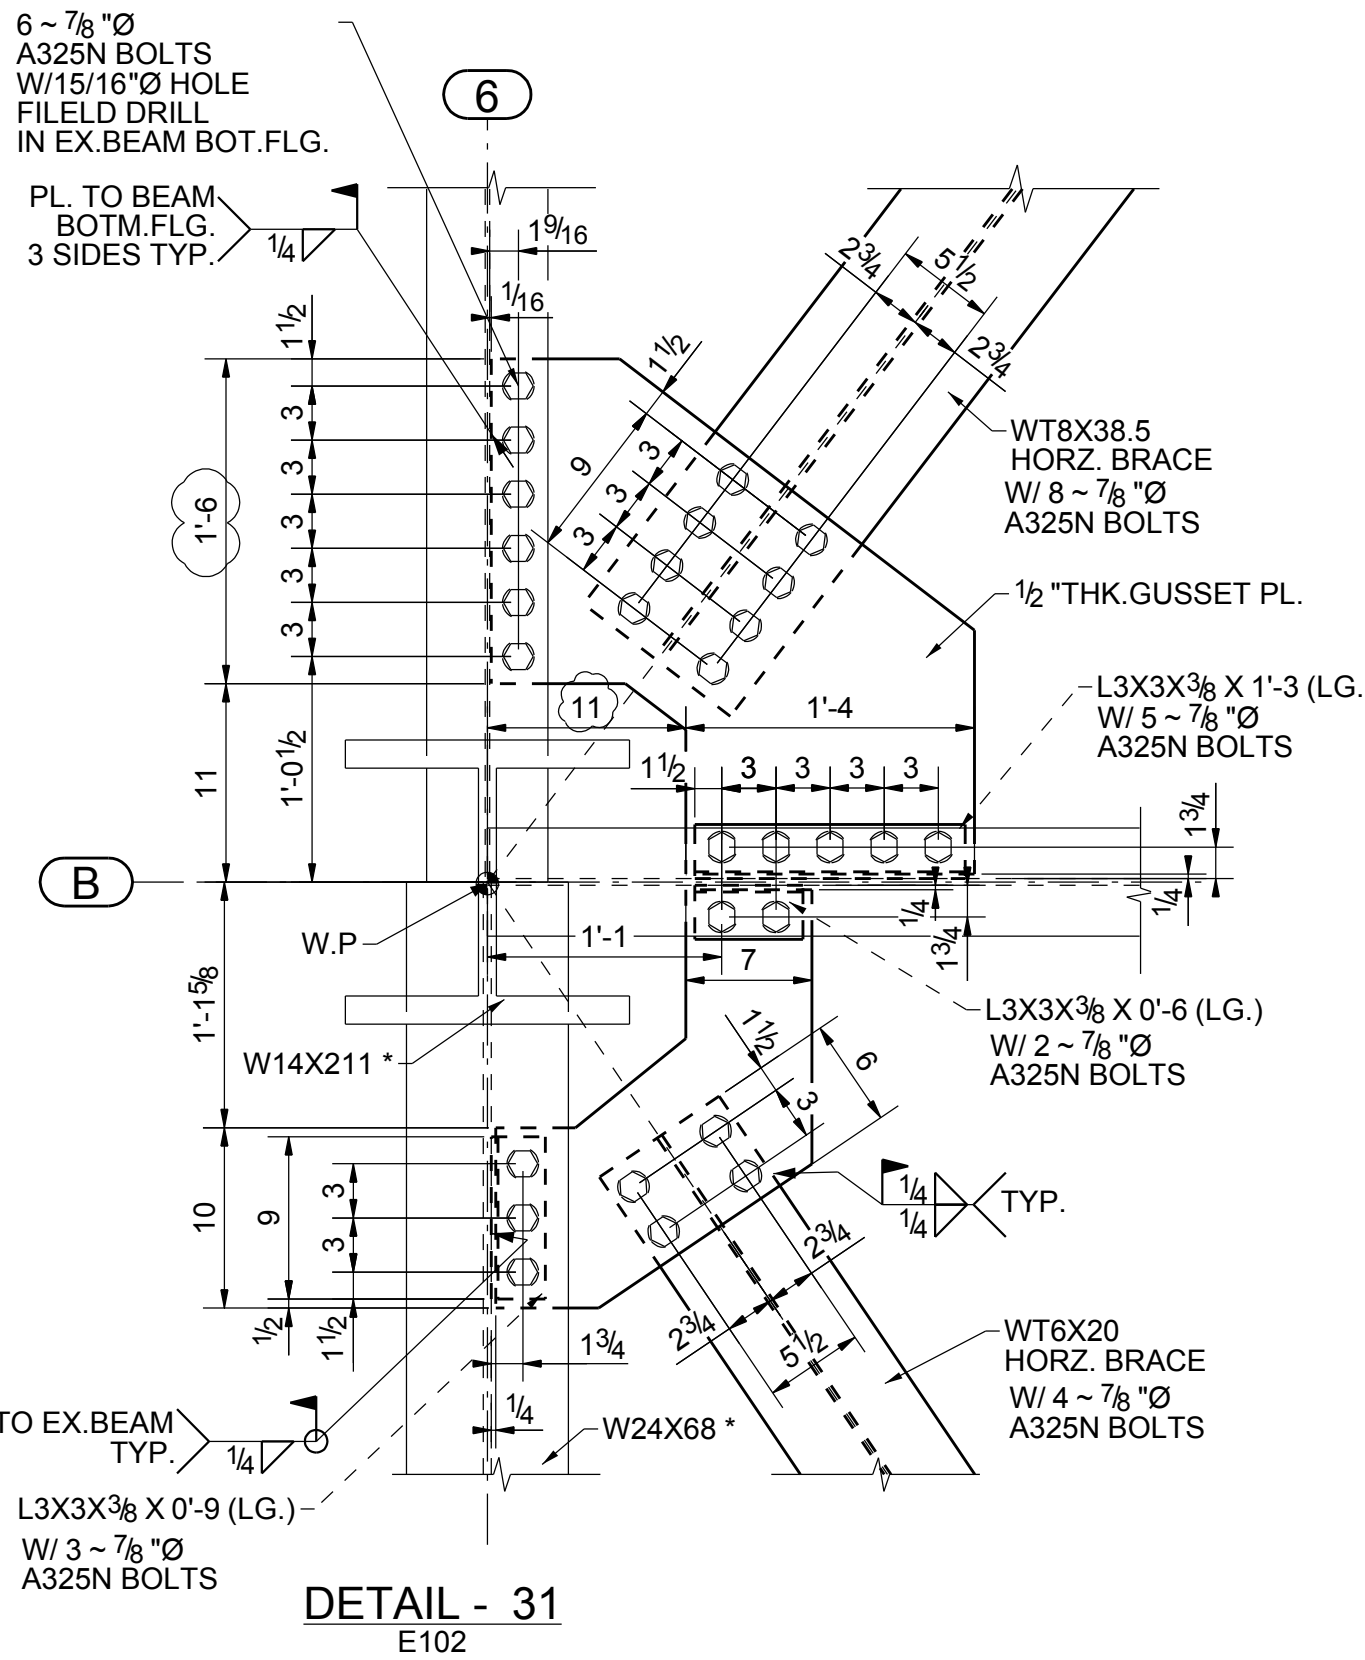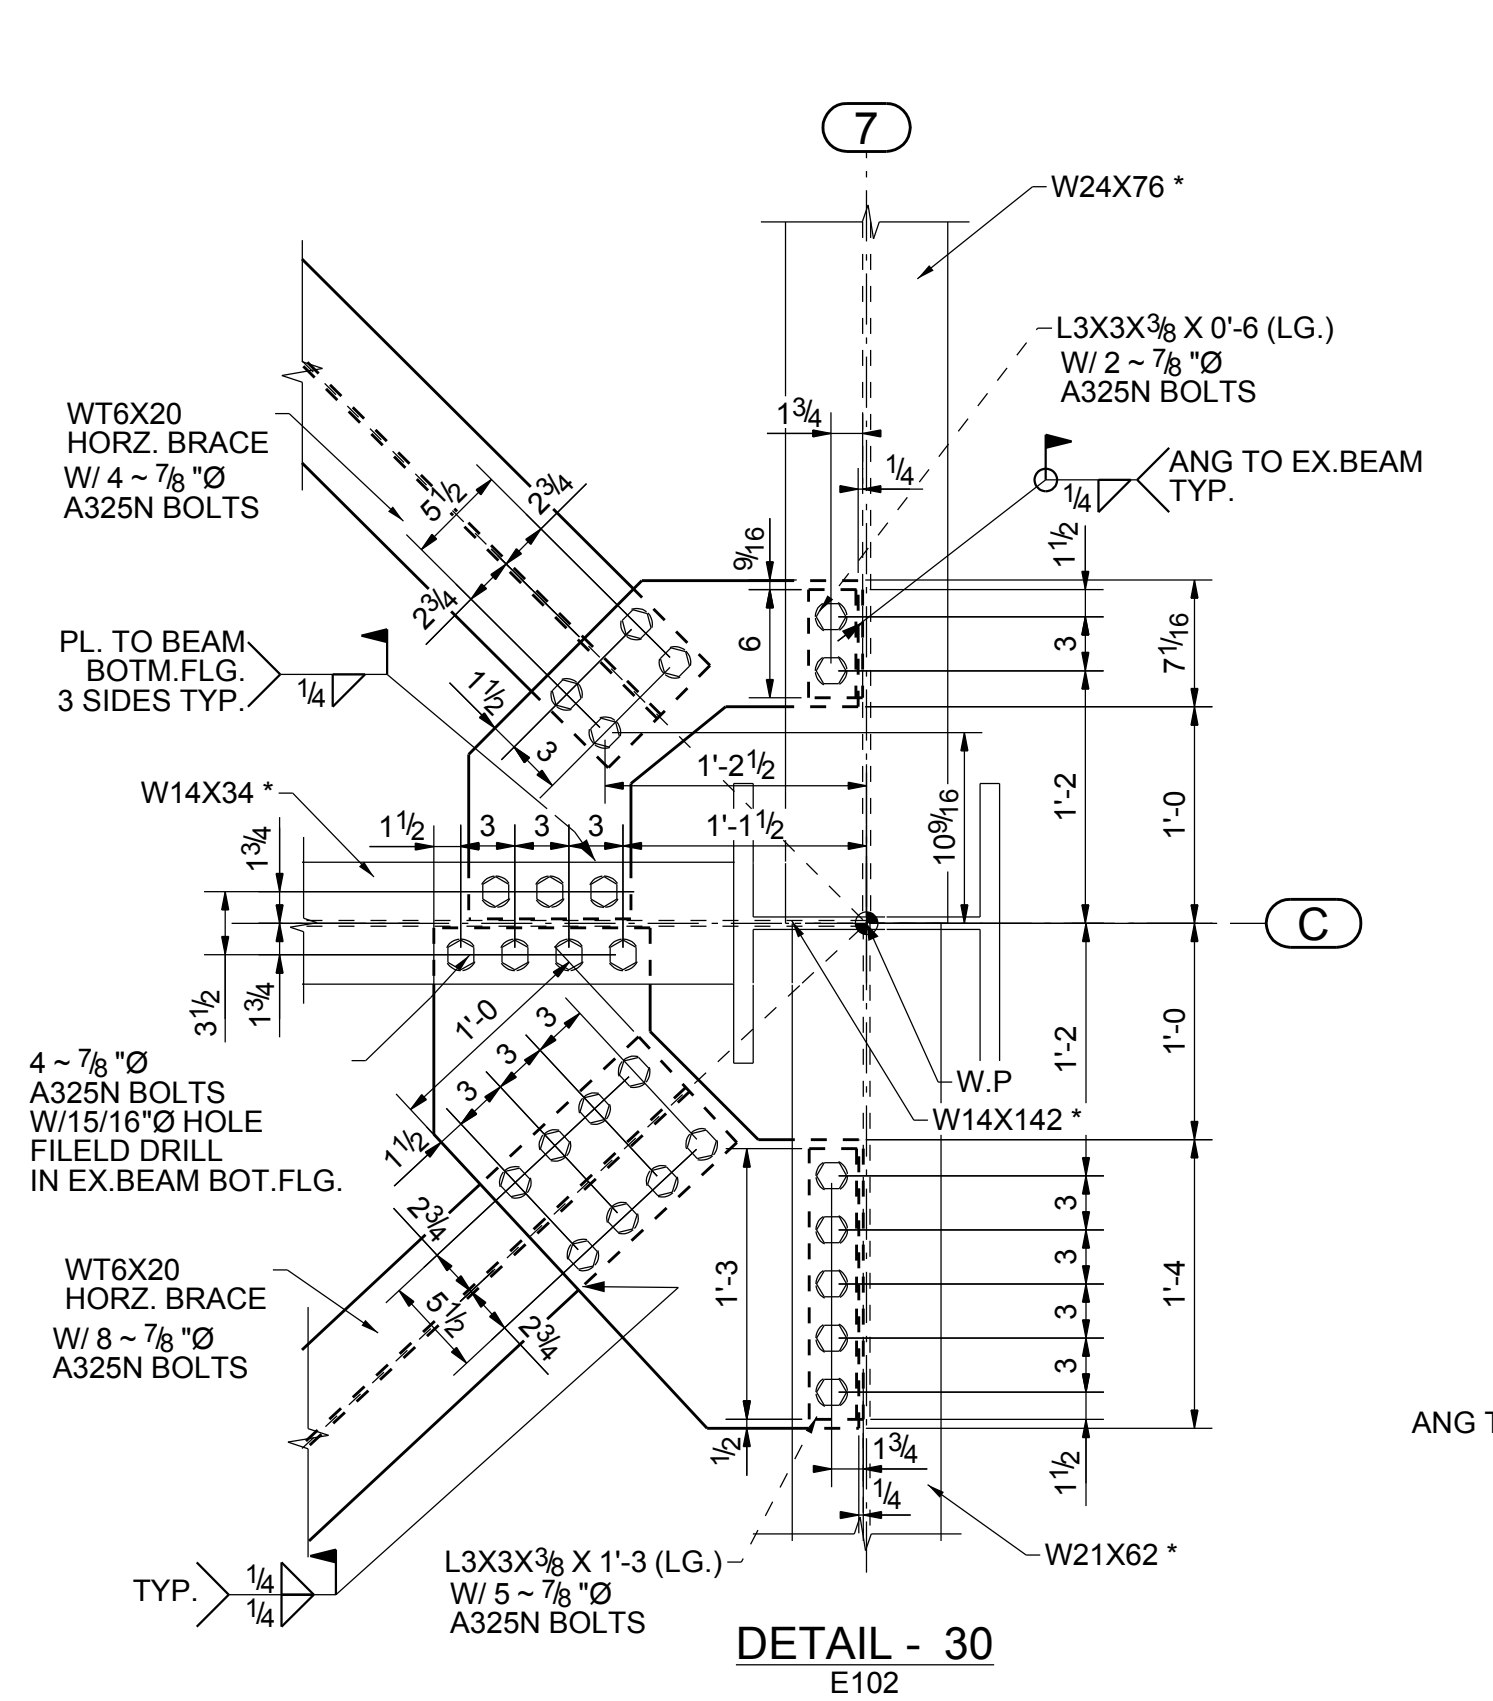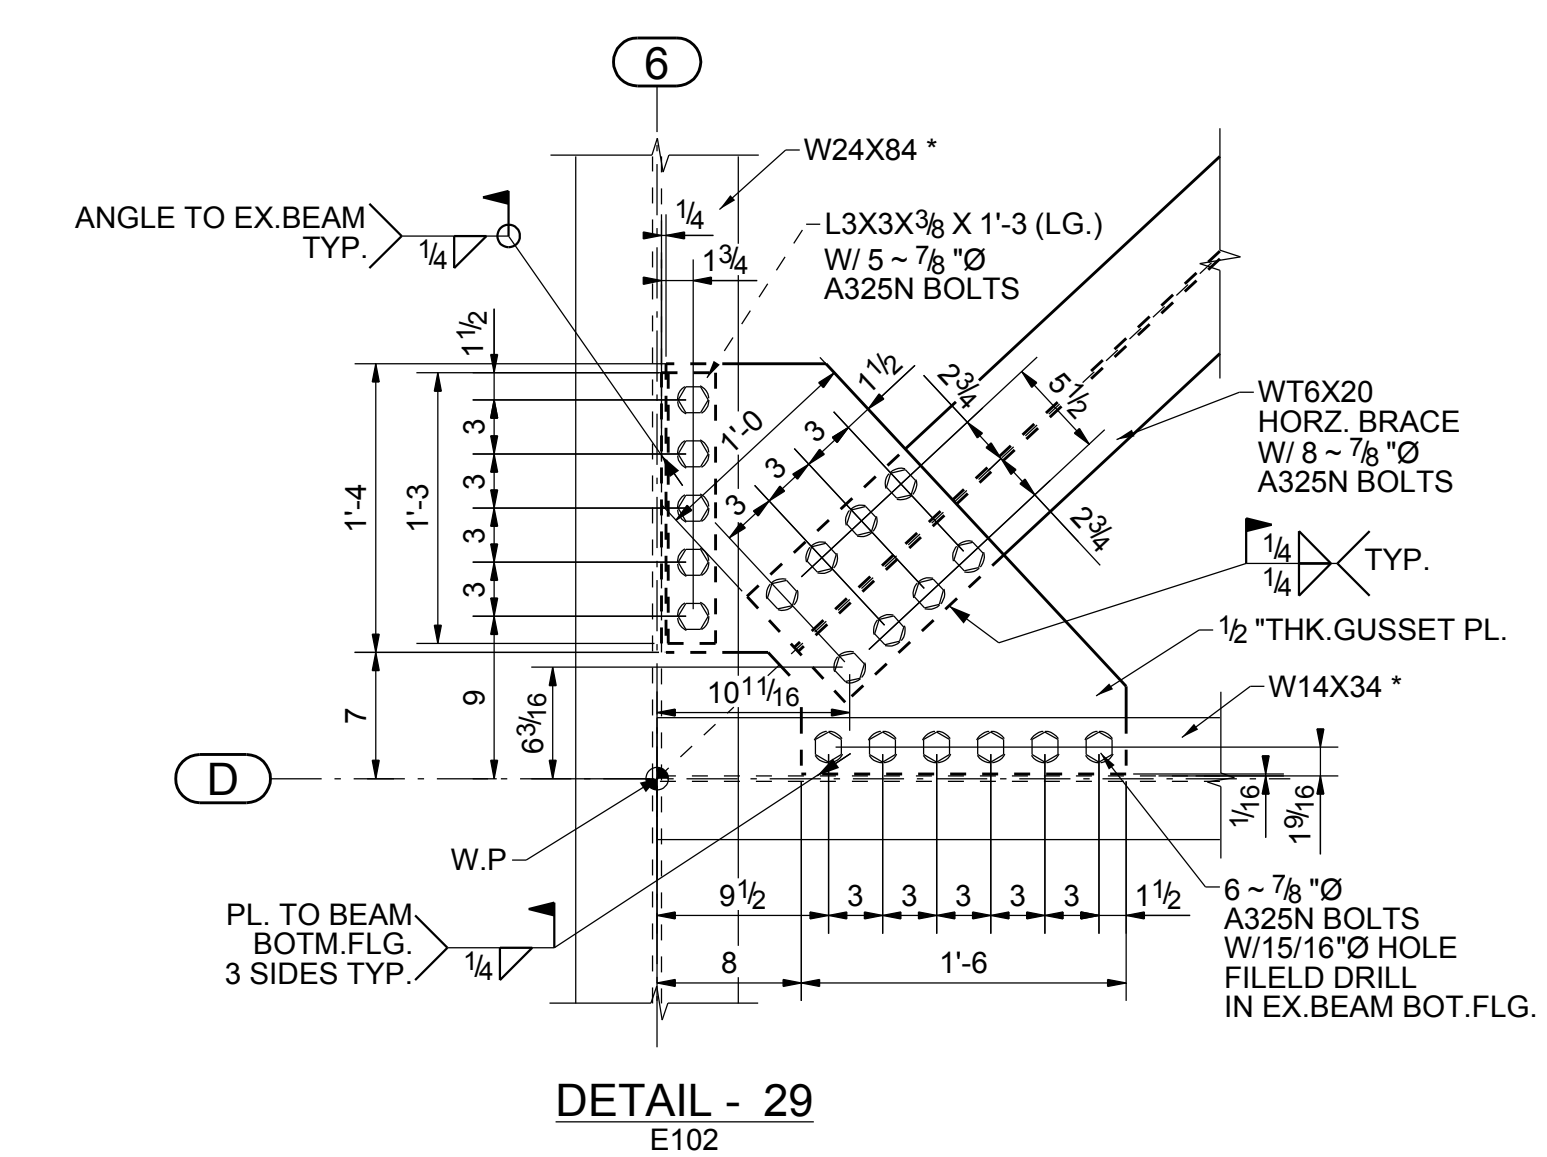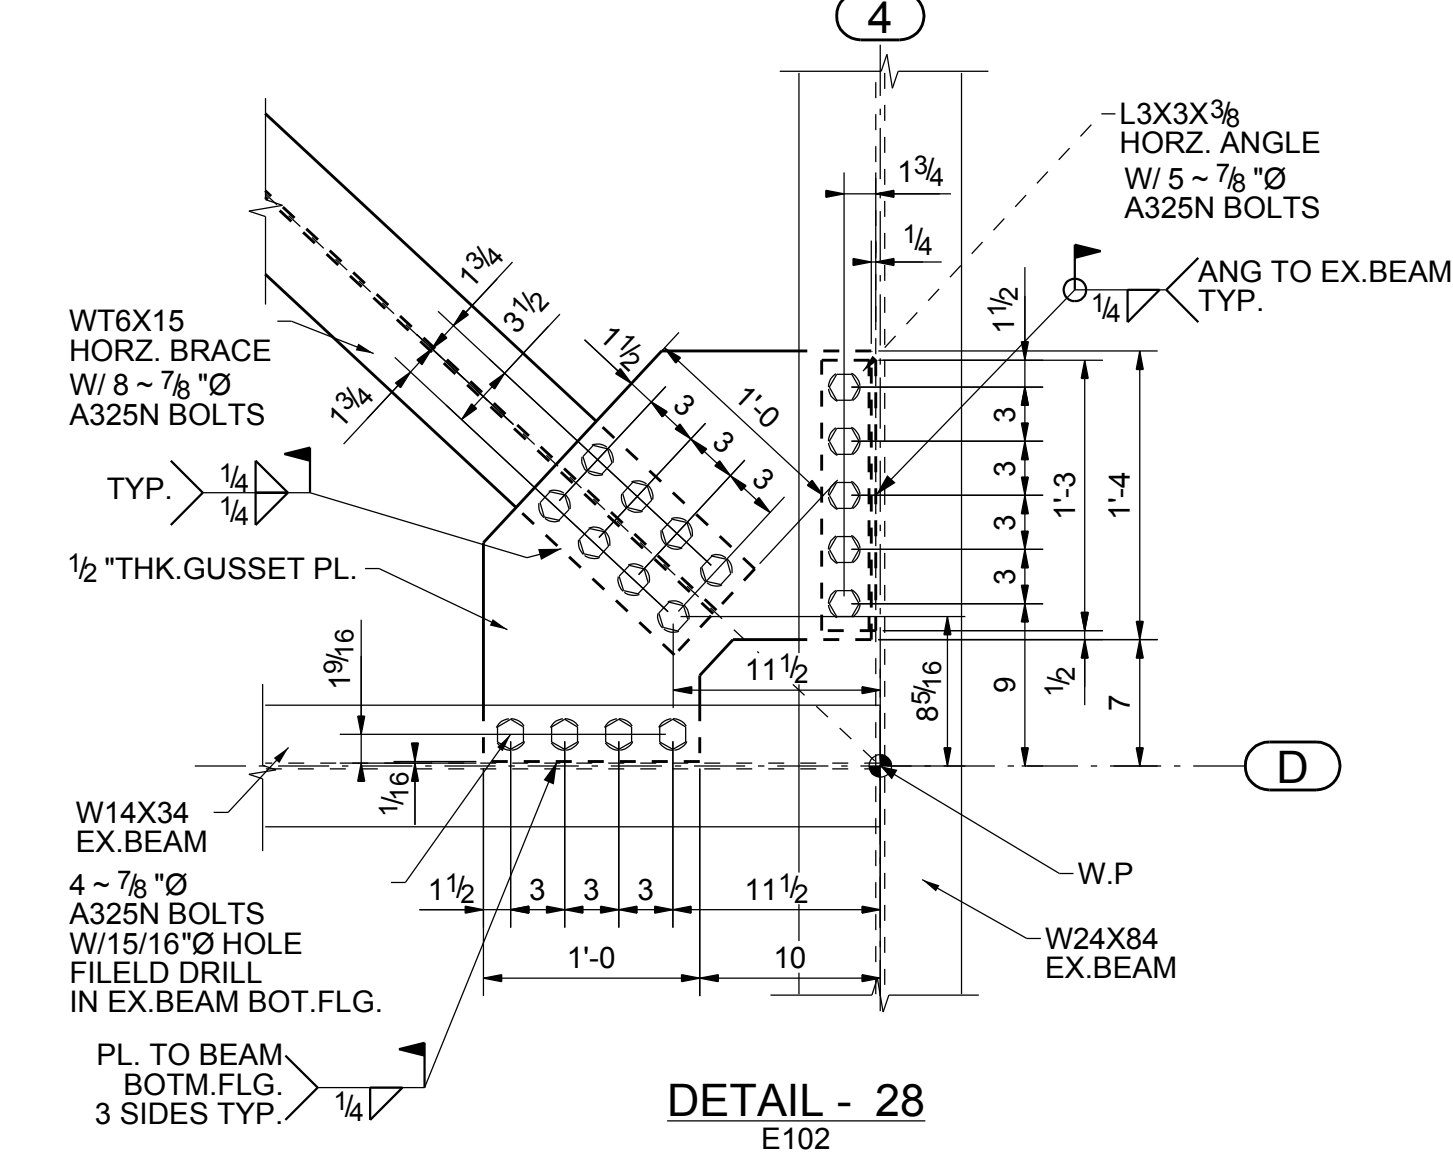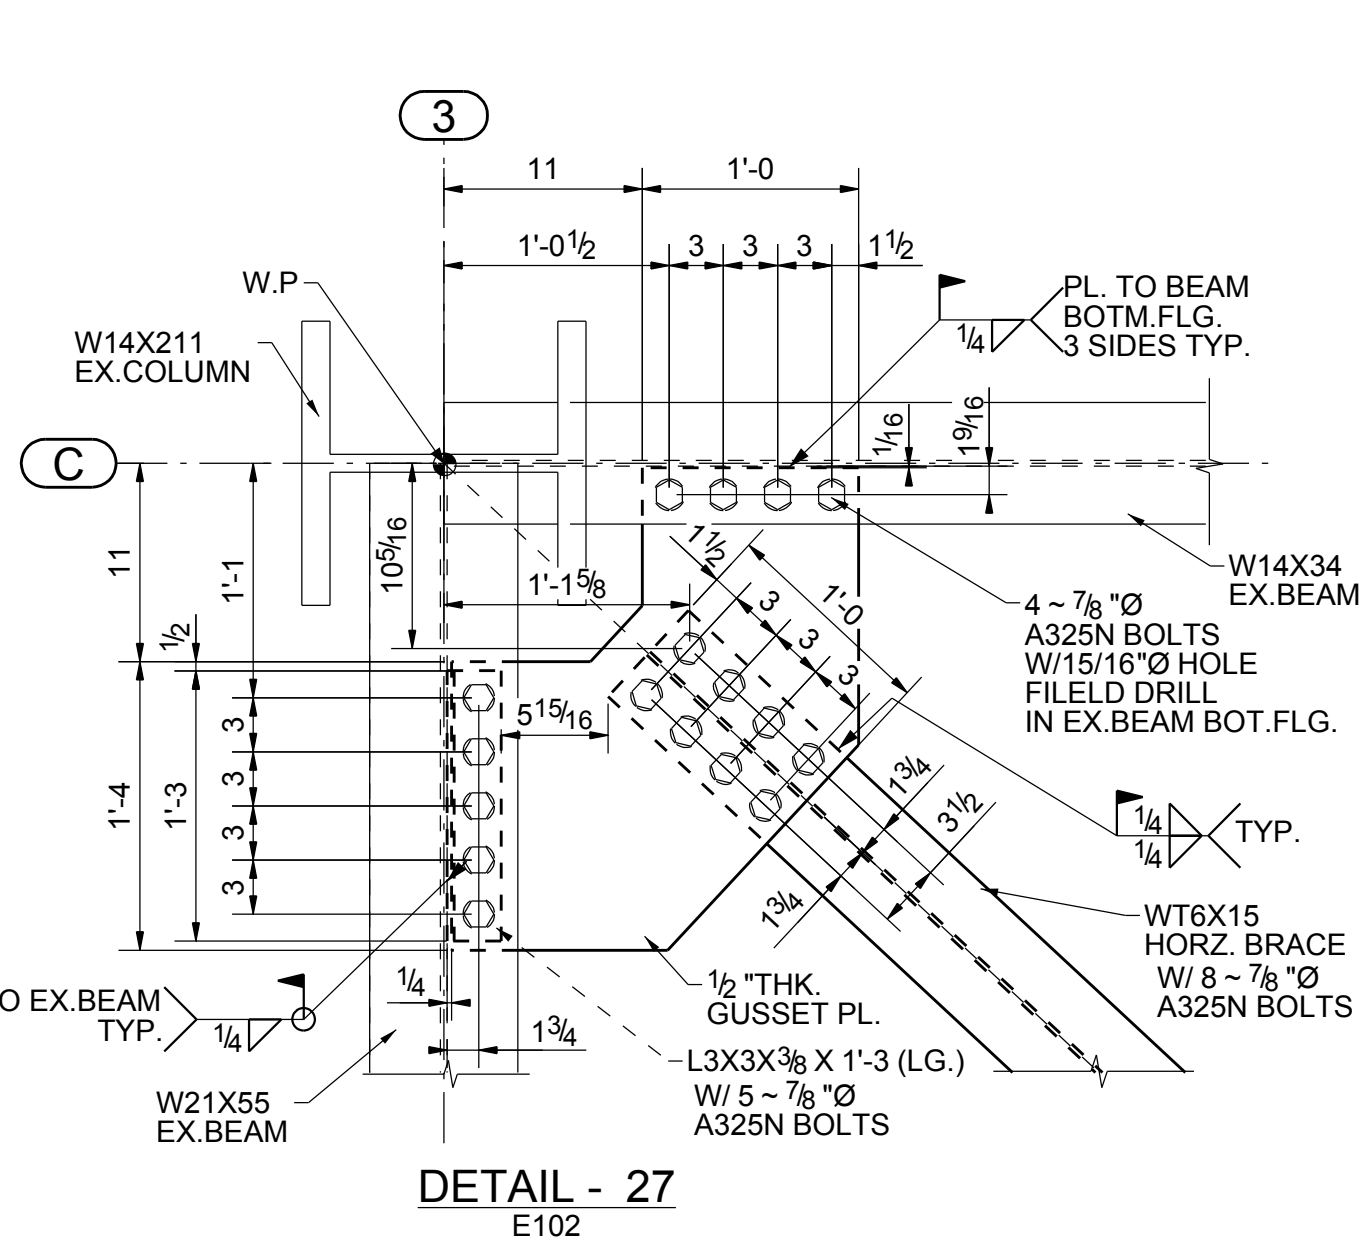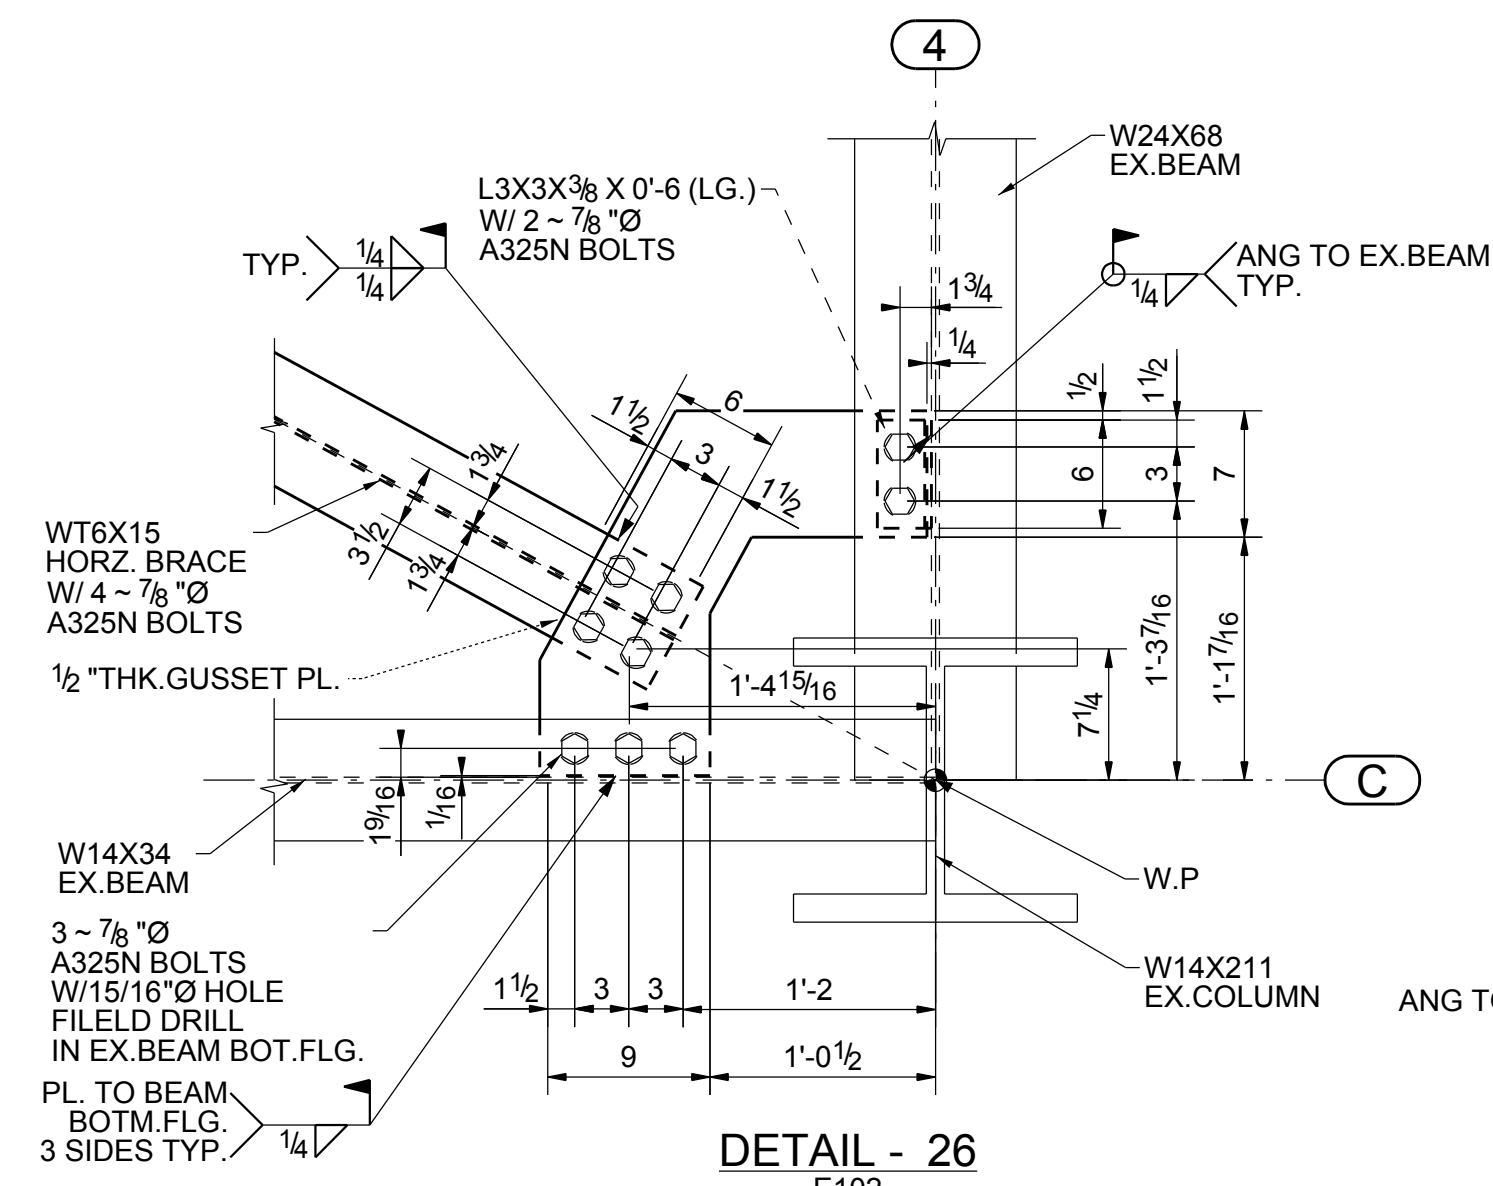

ANNOTATION:-


W14X43 *
 → EXISTING MEMBER
 → EXISTING MEMBER SIZE

ERECTOR NOTE:
 FOR ALL HORIZONTAL BRACE END GUSSET PLATES FIELD WELD ARE ALSO SHOWN IN DETAILS. FIELD WELDING NEED TO BE DONE ONLY IF EXISTING MEMBER HOLES DOES NOT MATCH WITH NEW MEMBER HOLES TYPICAL UNLESS NOTED.

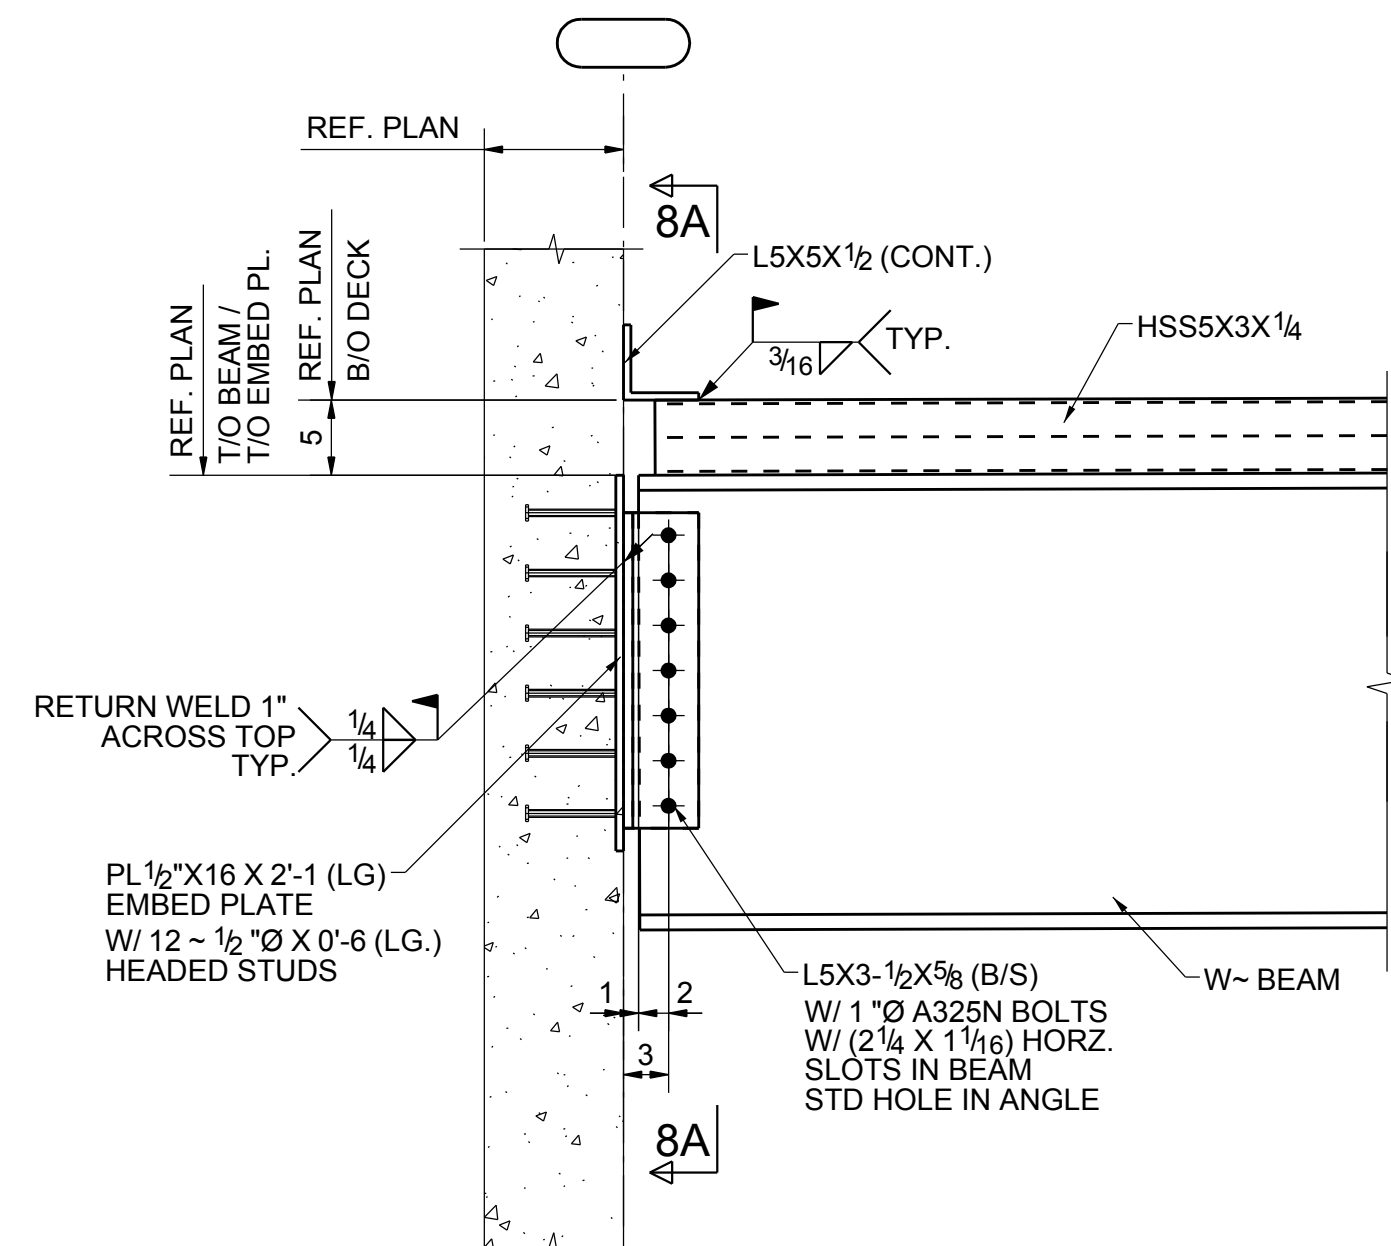


SECTION 8 - 8
E102 & E105

(REFER : C1/S-511 BEAM TO PANEL CONNECTION SCHEDULE)

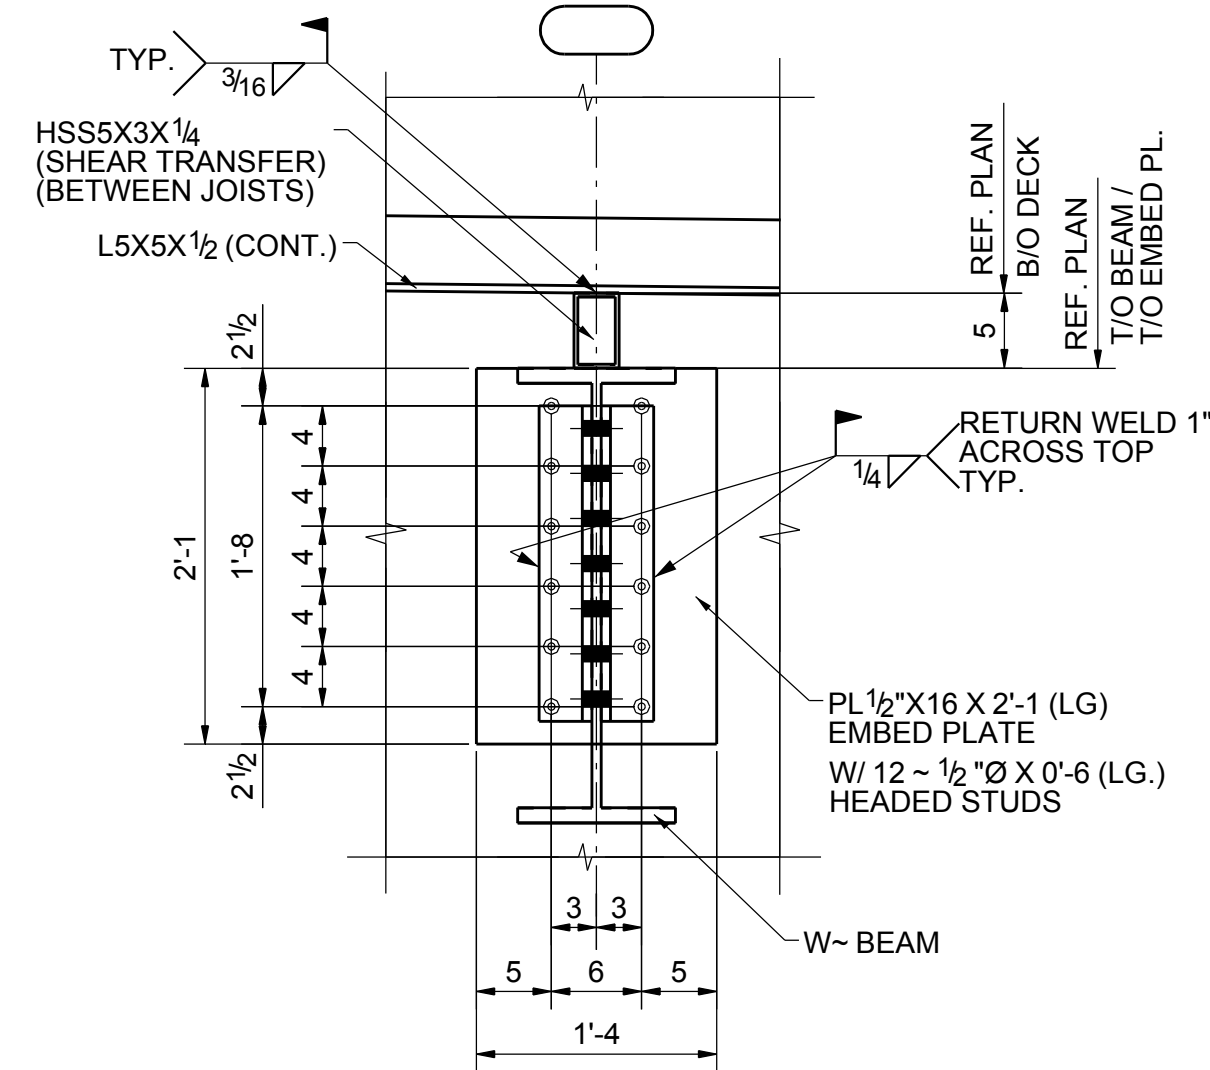


SECTION 8A - 8A

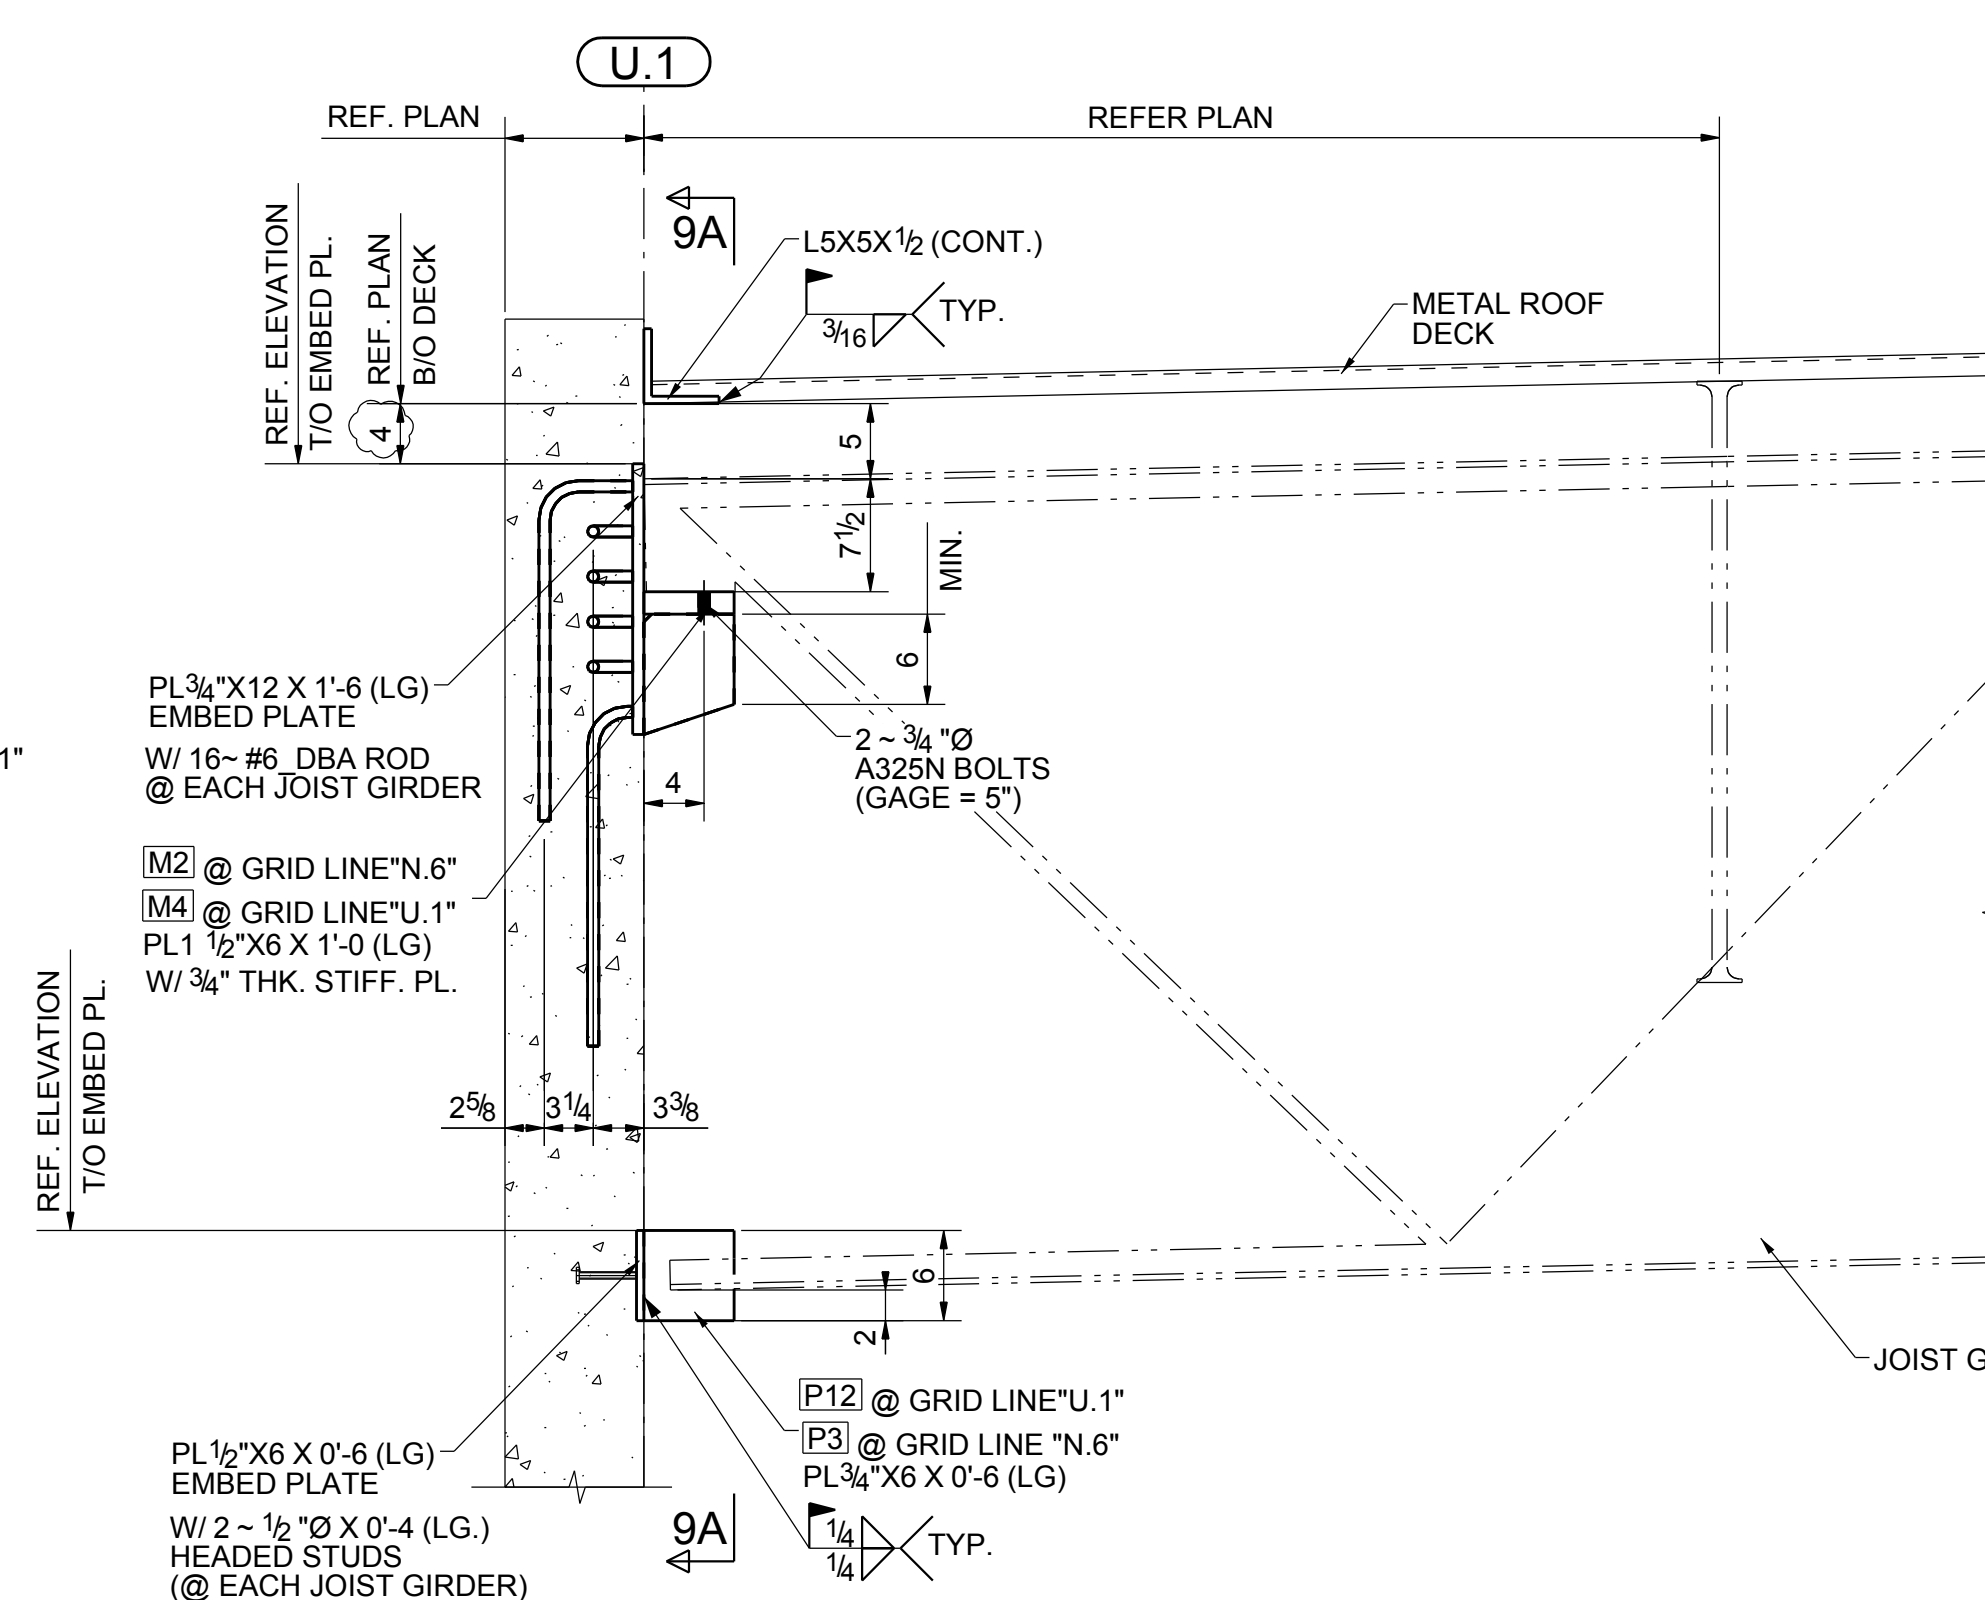


SECTION 9 - 9
E102 & E105

TYPICAL GIRDER TO TILT-UP PANEL CONNECTION DETAIL

(REFER : C4/S-511 GIRDER TO TILT-UP/THERMOMASS CONN.)

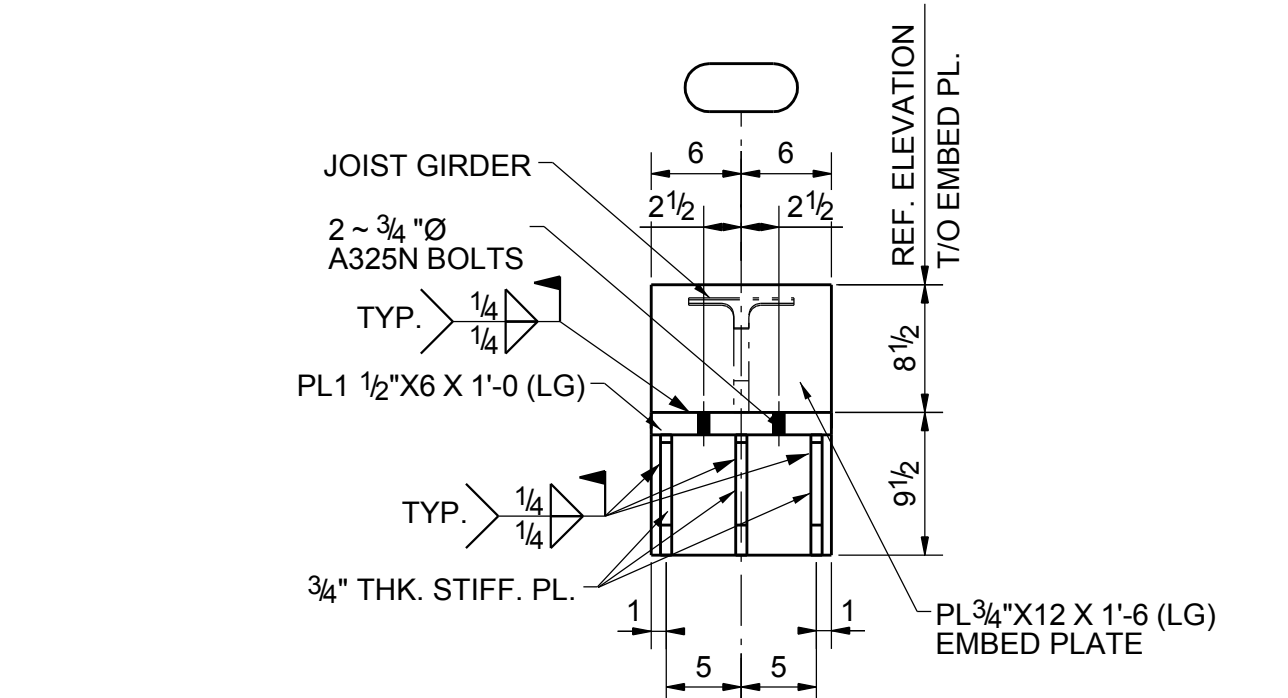


DETAIL 9B

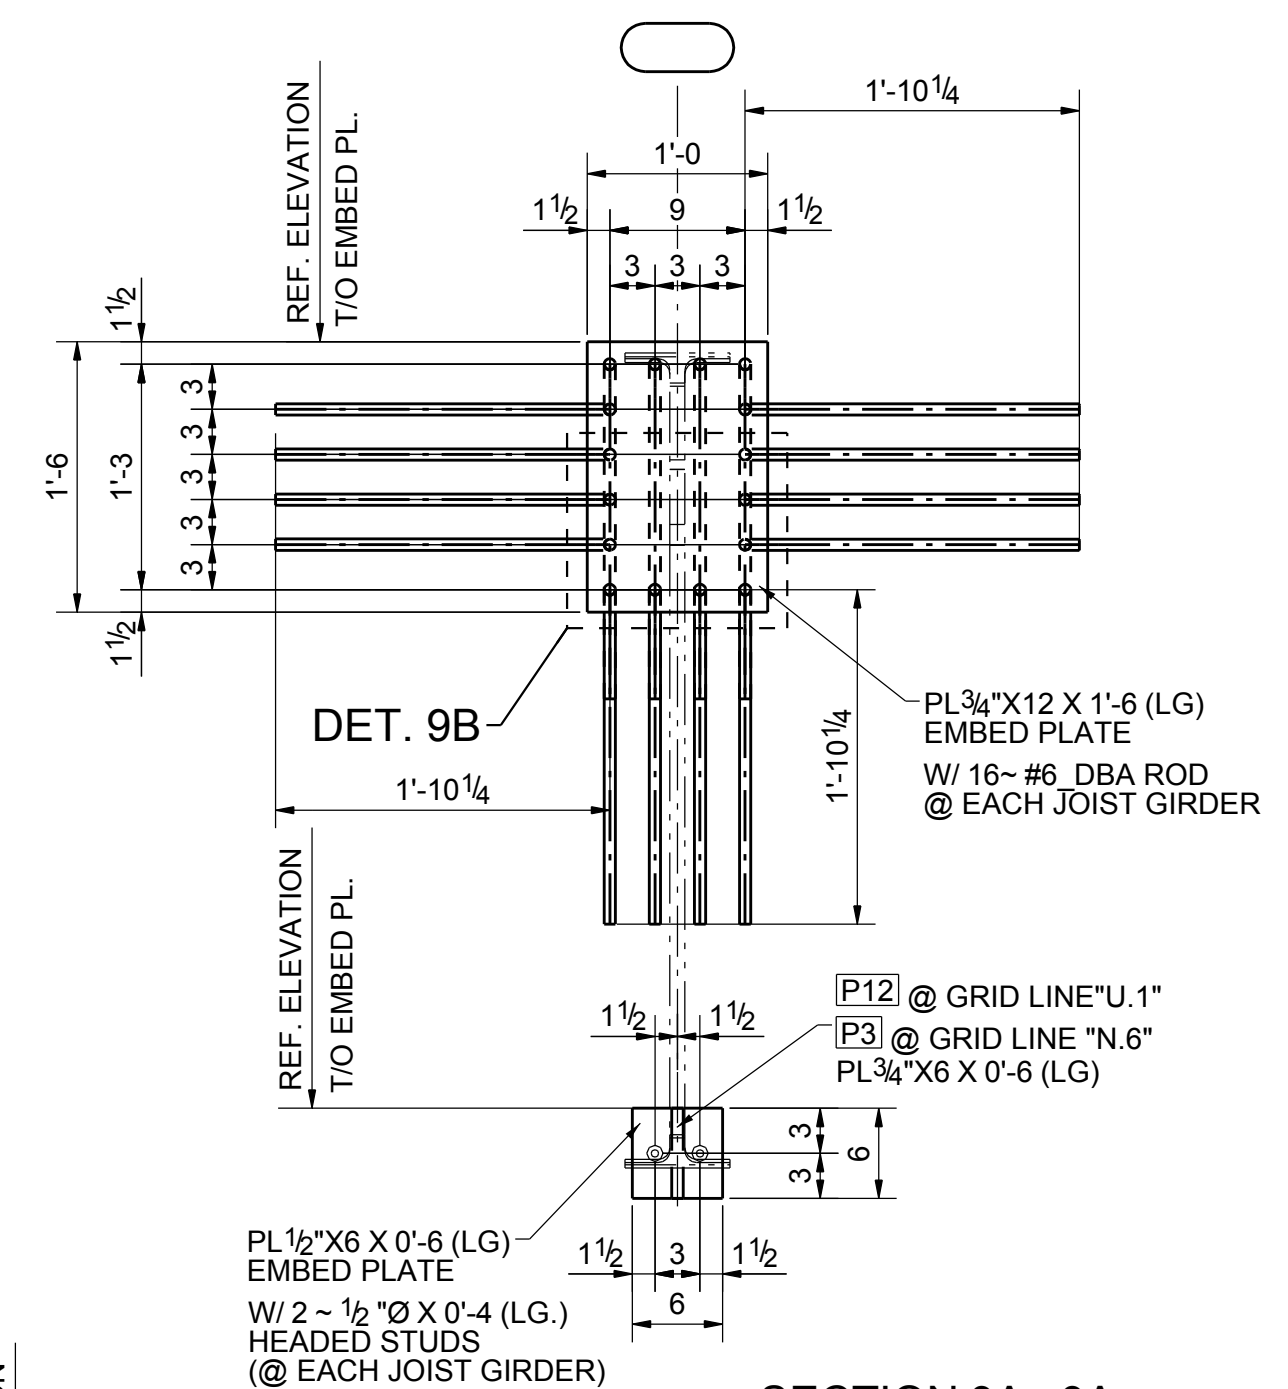

SECTION 9A - 9A


(REFER : C5/S-511 JOIST GIRDER TO EMBED)

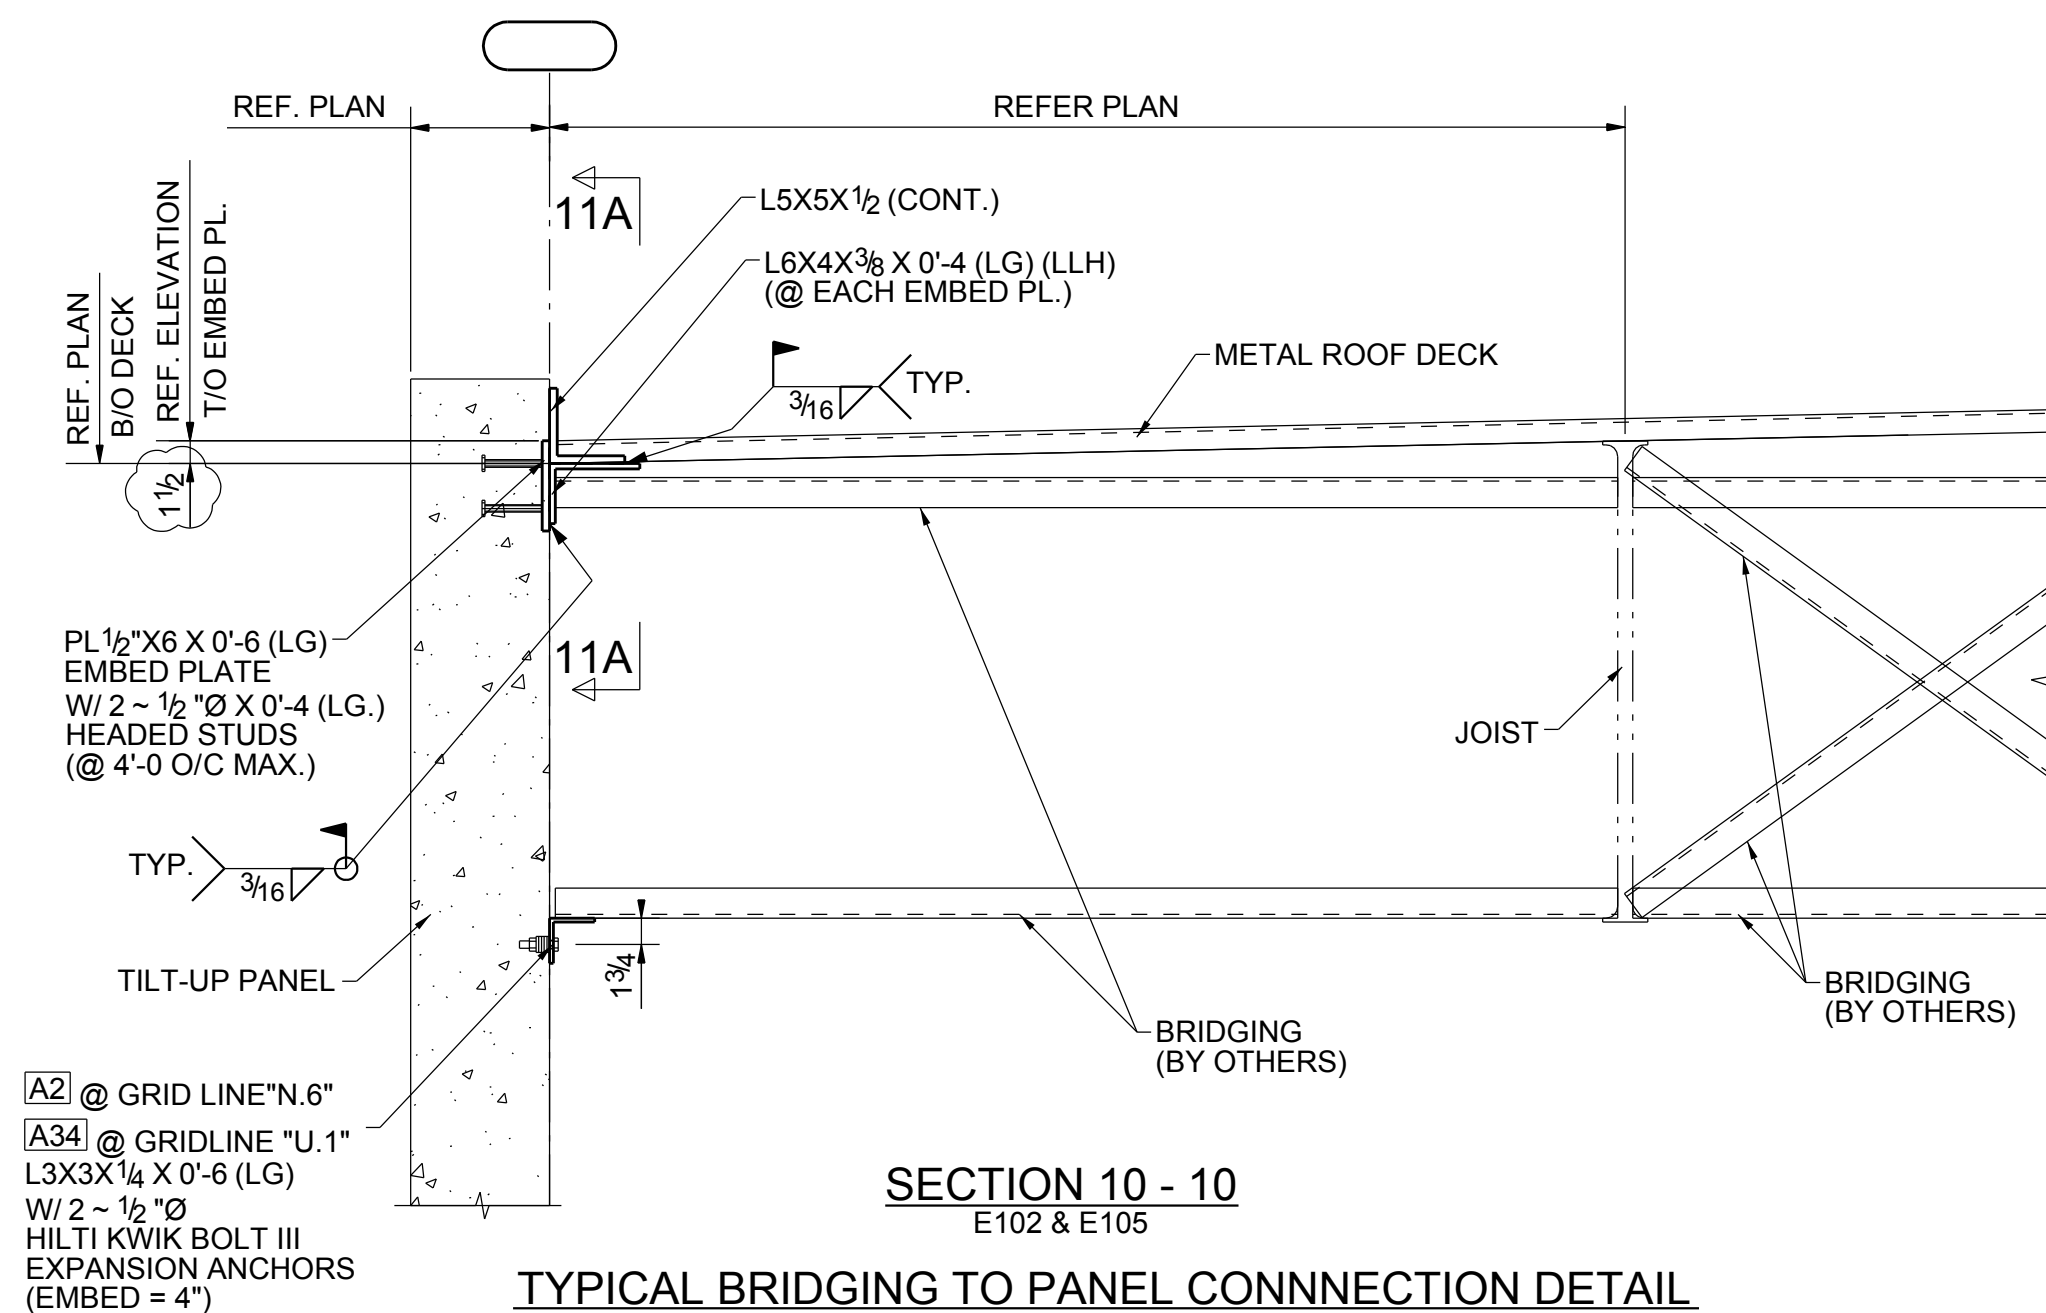

SECTION 10 - 10
E102 & E105

TYPICAL BRIDGING TO PANEL CONNECTION DETAIL


(REFER : C2/S-511 BRIDGING TO PANEL)

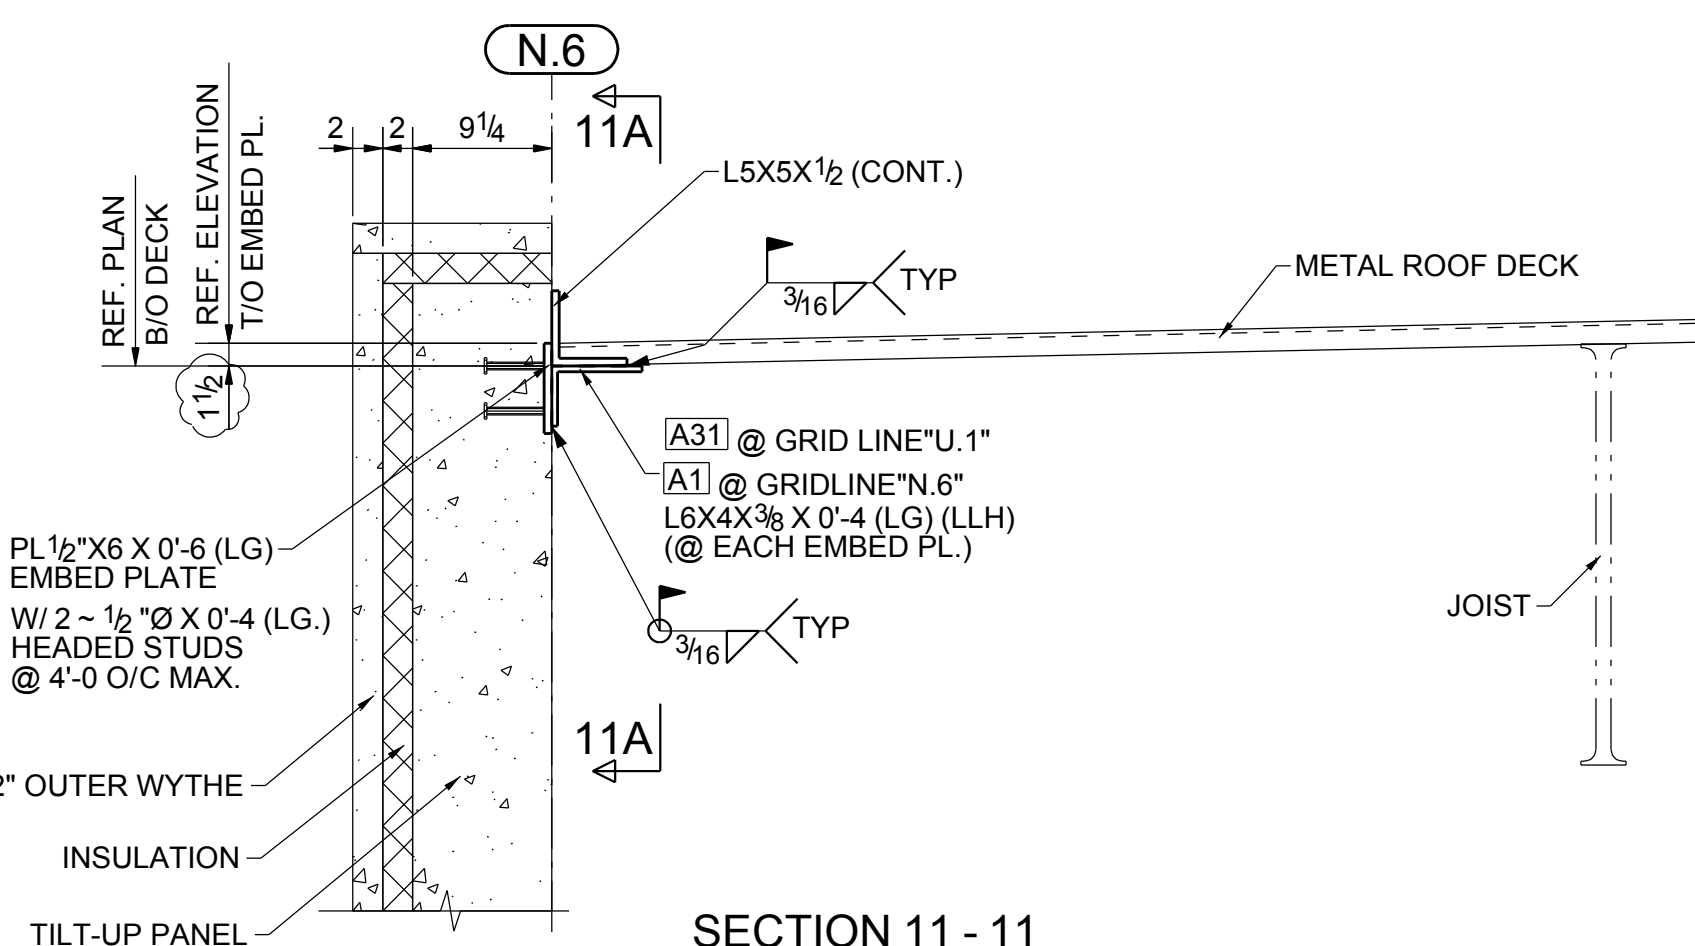

SECTION 11 - 11
E102 & E105


TYPICAL PERIMETER ANGLE TO EMBED PLATE

(REFER : C3/S-511 BRIDGING TO PANEL)

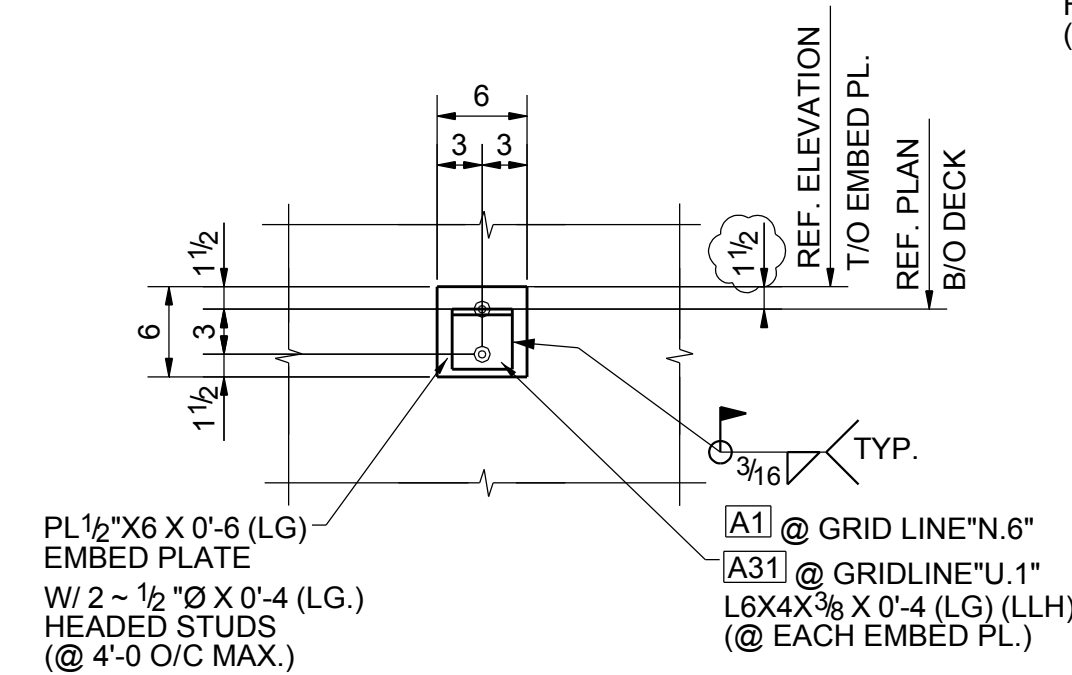


SECTION 11A - 11A


APPROVER VERIFY / FURNISH
ALL CLOUDED INFORMATIONS
TYPICAL

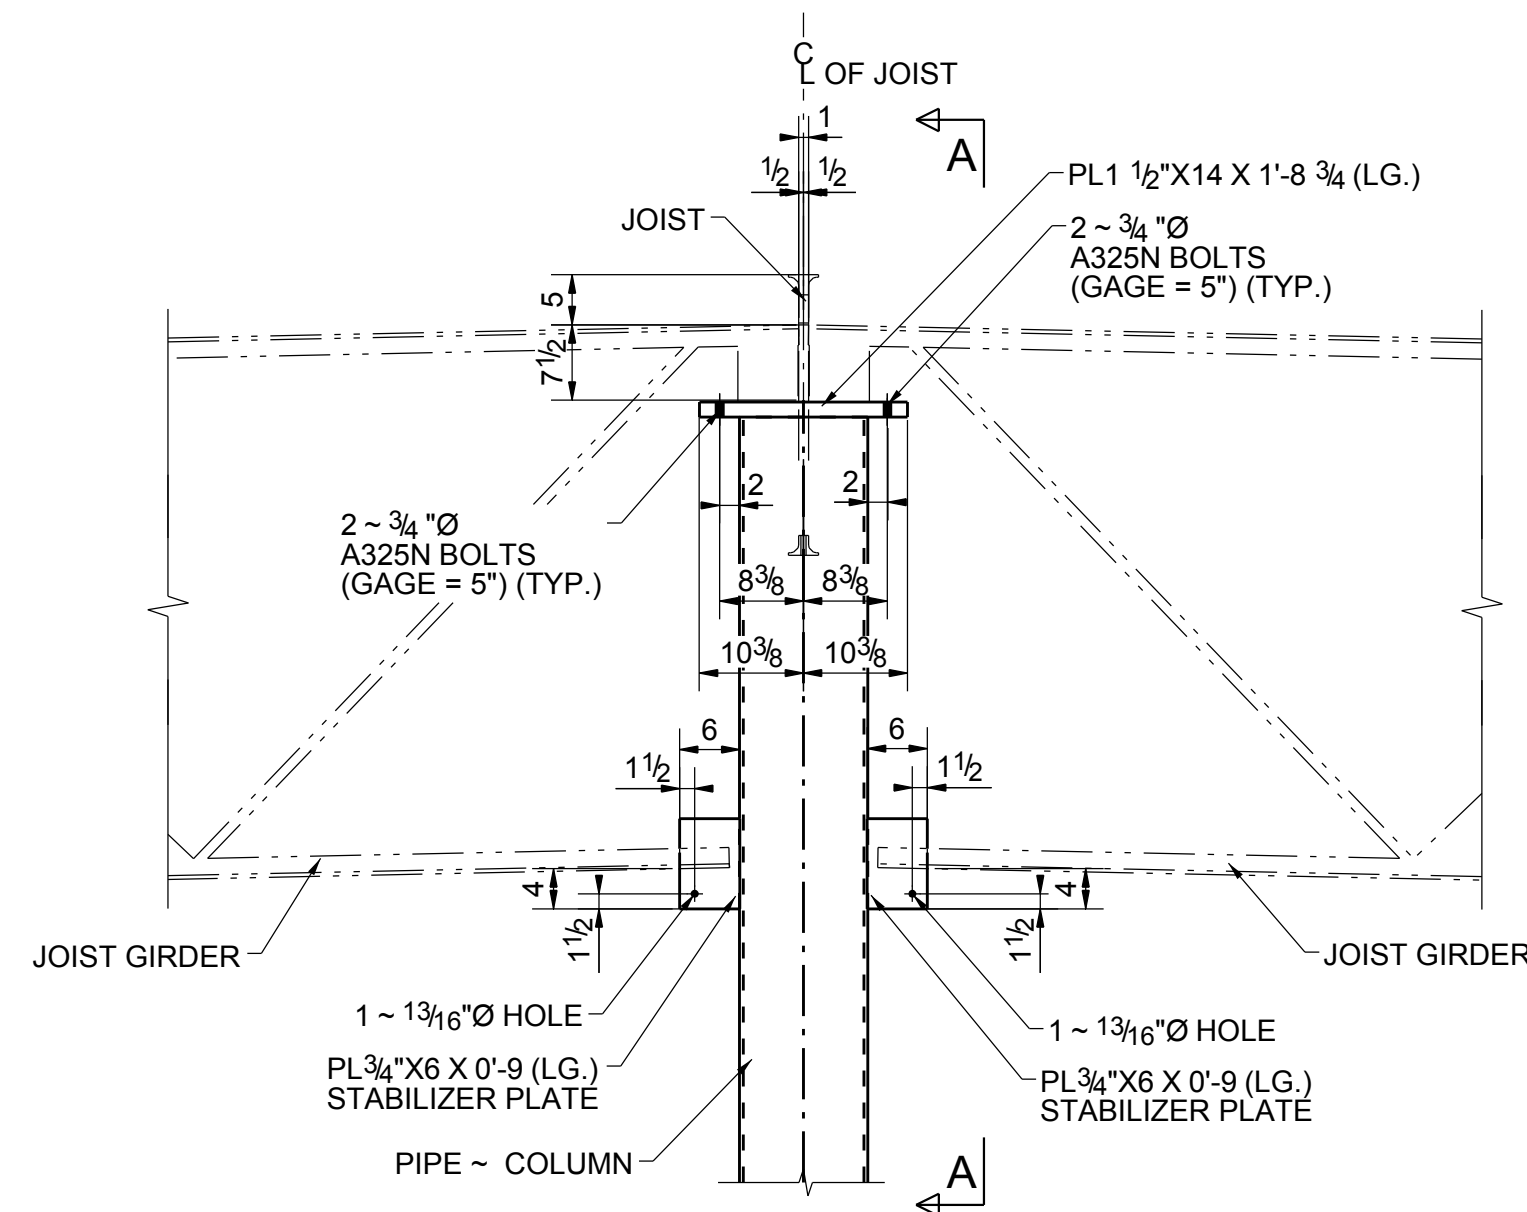


**TYPICAL JOIST GIRDER RESTING ABOVE PIPE ~ COLUMN
TIE JOIST CONNECTION DETAIL**

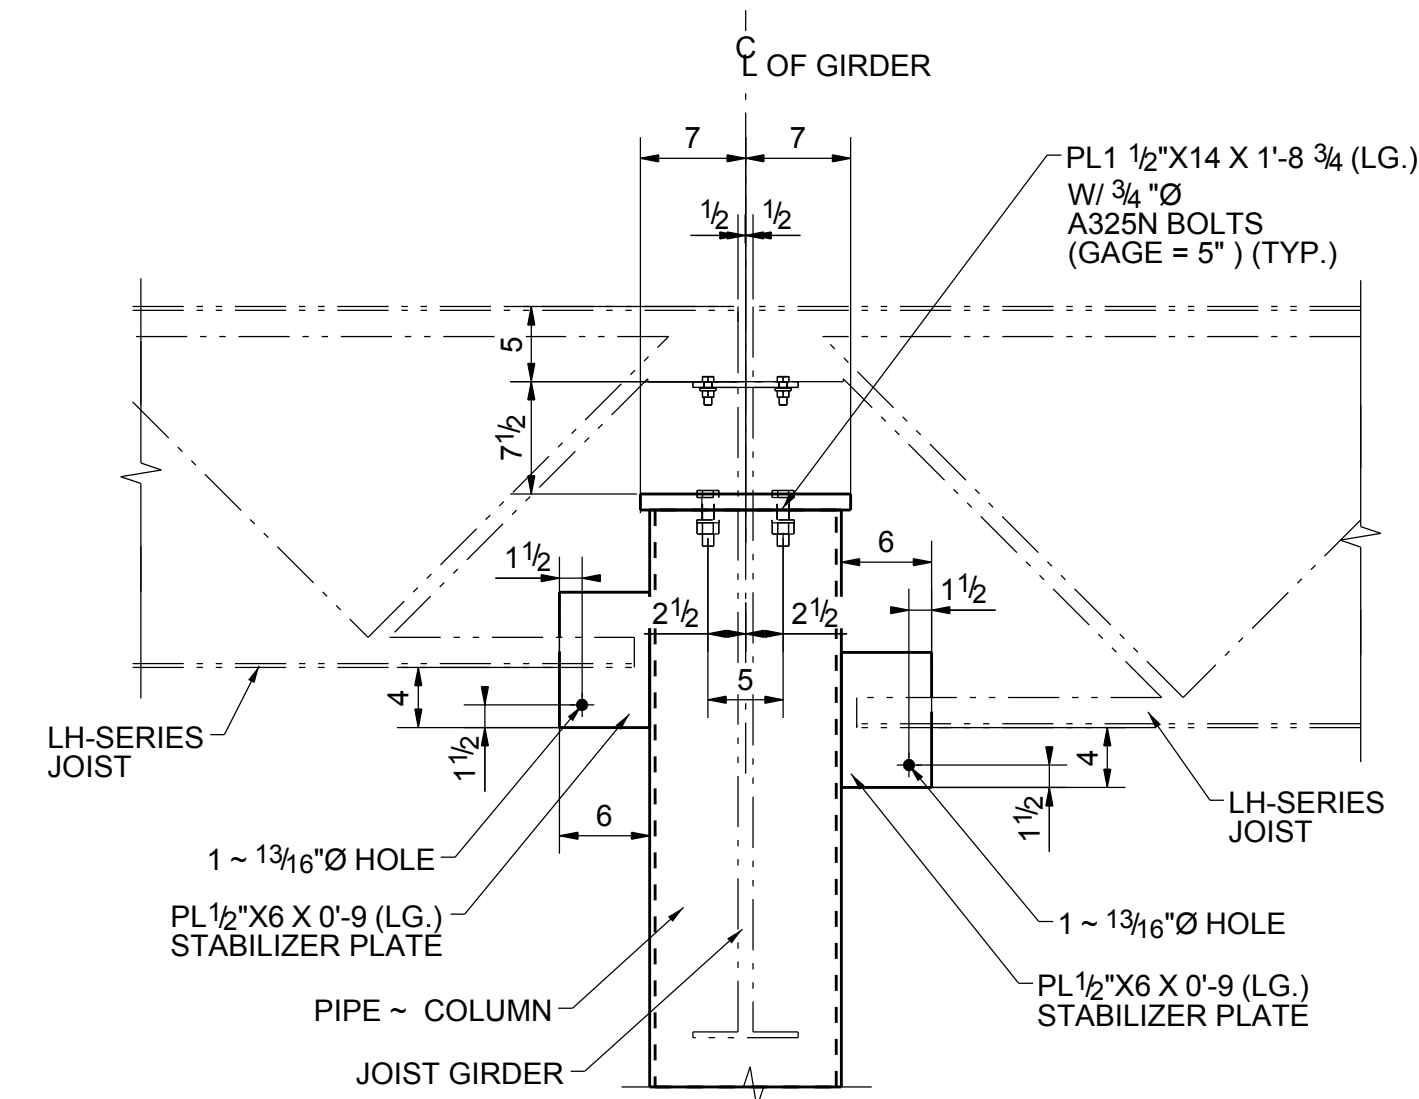


SECTION A - A

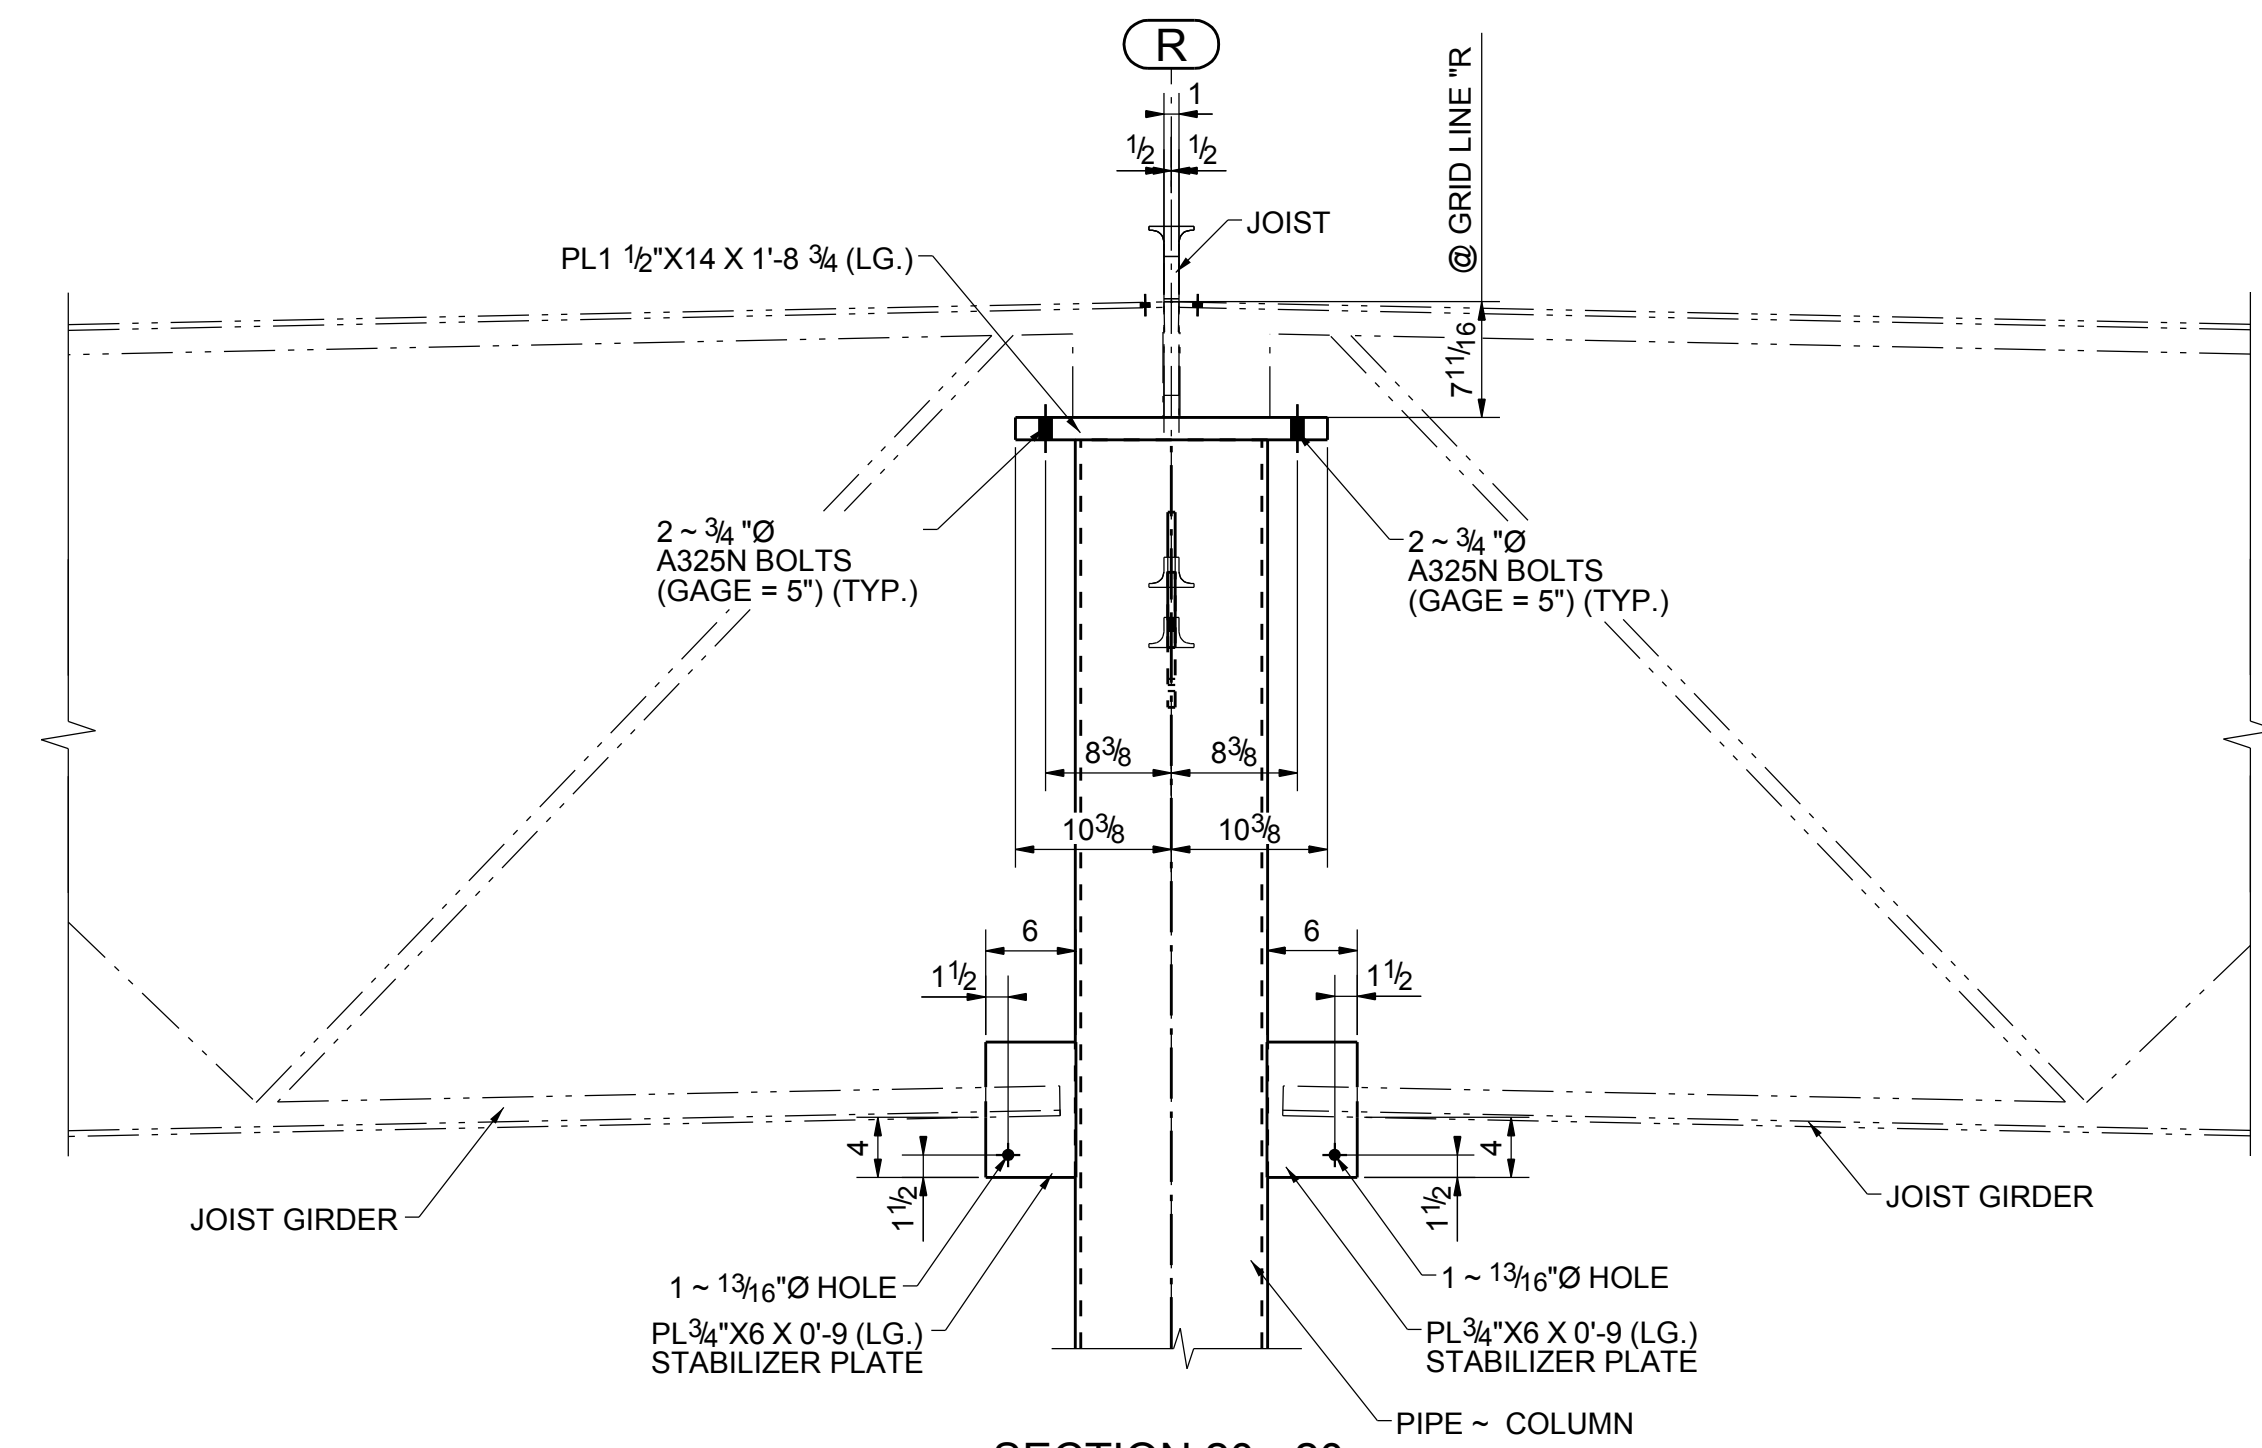


**SECTION 20 - 20
E102
TYPICAL JOIST GIRDER RESTING ABOVE PIPE ~ COLUMN
TIE JOIST CONNECTION DETAIL ALONG GRID LINE "R"**

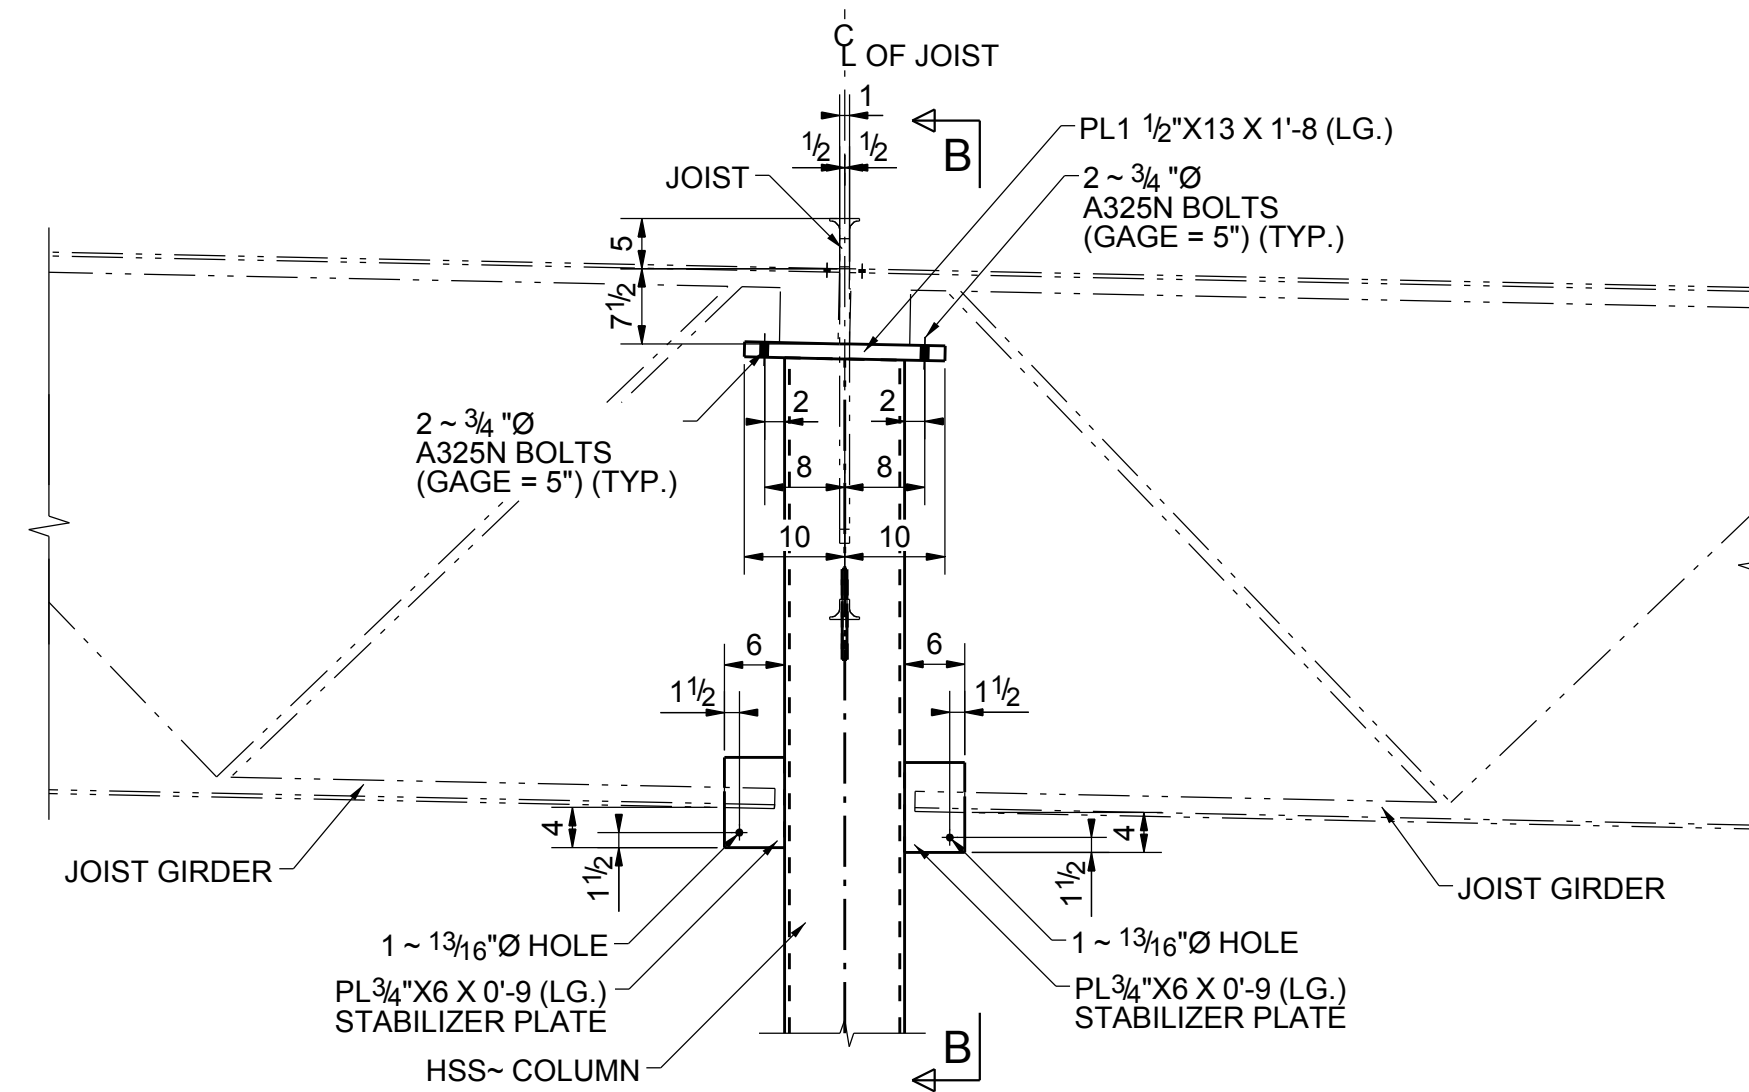


**TYPICAL JOIST GIRDER RESTING ABOVE HSS ~ COLUMN
TIE JOIST CONNECTION DETAIL**

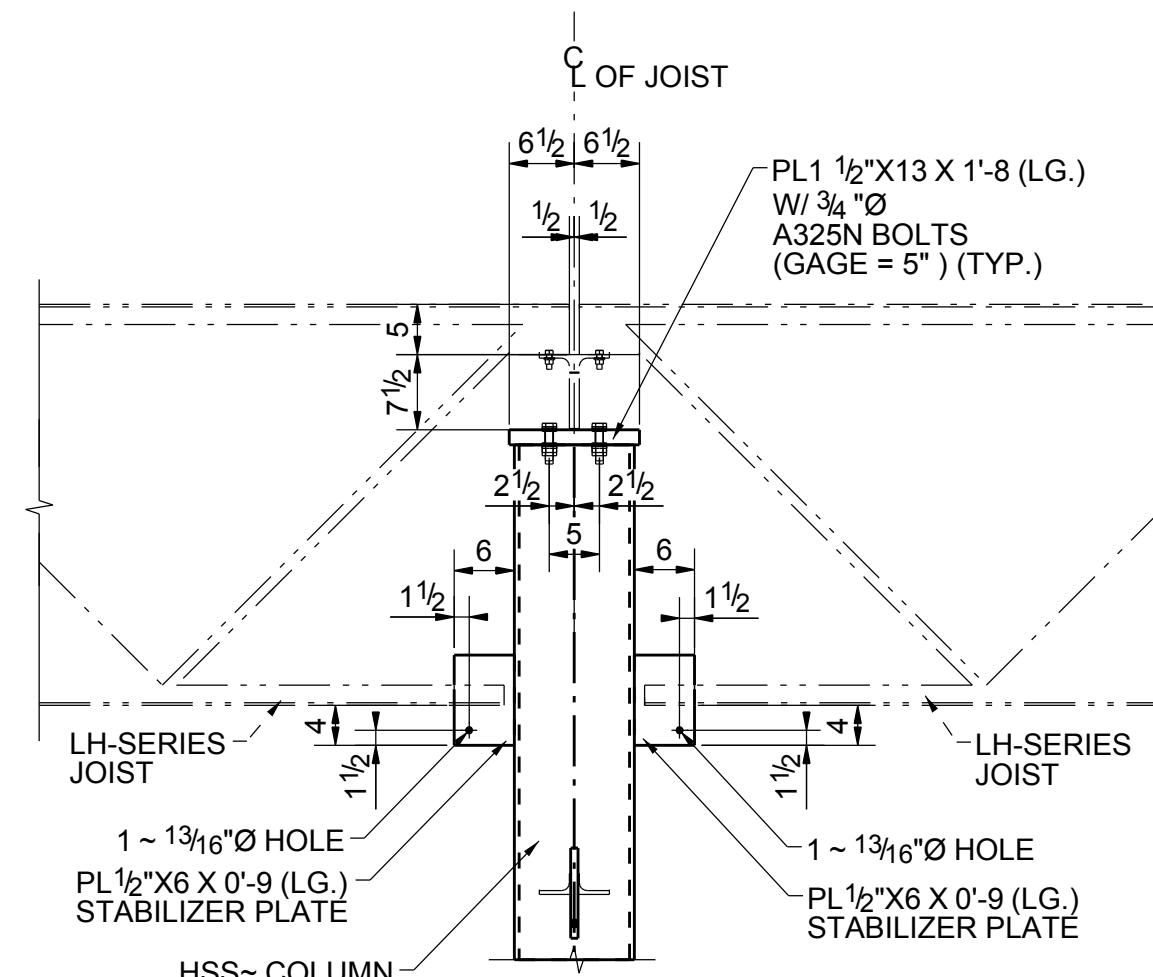


SECTION B - B

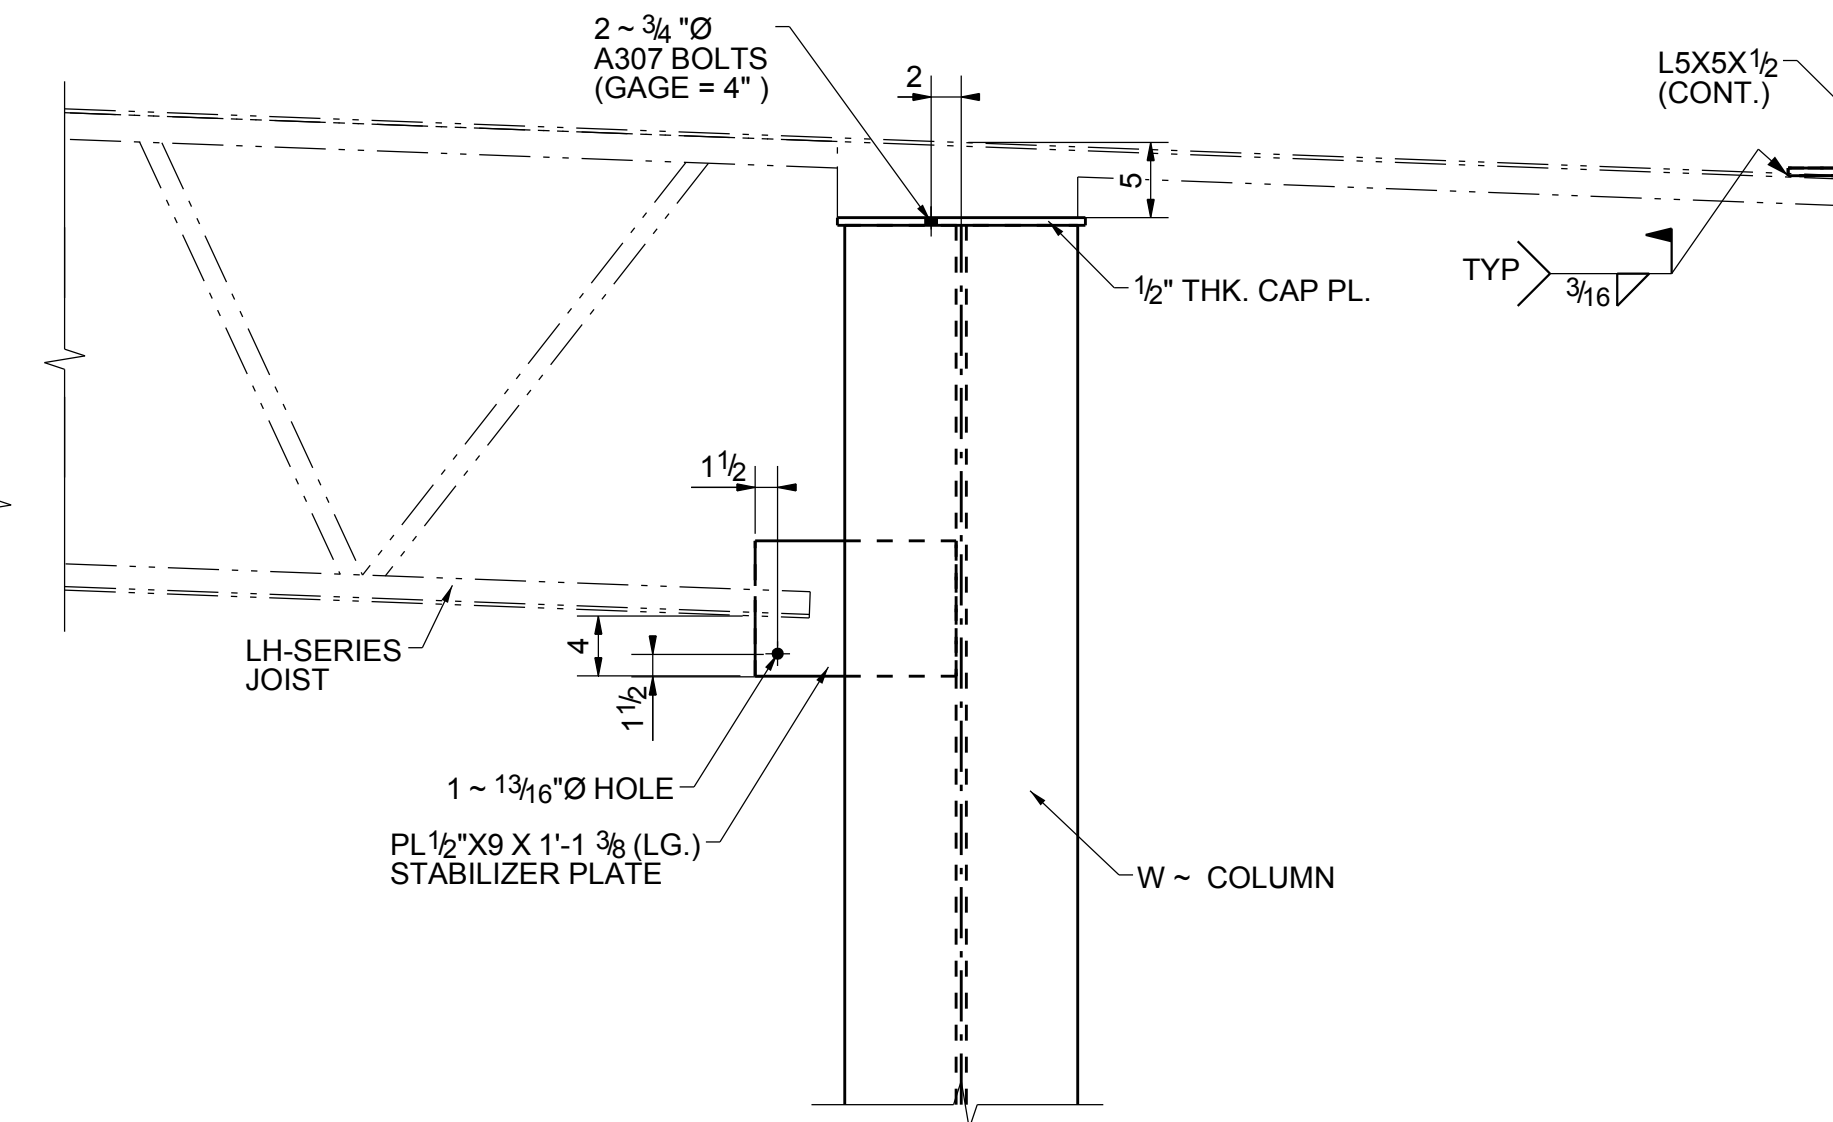


**TYPICAL JOIST TO W ~ COLUMN WEB
TIE JOIST CONNECTION DETAIL**

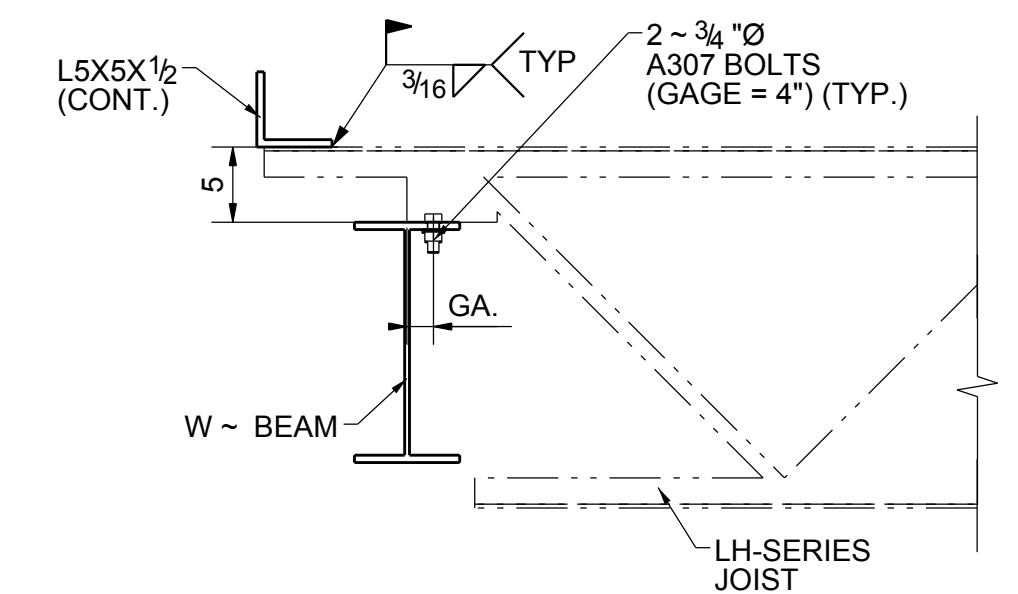


**TYPICAL JOIST TO W ~ BEAM
CONNECTION DETAIL**

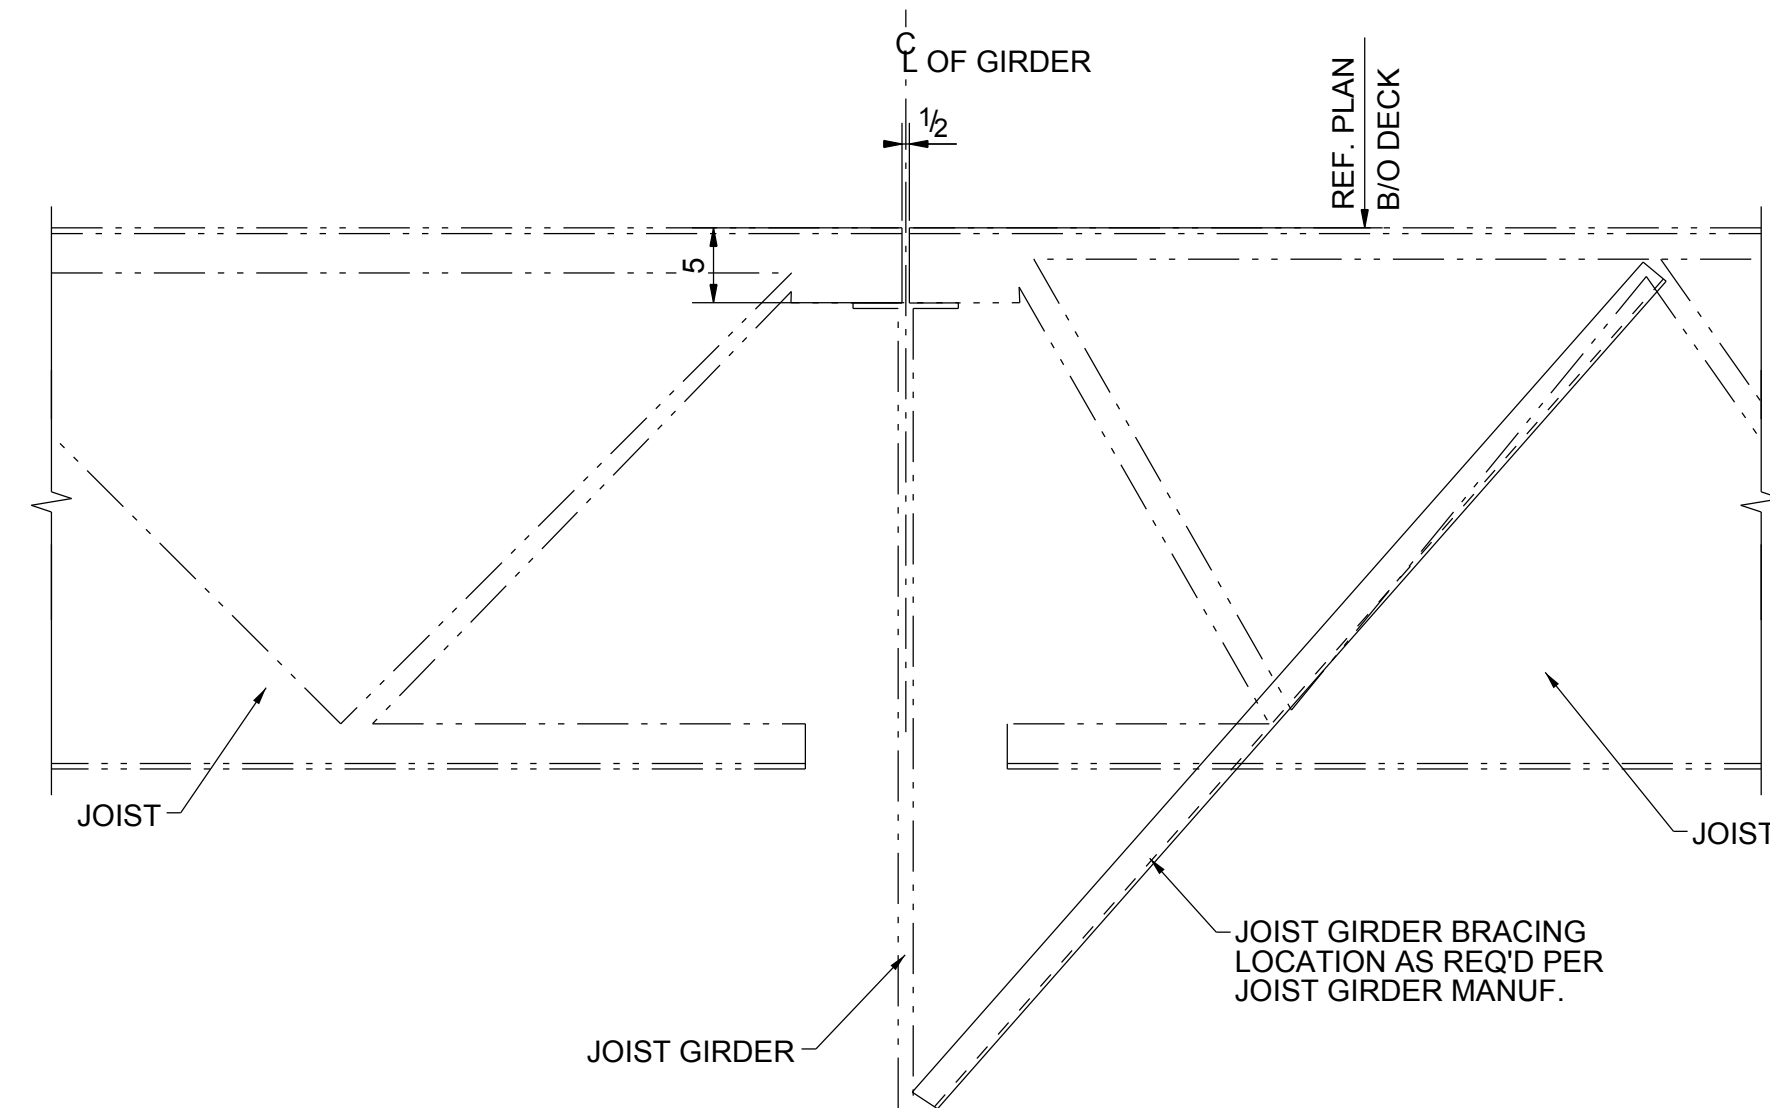


**TYPICAL JOIST TO GIRDER
CONNECTION DETAIL**

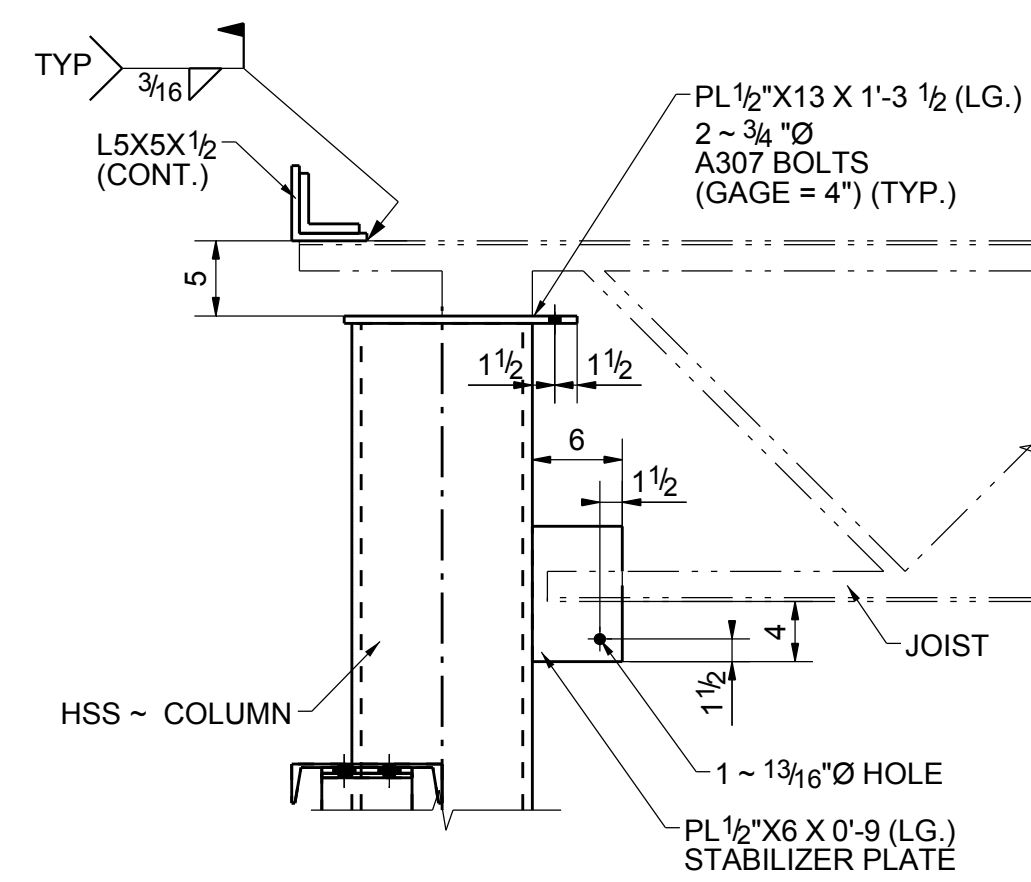


**TYPICAL JOIST TO HSS ~ COLUMN
TIE JOIST CONNECTION DETAIL**

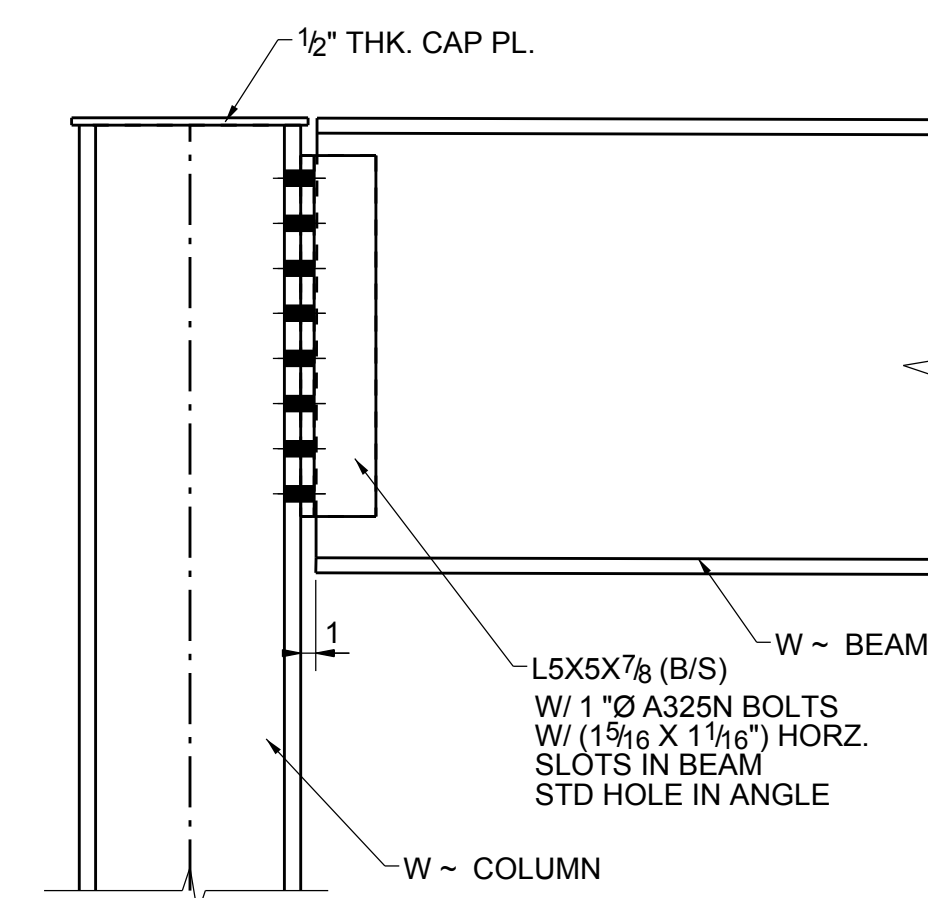


**TYPICAL W ~ BEAM TO W ~ COLUMN
KNIFE ANGLE CONNECTION DETAIL
ALONG GRID LINE "16"**

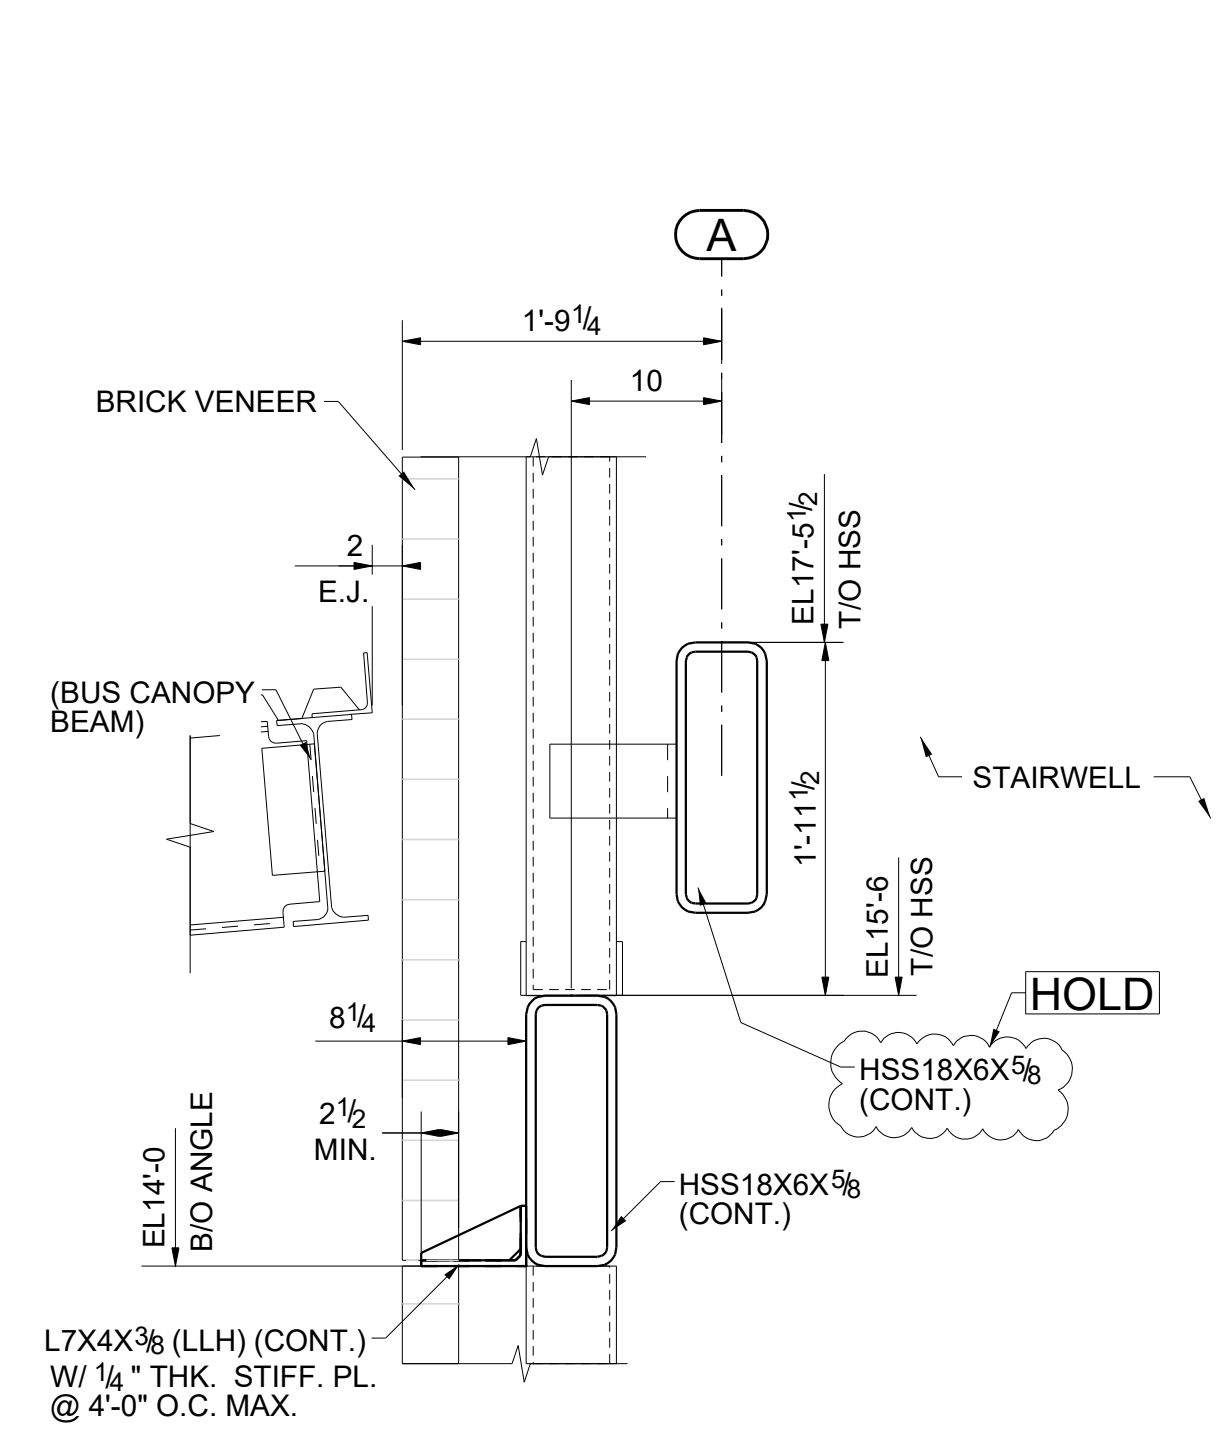


SECTION 7 - 7
E102
(REFER:SECTION 1/S5.006)

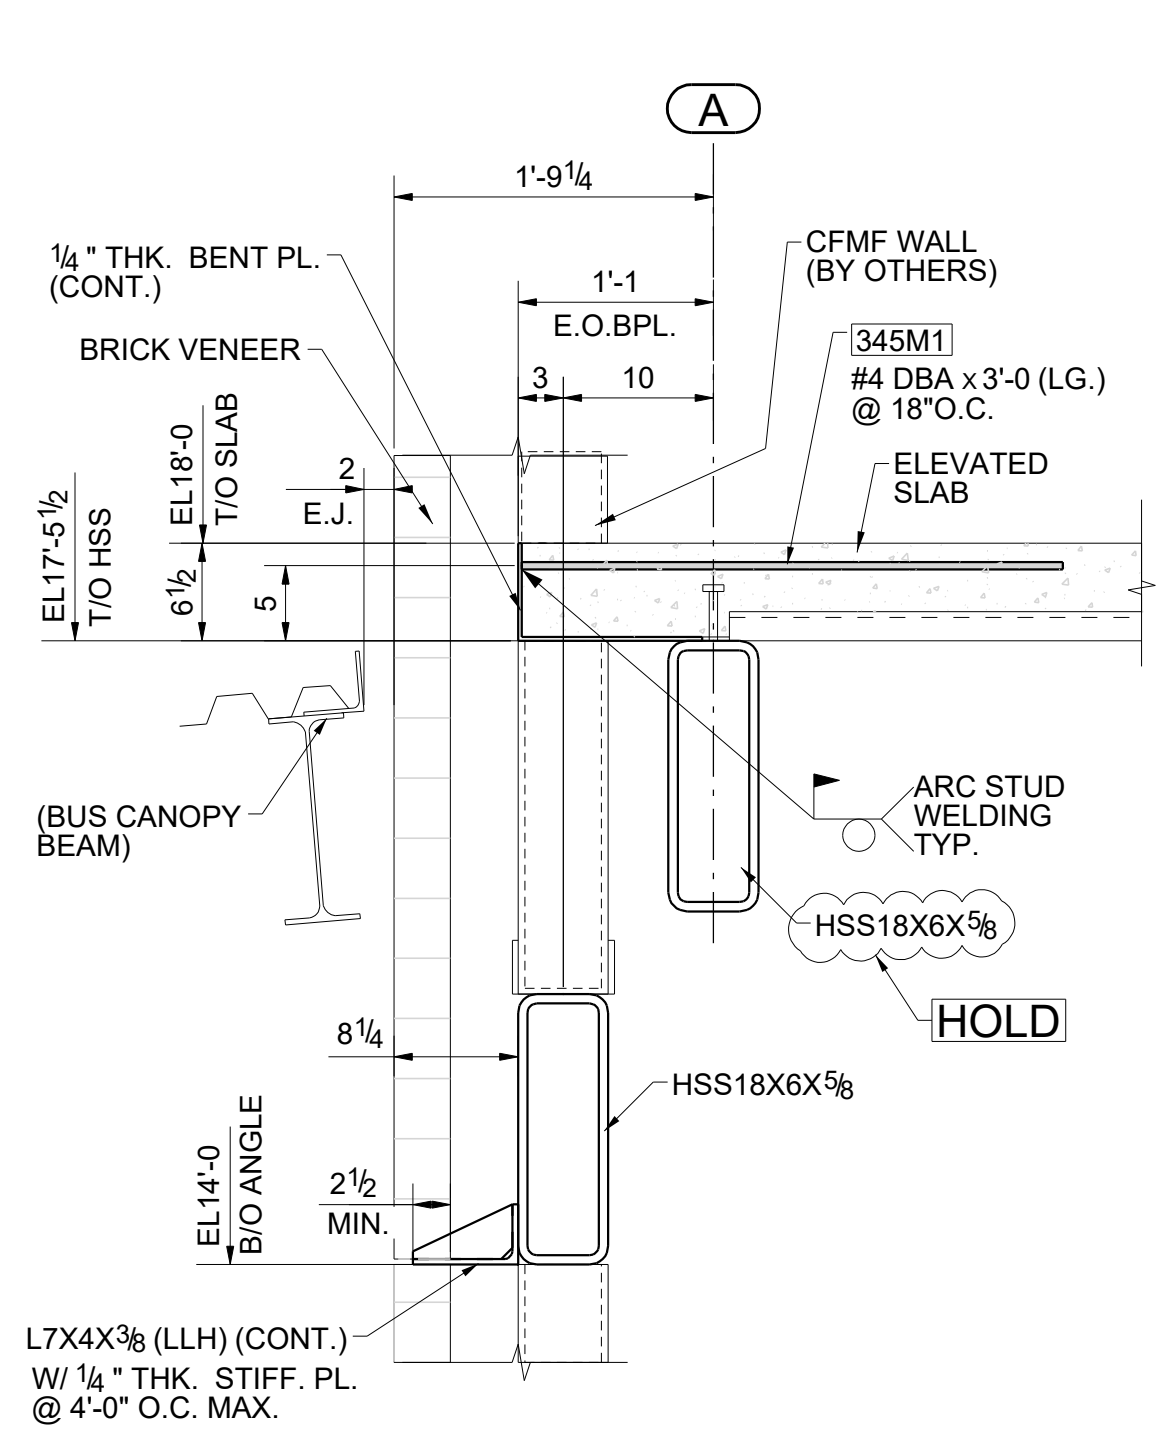


SECTION 8 - 8
E102
(REFER:SECTION 11/S5.006)

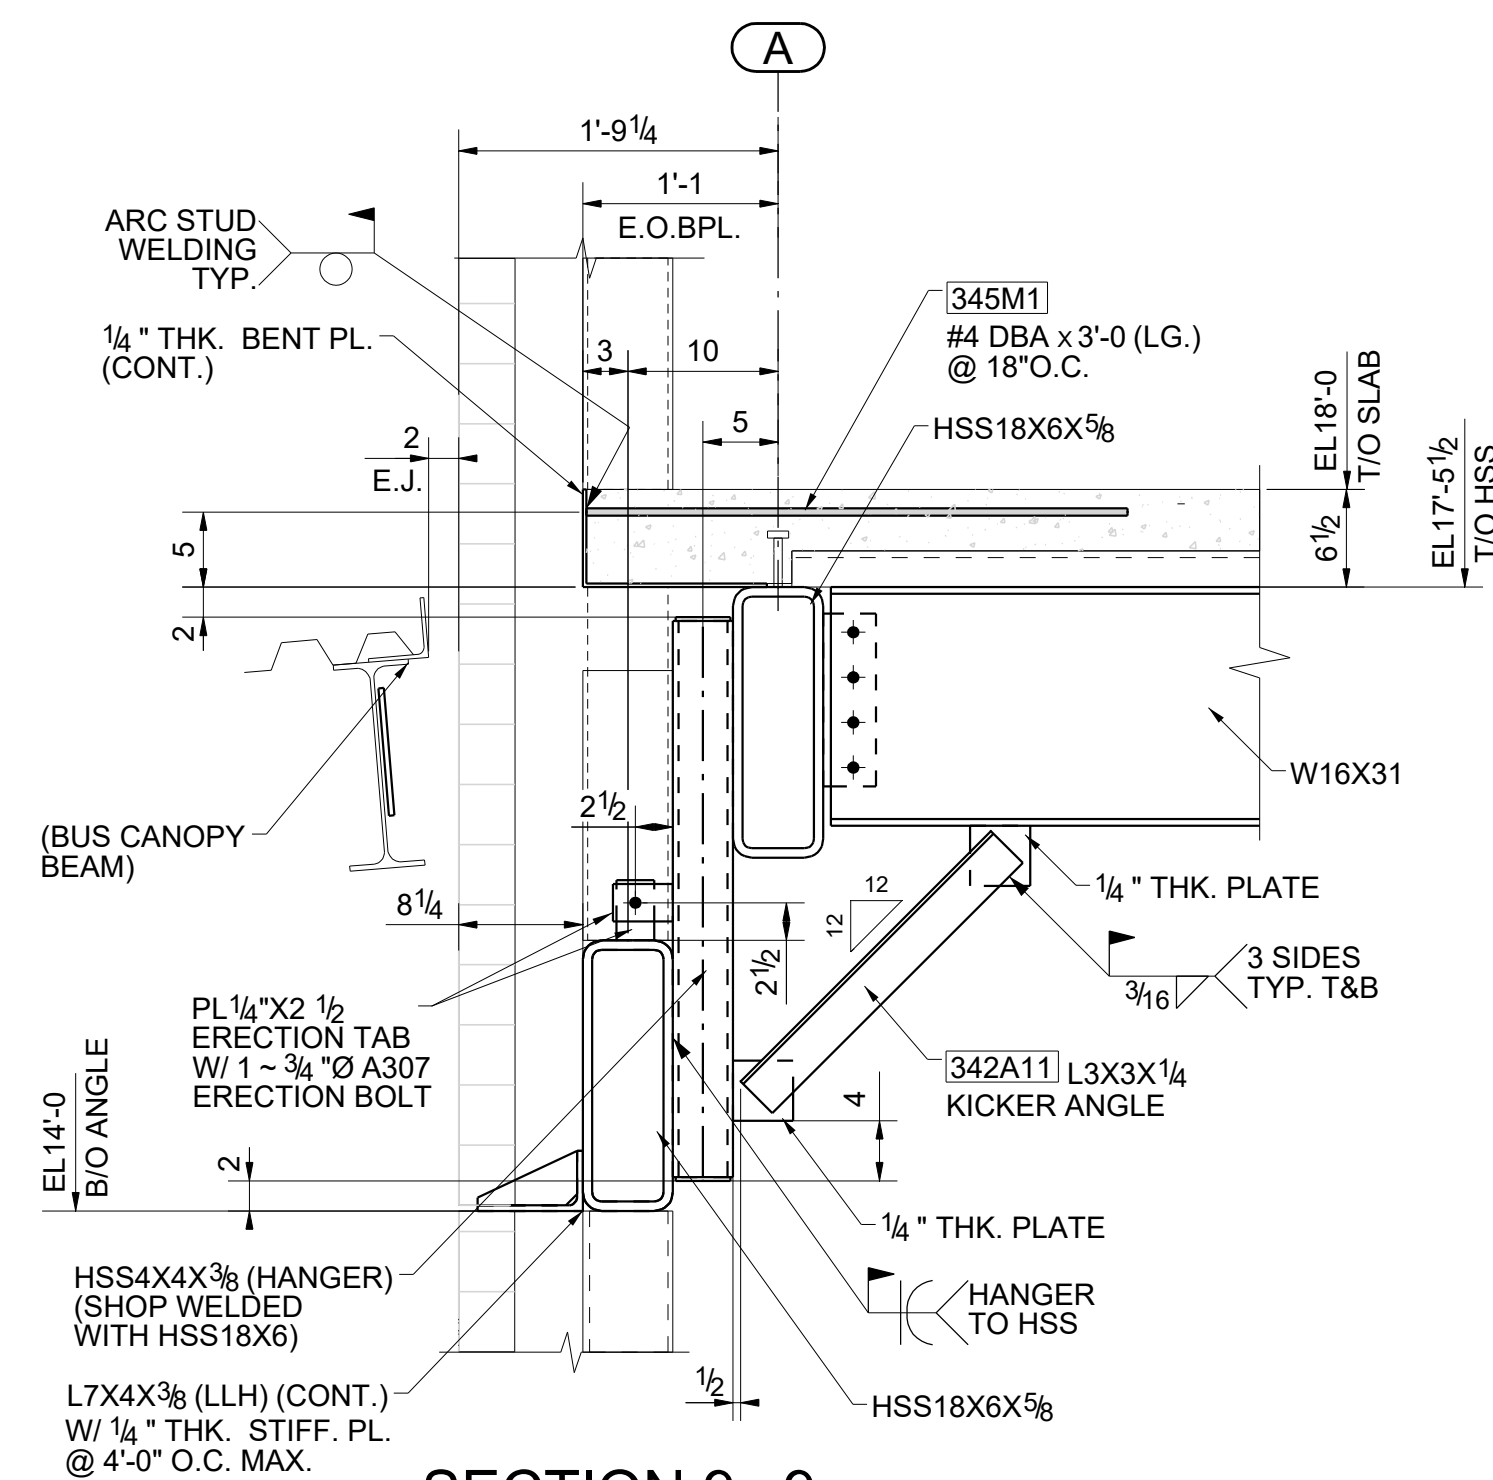


SECTION 9 - 9
E102
(REFER:SECTION 15/S5.006)

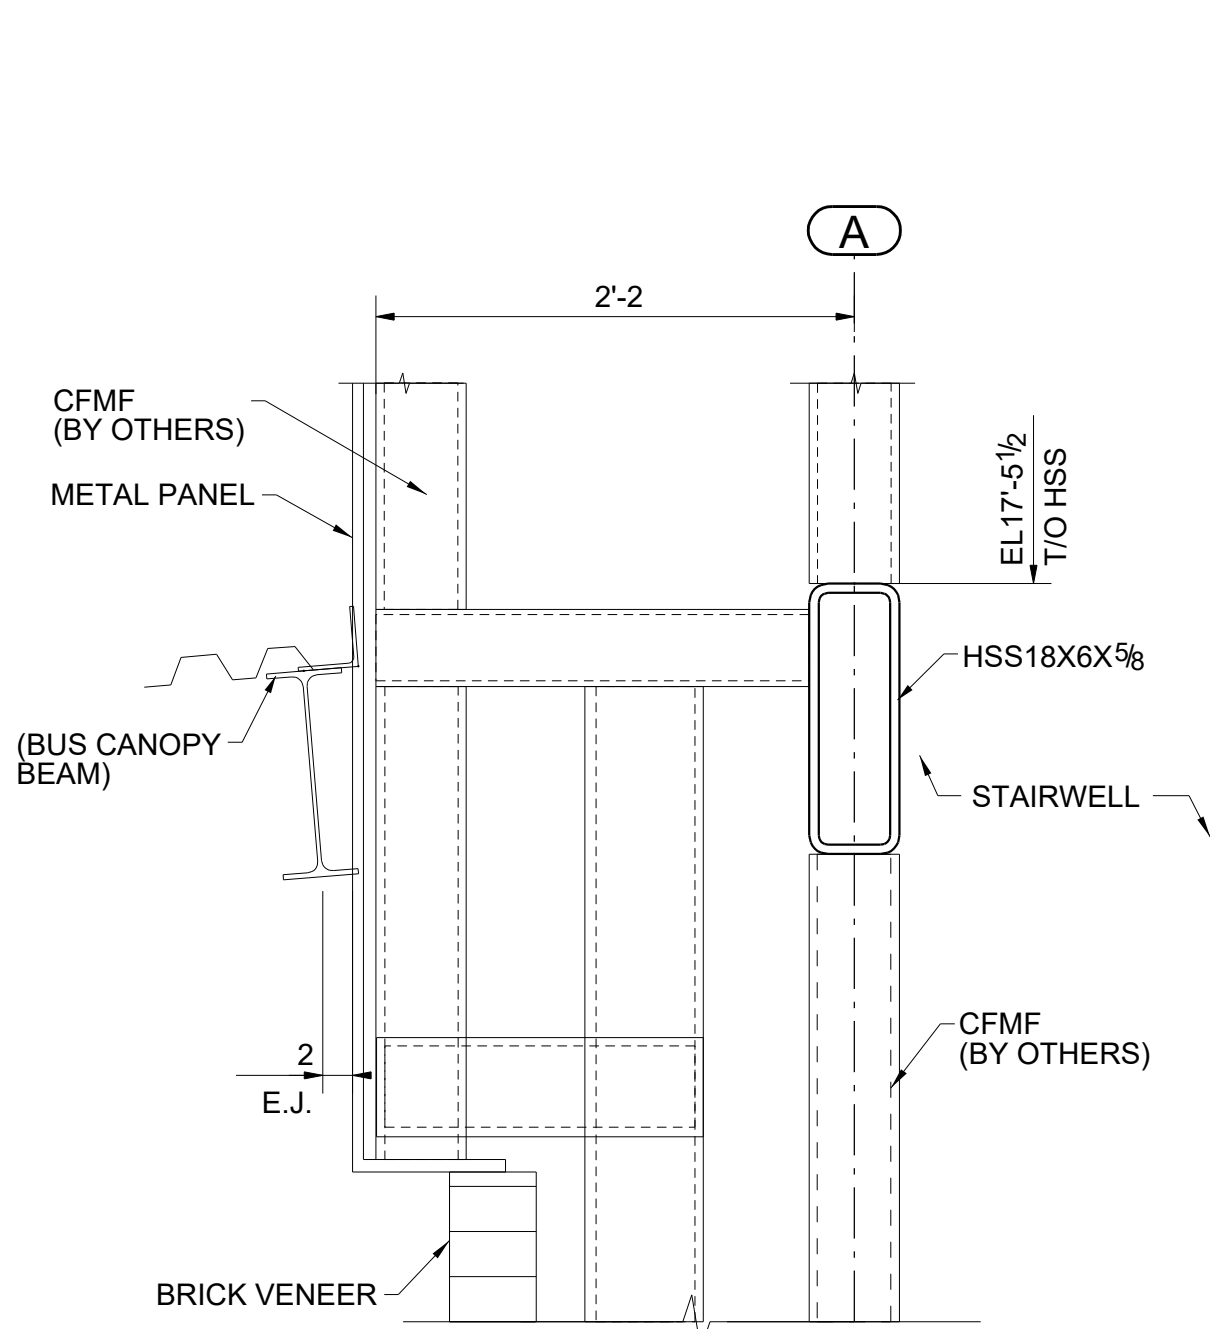


SECTION 10 - 10
E102
(REFER:SECTION 3/S5.006)

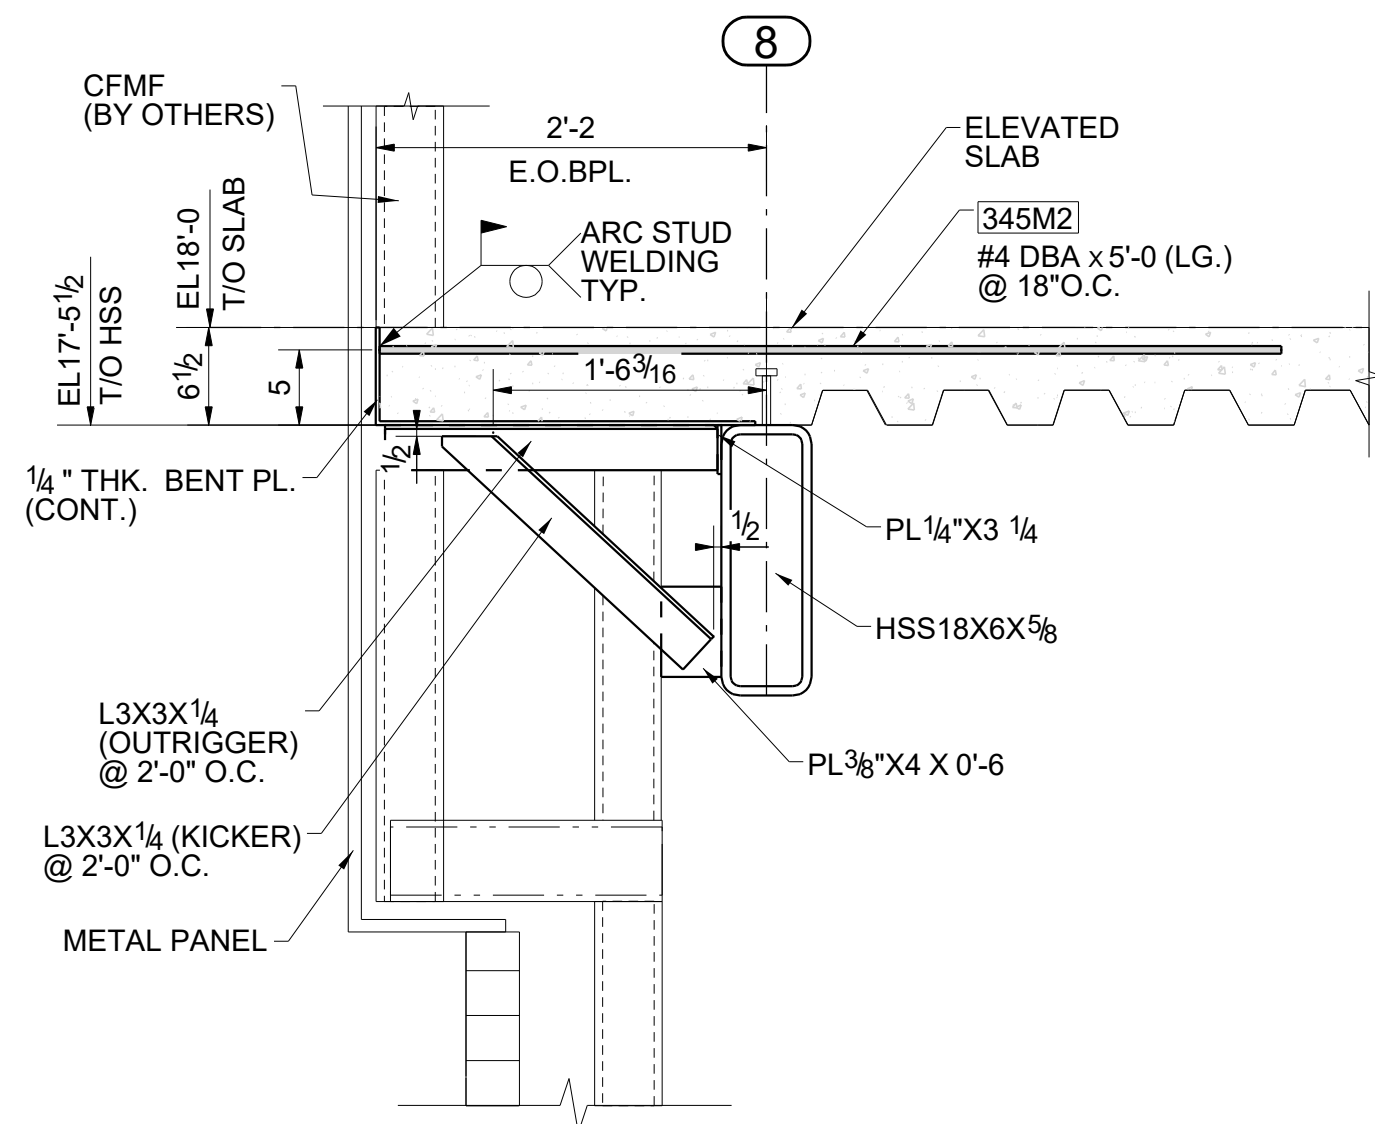


SECTION 11 - 11
E102
(REFER:SECTION 2/S5.006)

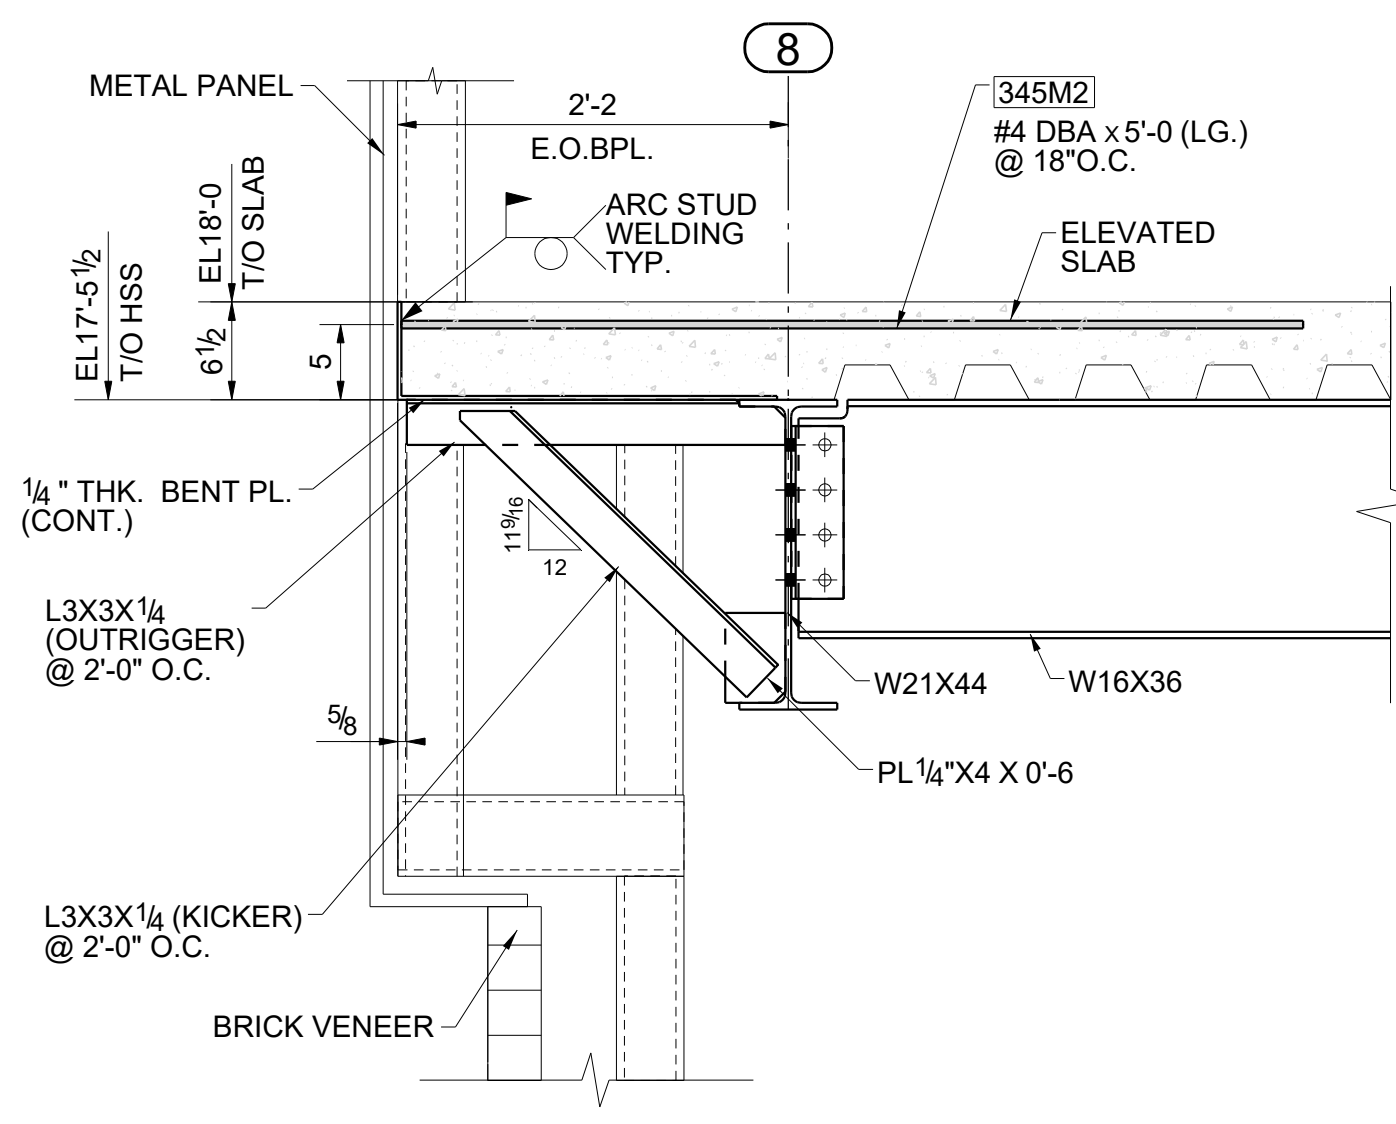


SECTION 12 - 12
E102
(REFER:SECTION 4/S5.006)

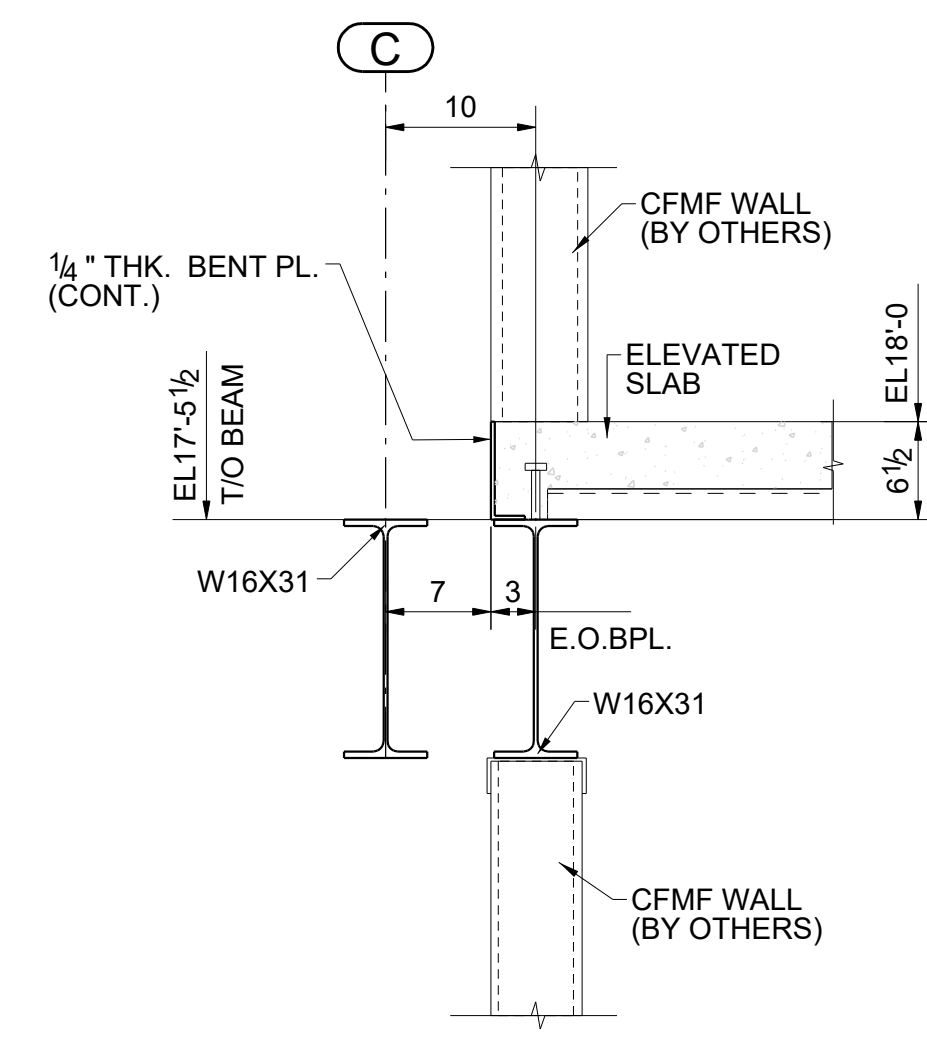


SECTION 13 - 13
E102
(REFER:SECTION 5/S5.006)

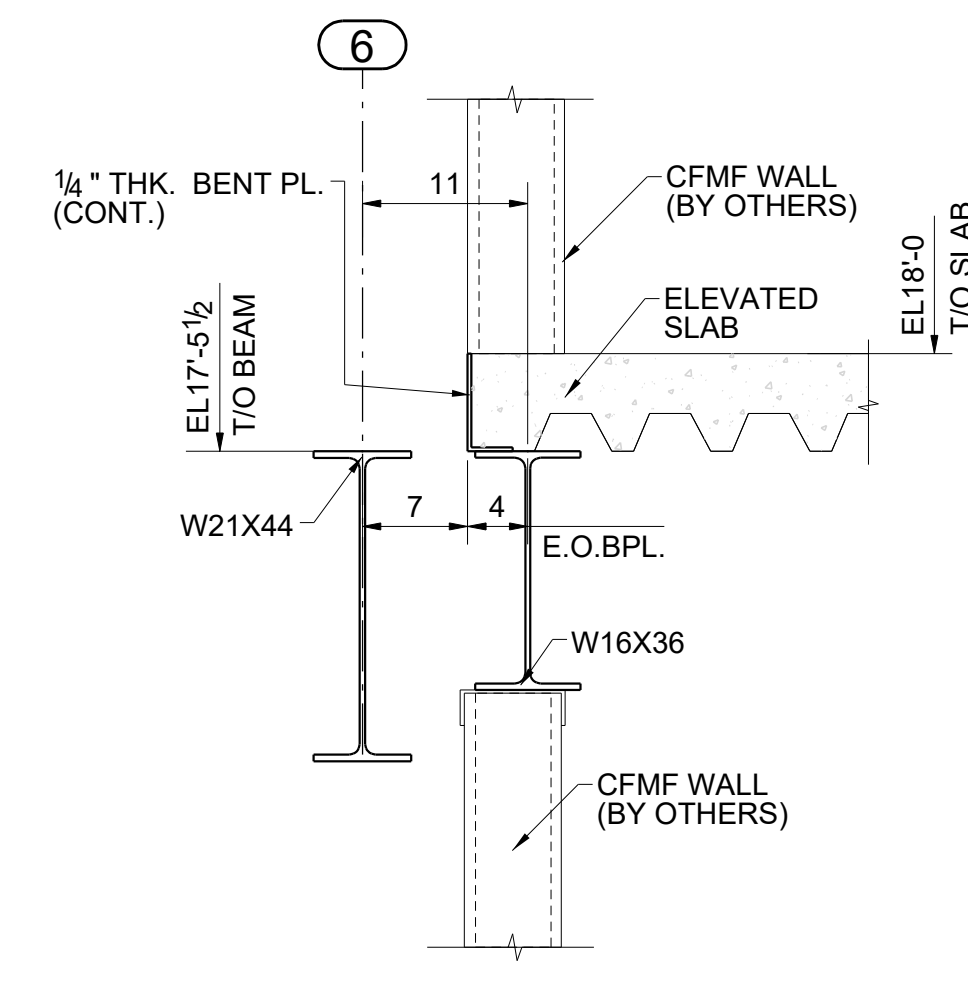


SECTION 14 - 14
E102
(REFER:SECTION 6/S5.006)

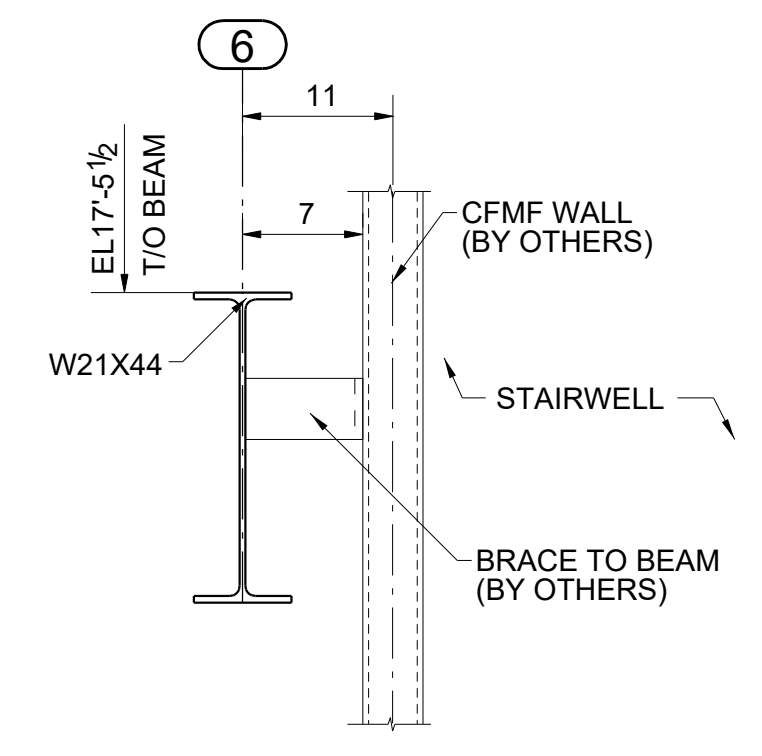

SECTION 15 - 15
E102
(REFER:SECTION 7/S5.007)

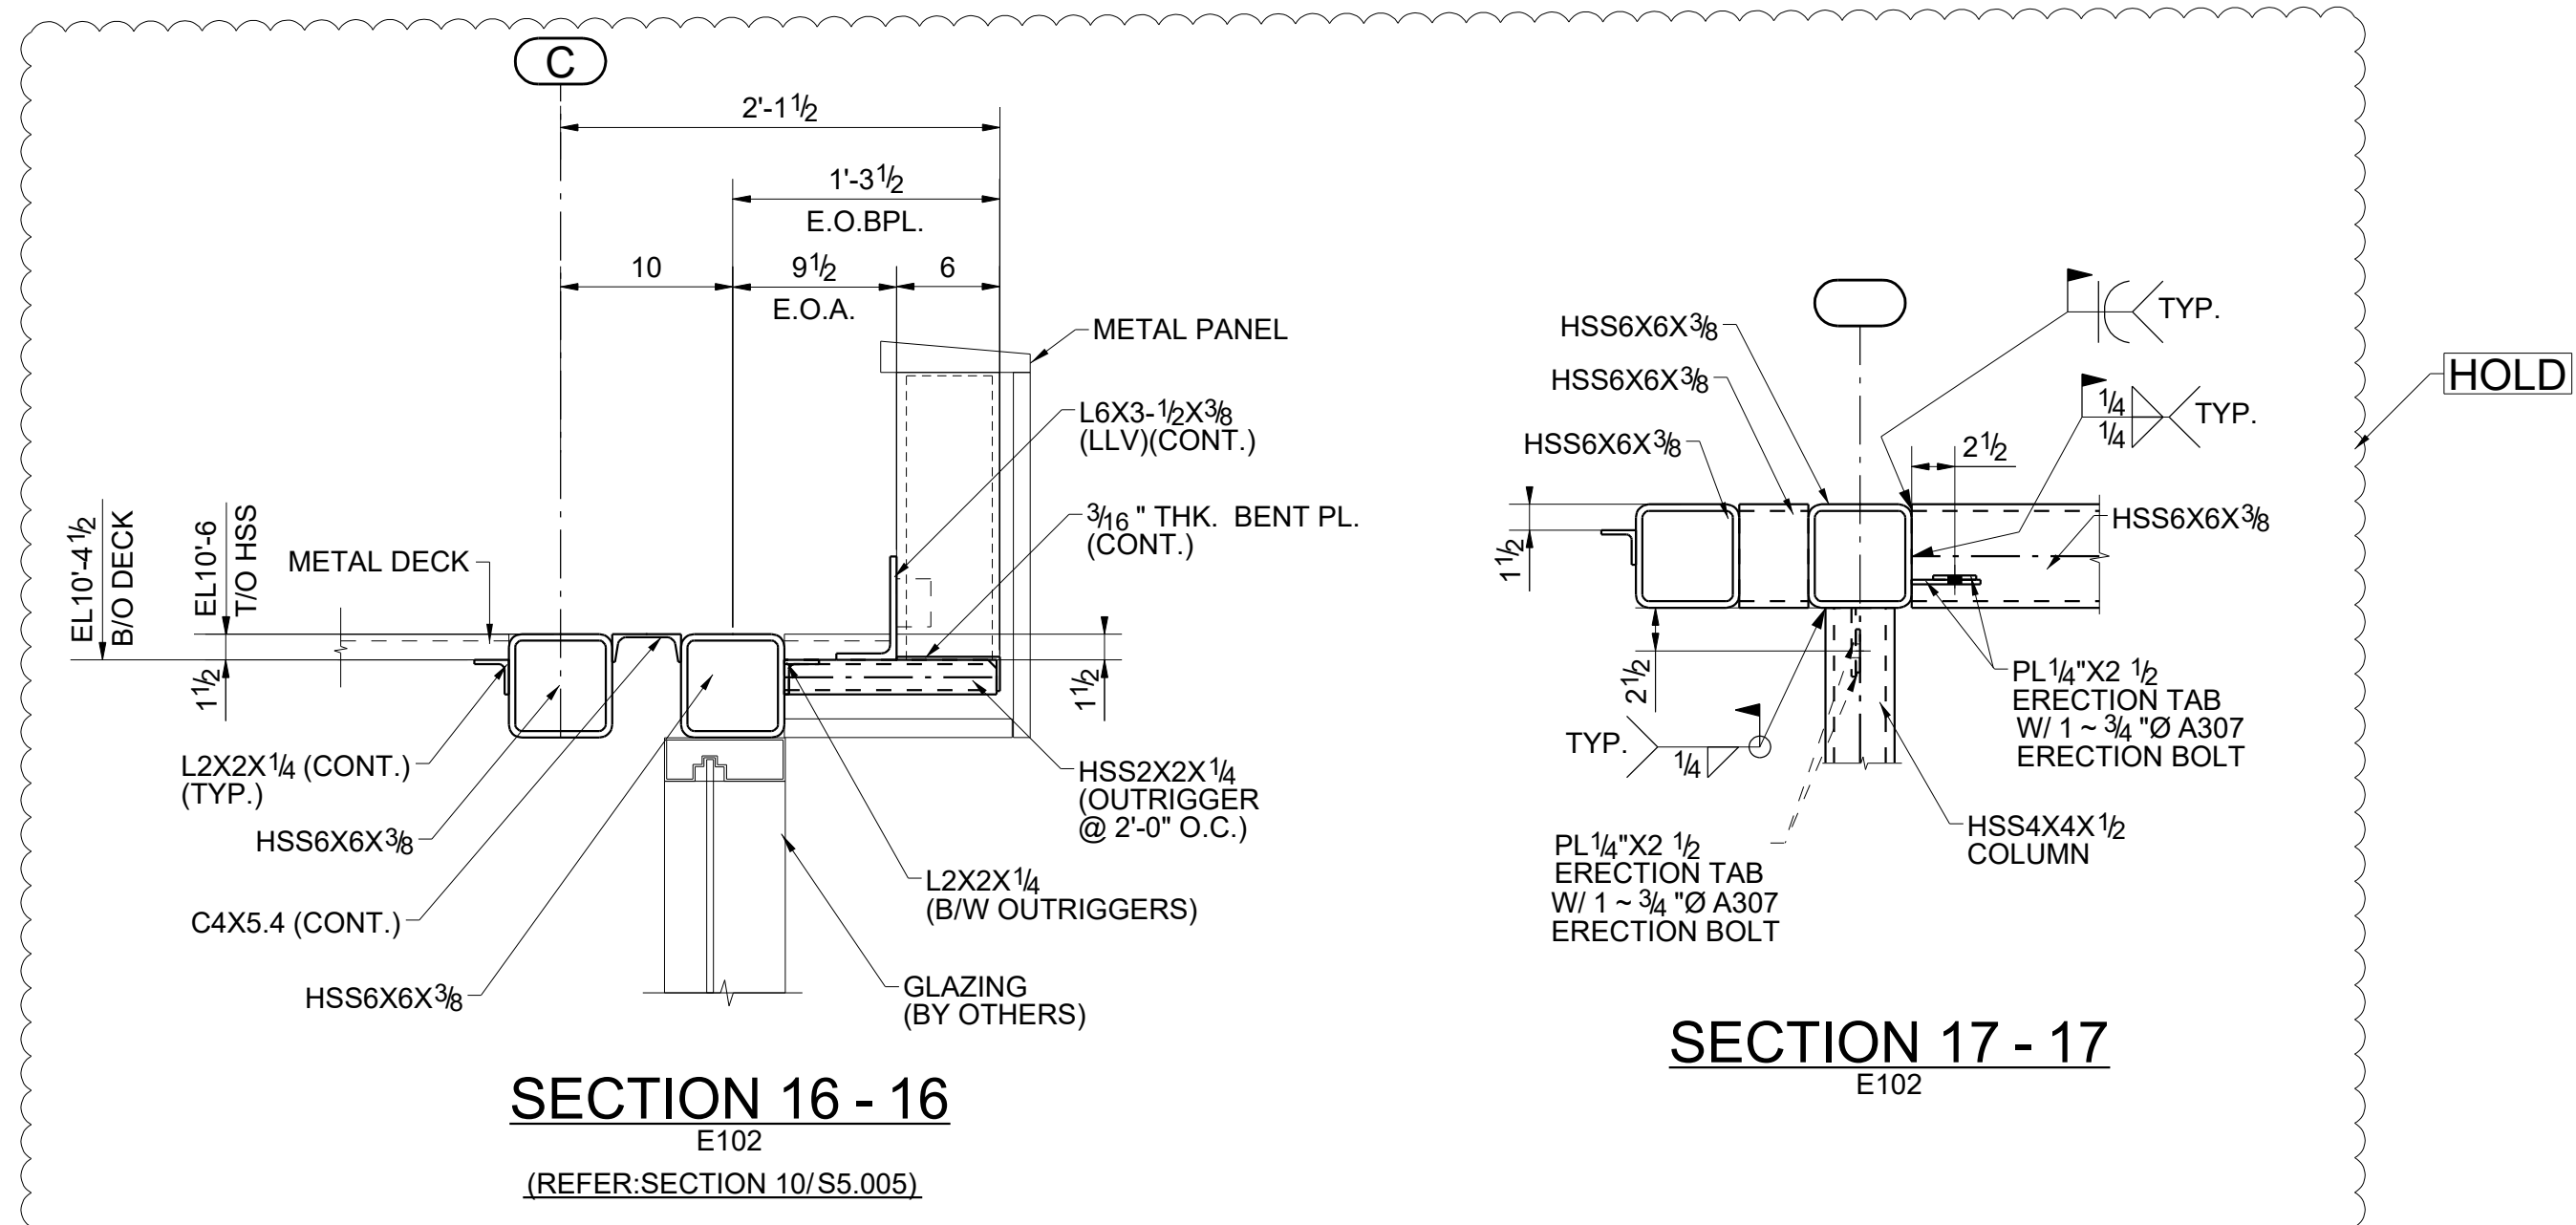


SECTION 16 - 16
E102
(REFER:SECTION 10/S5.005)

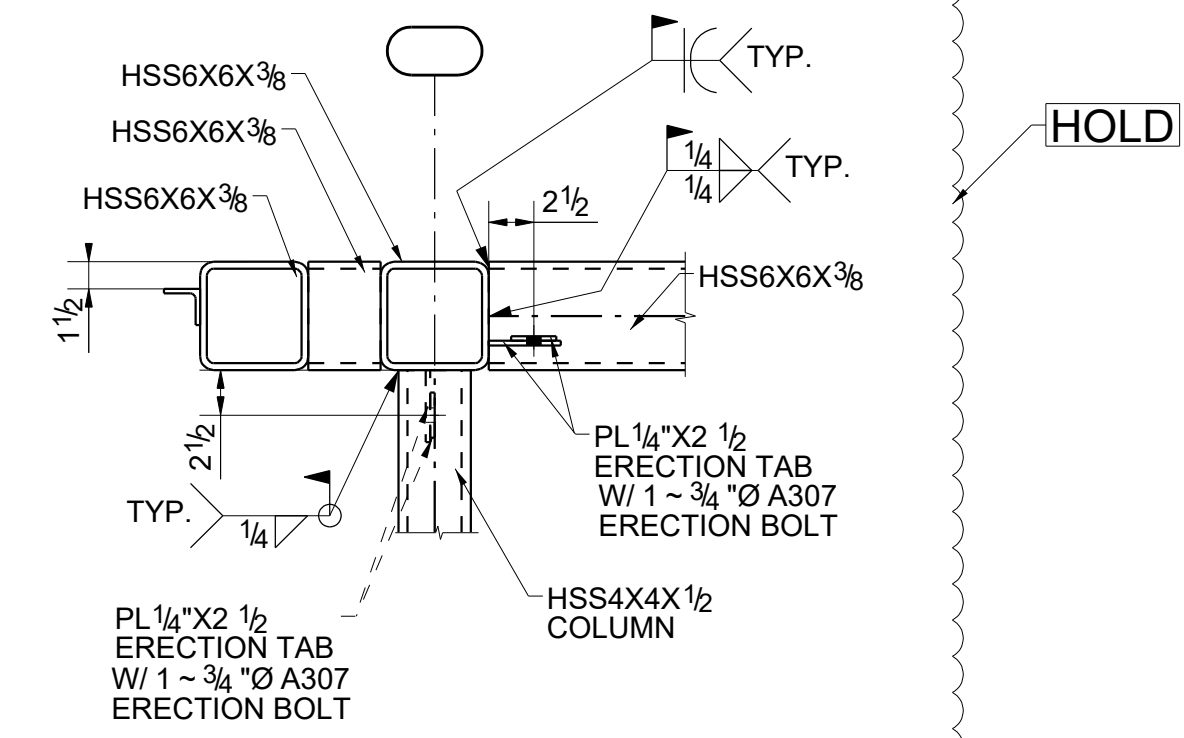


SECTION 17 - 17
E102

ERECTOR NOTE:
REMOVE ERECTION TABS AFTER THE BEAMS AND COLUMNS GOT FIELD WELDED TYPICAL, IF REQUIRED.

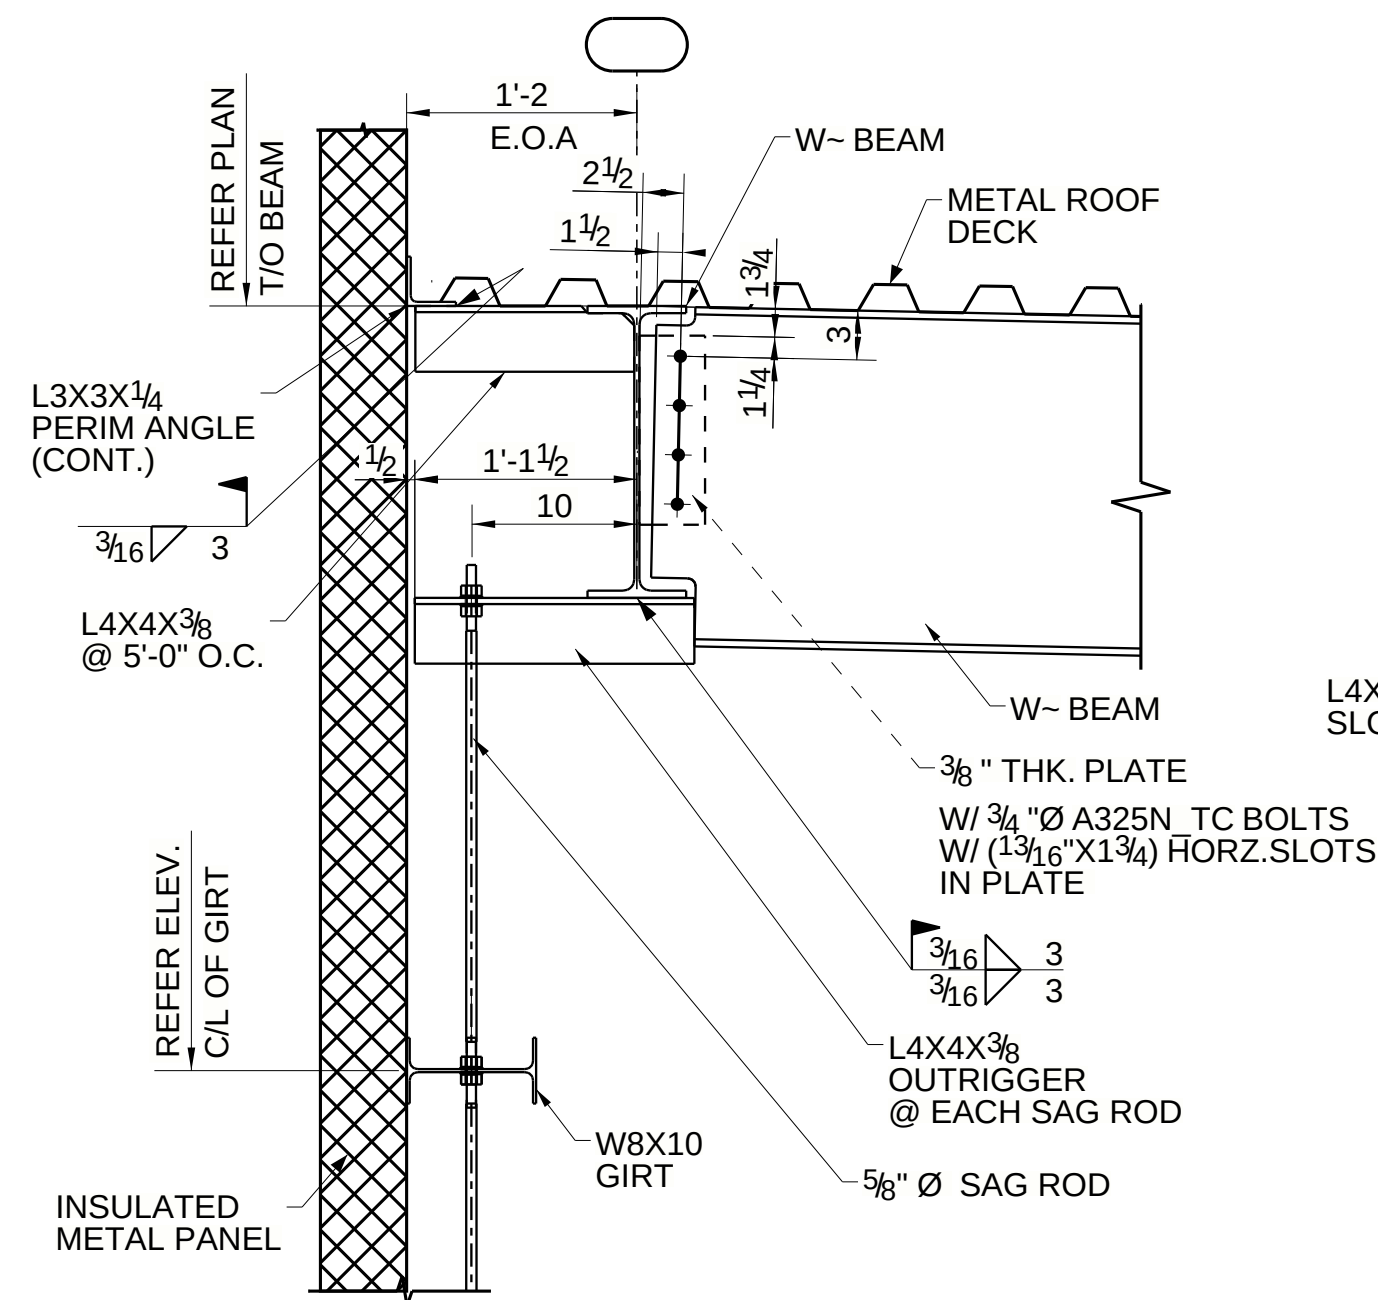


SECTION 27 - 27
E102

(REFER : A3 / 030.A2.94.S.05.22)

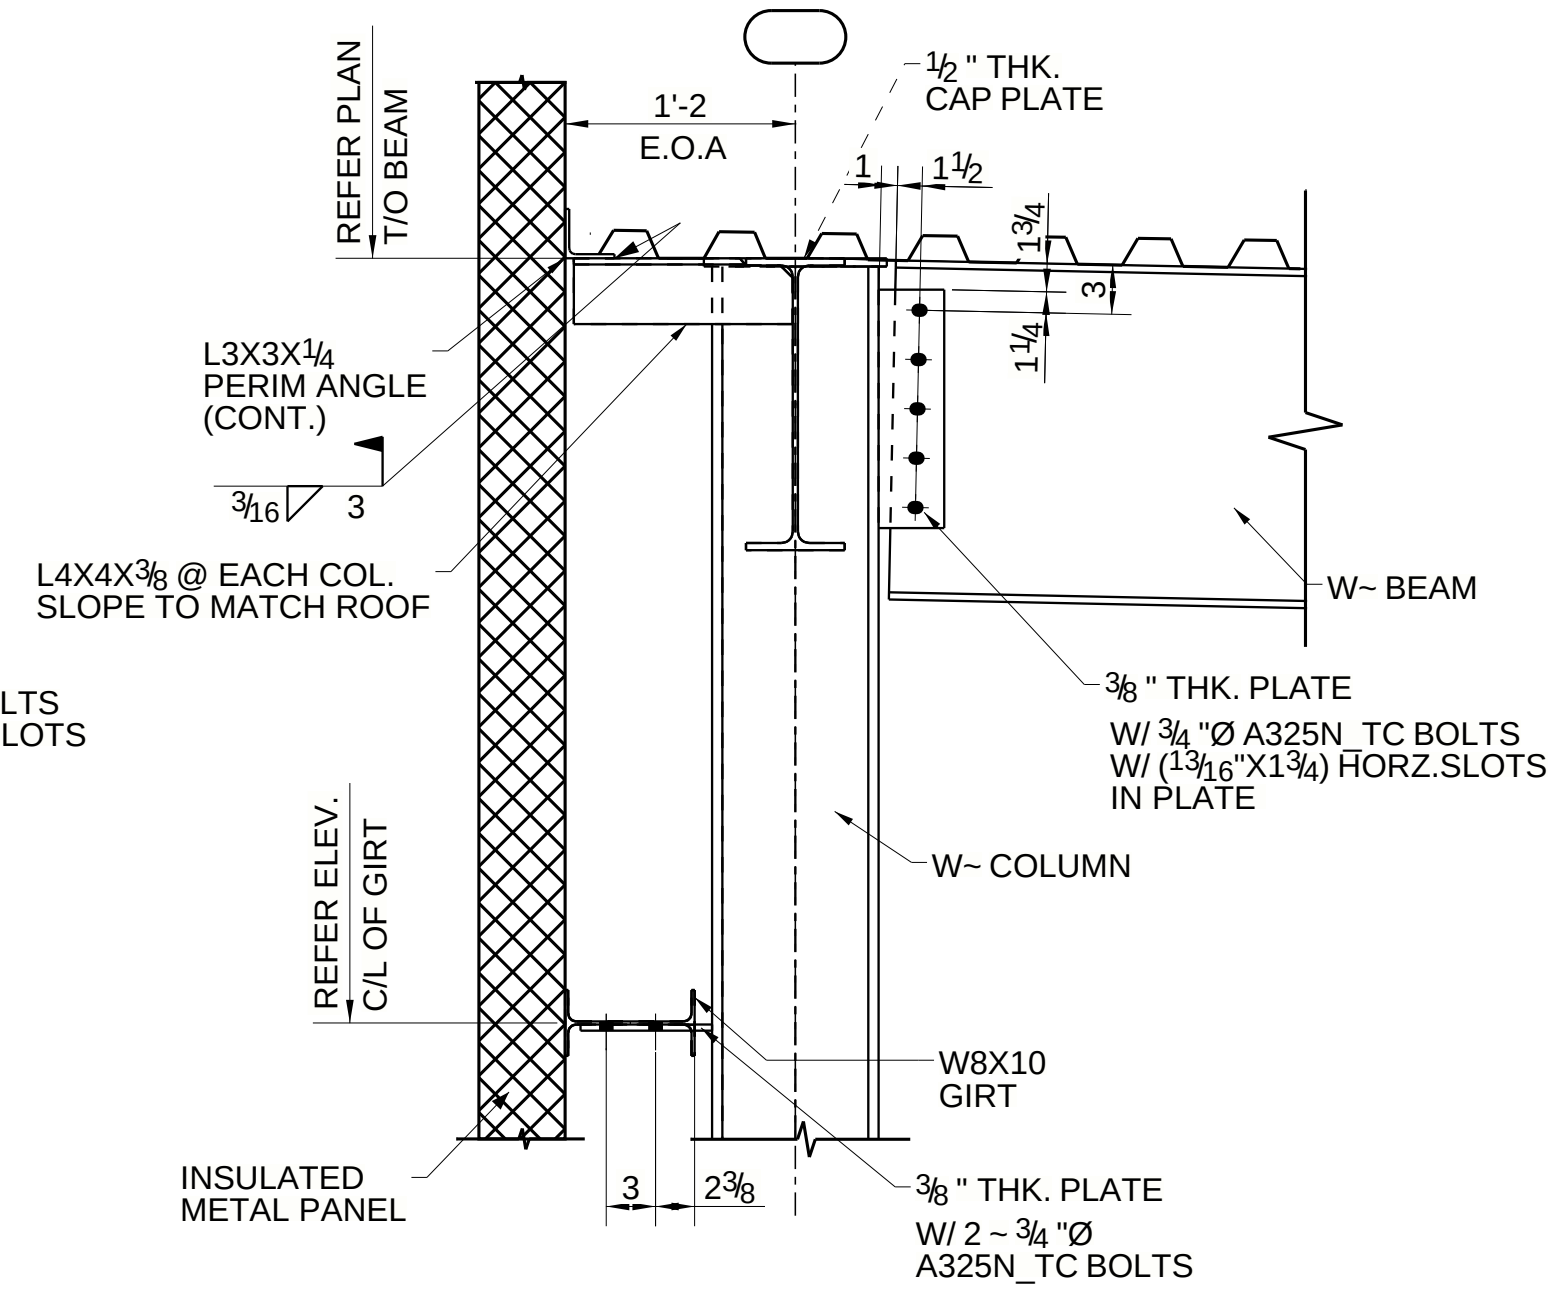


SECTION 28 - 28
E102

(REFER : A4 / 030.A2.94.S.05.22)

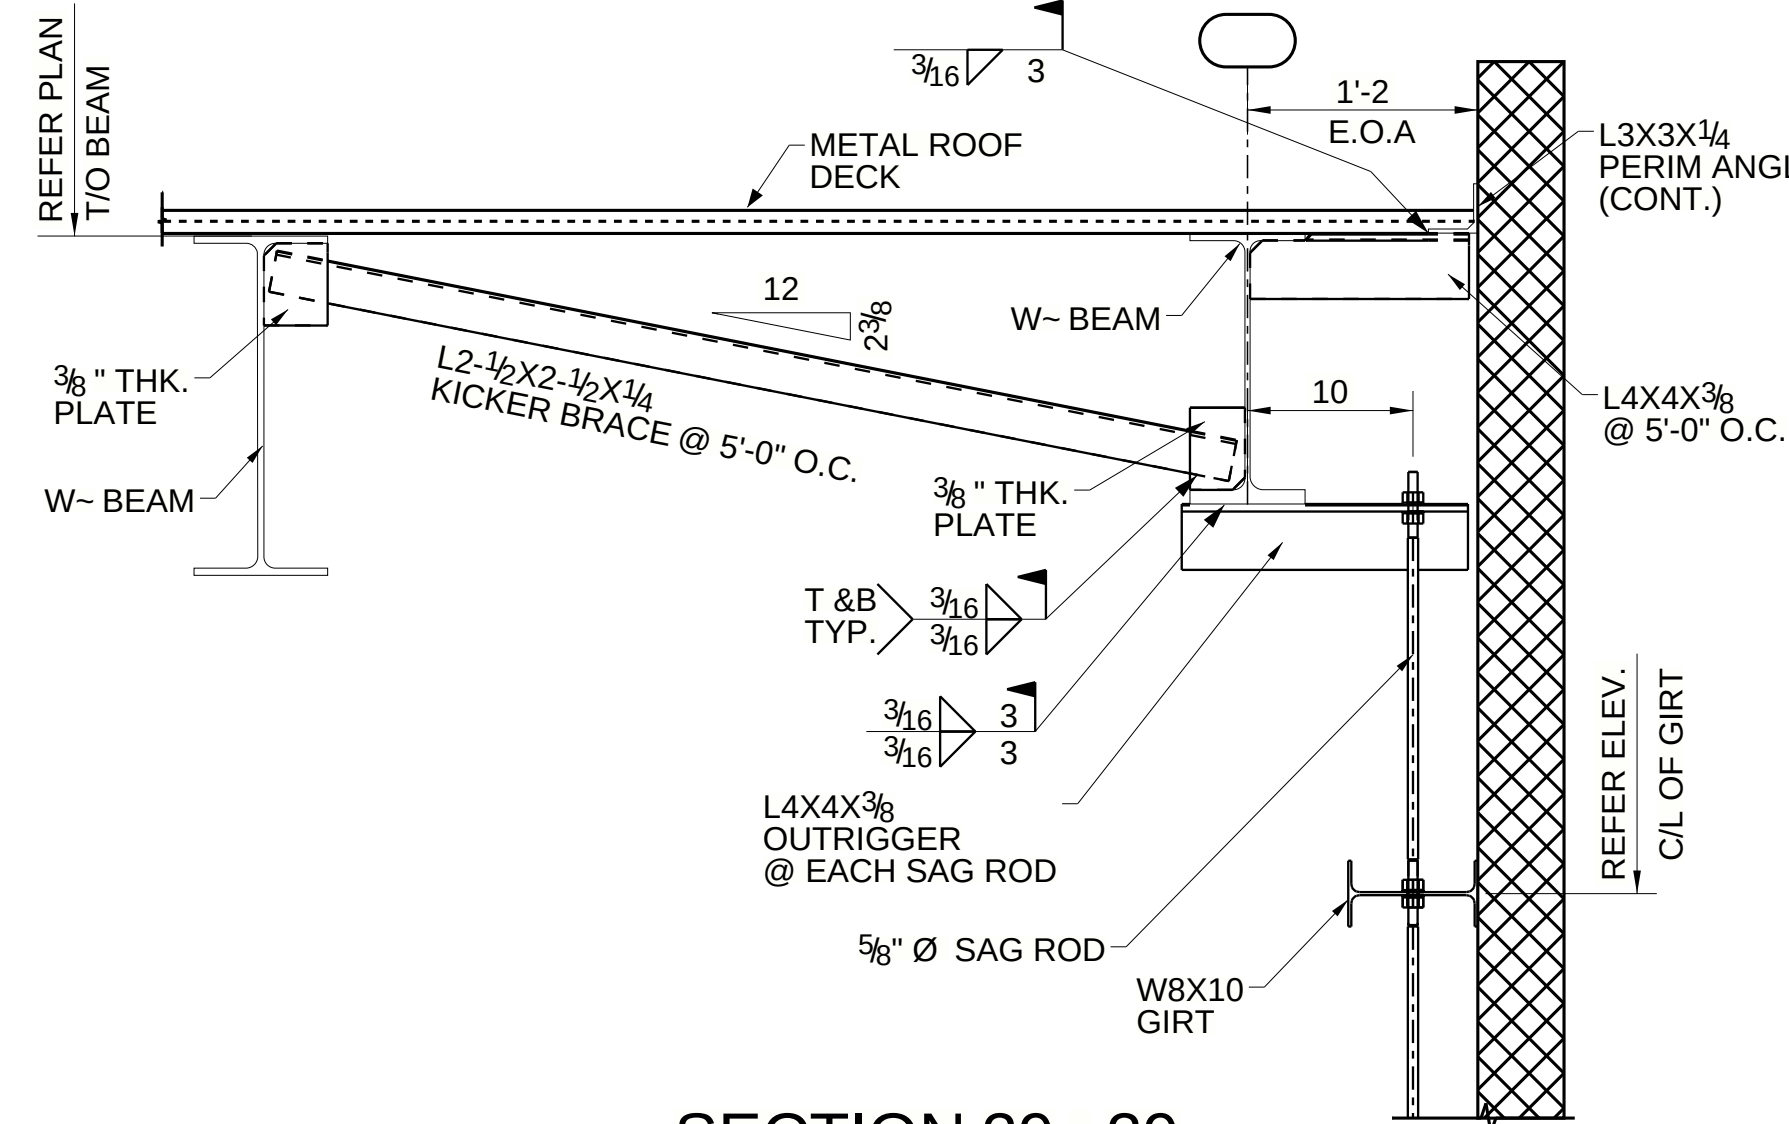


SECTION 29 - 29
E102

(REFER : A1 / 030.A2.94.S.05.22)

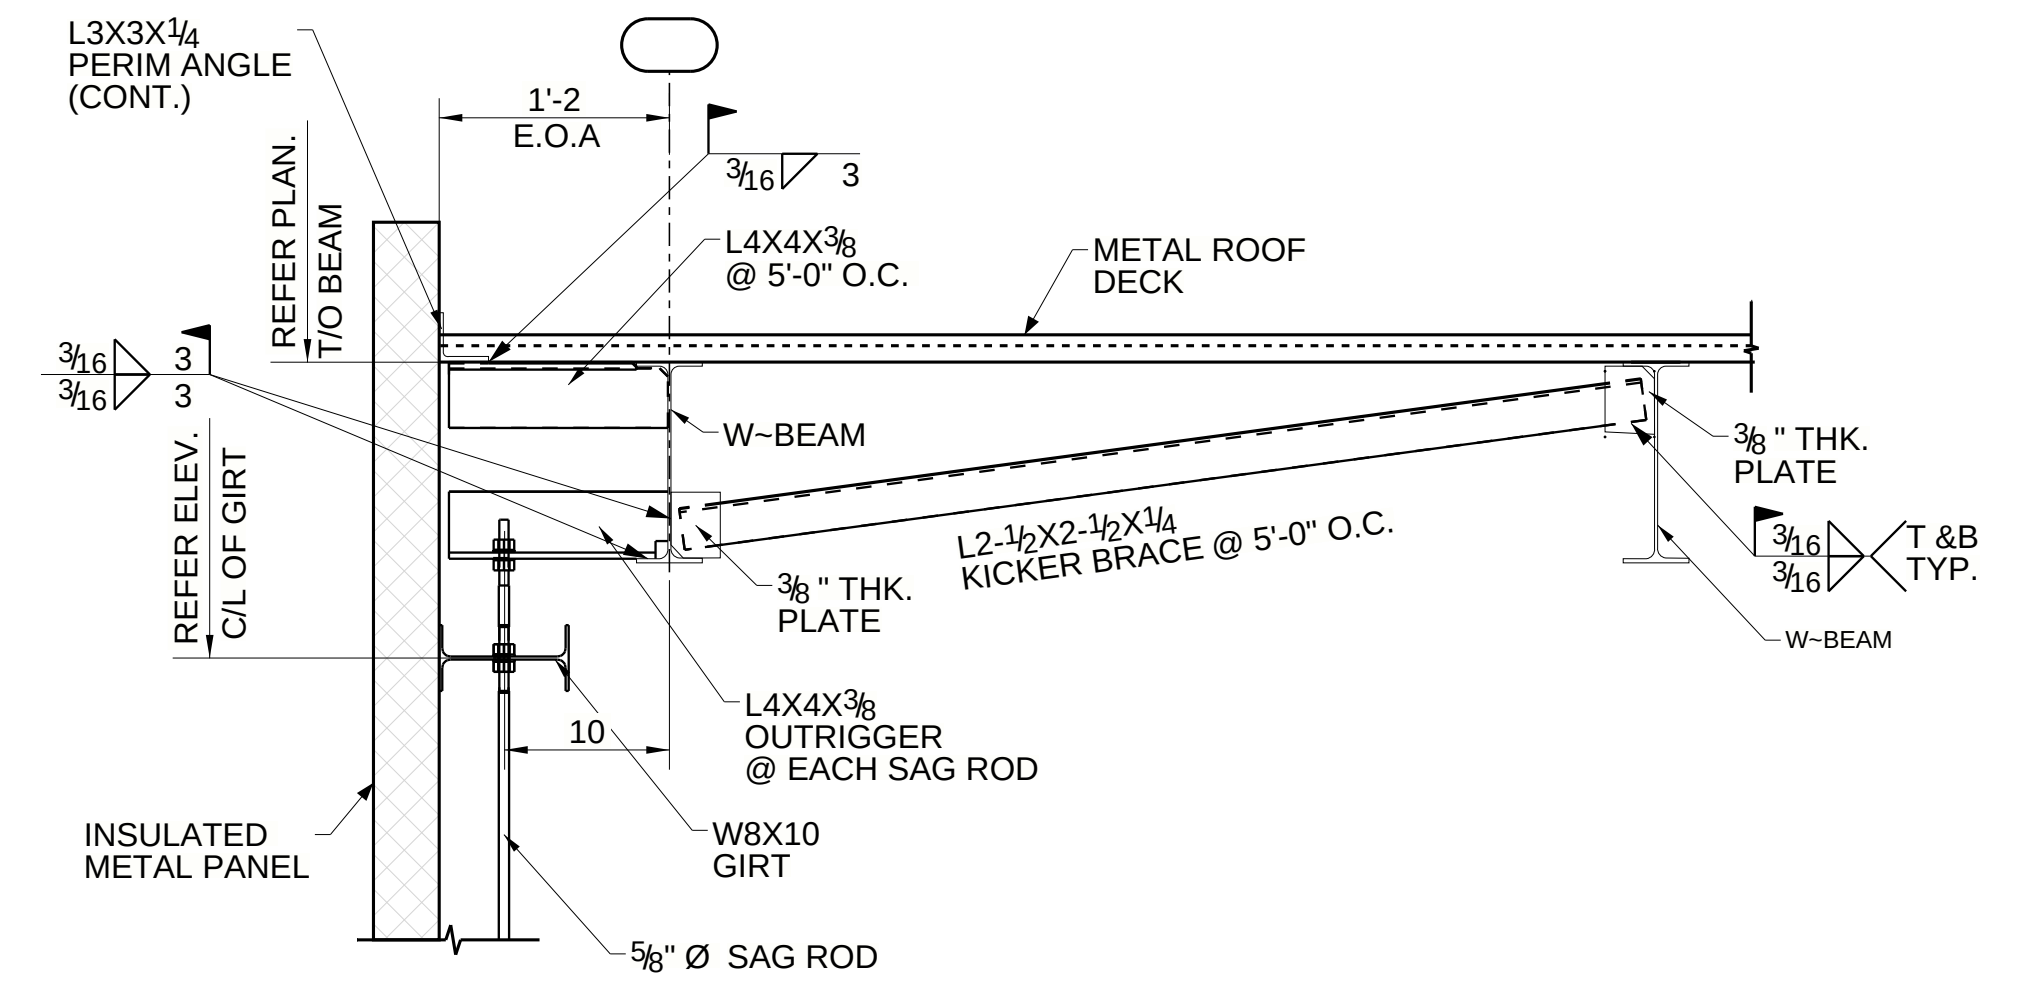


SECTION 30 - 30
E103

(REFER : A2 / 030.A2.94.S.05.22)

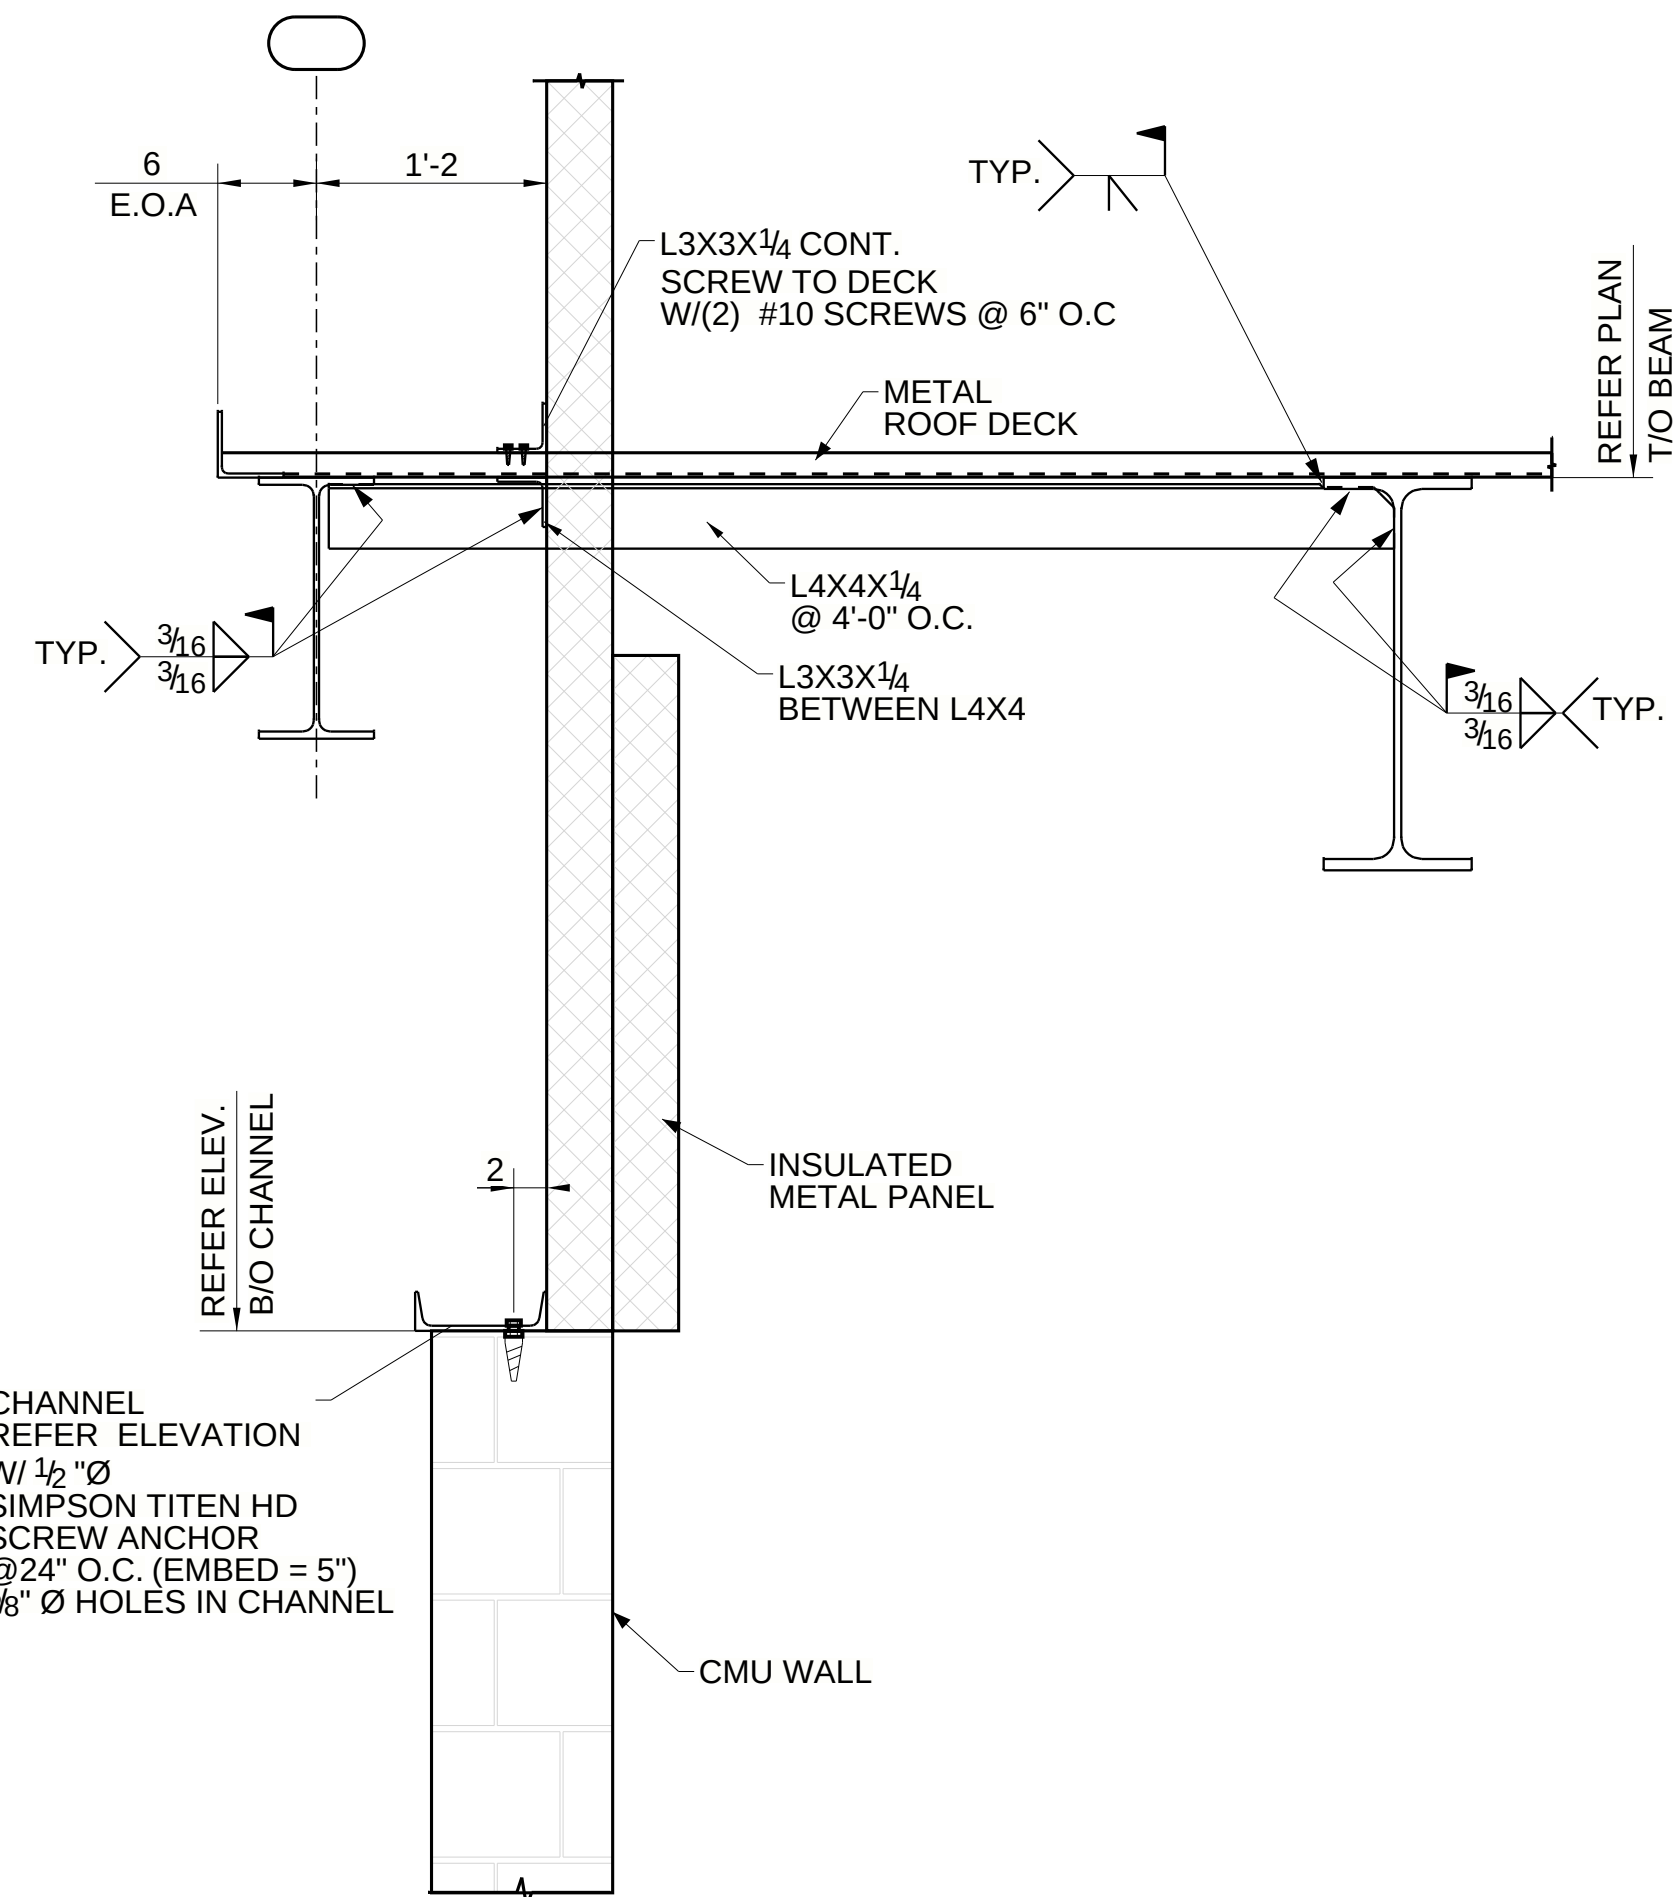


SECTION 31 - 31
E104

(REFER : SECTION A1/030.A2.94.S.05.22)

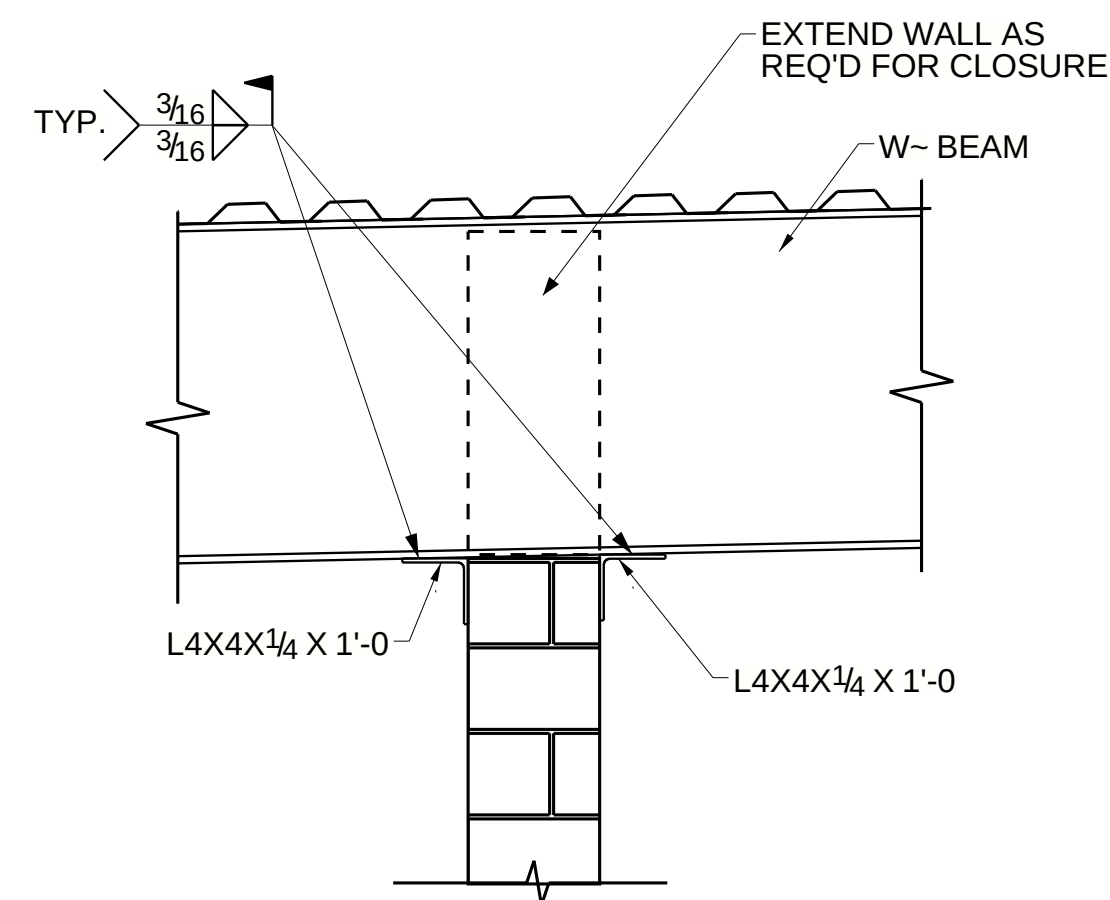


SECTION 32 - 32
E104

(REFER : SECTION A2/030.A2.94.S.00.04A)

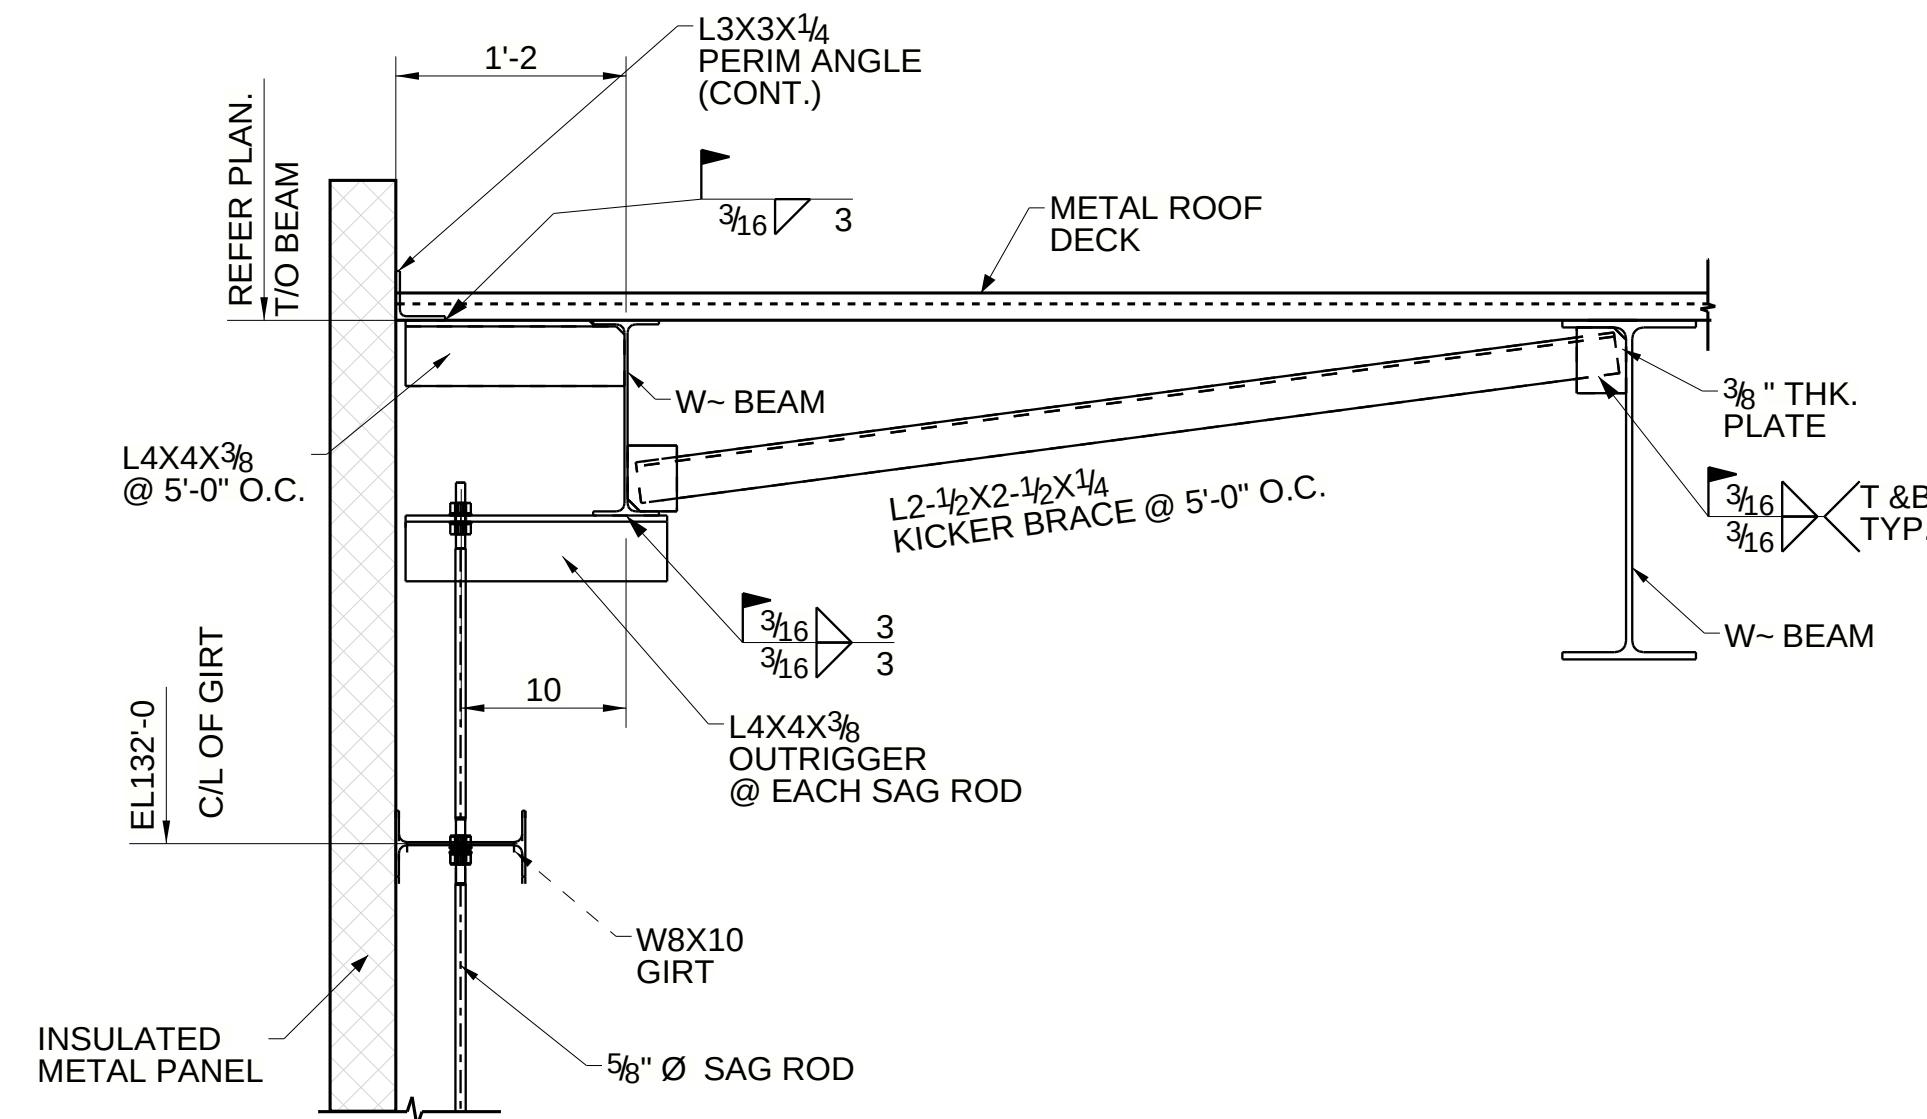


SECTION 30A-30A
E102

(REFER : A2 / 030.A2.94.S.05.22)

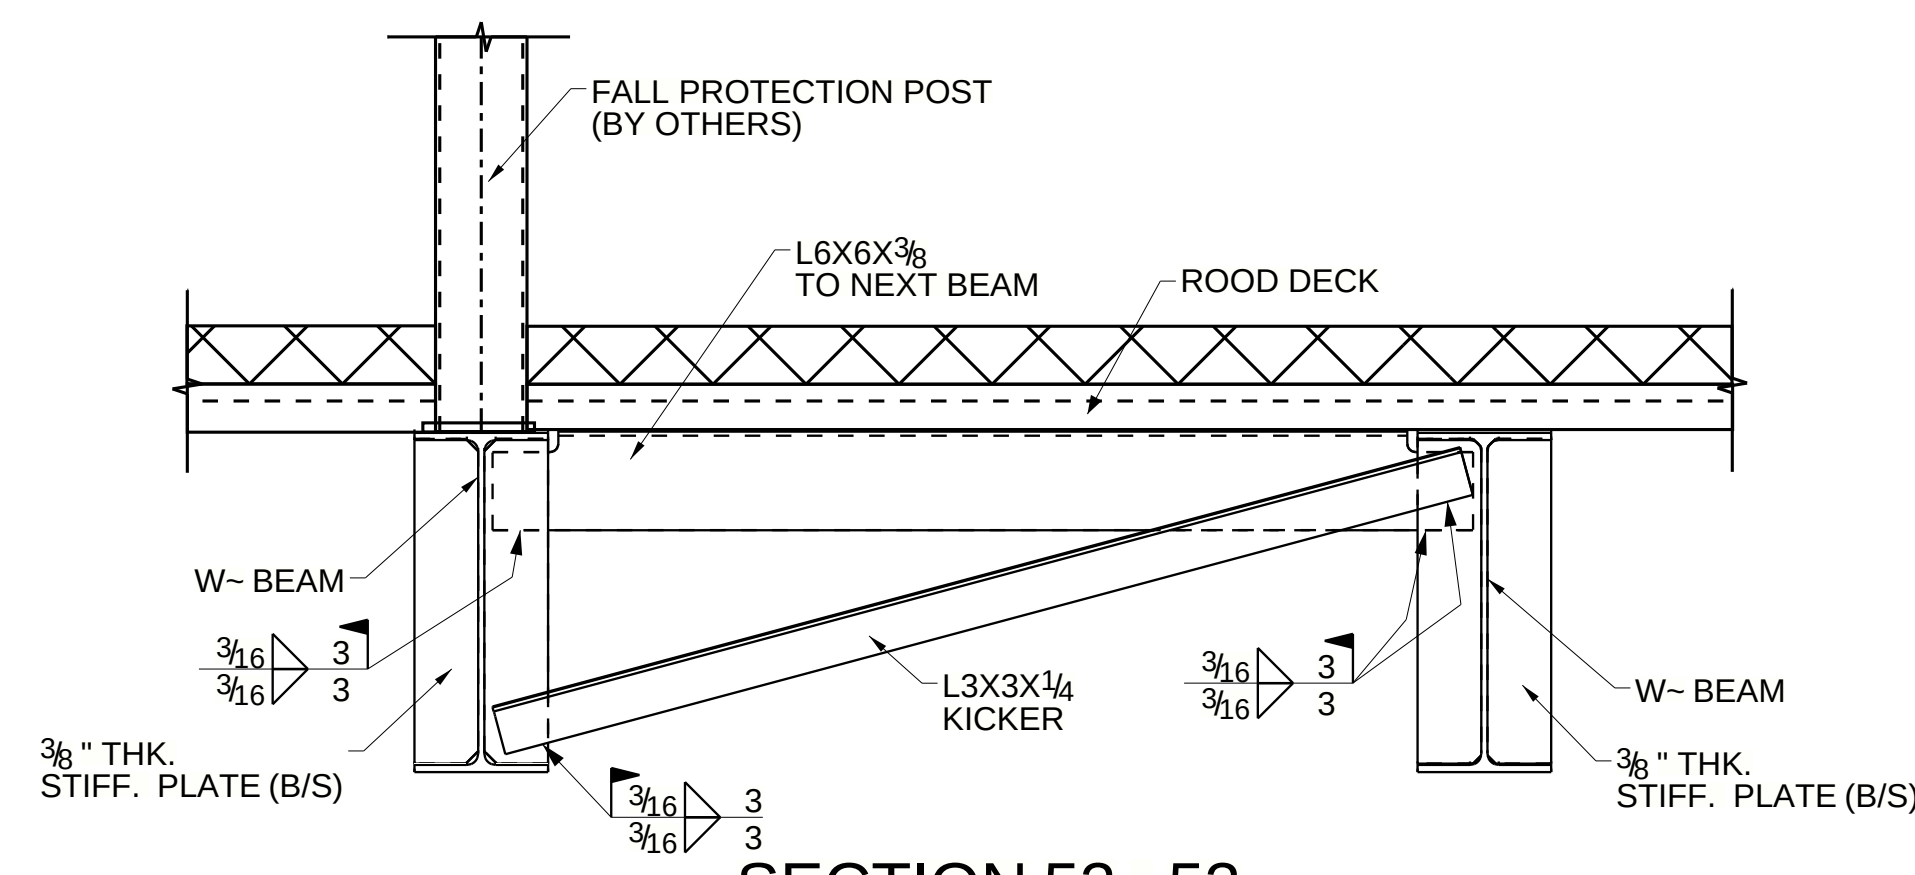


SECTION 53 - 53
E102


(REFER : A2 / 030.A2.94.S.05.21)

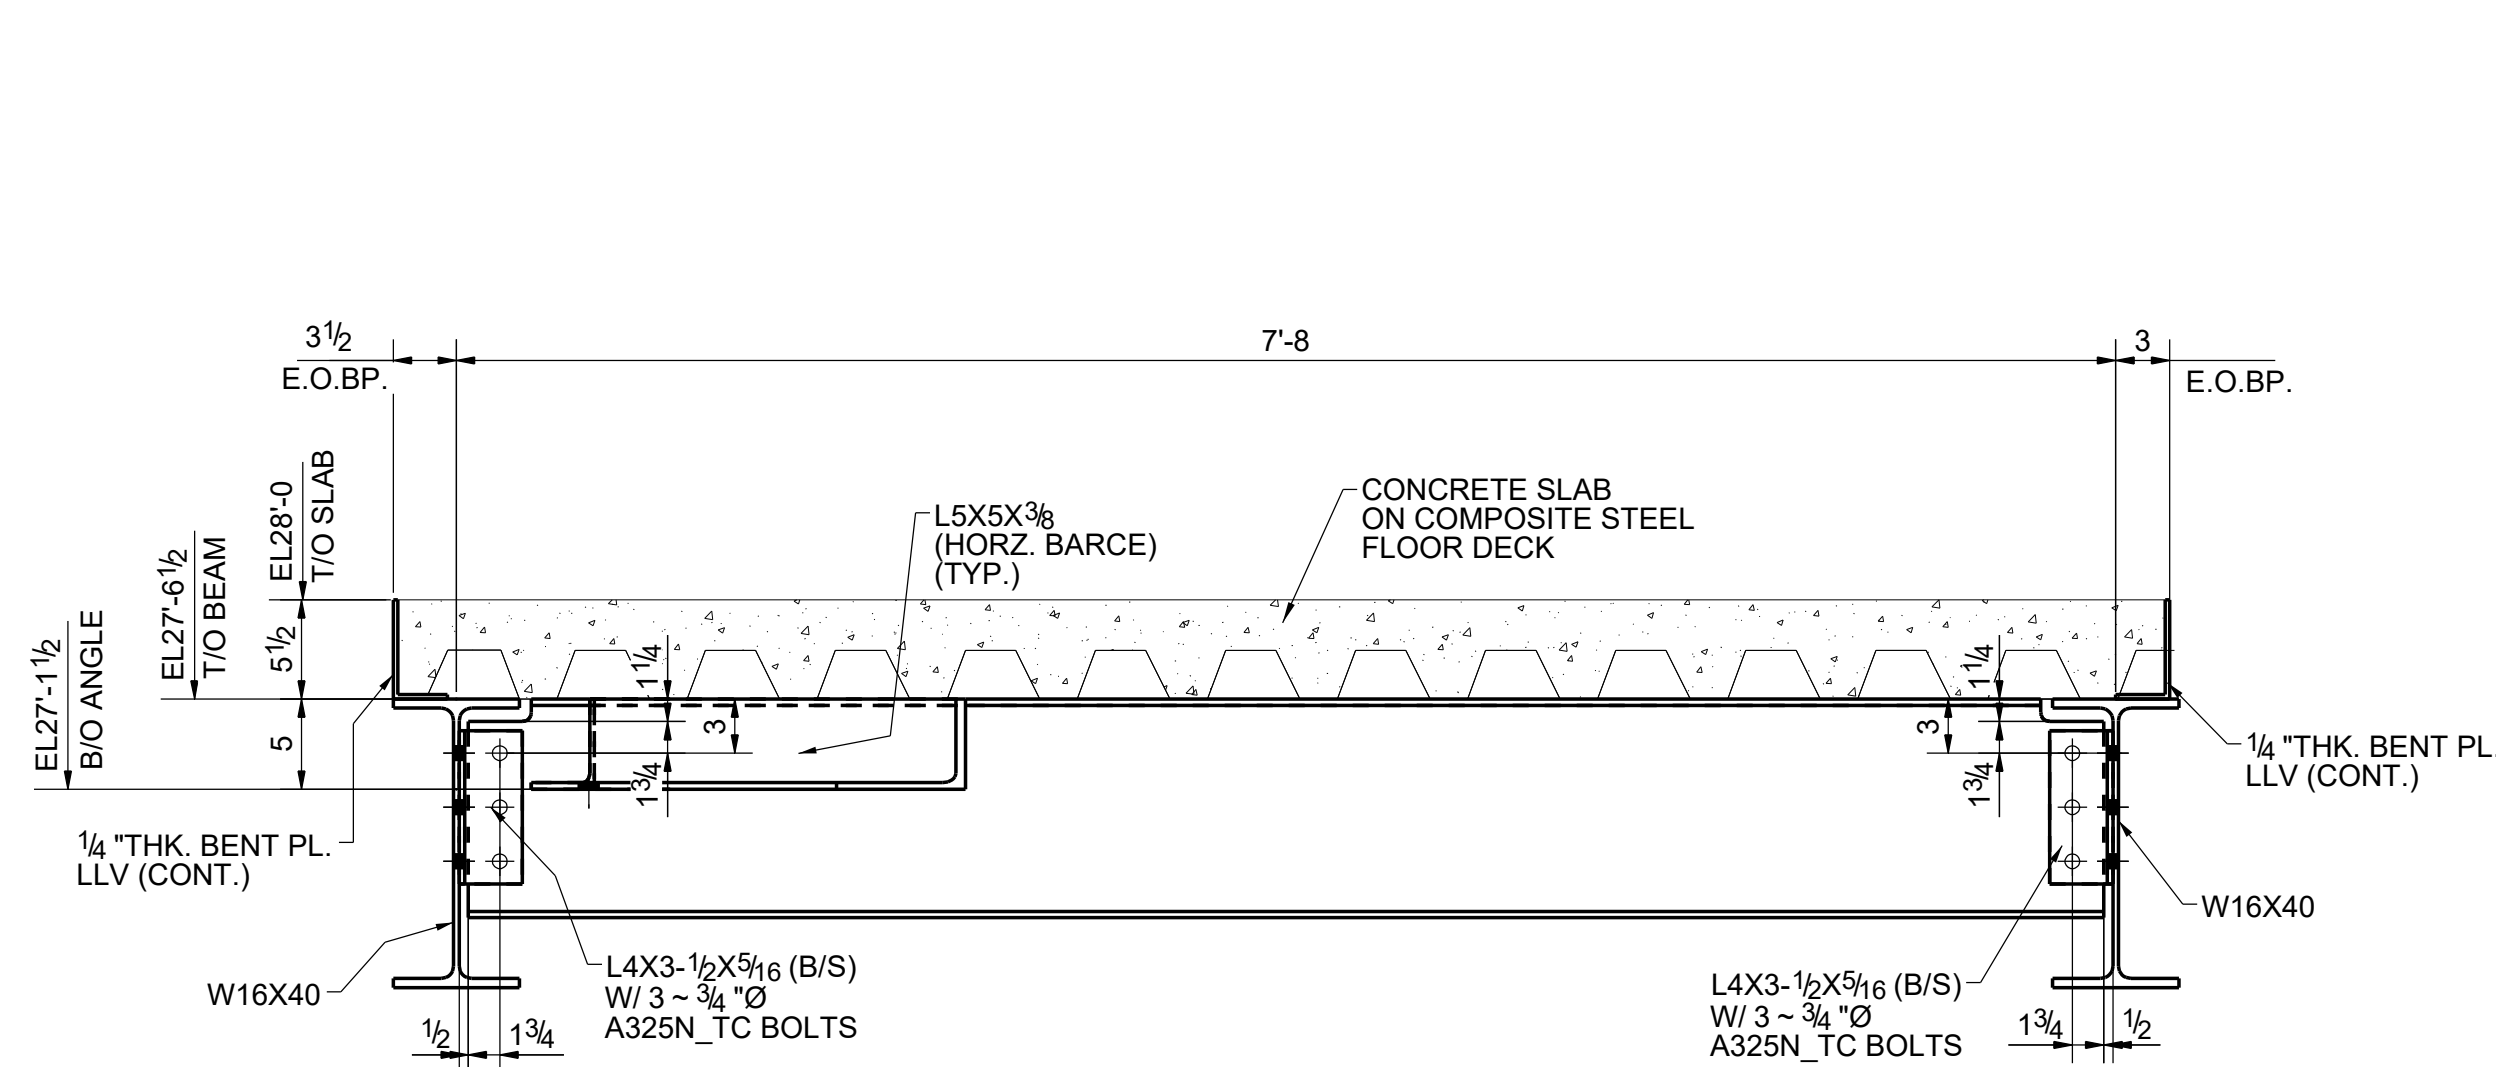


SECTION 84 - 84
E110
(REFER : SECTION 3/S-607)

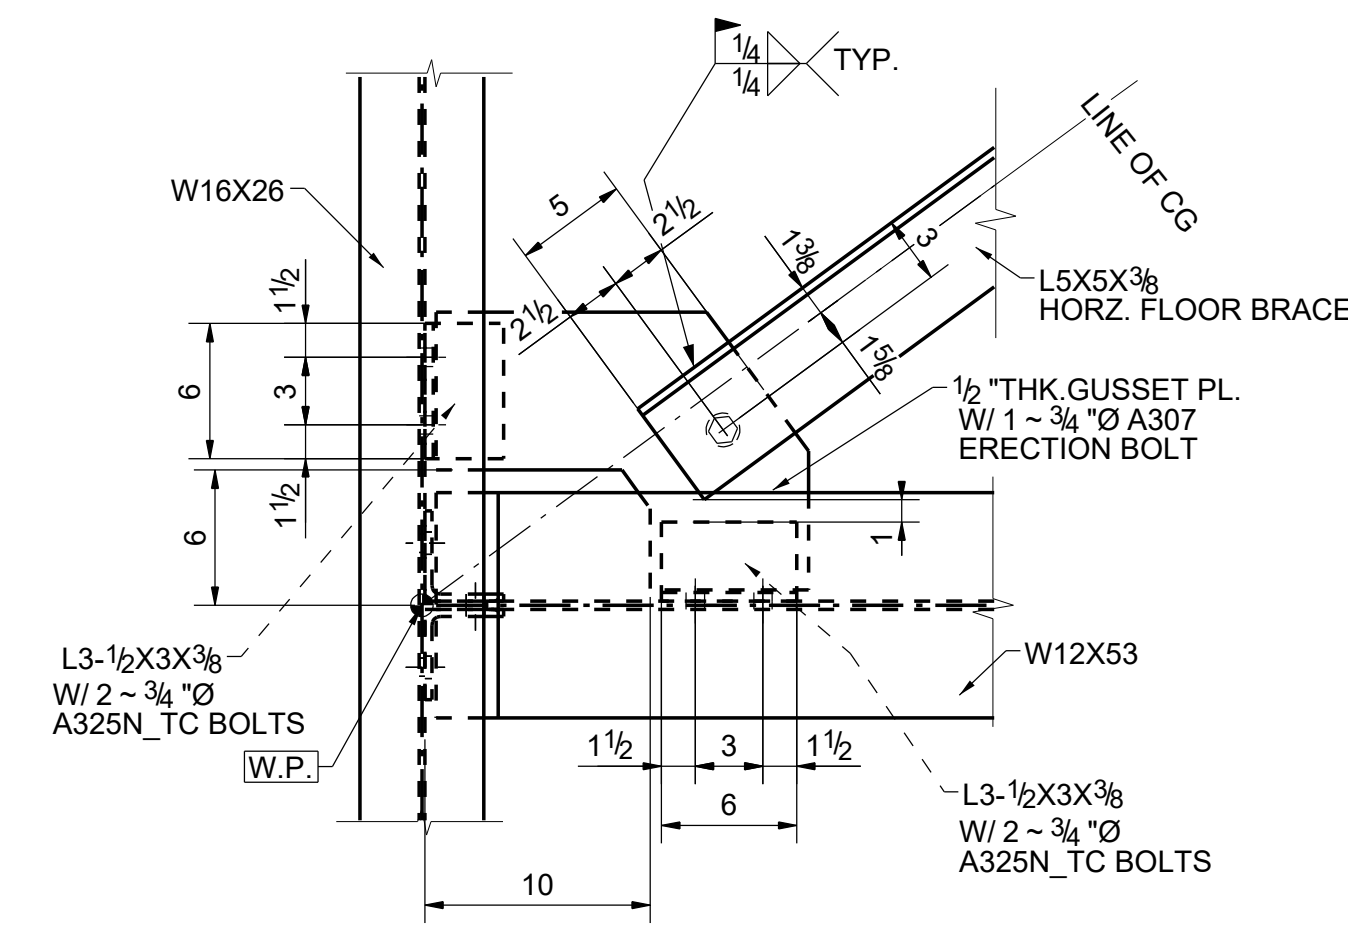


DETAIL 85
E104

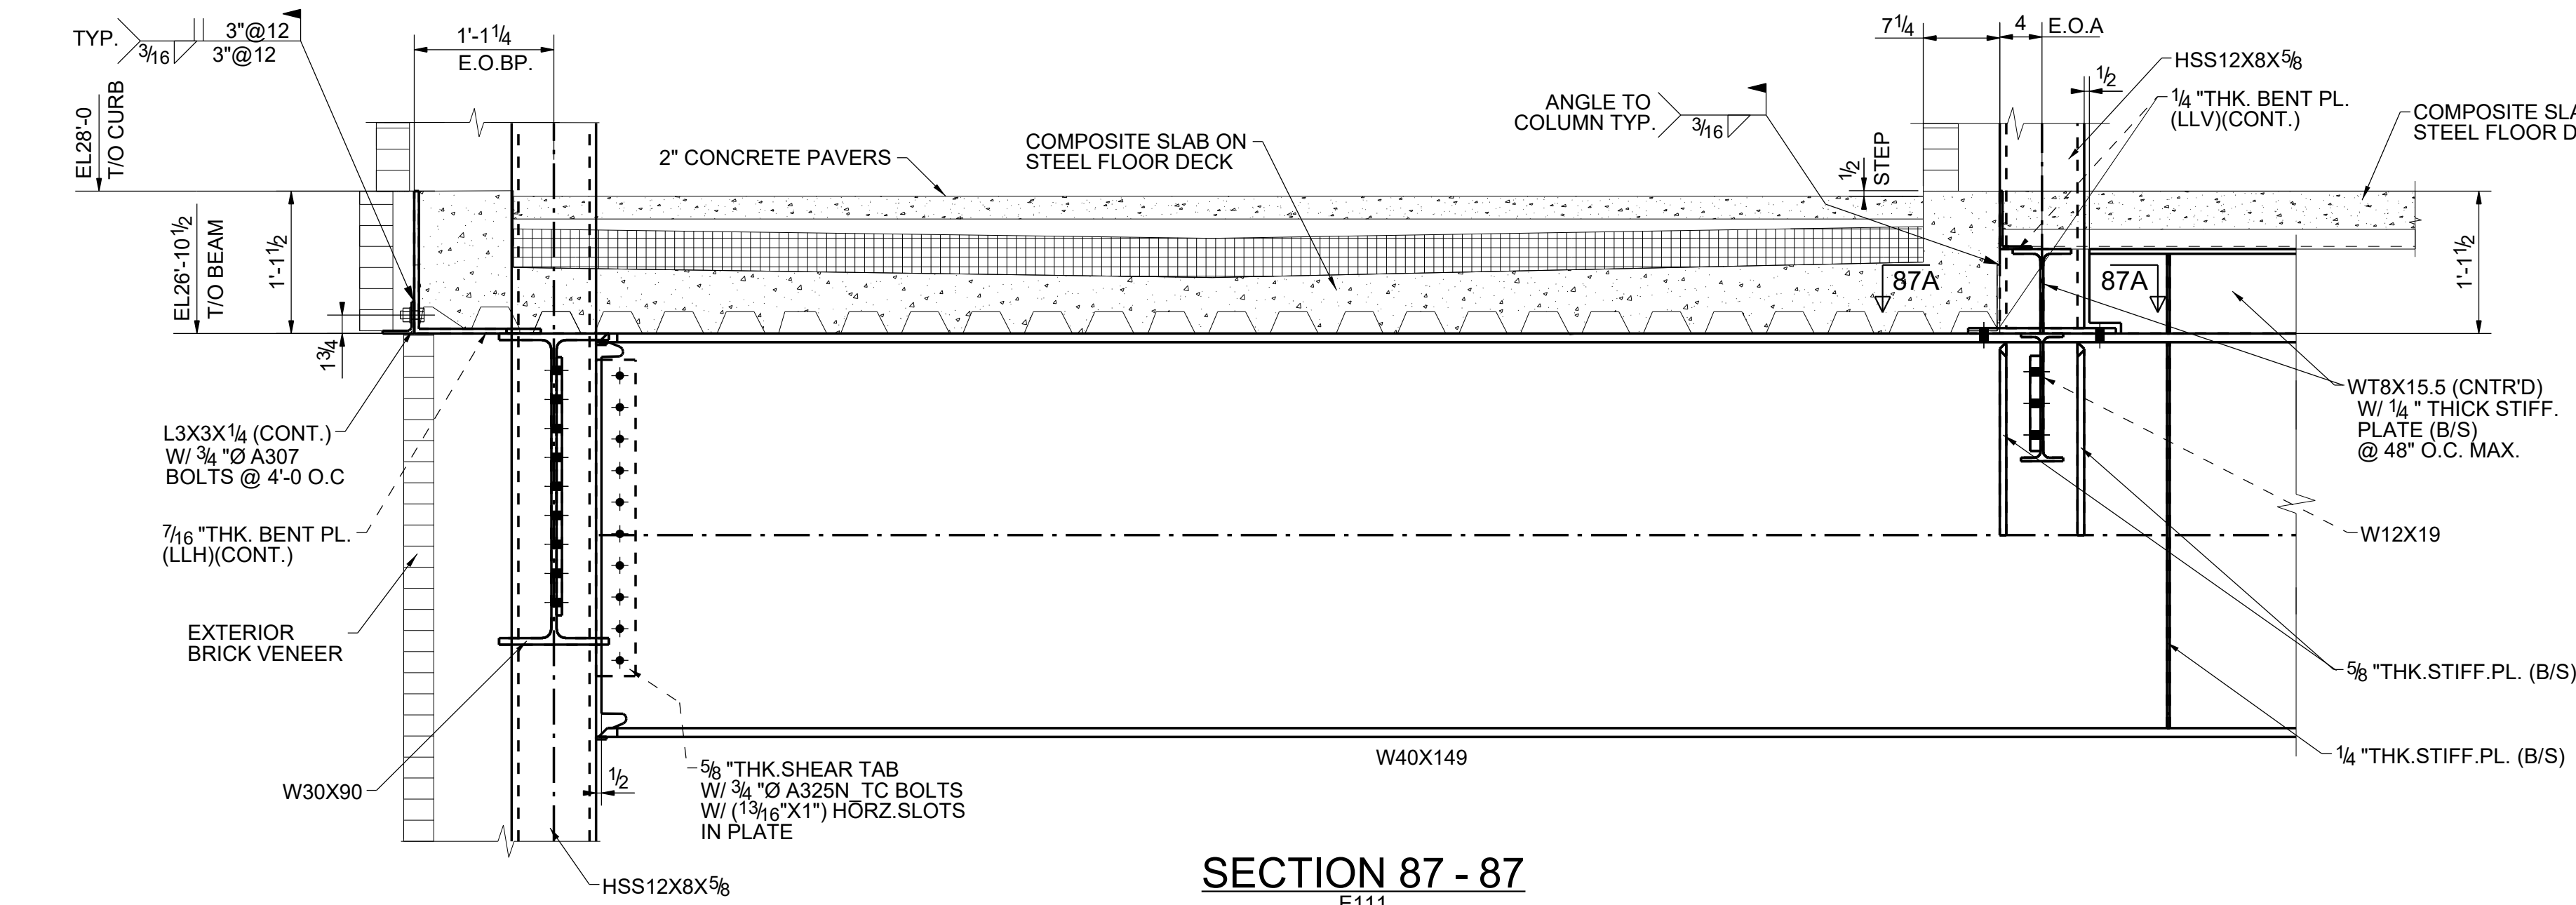


SECTION 87 - 87
E111
(REFER : SECTION 5/S-607)

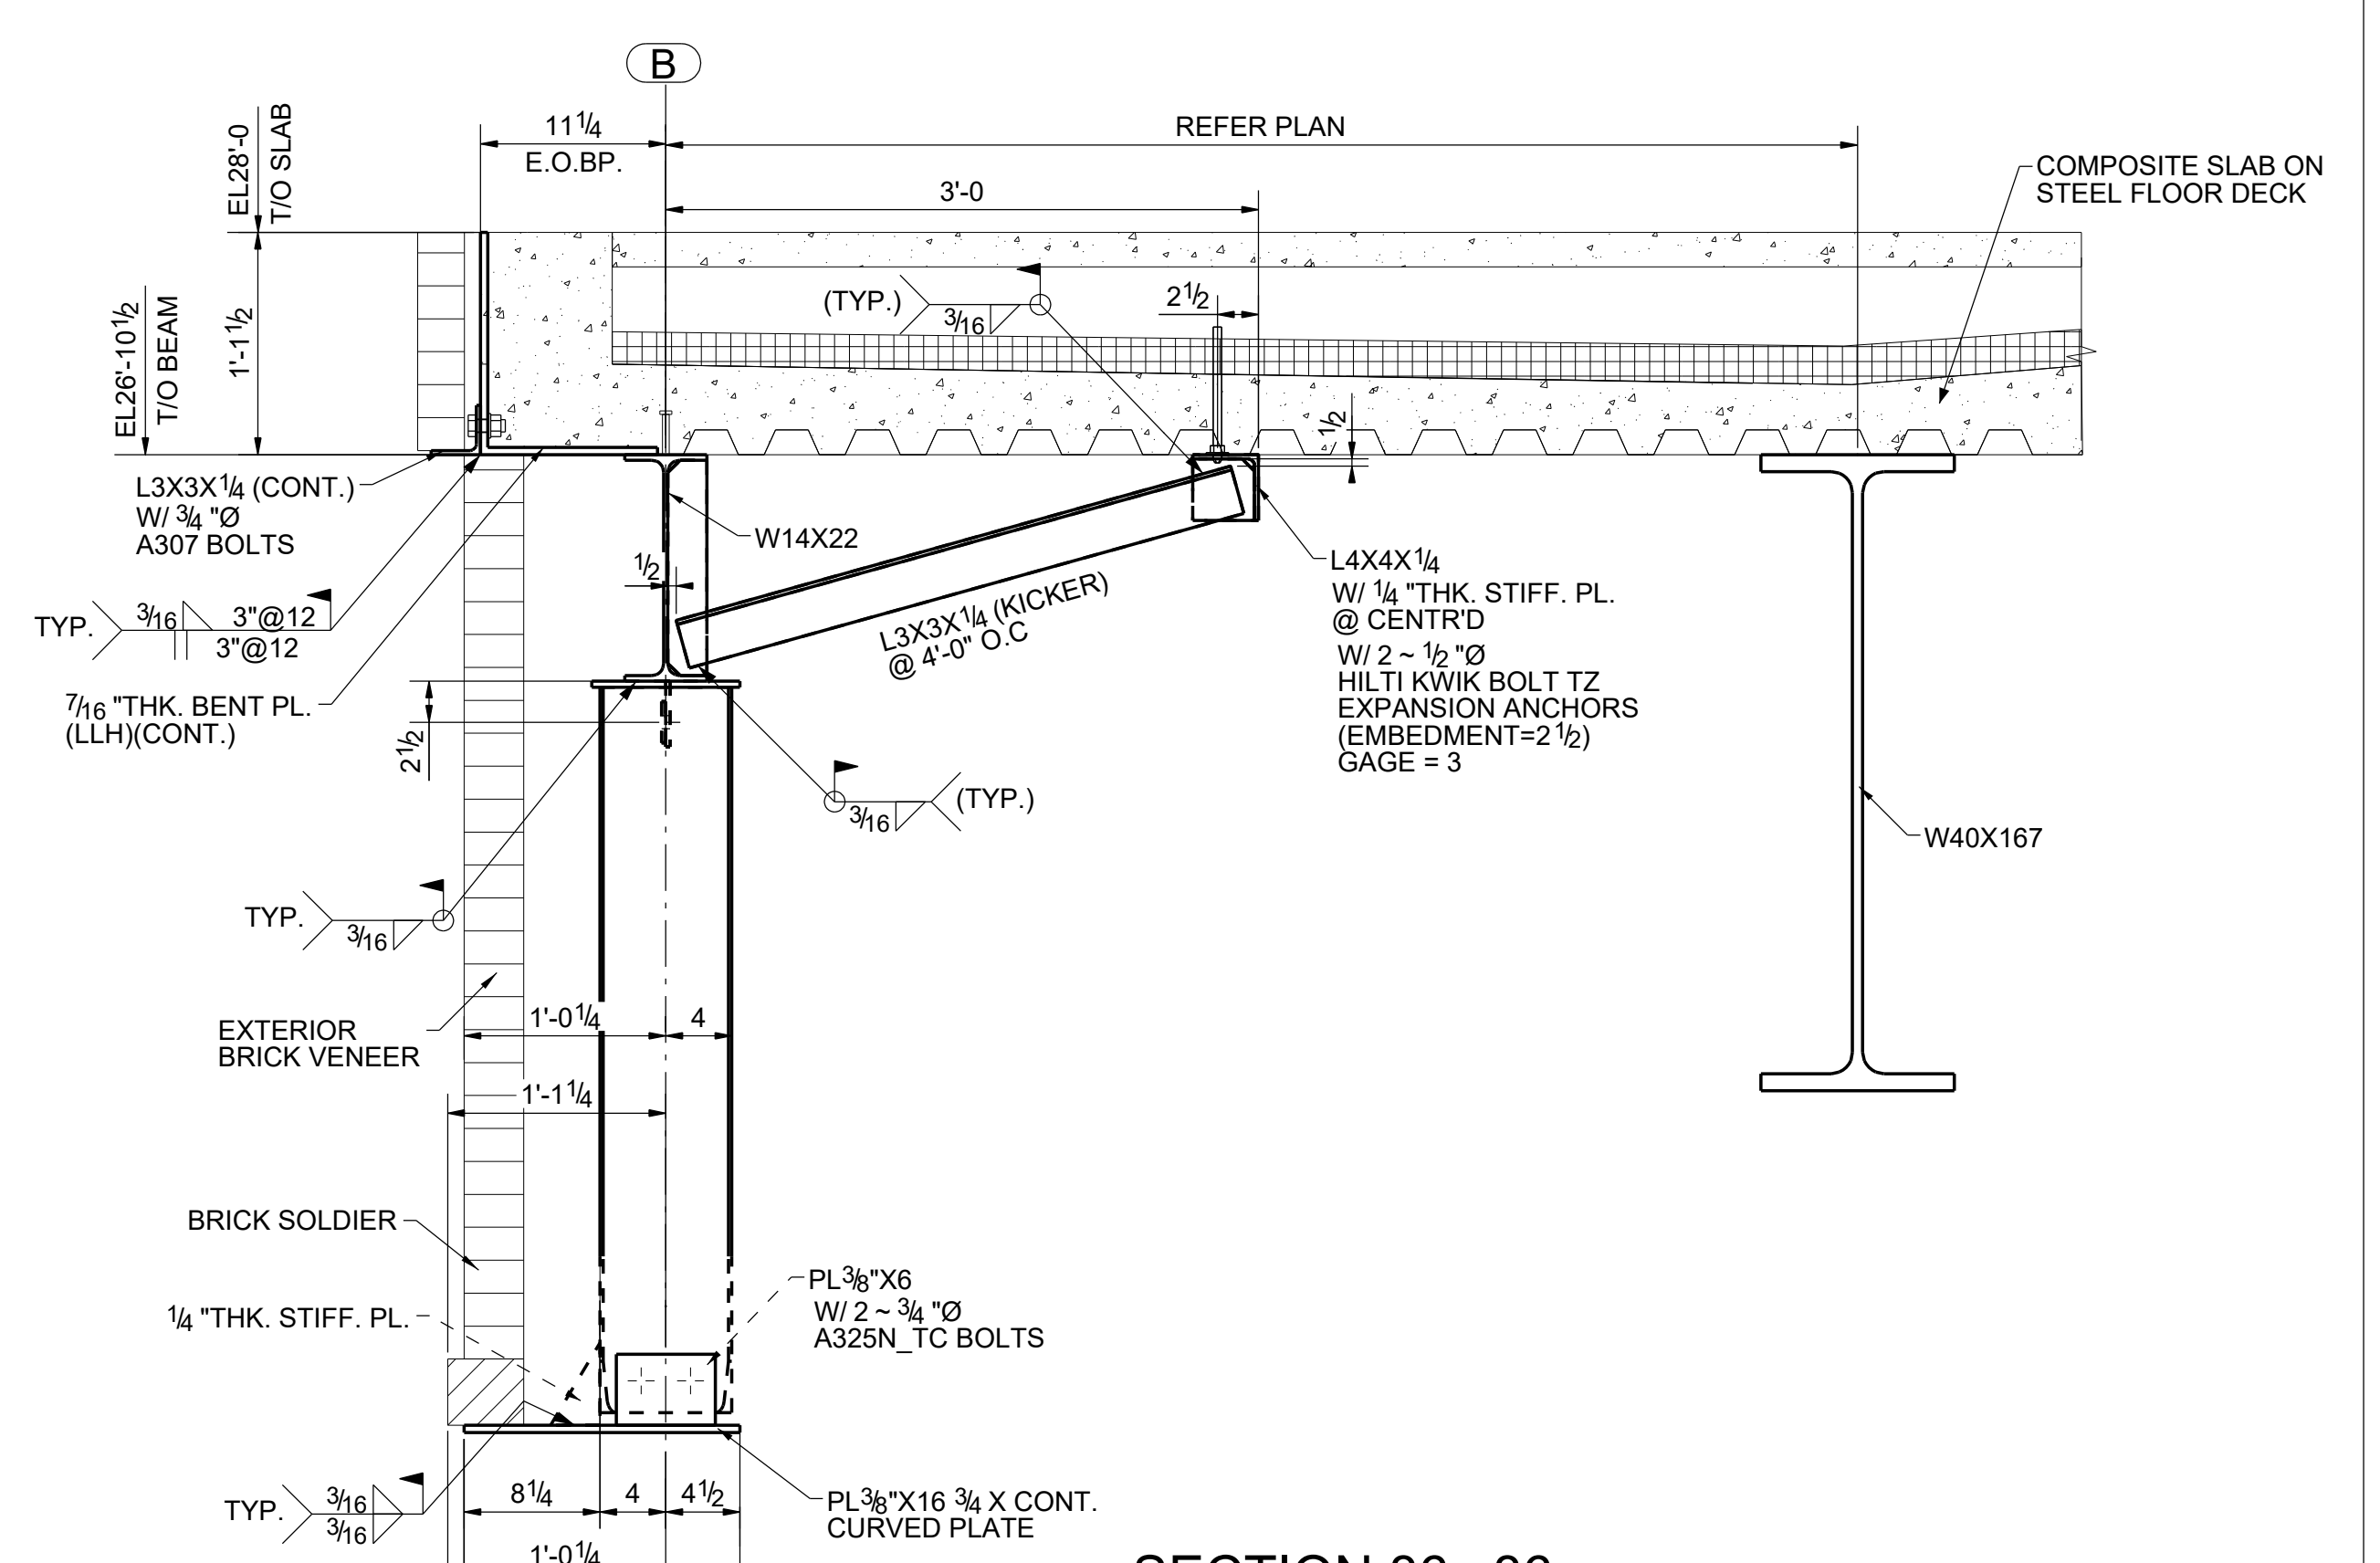


SECTION 86 - 86
E111
(REFER : SECTION 8/S-607)

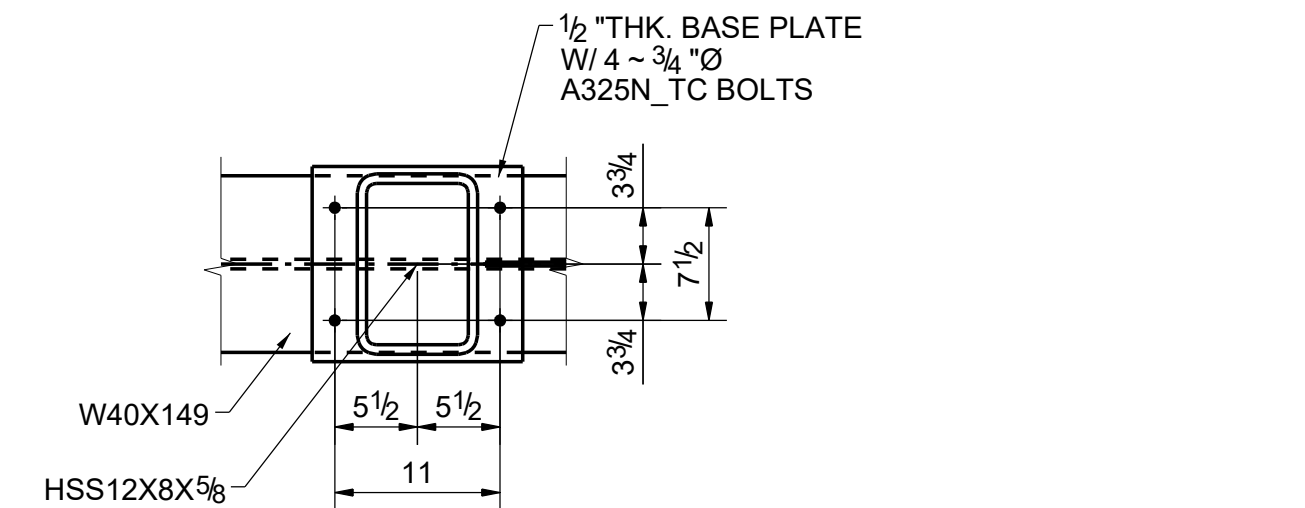






SECTION 87A - 87A

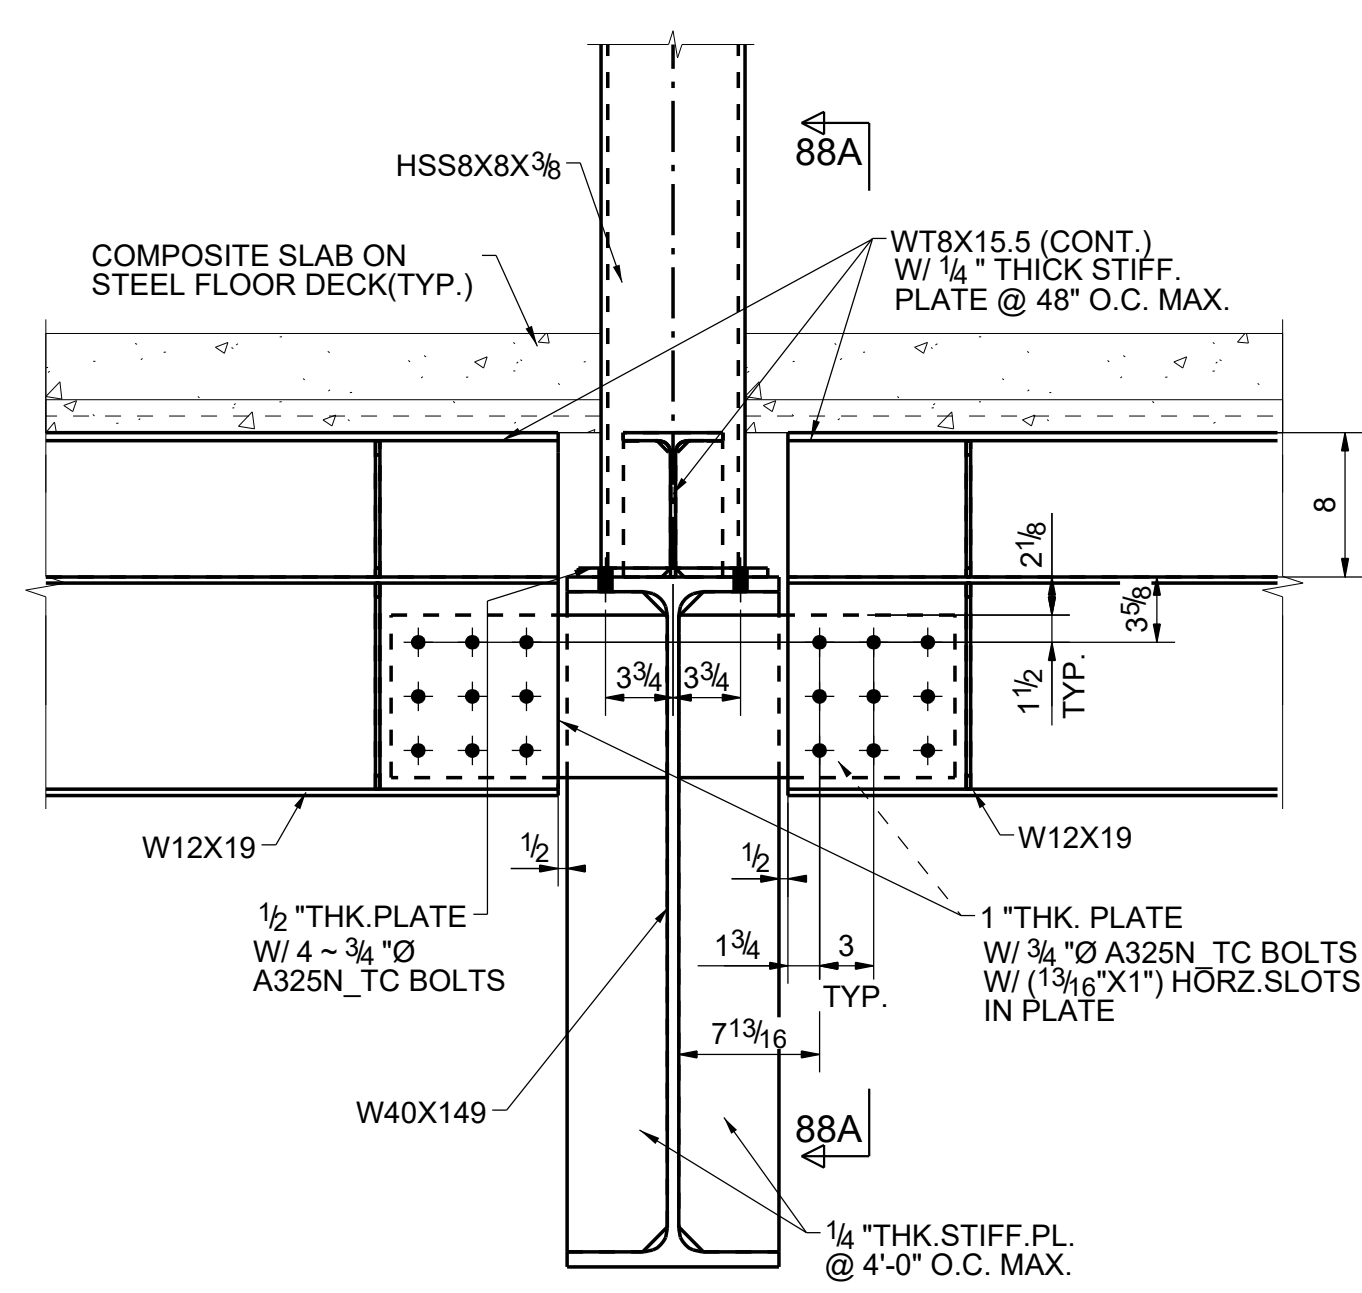



SECTION 88 - 88
E111
(REFER : SECTION 6/S-607)

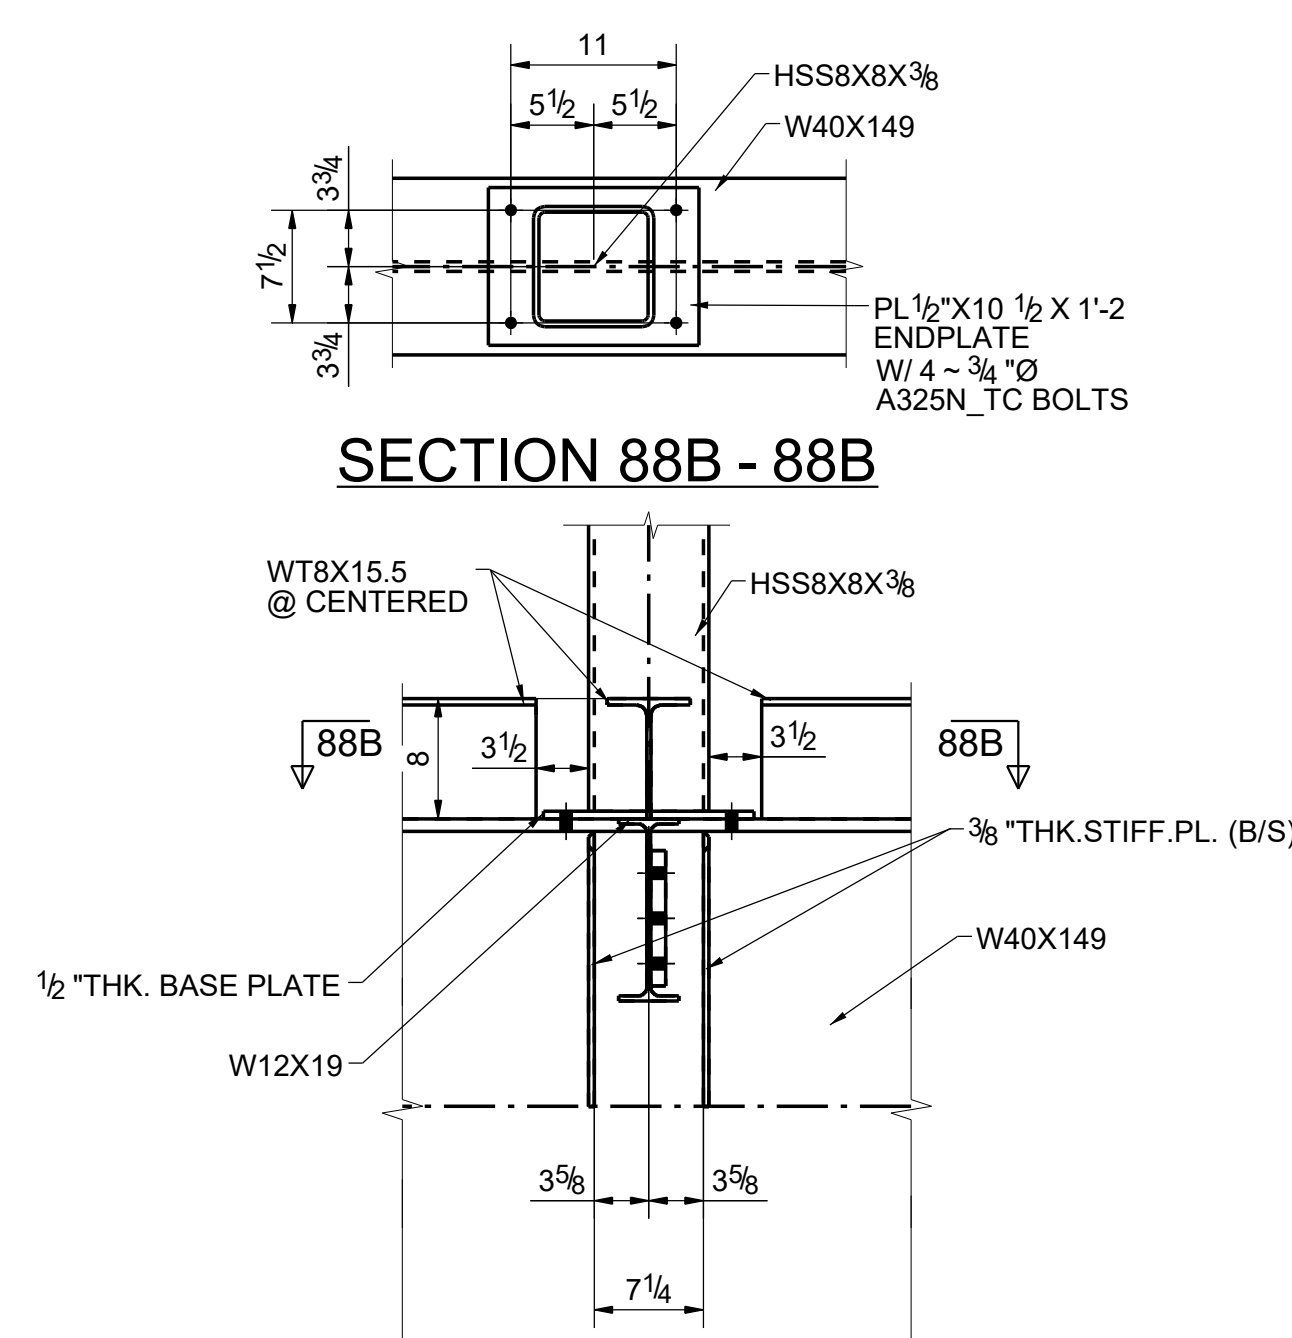

SECTION 88A - 88A

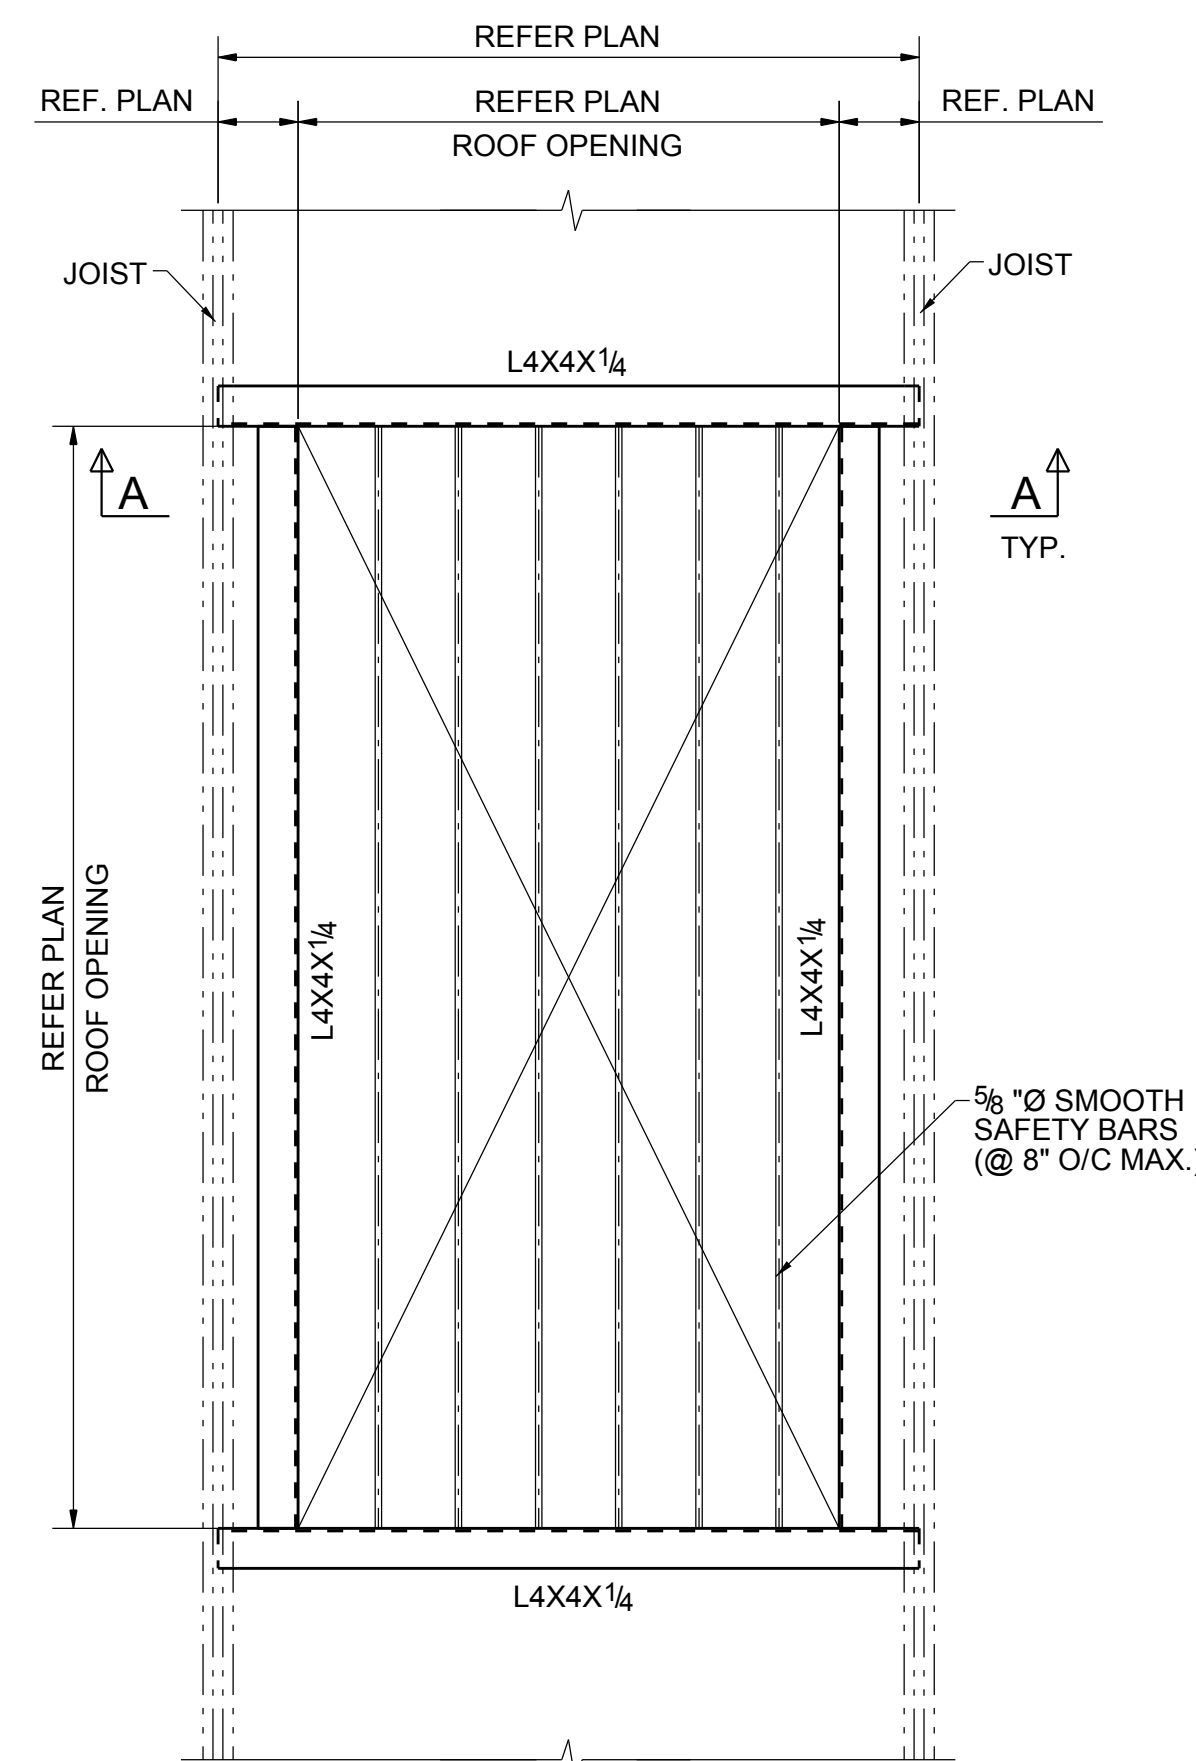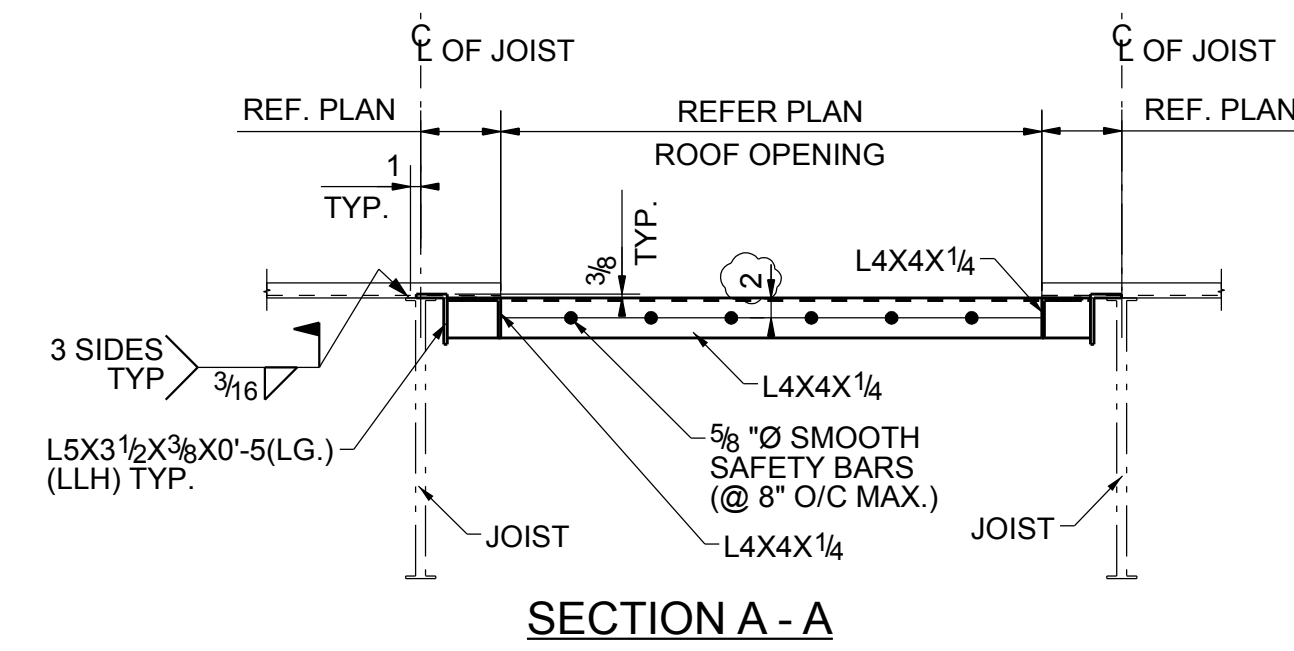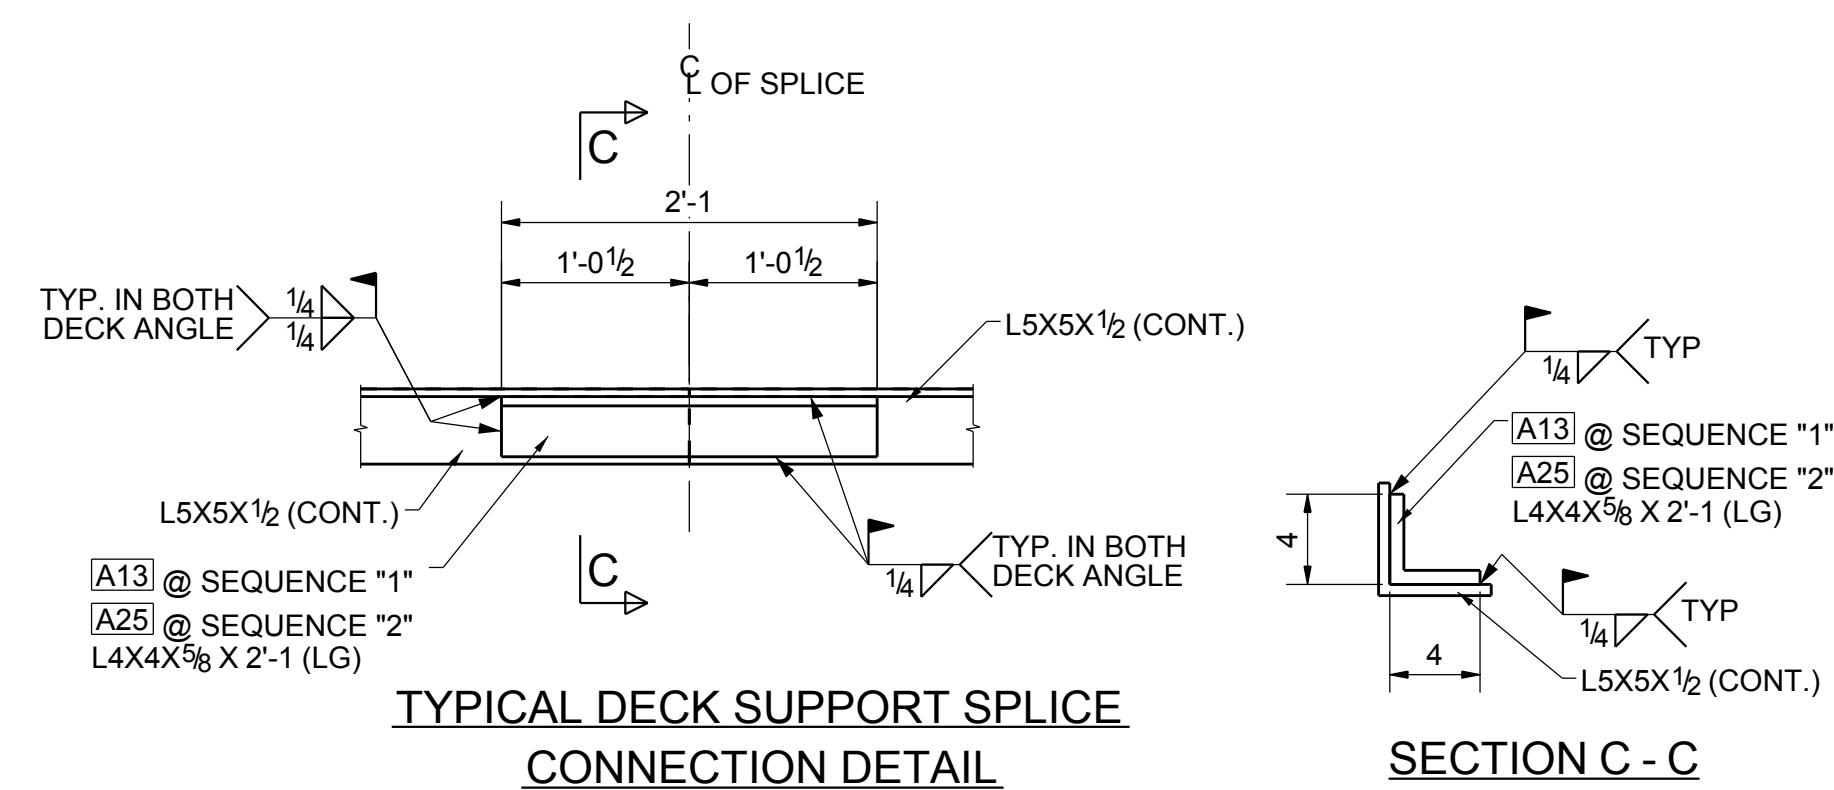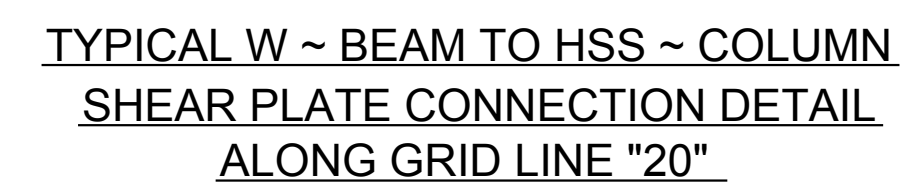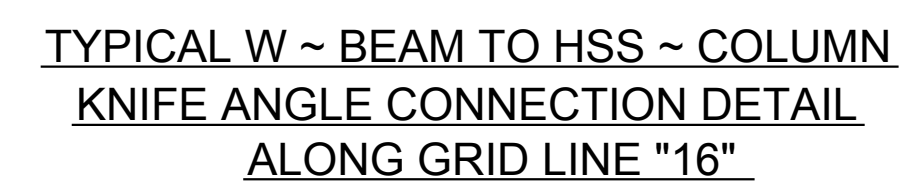

TYPICAL ROOF OPENING DECK SUPPORT DETAIL

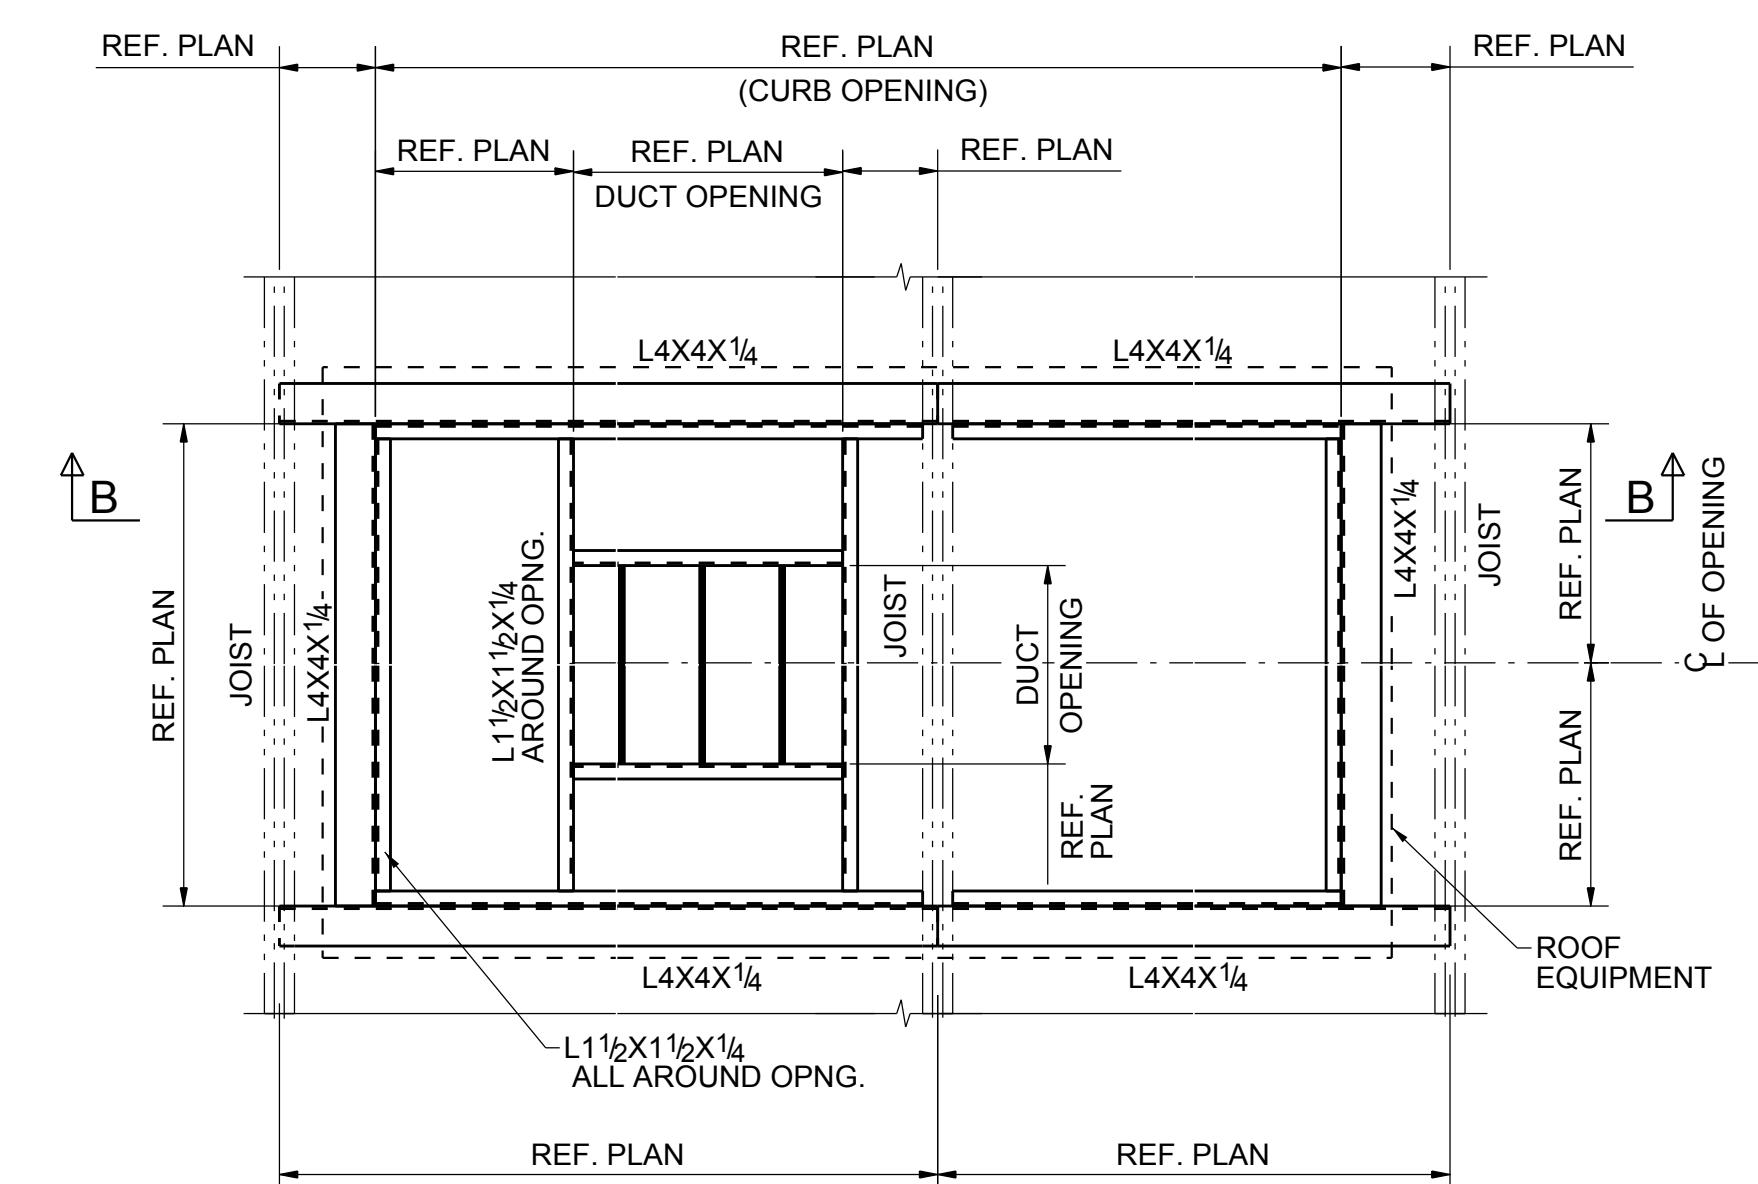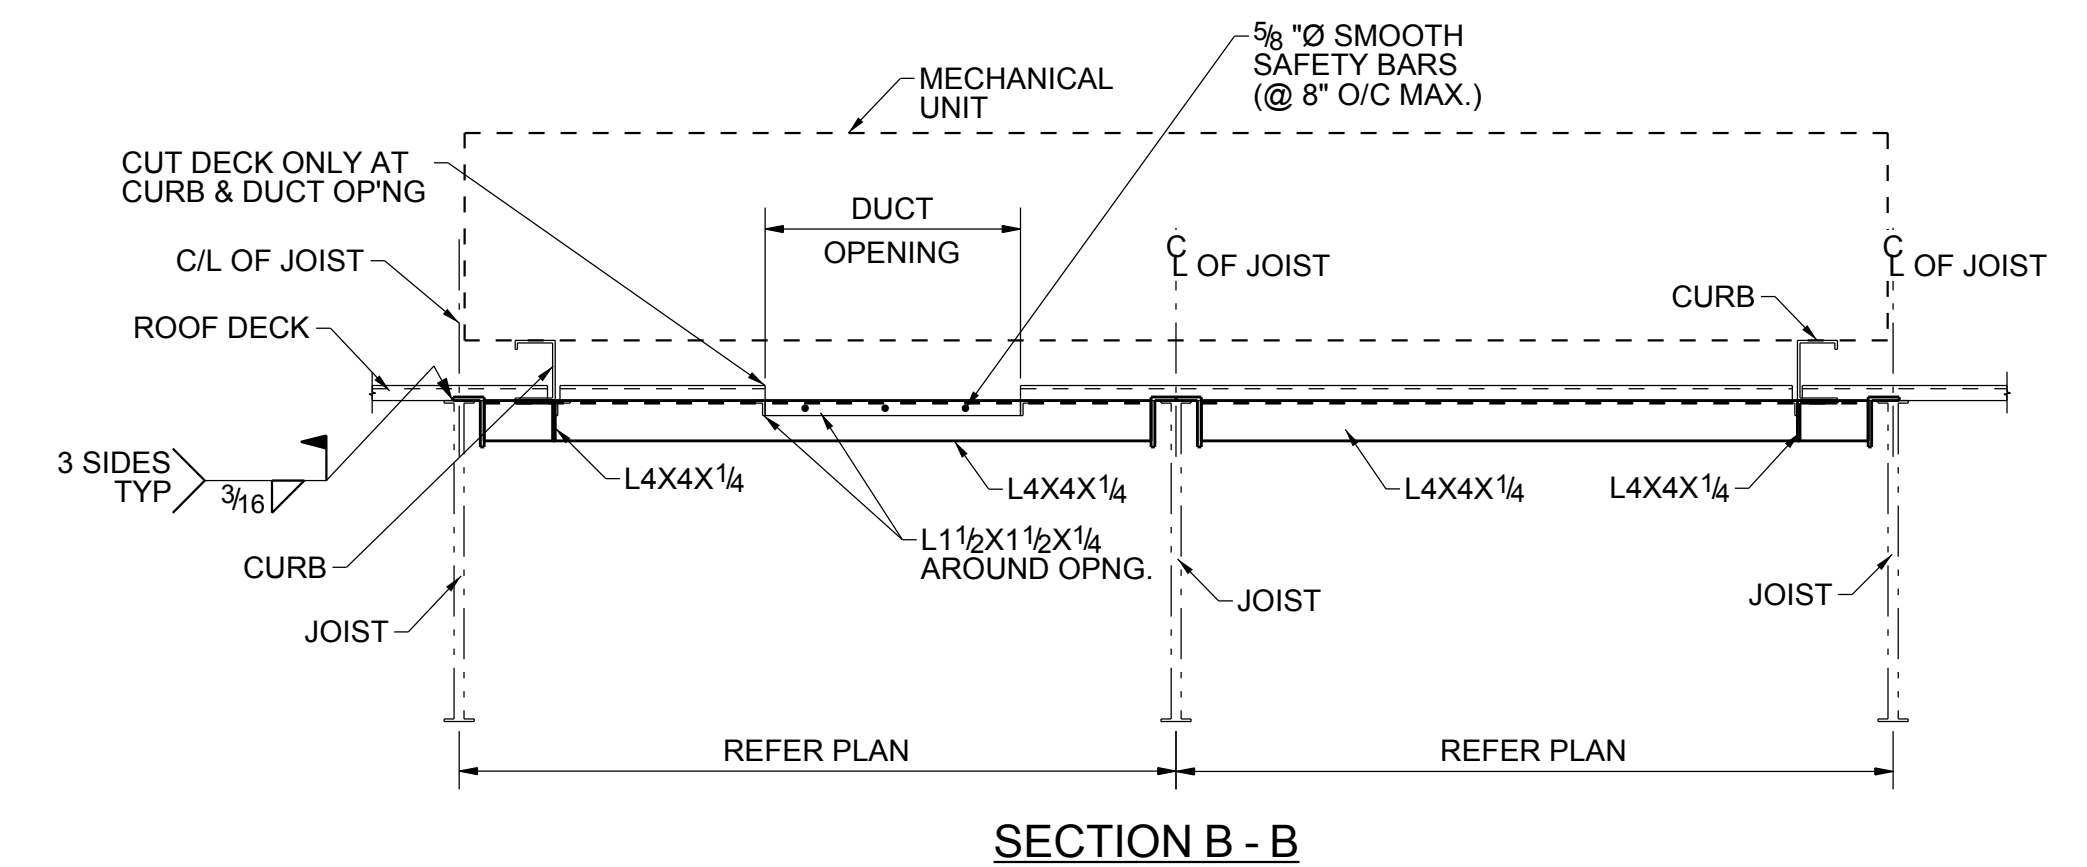

TYPICAL ROOF EQUIPMENT SUPPORT FRAME DETAIL