


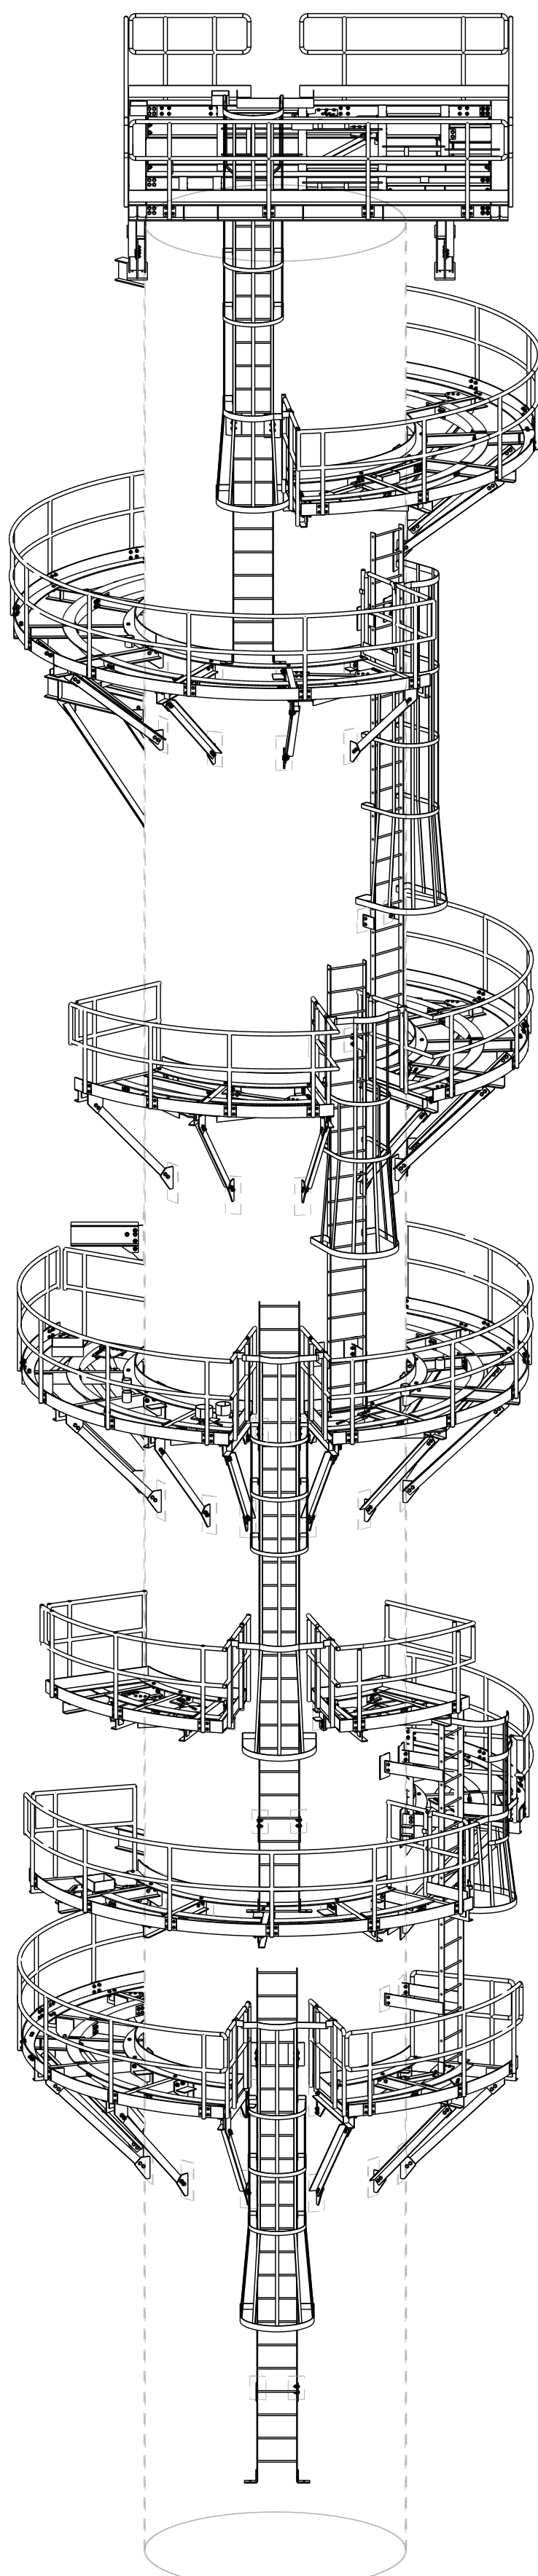

ISOMETRIC VIEW

DETAIL MARK	CONNECTION DETAIL TYPE
FBP	BEAM TO BEAM FIN PLATE CONNECTION
FPC	BEAM TO COLUMN FIN PLATE CONNECTION
EPB	BEAM TO BEAM END PLATE CONNECTION
EPC	BEAM TO COLUMN END PLATE CONNECTION
MC	BEAM TO COLUMN FLANGE MOMENT CONNECTION
MCW	BEAM TO COLUMN WEB MOMENT CONNECTION
MH	BEAM TO COLUMN FLANGE MOMENT CONNECTION WITH HAUNCH
MHW	BEAM TO COLUMN WEB MOMENT CONNECTION WITH HAUNCH
HB	HORIZONTAL BRACING CONNECTION
VB	VERTICAL BRACING CONNECTION
CSP	COLUMN SPLICE CONNECTION
BSP	BEAM SPLICE CONNECTION
PC	POST CONNECTION
RB	RESTED BEAM CONNECTION
EPCW	BEAM TO COLUMN WEB END PLATE CONNECTION
FPP	BEAM TO PLATE FIN PLATE CONNECTION
WB	WELDED BEAM MOMENT CONNECTION

NOTES



- All dimensions are in millimeters & all elevations are in meters Unless noted otherwise.
- Grade of structural shall be S275JR complying with BS EN 10025 or Equivalent U.N.O
- Grade of connection plates shall be S355JR complying with BS EN 10025 or Equivalent U.N.O
- Handrail units (Including handrails, mid rails & stanchions) shall be in accordance to ASTM A53-Grade B
- For primary structural members High strength bolts, nuts and washers shall be as per :-
Bolt ASTM A325/A325M or A193-B7/A193M-B7, (20mm dia min).
Heavy Hex Nut ASTM A563/A563M Gr.DH and washer ASTM F436/F436M
- For secondary members (railing, ladder, purlins and girts etc.)
Standard bolt assemblies shall be as per:-
Bolt ASTM A325M (limited in size to 16mm diameter)
Heavy Hex Nut ASTM A563/A563M Gr.A and Washer ASTM F436
Washer ASTM F436/F436M
- Bolt, Nuts and Washers shall be hot-dip galvanized in accordance with ASTM A153/A153M or ASTM B695.
- All bolted connection are bearing type & all bolted joints shall be snug tightened (s/t) U.N.O
- Minimum weld size shall be 6mm, unless otherwise noted.
- All structural shall be painted as per specification AD282-732-G-01801

LEGENDS:

- | | |
|-----------|-------------------------|
| 1. U.N.O | UNLESS NOTED OTHERWISE |
| 2. U/S BP | UNDERSIDE OF BASE PLATE |
| 3. T.O.S | TOP OF STEEL |
| 4. T.O.G | TOP OF GRATING |
| 5. EX. | EXISTING MEMBER |

HOLE DIAMETER SHALL BE AS FOLLOWS U.N.O

BOT DIA (mm)	HOLE DIA
16	18
20	22
22	24
24	27
27	30
30	33
> 36	D+3

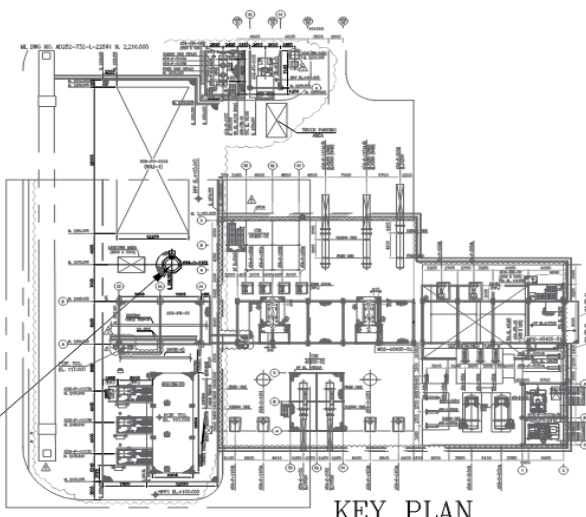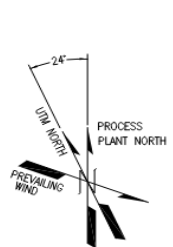


THIS DRAWING

KEY PLAN

REFERENCE DRAWINGS:

Sr. No.	DOC / DRAWING NO.	DOC / DRAWING TITTLE
1	AD282-732-C-38068 SHEET - 001 & 002	GENERAL NOTE
2	AD282-732-C-38070 SHEET - 001 & 002	GRATING DETAILS
3	AD282-732-C-38074 SHEET - 001 & 002	STAIR & HANDRAIL
4	AD282-732-C-38075	STANDARD DRAWING LADDER
5	AD282-604-C-33217	BASE PLATE LAYOUT & DETAILS
6	AD282-604-C-33217 & 218 & 219	PLAN, ELEVATION & SECTIONS
7	AD282-604-C-33220 & 33526	PLAN, ELEVATION & SECTIONS

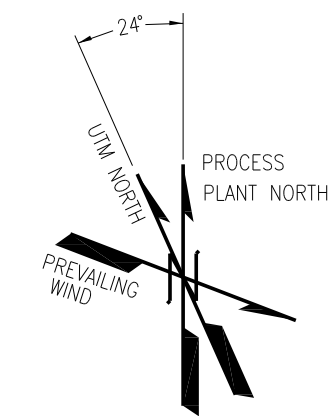

NOTES



1. All dimensions are in millimeters & all elevations are in meters Unless noted otherwise.
2. Grade of structural shall be S275JR complying with BS EN 10025 or Equivalent U.N.O
3. Handrail units (Including handrails, mid rails & stanchions) shall be in accordance to ASTM A53-Grade B
4. For primary structural members High strength bolts, nuts and washers shall be as per :-
Bolt ASTM A325/A325M or A193-B7/A193M-B7, (20mm dia min).
Heavy Hex Nut ASTM A563/A563M Gr.DH and washer ASTM F436/F436M
5. For secondary members (railing, ladder, purlins and girts etc.)
Standard bolt assemblies shall be as per:-
Bolt ASTM A325M (limited in size to 16mm diameter)
Heavy Hex Nut ASTM A563/A563M Gr.A and Washer ASTM F436
Washer ASTM F436/F436M
6. Bolt, Nuts and Washers shall be hot-dip galvanized in accordance with ASTM A153/A153M or ASTM B695.
7. All bolted connection are bearing type & all bolted joints shall be snug tightened (s/t) U.N.O
8. Minimum weld size shall be 6mm, unless otherwise noted.
9. All structural shall be painted as per specification AD282-732-G-01801

LEGENDS:

- | | |
|-----------|-------------------------|
| 1. U.N.O | UNLESS NOTED OTHERWISE |
| 2. U/S BP | UNDERSIDE OF BASE PLATE |
| 3. T.O.S | TOP OF STEEL |
| 4. T.O.G | TOP OF GRATING |
| 5. EX. | EXISTING MEMBER |

HOLE DIAMETER SHALL BE AS FOLLOWS U.N.O

BOT DIA (mm)	HOLE DIA
16	18
20	22
22	24
24	27
27	30
30	33
> 36	D+3

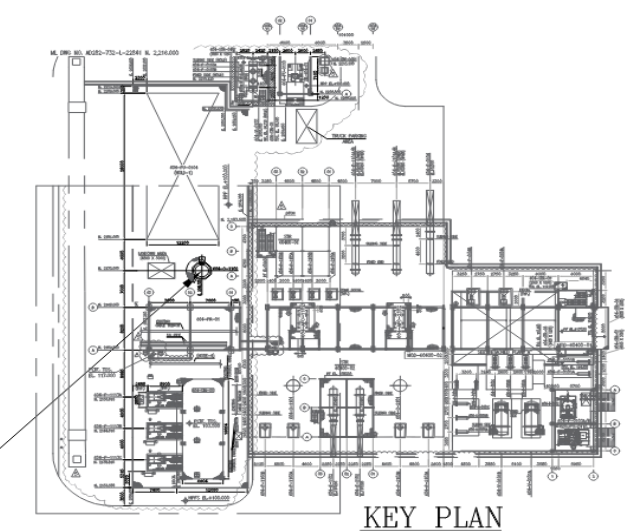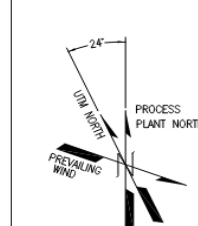


THIS DRAWING


KEY PLAN

REFERENCE DRAWINGS:


Sr. No.	DOC / DRAWING NO.	DOC / DRAWING TITLE
1	AD282-732-C-38068 SHEET - 001 & 002	GENERAL NOTE
2	AD282-732-C-38070 SHEET - 001 & 002	GRATING DETAILS
3	AD282-732-C-38074 SHEET - 001 & 002	STAIR & HANDRAIL
4	AD282-732-C-38075	STANDARD DRAWING LADDER
5	AD282-604-C-33217	BASE PLATE LAYOUT & DETAILS
6	AD282-604-C-33217 & 218 & 219	PLAN, ELEVATION & SECTIONS
7	AD282-604-C-33220 & 33526	PLAN, ELEVATION & SECTIONS

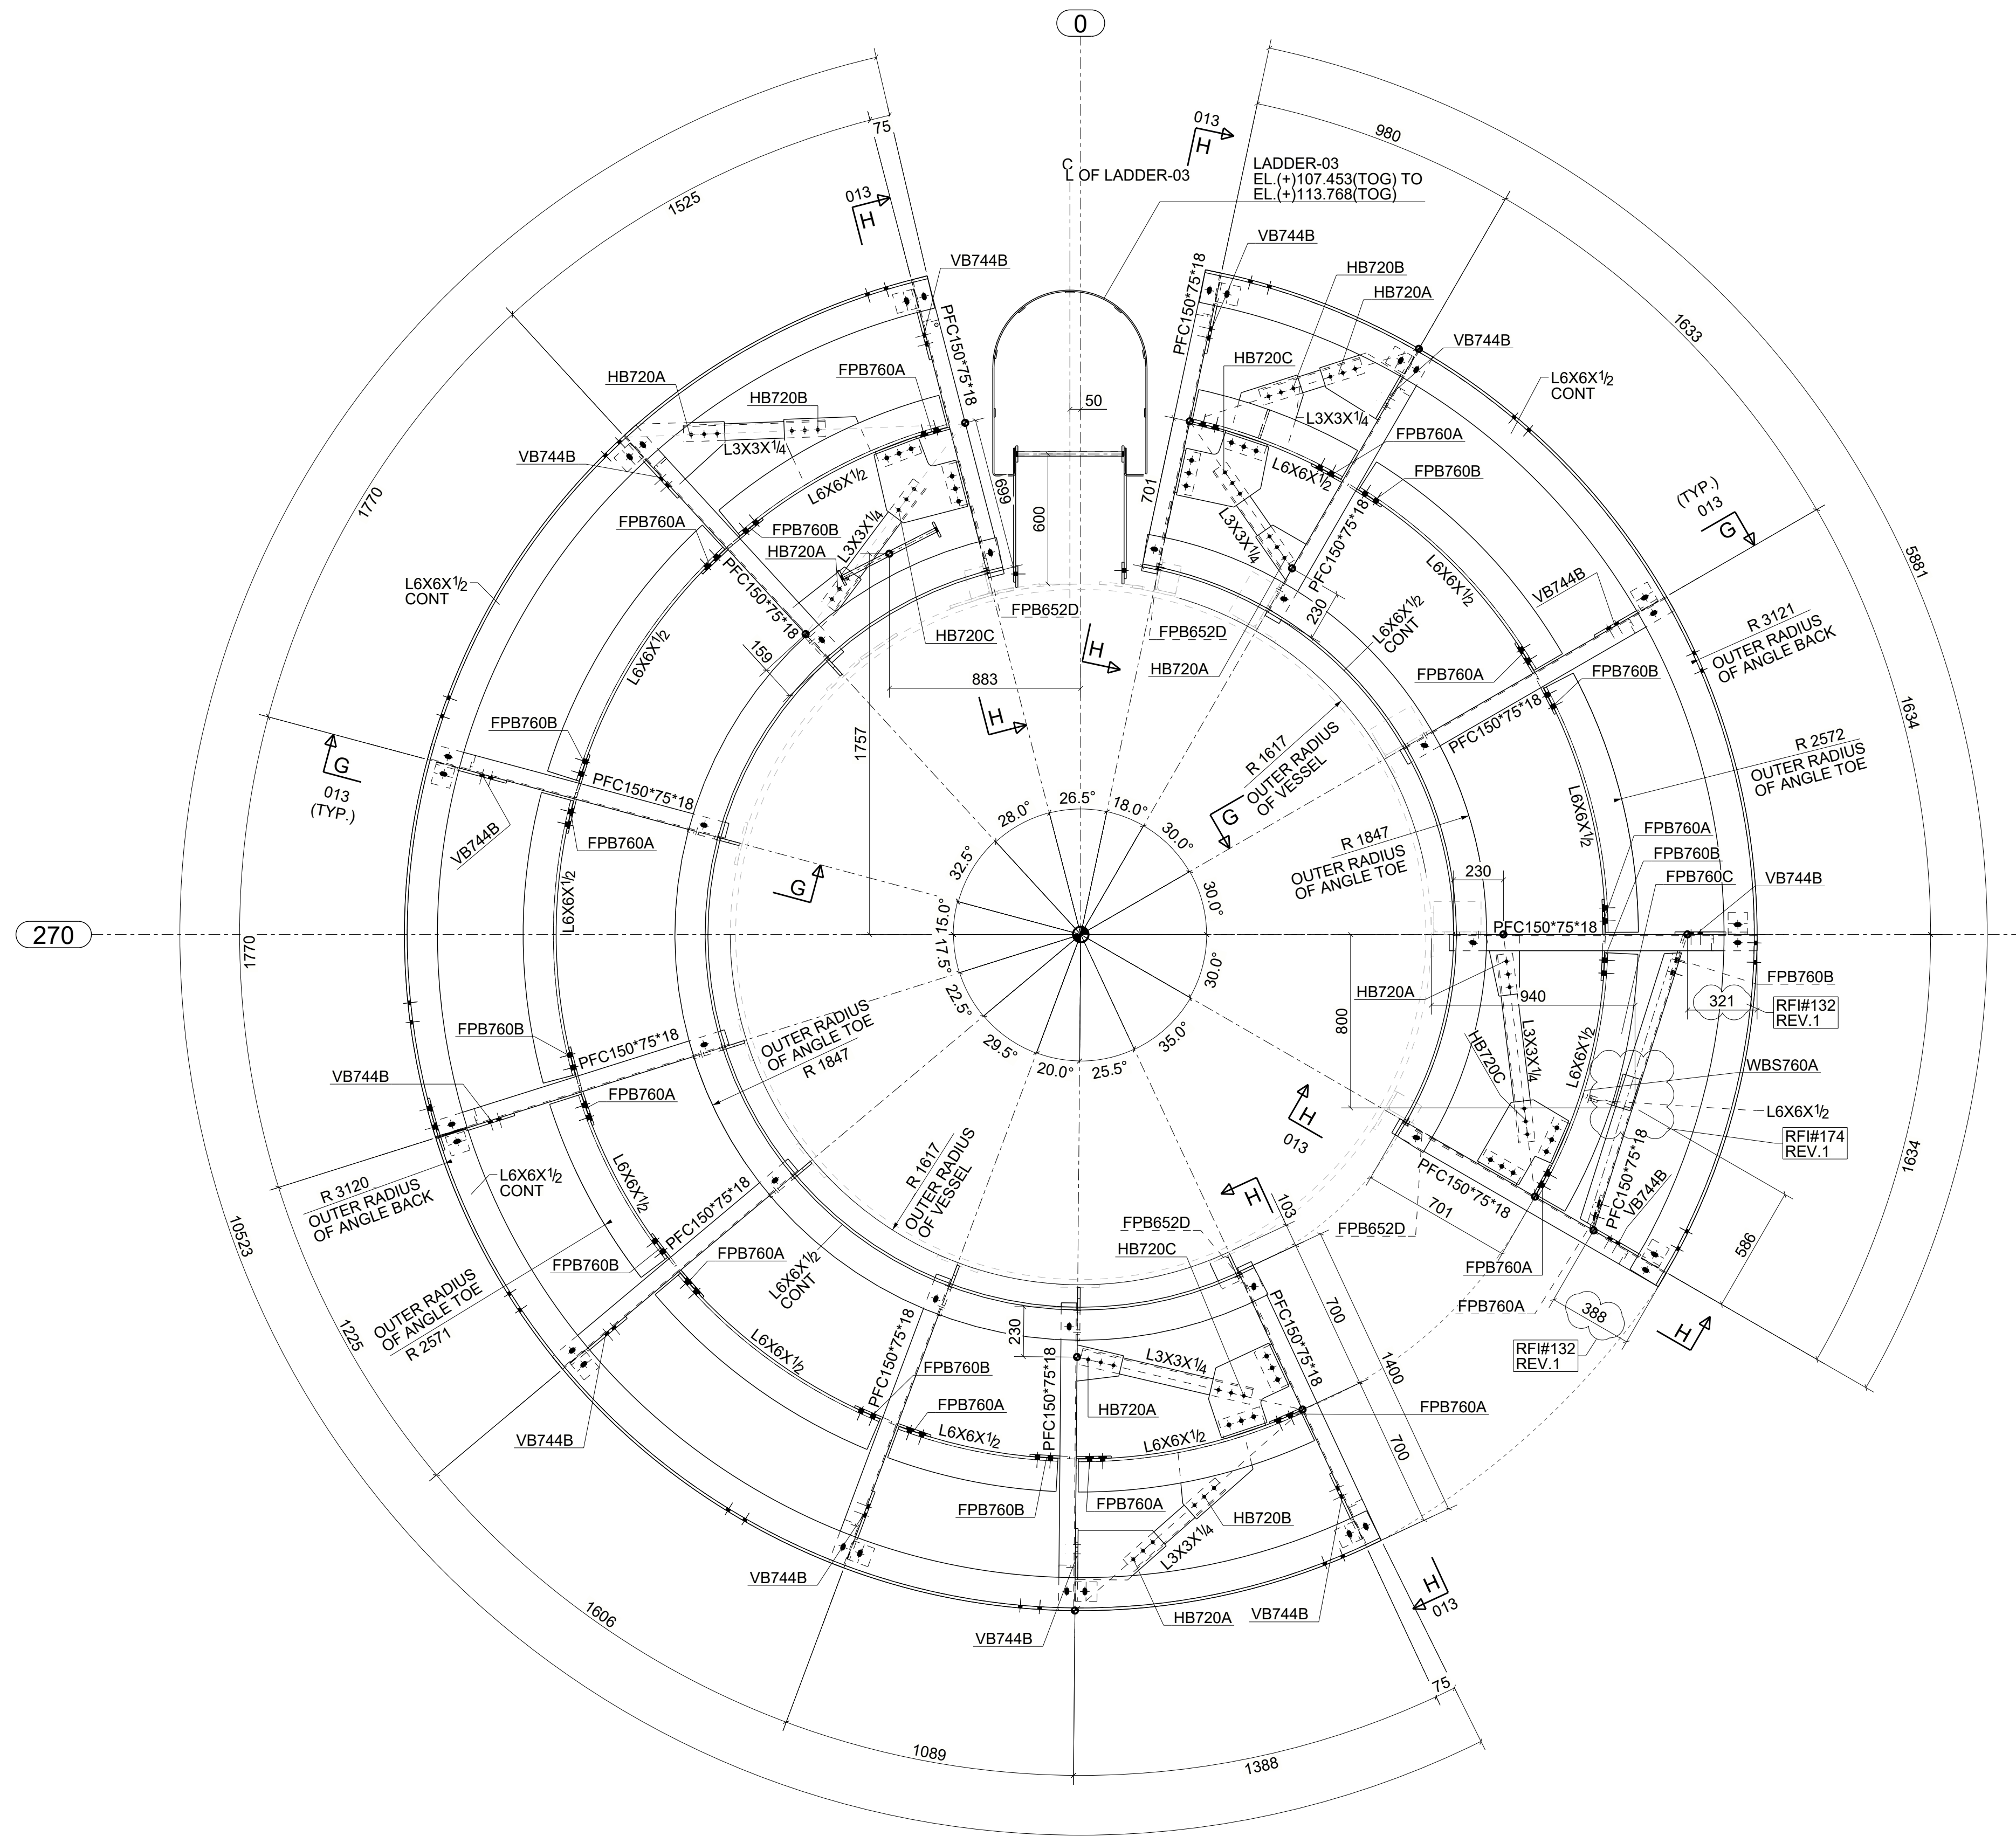

PLATFORM FRAMING PLAN AT EL. + 113.725 (TOS)
ALL PLAN BRACING ARE AT (-50) UNO

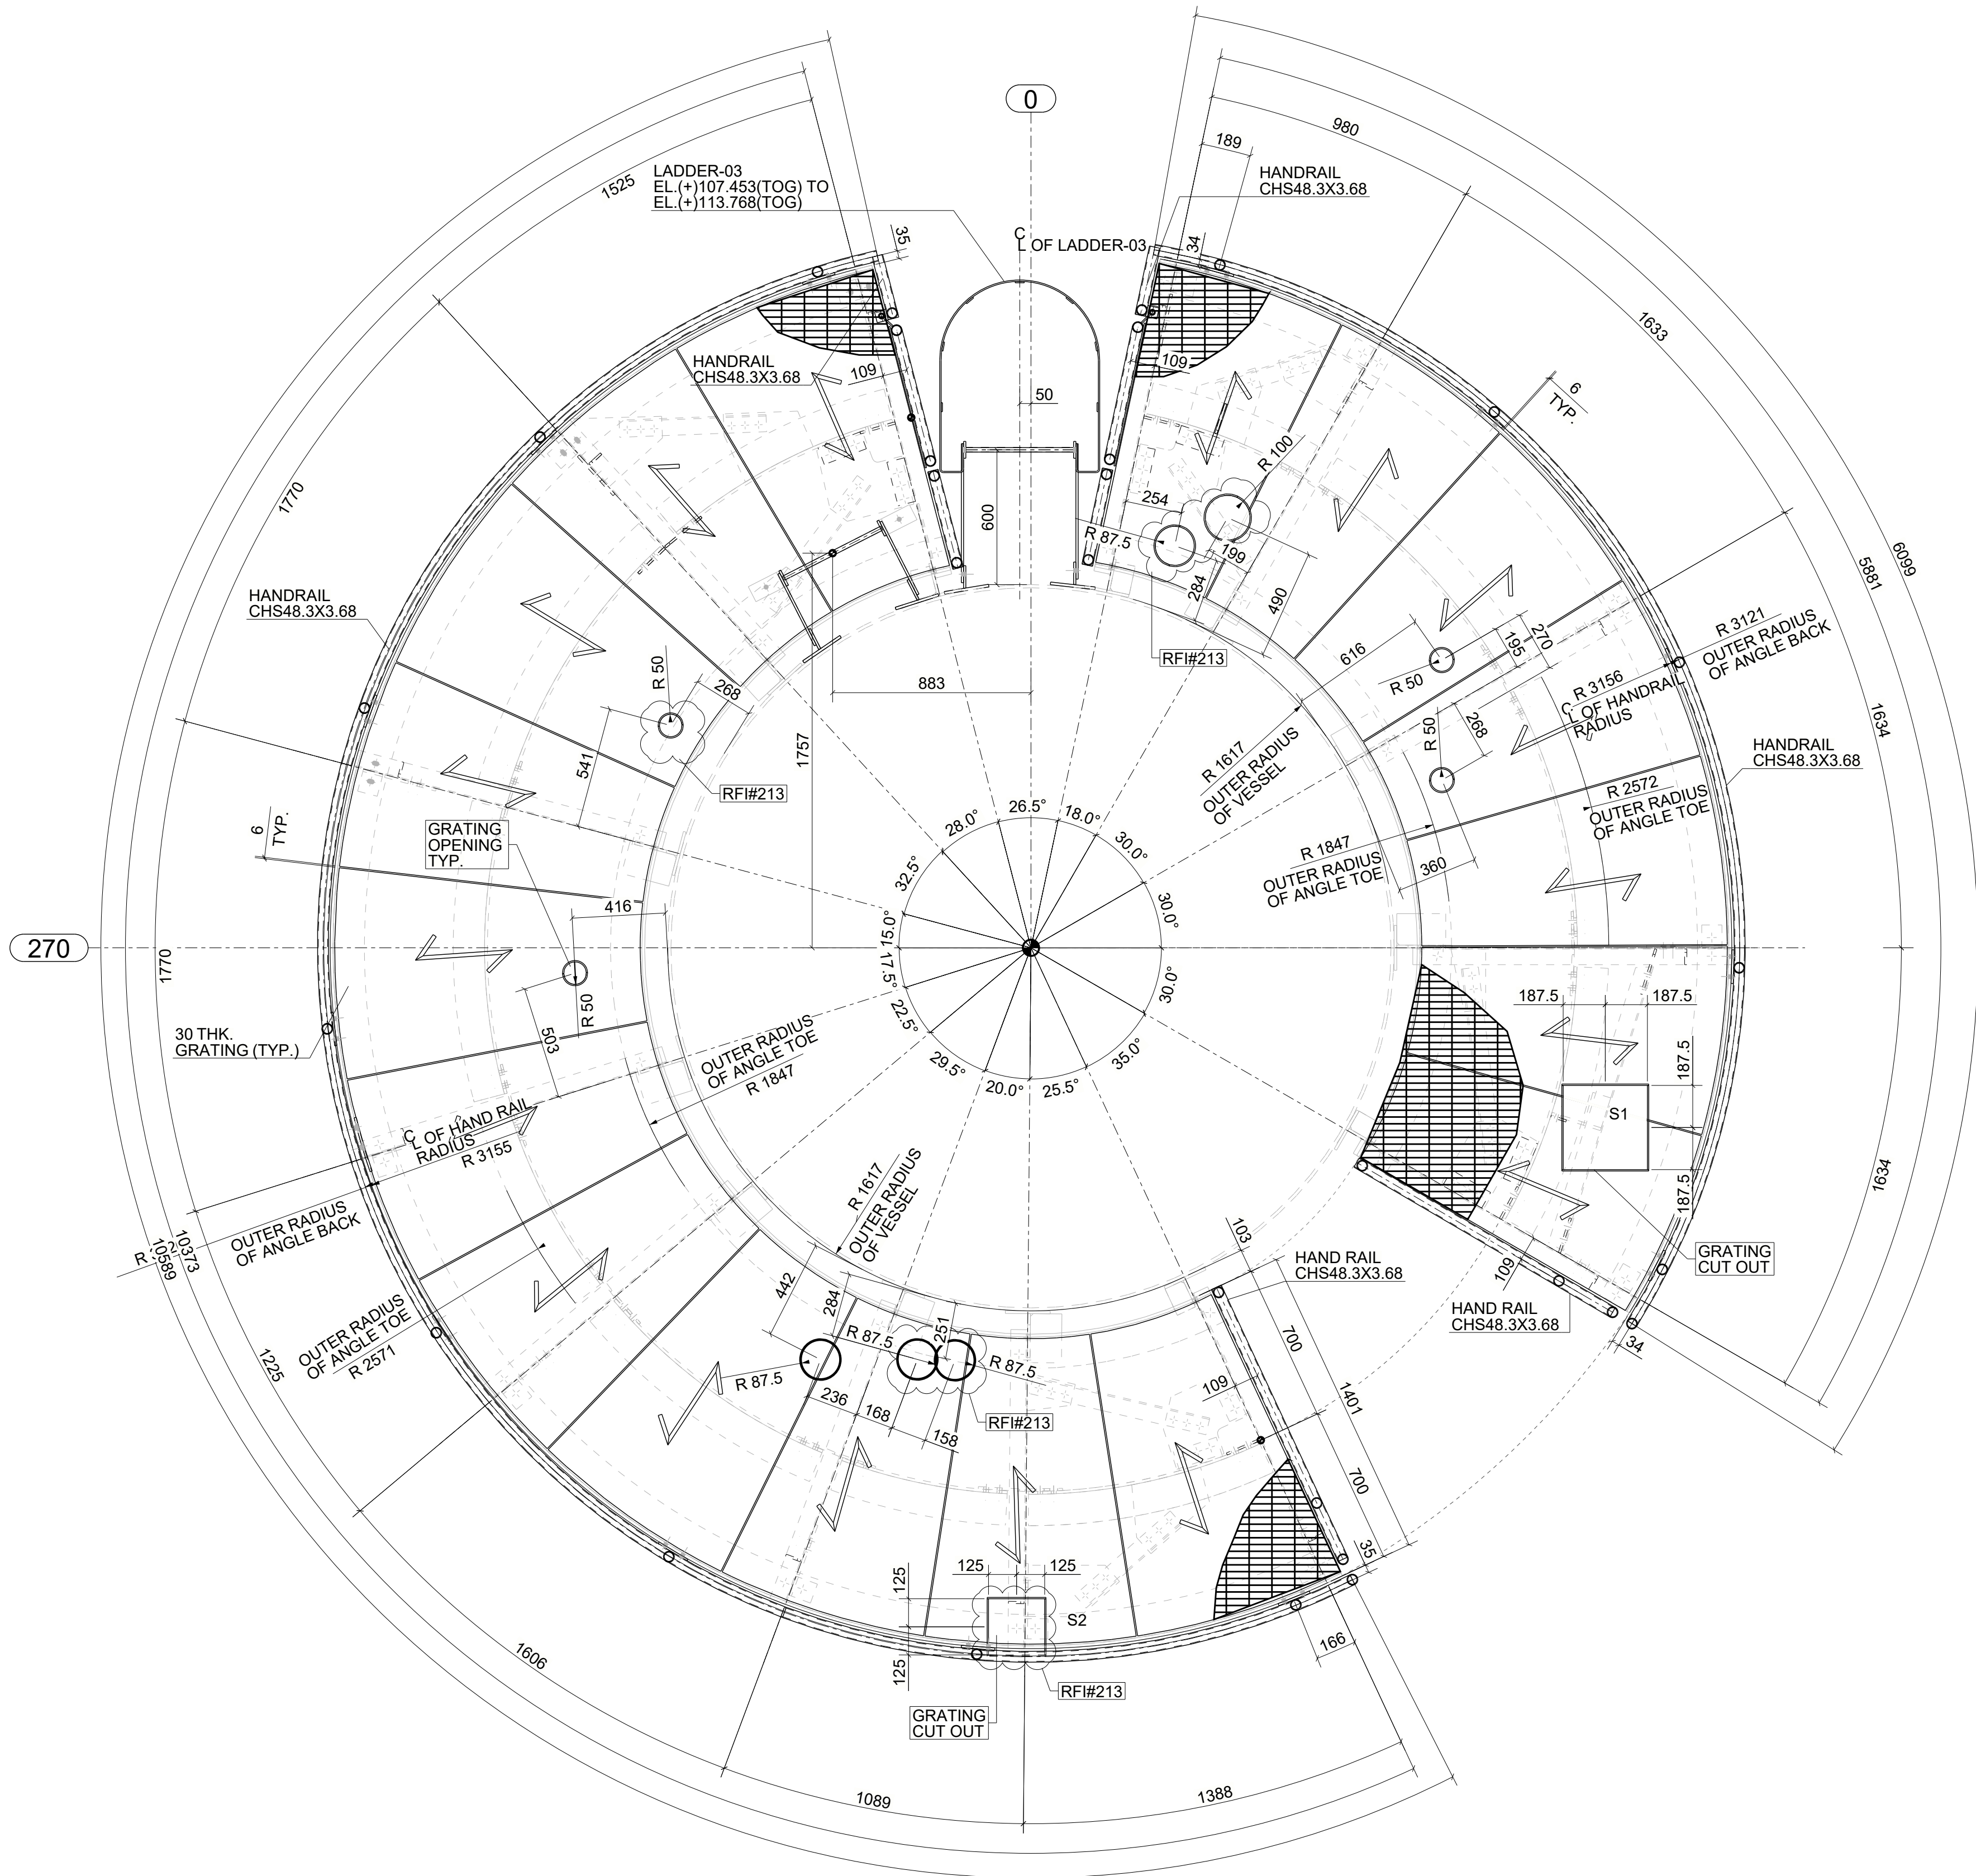

GRATING & HANDRAIL PLAN AT EL. + 113.768 (TOG)
ALL PLAN BRACING ARE AT (-50) UNO

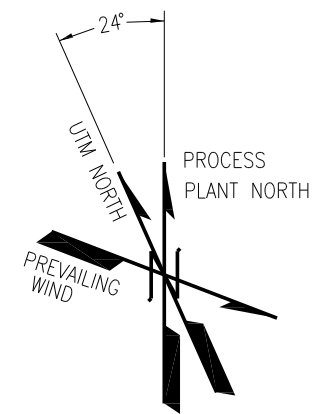

NOTES



1. All dimensions are in millimeters & all elevations are in meters Unless noted otherwise.
2. Grade of structural shall be S275JR complying with BS EN 10025 or Equivalent U.N.O
3. Grade of connection plates shall be S355JR complying with BS EN 10025 or Equivalent U.N.O
4. Handrail units (Including handrails, mid rails & stanchions) shall be in accordance to ASTM A53-Grade B
5. For primary structural members High strength bolts, nuts and washers shall be as per :-
Bolt ASTM A325/A325M or A193-B7/A193M-B7, (20mm dia min).
Heavy Hex Nut ASTM A563/A563M Gr.DH and washer ASTM F436/F436M
6. For secondary members (railing, ladder, purlins and girts etc.)
Standard bolt assemblies shall be as per:-
Bolt ASTM A325M (limited in size to 16mm diameter)
Heavy Hex Nut ASTM A563/A563M Gr.A and Washer ASTM F436
Washer ASTM F436/F436M
7. Bolt, Nuts and Washers shall be hot-dip galvanized in accordance with ASTM A153/A153M or ASTM B695.
8. All bolted connection are bearing type & all bolted joints shall be snug tightened (s/t) U.N.O
9. Minimum weld size shall be 6mm, unless otherwise noted.
10. All structural shall be painted as per specification AD282-732-G-01801

LEGENDS:

1. U.N.O UNLESS NOTED OTHERWISE
2. U/S BP UNDERSIDE OF BASE PLATE
3. T.O.S TOP OF STEEL
4. T.O.G TOP OF GRATING
5. EX. EXISTING MEMBER

HOLE DIAMETER SHALL BE AS FOLLOWS U.N.O

BOT DIA (mm)	HOLE DIA
16	18
20	22
22	24
24	27
27	30
30	33
> 36	D+3

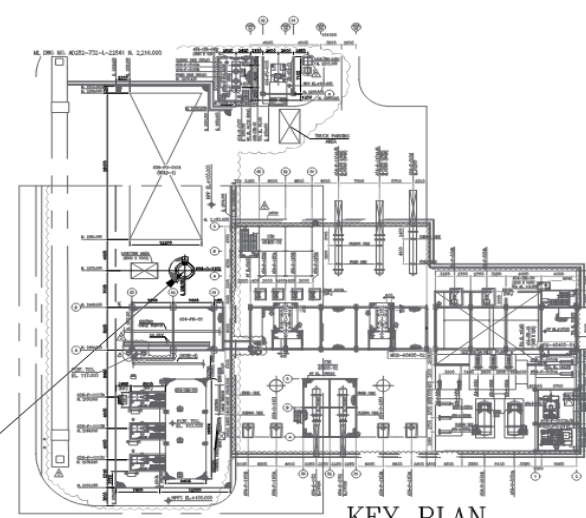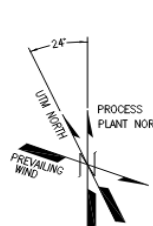



REFERENCE DRAWINGS:

Sr. No.	DOC / DRAWING NO.	DOC / DRAWING TITLE
1	AD282-732-C-38068 SHEET - 001 & 002	GENERAL NOTE
2	AD282-732-C-38070 SHEET - 001 & 002	GRATING DETAILS
3	AD282-732-C-38074 SHEET - 001 & 002	STAIR & HANDRAIL
4	AD282-732-C-38075	STANDARD DRAWING LADDER
5	AD282-604-C-33217	BASE PLATE LAYOUT & DETAILS
6	AD282-604-C-33217 & 218 & 219	PLAN, ELEVATION & SECTIONS
7	AD282-604-C-33220 & 33526	PLAN, ELEVATION & SECTIONS




LEGENDS:	
1. U.N.O	UNLESS NOTED OTHERWISE
2. U/S BP	UNDERSIDE OF BASE PLATE
3. T.O.S	TOP OF STEEL
4. T.O.G	TOP OF GRATING
5. EX.	EXISTING MEMBER

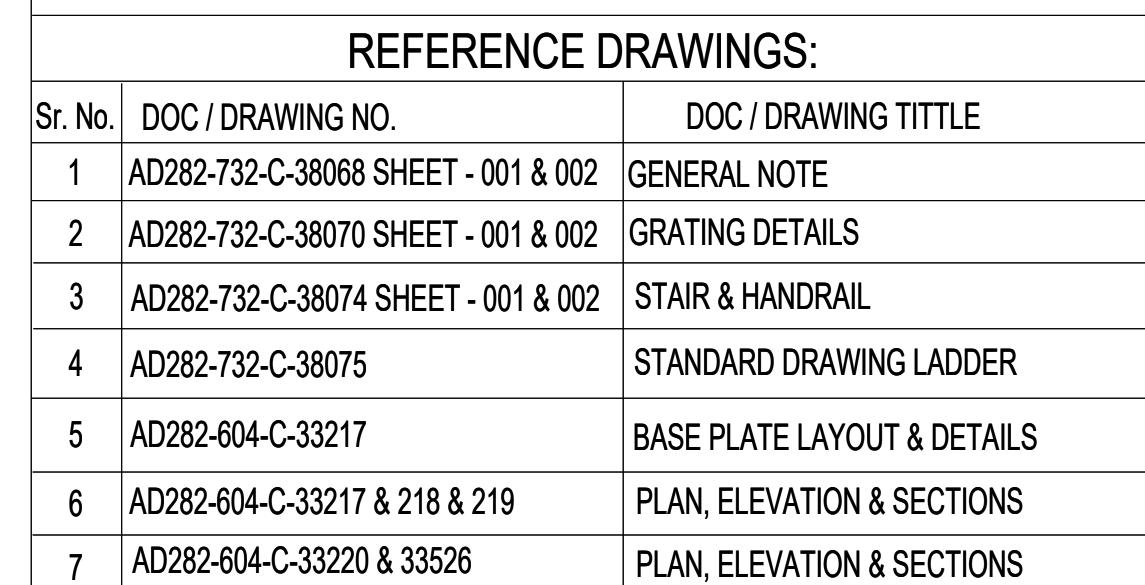[illegible]

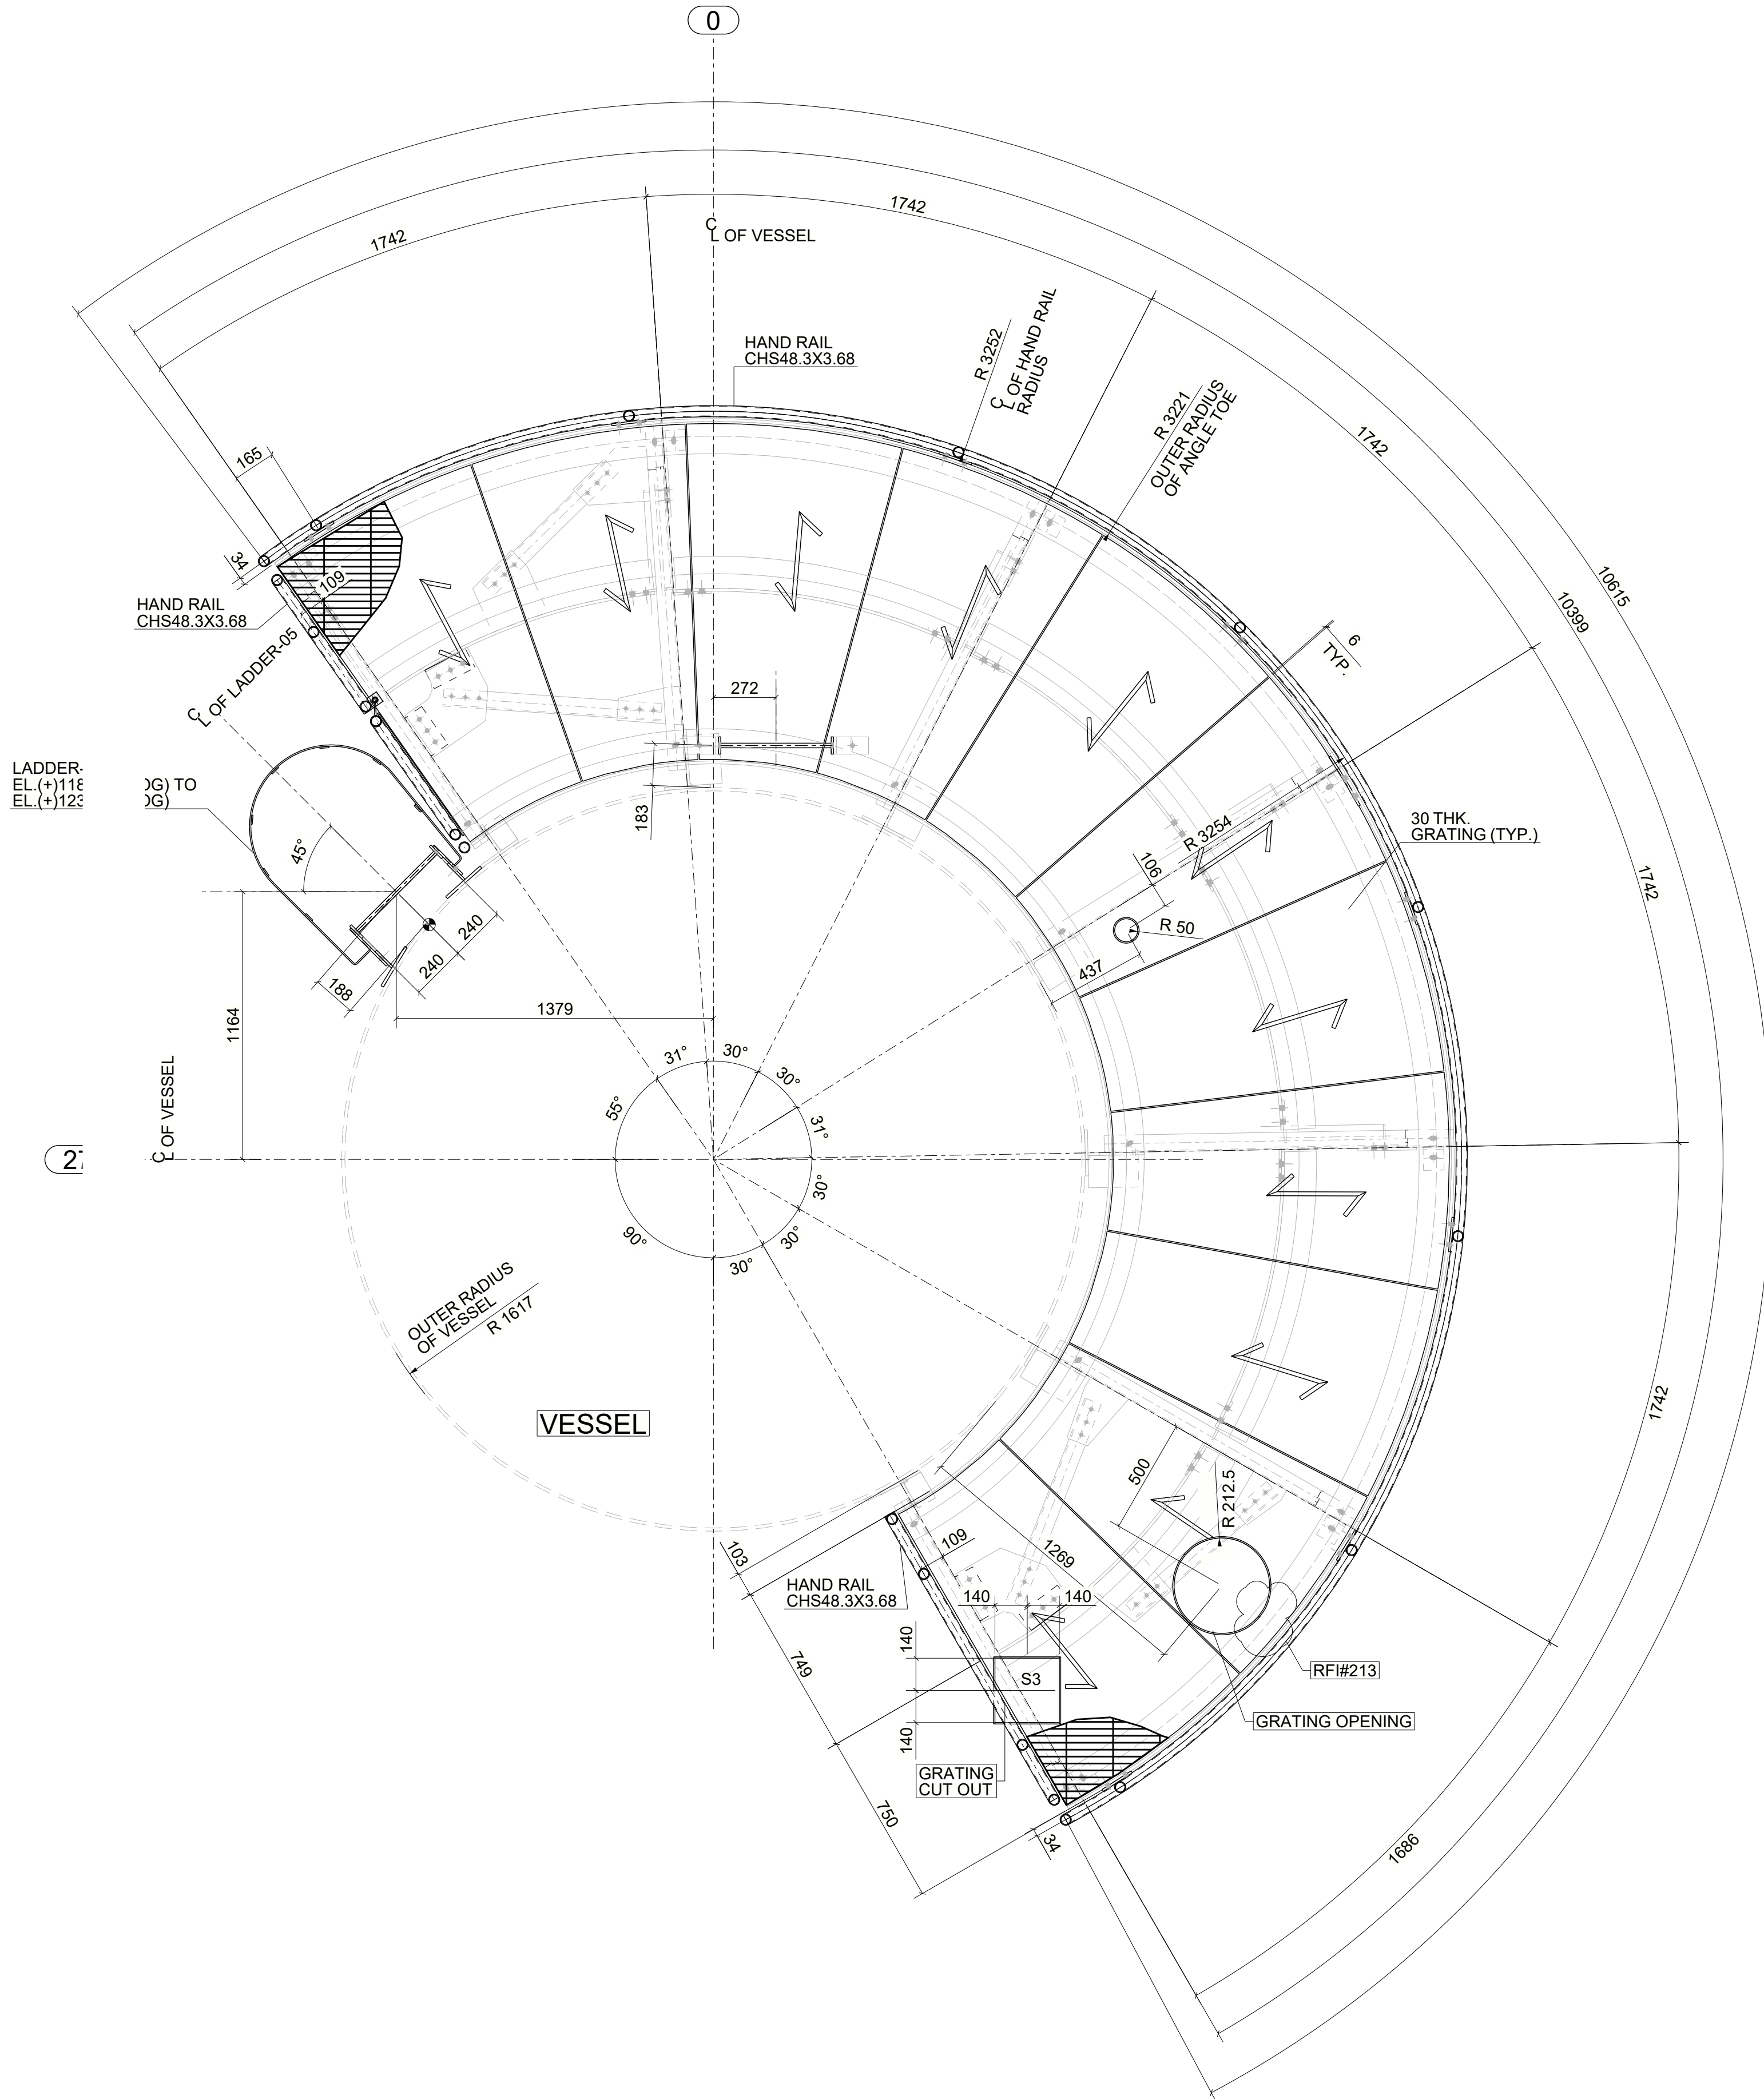

GRATING & HANDRAIL PLAN AT EL.+123.418 (TOG)
ALL PLAN BRACING ARE AT (-50) UNO

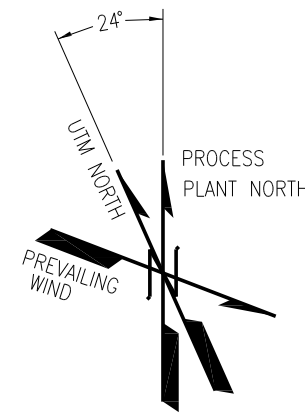

NOTES



1. All dimensions are in millimeters & all elevations are in meters Unless noted otherwise.
2. Grade of structural shall be S275JR complying with BS EN 10025 or Equivalent U.N.O
3. Grade of connection plates shall be S355JR complying with BS EN 10025 or Equivalent U.N.O
3. Handrail units (Including handrails, mid rails & stanchions) shall be in accordance to ASTM A53-Grade B
4. For primary structural members High strength bolts, nuts and washers shall be as per :-
Bolt ASTM A325/A325M or A193-B7/A193M-B7, (20mm dia min).
Heavy Hex Nut ASTM A563/A563M Gr.DH and washer ASTM F436/F436M
5. For secondary members (railing, ladder, purlins and girts etc.)
Standard bolt assemblies shall be as per:-
Bolt ASTM A325M (limited in size to 16mm diameter)
Heavy Hex Nut ASTM A563/A563M Gr.A and Washer ASTM F436
Washer ASTM F436/F436M
6. Bolt, Nuts and Washers shall be hot-dip galvanized in accordance with ASTM A153/A153M or ASTM B695.
7. All bolted connection are bearing type & all bolted joints shall be snug tightened (s/t) U.N.O
8. Minimum weld size shall be 6mm, unless otherwise noted.
9. All structural shall be painted as per specification AD282-732-G-01801

LEGENDS:

1. U.N.O	UNLESS NOTED OTHERWISE
2. U/S BP	UNDERSIDE OF BASE PLATE
3. T.O.S	TOP OF STEEL
4. T.O.G	TOP OF GRATING
5. EX.	EXISTING MEMBER

HOLE DIAMETER SHALL BE AS FOLLOWS U.N.O

BOT DIA (mm)	HOLE DIA
16	18
20	22
22	24
24	27
27	30
30	33
> 36	D+3

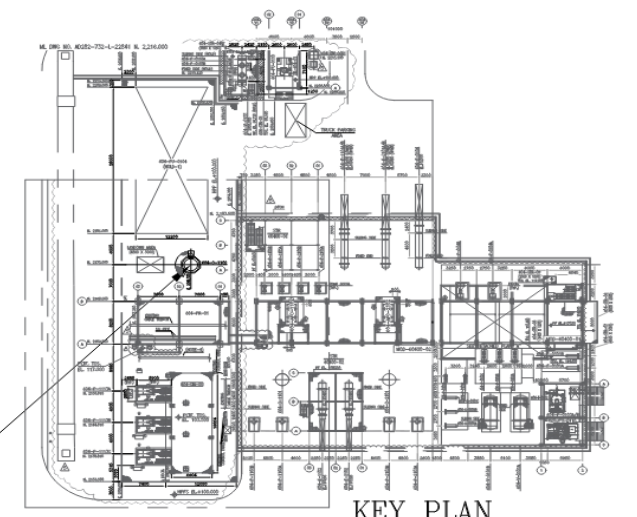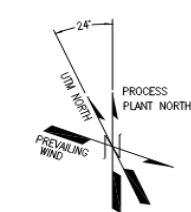

THIS DRAWING

KEY PLAN

REFERENCE DRAWINGS:

Sr. No.	DOC / DRAWING NO.	DOC / DRAWING TITLE
1	AD282-732-C-38068 SHEET - 001 & 002	GENERAL NOTE
2	AD282-732-C-38070 SHEET - 001 & 002	GRATING DETAILS
3	AD282-732-C-38074 SHEET - 001 & 002	STAIR & HANDRAIL
4	AD282-732-C-38075	STANDARD DRAWING LADDER
5	AD282-604-C-33217	BASE PLATE LAYOUT & DETAILS
6	AD282-604-C-33217 & 218 & 219	PLAN, ELEVATION & SECTIONS
7	AD282-604-C-33220 & 33526	PLAN, ELEVATION & SECTIONS



