


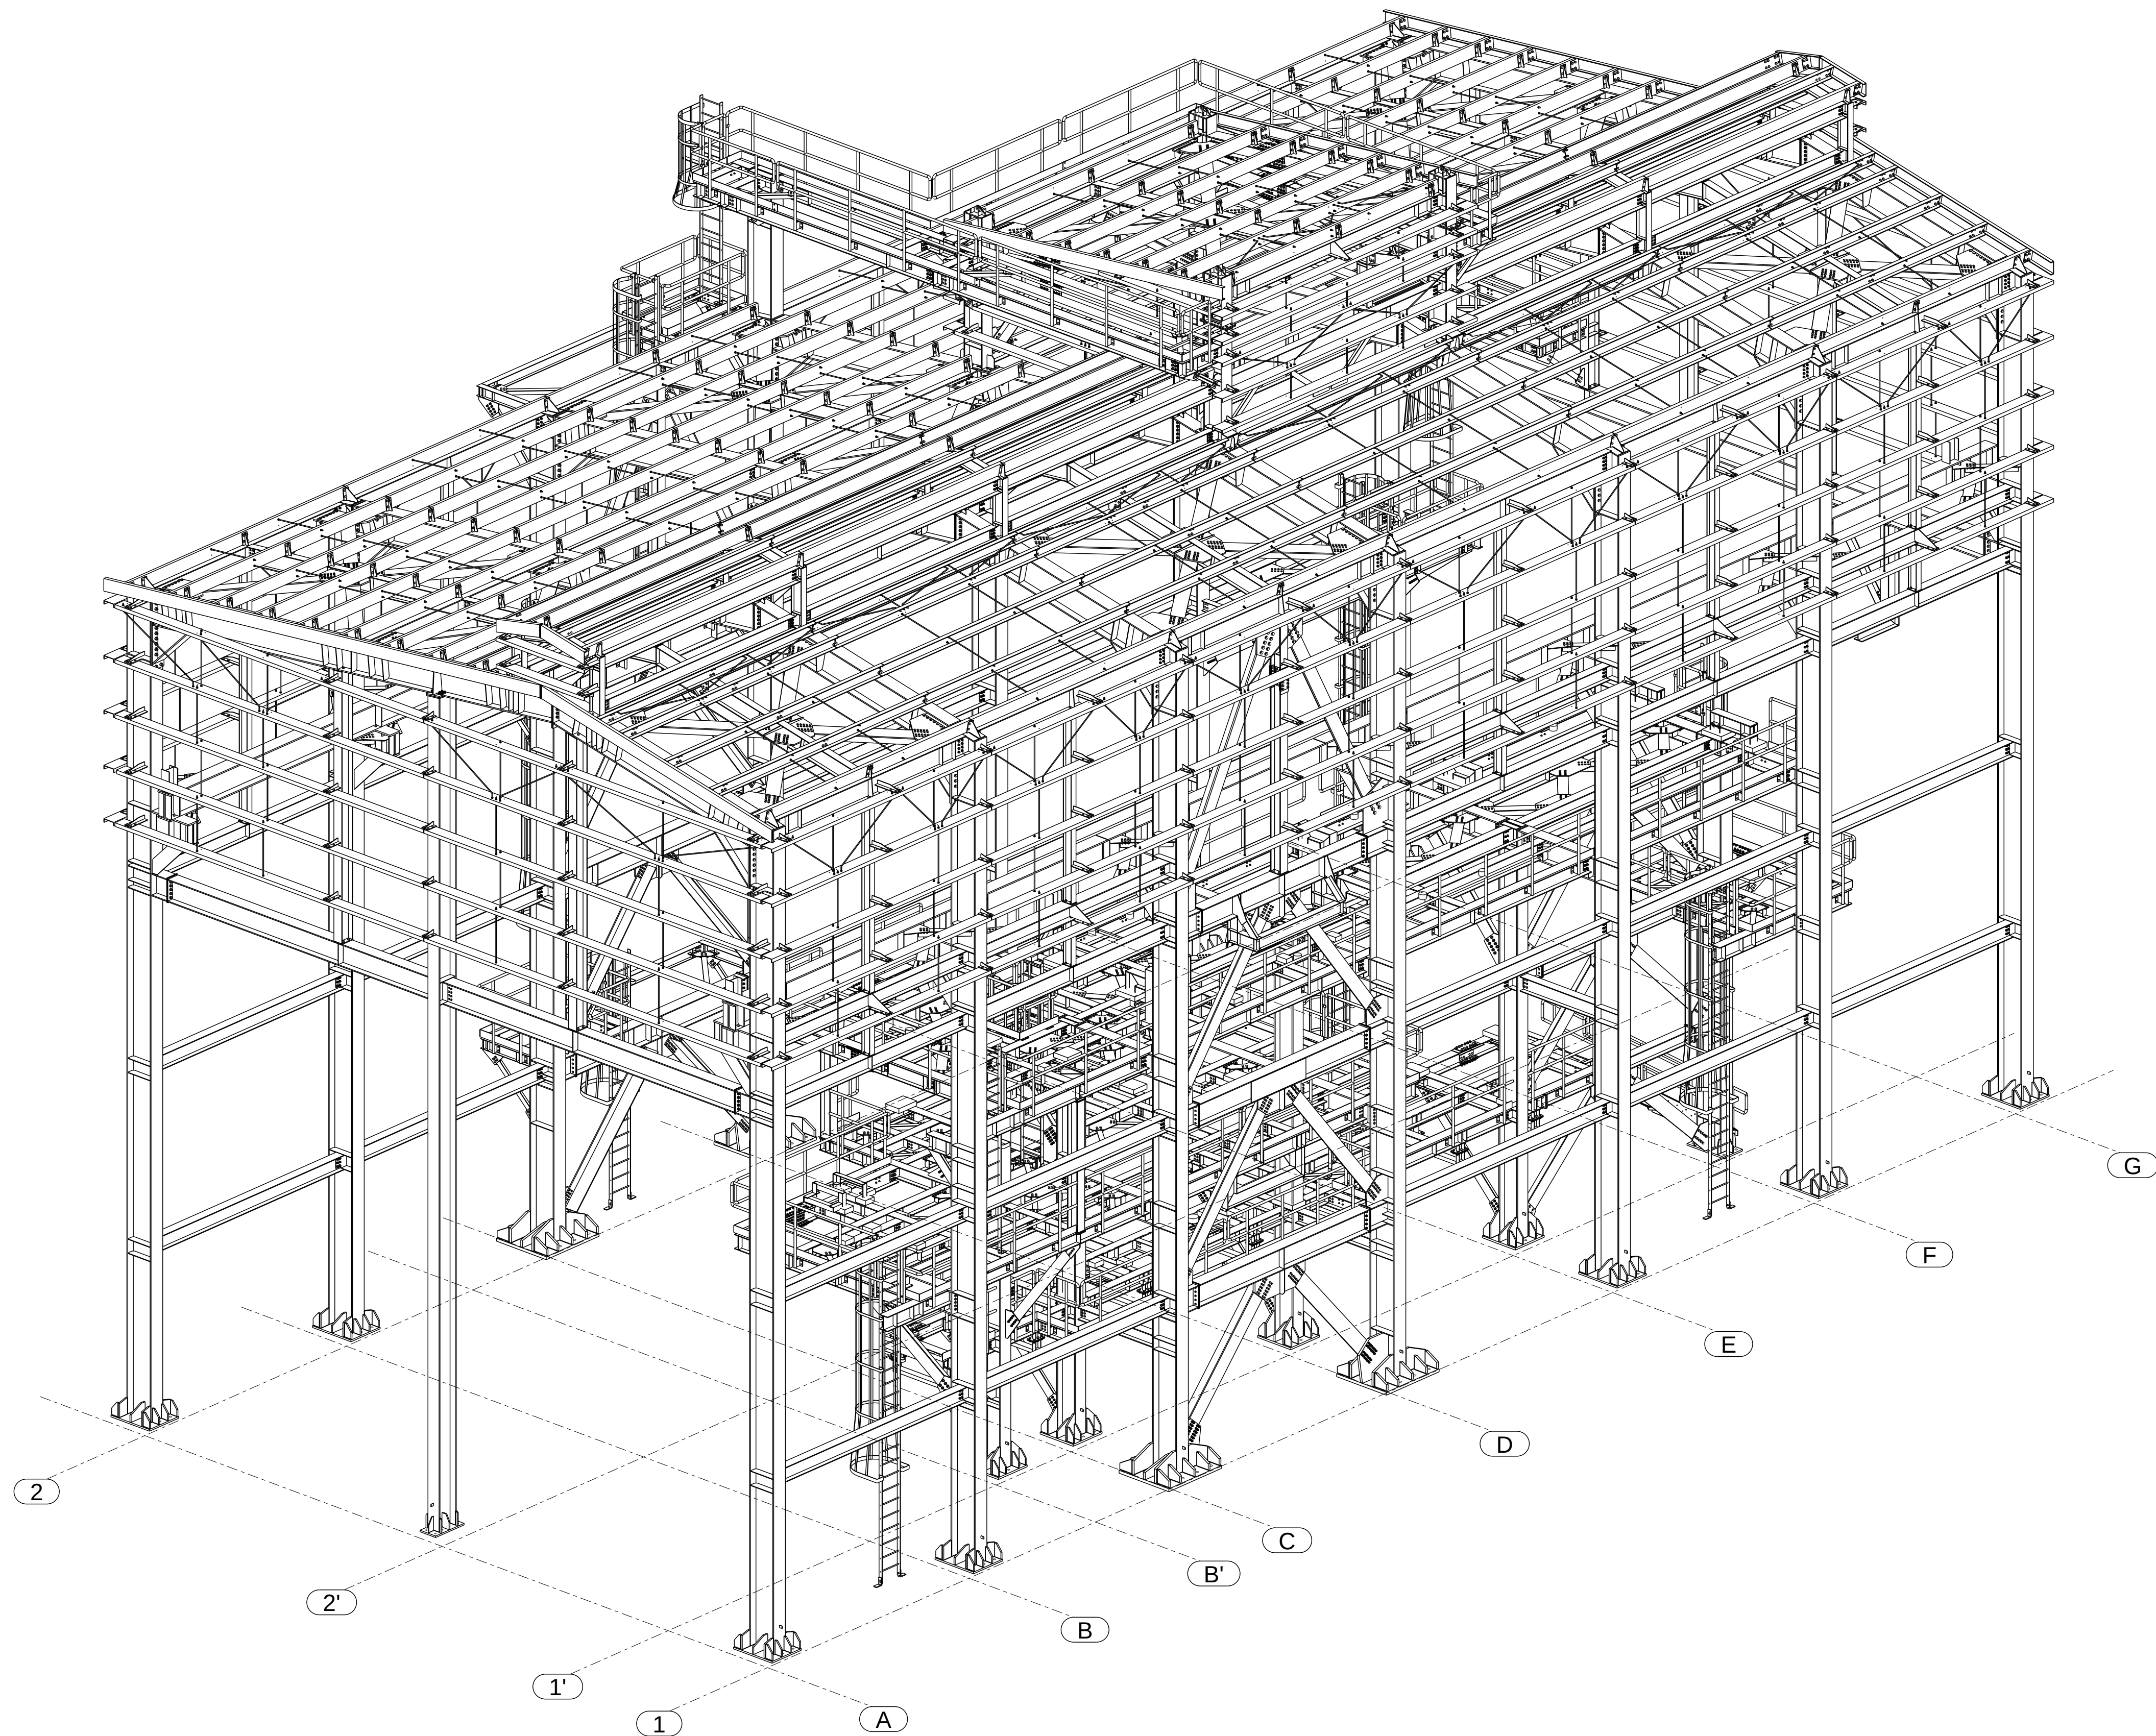

ISOMETRIC VIEW

NOTES


- 1. All dimensions are in millimeters & all elevations are in meters Unless noted otherwise.
- 2. Grade of structural shall be S275JR complying with BS EN 10025 or Equivalent U.N.O
- 3. Grade of connection plates shall be S355JR complying with BS EN 10025 or Equivalent U.N.O
- 3. Handrail units (Including handrails, mid rails & stanchions) shall be in accordance to ASTM A53-Grade B
- 4. For primary structural members High strength bolts, nuts and washers shall be as per :-
Bolt ASTM A325/A325M or A193-B7/A193M-B7, (20mm dia min).
Heavy Hex Nut ASTM A563/A563M Gr.DH and washer ASTM F436/F436M
- 5. Secondary Member (railing, ladder, purlins and girt etc.),
standard bolt grade is ASTM A325M.
Heavy hex nut ASTM A563/563M Gr.A and Washer ASTM F436/F436M
- 6. Bolt, Nuts and Washers shall be hot-dip galvanized in accordance with ASTM A153/A153M or ASTM B695.
- 7. All bolted connection are bearing type & all bolted joints shall be snug tightened (s/t) U.N.O
- 8. Minimum weld size shall be 6mm, unless otherwise noted.
- 9. All structural shall be painted as per specification AD282-732-G-01801
- 10. All the Assembly marks should be prefixed with 2307085-STL-732-01

LEGENDS:

1. U.N.O	UNLESS NOTED OTHERWISE
2. U/S BP	UNDERSIDE OF BASE PLATE
3. T.O.S	TOP OF STEEL
4. T.O.G	TOP OF GRATING
5. EX.	EXISTING MEMBER


HOLE DIAMETER SHALL BE AS FOLLOWS U.N.O

BOLT DIA (mm)	HOLE DIA
16	18
20	22
22	24
24	27
27	30
30	33
> 36	D+3

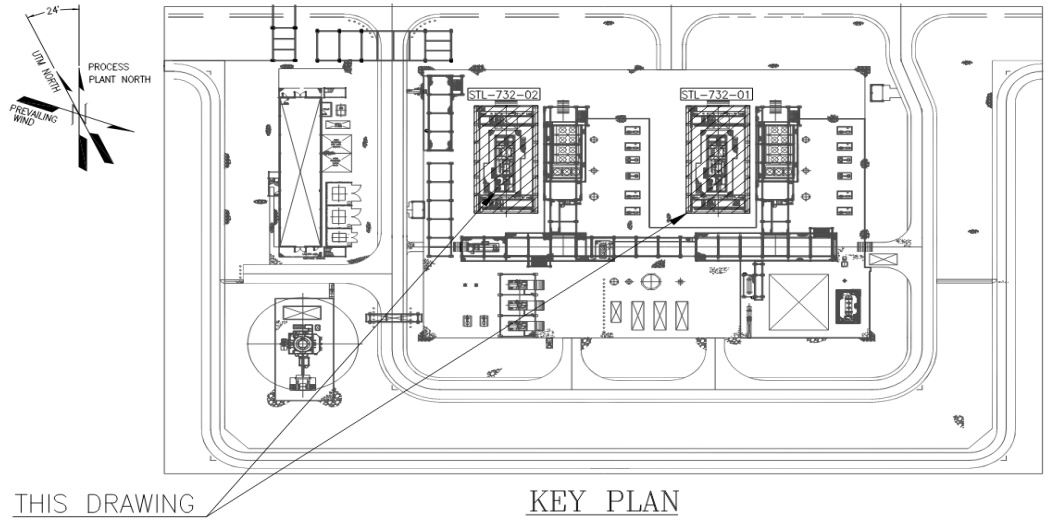

REFERENCE DRAWINGS:

Sr. No.	DOC / DRAWING NO.	DOC / DRAWING TITTLE
1	AD282-732-C-38068 SHEET - 001 & 002	GENERAL NOTE
2	AD282-732-C-38070 SHEET - 001 & 002	GRATING DETAILS
3	AD282-732-C-38074 SHEET - 001 & 002	STAIR & HANDRAIL
4	AD282-732-C-38075	STANDARD DRAWING LADDER
5	AD282-732-C-33188	BASE PLATE LAYOUT & DETAILS
6	AD282-732-C-33189	PLAN, ELEVATION & SECTIONS
7	AD282-732-C-33190	PLAN, ELEVATION & SECTIONS

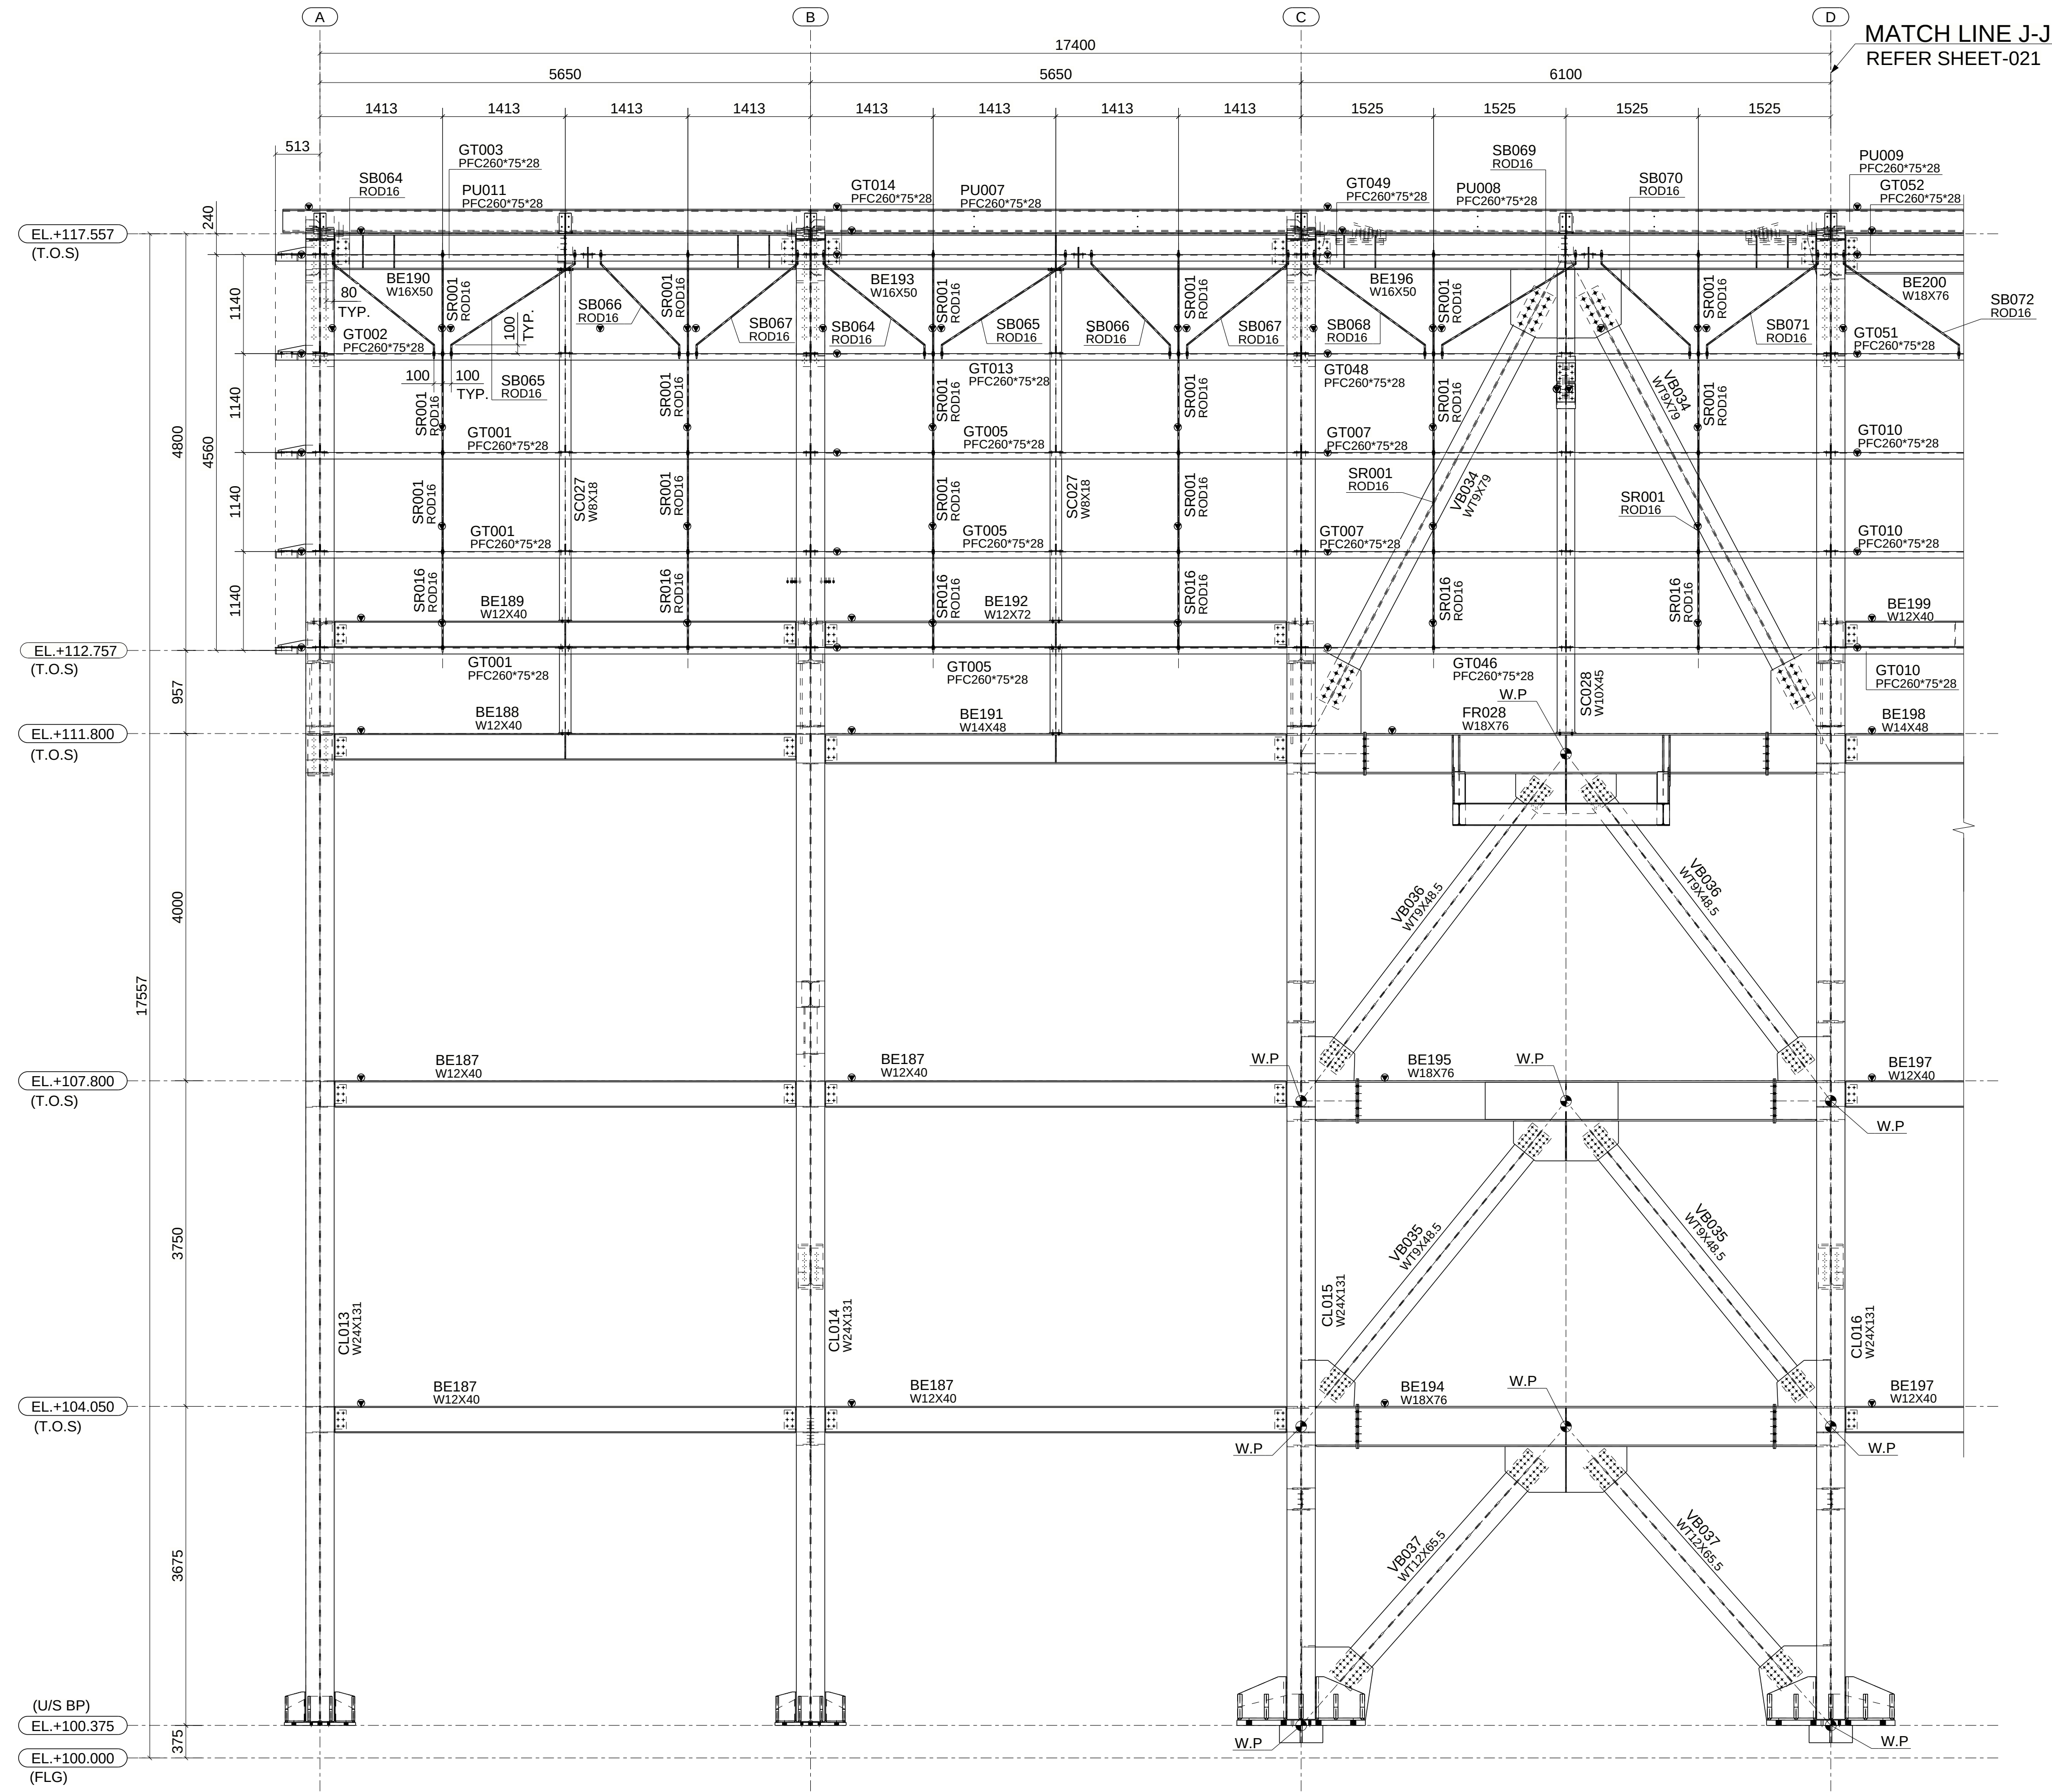

GIRT ELEVATION ALONG GRID-1
(LOOKING TOWARDS WEST)
(GIRT ELEVATION)

NOTES


1. All dimensions are in millimeters & all elevations are in meters Unless noted otherwise.
2. Grade of structural shall be S275JR complying with BS EN 10025 or Equivalent U.N.O
3. Grade of connection plates shall be S355JR complying with BS EN 10025 or Equivalent U.N.O
4. Handrail units (Including handrails, mid rails & stanchions) shall be in accordance to ASTM A53-Grade B
5. For primary structural members High strength bolts, nuts and washers shall be as per :- Bolt ASTM A325/A325M or A193-B7/A193M-B7, (20mm dia min), Heavy Hex Nut ASTM A563/A563M Gr.DH and washer ASTM F436/F436M
6. Secondary Member (railing, ladder, putlins and girt etc.), standard bolt grade is ASTM A325M. Heavy hex nut ASTM A563/563M Gr.A and Washer ASTM F436/F436M
7. Bolt, Nuts and Washers shall be hot-dip galvanized in accordance with ASTM A153/A153M or ASTM B695.
8. All bolted connection are bearing type & all bolted joints shall be snug tightened (s/t) U.N.O
9. Minimum weld size shall be 6mm, unless otherwise noted.
10. All structural shall be painted as per specification AD282-732-G-01801
11. All the Assembly marks should be prefixed with 2307085-STL-732-01

LEGENDS:

1. U.N.O UNLESS NOTED OTHERWISE
2. U/S BP UNDERSIDE OF BASE PLATE
3. T.O.S TOP OF STEEL
4. T.O.G TOP OF GRATING
5. EX. EXISTING MEMBER


HOLE DIAMETER SHALL BE AS FOLLOWS U.N.O

BOLT DIA (mm)	HOLE DIA
16	18
20	22
22	24
24	27
27	30
30	33
>36	D+3

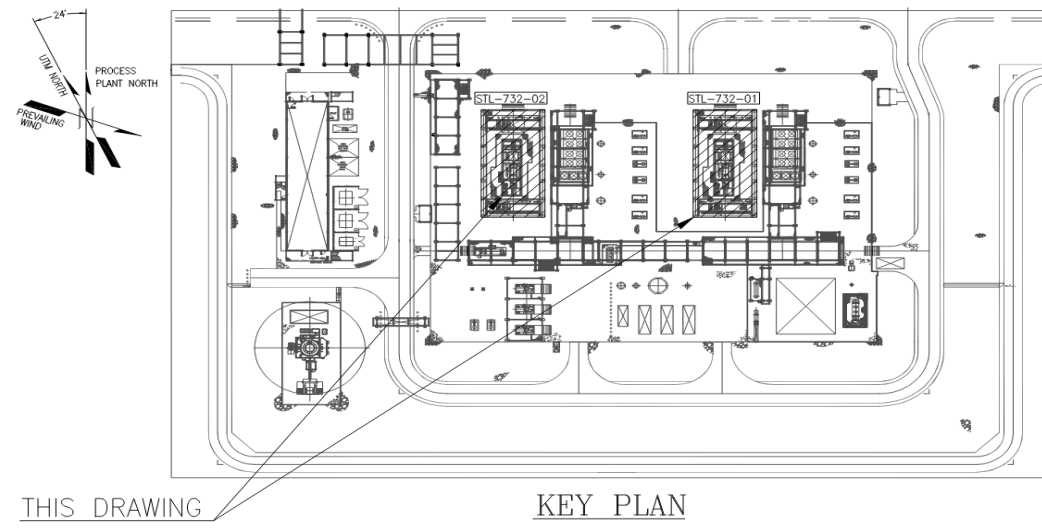

REFERENCE DRAWINGS:

Sr. No.	DOC / DRAWING NO.	DOC / DRAWING TITTLE
1	AD282-732-C-38068 SHEET - 001 & 002	GENERAL NOTE
2	AD282-732-C-38070 SHEET - 001 & 002	GRATING DETAILS
3	AD282-732-C-38074 SHEET - 001 & 002	STAIR & HANDRAIL
4	AD282-732-C-38075	STANDARD DRAWING LADDER
5	AD282-732-C-33188	BASE PLATE LAYOUT & DETAILS
6	AD282-732-C-33189	PLAN, ELEVATION & SECTIONS
7	AD282-732-C-33190	PLAN, ELEVATION & SECTIONS

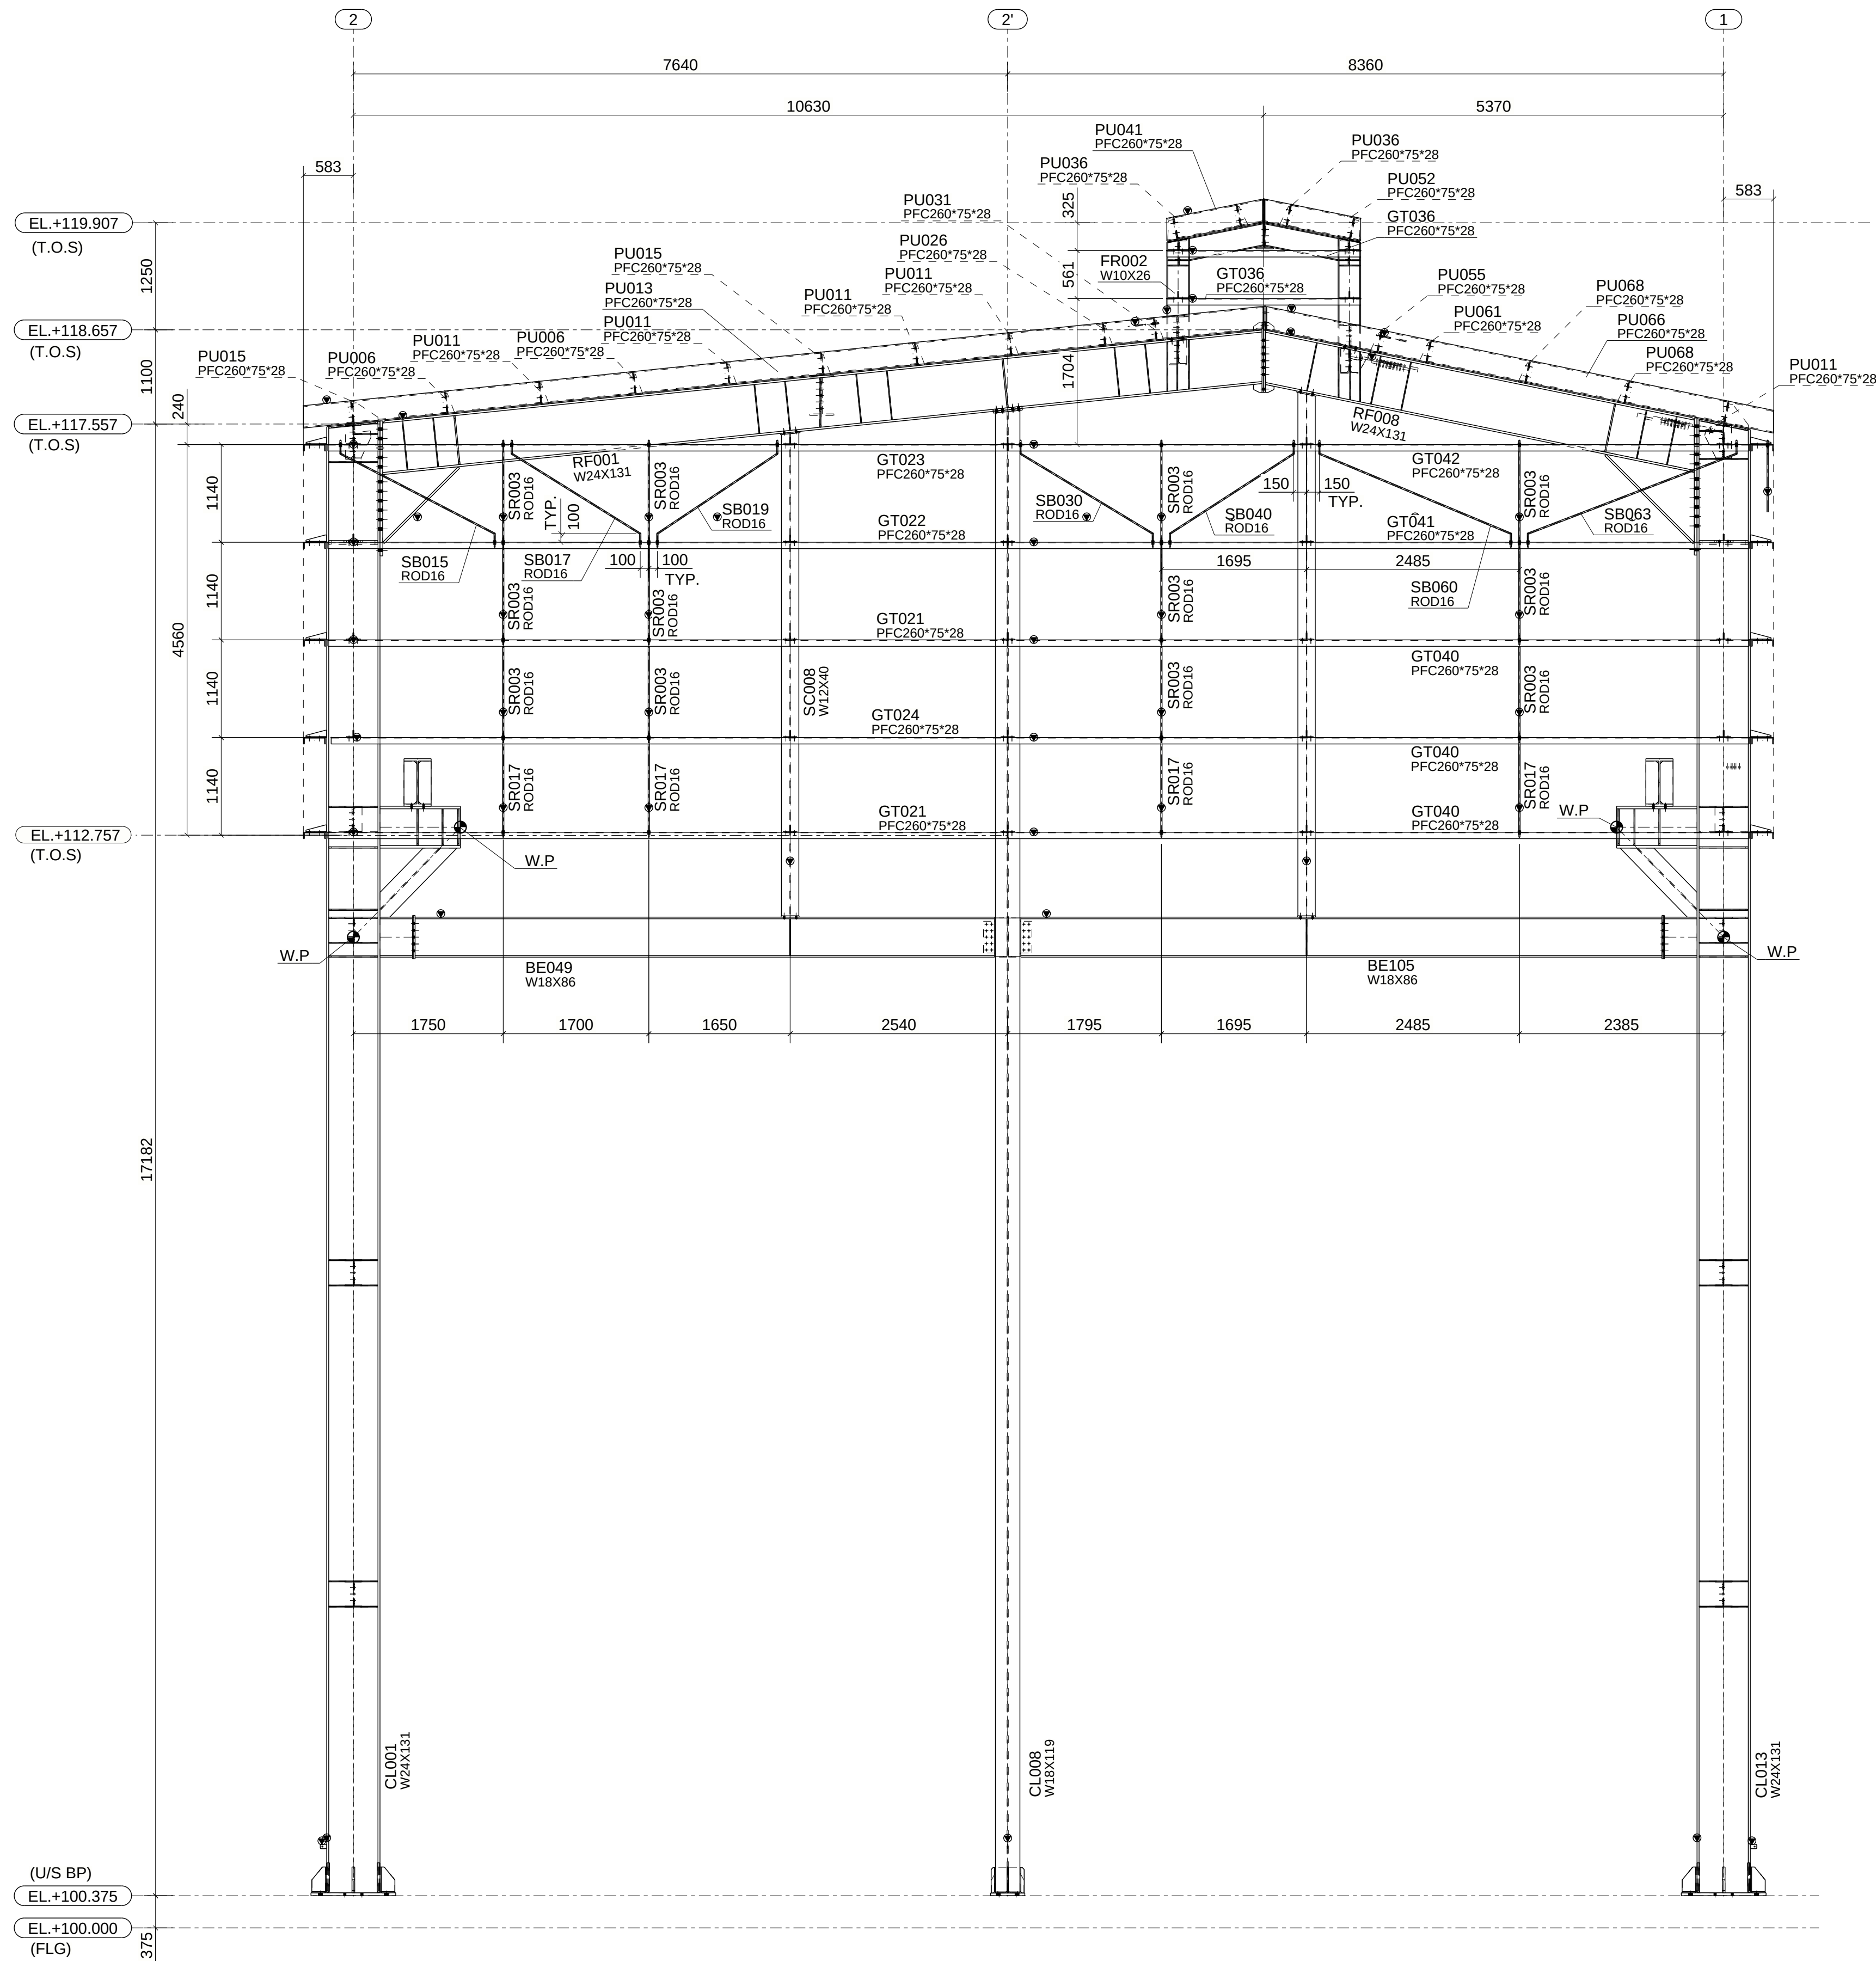

ELEVATION ALONG GRID-A
(LOOKING TOWARDS NORTH)
(GIRTS & PURLINS)

NOTES


- All dimensions are in millimeters & all elevations are in meters Unless noted otherwise.
- Grade of structural shall be S275JR complying with BS EN 10025 or Equivalent U.N.O
- Grade of connection plates shall be S355JR complying with BS EN 10025 or Equivalent U.N.O
- Handrail units (Including handrails, mid rails & stanchions) shall be in accordance to ASTM A53-Grade B
- For primary structural members High strength bolts, nuts and washers shall be as per :-
Bolt ASTM A325/A325M or A193-B7/A193M-B7, (20mm dia min).
Heavy Hex Nut ASTM A563/A563M Gr.DH and washer ASTM F436/F436M
- Secondary Member (railing, ladder, purlins and girt etc.),
standard bolt grade is ASTM A325M.
Heavy hex nut ASTM A563/563M Gr.A and Washer ASTM F436/F436M
- Bolt, Nuts and Washers shall be hot-dip galvanized
in accordance with ASTM A153/A153M or ASTM B695.
- All bolted connection are bearing type & all bolted joints shall be
snug tightened (s/t) U.N.O
- Minimum weld size shall be 6mm, unless otherwise noted.
- All structural shall be painted as per specification AD282-732-G-01801
- All the Assembly marks should be prefixed with 2307085-STL-732-01

LEGENDS:

- U.N.O UNLESS NOTED OTHERWISE
- U/S BP UNDERSIDE OF BASE PLATE
- T.O.S TOP OF STEEL
- T.O.G TOP OF GRATING
- EX. EXISTING MEMBER

HOLE DIAMETER SHALL BE AS FOLLOWS U.N.O

BOLT DIA (mm)	HOLE DIA
16	18
20	22
22	24
24	27
27	30
30	33
>36	D+3

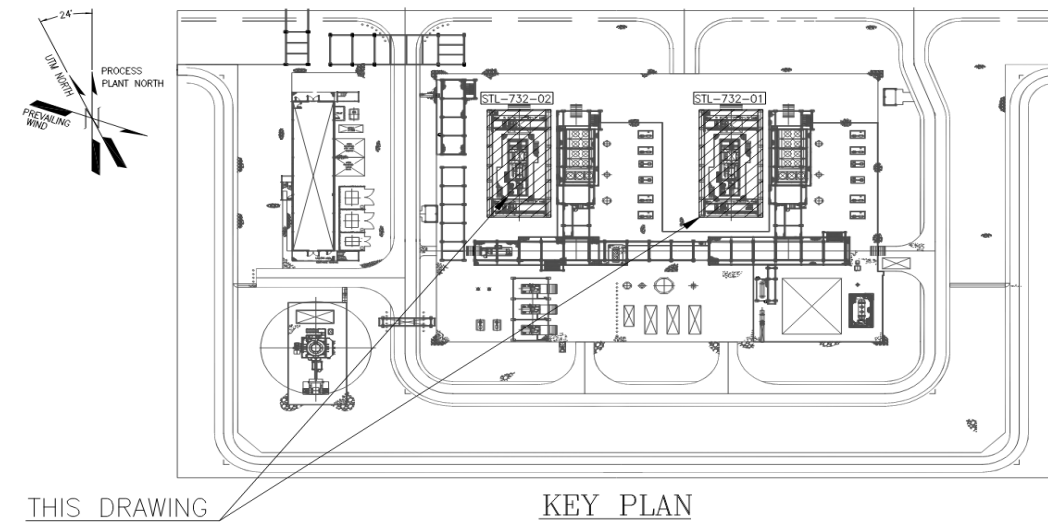

REFERENCE DRAWINGS:


Sr. No.	DOC / DRAWING NO.	DOC / DRAWING TITTLE
1	AD282-732-C-38068 SHEET - 001 & 002	GENERAL NOTE
2	AD282-732-C-38070 SHEET - 001 & 002	GRATING DETAILS
3	AD282-732-C-38074 SHEET - 001 & 002	STAIR & HANDRAIL
4	AD282-732-C-38075	STANDARD DRAWING LADDER
5	AD282-732-C-33188	BASE PLATE LAYOUT & DETAILS
6	AD282-732-C-33189	PLAN, ELEVATION & SECTIONS
7	AD282-732-C-33190	PLAN, ELEVATION & SECTIONS



1. All dimensions are in millimeters & all elevations are in meters Unless noted otherwise.
2. Grade of structural shall be S275JR complying with BS EN 10025 or Equivalent U.N.O
Grade of connection plates shall be S355JR complying with BS EN 10025 or Equivalent U.N.O
3. Handrail units (Including handrails, mid rails & stanchions) shall be in accordance to ASTM A53-Grade B
4. For primary structural members High strength bolts, nuts and washers shall be as per :-
Bolt ASTM A325/A325M or A193-B7/A193M-B7, (20mm dia min).
Heavy Hex Nut ASTM A563/A563M Gr.DH and washer ASTM F436/F436M
5. Secondary Member (railing, ladder, purfins and girt etc.),
standard bolt grade is ASTM A325M.
Heavy hex nut ASTM A563/563M Gr.A and Washer ASTM F436/F436M
6. Bolt, Nuts and Washers shall be hot-dip galvanized
in accordance with ASTM A153/A153M or ASTM B695.
7. All bolted connection are bearing type & all bolted joints shall be
snug tightened (st) U.N.O
8. Minimum weld size shall be 6mm, unless otherwise noted.
9. All structural shall be painted as per specification AD282-732-G-01801
10. All the Assembly marks should be prefixed with 2307085-STL-732-01

1. U.N.O	UNLESS NOTED OTHERWISE
2. U/S BP	UNDERSIDE OF BASE PLATE
3. T.O.S	TOP OF STEEL
4. T.O.G	TOP OF GRATING
5. EX.	EXISTING MEMBER

BOLT DIA (mm)	HOLE DIA
16	18
20	22
22	24
24	27
27	30
30	33
> 36	D+3

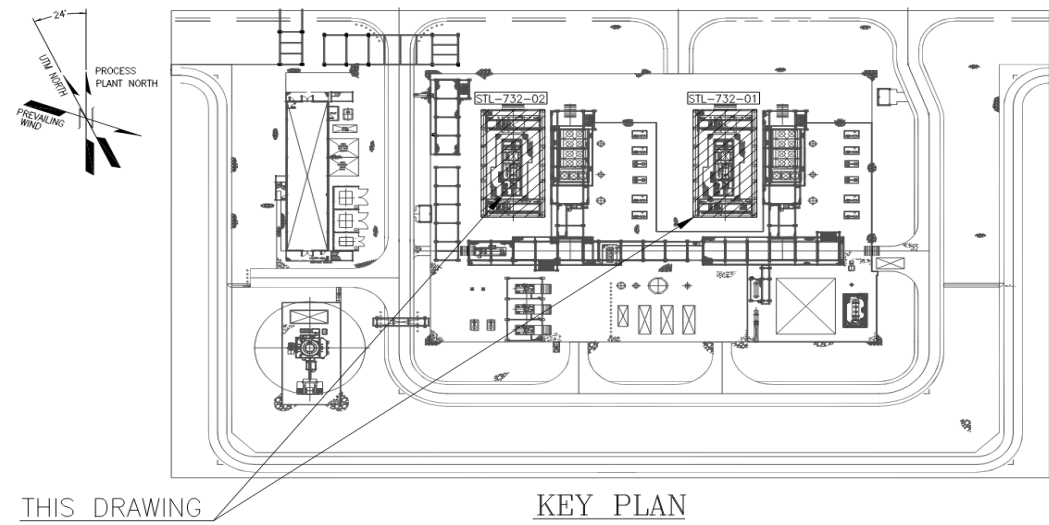

Sr. No.	DOC / DRAWING NO.	DOC / DRAWING TITTLE
1	AD282-732-C-38068 SHEET - 001 & 002	GENERAL NOTE
2	AD282-732-C-38070 SHEET - 001 & 002	GRATING DETAILS
3	AD282-732-C-38074 SHEET - 001 & 002	STAIR & HANDRAIL
4	AD282-732-C-38075	STANDARD DRAWING LADDER
5	AD282-732-C-33188	BASE PLATE LAYOUT & DETAILS
6	AD282-732-C-33189	PLAN, ELEVATION & SECTIONS
7	AD282-732-C-33190	PLAN, ELEVATION & SECTIONS