




GRID LOCATION	
EL +120.000	732/07/732E

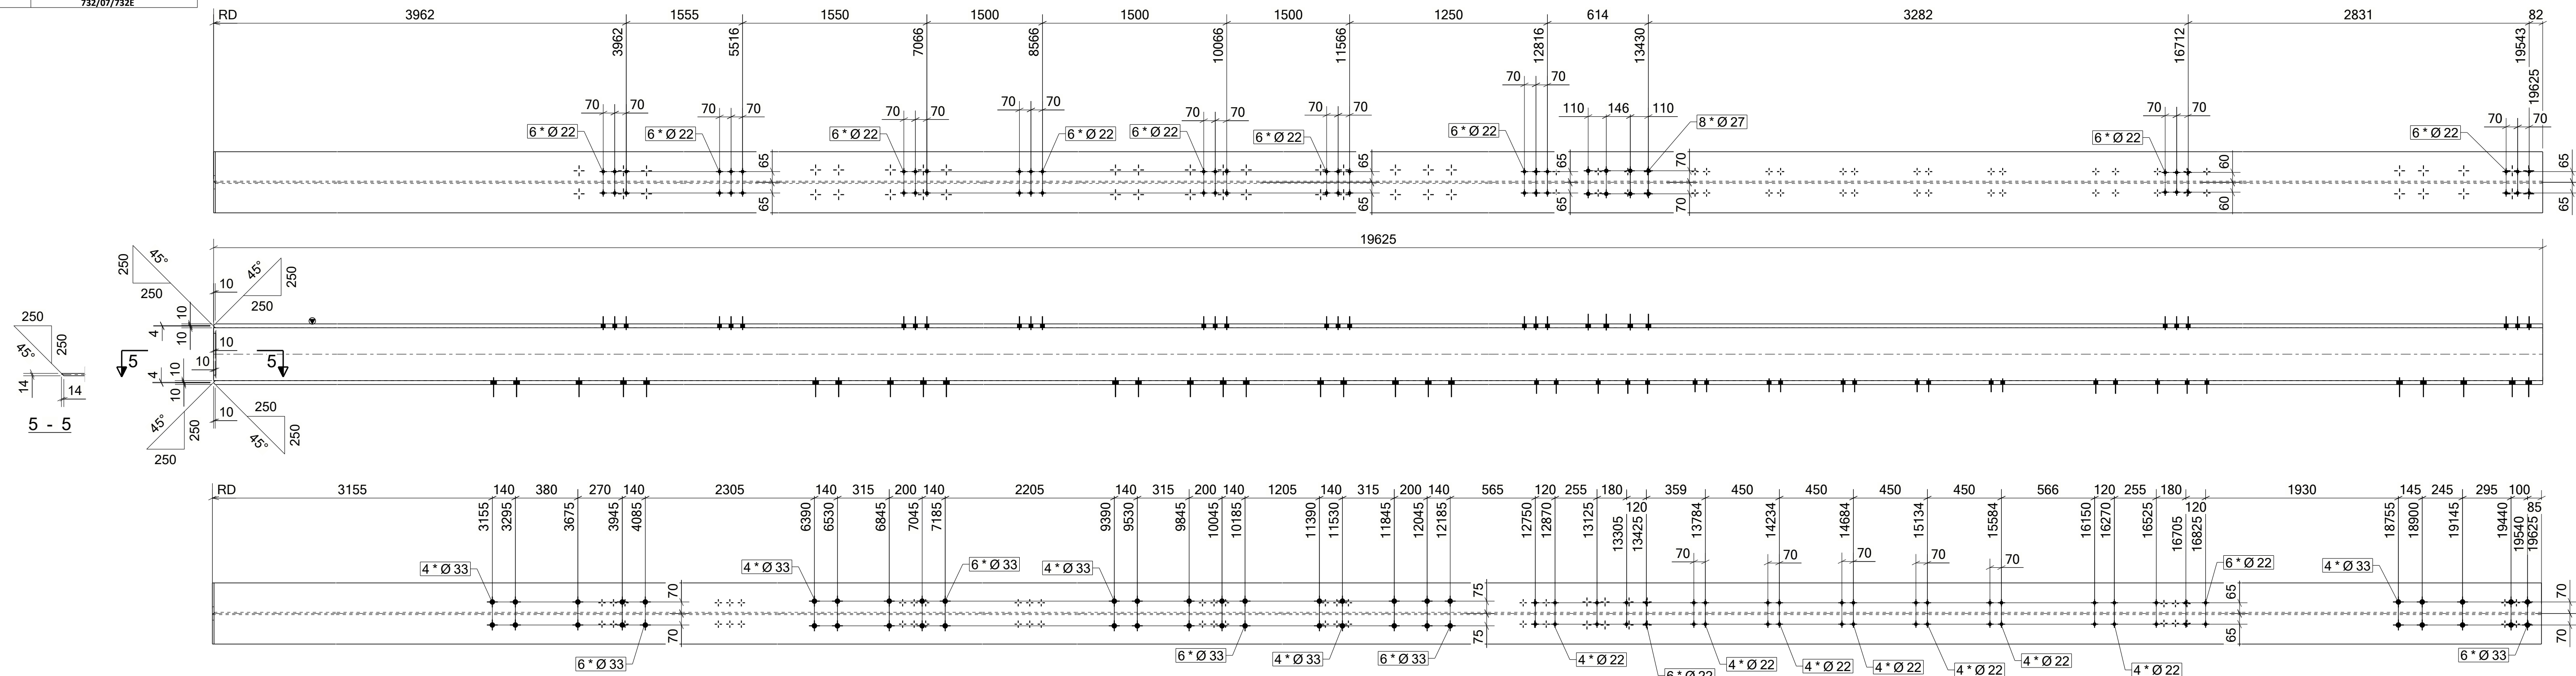

DETAIL OF CL001

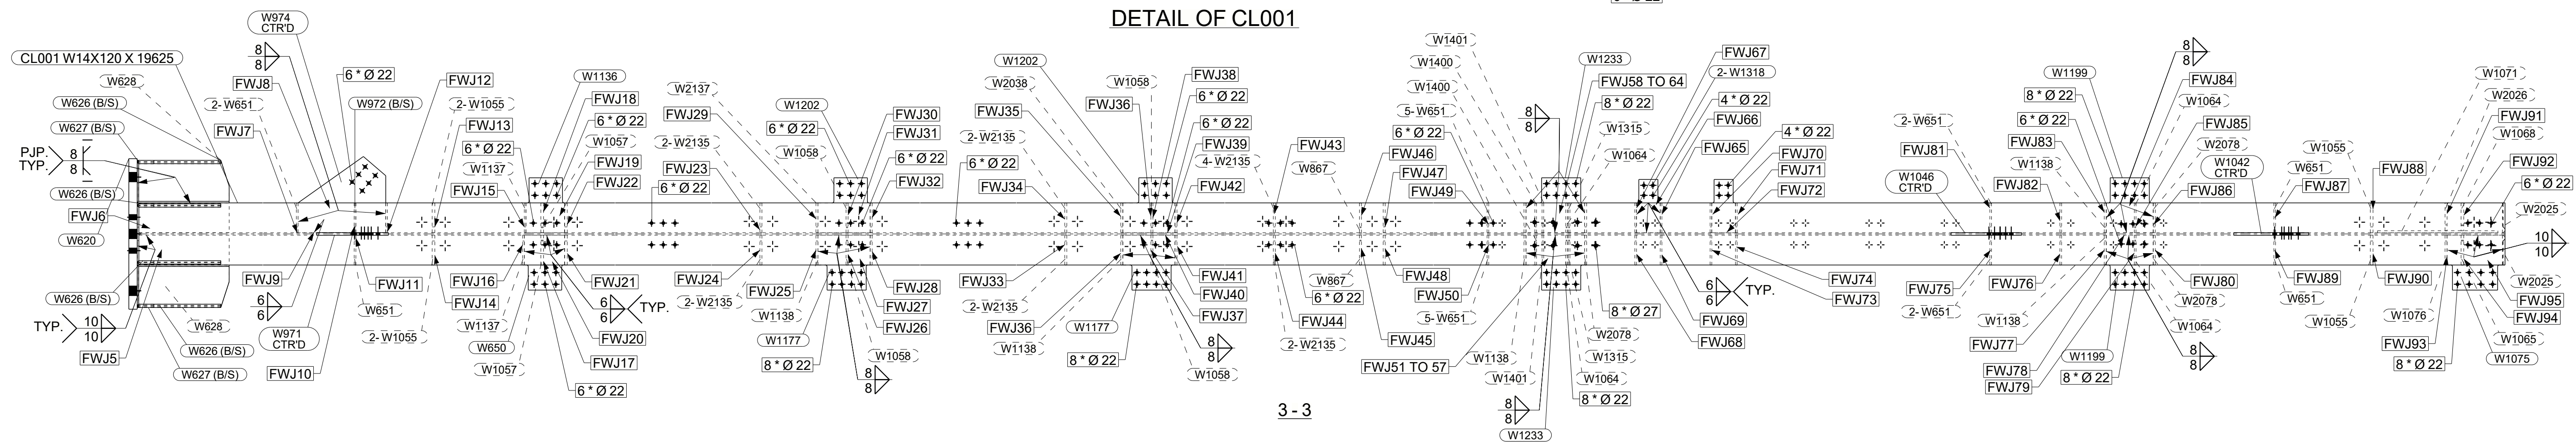

3 - 3

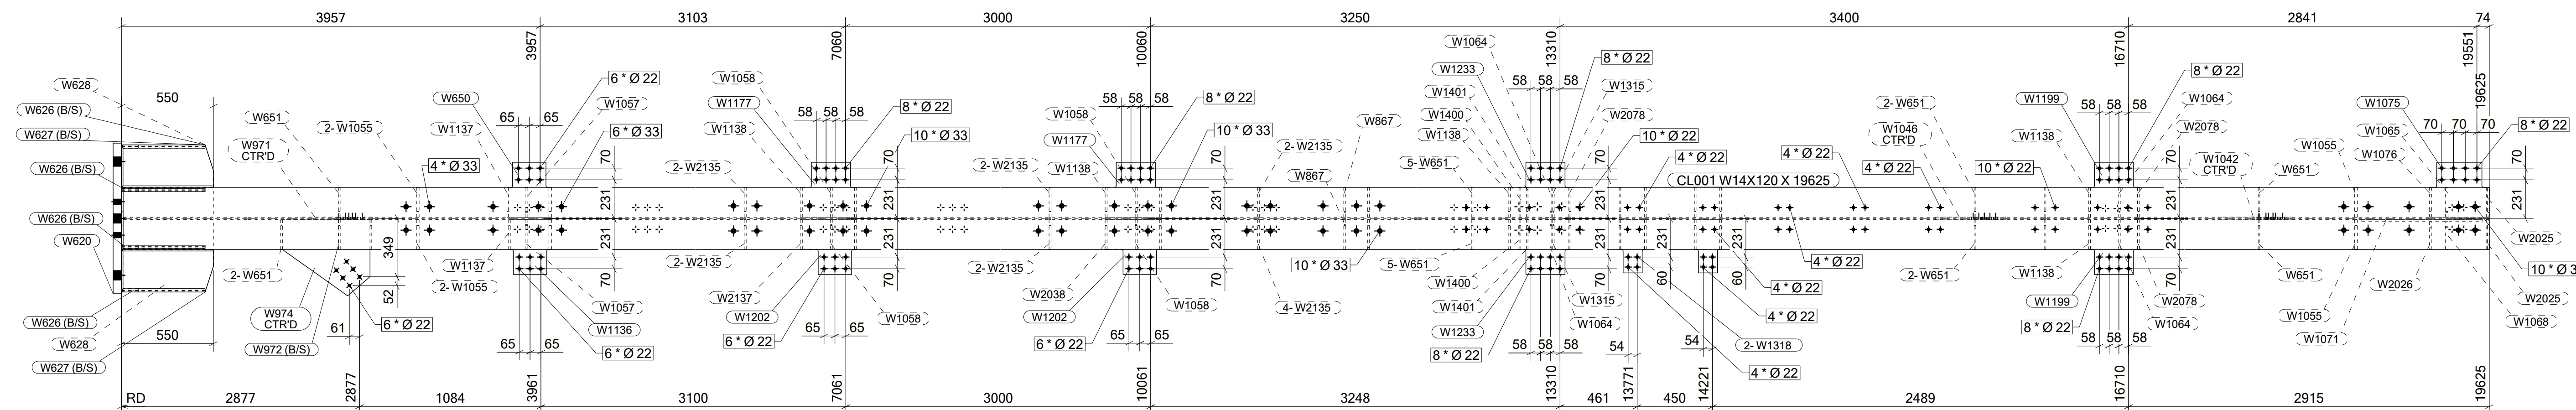


4 - 4

WORK THIS SHEET WITH 2307033-732-PR-10-CL001

GA & IFC DRAWINGS REFERENCE	REV.
AD282-732-C-33158-61	6
AD282-732-C-33170-73,33539	6
AD282-732-C-34311	2
AD282-732-C-34274	2

NOTES :









































- 1-ALL DIMENSIONS ARE GIVEN IN MILLIMETERS (U.N.O.).
- 2-  DENOTES ASSEMBLY ORIENTATION MARK.
- 3-DON'T SCALE THE DRAWING. FOLLOW THE WRITTEN DIMENSIONS.
- 4- FINISH AS PER PROJECT SPEC.
- 5- STRUCTURAL STEELWORK SHALL BE IN ACCORDANCE WITH PROJECT SPECIFICATIONS AD282-732-6-03520 & AD282-732-6-03527
- 6-WHEREVER THERE IS NO ACCESS FOR FILLET WELDING TO BE REPLACED BY FULL PENETRATION BUTT WELDING
- 7-FOR CIP WELD MARKED LOCATIONS FOLLOW THIS DETAIL

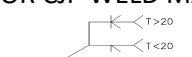

8-ALL WELDS TO BE 6mm FILLET WELD U.N.O.

SPECIAL CATEGORY*

FW-J1 TO J100
PJP-J1 TO J 21

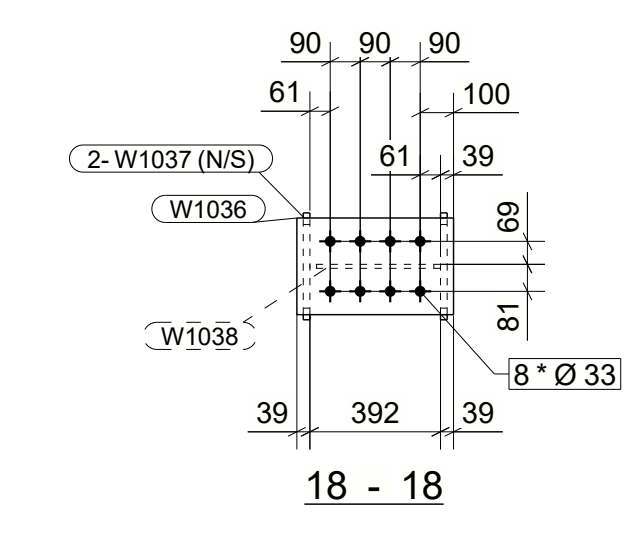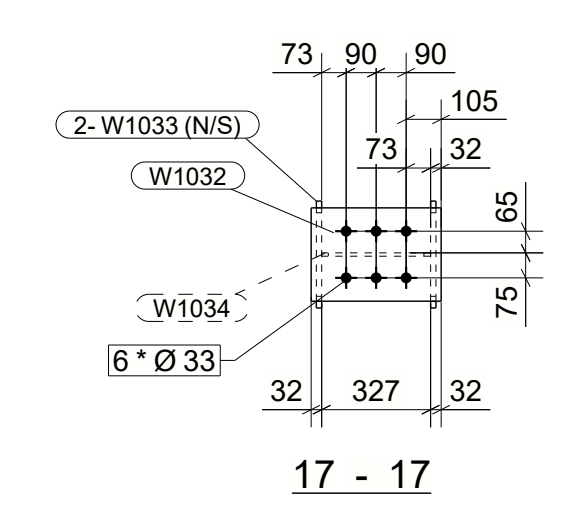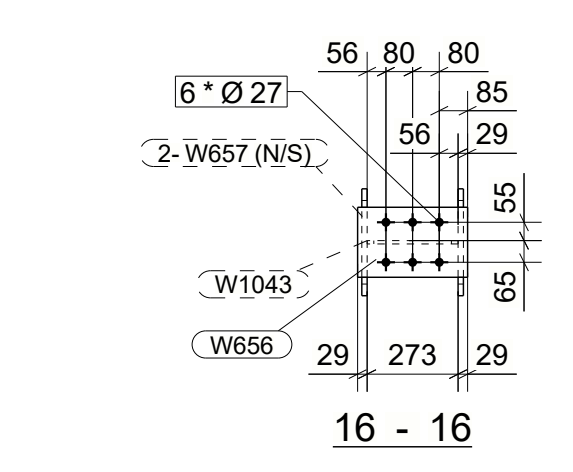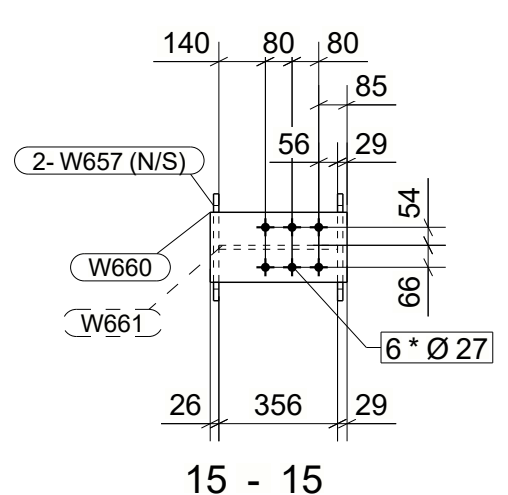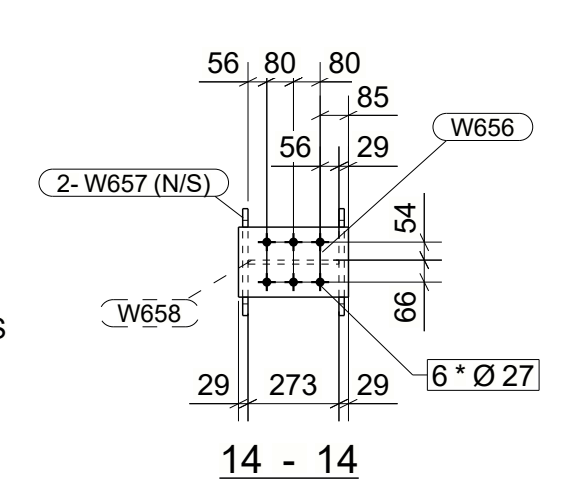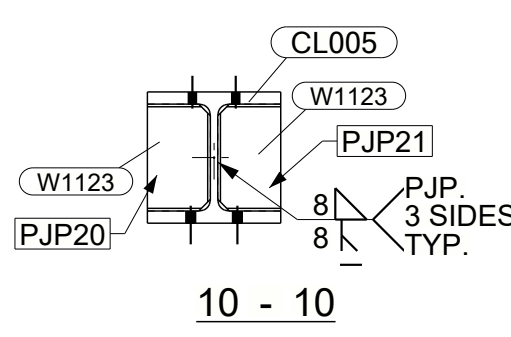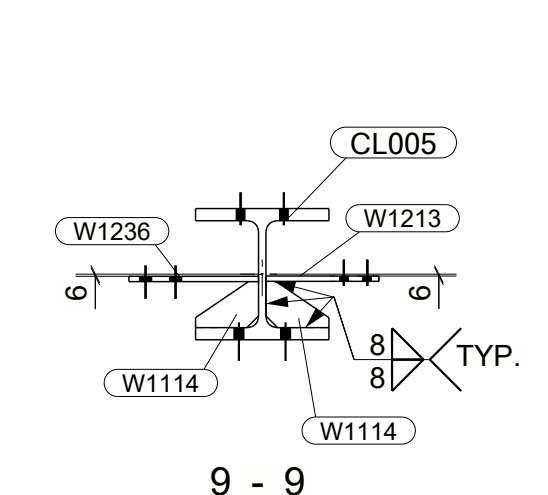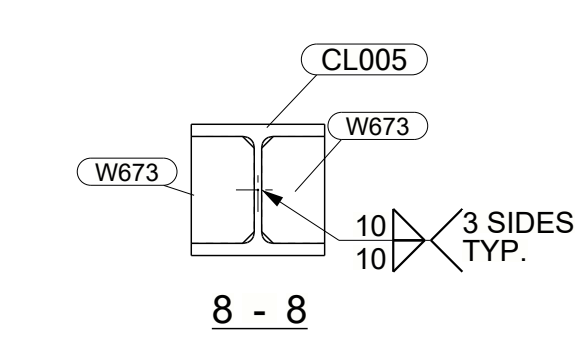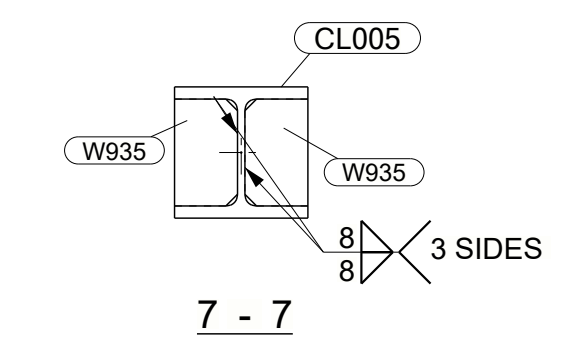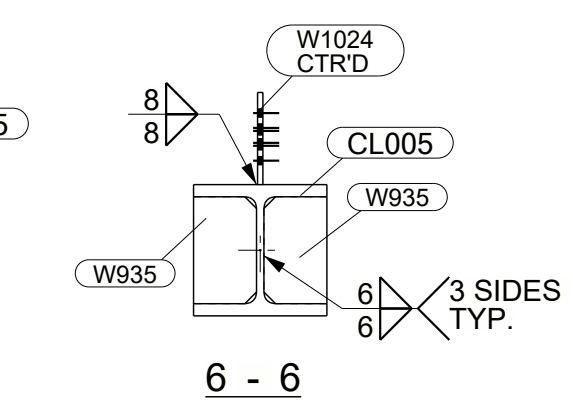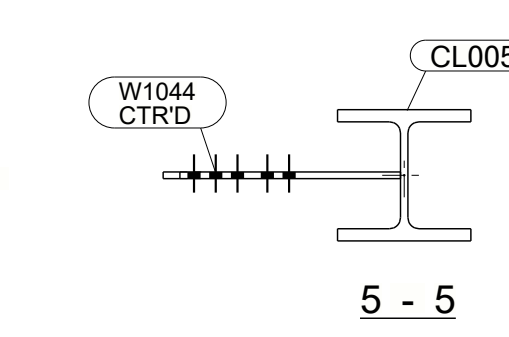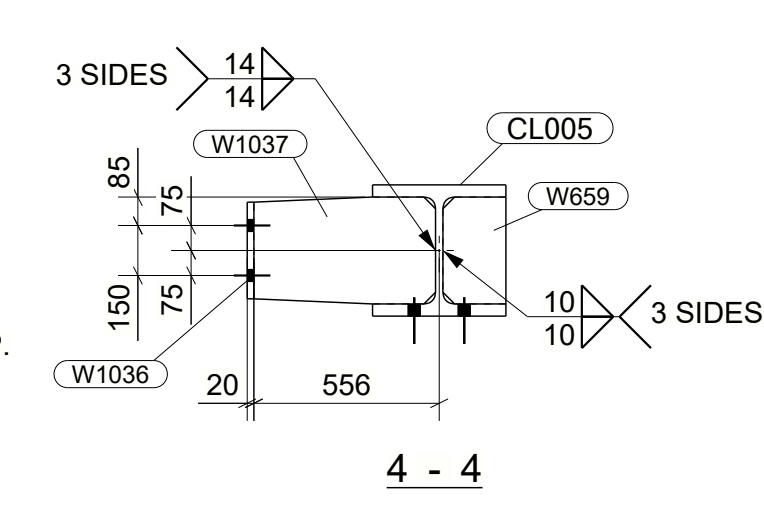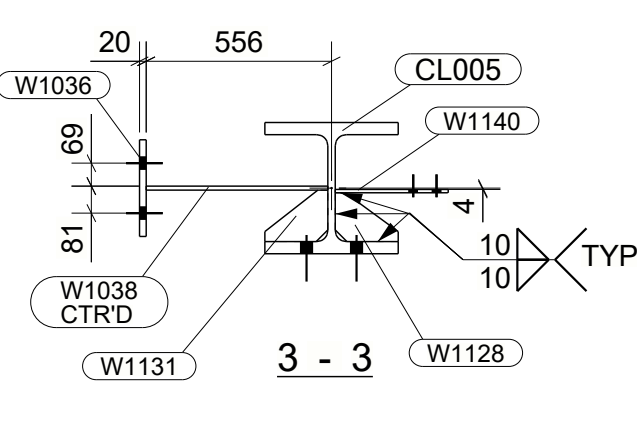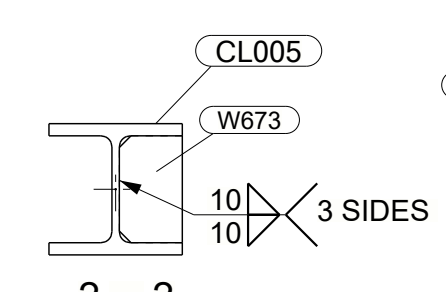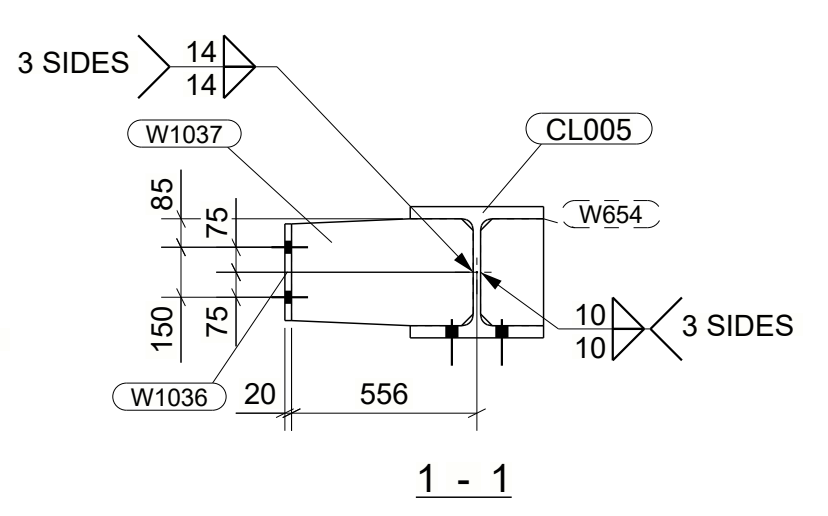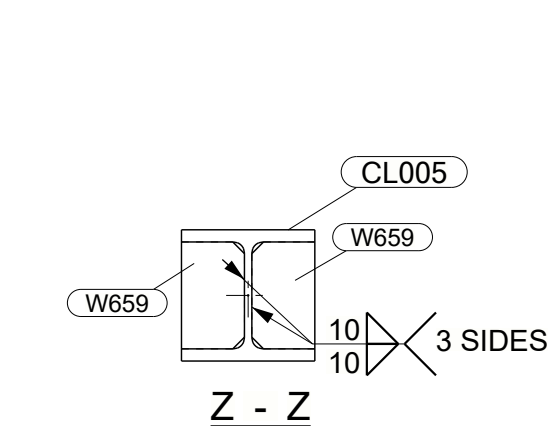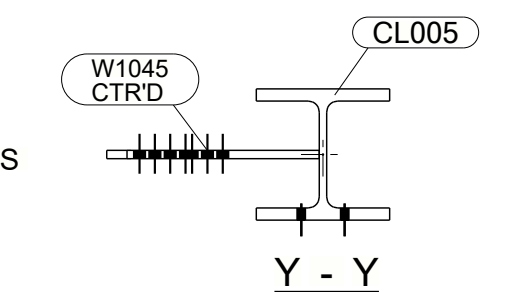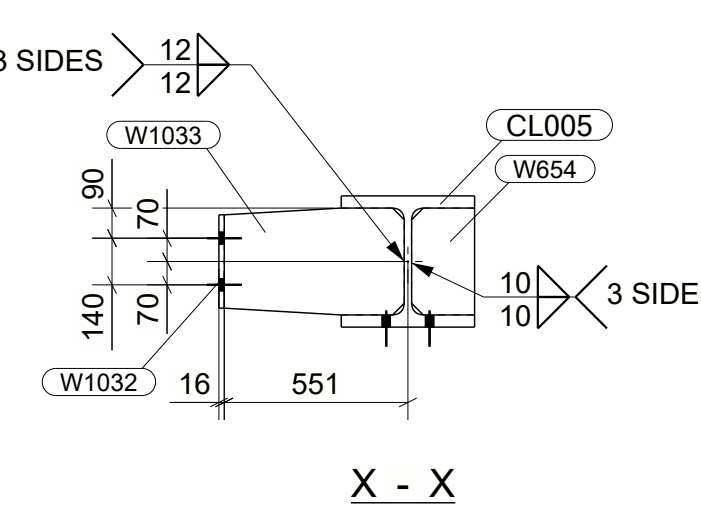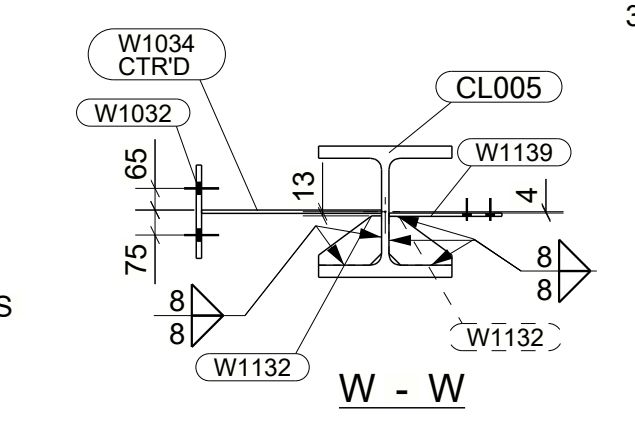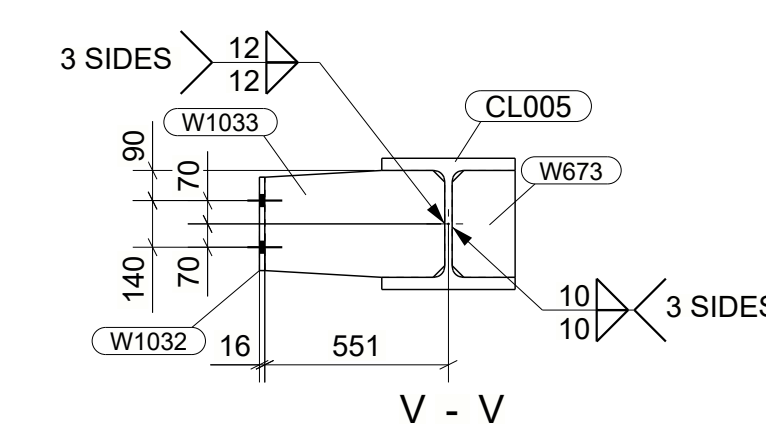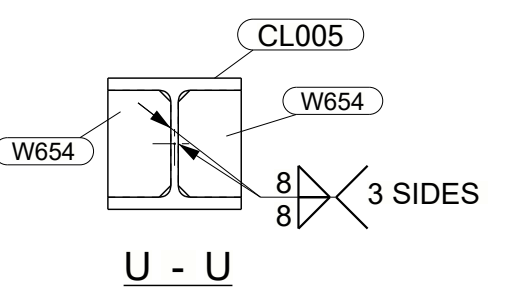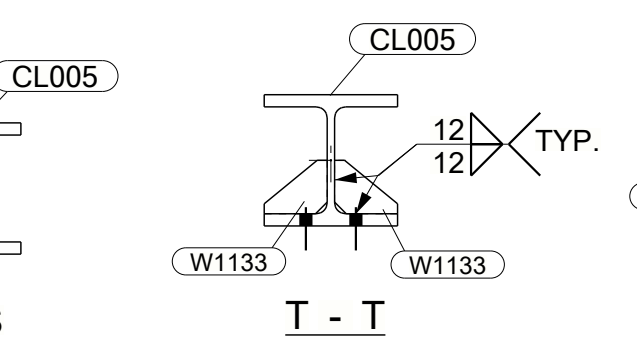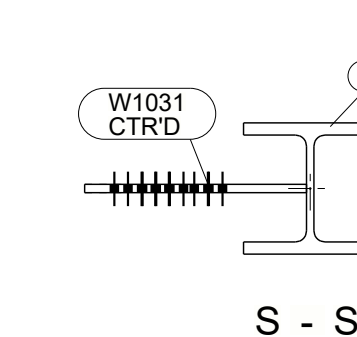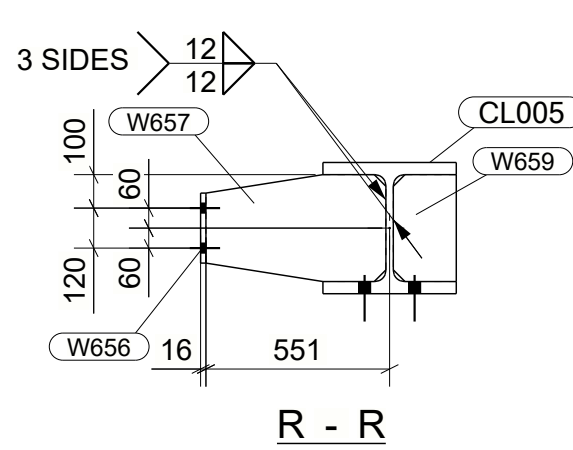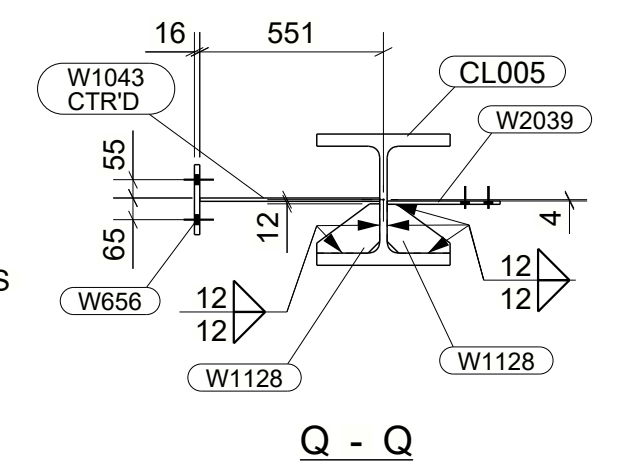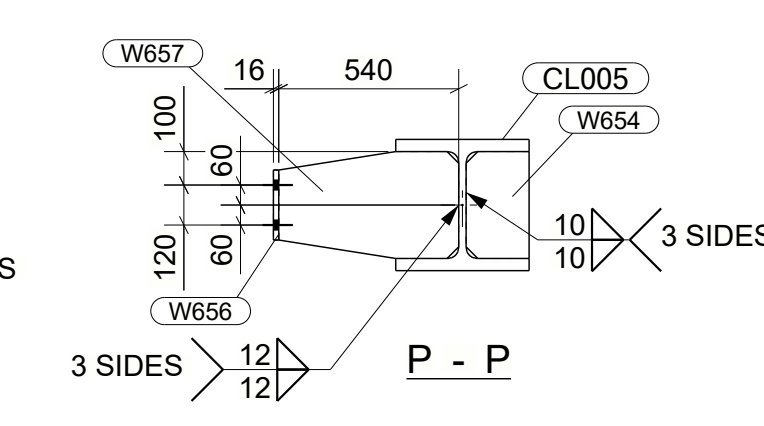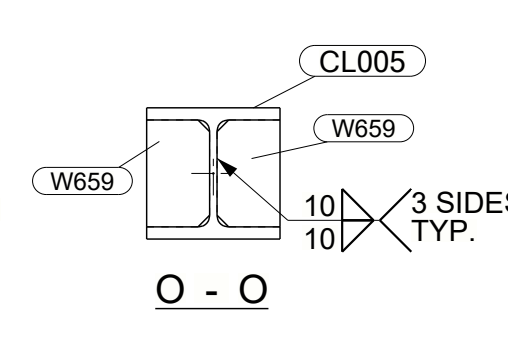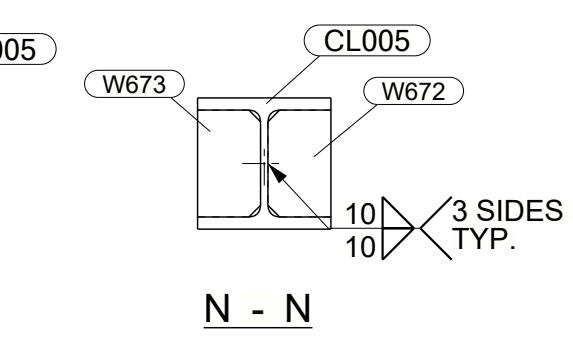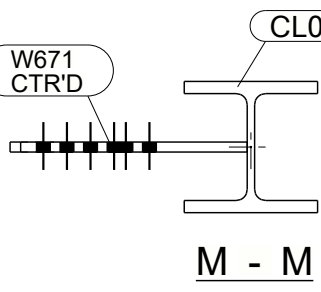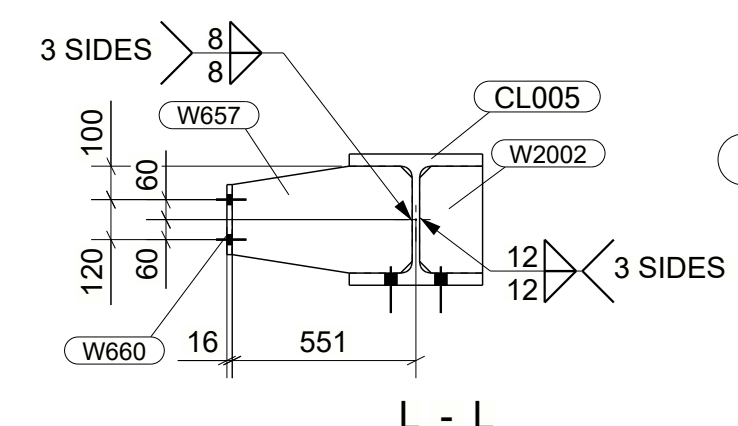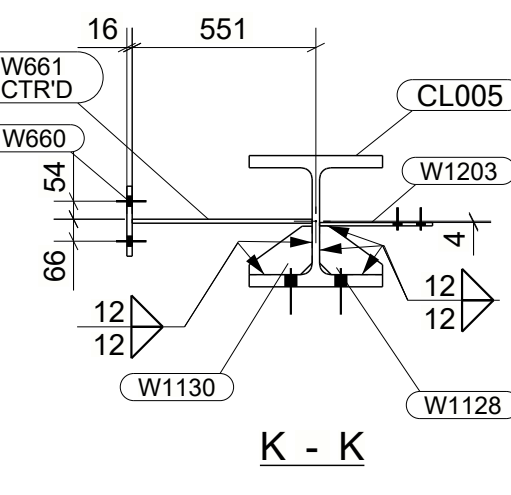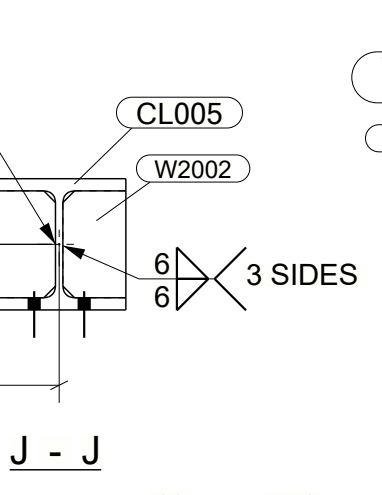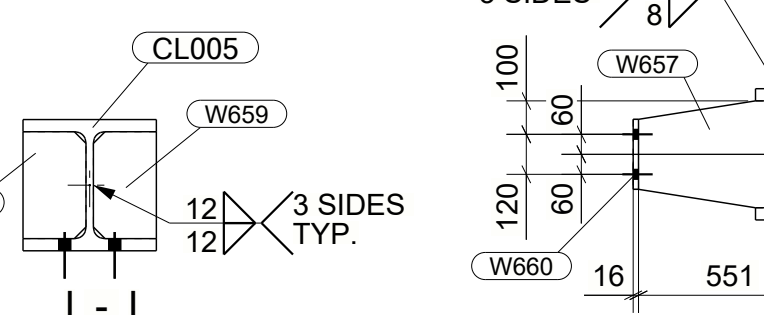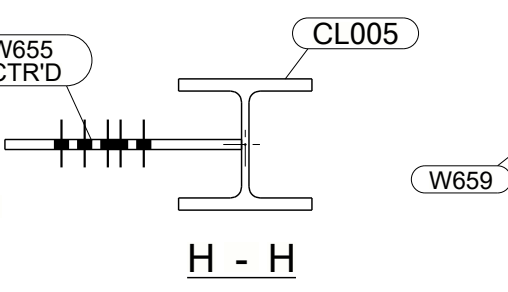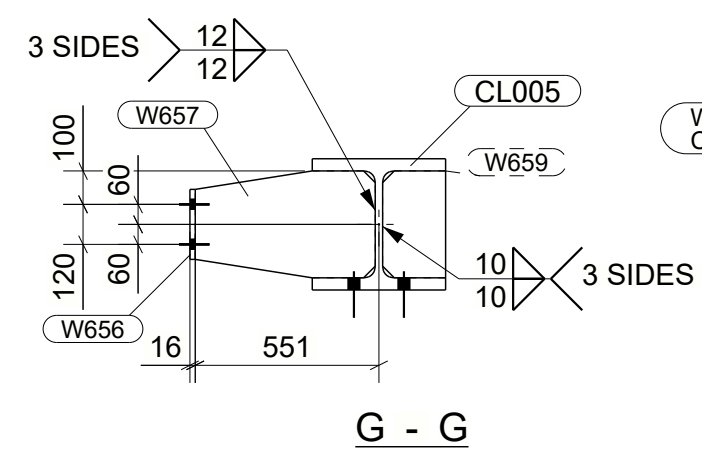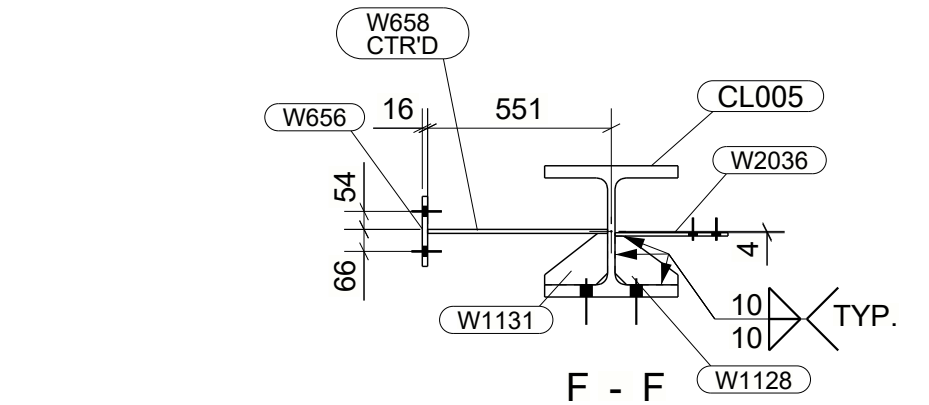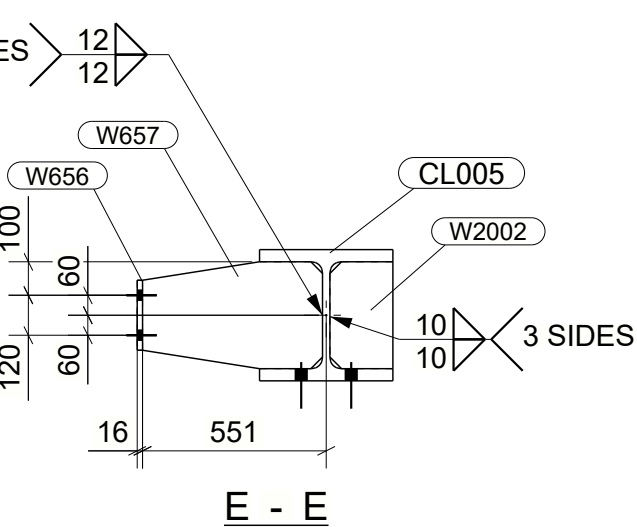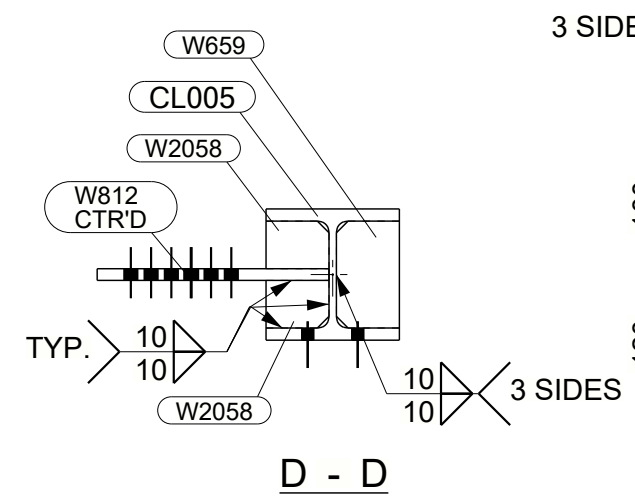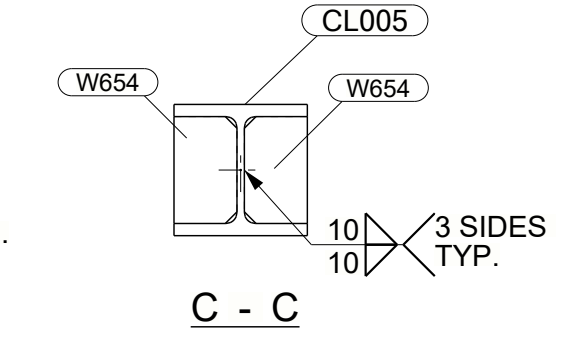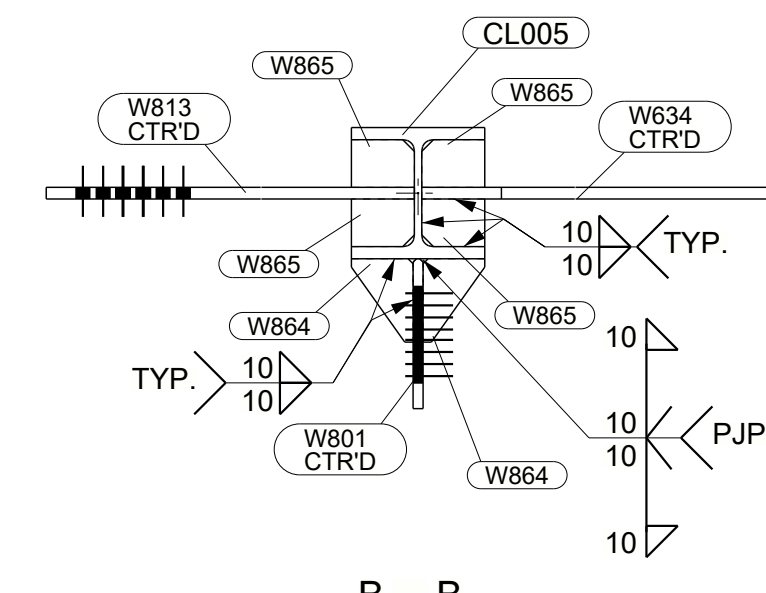

BOLT LIST:-						
BOLT \ STUD	BOLT DESCRIPTION	QTY/ONE	QTY/ALL	FINISH	REMARKS	
BOLT	B1N1W 0 x 75 ASTM F3125 Gr F1852	1	1			


	GA & IFC DRAWINGS REFERENCE	REV.
	AD282-732-C-33158-61	6
	AD282-732-C-33170-73,33539	6
	AD282-732-C-34311	2
	AD282-732-C-34274	2

NOTES :


- 1-ALL DIMENSIONS ARE GIVEN IN MILLIMETERS (U.N.O.).
- 2- ▼ DENOTES ASSEMBLY ORIENTATION MARK.
- 3-DON'T SCALE THE DRAWING. FOLLOW THE WRITTEN DIMENSIONS.
- 4-FINISH AS PER PROJECT SPEC.
- 5- STRUCTURAL STEELWORK SHALL BE IN ACCORDANCE WITH PROJECT SPECIFICATIONS AD282-732-G-03520 & AD282-732-G-03527
- 6-WHEREVER THERE IS NO ACCESS FOR FILLET WELDING TO BE REPLACED BY FULL PENETRATION BUTT WELDING
- 7-FOR CIP WELD MARKED LOCATIONS FOLLOW THIS DETAIL

A technical drawing of a fillet weld joint between two plates. The top plate has a thickness labeled 'R=10mm'. The bottom plate has a thickness labeled 'T=10mm'. The height of the fillet weld from the bottom plate surface is labeled 'S=10mm'.


8-ALL WELDS TO BE 6mm FILLET WELD U.N.O.

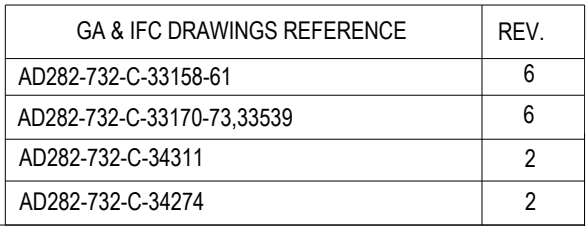

GRID LOCATION	
EL +120.000	732/05/732E

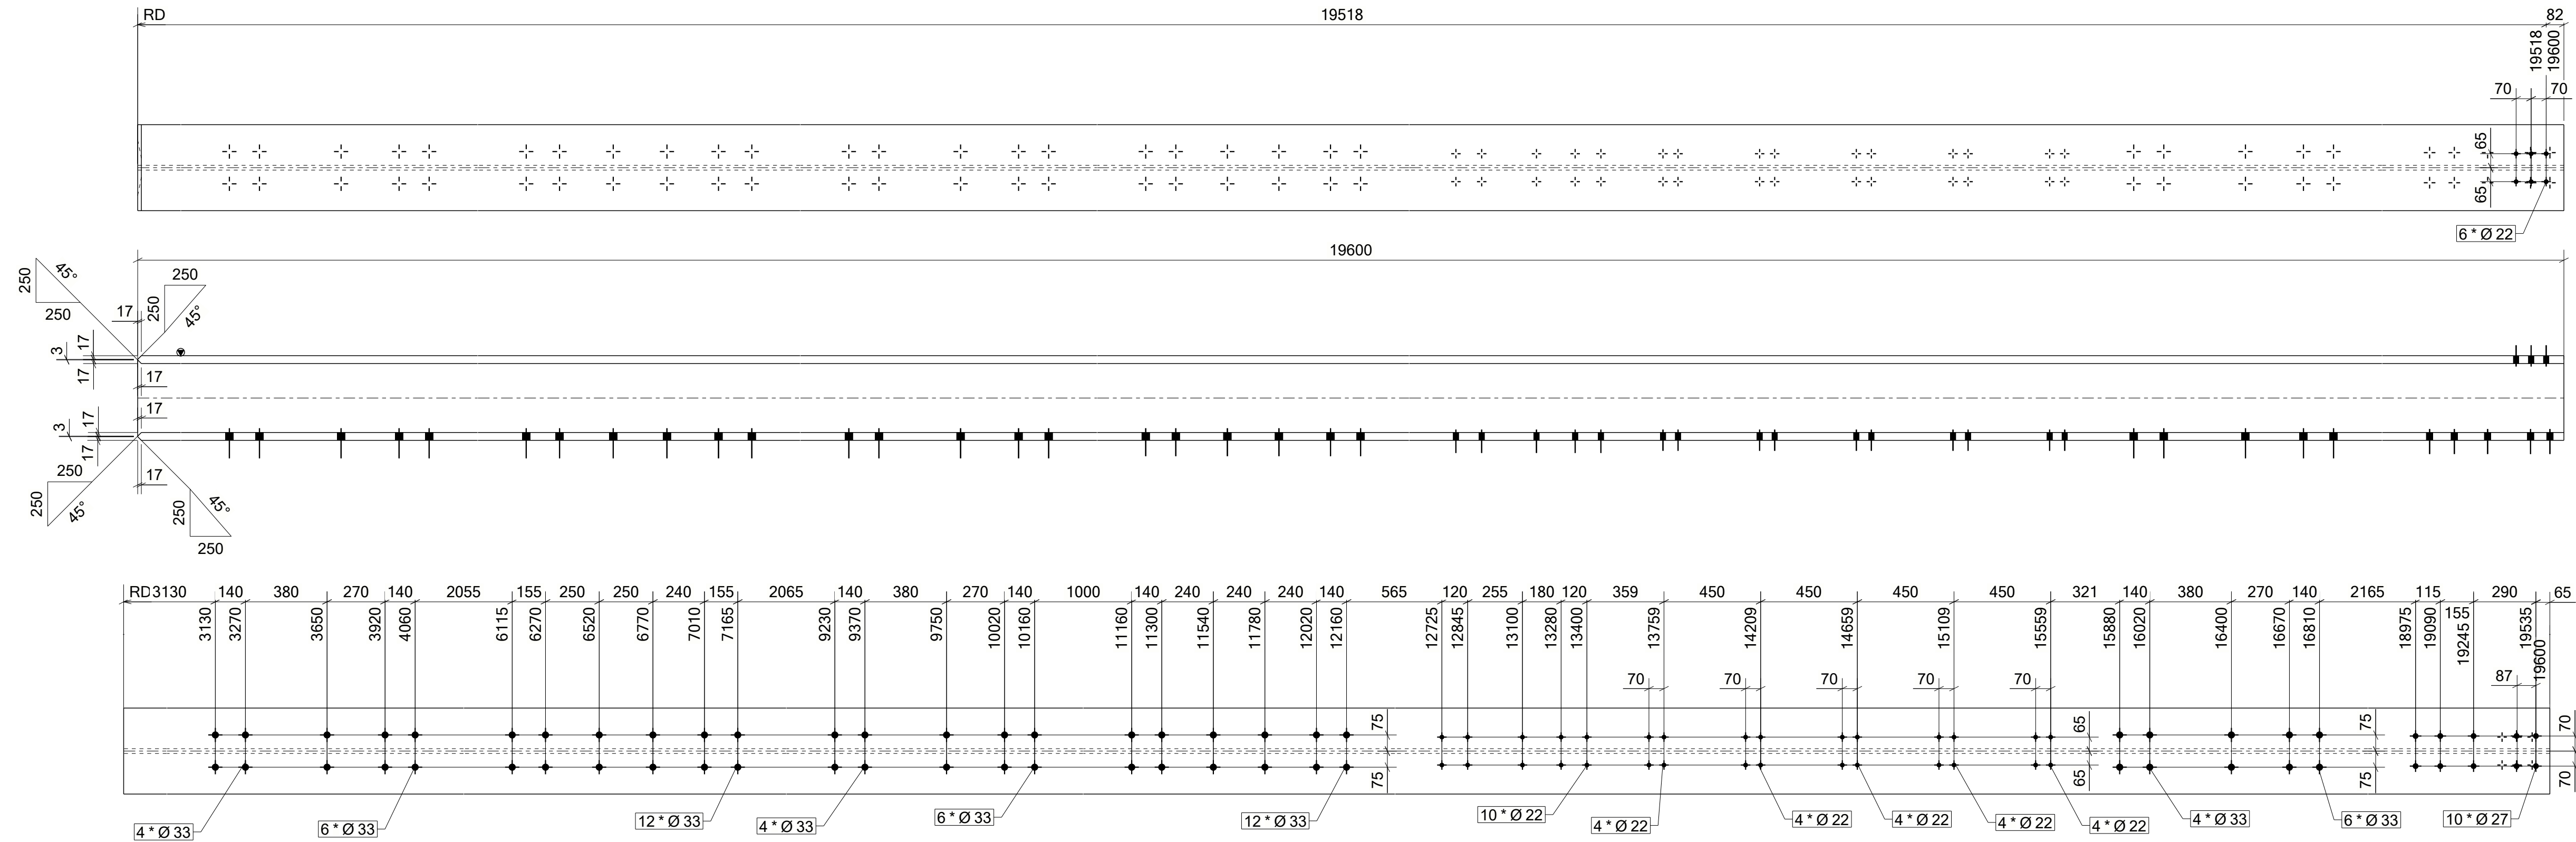

DETAIL OF CL005

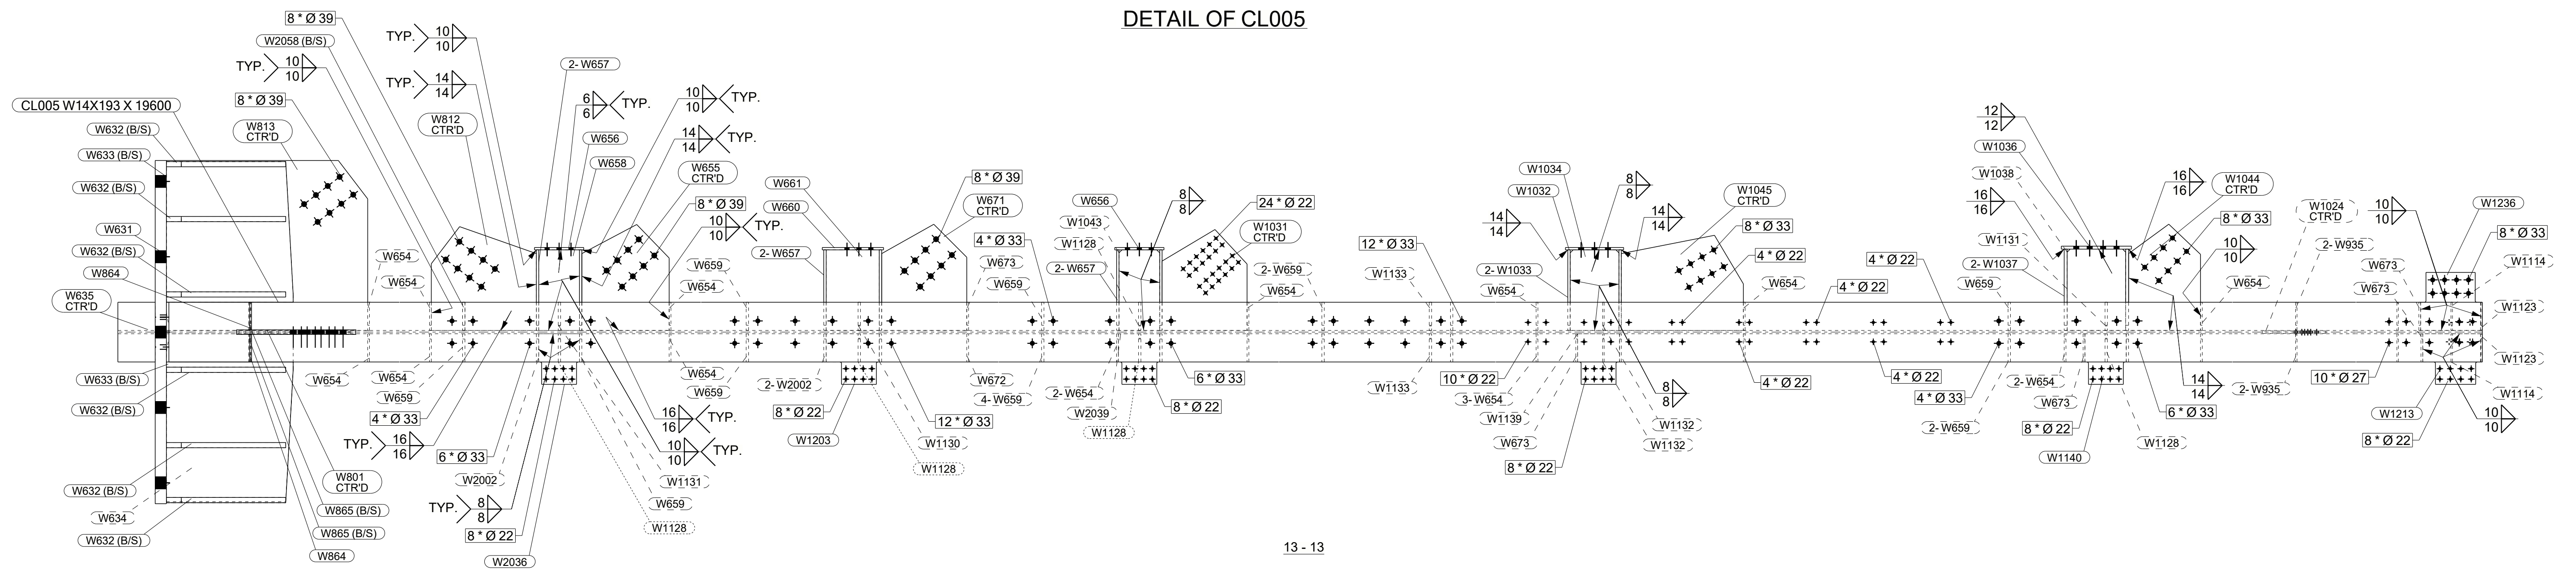

13 - 13

WORK THIS SHEET WITH 2307033-732-PR-10-CL005, CL005-1


GA & IFC DRAWINGS REFERENCE	REV.
AD282-732-C-33158-61	6
AD282-732-C-33170-73,33539	6
AD282-732-C-34311	2
AD282-732-C-34274	2

NOTES :

- 1- ALL DIMENSIONS ARE GIVEN IN MILLIMETERS (U.N.O.).
- 2-  DENOTES ASSEMBLY ORIENTATION MARK.
- 3- DON'T SCALE THE DRAWING. FOLLOW THE WRITTEN DIMENSIONS.
- 4- FINISH AS PER PROJECT SPEC.
- 5- STRUCTURAL STEELWORK SHALL BE IN ACCORDANCE WITH PROJECT SPECIFICATIONS AD282-732-G-03520 & AD282-732-G-03527
- 6- WHEREVER THERE IS NO ACCESS FOR FILLET WELDING TO BE REPLACED BY FULL PENETRATION BUTT WELDING
- 7- FOR CIP WELD MARKED LOCATIONS FOLLOW THIS DETAIL

8-ALL WELDS TO BE 6mm FILLET WELD U.N.O.

GRID LOCATION	
EL+113.433	C732/07/732E

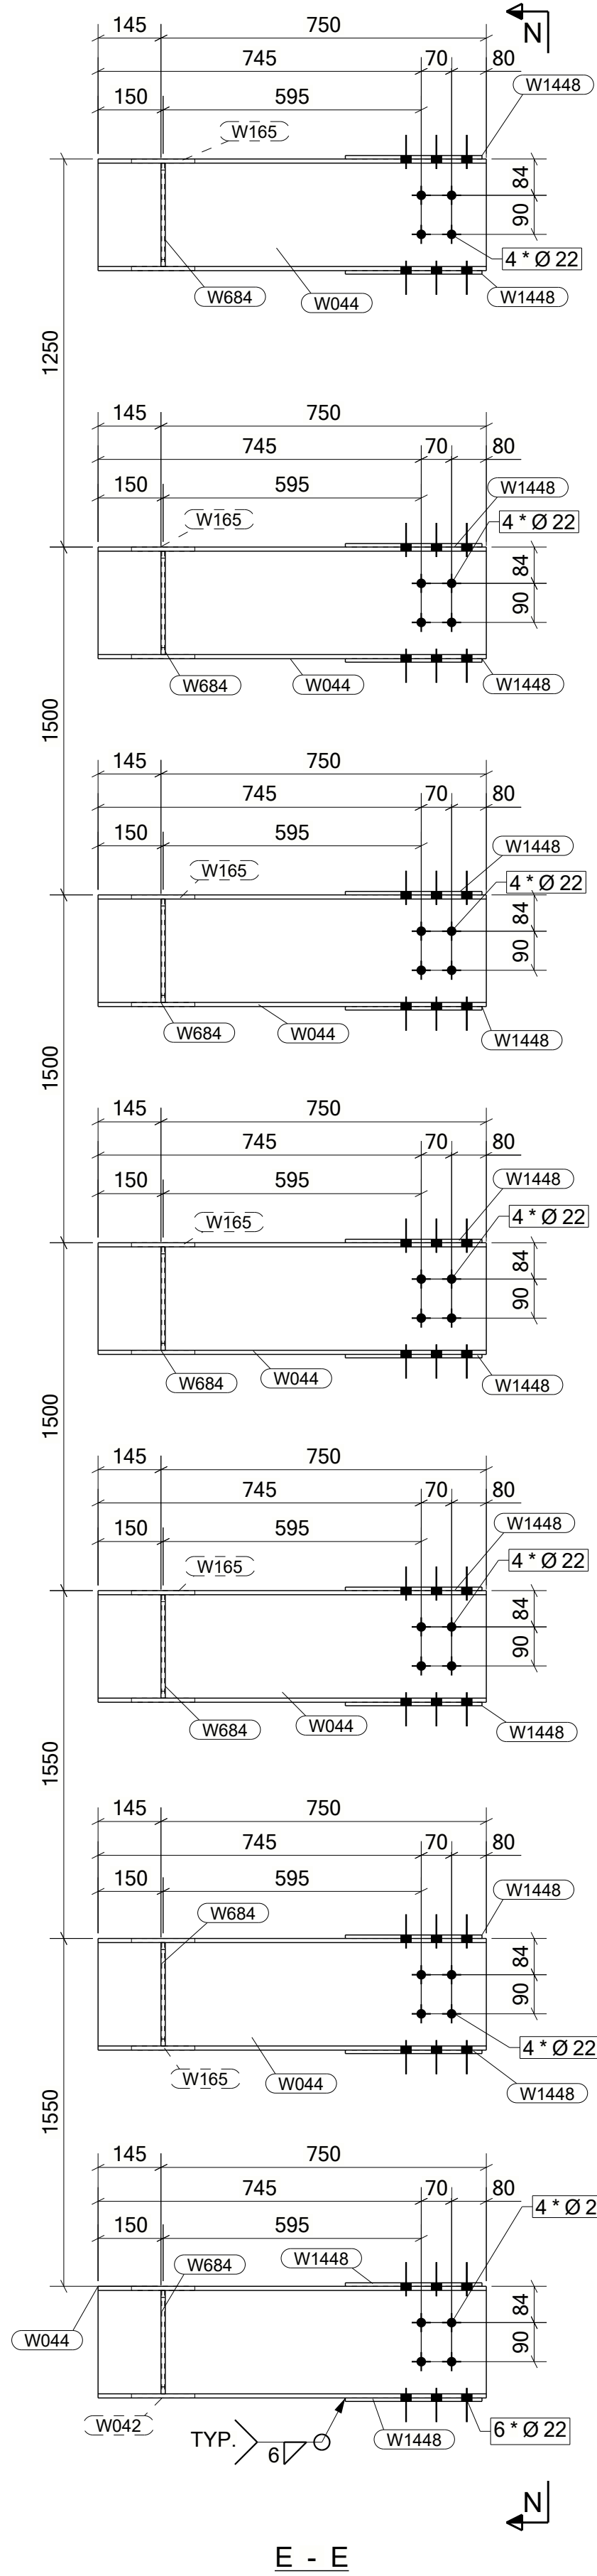





WORK THIS SHEET WITH 2307033-732-PR-10-FR001

1 NO. FRAME MKD' 2307033-732-PR-10-FR001








GA & IFC DRAWINGS REFERENCE	REV.
AD282-732-C-33158-61	6
AD282-732-C-33170-73.33539	6
AD282-732-C-34311	2
AD282-732-C-34274	2

- NOTES :**
- 1-ALL DIMENSIONS ARE GIVEN IN MILLIMETERS (U.N.O.).
 - 2-  DENOTES ASSEMBLY ORIENTATION MARK.
 - 3-DON'T SCALE THE DRAWING. FOLLOW THE WRITTEN DIMENSIONS.
 - 4- FINISH AS PER PROJECT SPEC.
 - 5- STRUCTURAL STEELWORK SHALL BE IN ACCORDANCE WITH PROJECT SPECIFICATIONS AD282-732-G-03520 & AD282-732-G-03527
 - 6-WHEREVER THERE IS NO ACCESS FOR FILLET WELDING TO BE REPLACED BY FULL PENETRATION BUTT WELDING
 - 7-FOR CIP WELD MARKED LOCATIONS FOLLOW THIS DETAIL
 - 8-ALL WELDS TO BE 6mm FILLET WELD U.N.O.

GRID LOCATION	
EL +97.370	2/B-A

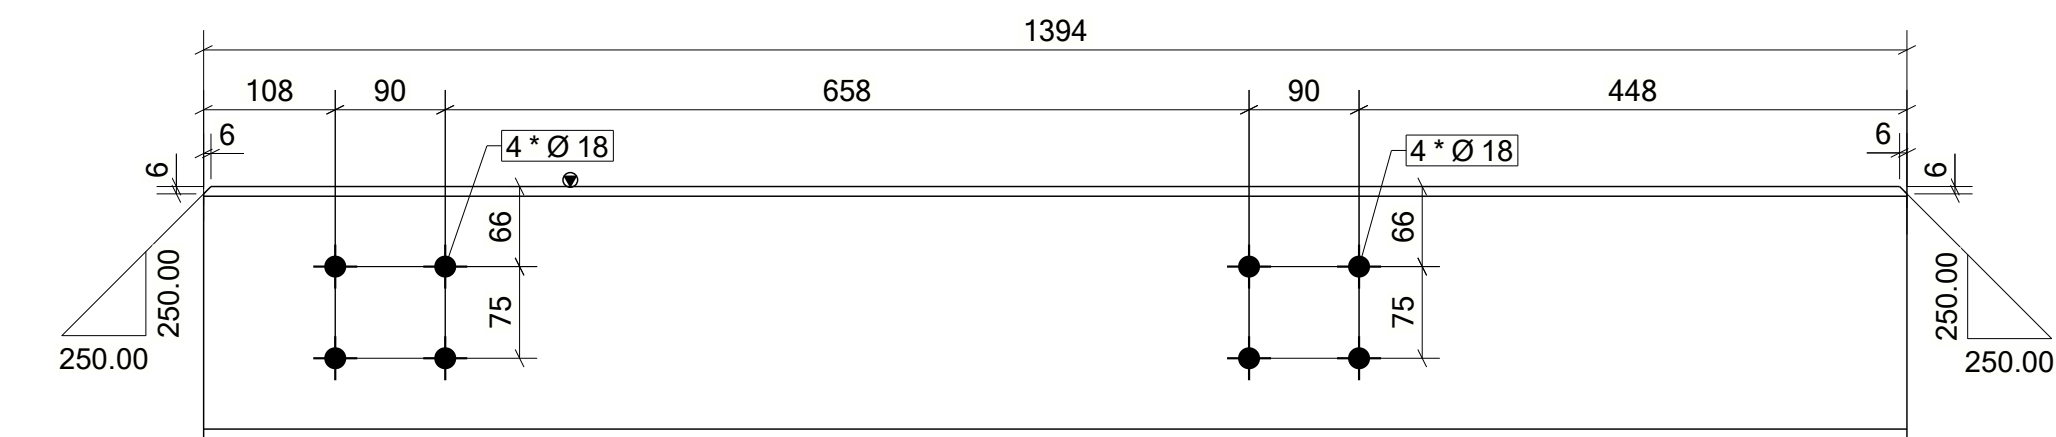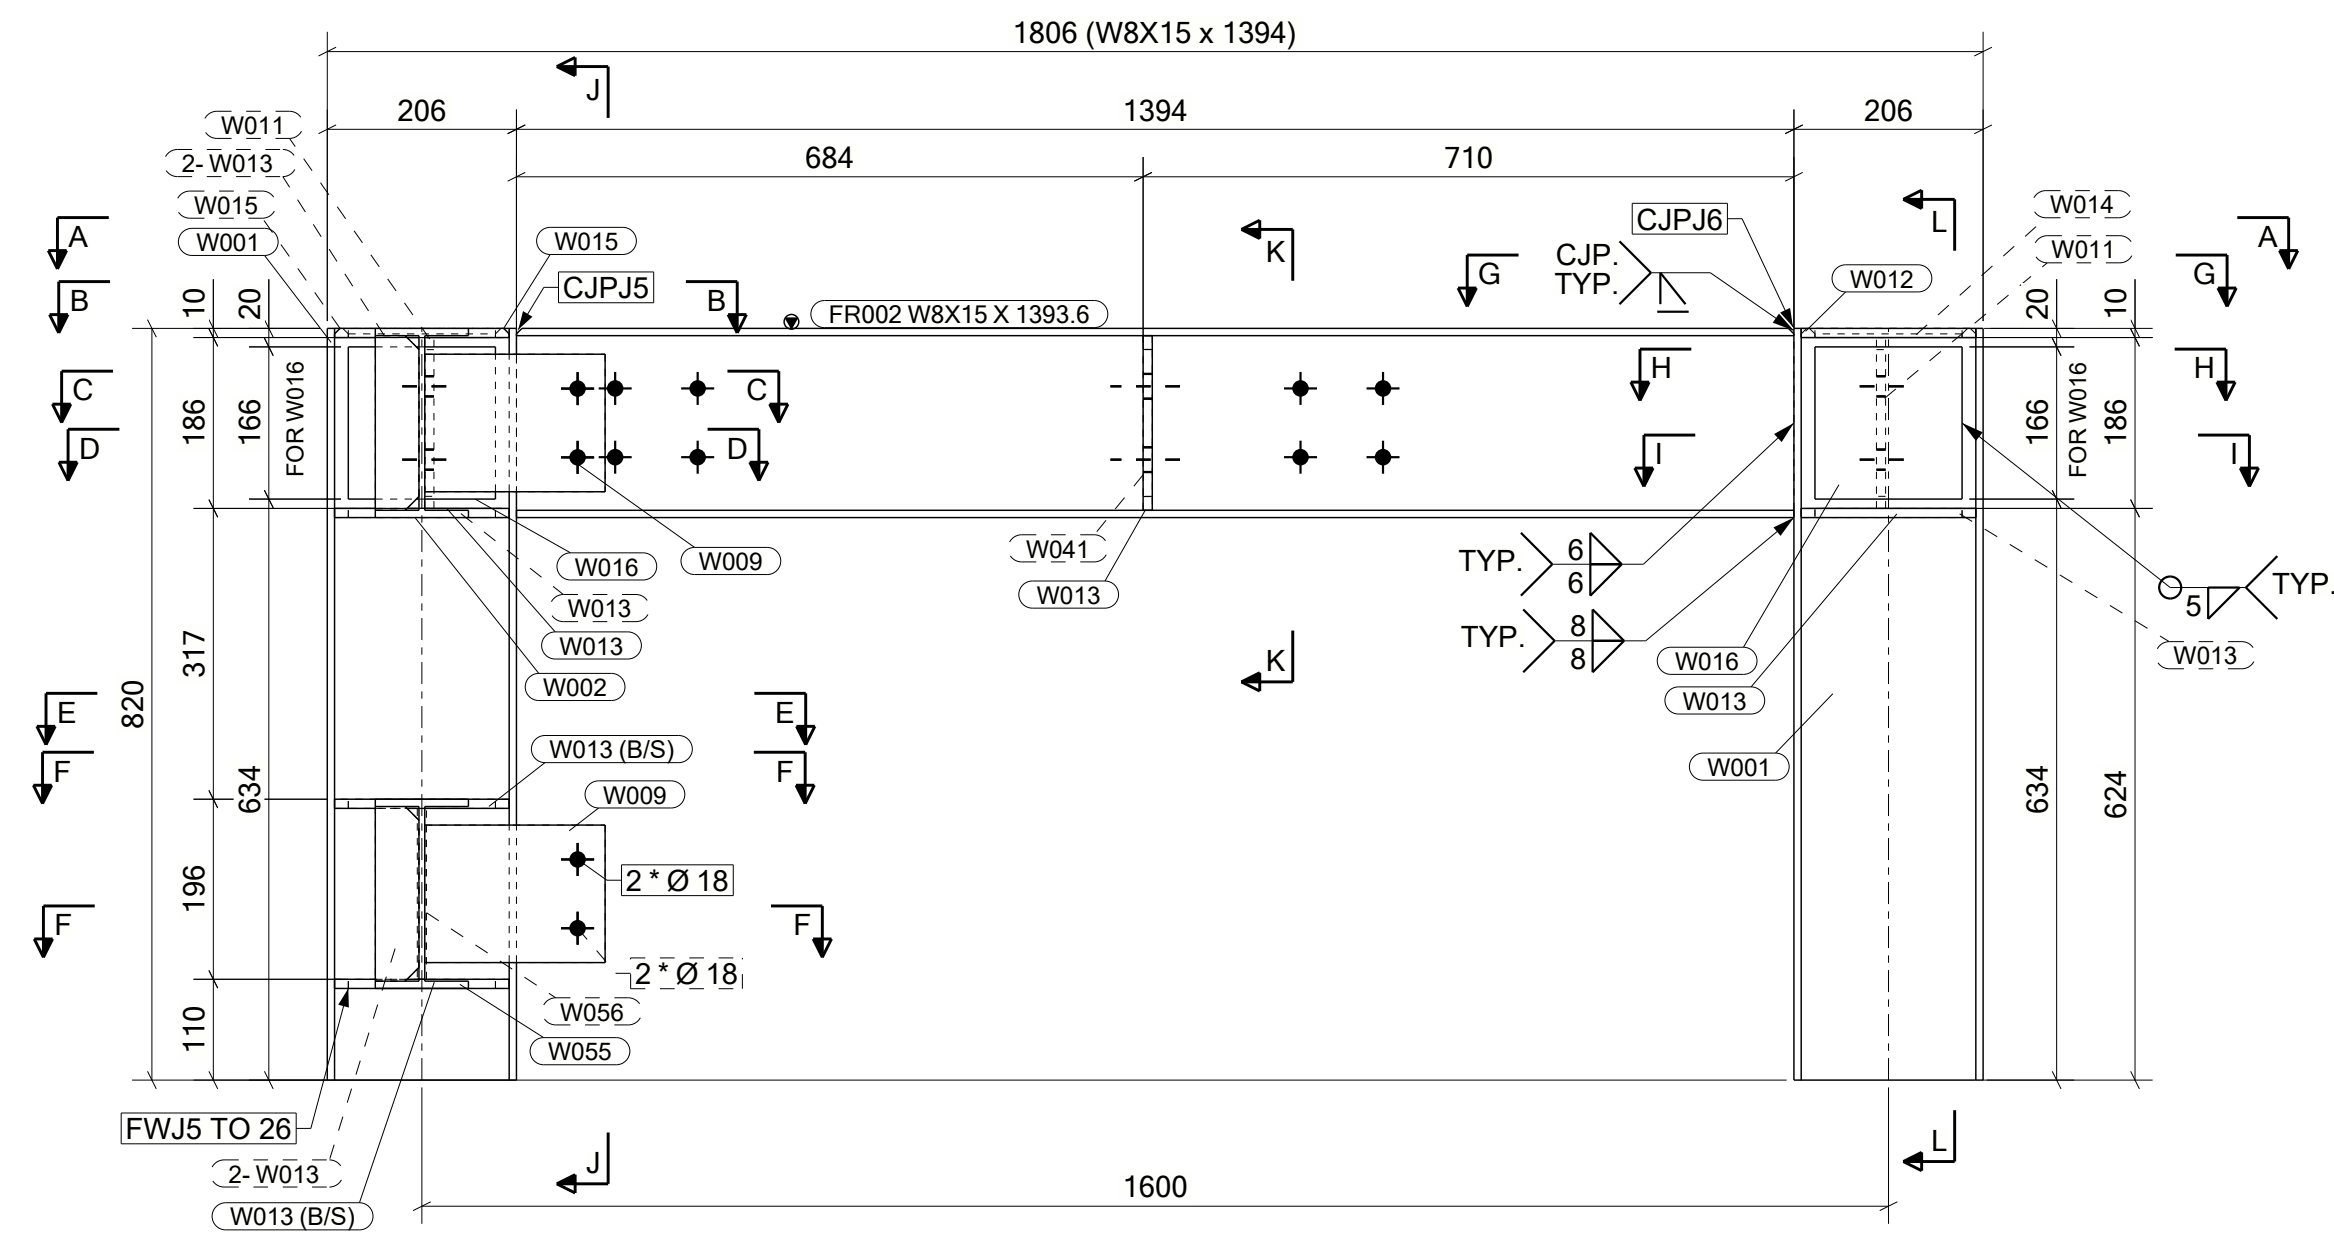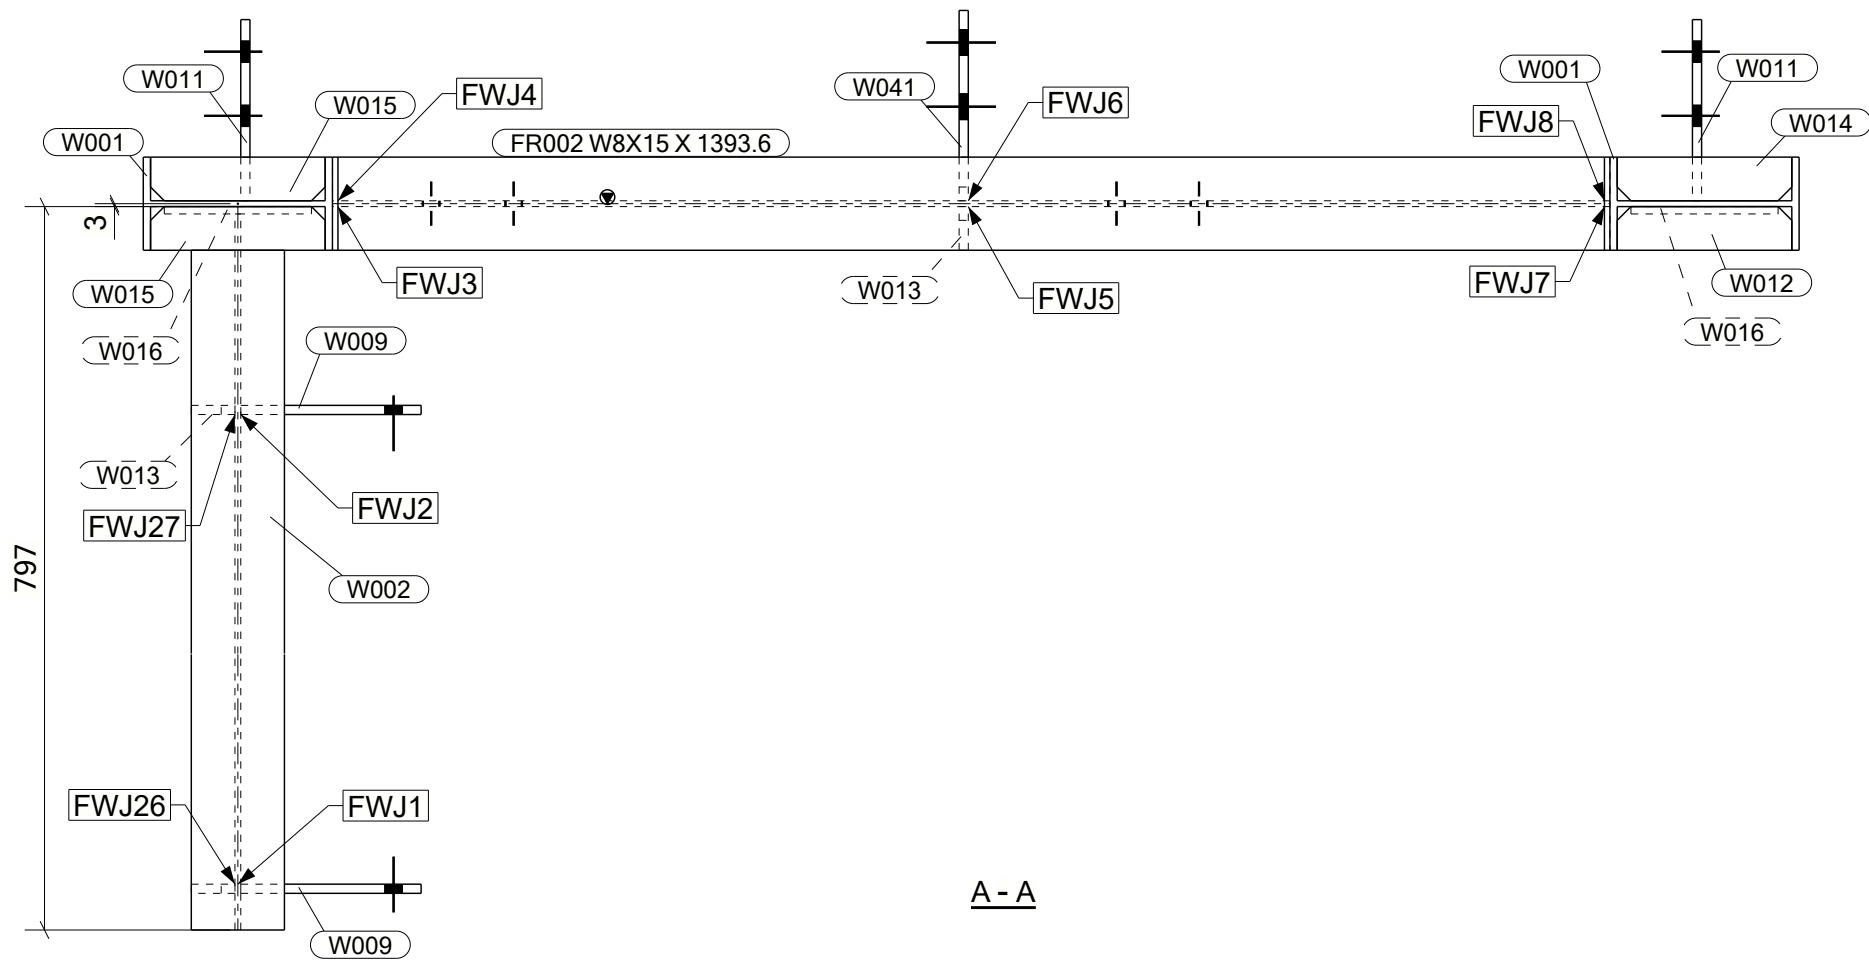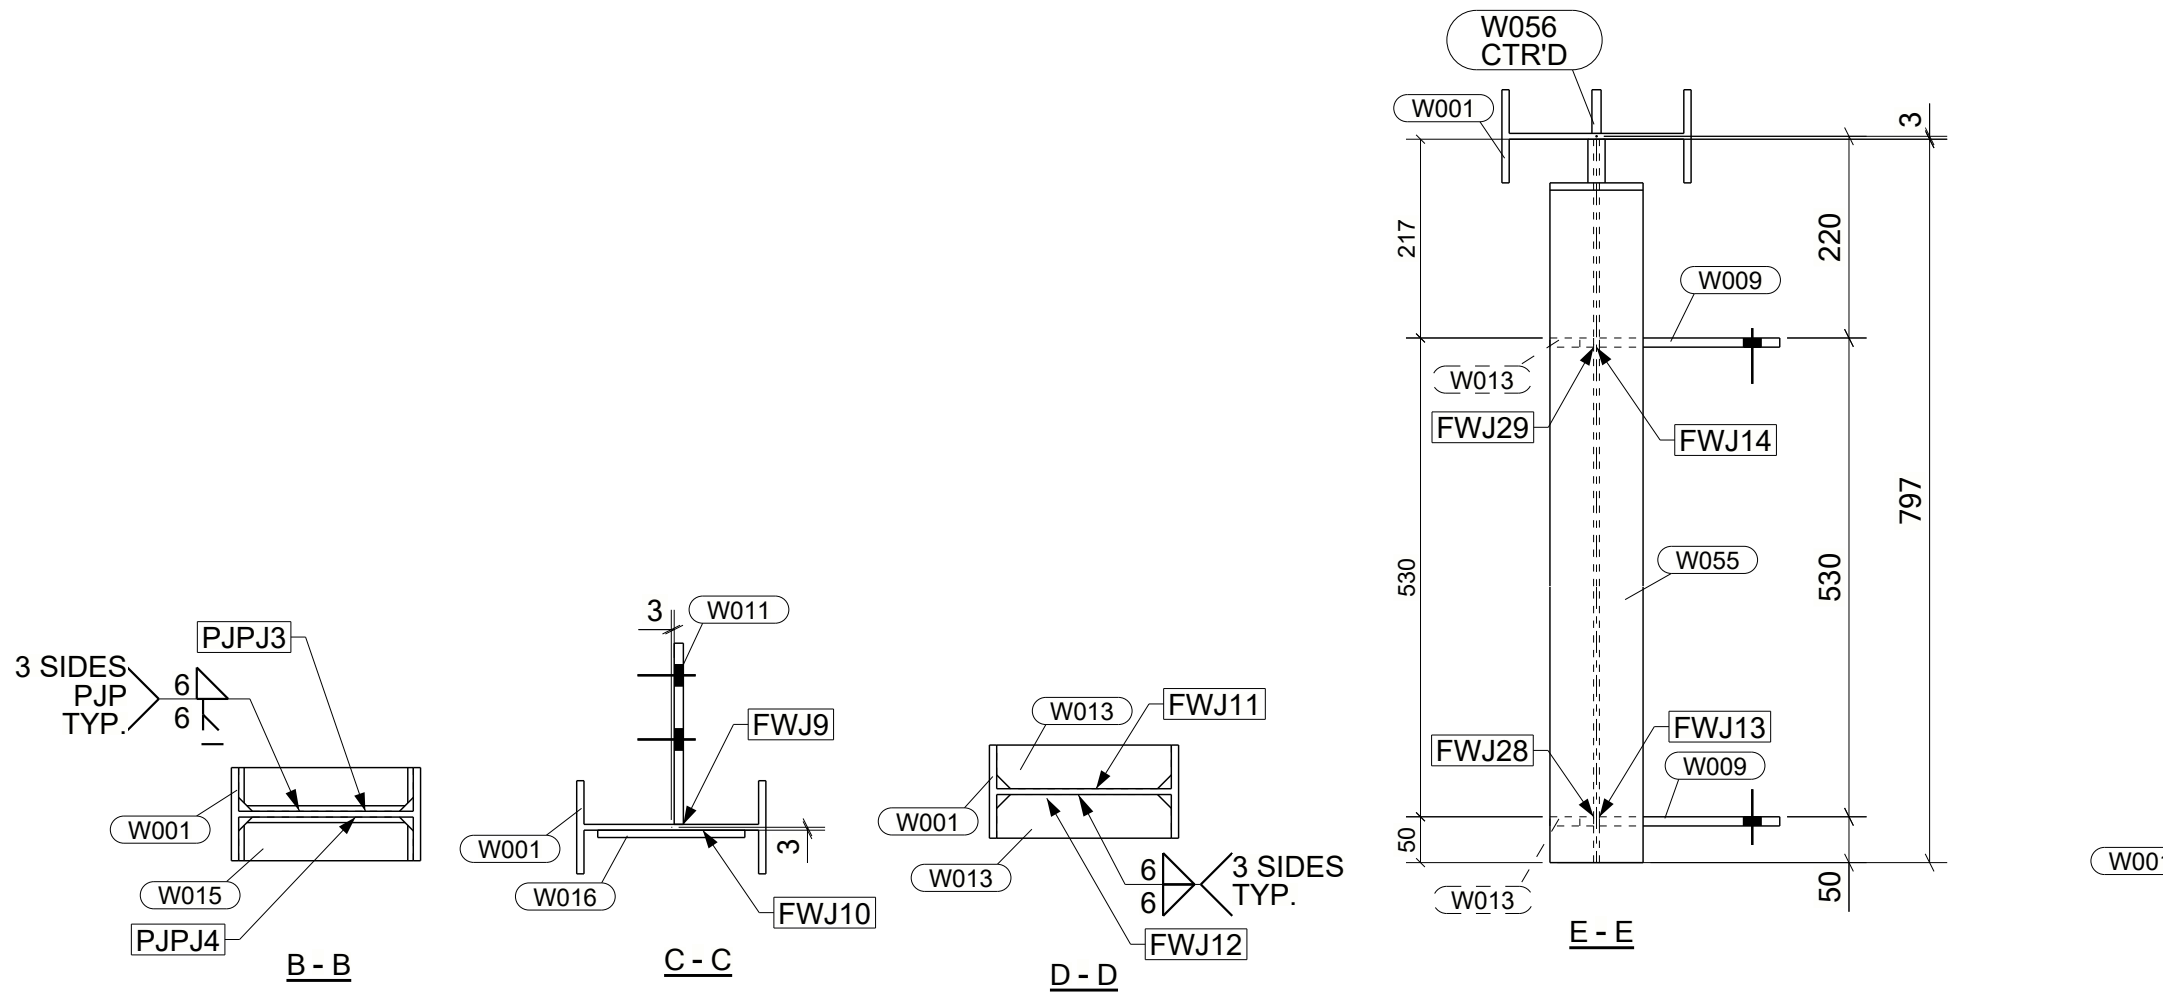

DETAIL OF FR002

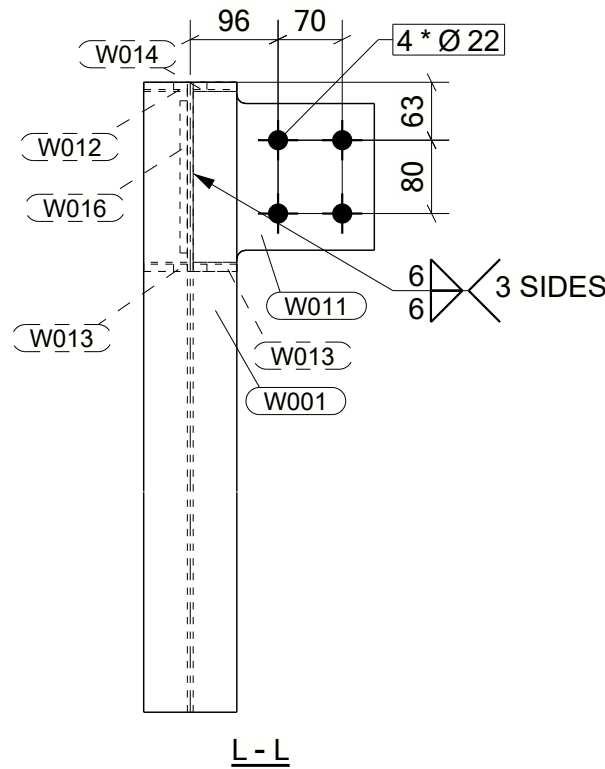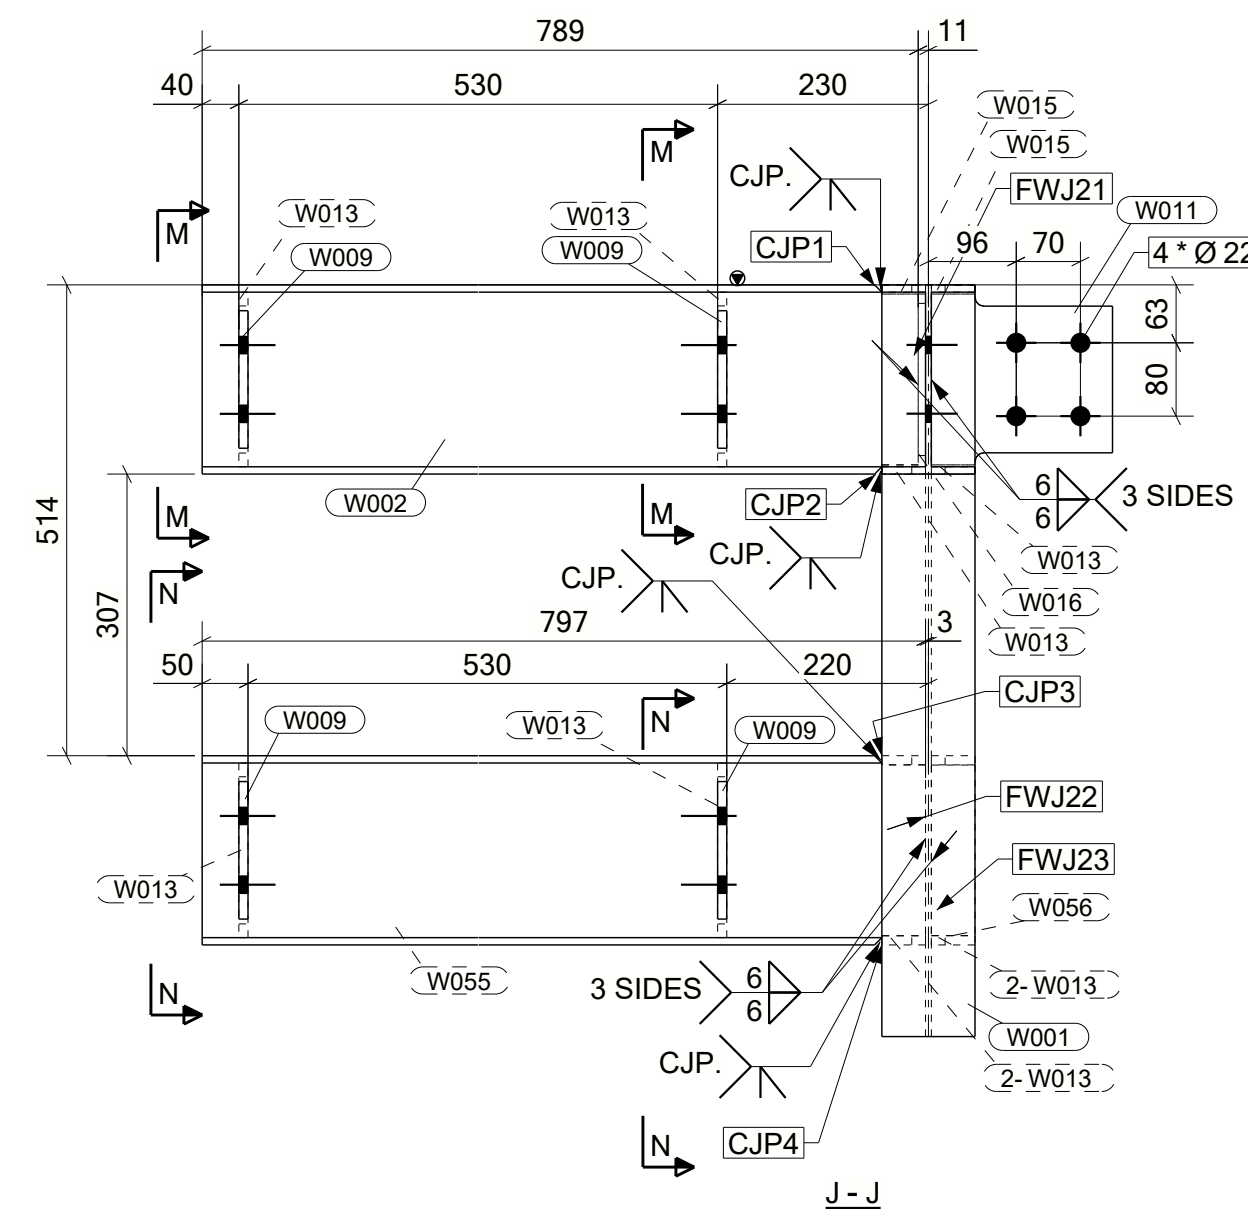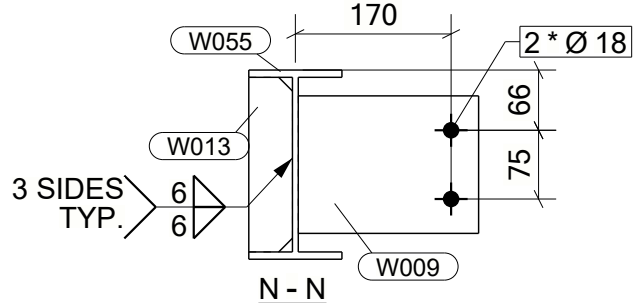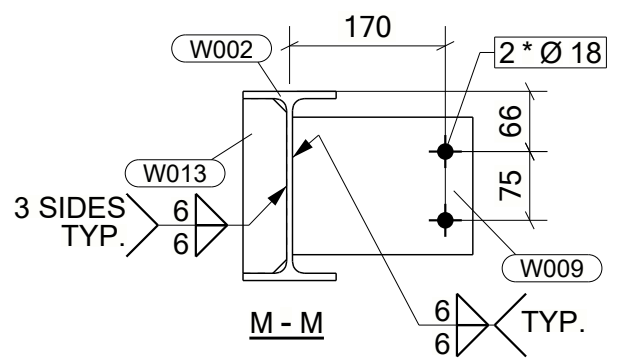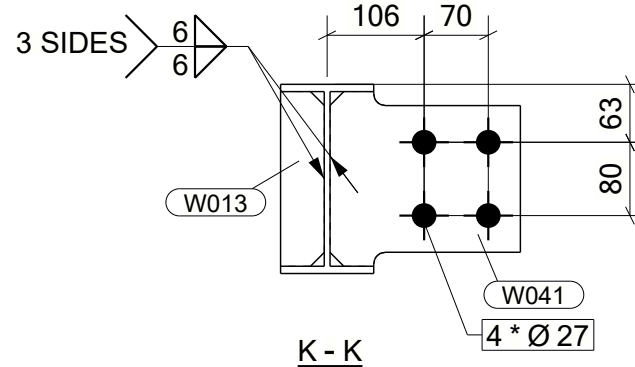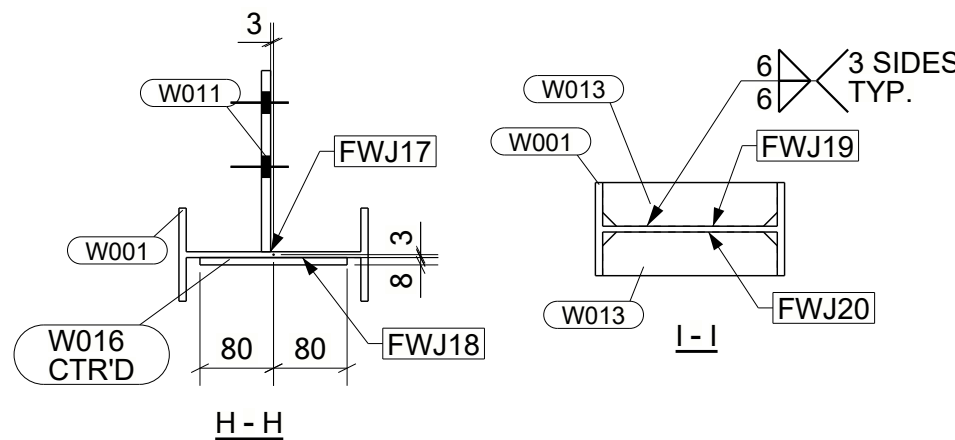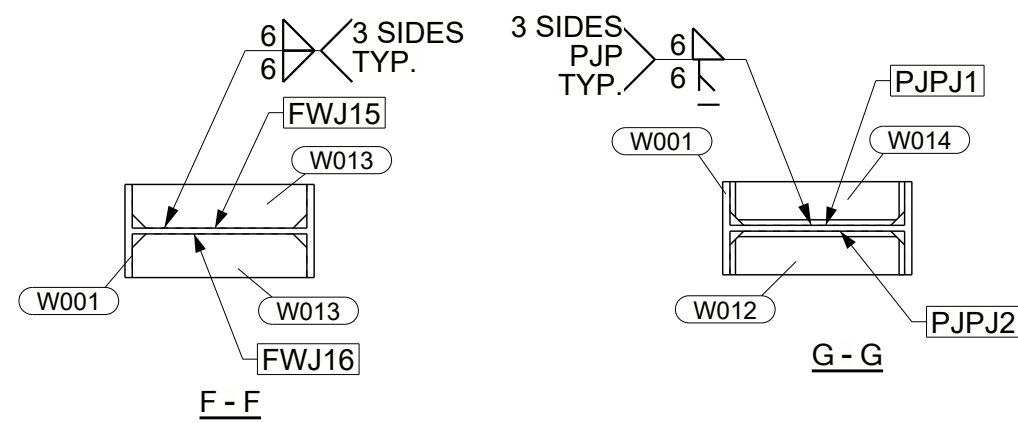



DRAWING NO. : 2307053-732-STR-02-FR002								REV.: 00				
ERECTION MARK : 2307053-732-STR-02-FR002			DESCRIPTION : FRAME			COLOR CODE : 10 B 15			QTY : 1		NOS	
HOLD:		TYPE: W		TREAT: PN		COST CODE: 2.01			REMARKS:			
LENGTH: 1806		WIDTH: 1011		HEIGHT: 820		TOTAL S.AREA: 4.7			(M2)			
POSITION NO.	QTY PER ASSLY	SECTION	LENGTH	UNIT WEIGHT (KG)	TOTAL WIEGHT (KG)		GRADE	REVISION	PART ID	TREATMENT	REMARKS	
					QTY	WEIGHT						
FR002	1	W8X15	1394	31.338	1	31.34	S275JR	1	MM	PN		
W001	2	W8X15	820	18.439	2	36.88	S275JR	1	WI			
W002	1	W8X15	789	17.738	1	17.74	S275JR	1	WI			
W009	4	FLT150X10	197	2.316	4	9.27	S275JR	1	WI			
W011	2	PL10X198	186	2.584	2	5.17	S355JR	1	WI			
W012	1	PL10X48	190	0.661	1	0.66	S355JR	1	WI			
W013	13	PL10X48	190	0.694	13	9.03	S355JR	1	WI			
W014	1	PL10X48	190	0.661	1	0.66	S355JR	1	WI			
W015	2	PL10X48	190	0.661	2	1.32	S355JR	1	WI			
W016	2	PL8X166	160	1.673	2	3.35	S355JR	1	WI			
W041	1	PL10X191	208	2.710	1	2.71	S355JR	1	WI			
W055	1	W8X15	797	17.918	1	17.92	S275JR	1	WI			
W056	1	FLT10X186	48	0.695	1	0.70	S275JR	1	WI			
					UNIT WEIGHT	136.73						
					TOTAL WEIGHT	136.73						
BOLT LIST:-												
BOLT \ STUD		BOLT DESCRIPTION		QTY/ONE		QTY/ALL		FINISH		REMARKS		

ANCILLARY CATEGORY

FW-J1 TO J29
CJP- J1 TO J6
PJP- J1 TO J4

GA & IFC DRAWINGS REFERENCE	REV.
AD282-732-C-33293	3
AD282-732-C-34321	1
AD282-732-C-34284	1


- NOTES :**
- ALL DIMENSIONS ARE GIVEN IN MILLIMETERS (U.N.O.).
 - ▼ DENOTES ASSEMBLY ORIENTATION MARK.
 - DON'T SCALE THE DRAWING. FOLLOW THE WRITTEN DIMENSIONS.
 - FINISH AS PER PROJECT SPEC.
 - STRUCTURAL STEELWORK SHALL BE IN ACCORDANCE WITH PROJECT SPECIFICATIONS AD282-732-G-03520 & AD282-732-G-03527
 - WHEREVER THERE IS NO ACCESS FOR FILLET WELDING TO BE REPLACED BY FULL PENETRATION BUTT WELDING
 - FOR CIP WELD MARKED LOCATIONS FOLLOW THIS DETAIL
 - ALL WELDS TO BE 6mm FILLET WELD U.N.O.

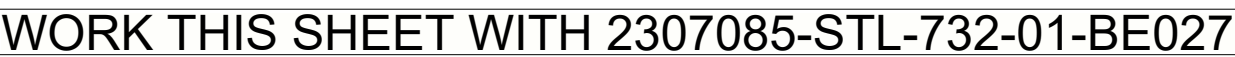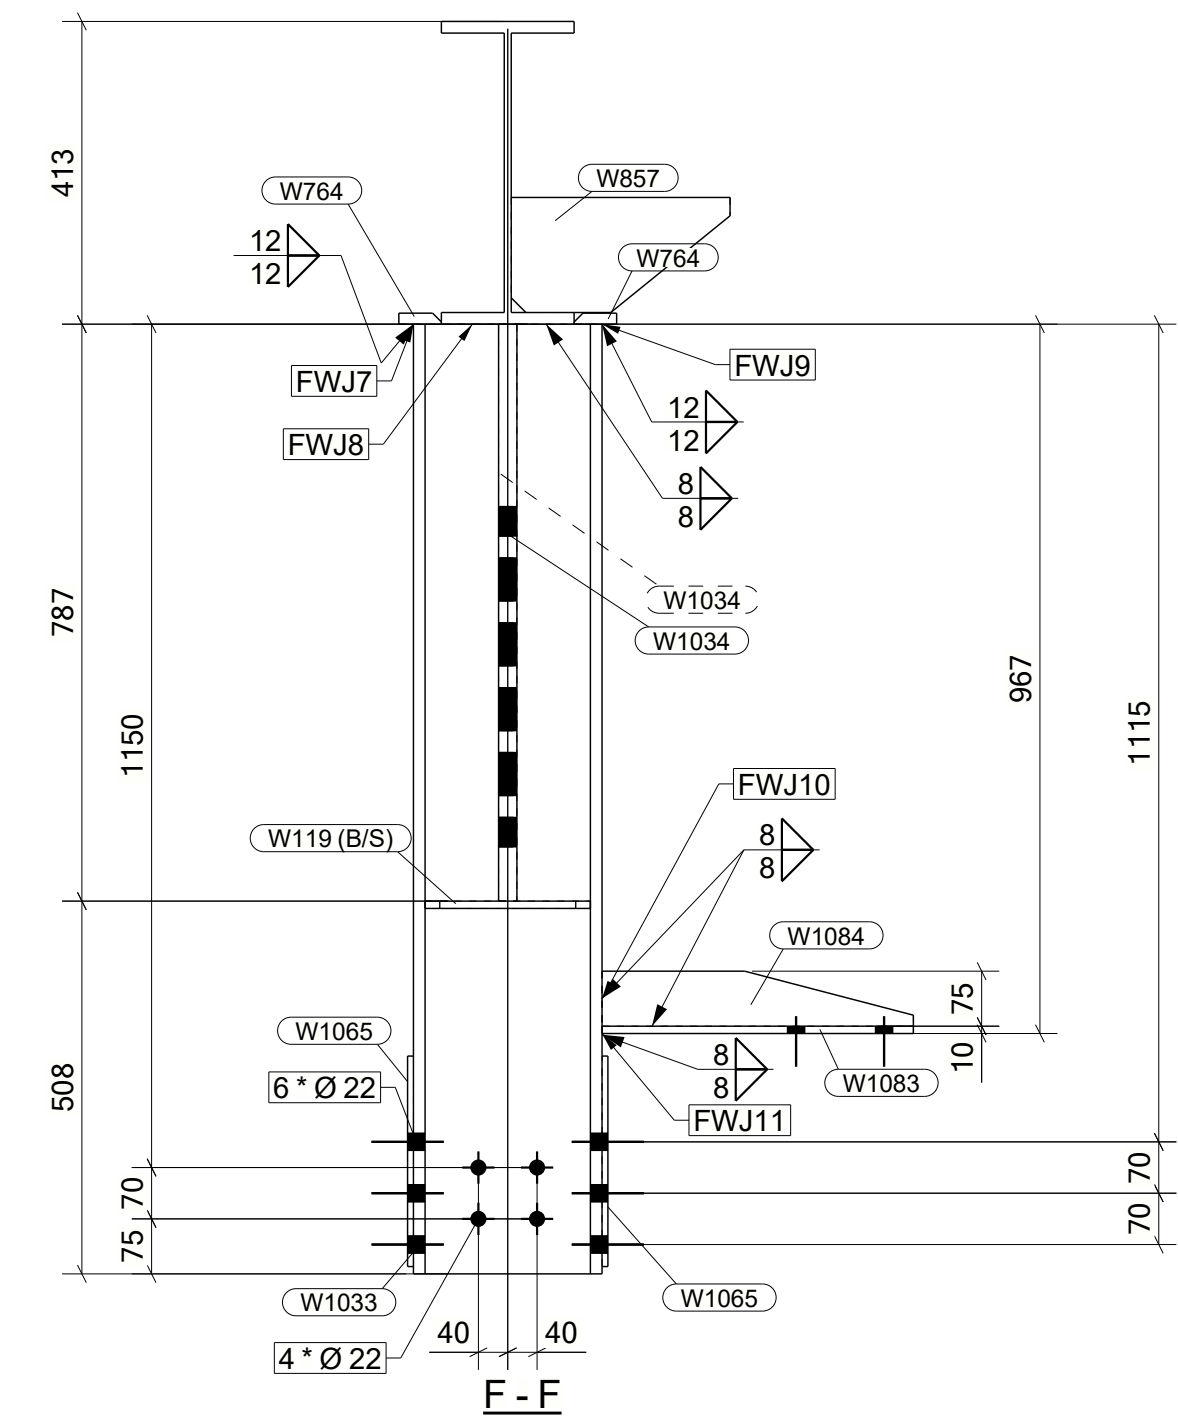

GA & IFC DRAWINGS REFERENCE	REV.
AD282-732-C-33226,27,28,29,30,31	4
AD282-732-C-33233,34,35,33499,33500	4
AD282-732-C-34337	2
AD282-732-C-34300	2

NOTES :

- 1-ALL DIMENSIONS ARE GIVEN IN MILLIMETERS (U.N.O.).
- 2-  DENOTES ASSEMBLY ORIENTATION MARK.
- 3-DON'T SCALE THE DRAWING. FOLLOW THE WRITTEN DIMENSIONS.
- 4- FINISH AS PER PROJECT SPEC.
- 5- STRUCTURAL STEELWORK SHALL BE IN ACCORDANCE WITH PROJECT SPECIFICATIONS AD282-732-G-03520 & AD282-732-G-03527
- 6-WHEREVER THERE IS NO ACCESS FOR FILLET WELDING TO BE REPLACED BY FULL PENETRATION BUTT WELDING
- 7-FOR CIP WELD MARKED LOCATIONS FOLLOW THIS DETAIL

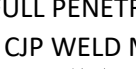

(1) Minimum Weld

- 8-ALL WELDS TO BE 6mm FILLET WELD U.N.O.

GRID LOCATION	
EL+118.655	2-1/A

DRAWING NO. : 2307085-STL-732-01-RF001										REV.: 00							
ERECTION MARK : 2307085-STL-732-01-RF001										DESCRIPTION : RAFTER		COLOR CODE : 10 B 15		QTY : 1		NOS	
HOLD:		TYPE: W		TREAT: PN		COST CODE: 7.03				REMARKS:							
LENGTH: 10545		WIDTH: 574		HEIGHT: 1810		TOTAL S.AREA: 39.5				(M2)							
POSITION NO.	QTY PER ASSLY	SECTION	LENGTH	UNIT WEIGHT (KG)	TOTAL WIEGHT (KG)		GRADE	REVISION	PART ID	TREATMENT	REMARKS						
					QTY	WEIGHT											
RF001	1	W24X131	10386	2030.372	1	2030.37	S275JR	1	MM	PN							
W053	8	PL10X156	575	6.922	8	55.38	S355JR	1	WI								
W059	9	PL10X75	243	0.894	9	8.04	S355JR	1	WI								
W101	1	W24X131	1925	376.310	1	376.31	S275JR	1	WI								
W102	1	PL32X327	1575	129.374	1	129.37	S355JR	1	WI								
W106	2	PL15X152	575	10.168	2	20.34	S355JR	1	WI								
W454	1	PL10X156	576	6.940	1	6.94	S355JR	1	WI								
W744	1	PL20X306	576	22.590	1	22.59	S355JR	1	WI								
W745	1	PL12X156	576	8.325	1	8.32	S355JR	1	WI								
W746	9	PL10X140	243	2.671	9	24.04	S355JR	1	WI								
W771	1	PL20X340	820	43.751	1	43.75	S355JR	1	WI								
W773	1	PL10X100	104	0.680	1	0.68	S355JR	1	WI								
W775	1	PL10X100	100	0.610	1	0.61	S355JR	1	WI								
W780	4	PL10X156	577	6.947	4	27.79	S355JR	1	WI								
W801	4	PL25X260	550	28.064	4	112.26	S355JR	1	WI								
W802	8	PL10X260	474	7.889	8	63.11	S355JR	1	WI								
W803	1	PL10X296	577	9.368	1	9.37	S355JR	1	WI								
W1016	2	PL15X252	573	13.619	2	27.24	S355JR	1	WI								
W1017	2	PL25X96	340	5.792	2	11.58	S355JR	1	WI								
					UNIT WEIGHT		2978.09										
					TOTAL WEIGHT		2978.09										
BOLT LIST:-																	
BOLT \ STUD		BOLT DESCRIPTION		QTY/ONE	QTY/ALL	FINISH	REMARKS										
BOLT		B1N1W30 × 110 A325M		24	24												

PRIMARY CATEGORY

FW- J1 TO J60
CJP- J1 TO J3
PJP-J1 TO J2

WORK THIS SHEET WITH 2307085-STL-732-01-RF001-1

1 NO. RAFTER MKD' 2307085-STL-732-01-RF001











GA & IFC DRAWINGS REFERENCE	REV.
AD282-732-C-33226,27,28,29,30,31	4
AD282-732-C-33233,34,35,33499,33500	4
AD282-732-C-34337	2
AD282-732-C-34300	2

NOTES :

- ALL DIMENSIONS ARE GIVEN IN MILLIMETERS (U.N.O.).
- ☛ DENOTES ASSEMBLY ORIENTATION MARK.
- DON'T SCALE THE DRAWING. FOLLOW THE WRITTEN DIMENSIONS.
- FINISH AS PER PROJECT SPEC.
- STRUCTURAL STEELWORK SHALL BE IN ACCORDANCE WITH PROJECT SPECIFICATIONS AD282-732-G-03520 & AD282-732-G-03527
- WHEREVER THERE IS NO ACCESS FOR FILLET WELDING TO BE REPLACED BY FULL PENETRATION BUTT WELDING
- FOR CJP WELD MARKED LOCATIONS FOLLOW THIS DETAIL

- ALL WELDS TO BE 6mm FILLET WELD U.N.O.

GRID LOCATION	
EL+118.655	2-1/A

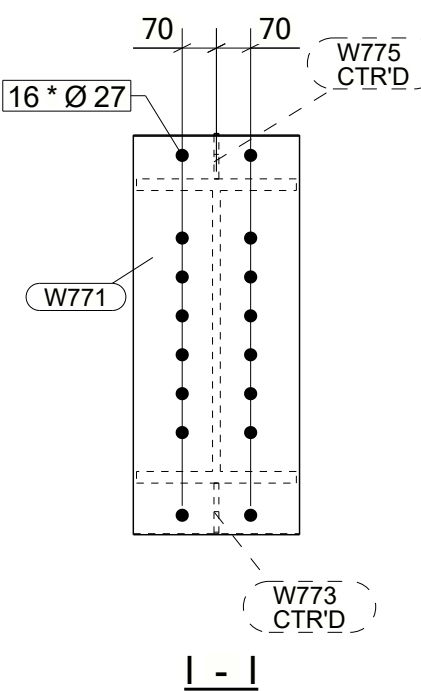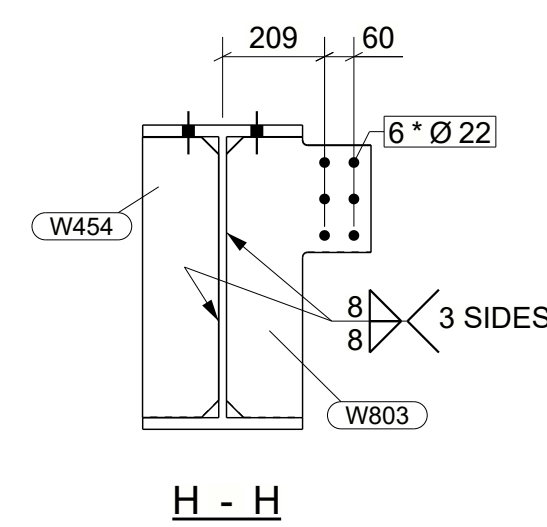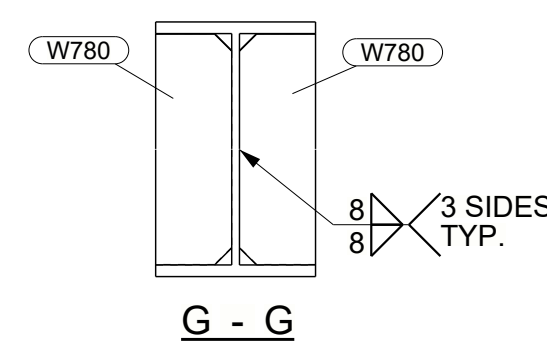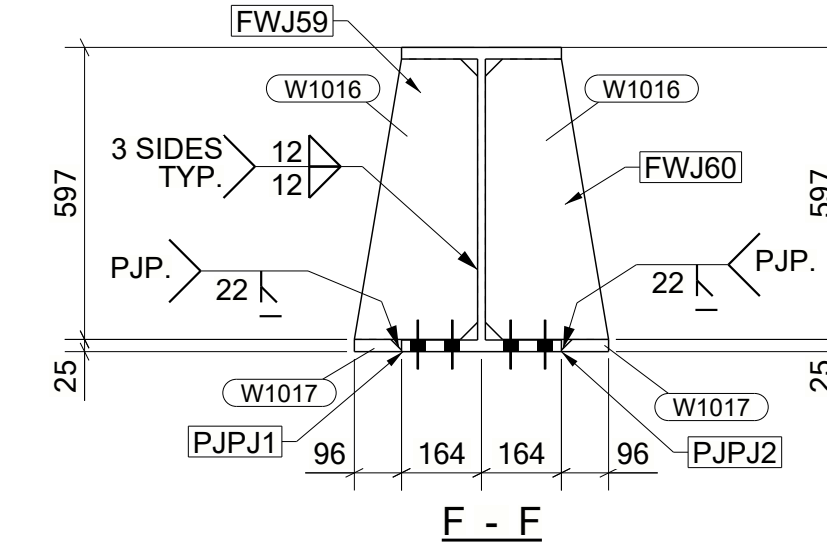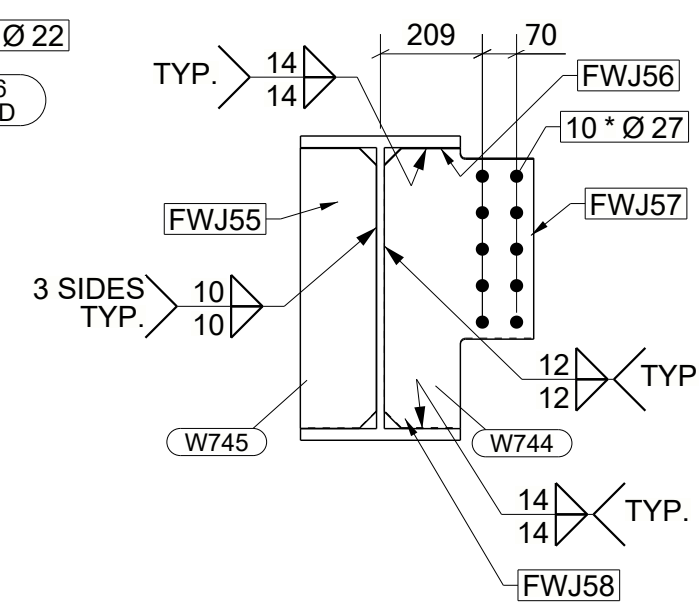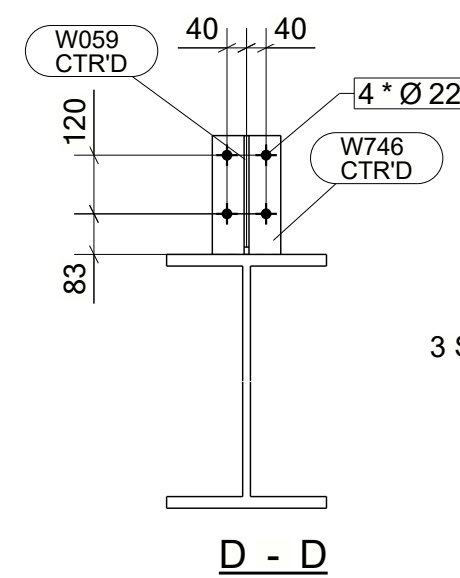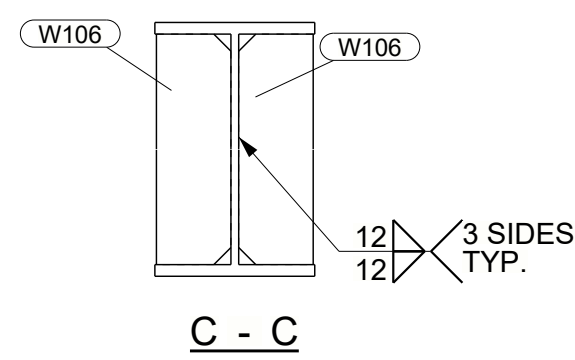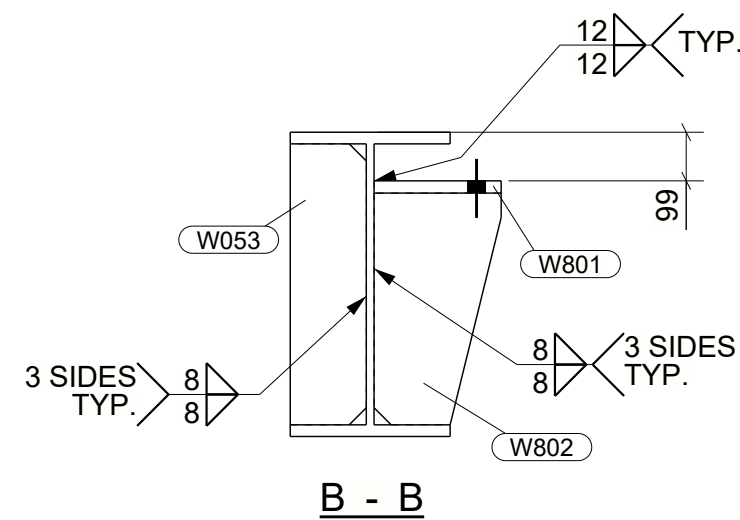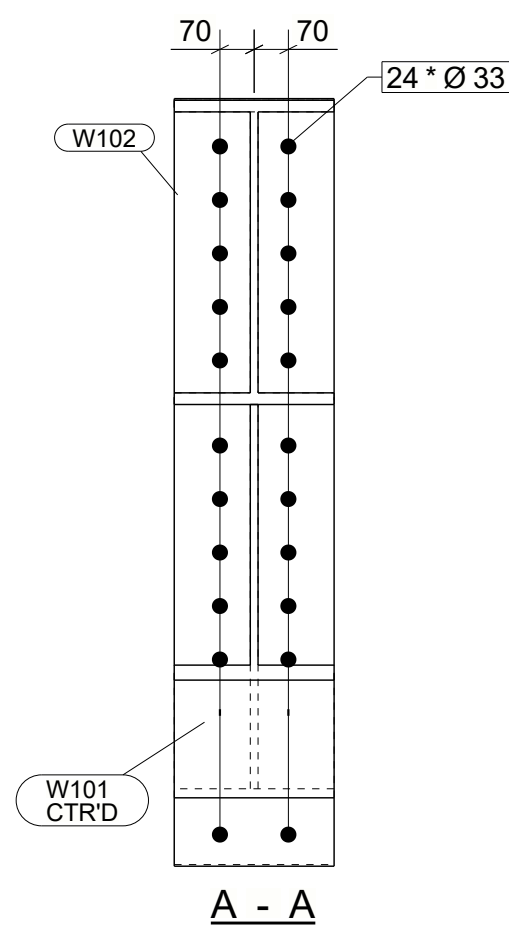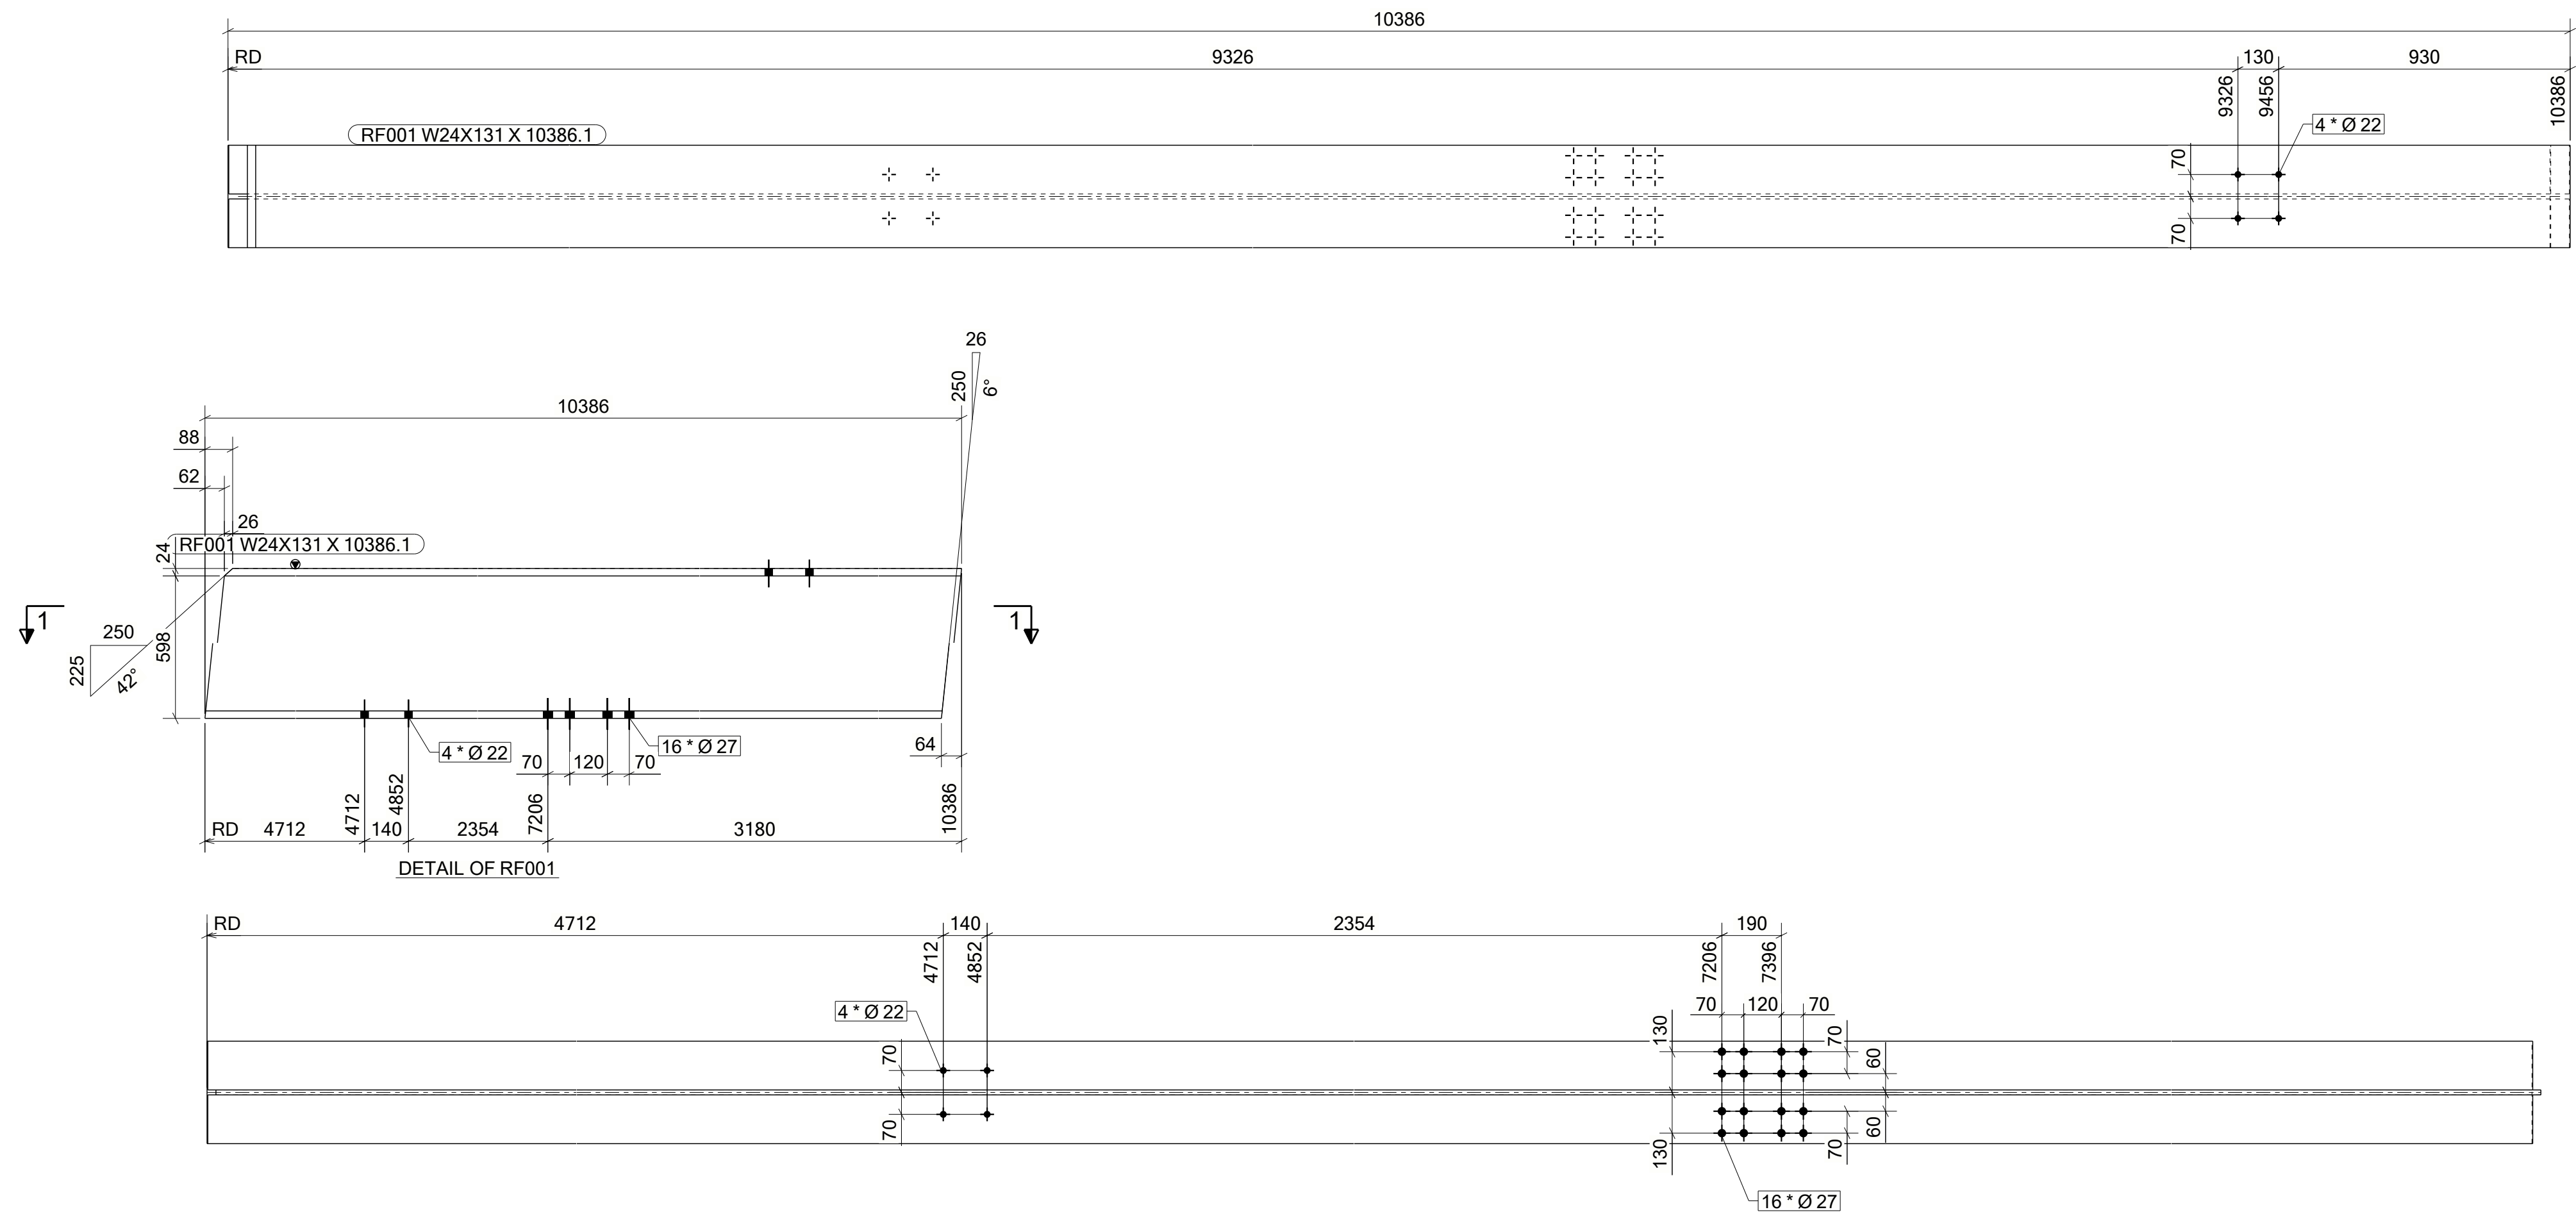

WORK THIS SHEET WITH 2307085-STL-732-01-RF001



GA & IFC DRAWINGS REFERENCE	REV.
AD282-732-C-33226,27,28,29,30,31	4
AD282-732-C-33233,34,35,33499,33600	4
AD282-732-C-34337	2
AD282-732-C-34300	2

NOTES :

- 1-ALL DIMENSIONS ARE GIVEN IN MILLIMETERS (U.N.O.).
- 2-  DENOTES ASSEMBLY ORIENTATION MARK.
- 3-DON'T SCALE THE DRAWING. FOLLOW THE WRITTEN DIMENSIONS.
- 4- FINISH AS PER PROJECT SPEC.
- 5- STRUCTURAL STEELWORK SHALL BE IN ACCORDANCE WITH PROJECT SPECIFICATIONS AD282-732-G-03520 & AD282-732-G-03527
- 6-WHEREVER THERE IS NO ACCESS FOR FILLET WELDING TO BE REPLACED BY FULL PENETRATION BUTT WELDING
- 7-FOR CIP WELD MARKED LOCATIONS FOLLOW THIS DETAIL


8-ALL WELDS TO BE 6mm FILLET WELD U.N.O.

GRID LOCATION	
EL +115.215	<732-09/<732-8

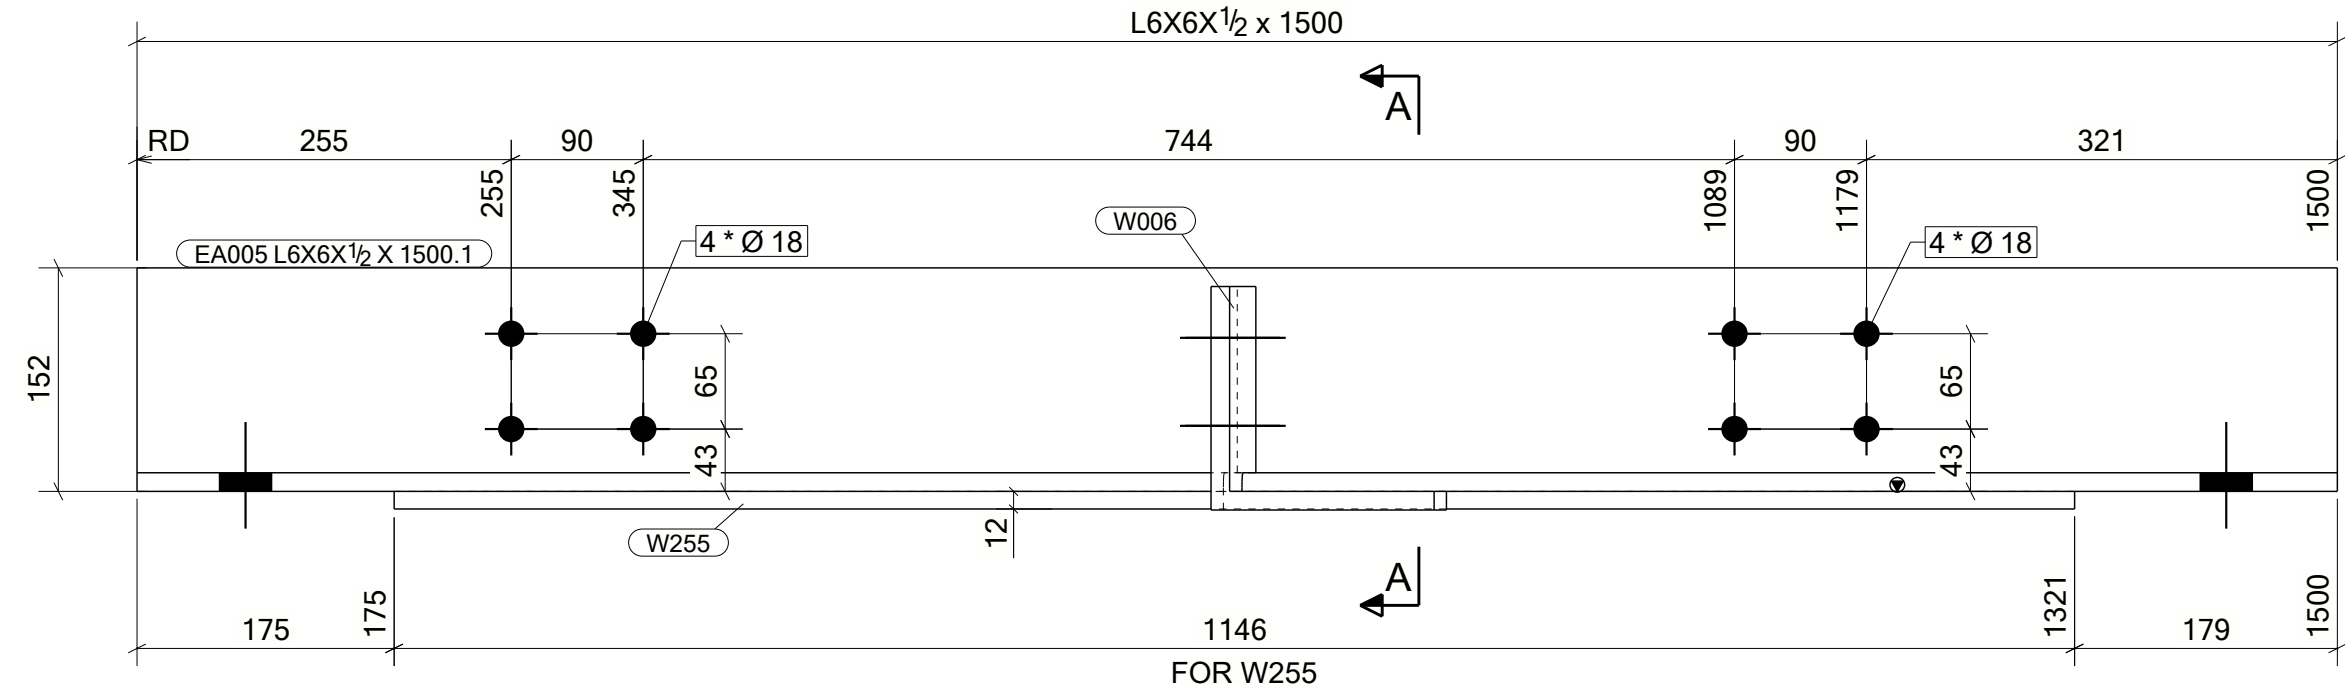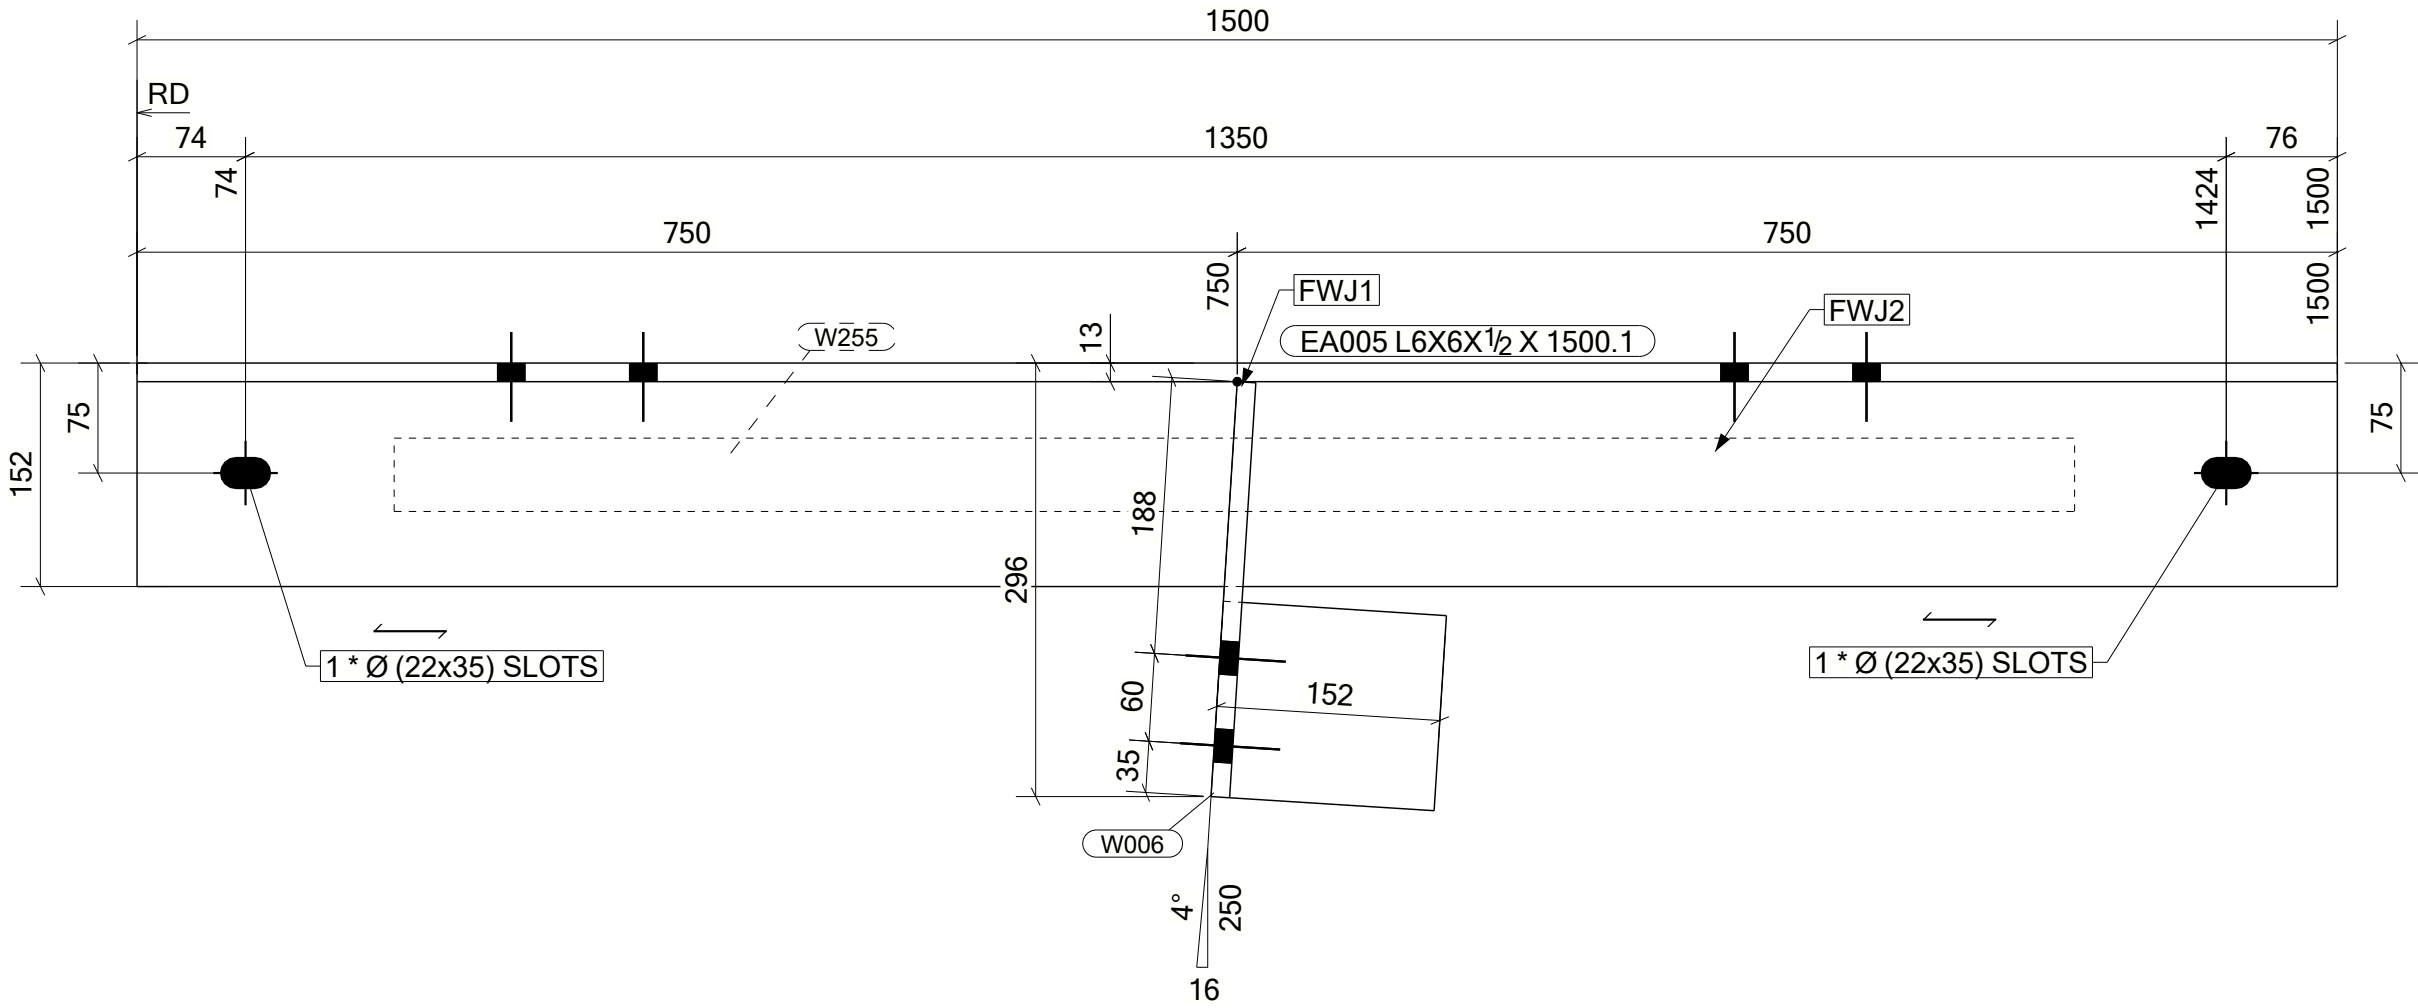

DRAWING NO. : 2307059-732-V-132-EA005										REV.: 00	
ERECTION MARK : 2307059-732-V-132-EA005			DESCRIPTION : EDGE_ANGLE			COLOR CODE : 10 B 15			QTY : 1		NOS
HOLD:		TYPE: W		TREAT: PN		COST CODE: 2.01			REMARKS:		
LENGTH: 1500		WIDTH: 305		HEIGHT: 165		TOTAL S.AREA: 1.2			(M2)		
POSITION NO.	QTY PER ASSLY	SECTION	LENGTH	UNIT WEIGHT (KG)	TOTAL WIEGHT (KG)		GRADE	REVISION	PART ID	TREATMENT	REMARKS
					QTY	WEIGHT					
EA005	1	L6X6X1/2	1500	43.837	1	43.84	A572-GR.50	1	MM	PN	
W006	1	L6X6X1/2	283	8.284	1	8.28	A572-GR.50	1	WI		
W255	1	PL12X50	1146	5.396	1	5.40	S355JR	1	WI		
					UNIT WEIGHT	57.52					
					TOTAL WEIGHT	57.52					
BOLT LIST:-											
BOLT \ STUD		BOLT DESCRIPTION		QTY/ONE	QTY/ALL	FINISH	REMARKS				
BOLT		B1N1W20 × 55 A325M		4	4						
BOLT		B2N1W20 × 60 SHOULDER BOLT		1	2						


ANCILLARY CATEGORY
FW-J1 TO J2

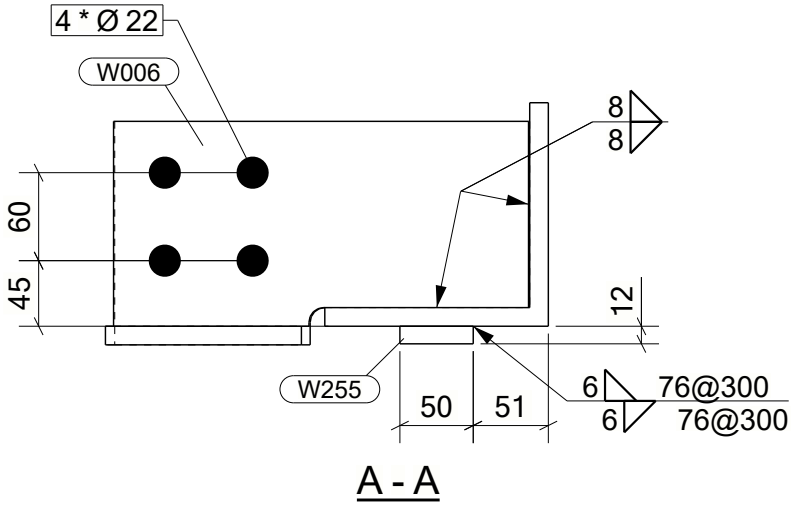

GA & IFC DRAWINGS REFERENCE	REV.
AD282-732-C-33298,299 & 300	3
AD282-732-C-34324	1
AD282-732-C-34287	1

NOTES :


- 1-ALL DIMENSIONS ARE GIVEN IN MILLIMETERS (U.N.O.).
- 2-● DENOTES ASSEMBLY ORIENTATION MARK.
- 3-DON'T SCALE THE DRAWING. FOLLOW THE WRITTEN DIMENSIONS.
- 4- FINISH AS PER PROJECT SPEC.
- 5- STRUCTURAL STEELWORK SHALL BE IN ACCORDANCE WITH PROJECT SPECIFICATIONS AD282-732-G-03520 & AD282-732-G-03527
- 6-WHEREVER THERE IS NO ACCESS FOR FILLET WELDING TO BE REPLACED BY FULL PENETRATION BUTT WELDING
- 7-FOR CJP WELD MARKED LOCATIONS FOLLOW THIS DETAIL

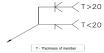

- 8-ALL WELDS TO BE 6mm FILLET WELD U.N.O.

GRID LOCATION	
EL +115.367	<732-09/<732-B

DRAWING NO. : 2307059-732-V-132-EA007										REV.: 00							
ERECTION MARK : 2307059-732-V-132-EA007										DESCRIPTION : EDGE_ANGLE		COLOR CODE : 10 B 15		QTY : 1		NOS	
HOLD:		TYPE: P		TREAT: PN		COST CODE: 2.01				REMARKS:							
LENGTH: 1735		WIDTH: 305		HEIGHT: 152		TOTAL S.AREA: 1.1				(M2)							
POSITION NO.	QTY PER ASSLY	SECTION		LENGTH	UNIT WEIGHT (KG)		TOTAL WIEGHT (KG)		GRADE	REVISION	PART ID	TREATMENT	REMARKS				
							QTY	WEIGHT									
EA007	1	L6X6X1/2		1754	51.242		1	51.24	A572-GR.50	1	MM	PN	ROLLING				
							UNIT WEIGHT		51.24								
							TOTAL WEIGHT		51.24								
BOLT LIST:-																	
BOLT \ STUD		BOLT DESCRIPTION			QTY/ONE		QTY/ALL		FINISH		REMARKS						
BOLT		B1N1W20 × 55 A325M			2		2										
BOLT		B2N1W20 × 60 SHOULDER BOLT			1		2										

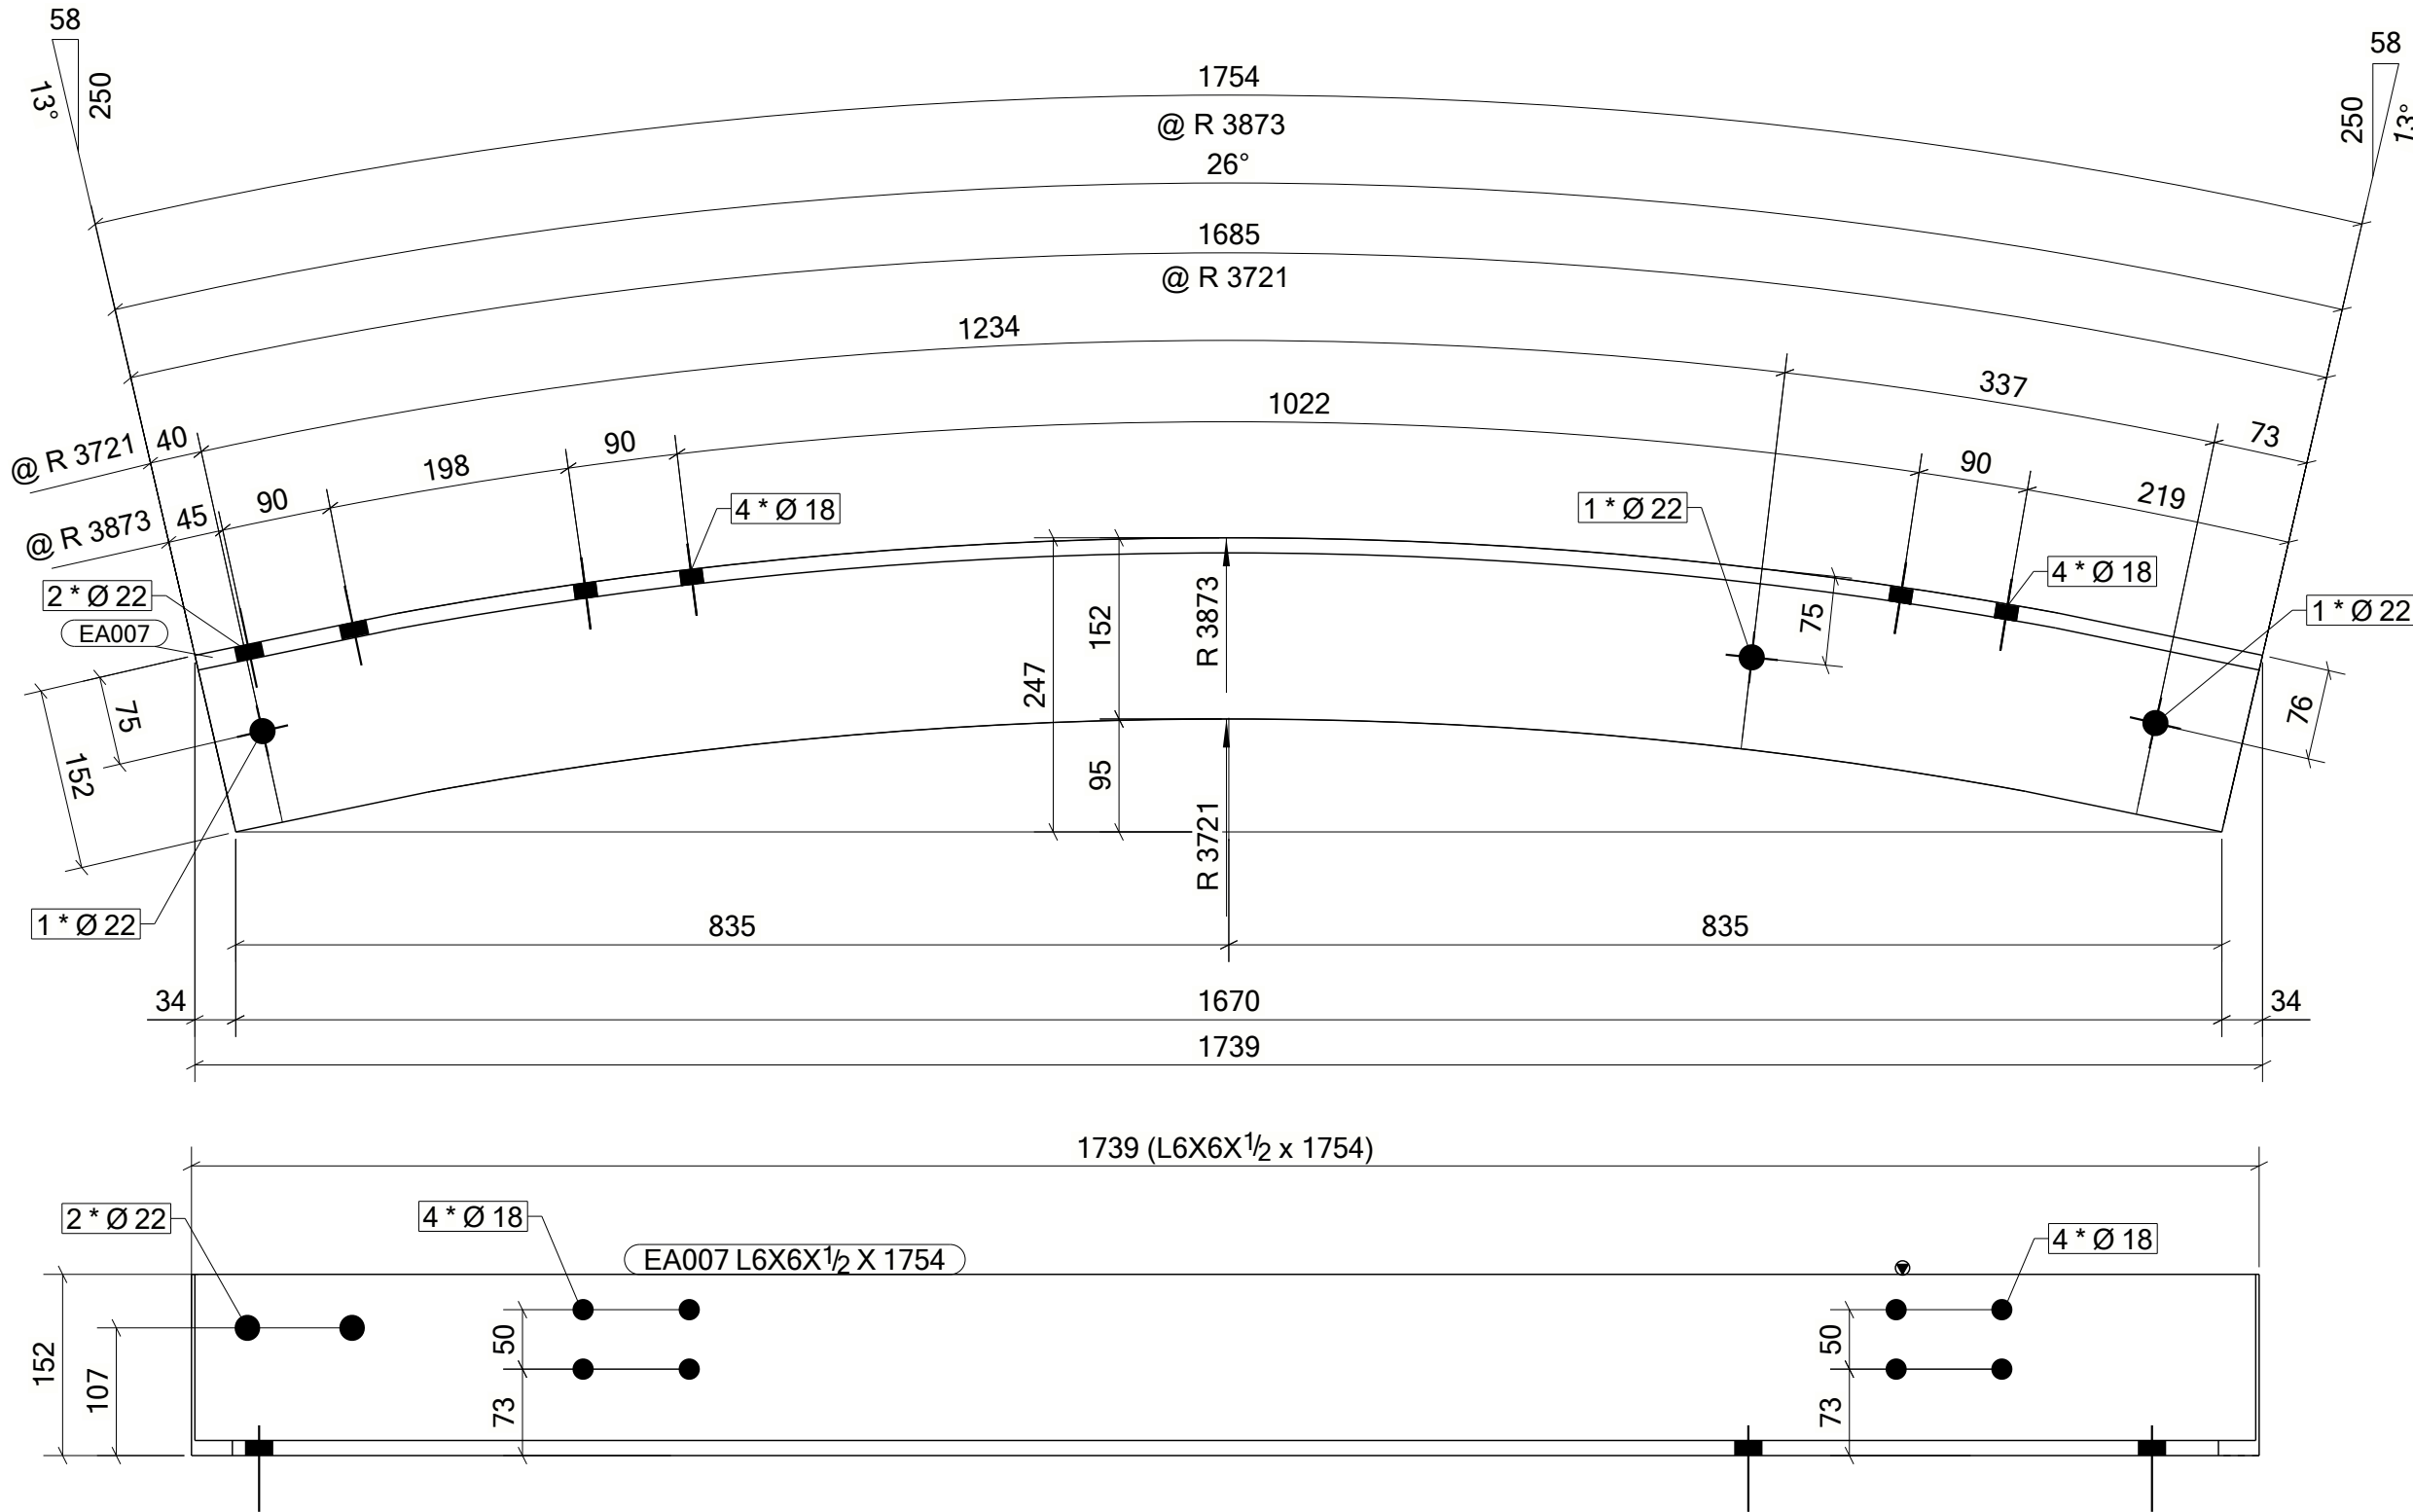

GA & IFC DRAWINGS REFERENCE	REV.
AD282-732-C-33298,299 & 300	3
AD282-732-C-34324	1
AD282-732-C-34287	1


NOTES :

- 1-ALL DIMENSIONS ARE GIVEN IN MILLIMETERS (U.N.O.).
- 2-  DENOTES ASSEMBLY ORIENTATION MARK.
- 3-DON'T SCALE THE DRAWING. FOLLOW THE WRITTEN DIMENSIONS.
- 4- FINISH AS PER PROJECT SPEC.
- 5- STRUCTURAL STEELWORK SHALL BE IN ACCORDANCE WITH PROJECT SPECIFICATIONS AD282-732-G-03520 & AD282-732-G-03527
- 6-WHEREVER THERE IS NO ACCESS FOR FILLET WELDING TO BE REPLACED BY FULL PENETRATION BUTT WELDING
- 7-FOR CJP WELD MARKED LOCATIONS FOLLOW THIS DETAIL

- 8-ALL WELDS TO BE 6mm FILLET WELD U.N.O.

GRID LOCATION	
EL +115.367	<732-09-732-09>/<732-B

DRAWING NO. : 2307059-732-V-132-EA017										REV.: 00	
ERECTION MARK : 2307059-732-V-132-EA017			DESCRIPTION : EDGE_ANGLE			COLOR CODE : 10 B 15			QTY : 1		NOS
HOLD:		TYPE: P	TREAT: PN		COST CODE: 2.01			REMARKS:			
LENGTH: 3139		WIDTH: 1575		HEIGHT: 152		TOTAL S.AREA: 2.2			(M2)		
POSITION NO.	QTY PER ASSLY	SECTION	LENGTH	UNIT WEIGHT (KG)	TOTAL WIEGHT (KG)		GRADE	REVISION	PART ID	TREATMENT	REMARKS
					QTY	WEIGHT					
EA017	1	L6X6X1/2	3539	103.423	1	103.42	A572-GR.50	1	MM	PN	ROLLING
					UNIT WEIGHT	103.42					
					TOTAL WEIGHT	103.42					
BOLT LIST:-											
BOLT \ STUD	BOLT DESCRIPTION			QTY/ONE	QTY/ALL	FINISH	REMARKS				
BOLT	B2N1W20 × 60 SHOULDER BOLT			1	4						

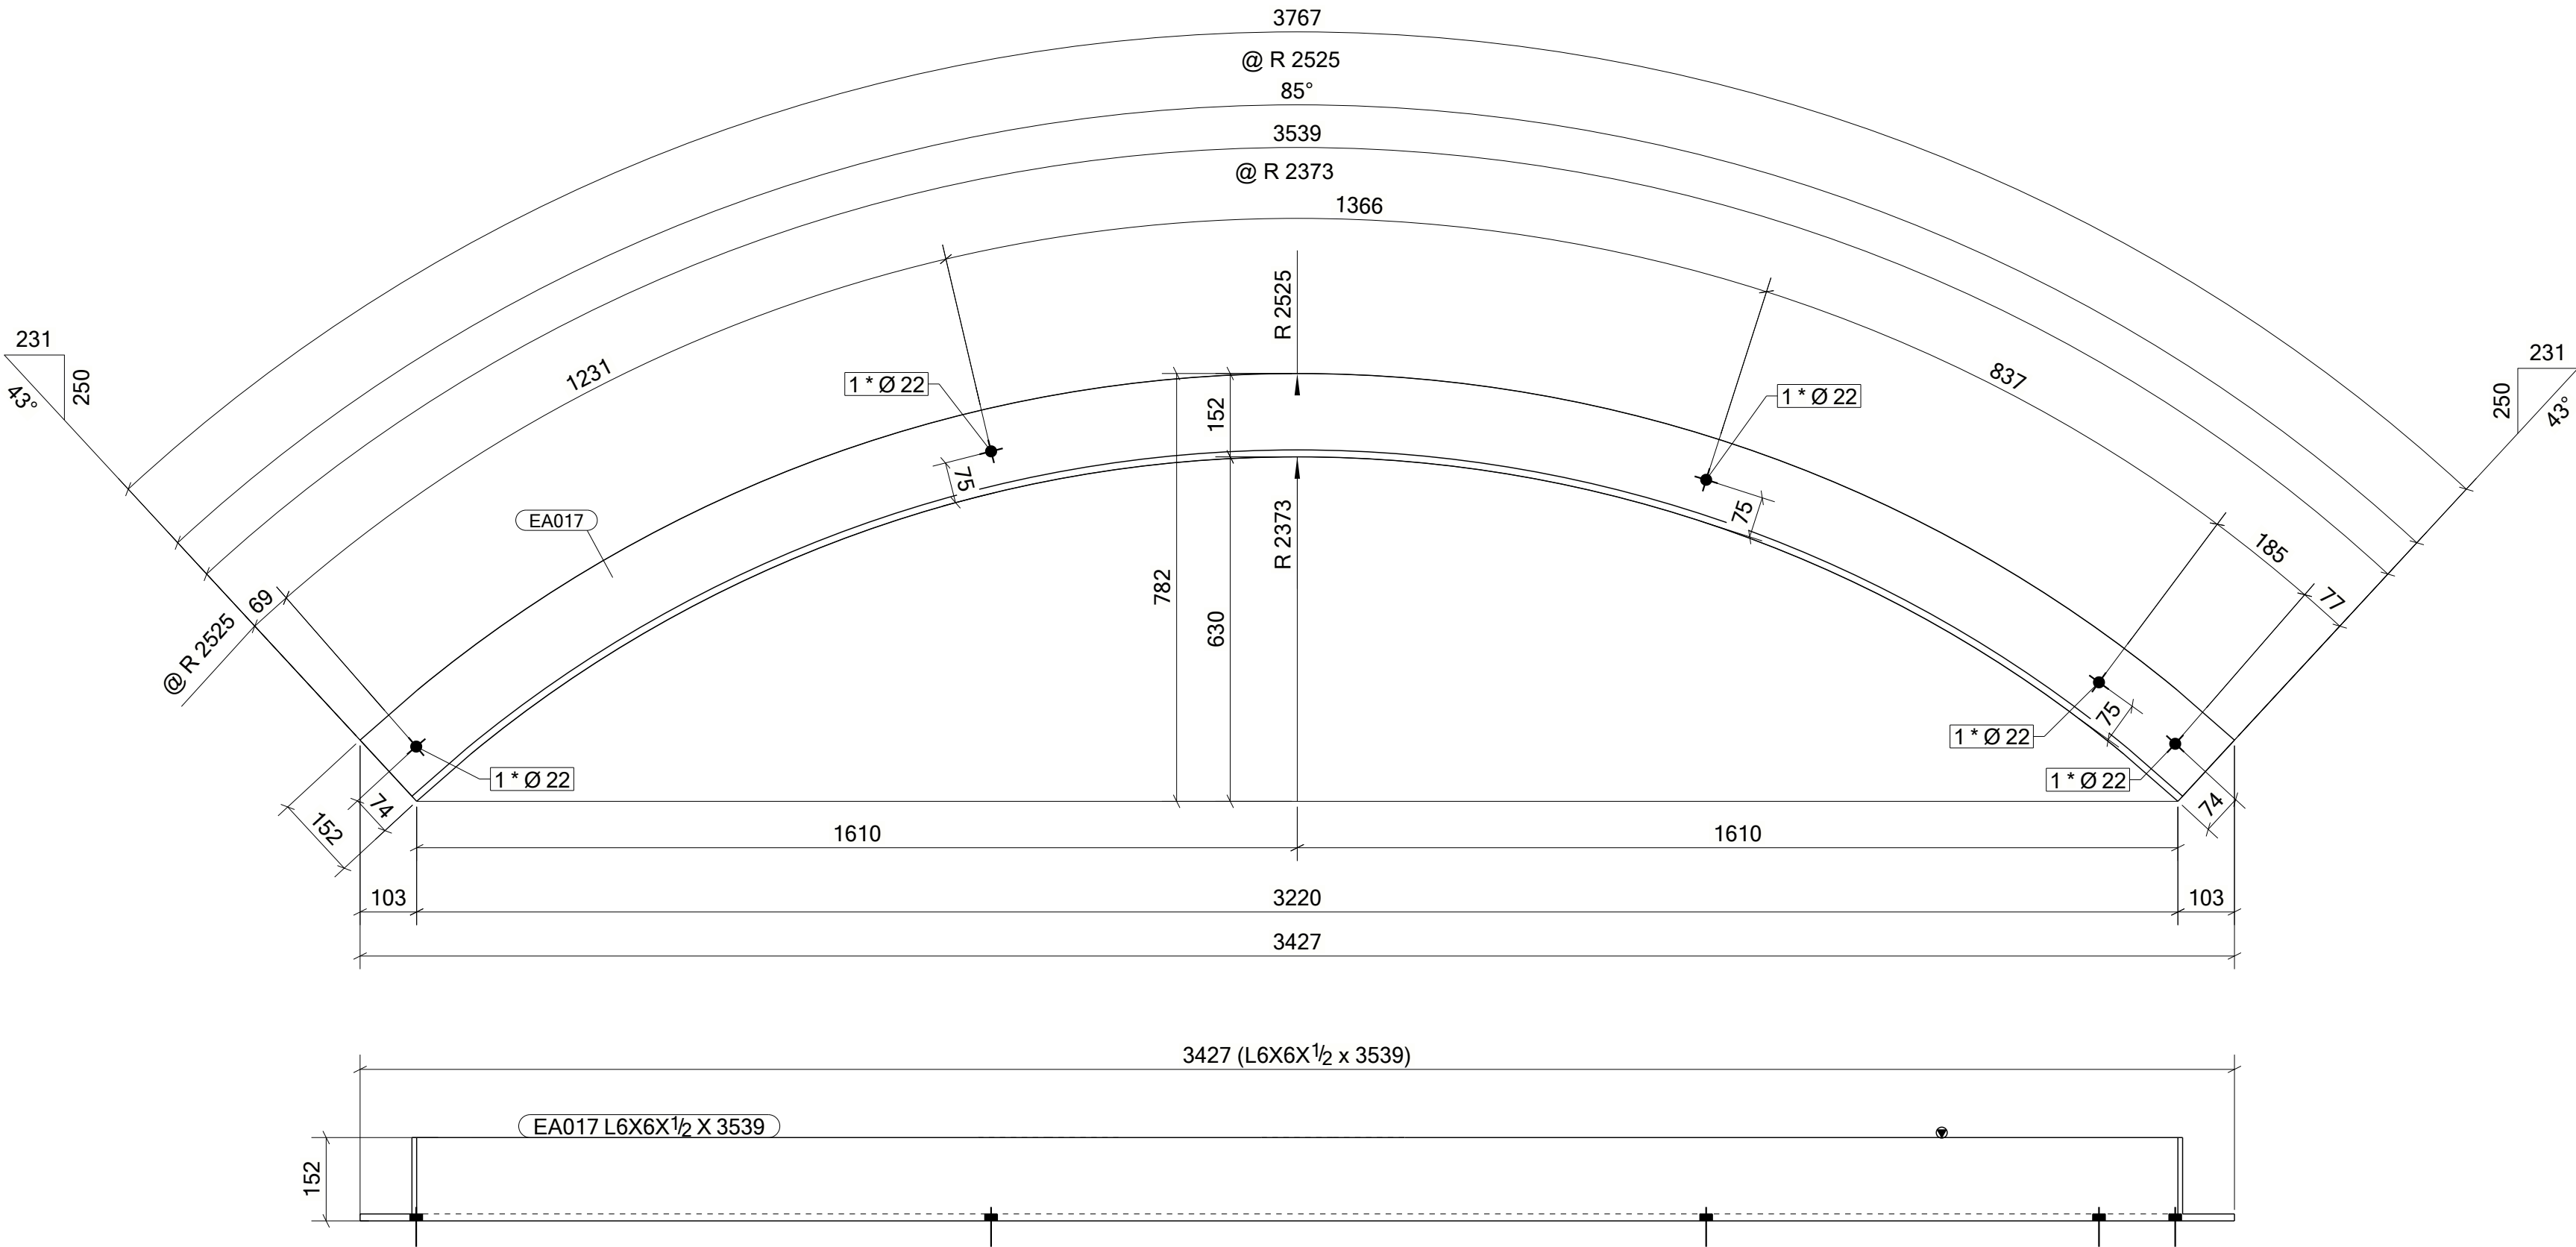


GA & IFC DRAWINGS REFERENCE	REV.
AD282-732-C-33298,299 & 300	3
AD282-732-C-34324	1
AD282-732-C-34287	1


- NOTES :**
- 1-ALL DIMENSIONS ARE GIVEN IN MILLIMETERS (U.N.O.).
 - 2-  DENOTES ASSEMBLY ORIENTATION MARK.
 - 3-DON'T SCALE THE DRAWING. FOLLOW THE WRITTEN DIMENSIONS.
 - 4- FINISH AS PER PROJECT SPEC.
 - 5- STRUCTURAL STEELWORK SHALL BE IN ACCORDANCE WITH PROJECT SPECIFICATIONS AD282-732-G-03520 & AD282-732-G-03527
 - 6-WHEREVER THERE IS NO ACCESS FOR FILLET WELDING TO BE REPLACED BY FULL PENETRATION BUTT WELDING
 - 7-FOR CJP WELD MARKED LOCATIONS FOLLOW THIS DETAIL
- 
- 8-ALL WELDS TO BE 6mm FILLET WELD U.N.O.

GRID LOCATION	
EL +118.185	<732-09/<732-B-732-B>

DRAWING NO. : 2307059-732-V-132-BE001										REV.: 00	
ERECTION MARK : 2307059-732-V-132-BE001				DESCRIPTION : BEAM			COLOR CODE : 10 B 15		QTY : 1		NOS
HOLD:		TYPE: W		TREAT: PN		COST CODE: 2.02		REMARKS:			
LENGTH: 4689		WIDTH: 286		HEIGHT: 210		TOTAL S.AREA: 6.5		(M2)			
POSITION NO.	QTY PER ASSLY	SECTION	LENGTH	UNIT WEIGHT (KG)	TOTAL WIEGHT (KG)		GRADE	REVISION	PART ID	TREATMENT	REMARKS
					QTY	WEIGHT					
BE001	1	W8X40	4689	277.823	1	277.82	S275JR	1	MM	PN	
W095	7	PL10X98	181	1.398	7	9.79	S355JR	1	WI		
W096	2	PL10X178	181	2.218	2	4.44	S355JR	1	WI		
W099	5	PL16X90	220	2.487	5	12.43	S355JR	1	WI		
W145	5	PL10X79	98	0.612	5	3.06	S355JR	1	WI		
					UNIT WEIGHT	307.54					
					TOTAL WEIGHT	307.54					
BOLT LIST:-											
BOLT \ STUD		BOLT DESCRIPTION		QTY/ONE		QTY/ALL		FINISH		REMARKS	
BOLT		B1N1W20 X 50 A325M		4		8					

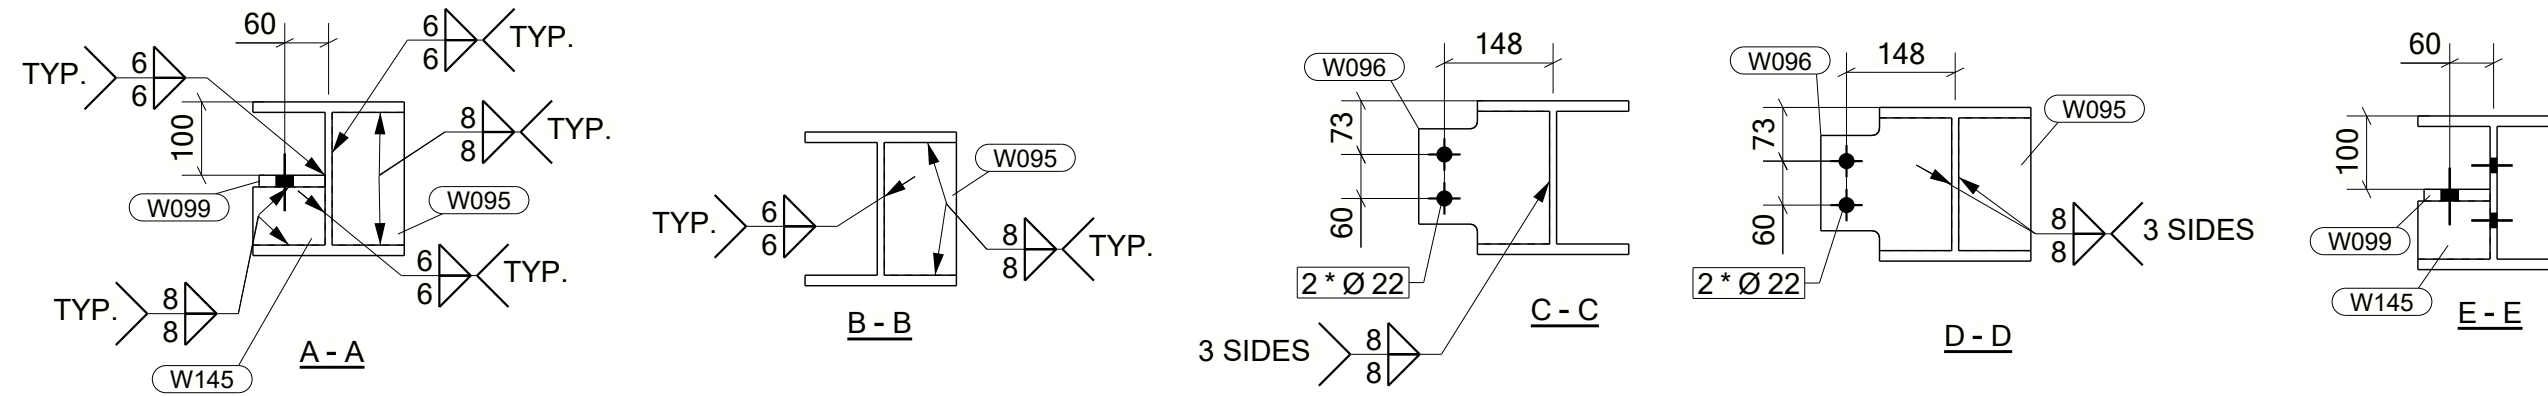

<u>ANCILLARY CATEGORY</u> FW-J1 TO J30
--


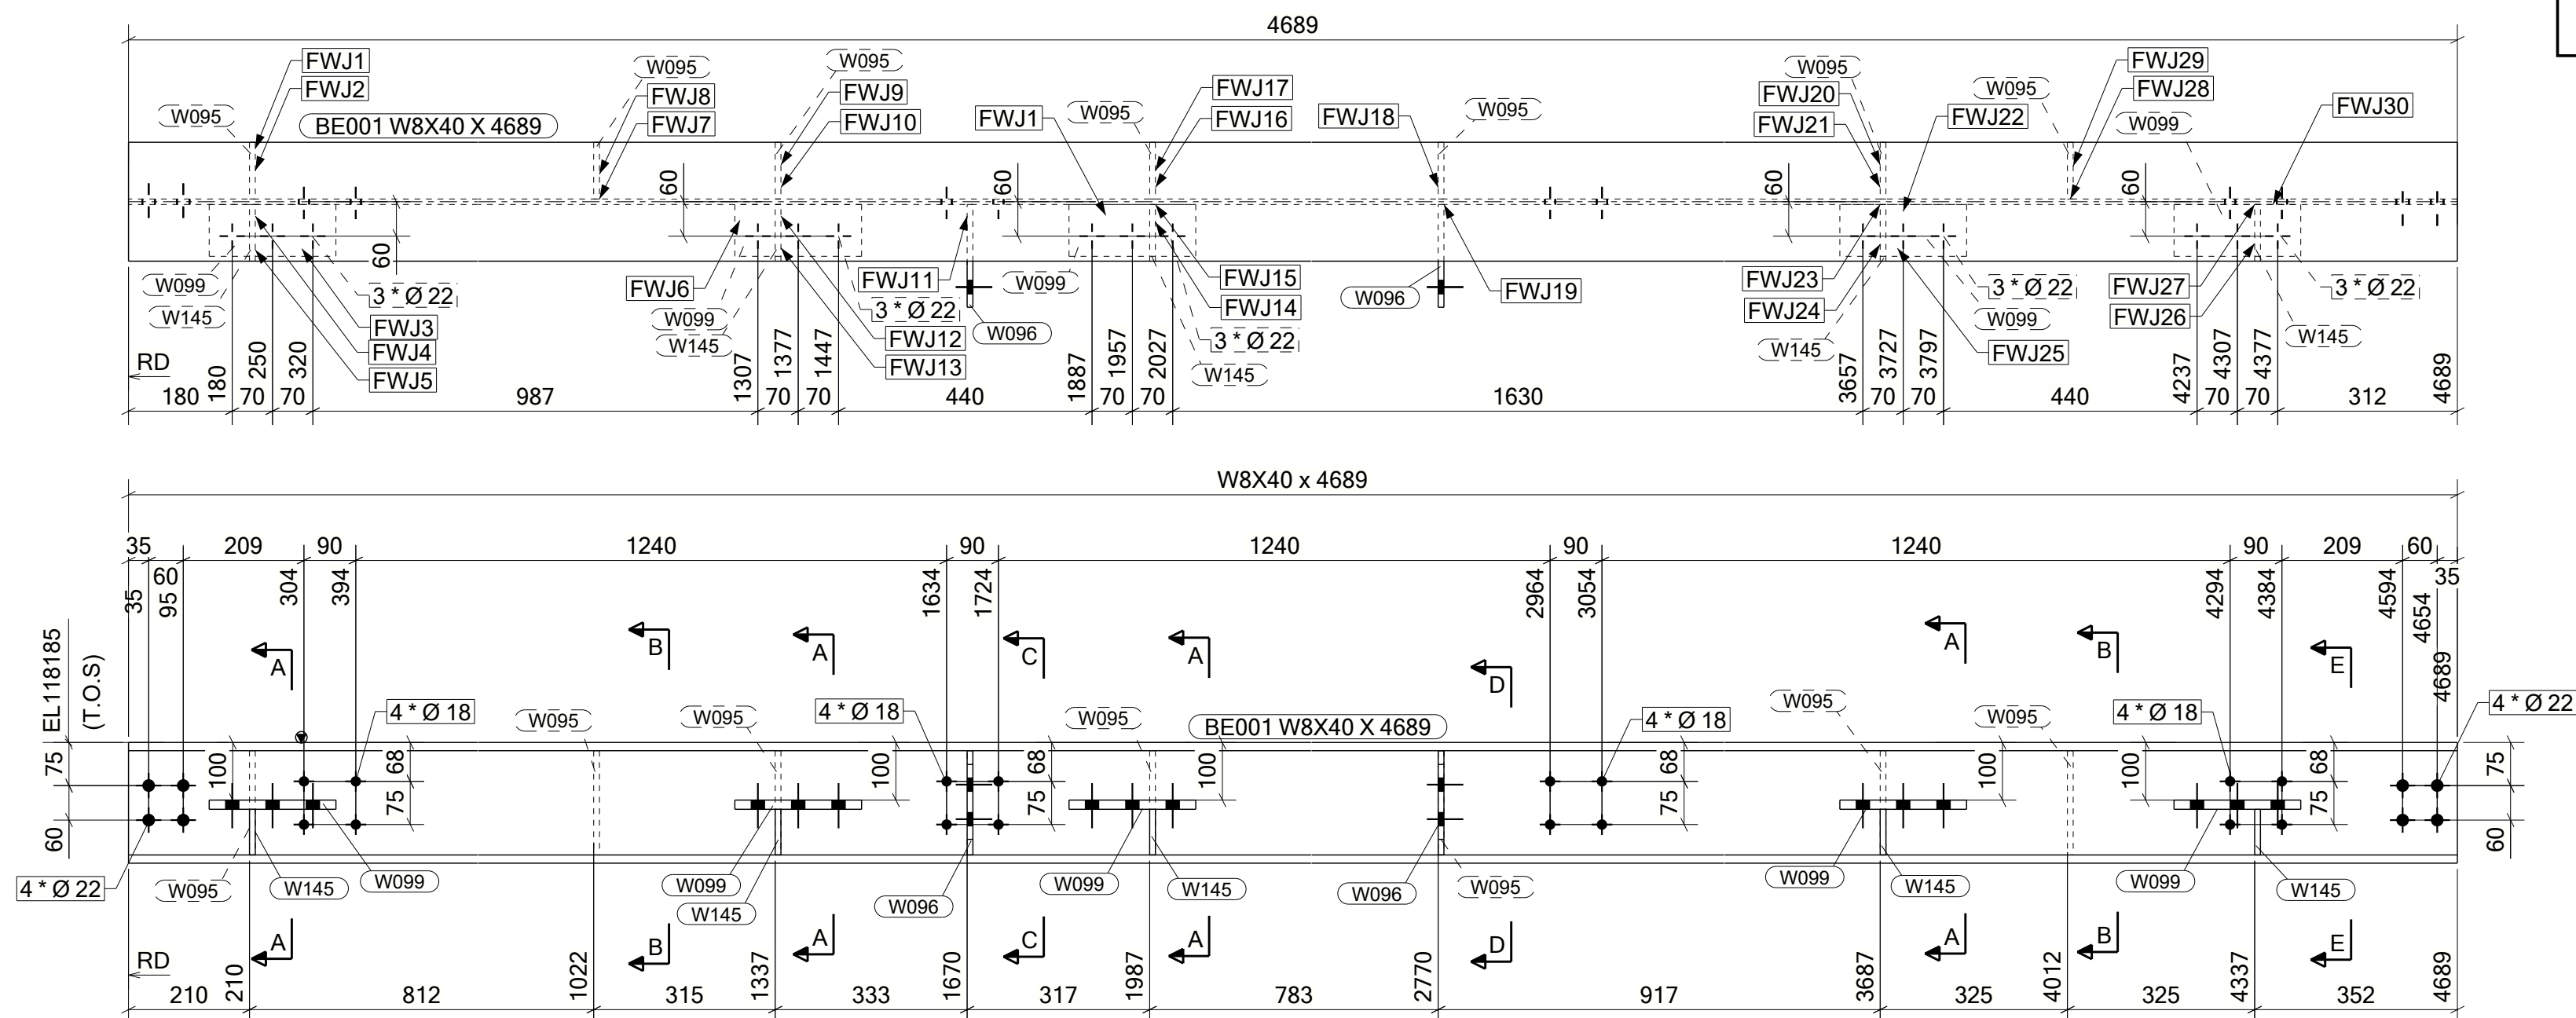


GA & IFC DRAWINGS REFERENCE	REV.
AD282-732-C-33298,299 & 300	3
AD282-732-C-34324	1
AD282-732-C-34287	1

- ## NOTES :
- 1-ALL DIMENSIONS ARE GIVEN IN MILLIMETERS (U.N.O.).
 - 2-  DENOTES ASSEMBLY ORIENTATION MARK.
 - 3-DON'T SCALE THE DRAWING. FOLLOW THE WRITTEN DIMENSIONS.
 - 4- FINISH AS PER PROJECT SPEC.
 - 5- STRUCTURAL STEELWORK SHALL BE IN ACCORDANCE WITH PROJECT SPECIFICATIONS AD282-732-G-03520 & AD282-732-G-03527
 - 6-WHEREVER THERE IS NO ACCESS FOR FILLET WELDING TO BE REPLACED BY FULL PENETRATION BUTT WELDING
 - 7-FOR CIP WELD MARKED LOCATIONS FOLLOW THIS DETAIL
- 

(1) MINIMUM WELDS
- 8-ALL WELDS TO BE 6mm FILLET WELD U.N.O.


GRID LOCATION	
EL +118.185	<732-09/732-B>

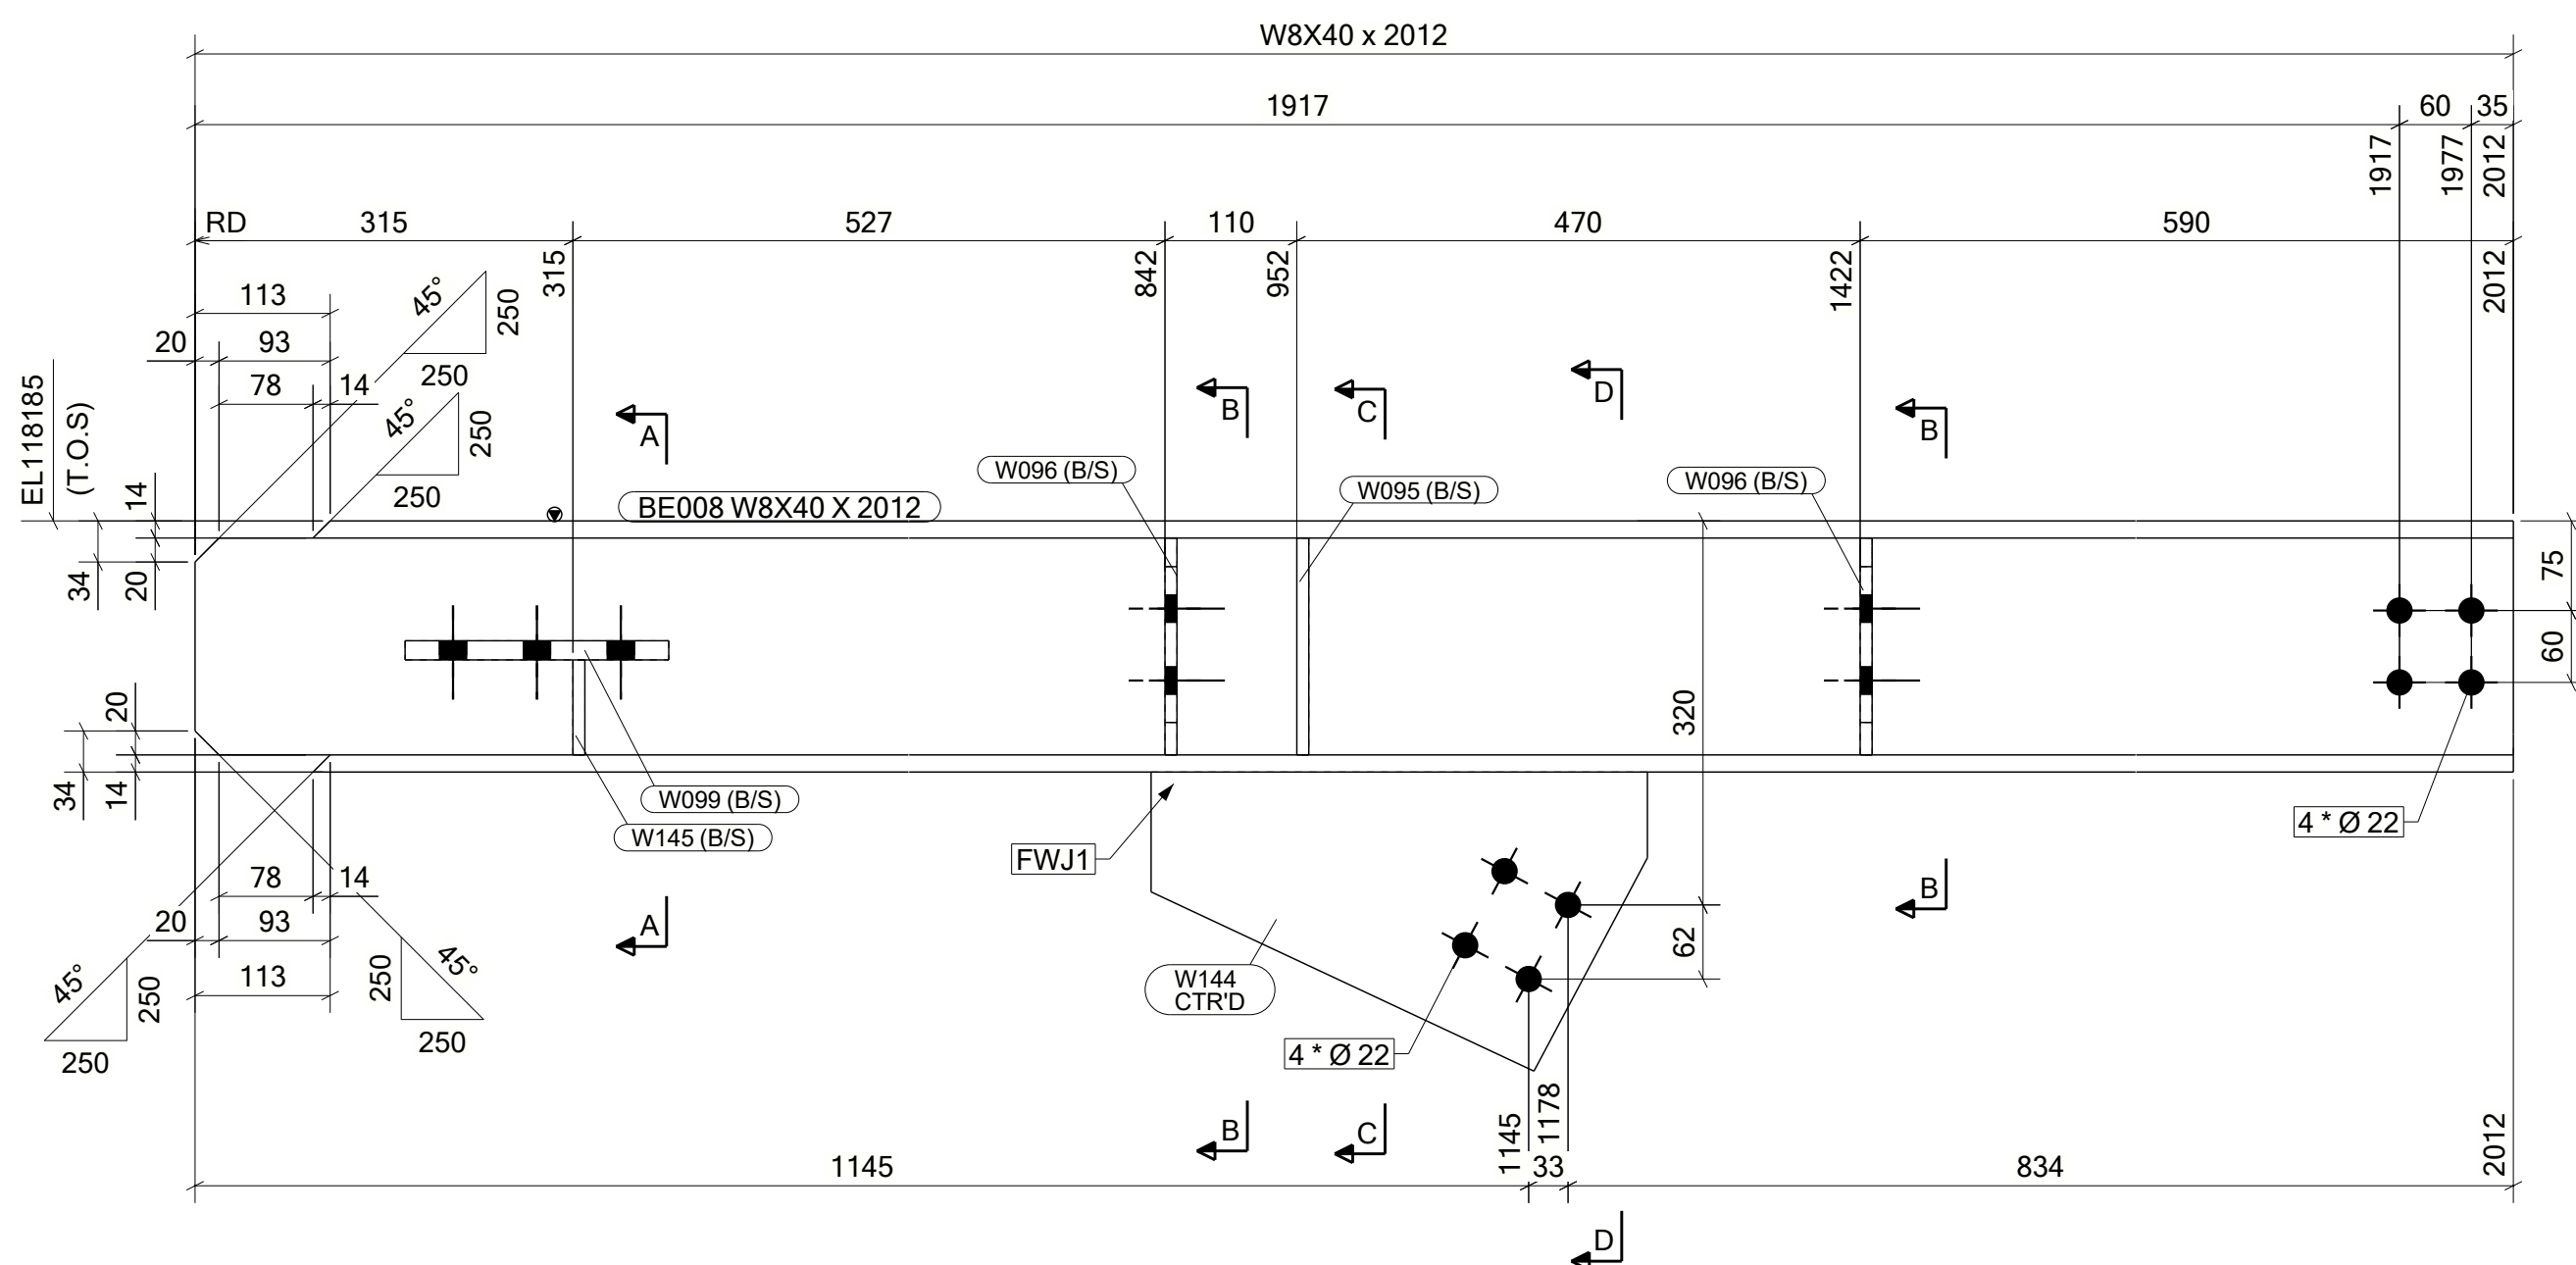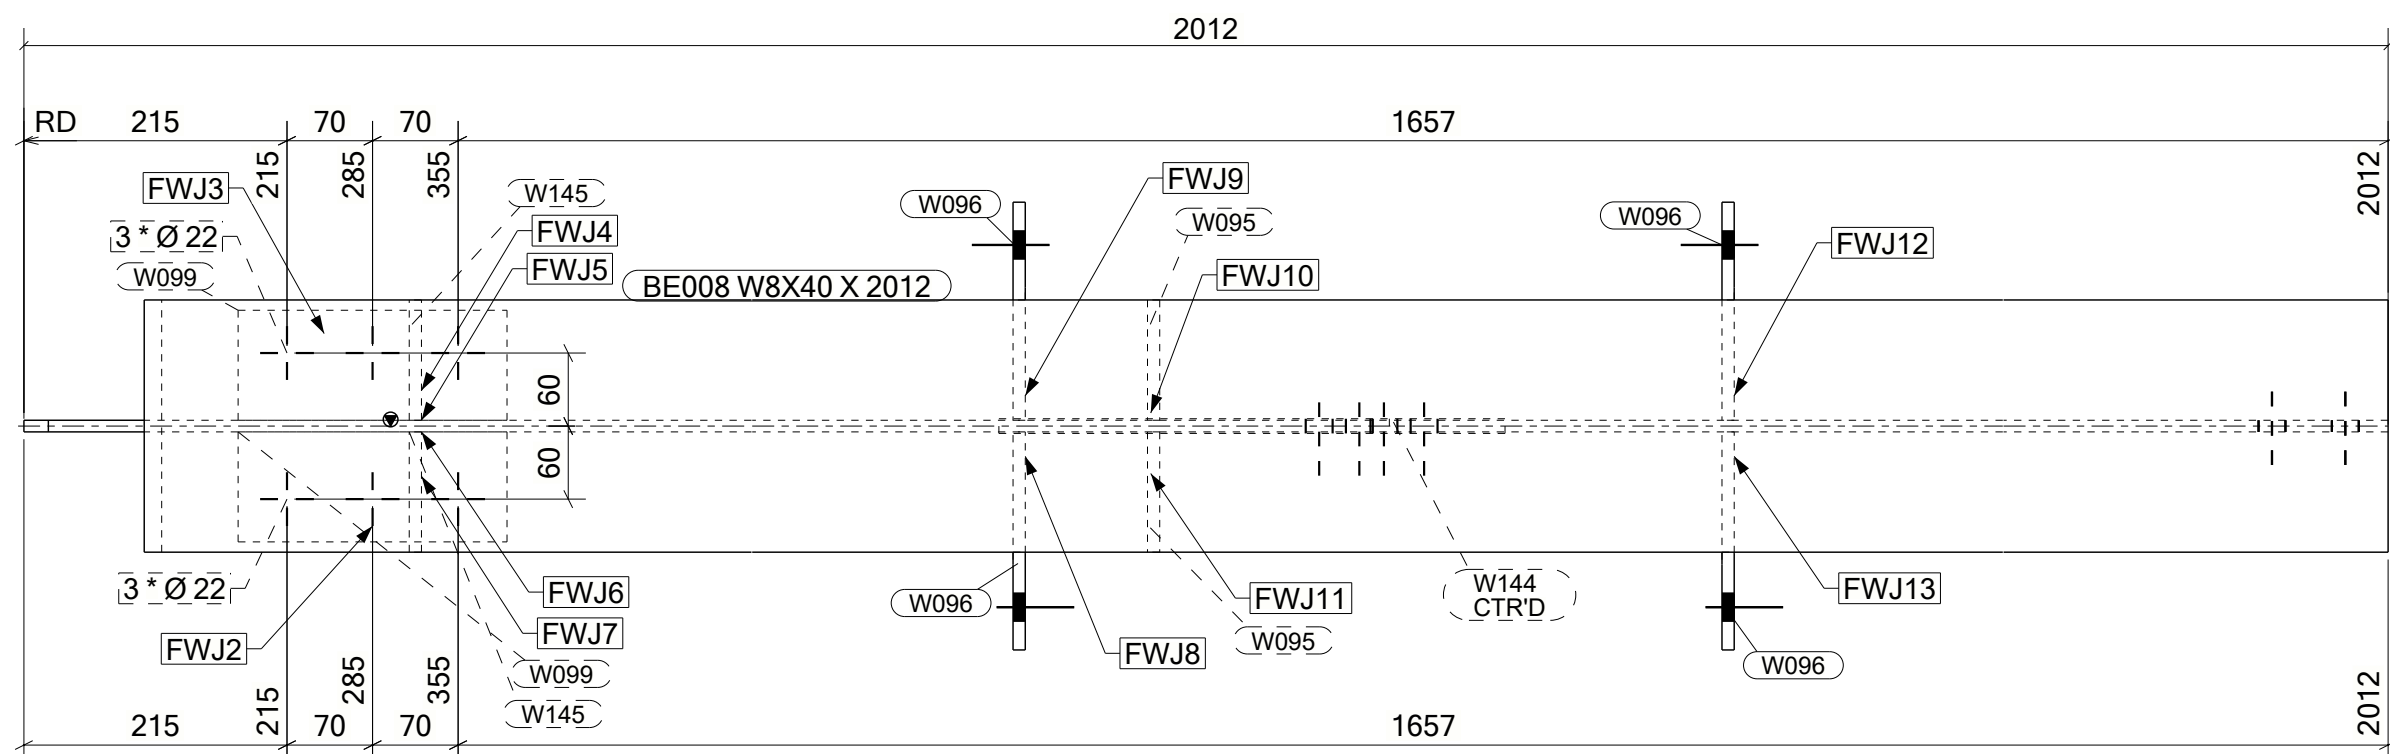

DRAWING NO. : 2307059-732-V-132-BE008										REV.: 00	
ERECTION MARK : 2307059-732-V-132-BE008				DESCRIPTION : BEAM			COLOR CODE : 10 B 15		QTY : 1		NOS
HOLD: WB020A		TYPE: W		TREAT: PN		COST CODE: 2.02		REMARKS:			
LENGTH: 2012		WIDTH: 366		HEIGHT: 459		TOTAL S.AREA: 3.0		(M2)			
POSITION NO.	QTY PER ASSLY	SECTION	LENGTH	UNIT WEIGHT (KG)	TOTAL WIEGHT (KG)		GRADE	REVISION	PART ID	TREATMENT	REMARKS
					QTY	WEIGHT					
BE008	1	W8X40	2012	119.223	1	119.22	S275JR	1	MM	PN	
W095	2	PL10X98	181	1.398	2	2.80	S355JR	1	WI		
W096	4	PL10X178	181	2.218	4	8.87	S355JR	1	WI		
W099	2	PL16X90	220	2.487	2	4.97	S355JR	1	WI		
W144	1	PL12X250	414	6.691	1	6.69	S355JR	1	WI		
W145	2	PL10X79	98	0.612	2	1.22	S355JR	1	WI		
					UNIT WEIGHT	143.78					
					TOTAL WEIGHT	143.78					
BOLT LIST:-											
BOLT \ STUD		BOLT DESCRIPTION		QTY/ONE	QTY/ALL	FINISH	REMARKS				
BOLT		B1N1W20 × 50 A325M		4	4						

ANCILLARY CATEGORY

FW-J1 TO J13

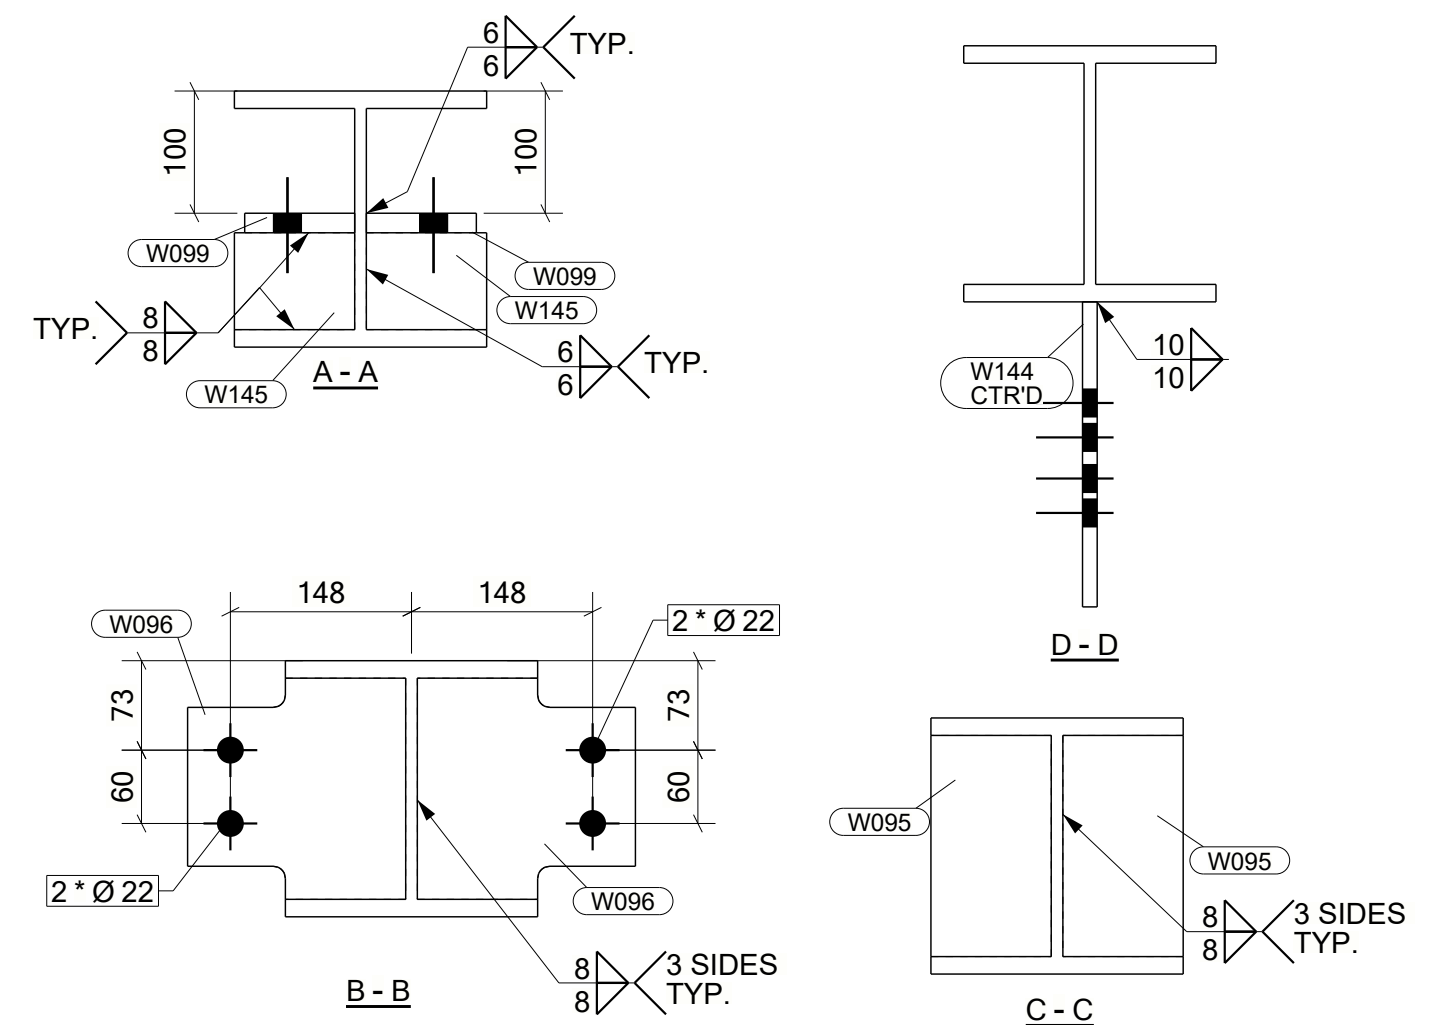

GA & IFC DRAWINGS REFERENCE	REV.
AD282-732-C-33298,299 & 300	3
AD282-732-C-34324	1
AD282-732-C-34287	1

NOTES :



- 1-ALL DIMENSIONS ARE GIVEN IN MILLIMETERS (U.N.O.).
- 2-  DENOTES ASSEMBLY ORIENTATION MARK.
- 3-DON'T SCALE THE DRAWING. FOLLOW THE WRITTEN DIMENSIONS.
- 4- FINISH AS PER PROJECT SPEC.
- 5- STRUCTURAL STEELWORK SHALL BE IN ACCORDANCE WITH PROJECT SPECIFICATIONS AD282-732-G-03520 & AD282-732-G-03527
- 6-WHEREVER THERE IS NO ACCESS FOR FILLET WELDING TO BE REPLACED BY FULL PENETRATION BUTT WELDING
- 7-FOR CIP WELD MARKED LOCATIONS FOLLOW THIS DETAIL

8-ALL WELDS TO BE 6mm FILLET WELD U.N.O.

GRID LOCATION	
EL +118.185	<732-09/732-B>

DRAWING NO. : 2307059-732-V-132-BE026										REV.: 00				
ERECTION MARK : 2307059-732-V-132-BE026				DESCRIPTION : BEAM				COLOR CODE : 10 B 15			QTY : 1		NOS	
HOLD:		TYPE: W		TREAT: PN		COST CODE: 2.01				REMARKS:				
LENGTH: 1256		WIDTH: 282		HEIGHT: 206		TOTAL S.AREA: 1.2				(M2)				
POSITION NO.	QTY PER ASSLY	SECTION	LENGTH	UNIT WEIGHT (KG)	TOTAL WIEGHT (KG)		GRADE	REVISION	PART ID	TREATMENT	REMARKS			
					QTY	WEIGHT								
BE026	1	W8X15	1256	28.243	1	28.24	S275JR	1	MM	PN				
W097	2	PL10X128	190	1.532	2	3.06	S355JR	1	WI					
W146	2	PL10X48	190	0.712	2	1.42	S355JR	1	WI					
W246	2	PL10X75	148	0.759	2	1.52	S355JR	1	WI					
					UNIT WEIGHT		34.25							
					TOTAL WEIGHT		34.25							
BOLT LIST:-														
BOLT / STUD		BOLT DESCRIPTION		QTY/ONE	QTY/ALL	FINISH	REMARKS							
BOLT		B1N1W20 × 50 A325M		2	4									


ANCILLARY CATEGORY
FW-J1 TO J5

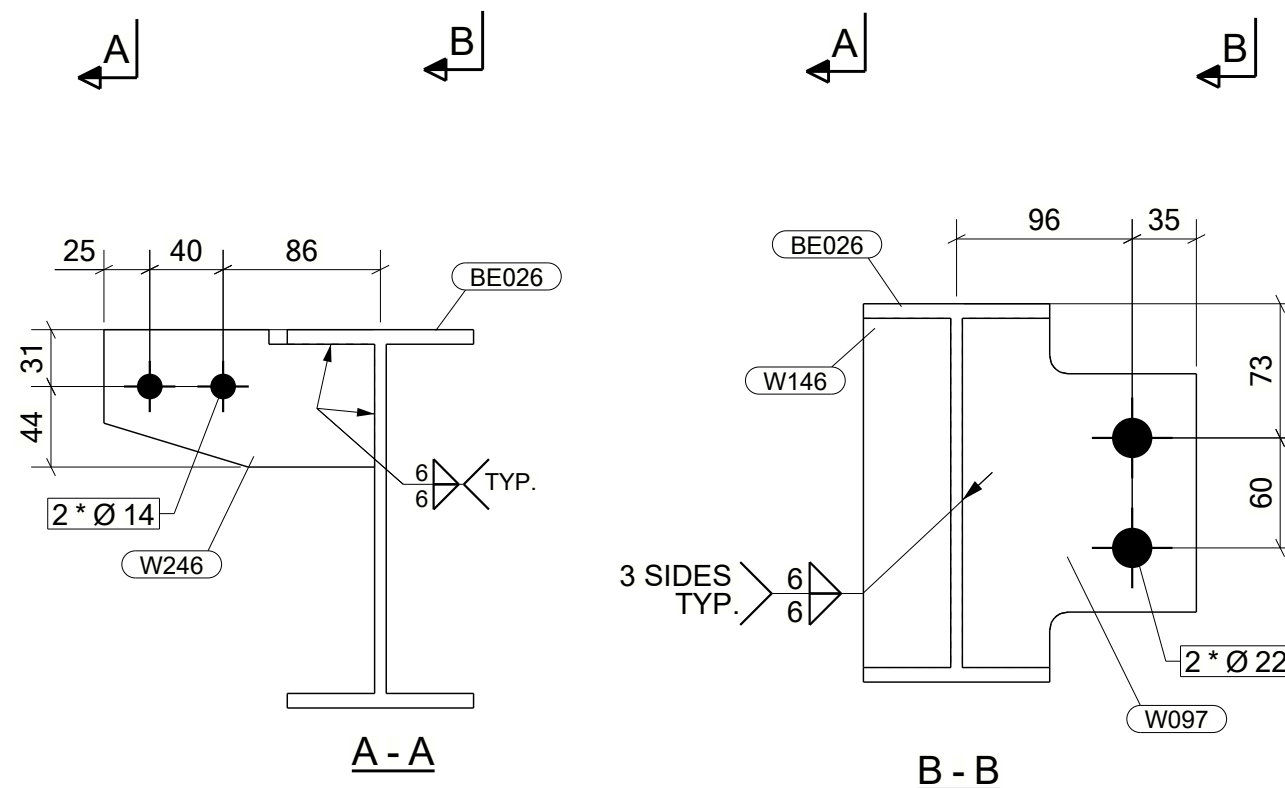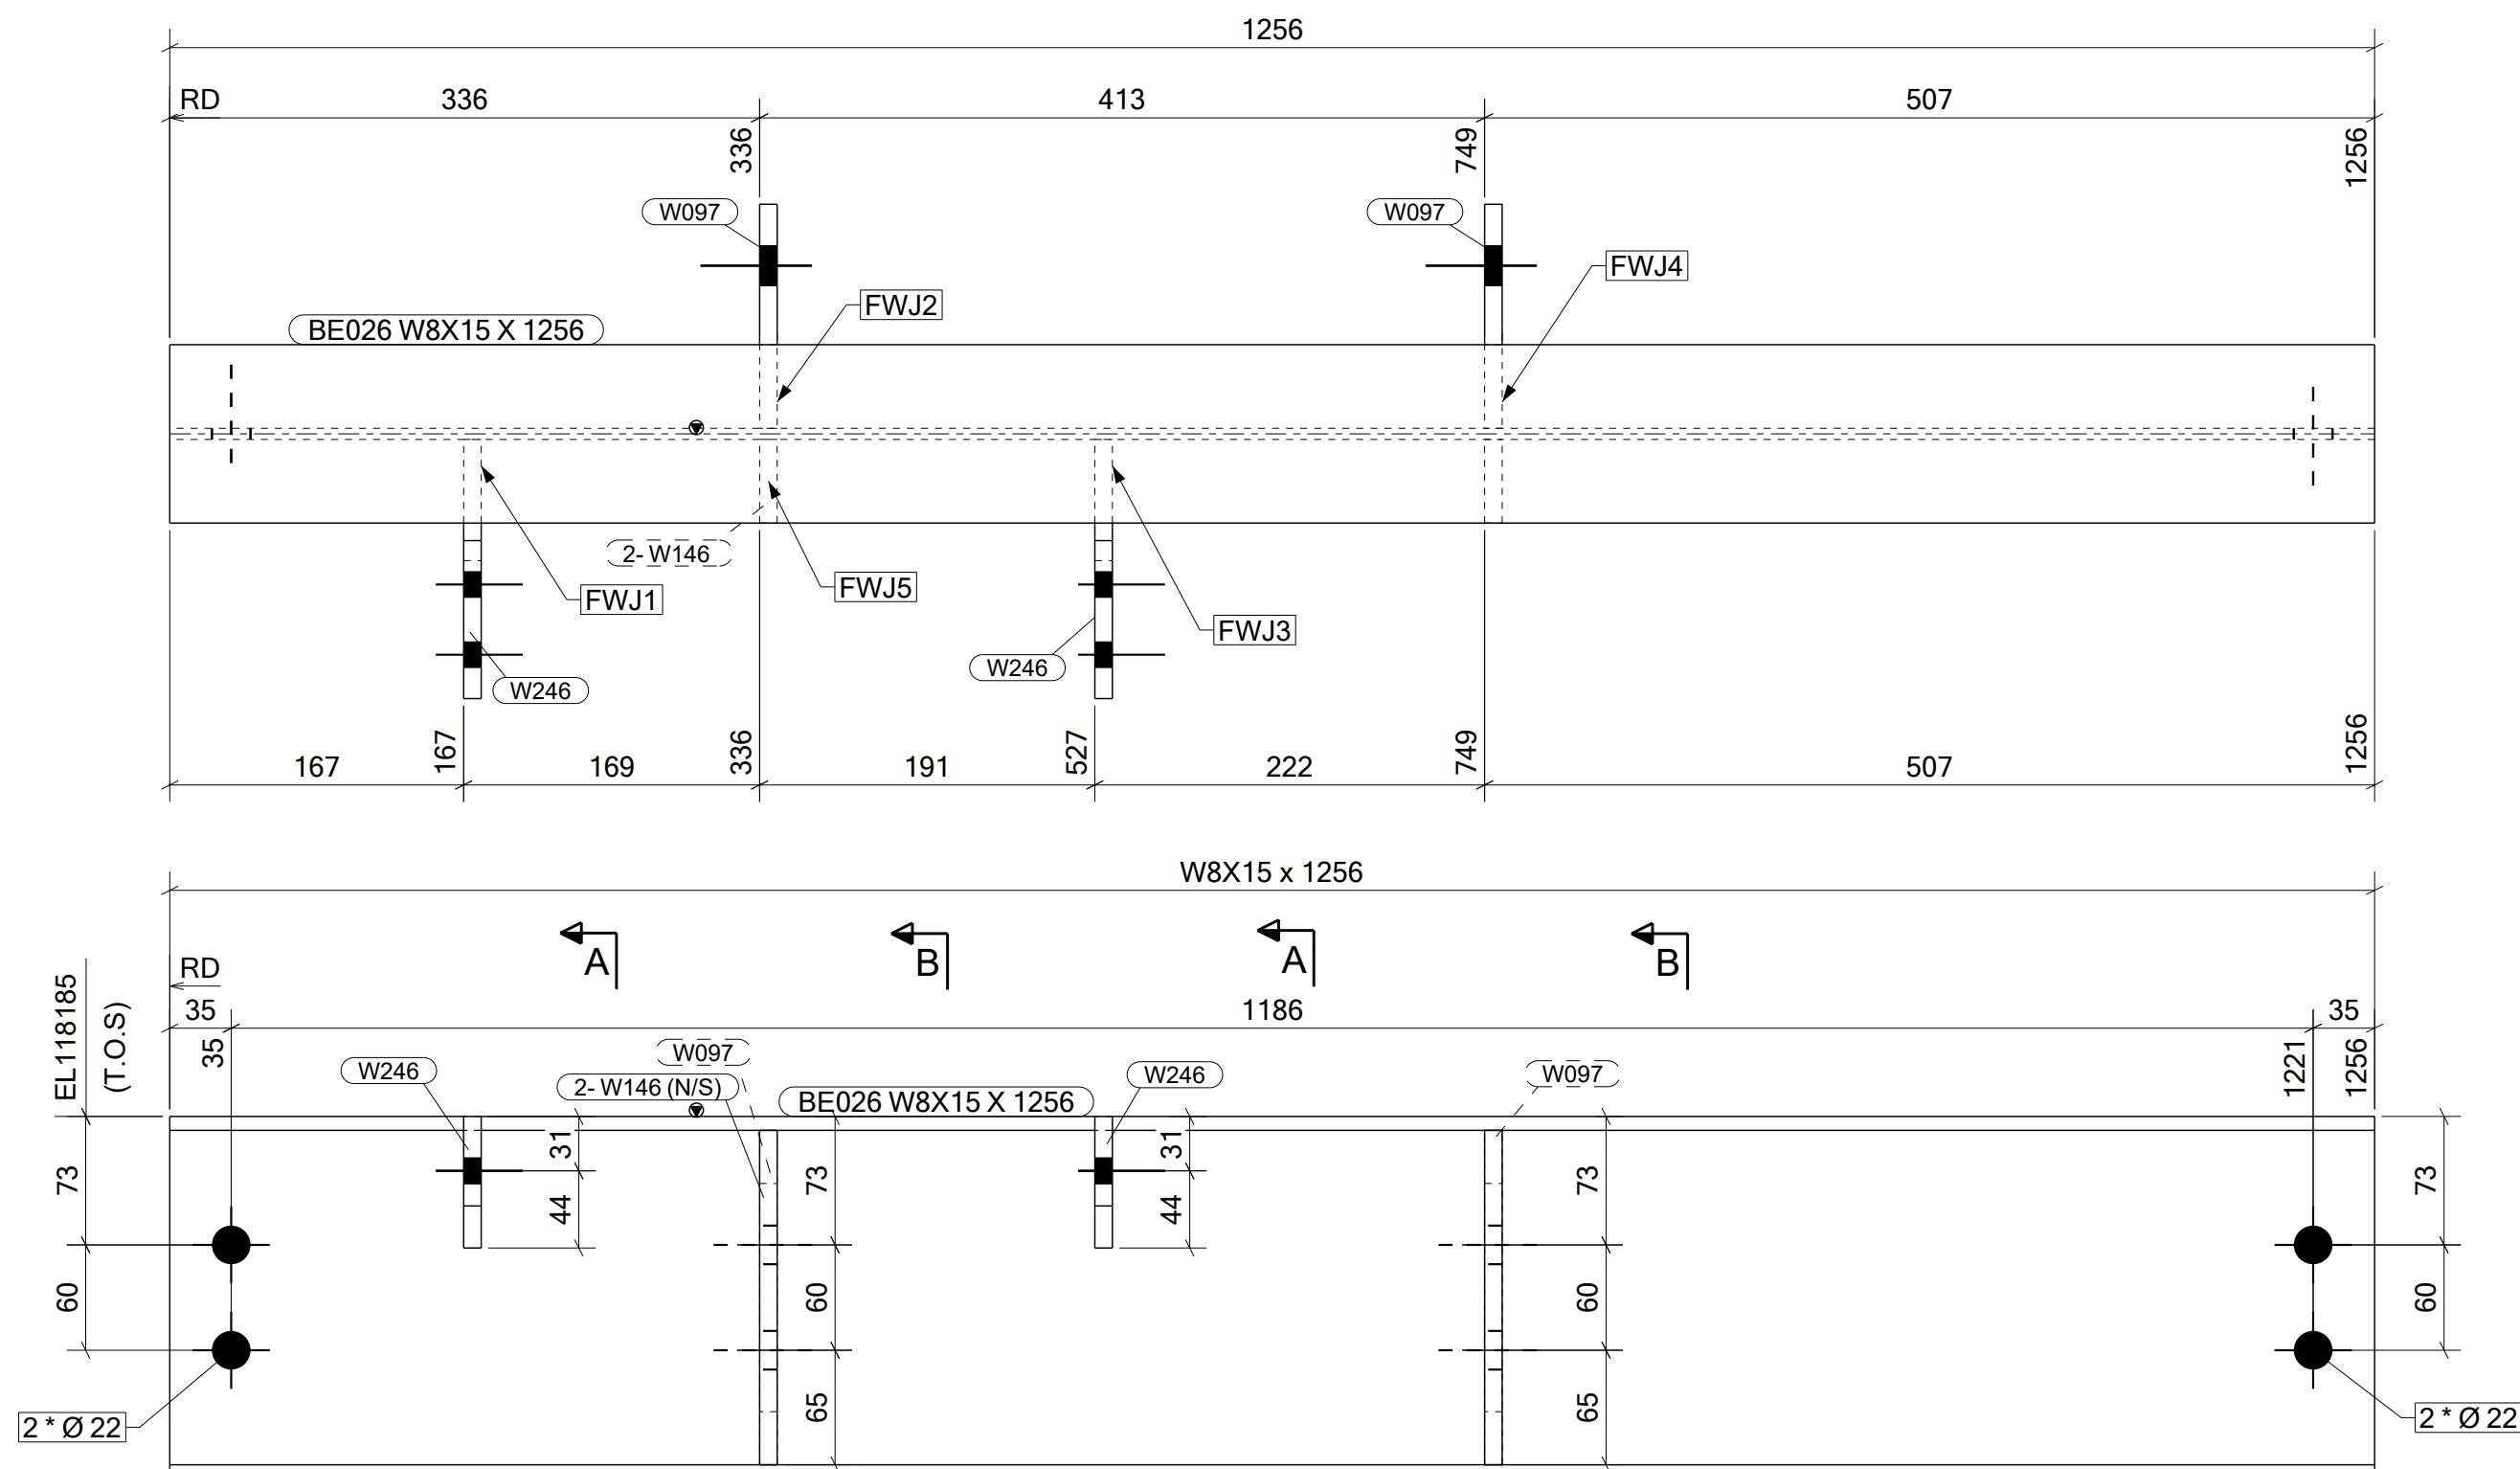

GA & IFC DRAWINGS REFERENCE	REV.
AD282-732-C-33298,299 & 300	3
AD282-732-C-34324	1
AD282-732-C-34287	1

NOTES :


- 1-ALL DIMENSIONS ARE GIVEN IN MILLIMETERS (U.N.O.).
- 2-  DENOTES ASSEMBLY ORIENTATION MARK.
- 3- DON'T SCALE THE DRAWING. FOLLOW THE WRITTEN DIMENSIONS.
- 4- FINISH AS PER PROJECT SPEC.
- 5- STRUCTURAL STEELWORK SHALL BE IN ACCORDANCE WITH PROJECT SPECIFICATIONS AD282-732-G-03520 & AD282-732-G-03527
- 6-WHEREVER THERE IS NO ACCESS FOR FILLET WELDING TO BE REPLACED BY FULL PENETRATION BUTT WELDING
- 7-FOR CJP WELD MARKED LOCATIONS FOLLOW THIS DETAIL

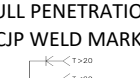

8-ALL WELDS TO BE 6mm FILLET WELD U.N.O.

GRID LOCATION	
EL +118.085	<732-09/732-B>

DRAWING NO. : 2307059-732-V-132-HB002										REV.: 00	
ERECTION MARK : 2307059-732-V-132-HB002			DESCRIPTION : HORIZONTAL_BRACE			COLOR CODE : 10 B 15			QTY : 1	NOS	
HOLD:		TYPE: P	TREAT: PN		COST CODE: 2.01			REMARKS:			
LENGTH: 693		WIDTH: 76		HEIGHT: 76		TOTAL S.AREA: 0.2 (M2)					
POSITION NO.	QTY PER ASSLY	SECTION	LENGTH	UNIT WEIGHT (KG)	TOTAL WIEGHT (KG)		GRADE	REVISION	PART ID	TREATMENT	REMARKS
					QTY	WEIGHT					
HB002	1	L3X3X1/4	693	5.054	1	5.05	A572-GR.50	1	MM	PN	
					UNIT WEIGHT	5.05					
					TOTAL WEIGHT	5.05					
BOLT LIST:-											
BOLT \ STUD		BOLT DESCRIPTION		QTY/ONE	QTY/ALL	FINISH	REMARKS				
BOLT		B1N1W20 × 55 A325M		3	6						

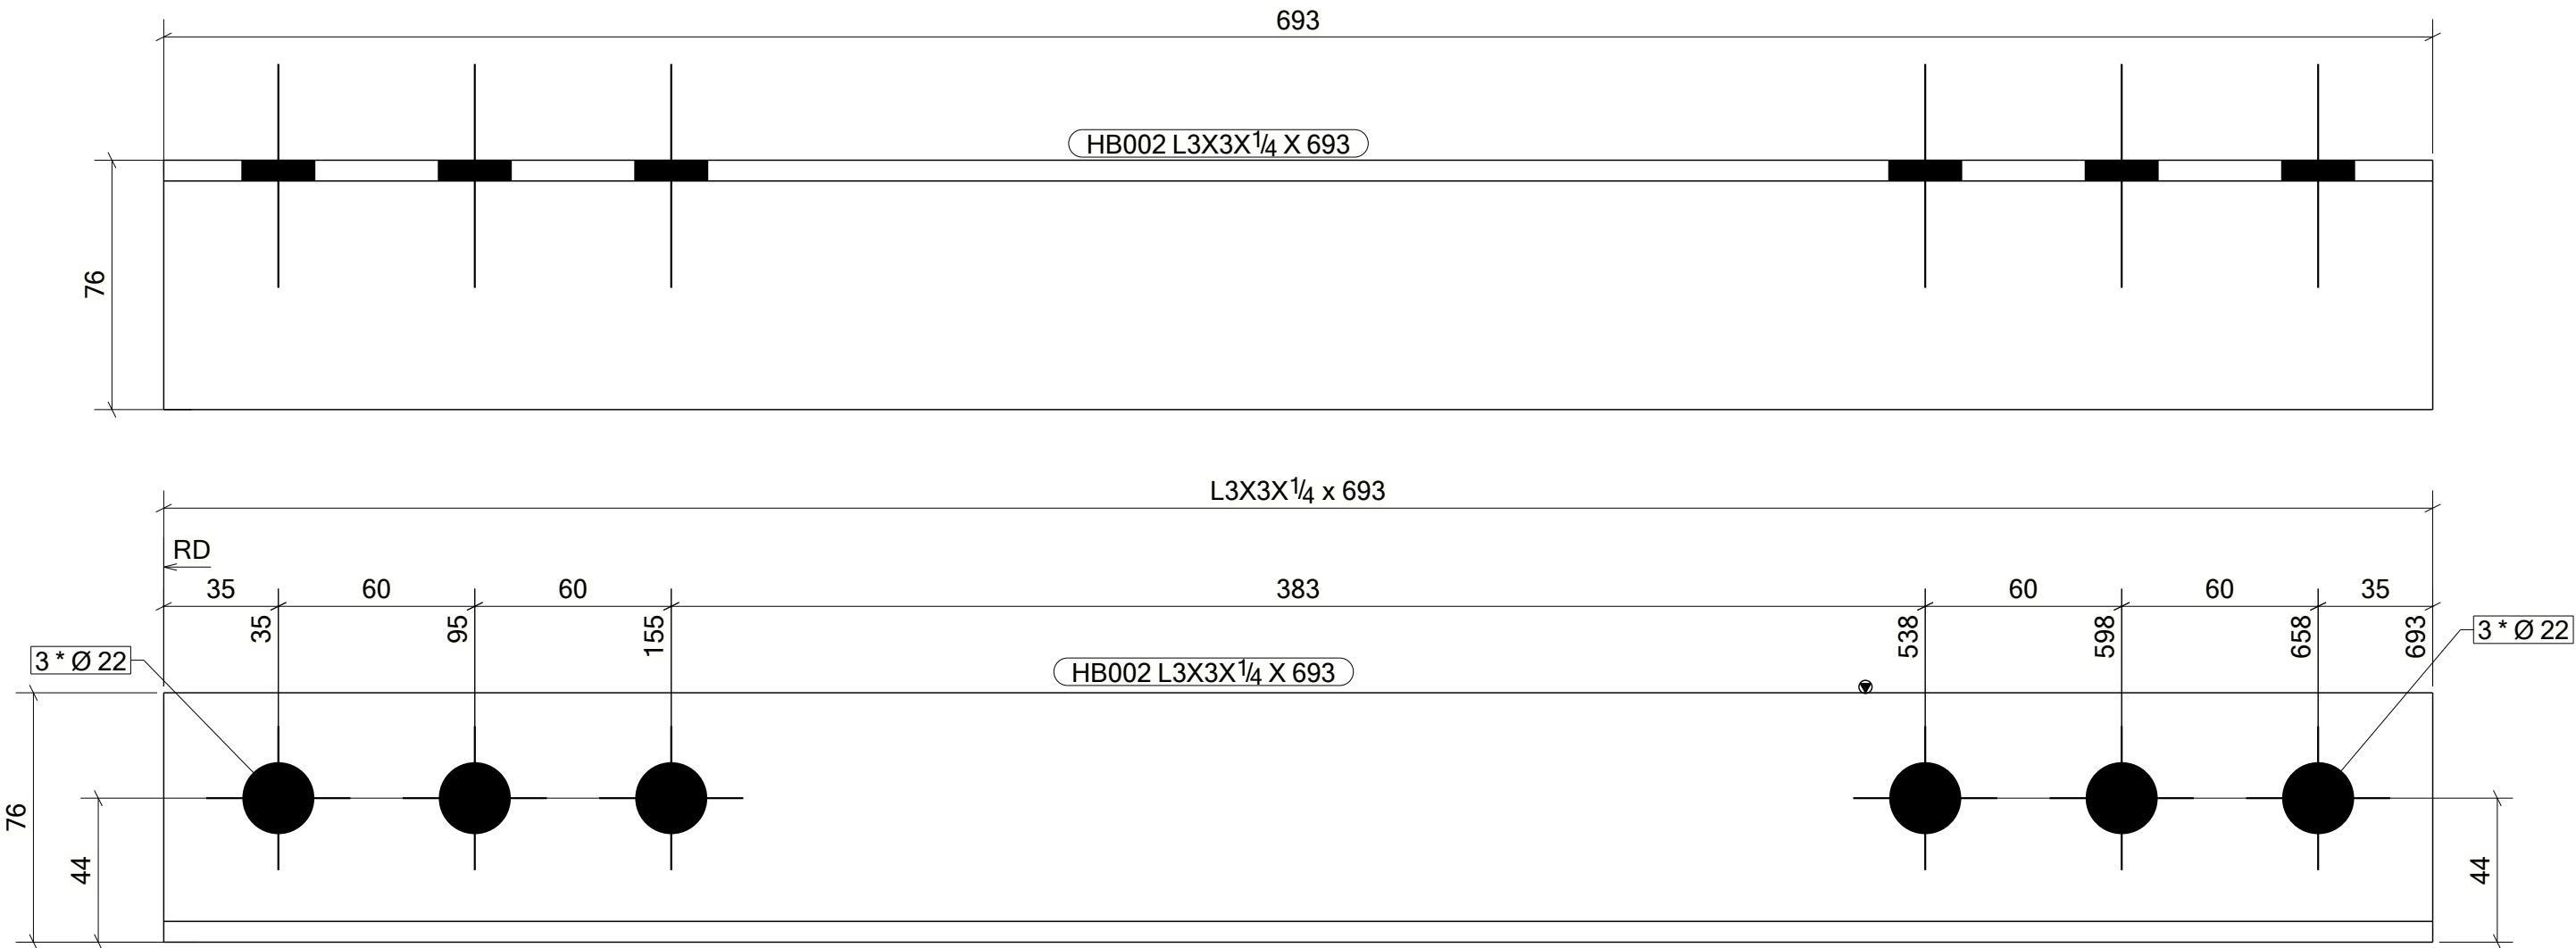


GA & IFC DRAWINGS REFERENCE	REV.
AD282-732-C-33298,299 & 300	3
AD282-732-C-34324	1
AD282-732-C-34287	1

- NOTES :**
- 1-ALL DIMENSIONS ARE GIVEN IN MILLIMETERS (U.N.O.).
 - 2-  DENOTES ASSEMBLY ORIENTATION MARK.
 - 3-DON'T SCALE THE DRAWING. FOLLOW THE WRITTEN DIMENSIONS.
 - 4- FINISH AS PER PROJECT SPEC.
 - 5- STRUCTURAL STEELWORK SHALL BE IN ACCORDANCE WITH PROJECT SPECIFICATIONS AD282-732-G-03520 & AD282-732-G-03527
 - 6-WHEREVER THERE IS NO ACCESS FOR FILLET WELDING TO BE REPLACED BY FULL PENETRATION BUTT WELDING
 - 7-FOR CJP WELD MARKED LOCATIONS FOLLOW THIS DETAIL

 - 8-ALL WELDS TO BE 6mm FILLET WELD U.N.O.

GRID LOCATION	
EL +118.085	<732-09/732-B>

DRAWING NO. : 2307059-732-V-132-HB003										REV.: 00	
ERECTION MARK : 2307059-732-V-132-HB003				DESCRIPTION : HORIZONTAL_BRACE			COLOR CODE : 10 B 15		QTY : 1		NOS
HOLD:		TYPE: P	TREAT: PN		COST CODE: 2.01			REMARKS:			
LENGTH: 911		WIDTH: 76		HEIGHT: 76		TOTAL S.AREA: 0.3		(M2)			
POSITION NO.	QTY PER ASSLY	SECTION	LENGTH	UNIT WEIGHT (KG)	TOTAL WIEGHT (KG)		GRADE	REVISION	PART ID	TREATMENT	REMARKS
					QTY	WEIGHT					
HB003	1	L3X3X1/4	911	6.646	1	6.65	A572-GR.50	1	MM	PN	
					UNIT WEIGHT	6.65					
					TOTAL WEIGHT	6.65					
BOLT LIST:-											
BOLT \ STUD		BOLT DESCRIPTION		QTY/ONE	QTY/ALL	FINISH	REMARKS				
BOLT		B1N1W20 × 55	A325M	3	6						

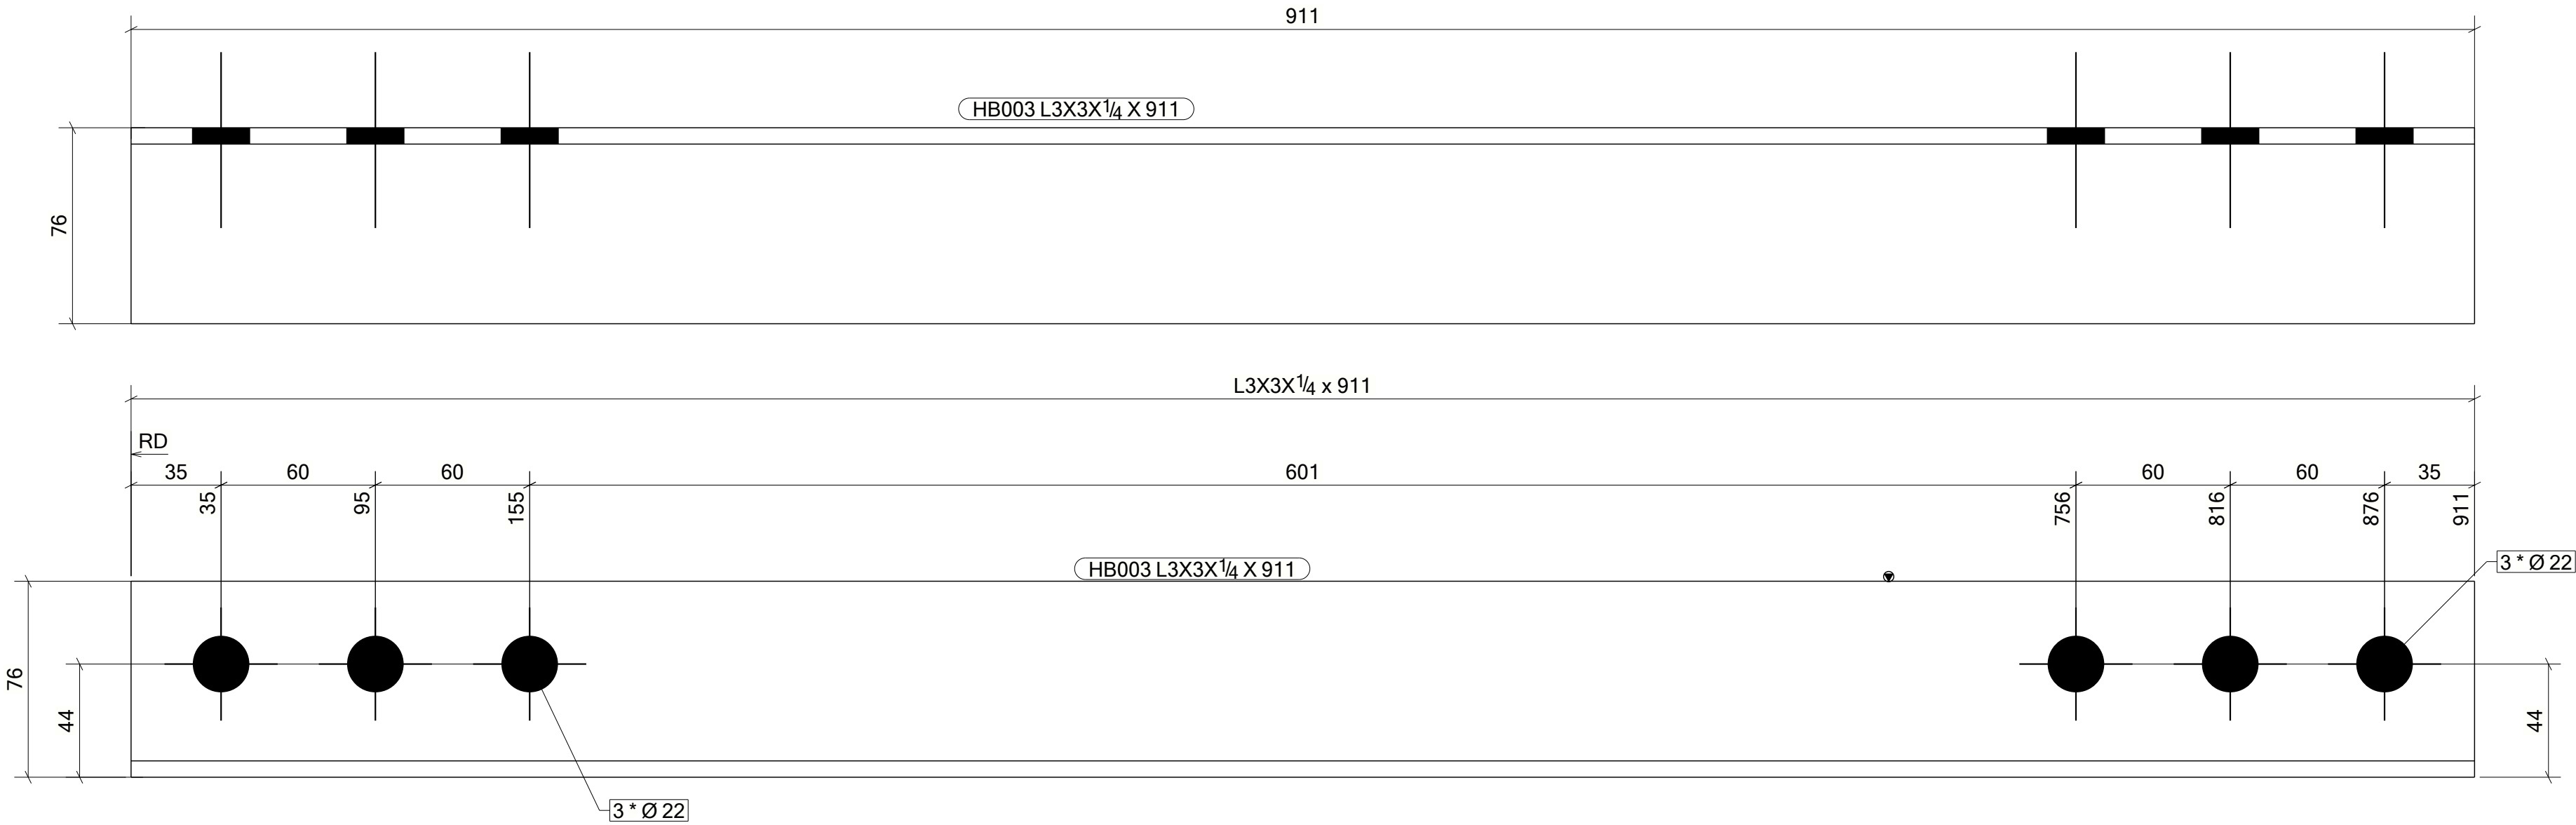

GA & IFC DRAWINGS REFERENCE	REV.
AD282-732-C-33298,299 & 300	3
AD282-732-C-34324	1
AD282-732-C-34287	1

NOTES :

1-ALL DIMENSIONS ARE GIVEN IN MILLIMETERS (U.N.O.).

2- DENOTES ASSEMBLY ORIENTATION MARK.

3-DON'T SCALE THE DRAWING. FOLLOW THE WRITTEN DIMENSIONS.

4- FINISH AS PER PROJECT SPEC.

5- STRUCTURAL STEELWORK SHALL BE IN ACCORDANCE WITH PROJECT SPECIFICATIONS AD282-732-G-03520 & AD282-732-G-03527


6-WHEREVER THERE IS NO ACCESS FOR FILLET WELDING TO BE REPLACED BY FULL PENETRATION BUTT WELDING

7-FOR CJP WELD MARKED LOCATIONS FOLLOW THIS DETAIL






8-ALL WELDS TO BE 6mm FILLET WELD U.N.O.

GRID LOCATION	
EL +119.421	<732-09/<732-B

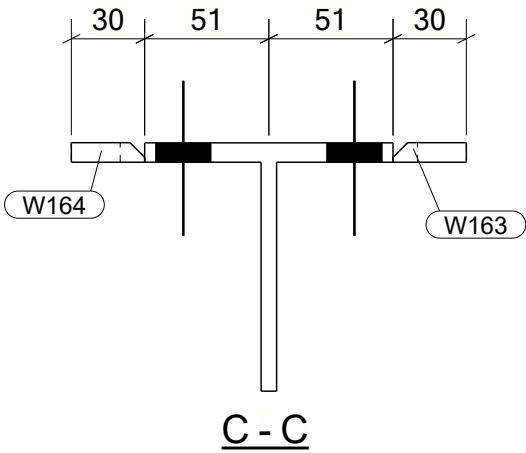

ANCILLARY CATEGORY
PJP-J1 TO J4

DRAWING NO. : 2307059-732-V-132-VB002										REV.: 00	
ERECTION MARK : 2307059-732-V-132-VB002			DESCRIPTION : VERTICAL_BRACE			COLOR CODE : 10 B 15			QTY : 1	NOS	
HOLD:		TYPE: W	TREAT: PN		COST CODE: 2.01			REMARKS:			
LENGTH: 1357		WIDTH: 162	HEIGHT: 102		TOTAL S.AREA: 0.6			(M2)			
POSITION NO.	QTY PER ASSLY	SECTION	LENGTH	UNIT WEIGHT (KG)	TOTAL WIEGHT (KG)		GRADE	REVISION	PART ID	TREATMENT	REMARKS
					QTY	WEIGHT					
VB002	1	WT4X7.5	1357	15.261	1	15.26	S275JR	1	MM	PN	
W163	2	PL8X30	170	0.284	2	0.57	S355JR	1	WI		
W164	2	PL8X30	170	0.284	2	0.57	S355JR	1	WI		
					UNIT WEIGHT	16.40					
					TOTAL WEIGHT	16.40					
BOLT LIST:-											
BOLT \ STUD		BOLT DESCRIPTION		QTY/ONE	QTY/ALL	FINISH	REMARKS				
BOLT		B1N1W20 X 50 A325M		4	8						

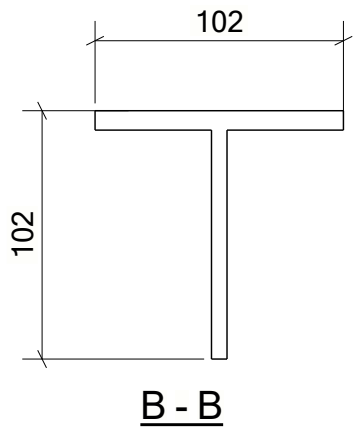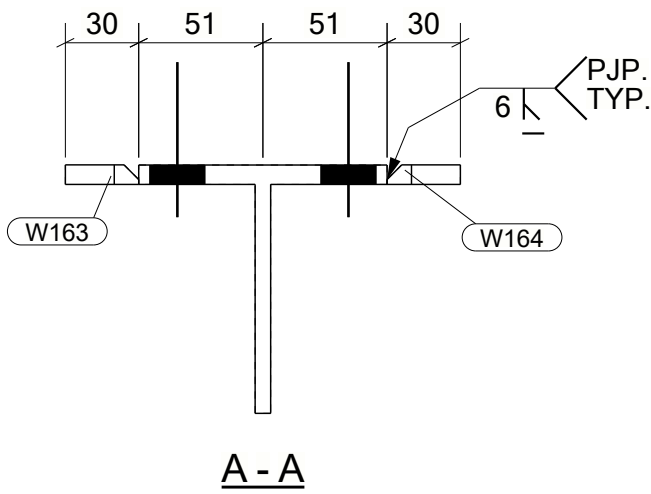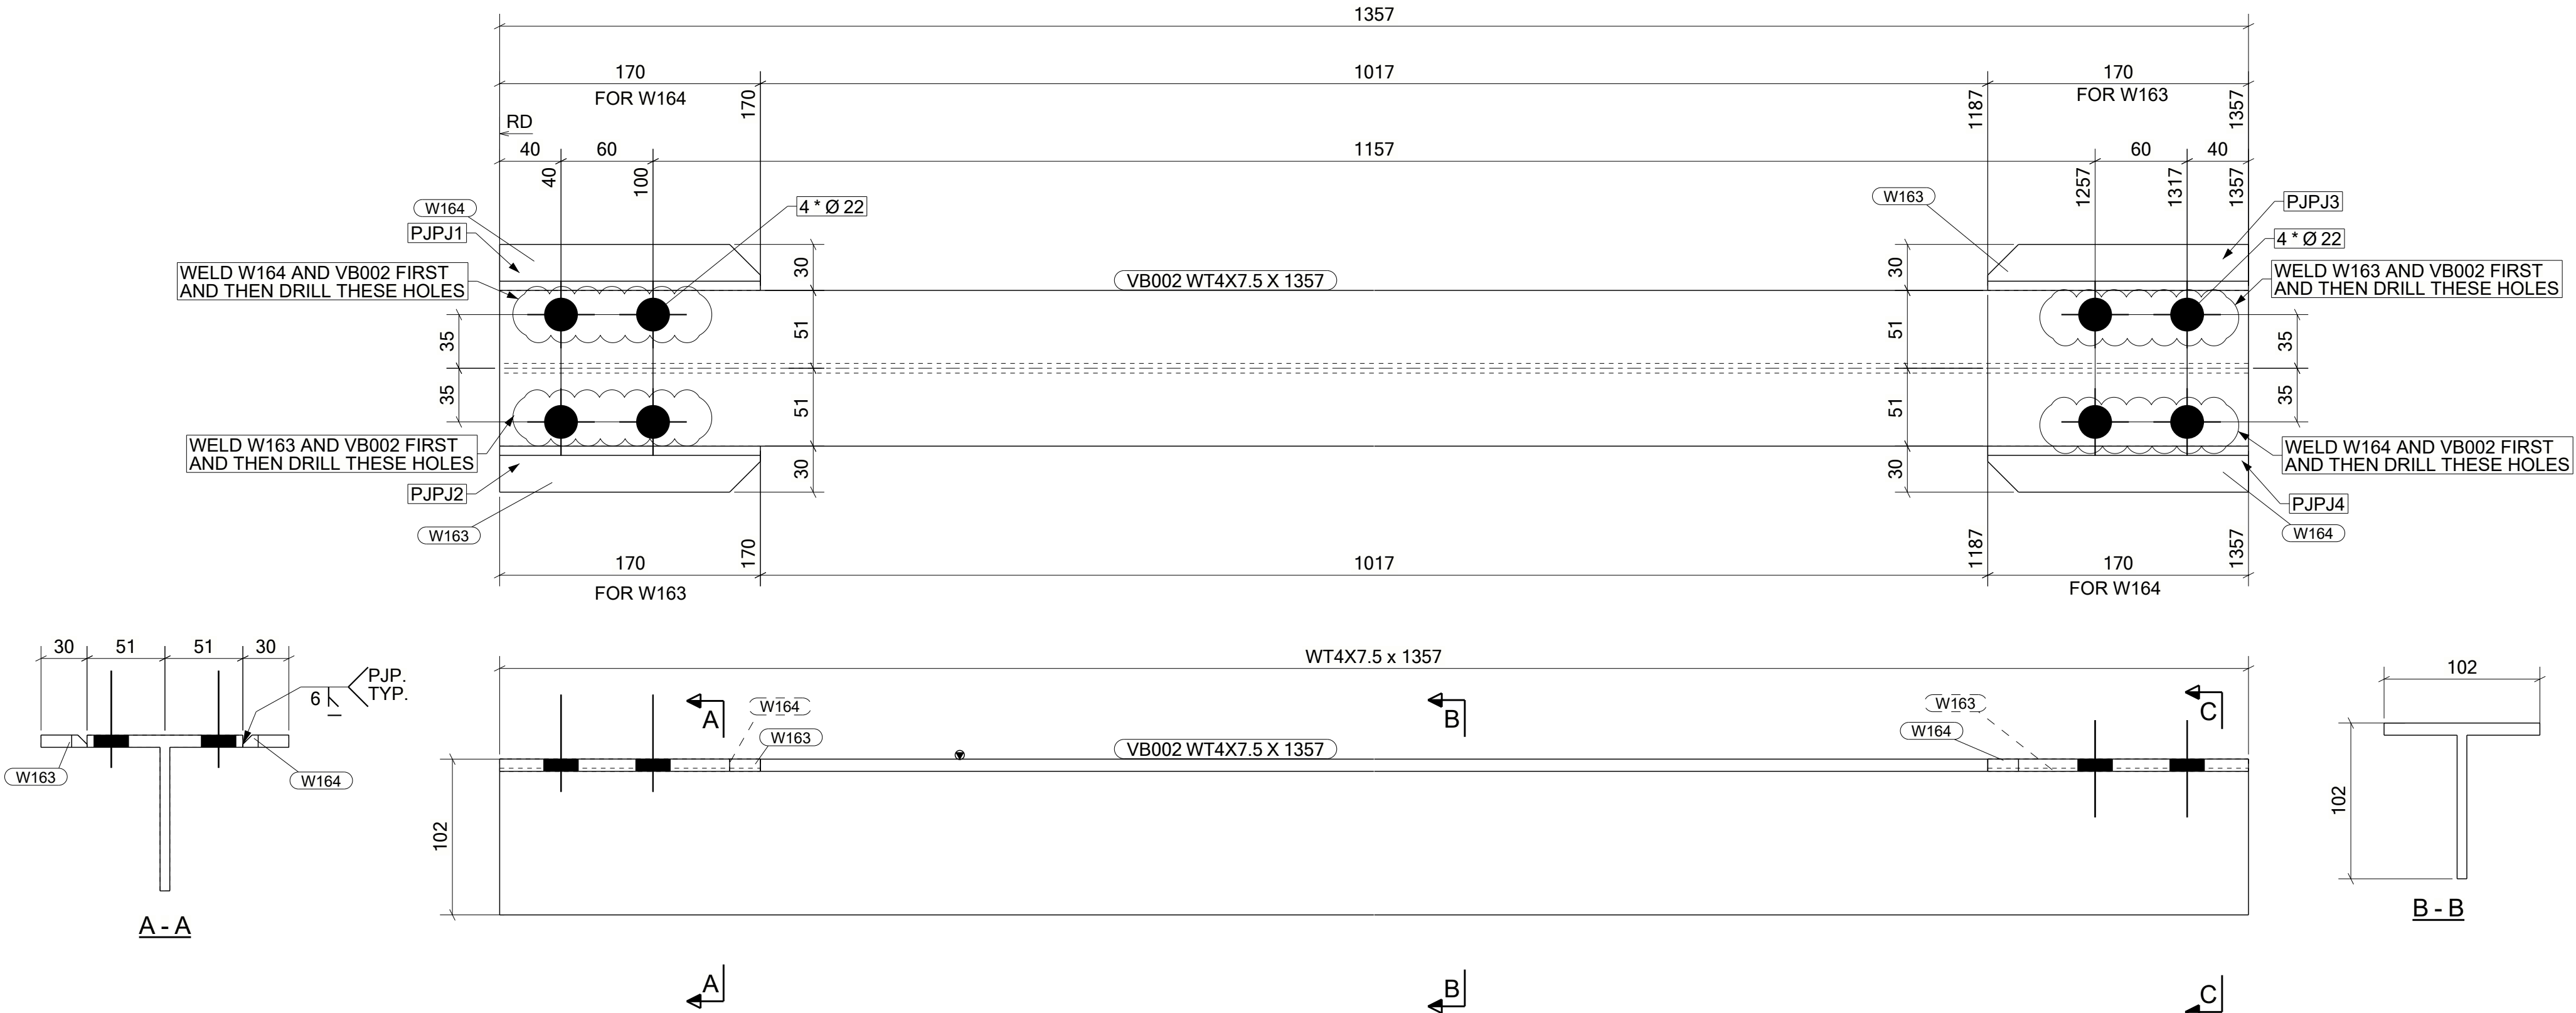

GA & IFC DRAWINGS REFERENCE	REV.
AD282-732-C-33298,299 & 300	3
AD282-732-C-34324	1
AD282-732-C-34287	1


NOTES :

- 1-ALL DIMENSIONS ARE GIVEN IN MILLIMETERS (U.N.O.).
- 2-  DENOTES ASSEMBLY ORIENTATION MARK.
- 3-DON'T SCALE THE DRAWING. FOLLOW THE WRITTEN DIMENSIONS.
- 4- FINISH AS PER PROJECT SPEC.
- 5- STRUCTURAL STEELWORK SHALL BE IN ACCORDANCE WITH PROJECT SPECIFICATIONS AD282-732-G-03520 & AD282-732-G-03527
- 6-WHEREVER THERE IS NO ACCESS FOR FILLET WELDING TO BE REPLACED BY FULL PENETRATION BUTT WELDING
- 7-FOR CJP WELD MARKED LOCATIONS FOLLOW THIS DETAIL 
- 8-ALL WELDS TO BE 6mm FILLET WELD U.N.O.

GRID LOCATION	
EL +117.925	<732-09/732-B>
EL +117.925	<732-09/<732-B

ANCILLARY CATEGORY
PJP-J1 TO J4






DRAWING NO. : 2307059-732-V-132-VB004										REV.: 00	
ERECTION MARK : 2307059-732-V-132-VB004			DESCRIPTION : VERTICAL_BRACE			COLOR CODE : 10 B 15			QTY : 2		NOS
HOLD:		TYPE: W	TREAT: PN		COST CODE: 2.01			REMARKS:			
LENGTH: 804		WIDTH: 202		HEIGHT: 102		TOTAL S.AREA: 0.4			(M2)		
POSITION NO.	QTY PER ASSLY	SECTION	LENGTH	UNIT WEIGHT (KG)	TOTAL WIEGHT (KG)		GRADE	REVISION	PART ID	TREATMENT	REMARKS
					QTY	WEIGHT					
VB004	1	WT4X7.5	804	9.042	2	18.08	S275JR	1	MM	PN	
W163	1	PL8X30	170	0.284	2	0.57	S355JR	1	WI		
W164	1	PL8X30	170	0.284	2	0.57	S355JR	1	WI		
W165	1	PL8X50	290	0.857	2	1.71	S355JR	1	WI		
W166	1	PL8X50	290	0.857	2	1.71	S355JR	1	WI		
					UNIT WEIGHT	11.32					
					TOTAL WEIGHT	22.65					
BOLT LIST:-											
BOLT \ STUD		BOLT DESCRIPTION		QTY/ONE	QTY/ALL	FINISH	REMARKS				
BOLT		B1N1W20 × 50 A325M		8	8						

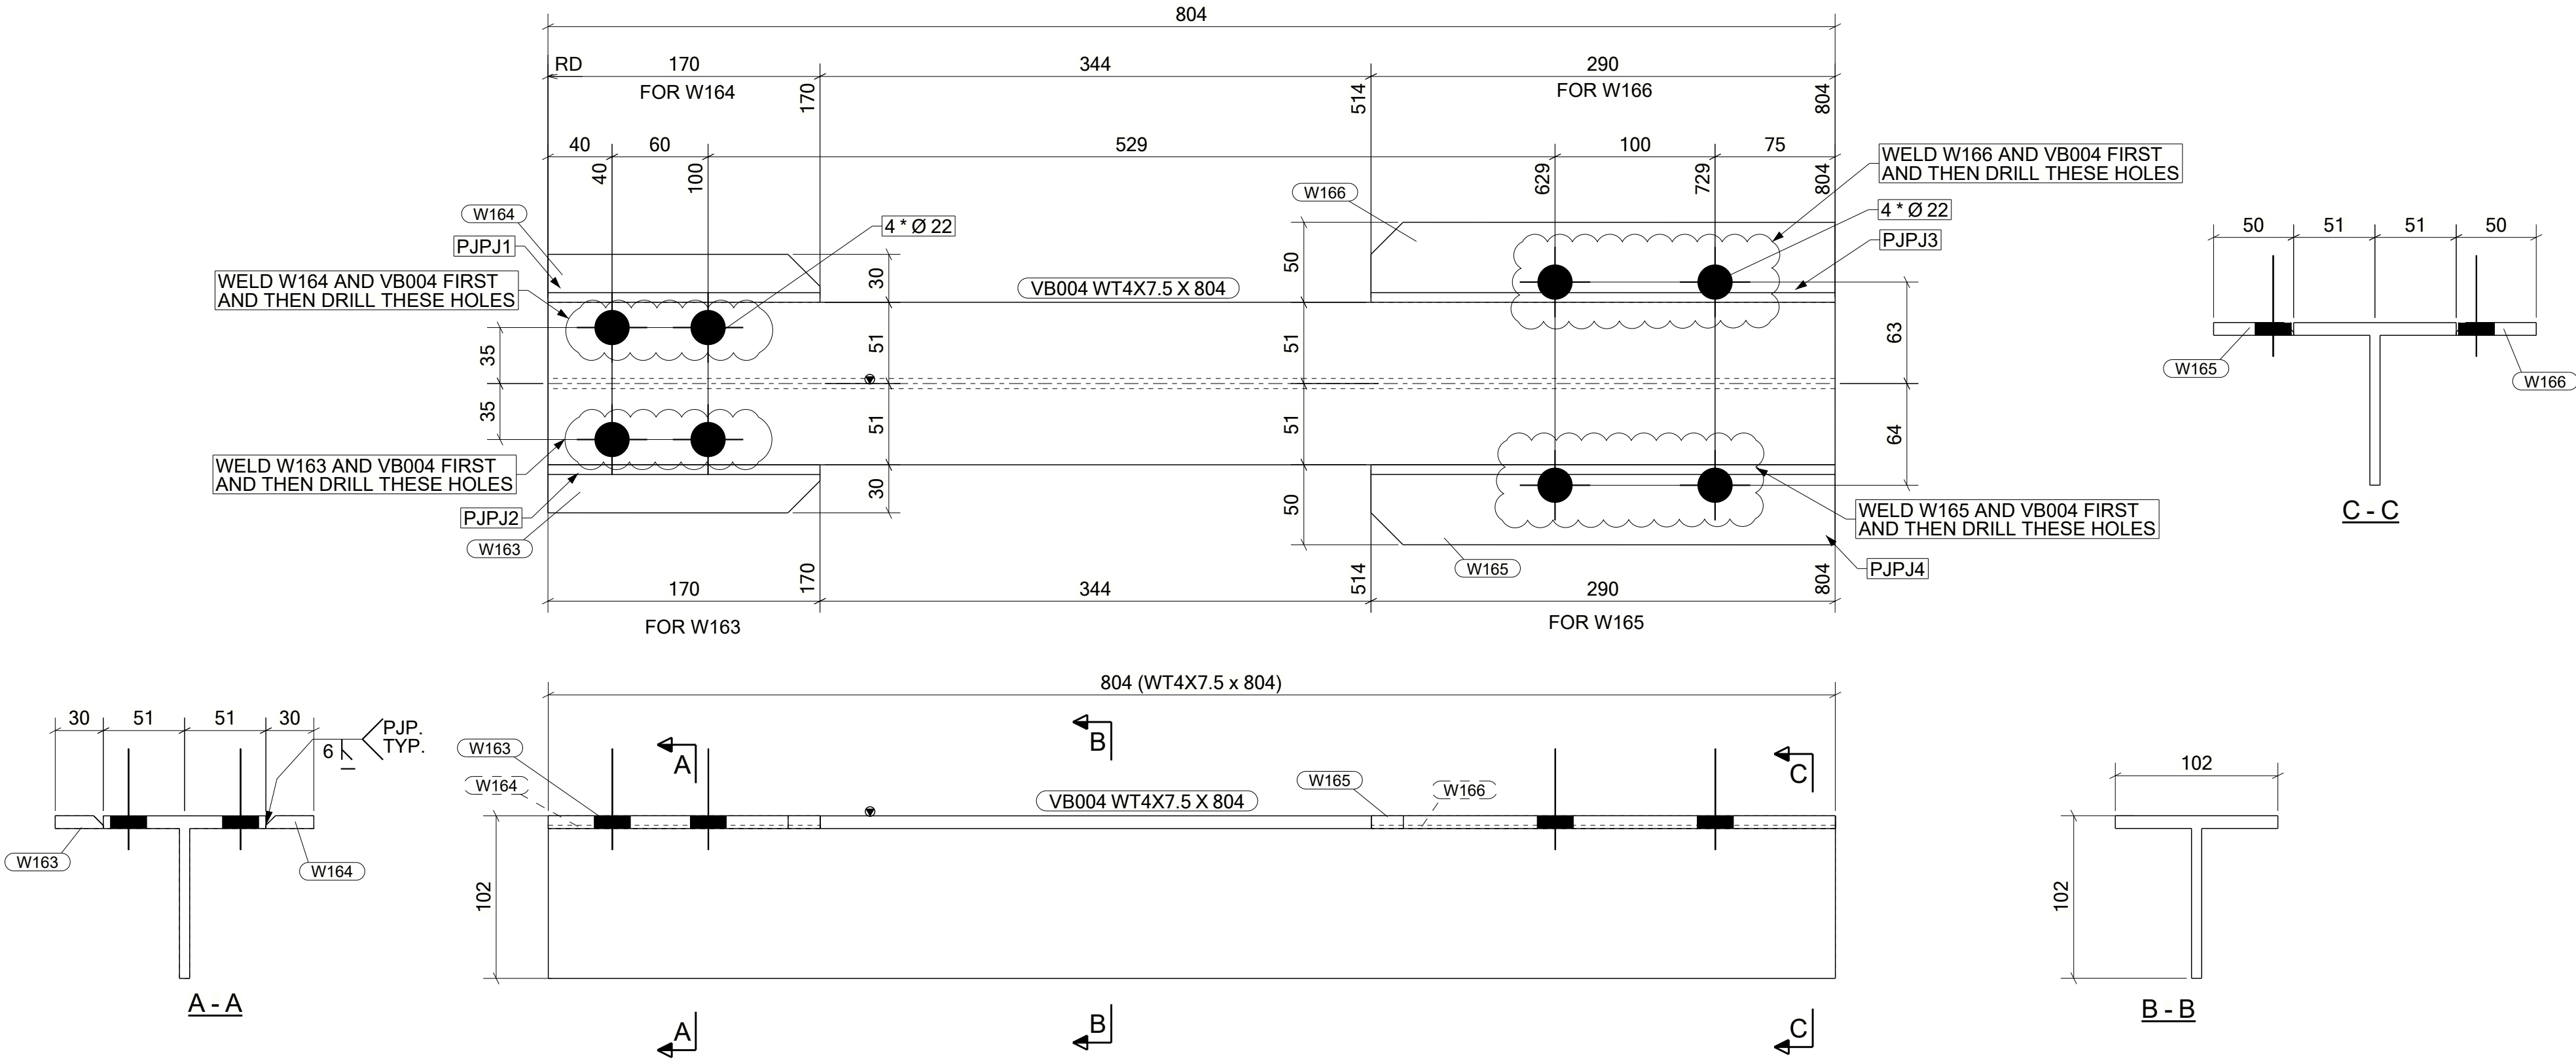

GA & IFC DRAWINGS REFERENCE	REV.
AD282-732-C-33298,299 & 300	3
AD282-732-C-34324	1
AD282-732-C-34287	1

- NOTES :**
- 1-ALL DIMENSIONS ARE GIVEN IN MILLIMETERS (U.N.O.).
 - 2-  DENOTES ASSEMBLY ORIENTATION MARK.
 - 3-DON'T SCALE THE DRAWING. FOLLOW THE WRITTEN DIMENSIONS.
 - 4- FINISH AS PER PROJECT SPEC.
 - 5- STRUCTURAL STEELWORK SHALL BE IN ACCORDANCE WITH PROJECT SPECIFICATIONS AD282-732-G-03520 & AD282-732-G-03527
 - 6-WHEREVER THERE IS NO ACCESS FOR FILLET WELDING TO BE REPLACED BY FULL PENETRATION BUTT WELDING
 - 7-FOR CJP MARKED LOCATIONS FOLLOW THIS DETAIL 
 - 8-ALL WELDS TO BE 6mm FILLET WELD U.N.O.

GRID LOCATION	
EL +103.165	<732-09/<732-B

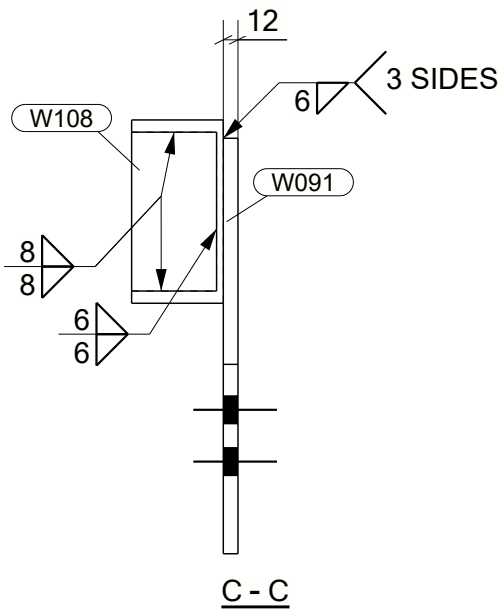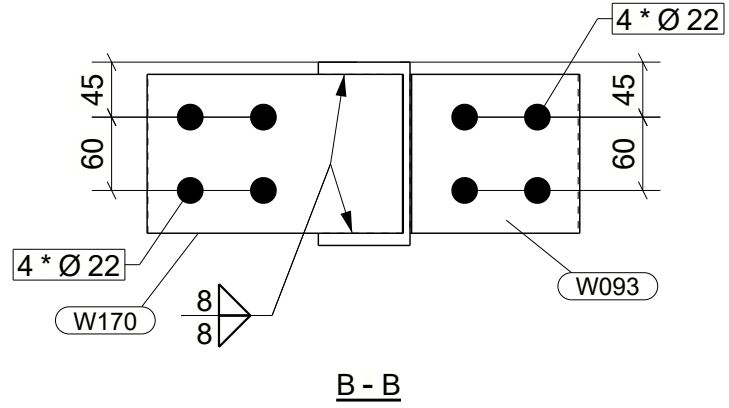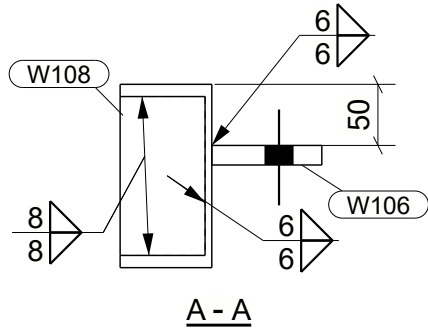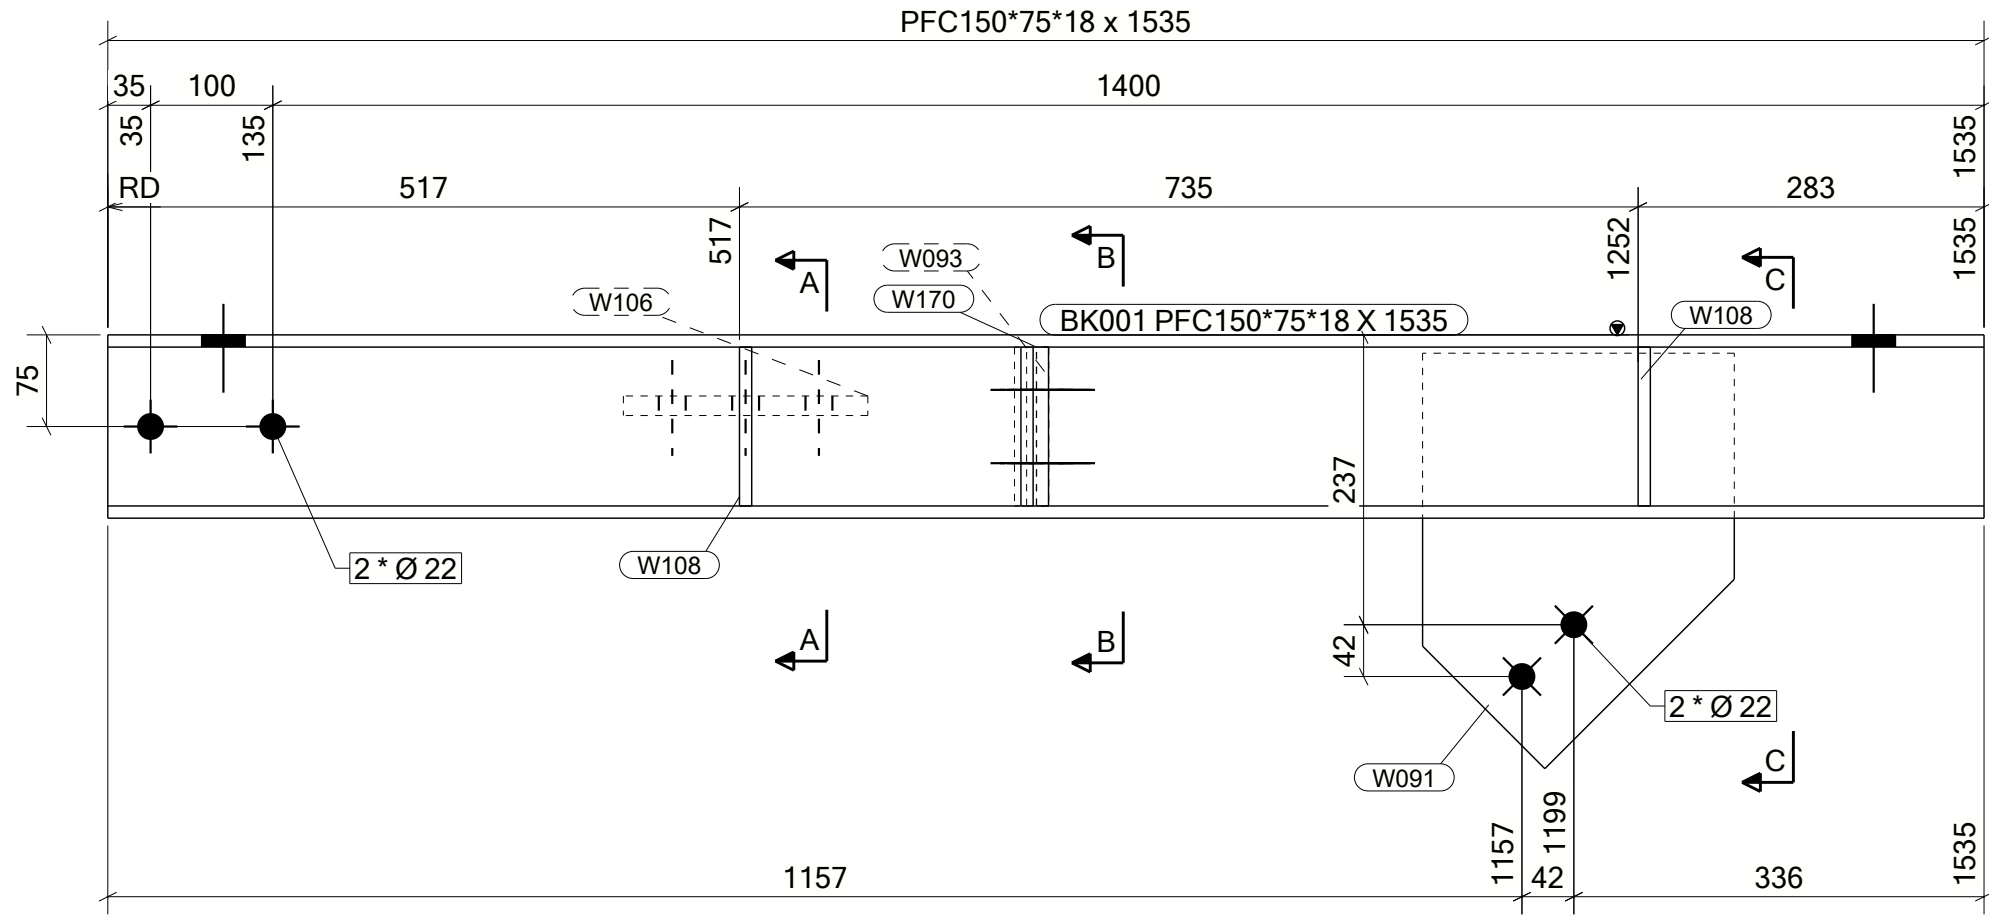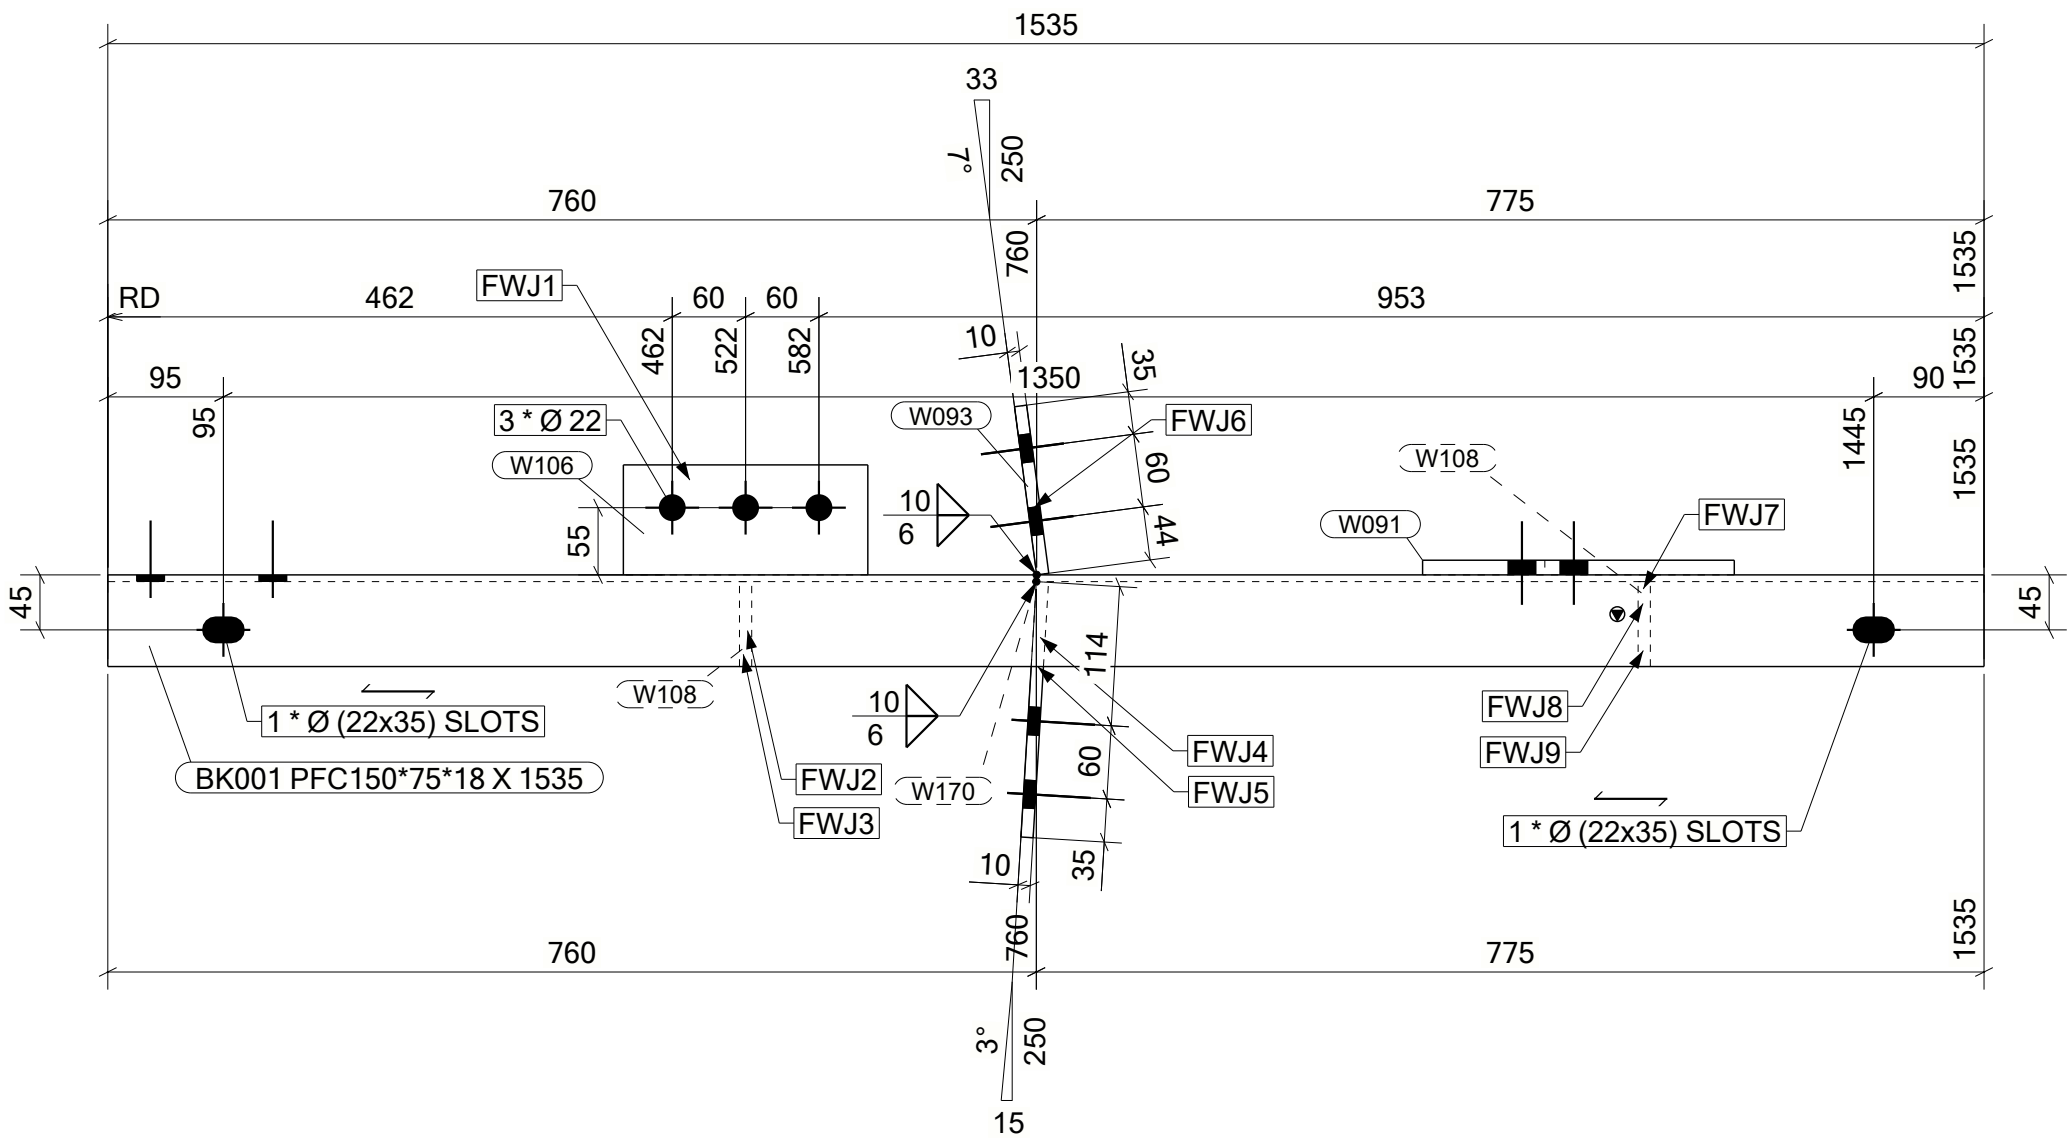



DRAWING NO. : 2307059-732-V-132-BK001										REV.: 00	
ERECTION MARK : 2307059-732-V-132-BK001				DESCRIPTION : BRACKET				COLOR CODE : 10 B 15		QTY : 1	NOS
HOLD:		TYPE: W	TREAT: PN		COST CODE: 2.01			REMARKS:			
LENGTH: 1535		WIDTH: 354	HEIGHT: 355		TOTAL S.AREA: 1.2			(M2)			
POSITION NO.	QTY PER ASSLY	SECTION	LENGTH	UNIT WEIGHT (KG)	TOTAL WIEGHT (KG)		GRADE	REVISION	PART ID	TREATMENT	REMARKS
					QTY	WEIGHT					
BK001	1	PFC150*75*18	1535	27.473	1	27.47	S275JR	1	MM	PN	
W091	1	PL12X340	255	6.563	1	6.56	S355JR	1	WI		
W093	1	PL10X130	139	1.416	1	1.42	S355JR	1	WI		
W106	1	PL16X90	200	2.261	1	2.26	S355JR	1	WI		
W108	2	PL10X69	130	0.709	2	1.42	S355JR	1	WI		
W170	1	PL10X130	209	2.137	1	2.14	S355JR	1	WI		
					UNIT WEIGHT	41.27					
					TOTAL WEIGHT	41.27					
BOLT LIST:-											
BOLT \ STUD		BOLT DESCRIPTION		QTY/ONE	QTY/ALL	FINISH	REMARKS				
BOLT		B1N1W20 × 50 A325M		2	2						

ANCILLARY CATEGORY
FW-J1 TO J9

GA & IFC DRAWINGS REFERENCE	REV.
AD282-732-C-33298,299 & 300	3
AD282-732-C-34324	1
AD282-732-C-34287	1





- NOTES :
- 1-ALL DIMENSIONS ARE GIVEN IN MILLIMETERS (U.N.O.).
 - 2-☛ DENOTES ASSEMBLY ORIENTATION MARK.
 - 3-DON'T SCALE THE DRAWING. FOLLOW THE WRITTEN DIMENSIONS.
 - 4- FINISH AS PER PROJECT SPEC.
 - 5- STRUCTURAL STEELWORK SHALL BE IN ACCORDANCE WITH PROJECT SPECIFICATIONS AD282-732-G-03520 & AD282-732-G-03527
 - 6-WHEREVER THERE IS NO ACCESS FOR FILLET WELDING TO BE REPLACED BY FULL PENETRATION BUTT WELDING
 - 7-FOR CJP WELD MARKED LOCATIONS FOLLOW THIS DETAIL
 - 8-ALL WELDS TO BE 6mm FILLET WELD U.N.O.

GRID LOCATION	
EL +103.165	<732-09/<732-B

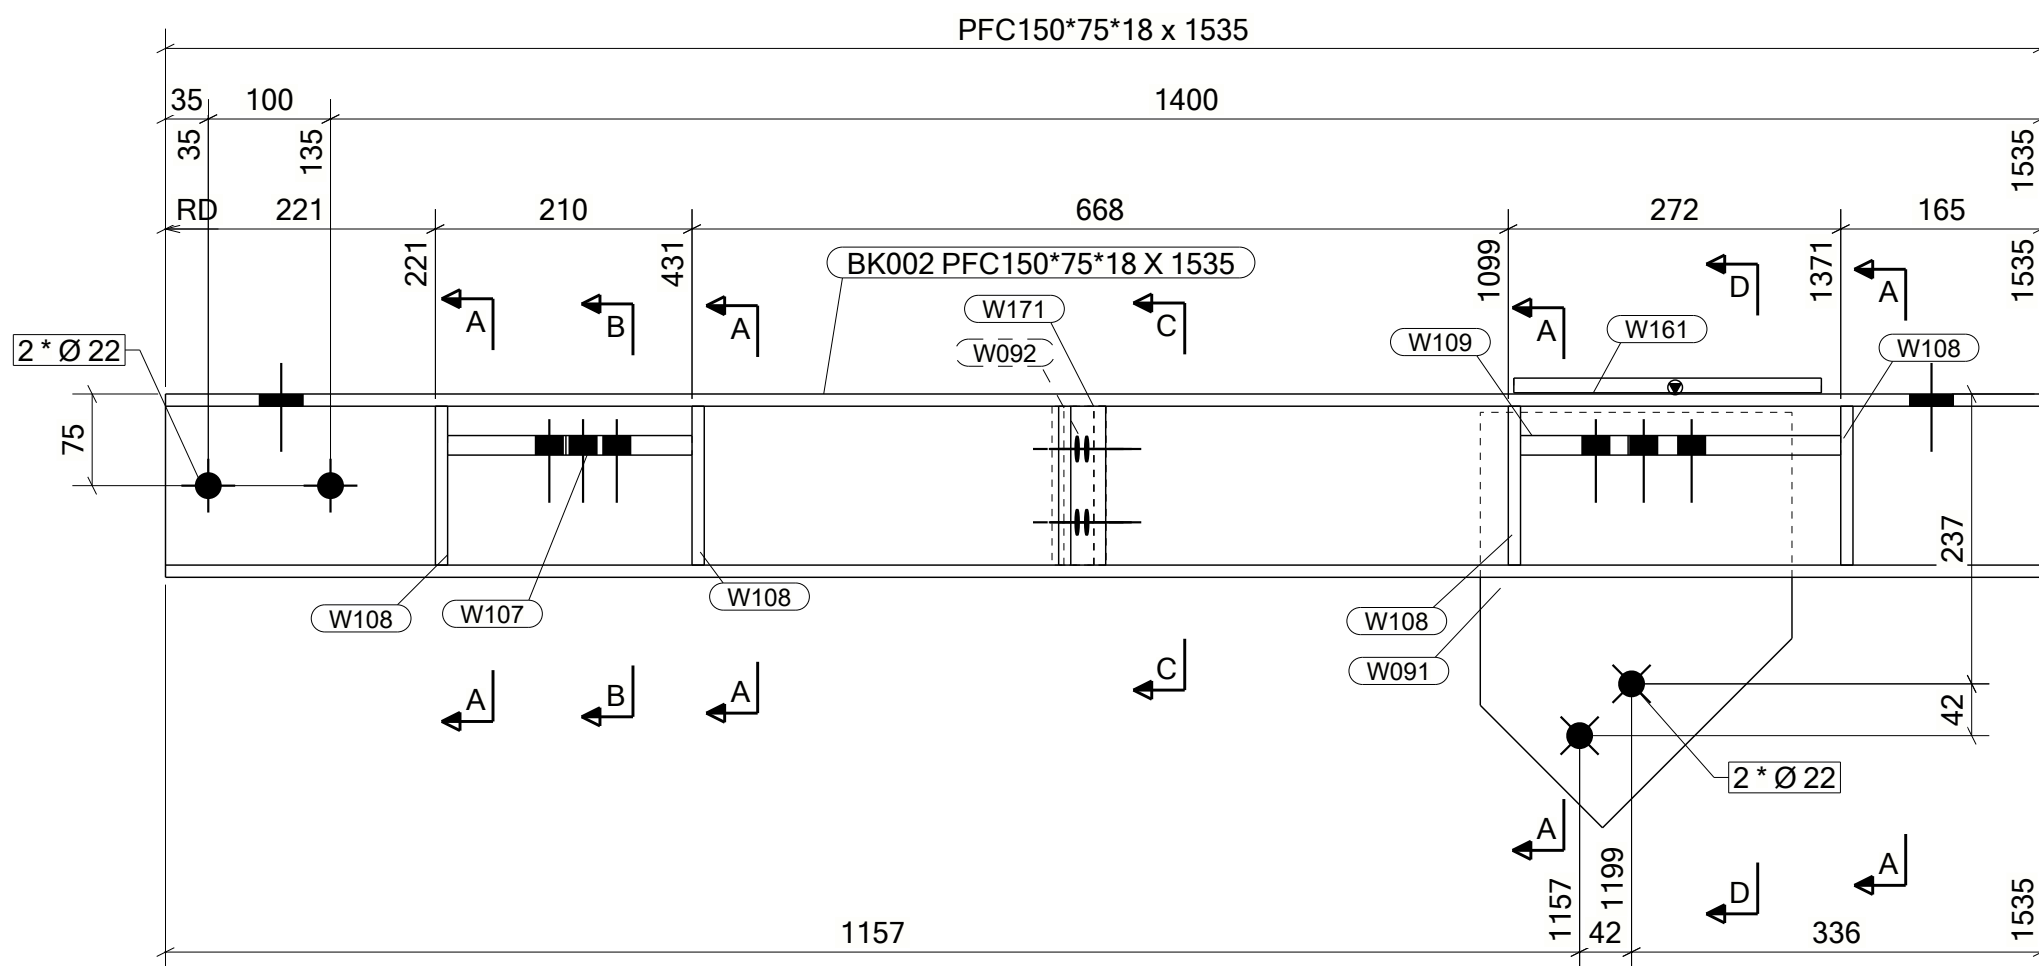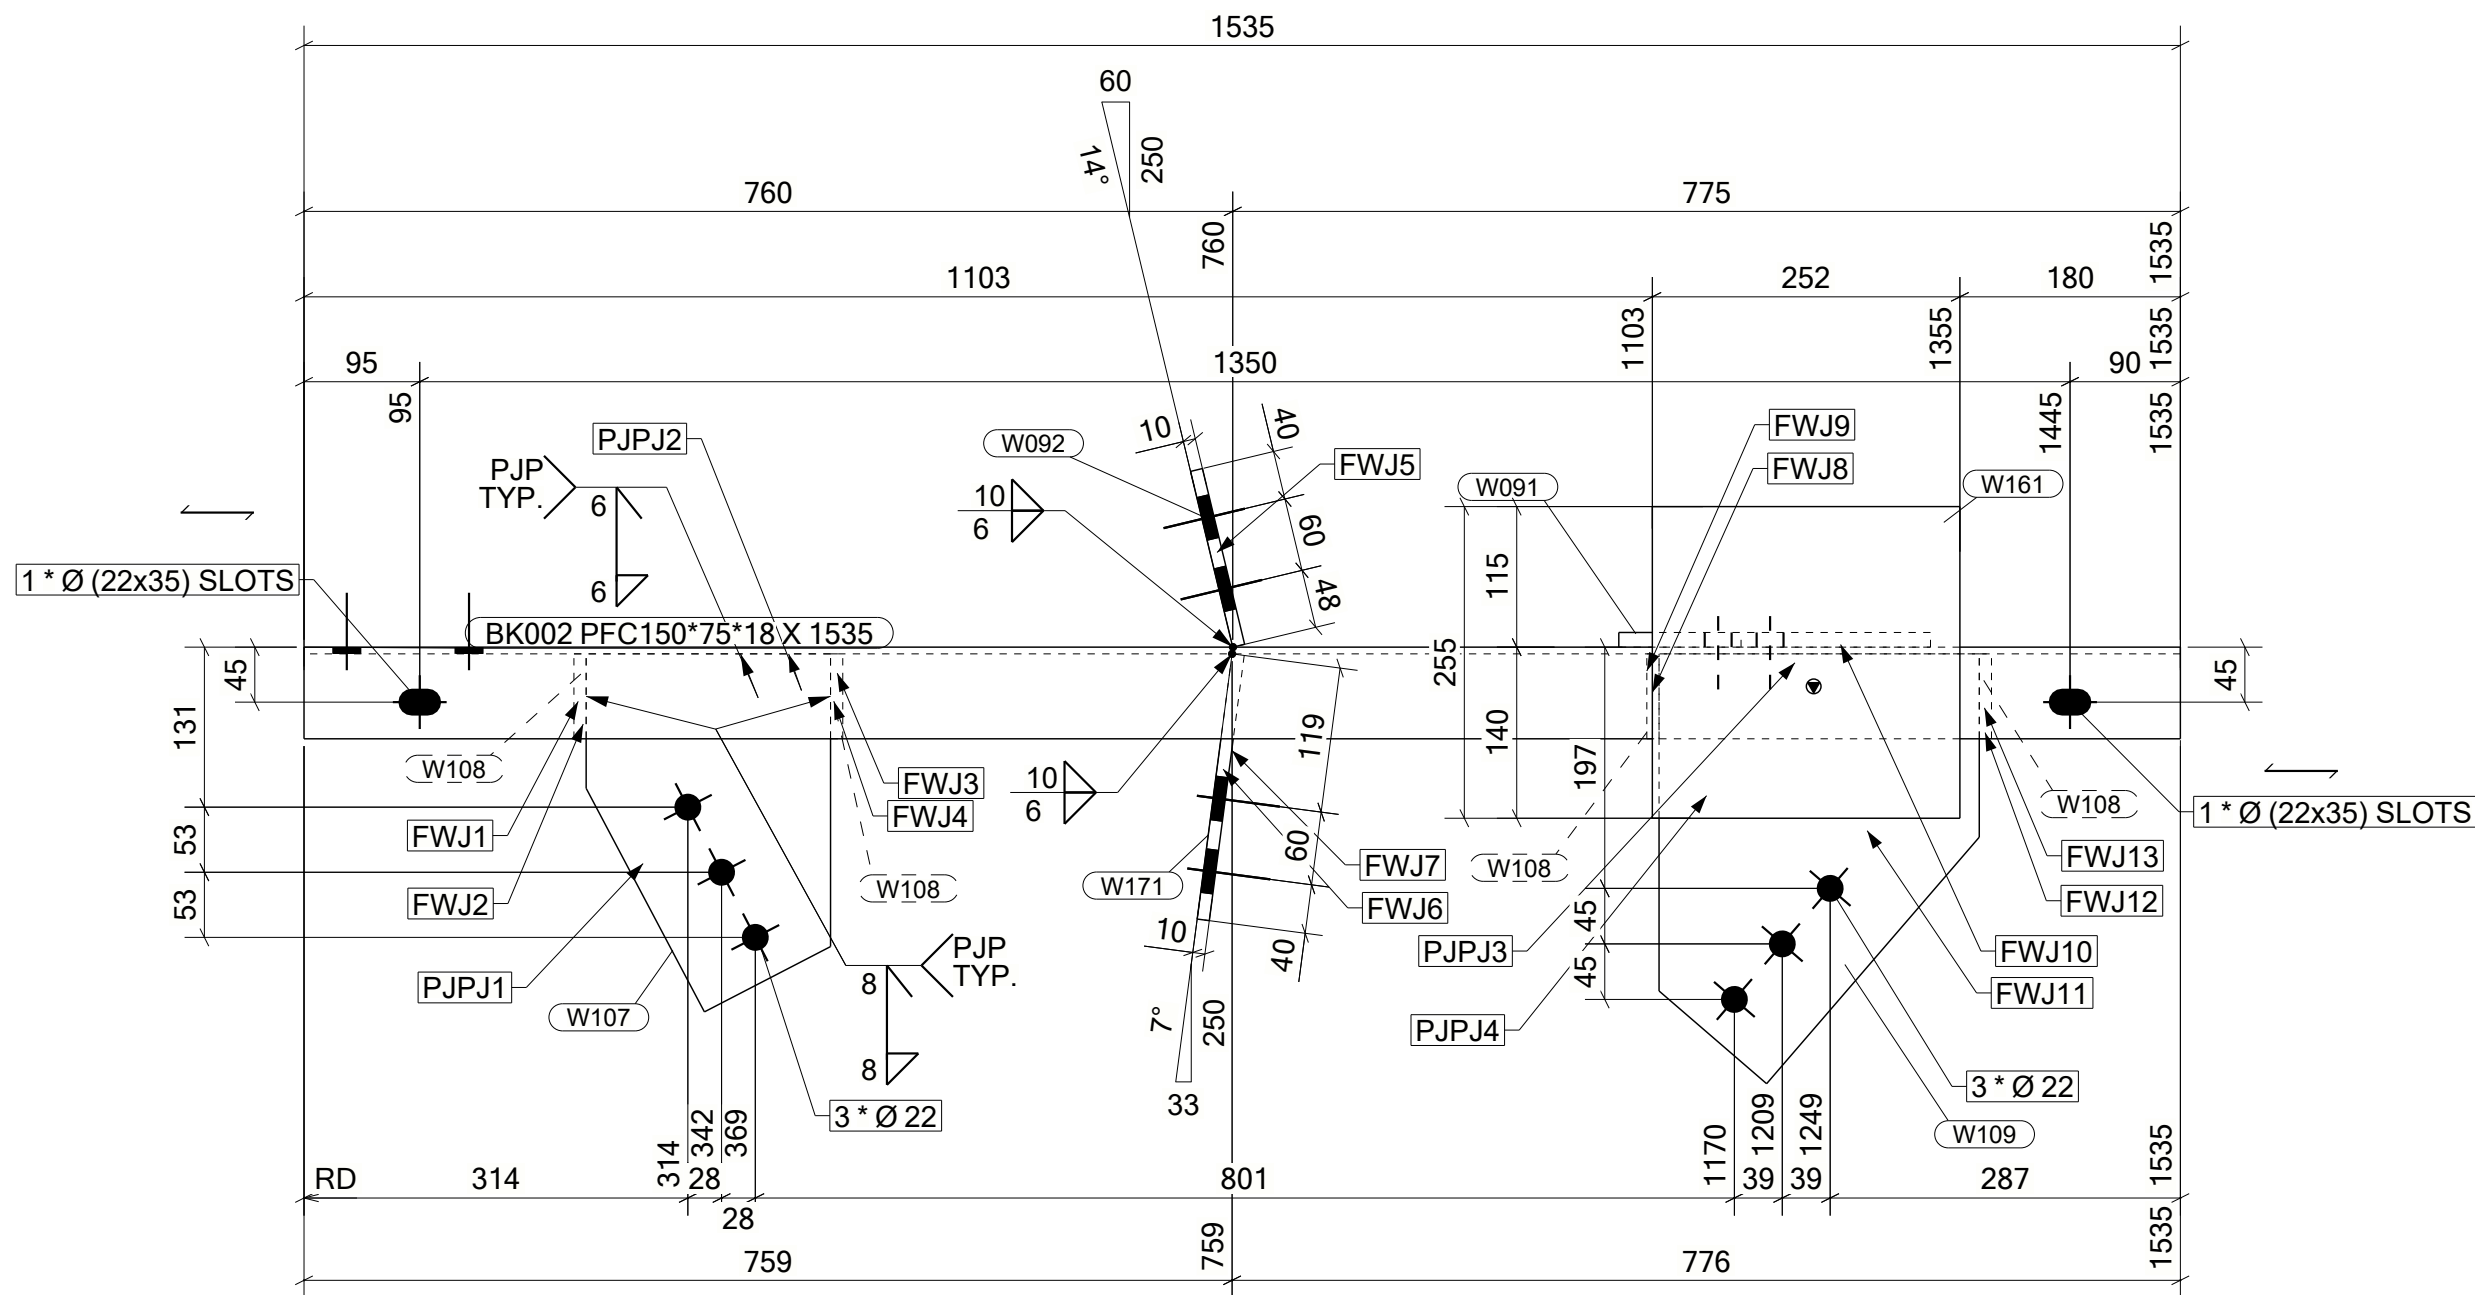

DRAWING NO. : 2307059-732-V-132-BK002										REV. : 00	
ERECTION MARK : 2307059-732-V-132-BK002				DESCRIPTION : BRACKET			COLOR CODE : 10 B 15		QTY : 1		NOS
HOLD:		TYPE: W		TREAT: PN		COST CODE: 2.01		REMARKS:			
LENGTH: 1535		WIDTH: 503		HEIGHT: 368		TOTAL S.AREA: 1.6		(M2)			
POSITION NO.	QTY PER ASSY	SECTION	LENGTH	UNIT WEIGHT (KG)	TOTAL WIEGHT (KG)		GRADE	REVISION	PART ID	TREATMENT	REMARKS
					QTY	WEIGHT					
BK002	1	PF150*75*18	1535	27.475	1	27.48	S275JR	1	MM	PN	
W091	1	PL12X340	255	6.563	1	6.56	S355JR	1	WI		
W092	1	PL10X130	148	1.509	1	1.51	S355JR	1	WI		
W107	1	PL16X200	293	5.899	1	5.90	S355JR	1	WI		
W108	4	PL10X69	130	0.709	4	2.84	S355JR	1	WI		
W109	1	PL16X262	352	8.950	1	8.95	S355JR	1	WI		
W161	1	PL12X255	252	6.044	1	6.04	S355JR	1	WI		
W171	1	PL10X130	219	2.234	1	2.23	S355JR	1	WI		
					UNIT WEIGHT	61.51					
					TOTAL WEIGHT	61.51					
BOLT LIST:-											
BOLT \ STUD		BOLT DESCRIPTION		QTY/ONE		QTY/ALL		FINISH		REMARKS	
BOLT		B1N1W20 X 50 A325M		2		2					


ANCILLARY CATEGORY

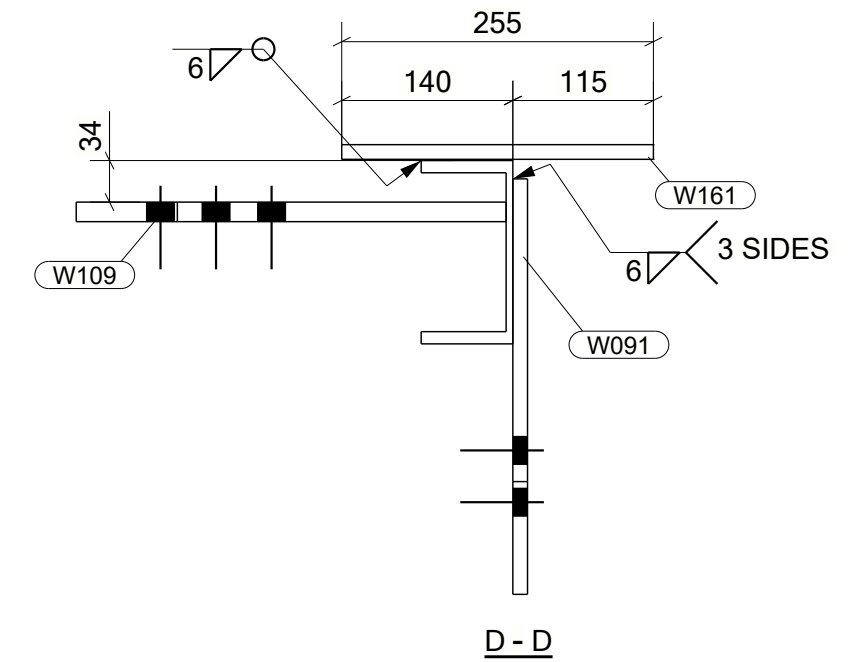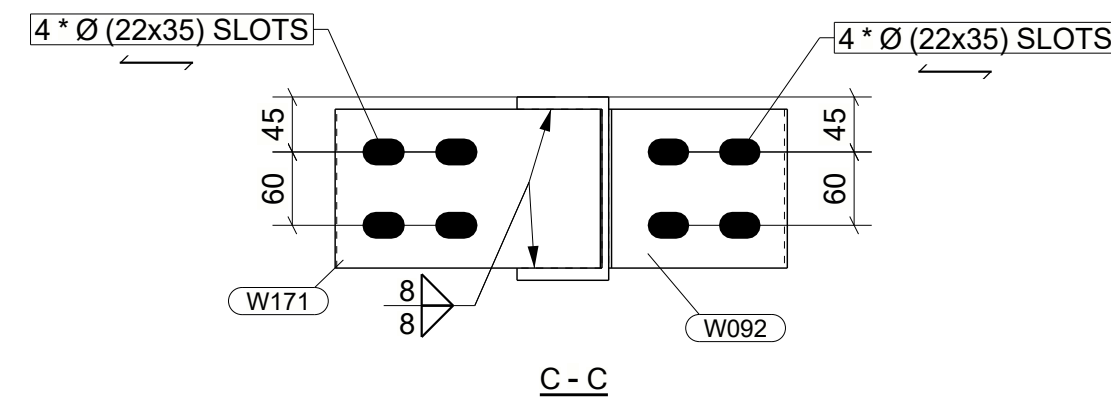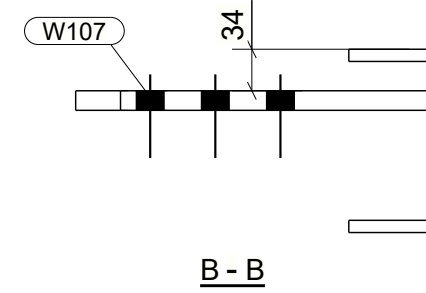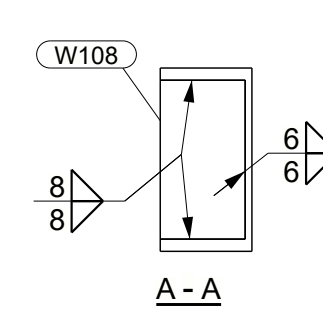FW-J1 TO J13
PJP - J1 TO J4

GA & IFC DRAWINGS REFERENCE	REV.
AD282-732-C-33298,299 & 300	3
AD282-732-C-34324	1
AD282-732-C-34287	1

NOTES :

- 1-ALL DIMENSIONS ARE GIVEN IN MILLIMETERS (U.N.O.).
- 2-  DENOTES ASSEMBLY ORIENTATION MARK.
- 3- DON'T SCALE THE DRAWING. FOLLOW THE WRITTEN DIMENSIONS.
- 4- FINISH AS PER PROJECT SPEC.
- 5- STRUCTURAL STEELWORK SHALL BE IN ACCORDANCE WITH PROJECT SPECIFICATIONS AD282-732-G-03520 & AD282-732-G-03527
- 6-WHEREVER THERE IS NO ACCESS FOR FILLET WELDING TO BE REPLACED BY FULL PENETRATION BUTT WELDING
- 7-FOR CP WELD MARKED LOCATIONS FOLLOW THIS DETAIL

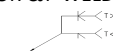


8-ALL WELDS TO BE 6mm FILLET WELD U.N.O.


GRID LOCATION	
EL +115.215	<732-09/<732-B

ANCILLARY CATEGORY

FW-J1 TO J9

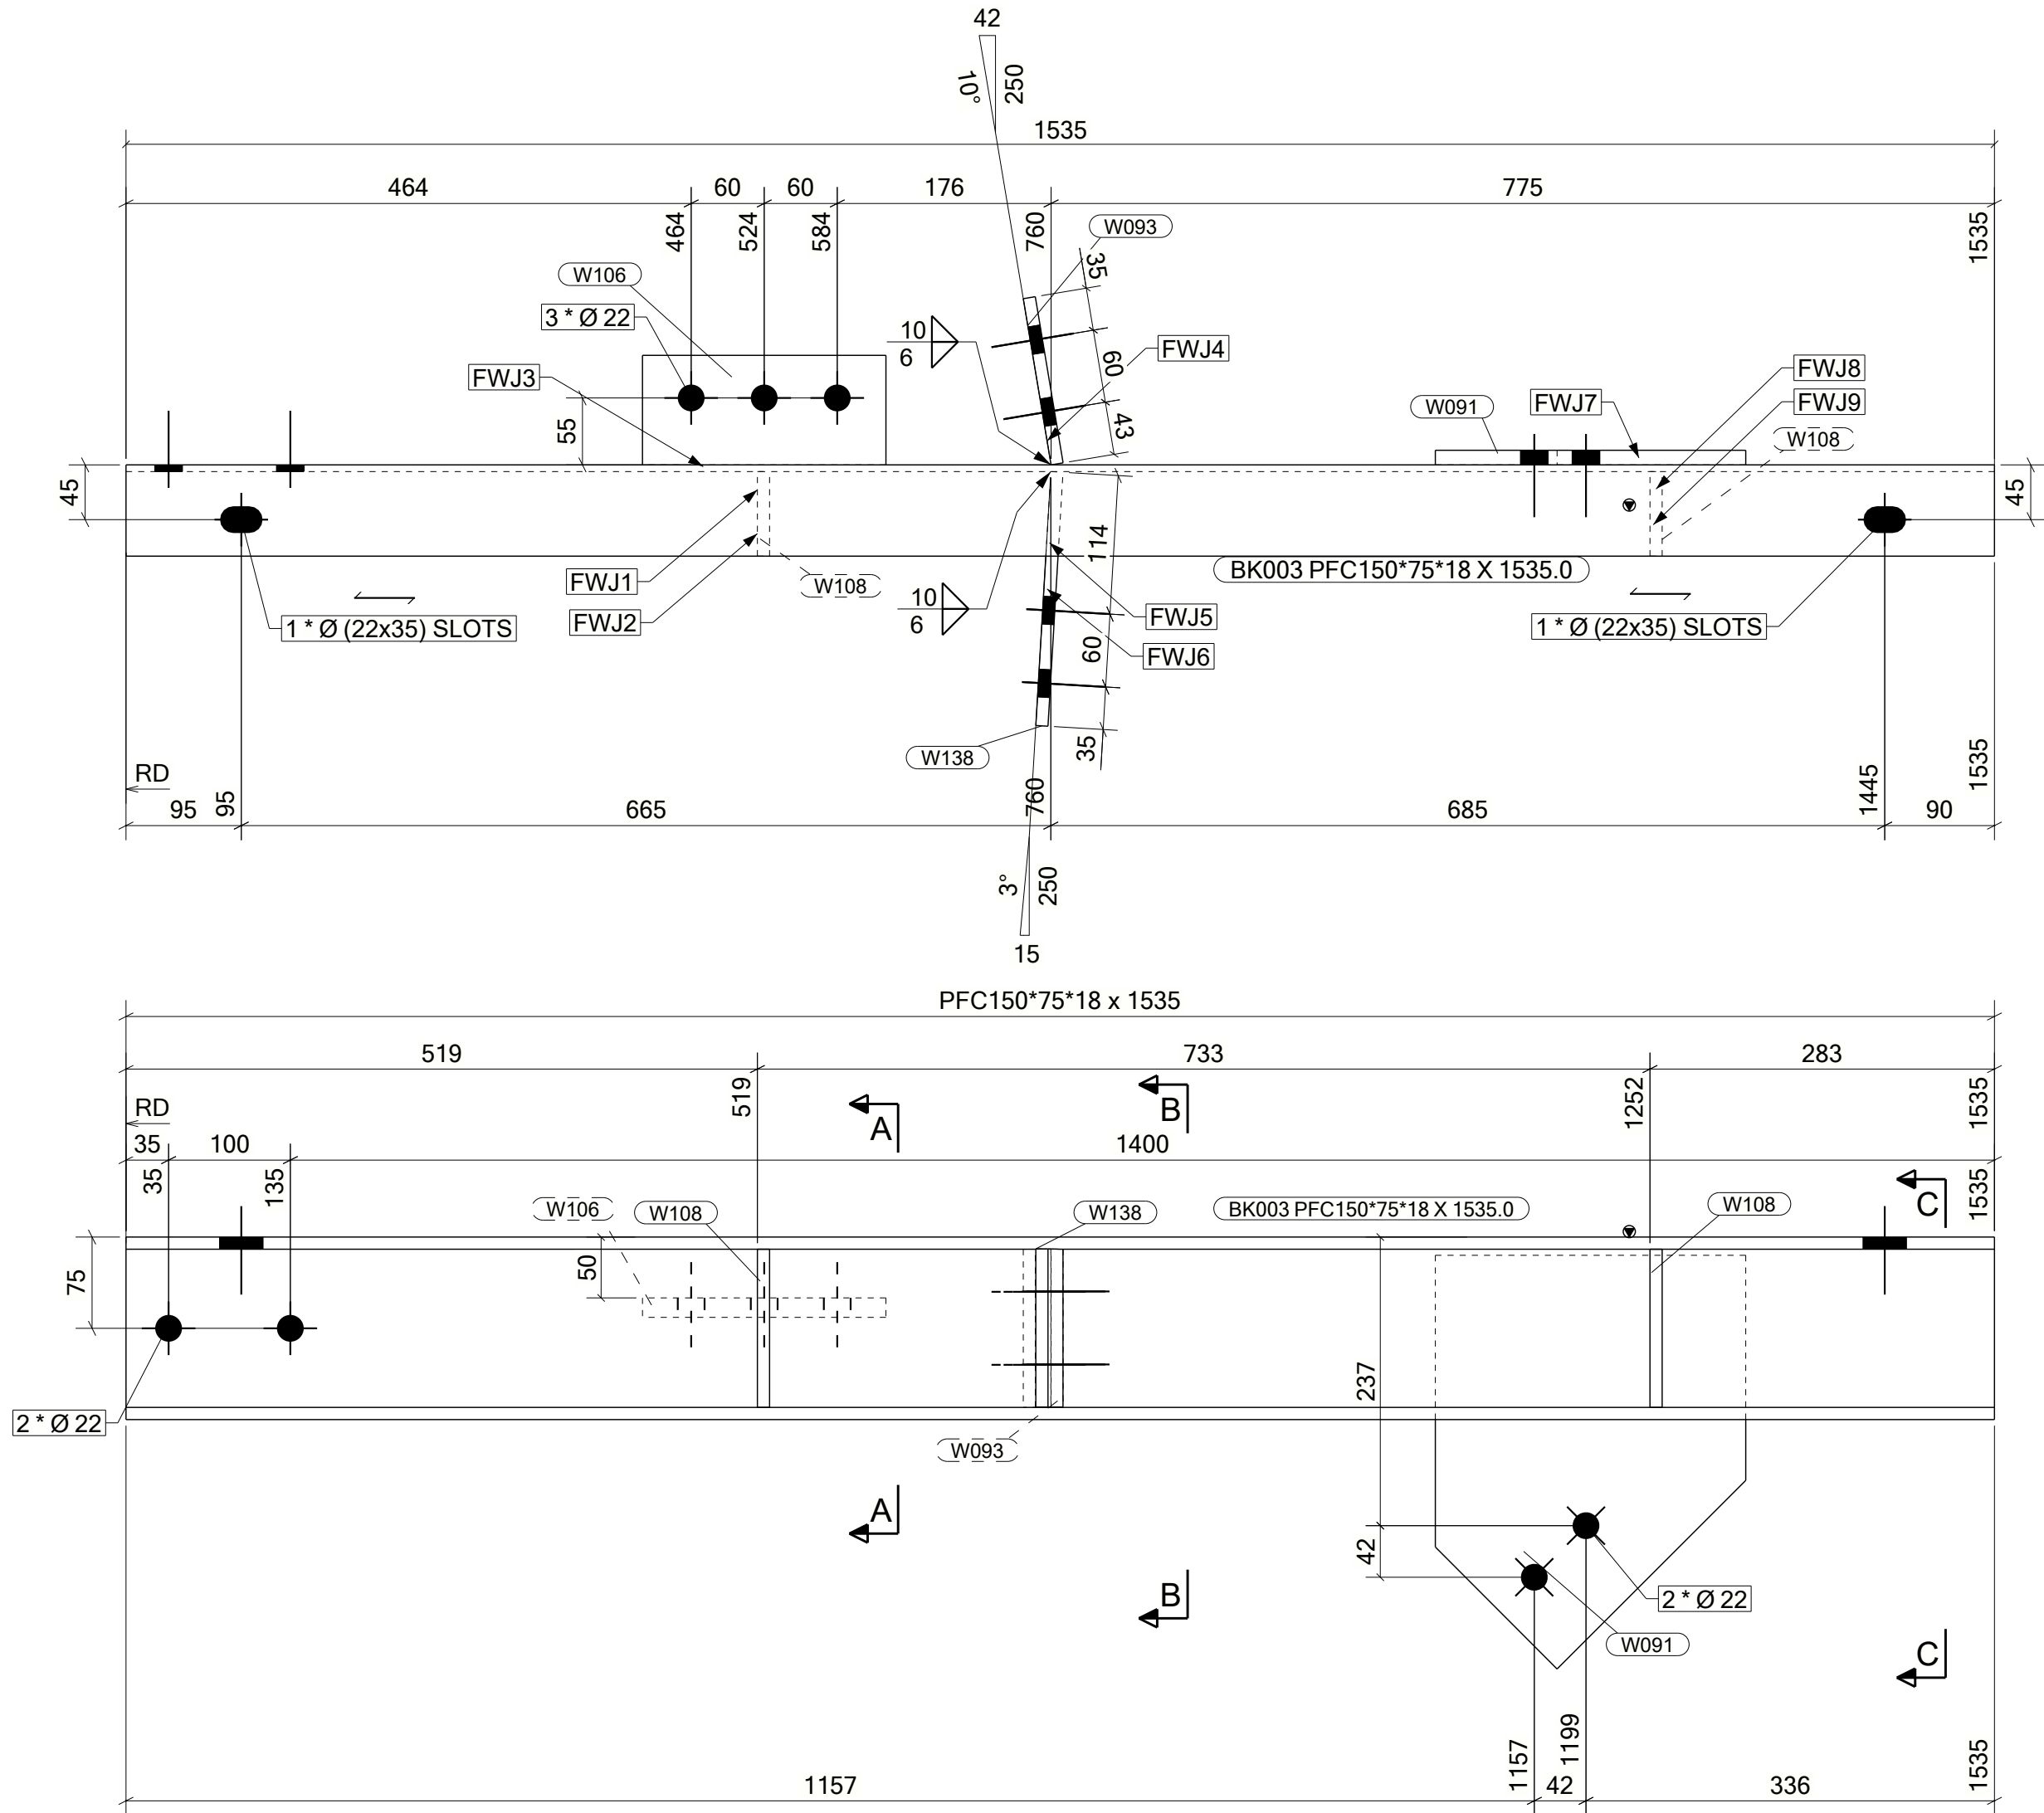



DRAWING NO. : 2307059-732-V-132-BK003								REV.: 00					
ERECTION MARK : 2307059-732-V-132-BK003				DESCRIPTION : BRACKET				COLOR CODE : 10 B 15		QTY : 1		NOS	
HOLD:		TYPE: W		TREAT: PN		COST CODE: 2.01				REMARKS:			
LENGTH: 1535		WIDTH: 353		HEIGHT: 355		TOTAL S.AREA: 1.2				(M2)			
POSITION NO.	QTY PER ASSLY	SECTION	LENGTH	UNIT WEIGHT (KG)	TOTAL WIEGHT (KG)		GRADE	REVISION	PART ID	TREATMENT	REMARKS		
					QTY	WEIGHT							
BK003	1	PFC150*75*18	1535	27.473	1	27.47	S275JR	1	MM	PN			
W091	1	PL12X340	255	6.563	1	6.56	S355JR	1	WI				
W093	1	PL10X130	138	1.413	1	1.41	S355JR	1	WI				
W106	1	PL16X90	200	2.261	1	2.26	S355JR	1	WI				
W108	2	PL10X69	130	0.709	2	1.42	S355JR	1	WI				
W138	1	PL10X130	209	2.131	1	2.13	S355JR	1	WI				
					UNIT WEIGHT	41.26							
					TOTAL WEIGHT	41.26							
BOLT LIST:-													
BOLT \ STUD		BOLT DESCRIPTION		QTY/ONE		QTY/ALL		FINISH		REMARKS			
BOLT		B1N1W20 × 50 A325M		2		2							

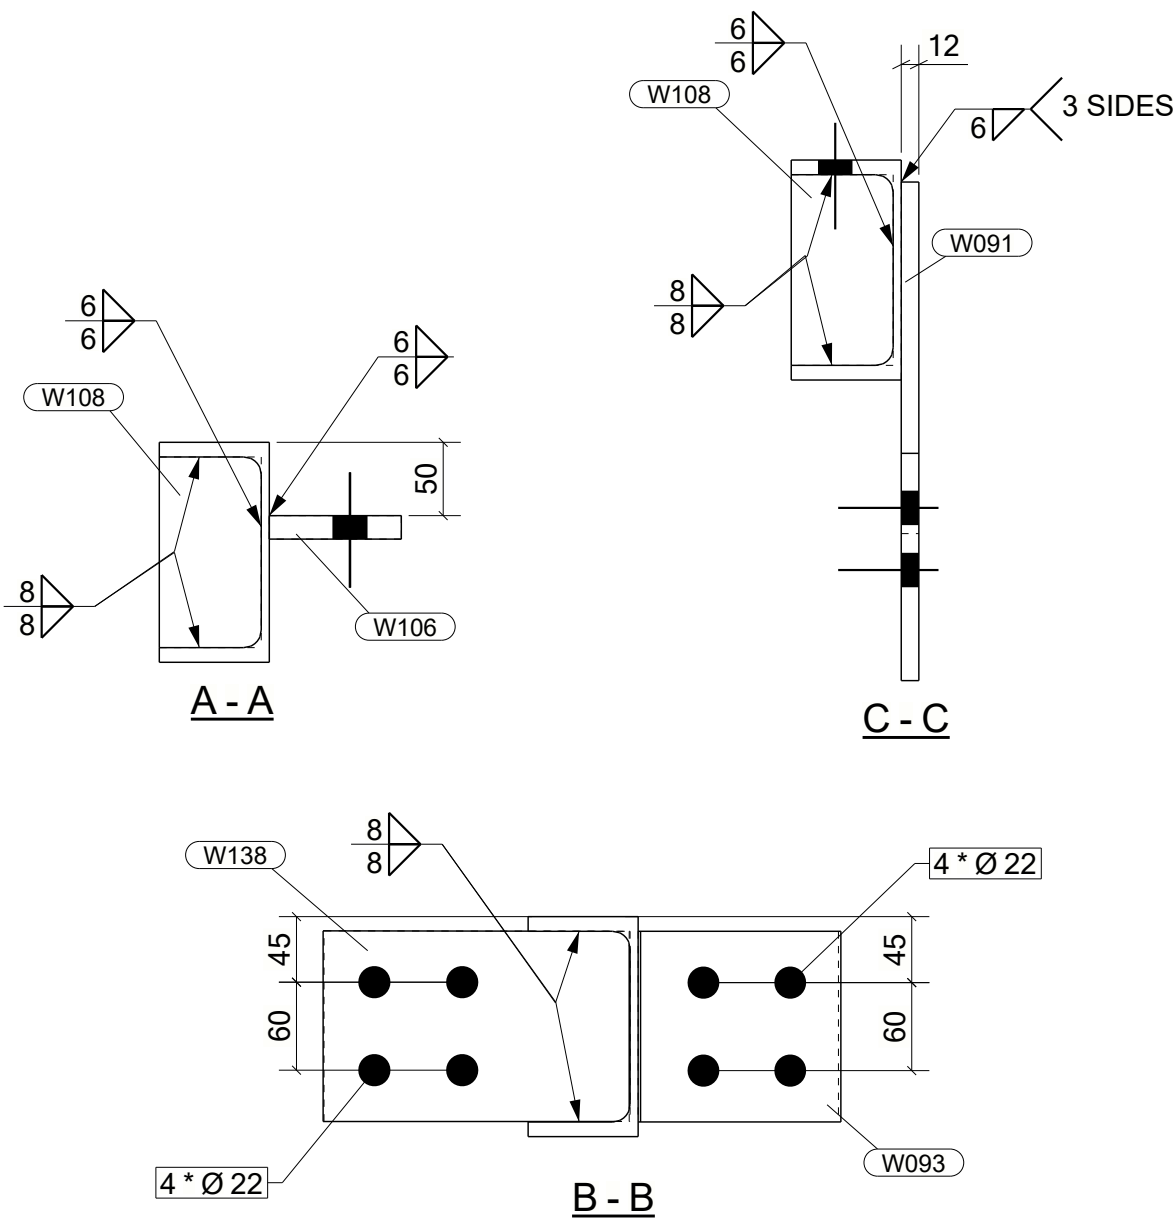

GA & IFC DRAWINGS REFERENCE	REV.
AD282-732-C-33298,299 & 300	3
AD282-732-C-34324	1
AD282-732-C-34287	1

- NOTES :
- 1-ALL DIMENSIONS ARE GIVEN IN MILLIMETERS (U.N.O.).
 - 2- DENOTES ASSEMBLY ORIENTATION MARK.
 - 3-DON'T SCALE THE DRAWING. FOLLOW THE WRITTEN DIMENSIONS.
 - 4- FINISH AS PER PROJECT SPEC.
 - 5- STRUCTURAL STEELWORK SHALL BE IN ACCORDANCE WITH PROJECT SPECIFICATIONS AD282-732-G-03520 & AD282-732-G-03527
 - 6-WHEREVER THERE IS NO ACCESS FOR FILLET WELDING TO BE REPLACED BY FULL PENETRATION BUTT WELDING
 - 7-FOR CJP WELD MARKED LOCATIONS FOLLOW THIS DETAIL
 - 8-ALL WELDS TO BE 6mm FILLET WELD U.N.O.








GRID LOCATION	
EL +120.900	<732-09/<732-B

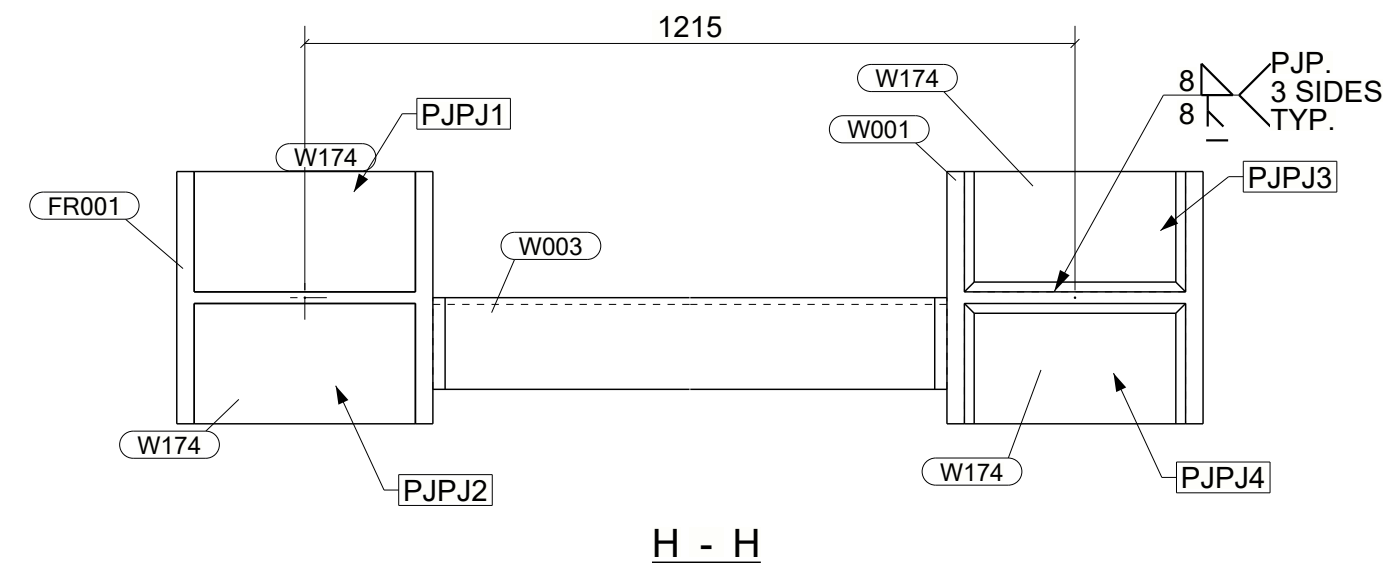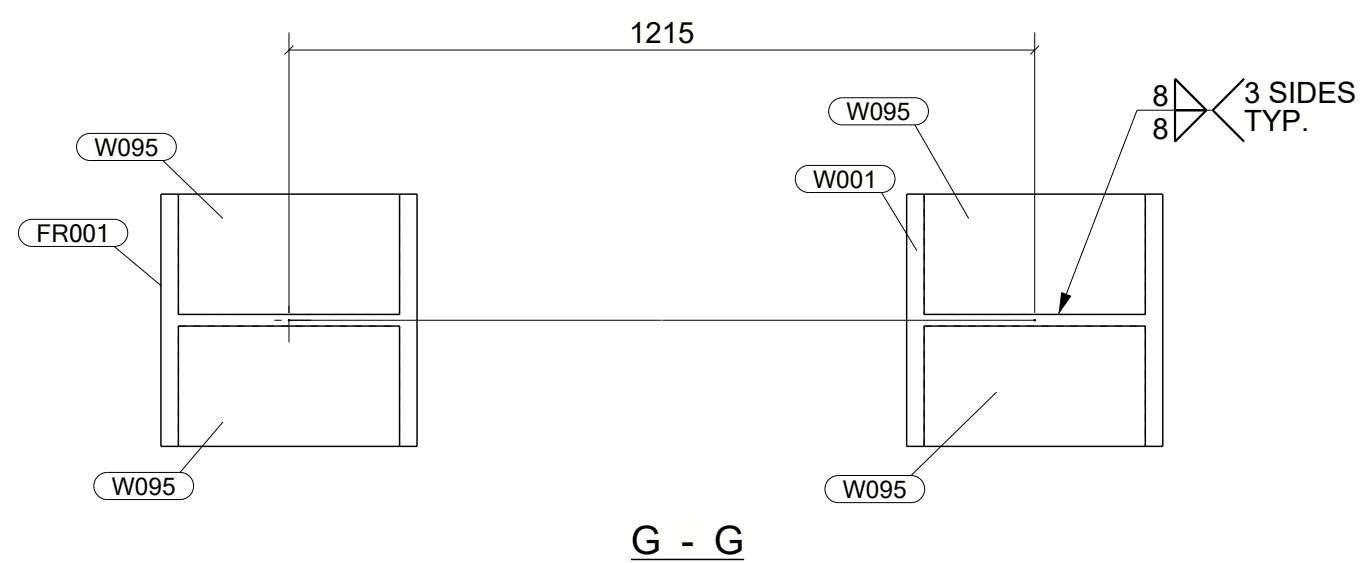

ANCILLARY CATEGORY

FW-J1 TO J30
PJP-J1 TO J4
CJP-J1 TO J2

DRAWING NO. : 2307059-732-V-132-FR001										REV. : 00	
ERECTION MARK : 2307059-732-V-132-FR001				DESCRIPTION : FRAME			COLOR CODE : 10 B 15		QTY : 1		NOS
HOLD:		TYPE: W		TREAT: PN		COST CODE: 2.02		REMARKS:			
LENGTH: 2715		WIDTH: 458		HEIGHT: 1505		TOTAL S.AREA: 9.9		(M2)			
POSITION NO.	QTY PER ASSLY	SECTION	LENGTH	UNIT WEIGHT (KG)	TOTAL WIEGHT (KG)		GRADE	REVISION	PAINT ID	TREATMENT	REMARKS
					QTY	WEIGHT					
FR001	1	W8X40	2699	159.928	1	159.93	S275JR	1	MM	PN	
W001	1	W8X40	2699	159.928	1	159.93	S275JR	1	WI		
W002	1	W8X40	1005	59.578	1	59.58	S275JR	1	WI		
W003	1	PF150*75*18	1005	17.996	1	18.00	S275JR	1	WI		
W095	14	PL10X98	181	1.398	14	19.58	S355JR	1	WI		
W100	1	PL12X338	432	9.543	1	9.54	S355JR	1	WI		
W172	1	PL16X230	290	8.378	1	8.38	S355JR	1	WI		
W174	4	PL10X98	181	1.306	4	5.22	S355JR	1	WI		
W175	1	PL12X337	444	9.767	1	9.77	S355JR	1	WI		
W260	1	PL16X230	230	6.644	1	6.64	S355JR	1	WI		
					UNIT WEIGHT	456.56					
					TOTAL WEIGHT	456.56					
BOLT LIST:-											
BOLT \ STUD	BOLT DESCRIPTION			QTY/ONE	QTY/ALL	FINISH	REMARKS				
BOLT	B1N1W20 X 60 A325M			4	8						

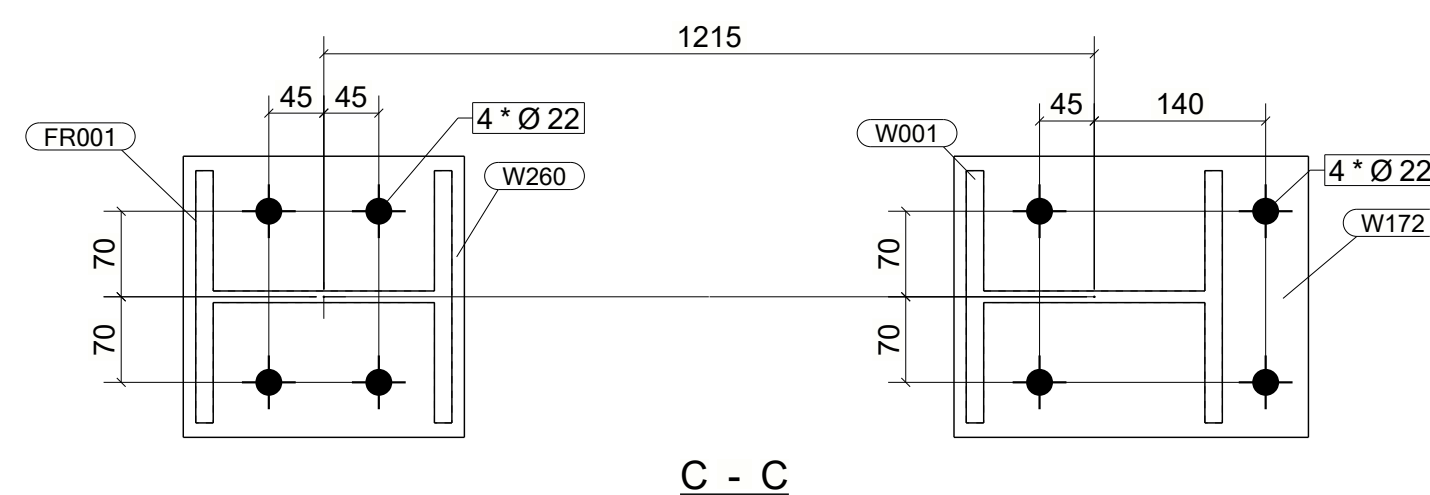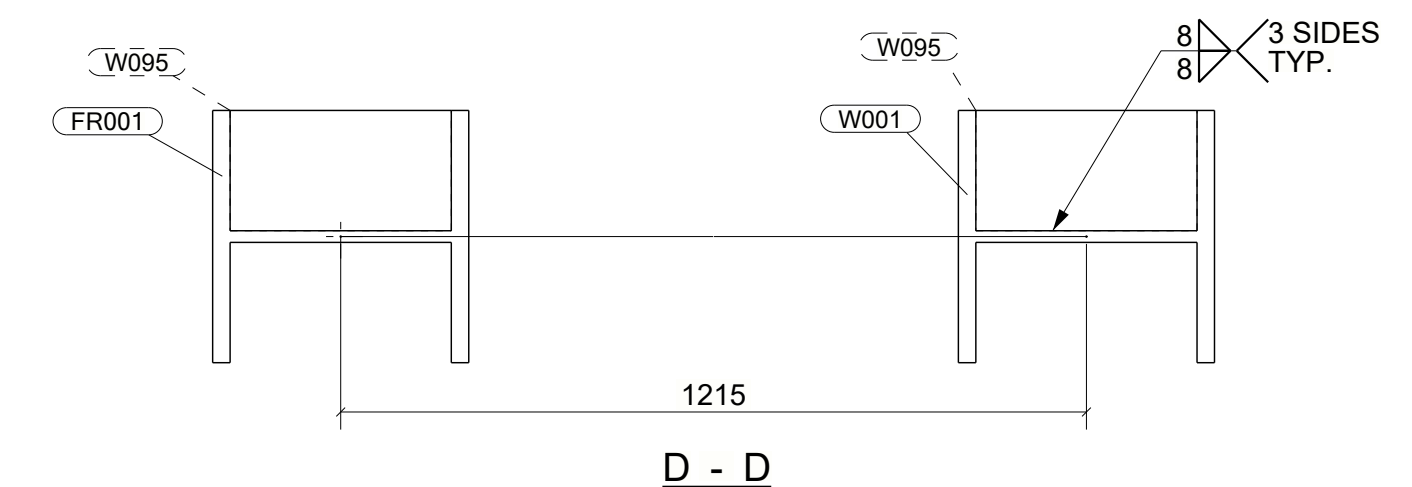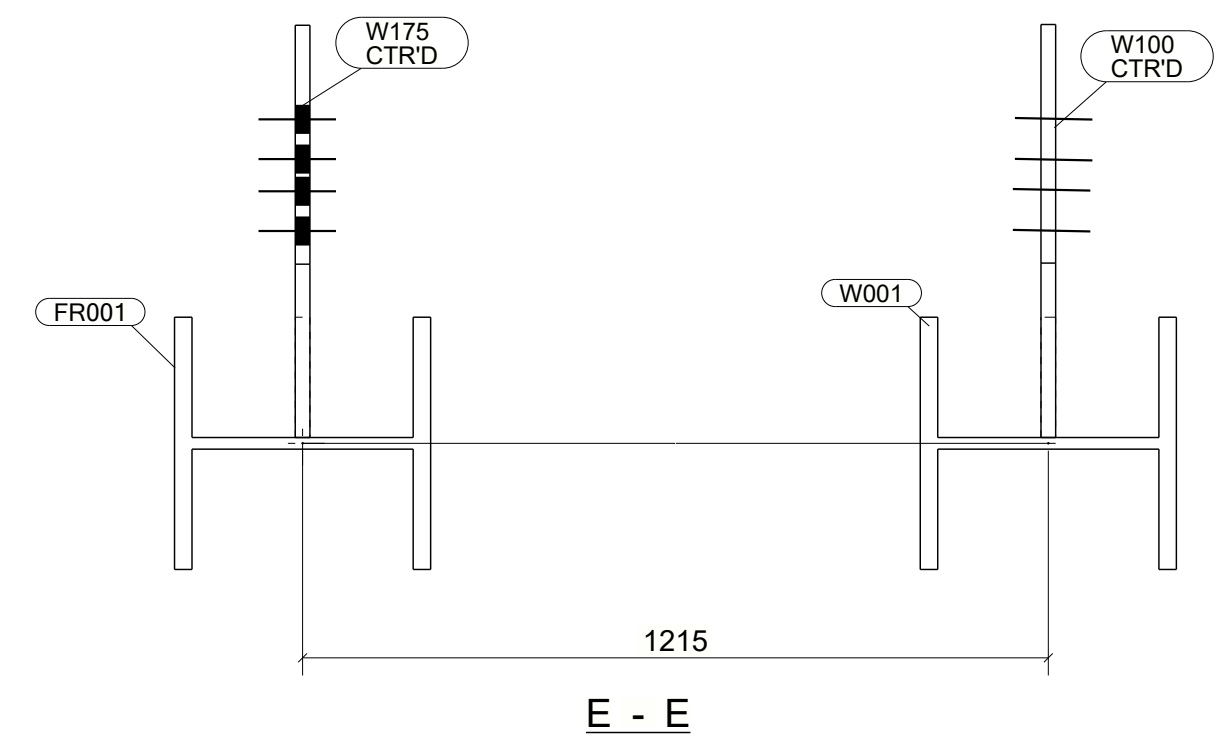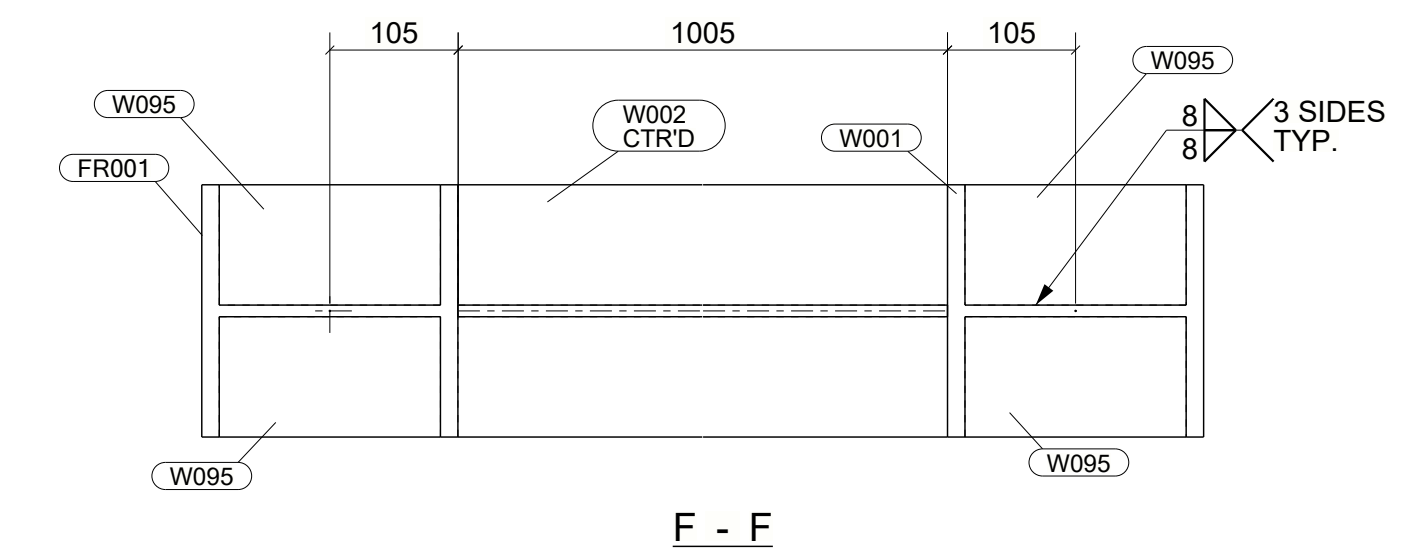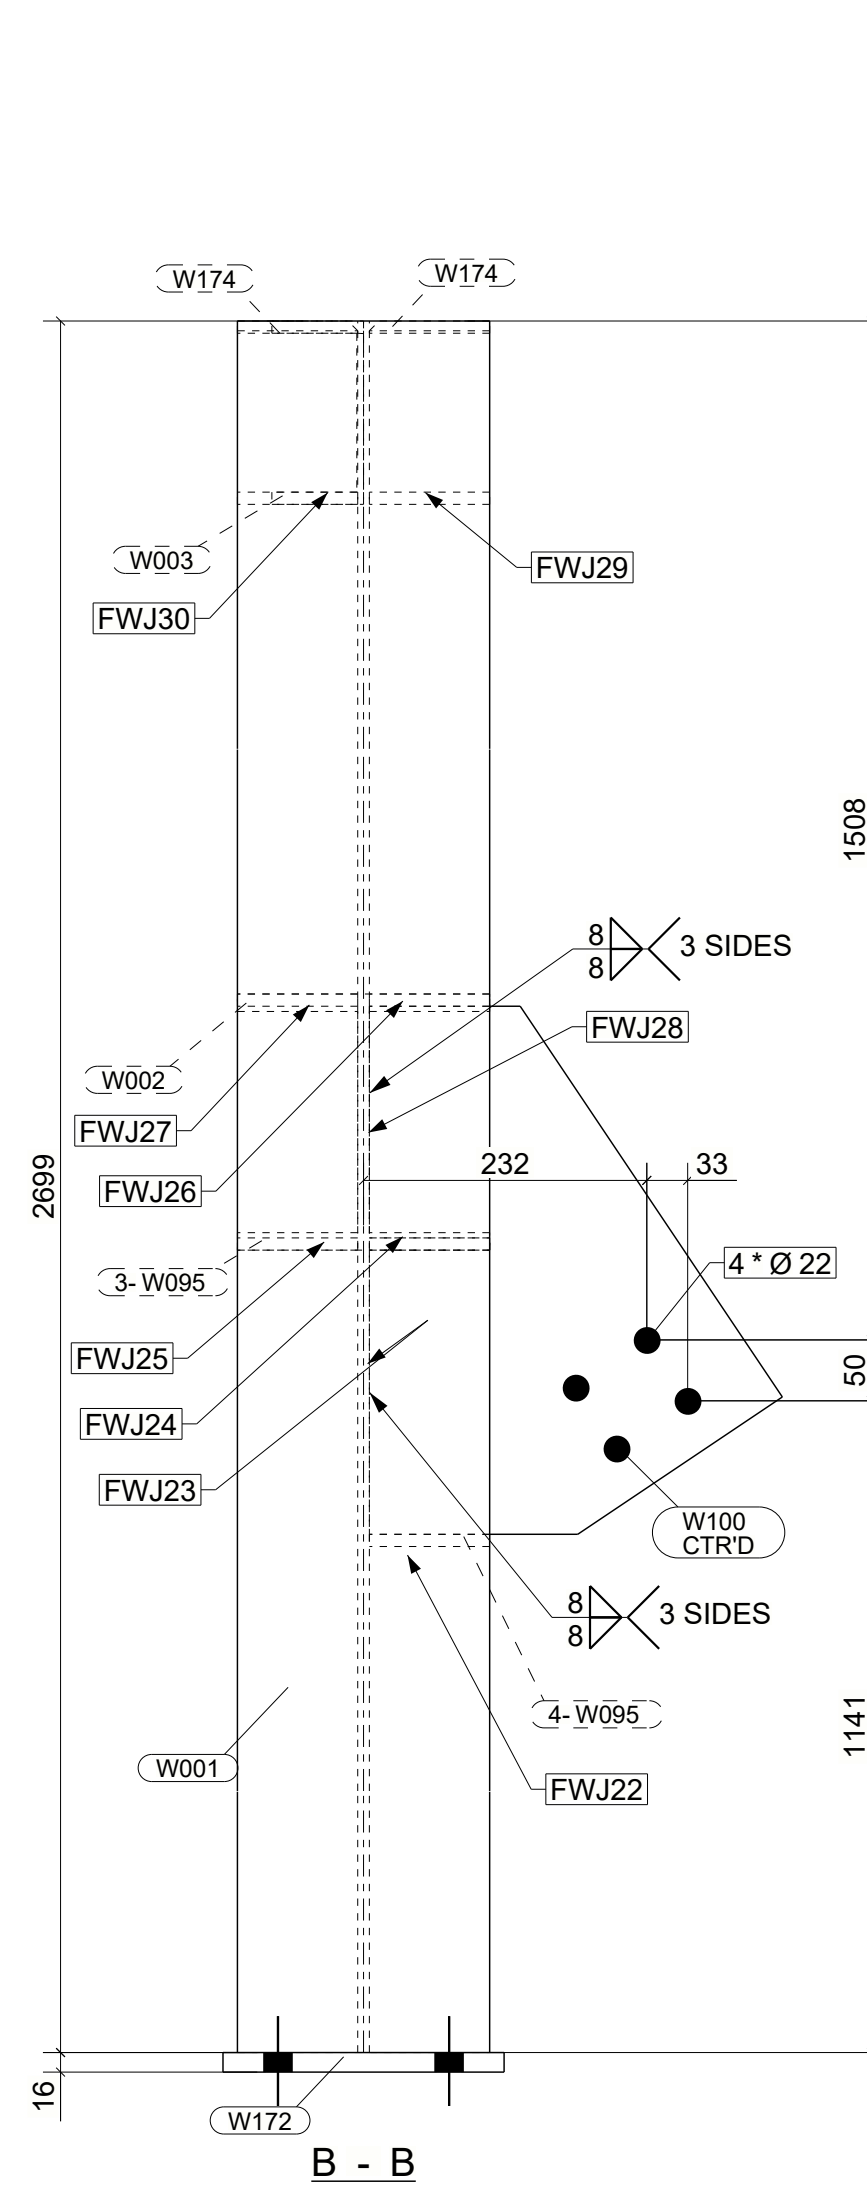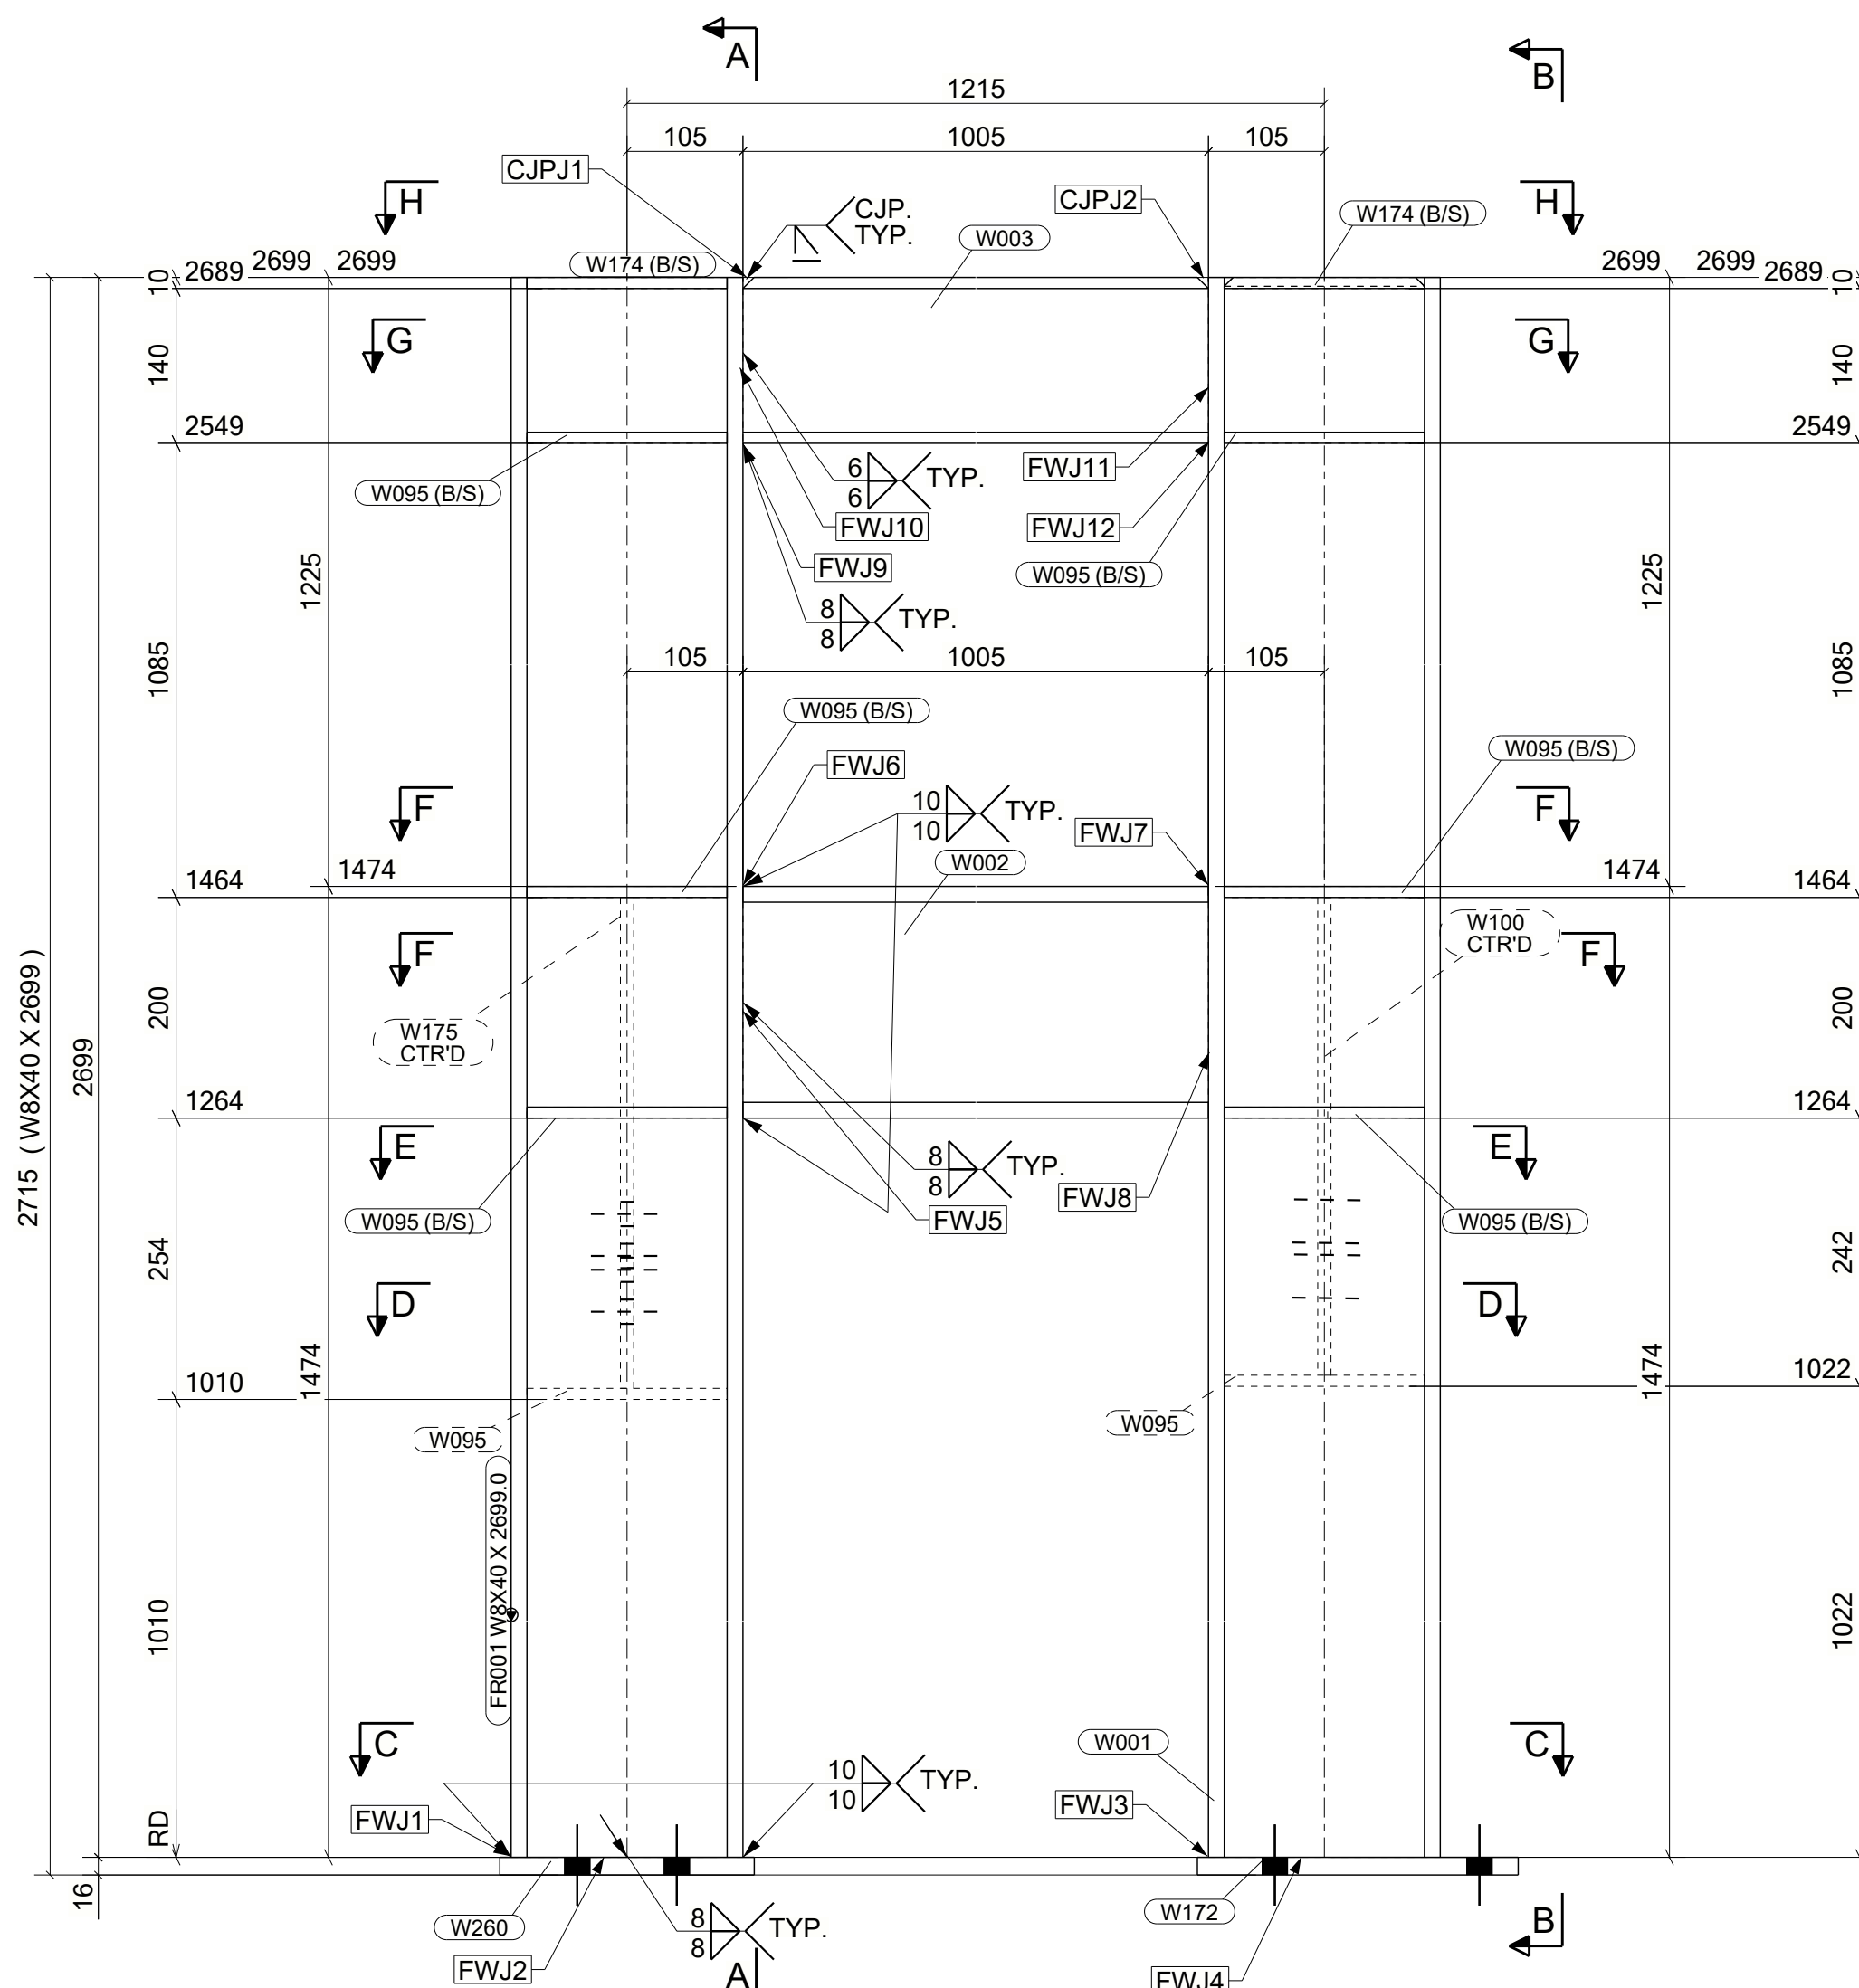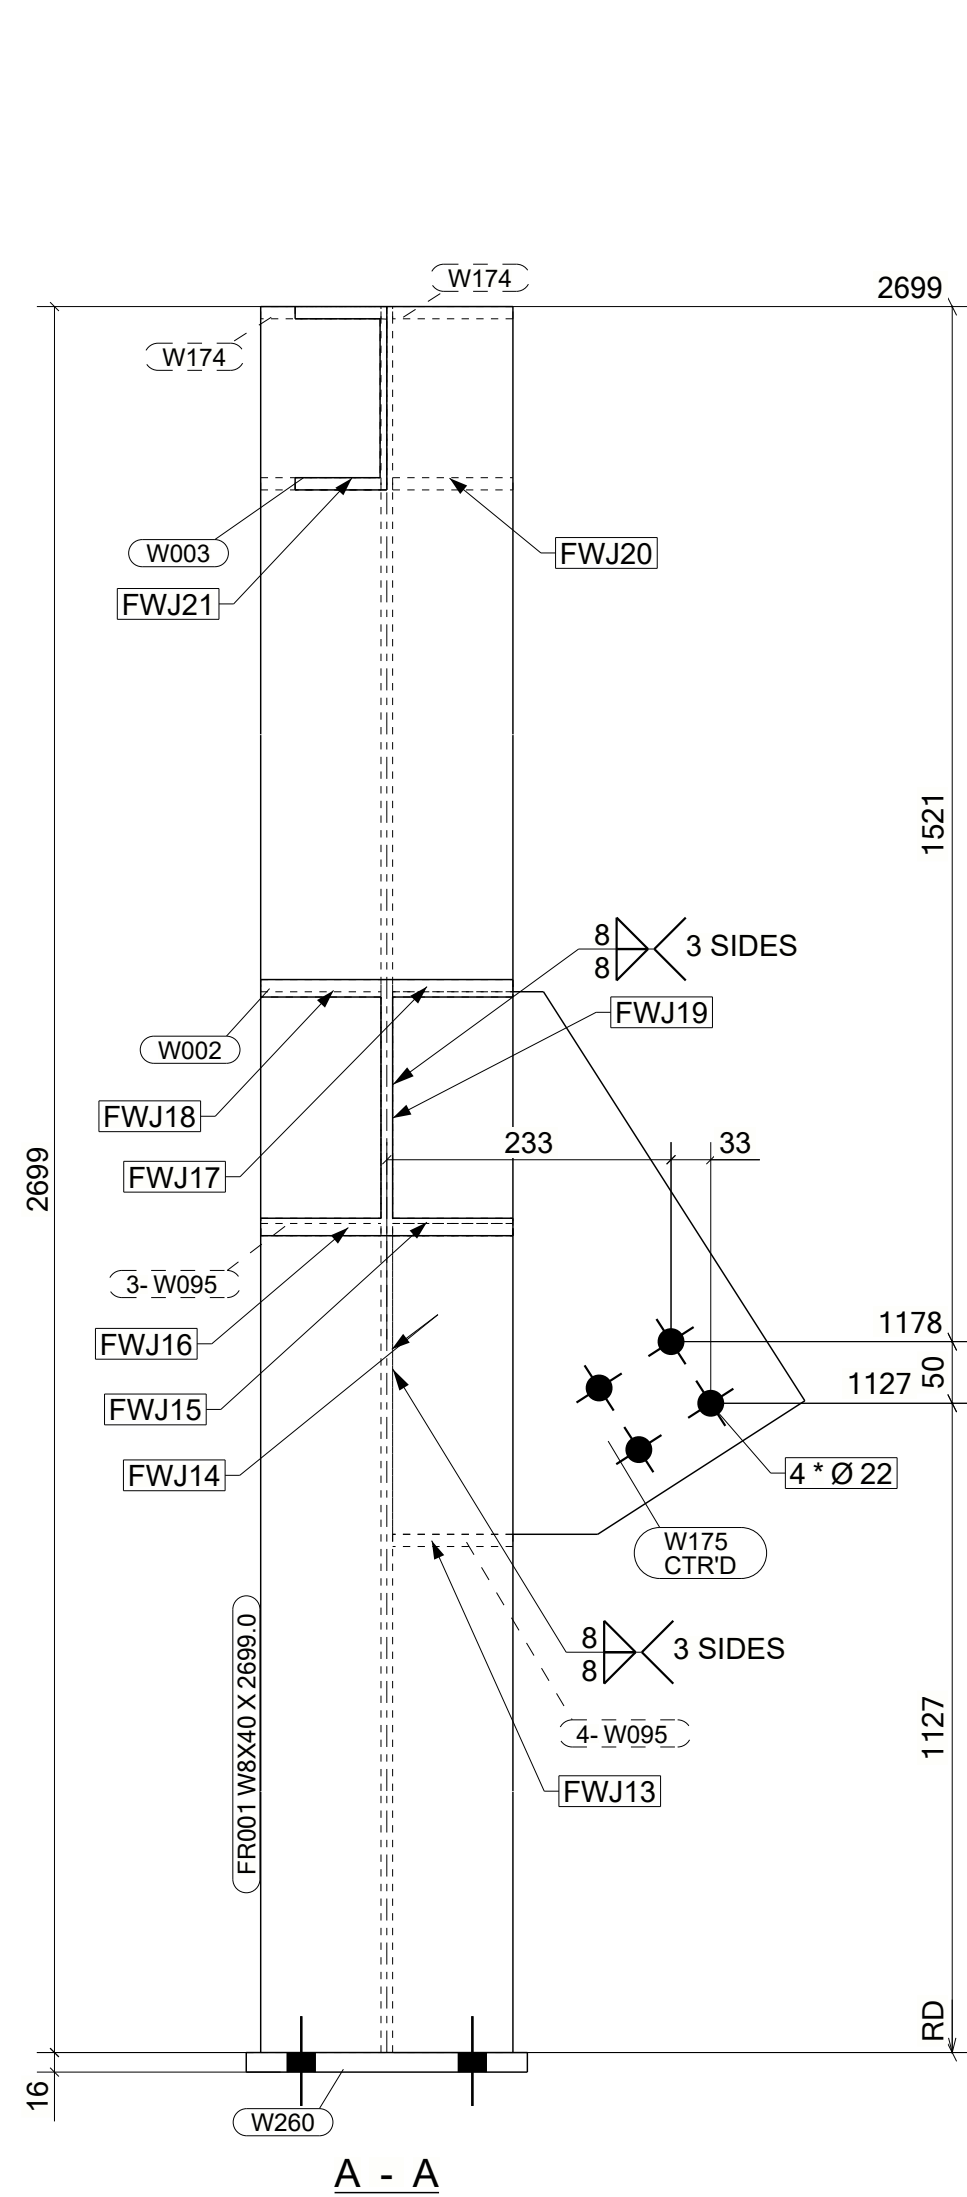


GA & IFC DRAWINGS REFERENCE	REV.
AD282-732-C-33298,299 & 300	3
AD282-732-C-34324	1
AD282-732-C-34287	1

NOTES :

- 1-ALL DIMENSIONS ARE GIVEN IN MILLIMETERS (U.N.O.).
- 2-  DENOTES ASSEMBLY ORIENTATION MARK.
- 3- DON'T SCALE THE DRAWING. FOLLOW THE WRITTEN DIMENSIONS.
- 4- FINISH AS PER PROJECT SPEC.
- 5- STRUCTURAL STEELWORK SHALL BE IN ACCORDANCE WITH PROJECT SPECIFICATIONS AD282-73-G-03520 & AD282-73-G-03527
- 6-WHEREVER THERE IS NO ACCESS FOR FILLET WELDING TO BE REPLACED BY FULL PENETRATION BUTT WELDING
- 7-FOR CIP WELD MARKED LOCATIONS FOLLOW THIS DETAIL

- 8-ALL WELDS TO BE 6mm FILLET WELD U.N.O.

GRID LOCATION	
EL +120.030	732/07-732/06/732F-732G-1

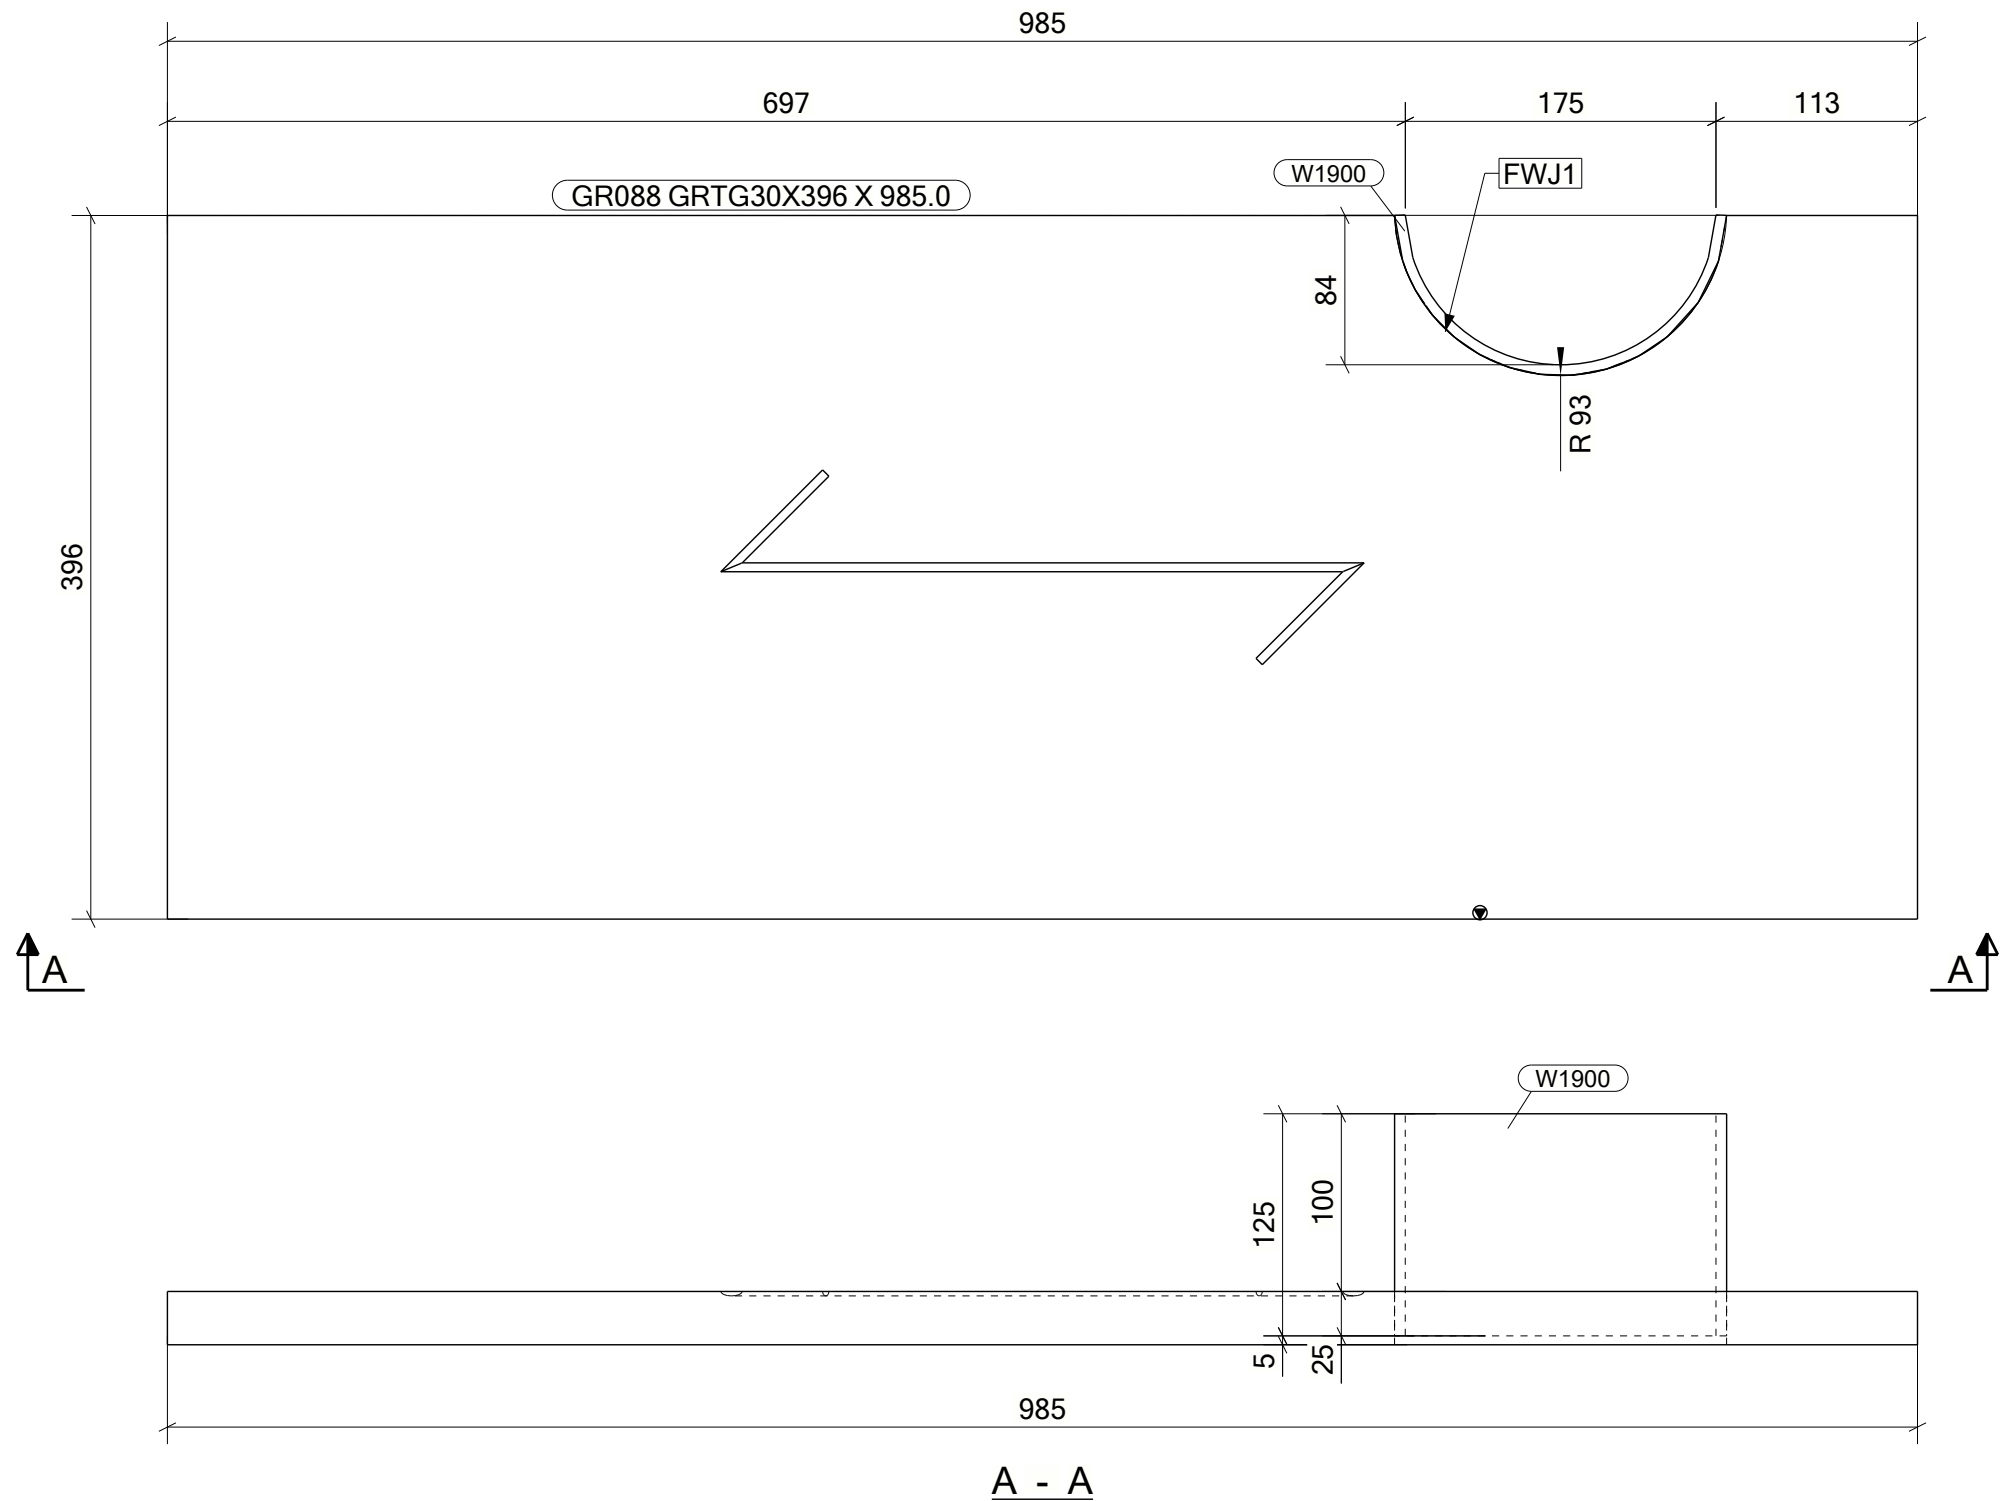


A - A

DRAWING NO. :				2307033-732-PR-10-GR088				REV.: 00					
ERECTION MARK :		2307033-732-PR-10-GR088		DESCRIPTION :		GRATING		COLOR CODE :		QTY : 1		NOS	
HOLD:		TYPE: W		TREAT: GN		COST CODE: 5.01				REMARKS:			
LENGTH: 985		WIDTH: 130		HEIGHT: 396		TOTAL S.AREA: 0.9				(M2)			
POSITION NO.	QTY PER ASSLY	SECTION	LENGTH	UNIT WEIGHT (KG)	TOTAL WIEGHT (KG)		GRADE	REVISION	PART ID	TREATMENT	REMARKS		
					QTY	WEIGHT							
GR088	1	GRTG30X396	985	0.000	1	0.00	A1011M		MM	GN			
W1900	1	FLT125X6	284	1.614	1	1.61	S275JR		WI				
					UNIT WEIGHT	1.61							
					TOTAL WEIGHT	1.61							
BOLT LIST:-													
BOLT \ STUD		BOLT DESCRIPTION		QTY/ONE		QTY/ALL		FINISH		REMARKS			

ANCILLARY CATEGORY

FW- J1

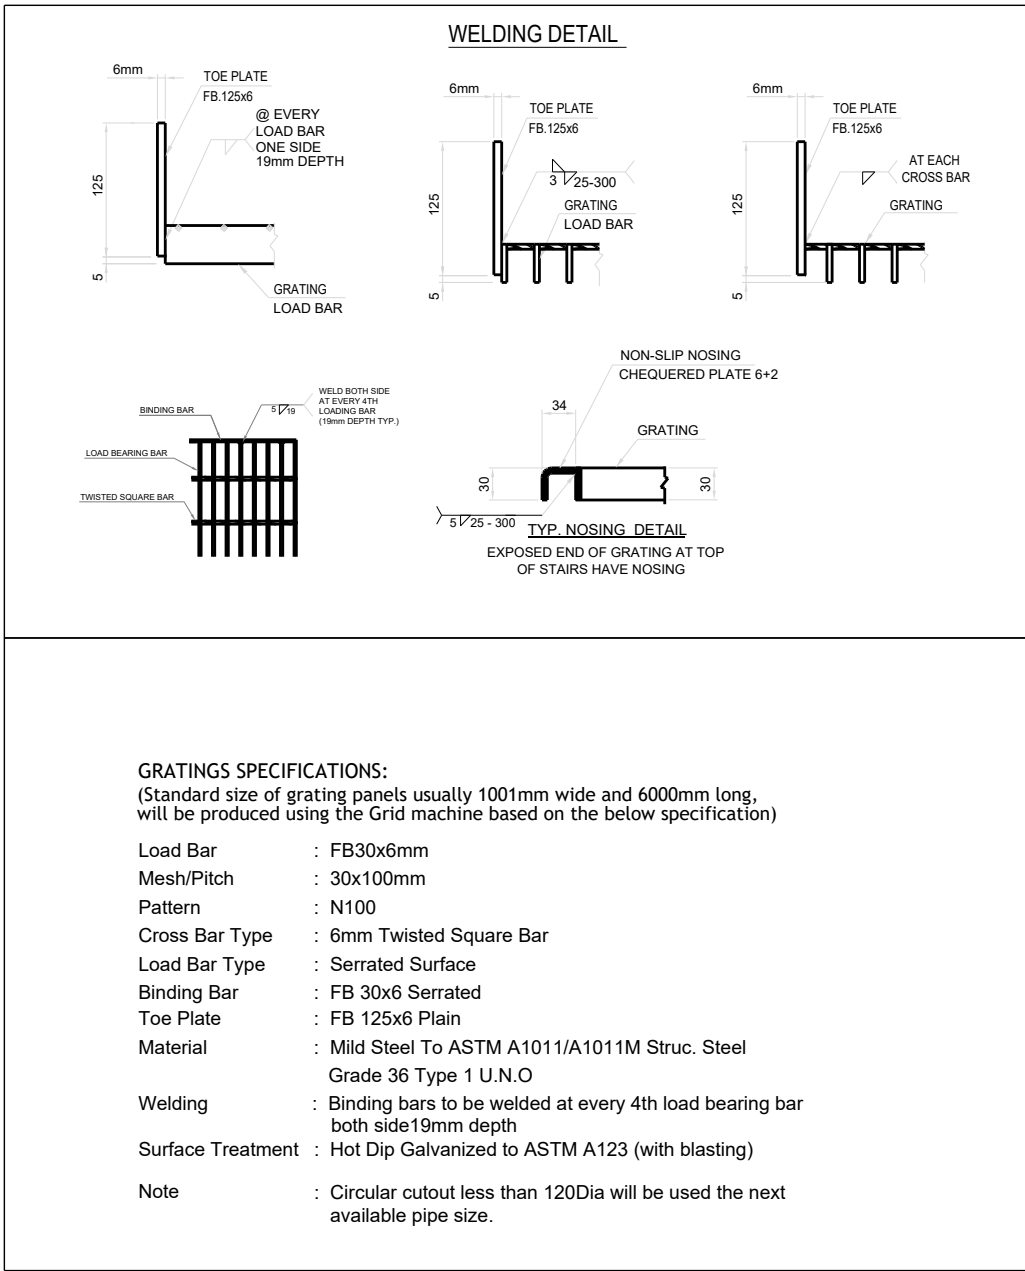

GA & IFC DRAWINGS REFERENCE	REV.
AD282-732-C-33158-61	6
AD282-732-C-33170-73.33539	6
AD282-732-C-34311	2
AD282-732-C-34274	2


NOTES :

- 1-ALL DIMENSIONS ARE GIVEN IN MILLIMETERS (U.N.O.).
- 2-  DENOTES ASSEMBLY ORIENTATION MARK.
- 3-DON'T SCALE THE DRAWING. FOLLOW THE WRITTEN DIMENSIONS.
- 4- FINISH AS PER PROJECT SPEC.
- 5- STRUCTURAL STEELWORK SHALL BE IN ACCORDANCE WITH PROJECT SPECIFICATIONS AD282-732-G-03520 & AD282-732-G-03527
- 6-WHEREVER THERE IS NO ACCESS FOR FILLET WELDING TO BE REPLACED BY FULL PENETRATION BUTT WELDING
- 7-FOR CJP WELD MARKED LOCATIONS FOLLOW THIS DETAIL



- 8-ALL WELDS TO BE 6mm FILLET WELD U.N.O.


GRID LOCATION	
EL +120.030	732/06-732/05/<732E

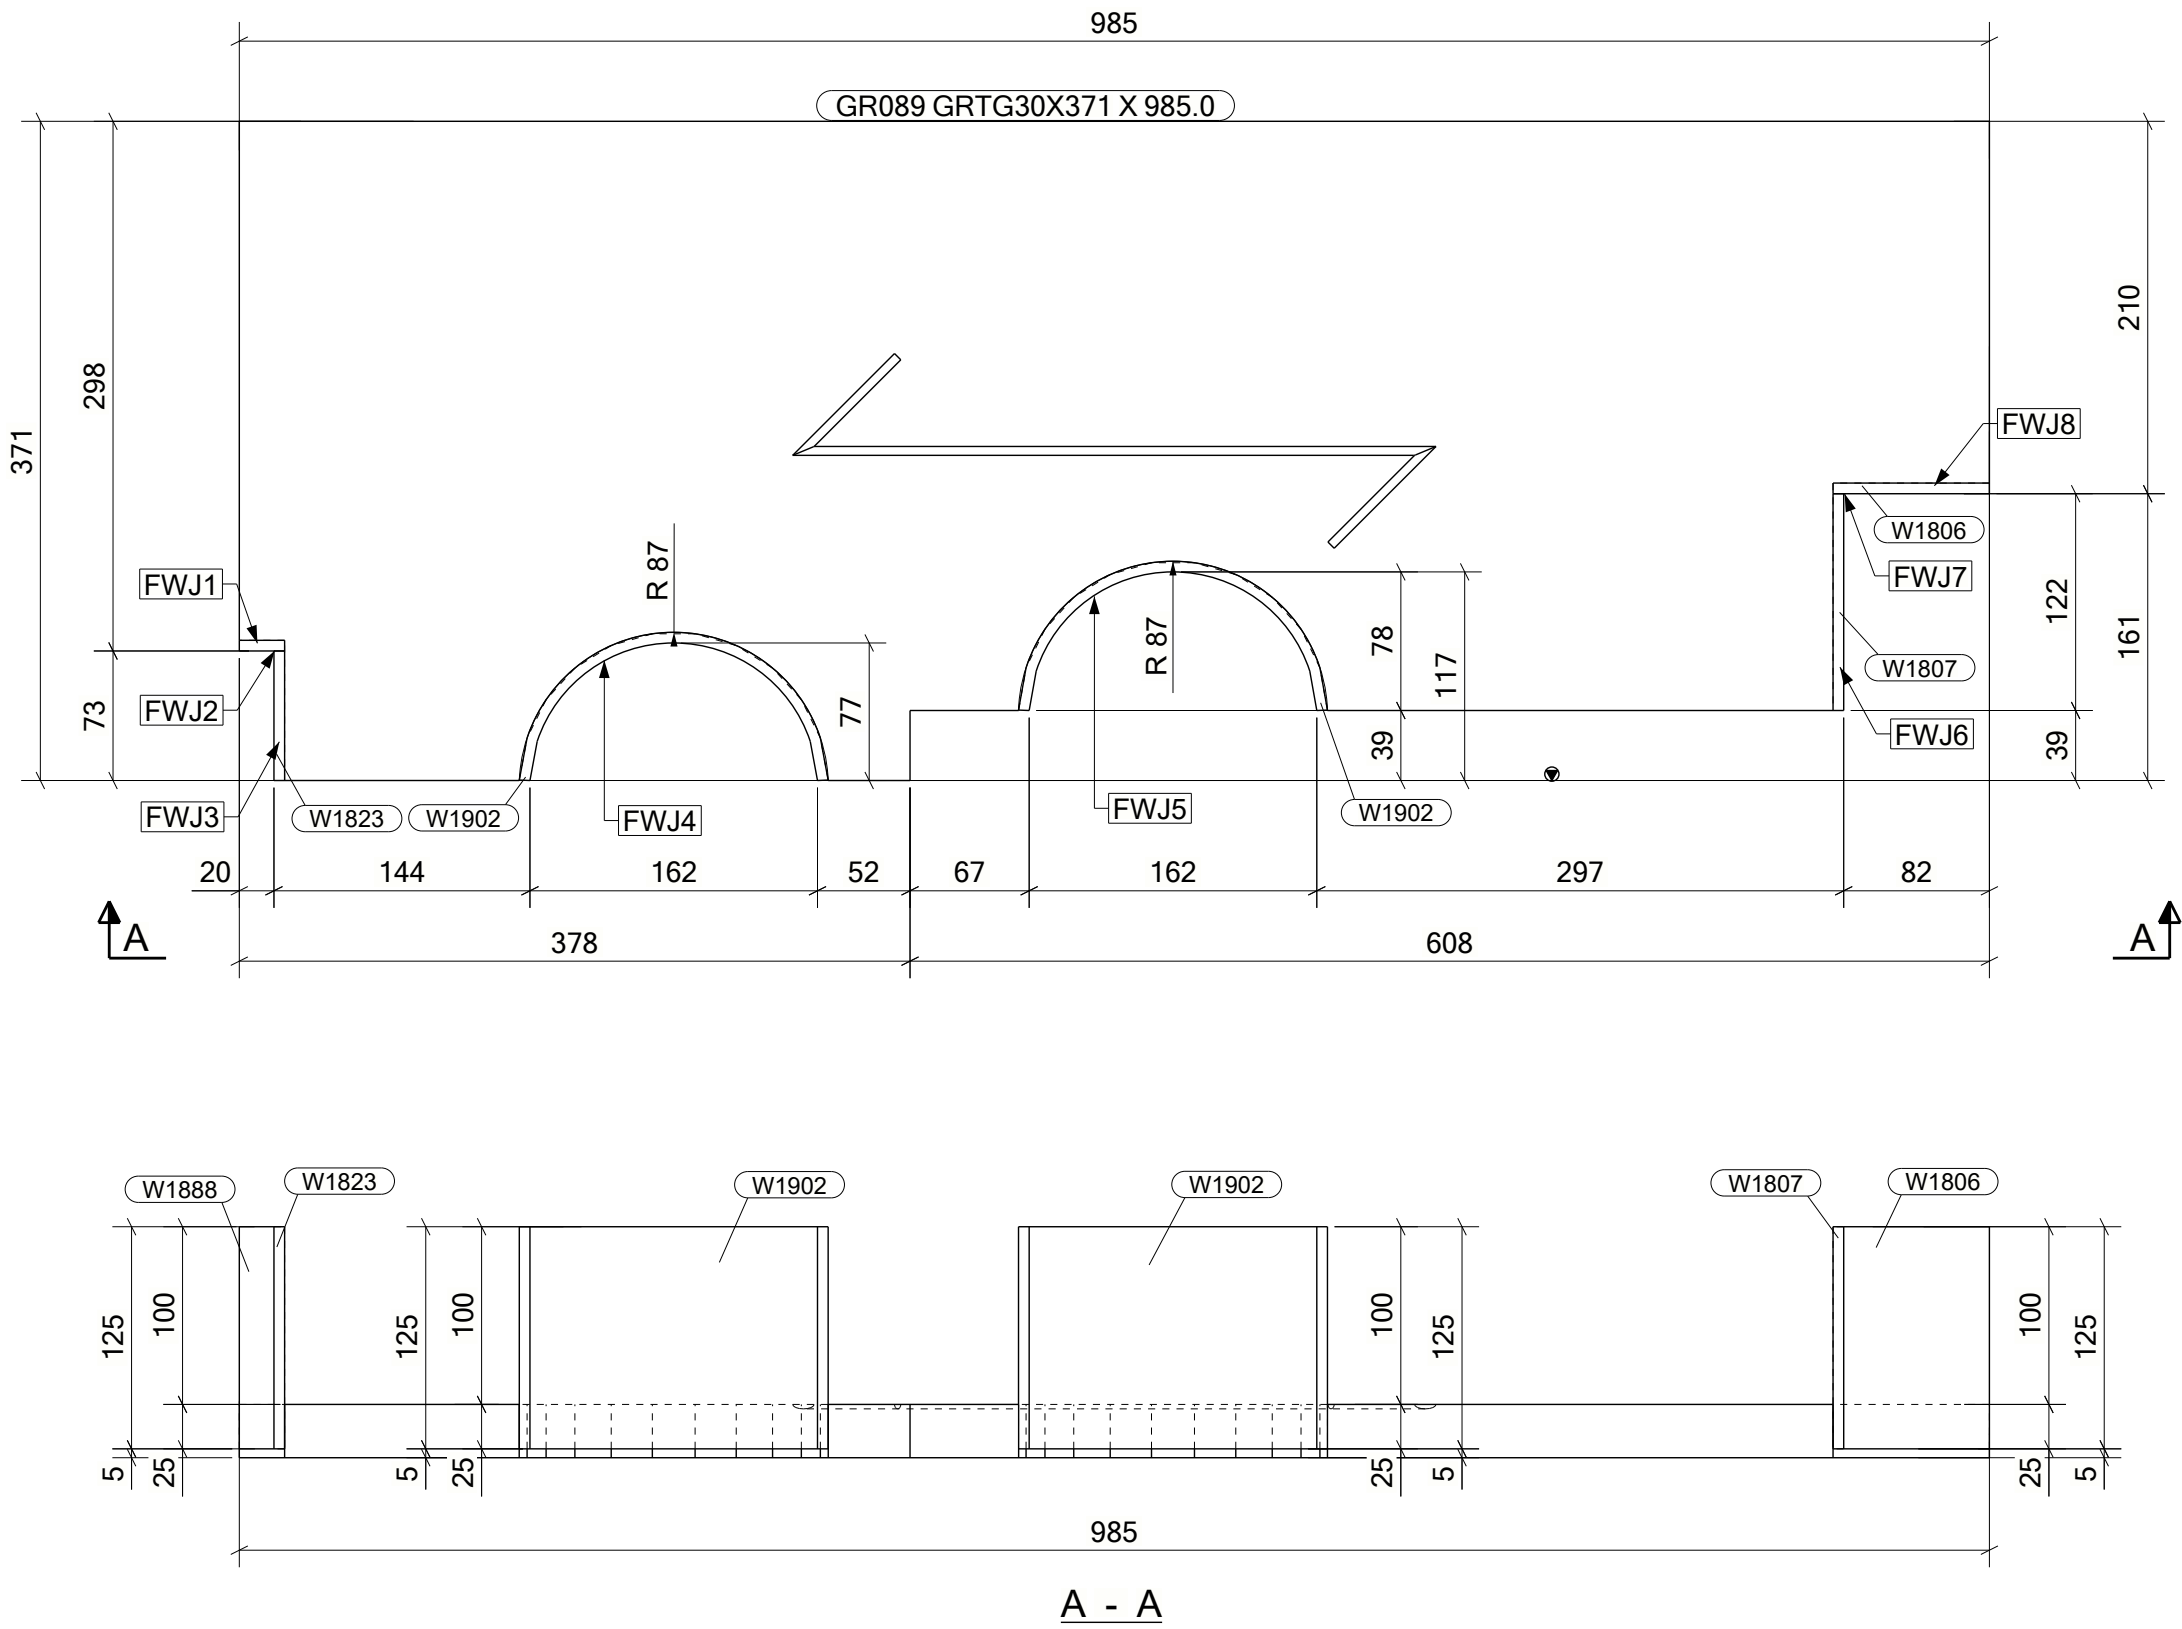

DRAWING NO. : 2307033-732-PR-10-GR089								REV.: 00			
ERECTION MARK : 2307033-732-PR-10-GR089			DESCRIPTION : GRATING				COLOR CODE :		QTY : 1		NOS
HOLD:		TYPE: W	TREAT: GN		COST CODE: 5.01			REMARKS:			
LENGTH: 985		WIDTH: 130		HEIGHT: 371		TOTAL S.AREA: 0.9			(M2)		
POSITION NO.	QTY PER ASSLY	SECTION	LENGTH	UNIT WEIGHT (KG)	TOTAL WIEGHT (KG)		GRADE	REVISION	PART ID	TREATMENT	REMARKS
					QTY	WEIGHT					
GR089	1	GRTG30X371	985	0.000	1	0.00	A1011M		MM	GN	
W1806	1	FLT125X6	88	0.518	1	0.52	S275JR		WI		
W1807	1	FLT125X6	122	0.718	1	0.72	S275JR		WI		
W1823	1	FLT125X6	73	0.429	1	0.43	S275JR		WI		
W1888	1	FLT125X6	26	0.150	1	0.15	S275JR		WI		
W1902	2	FLT125X6	249	1.497	2	2.99	S275JR		WI		
					UNIT WEIGHT	4.80					
					TOTAL WEIGHT	4.80					
BOLT LIST:-											
BOLT \ STUD BOLT DESCRIPTION											

ANCILLARY CATEGORY

FW- J1 TO J8

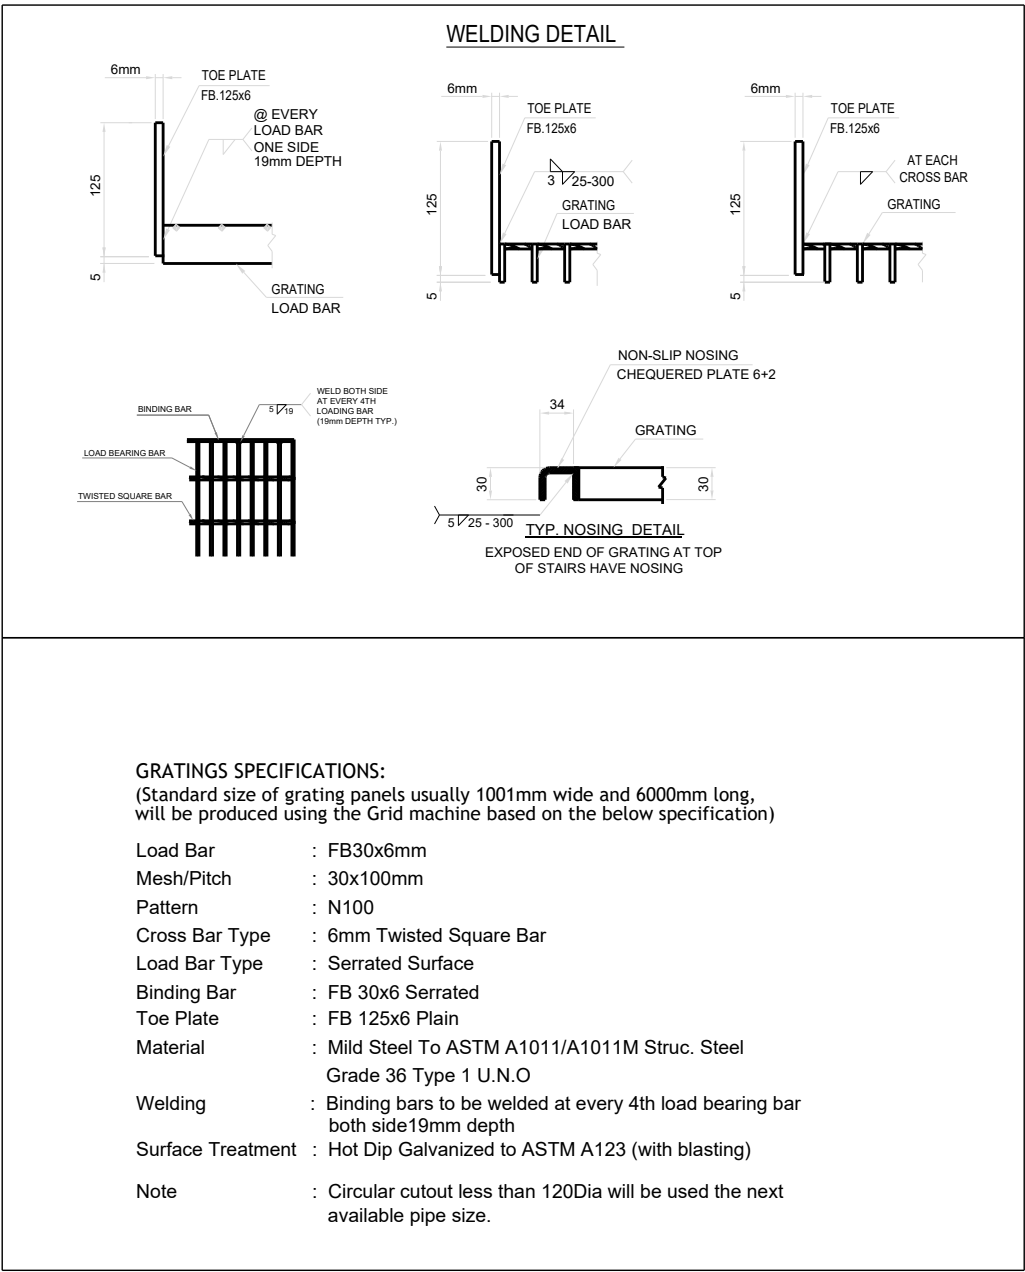

GA & IFC DRAWINGS REFERENCE	REV.
AD282-732-C-33158-61	6
AD282-732-C-33170-73.33539	6
AD282-732-C-34311	2
AD282-732-C-34274	2





- NOTES :**
- 1-ALL DIMENSIONS ARE GIVEN IN MILLIMETERS (U.N.O.).
 - 2-  DENOTES ASSEMBLY ORIENTATION MARK.
 - 3-DON'T SCALE THE DRAWING. FOLLOW THE WRITTEN DIMENSIONS.
 - 4- FINISH AS PER PROJECT SPEC.
 - 5- STRUCTURAL STEELWORK SHALL BE IN ACCORDANCE WITH PROJECT SPECIFICATIONS AD282-732-G-03520 & AD282-732-G-03527
 - 6-WHEREVER THERE IS NO ACCESS FOR FILLET WELDING TO BE REPLACED BY FULL PENETRATION BUTT WELDING
 - 7-FOR CJP WELD MARKED LOCATIONS FOLLOW THIS DETAIL
-  8-ALL WELDS TO BE 6mm FILLET WELD U.N.O.

GRID LOCATION	
EL +104.282	<732-09/<732-8

DRAWING NO. : 2307059-732-V-132-HR003										REV.: 00			
ERECTION MARK : 2307059-732-V-132-HR003				DESCRIPTION : HANDRAIL			COLOR CODE : 10 B 15			QTY : 1		NOS	
HOLD:		TYPE: W		TREAT: GPN		COST CODE: 3.01			REMARKS:				
LENGTH: 3059		WIDTH: 1384		HEIGHT: 1080		TOTAL S.AREA: 1.7 (M2)							
POSITION NO.	QTY PER ASSLY	SECTION	LENGTH	UNIT WEIGHT (KG)	TOTAL WIEGHT (KG)		GRADE	REVISION	PART ID	TREATMENT	REMARKS		
					QTY	WEIGHT							
HR003	1	CHS48.3X3.68	3308	13.234	1	13.23	A53-GR.B	1	MM	GPN	ROLLING		
W023	2	CHS48.3X3.68	361	1.454	2	2.91	A53-GR.B	1	WI				
W029	4	CHS48.3X3.68	127	0.357	4	1.43	A53-GR.B	1	WI		ELBOW		
W067	1	CHS48.3X3.68	1049	4.162	1	4.16	A53-GR.B	1	WI				
W068	1	CHS48.3X3.68	1050	4.162	1	4.16	A53-GR.B	1	WI				
W077	1	CHS48.3X3.68	1050	4.162	1	4.16	A53-GR.B	1	WI				
W112	3	PL6X44	44	0.072	3	0.22	S355JR	1	WI				
W113	3	PL10X110	150	1.295	3	3.89	S355JR	1	WI				
W205	1	CHS48.3X3.68	496	1.916	1	1.92	A53-GR.B	1	WI		ROLLING		
W206	1	CHS48.3X3.68	1157	4.492	1	4.49	A53-GR.B	1	WI		ROLLING		
W207	1	CHS48.3X3.68	1156	4.492	1	4.49	A53-GR.B	1	WI		ROLLING		
W208	1	CHS48.3X3.68	496	1.916	1	1.92	A53-GR.B	1	WI		ROLLING		
					UNIT WEIGHT		46.97						
					TOTAL WEIGHT		46.97						
BOLT LIST:-													
BOLT \ STUD		BOLT DESCRIPTION		QTY/ONE		QTY/ALL		FINISH		REMARKS			
BOLT		B1N1W16 × 50 A307		4		12							





ANCILLARY CATEGORY

FW-J1 TO J15
CJP-J1 TO J8

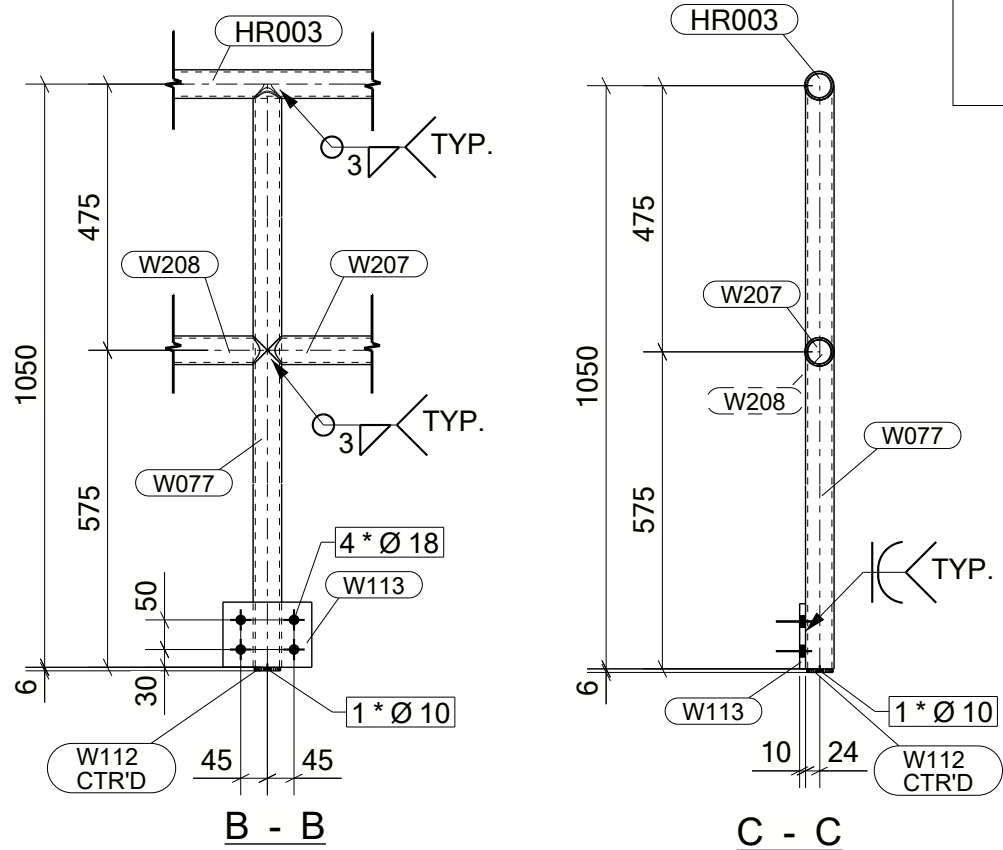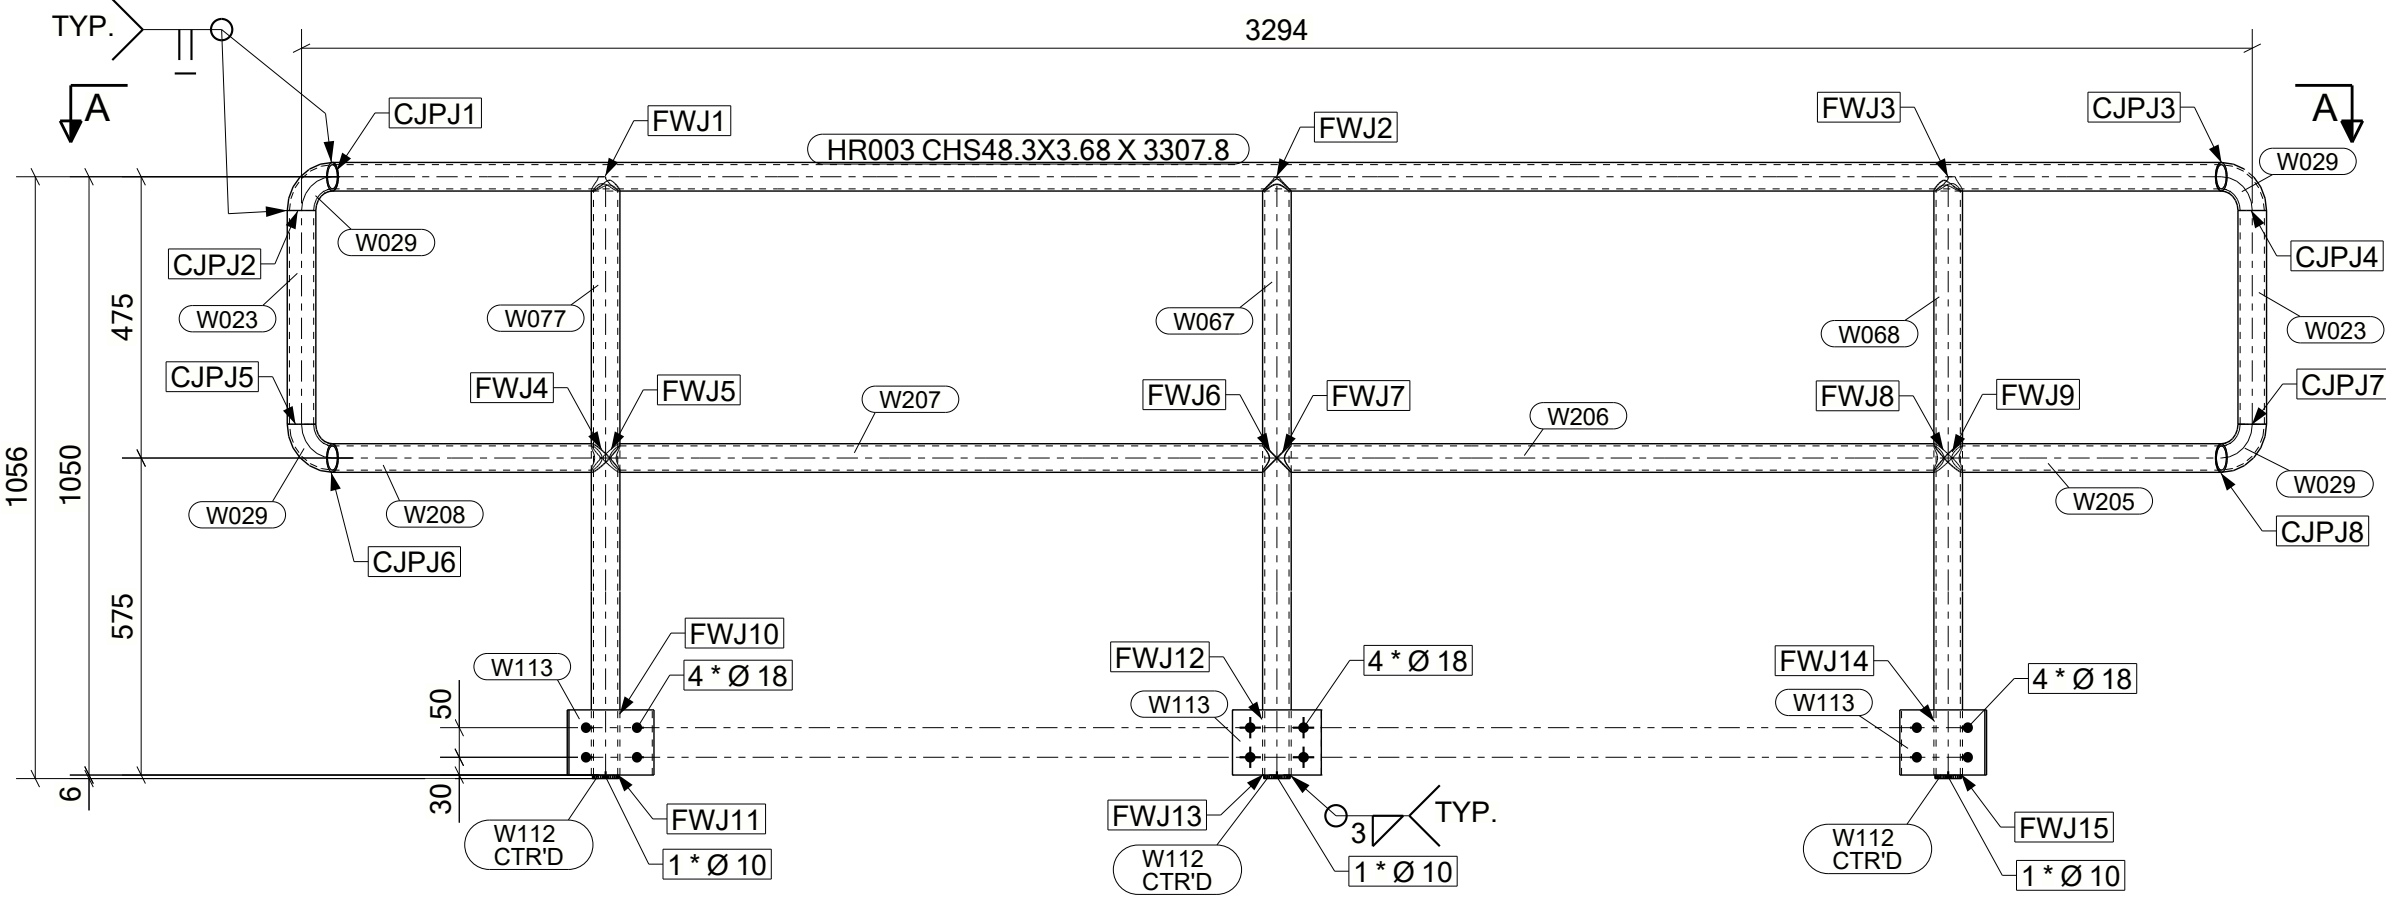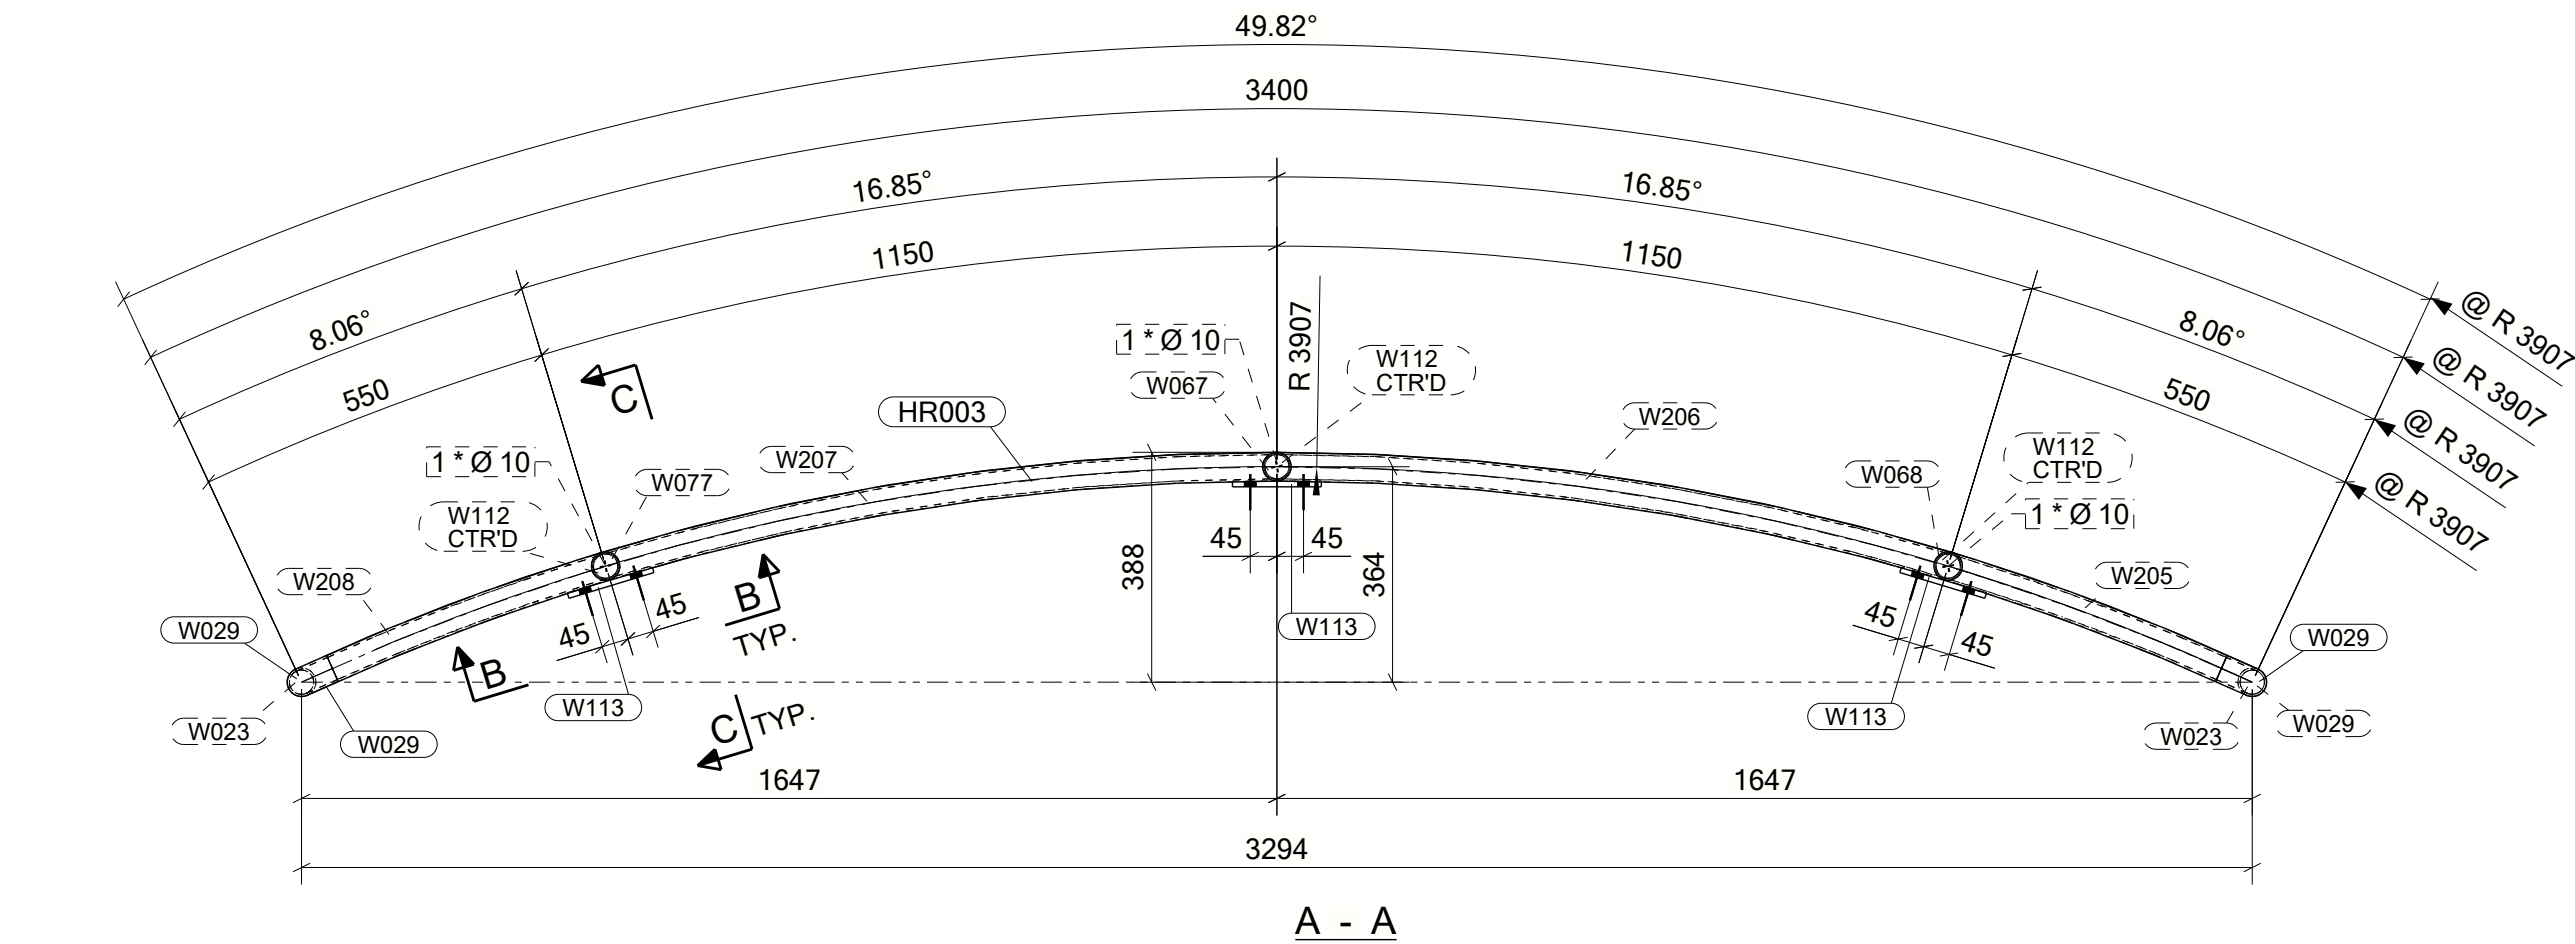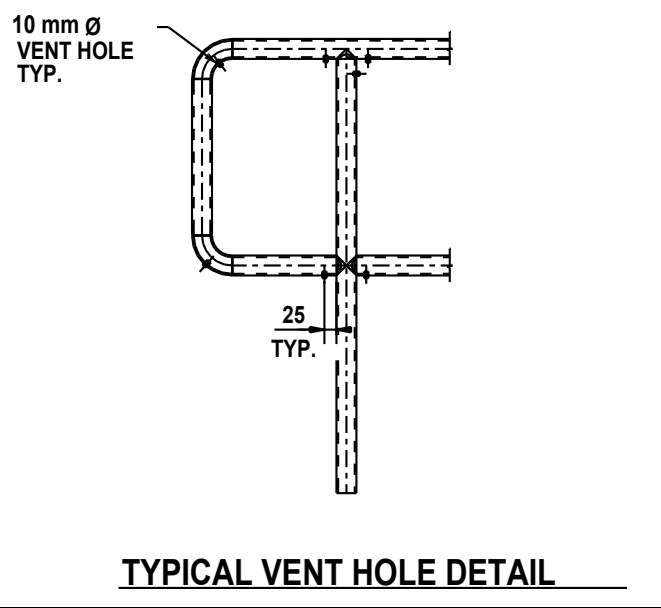

GA & IFC DRAWINGS REFERENCE	REV.
AD282-732-C-33288,299 & 300	3
AD282-732-C-34324	1
AD282-732-C-34287	1

- NOTES :
- 1-ALL DIMENSIONS ARE GIVEN IN MILLIMETERS (U.N.O.).
 - 2- DENOTES ASSEMBLY ORIENTATION MARK.
 - 3-DON'T SCALE THE DRAWING. FOLLOW THE WRITTEN DIMENSIONS.
 - 4- FINISH AS PER PROJECT SPEC.
 - 5- STRUCTURAL STEELWORK SHALL BE IN ACCORDANCE WITH PROJECT SPECIFICATIONS AD282-732-G-03520 & AD282-732-G-03527
 - 6-WHEREVER THERE IS NO ACCESS FOR FILLET WELDING TO BE REPLACED BY FULL PENETRATION BUTT WELDING
 - 7-FOR CJP WELD MARKED LOCATIONS FOLLOW THIS DETAIL
 - 8-ALL WELDS TO BE 6mm FILLET WELD U.N.O.

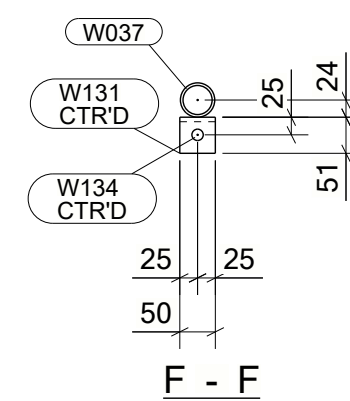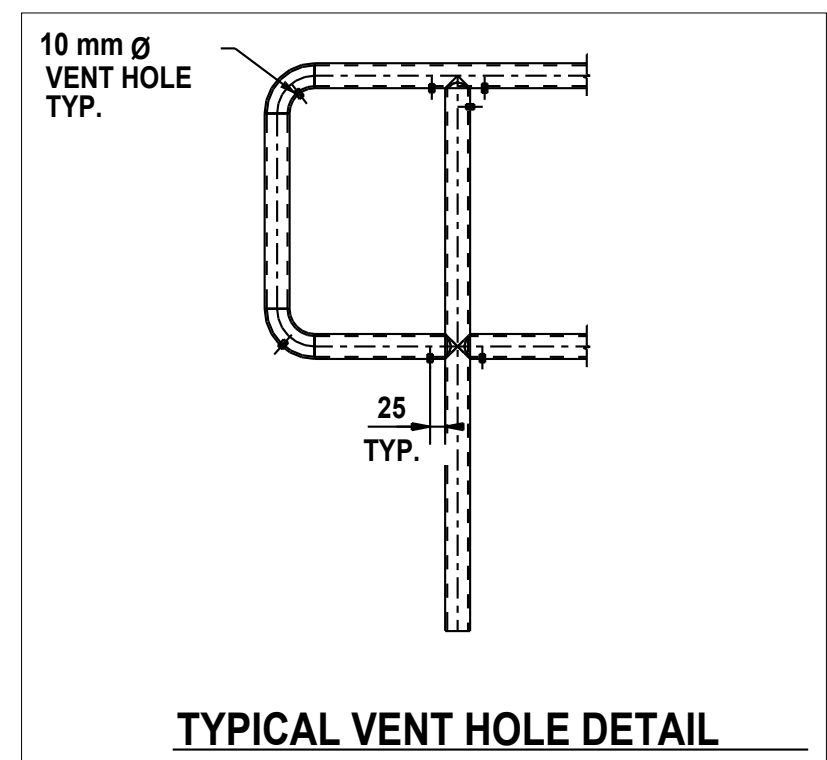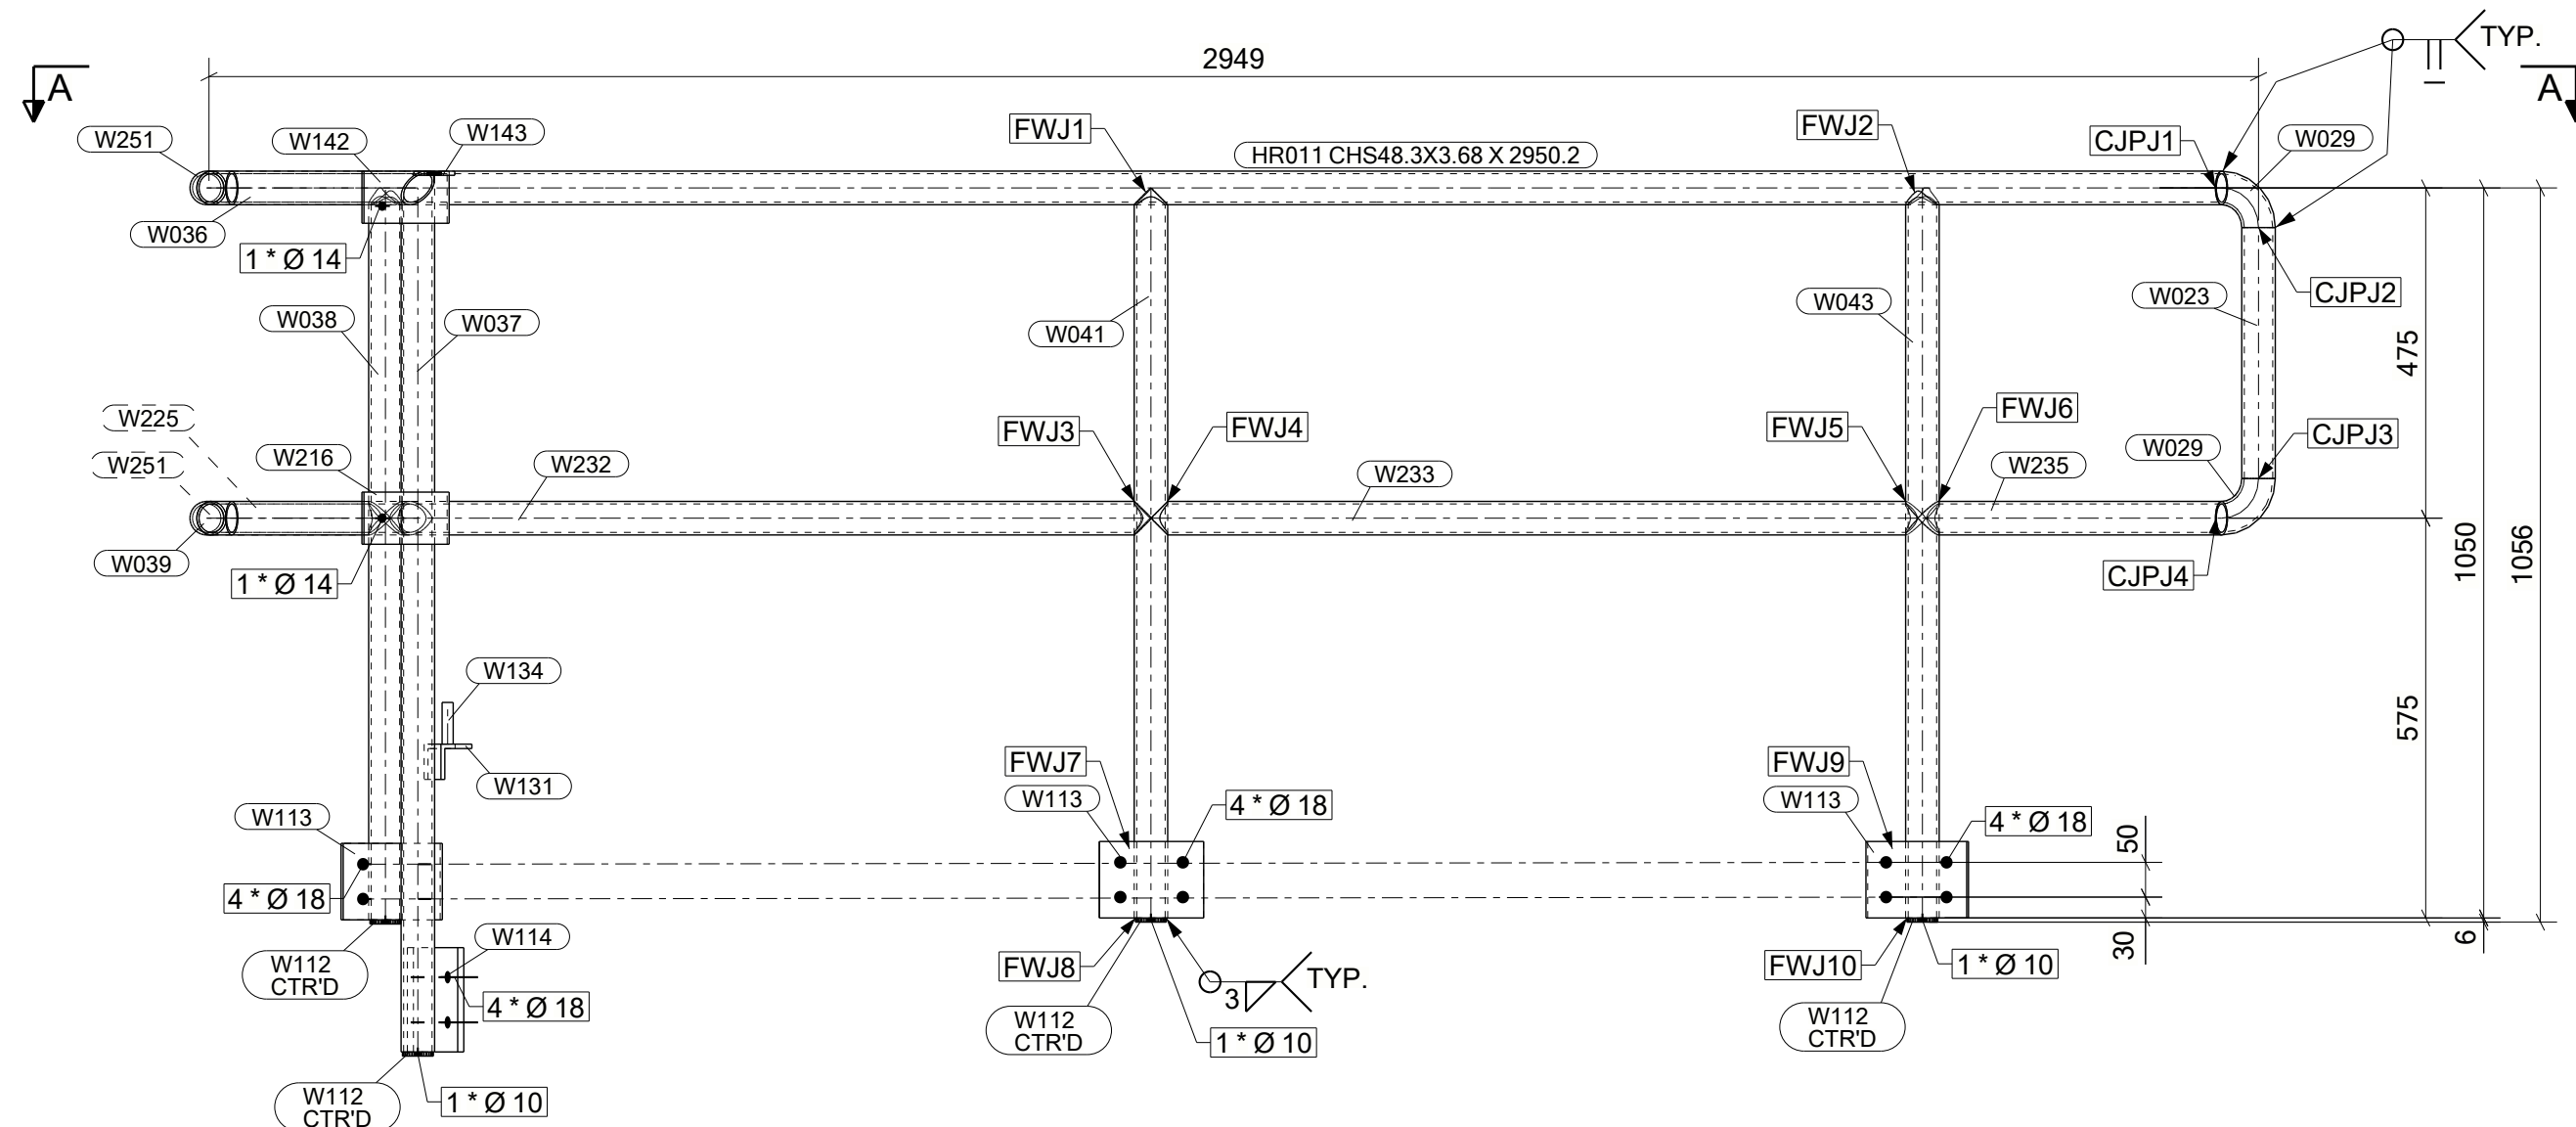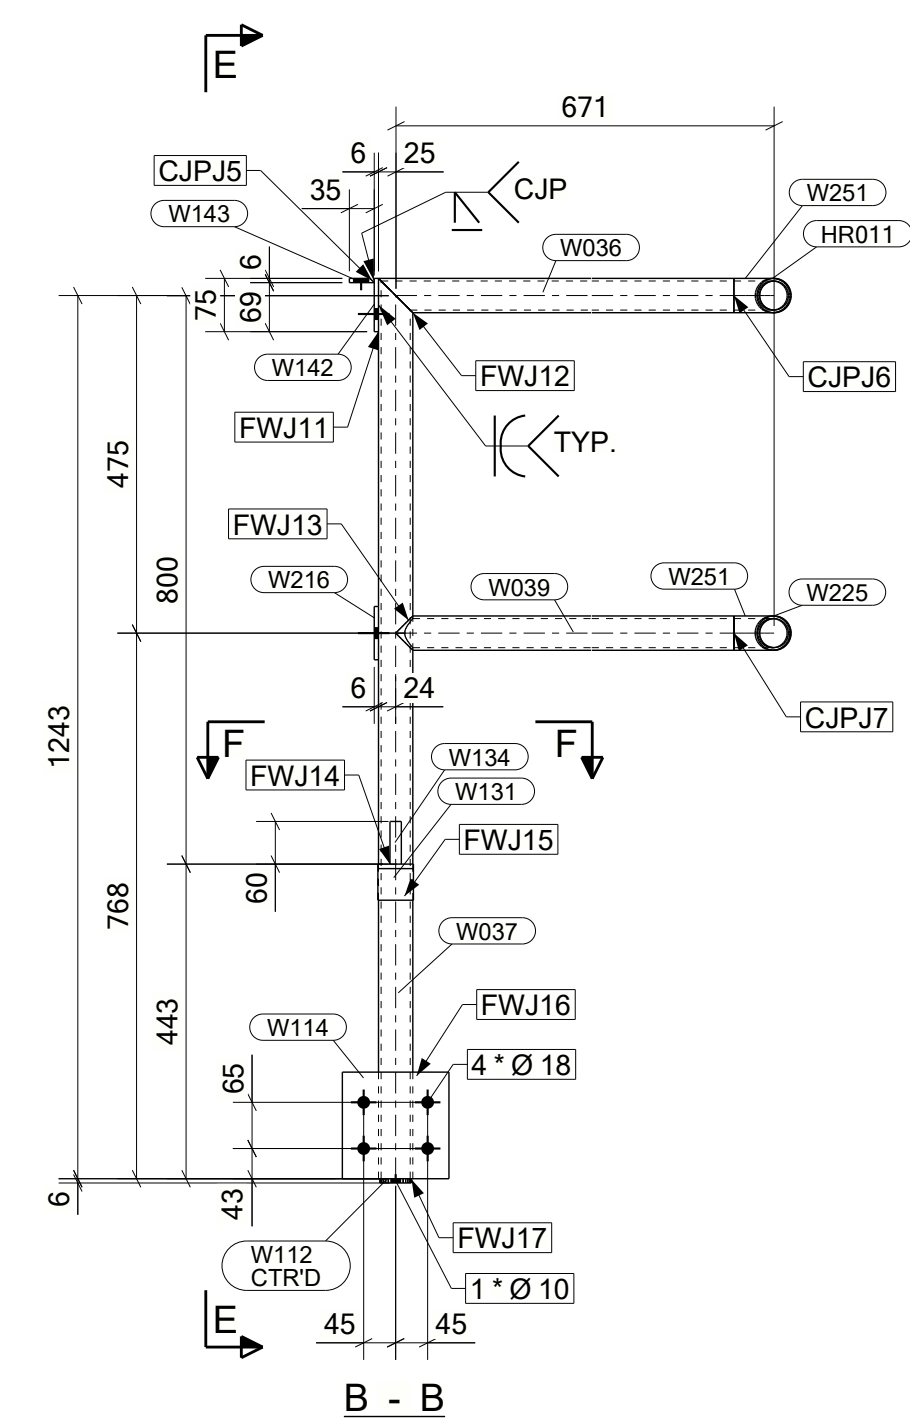

ANCILLARY CATEGORY
FW- J1 TO J22
CJP-J1 TO J9


NOTES :

- 1- ALL DIMENSIONS ARE GIVEN IN MILLIMETERS (U.N.O.).
- 2-  DENOTES ASSEMBLY ORIENTATION MARK.
- 3- DON'T SCALE THE DRAWING. FOLLOW THE WRITTEN DIMENSIONS.
- 4- FINISH AS PER PROJECT SPEC.
- 5- STRUCTURAL STEELWORK SHALL BE IN ACCORDANCE WITH PROJECT SPECIFICATIONS AD282-732-G-03520 & AD282-732-G-03527
- 6-WHEREVER THERE IS NO ACCESS FOR FILLET WELDING TO BE REPLACED BY FULL PENETRATION BUTT WELDING
- 7-FOR CIP WELD MARKED LOCATIONS FOLLOW THIS DETAIL



- 8- ALL WELDS TO BE 6mm FILLET WELD U.N.O.

GRID LOCATION		
EL +104.084	1/E-G	
EL +104.084	2-1/E-G	


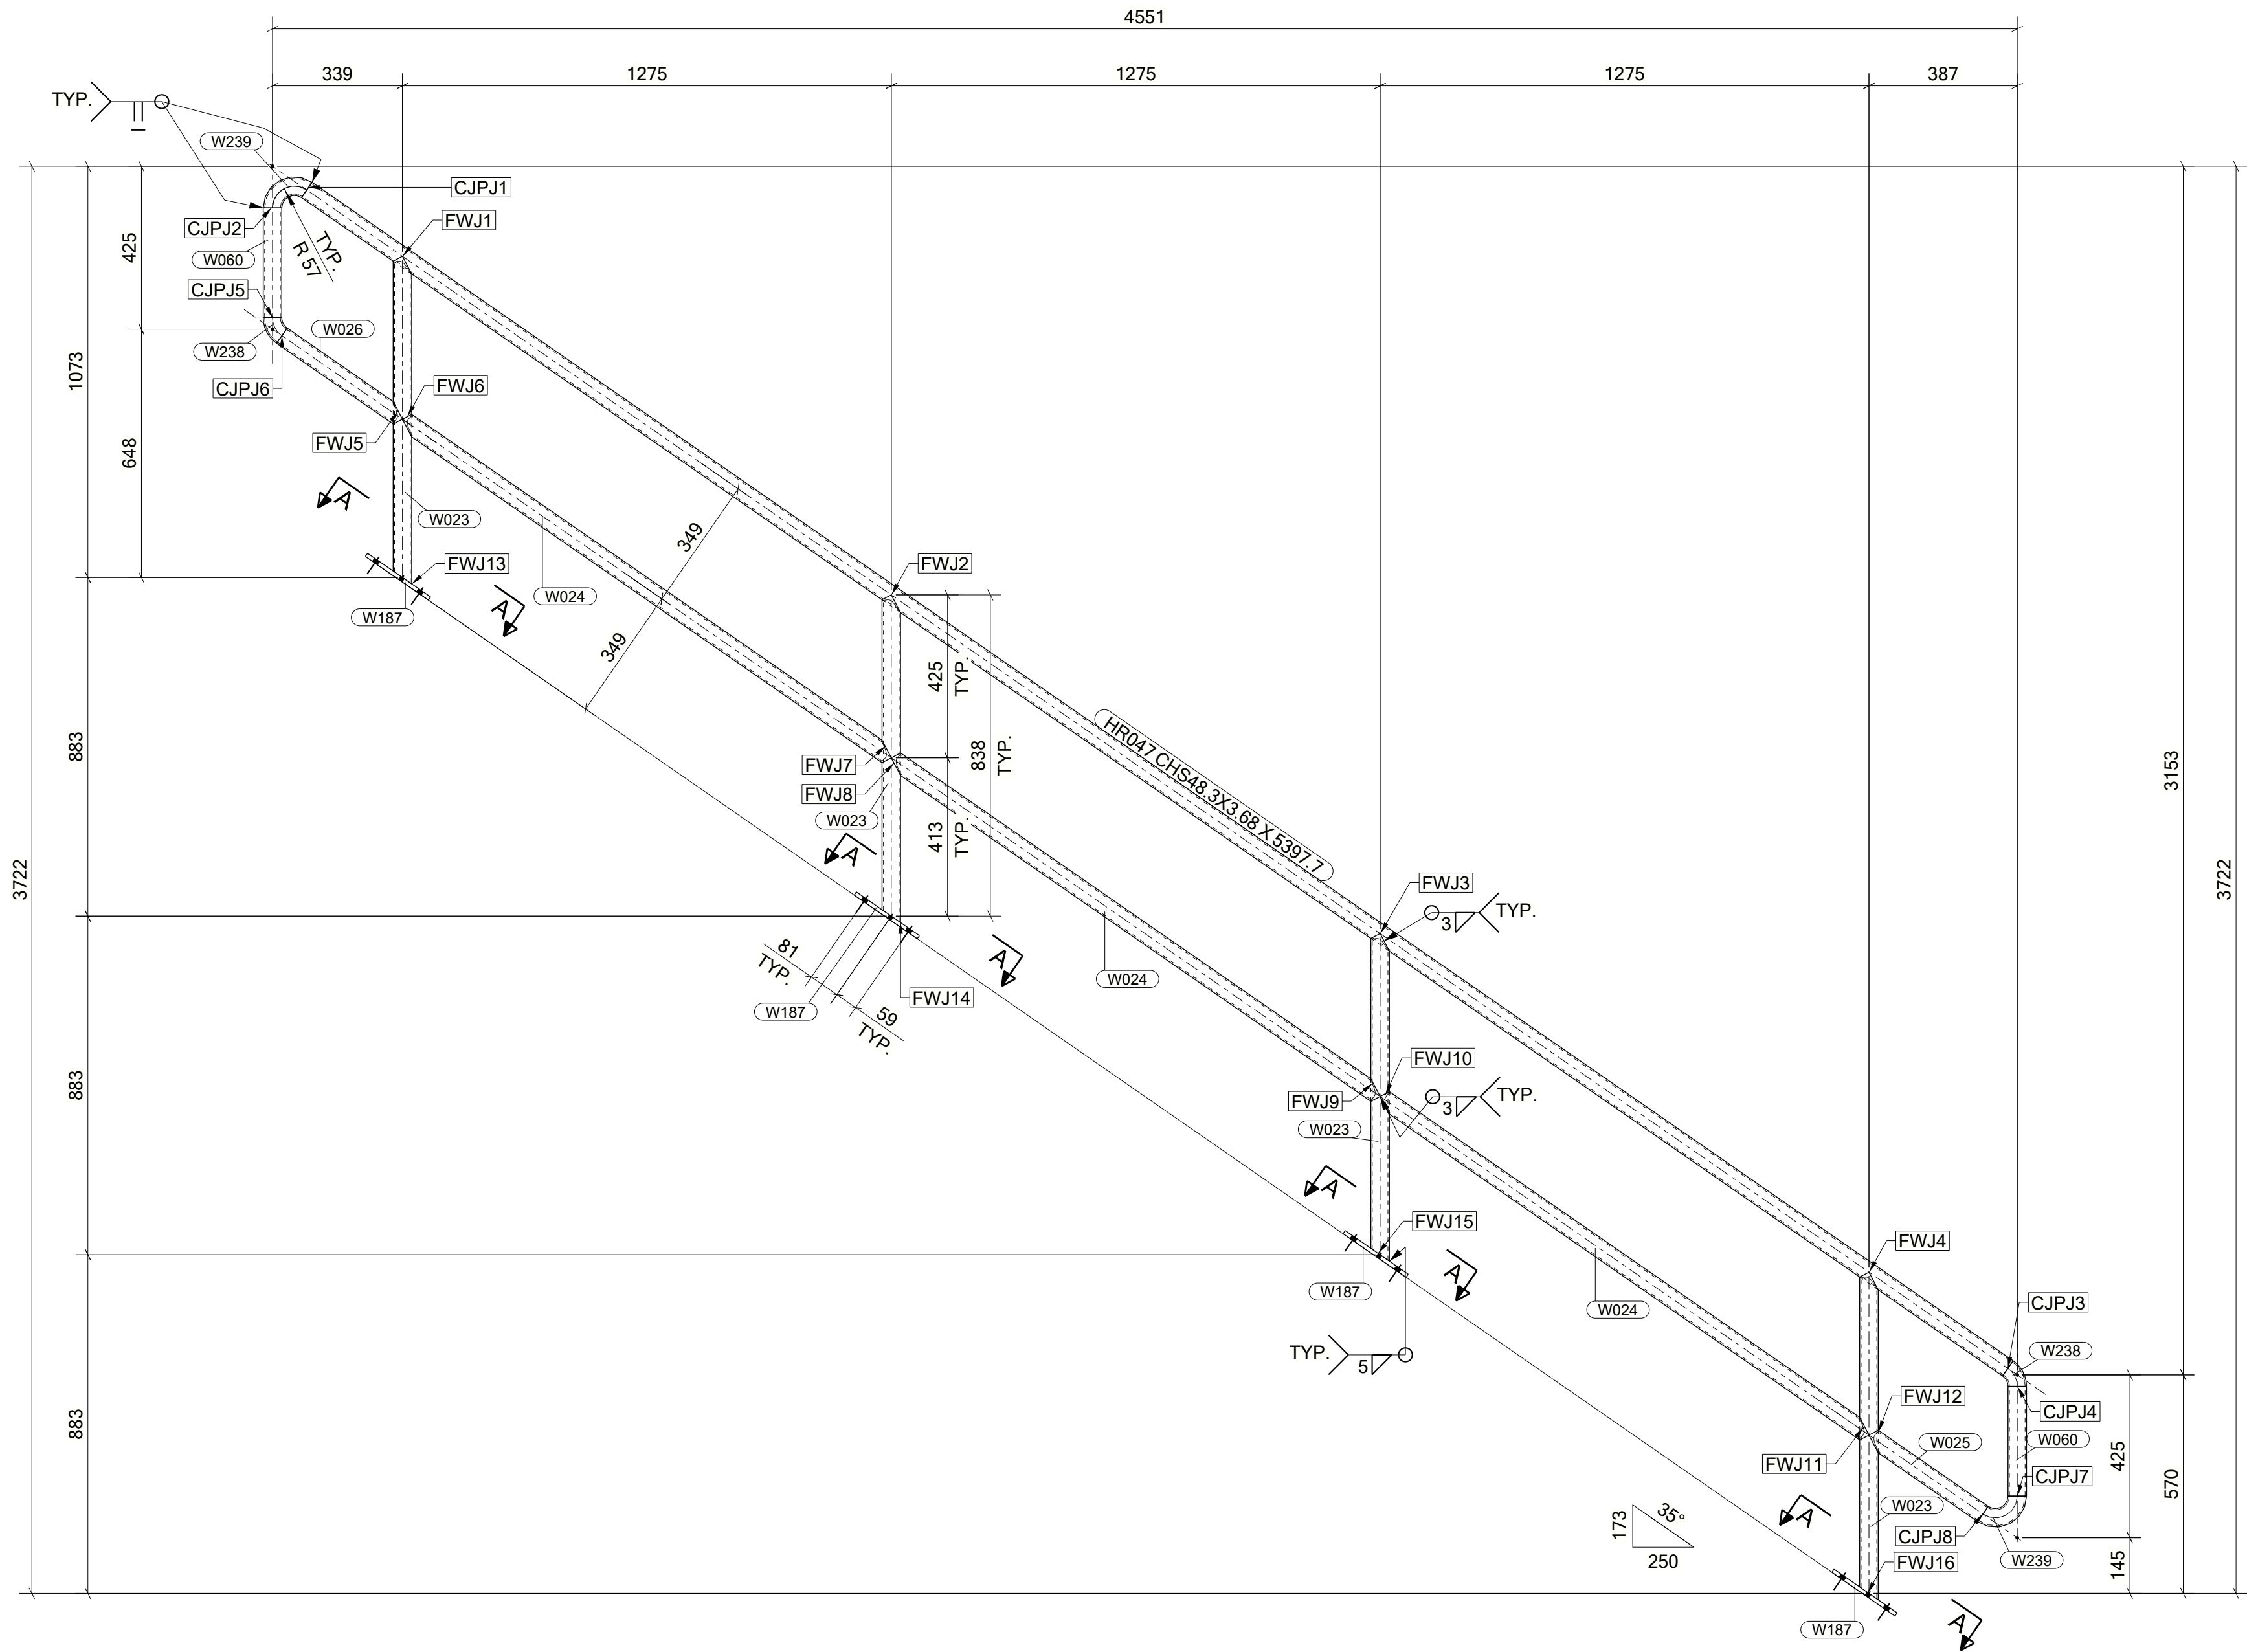


DRAWING NO. : 2307087-STL-732-02-HR047										REV.: 00							
ERECTION MARK : 2307087-STL-732-02-HR047										DESCRIPTION : HANDRAIL		COLOR CODE : 10 B 15		QTY : 2		NOS	
HOLD:		TYPE: W		TREAT: GPN		COST CODE: 3.01				REMARKS:							
LENGTH: 5722		WIDTH: 723		HEIGHT: 60		TOTAL S-AREA: 2.4				(M2)							
POSITION NO.	QTY PER ASSLY	SECTION	LENGTH	UNIT WEIGHT (KG)	TOTAL WIEGHT (KG)		GRADE	REVISION	PART ID	TREATMENT	REMARKS						
					QTY	WEIGHT											
HR047	1	CHS48.3X3.68	5398	21.747	2	43.49	A53-GR.B	1	MM	GPN							
W023	4	CHS48.3X3.68	855	3.291	8	26.32	A53-GR.B	1	WI								
W024	3	CHS48.3X3.68	1551	6.079	6	36.48	A53-GR.B	1	WI								
W025	1	CHS48.3X3.68	362	1.373	2	2.75	A53-GR.B	1	WI								
W026	1	CHS48.3X3.68	382	1.456	2	2.91	A53-GR.B	1	WI								
W060	2	CHS48.3X3.68	286	1.154	4	4.61	A53-GR.B	1	WI								
W187	4	PL10X60	200	0.942	8	7.54	S355JR	1	WI								
W238	2	CHS48.3X3.68	78	0.221	4	0.88	A53-GR.B	1	WI		ELBOW						
W239	2	CHS48.3X3.68	177	0.489	4	1.96	A53-GR.B	1	WI		ELBOW						
					UNIT WEIGHT												
					TOTAL WEIGHT												
					63.47												
					126.94												
BOLT LIST:-																	
BOLT \ STUD		BOLT DESCRIPTION		QTY/ONE		QTY/ALL		FINISH		REMARKS							
BOLT		B1N2W12 × 45 A307		4		8											

ANCILLARY CATEGORY


FW- J1 TO J16

CJP- J1 TO J8

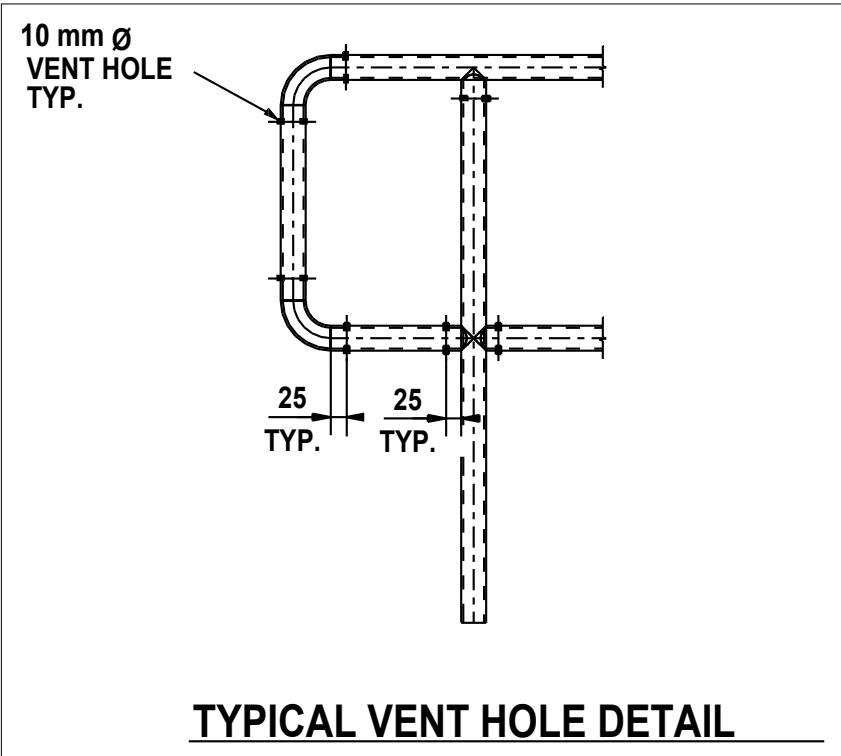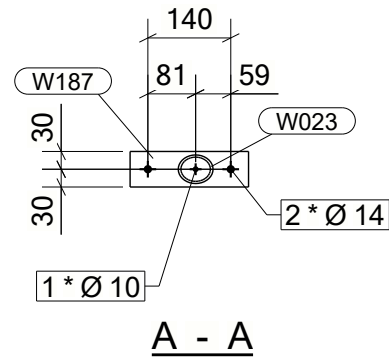

GA & IFC DRAWINGS REFERENCE	REV.
AD282-732-C-33226,27,28,29,30,31	4
AD282-732-C-33233,34,35,33499,33500	4
AD282-732-C-34337	2
AD282-732-C-34300	2

- NOTES :
- 1-ALL DIMENSIONS ARE GIVEN IN MILLIMETERS (U.N.O.).
 - 2- DENOTES ASSEMBLY ORIENTATION MARK.
 - 3-DON'T SCALE THE DRAWING. FOLLOW THE WRITTEN DIMENSIONS.
 - 4- FINISH AS PER PROJECT SPEC.
 - 5- STRUCTURAL STEELWORK SHALL BE IN ACCORDANCE WITH PROJECT SPECIFICATIONS AD282-732-G-03520 & AD282-732-G-03527
 - 6-WHEREVER THERE IS NO ACCESS FOR FILLET WELDING TO BE REPLACED BY FULL PENETRATION BUTT WELDING
 - 7-FOR CJP WELD MARKED LOCATIONS FOLLOW THIS DETAIL
 - 8-ALL WELDS TO BE 6mm FILLET WELD U.N.O.

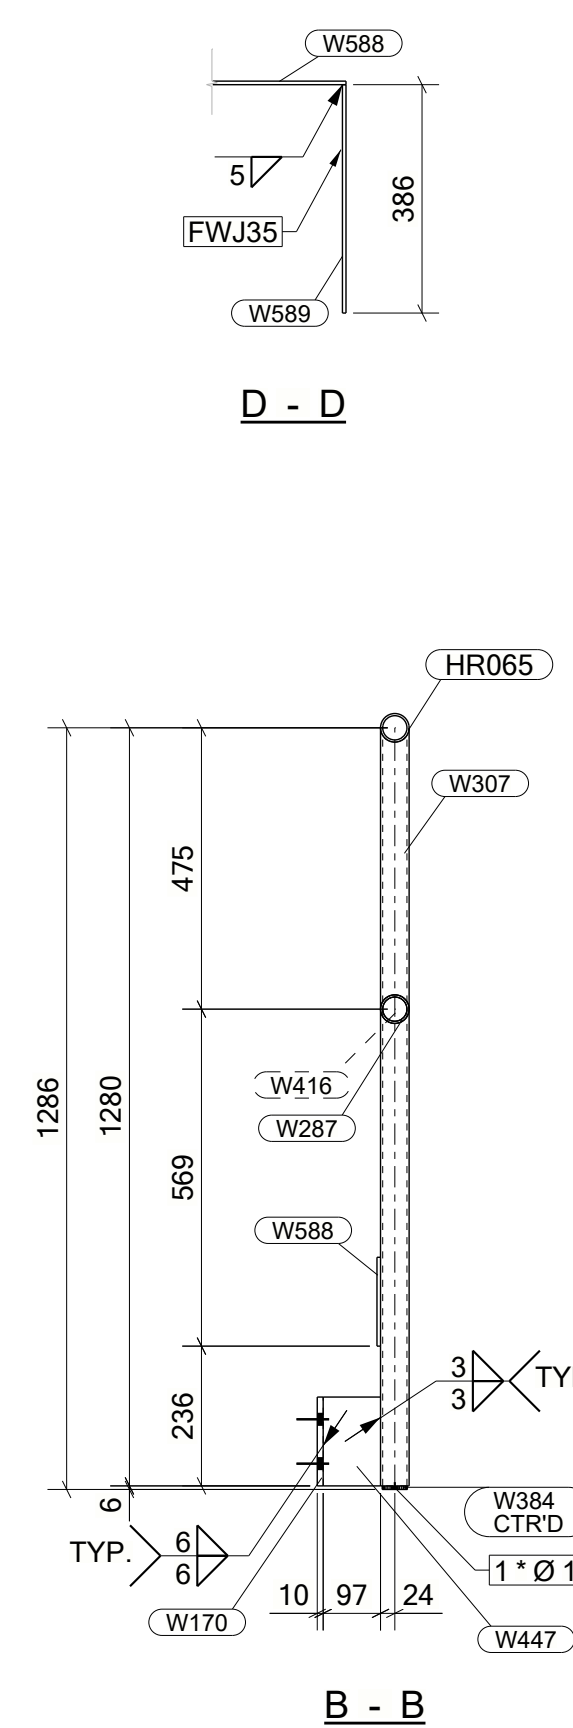

ANCILLARY CATEGORY
FW- J1 TO J35
CJP- J1 TO J6

NOTES :

- 1-ALL DIMENSIONS ARE GIVEN IN MILLIMETERS (U.N.O.).
- 2-  DENOTES ASSEMBLY ORIENTATION MARK.
- 3-DON'T SCALE THE DRAWING. FOLLOW THE WRITTEN DIMENSIONS.
- 4-FINISH AS PER PROJECT SPEC.
- 5- STRUCTURAL STEELWORK SHALL BE IN ACCORDANCE WITH PROJECT SPECIFICATIONS AD282-732-G-03520 & AD282-732-G-03527
- 6-WHEREVER THERE IS NO ACCESS FOR FILLET WELDING TO BE REPLACED BY FULL PENETRATION BUTT WELDING
- 7-FOR CIP WELD MARKED LOCATIONS FOLLOW THIS DETAIL





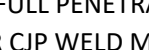


Diagram showing a fillet weld joint with dimensions: 6mm, 45°, and 45°.

- 8-ALL WELDS TO BE 6mm FILLET WELD U.N.O.

GRID LOCATION	
EL +110.054	1/E-F

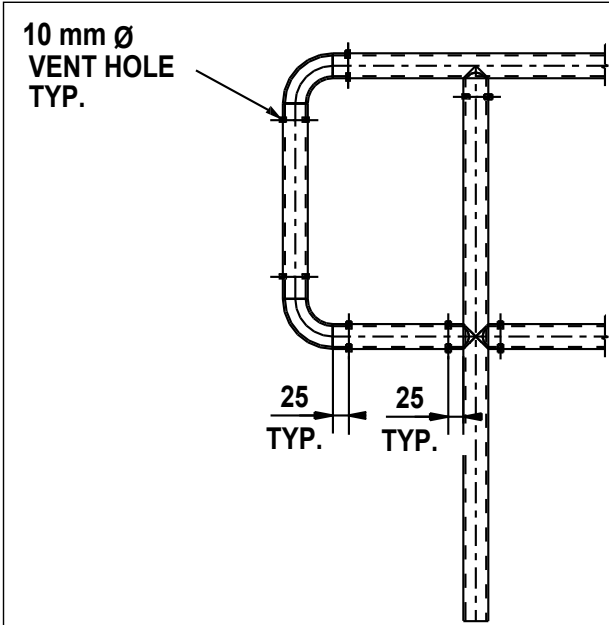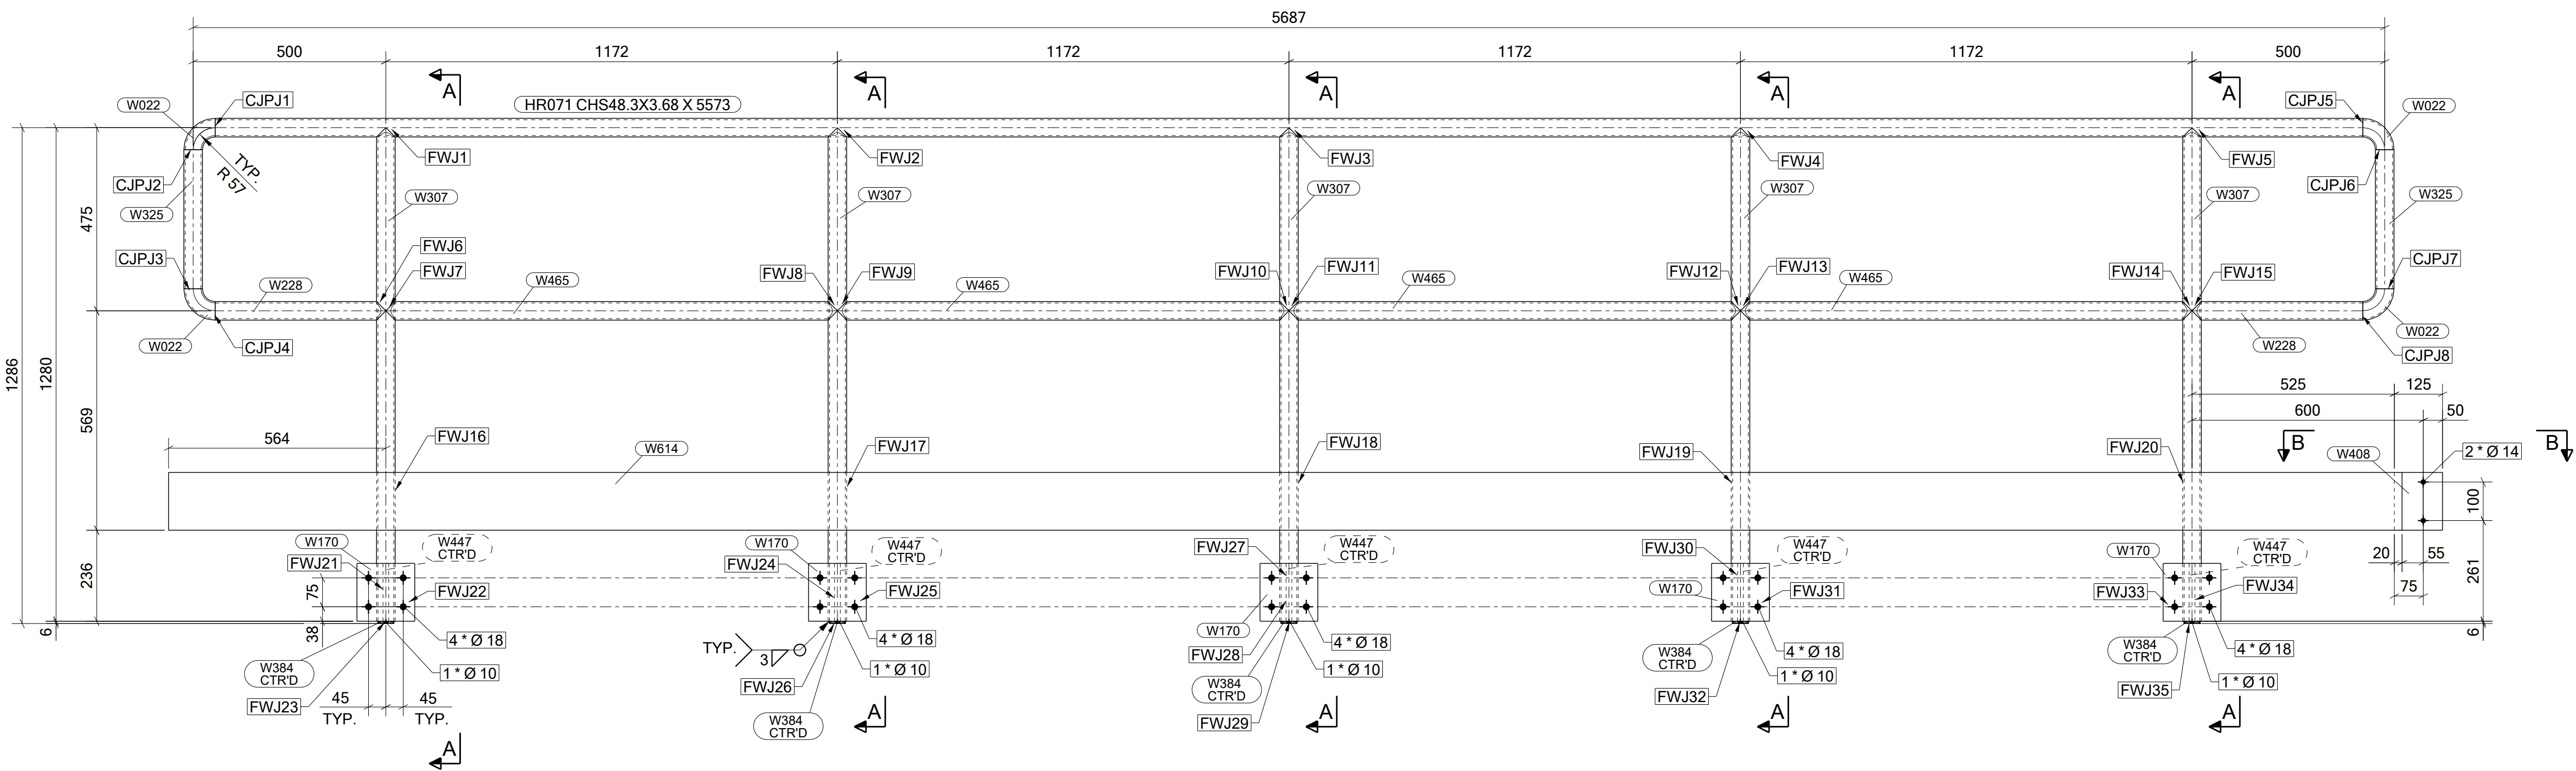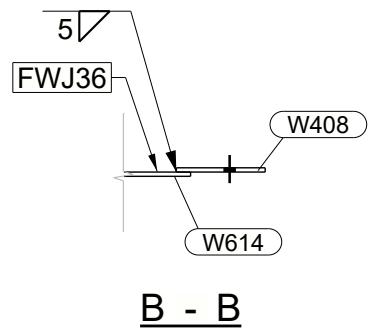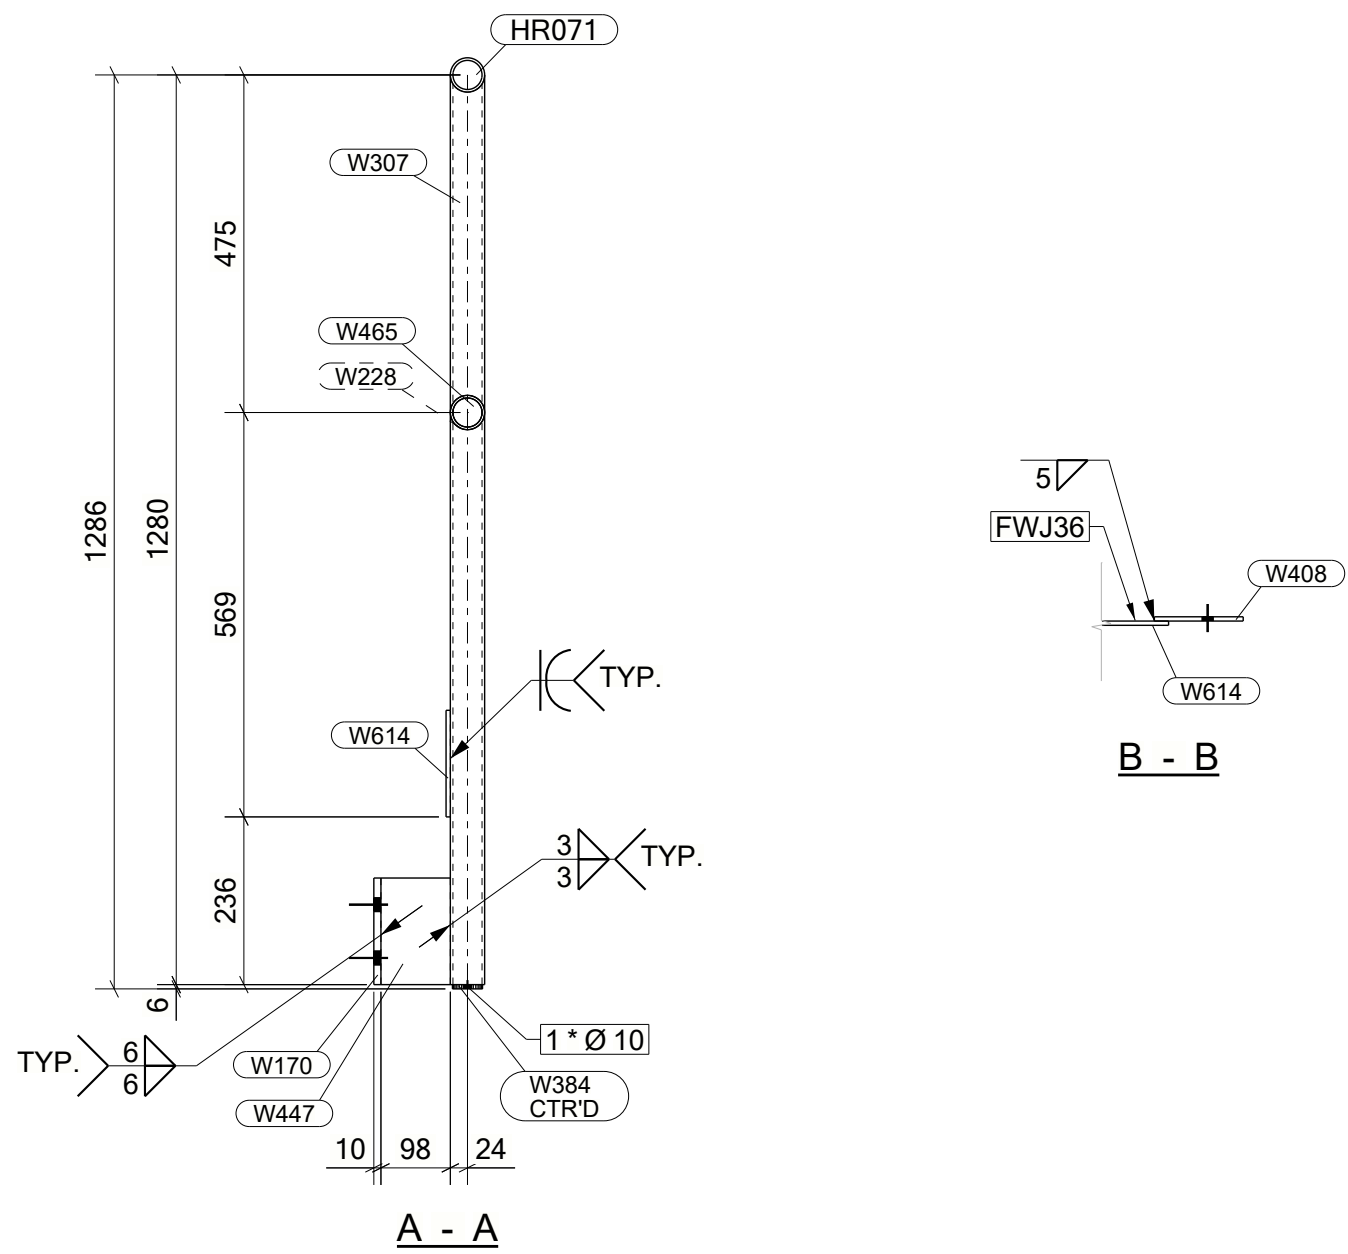

TYPICAL VENT HOLE DETAIL


DRAWING NO. : 2307087-STL-732-02-HR071										REV. : 00							
ERECTION MARK : 2307087-STL-732-02-HR071										DESCRIPTION : HANDRAIL		COLOR CODE : 10 B 15		QTY : 1		NOS	
HOLD: TYPE: W TREAT: GPN										COST CODE: 3.01		REMARKS:					
LENGTH: 5900		WIDTH: 1310		HEIGHT: 156		TOTAL S.AREA: 5.1 (M2)											
POSITION NO.	QTY PER ASSLY	SECTION	LENGTH	UNIT WEIGHT (KG)	TOTAL WIEGHT (KG)		GRADE	REVISION	PART ID	TREATMENT	REMARKS						
					QTY	WEIGHT											
HR071	1	CHS48.3X3.68	5573	22.451	1	22.45	A53-GR.B	1	MM	GPN							
W022	4	CHS48.3X3.68	127	0.357	4	1.43	A53-GR.B	1	WI		ELBOW						
W170	5	PL10X150	150	1.766	5	8.83	S355JR	1	WI								
W228	2	CHS48.3X3.68	443	1.715	2	3.43	A53-GR.B	1	WI								
W307	5	CHS48.3X3.68	1280	5.087	5	25.44	A53-GR.B	1	WI								
W325	2	CHS48.3X3.68	361	1.454	2	2.91	A53-GR.B	1	WI								
W384	5	PL6X42	42	0.066	5	0.33	S355JR	1	WI								
W408	1	PL6X125	150	0.883	1	0.88	S355JR	1	WI								
W447	5	PL15X150	98	1.724	5	8.62	S355JR	1	WI								
W465	4	CHS48.3X3.68	1172	4.581	4	18.32	A53-GR.B	1	WI								
W614	1	FLT6X150	5795	40.945	1	40.94	S275JR	1	WI								
					UNIT WEIGHT		133.58										
					TOTAL WEIGHT		133.58										
BOLT LIST:-																	
BOLT \ STUD		BOLT DESCRIPTION		QTY/ONE		QTY/ALL		FINISH		REMARKS							
BOLT		B1N1W16 × 45 A307		4		20											

ANCILLARY CATEGORY


FW- J1 TO J36
CJP- J1 TO J8

GA & IFC DRAWINGS REFERENCE	REV.
AD282-732-C-33226,27,28,29,30,31	4
AD282-732-C-33233,34,35,33499,33500	4
AD282-732-C-34337	2
AD282-732-C-34300	2



NOTES :

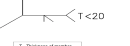- 1-ALL DIMENSIONS ARE GIVEN IN MILLIMETERS (U.N.O.).
- 2-  DENOTES ASSEMBLY ORIENTATION MARK.
- 3-DON'T SCALE THE DRAWING. FOLLOW THE WRITTEN DIMENSIONS.
- 4- FINISH AS PER PROJECT SPEC.
- 5- STRUCTURAL STEELWORK SHALL BE IN ACCORDANCE WITH PROJECT SPECIFICATIONS AD282-732-G-03520 & AD282-732-G-03527
- 6-WHEREVER THERE IS NO ACCESS FOR FILLET WELDING TO BE REPLACED BY FULL PENETRATION BUTT WELDING
- 7-FOR CIP WELD MARKED LOCATIONS FOLLOW THIS DETAIL 
- 8-ALL WELDS TO BE 6mm FILLET WELD U.N.O.

EL+107180
(T.O.S) ---
H

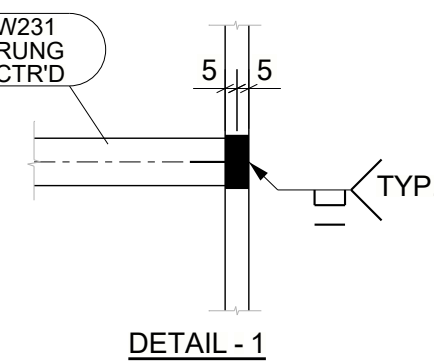

BOLT LIST:-						
BOLT \ STUD	BOLT DESCRIPTION		QTY/ONE	QTY/ALL	FINISH	REMARKS
BOLT	B1N1W12 × 30	A307	1	2		
BOLT	B1N1W16 × 45	A307	2	4		







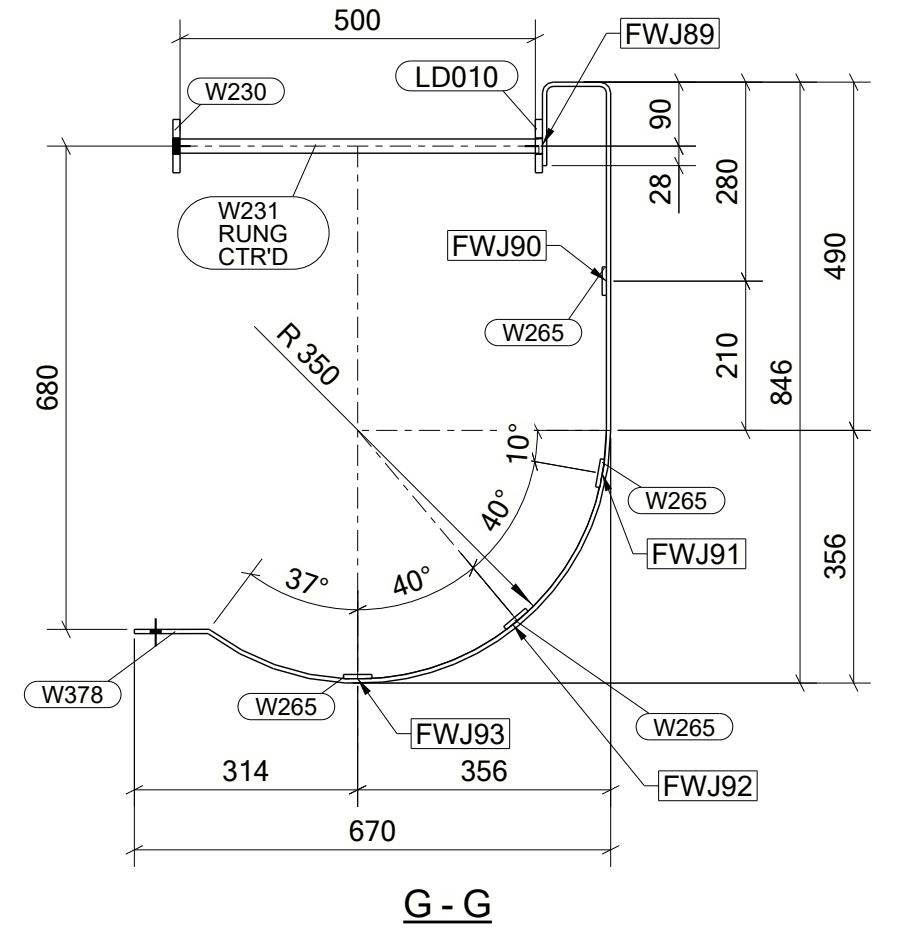
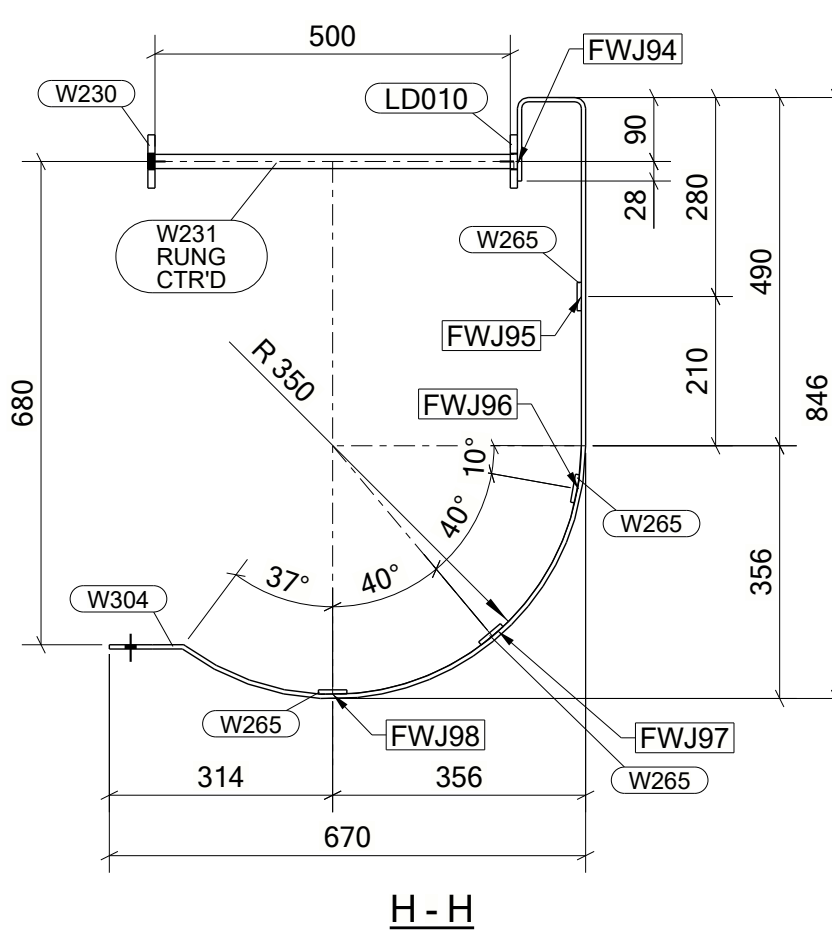


ANCILLARY CATEGORY
FW-J1 TO J98

GA & IFC DRAWINGS REFERENCE	REV.
AD282-732-C-33226,27,28,29,30,31	4
AD282-732-C-33233,34,35,33499,33500	4
AD282-732-C-34337	2
AD282-732-C-34300	2

- NOTES :**
- 1-ALL DIMENSIONS ARE GIVEN IN MILLIMETERS (U.N.O.).
 - 2-  DENOTES ASSEMBLY ORIENTATION MARK.
 - 3-DON'T SCALE THE DRAWING. FOLLOW THE WRITTEN DIMENSIONS.
 - 4-FINISH AS PER PROJECT SPEC.
 - 5-STRUCTURAL STEELWORK SHALL BE IN ACCORDANCE WITH PROJECT SPECIFICATIONS AD282-732-G-03520 & AD282-732-G-03527
 - 6-WHEREVER THERE IS NO ACCESS FOR FILLET WELDING TO BE REPLACED BY FULL PENETRATION BUTT WELDING
 - 7-FOR CJP WELD MARKED LOCATIONS FOLLOW THIS DETAIL
- 
- 8-ALL WELDS TO BE 6mm FILLET WELD U.N.O.

GRID LOCATION	
0 230	1'-1/B-B'

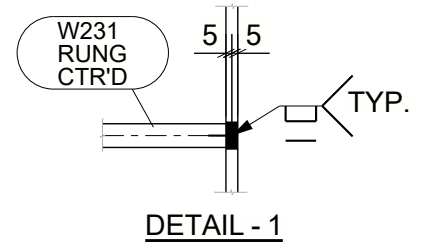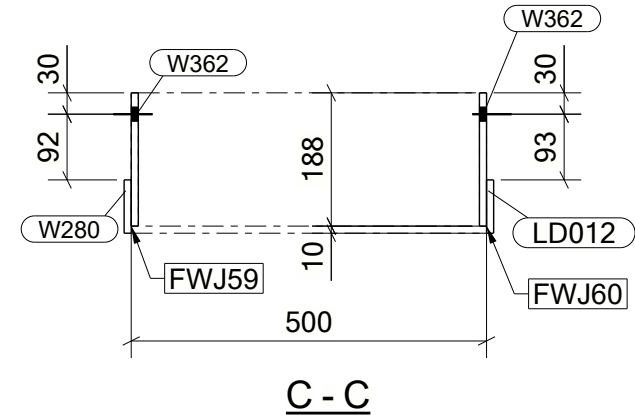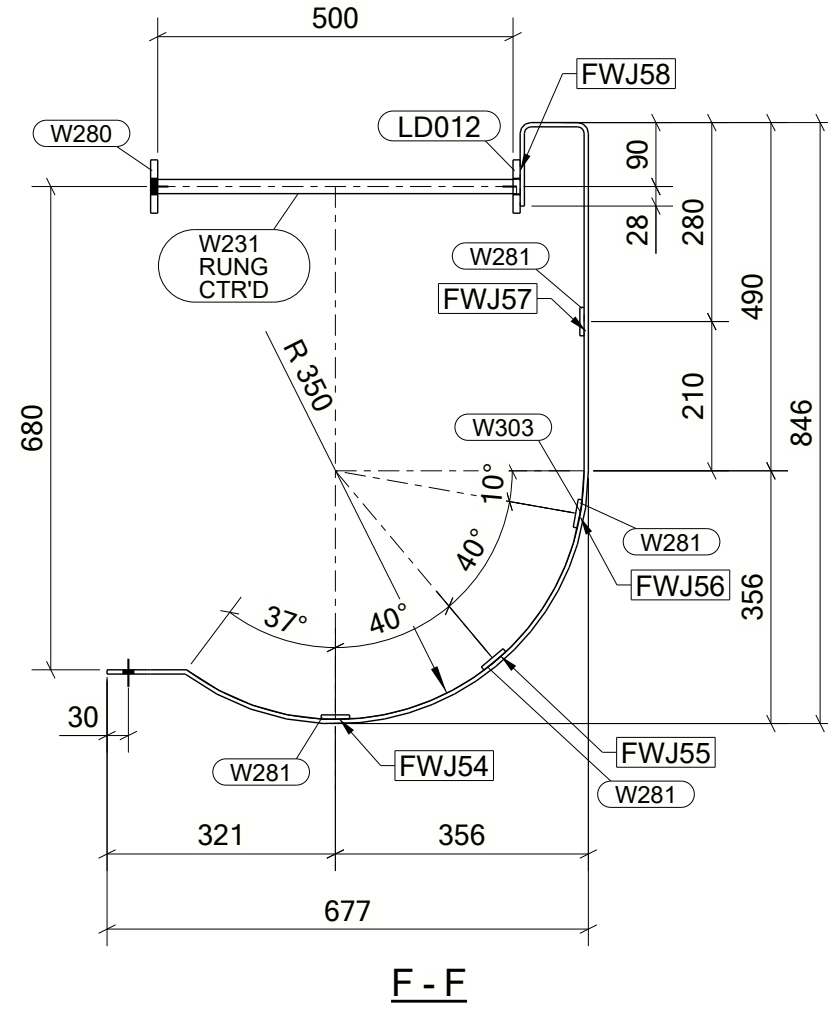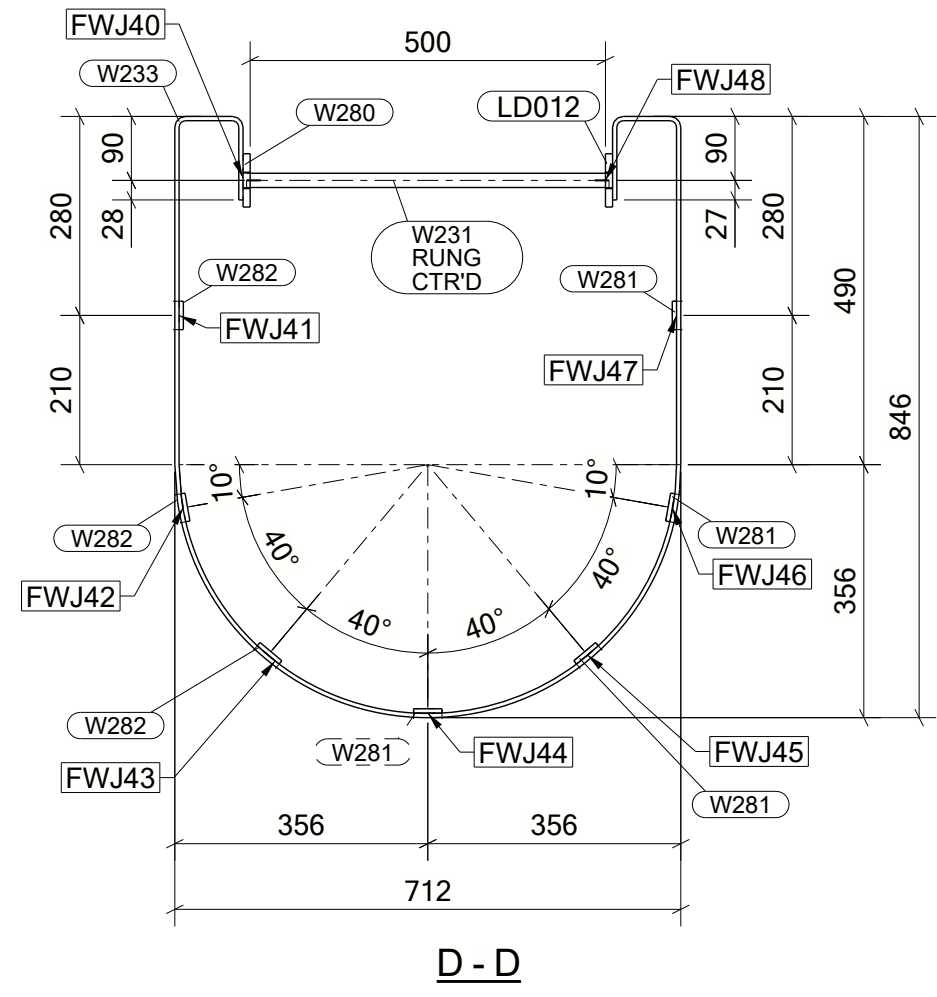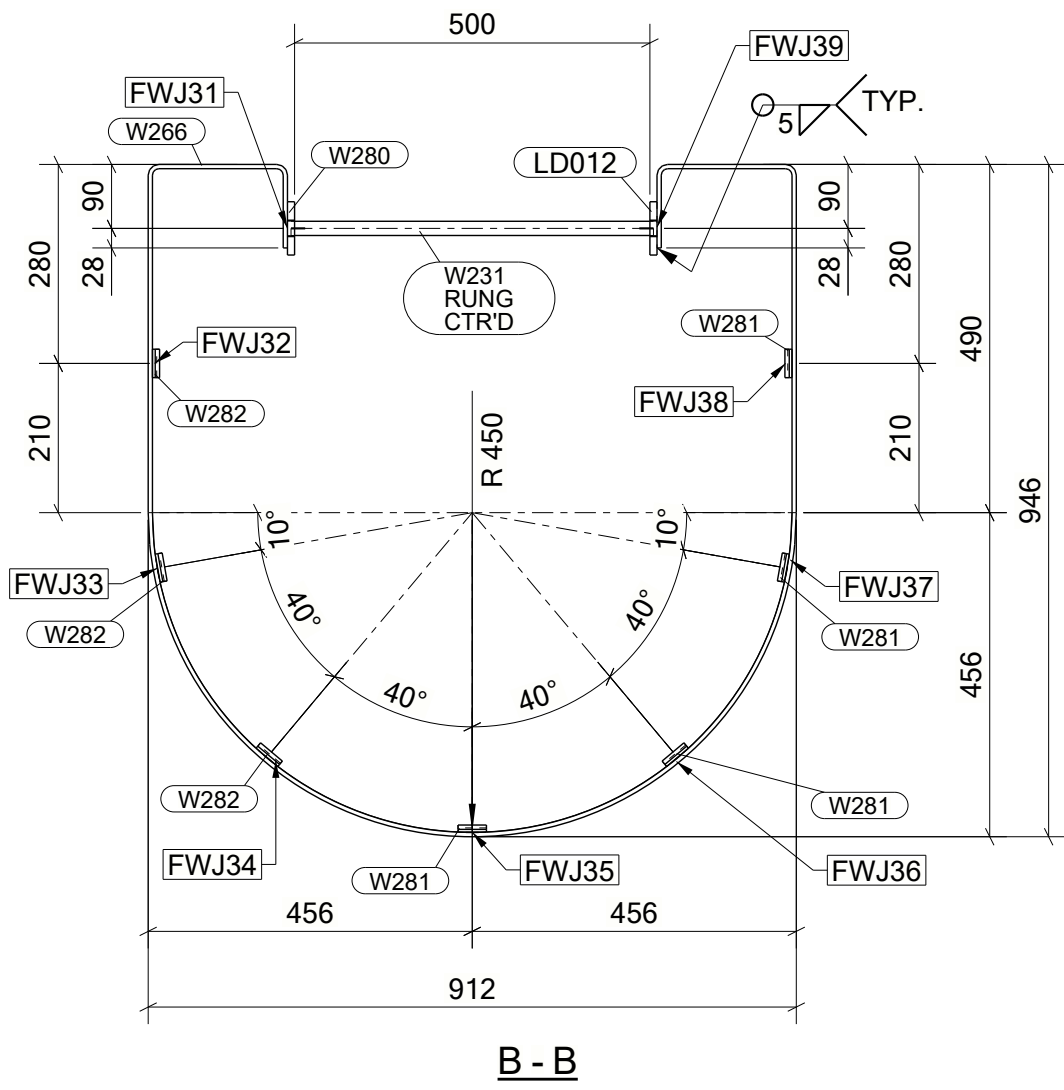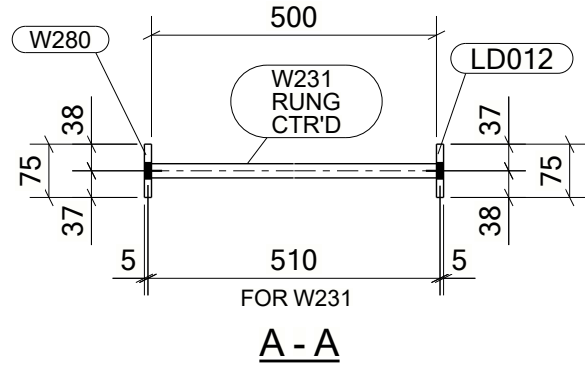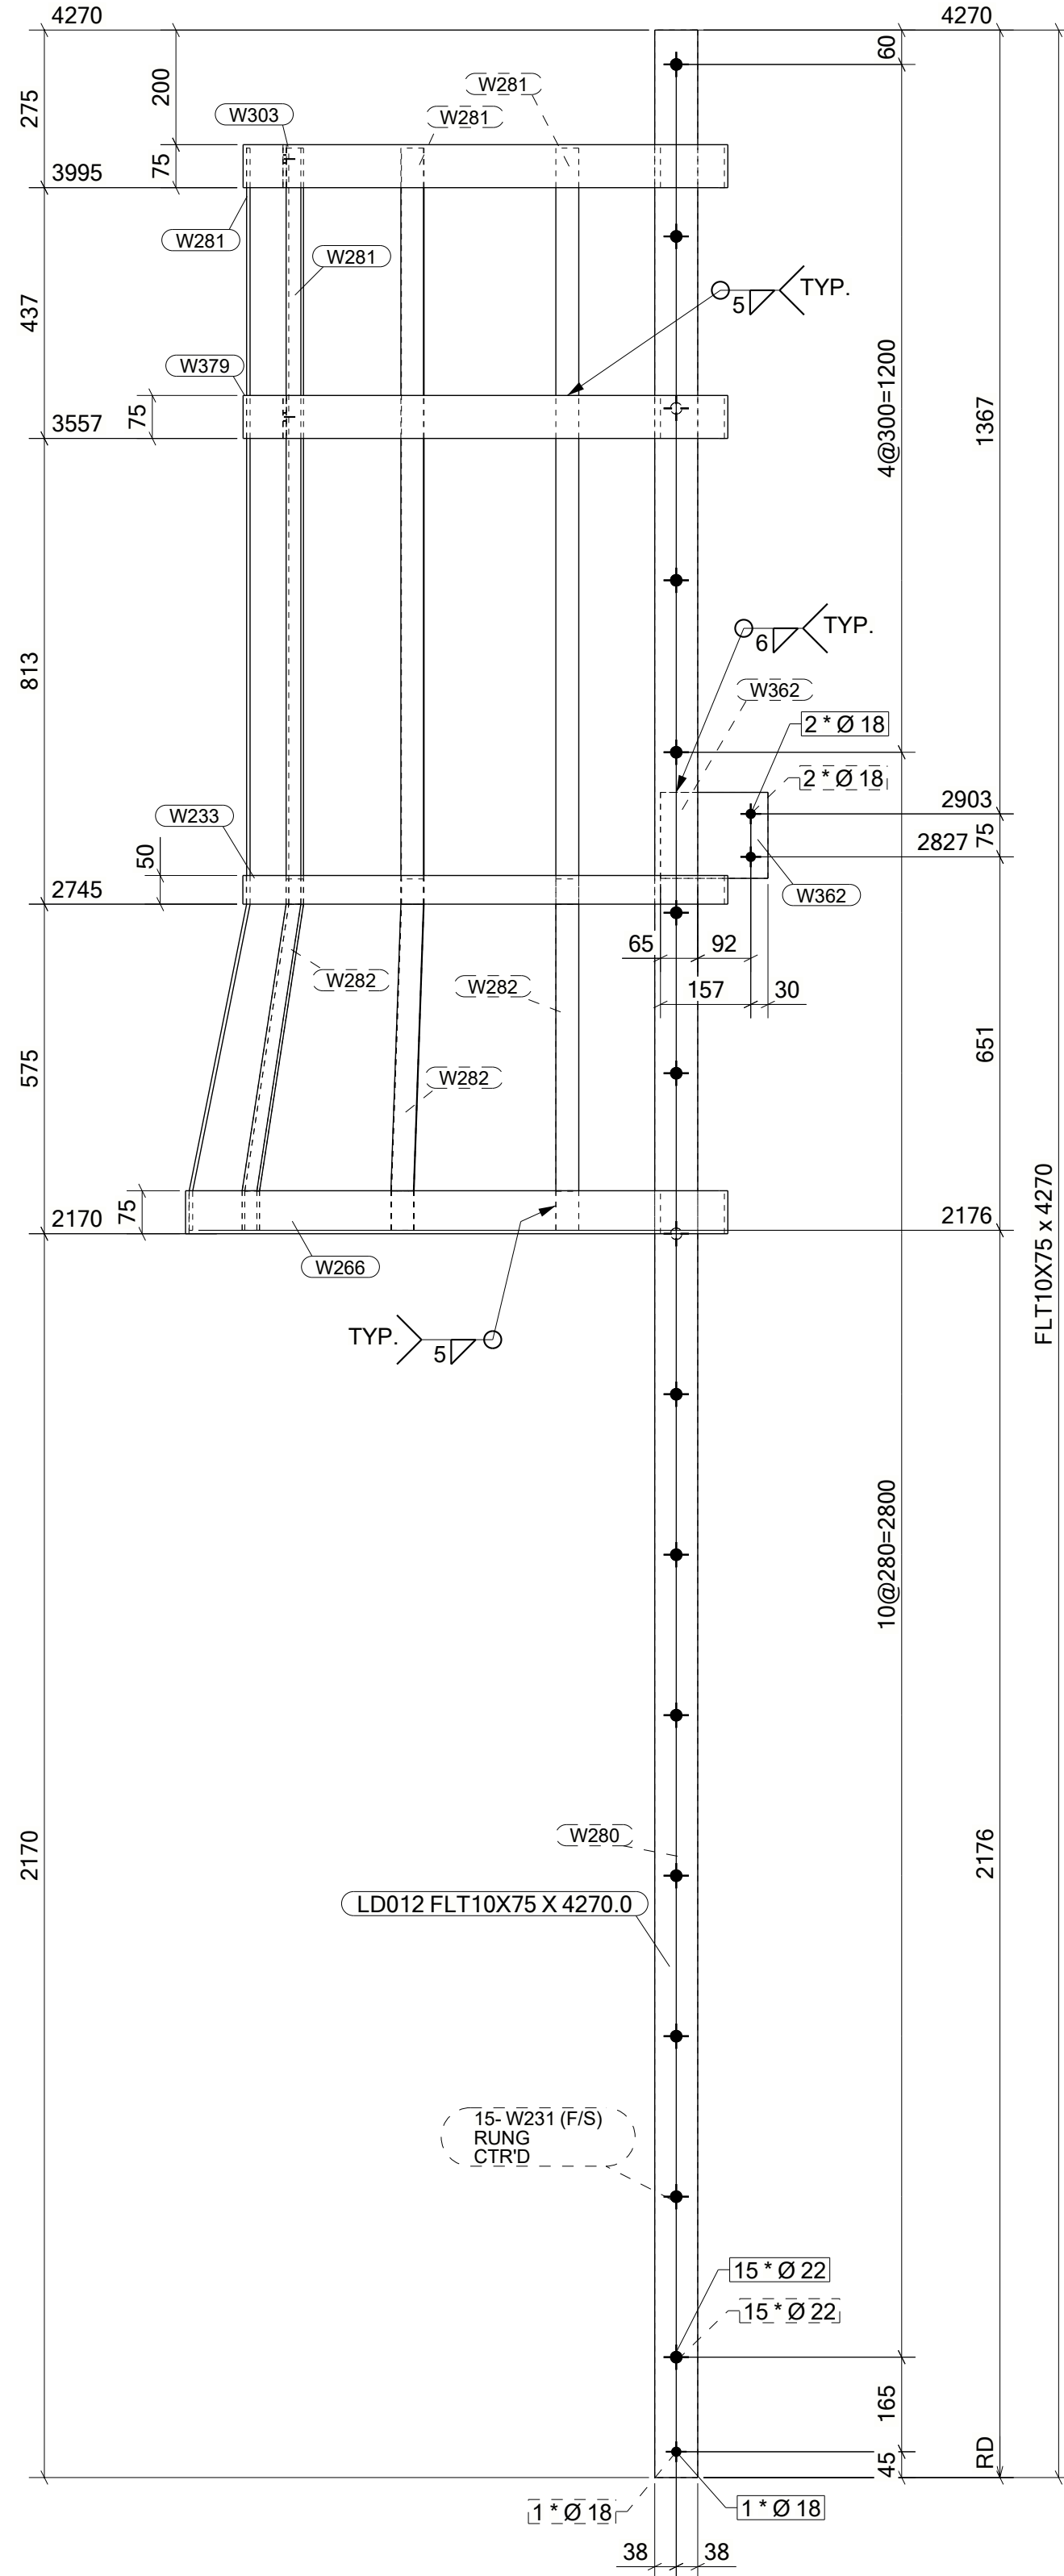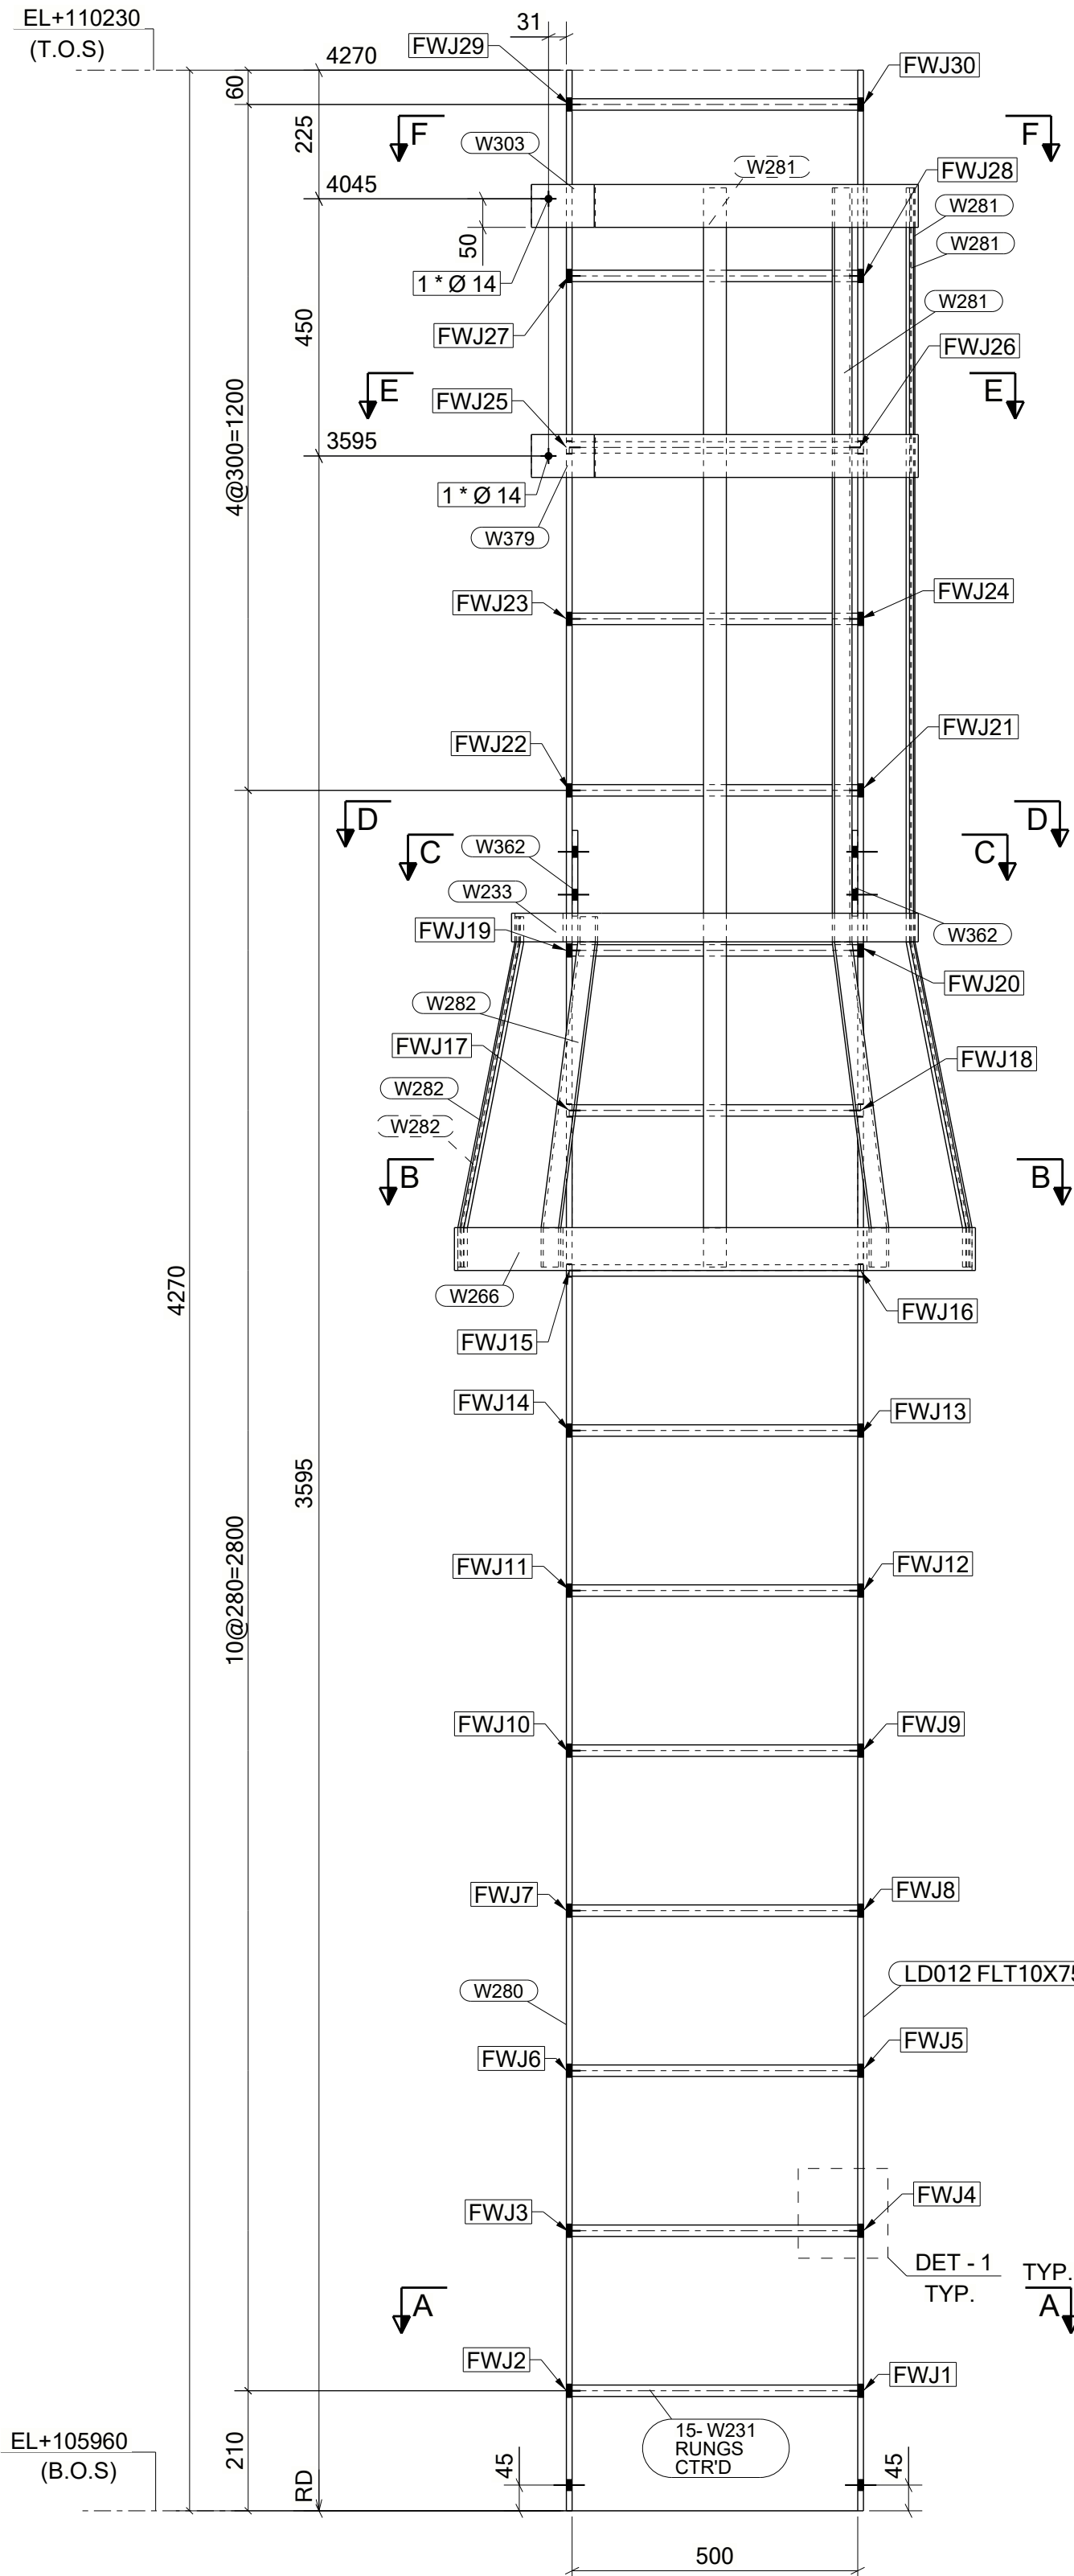

DRAWING NO. : 2307087-STL-732-02-LD012				REV. : 00							
ERECTION MARK : 2307087-STL-732-02-LD012				DESCRIPTION : LADDER		COLOR CODE : 10 B 15		QTY : 1		NO. :	
HOLD:		TYPE: W		TREAT: GPN		COST CODE: 4.01		REMARKS:			
LENGTH: 4270		WIDTH: 912		HEIGHT: 1016		TOTAL S.AREA: 4.2		(M2)			
POSITION NO.	QTY PER ASSY	SECTION	LENGTH	UNIT WEIGHT (KG)	TOTAL WEIGHT (KG)		GRADE	REVISION	PART ID	TREATMENT	REMARKS
					QTY	WEIGHT					
LD012	1	FLT10X75	4270	25.140	1	25.14	S275JR	1	MM	GPN	
W231	15	ROD20	510	1.243	15	18.65	S275JR	1	WI		SMOOTH BAR
W233	1	FLT6X50	2443	5.807	1	5.81	S275JR	1	WI		
W266	1	FLT6X75	2957	10.526	1	10.53	S275JR	1	WI		
W280	1	FLT10X75	4270	25.140	1	25.14	S275JR	1	WI		
W281	4	FLT6X40	1898	3.576	4	14.30	S275JR	1	WI		
W282	3	FLT6X40	623	1.174	3	3.52	S275JR	1	WI		
W303	1	FLT6X75	1556	5.541	1	5.54	S275JR	1	WI		
W362	2	FLT10X150	188	2.208	2	4.42	S275I50	1	WI		
W379	1	FLT6X75	1556	5.541	1	5.54	S275JR	1	WI		
					UNIT WEIGHT	118.58					
					TOTAL WEIGHT	118.58					

BOLT LIST:-						
BOLT \ STUD	BOLT DESCRIPTION		QTY/ONE	QTY/ALL	FINISH	REMARKS
BOLT	B1N1W12 × 30	A307	1	2		
BOLT	B1N1W16 × 45	A307	2	4		

ANCILLARY CATEGORY
FW-J1 TO J60

GA & IFC DRAWINGS REFERENCE	REV.
AD282-732-C-33226,27,28,29,30,31	4
AD282-732-C-33233,34,35,33499,33500	4
AD282-732-C-34337	2
AD282-732-C-34300	2


NOTES

- 1-ALL DIMENSIONS ARE GIVEN IN MILLIMETERS (U.N.O.).
- 2-  DENOTES ASSEMBLY ORIENTATION MARK.
- 3-DON'T SCALE THE DRAWING. FOLLOW THE WRITTEN DIMENSIONS.
- 4-FINISH AS PER PROJECT SPEC.
- 5- STRUCTURAL STEELWORK SHALL BE IN ACCORDANCE WITH PROJECT SPECIFICATIONS AD282-732-G-03520 & AD282-732-G-03527
- 6-WHEREVER THERE IS NO ACCESS FOR FILLET WELDING TO BE REPLACED BY FULL PENETRATION BUTT WELDING
- 7-FOR CIP WELD MARKED LOCATIONS FOLLOW THIS DETAIL

8-ALL WELDS TO BE 6mm FILLET WELD U.N.O.

GRID LOCATION	
EL +118.101	<732-09/732-B>

DRAWING NO. : 2307059-732-V-132-LP009										REV.: 00	
ERECTION MARK : 2307059-732-V-132-LP009				DESCRIPTION : LOOSE_GUSSET_PLATE			COLOR CODE : 10 B 15		QTY : 1		NOS
HOLD:		TYPE: L	TREAT: PN		COST CODE: 2.03			REMARKS:			
LENGTH: 338		WIDTH: 16		HEIGHT: 395		TOTAL S.AREA: 0.2			(M2)		
POSITION NO.	QTY PER ASSLY	SECTION	LENGTH	UNIT WEIGHT (KG)	TOTAL WIEGHT (KG)		GRADE	REVISION	PART ID	TREATMENT	REMARKS
					QTY	WEIGHT					
LP009	1	PL16X338	395	12.478	1	12.48	S355JR	1	MM	PN	
					UNIT WEIGHT	12.48					
					TOTAL WEIGHT	12.48					
BOLT LIST:-											
BOLT \ STUD	BOLT DESCRIPTION			QTY/ONE	QTY/ALL	FINISH	REMARKS				
BOLT	B1N1W20 × 65 A325M			3	6						

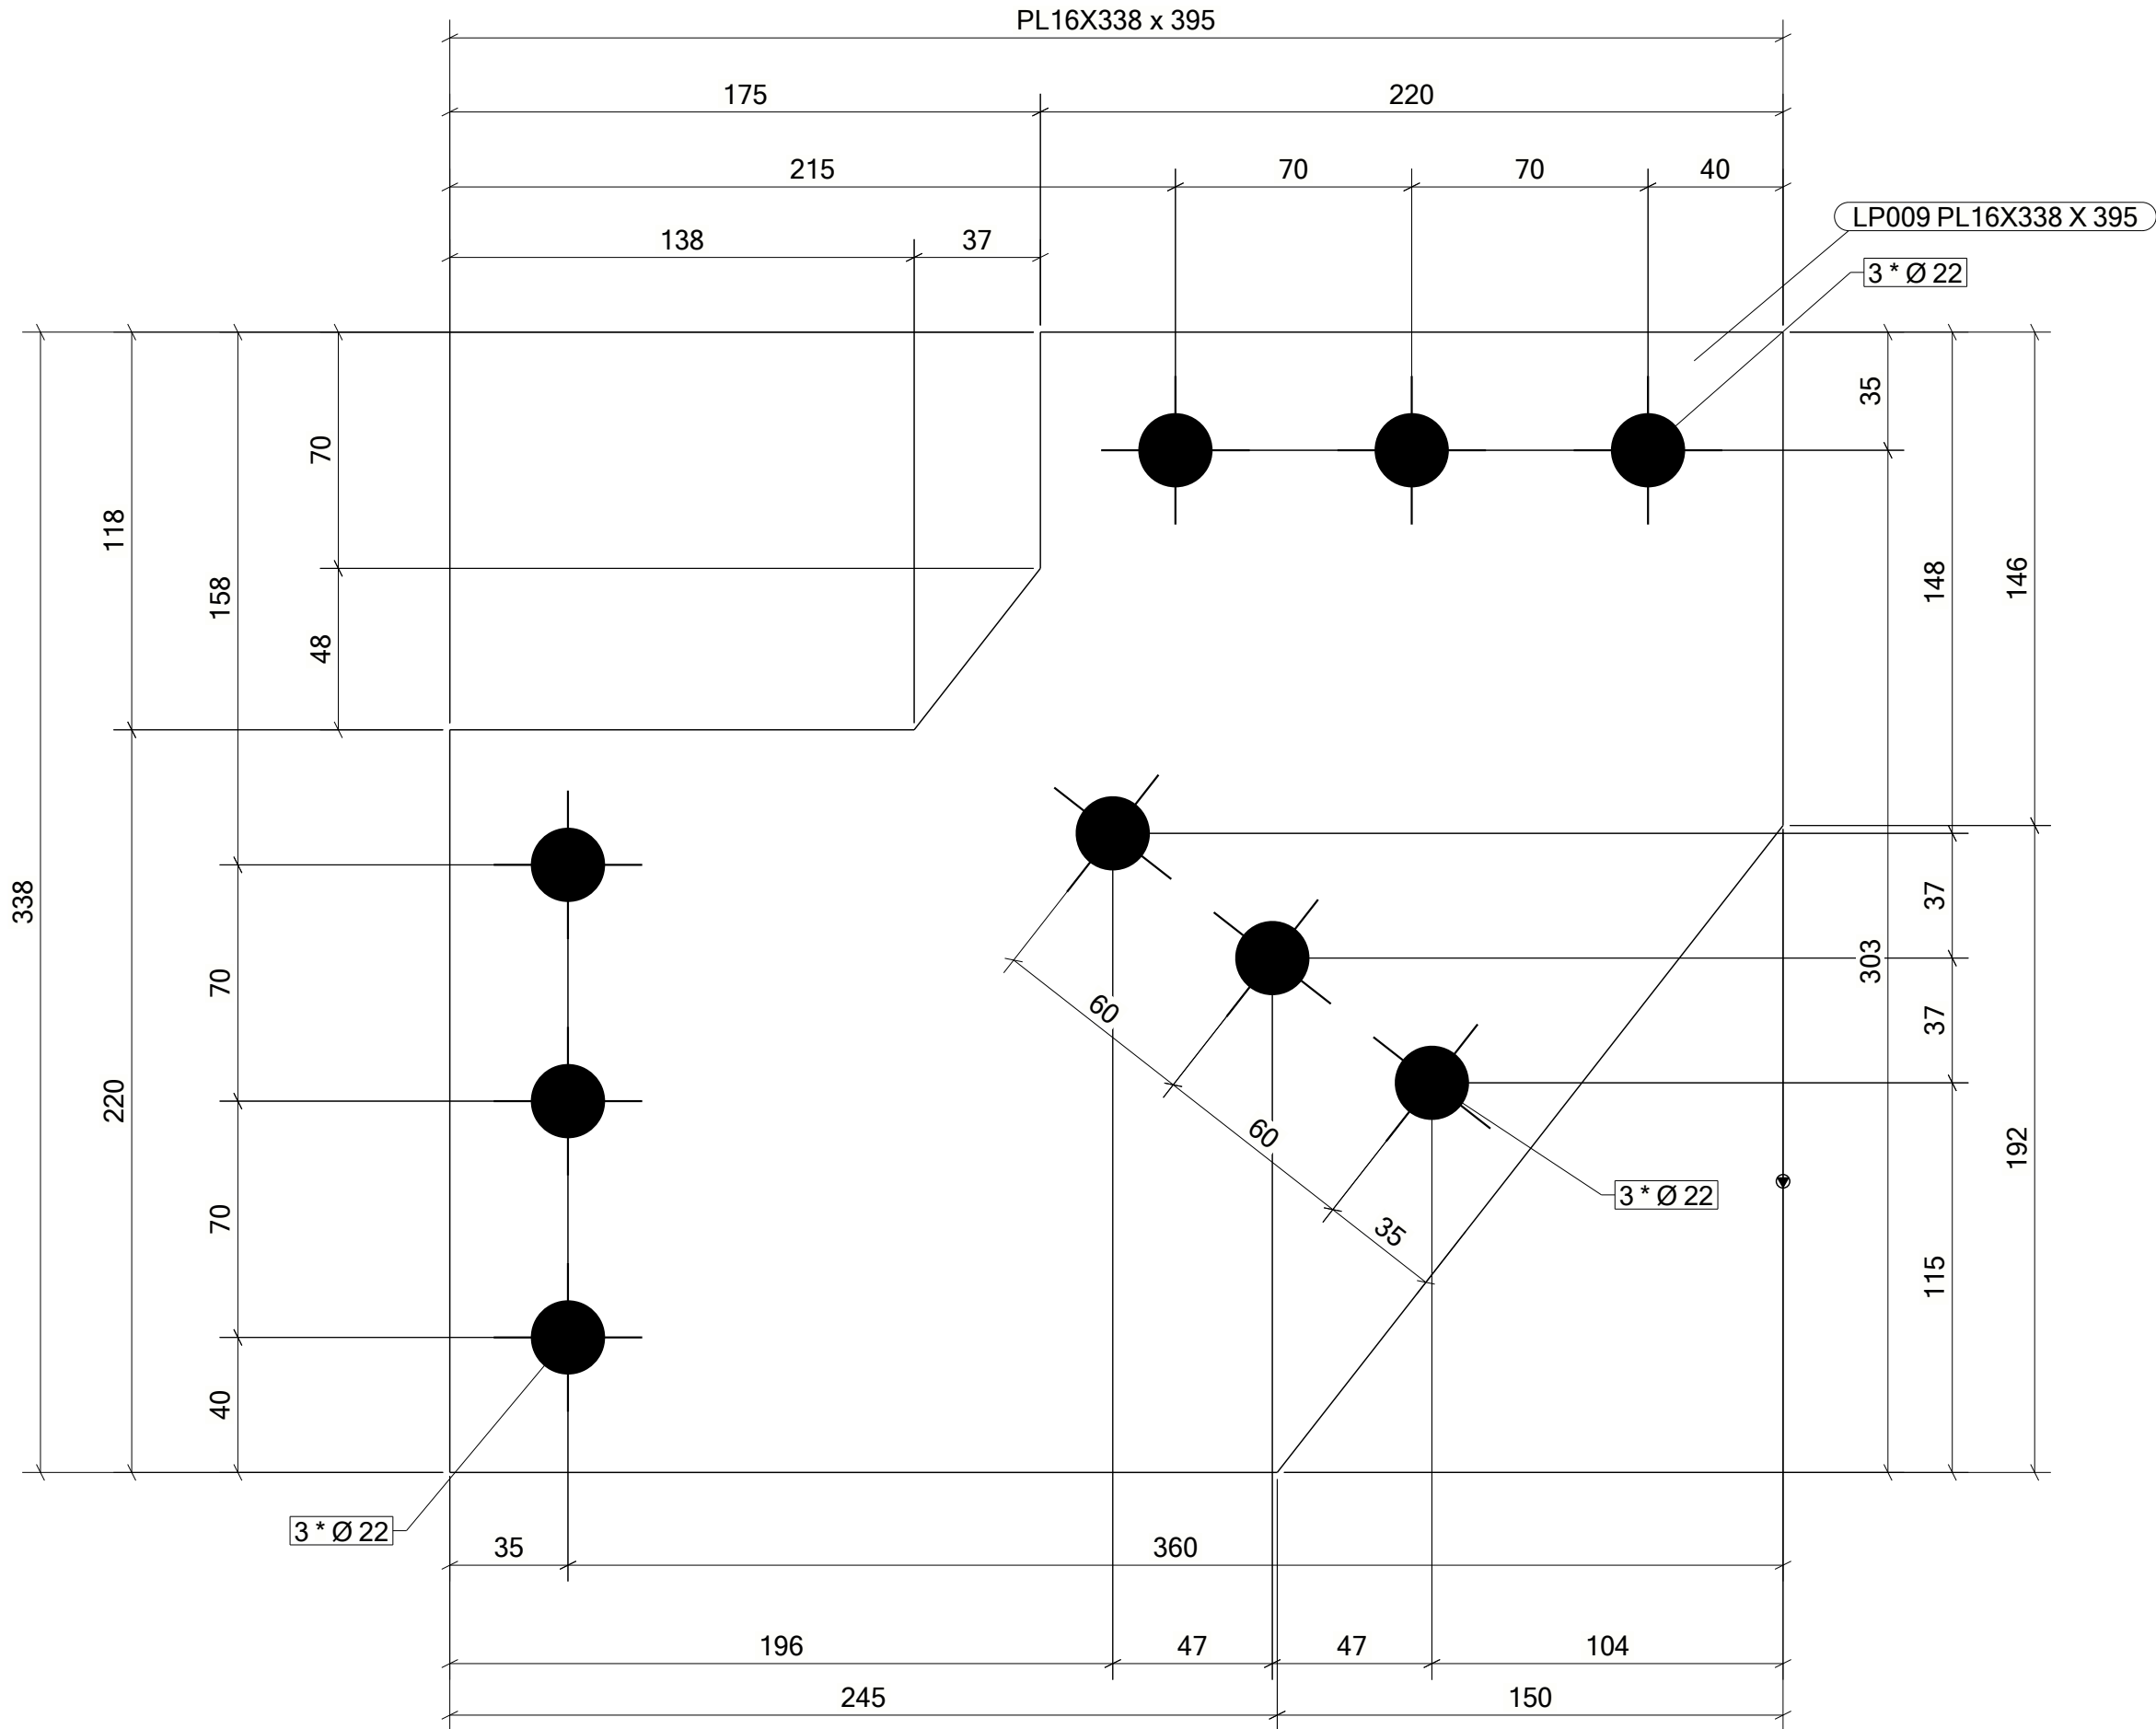


GA & IFC DRAWINGS REFERENCE	REV.
AD282-732-C-33298,299 & 300	3
AD282-732-C-34324	1
AD282-732-C-34287	1

- NOTES :**
- 1-ALL DIMENSIONS ARE GIVEN IN MILLIMETERS (U.N.O.).
 - 2-  DENOTES ASSEMBLY ORIENTATION MARK.
 - 3-DON'T SCALE THE DRAWING. FOLLOW THE WRITTEN DIMENSIONS.
 - 4- FINISH AS PER PROJECT SPEC.
 - 5- STRUCTURAL STEELWORK SHALL BE IN ACCORDANCE WITH PROJECT SPECIFICATIONS AD282-732-G-03520 & AD282-732-G-03527
 - 6-WHEREVER THERE IS NO ACCESS FOR FILLET WELDING TO BE REPLACED BY FULL PENETRATION BUTT WELDING
 - 7-FOR CJP WELD MARKED LOCATIONS FOLLOW THIS DETAIL

 - 8-ALL WELDS TO BE 6mm FILLET WELD U.N.O.

GRID LOCATION	
EL +118.101	<732-09/732-B>

DRAWING NO. : 2307059-732-V-132-LP010										REV.: 00							
ERECTION MARK : 2307059-732-V-132-LP010										DESCRIPTION : LOOSE_GUSSET_PLATE		COLOR CODE : 10 B 15		QTY : 1		NOS	
HOLD:		TYPE: L		TREAT: PN		COST CODE: 2.03				REMARKS:							
LENGTH: 395		WIDTH: 16		HEIGHT: 338		TOTAL S.AREA: 0.2				(M2)							
POSITION NO.	QTY PER ASSLY	SECTION	LENGTH	UNIT WEIGHT (KG)	TOTAL WIEGHT (KG)		GRADE	REVISION	PART ID	TREATMENT	REMARKS						
					QTY	WEIGHT											
LP010	1	PL16X338	395	12.548	1	12.55	S355JR	1	MM	PN							
					UNIT WEIGHT	12.55											
					TOTAL WEIGHT	12.55											
BOLT LIST:-																	
BOLT \ STUD		BOLT DESCRIPTION			QTY/ONE	QTY/ALL	FINISH	REMARKS									
BOLT		B1N1W20 × 65		A325M	3	6											

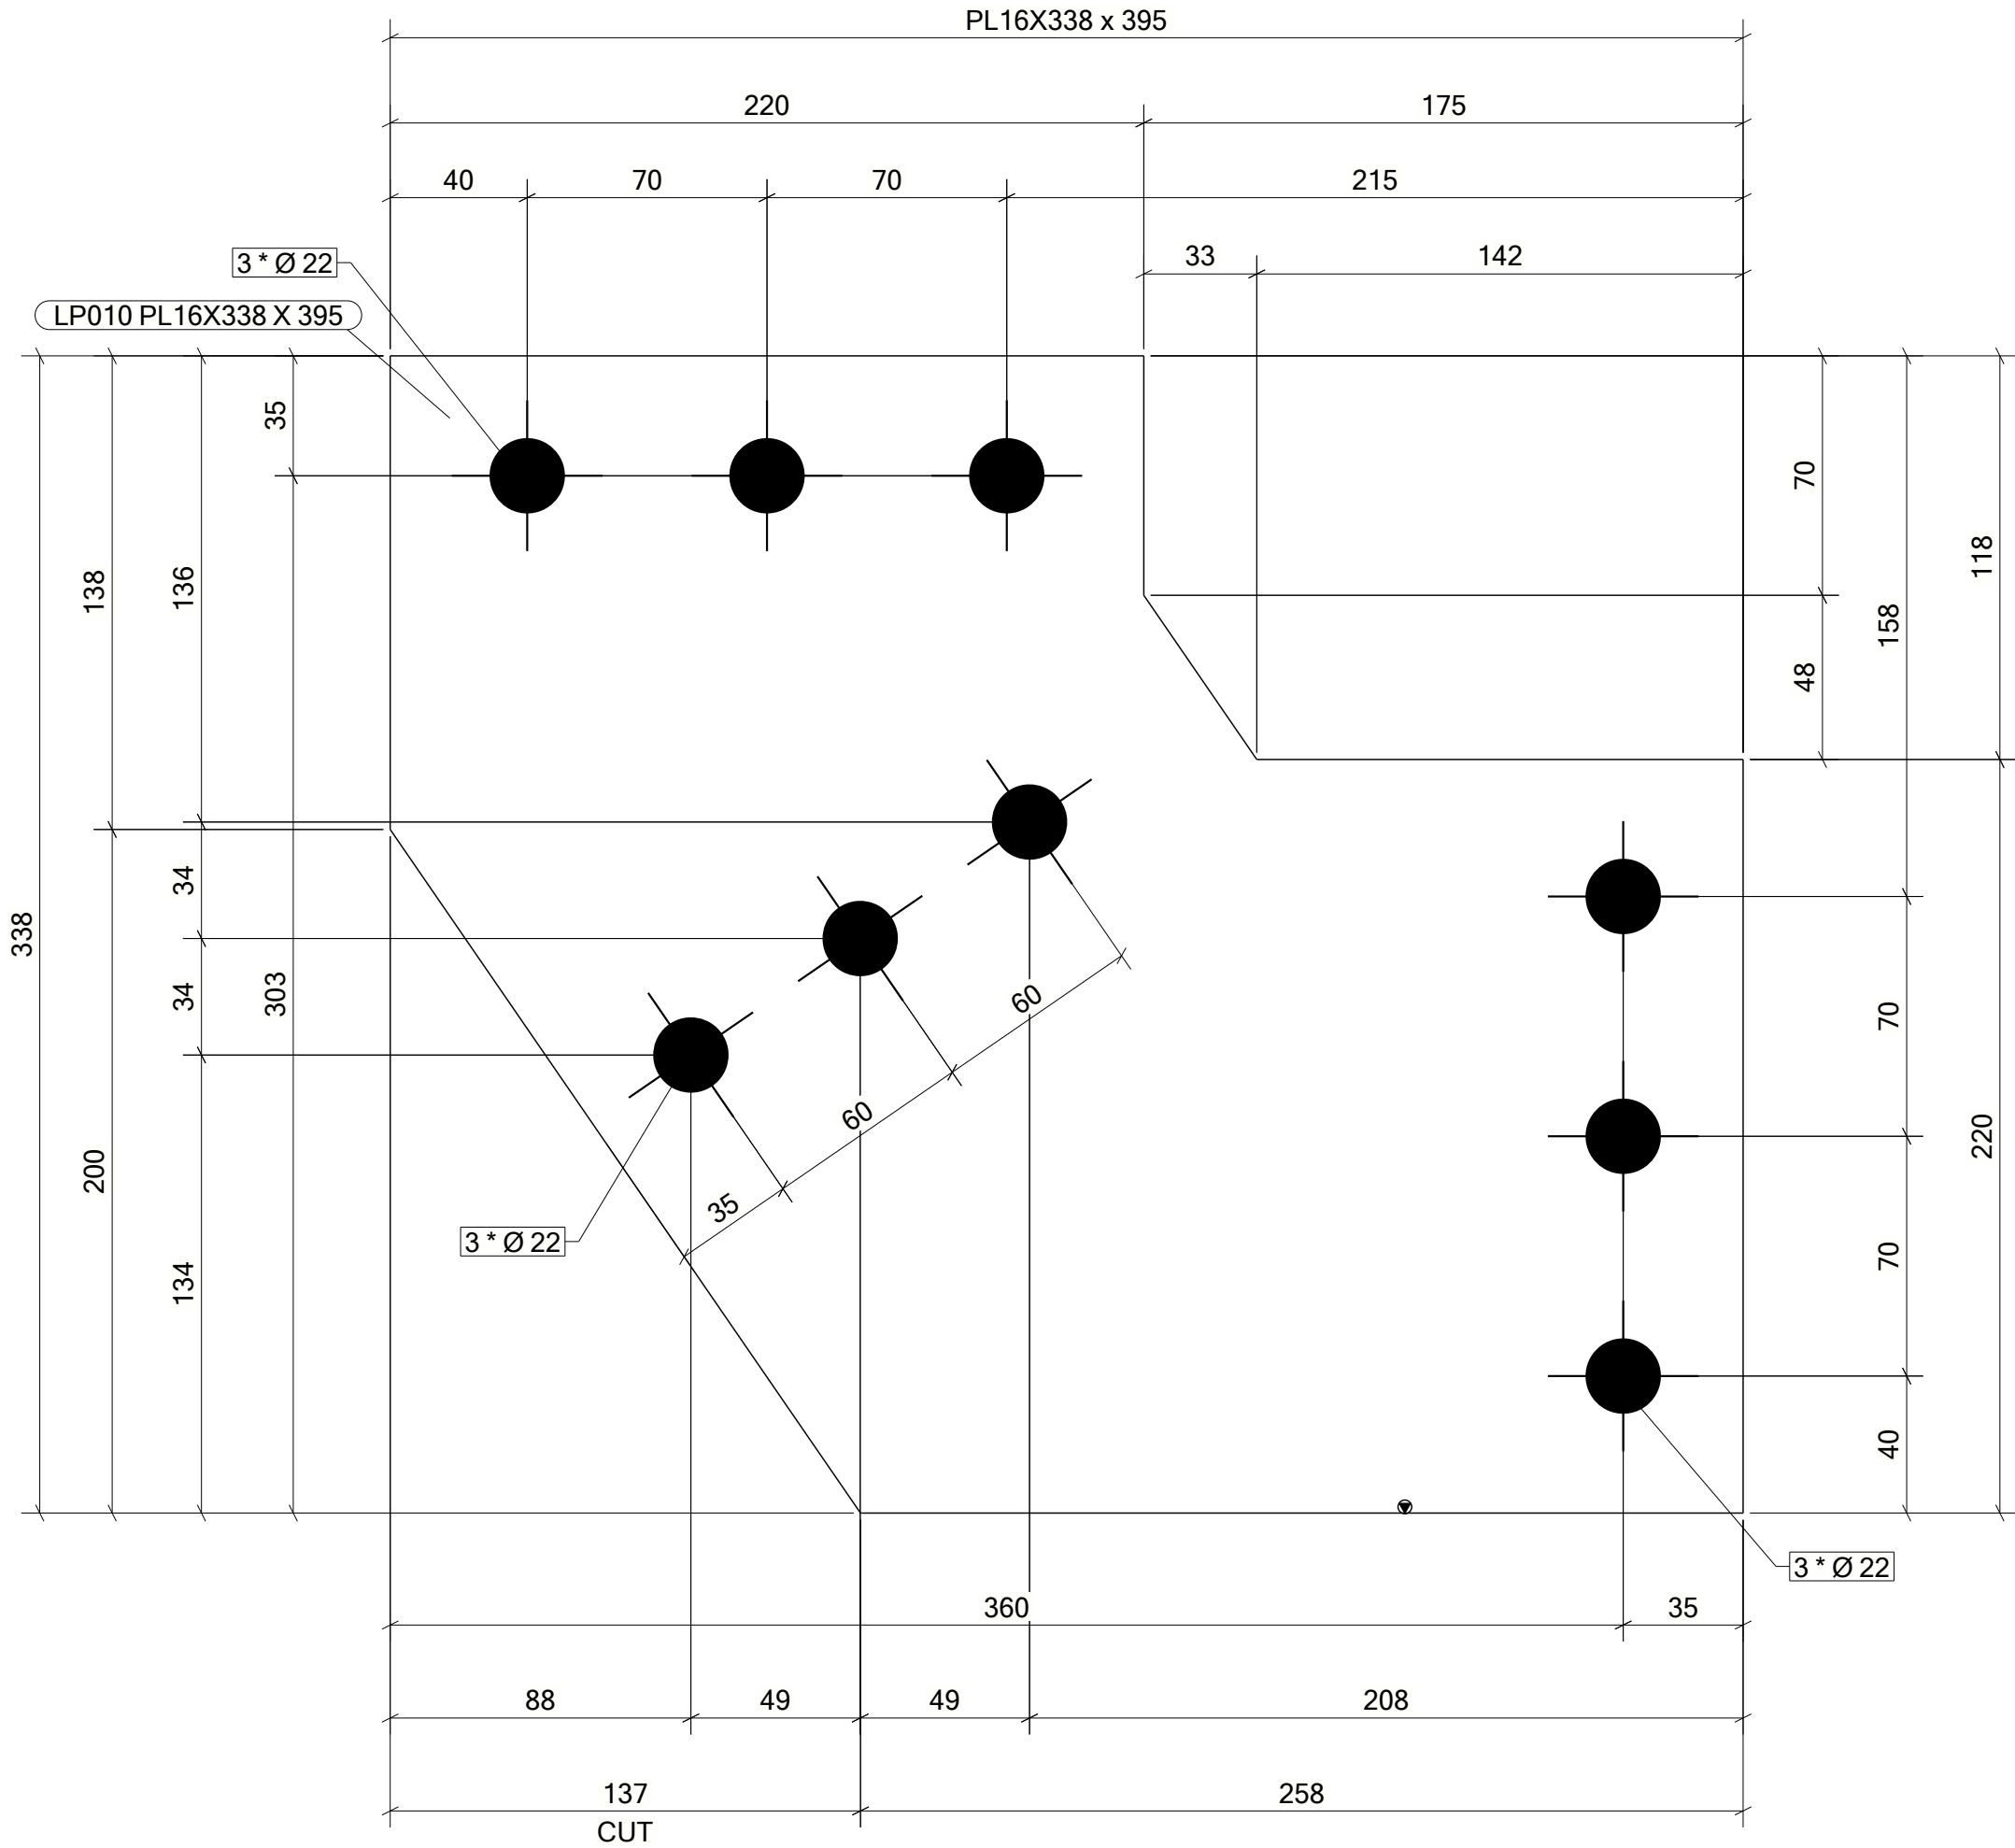

GA & IFC DRAWINGS REFERENCE	REV.
AD282-732-C-33298,299 & 300	3
AD282-732-C-34324	1
AD282-732-C-34287	1

NOTES :

1-ALL DIMENSIONS ARE GIVEN IN MILLIMETERS (U.N.O.).

2-  DENOTES ASSEMBLY ORIENTATION MARK.

3-DON'T SCALE THE DRAWING. FOLLOW THE WRITTEN DIMENSIONS.

4- FINISH AS PER PROJECT SPEC.

5- STRUCTURAL STEELWORK SHALL BE IN ACCORDANCE WITH PROJECT SPECIFICATIONS AD282-732-G-03520 & AD282-732-G-03527



6-WHEREVER THERE IS NO ACCESS FOR FILLET WELDING TO BE REPLACED BY FULL PENETRATION BUTT WELDING

7-FOR CJP WELD MARKED LOCATIONS FOLLOW THIS DETAIL



8-ALL WELDS TO BE 6mm FILLET WELD U.N.O.

GRID LOCATION	
EL +110.481	732-09>/<732-8


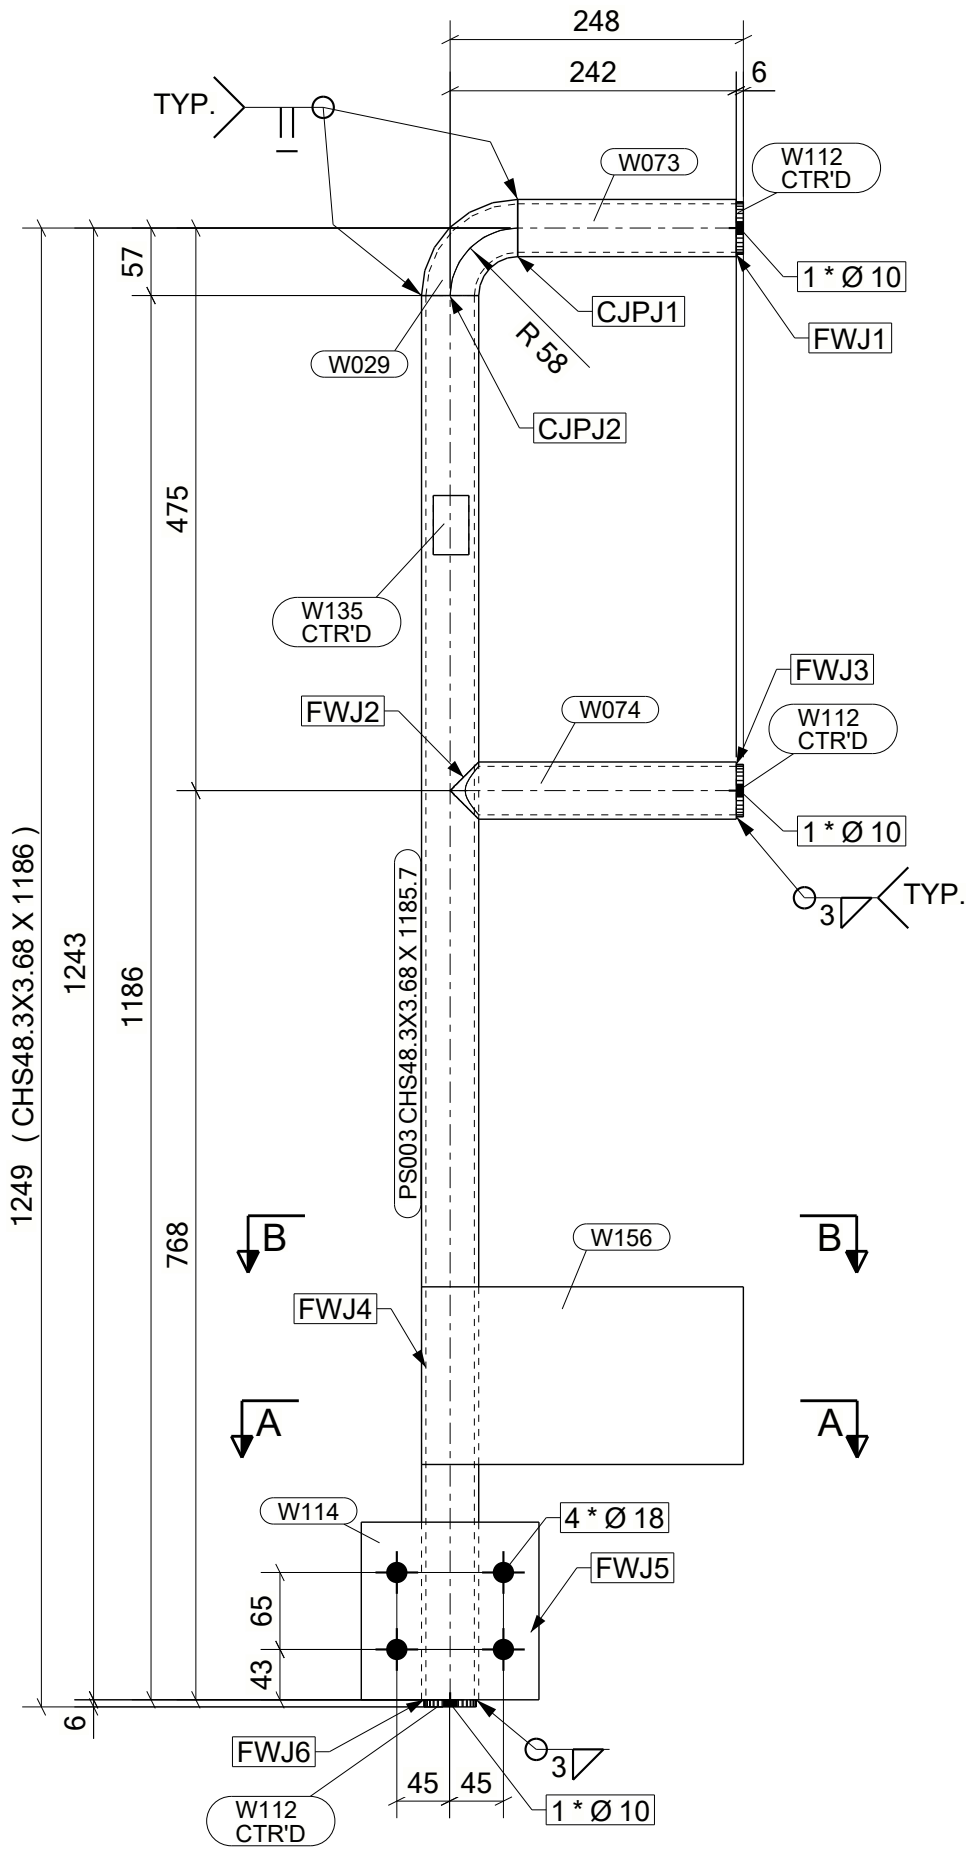
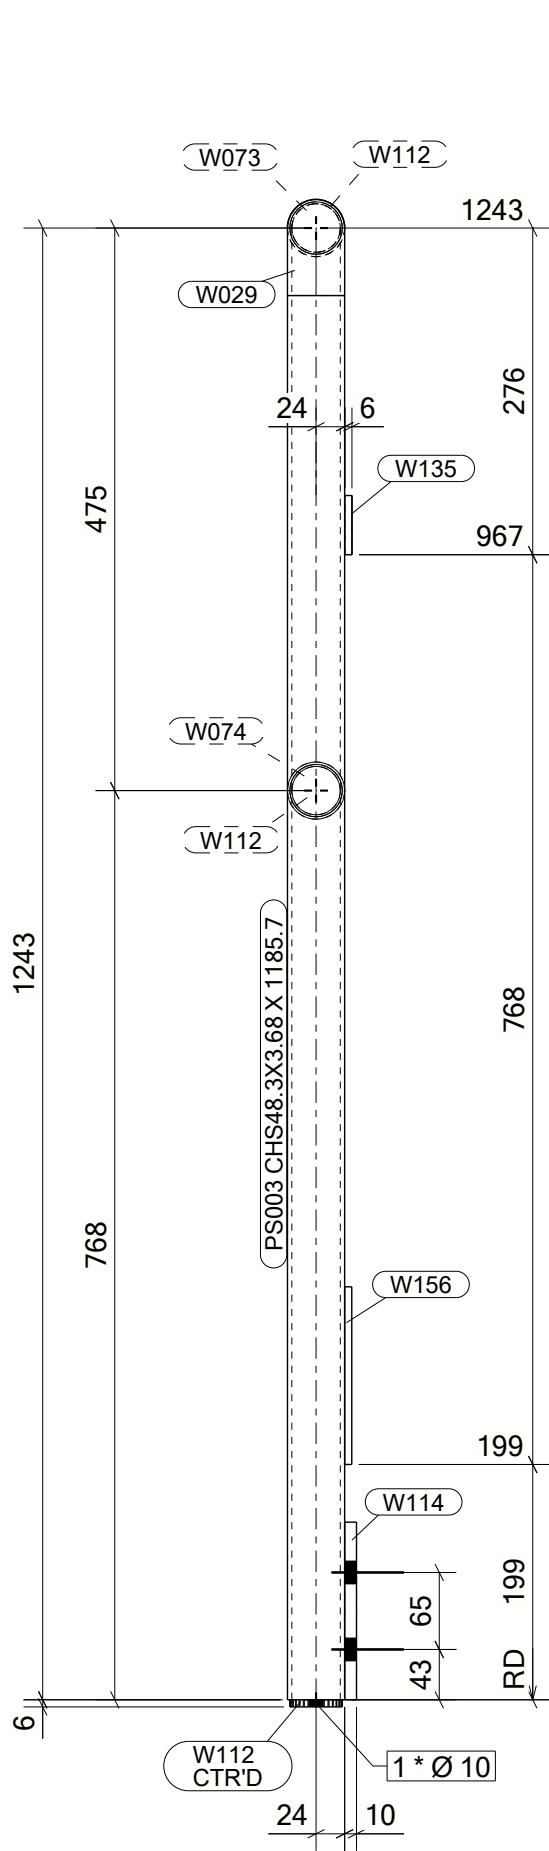


DRAWING NO. : 2307059-732-V-132-PS003										REV.: 00		
ERECTION MARK : 2307059-732-V-132-PS003				DESCRIPTION : POST			COLOR CODE : 10 B 15			QTY : 1		NOS
HOLD:		TYPE: W		TREAT: GPN		COST CODE: 3.01			REMARKS:			
LENGTH: 1273		WIDTH: 257		HEIGHT: 244		TOTAL S.AREA: 0.4						(M2)
POSITION NO.	QTY PER ASSLY	SECTION	LENGTH	UNIT WEIGHT (KG)	TOTAL WIEGHT (KG)		GRADE	REVISION	PART ID	TREATMENT	REMARKS	
					QTY	WEIGHT						
PS003	1	CHS48.3X3.68	1186	4.777	1	4.78	A53-GR.B	1	MM	GPN		
W029	1	CHS48.3X3.68	127	0.357	1	0.36	A53-GR.B	1	WI		ELBOW	
W073	1	CHS48.3X3.68	185	0.744	1	0.74	A53-GR.B	1	WI			
W074	1	CHS48.3X3.68	242	0.903	1	0.90	A53-GR.B	1	WI			
W112	3	PL6X44	44	0.072	3	0.22	S355JR	1	WI			
W114	1	PL10X150	150	1.766	1	1.77	S355JR	1	WI			
W135	1	PL6X50	30	0.013	1	0.01	Neoprene	1	WI		NEOPRENE	
W156	1	FLT6X150	272	1.920	1	1.92	S275JR	1	WI			
					UNIT WEIGHT	10.70						
					TOTAL WEIGHT	10.70						
BOLT LIST:-												
BOLT \ STUD		BOLT DESCRIPTION		QTY/ONE		QTY/ALL		FINISH		REMARKS		
BOLT		B1N1W16 × 50 A307		4		4						

ANCILLARY CATEGORY

FW- J1 TO J6

CJP-J1 TO J2

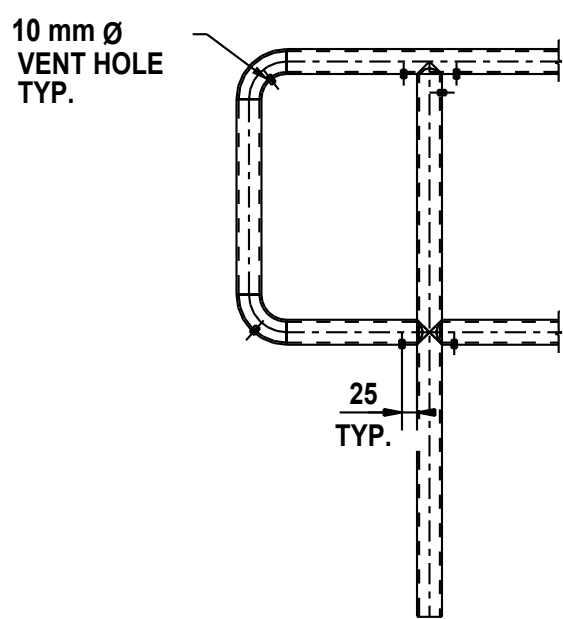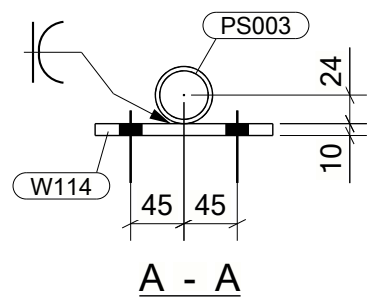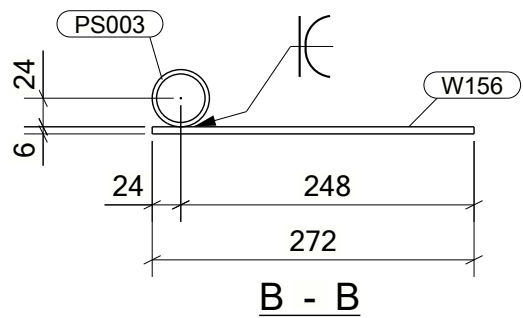




TYPICAL VENT HOLE DETAIL

GA & IFC DRAWINGS REFERENCE	REV.
AD282-732-C-33288,299 & 300	3
AD282-732-C-34324	1
AD282-732-C-34287	1

NOTES :

- 1-ALL DIMENSIONS ARE GIVEN IN MILLIMETERS (U.N.O.).
- 2-  DENOTES ASSEMBLY ORIENTATION MARK.
- 3-DON'T SCALE THE DRAWING. FOLLOW THE WRITTEN DIMENSIONS.
- 4- FINISH AS PER PROJECT SPEC.
- 5- STRUCTURAL STEELWORK SHALL BE IN ACCORDANCE WITH PROJECT SPECIFICATIONS AD282-732-G-03520 & AD282-732-G-03527
- 6-WHEREVER THERE IS NO ACCESS FOR FILLET WELDING TO BE REPLACED BY FULL PENETRATION BUTT WELDING
- 7-FOR CJP WELD MARKED LOCATIONS FOLLOW THIS DETAIL
- 8-ALL WELDS TO BE 6mm FILLET WELD U.N.O.

GRID LOCATION	
EL +112.898	<2/C-D

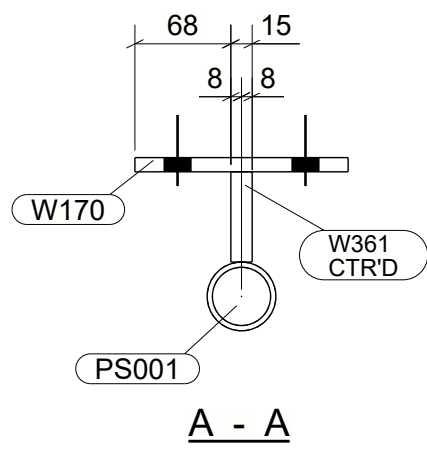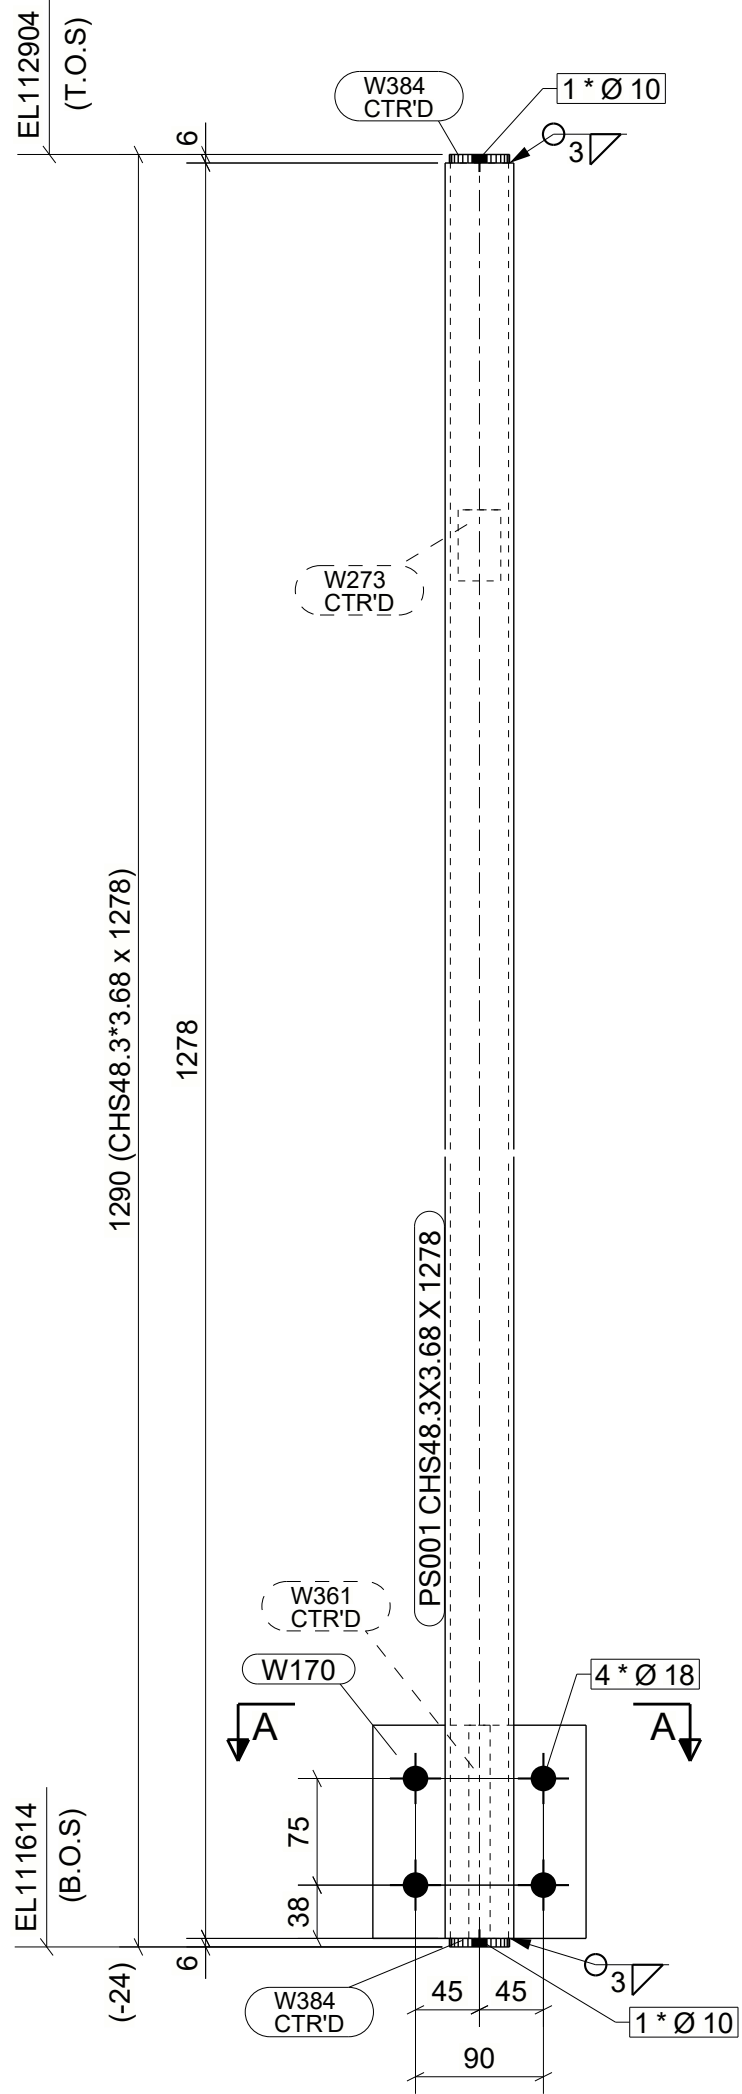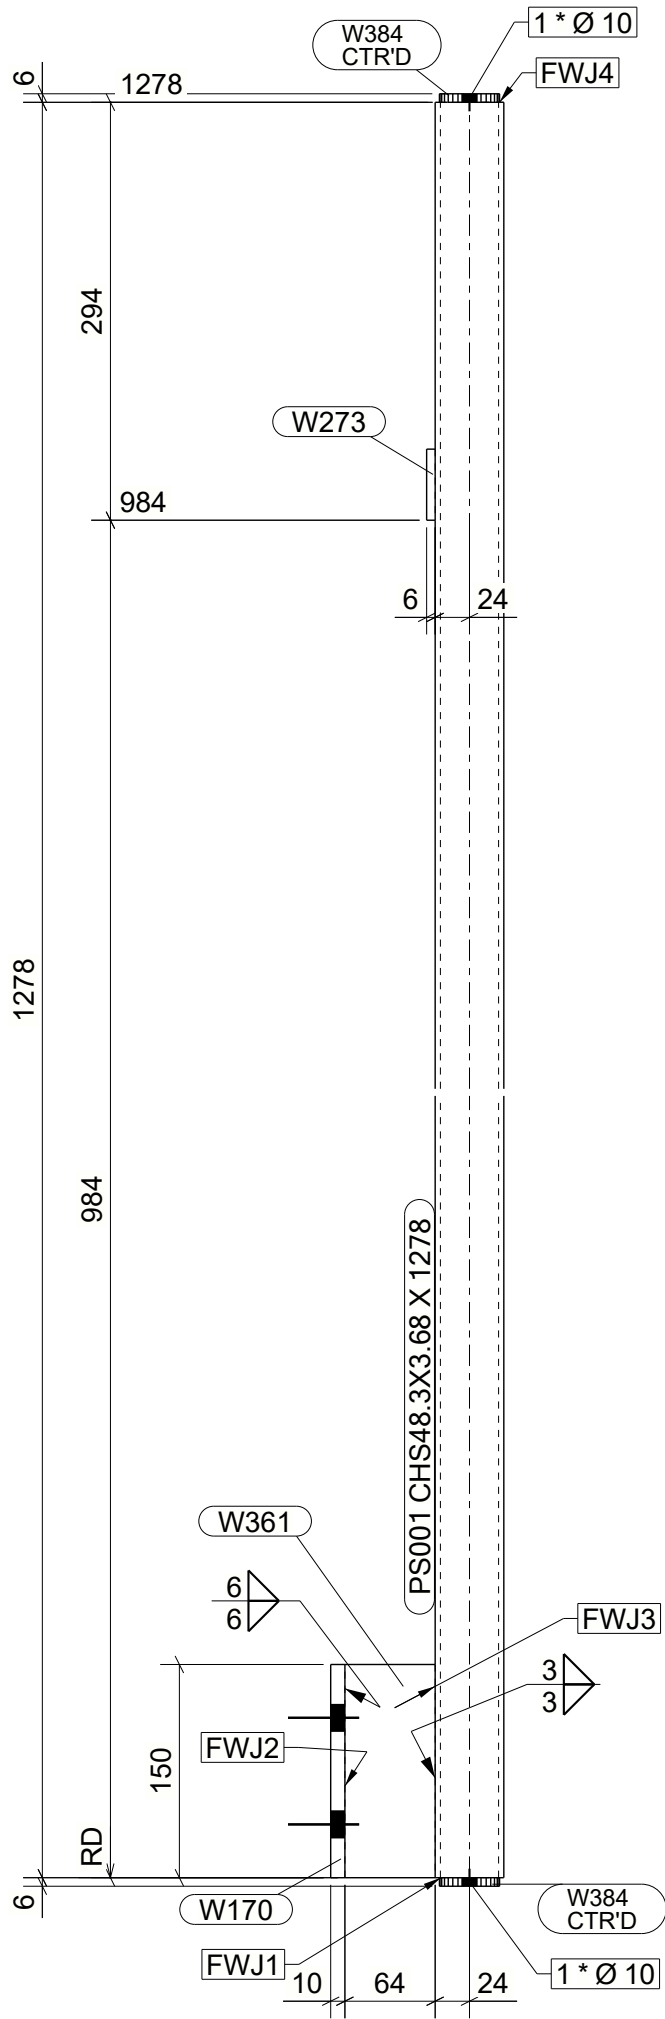




DRAWING NO. : 2307087-STL-732-02-PS001										REV.: 00	
ERECTION MARK : 2307087-STL-732-02-PS001				DESCRIPTION : POST				COLOR CODE : 10 B 15		QTY : 1	NOS
HOLD:		TYPE: W	TREAT: GPN		COST CODE: 3.01				REMARKS:		
LENGTH: 1290		WIDTH: 122		HEIGHT: 150		TOTAL S.AREA: 0.3				(M2)	
POSITION NO.	QTY PER ASSLY	SECTION	LENGTH	UNIT WEIGHT (KG)	TOTAL WIEGHT (KG)		GRADE	REVISION	PART ID	TREATMENT	REMARKS
					QTY	WEIGHT					
PS001	1	CHS48.3X3.68	1278	5.150	1	5.15	A53-GR.B	1	MM	GPN	
W170	1	PL10X150	150	1.766	1	1.77	S355JR	1	WI		
W273	1	PL6X30	50	0.013	1	0.01	Neoprene	1	WI		NEOPRENE
W361	1	PL15X150	64	1.122	1	1.12	S355JR	1	WI		
W384	2	PL6X42	42	0.066	2	0.13	S355JR	1	WI		
					UNIT WEIGHT	8.18					
					TOTAL WEIGHT	8.18					
BOLT LIST:-											
BOLT \ STUD	BOLT DESCRIPTION			QTY/ONE	QTY/ALL	FINISH	REMARKS				
BOLT	B1N1W16 × 40 A307			4	4						

ANCILLARY CATEGORY
FW-J1 TO J4

GA & IFC DRAWINGS REFERENCE	REV.
AD282-732-C-33226,27,28,29,30,31	4
AD282-732-C-33233,34,35,33499,33500	4
AD282-732-C-34337	2
AD282-732-C-34300	2

- NOTES :**
- 1-ALL DIMENSIONS ARE GIVEN IN MILLIMETERS (U.N.O.).
 - 2-  DENOTES ASSEMBLY ORIENTATION MARK.
 - 3-DON'T SCALE THE DRAWING. FOLLOW THE WRITTEN DIMENSIONS.
 - 4- FINISH AS PER PROJECT SPEC.
 - 5- STRUCTURAL STEELWORK SHALL BE IN ACCORDANCE WITH PROJECT SPECIFICATIONS AD282-732-G-03520 & AD282-732-G-03527
 - 6-WHEREVER THERE IS NO ACCESS FOR FILLET WELDING TO BE REPLACED BY FULL PENETRATION BUTT WELDING
 - 7-FOR CJP WELD MARKED LOCATIONS FOLLOW THIS DETAIL
 - 8-ALL WELDS TO BE 6mm FILLET WELD U.N.O.

GRID LOCATION	
EL +110.048	2'-1"/F

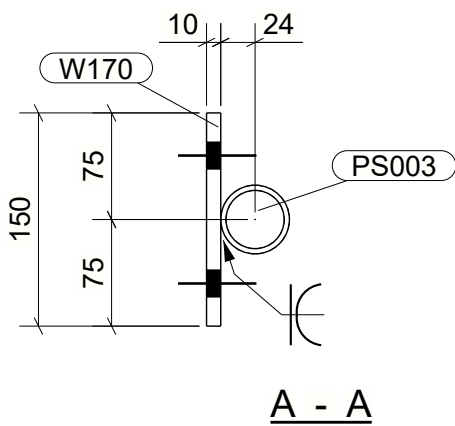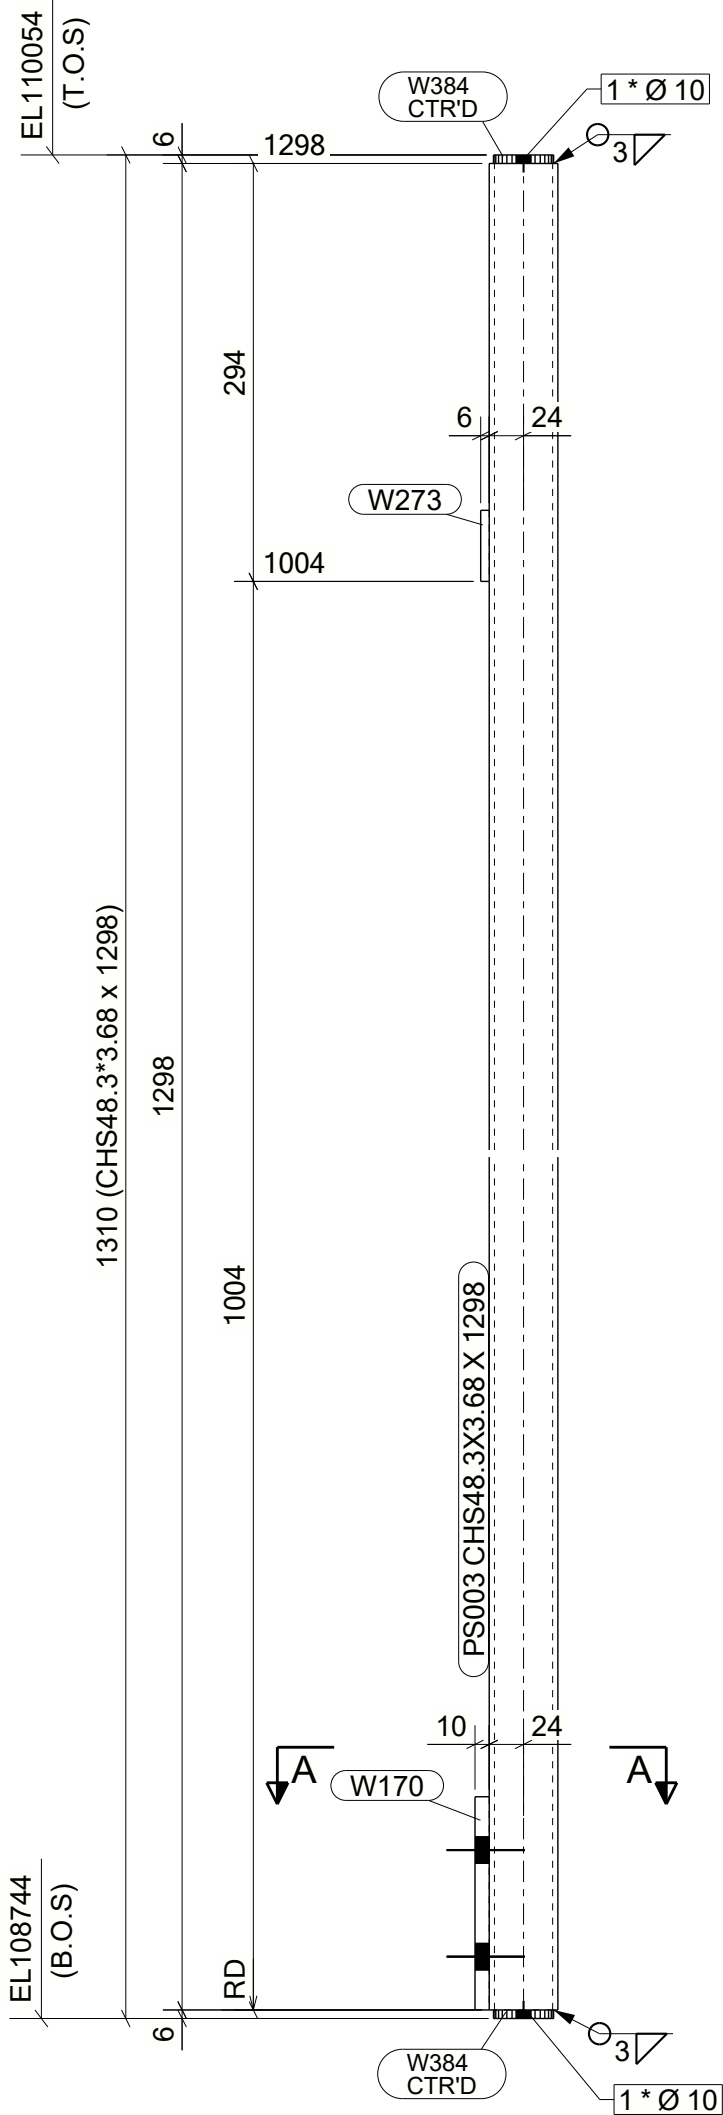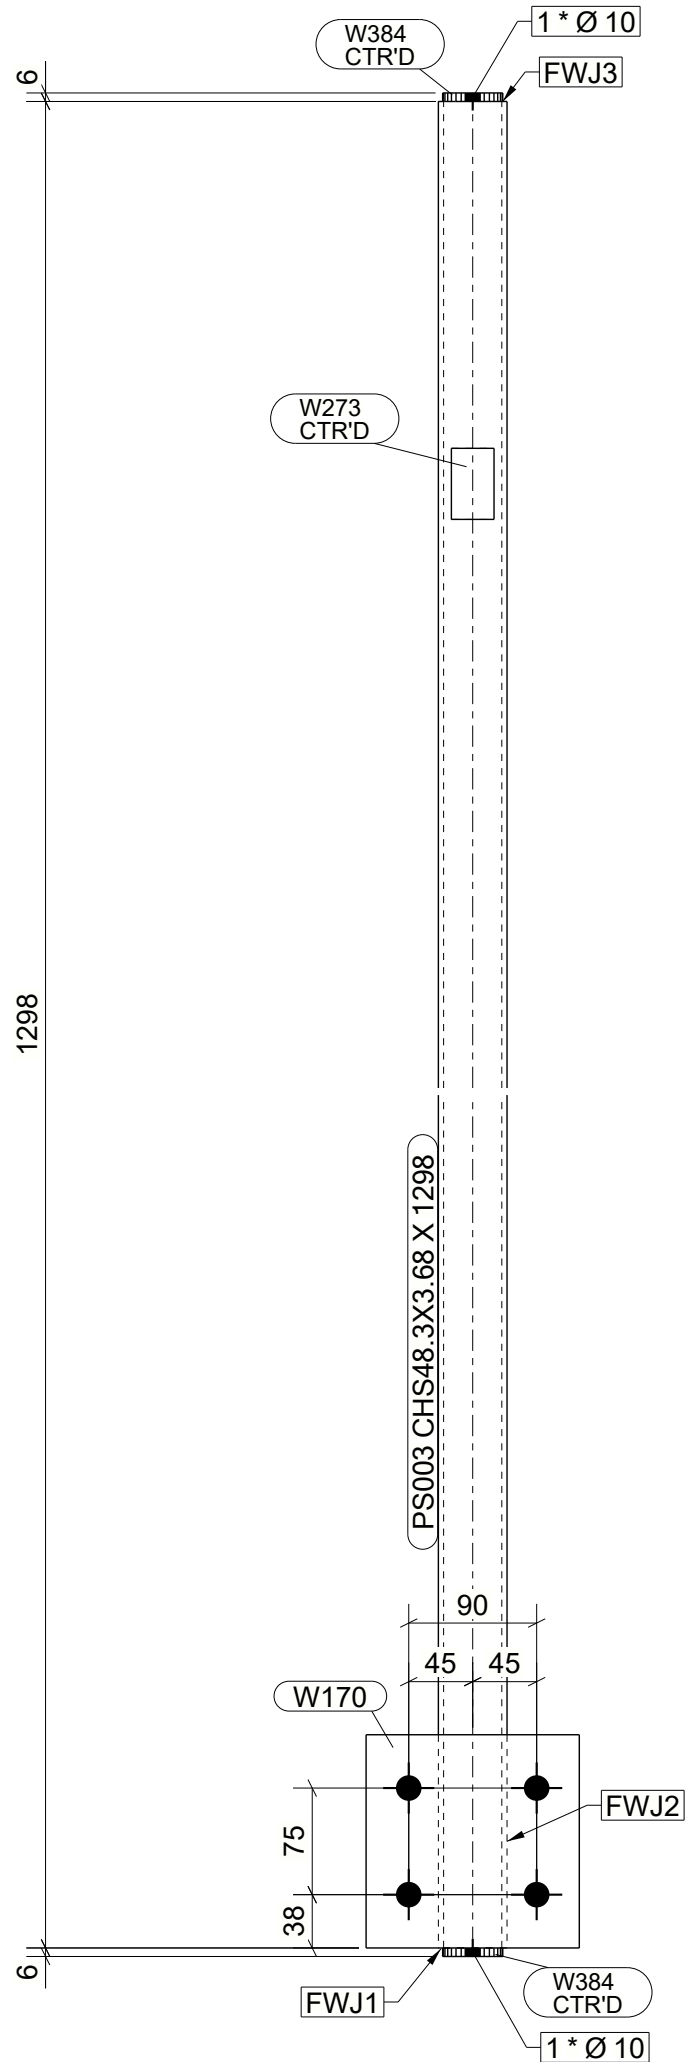

DRAWING NO. : 2307087-STL-732-02-PS003										REV.: 00		
ERECTION MARK : 2307087-STL-732-02-PS003			DESCRIPTION : POST				COLOR CODE : 10 B 15			QTY : 1		NOS
HOLD:		TYPE: W		TREAT: GPN		COST CODE: 3.01			REMARKS:			
LENGTH: 1310		WIDTH: 150		HEIGHT: 58		TOTAL S.AREA: 0.3			(M2)			
POSITION NO.	QTY PER ASSLY	SECTION	LENGTH	UNIT WEIGHT (KG)	TOTAL WIEGHT (KG)		GRADE	REVISION	PART ID	TREATMENT	REMARKS	
					QTY	WEIGHT						
PS003	1	CHS48.3X3.68	1298	5.230	1	5.23	A53-GR.B	1	MM	GPN		
W170	1	PL10X150	150	1.766	1	1.77	S355JR	1	WI			
W273	1	PL6X30	50	0.013	1	0.01	Neoprene	1	WI		NEOPRENE	
W384	2	PL6X42	42	0.066	2	0.13	S355JR	1	WI			
					UNIT WEIGHT		7.14					
					TOTAL WEIGHT		7.14					
BOLT LIST:-												
BOLT \ STUD		BOLT DESCRIPTION			QTY/ONE	QTY/ALL	FINISH	REMARKS				
BOLT		B1N1W16 × 45 A307			4	4						


ANCILLARY CATEGORY
FW-J1 TO J3

GA & IFC DRAWINGS REFERENCE	REV.
AD282-732-C-33226,27,28,29,30,31	4
AD282-732-C-33233,34,35,33499,33500	4
AD282-732-C-34337	2
AD282-732-C-34300	2

- NOTES :**
- 1-ALL DIMENSIONS ARE GIVEN IN MILLIMETERS (U.N.O.).
 - 2-  DENOTES ASSEMBLY ORIENTATION MARK.
 - 3-DON'T SCALE THE DRAWING. FOLLOW THE WRITTEN DIMENSIONS.
 - 4- FINISH AS PER PROJECT SPEC.
 - 5- STRUCTURAL STEELWORK SHALL BE IN ACCORDANCE WITH PROJECT SPECIFICATIONS AD282-732-G-03520 & AD282-732-G-03527
 - 6-WHEREVER THERE IS NO ACCESS FOR FILLET WELDING TO BE REPLACED BY FULL PENETRATION BUTT WELDING
 - 7-FOR CJP WELD MARKED LOCATIONS FOLLOW THIS DETAIL

 - 8-ALL WELDS TO BE 6mm FILLET WELD U.N.O.

GRID LOCATION	
EL +110.054	1'-1/B-B'
EL +112.904	<2/C-D
EL +118.661	<2/C-D


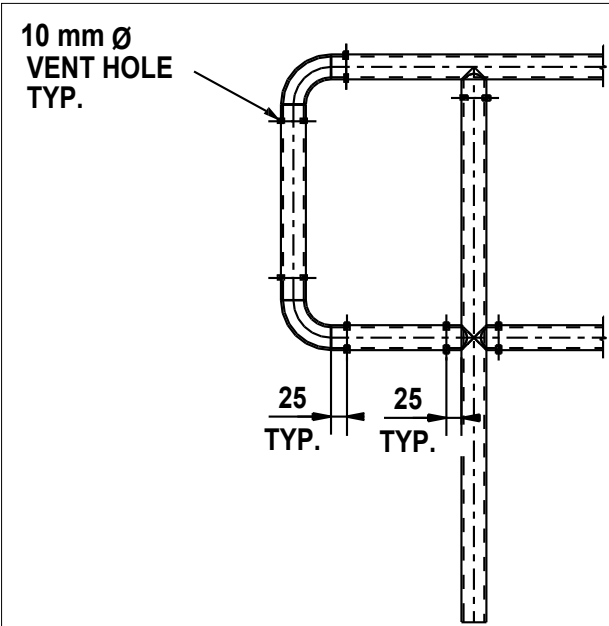


TYPICAL VENT HOLE DETAIL

DRAWING NO. : 2307087-STL-732-02-SG001										REV.: 00							
ERECTION MARK : 2307087-STL-732-02-SG001										DESCRIPTION : SAFETY_GATE		COLOR CODE : 10 B 15		QTY : 3		NOS	
HOLD:		TYPE: W		TREAT: GPN		COST CODE: 4.04				REMARKS:							
LENGTH: 777		WIDTH: 1078		HEIGHT: 86		TOTAL S.AREA: 0.7				(M2)							
POSITION NO.	QTY PER ASSLY	SECTION	LENGTH	UNIT WEIGHT (KG)	TOTAL WIEGHT (KG)		GRADE	REVISION	PART ID	TREATMENT	REMARKS						
					QTY	WEIGHT											
SG001	1	CHS48.3X3.68	488	1.965	3	5.89	A53-GR.B	1	MM	GPN							
W022	2	CHS48.3X3.68	127	0.357	6	2.14	A53-GR.B	1	WI		ELBOW						
W186	1	FLT6X150	650	4.592	3	13.78	S275JR	1	WI								
W267	2	CHS48.3X3.68	981	3.952	6	23.71	A53-GR.B	1	WI								
W270	1	PIPE3/4SCH40	50	0.078	3	0.24	A53-GR.B	1	WI								
W272	1	FLT6X50	73	0.172	3	0.52	S275JR	1	WI								
W284	1	CHS48.3X3.68	602	2.284	3	6.85	A53-GR.B	1	WI								
W285	1	FLT6X50	55	0.130	3	0.39	S275JR	1	WI								
W300	1	ROD16	150	0.234	3	0.70	8.8	1	WI		WELDABLE PIN						
W384	2	PL6X42	42	0.066	6	0.39	S355JR	1	WI								
					UNIT WEIGHT		18.21										
					TOTAL WEIGHT		54.62										
BOLT LIST:-																	
BOLT \ STUD		BOLT DESCRIPTION		QTY/ONE		QTY/ALL		FINISH		REMARKS							

ANCILLARY CATEGORY


FW- J1 TO J10
CJP- J1 TO J4

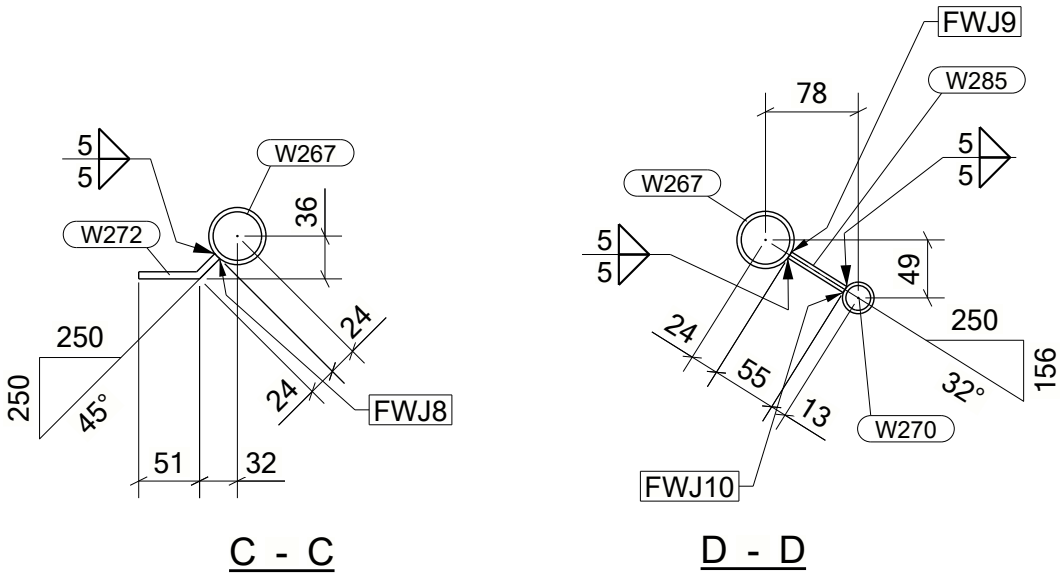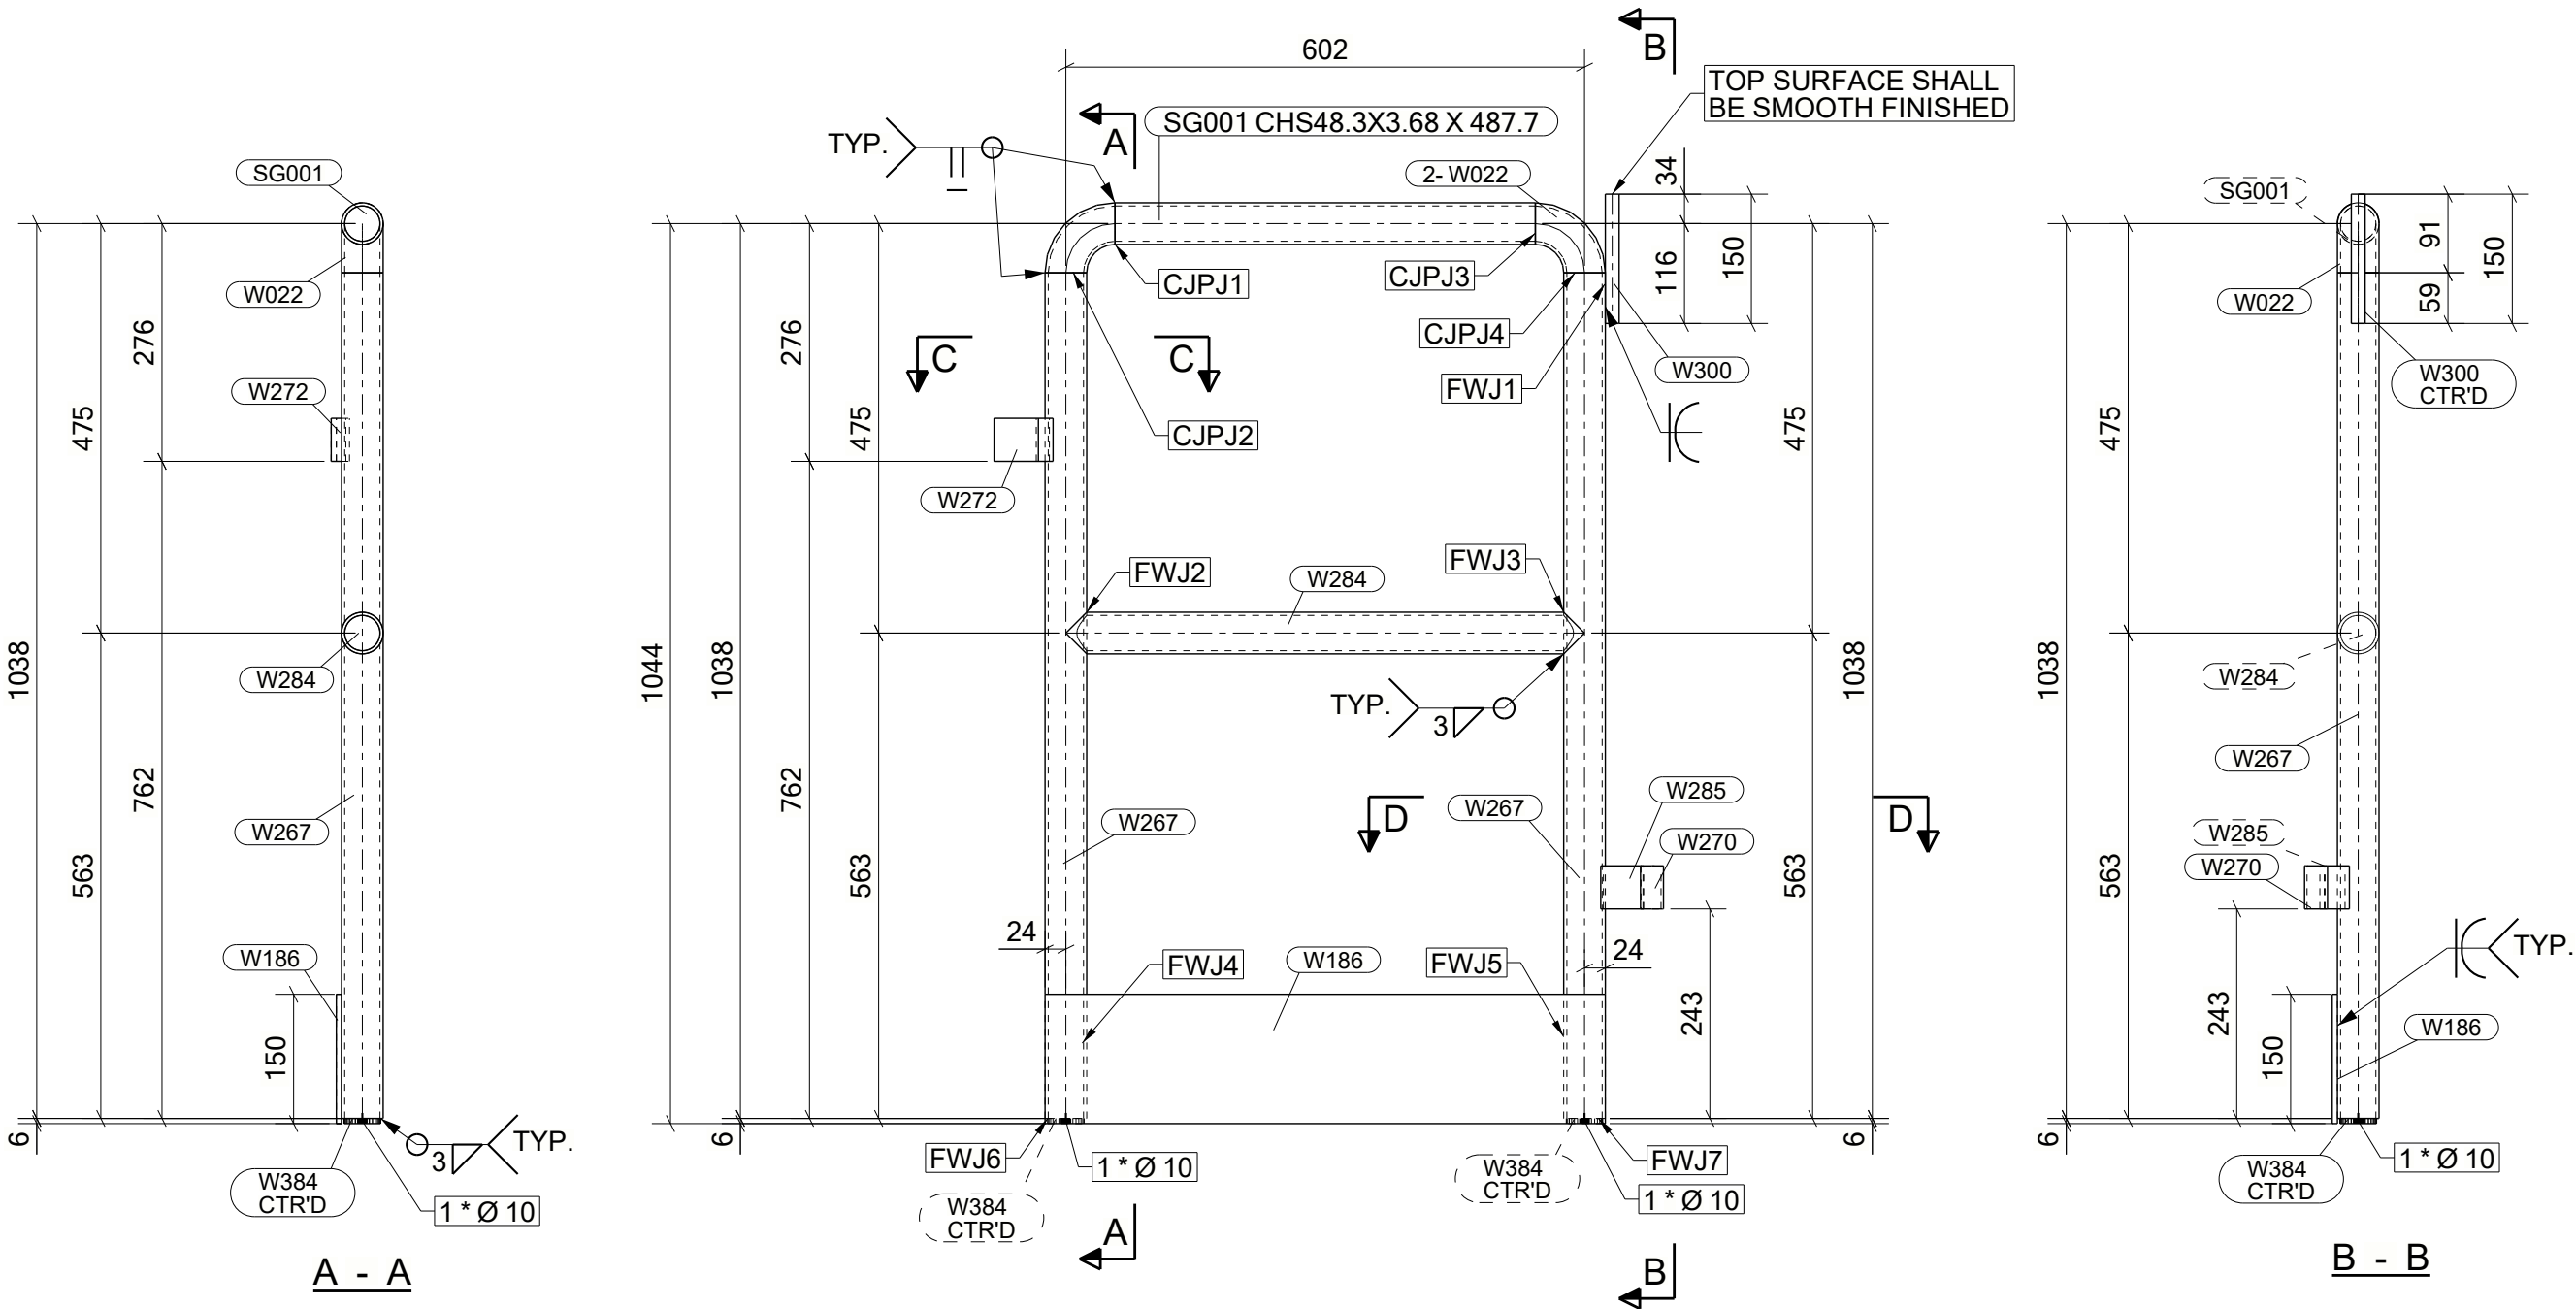

GA & IFC DRAWINGS REFERENCE	REV.
AD282-732-C-33226,27,28,29,30,31	4
AD282-732-C-33233,34,35,33499,33500	4
AD282-732-C-34337	2
AD282-732-C-34300	2

- NOTES :**
- 1-ALL DIMENSIONS ARE GIVEN IN MILLIMETERS (U.N.O.).
 - 2- DENOTES ASSEMBLY ORIENTATION MARK.
 - 3-DON'T SCALE THE DRAWING. FOLLOW THE WRITTEN DIMENSIONS.
 - 4- FINISH AS PER PROJECT SPEC.
 - 5- STRUCTURAL STEELWORK SHALL BE IN ACCORDANCE WITH PROJECT SPECIFICATIONS AD282-732-G-03520 & AD282-732-G-03527
 - 6-WHEREVER THERE IS NO ACCESS FOR FILLET WELDING TO BE REPLACED BY FULL PENETRATION BUTT WELDING
 - 7-FOR CJP WELD MARKED LOCATIONS FOLLOW THIS DETAIL
 - 8-ALL WELDS TO BE 6mm FILLET WELD U.N.O.

GRID LOCATION	
EL +110.054	2'-1"/F


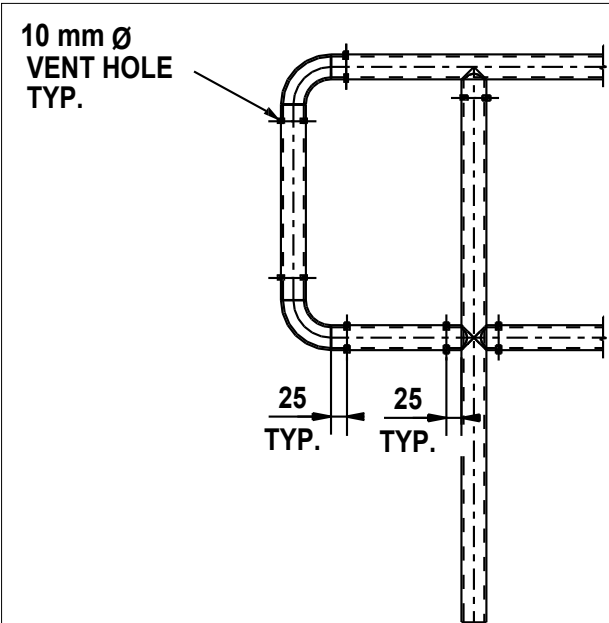


TYPICAL VENT HOLE DETAIL

DRAWING NO. : 2307087-STL-732-02-SG007								REV.: 00				
ERECTION MARK : 2307087-STL-732-02-SG007			DESCRIPTION : SAFETY_GATE			COLOR CODE : 10 B 15			QTY : 1		NOS	
HOLD:		TYPE: W		TREAT: GPN		COST CODE: 4.04			REMARKS:			
LENGTH: 777		WIDTH: 1078		HEIGHT: 86		TOTAL S.AREA: 0.7			(M2)			
POSITION NO.	QTY PER ASSLY	SECTION	LENGTH	UNIT WEIGHT (KG)	TOTAL WIEGHT (KG)		GRADE	REVISION	PART ID	TREATMENT	REMARKS	
					QTY	WEIGHT						
SG007	1	CHS48.3X3.68	488	1.965	1	1.96	A53-GR.B	1	MM	GPN		
W022	2	CHS48.3X3.68	127	0.357	2	0.71	A53-GR.B	1	WI		ELBOW	
W186	1	FLT6X150	650	4.592	1	4.59	S275JR	1	WI			
W267	2	CHS48.3X3.68	981	3.952	2	7.90	A53-GR.B	1	WI			
W270	1	PIPE3/4SCH40	50	0.078	1	0.08	A53-GR.B	1	WI			
W272	1	FLT6X50	73	0.172	1	0.17	S275JR	1	WI			
W284	1	CHS48.3X3.68	602	2.284	1	2.28	A53-GR.B	1	WI			
W285	1	FLT6X50	55	0.129	1	0.13	S275JR	1	WI			
W300	1	ROD16	150	0.234	1	0.23	8.8	1	WI		WELDABLE PIN	
W384	2	PL6X42	42	0.066	2	0.13	S355JR	1	WI			
					UNIT WEIGHT		18.20					
					TOTAL WEIGHT		18.20					
BOLT LIST:-												
BOLT \ STUD		BOLT DESCRIPTION		QTY/ONE		QTY/ALL		FINISH		REMARKS		

ANCILLARY CATEGORY



FW- J1 TO J10
CJP- J1 TO J4

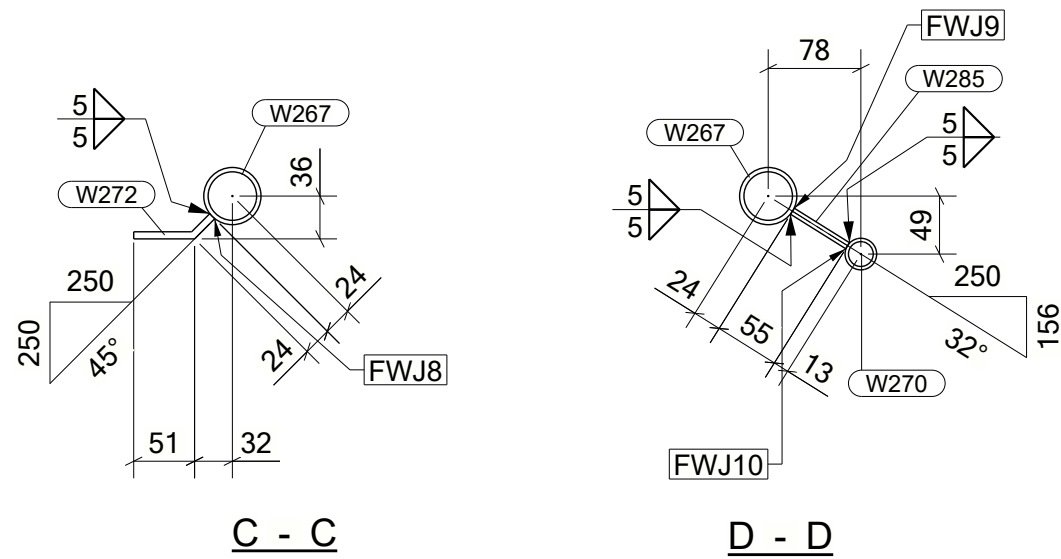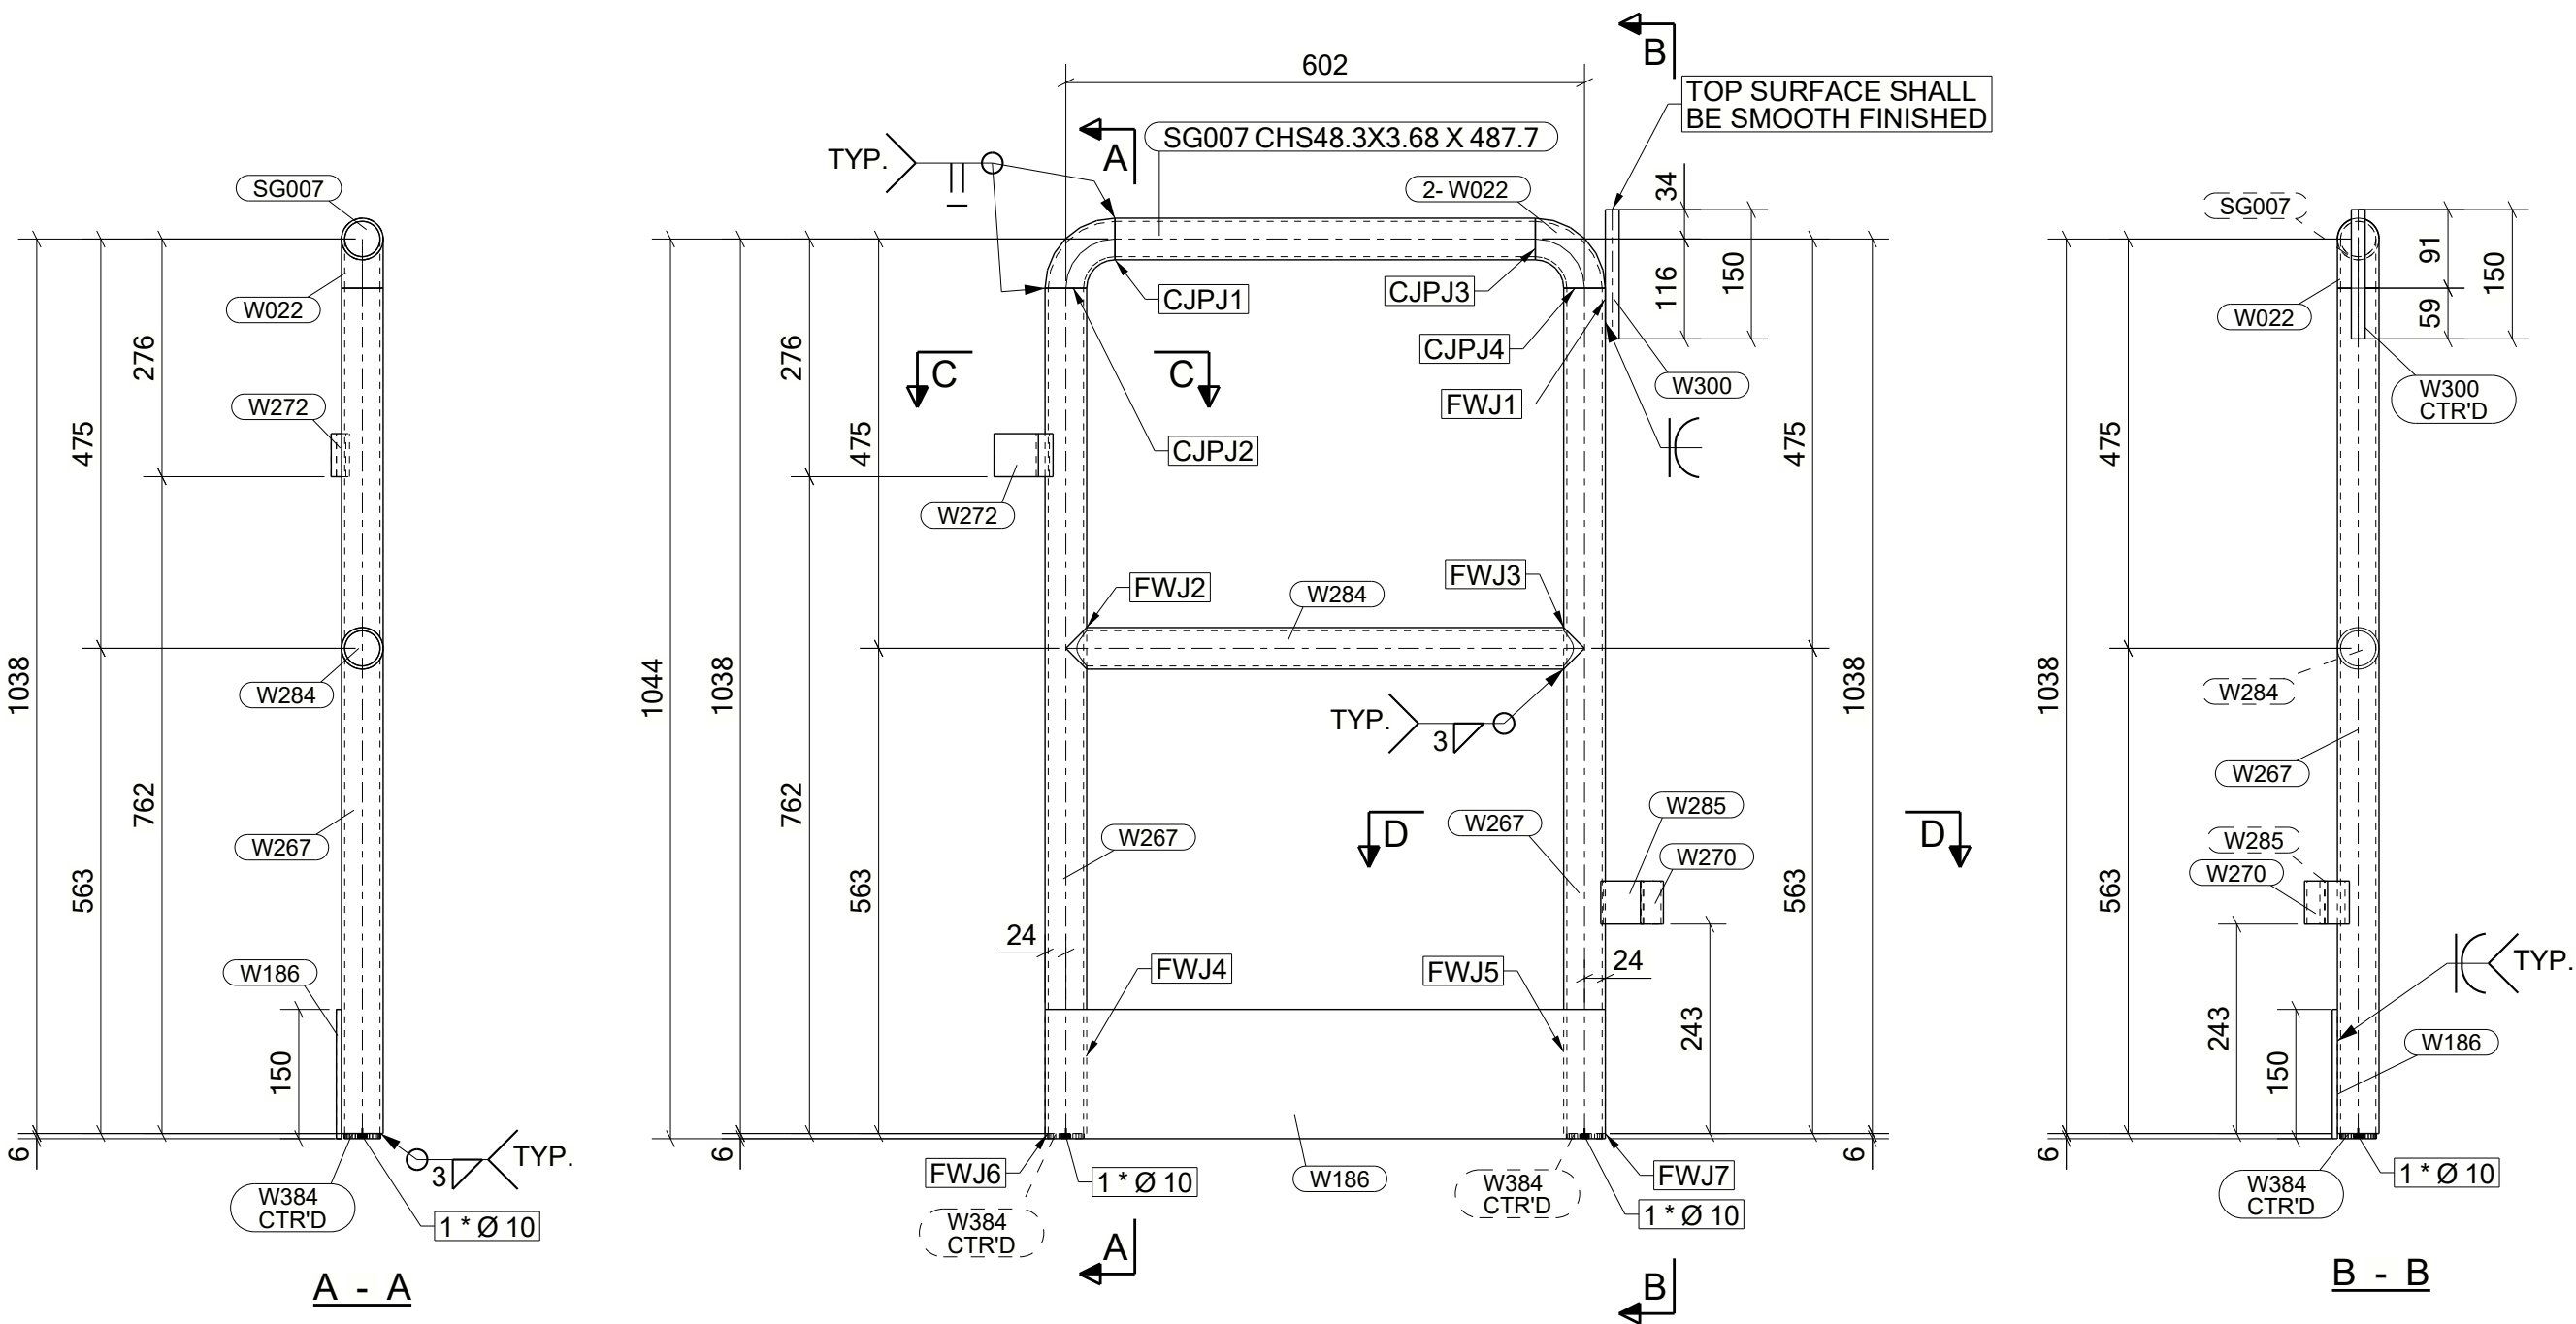

GA & IFC DRAWINGS REFERENCE	REV.
AD282-732-C-33226,27,28,29,30,31	4
AD282-732-C-33233,34,35,33499,33500	4
AD282-732-C-34337	2
AD282-732-C-34300	2

- NOTES :**
- 1-ALL DIMENSIONS ARE GIVEN IN MILLIMETERS (U.N.O.).
 - 2- DENOTES ASSEMBLY ORIENTATION MARK.
 - 3-DON'T SCALE THE DRAWING. FOLLOW THE WRITTEN DIMENSIONS.
 - 4- FINISH AS PER PROJECT SPEC.
 - 5- STRUCTURAL STEELWORK SHALL BE IN ACCORDANCE WITH PROJECT SPECIFICATIONS AD282-732-G-03520 & AD282-732-G-03527
 - 6-WHEREVER THERE IS NO ACCESS FOR FILLET WELDING TO BE REPLACED BY FULL PENETRATION BUTT WELDING
 - 7-FOR CJP MARKED LOCATIONS FOLLOW THIS DETAIL
 - 8-ALL WELDS TO BE 6mm FILLET WELD U.N.O.




GRID LOCATION	
EL +113.750	732/02-732/01/732G-1

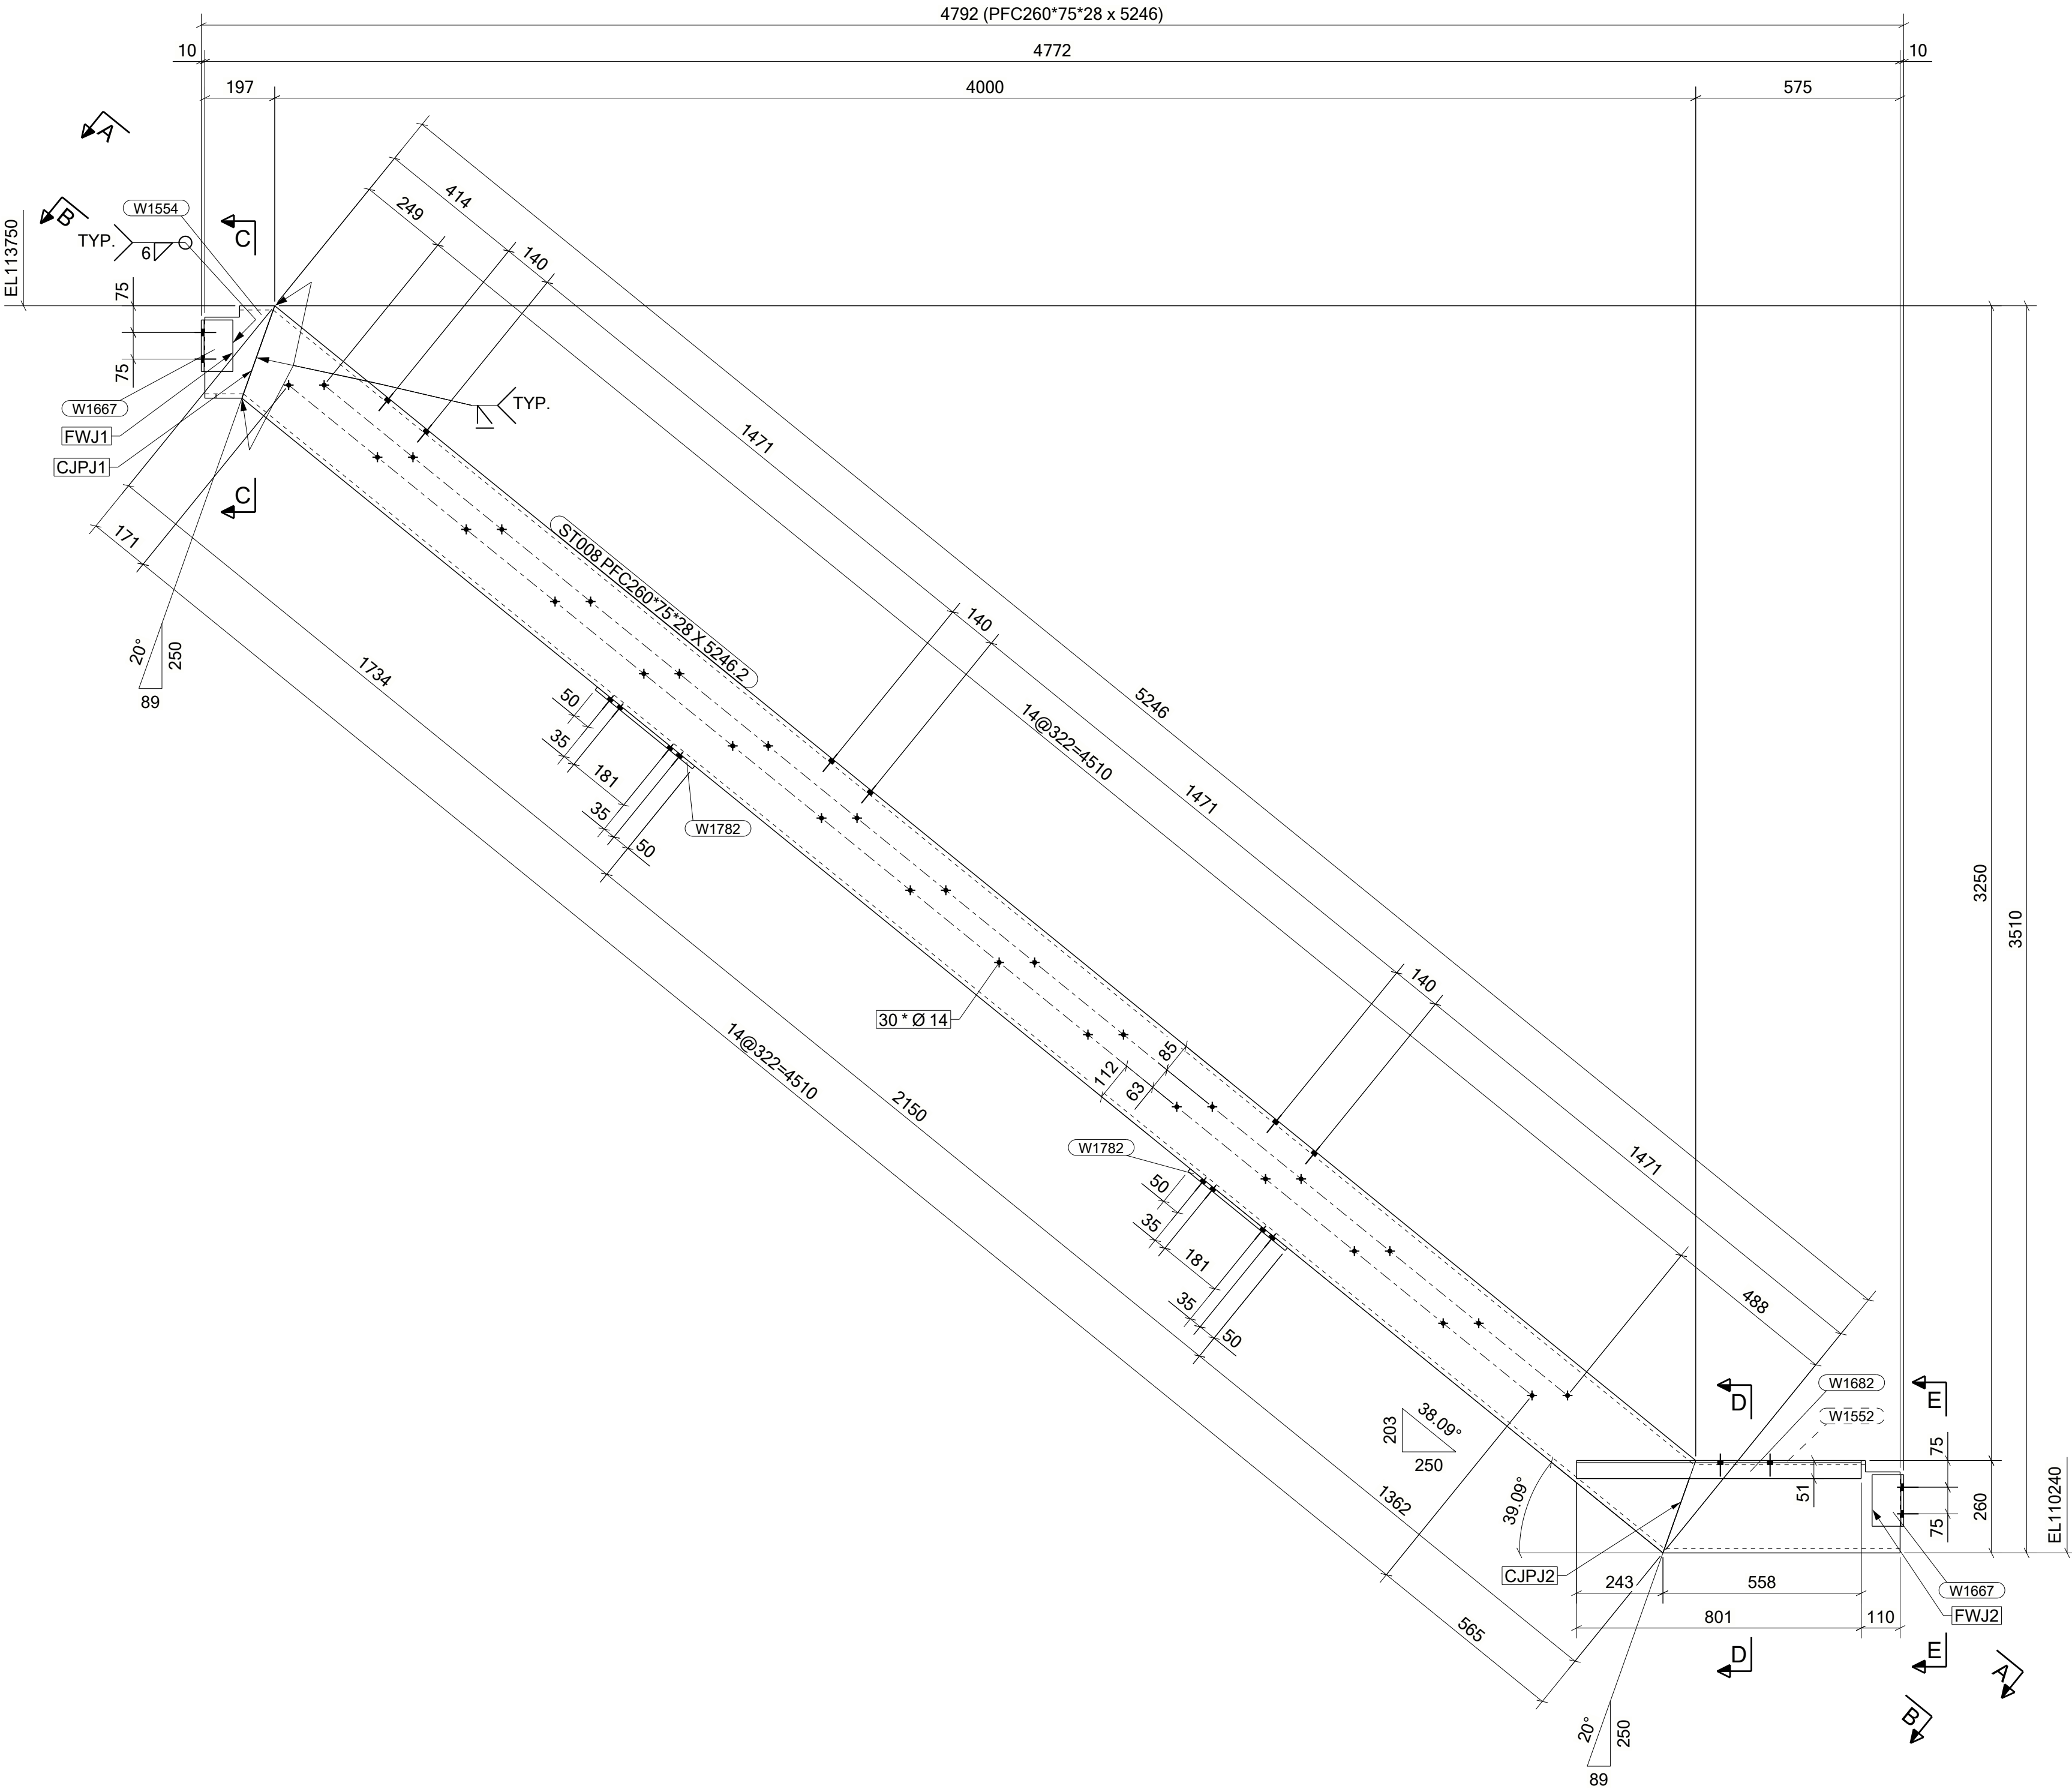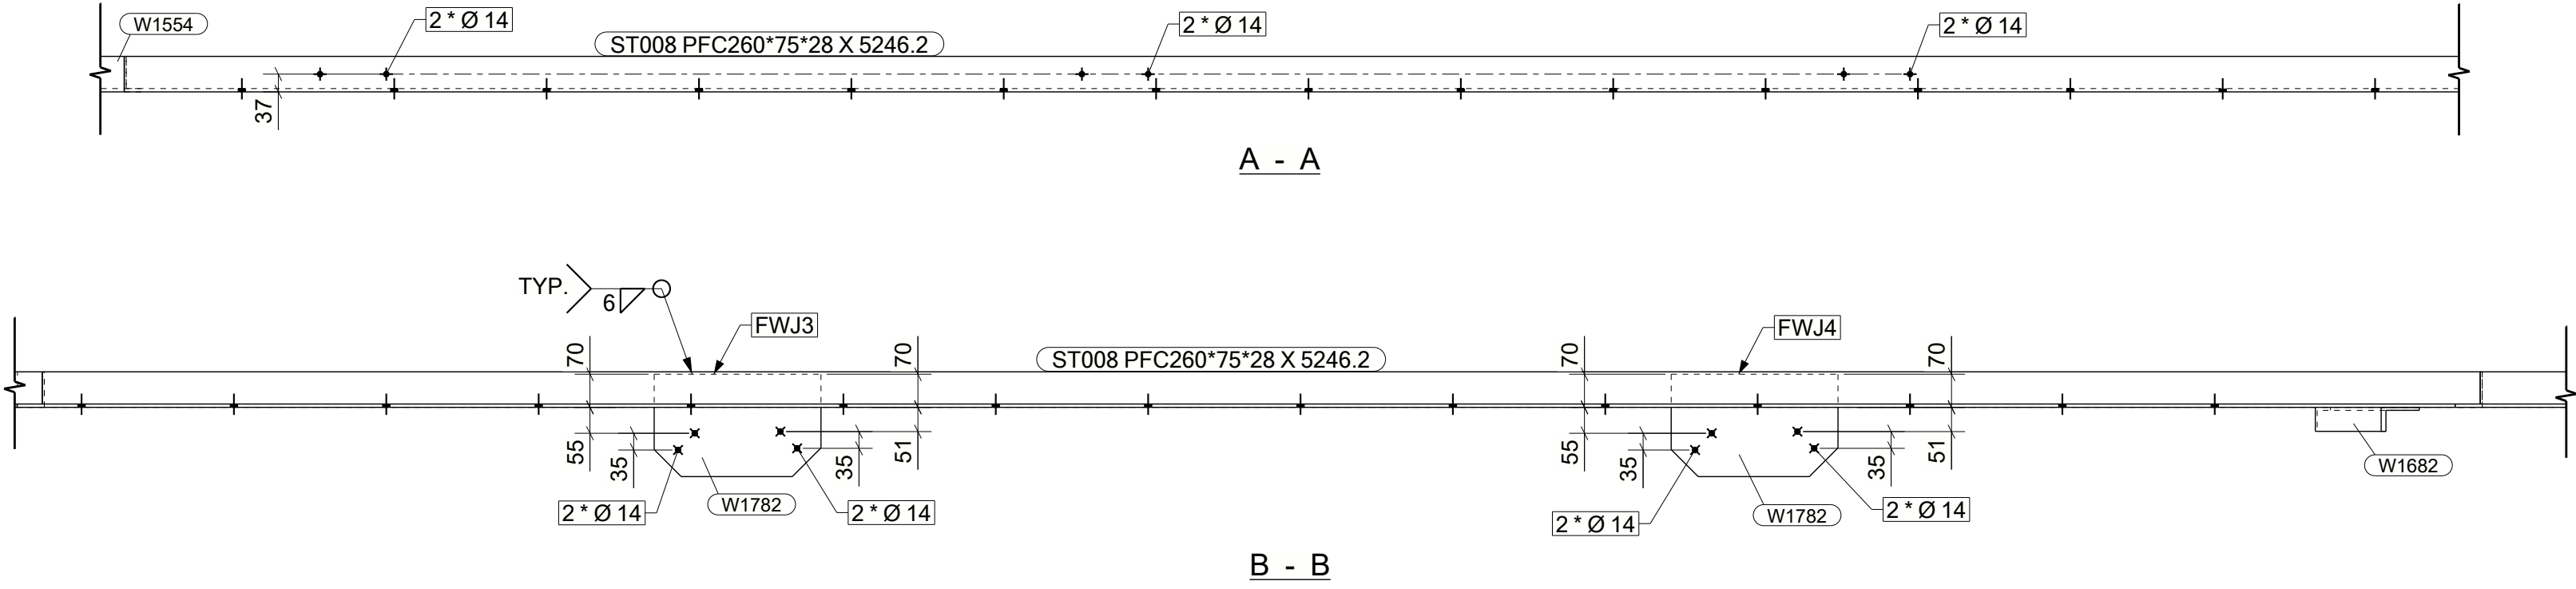


DRAWING NO. : 2307033-732-PR-10-ST008										REV.: 00							
ERECTION MARK : 2307033-732-PR-10-ST008										DESCRIPTION : STRINGER		COLOR CODE : 10 B 15		QTY : 1		NOS	
HOLD:		TYPE: W		TREAT: PN		COST CODE: 1.01				REMARKS:							
LENGTH: 5900		WIDTH: 221		HEIGHT: 664		TOTAL S.AREA: 5.4				(M2)							
POSITION NO.	QTY PER ASSLY	SECTION	LENGTH	UNIT WEIGHT (KG)	TOTAL WEIGHT (KG)		GRADE	REVISION	PART ID	TREATMENT	REMARKS						
					QTY	WEIGHT											
ST008	1	PFC260*75*28	5246	144.551	1	144.55	S275JR	1	MM	PN							
W1552	1	PFC260*75*28	668	18.396	1	18.40	S275JR	1	WI								
W1554	1	PFC260*75*28	197	5.421	1	5.42	S275JR	1	WI								
W1667	2	L3-1/2X3-1/2X5/16	145	1.542	2	3.08	A572-GR.50	1	WI								
W1682	1	L2X2X1/4	801	3.831	1	3.83	A572-GR.50	1	WI								
W1782	2	PL10X216	353	5.717	2	11.43	S355JR	1	WI								
					UNIT WEIGHT												
					TOTAL WEIGHT												
					186.72												
					186.72												
BOLT LIST:-																	
BOLT \ STUD																	
BOLT DESCRIPTION			QTY/ONE		QTY/ALL		FINISH		REMARKS								
B1N1W12 X 35 A307			1		30												
B1N1W16 X 50 ASTM F3125 Gr A325M			2		4												

SECONDARY CATEGORY


FW-J1 TO J5
CJP-J1 TO J2

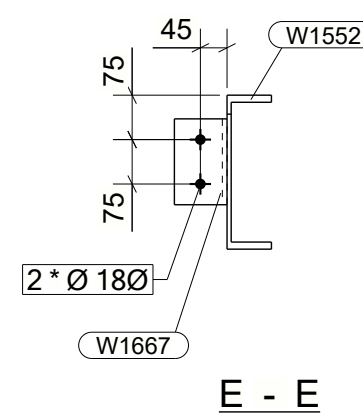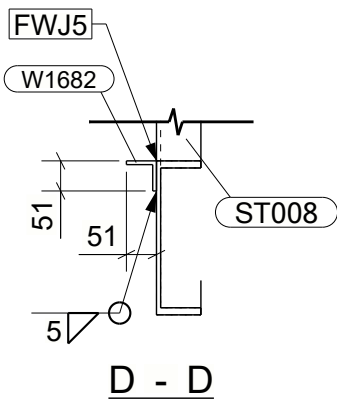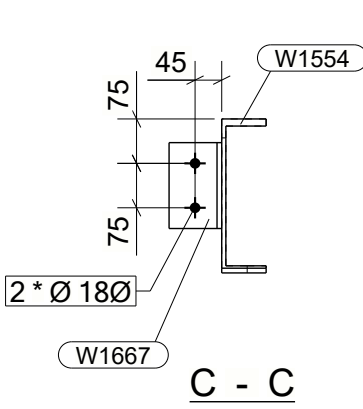

GA & IFC DRAWINGS REFERENCE	REV.
AD282-732-C-33158-61	6
AD282-732-C-33170-73.33539	6
AD282-732-C-34311	2
AD282-732-C-34274	2

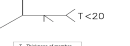
- NOTES :**
- 1-ALL DIMENSIONS ARE GIVEN IN MILLIMETERS (U.N.O.).
 - 2-  DENOTES ASSEMBLY ORIENTATION MARK.
 - 3-DON'T SCALE THE DRAWING. FOLLOW THE WRITTEN DIMENSIONS.
 - 4- FINISH AS PER PROJECT SPEC.
 - 5- STRUCTURAL STEELWORK SHALL BE IN ACCORDANCE WITH PROJECT SPECIFICATIONS AD282-732-G-03520 & AD282-732-G-03527
 - 6-WHEREVER THERE IS NO ACCESS FOR FILLET WELDING TO BE REPLACED BY FULL PENETRATION BUTT WELDING
 - 7-FOR CIP WELD MARKED LOCATIONS FOLLOW THIS DETAIL 
 - 8-ALL WELDS TO BE 6mm FILLET WELD U.N.O.

GRID LOCATION	
EL +117.150	732/02-732/01/732F

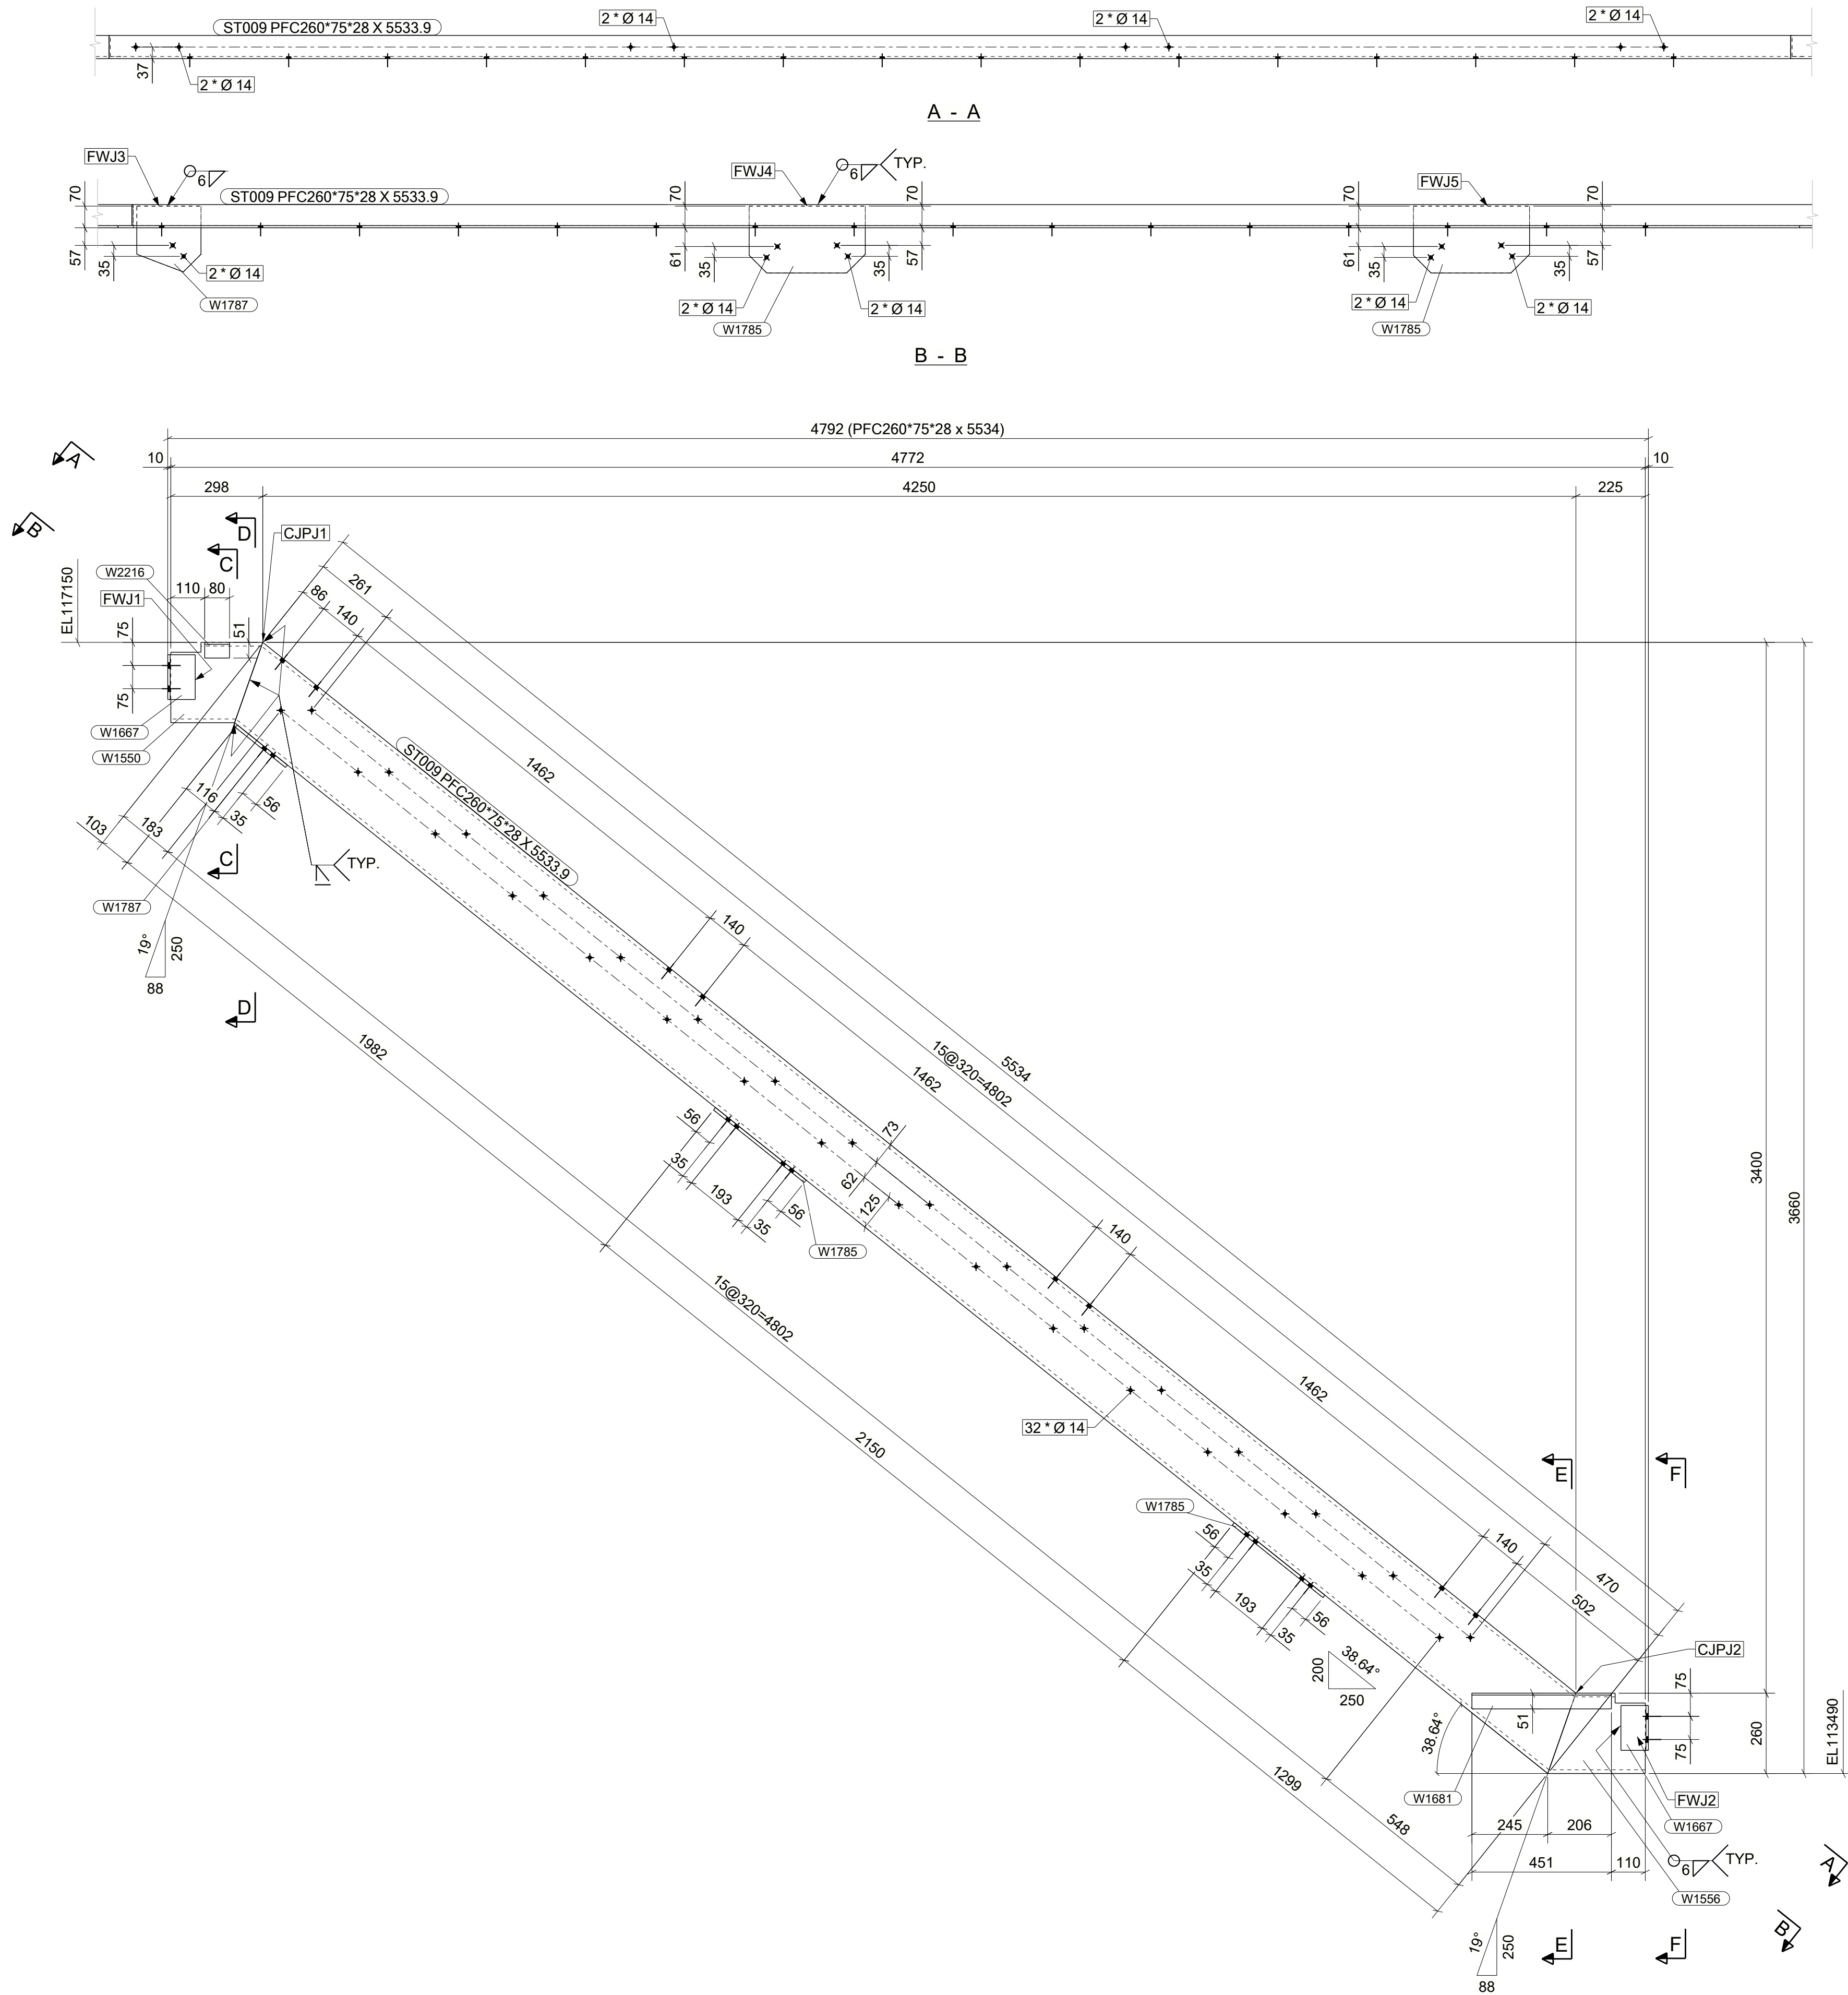

DRAWING NO. : 2307033-732-PR-10-ST009										REV.: 00	
ERECTION MARK : 2307033-732-PR-10-ST009										NOS	
DESCRIPTION : STRINGER										COLOR CODE : 10 B 15	
HOLD: TYPE: W TREAT: PN										COST CODE: 1.01	
REMARKS:										QTY : 1	
LENGTH: 5996 WIDTH: 221 HEIGHT: 504										TOTAL S.AREA: 5.5 (M2)	
POSITION NO.	QTY PER ASS'Y	SECTION	LENGTH	UNIT WEIGHT (KG)	TOTAL WEIGHT (KG)		GRADE	REVISION	PART ID	TREATMENT	REMARKS
					QTY	WEIGHT					
ST009	1	PFC260*75*28	5534	152.477	1	152.48	S275JR	1	MM	PN	
W1550	1	PFC260*75*28	298	8.198	1	8.20	S275JR	1	WI		
W1556	1	PFC260*75*28	316	8.699	1	8.70	S275JR	1	WI		
W1667	2	L3-1/2X3-1/2X5/16	145	1.542	2	3.08	A572-GR.50	1	WI		
W1681	1	L2X2X1/4	451	2.158	1	2.16	A572-GR.50	1	WI		
W1785	2	PL10X216	376	6.111	2	12.22	S355JR	1	WI		
W1787	1	PL10X213	208	3.005	1	3.00	S355JR	1	WI		
W2216	1	L2X2X1/4	80	0.384	1	0.38	A572-GR.50	1	WI		
					UNIT WEIGHT		190.23				
					TOTAL WEIGHT		190.23				
BOLT LIST:-											
BOLT \ STUD		BOLT DESCRIPTION		QTY/ONE		QTY/ALL		FINISH		REMARKS	
BOLT		B1N1W12 X 35 A307		1		32					
BOLT		B1N1W16 X 50 ASTM F3125 Gr A325M		2		4					

SECONDARY CATEGORY
FW-J1 TO J8
CJP- J1 TO J2

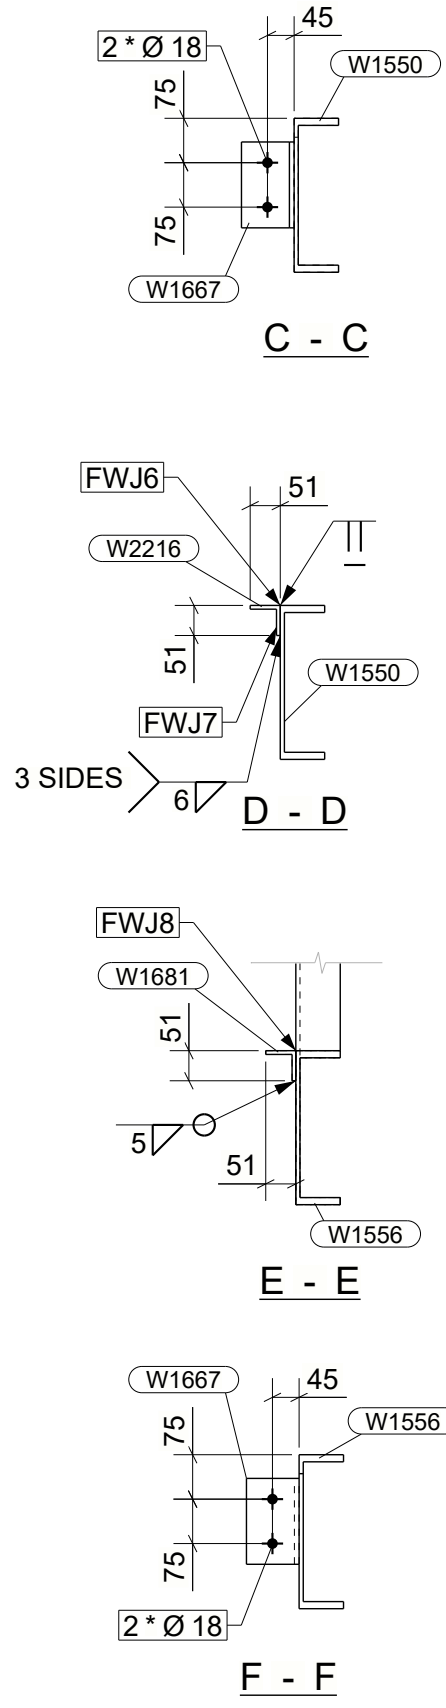

GA & IFC DRAWINGS REFERENCE	REV.
AD282-732-C-33158-61	6
AD282-732-C-33170-73.33539	6
AD282-732-C-34311	2
AD282-732-C-34274	2

- NOTES :**
- 1-ALL DIMENSIONS ARE GIVEN IN MILLIMETERS (U.N.O.).
 - 2-  DENOTES ASSEMBLY ORIENTATION MARK.
 - 3-DON'T SCALE THE DRAWING. FOLLOW THE WRITTEN DIMENSIONS.
 - 4- FINISH AS PER PROJECT SPEC.
 - 5- STRUCTURAL STEELWORK SHALL BE IN ACCORDANCE WITH PROJECT SPECIFICATIONS AD282-732-G-03520 & AD282-732-G-03527
 - 6- WHEREVER THERE IS NO ACCESS FOR FILLET WELDING TO BE REPLACED BY FULL PENETRATION BUTT WELDING
 - 7-FOR CIP WELD MARKED LOCATIONS FOLLOW THIS DETAIL
 - 8-ALL WELDS TO BE 6mm FILLET WELD U.N.O.